

SCALE - 1:100

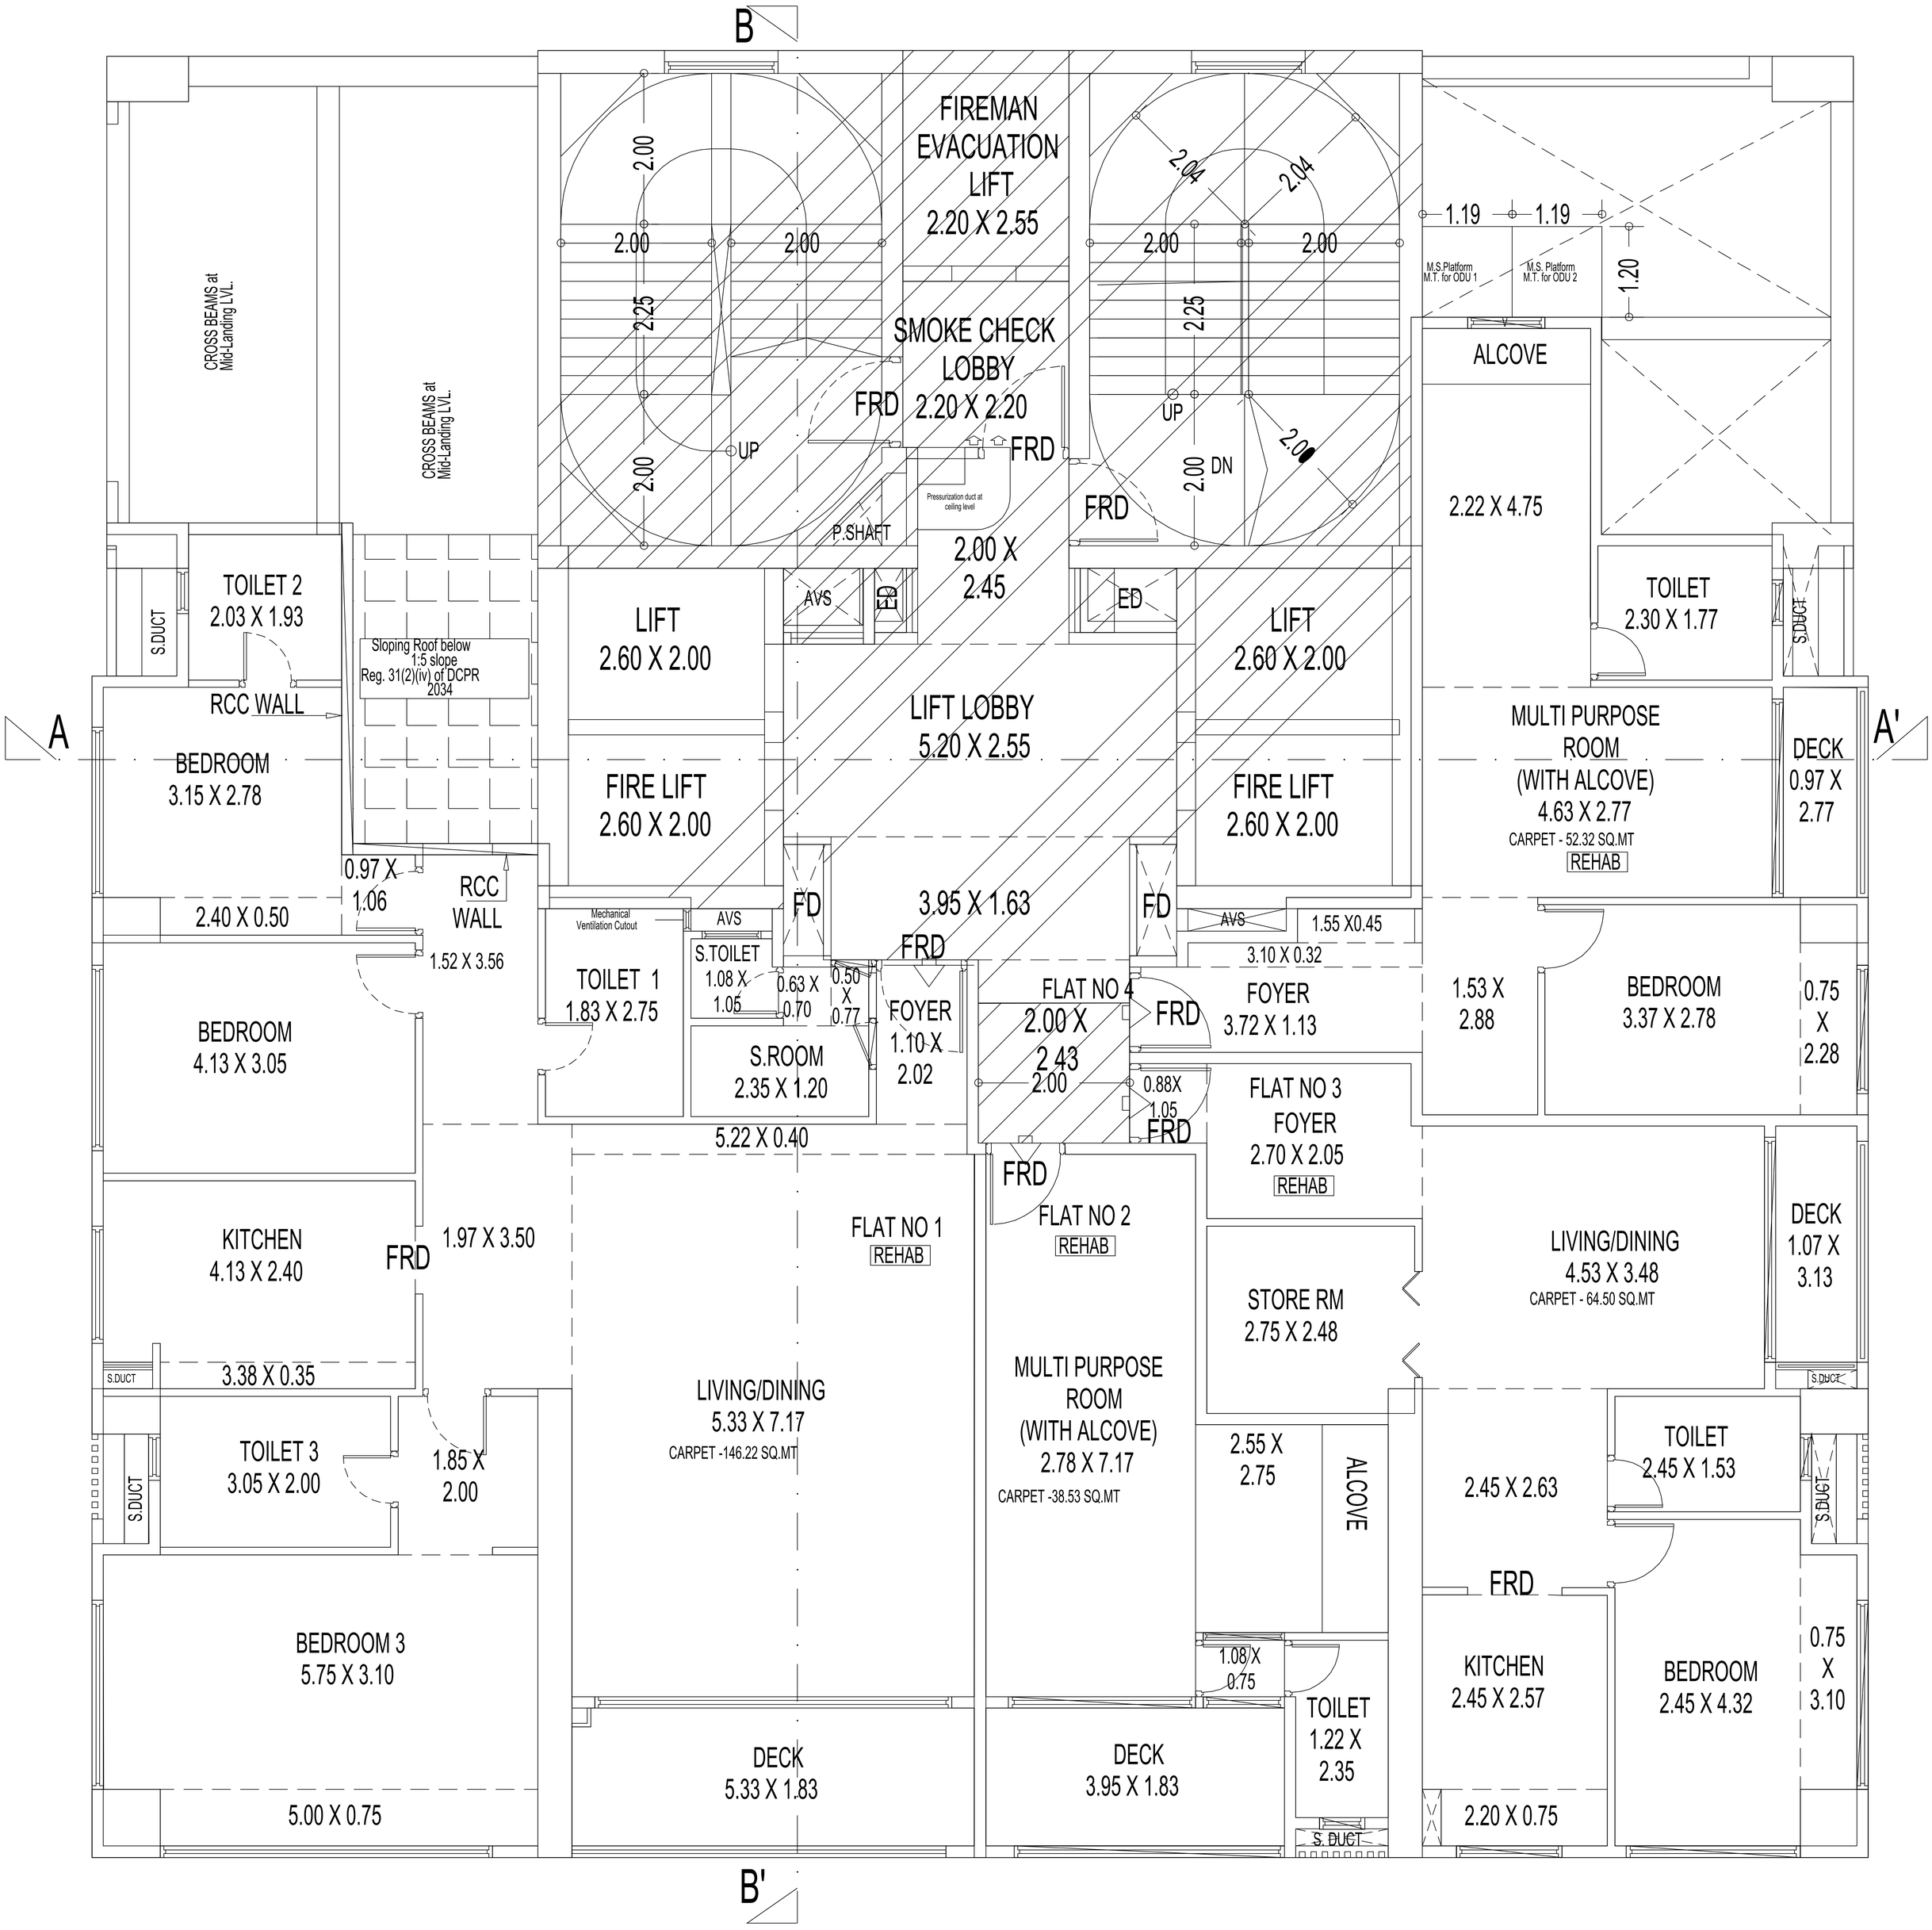

12TH FLOOR PLAN

SCALE - 1:100

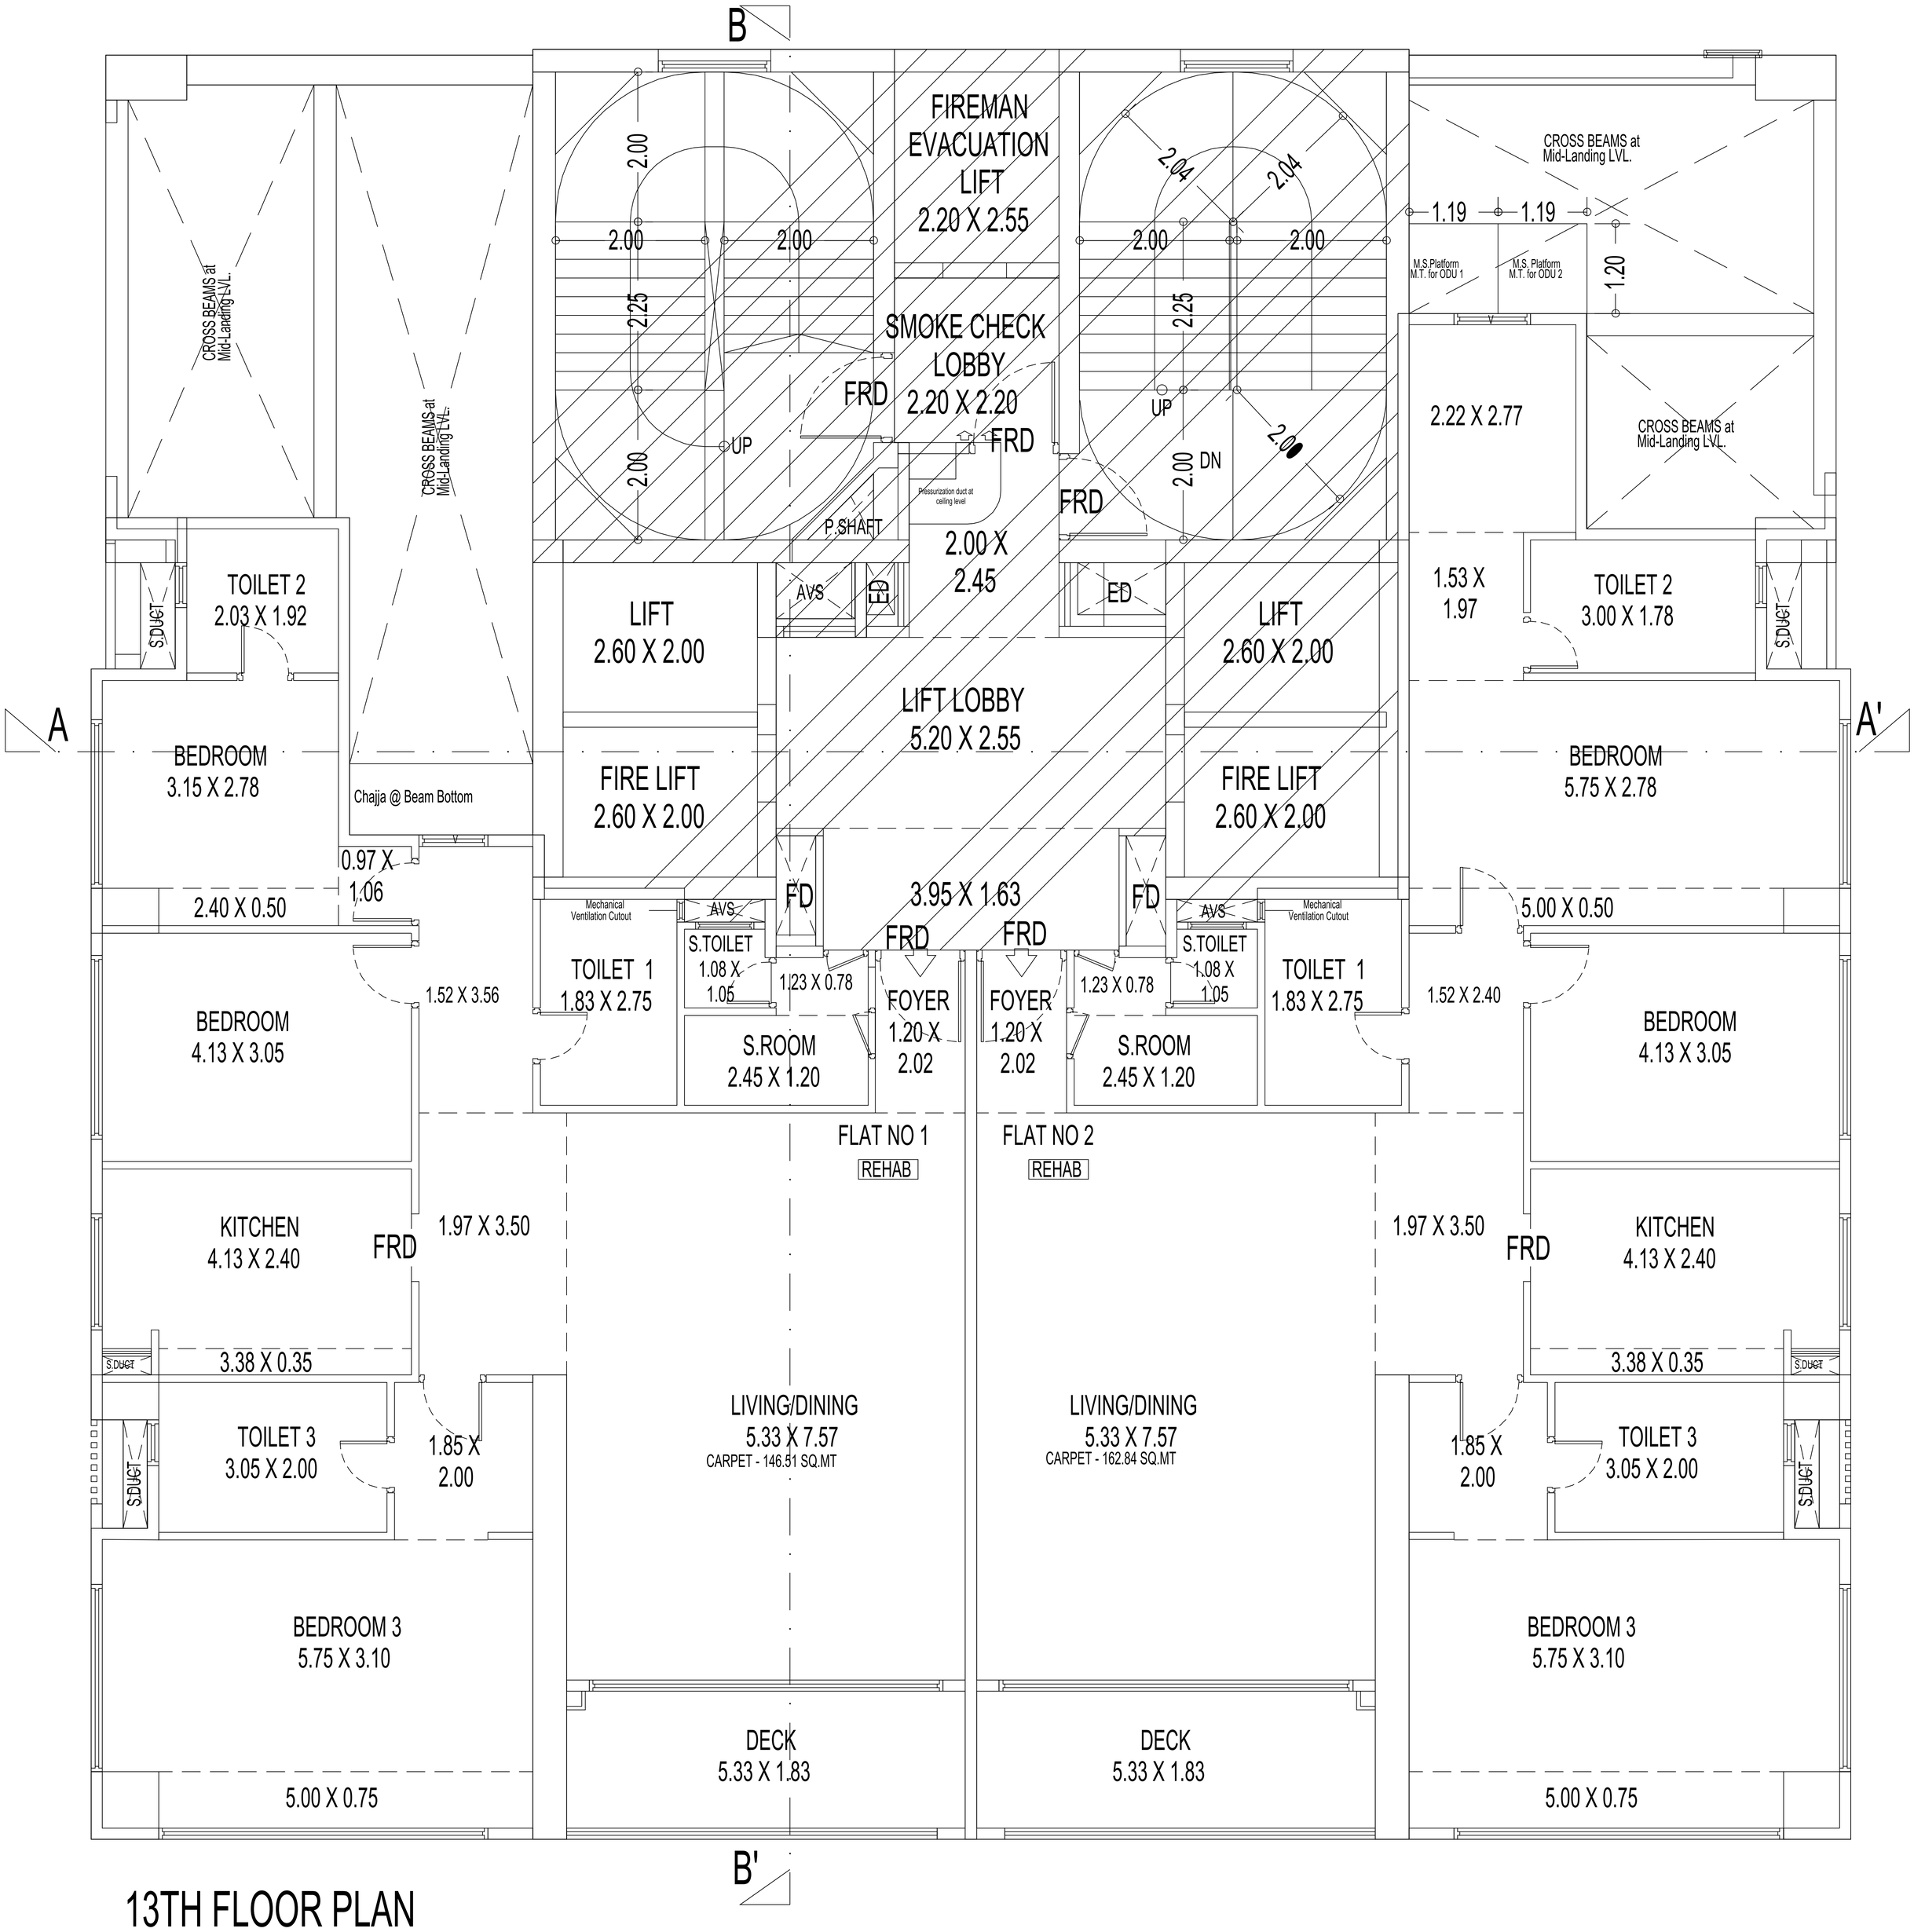

13TH FLOOR PLAN

SCALE - 1:100

B

A

A'

B'

FIREMAN EVACUATION LIFT 2.20 X 2.55

SMOKE CHECK LOBBY 2.20 X 2.20

FRD

UP

DN

2.00

2.25

2.04

Pressurization duct at ceiling level

P.SHAFT

2.00 X 2.45

AVS

ED

FD

LIFT 2.60 X 2.00

LIFT LOBBY 5.20 X 2.55

FIRE LIFT 2.60 X 2.00

3.95 X 1.63

CROSS BEAMS at Mid-Landing LVL.

1.19

1.20

M.S.Platform M.T. for ODU 1

M.S.Platform M.T. for ODU 2

2.22 X 2.77

1.53 X 1.97

TOILET 2 2.03 X 1.92

TOILET 2 3.00 X 1.78

S.DUCT

BEDROOM 3.15 X 2.78

BEDROOM 5.75 X 2.78

Chajja @ Beam Bottom

0.97 X 1.06

2.40 X 0.50

5.00 X 0.50

Mechanical Ventilation Cutout

TOILET 1 1.83 X 2.75

S.TOILET 1.08 X 1.05

1.23 X 0.78

FOYER 1.20 X 2.02

S.ROOM 2.45 X 1.20

1.52 X 3.56

1.52 X 2.40

BEDROOM 4.13 X 3.05

FLAT NO 1

REHAB

FLAT NO 2

REHAB

KITCHEN 4.13 X 2.40

1.97 X 3.50

3.38 X 0.35

TOILET 3 3.05 X 2.00

1.85 X 2.00

LIVING/DINING 5.33 X 7.57

CARPET - 146.51 SQ.MT

CARPET - 162.84 SQ.MT

BEDROOM 3 5.75 X 3.10

DECK 5.33 X 1.83

5.00 X 0.75

B

A

A'

B'

FIREMAN EVACUATION LIFT 2.20 X 2.55

SMOKE CHECK LOBBY 2.20 X 2.20

FRD

UP

DN

2.00

2.25

2.04

Pressurization duct at ceiling level

P.SHAFT

2.00 X 2.45

AVS

ED

FD

LIFT 2.60 X 2.00

LIFT LOBBY 5.20 X 2.55

FIRE LIFT 2.60 X 2.00

3.95 X 1.63

CROSS BEAMS at Mid-Landing LVL.

1.19

1.20

M.S.Platform M.T. for ODU 1

M.S.Platform M.T. for ODU 2

2.22 X 2.77

1.53 X 1.97

TOILET 2 2.03 X 1.92

TOILET 2 3.00 X 1.78

S.DUCT

BEDROOM 3.15 X 2.78

BEDROOM 5.75 X 2.78

Chajja @ Beam Bottom

0.97 X 1.06

2.40 X 0.50

5.00 X 0.50

Mechanical Ventilation Cutout

TOILET 1 1.83 X 2.75

S.TOILET 1.08 X 1.05

1.23 X 0.78

FOYER 1.20 X 2.02

S.ROOM 2.45 X 1.20

1.52 X 3.56

1.52 X 2.40

BEDROOM 4.13 X 3.05

FLAT NO 1

REHAB

FLAT NO 2

REHAB

KITCHEN 4.13 X 2.40

1.97 X 3.50

3.38 X 0.35

TOILET 3 3.05 X 2.00

1.85 X 2.00

LIVING/DINING 5.33 X 7.57

CARPET - 146.51 SQ.MT

CARPET - 162.84 SQ.MT

BEDROOM 3 5.75 X 3.10

DECK 5.33 X 1.83

5.00 X 0.75

B

A

A'

B'

FIREMAN EVACUATION LIFT 2.20 X 2.55

SMOKE CHECK LOBBY 2.20 X 2.20

FRD

UP

DN

2.00

2.25

2.04

Pressurization duct at ceiling level

P.SHAFT

2.00 X 2.45

AVS

ED

LIFT 2.60 X 2.00

LIFT LOBBY 5.20 X 2.55

FIRE LIFT 2.60 X 2.00

FD

3.95 X 1.63

CROSS BEAMS at Mid-Landing LVL.

M.S. Platform M.T. for ODU 1

M.S.Platform M.T. for ODU 2

1.19

1.20

2.22 X 2.77

1.53 X 1.97

TOILET 1 3.00 X 1.78

S.DUCT

BEDROOM 5.75 X 2.78

5.00 X 0.50

TOILET 1 2.03 X 1.92

BEDROOM 3.15 X 2.78

Chajja @ Beam Bottom

0.97 X 1.06

2.40 X 0.50

1.52 X 3.56

BEDROOM 4.13 X 3.05

Mechanical Ventilation Cutout

TOILET 2 1.83 X 2.75

S.TOILET 1.08 X 1.05

1.22 X 1.15

1.32 X 1.83

FOYER 1.20 X 1.94

FOYER 1.20 X 2.08

S.ROOM 1.23 X 1.98

1.23 X 1.20

1.52 X 2.40

FLAT NO 1

REHAB

FLAT NO 2

REHAB

KITCHEN 4.13 X 2.40

1.97 X 3.50

1.98 X 3.50

3.38 X 0.35

LIVING/DINING 3.35 X 7.57

CARPET - 127.74 SQ.MT

LIVING/DINING 7.30 X 7.58

CARPET - 181.80 SQ.MT

TOILET 3 3.05 X 2.00

1.85 X 2.00

BEDROOM 5.75 X 3.10

DECK 3.35 X 1.83


DECK 7.30 X 1.83

5.00 X 0.75

15TH FLOOR PLAN


14TH FLOOR PLAN

SCALE - 1:100

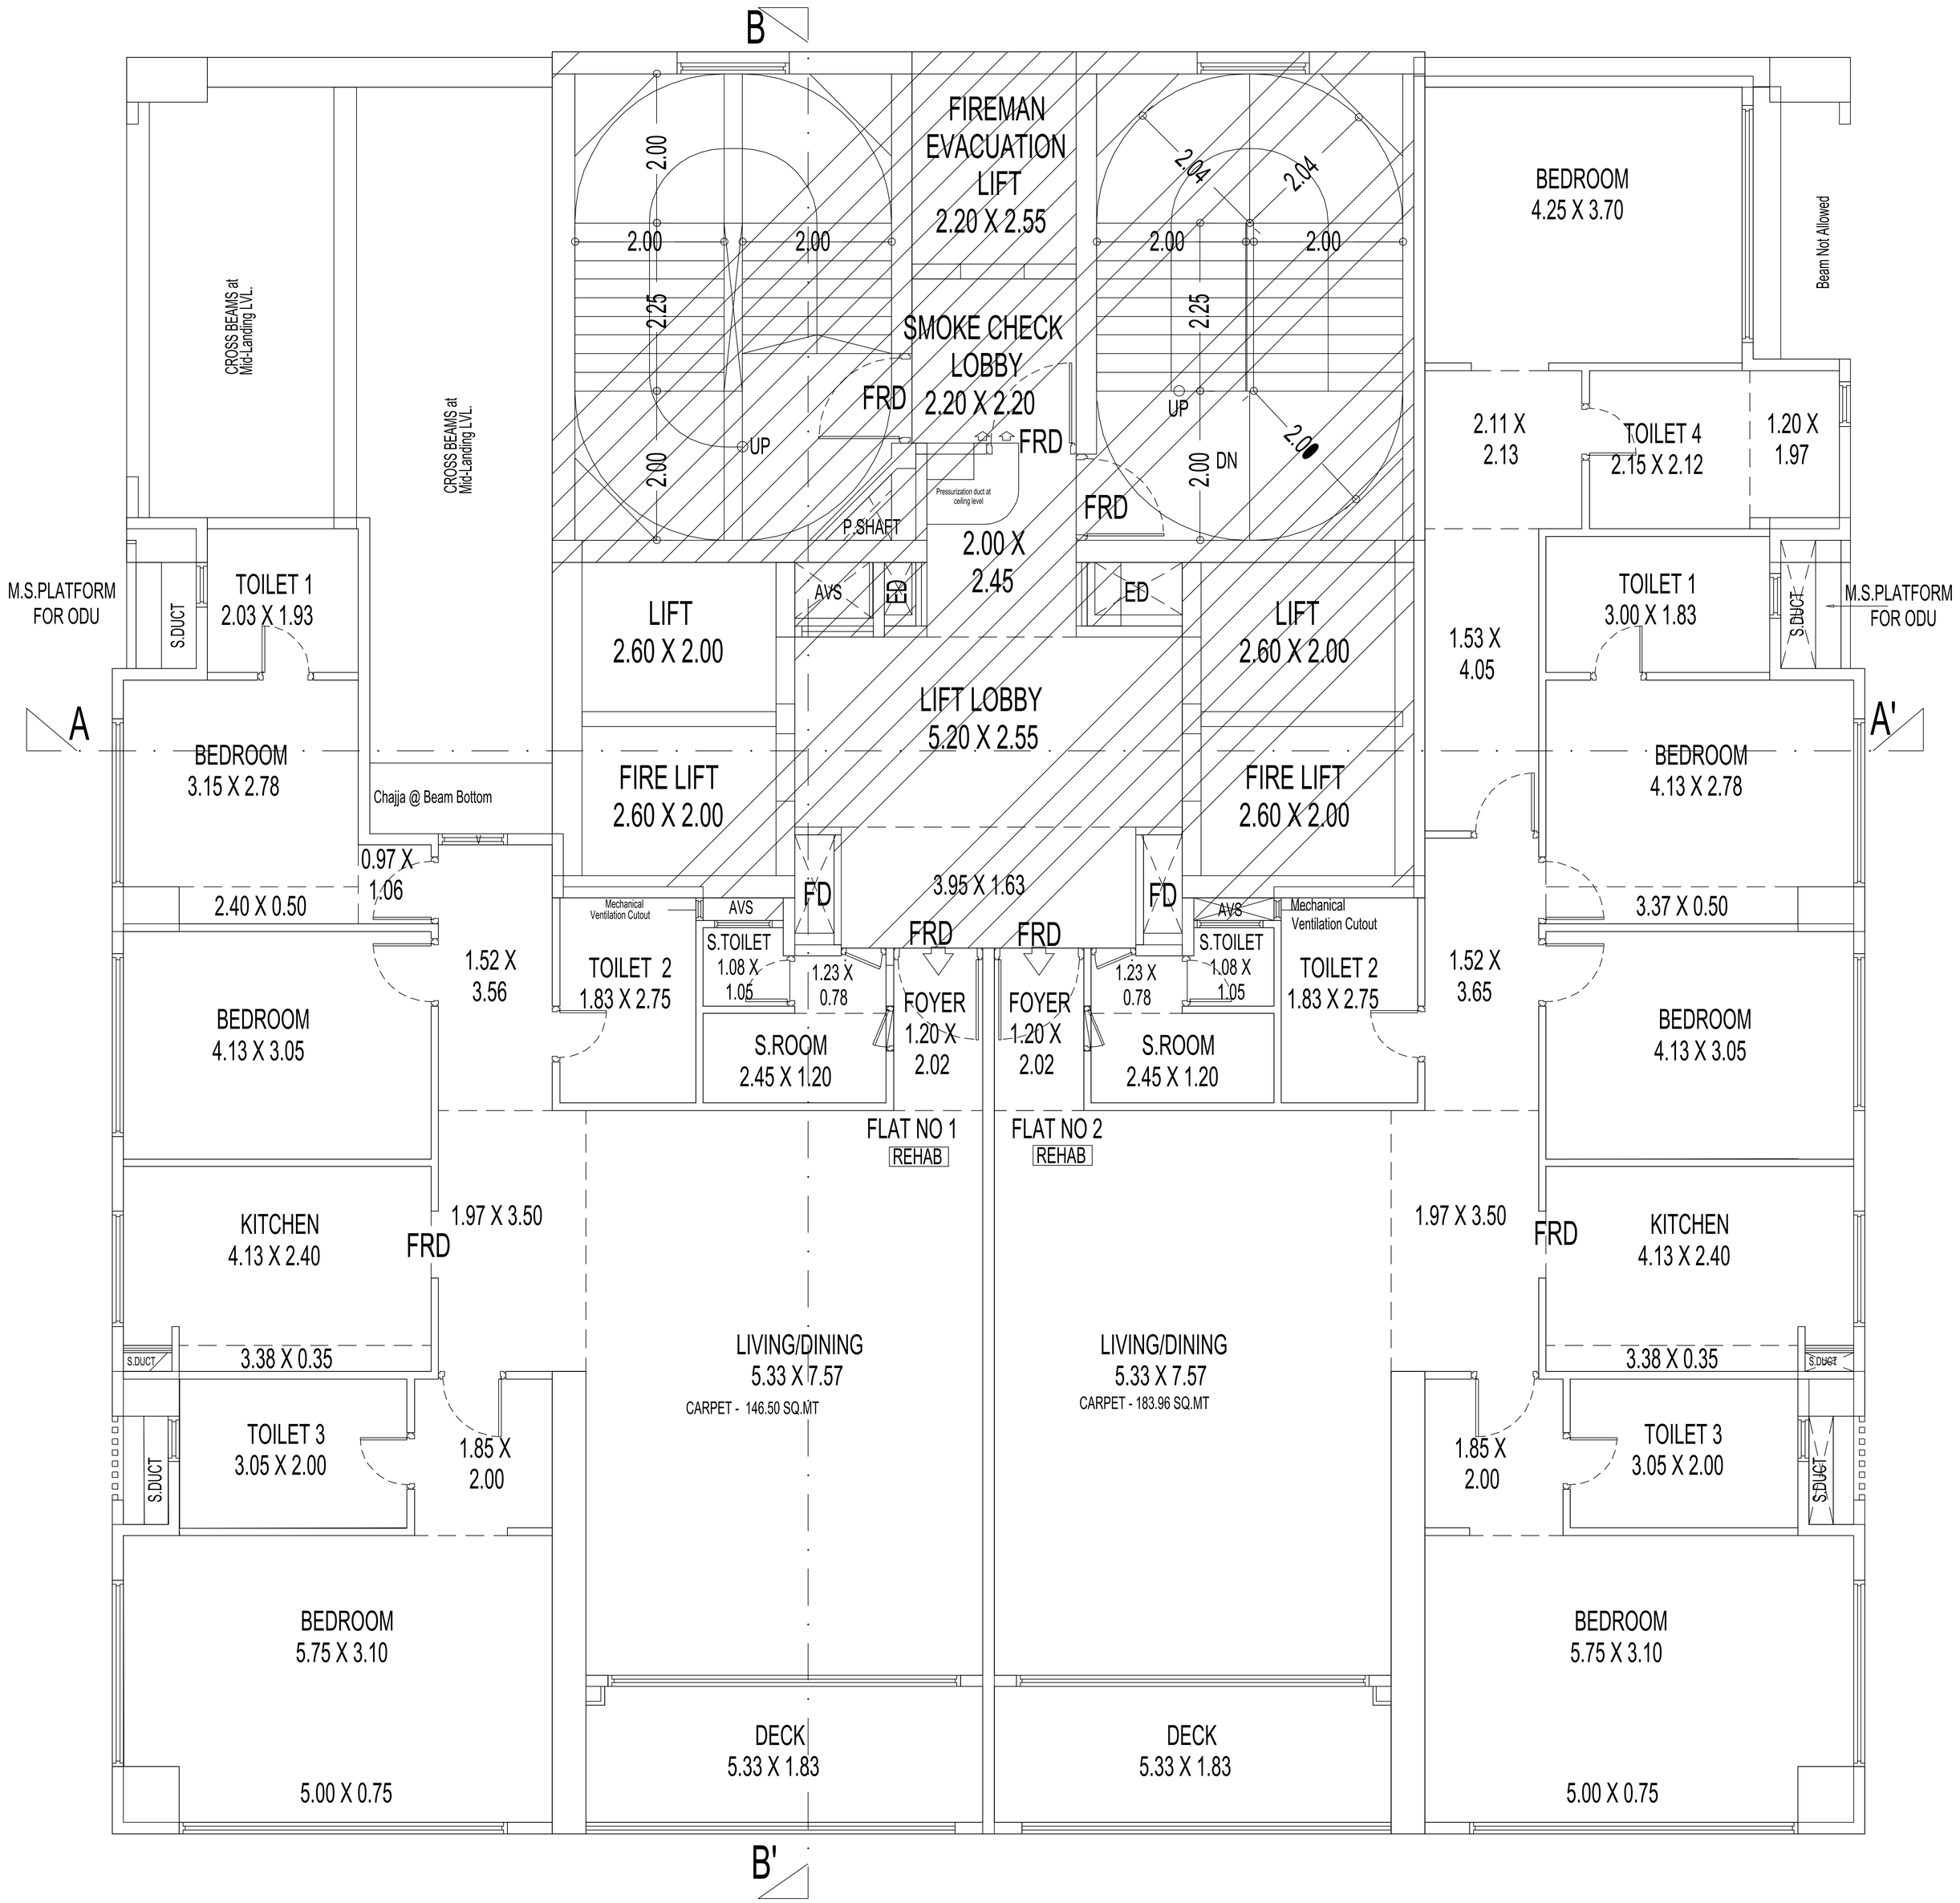


16TH FLOOR PLAN

SCALE - 1:100

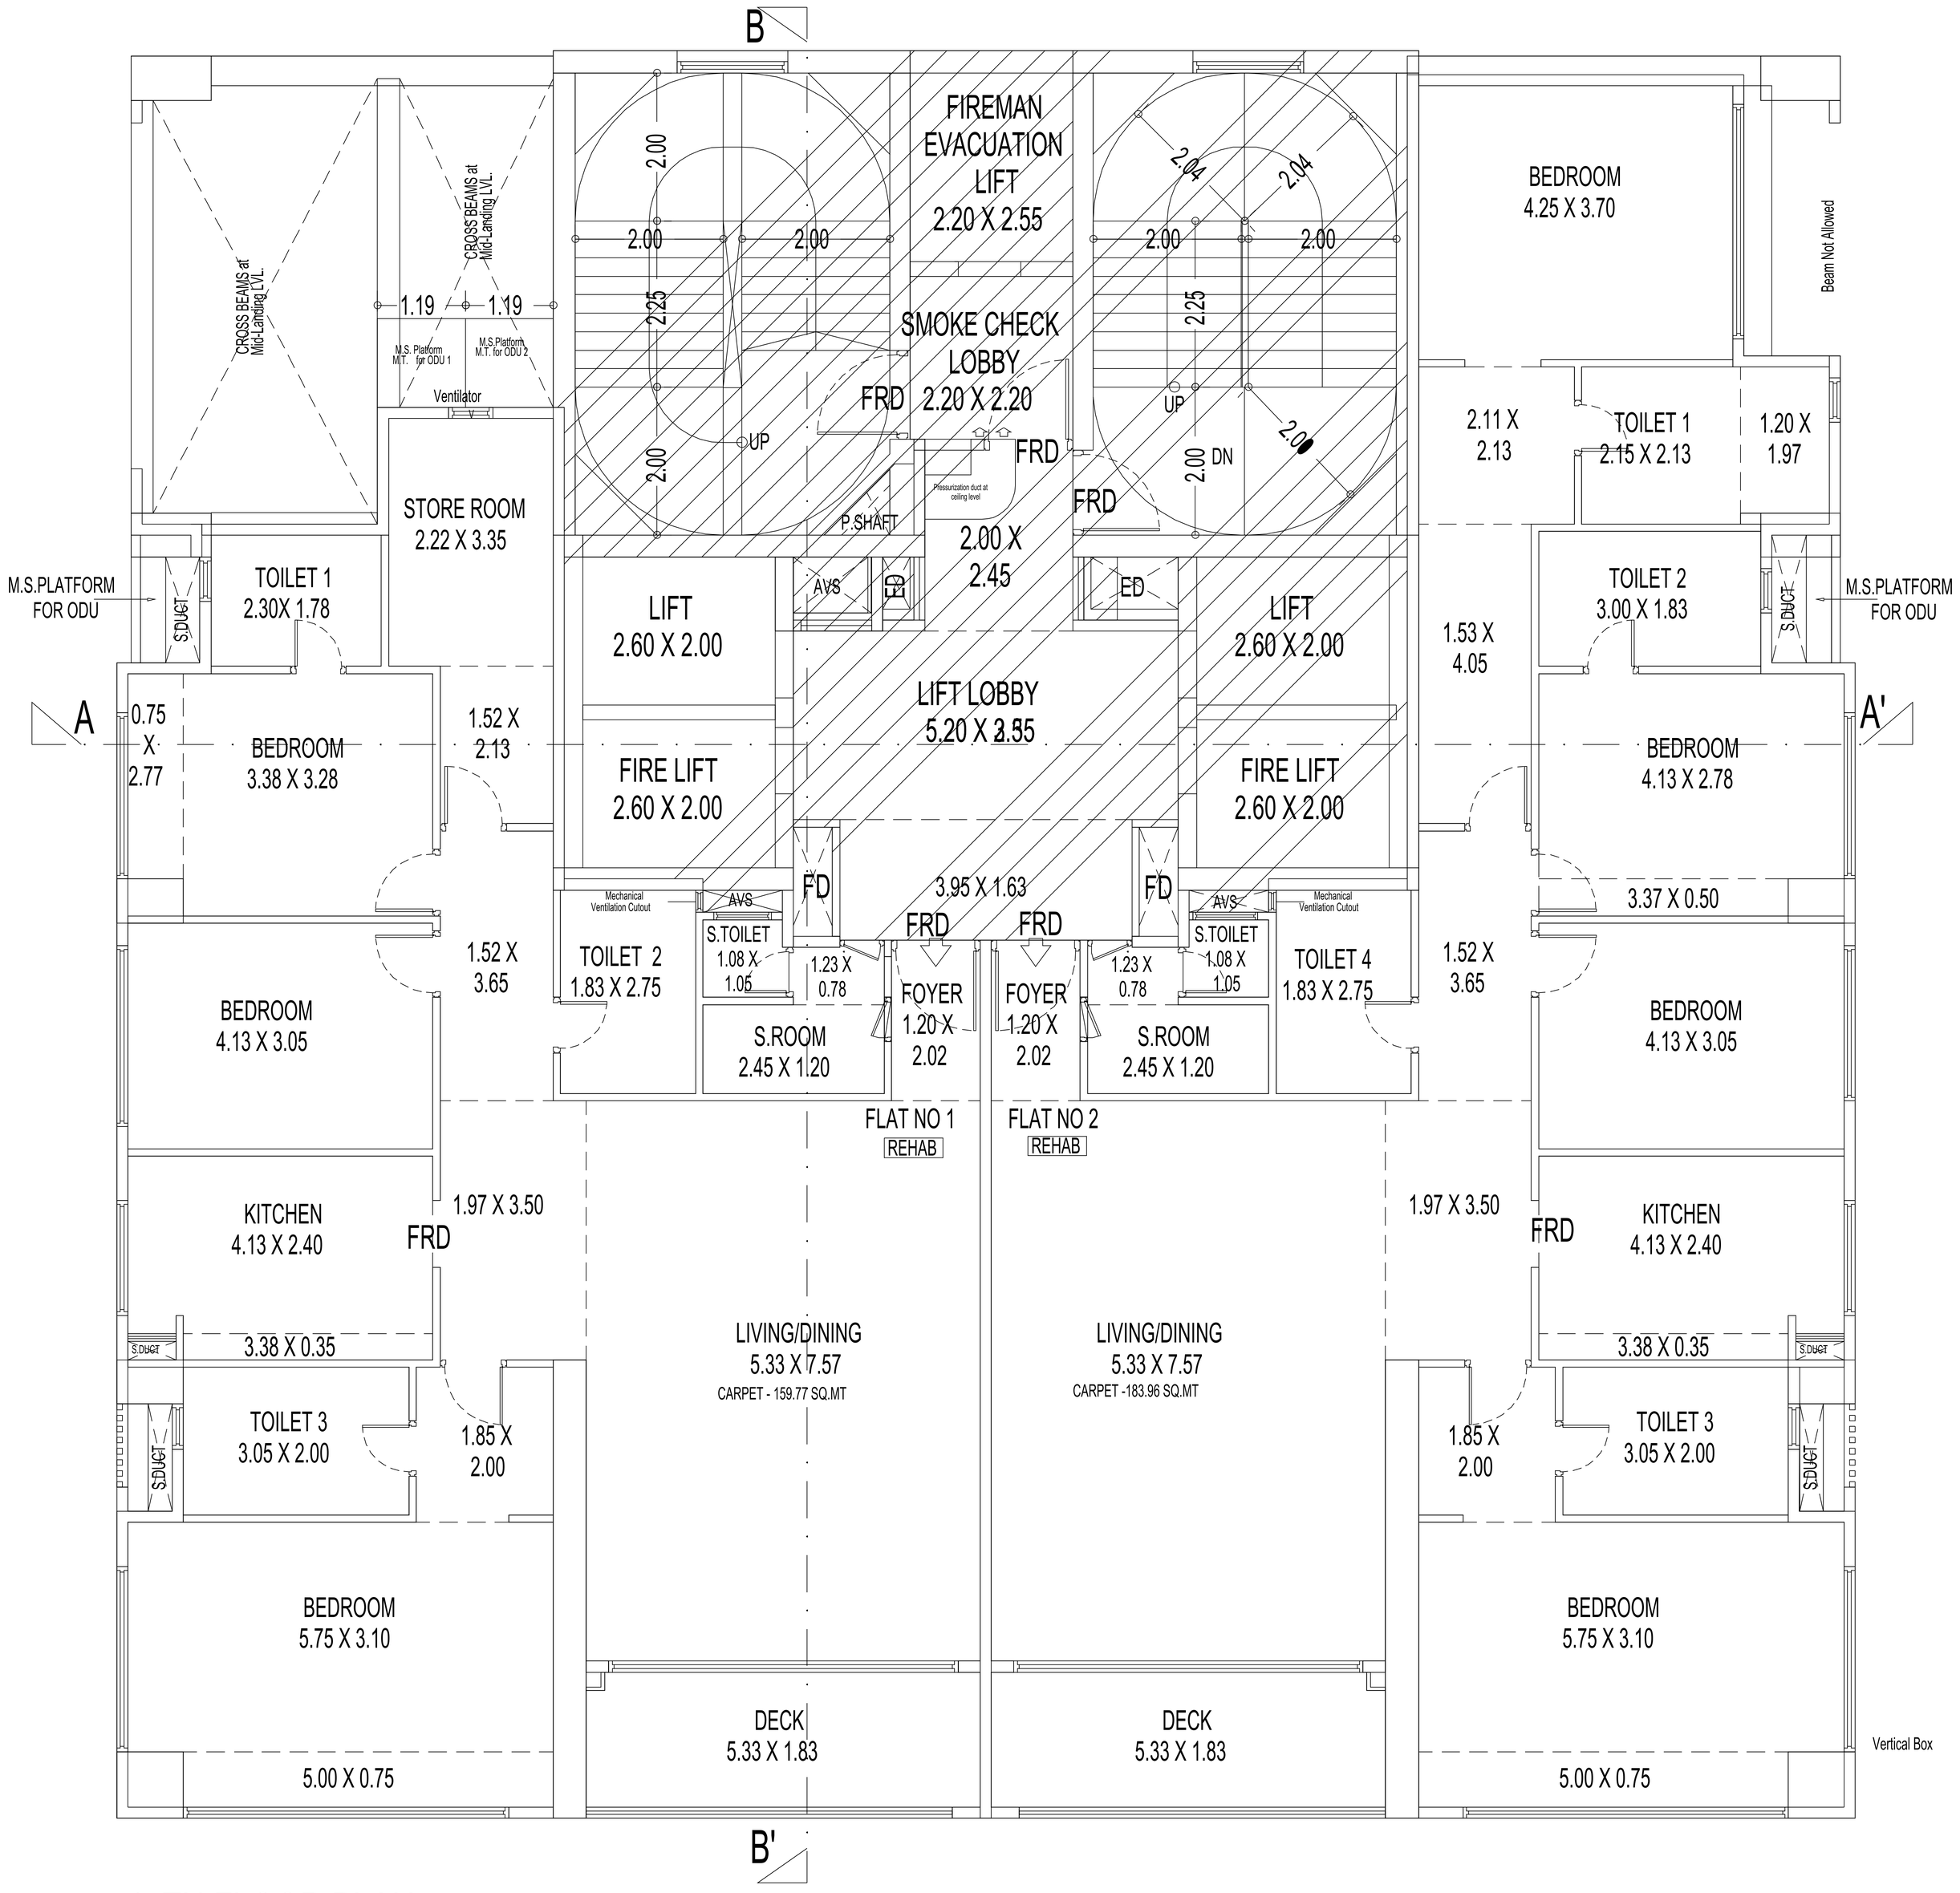


17TH FLOOR PLAN

SCALE - 1:100

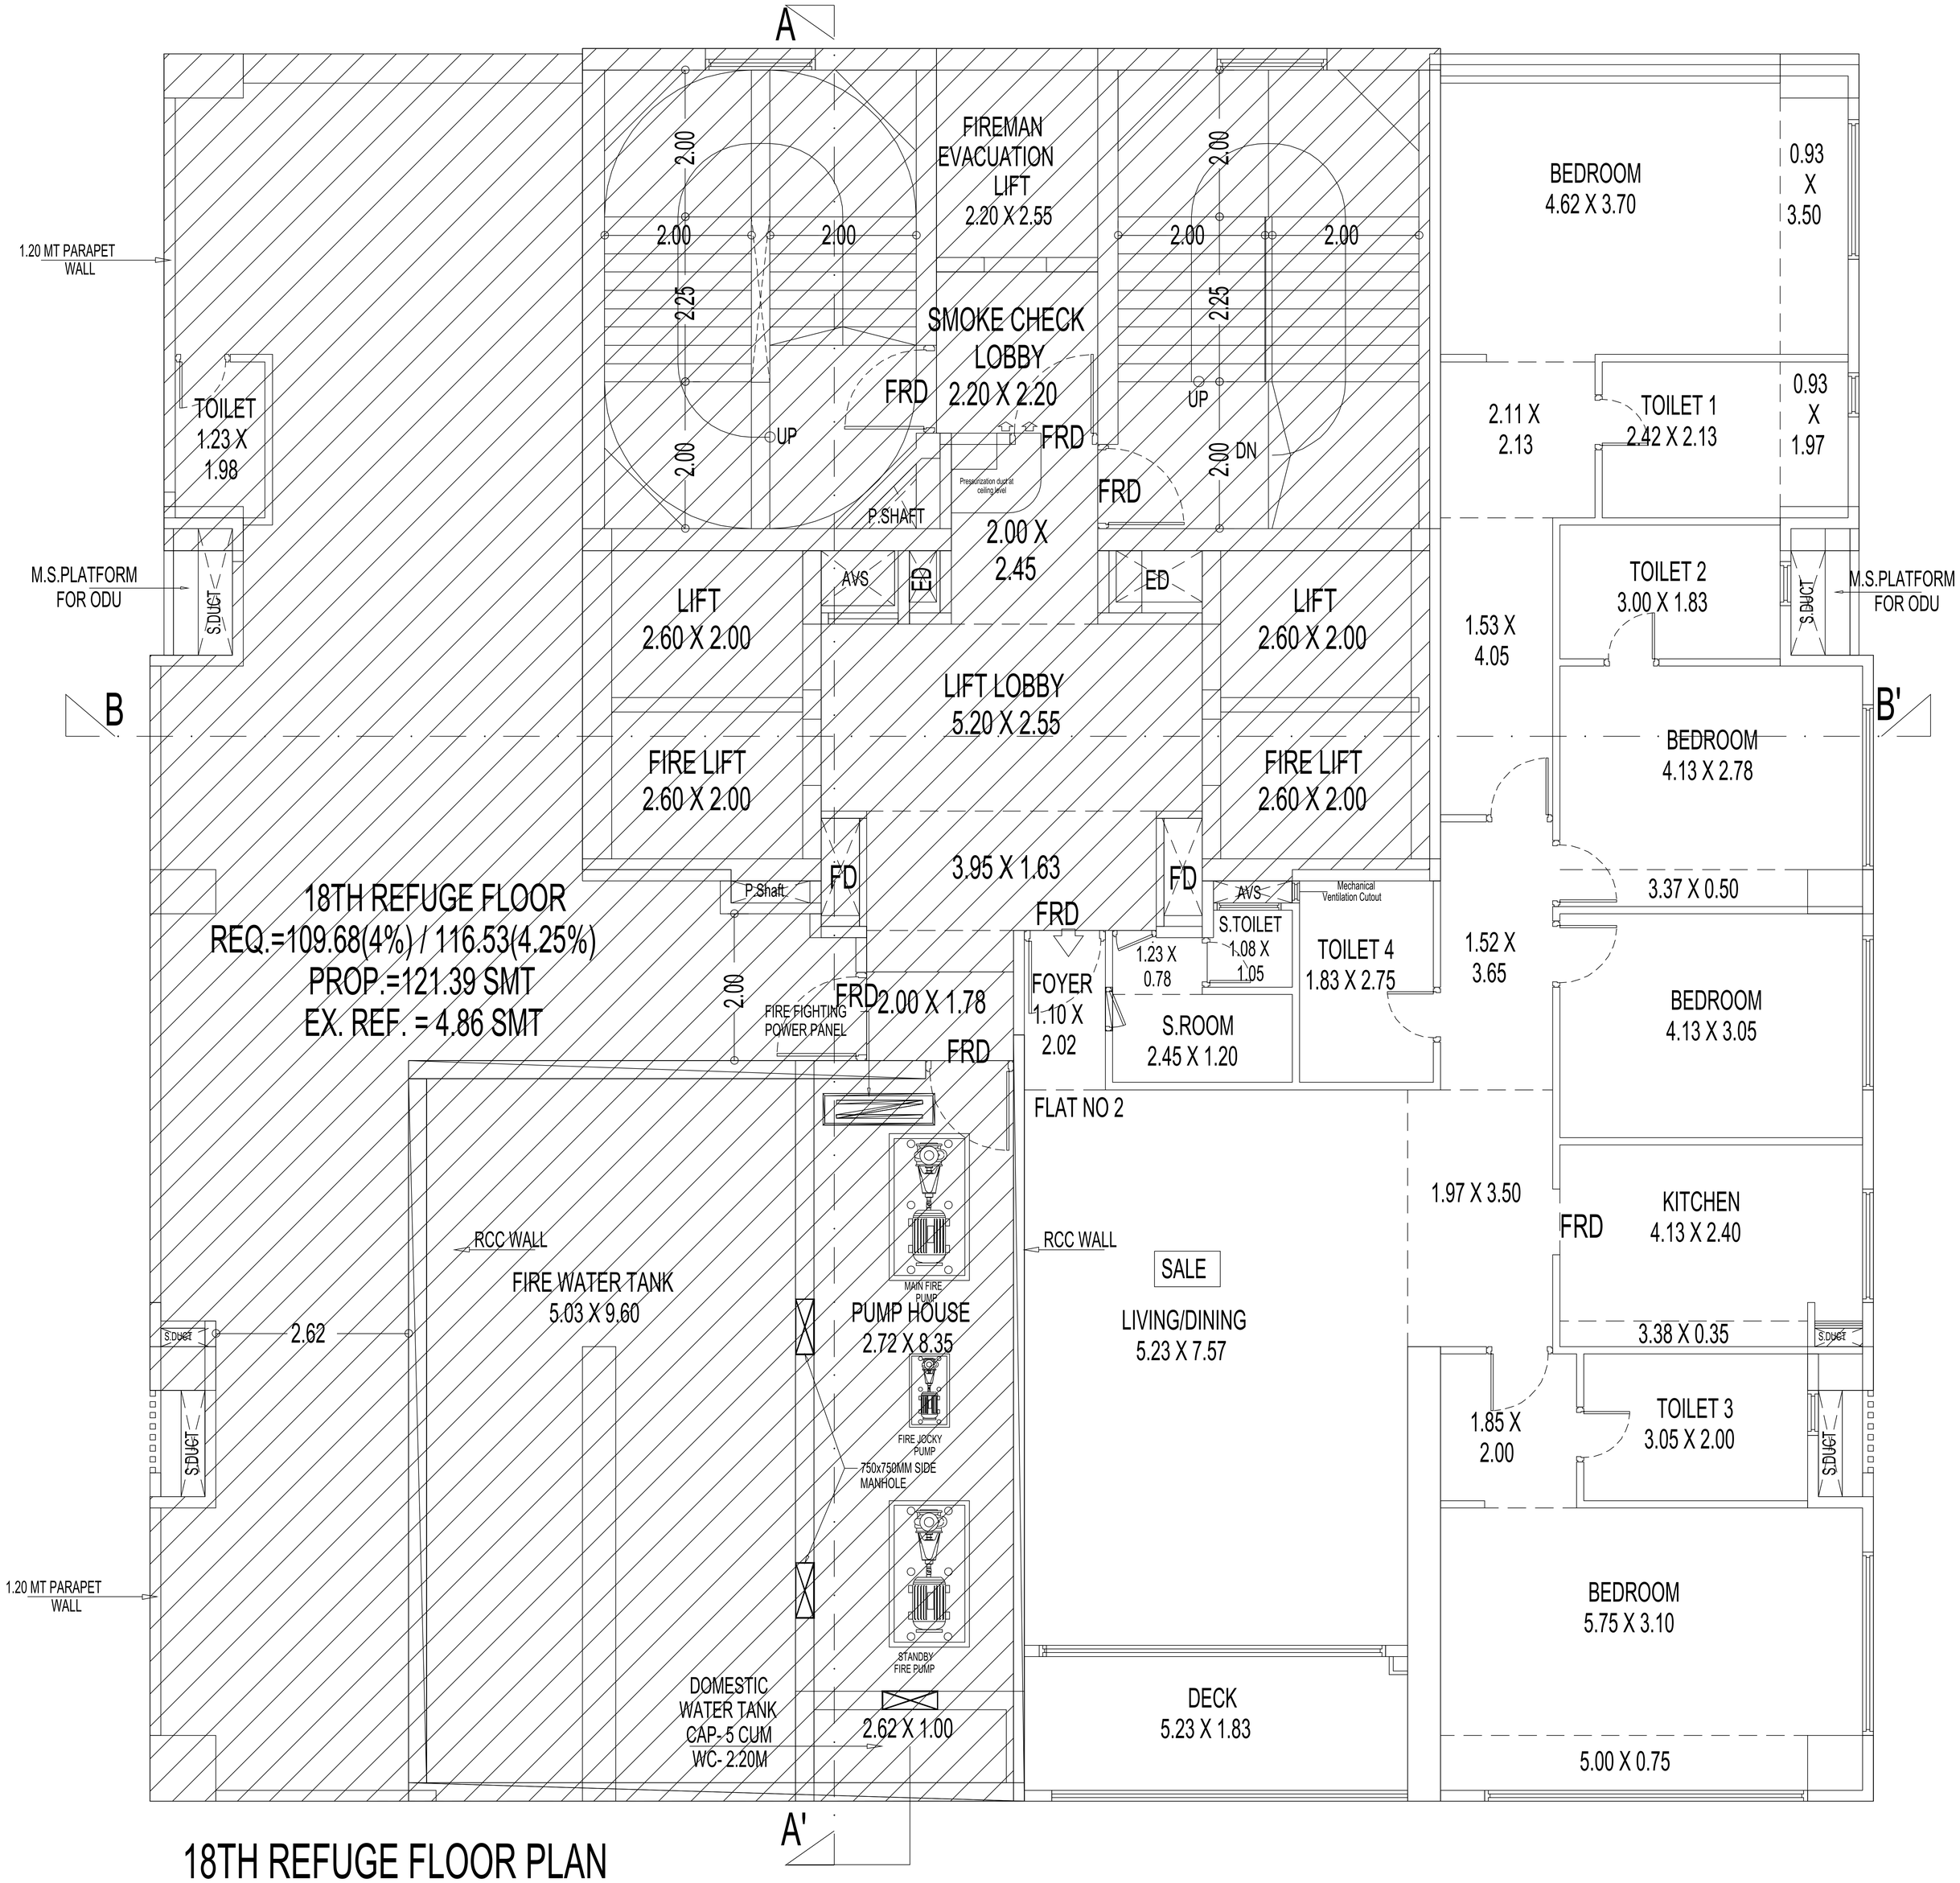


18TH REFUGE FLOOR PLAN

SCALE - 1:100

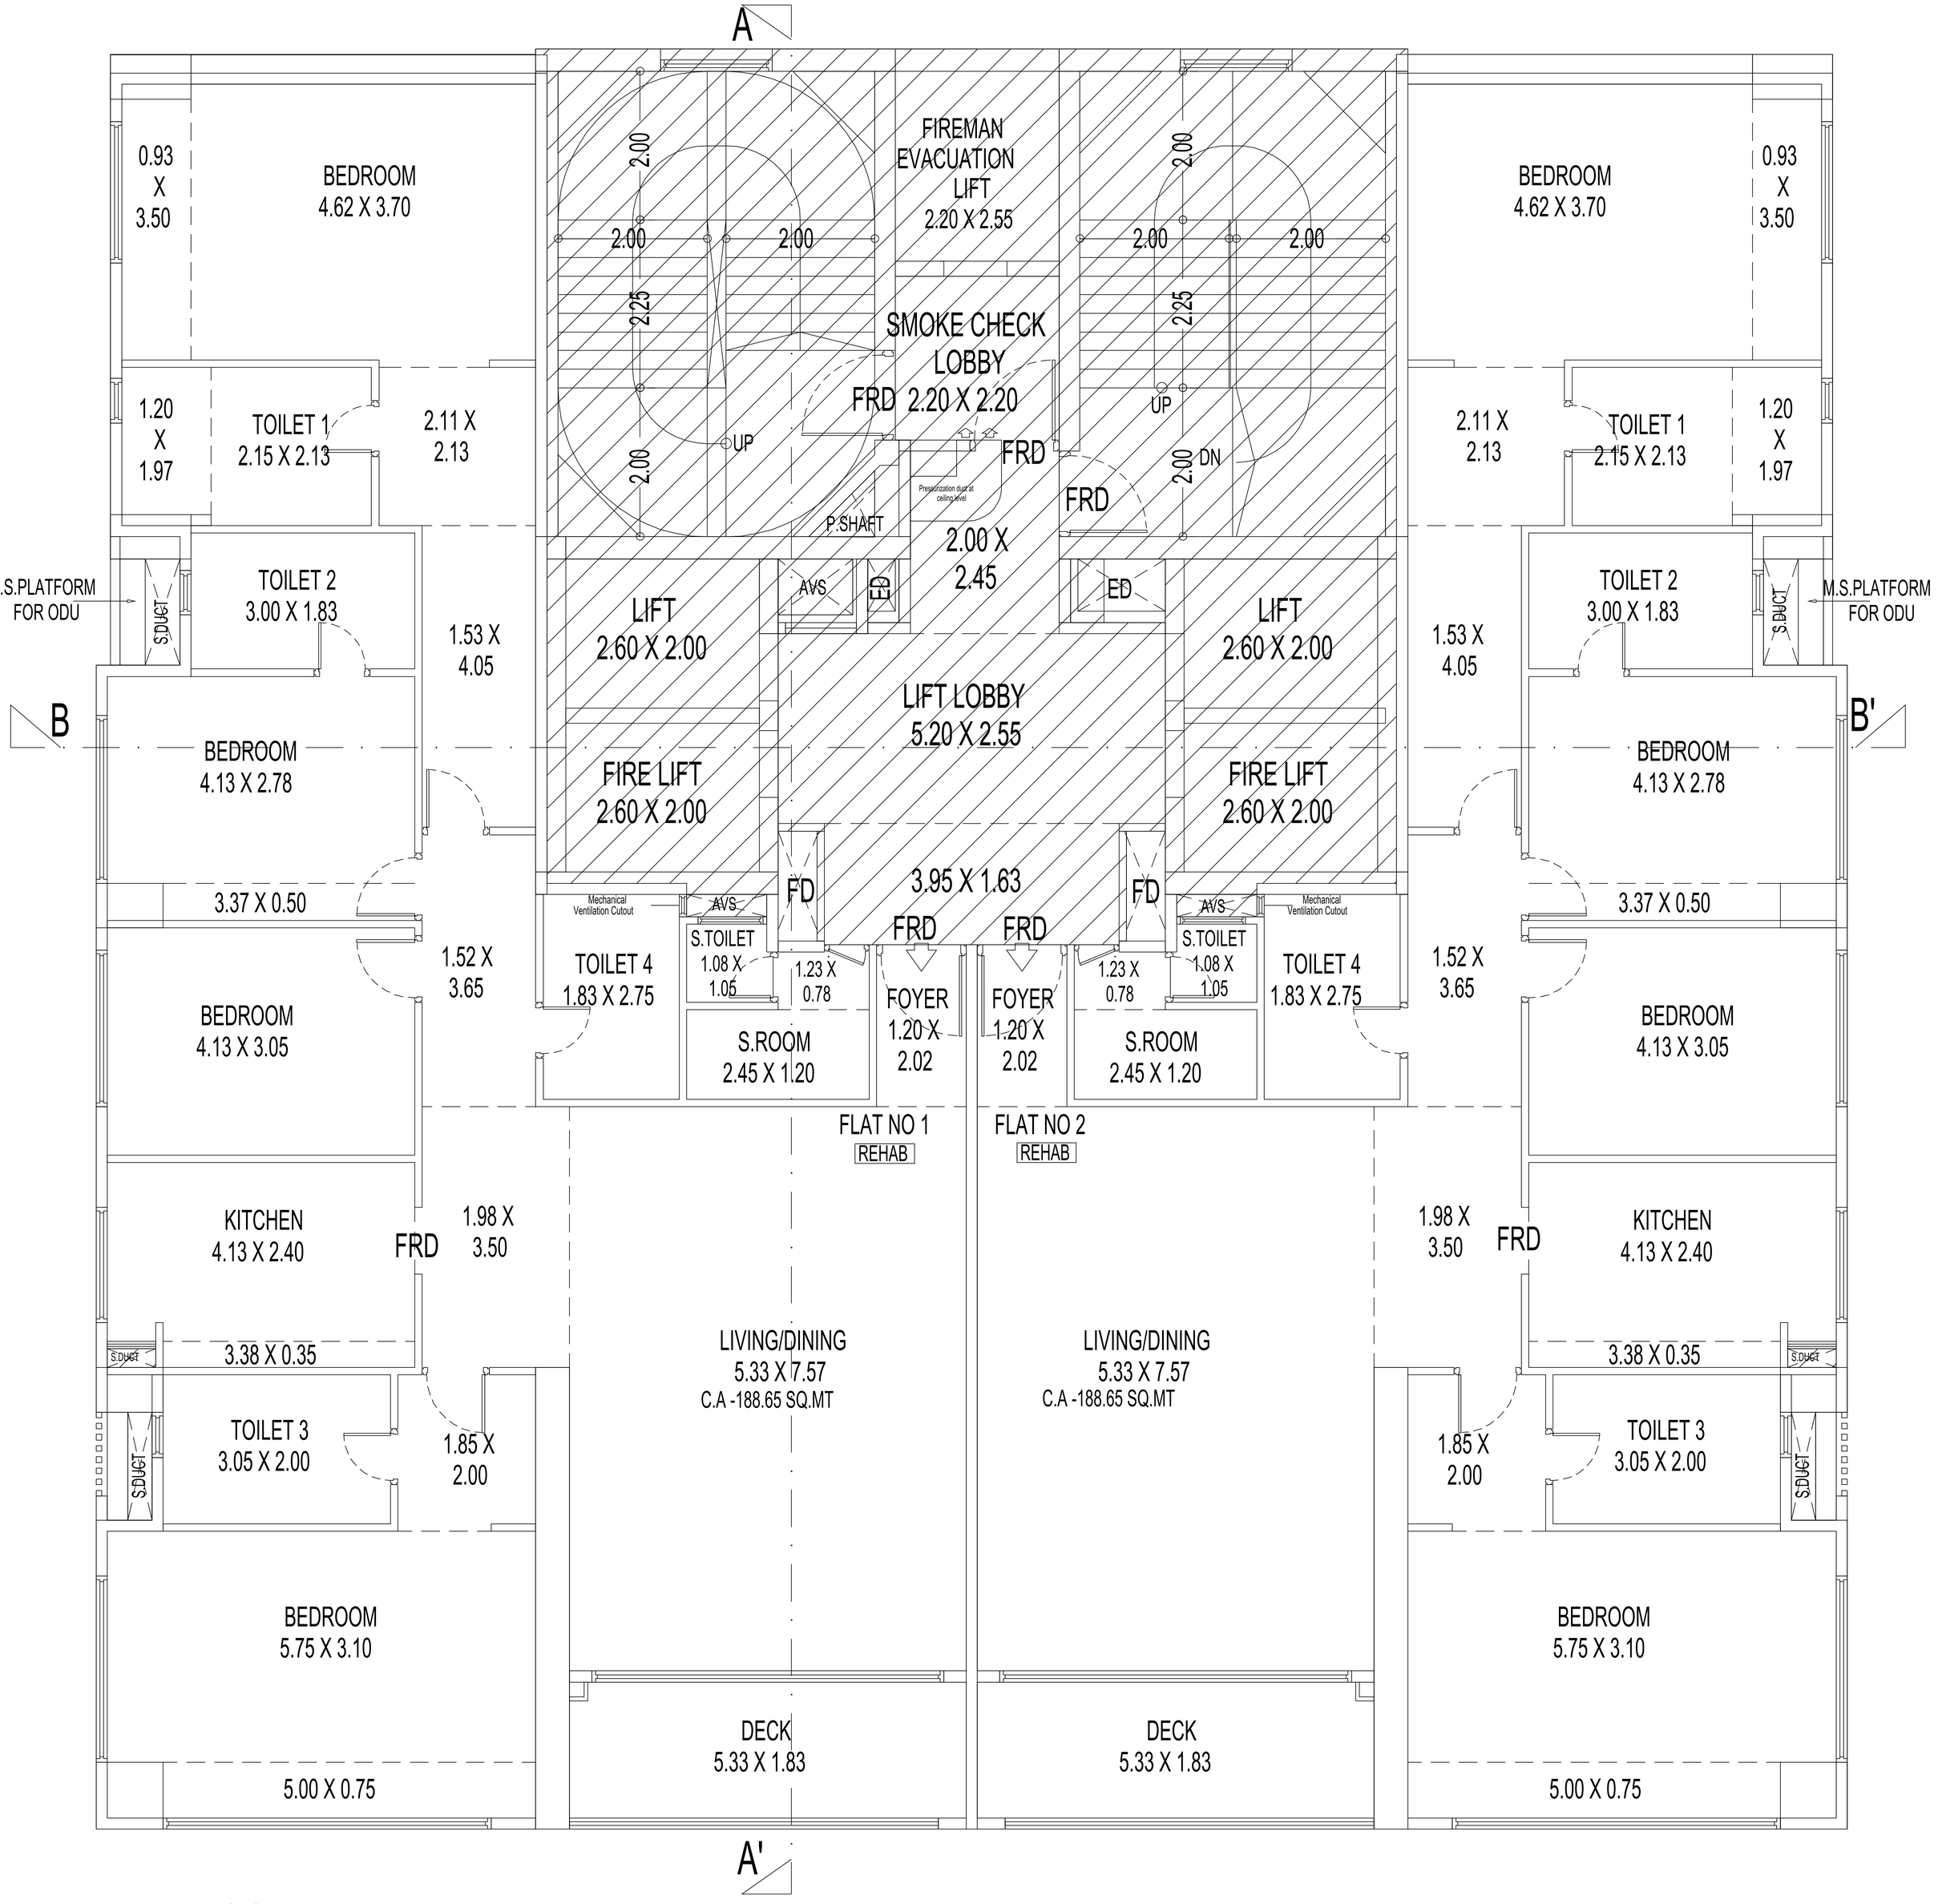


19TH FLOOR PLAN


SCALE - 1:100

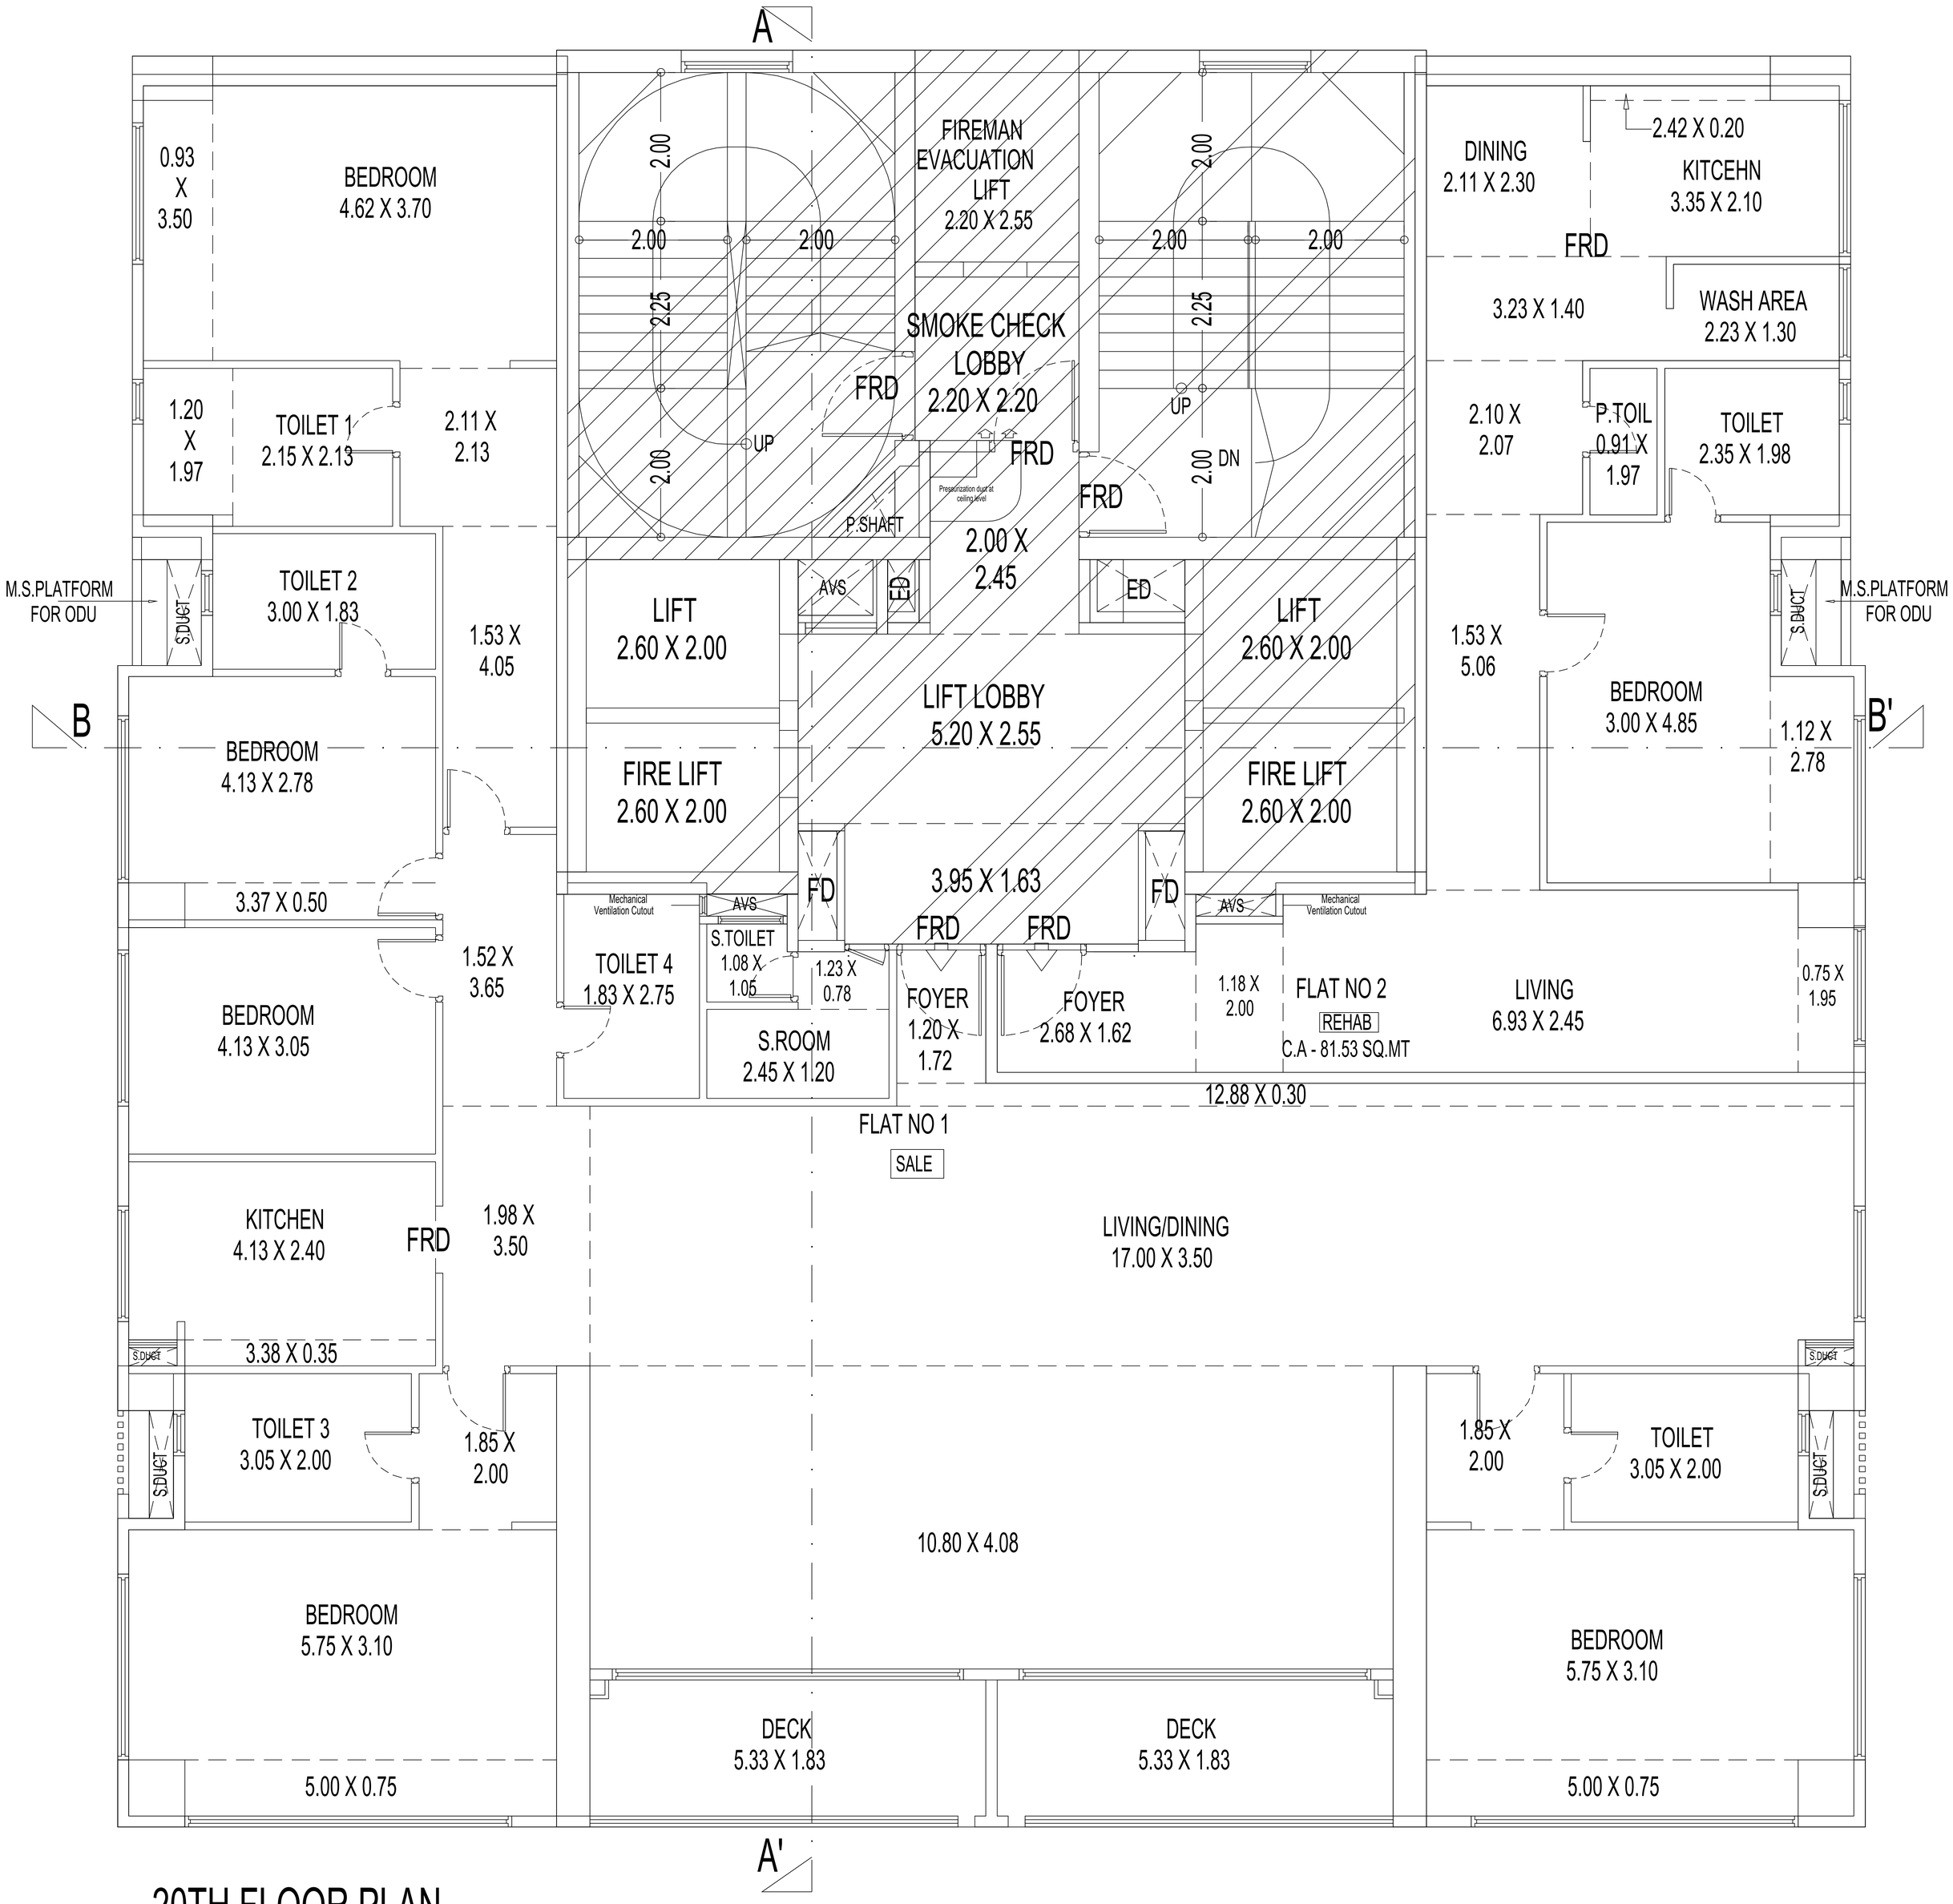

20TH FLOOR PLAN


SCALE - 1:100

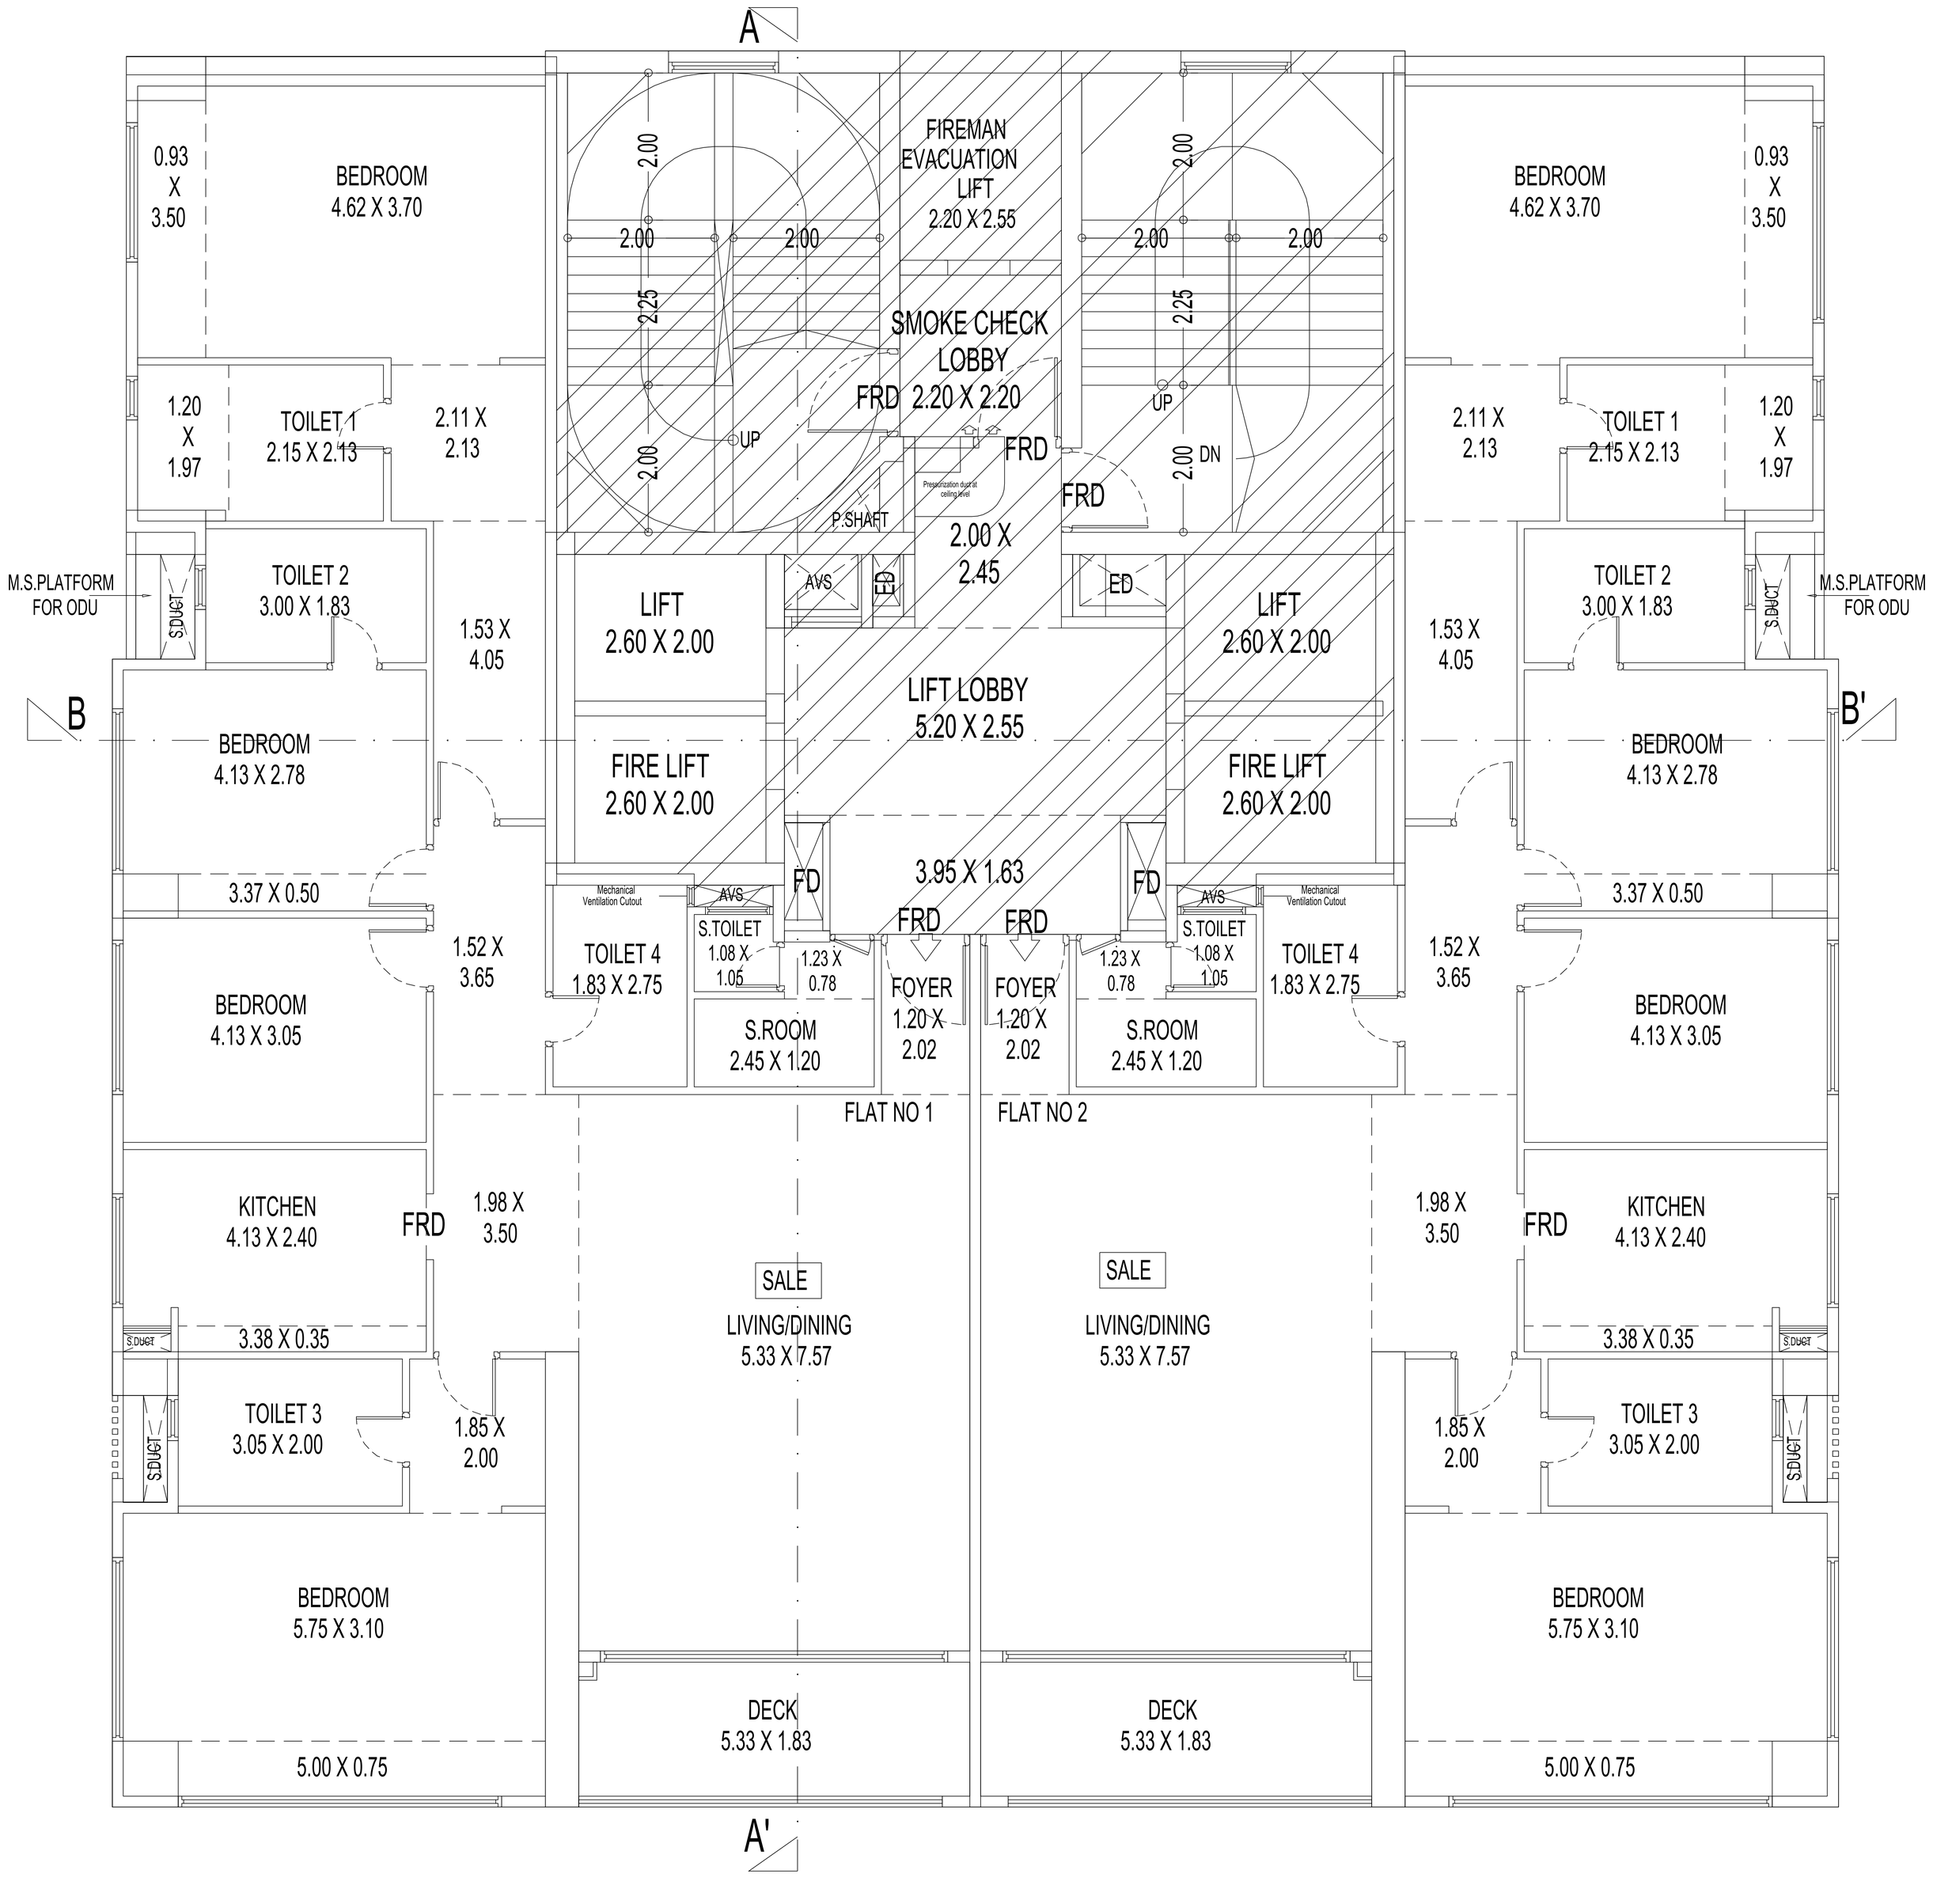
A
A'
B
B'
0.93 X 3.50
BEDROOM 4.62 X 3.70
FIREMAN EVACUATION LIFT 2.20 X 2.55
SMOKE CHECK LOBBY FRD 2.20 X 2.20
2.00
2.25
UP
DN
FRD
Pressurization duct at ceiling level
P.SHAFT
2.00 X 2.45
1.20 X 1.97
TOILET 1 2.15 X 2.13
2.11 X 2.13
M.S.PLATFORM FOR ODU
S.DUCT
TOILET 2 3.00 X 1.83
1.53 X 4.05
AVS
ED
LIFT 2.60 X 2.00
LIFT LOBBY 5.20 X 2.55
FIRE LIFT 2.60 X 2.00
3.37 X 0.50
1.52 X 3.65
BEDROOM 4.13 X 3.05
BEDROOM 4.13 X 2.78
Mechanical Ventilation Cutout
FD
3.95 X 1.63
S.TOILET 1.08 X 1.05
1.23 X 0.78
TOILET 4 1.83 X 2.75
FOYER 1.20 X 2.02
S.ROOM 2.45 X 1.20
FLAT NO 1
FLAT NO 2
KITCHEN 4.13 X 2.40
1.98 X 3.50
SALE
LIVING/DINING 5.33 X 7.57
3.38 X 0.35
TOILET 3 3.05 X 2.00
1.85 X 2.00
BEDROOM 5.75 X 3.10
5.00 X 0.75
DECK 5.33 X 1.83

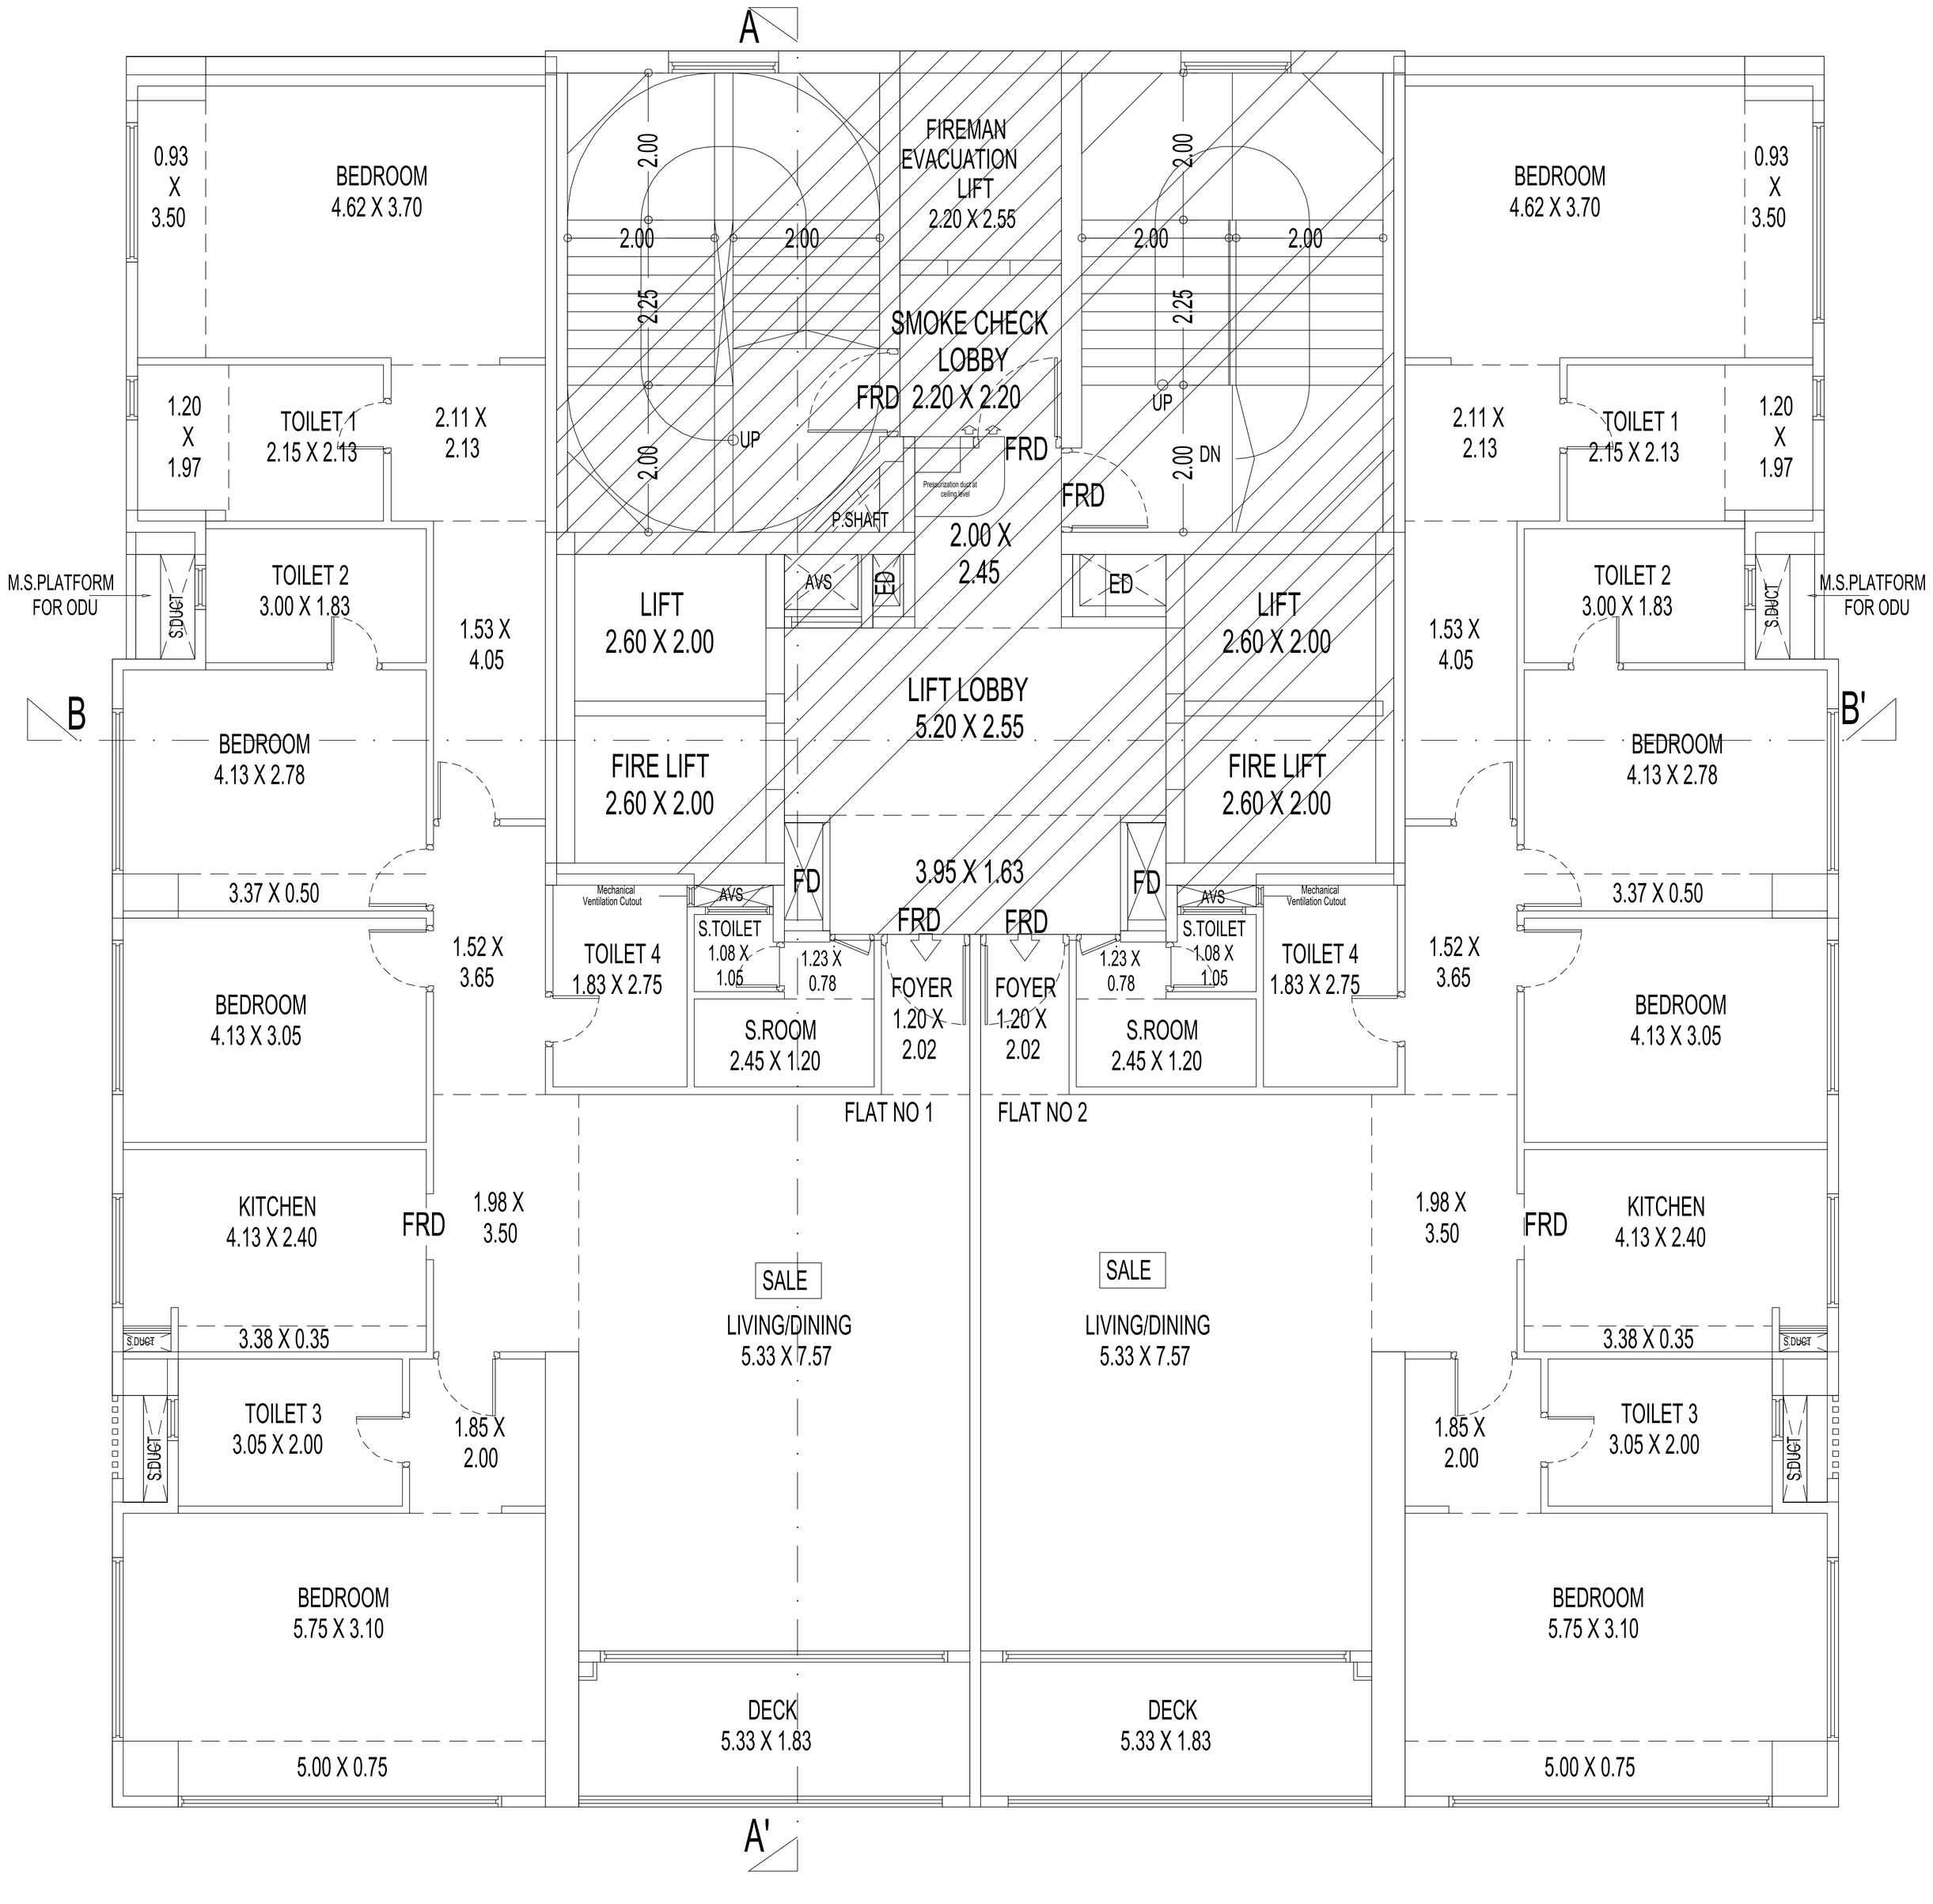
A
A'
B
B'
0.93 X 3.50
BEDROOM 4.62 X 3.70
FIREMAN EVACUATION LIFT 2.20 X 2.55
SMOKE CHECK LOBBY FRD 2.20 X 2.20
2.00
2.25
UP
DN
FRD
Pressurization duct at ceiling level
P.SHAFT
2.00 X 2.45
1.20 X 1.97
TOILET 1 2.15 X 2.13
2.11 X 2.13
M.S.PLATFORM FOR ODU
S.DUCT
TOILET 2 3.00 X 1.83
1.53 X 4.05
AVS
ED
LIFT 2.60 X 2.00
LIFT LOBBY 5.20 X 2.55
FIRE LIFT 2.60 X 2.00
3.37 X 0.50
1.52 X 3.65
BEDROOM 4.13 X 3.05
BEDROOM 4.13 X 2.78
Mechanical Ventilation Cutout
FD
3.95 X 1.63
S.TOILET 1.08 X 1.05
1.23 X 0.78
TOILET 4 1.83 X 2.75
FOYER 1.20 X 2.02
S.ROOM 2.45 X 1.20
FLAT NO 1
FLAT NO 2
KITCHEN 4.13 X 2.40
1.98 X 3.50
SALE
LIVING/DINING 5.33 X 7.57
3.38 X 0.35
TOILET 3 3.05 X 2.00
1.85 X 2.00
BEDROOM 5.75 X 3.10
5.00 X 0.75
DECK 5.33 X 1.83


21ST TO 23RD TYPICAL FLOOR PLAN

SCALE - 1:100

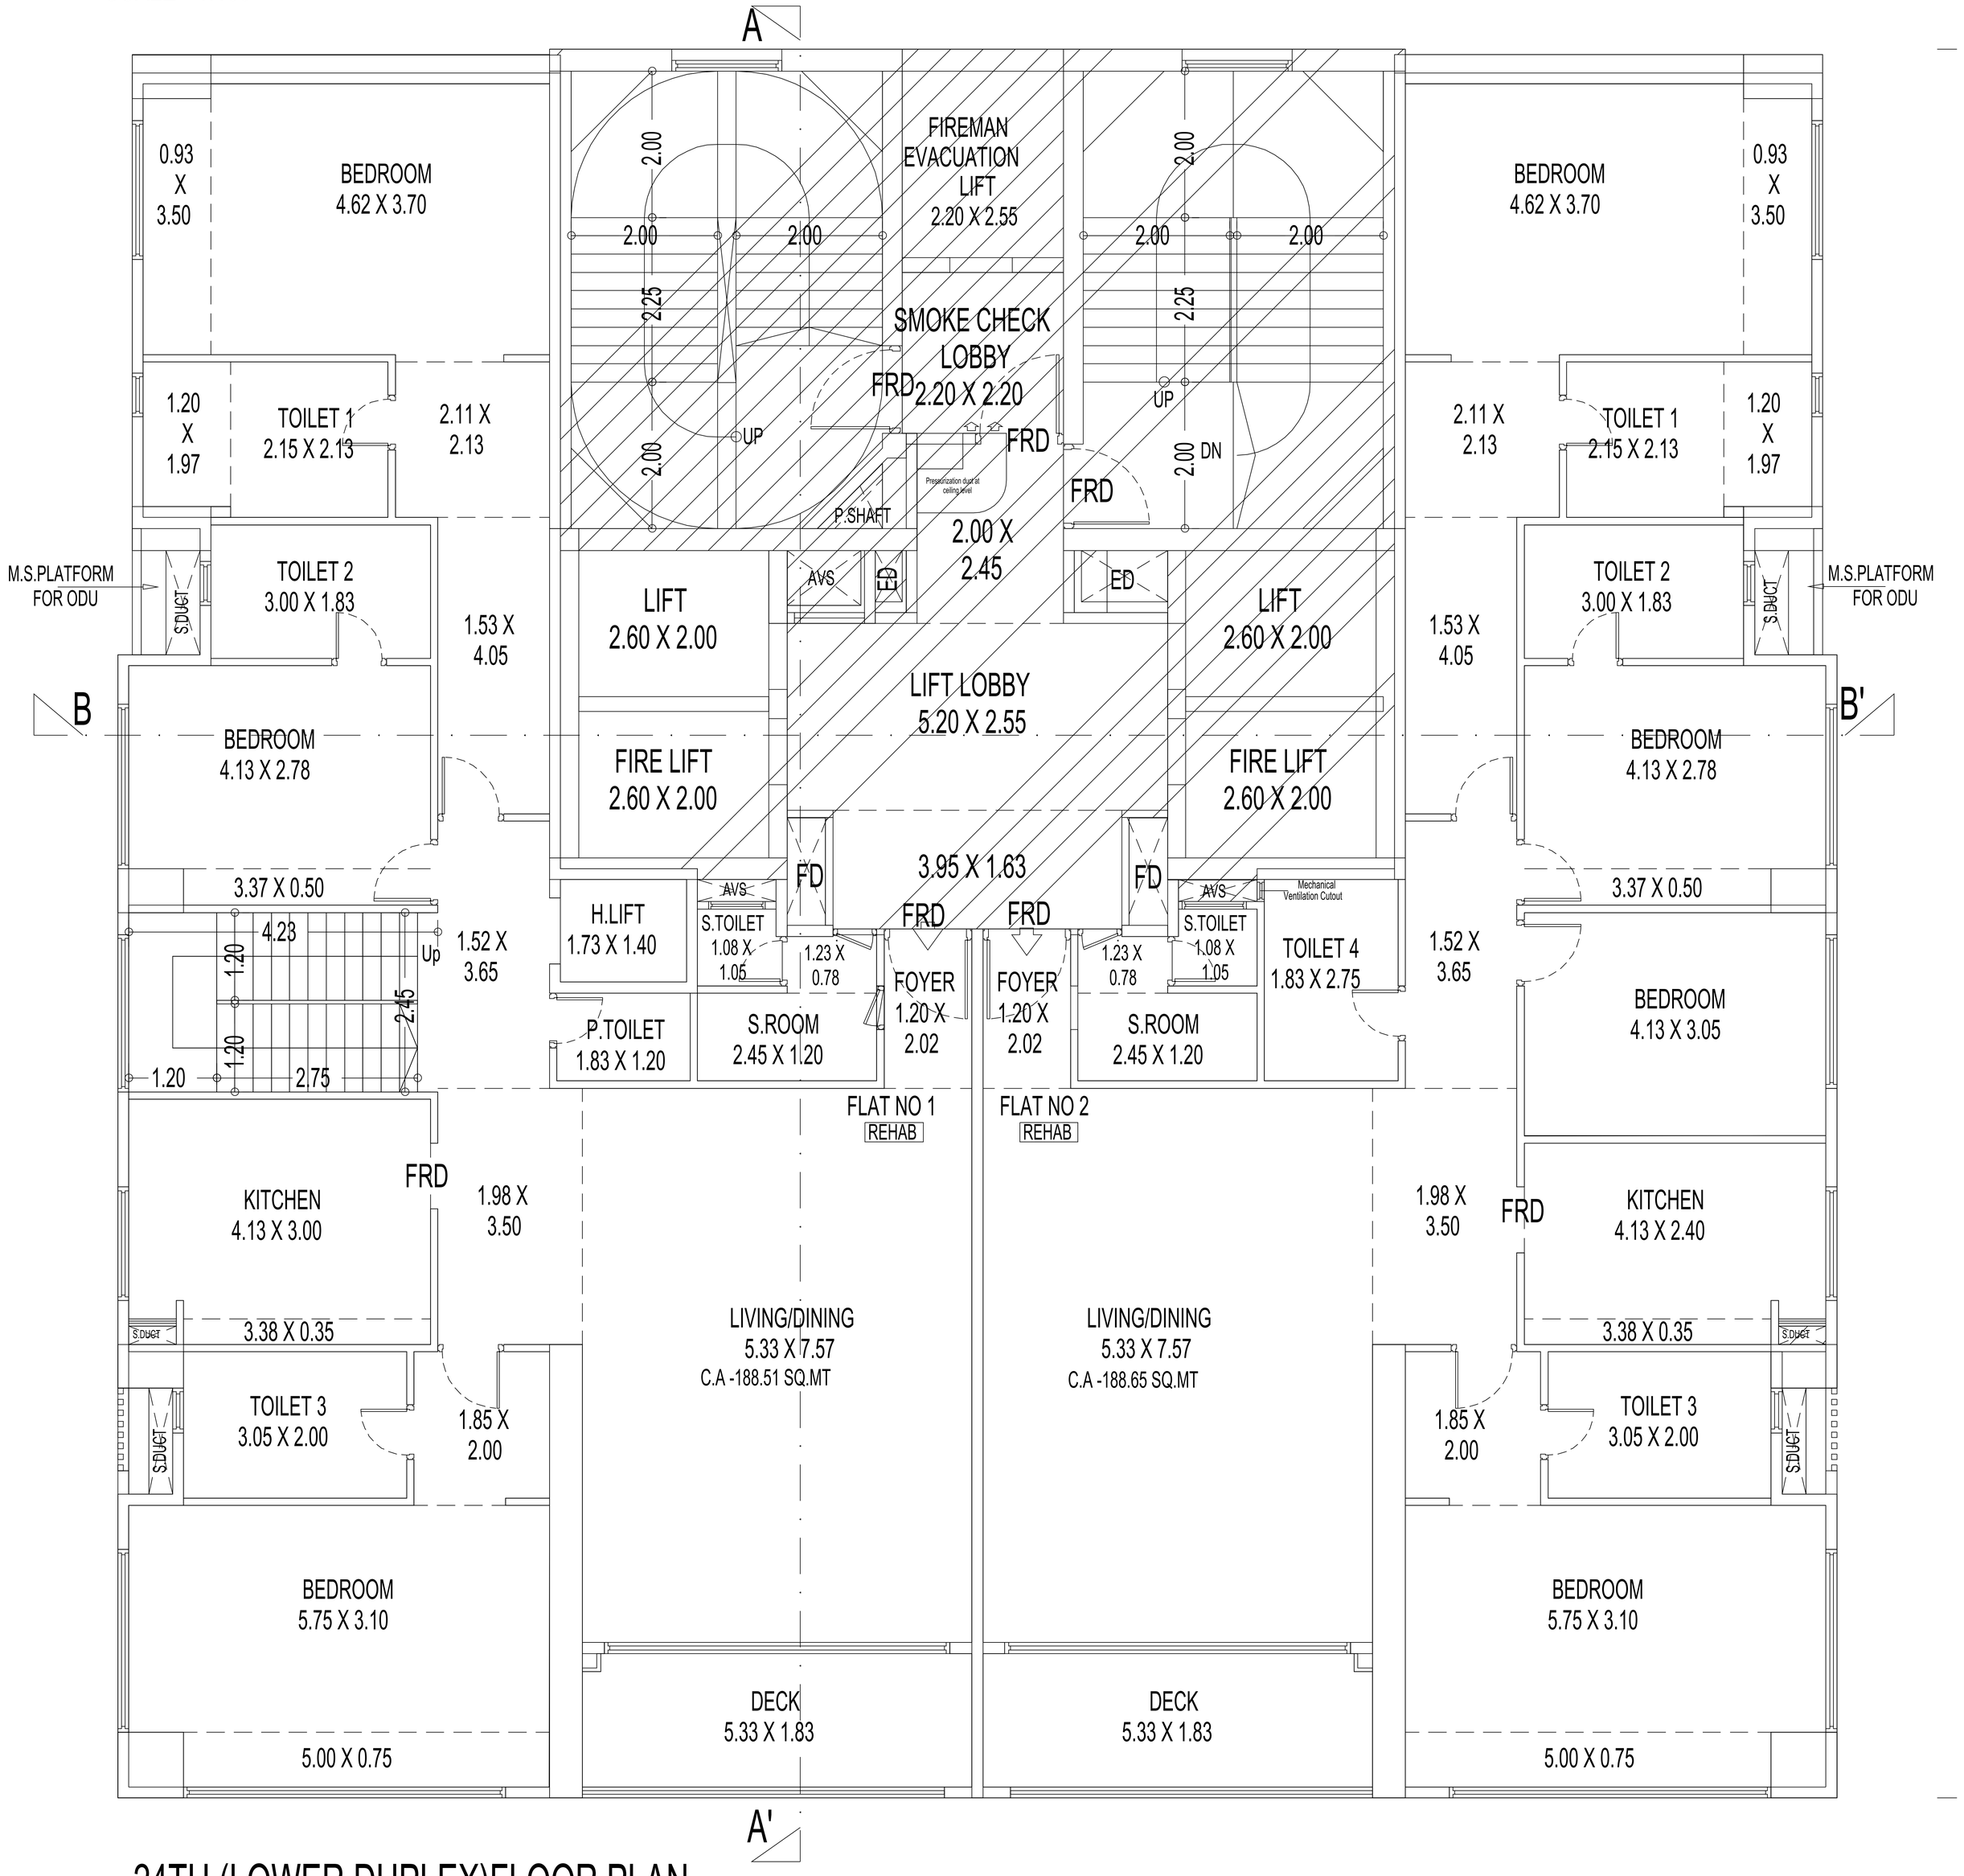

24TH (LOWER DUPLEX)FLOOR PLAN

SCALE - 1:100

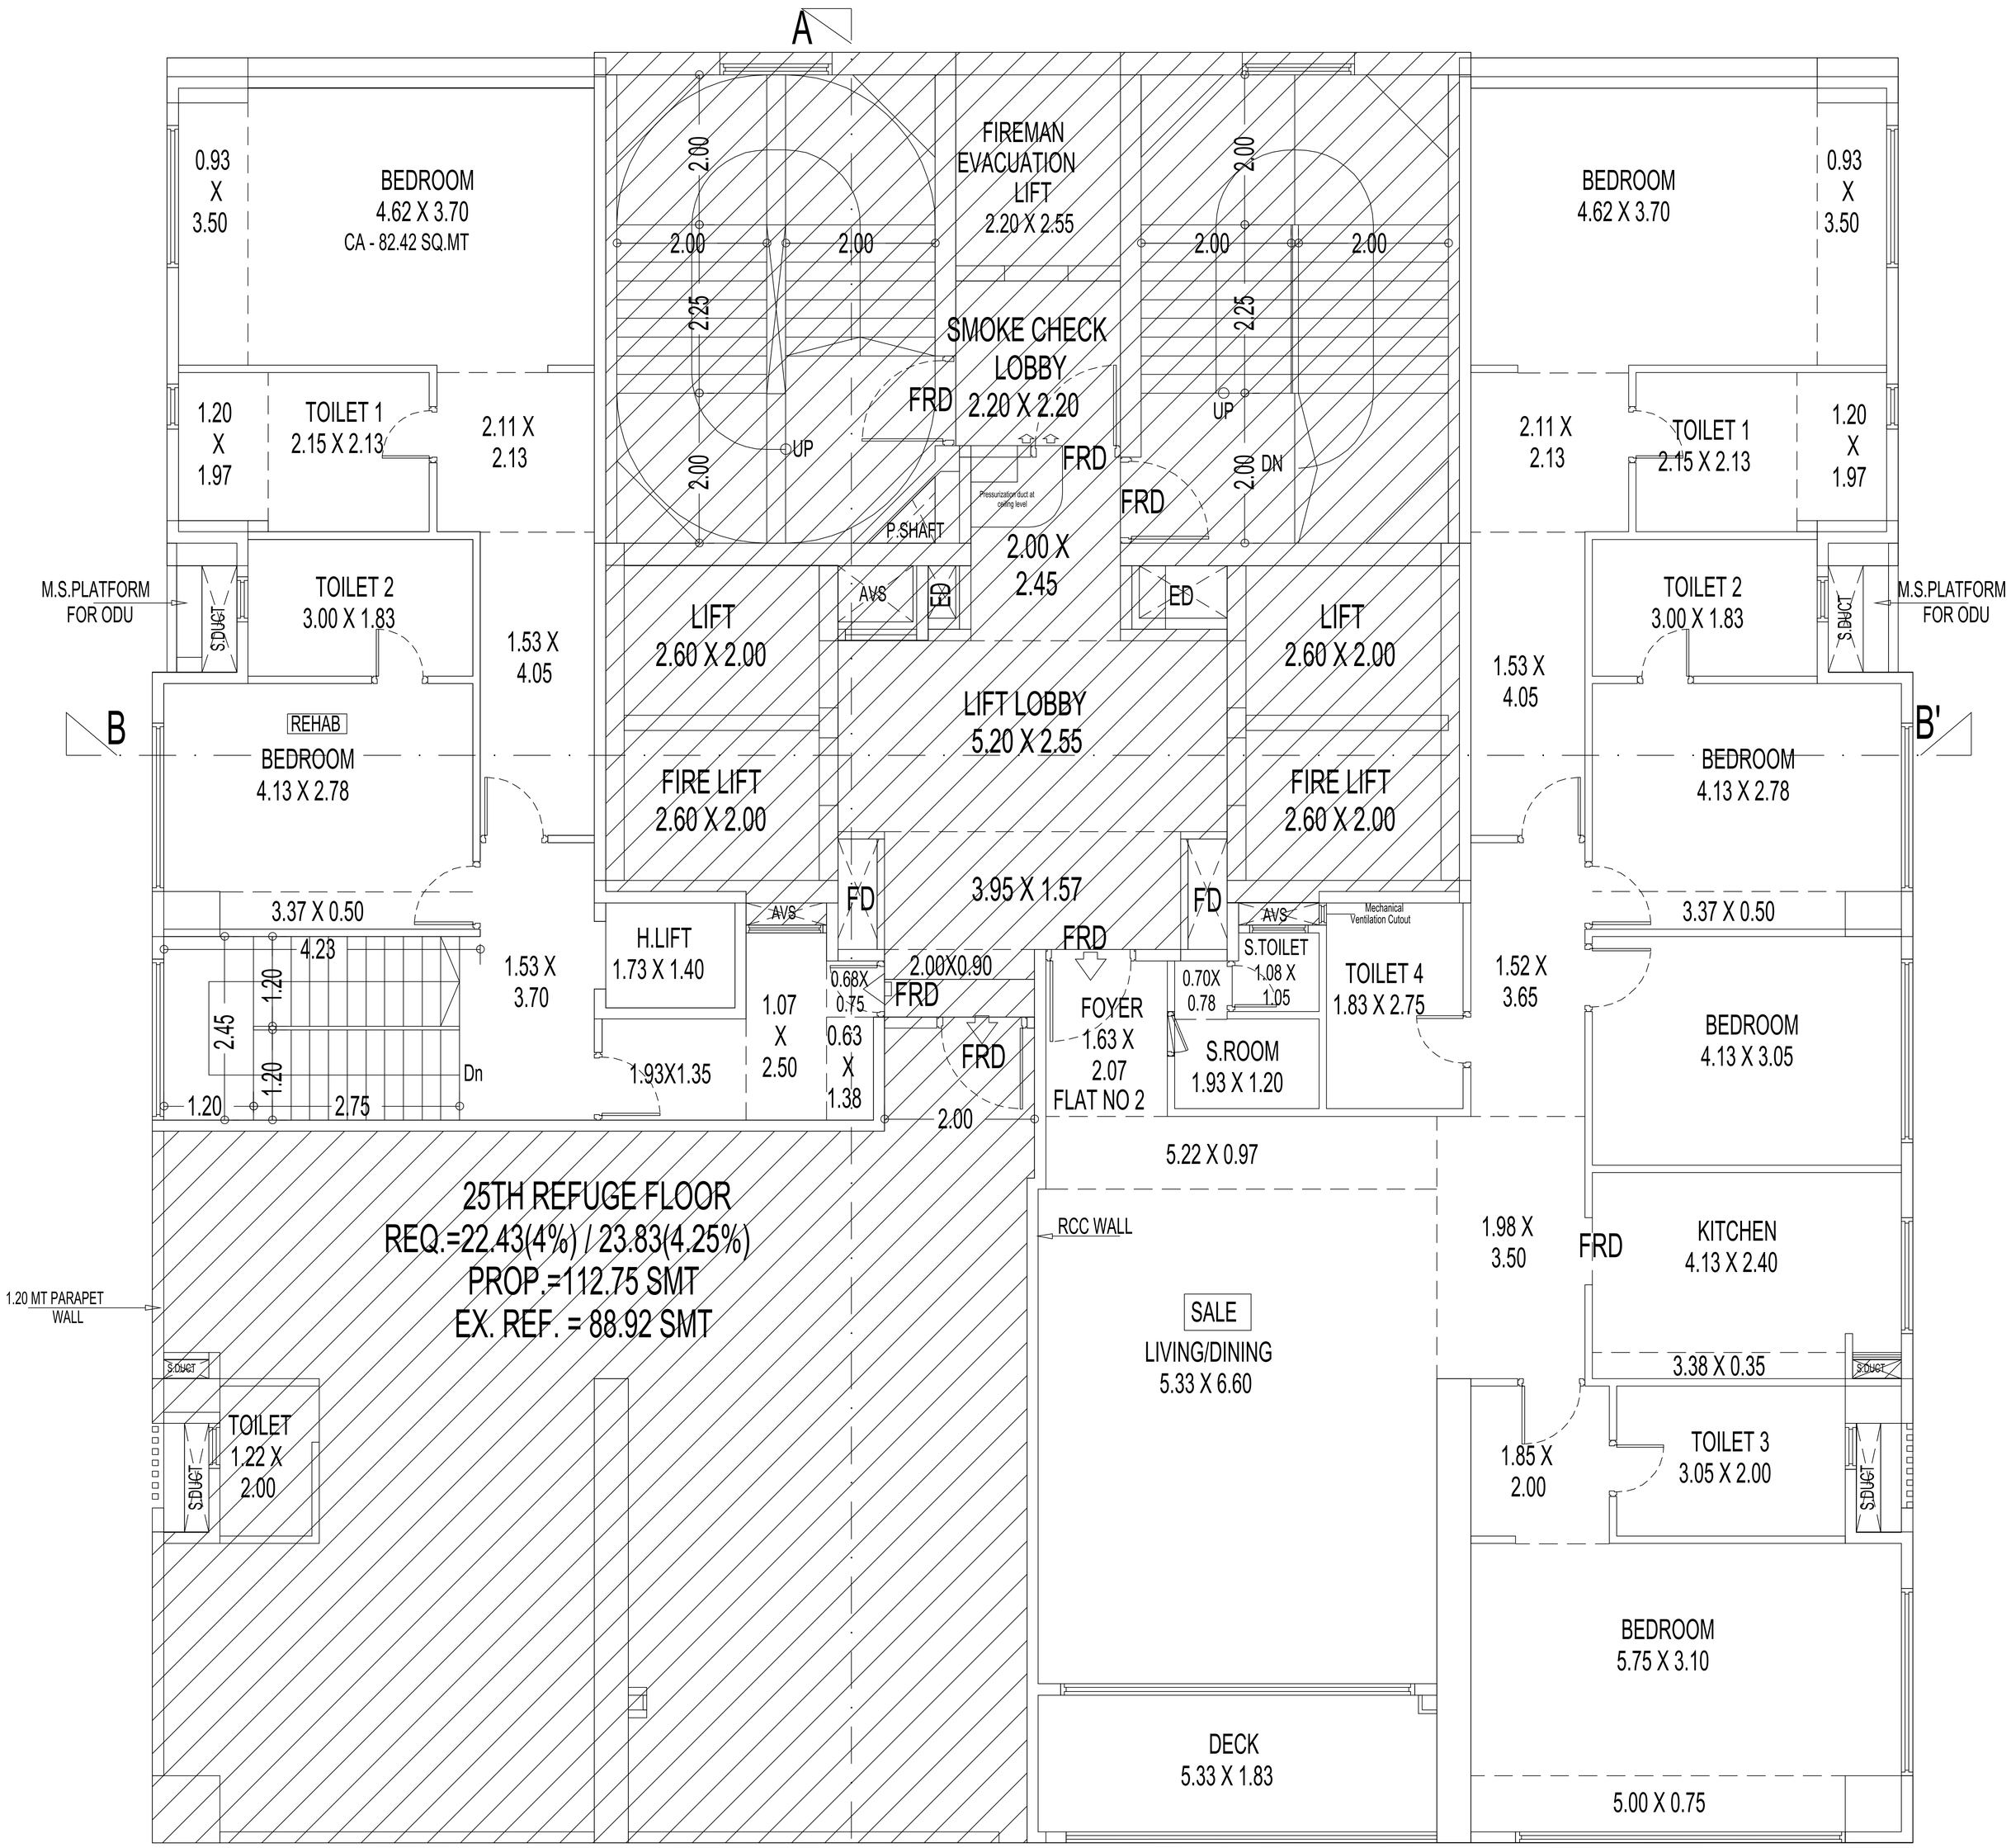

25TH REFUGE(UPPER DUPLEX)FLOOR PLAN

SCALE - 1:100



26TH FLOOR PLAN

SCALE - 1:100