

SCALE = 1 : 100

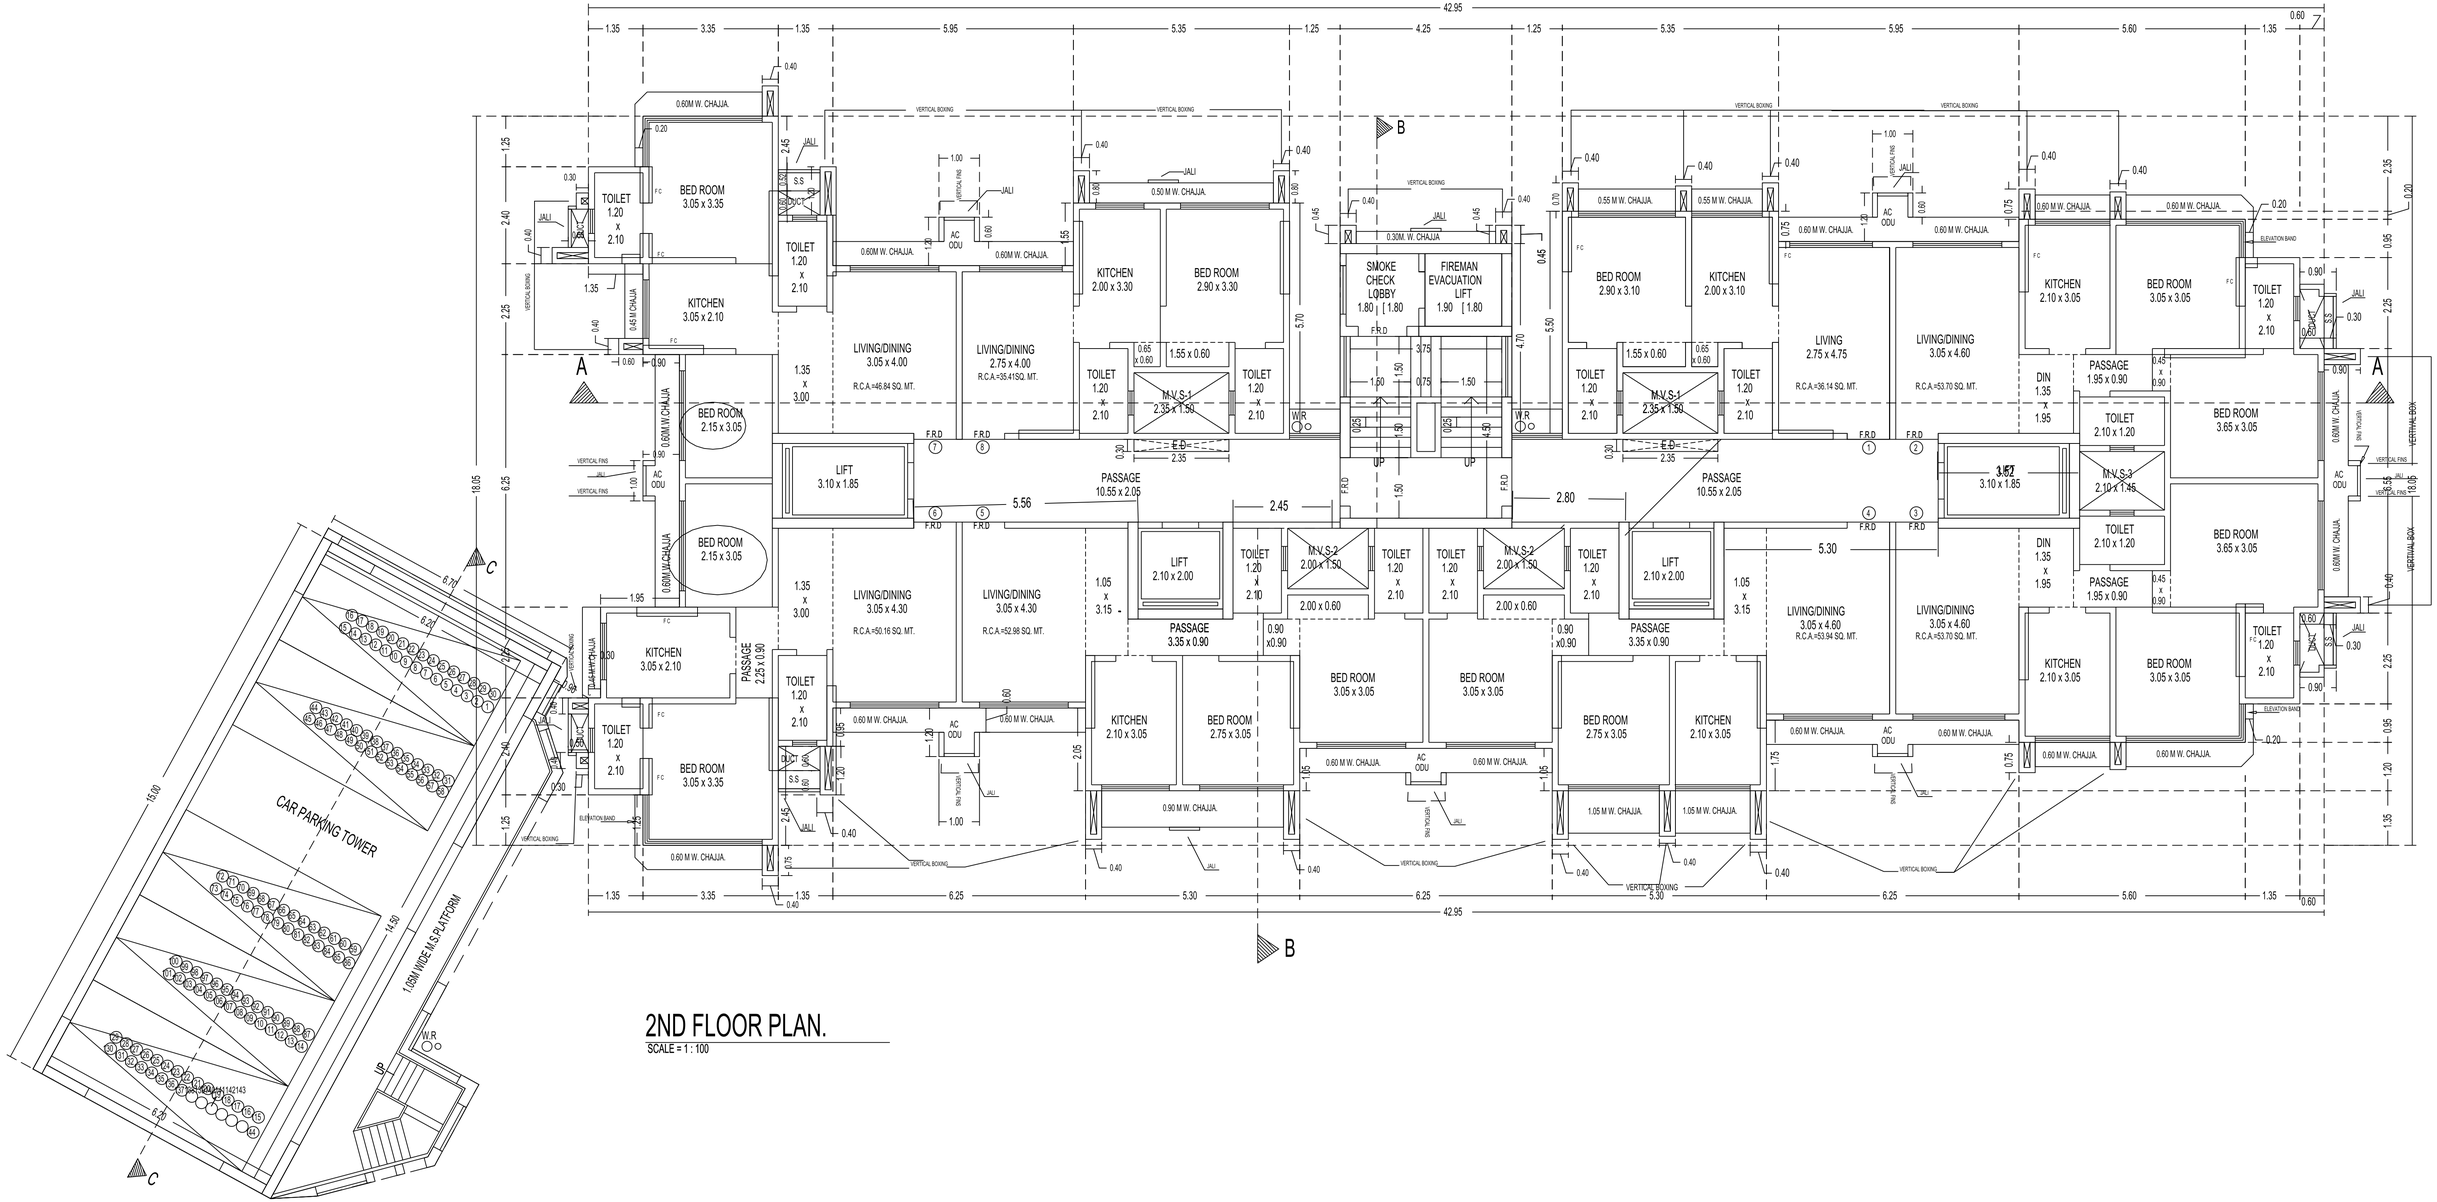


## 2ND FLOOR PLAN.


SCALE = 1 : 100

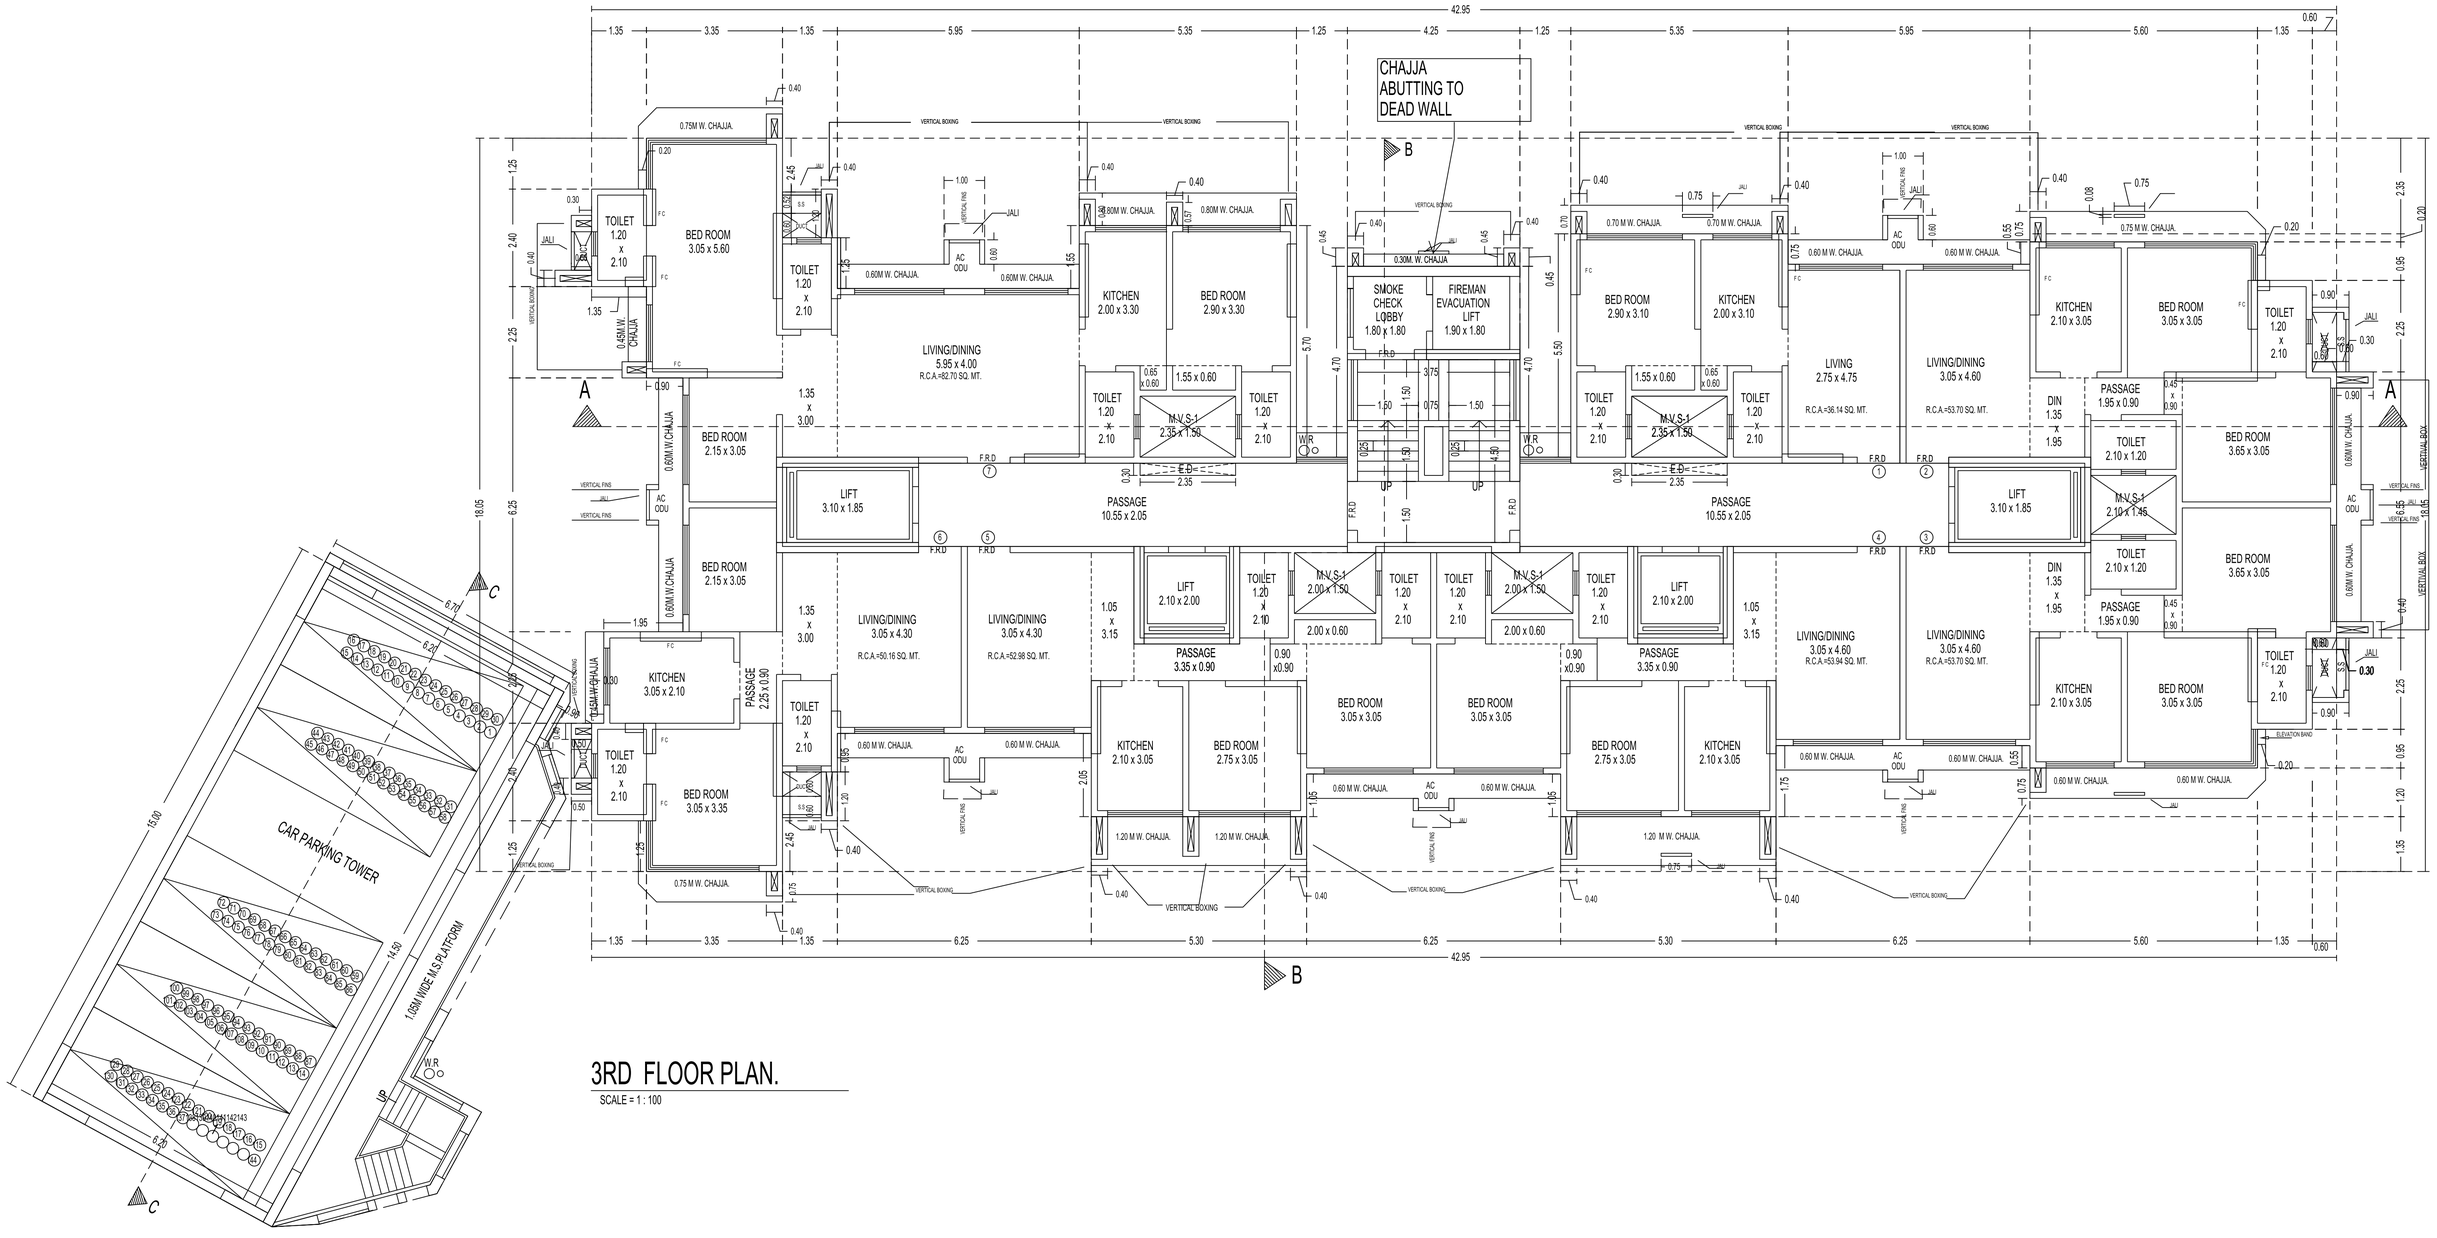


# 3RD FLOOR PLAN.


SCALE = 1 : 100

SCALE = 1 : 100

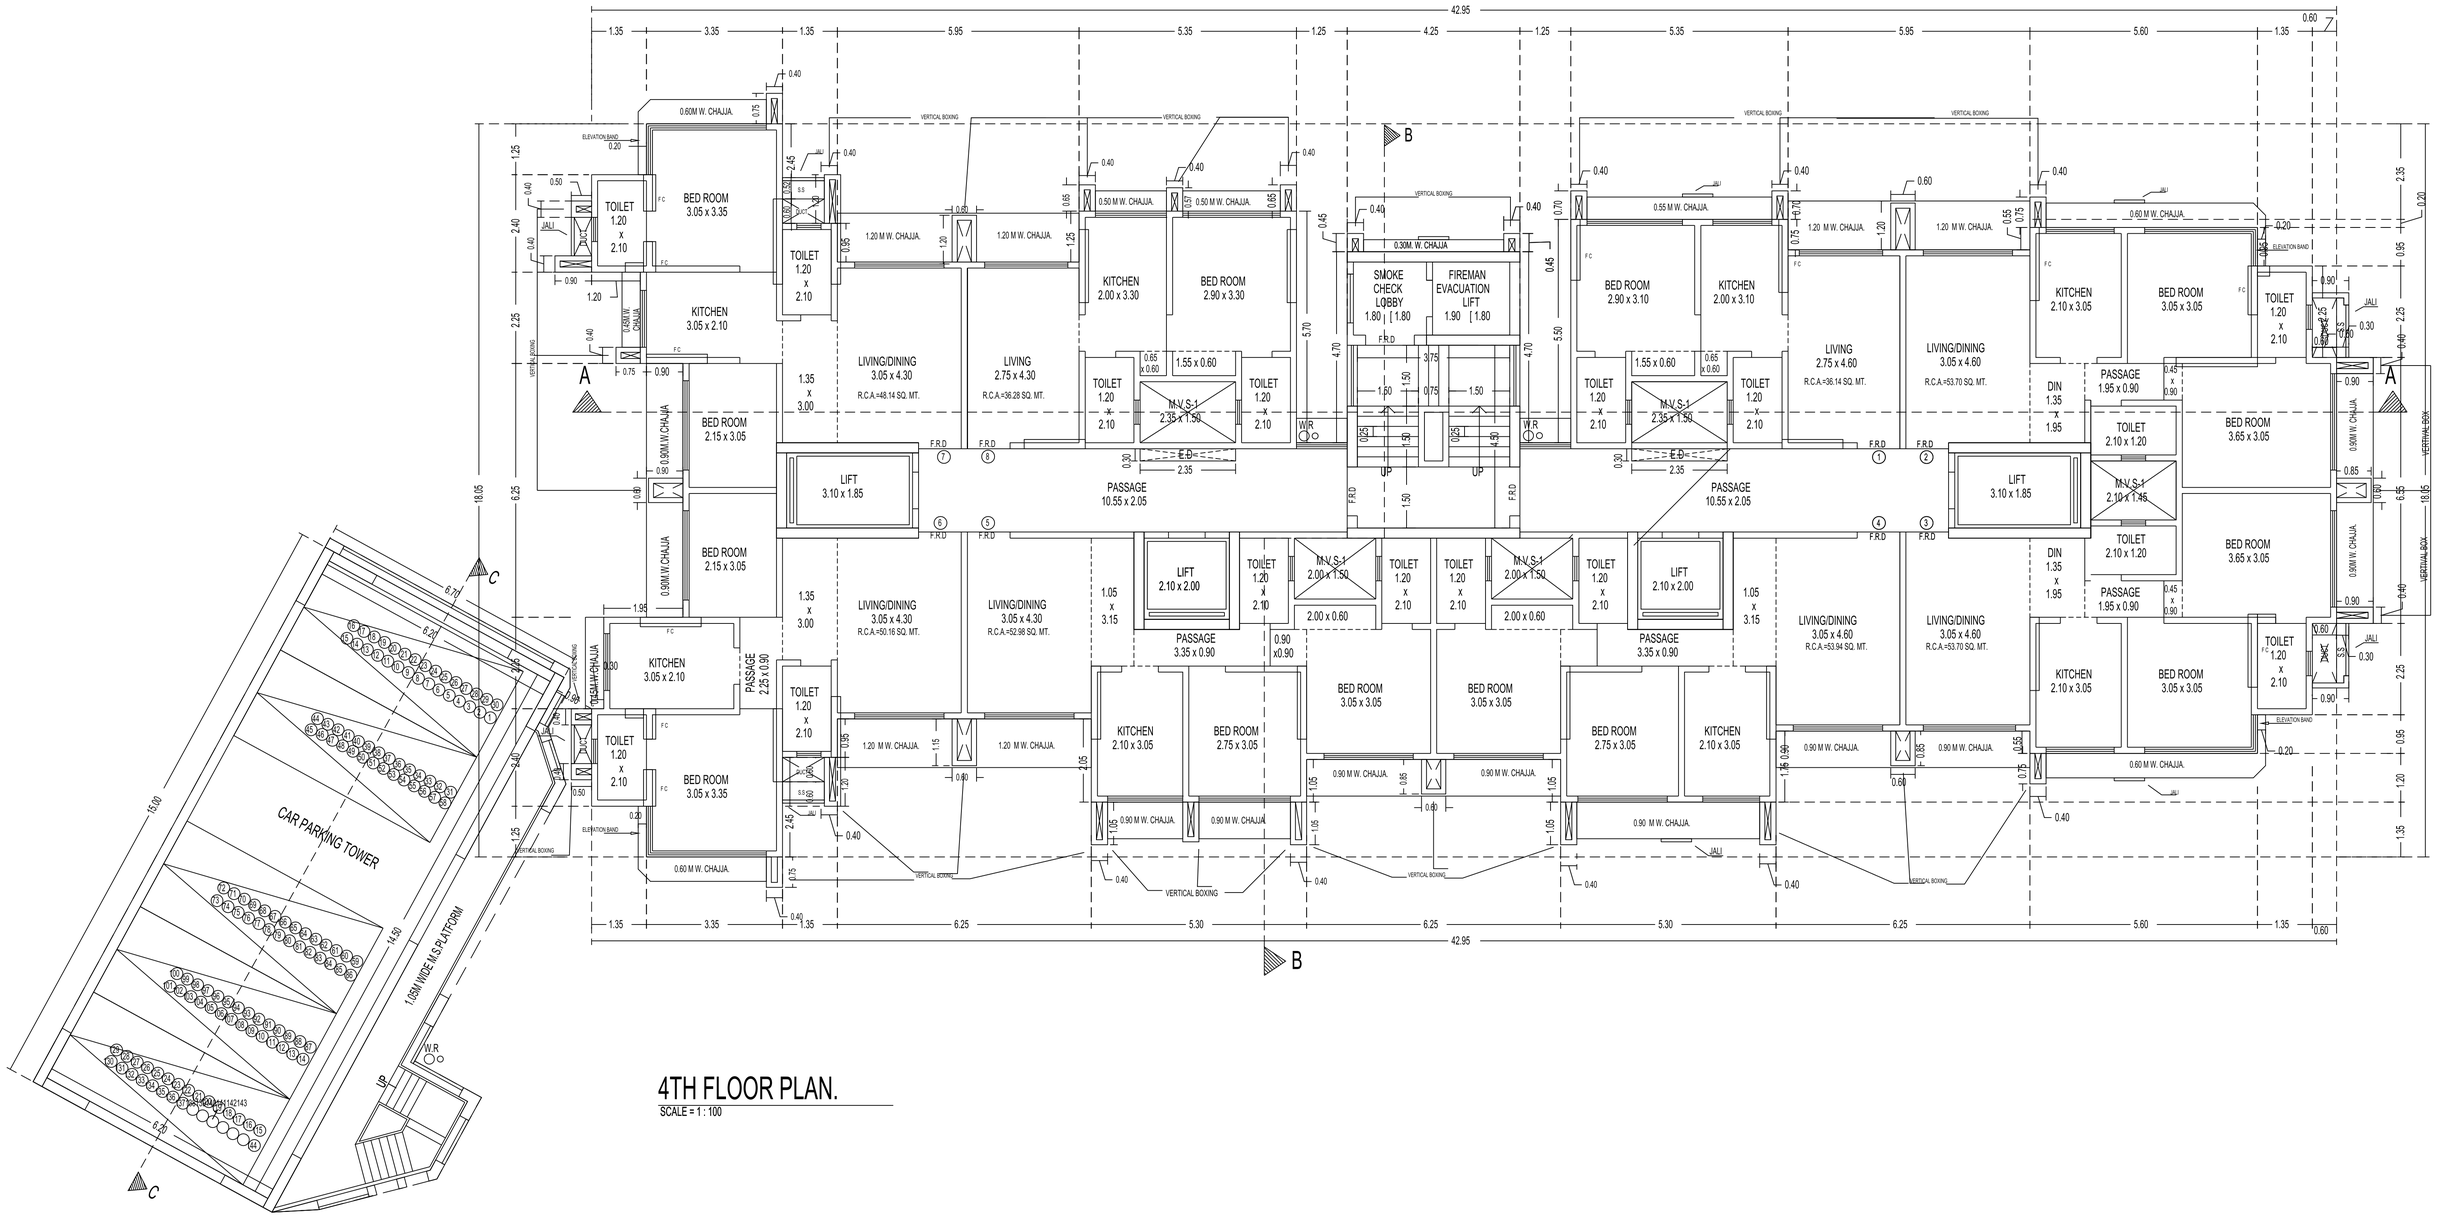



# 4TH FLOOR PLAN.


SCALE = 1 : 100

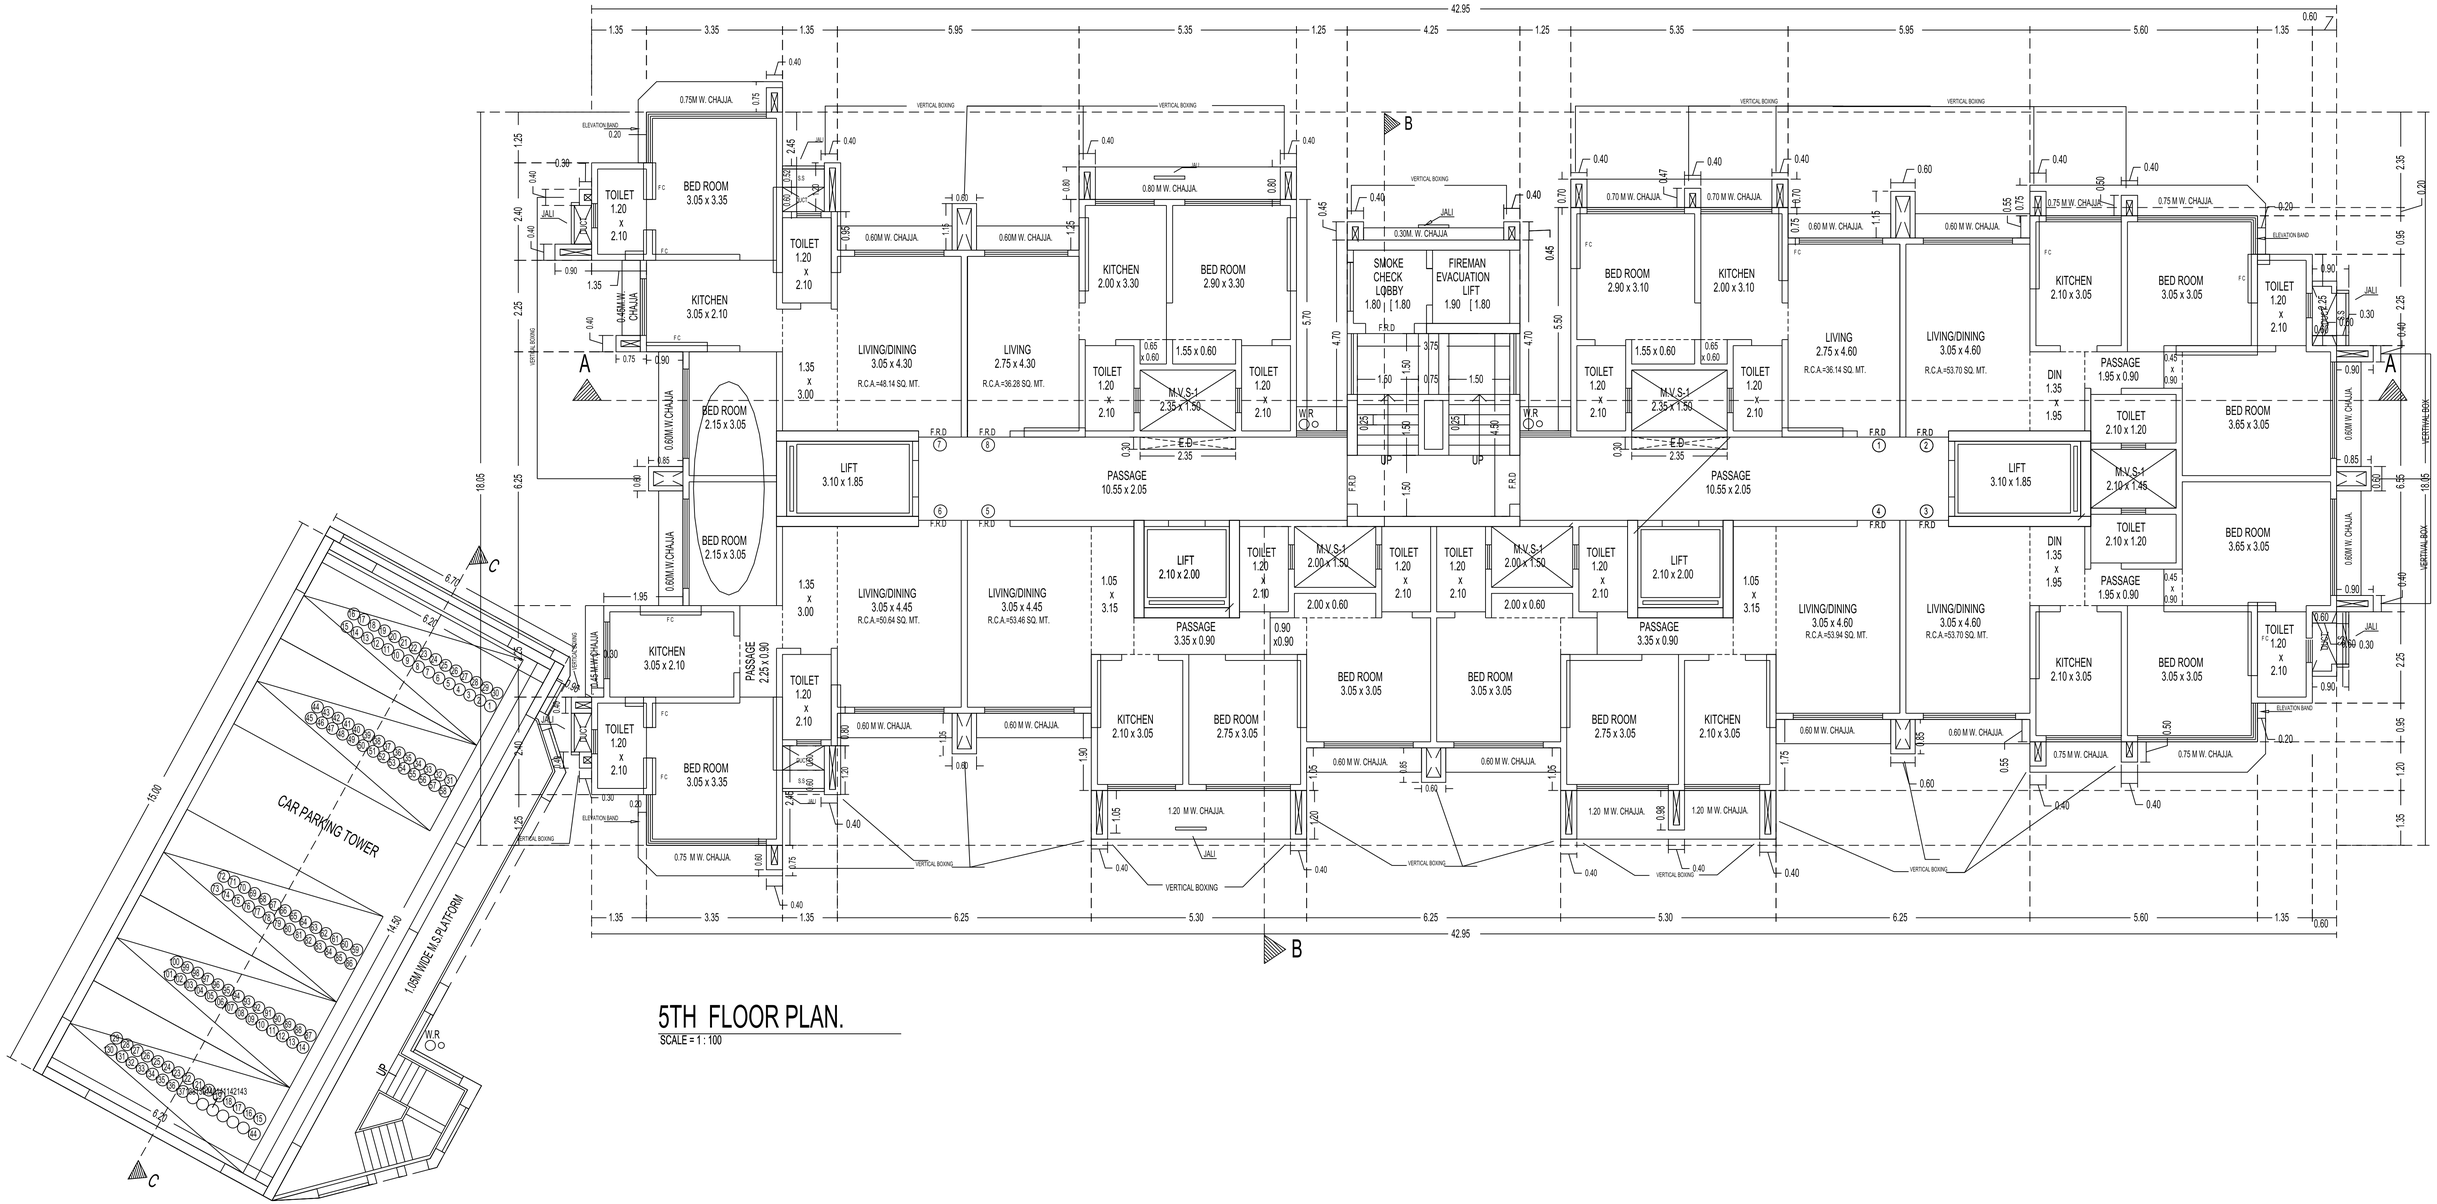



# 5TH FLOOR PLAN.

SCALE = 1 : 100

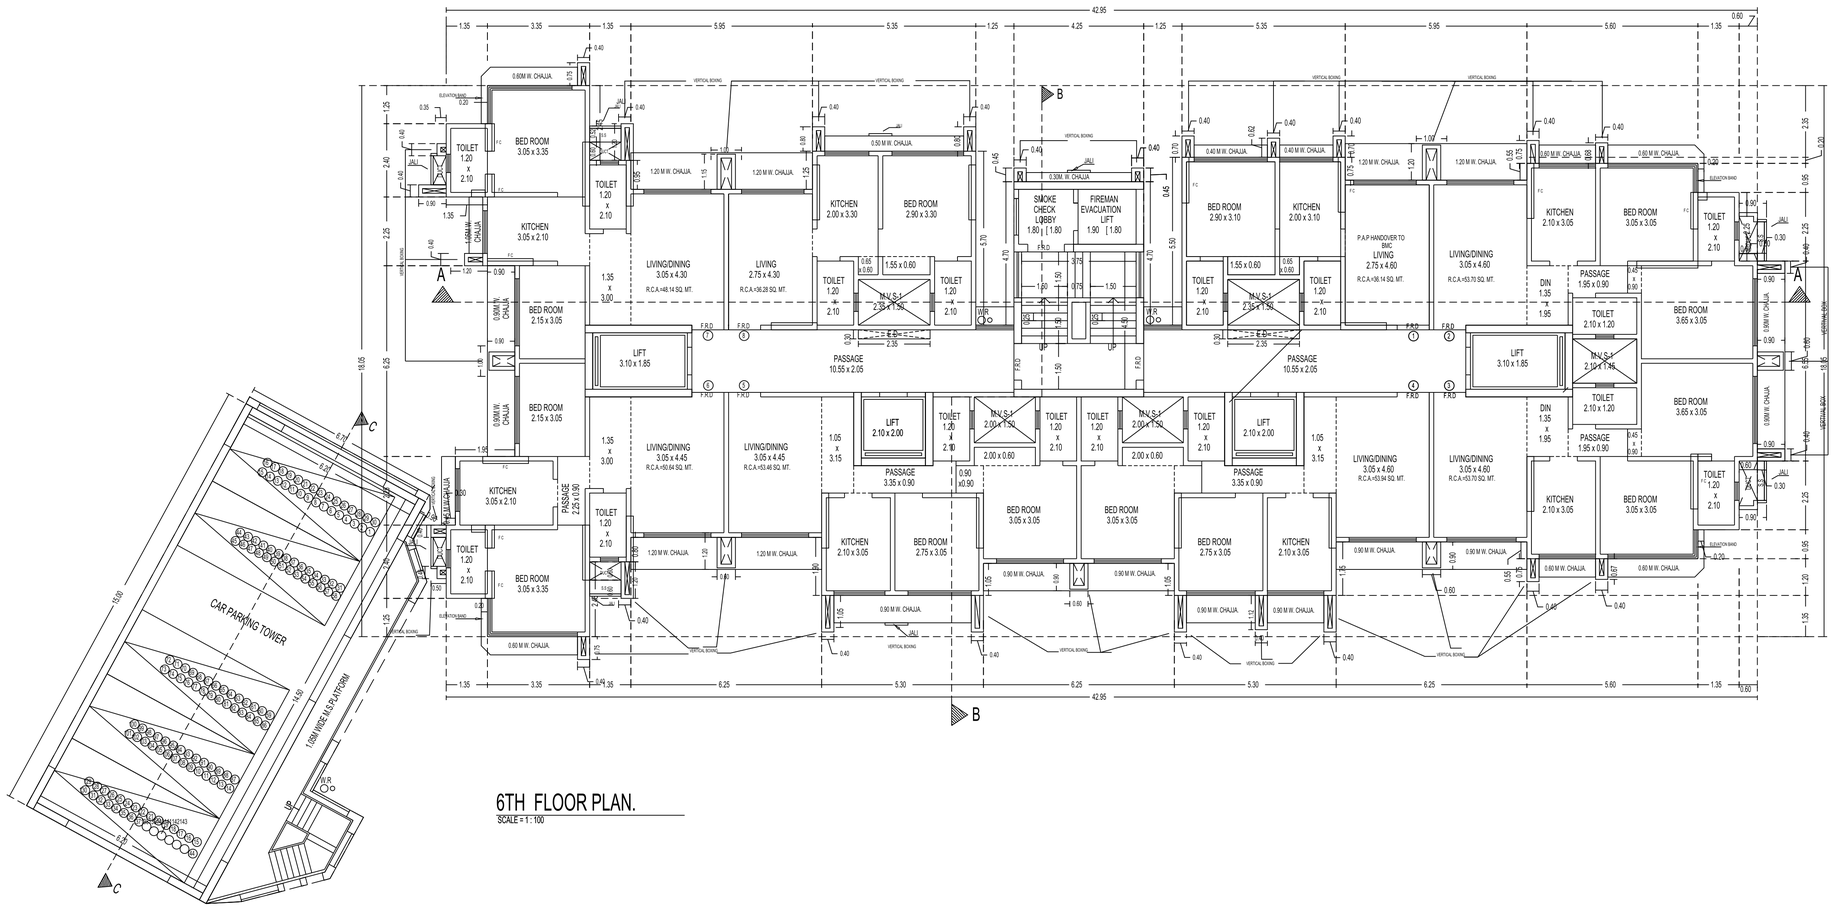
42.95
BED ROOM 3.05 x 3.35
TOILET 1.20 x 2.10
KITCHEN 3.05 x 2.10
LIVING/DINING 3.05 x 4.30
LIVING 2.75 x 4.30
BED ROOM 2.15 x 3.05
LIFT 3.10 x 1.85
PASSAGE 10.55 x 2.05
LIFT 2.10 x 2.00
M.S.-1 2.00 x 1.50
PASSAGE 3.35 x 0.90
KITCHEN 2.00 x 3.30
BED ROOM 2.90 x 3.30
SMOKE CHECK LOBBY
FIREMAN EVACUATION LIFT
BED ROOM 2.90 x 3.10
KITCHEN 2.00 x 3.10
P.A.P HANDOVER TO BMC
LIVING 2.75 x 4.60
LIVING/DINING 3.05 x 4.60
M.S.-1 2.10 x 1.45
PASSAGE 1.95 x 0.90
DIN 1.35 x 1.95
BED ROOM 3.65 x 3.05
KITCHEN 2.10 x 3.05
BED ROOM 3.05 x 3.05
BED ROOM 2.75 x 3.05
CAR PARKING TOWER
1.00M WIDE M.S.FLATFORM
SUMP
O.H.W.R
SR
6TH FLOOR PLAN.
SCALE = 1 : 100

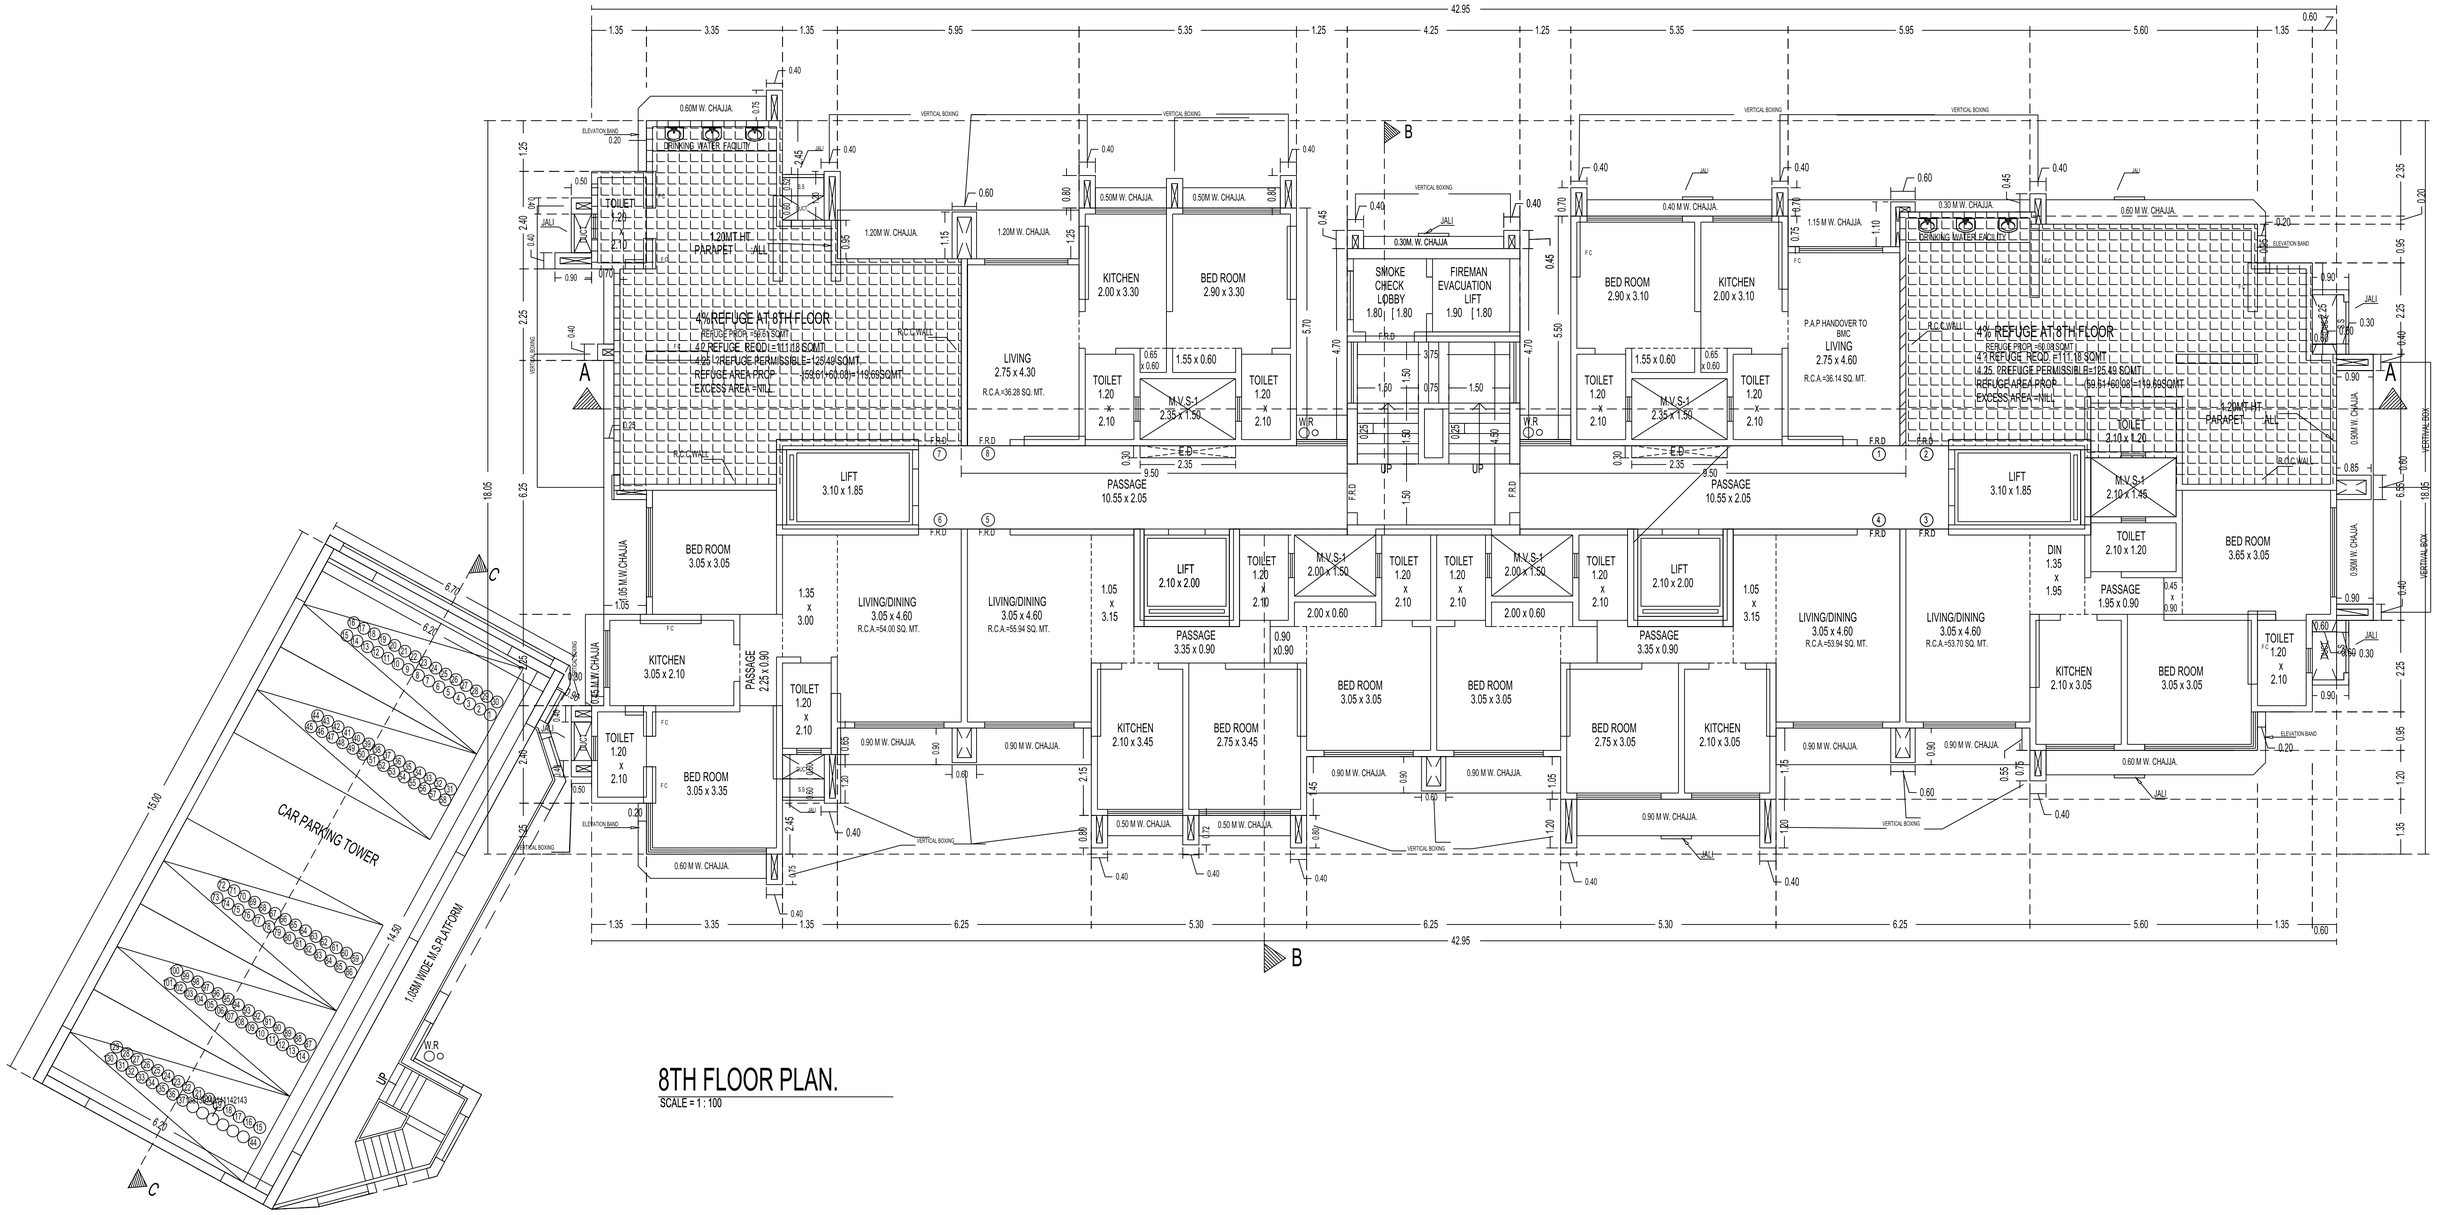

CAR PARKING TOWER
1.05M WIDE M.S PLATFORM
W.R
UP
4% REFUGE AT 8TH FLOOR
REFUGE PROP.=59.61SQMT.
4% REFUGE REQD.=111.18 SQMT.
4% OREFUGE PERMISSIBLE=125.49 SQMT.
REFUGE AREA PROP. 59.61+60.08=119.69SQMT.
EXCESS AREA =NIL
1.20MT.HT. PARAPET ALL
DRINKING WATER FACILITY
VERTICAL BOXING
ELEVATION BAND
LIFT 3.10 x 1.85
LIFT 2.10 x 2.00
PASSAGE 10.55 x 2.05
PASSAGE 3.35 x 0.90
PASSAGE 2.25 x 0.90
PASSAGE 1.95 x 0.90
LIVING 2.75 x 4.30
R.C.A.=36.28 SQ. MT.
LIVING 2.75 x 4.60
R.C.A.=36.14 SQ. MT.
LIVING/DINING 3.05 x 4.60
R.C.A.=54.00 SQ. MT.
LIVING/DINING 3.05 x 4.60
R.C.A.=55.94 SQ. MT.
LIVING/DINING 3.05 x 4.60
R.C.A.=53.94 SQ. MT.
LIVING/DINING 3.05 x 4.60
R.C.A.=53.70 SQ. MT.
KITCHEN 2.00 x 3.30
BED ROOM 2.90 x 3.30
BED ROOM 2.90 x 3.10
KITCHEN 2.00 x 3.10
KITCHEN 3.05 x 2.10
BED ROOM 3.05 x 3.35
KITCHEN 2.10 x 3.45
BED ROOM 2.75 x 3.45
BED ROOM 3.05 x 3.05
BED ROOM 2.75 x 3.05
KITCHEN 2.10 x 3.05
BED ROOM 3.65 x 3.05
KITCHEN 2.10 x 3.05
BED ROOM 3.05 x 3.05
SMOKE CHECK LOBBY 1.80 [ 1.80
FIREMAN EVACUATION LIFT 1.90 [ 1.80
P.A.P HANDOVER TO BMC
DIN 1.35 x 1.95
TOILET 1.20 x 2.10
M.V.S-1 2.35 x 1.50
M.V.S-1 2.00 x 1.50
M.V.S-1 2.10 x 1.45
1.55 x 0.60
2.00 x 0.60
0.65 x 0.60
42.95
18.05
15.00
14.50
8TH FLOOR PLAN.
SCALE = 1 : 100

SCALE = 1 : 100

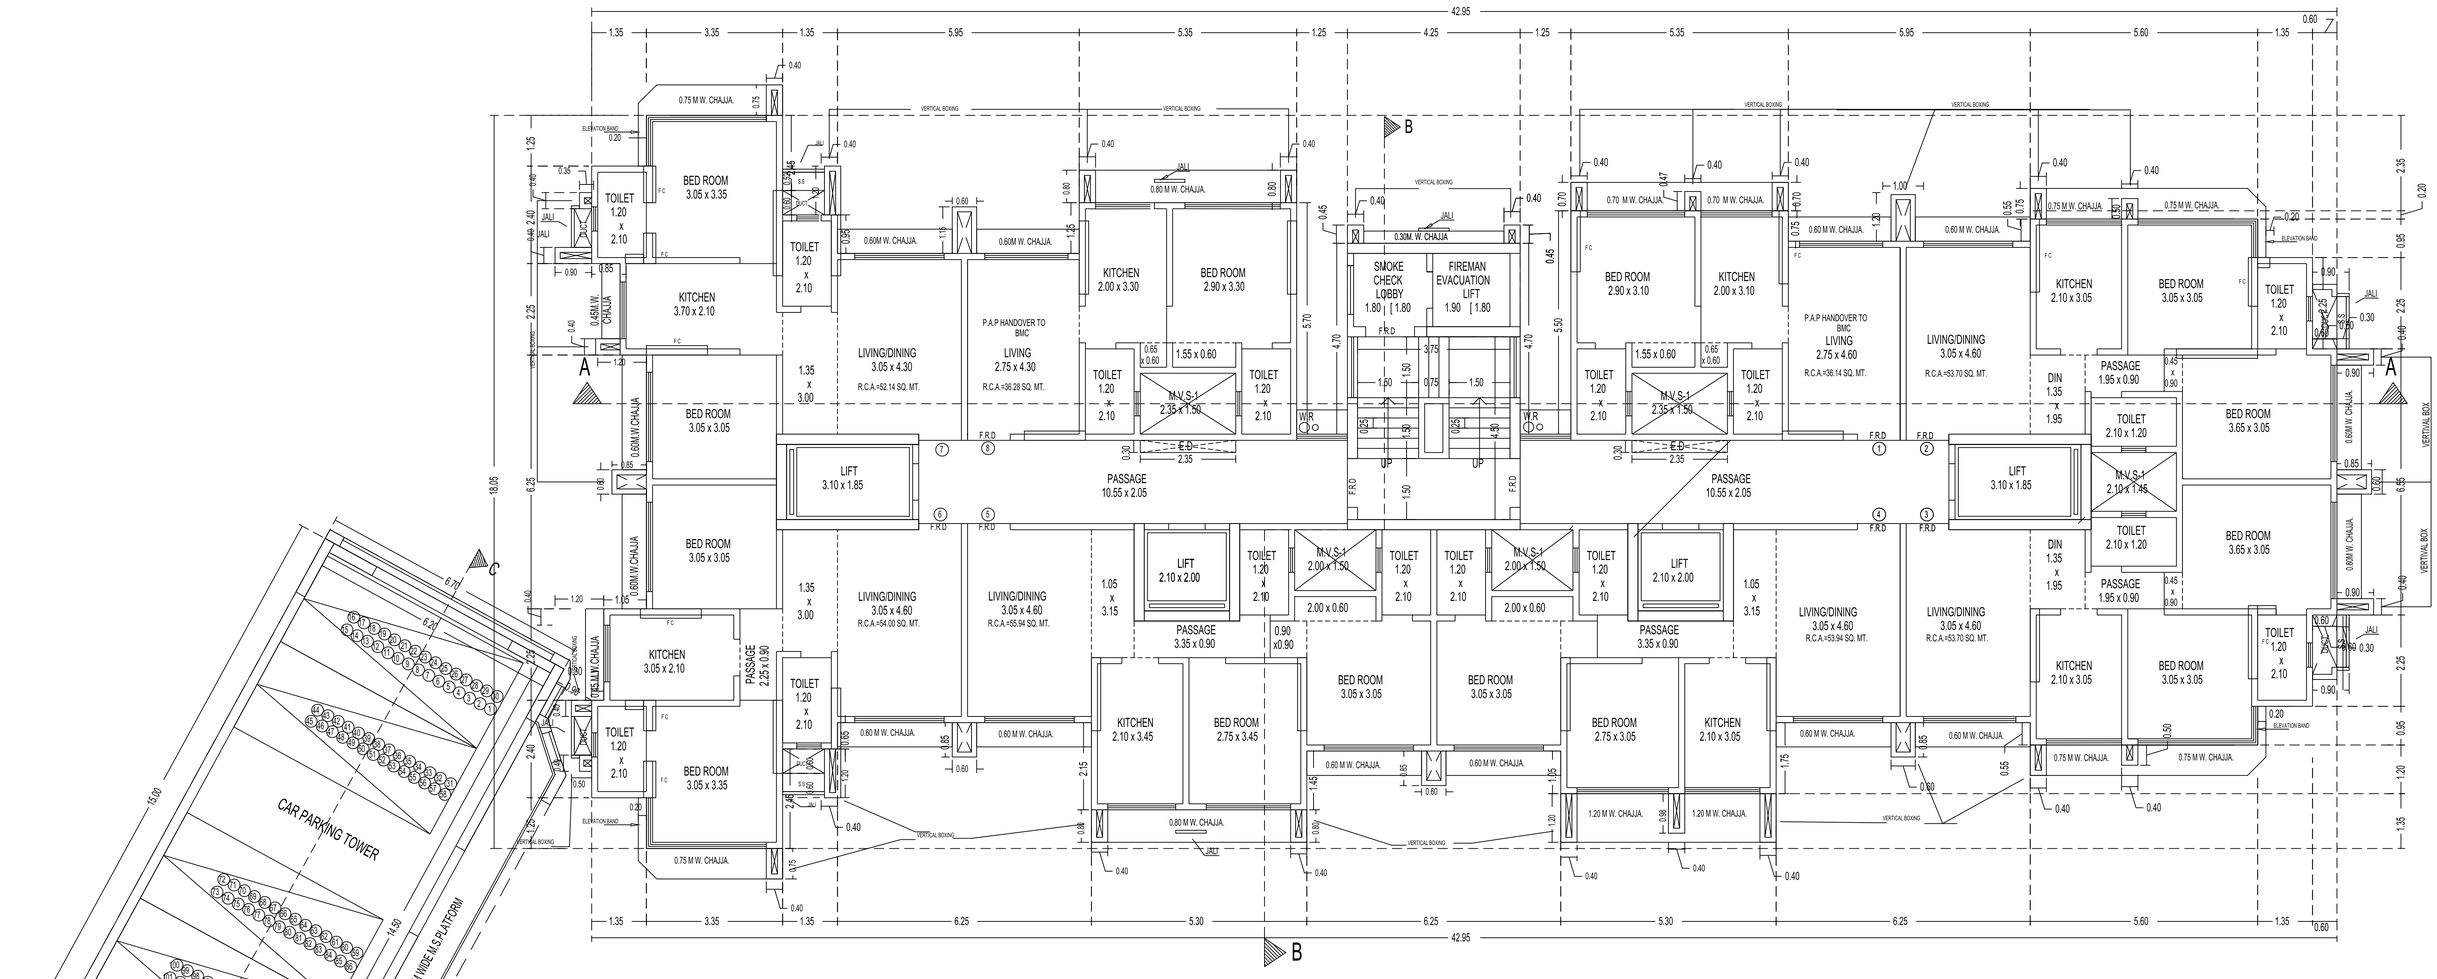


# 9TH FLOOR PLAN.


SCALE = 1 : 100

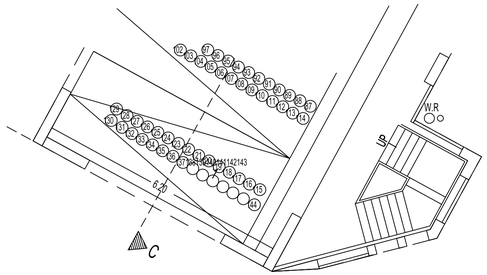


## 11TH FLOOR PLAN.


SCALE = 1 : 100

MENTION AH /RR TENEMENTS TO BE HANDED OVER TO BMC

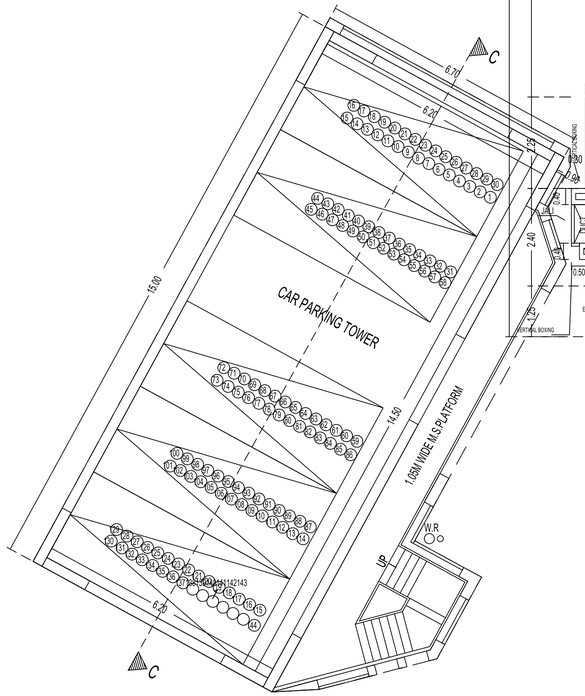


## 10TH FLOOR PLAN.


SCALE = 1 : 100

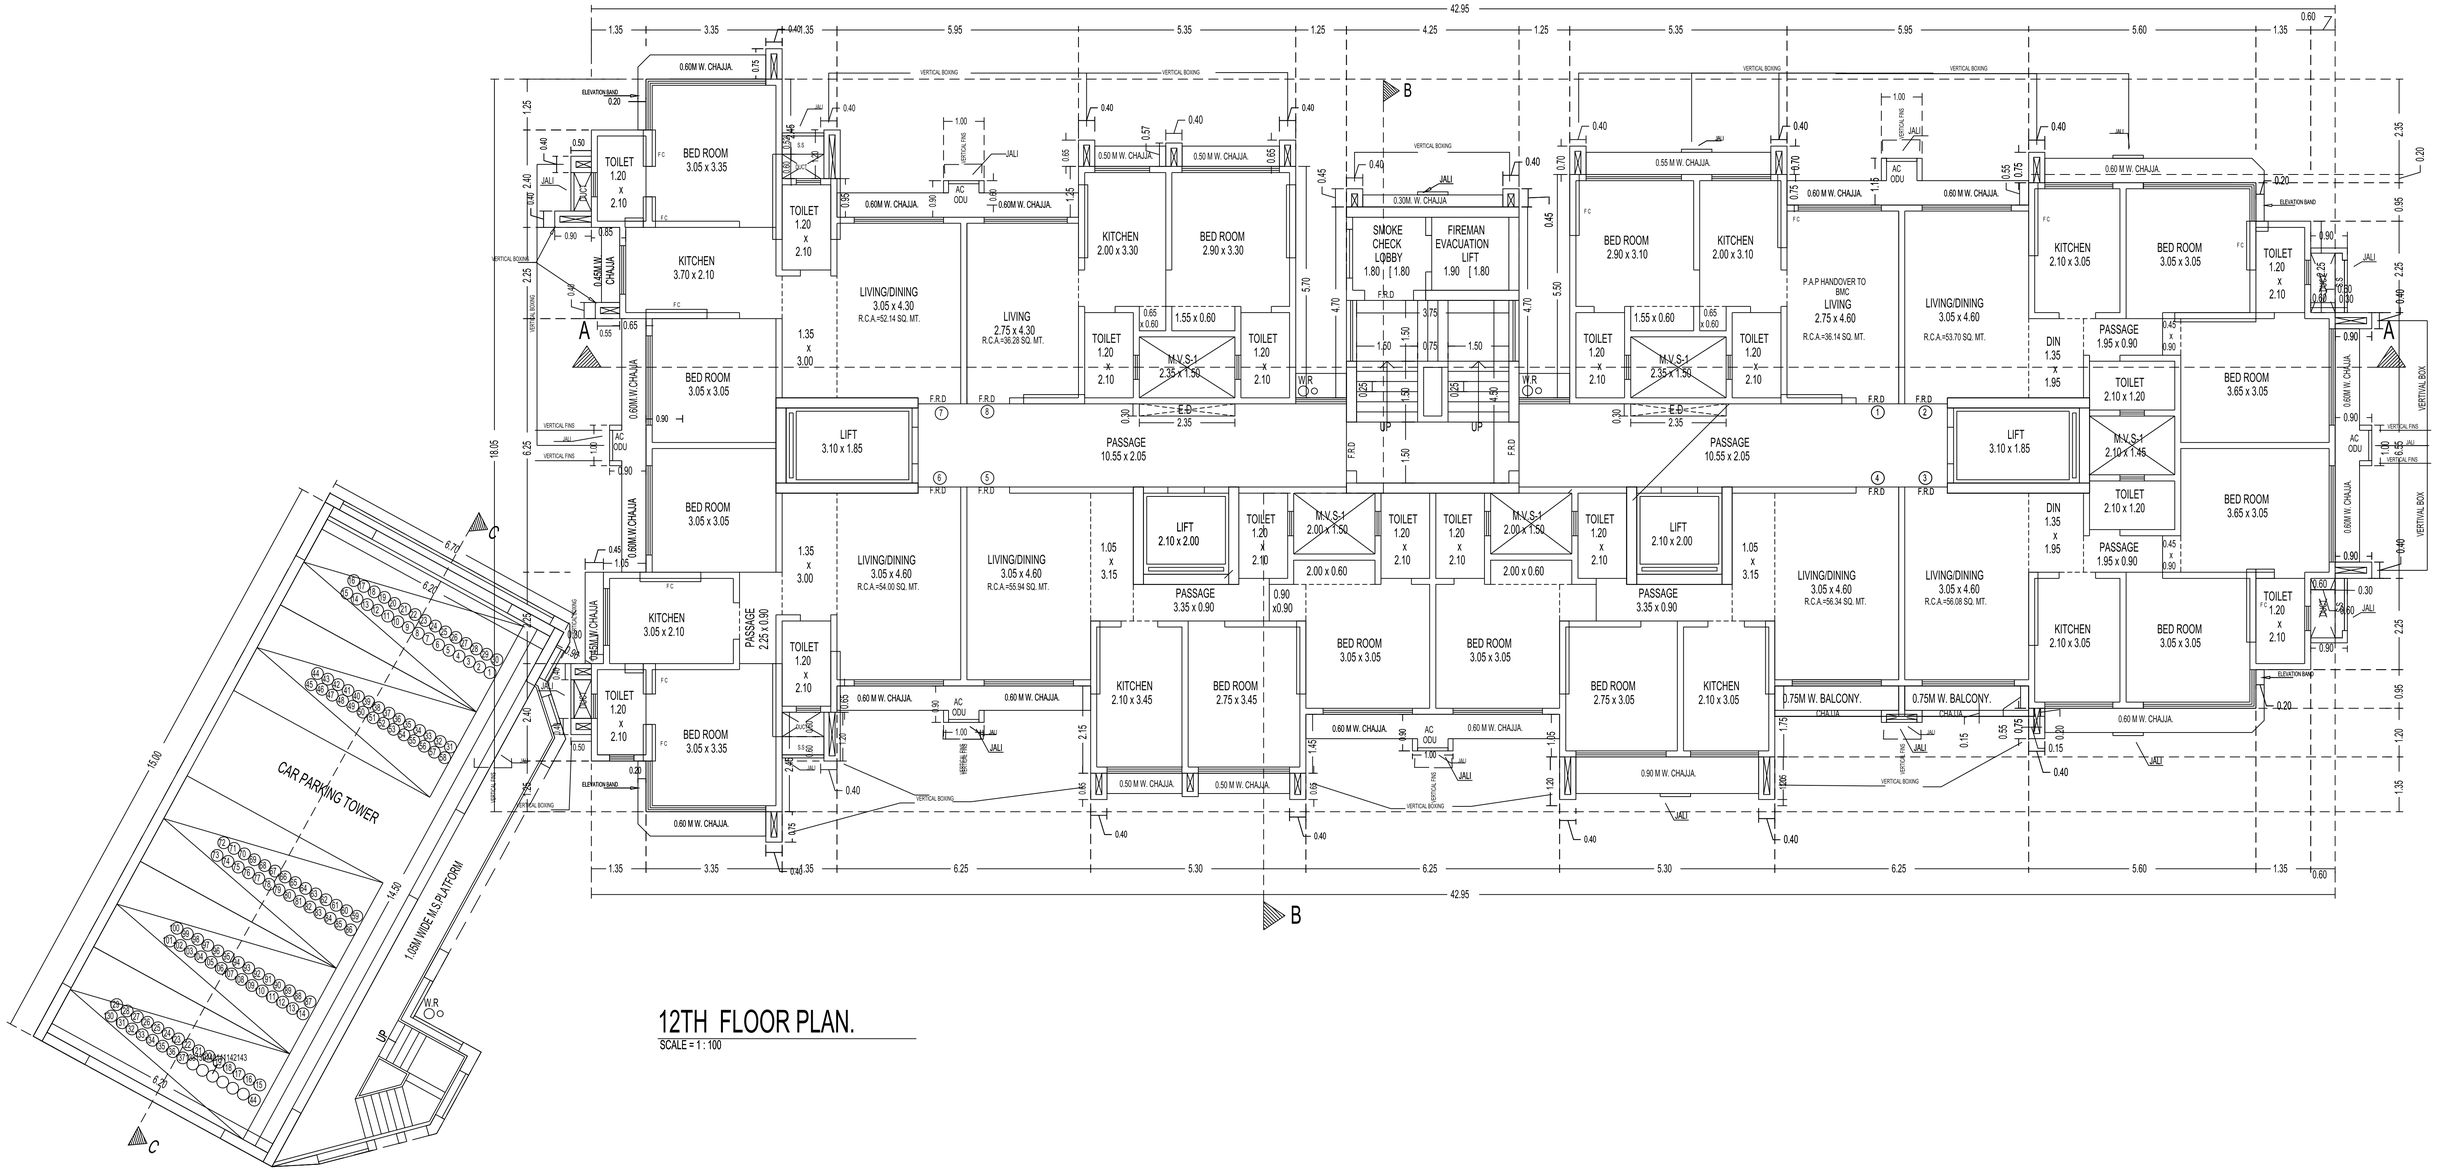


# 12TH FLOOR PLAN.

SCALE = 1 : 100

14TH FLOOR PLAN.
SCALE = 1 : 100

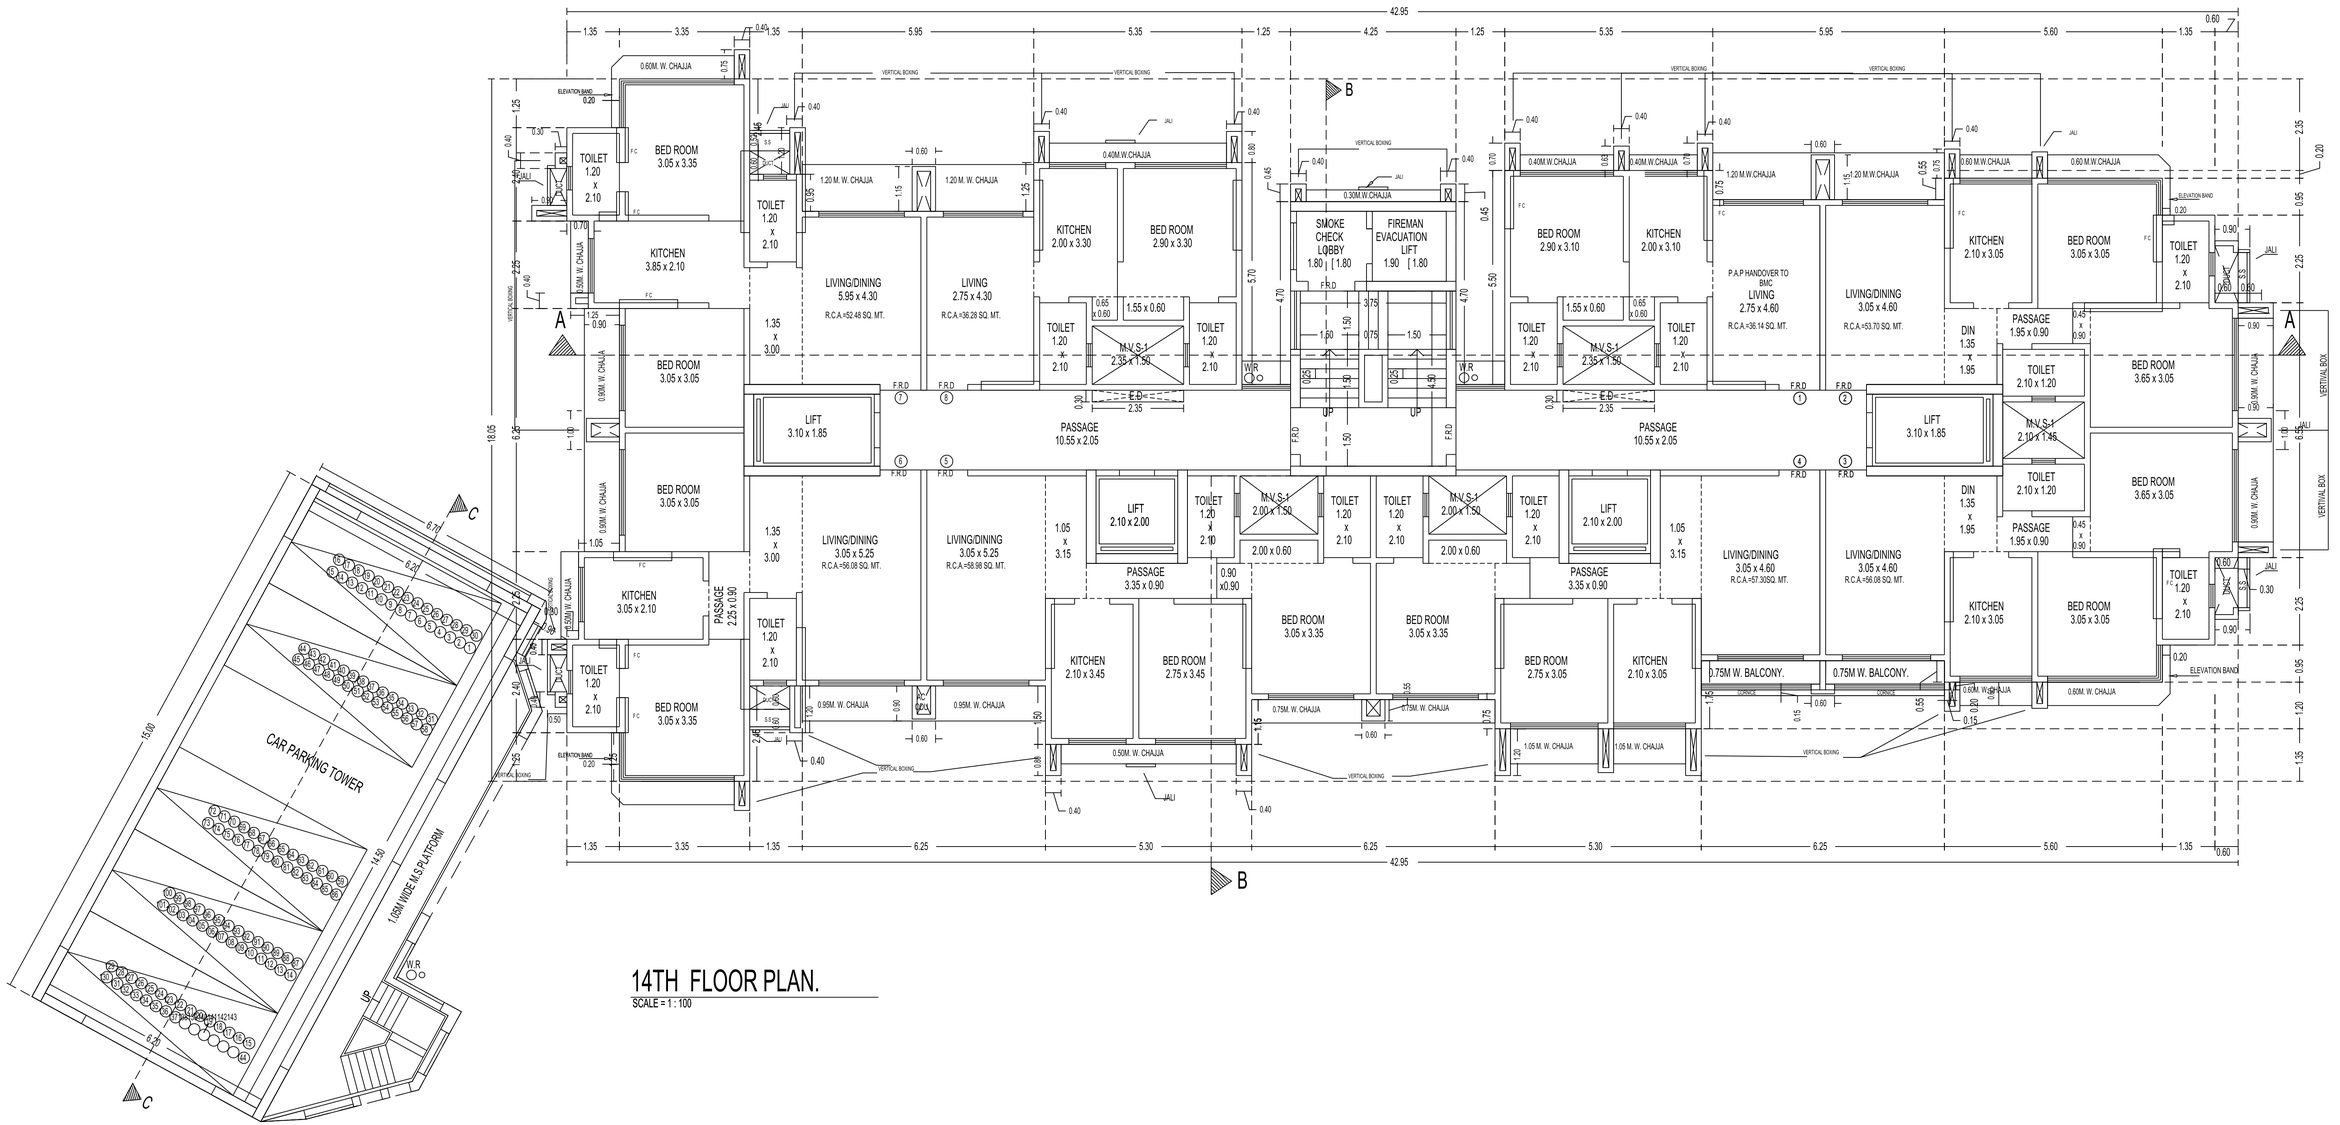


14TH FLOOR PLAN.
SCALE = 1 : 100

SCALE = 1 : 100

| 8TH FLOOR | | | | | | | | | |
|---|---|---|---|---|---|---|---|---|---|
| 1 | 3.05 | X | 4.90 | X | 1 | 1O | = | 14.94 | SQ.MT. |
| 2 | 1.35 | X | 5.45 | X | 1 | 1O | = | 7.36 | SQ.MT. |
| 3 | 2.25 | X | 5.75 | X | 1 | 1O | = | 12.94 | SQ.MT. |
| 4 | 2.00 | X | 0.95 | X | 1 | 1O | = | 1.90 | SQ.MT. |
| 5 | 3.35 | X | 2.25 | X | 1 | 1O | = | 7.54 | SQ.MT. |
| 6 | 3.95 | X | 3.20 | X | 1 | 1O | = | 12.64 | SQ.MT. |
| | | | | | TOTAL | | = | 57.32 | SQ.MT. -Y |
| TOTAL PROPOSED REFUGE AREA (X+Y) | | | | | | | = | 113.94 | SQ.MT. -X |

## REFUGE AREA REQU. AT 15th. FLOOR

TOTAL B. U. AREA OF 15 TH. TO 20TH(PT). FLOOR.

| | | |
|---|---|---|
| 15TH. FLR. | = 330.38 | 2448.06 SQ.MT. |
| 16TH. FLR. | = 450.49 | |
| 17TH. FLR. | = 451.29 | |
| 18TH. FLR. | = 453.07 | |
| 19TH. FLR. | = 455.79 | |
| 20TH.(PT) FLR. | = 307.04 | |


TOTAL REFUGE AREA REQD. = 4.00 % x TOTAL B.U.A. OF 7 FLR.


= 4.00 % x 2448.06 = 97.92 SQMT.

MAX. REFUGE AREA PERM. = 4.25 % x TOTAL B.U.A. OF 7 FLR.

= 4.25 % x 2448.06 = 104.04 SQMT.

| | | |
|---|---|---|
| TOTAL REFUGE AREA PROV. AT 15th. FLR. | = | 113.94 SQ.MT. |
| EXCESS AREA | = | 9.90 SQMT |

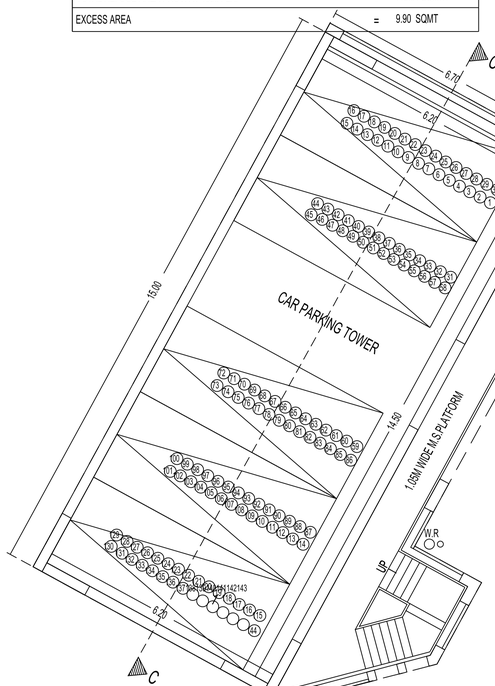

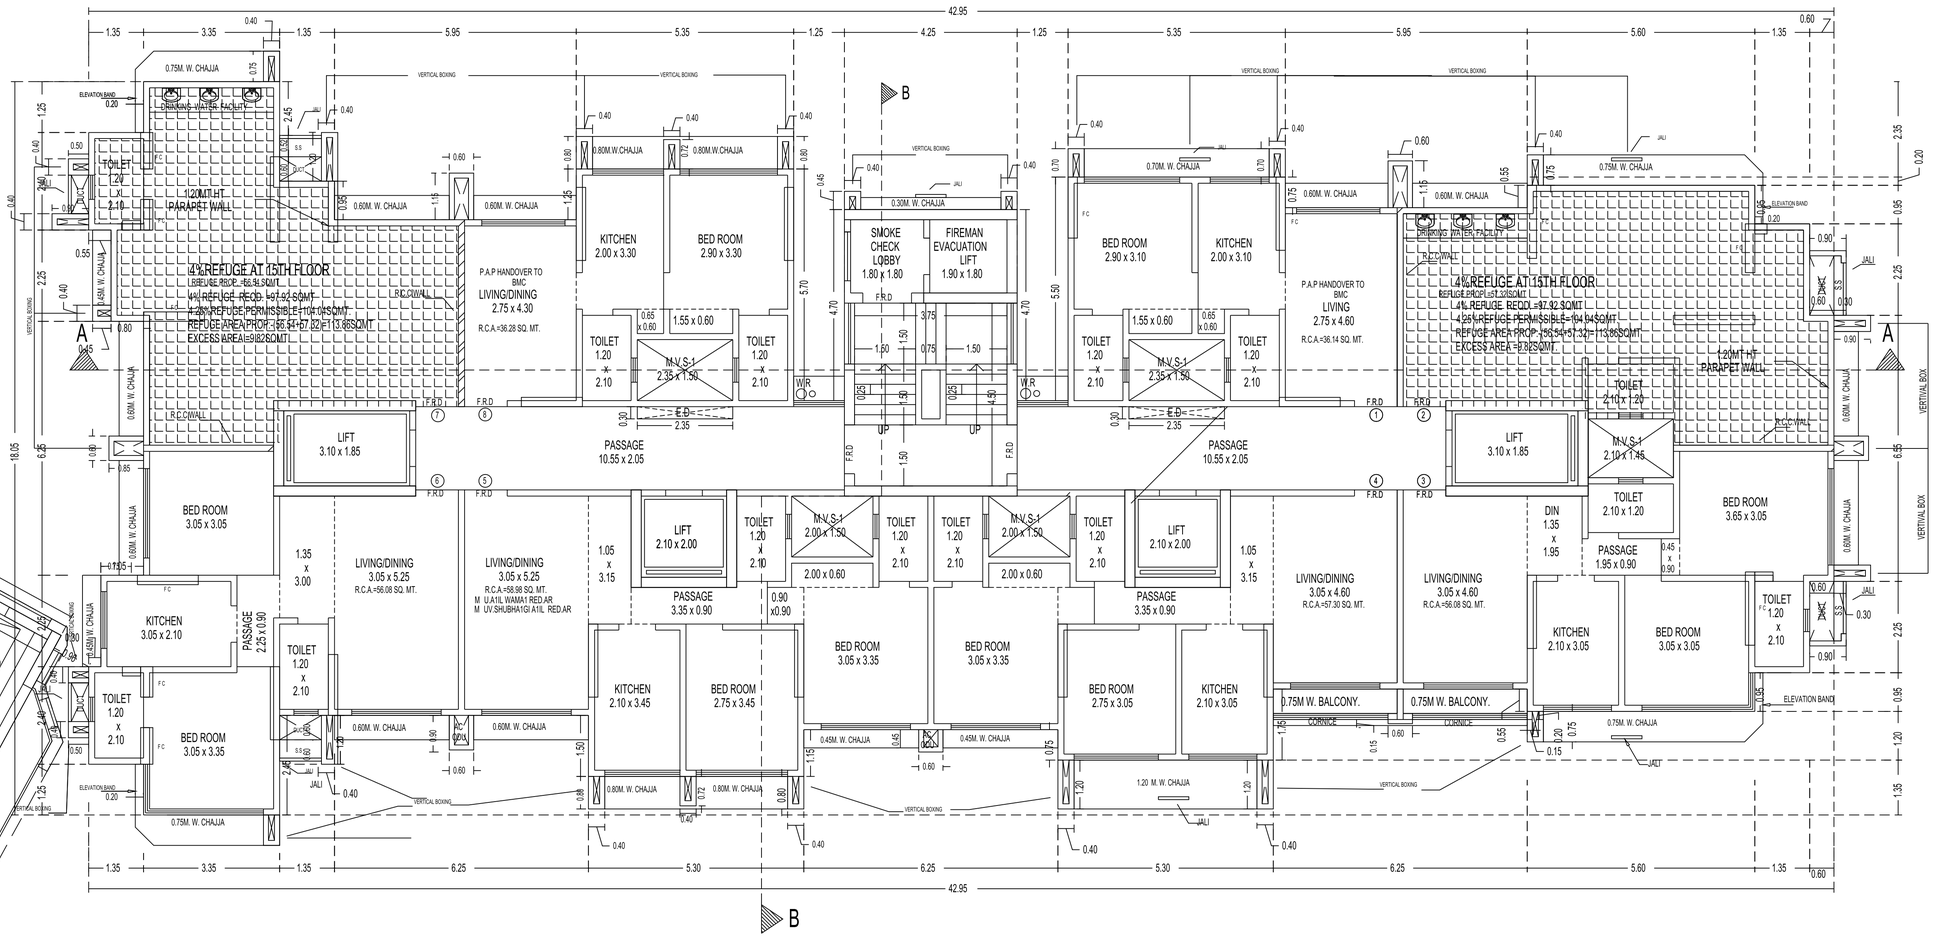




# 15TH FLOOR PLAN.

SCALE = 1 : 100


16TH FLOOR PLAN.
SCALE = 1 : 100

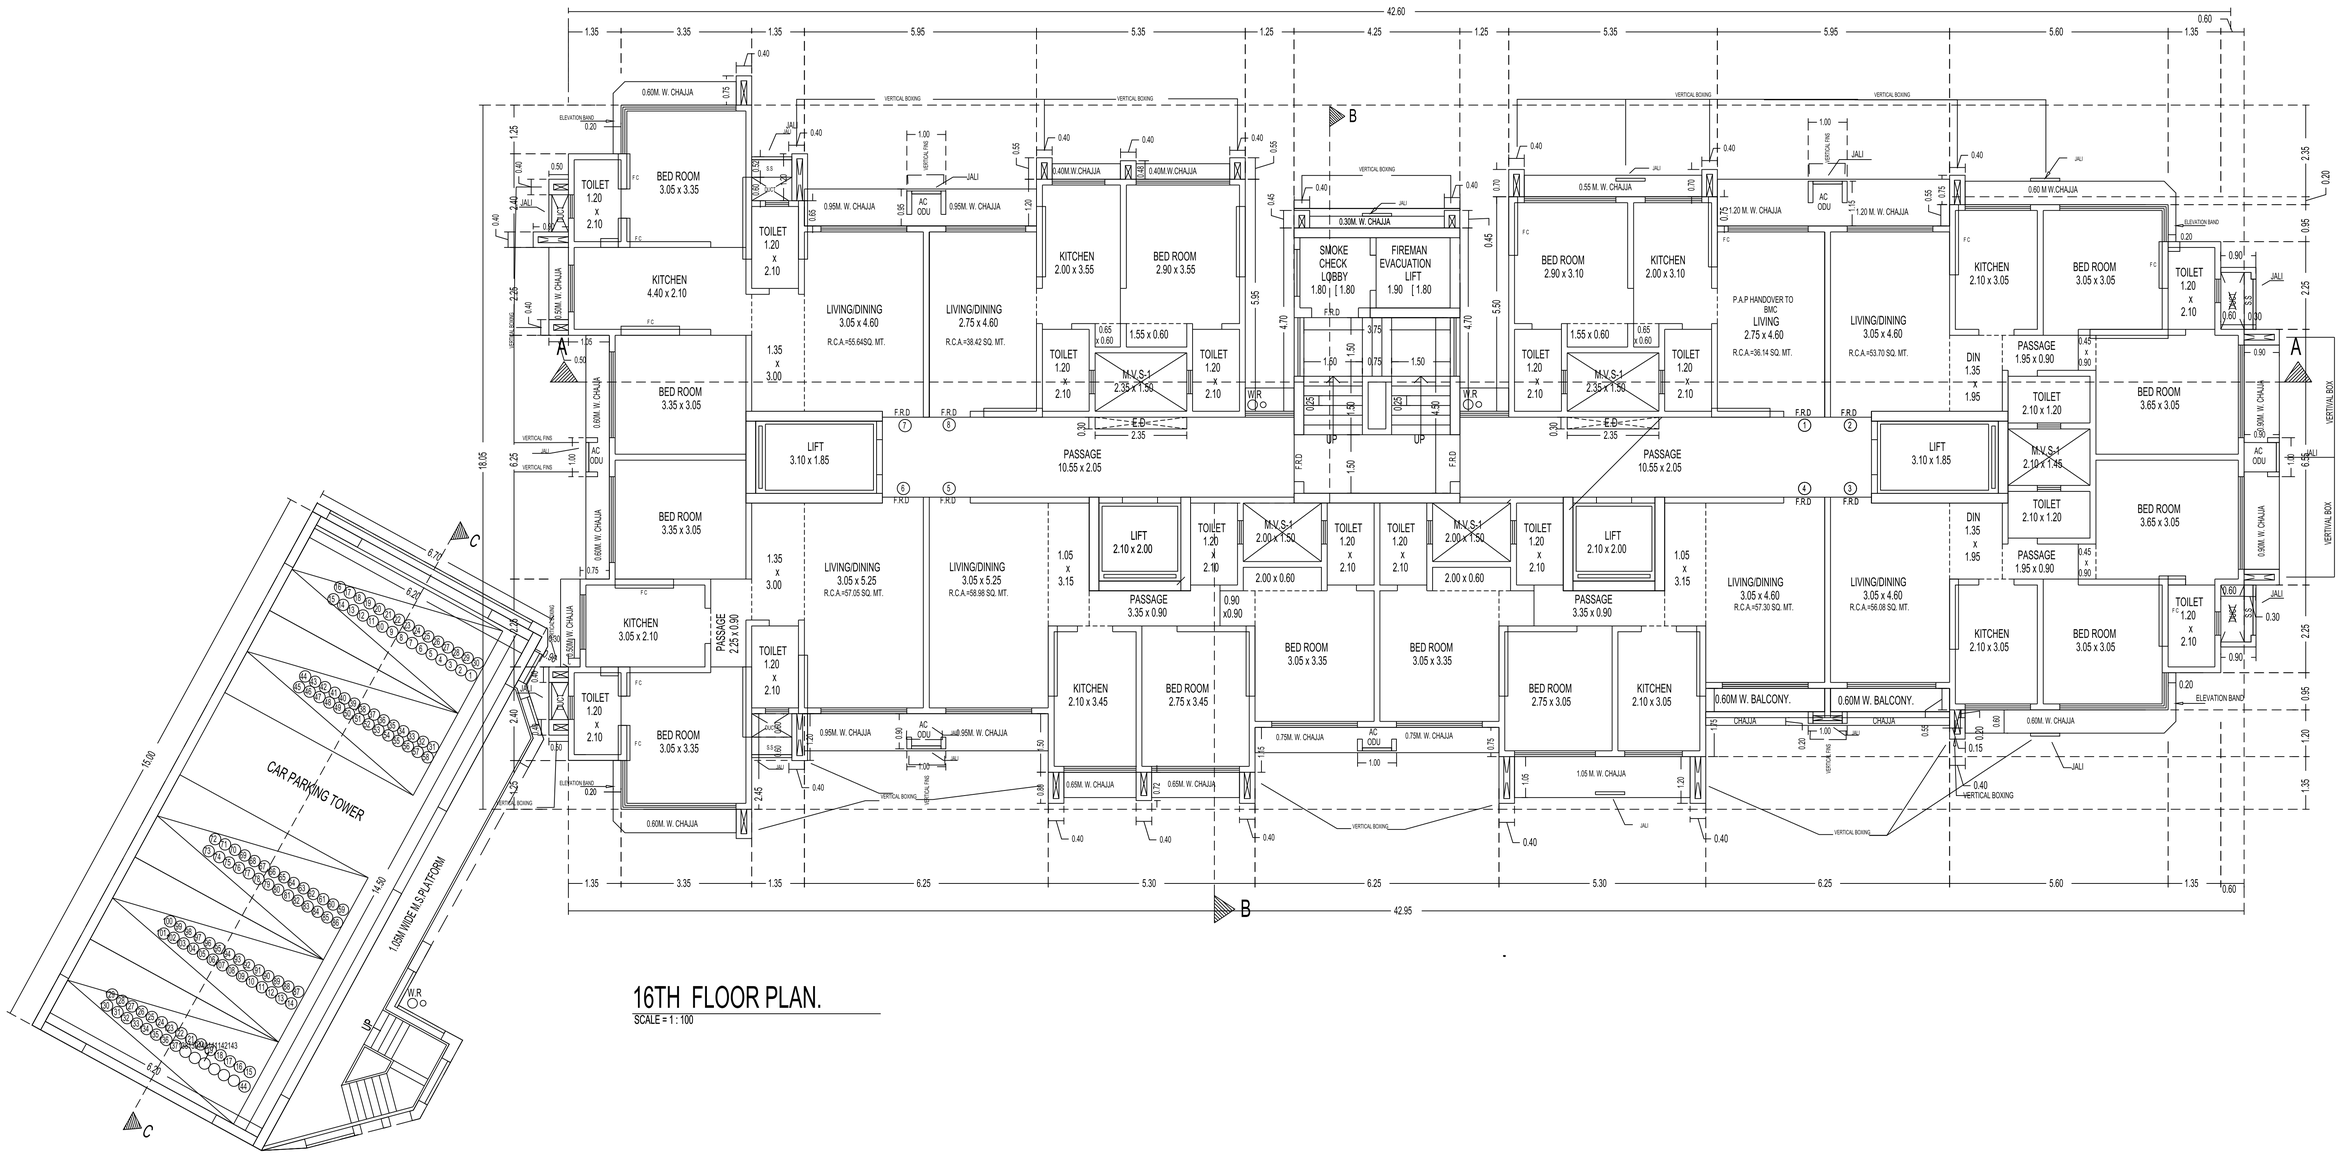C 0.08
TOTAL NET BUILT UP AREA





16TH FLOOR PLAN.
SCALE = 1 : 100

17TH FLOOR PLAN.
SCALE = 1 : 100

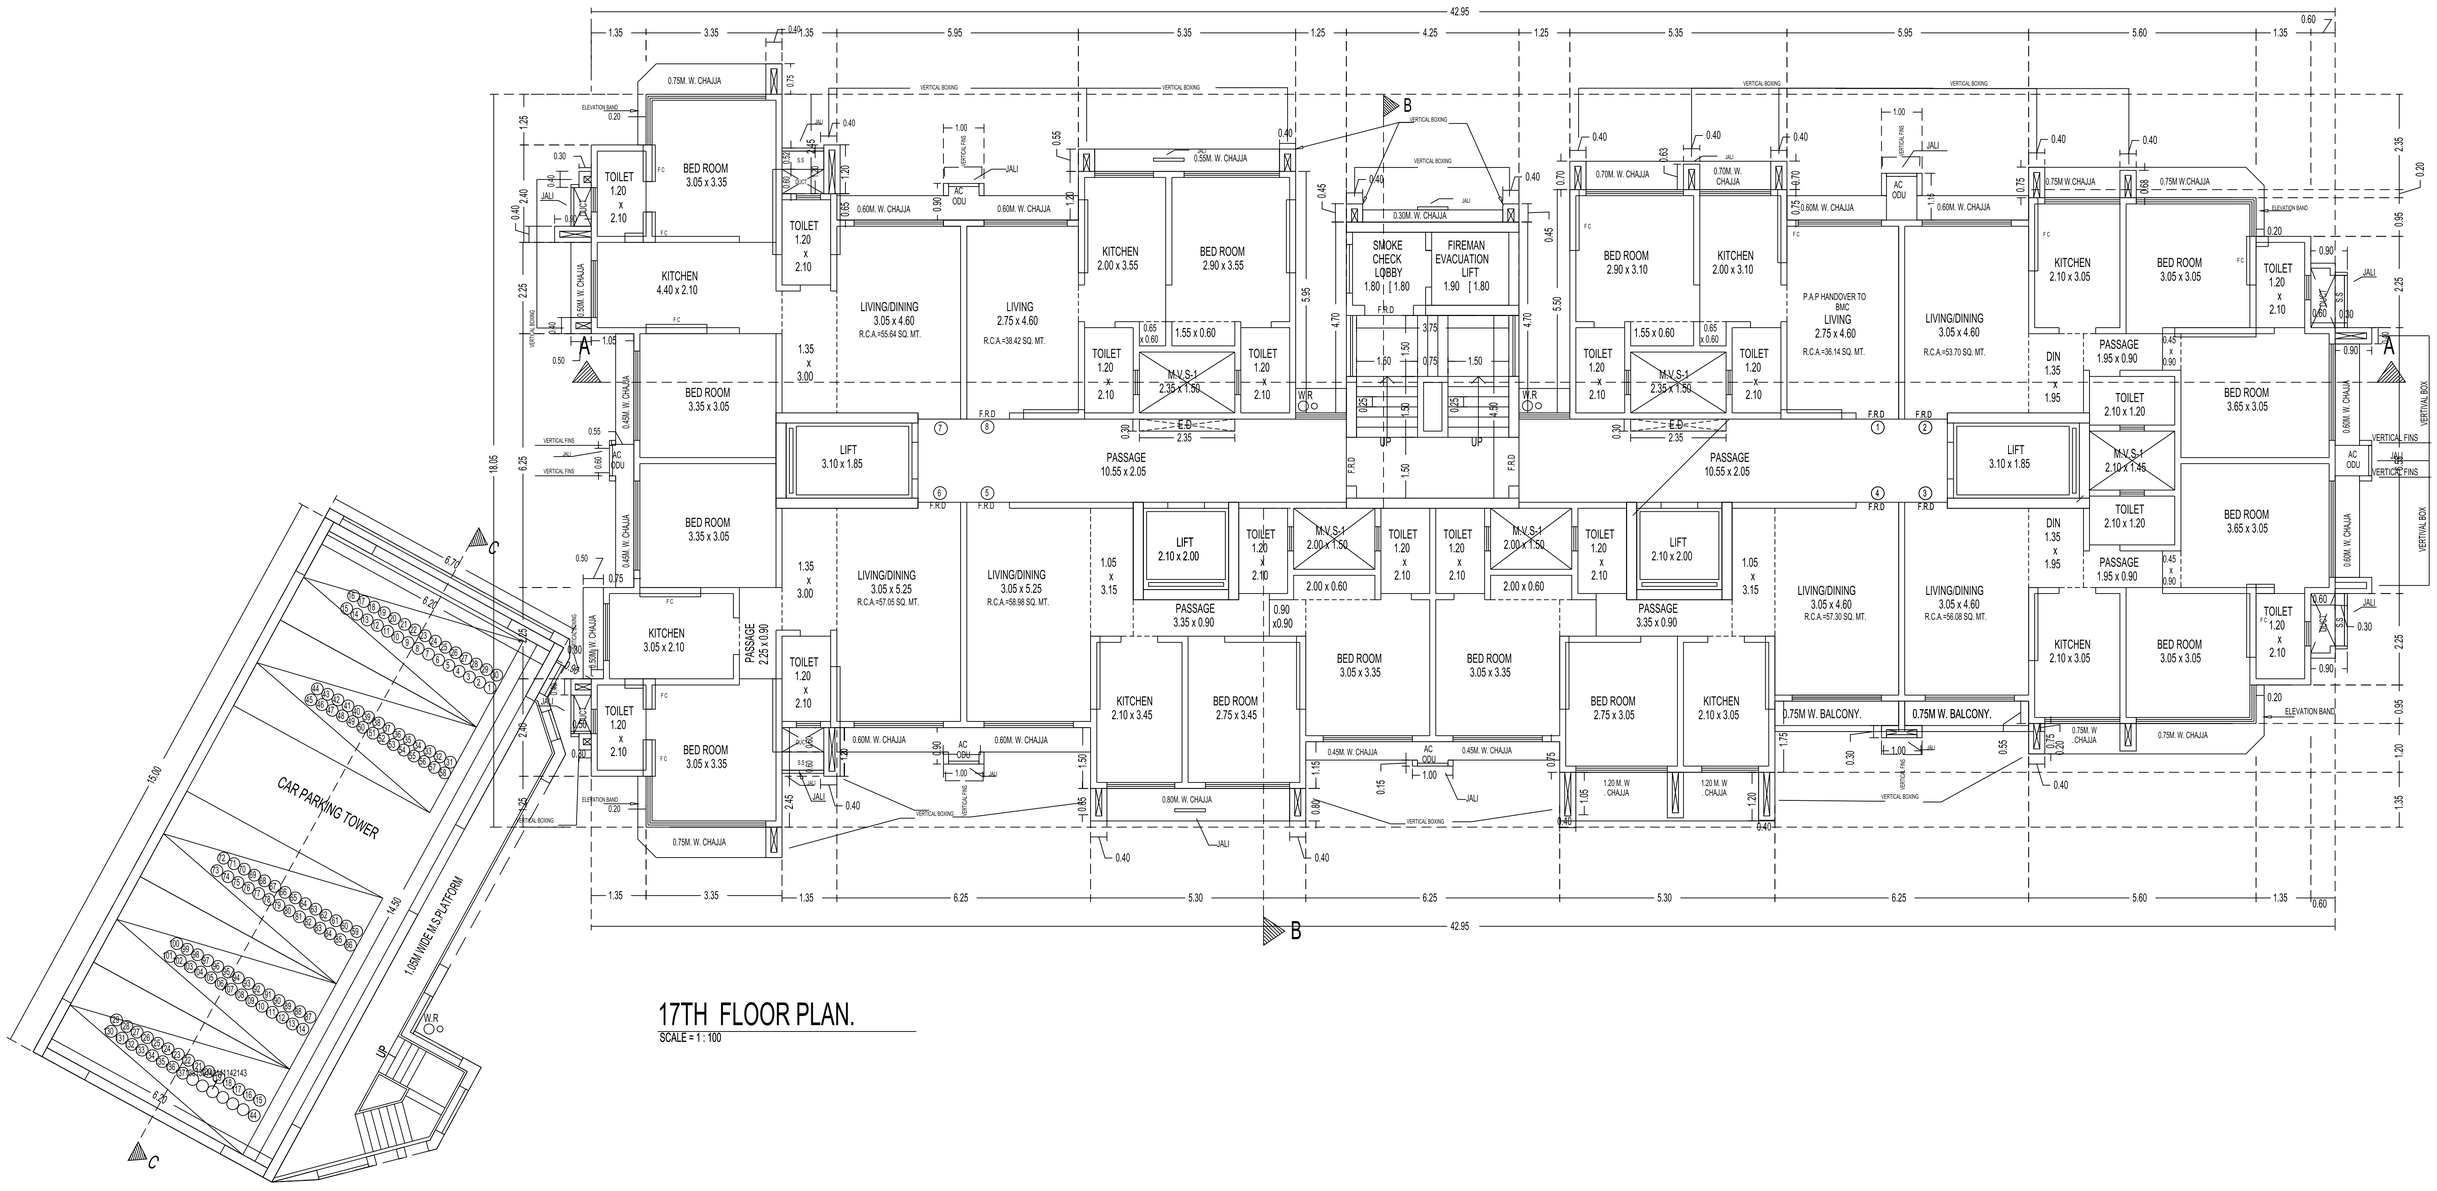



17TH FLOOR PLAN.
SCALE = 1 : 100

19TH FLOOR PLAN.
SCALE = 1 : 100

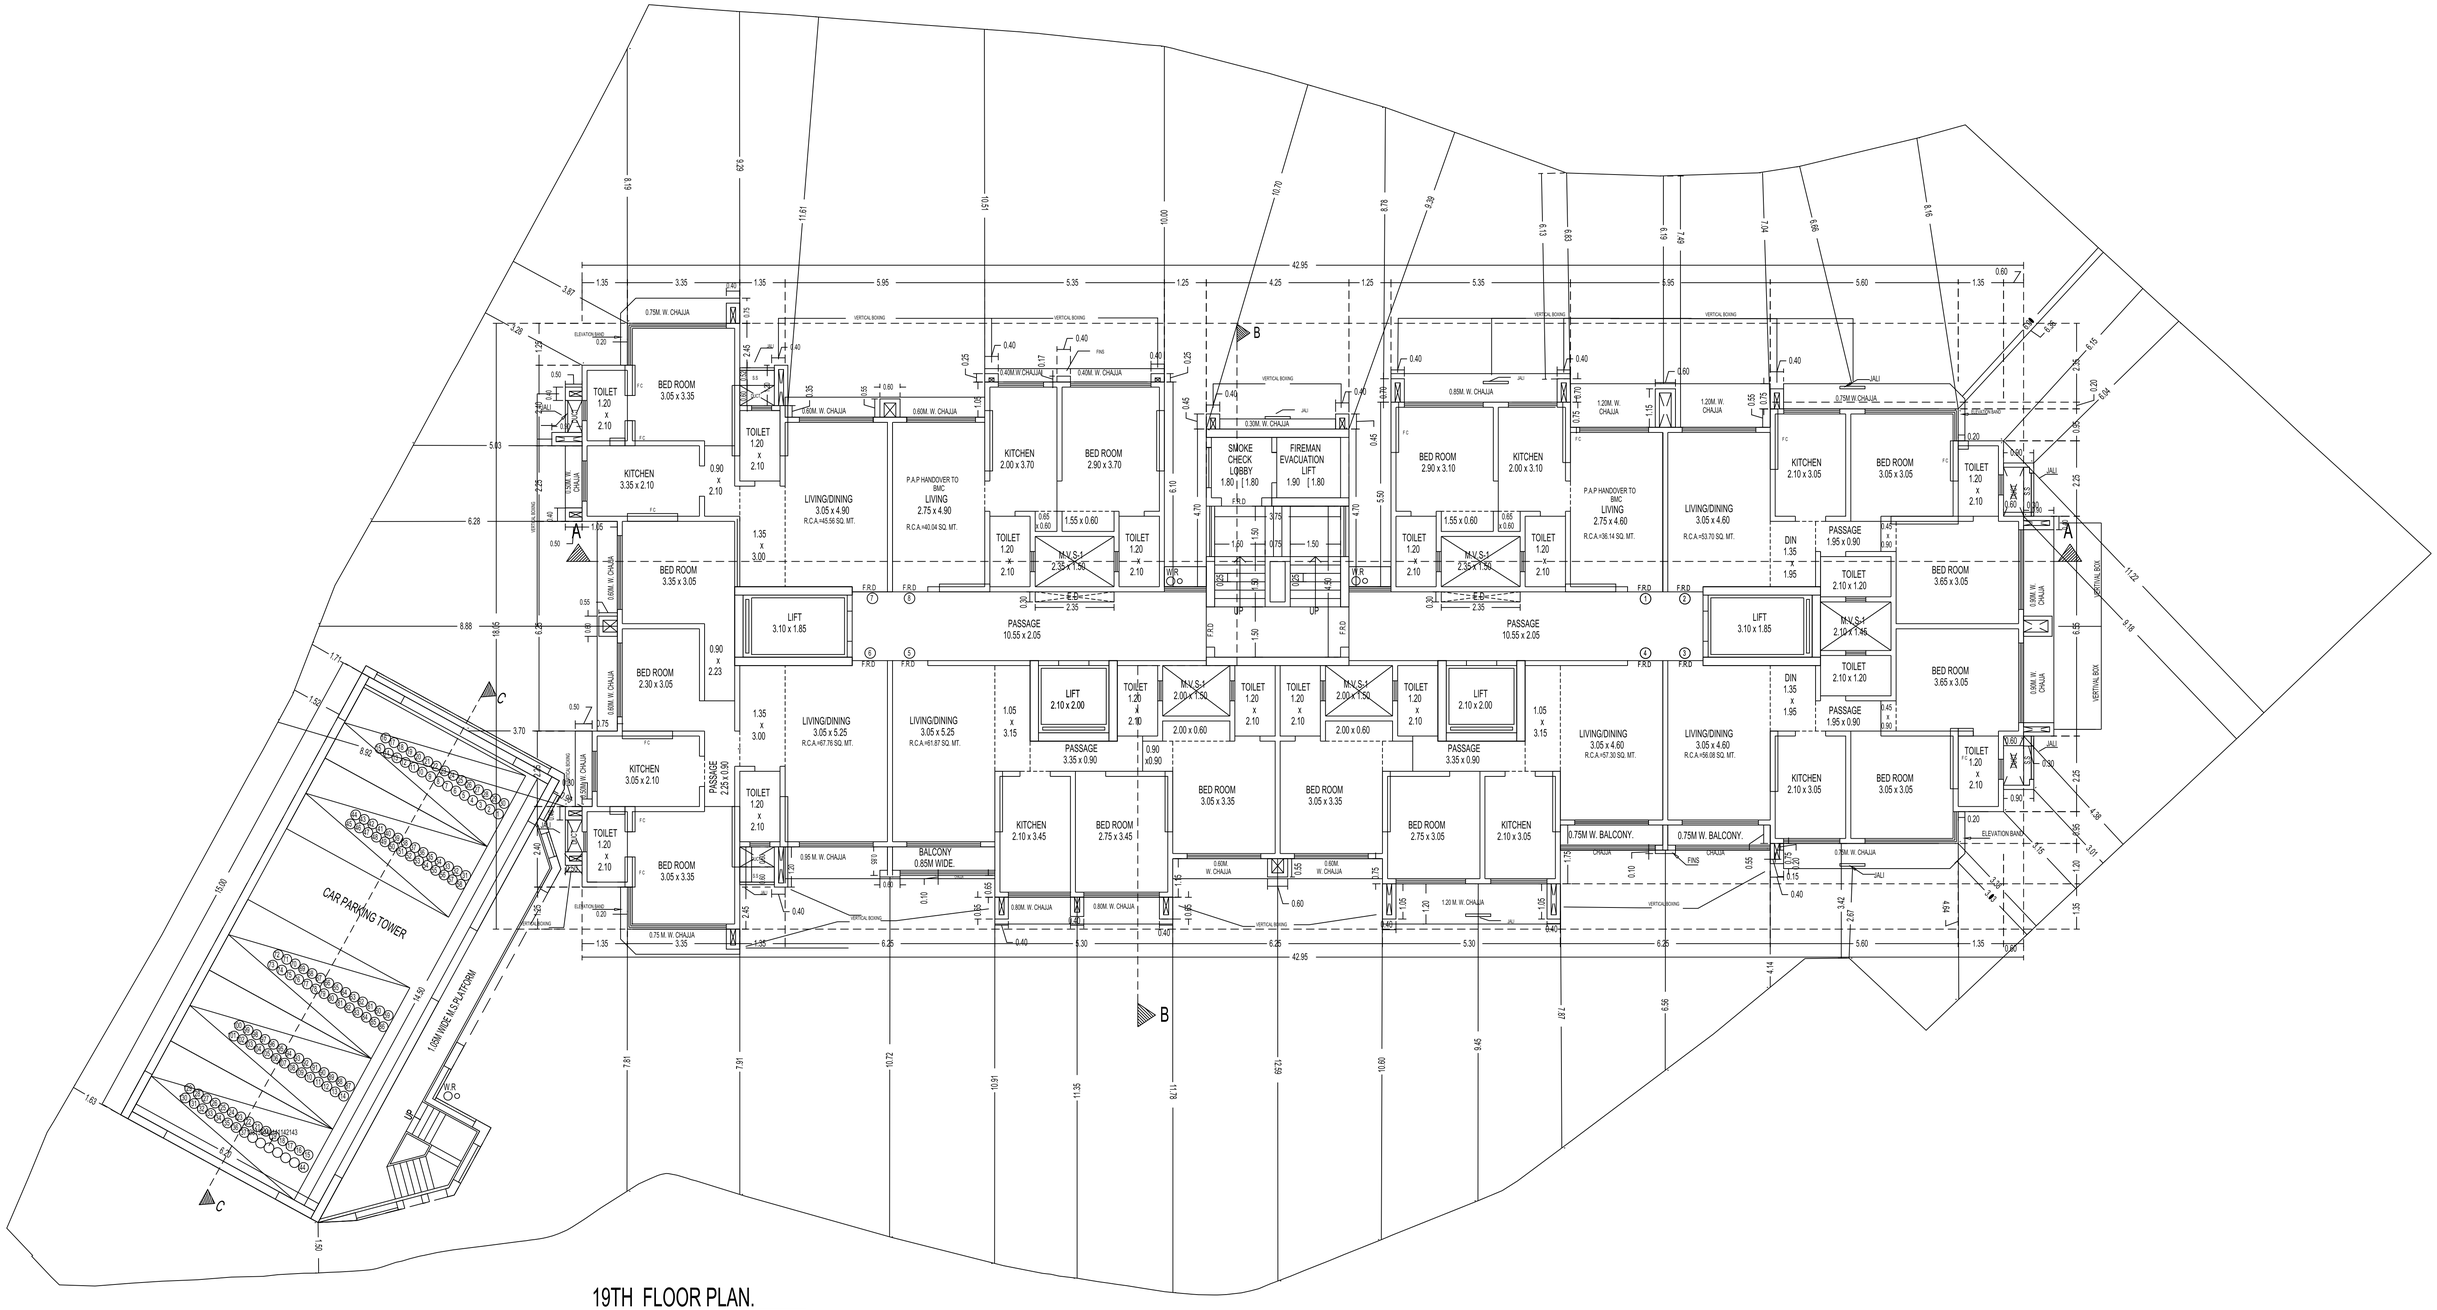


19TH FLOOR PLAN.
SCALE = 1 : 100

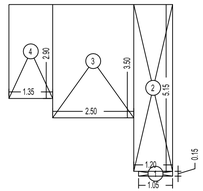



## SOCIETY OFFICE AREA DIA.&CAL.

SCALE = 1 : 100

ADDITIONS

| | | | | | | | | |
|---|---|---|---|---|---|---|---|---|
| 1 | 1.05 | X | 0.15 | X | 1 NO | = | 0.15 | SQ.MT. |
| 2 | 1.20 | X | 5.15 | X | 1 NO | = | 6.18 | SQ.MT. |
| 3 | 2.50 | X | 3.50 | X | 1 NO | = | 8.75 | SQ.MT. |
| 4 | 1.35 | X | 2.90 | X | 1 NO | = | 3.92 | SQ.MT. |
| | | | TOTAL DEDUCTION | | | = | 19.00 | SQ.MT. Y1 |

| | | | | |
|---|---|---|---|---|
| C | 0.08 | X | 1.25 | |
| D | 0.08 | X | 0.95 | X |
| NET BUILT UP AREA | | | | |

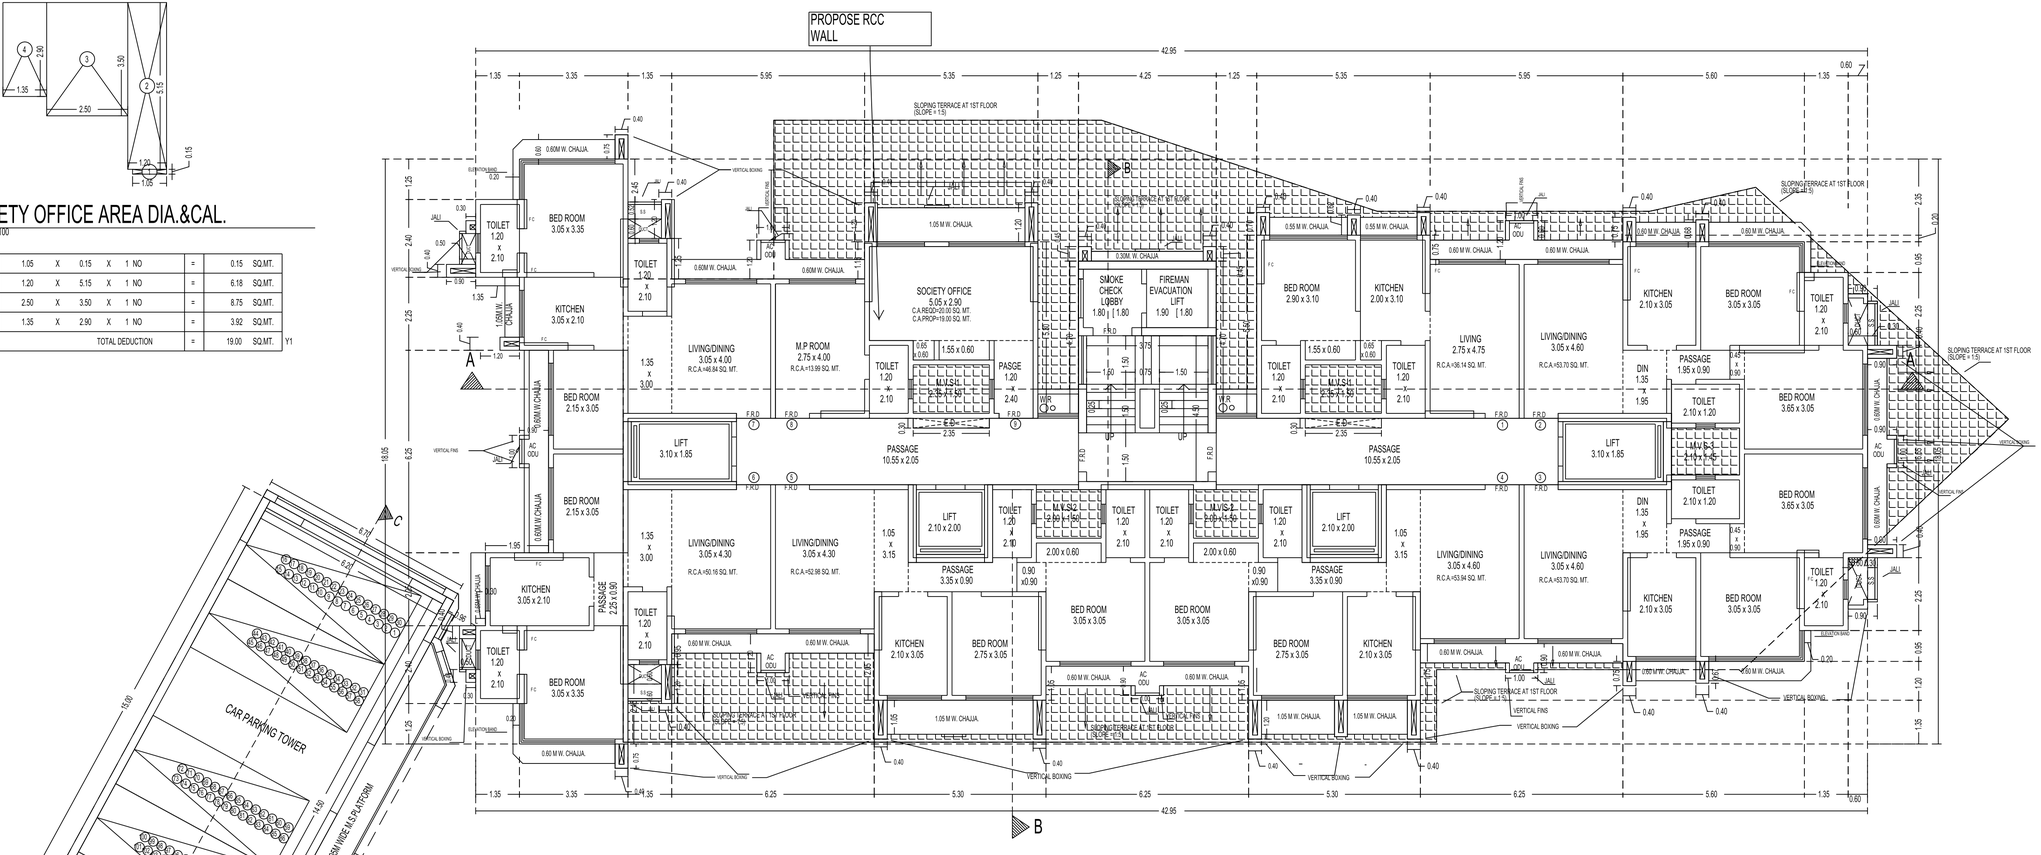


## 1ST FLOOR PLAN.

SCALE = 1 : 100