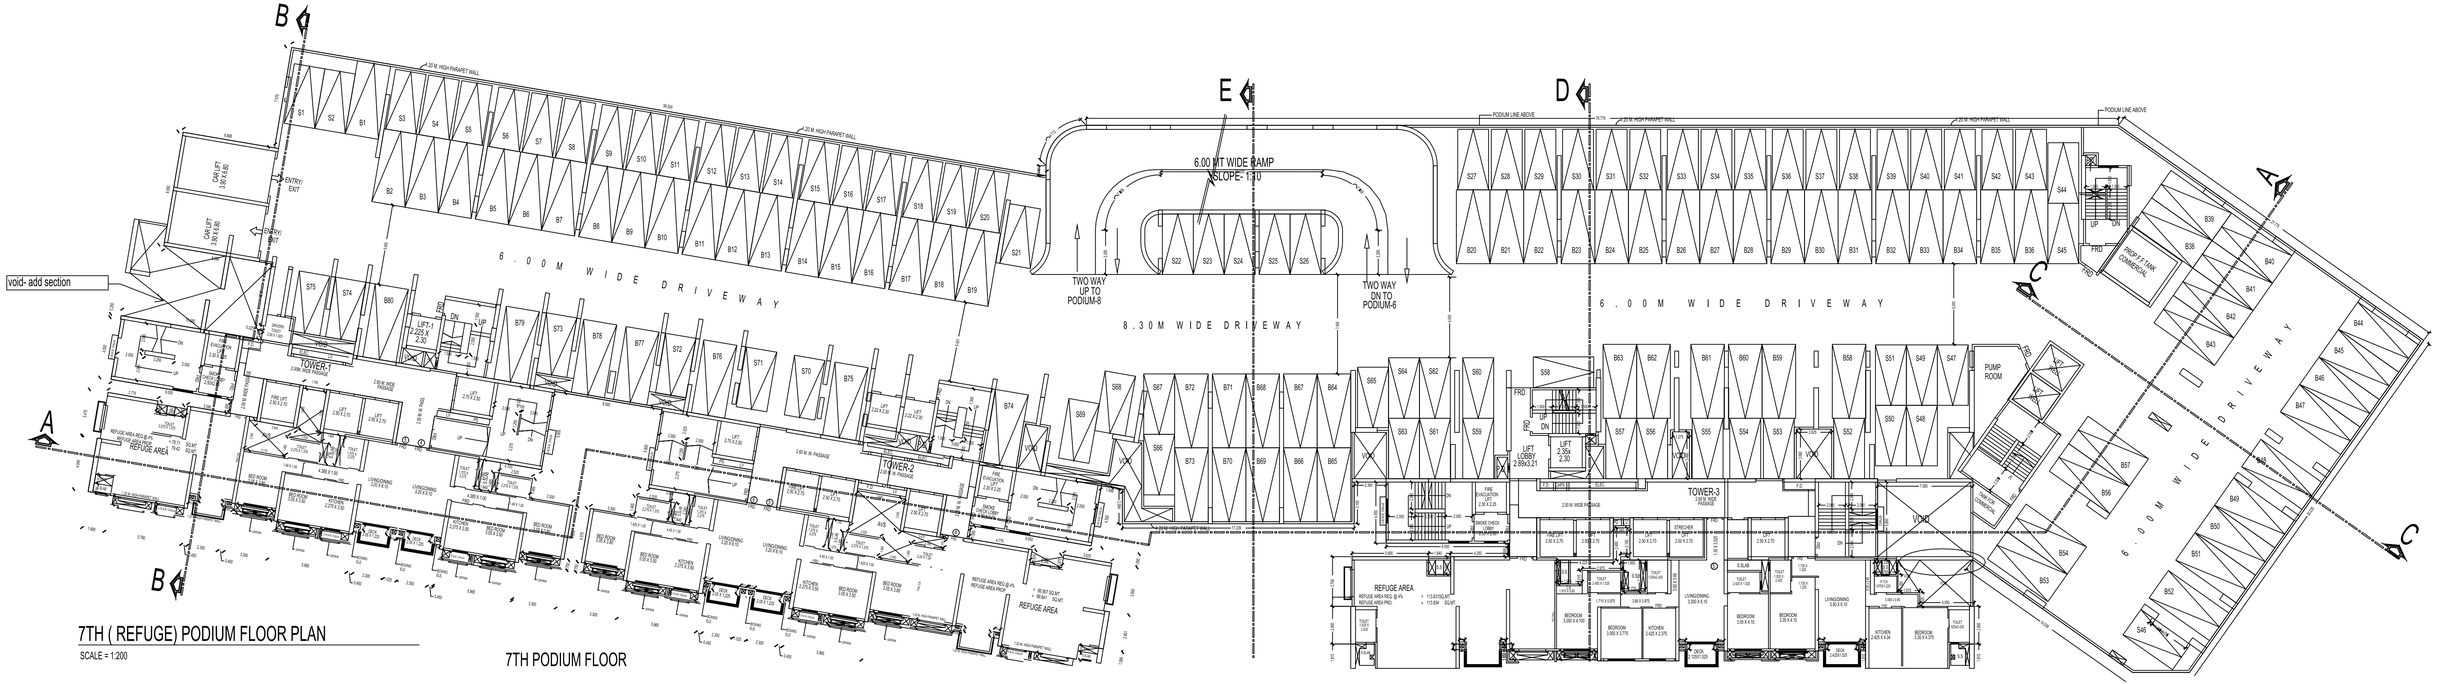

7TH (REFUGE) PODIUM FLOOR PLAN

SCALE = 1:200

7TH PODIUM FLOOR

BIG PARKING	SMALL PARKING	TOTAL PARKING
64 nos	70 nos	134 nos

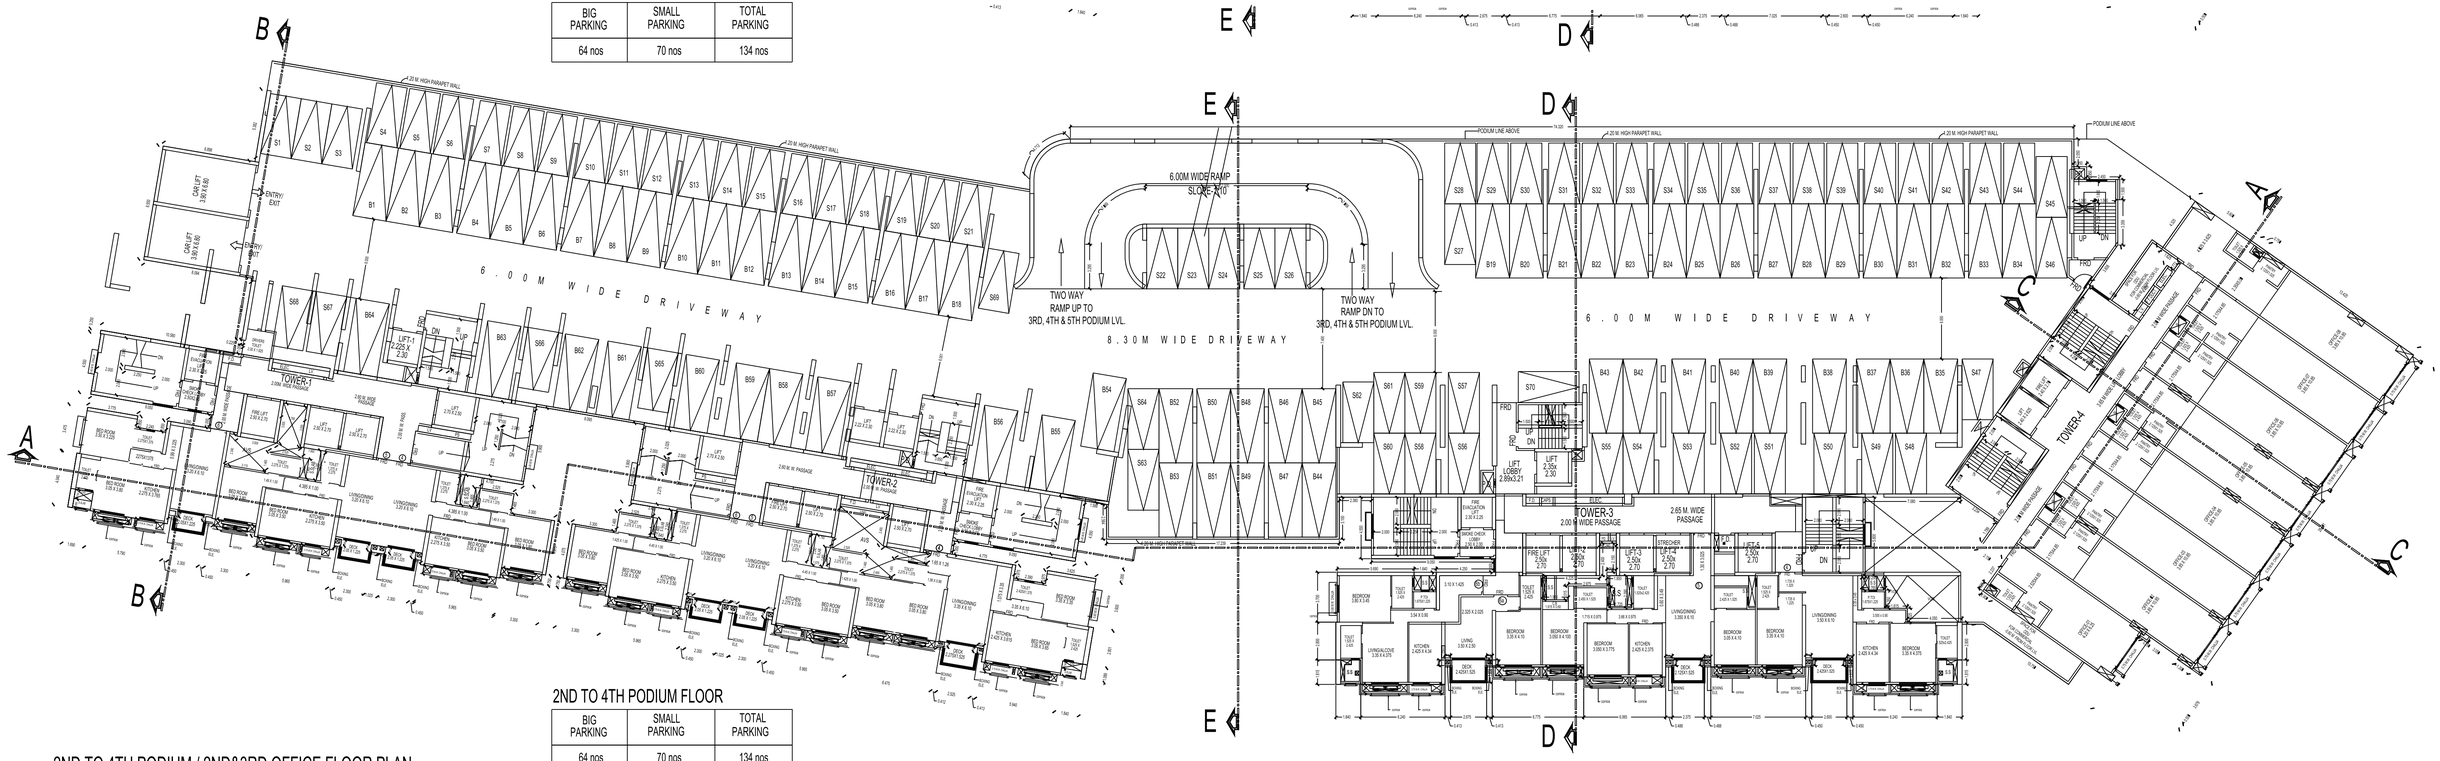
A
B
C
D
E
20 M. HIGH PARAPET WALL
PODIUM LINE ABOVE
ENTRY/ EXIT
CAR LIFT 3.00 X 6.60
6.00M WIDE RAMP SLOPE 1:10
TWO WAY RAMP UP TO 3RD, 4TH & 5TH PODIUM LVL.
TWO WAY RAMP DN TO 3RD, 4TH & 5TH PODIUM LVL.
6.00 M WIDE DRIVEWAY
8.30M WIDE DRIVEWAY
TOWER-1
TOWER-2
TOWER-3
TOWER-4
2.00 M WIDE PASSAGE
2.65 M. WIDE PASSAGE
LIFT LOBBY 2.80X2.21
FIRE LIFT 2.50 X 2.70
STRETCHER LIFT 2.50 X 2.70
LIFT-5 2.50 X 2.70
LIFT LOBBY 2.80X2.21
LIFT 2.25X 2.30
FRD
UP
DN
SD
LIFT 2.25 X 2.30
LIFT 2.70 X 2.30
LIFT 2.00 X 2.25
LIFT 2.00 X 2.75
LIFT 2.00 X 2.30
LIFT 2.00 X 2.20
LIFT 2.00 X 2.70
LIFT 2.00 X 2.50
LIFT 2.00

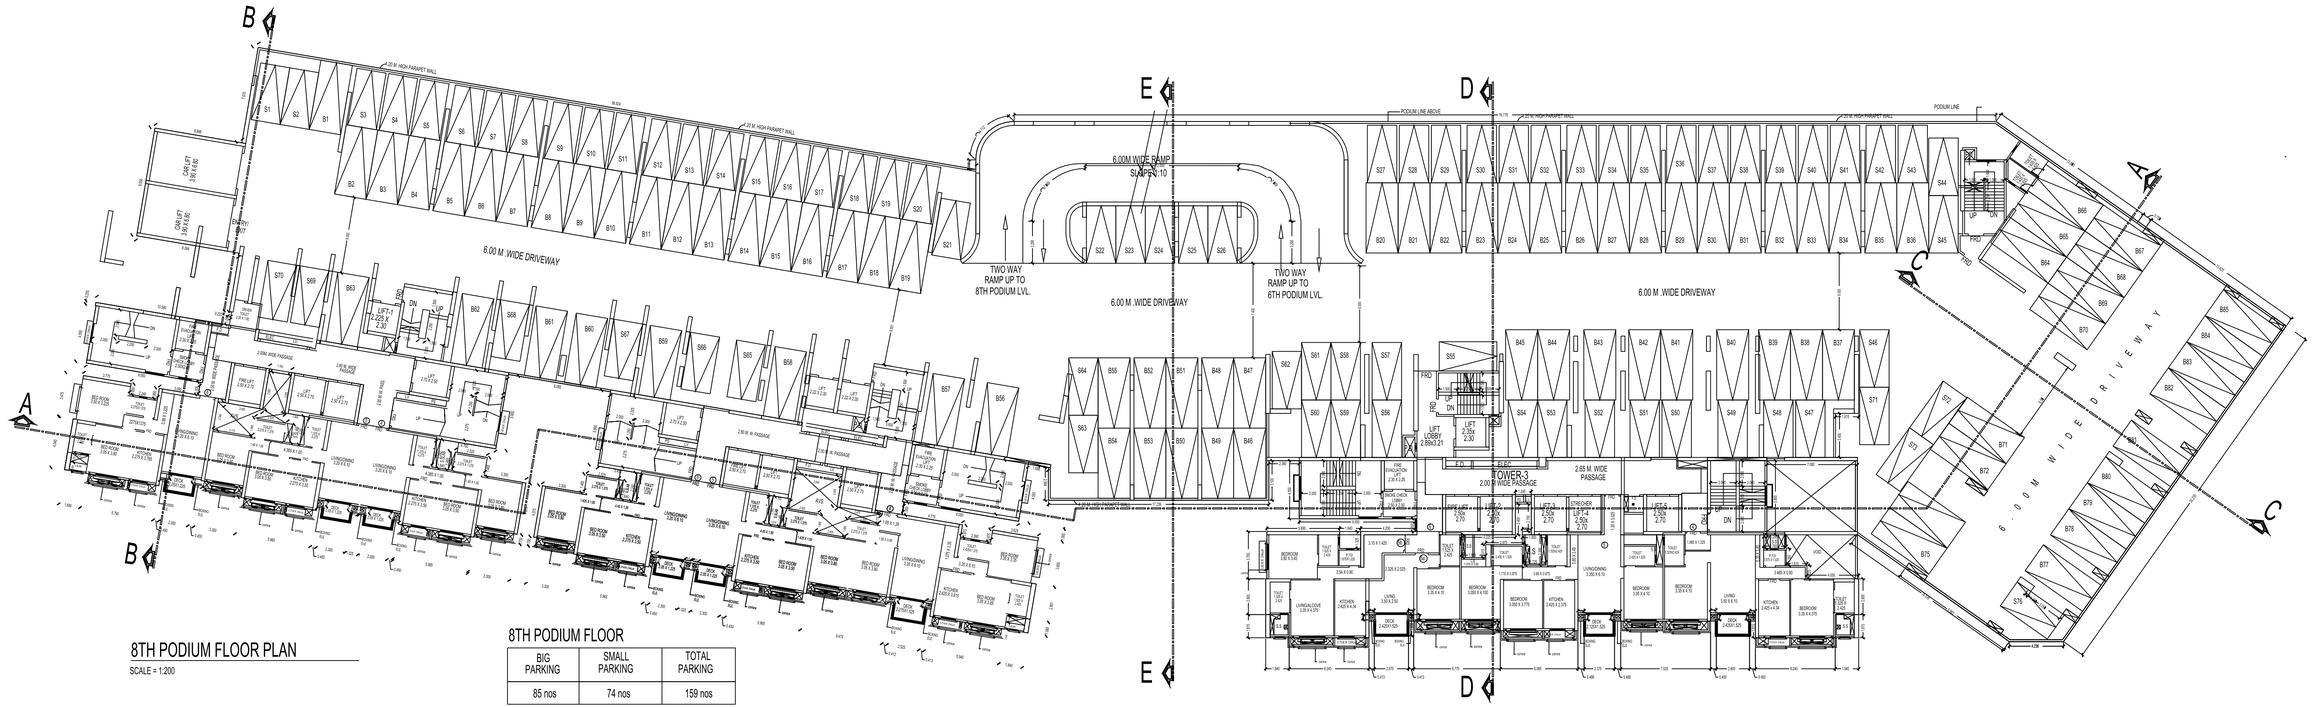

8TH PODIUM FLOOR PLAN

SCALE = 1:200

8TH PODIUM FLOOR

BIG PARKING	SMALL PARKING	TOTAL PARKING
85 nos	74 nos	159 nos

4 3 8b 2ND FLOOR TO 4TH - 8TH TO

TOTAL LIG AREA PROPOSED

NET PLOT AREA = 11822.01 SQ.MT.
REQUIRED 25% LIG AREA = 2955.50 SQ.MT.
PROPOSED LIG AREA = 2933.41 SQ.MT.

BIG PARKING	SMALL PARKING	TOTAL PARKING
76 nos	73 nos	149 nos

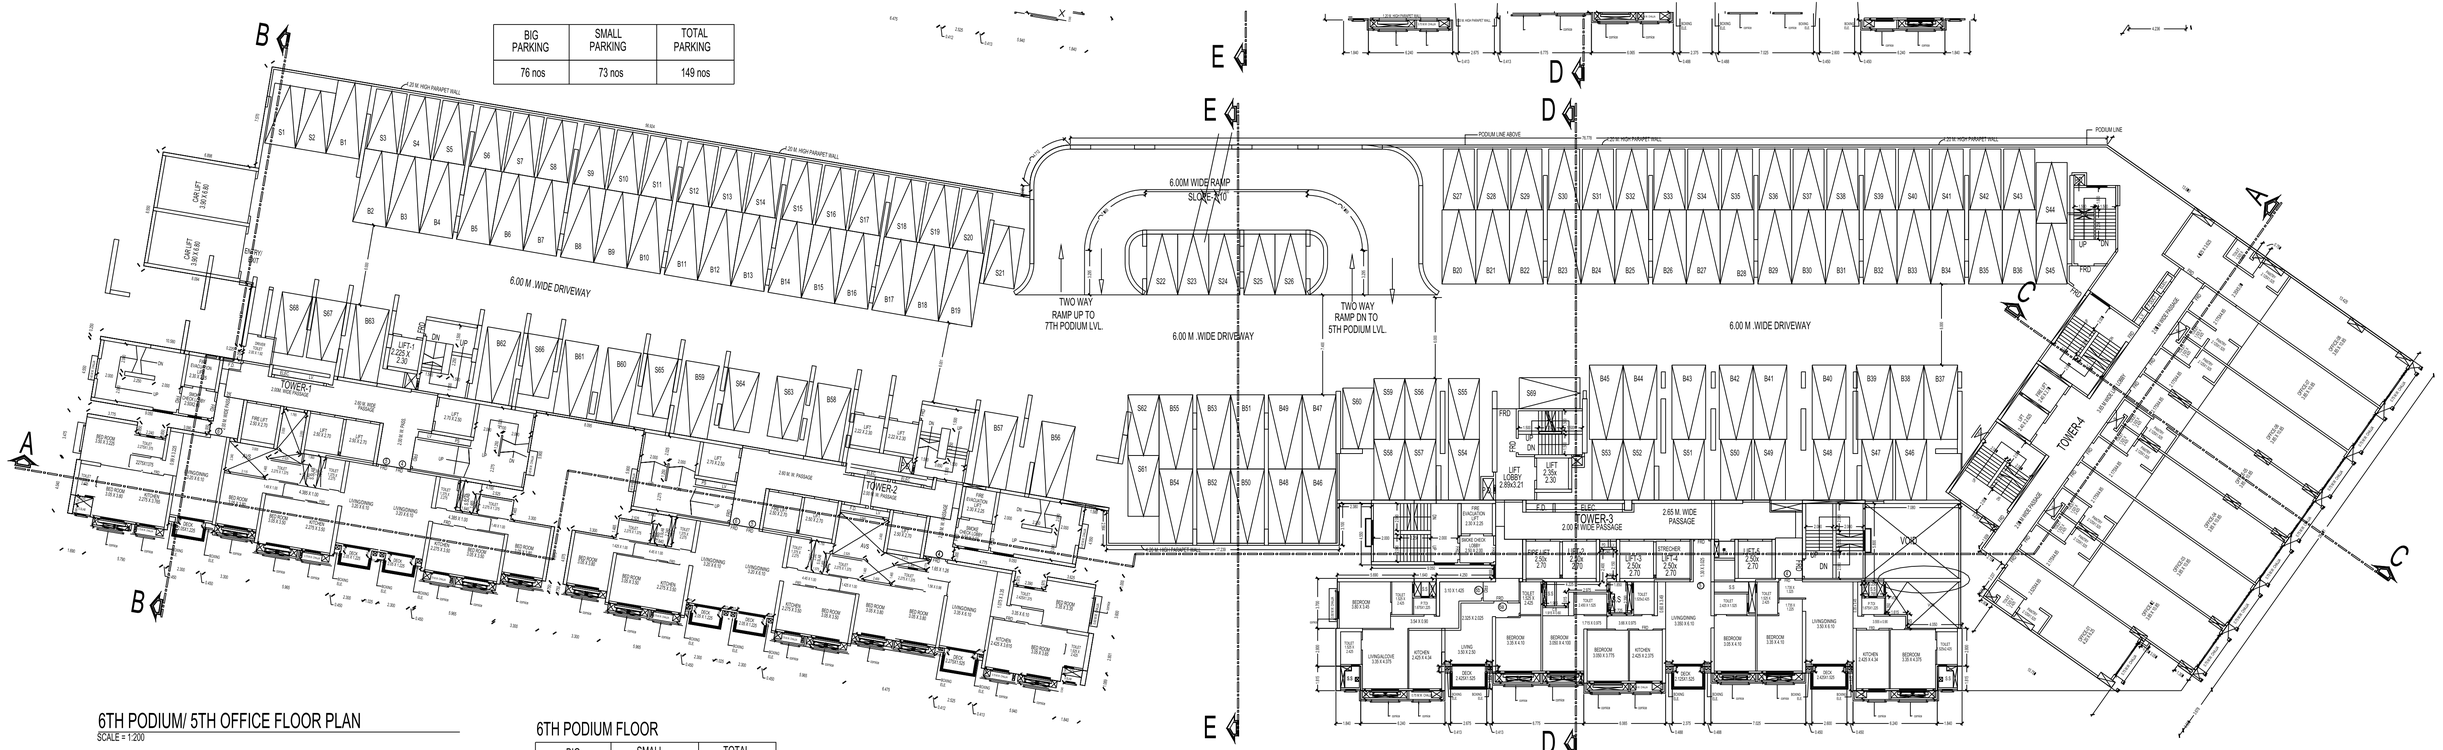

6TH PODIUM/ 5TH OFFICE FLOOR PLAN

SCALE = 1:200

6TH PODIUM FLOOR

BIG PARKING	SMALL PARKING	TOTAL PARKING
63 nos	69 nos	132 nos

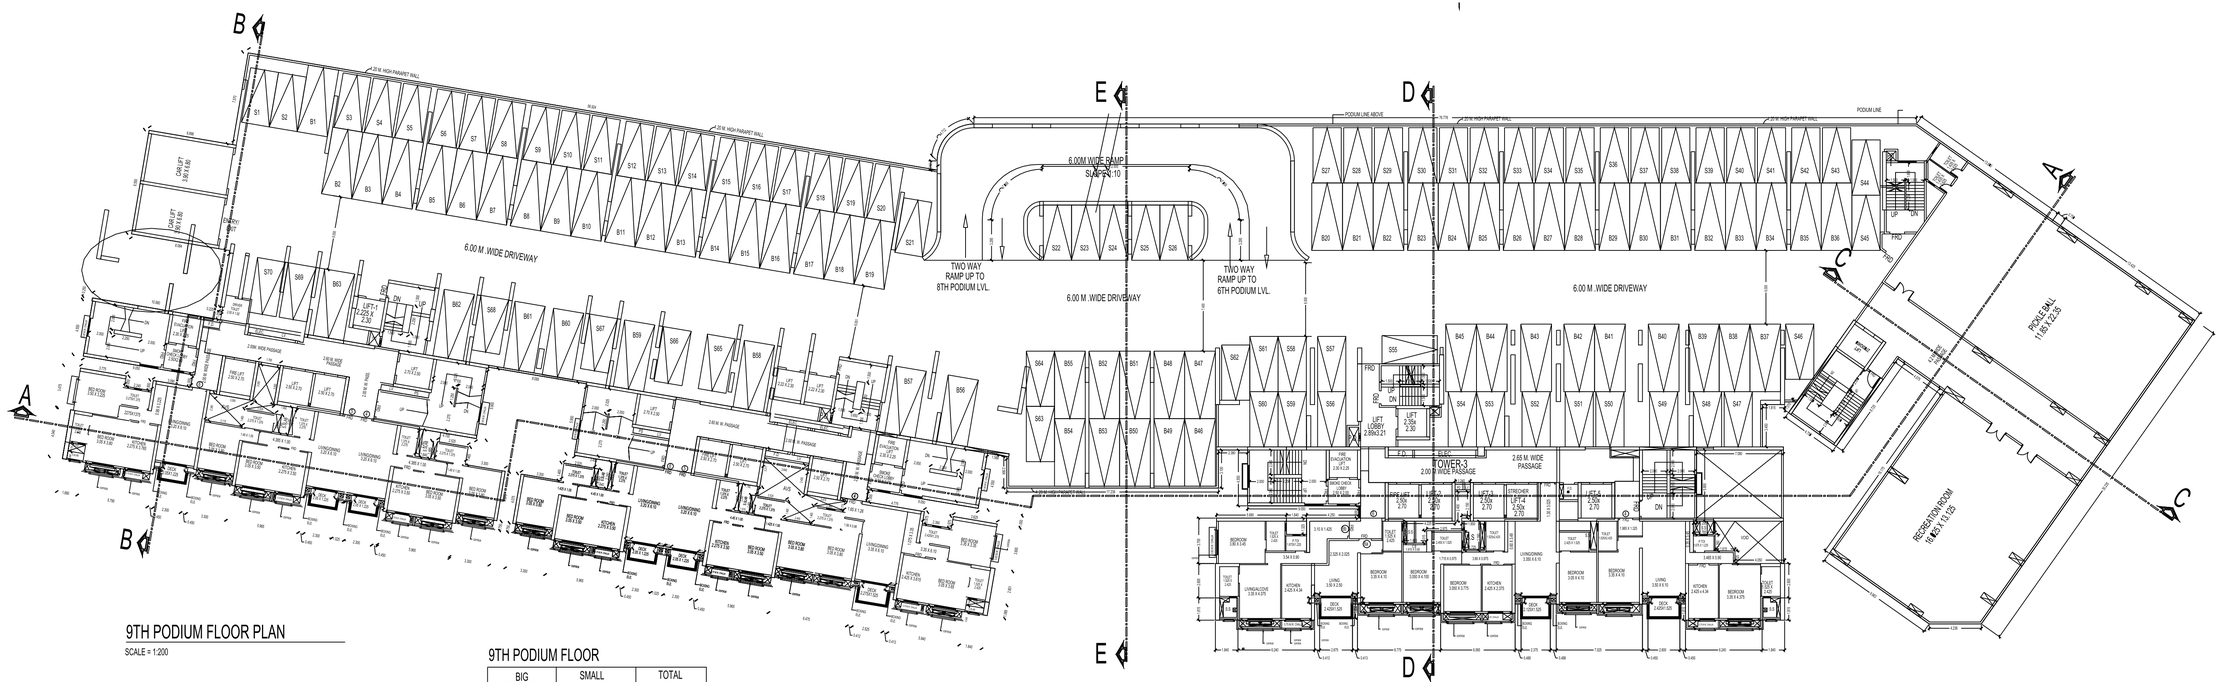

9TH PODIUM FLOOR PLAN

SCALE = 1:200

9TH PODIUM FLOOR

BIG PARKING	SMALL PARKING	TOTAL PARKING
63 nos	70 nos	133 nos

BUILT UP AREA CALCULATIONS OF LIG UNITS

END	TOWER	FLAT NO	FLOOR	
1	3	1A	GDN, 1STH, 10TH TO 16TH	56.23
2	3	4A	GDN, 1STH, 10TH TO 16TH	
3	3	5A	GDN FLR TO 6TH, 8TH TO 9TH & 16TH TO 20TH FLOOR	

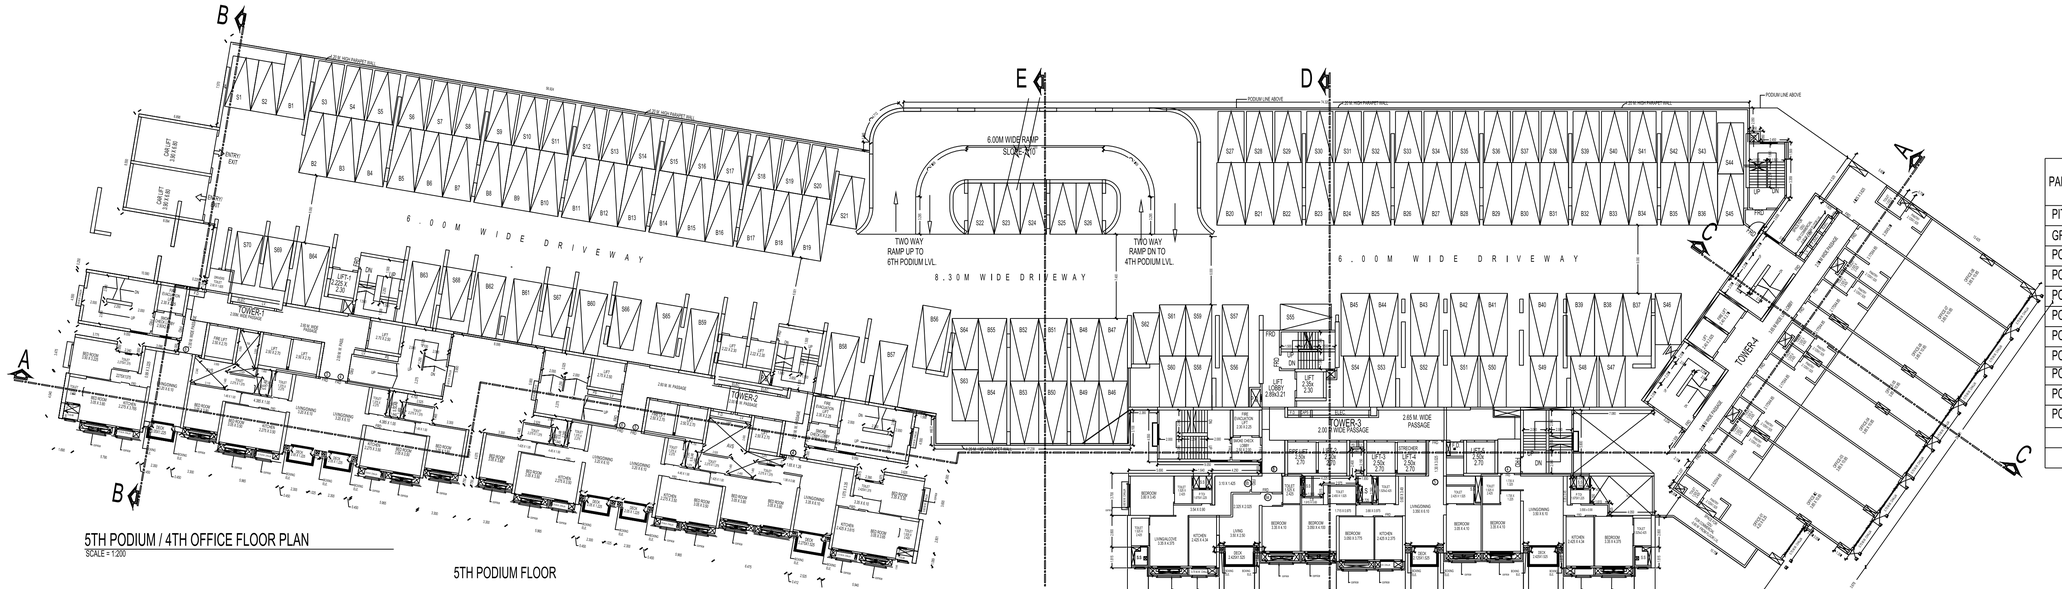
A
B
C
D
E
6.00M WIDE RAMP SLOPE 1:10
TWO WAY RAMP UP TO 6TH PODIUM LVL.
TWO WAY RAMP DN TO 4TH PODIUM LVL.
8.30M WIDE DRIVEWAY
6.00M WIDE DRIVEWAY
6.00M WIDE DRIVEWAY
TOWER-1
TOWER-2
TOWER-3
TOWER-4
2.00 M WIDE PASSAGE
2.65 M. WIDE PASSAGE
PODIUM LINE ABOVE
LIFT LOBBY 2.80X3.21
LIFT 2.00X 2.30
LIFT-1 2.00X 2.30
LIFT-2 2.00X 2.30
LIFT-3 2.00X 2.30
LIFT-4 2.00X 2.30
LIFT-5 2.00X 2.30
LIFT-6 2.00X 2.30
LIFT-7 2.00X 2.30
LIFT-8 2.00X 2.30
LIFT-9 2.00X 2.30
LIFT-10 2.00X 2.30
LIFT-11 2.00X 2.30
LIFT-12 2.00X 2.30
LIFT-13 2.00X 2.30

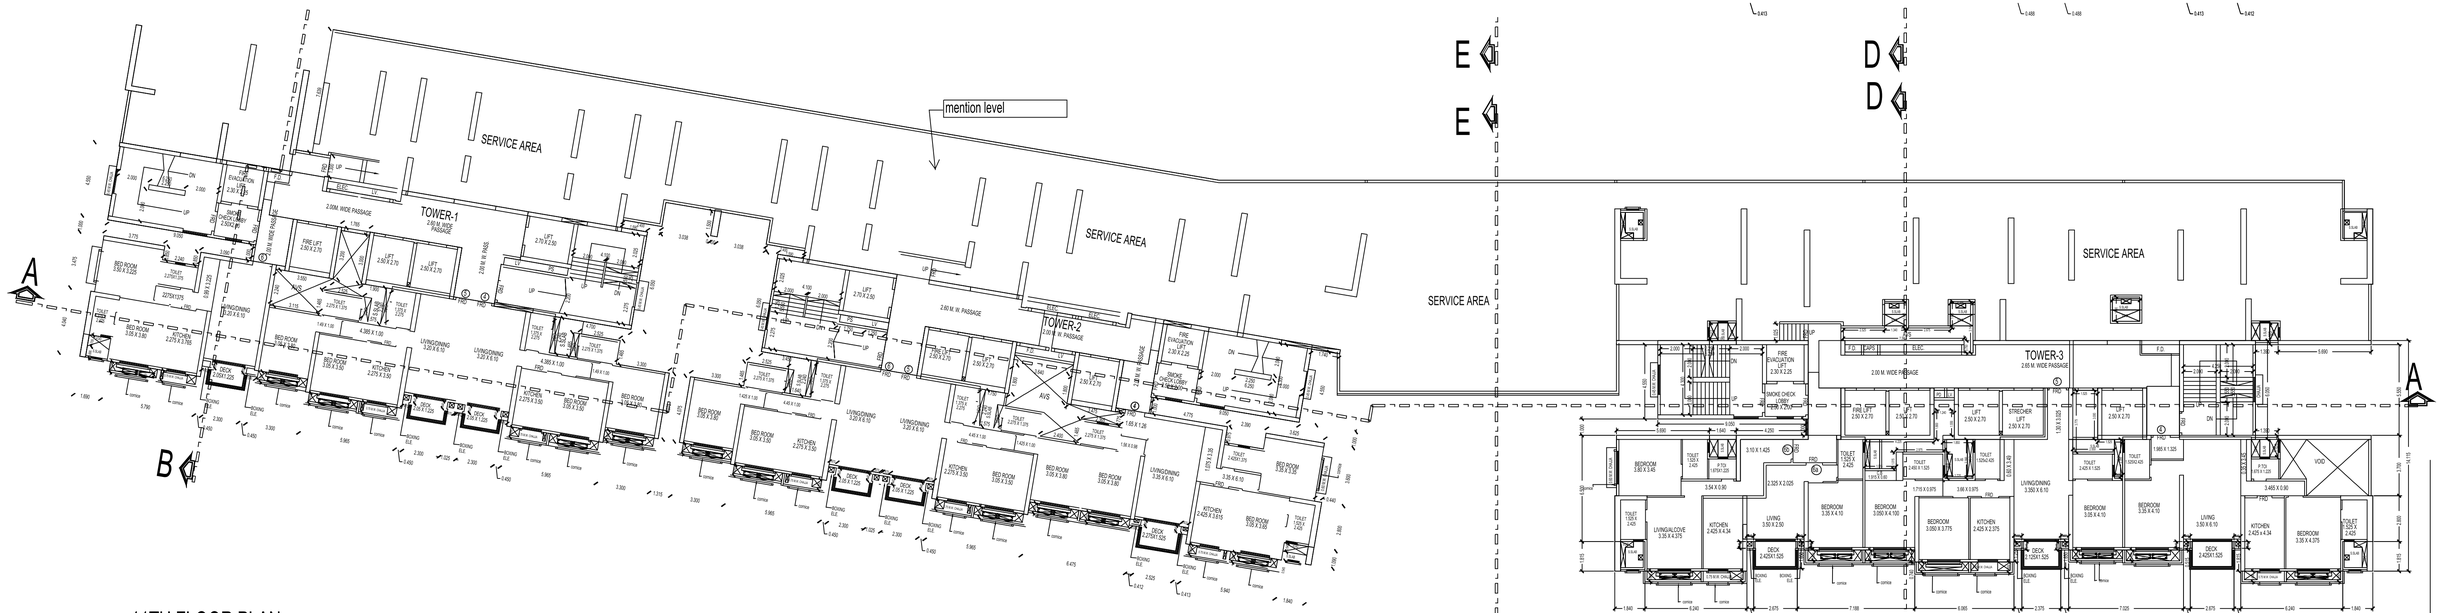

11TH FLOOR PLAN

SCALE = 1:100

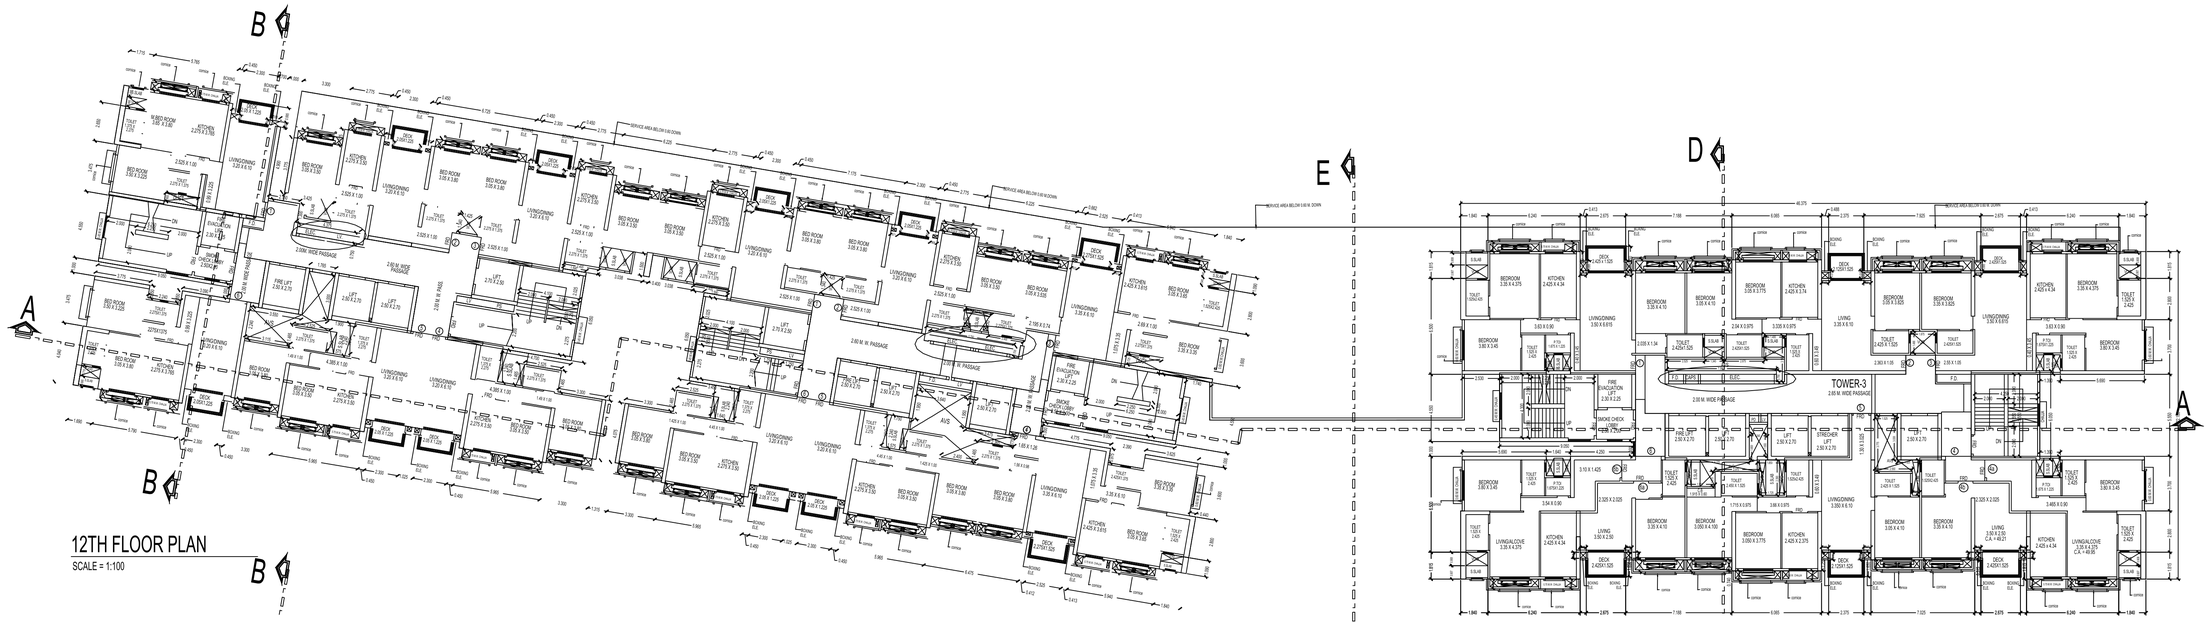

12TH FLOOR PLAN

SCALE = 1:100

22ND TO 27TH,29TH TO 34TH,36TH TO 40TH,43RD TO 49TH FLOOR PLAN

SCALE = 1:100

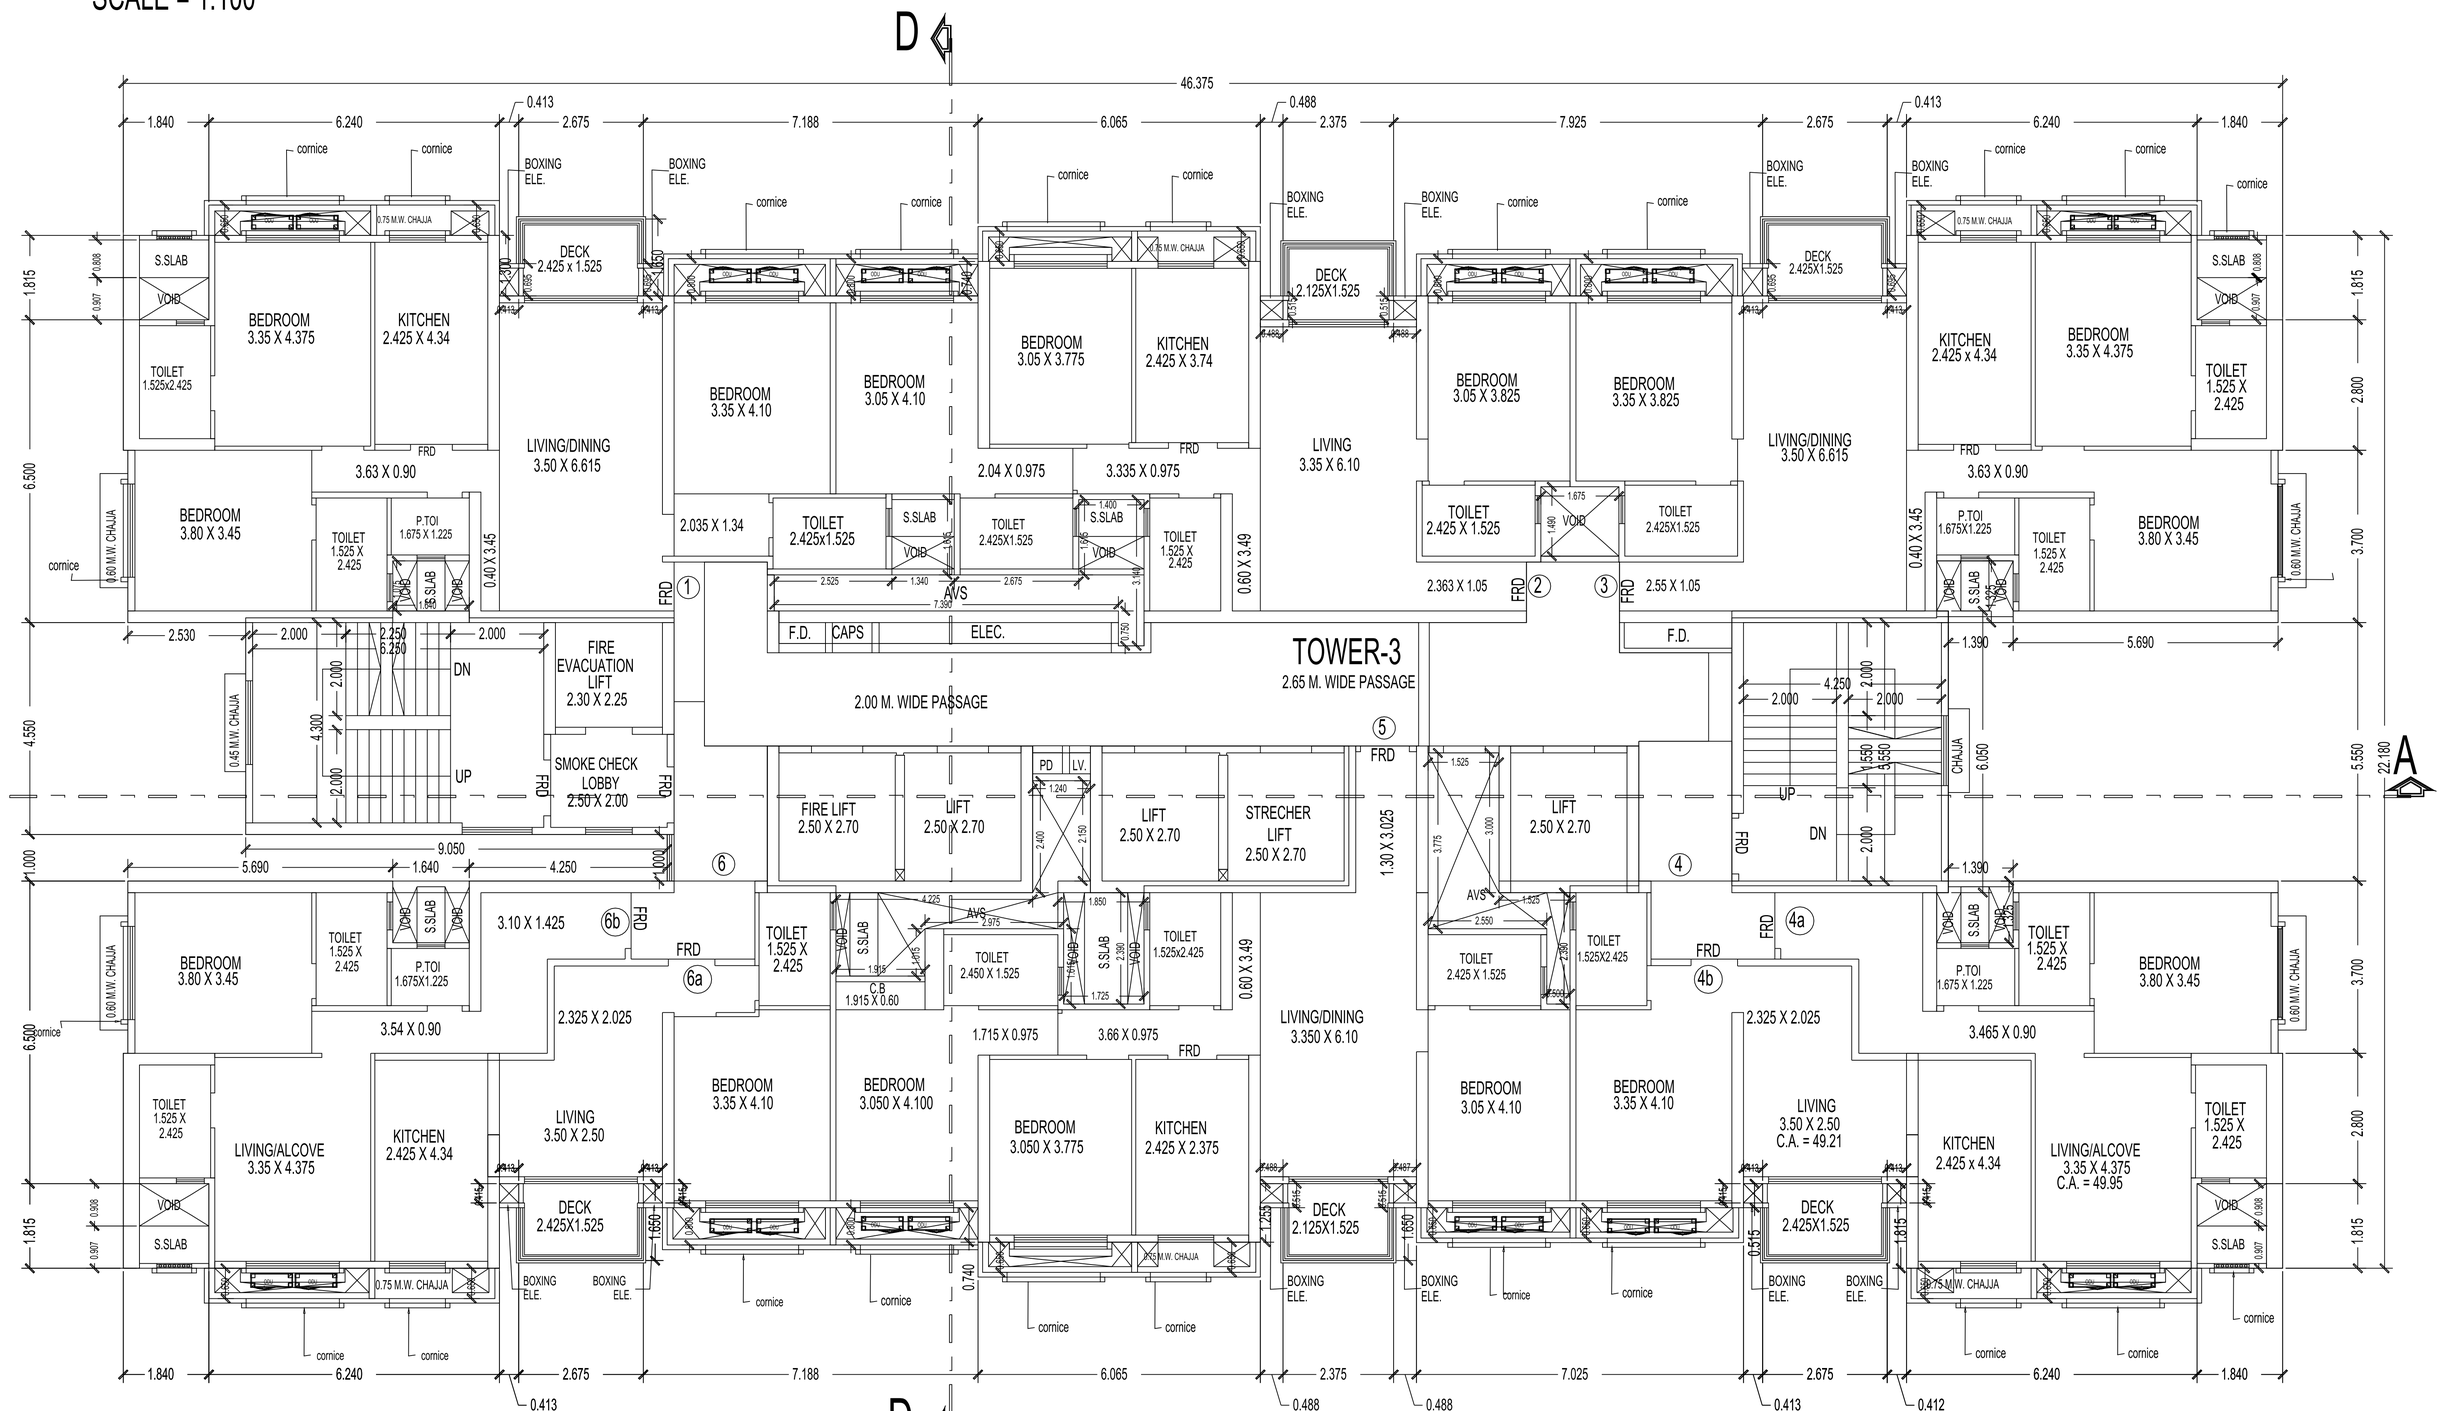

13TH,15TH TO 19TH FLOOR PLAN

SCALE = 1:100

SCALE = 1:100

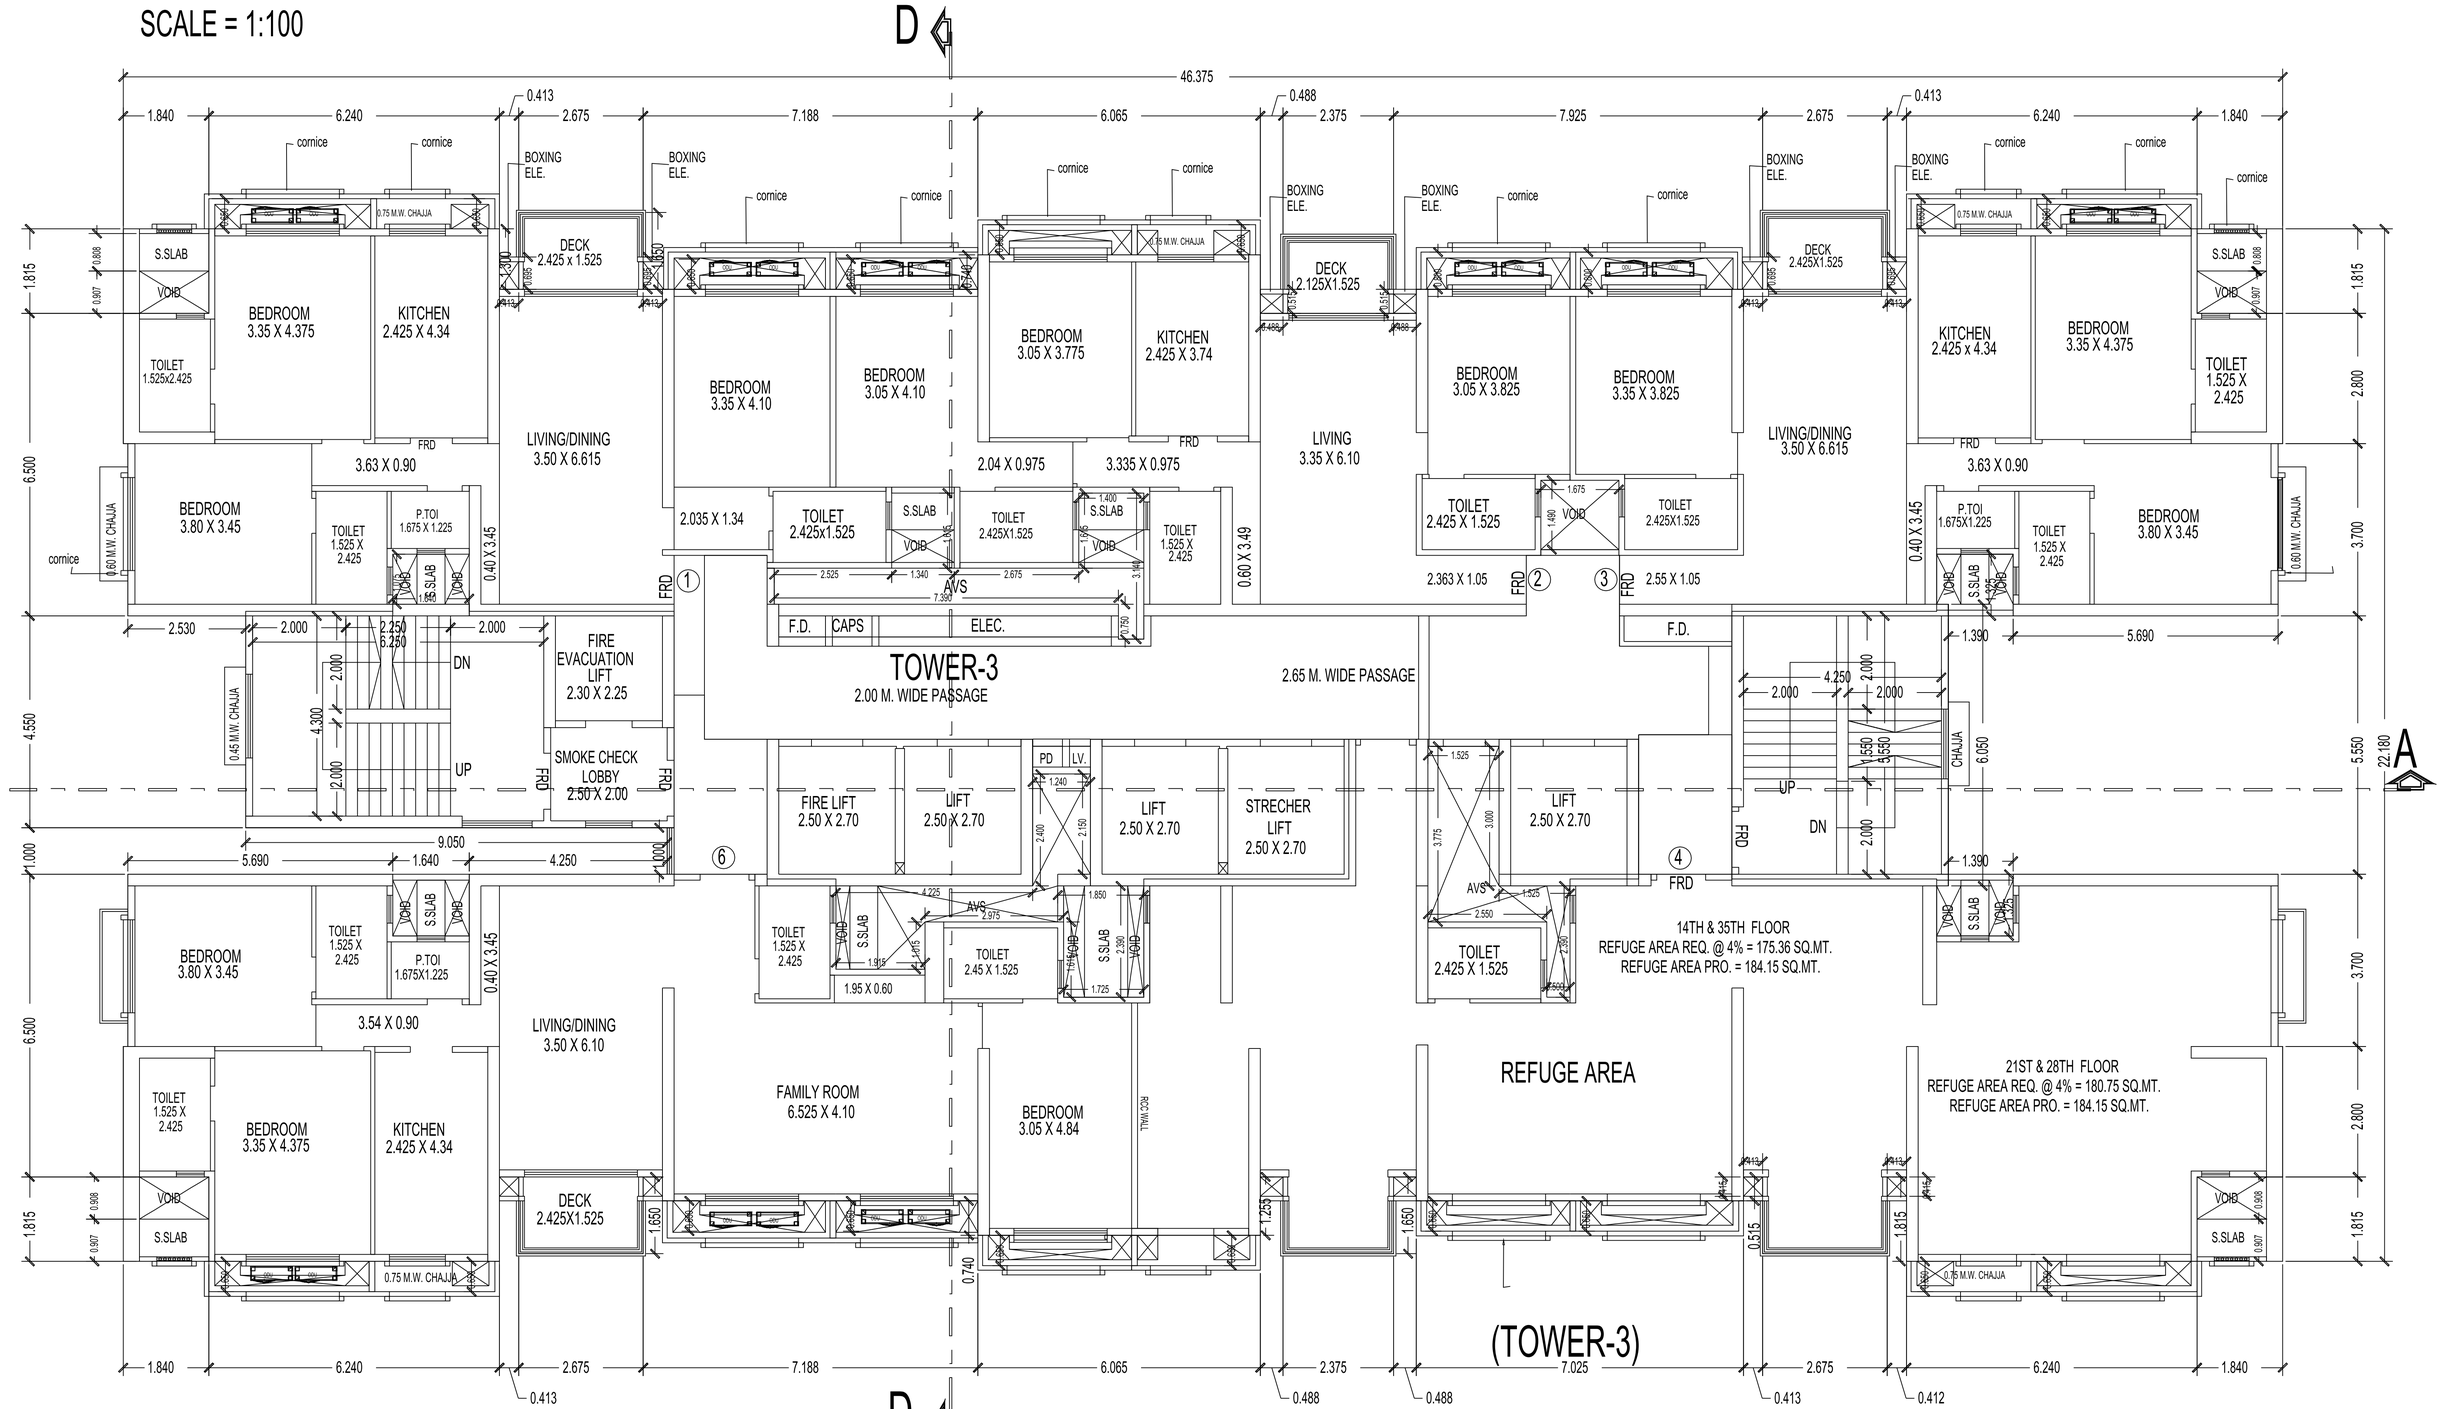

14TH, 21ST, 28TH & 35TH FLOOR REFUGE PLAN

SCALE = 1:100

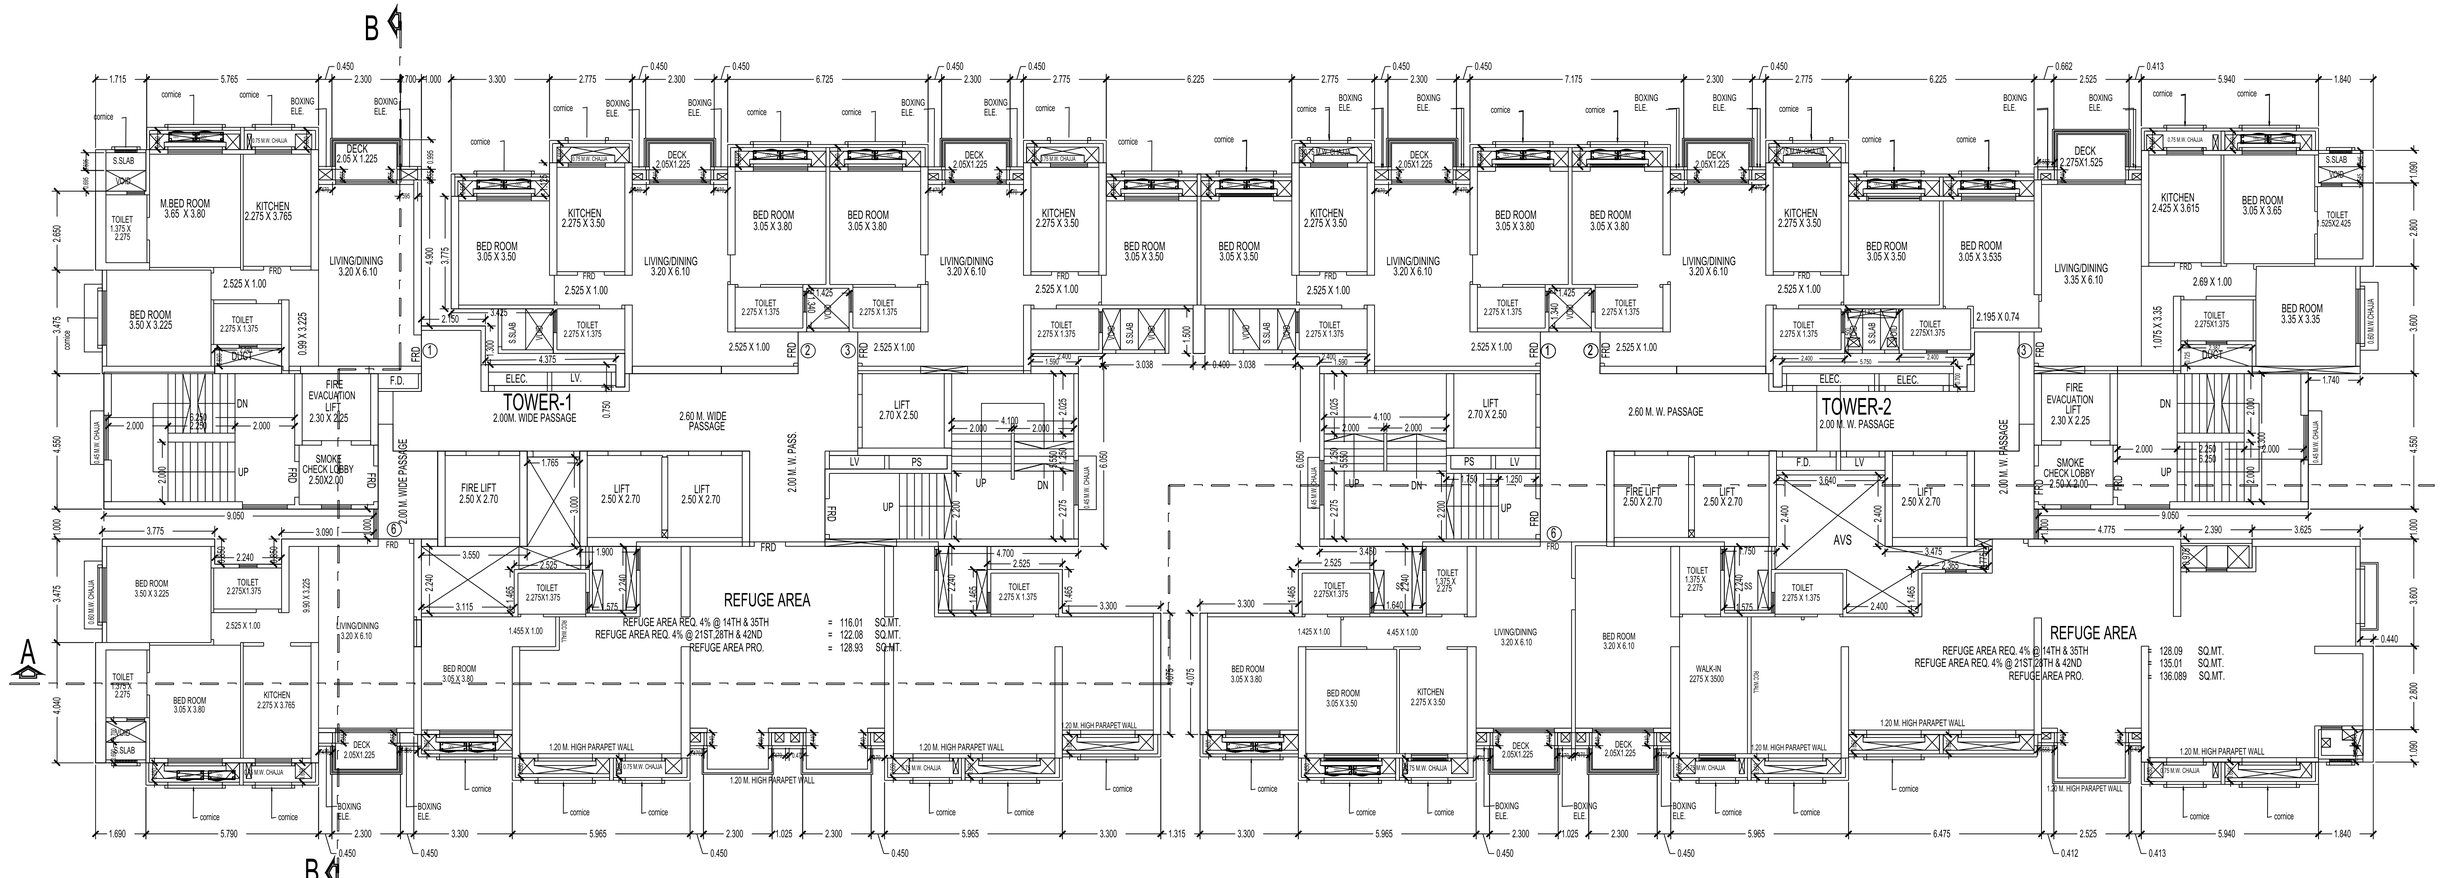

14TH, 21ST, 28TH, 35TH & 42ND FLOOR REFUGE PLAN

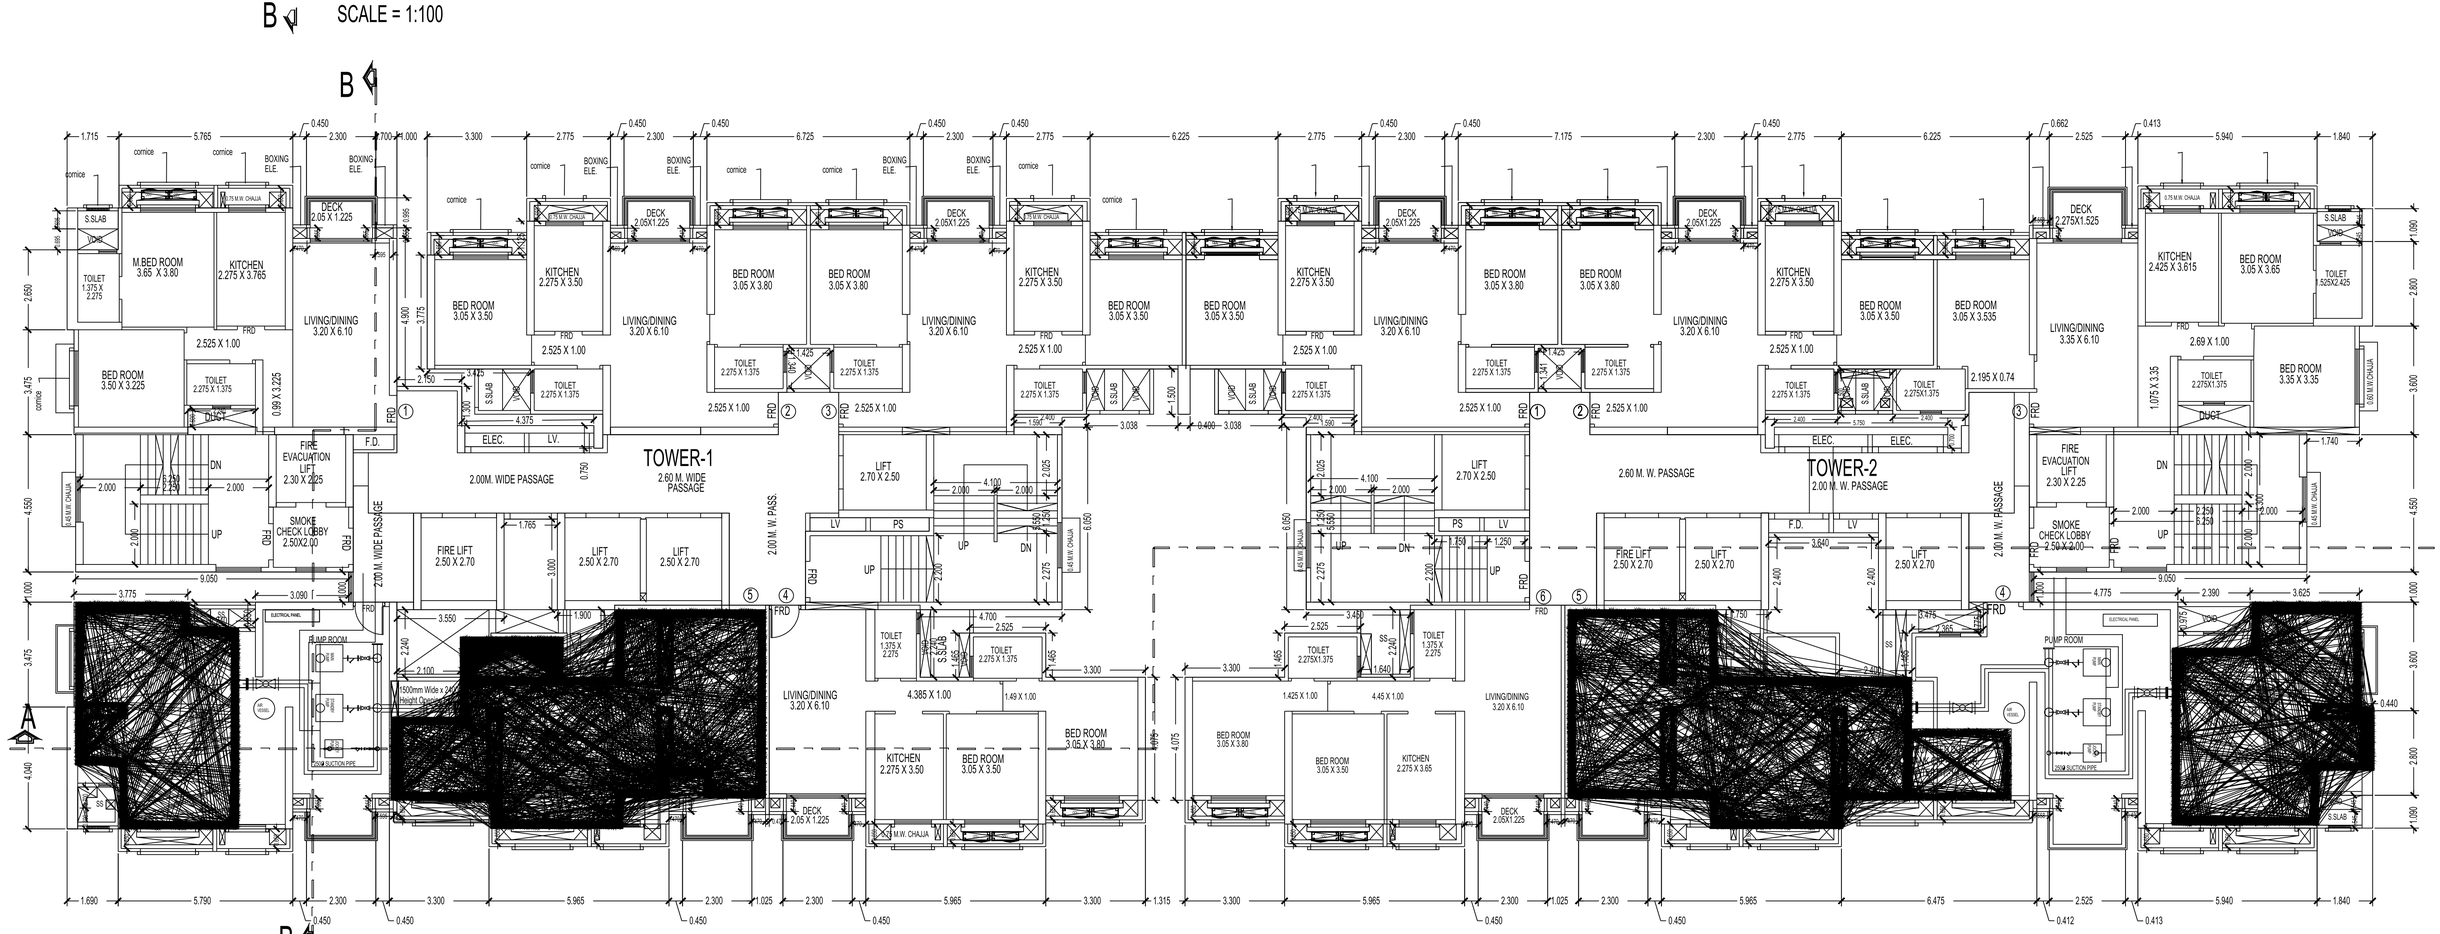

20TH & 41ST FLOOR (PART BREAK PRESSURE TANK) PLAN

SCALE = 1:100

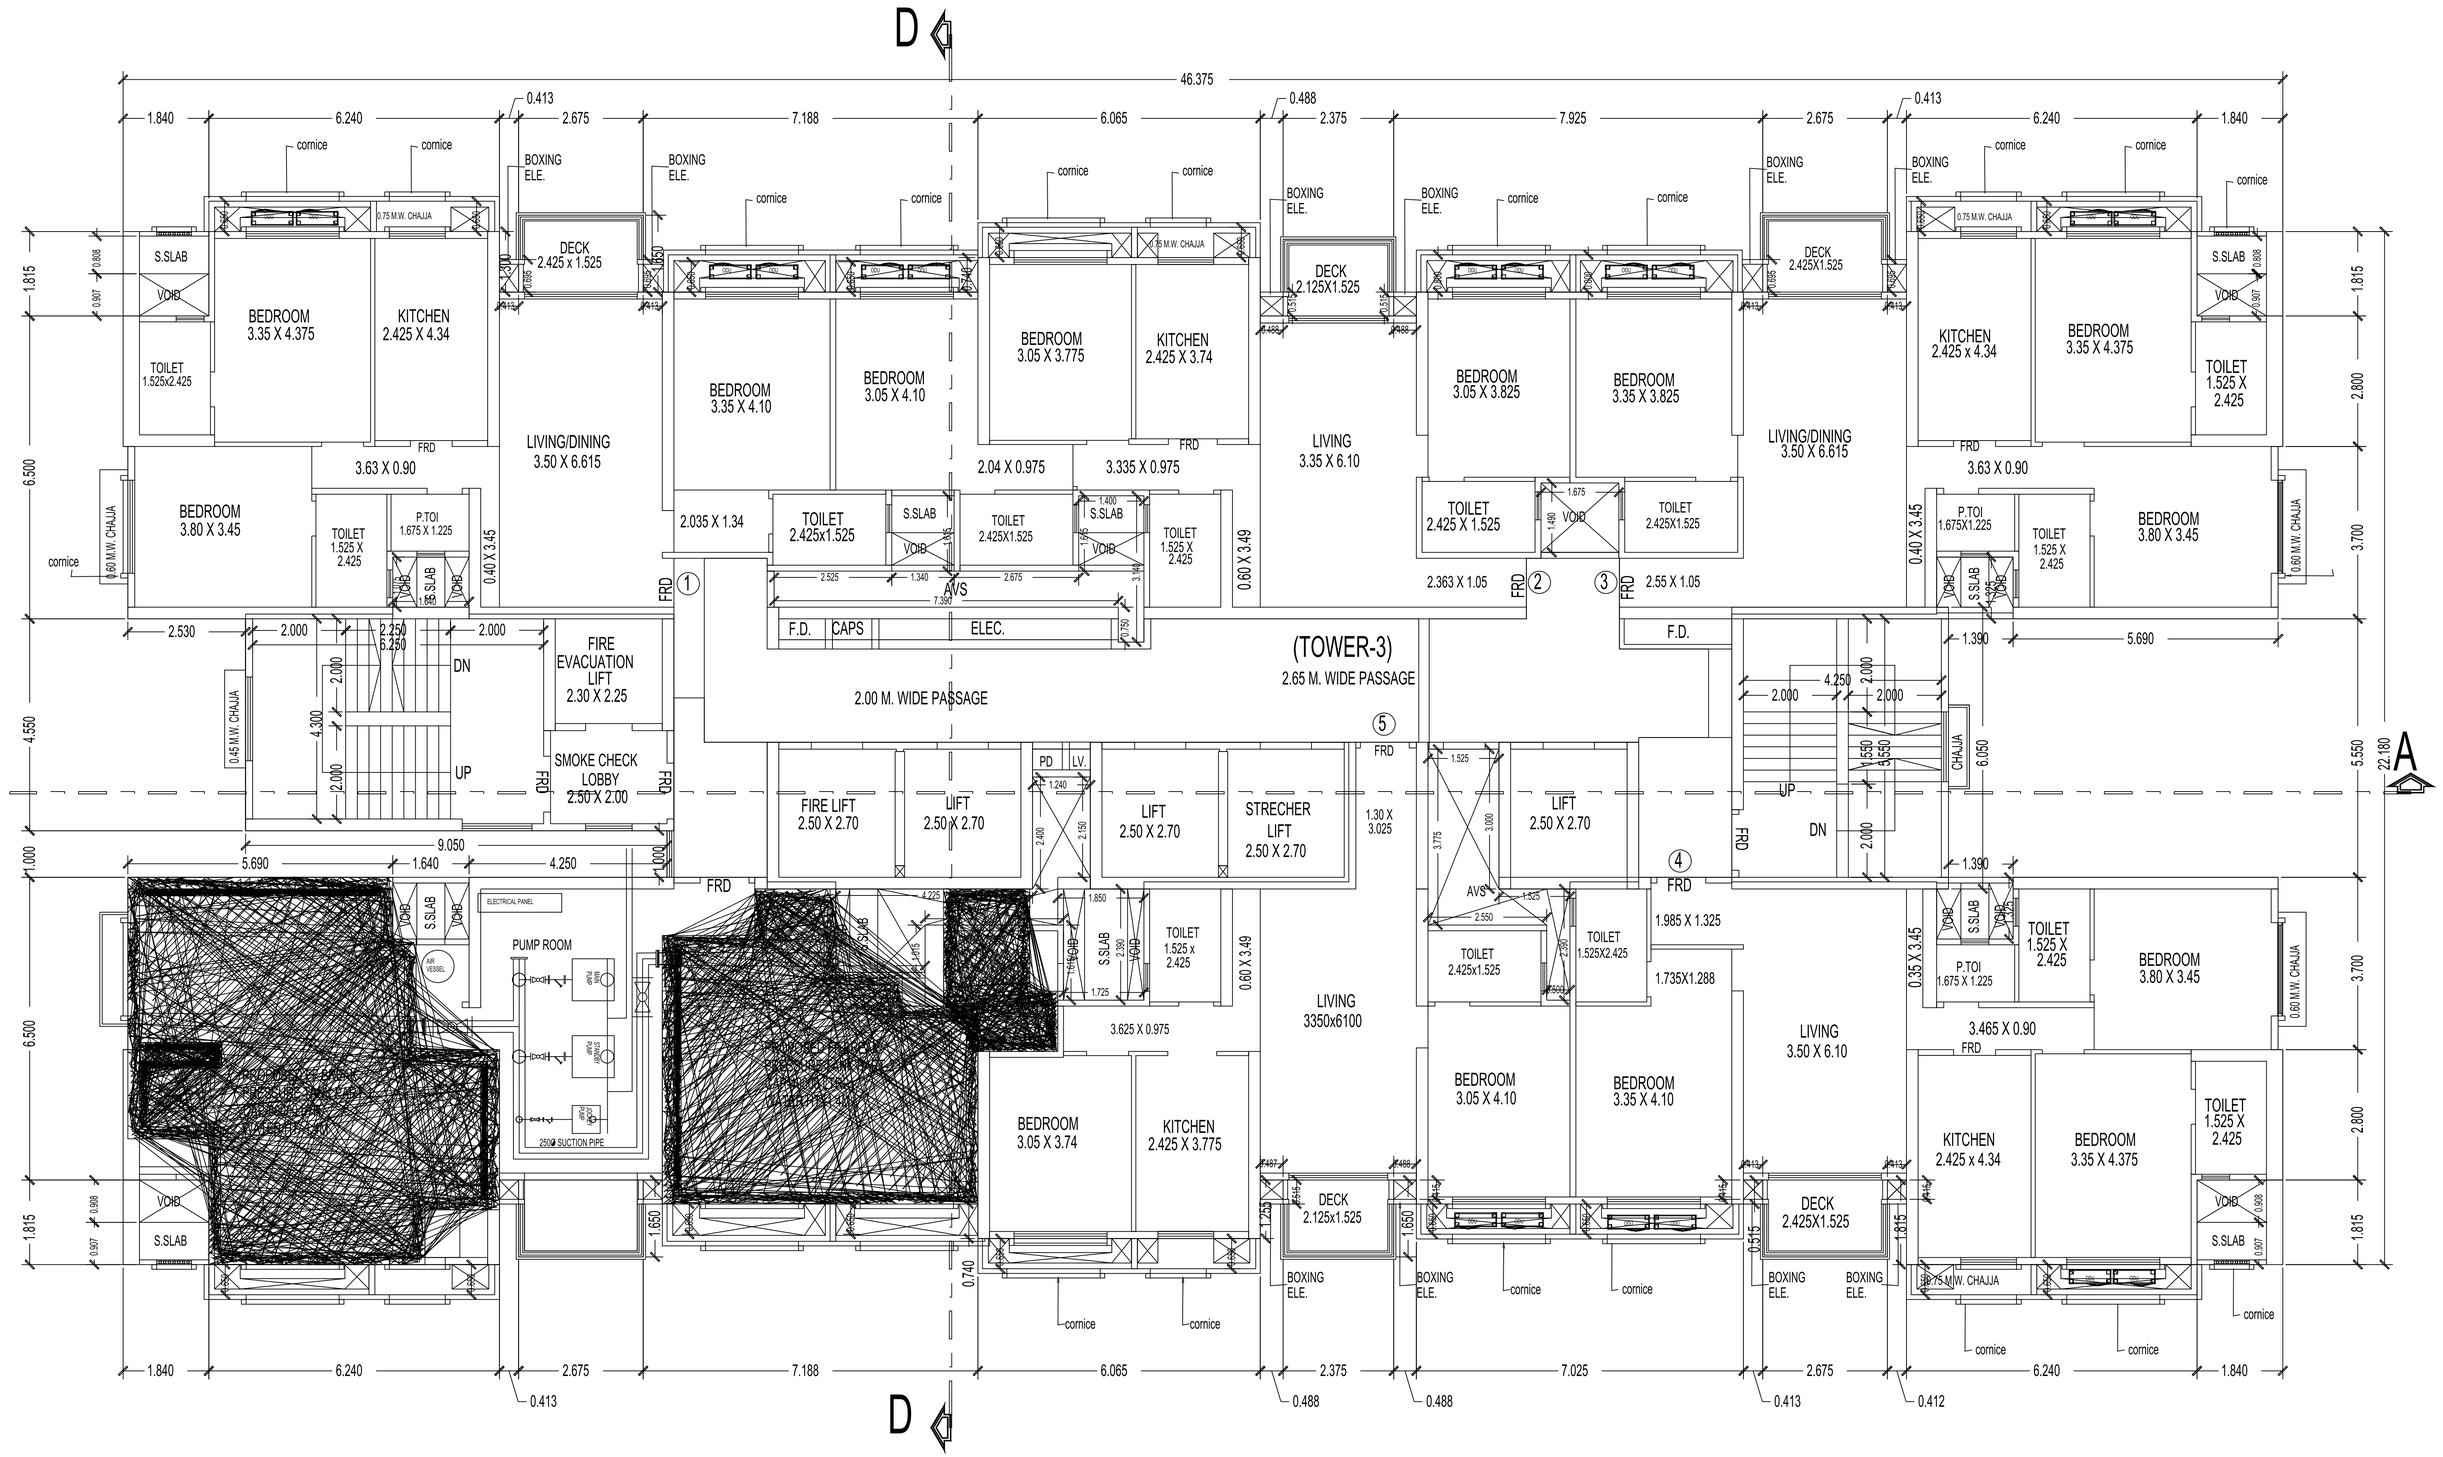

41ST FLOOR (PART BREAK PRESSURE TANK) PLAN

SCALE = 1:100

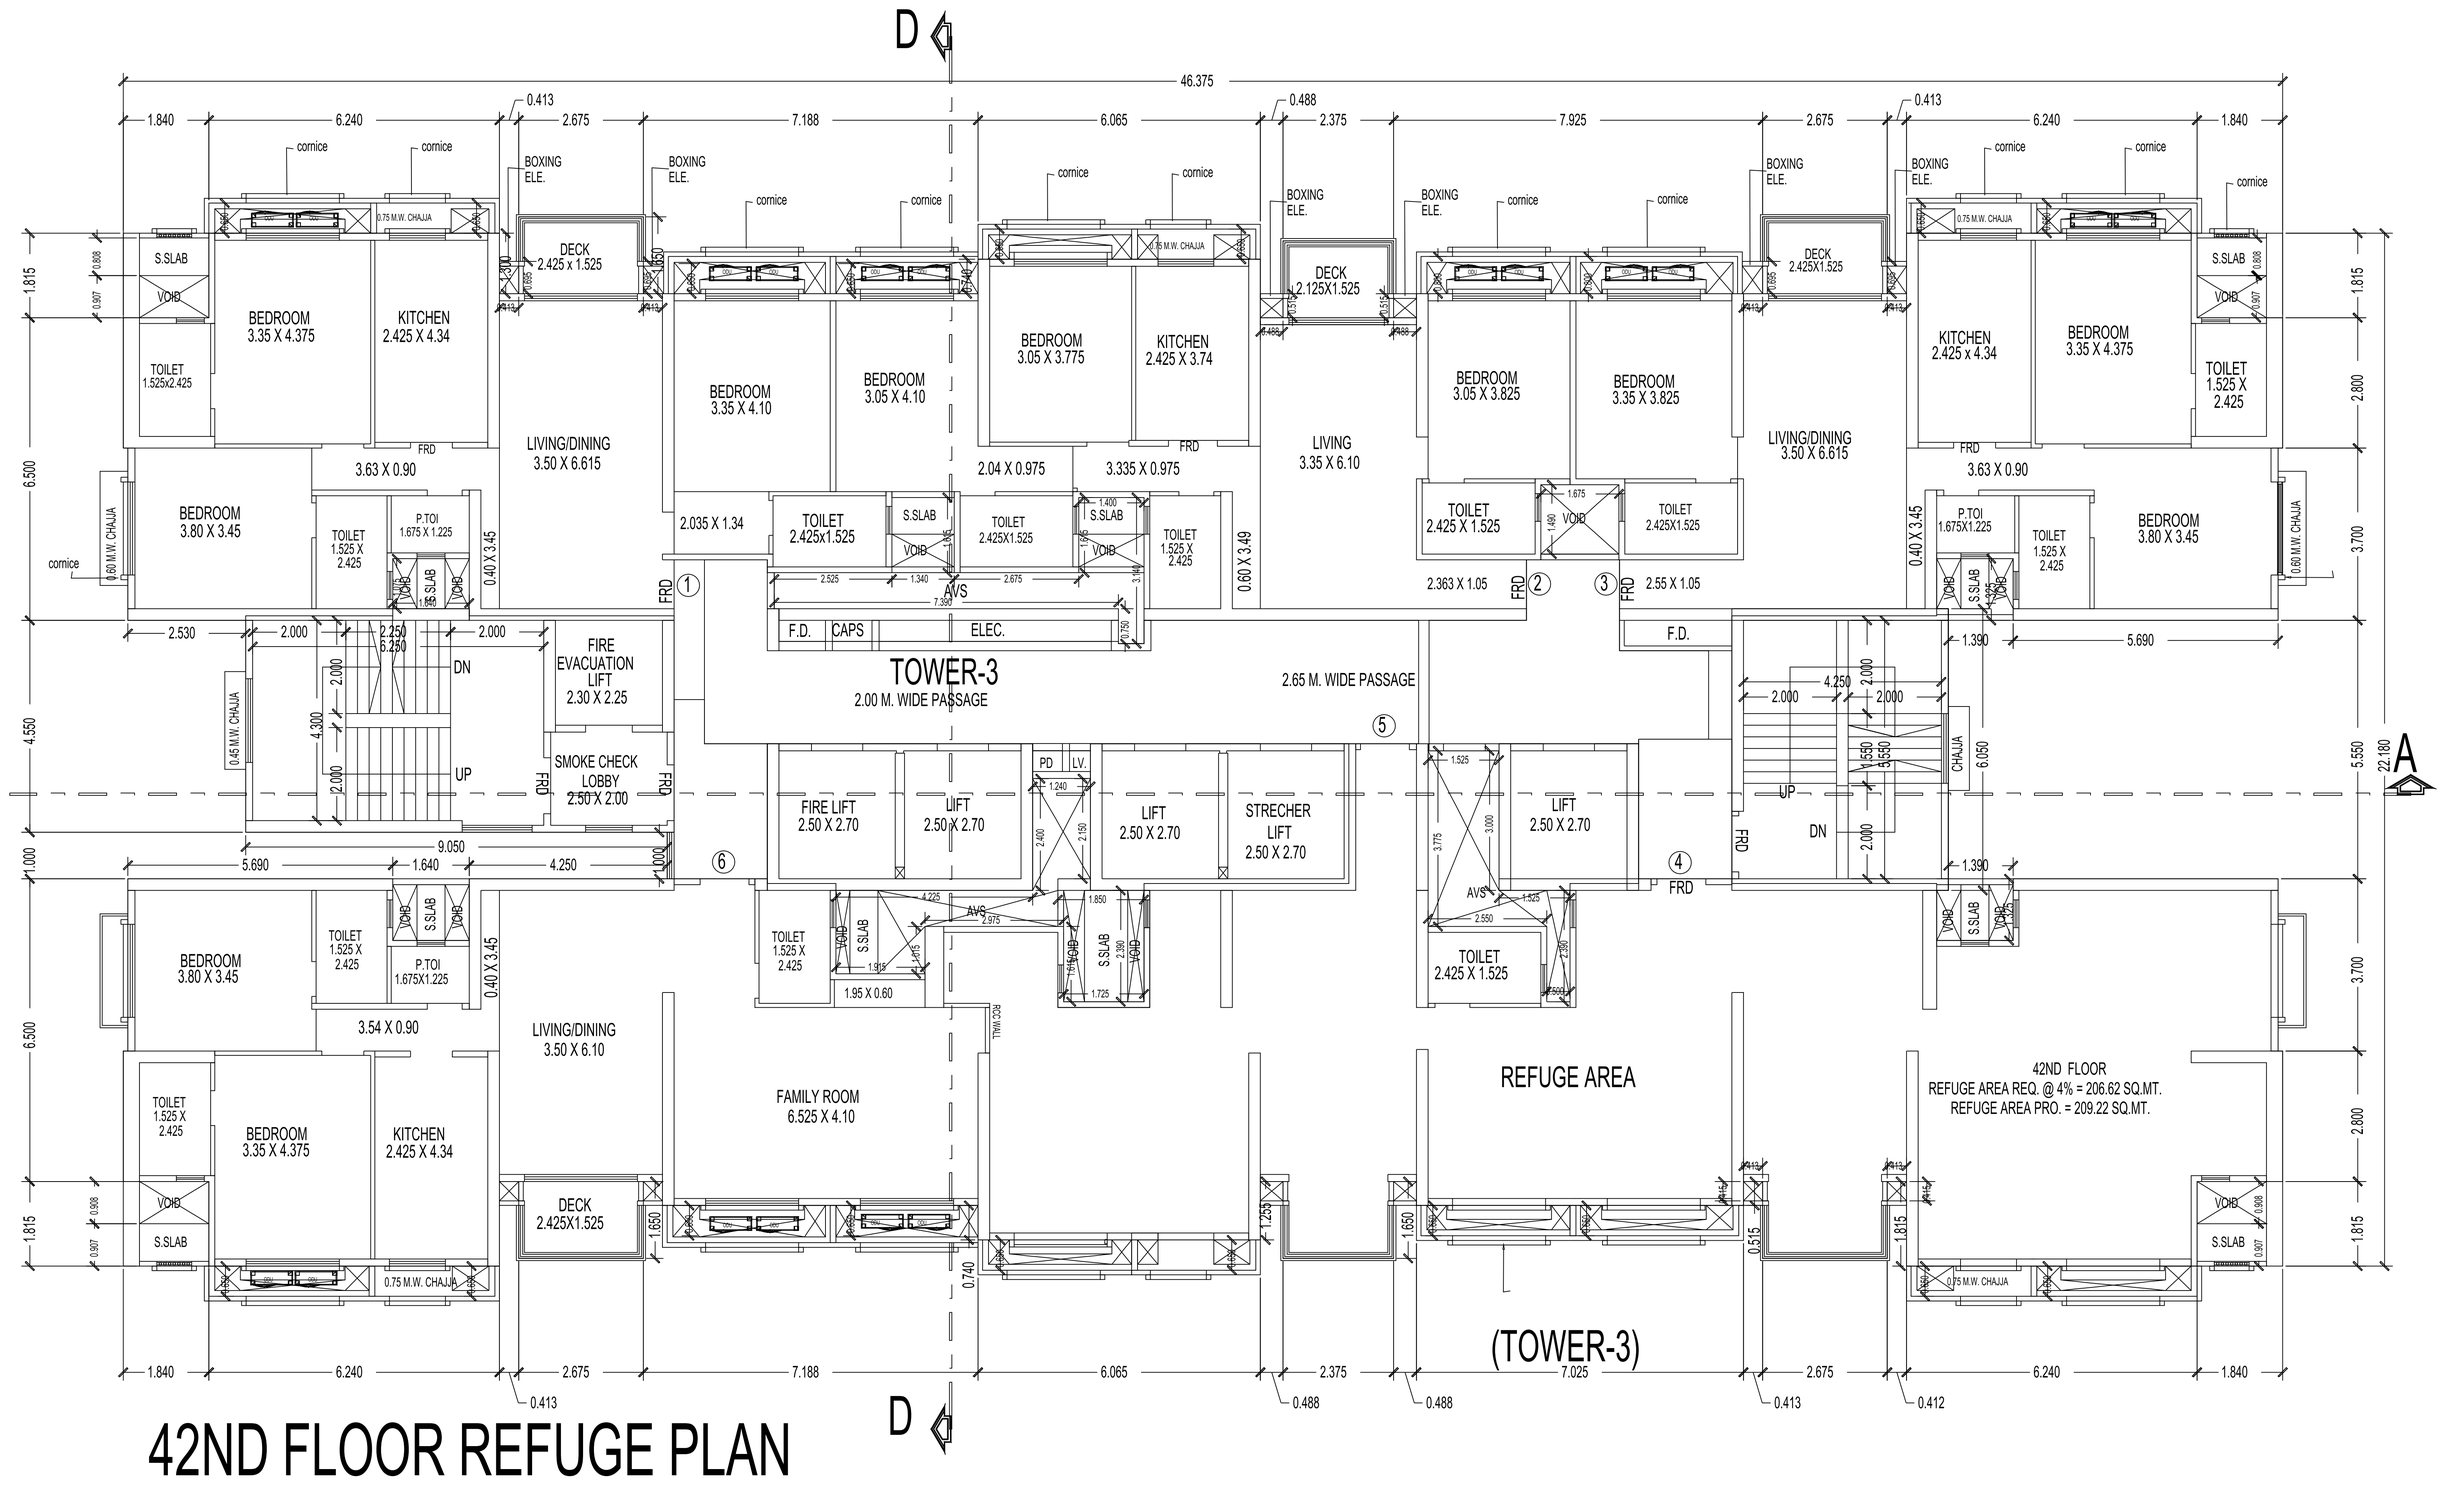

42ND FLOOR REFUGE PLAN