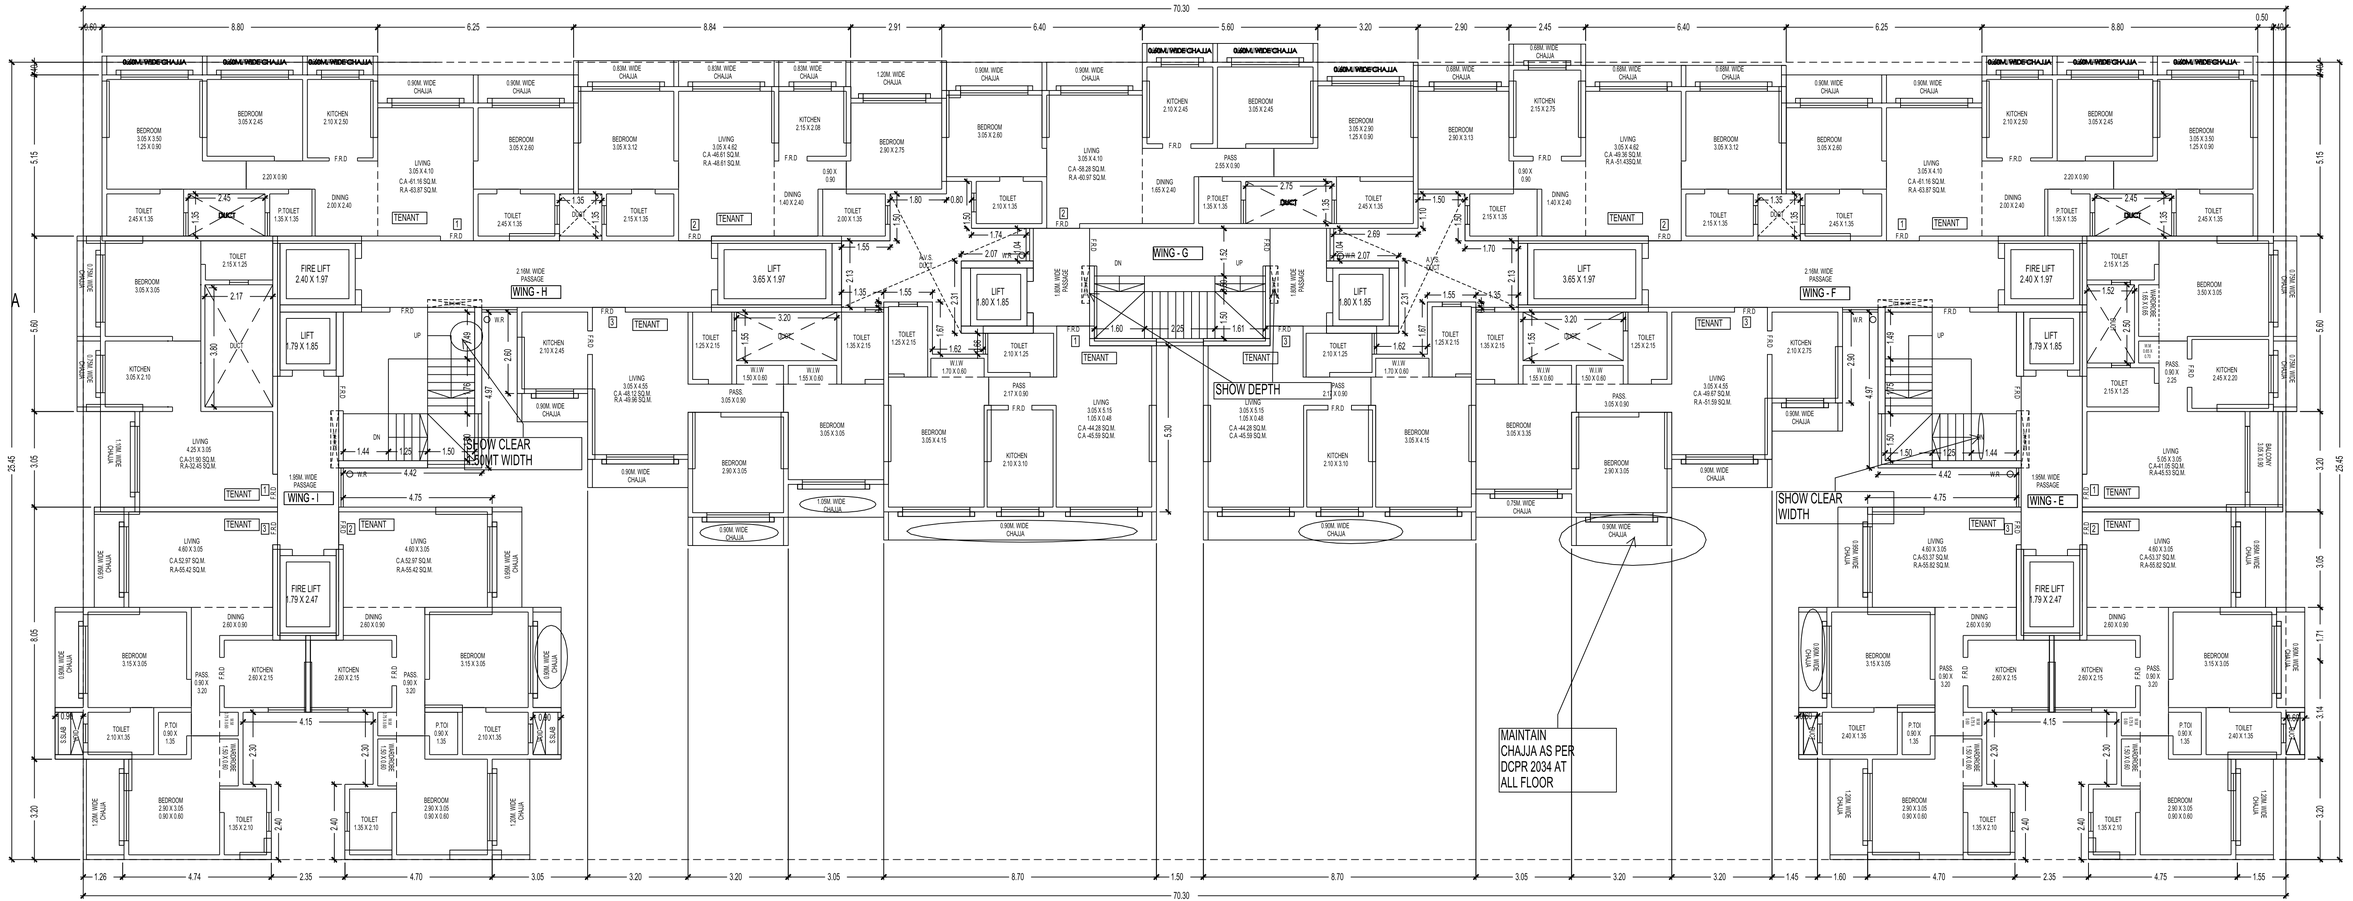

1ST FLOOR PLAN

(WING - E,F,G,H & I)

SCALE - 1:100

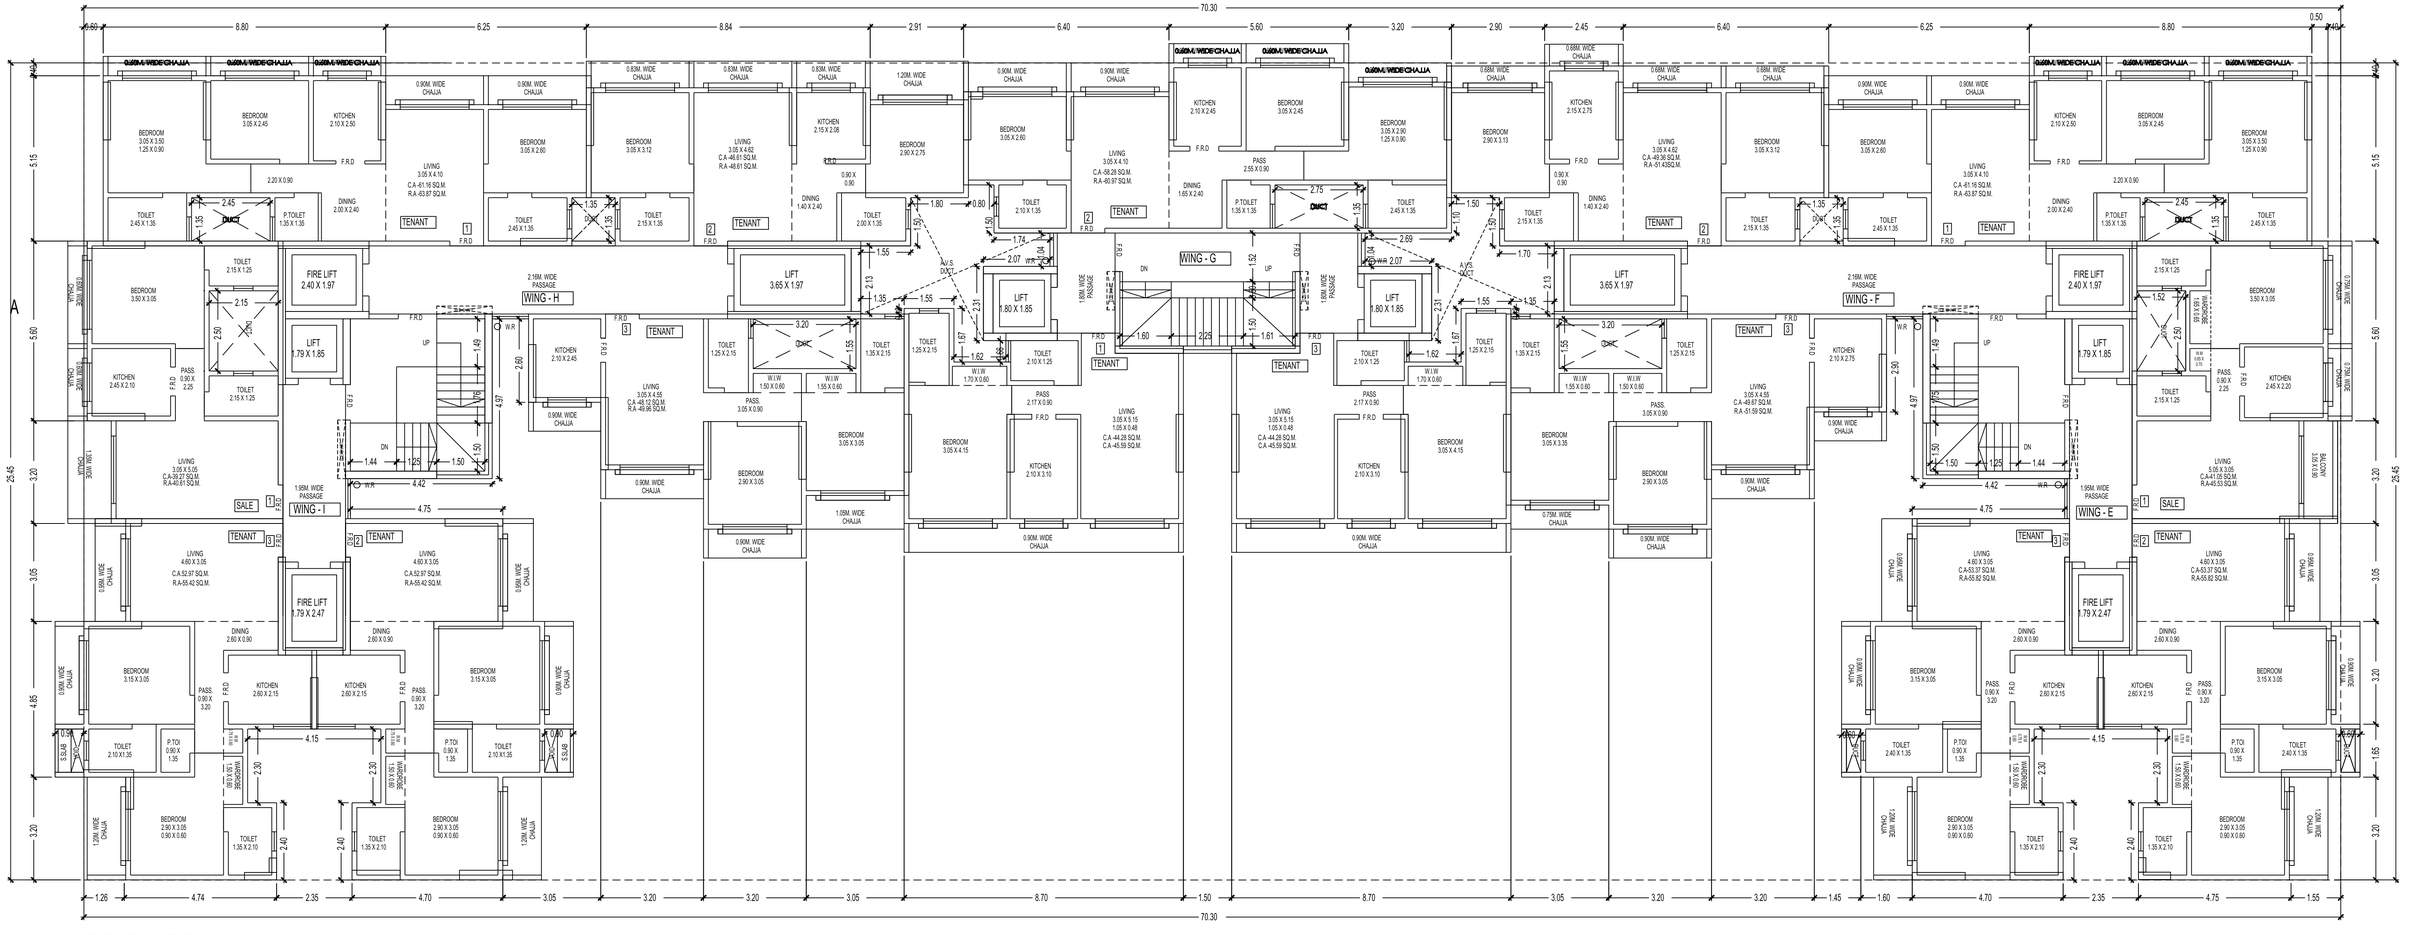

2ND FLOOR PLAN

(WING - E,F,G,H & I)

SCALE - 1:100

1.20M. HT. PARAPET WALL

1.20M. HT. PARAPET WALL

1 BIG | 2 BIG | 3 BIG | 4 BIG | 5 BIG | 6 BIG | 7 BIG | 8 BIG | 9 BIG | 10 BIG | 11 BIG | 12 BIG

SHOW RCC WALL

---5 .60M W IDED RIVEWAY- --

show CUT OUT

SCALE - 1:200

B

CUT out shall be shown to avoid the misuse.

B'

SPECIFY USER

BEDROOM 4.10 X 3.05 0.90 X 2.00 | TOILET 1.25 X 2.42 | F.R.D. | 1.75M. WIDE LOBBY | LIFT 1.80 X 1.90 | WING - A | BIG 20 | SMALL 19 | SMALL 18 | CAR LIFT 3.35 X 6.20 | CAR LIFT 3.35 X 6.20 | SMALL 17 | SMALL 16 | BIG 15 | WING - D | LIFT 1.80 X 1.90 | F.R.D. | SMALL 14 | SMALL 13

1.05M. WIDE CHAJJA | BEDROOM 3.05 X 2.90 | DUCT 0.45 X 1.25 | TOILET 1.25 X 2.30 | PASS. 0.90X 2.10 | W.R. | F.R.D. 1.50 | 1.00 | 1.50 | SHOW 1.50MT CLEAR WIDTH | SHOW 1.50MT CLEAR WIDTH OF STARICASE

KITCHEN 3.05 X 2.15 | F.R.D. | DINING 2.30 X 1.25 | 1.50 | 1.25 | 1.50

BALCONY 3.05 X 1.05 | LIVING 5.50 X 3.05 R.A - 691.00 SQ.FT | SALE | 2 | F.R.D. | WING - B 3.45 X 2.55 | SLC SHAFT | 0.67 X 1.20 | SLC SHAFT | 0.67 X 1.20 | WING - C 3.45 X 2.55 | F.R.D. | 3 | SALE | LIVING 5.50 X 3.35 R.A - 1038.00 SQ.FT | BALCONY 3.35 X 1.05

BALCONY 3.35 X 1.05 | LIVING 5.50 X 3.35 R.A - 1038.00 SQ.FT | 3 | F.R.D. | 2.00 X 2.10 | LIFT 2.08 X 2.00 | FIRE LIFT 3.00 X 1.70 | 2.25 | 0.95 | LIFT 2.08 X 2.00 | 2.00 X 2.10 | FIRE LIFT 3.00 X 1.70 | F.R.D. | 3 | SALE | LIVING 5.50 X 3.35 R.A - 1038.00 SQ.FT | BALCONY 3.35 X 1.05

DRY BAL. 2.30 X 1.05 | KITCHEN 3.20 X 2.30 | F.R.D. | DINING 2.15 X 2.60 | TOILET 1.35 X 2.45 | TOILET 2.75 X 1.35 | W.R. | F.R.D. | 4 | SALE 1.05 X 2.30 | KITCHEN 3.05 X 2.15 | DRY BAL. 2.15 X 0.85 | 2.30 | DUCT 0.95 | 1.25 | 2.75 | DUCT | 12.00 | F.R.D. | W.R. | F.R.D. | 4 | SALE 1.05 X 2.30 | KITCHEN 3.05 X 2.15 | DRY BAL. 2.15 X 0.85 | 2.30 | DUCT 0.95 | 1.25 | 2.75 | TOILET 2.75 X 1.35 | TOILET 1.35 X 2.45 | DINING 2.15 X 2.60 | F.R.D. | KITCHEN 3.20 X 2.30 | DRY BAL. 2.30 X 1.05

S. SLAB | VOID 1.20 | TOILET 2.15 X 1.35 | PASSAGE 3.05 X 0.90 | DINING 2.05 X 2.40 | P.TOILET 1.30 X 1.35 | 1.50 | DUCT 1.80 | TOILET 2.45 X 1.35 | TOILET 2.45 X 1.35 | DUCT 1.80 | 1.50 | P.TOILET 1.30 X 1.35 | DINING 2.05 X 2.40 | PASSAGE 3.05 X 0.90 | TOILET 2.15 X 1.35 | S. SLAB | VOID 1.20

1.20M. WIDE CHAJJA | BEDROOM 3.20 X 4.10 | BEDROOM 3.05 X 3.50 | BEDROOM 3.35 X 4.55 | PASSAGE 1.15 X 0.90 | LIVING 3.20 X 5.00 R.A - 808.00 SQ.FT | BEDROOM 3.05 X 3.50 | TOILET 2.25 X 1.35 | BEDROOM 3.27 X 4.55 1.50 X 0.90 | BEDROOM 3.27 X 4.55 1.50 X 0.90 | TOILET 2.25 X 1.35 | BEDROOM 3.05 X 3.50 | PASSAGE 1.15 X 0.90 | LIVING 3.20 X 5.00 R.A - 808.00 SQ.FT | BEDROOM 3.35 X 4.55 | BEDROOM 3.05 X 3.50 | BEDROOM 3.20 X 4.10 | 1.20M. WIDE CHAJJA

1.05M. WIDE CHAJJA | 1.05M. WIDE CHAJJA | BALCONY 3.20 X 0.90 | 0.60M. WIDE CHAJJA | VOID 1.20 | S. SLAB | 0.60M. WIDE CHAJJA | BALCONY 3.20 X 0.90 | 1.05M. WIDE CHAJJA | 1.05M. WIDE CHAJJA | 0.60M. WIDE CHAJJA

5.75

1.20 | 3.50 | 6.55 | 6.70 | 1.35 | 7.00 | 1.35 | 6.70 | 6.55 | 3.50 | 1.20

SLOPPING TERRACE

MAINTAIN 1.50

3RD FLOOR PLAN

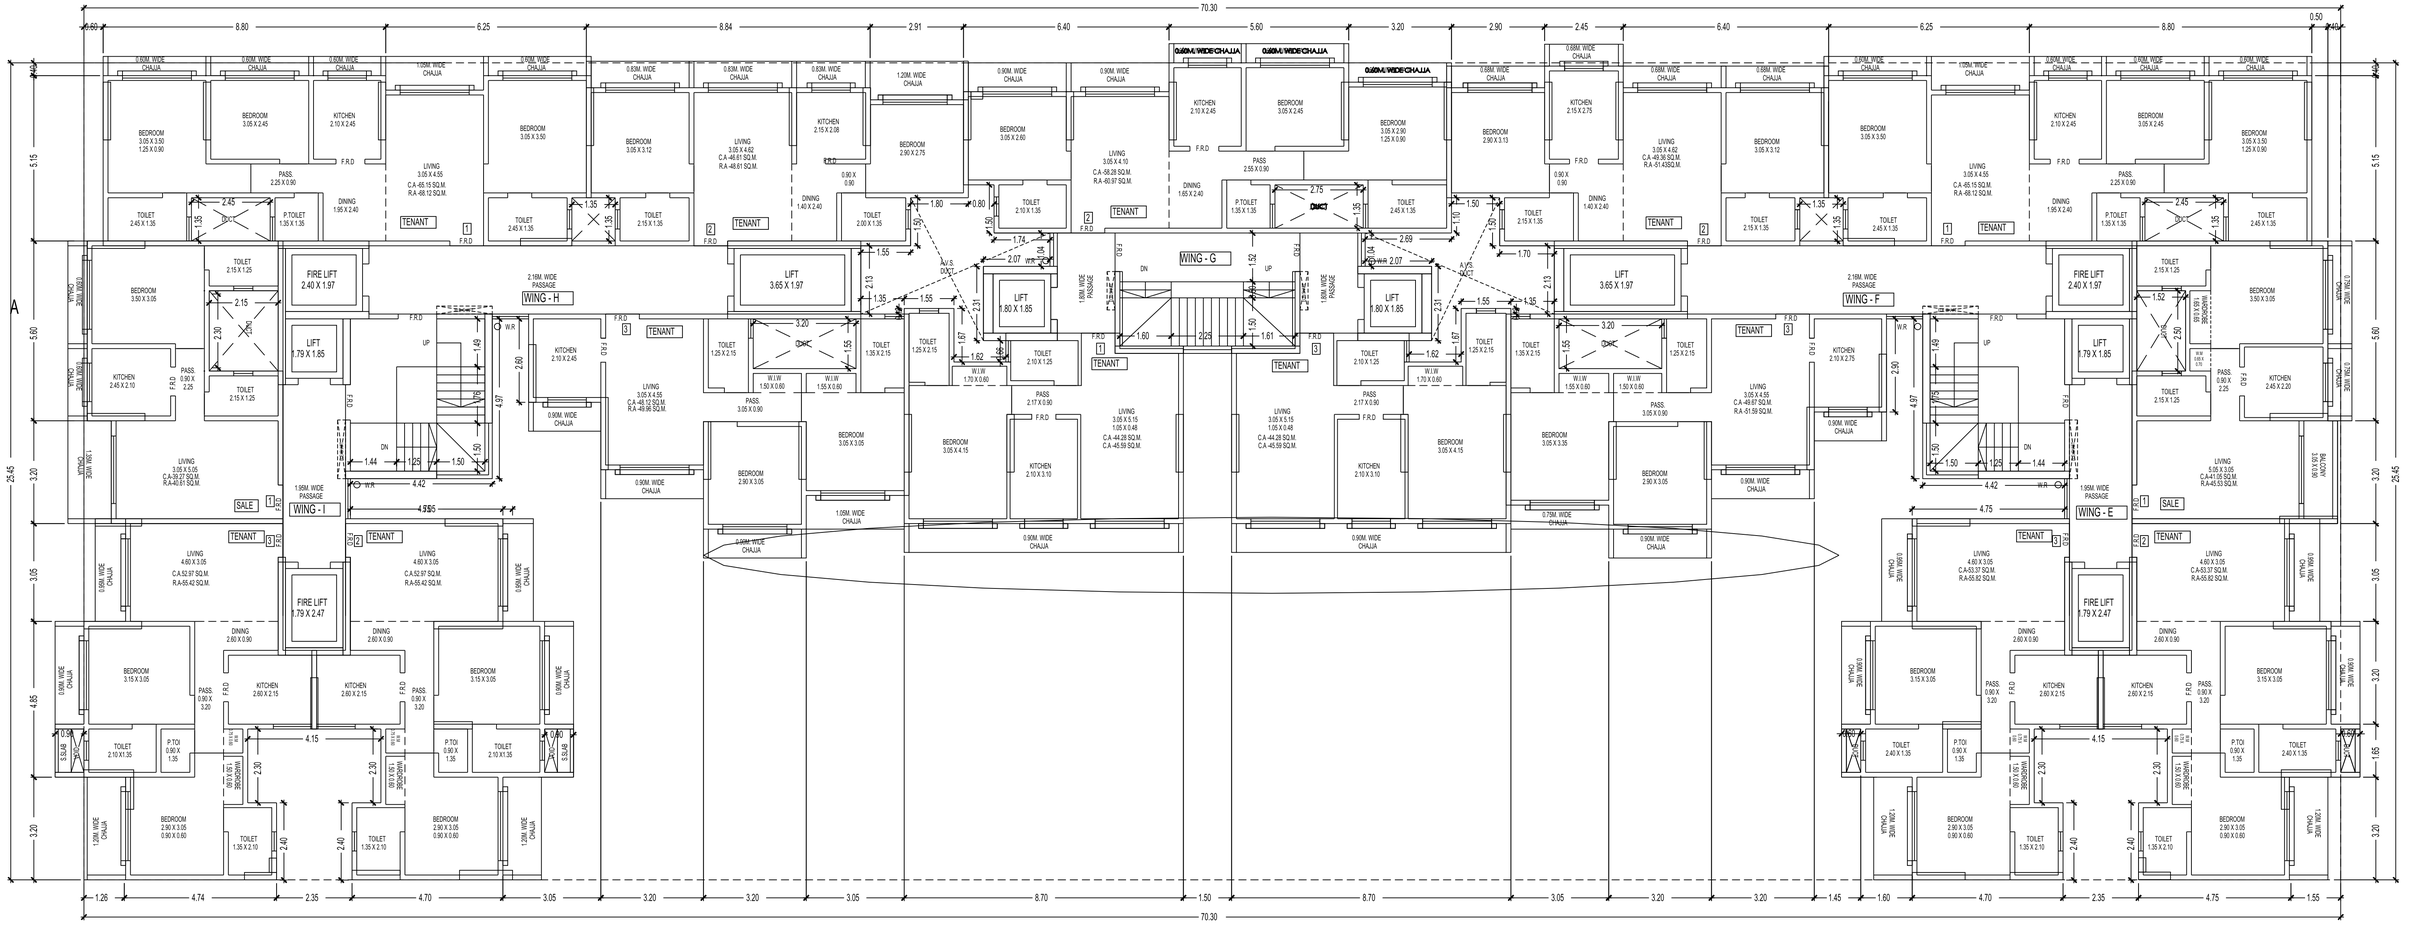

3RD FLOOR PLAN

(WING - E,F,G,H & I)

SCALE - 1:100

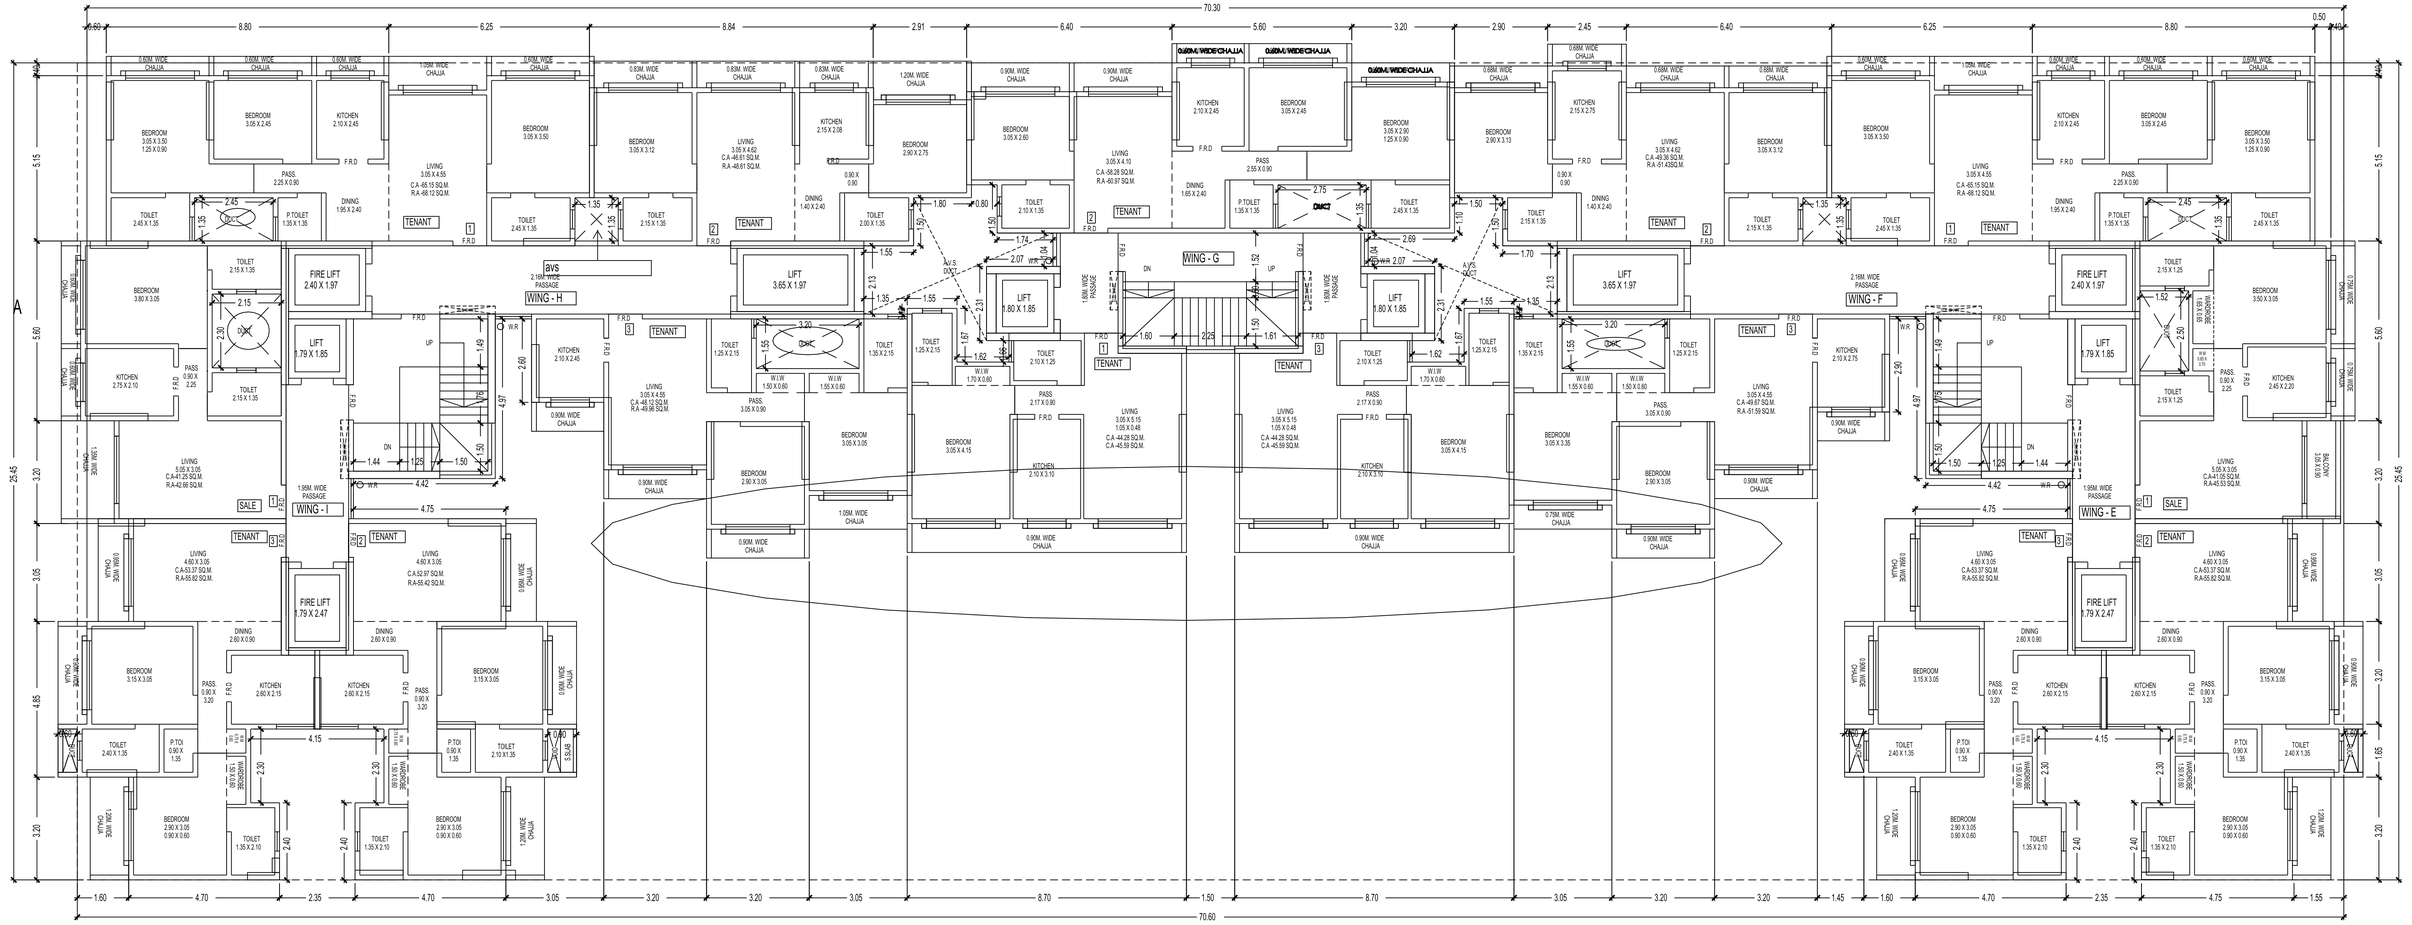

4TH FLOOR PLAN

(WING - E,F,G,H & I)

SCALE - 1:100

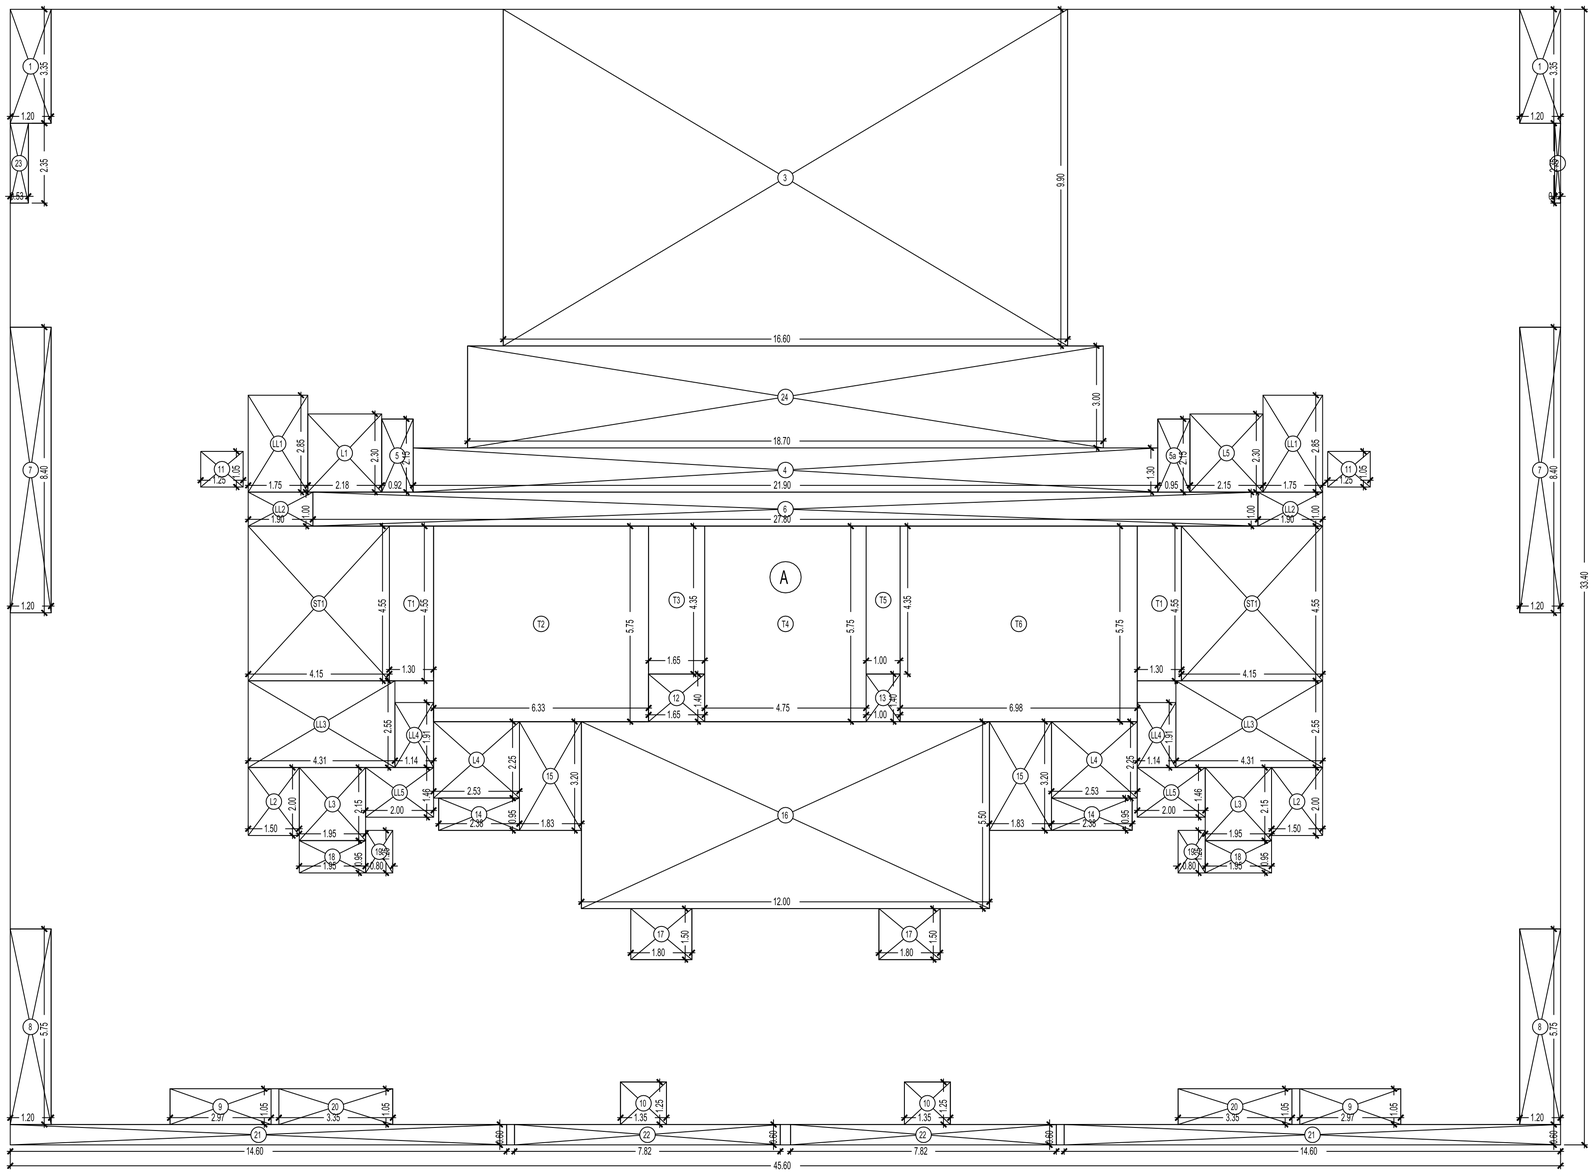

BUILT UP AREA OF TYPICAL FLOOR (4TH TO 7TH, 9TH TO 12TH)
(WING - A,B,C & D)
SCALE - 1:100

BUILT UP AREA CALCULATION

TYPICAL FLOOR (4TH TO 7TH, 9TH TO 12TH)									
A	45.60	X	33.40	X	1 NO	=	1523.04	SQ.MT.	
					TOTAL ADDITION	=	1523.04	SQ.MT.	X
DEDUCTIONS									
1	1.20	X	3.35	X	2 NOS	=	8.04	SQ.MT.	
2	0.17	X	2.35	X	1 NO	=	0.40	SQ.MT.	
3	16.60	X	9.90	X	1 NO	=	164.34	SQ.MT.	
4	21.90	X	1.30	X	1 NO	=	28.47	SQ.MT.	
5	0.93	X	2.15	X	1 NO	=	2.00	SQ.MT.	
5a	0.95	X	2.15	X	1 NO	=	2.04	SQ.MT.	
6	27.80	X	1.00	X	1 NO	=	27.80	SQ.MT.	
7	1.20	X	8.40	X	2 NOS	=	20.16	SQ.MT.	
8	1.20	X	5.75	X	2 NOS	=	13.80	SQ.MT.	
9	2.97	X	1.05	X	2 NOS	=	6.24	SQ.MT.	
10	1.35	X	1.25	X	2 NOS	=	3.38	SQ.MT.	
11	1.25	X	1.05	X	2 NOS	=	2.63	SQ.MT.	
12	1.65	X	1.40	X	1 NO	=	2.31	SQ.MT.	
13	1.00	X	1.40	X	1 NO	=	1.40	SQ.MT.	
14	2.38	X	0.95	X	2 NOS	=	4.52	SQ.MT.	
15	1.83	X	3.20	X	2 NOS	=	11.71	SQ.MT.	
16	12.00	X	5.50	X	1 NO	=	66.00	SQ.MT.	
17	1.80	X	1.50	X	2 NOS	=	5.40	SQ.MT.	
18	1.95	X	0.95	X	2 NOS	=	3.71	SQ.MT.	
19	0.80	X	1.25	X	2 NOS	=	2.00	SQ.MT.	
20	3.35	X	1.05	X	2 NOS	=	7.04	SQ.MT.	
21	14.60	X	0.60	X	2 NOS	=	17.52	SQ.MT.	
22	7.82	X	0.60	X	2 NOS	=	9.38	SQ.MT.	
23	0.53	X	2.35	X	1 NO	=	1.25	SQ.MT.	
24	18.70	X	3.00	X	1 NO	=	56.10	SQ.MT.	
					TOTAL DEDUCTION	=	467.64	SQ.MT.	Y1
TOTAL BUILT UP AREA [X - Y1]						=	1055.40	SQ.MT.	X1

STAIRCASE AREA CALCULATION

TYPICAL FLOOR									
L1	2.18	X	2.30	X	1 NO	=	5.01	SQ.MT.	
L2	1.50	X	2.00	X	2 NOS	=	6.00	SQ.MT.	
L3	1.95	X	2.15	X	2 NOS	=	8.39	SQ.MT.	
L4	2.53	X	2.25	X	2 NOS	=	11.39	SQ.MT.	
L5	2.15	X	2.30	X	1 NO	=	4.95	SQ.MT.	
LL1	1.75	X	2.85	X	2 NOS	=	9.98	SQ.MT.	
LL2	1.90	X	1.00	X	2 NOS	=	3.80	SQ.MT.	
LL3	4.31	X	2.55	X	2 NOS	=	21.98	SQ.MT.	
LL4	1.14	X	1.91	X	2 NOS	=	4.35	SQ.MT.	
LL5	2.00	X	1.46	X	2 NOS	=	5.84	SQ.MT.	
ST1	4.15	X	4.55	X	2 NOS	=	37.77	SQ.MT.	
TOTAL STAIRCASE AREA PER FL. (TYPICAL FLOOR)						=	119.46	SQ.MT.	Y2

NET BUILT UP AREA [X1 - Y2]	=	935.94	SQ.MT.

TENANT AREA CALCULATION

4TH TO 7TH, 9TH TO 12TH									
T1	1.30	X	4.55	X	2 NOS	=	11.83	SQ.MT.	
T2	6.33	X	5.75	X	1 NO	=	36.40	SQ.MT.	
T3	1.65	X	4.35	X	1 NO	=	7.18	SQ.MT.	
T4	4.75	X	5.75	X	1 NO	=	27.31	SQ.MT.	
T5	1.00	X	4.35	X	1 NO	=	4.35	SQ.MT.	
T6	6.98	X	5.75	X	1 NO	=	40.14	SQ.MT.	
					TOTAL ADDITION	=	127.21	SQ.MT.	X

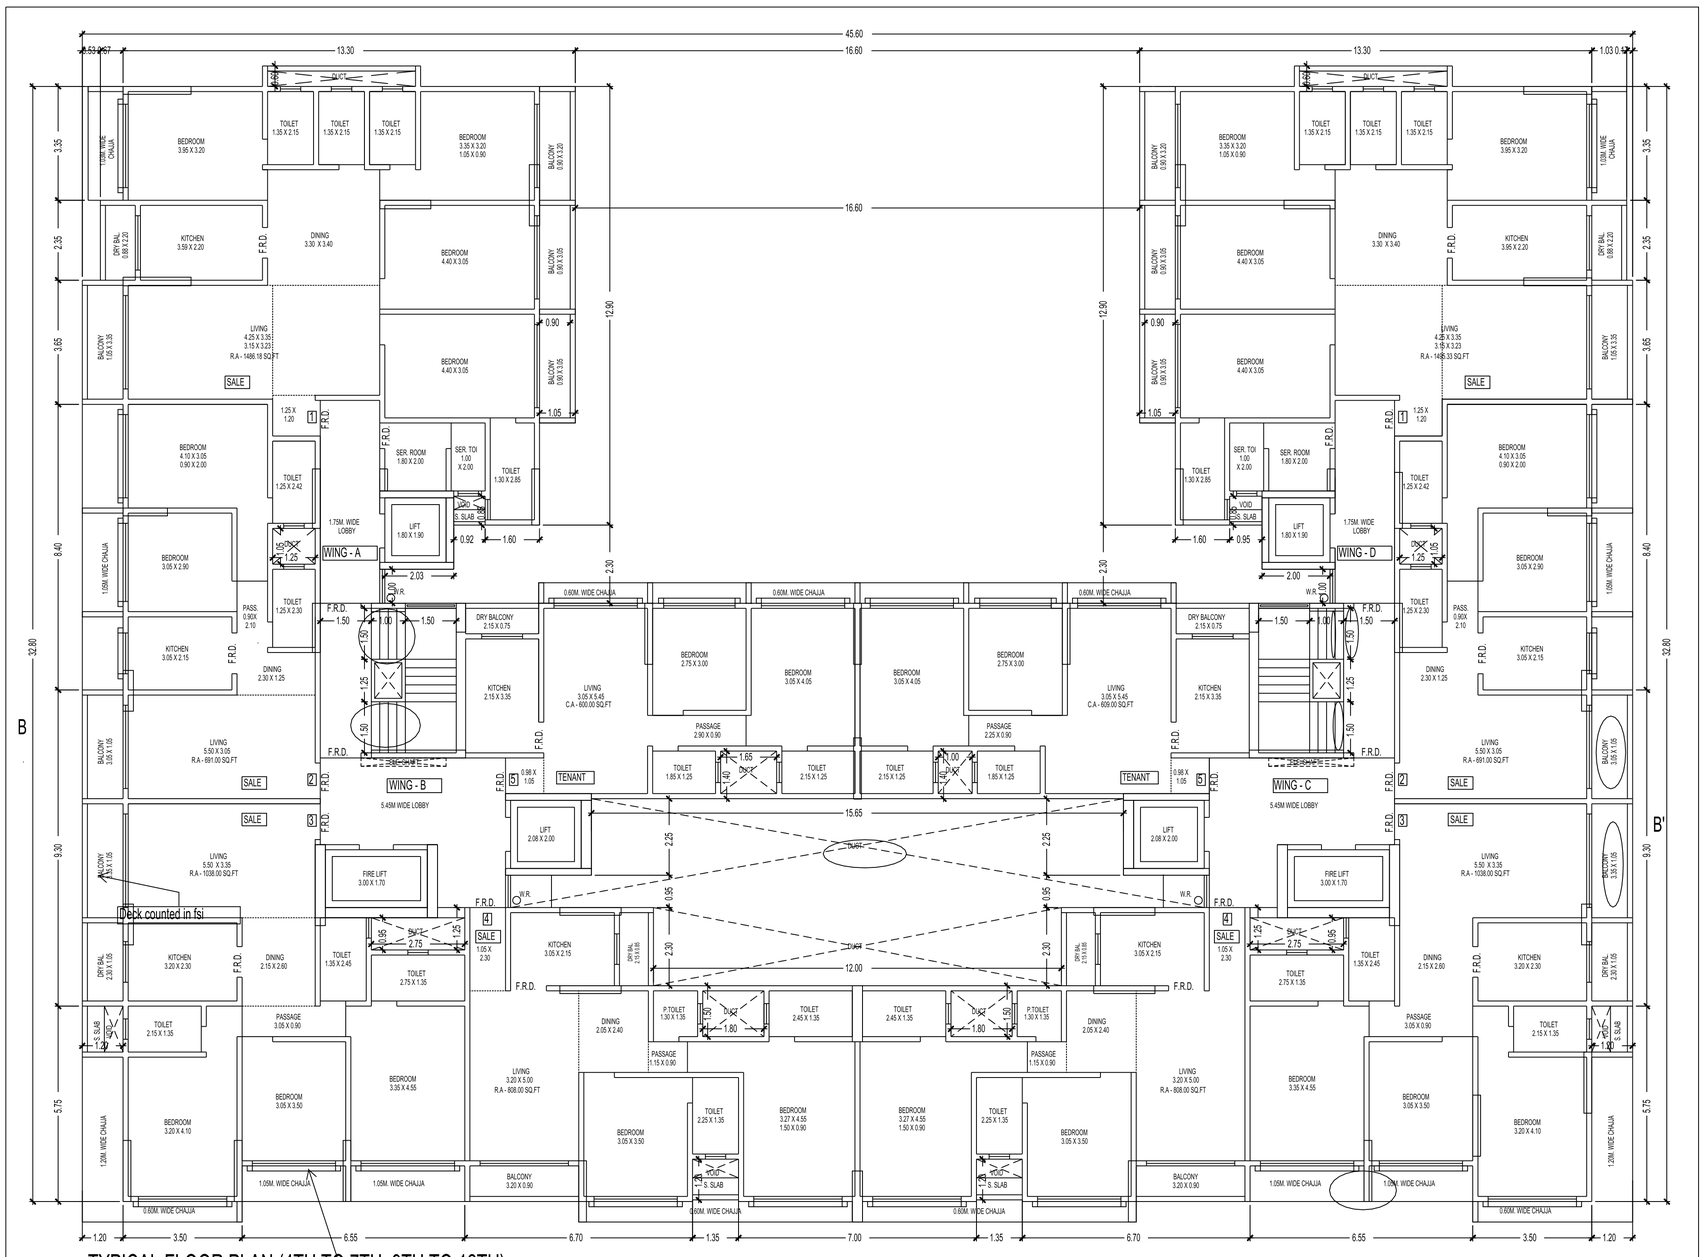

TYPICAL FLOOR PLAN (4TH TO 7TH, 9TH TO 12TH)
(WING - A,B,C & D)
SCALE - 1:100

Plan for Consideration

Shrikant Chintaman Godade

S.E.(BP) K/E-N

SHAIKH ASIF MUSA

A.E.(BP) K/East

Digitally signed by SHAIKH ASIF MUSA
DN: c=IN, o=BRIHANMUMBAI MUNICIPAL CORPORATION, ou=BUILDING PROPOSAL, 2.5.4.20=dc538dee2bc8ae44a0a24206efc4ca6d9817f07e6c4eea002678a87124eb0c3d6, st=Maharashtra, serialNumber=673174400a2a911c86f1019b5be280240407841b387a179d59e11fe669bc8900, cn=SHAIKH ASIF MUSA
Date: 2024.12.31 19:32:36 +05'30'

PROFORMA - B

CONTENTS OF THE SHEET
3RD FLOOR PLAN , BUILT UP AREA DIAGRAM & CALCULATION.
DESCRIPTION OF PROPOSAL & PROPERTY
PROPOSED REDEVELOPMENT OF BUILDING KNOWN AS "KALINA VIHAR DARSHAN CO-OP. HOUSING SOCIETY LTD" PLOT BEARING CTS NO.6934, 7261, 7270, 7270/B OF VILLAGE KOLEKALYAN, SANTACRUZ (E), MUMBAI- 400098.

NAME OF OWNER/APPLICANT	SIGNATURE
M/S. LAKHANI REALTY LLP	SUNNY VIJAY LAKHANI
NAME ADDRESS AND SIGNATURE OF ARCHITECT	Nitin Dattatray Gunjal — Digitally signed by Nitin Dattatray Gunjal Date: 2024.12.19 13:57:14 +05'30'

ALL DIMENSIONS ARE IN METER	
DRAWN	SHWETA
CHECKED	ARNITIN GUNJAL
SCALE	as shown
DATE	23.04.2024
DRG. NO.	--

NORTH

SPECO architect
AR.NITIN GUNJAL
REG. NO. CA/2008/42482

M/S. SPECO ARCHITECT
FLAT NO. -9, 2ND FLOOR,
MAYUR NIVAS, DR. AMBEDKAR ROAD,
DADAR T.T., DADAR, MUMBAI-400 014.
TEL : +91- 9820 998758.
Email : specoarchitect@gmail.com
: ar.nitingunjal@gmail.com

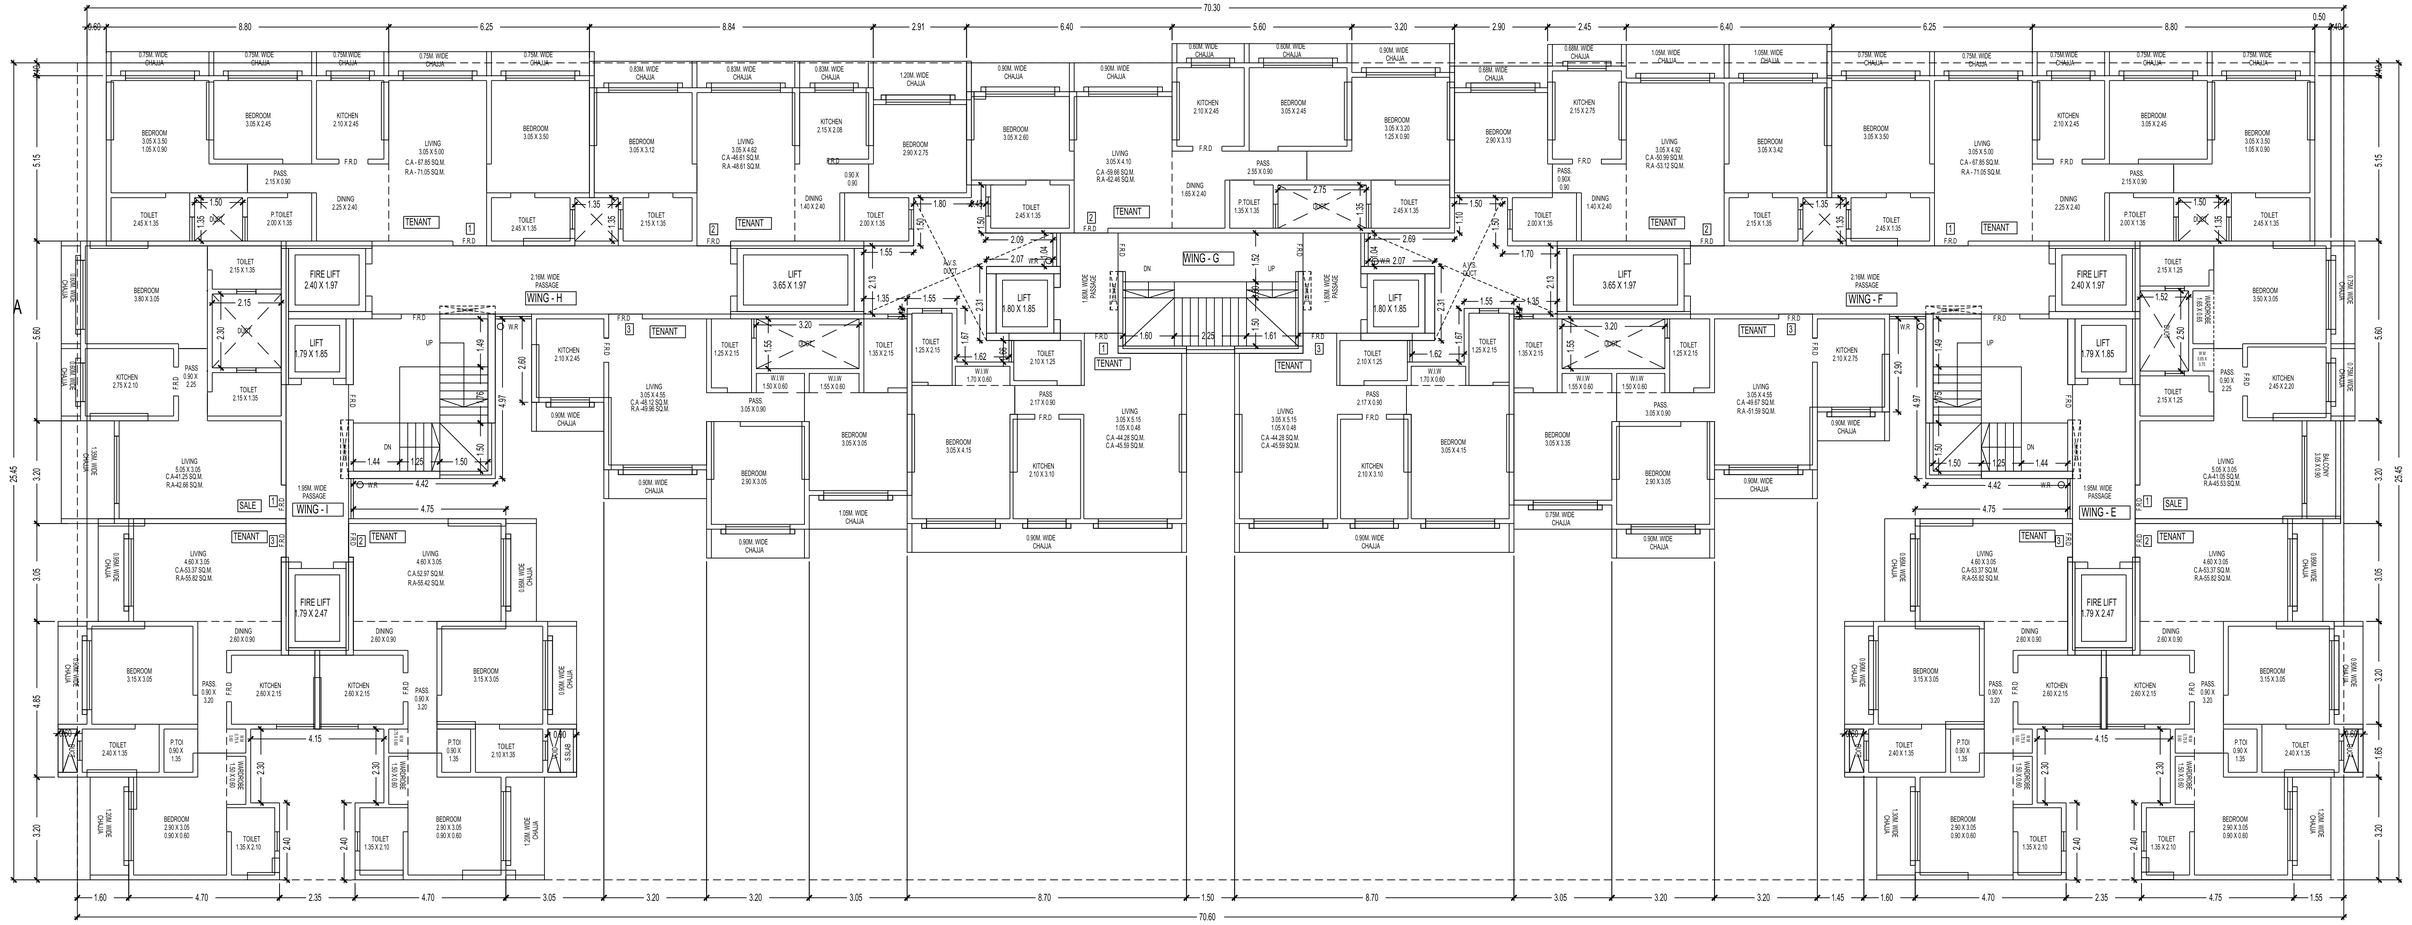

5TH FLOOR PLAN

(WING - E,F,G,H & I)

SCALE - 1:100

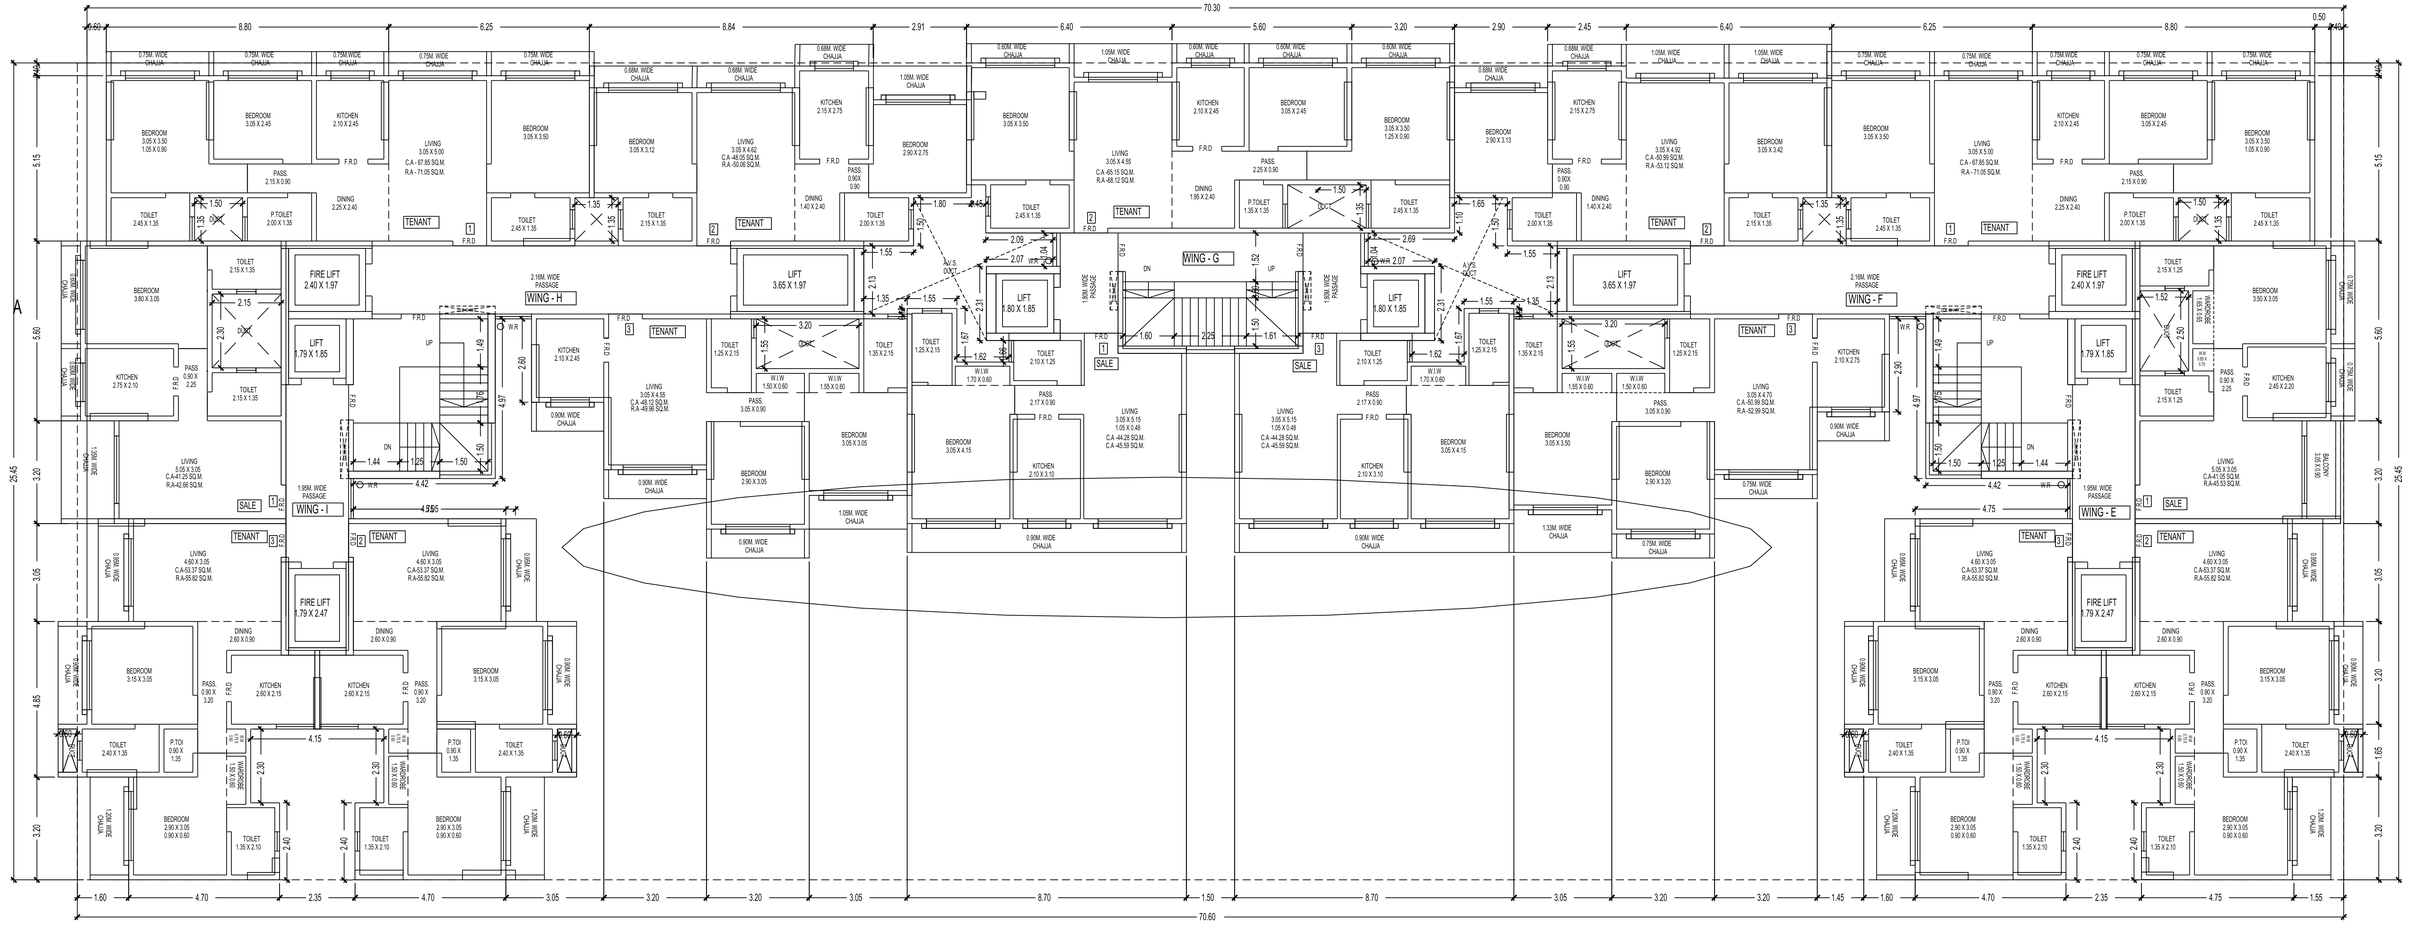

6TH FLOOR PLAN

(WING - E,F,G,H & I)

SCALE - 1:100

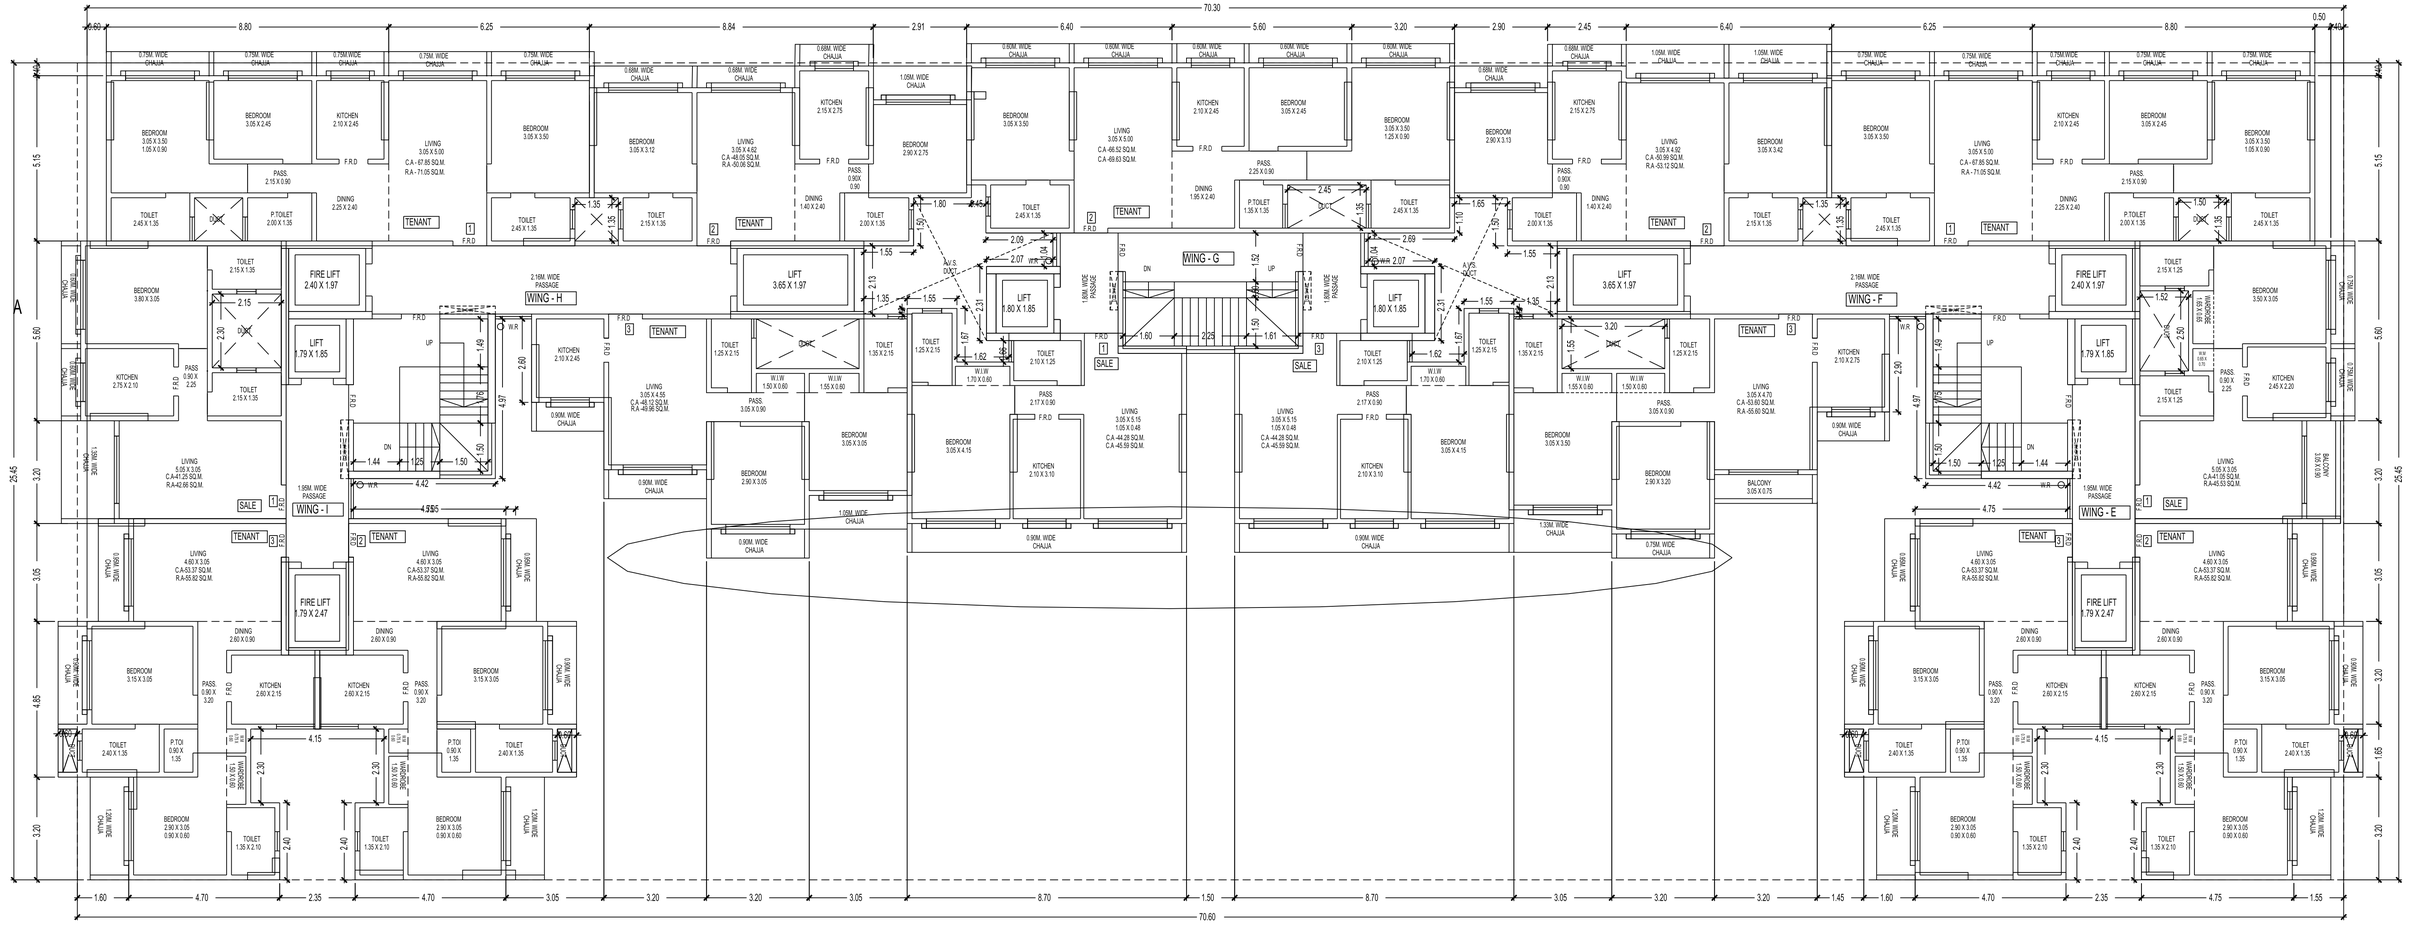

7TH FLOOR PLAN

(WING - E,F,G,H & I)

SCALE - 1:100

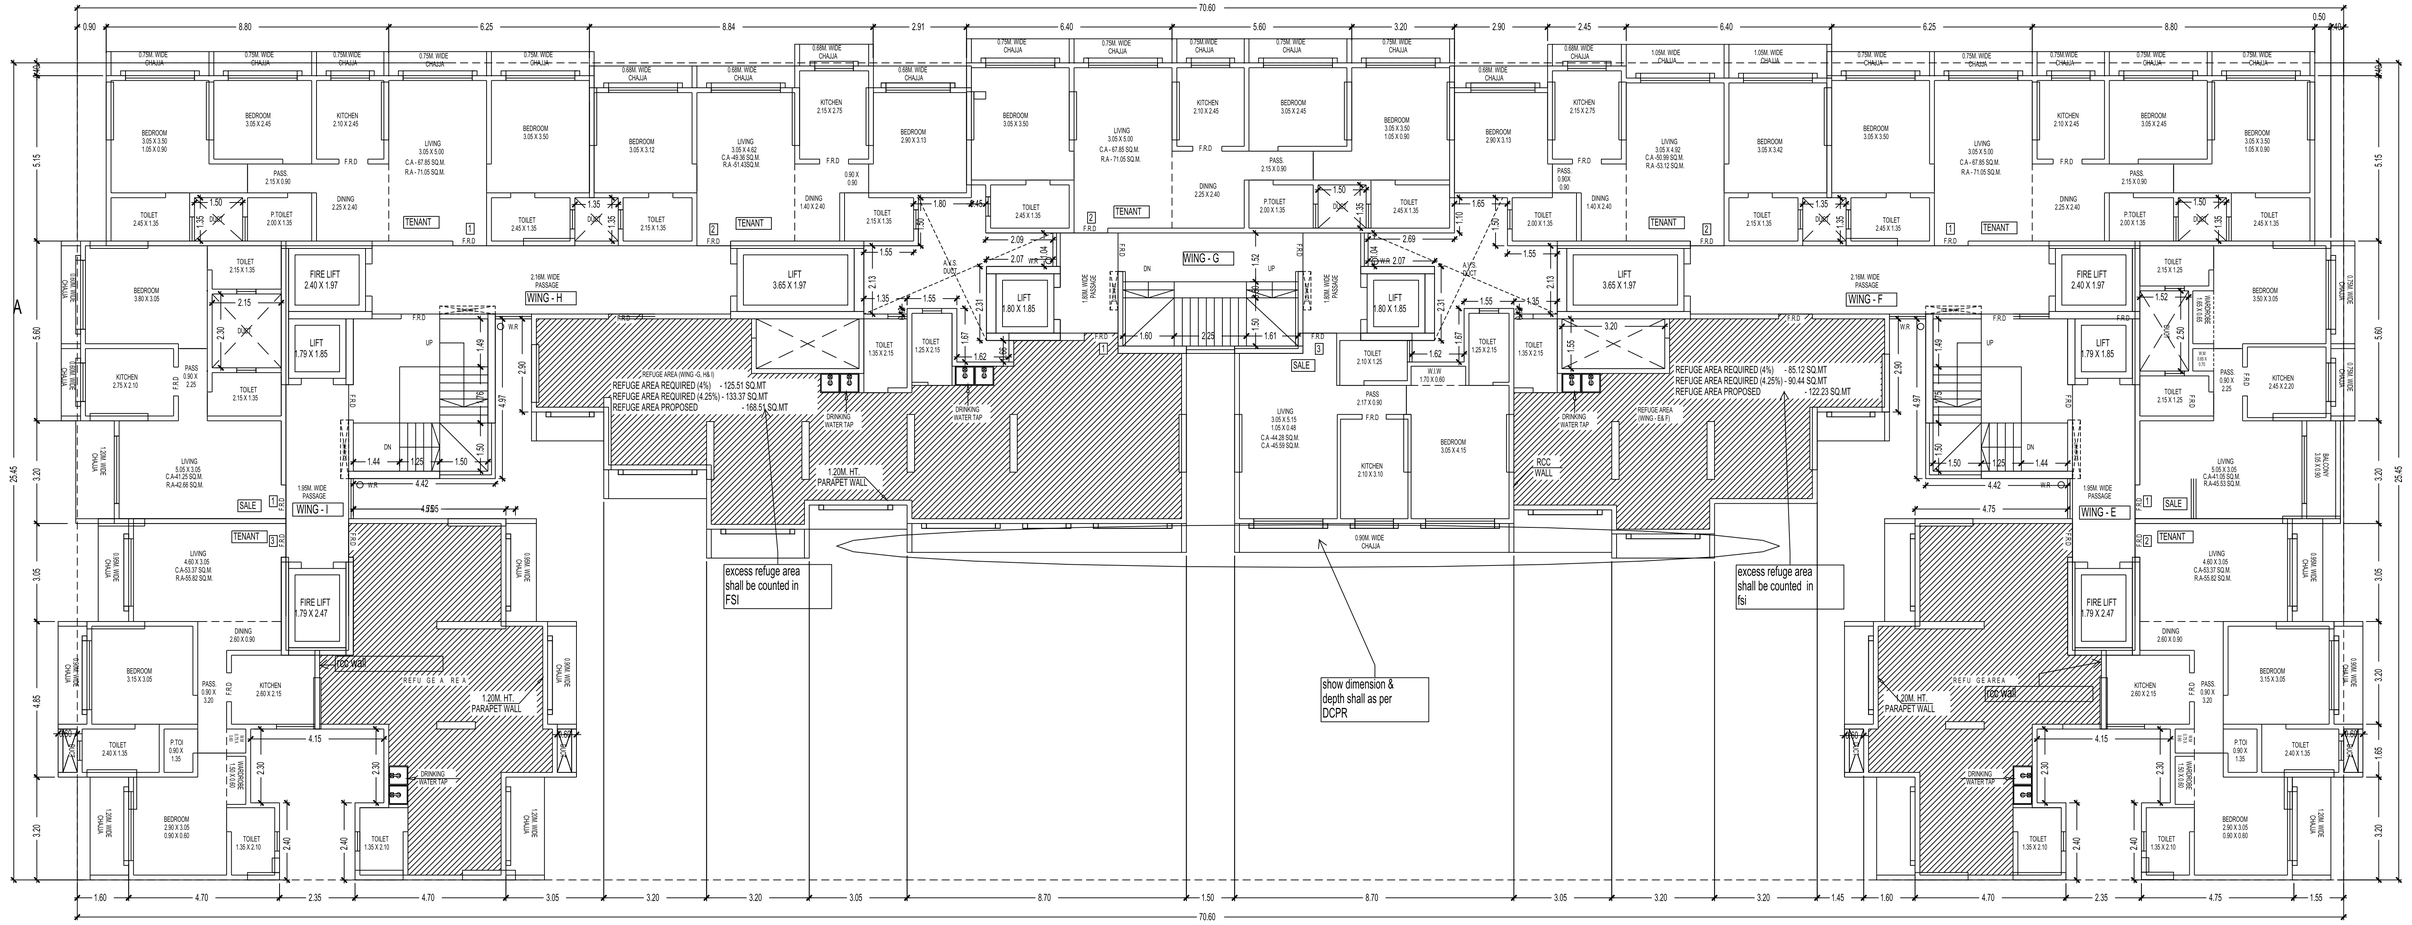

8TH FLOOR PLAN

(WING - E,F,G,H & I)

SCALE - 1:100

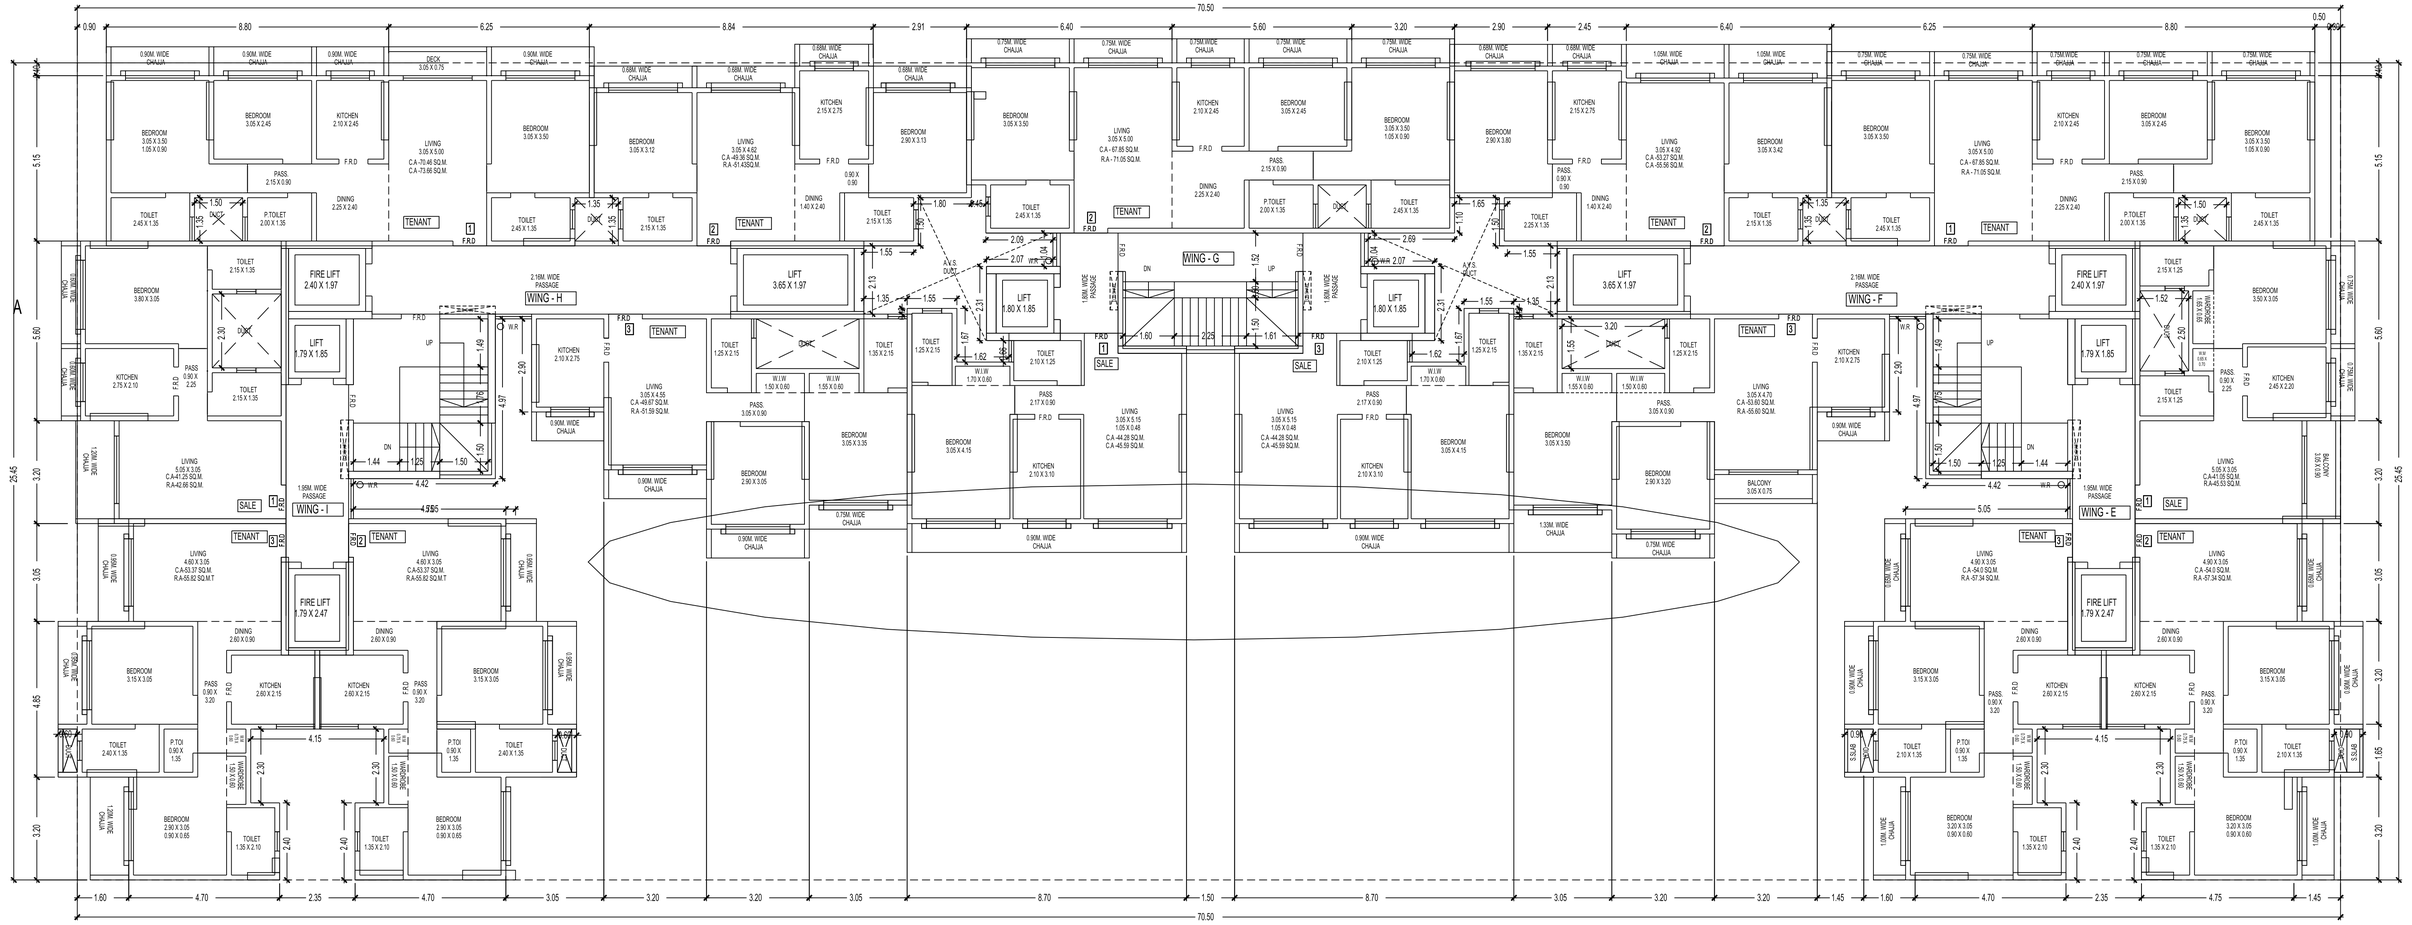

9TH FLOOR PLAN

(WING - E,F,G,H & I)

SCALE - 1:100

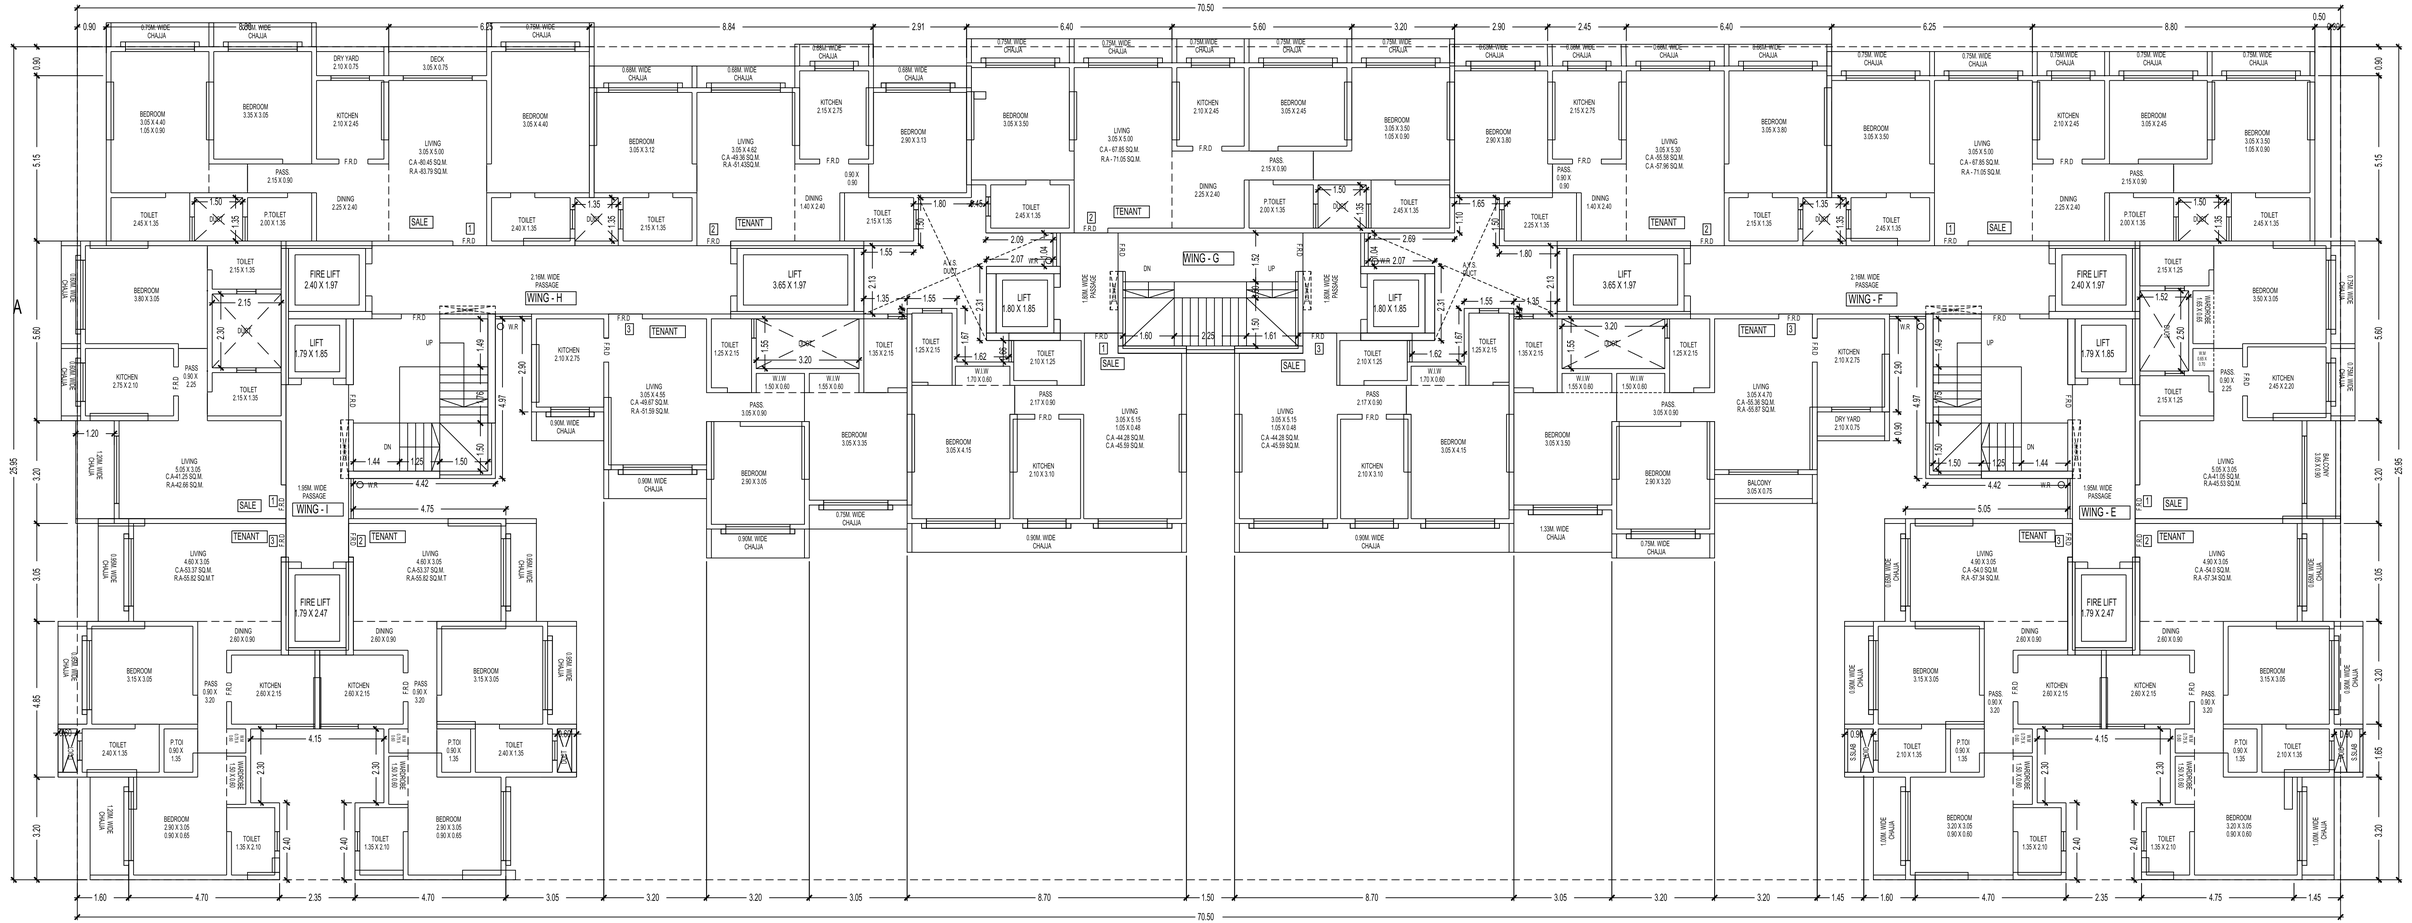

10TH FLOOR PLAN

(WING - E,F,G,H & I)

SCALE - 1:100

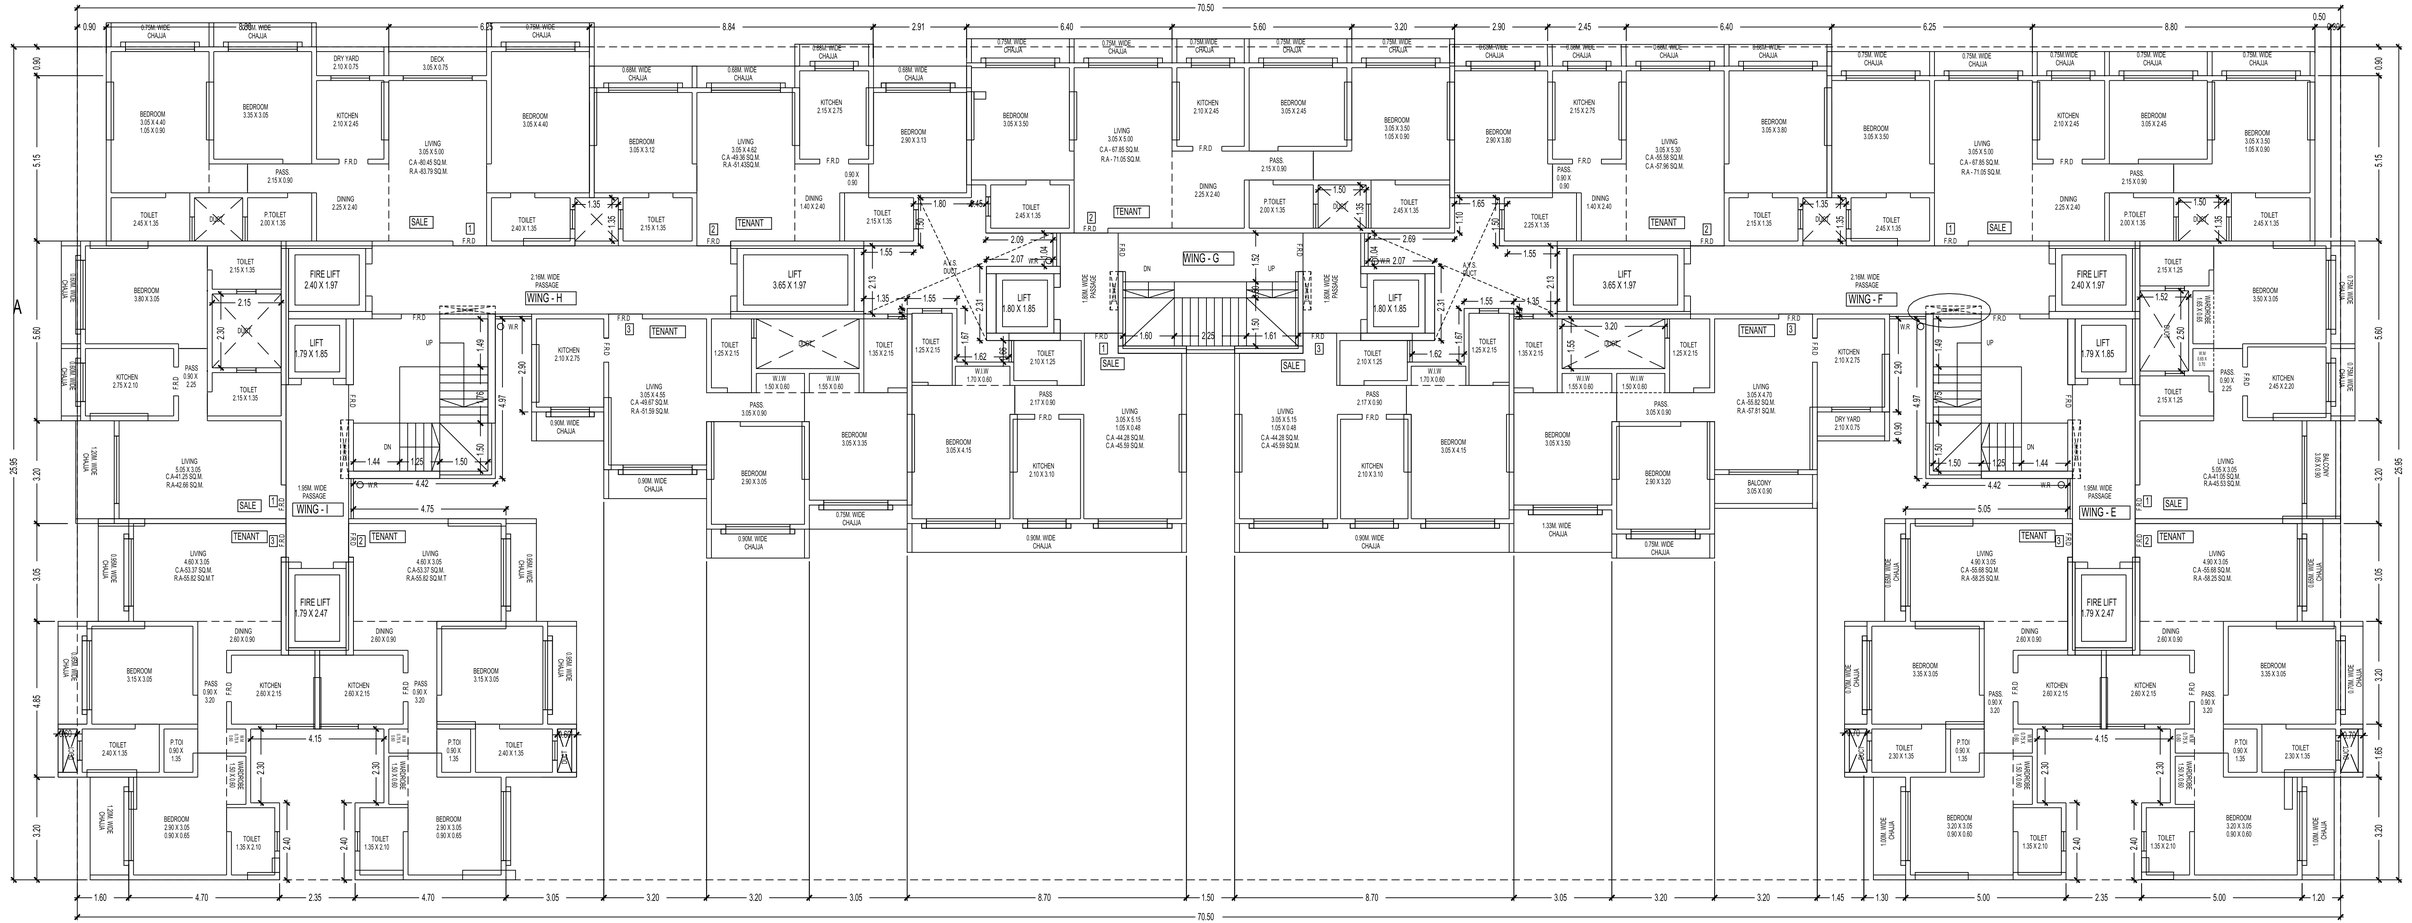

11TH FLOOR PLAN

(WING - E,F,G,H & I)

SCALE - 1:100

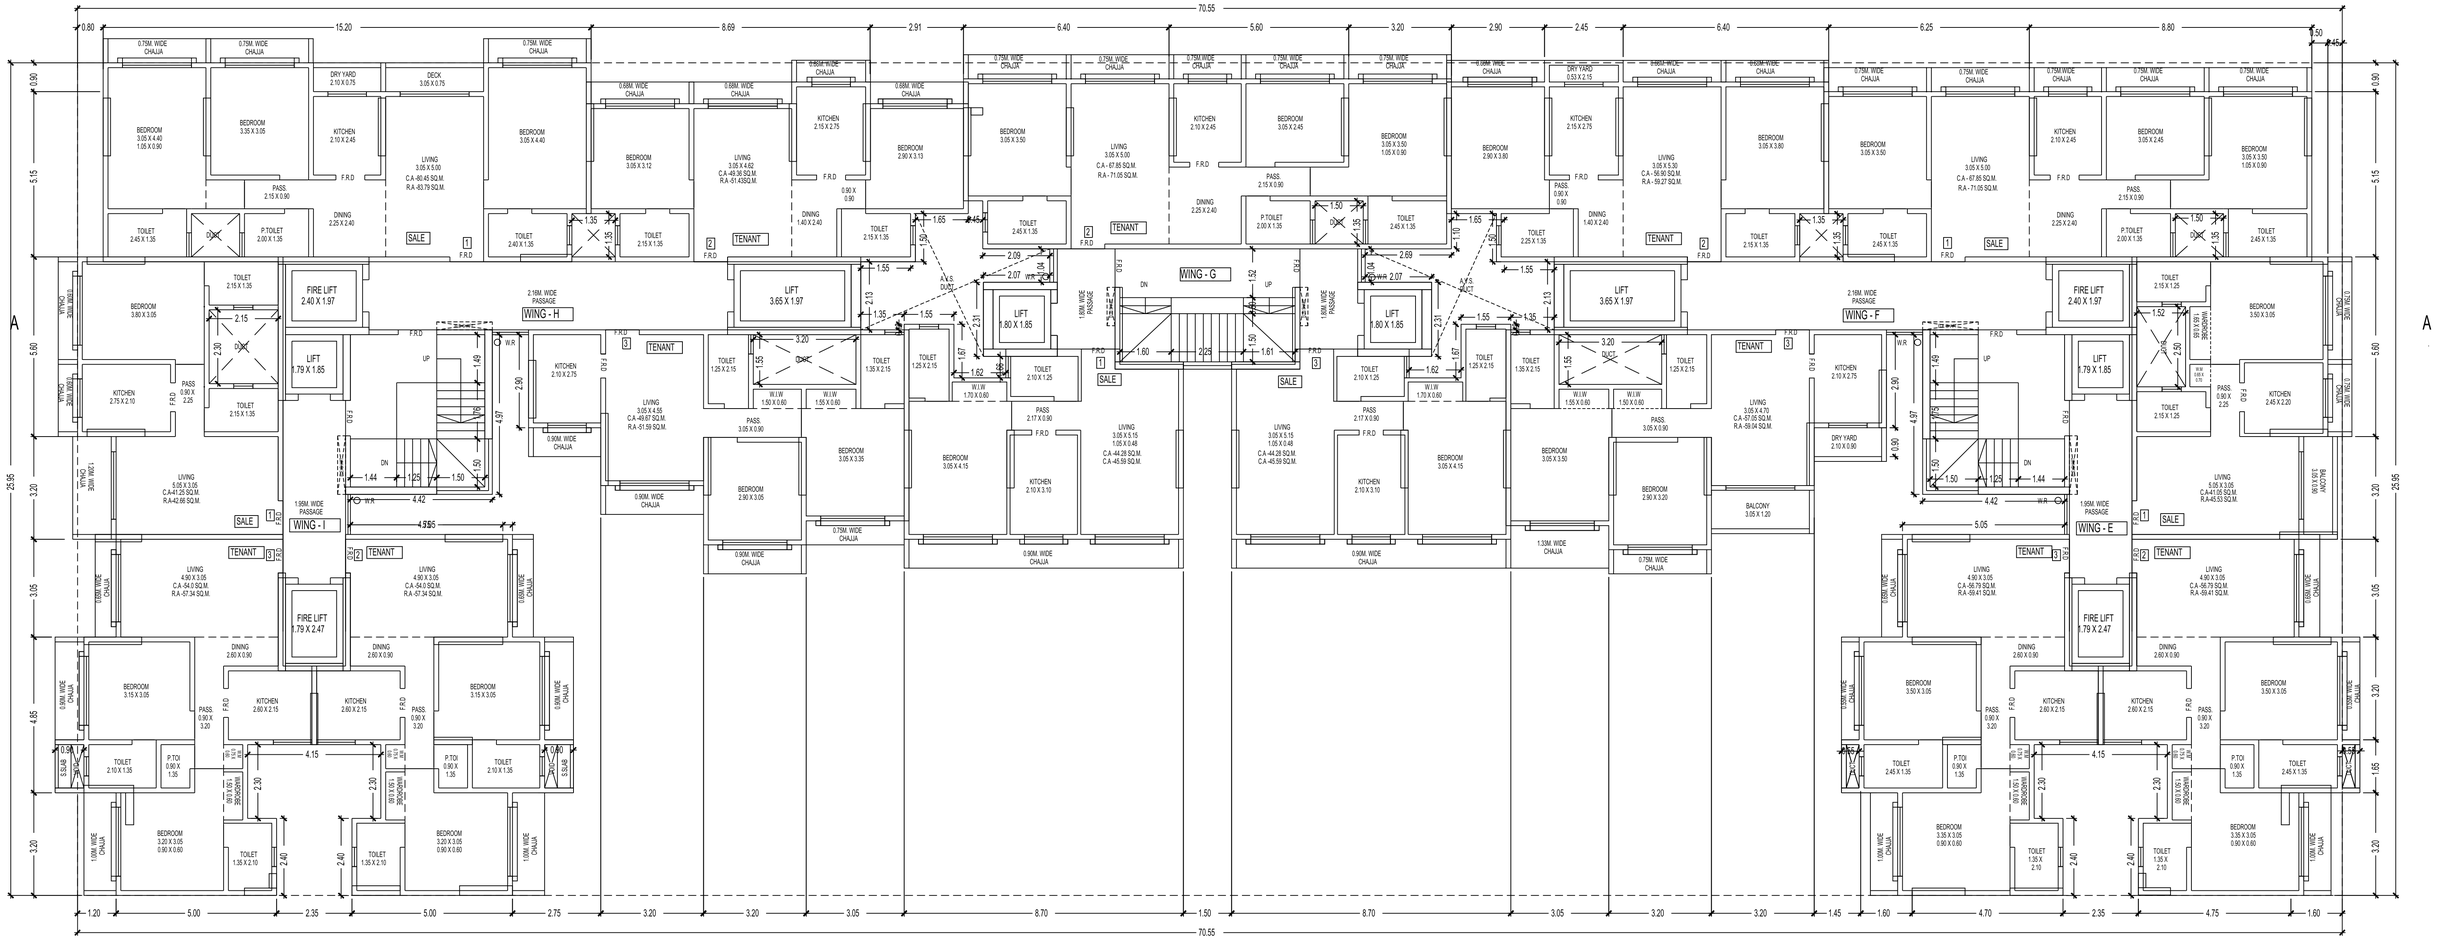

12TH FLOOR PLAN

(WING - E,F,G,H & I)

SCALE - 1:100

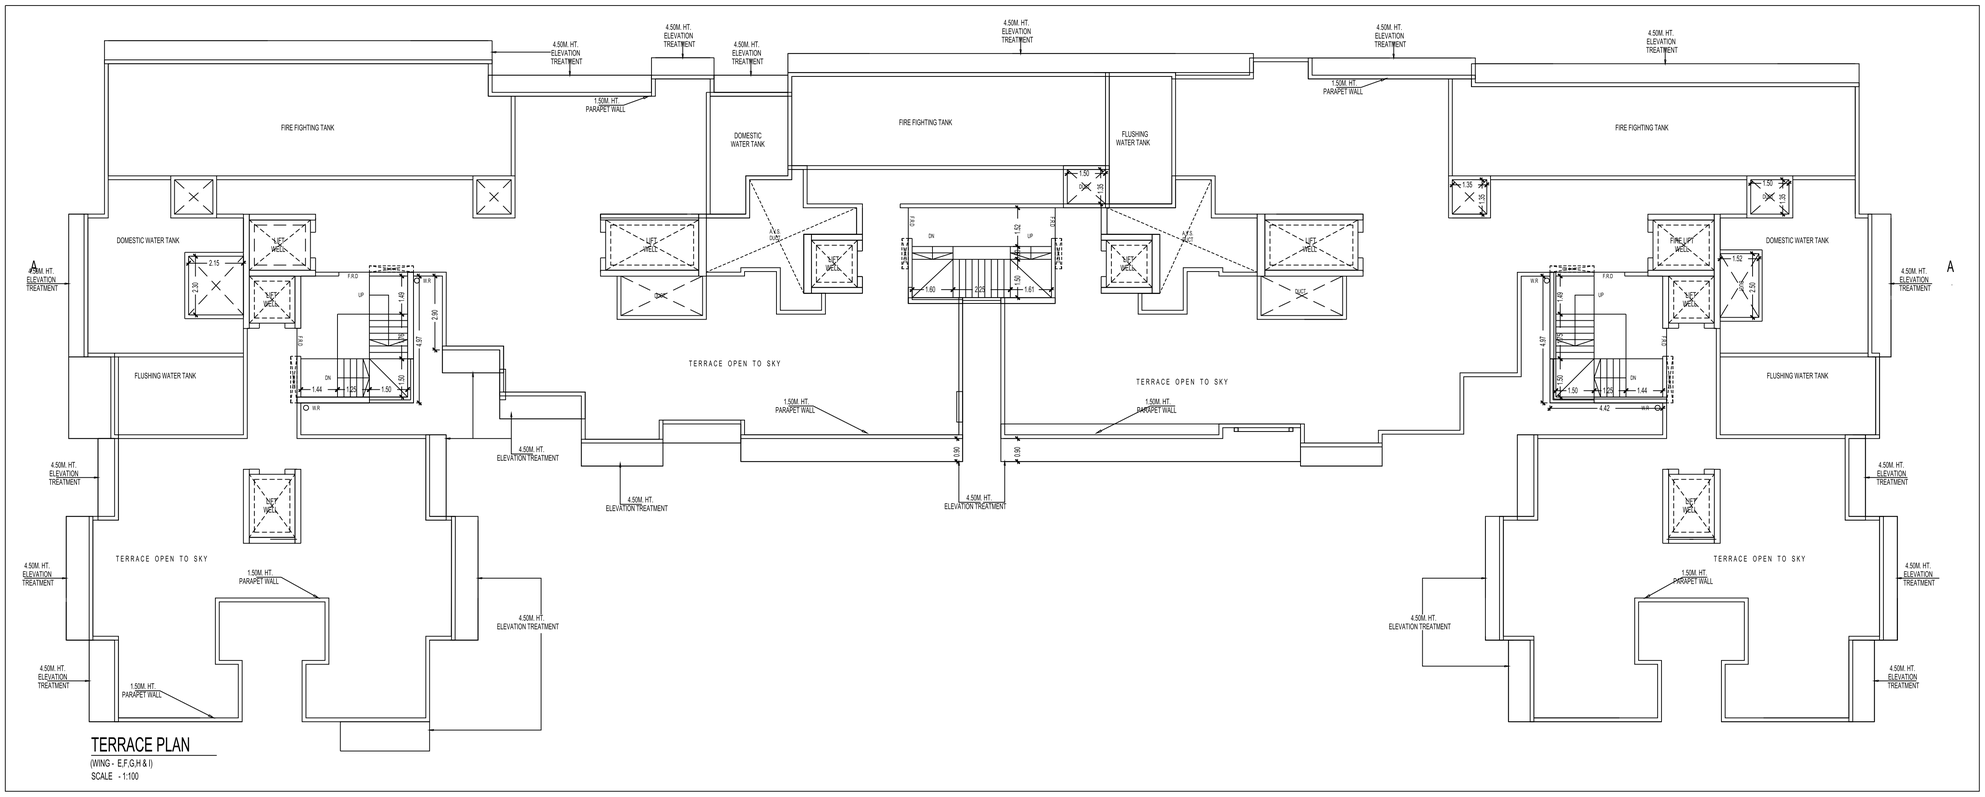

TERRACE PLAN

(WING - E,F,G,H & I)

SCALE - 1:100

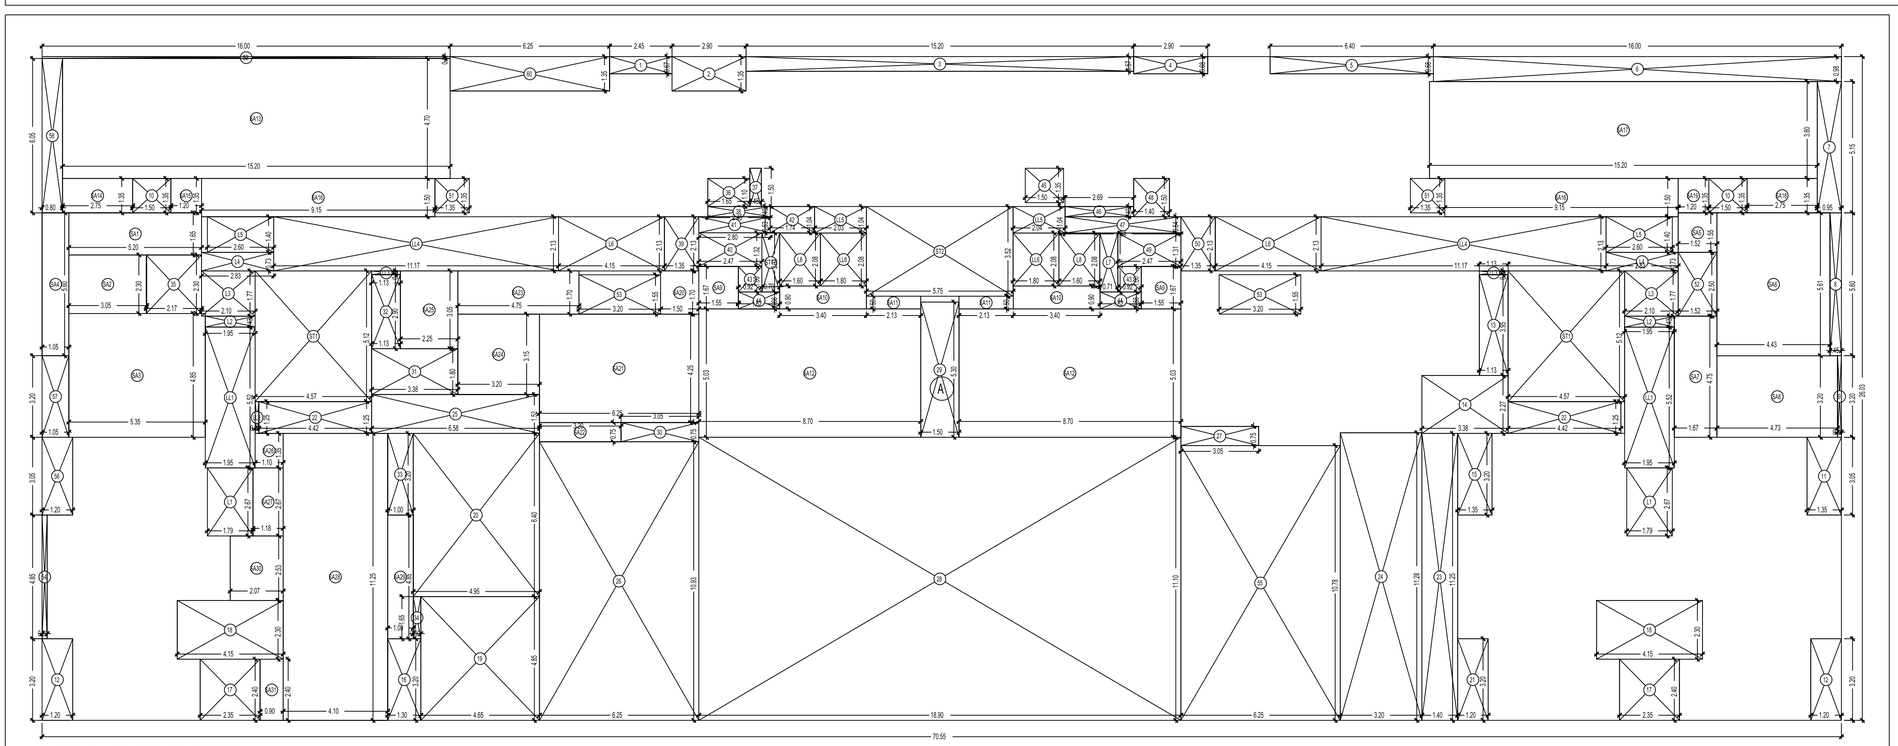

(WING - E,F,G,H & I)

SCALE - 1:100

BUILT UP AREA CALCULATION (WING - E,F,G,H & I)

13TH FLOOR									
A	70.55	X	26.03	X	1 NO	=	1836.42	SQ.MT.	
					TOTAL ADDITION	=	1836.42	SQ.MT.	X
DEDUCTIONS									
1	2.45	X	0.68	X	1 NO	=	1.67	SQ.MT.	
2	2.90	X	1.35	X	1 NO	=	3.92	SQ.MT.	
3	15.20	X	0.58	X	1 NO	=	8.82	SQ.MT.	
4	2.90	X	0.68	X	1 NO	=	1.97	SQ.MT.	
5	6.40	X	0.68	X	1 NO	=	4.35	SQ.MT.	
6	16.00	X	0.98	X	1 NO	=	15.68	SQ.MT.	
7	0.95	X	5.15	X	1 NO	=	4.89	SQ.MT.	
8	0.45	X	5.60	X	1 NO	=	2.52	SQ.MT.	
9	0.15	X	3.20	X	1 NO	=	0.48	SQ.MT.	
10	1.50	X	1.35	X	2 NOS	=	4.05	SQ.MT.	
11	1.35	X	3.05	X	1 NO	=	4.12	SQ.MT.	
12	1.20	X	3.20	X	2 NOS	=	7.68	SQ.MT.	
13	1.13	X	3.95	X	1 NO	=	4.46	SQ.MT.	
14	3.38	X	2.28	X	1 NO	=	7.71	SQ.MT.	
15	1.35	X	3.20	X	1 NO	=	4.32	SQ.MT.	
16	1.30	X	3.20	X	1 NO	=	4.16	SQ.MT.	
17	2.35	X	2.40	X	2 NOS	=	11.28	SQ.MT.	
18	4.15	X	2.30	X	2 NOS	=	19.09	SQ.MT.	
19	4.65	X	4.85	X	1 NO	=	22.55	SQ.MT.	
20	4.95	X	6.40	X	1 NO	=	31.68	SQ.MT.	
21	1.20	X	3.20	X	1 NO	=	3.84	SQ.MT.	
22	4.42	X	1.25	X	2 NOS	=	11.05	SQ.MT.	
23	1.40	X	11.25	X	1 NO	=	15.75	SQ.MT.	
24	3.20	X	11.28	X	1 NO	=	36.10	SQ.MT.	
25	6.58	X	1.53	X	1 NO	=	10.07	SQ.MT.	
26	6.25	X	10.93	X	1 NO	=	68.31	SQ.MT.	
27	3.05	X	0.75	X	1 NO	=	2.29	SQ.MT.	
28	18.90	X	11.10	X	1 NO	=	209.79	SQ.MT.	
29	1.50	X	5.30	X	1 NO	=	7.95	SQ.MT.	
30	3.05	X	0.75	X	1 NO	=	2.29	SQ.MT.	
31	3.38	X	1.80	X	1 NO	=	6.08	SQ.MT.	
32	1.13	X	2.90	X	1 NO	=	3.28	SQ.MT.	
33	1.00	X	3.20	X	1 NO	=	3.20	SQ.MT.	
34	0.30	X	1.65	X	1 NO	=	0.50	SQ.MT.	
35	2.17	X	2.30	X	1 NO	=	4.99	SQ.MT.	
36	1.65	X	1.10	X	1 NO	=	1.82	SQ.MT.	
37	0.45	X	1.50	X	1 NO	=	0.68	SQ.MT.	
38	2.45	X	0.40	X	1 NO	=	0.98	SQ.MT.	
39	1.35	X	2.13	X	1 NO	=	2.88	SQ.MT.	
40	2.47	X	1.32	X	1 NO	=	3.26	SQ.MT.	
41	2.80	X	0.63	X	1 NO	=	1.76	SQ.MT.	
42	1.74	X	1.04	X	1 NO	=	1.81	SQ.MT.	
43	0.92	X	1.01	X	2 NOS	=	1.86	SQ.MT.	
44	1.62	X	0.66	X	2 NOS	=	2.14	SQ.MT.	
45	1.50	X	1.35	X	1 NO	=	2.03	SQ.MT.	
46	2.69	X	0.40	X	1 NO	=	1.08	SQ.MT.	
47	4.54	X	0.64	X	1 NO	=	2.91	SQ.MT.	
48	1.40	X	1.50	X	1 NO	=	2.10	SQ.MT.	
49	2.47	X	1.31	X	1 NO	=	3.24	SQ.MT.	
50	1.35	X	2.13	X	1 NO	=	2.88	SQ.MT.	
51	1.35	X	1.35	X	2 NOS	=	3.65	SQ.MT.	
52	1.52	X	2.50	X	1 NO	=	3.80	SQ.MT.	
53	3.20	X	1.55	X	2 NOS	=	9.92	SQ.MT.	
54	0.20	X	4.85	X	1 NO	=	0.97	SQ.MT.	
55	6.25	X	10.78	X	1 NO	=	67.38	SQ.MT.	
56	1.20	X	3.05	X	1 NO	=	3.66	SQ.MT.	
57	1.05	X	3.20	X	1 NO	=	3.36	SQ.MT.	
58	0.80	X	6.05	X	1 NO	=	4.84	SQ.MT.	
59	16.00	X	0.08	X	1 NO	=	1.28	SQ.MT.	
60	6.25	X	1.35	X	1 NO	=	8.44	SQ.MT.	
					TOTAL DEDUCTION	=	689.62	SQ.MT.	Y1
TOTAL BUILT UP AREA [X - Y1]						=	1146.80	SQ.MT.	X1

STAIRCASE AREA CALCULATION

13TH FLOOR									
L1	1.79	X	2.67	X	2 NOS	=	9.56	SQ.MT.	
L2	1.95	X	0.43	X	1 NO	=	0.84	SQ.MT.	
L2	1.95	X	0.43	X	1 NO	=	0.84	SQ.MT.	
L3	2.10	X	1.78	X	2 NOS	=	7.48	SQ.MT.	
L4	2.83	X	0.73	X	2 NOS	=	4.13	SQ.MT.	
L5	2.60	X	1.40	X	2 NOS	=	7.28	SQ.MT.	
L6	4.15	X	2.13	X	2 NOS	=	17.68	SQ.MT.	
L7	0.71	X	2.31	X	1 NO	=	1.64	SQ.MT.	
L8	1.60	X	2.08	X	2 NOS	=	6.66	SQ.MT.	
LL1	1.95	X	5.52	X	2 NOS	=	21.53	SQ.MT.	
LL2	0.15	X	1.25	X	1 NO	=	0.19	SQ.MT.	
LL3	1.13	X	0.15	X	2 NOS	=	0.34	SQ.MT.	
LL4	11.17	X	2.13	X	2 NOS	=	47.58	SQ.MT.	
LL5	2.04	X	1.04	X	1 NO	=	2.12	SQ.MT.	
LL5	2.03	X	1.04	X	1 NO	=	2.11	SQ.MT.	
LL6	1.80	X	2.08	X	2 NOS	=	7.49	SQ.MT.	
ST1	4.57	X	5.13	X	2 NOS	=	46.69	SQ.MT.	
ST2	5.75	X	3.52	X	1 NO	=	20.24	SQ.MT.	
ST12	0.70	X	2.31	X	1 NO	=	1.62	SQ.MT.	
TOTAL STAIRCASE AREA PER FL. (13TH FLOOR)						=	206.22	SQ.MT.	Y2

NET BUILT UP AREA [X1 - Y2]	=	940.58	SQ.MT.

Plan for Consideration

Shrikant Chintaman Godase
S.E.(BP) K/E-N

SHAIKH ASIF MUSA
A.E./(BP) K/East

Digitally signed by SHAIKH ASIF MUSA
DN: c=IN, o=BRIHANMUMBAI MUNICIPAL CORPORATION, ou=BUILDING PROPOSAL, 2.5.4.20=e0c535fda2bf5ae44a2a24259e fc4a5e66f7f07efce4eed52875b877d4, 2.5.4.45=3e4f9e2f1f1f1