

SCALE - 1:100

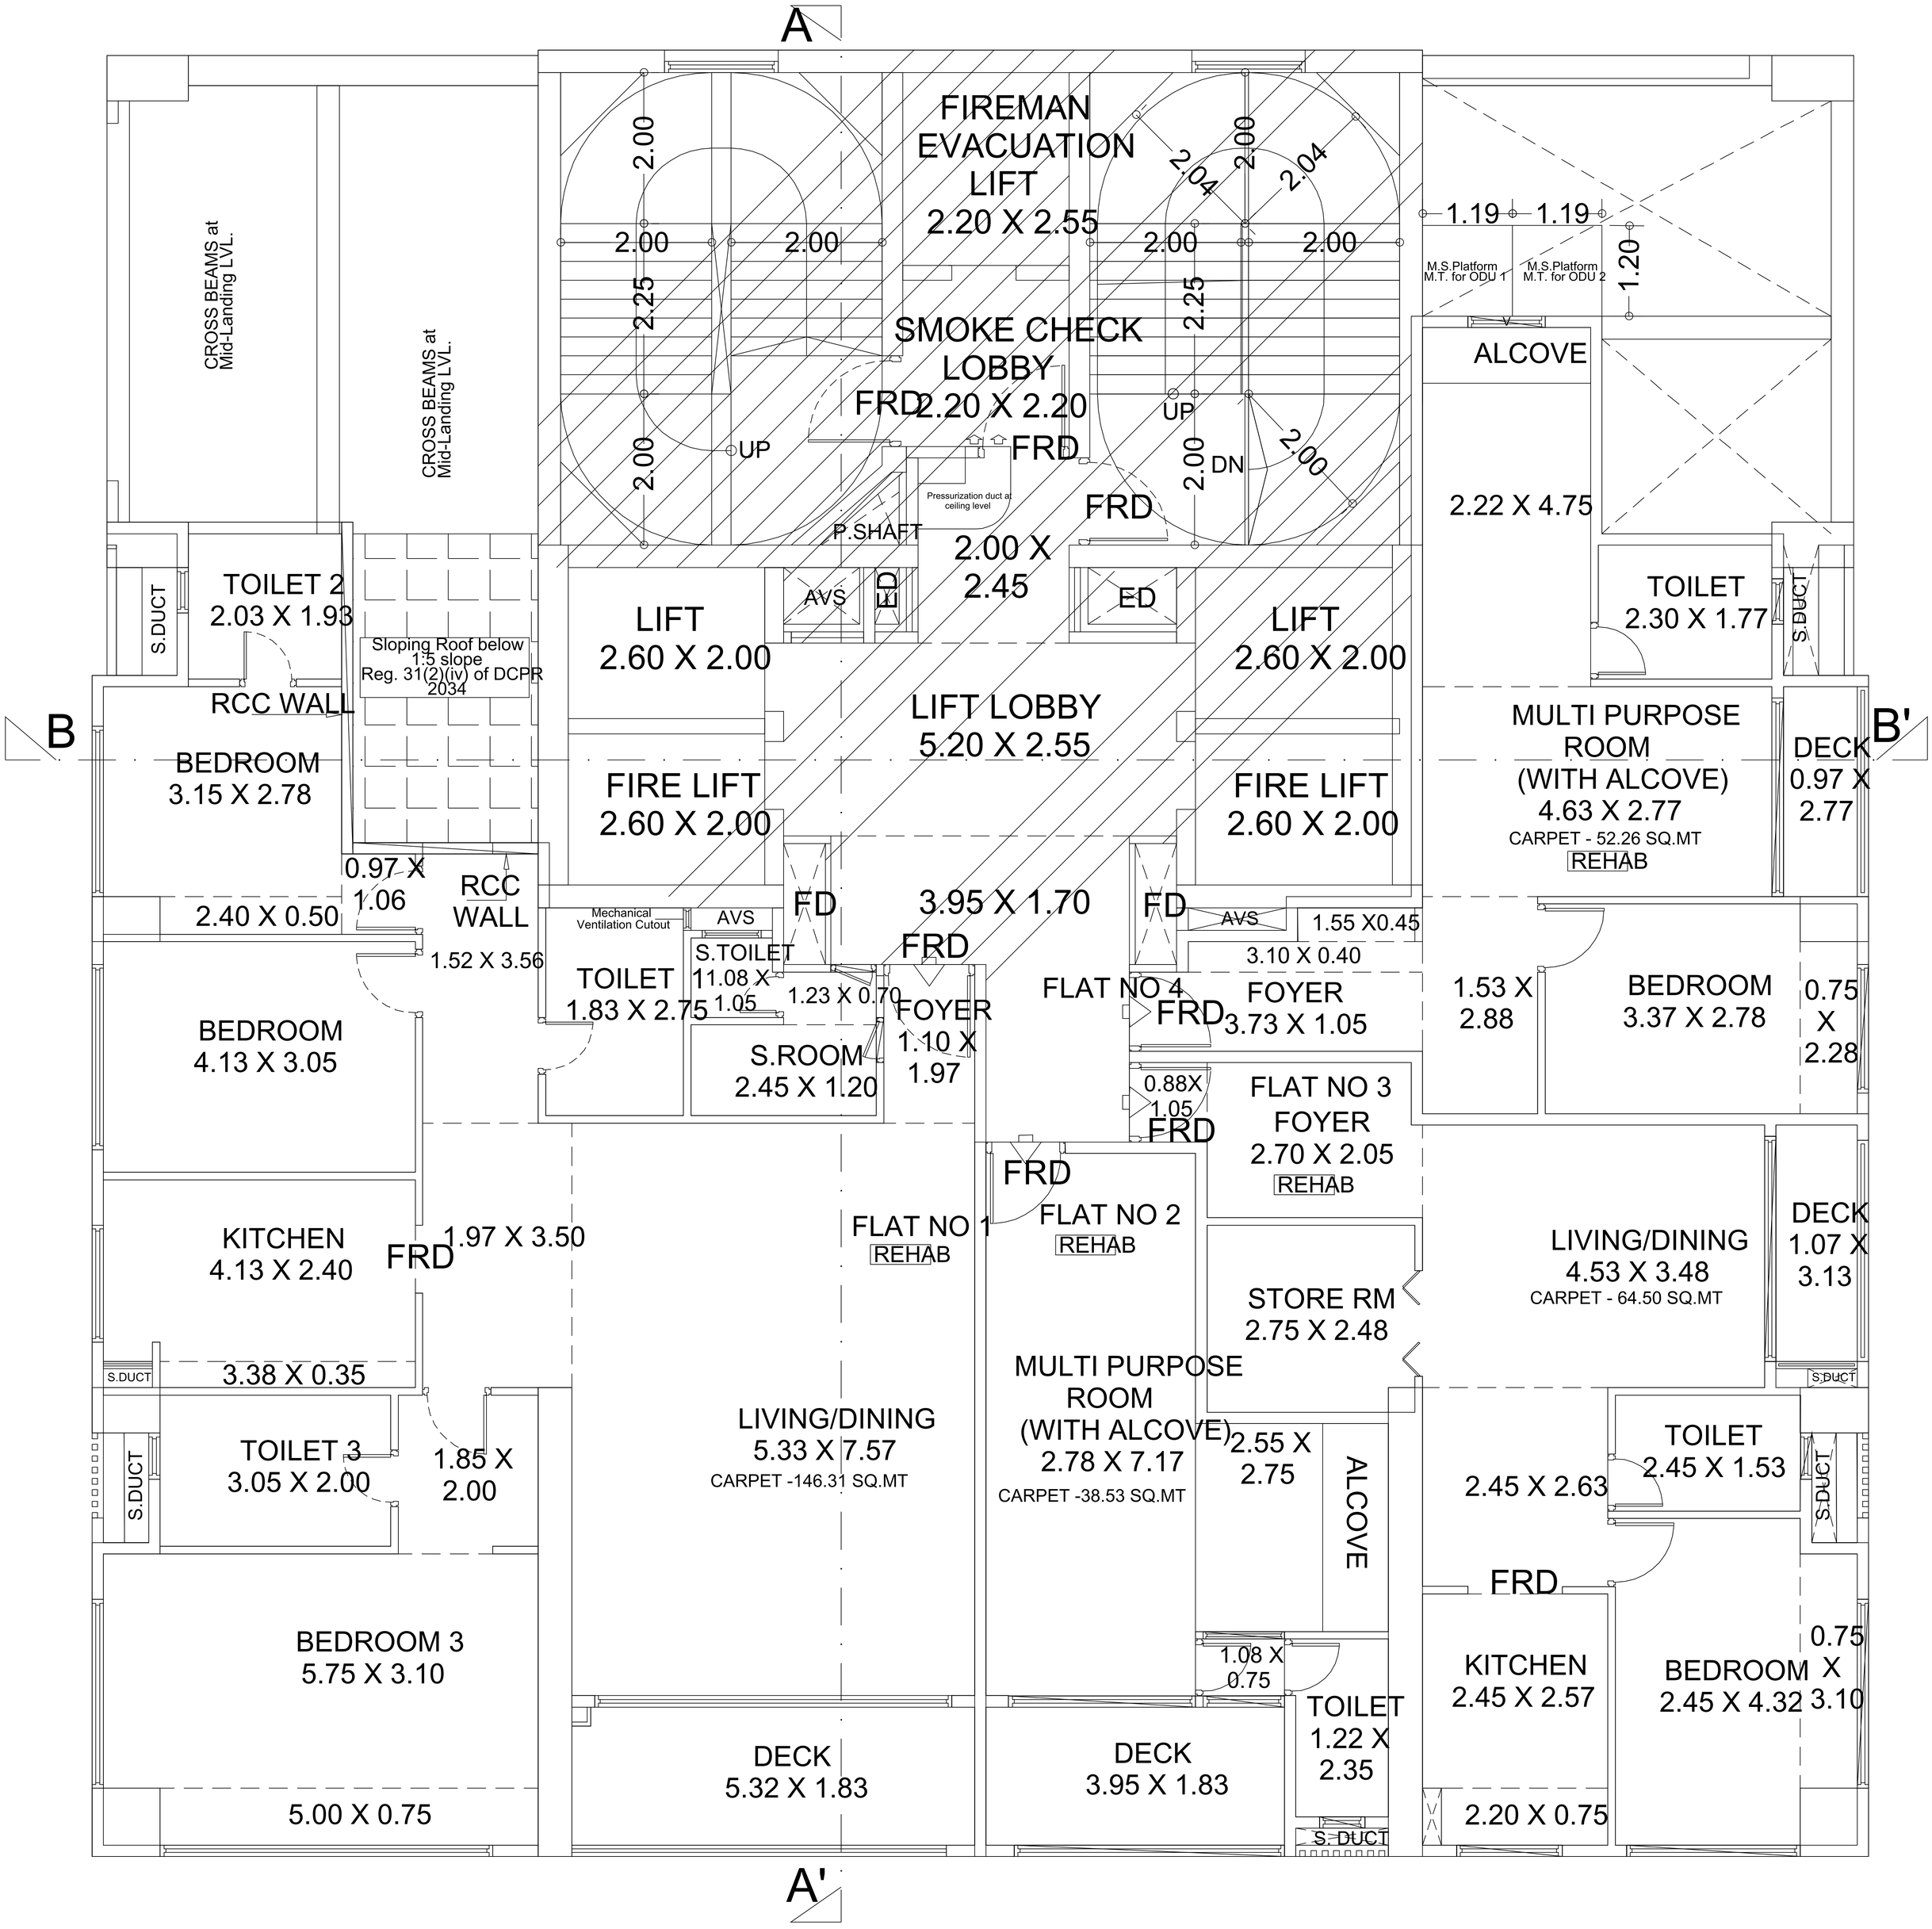

12TH FLOOR PLAN

SCALE - 1:100

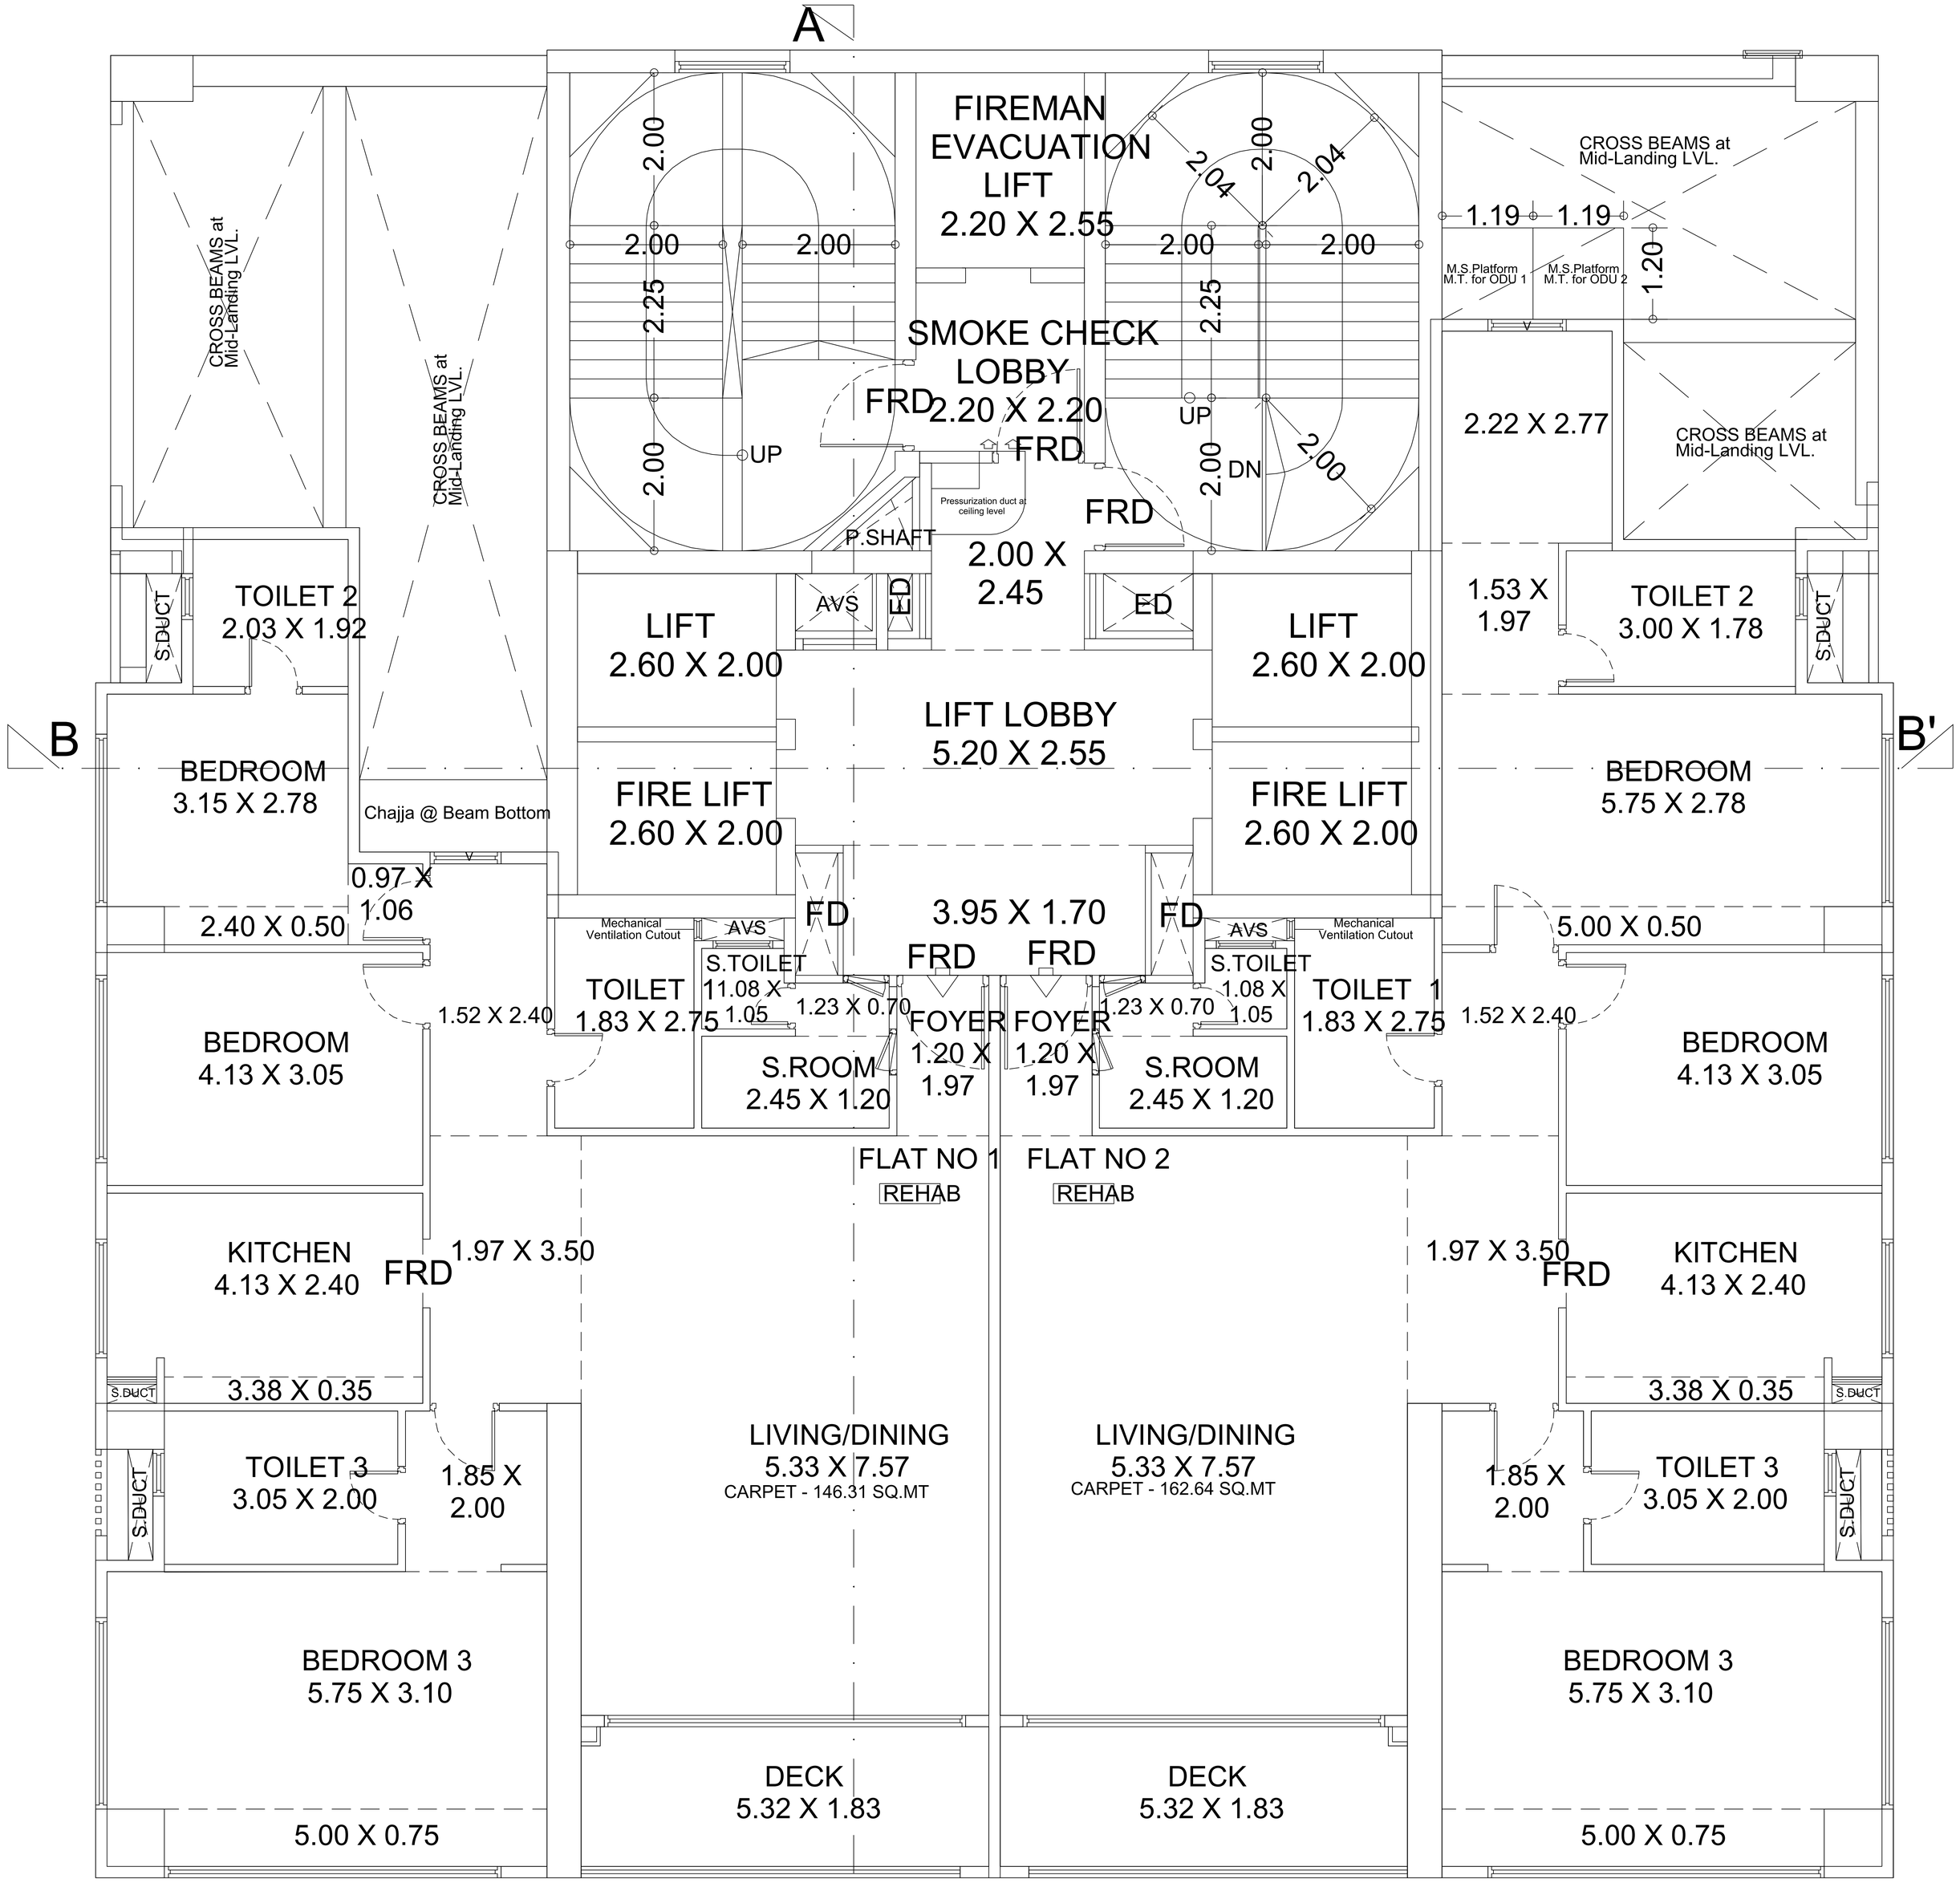

13TH FLOOR PLAN

SCALE - 1:100

A

A'

B

B'

FIREMAN EVACUATION LIFT 2.20 X 2.55

SMOKE CHECK LOBBY 2.20 X 2.20

FRD

UP

DN

2.00

2.25

2.04

Pressurization duct at ceiling level

P.SHAFT

2.00 X 2.45

AVS

ED

LIFT 2.60 X 2.00

LIFT LOBBY 5.20 X 2.55

FIRE LIFT 2.60 X 2.00

FD

3.95 X 1.70

CROSS BEAMS at Mid-Landing LVL.

1.19

1.20

M.S. Platform M.T. for ODU 1

M.S. Platform M.T. for ODU 2

2.22 X 2.77

1.53 X 1.97

TOILET 2 3.00 X 1.78

S.DUCT

BEDROOM 3.15 X 2.78

Chajja @ Beam Bottom

0.97 X 1.06

2.40 X 0.50

5.75 X 2.78

5.00 X 0.50

Mechanical Ventilation Cutout

S.TOILET 1.08 X 1.05

TOILET 1.83 X 2.75

1.23 X 0.70

FOYER 1.20 X 1.97

S.ROOM 2.45 X 1.20

TOILET 1 1.83 X 2.75

1.52 X 2.40

BEDROOM 4.13 X 3.05

FLAT NO 1 REHAB

FLAT NO 2 REHAB

KITCHEN 4.13 X 2.40

1.97 X 3.50

3.38 X 0.35

TOILET 3 3.05 X 2.00

1.85 X 2.00


LIVING/DINING 5.33 X 7.57 CARPET - 146.31 SQ.MT

LIVING/DINING 5.33 X 7.57 CARPET - 162.64 SQ.MT

BEDROOM 3 5.75 X 3.10

DECK 5.32 X 1.83


5.00 X 0.75

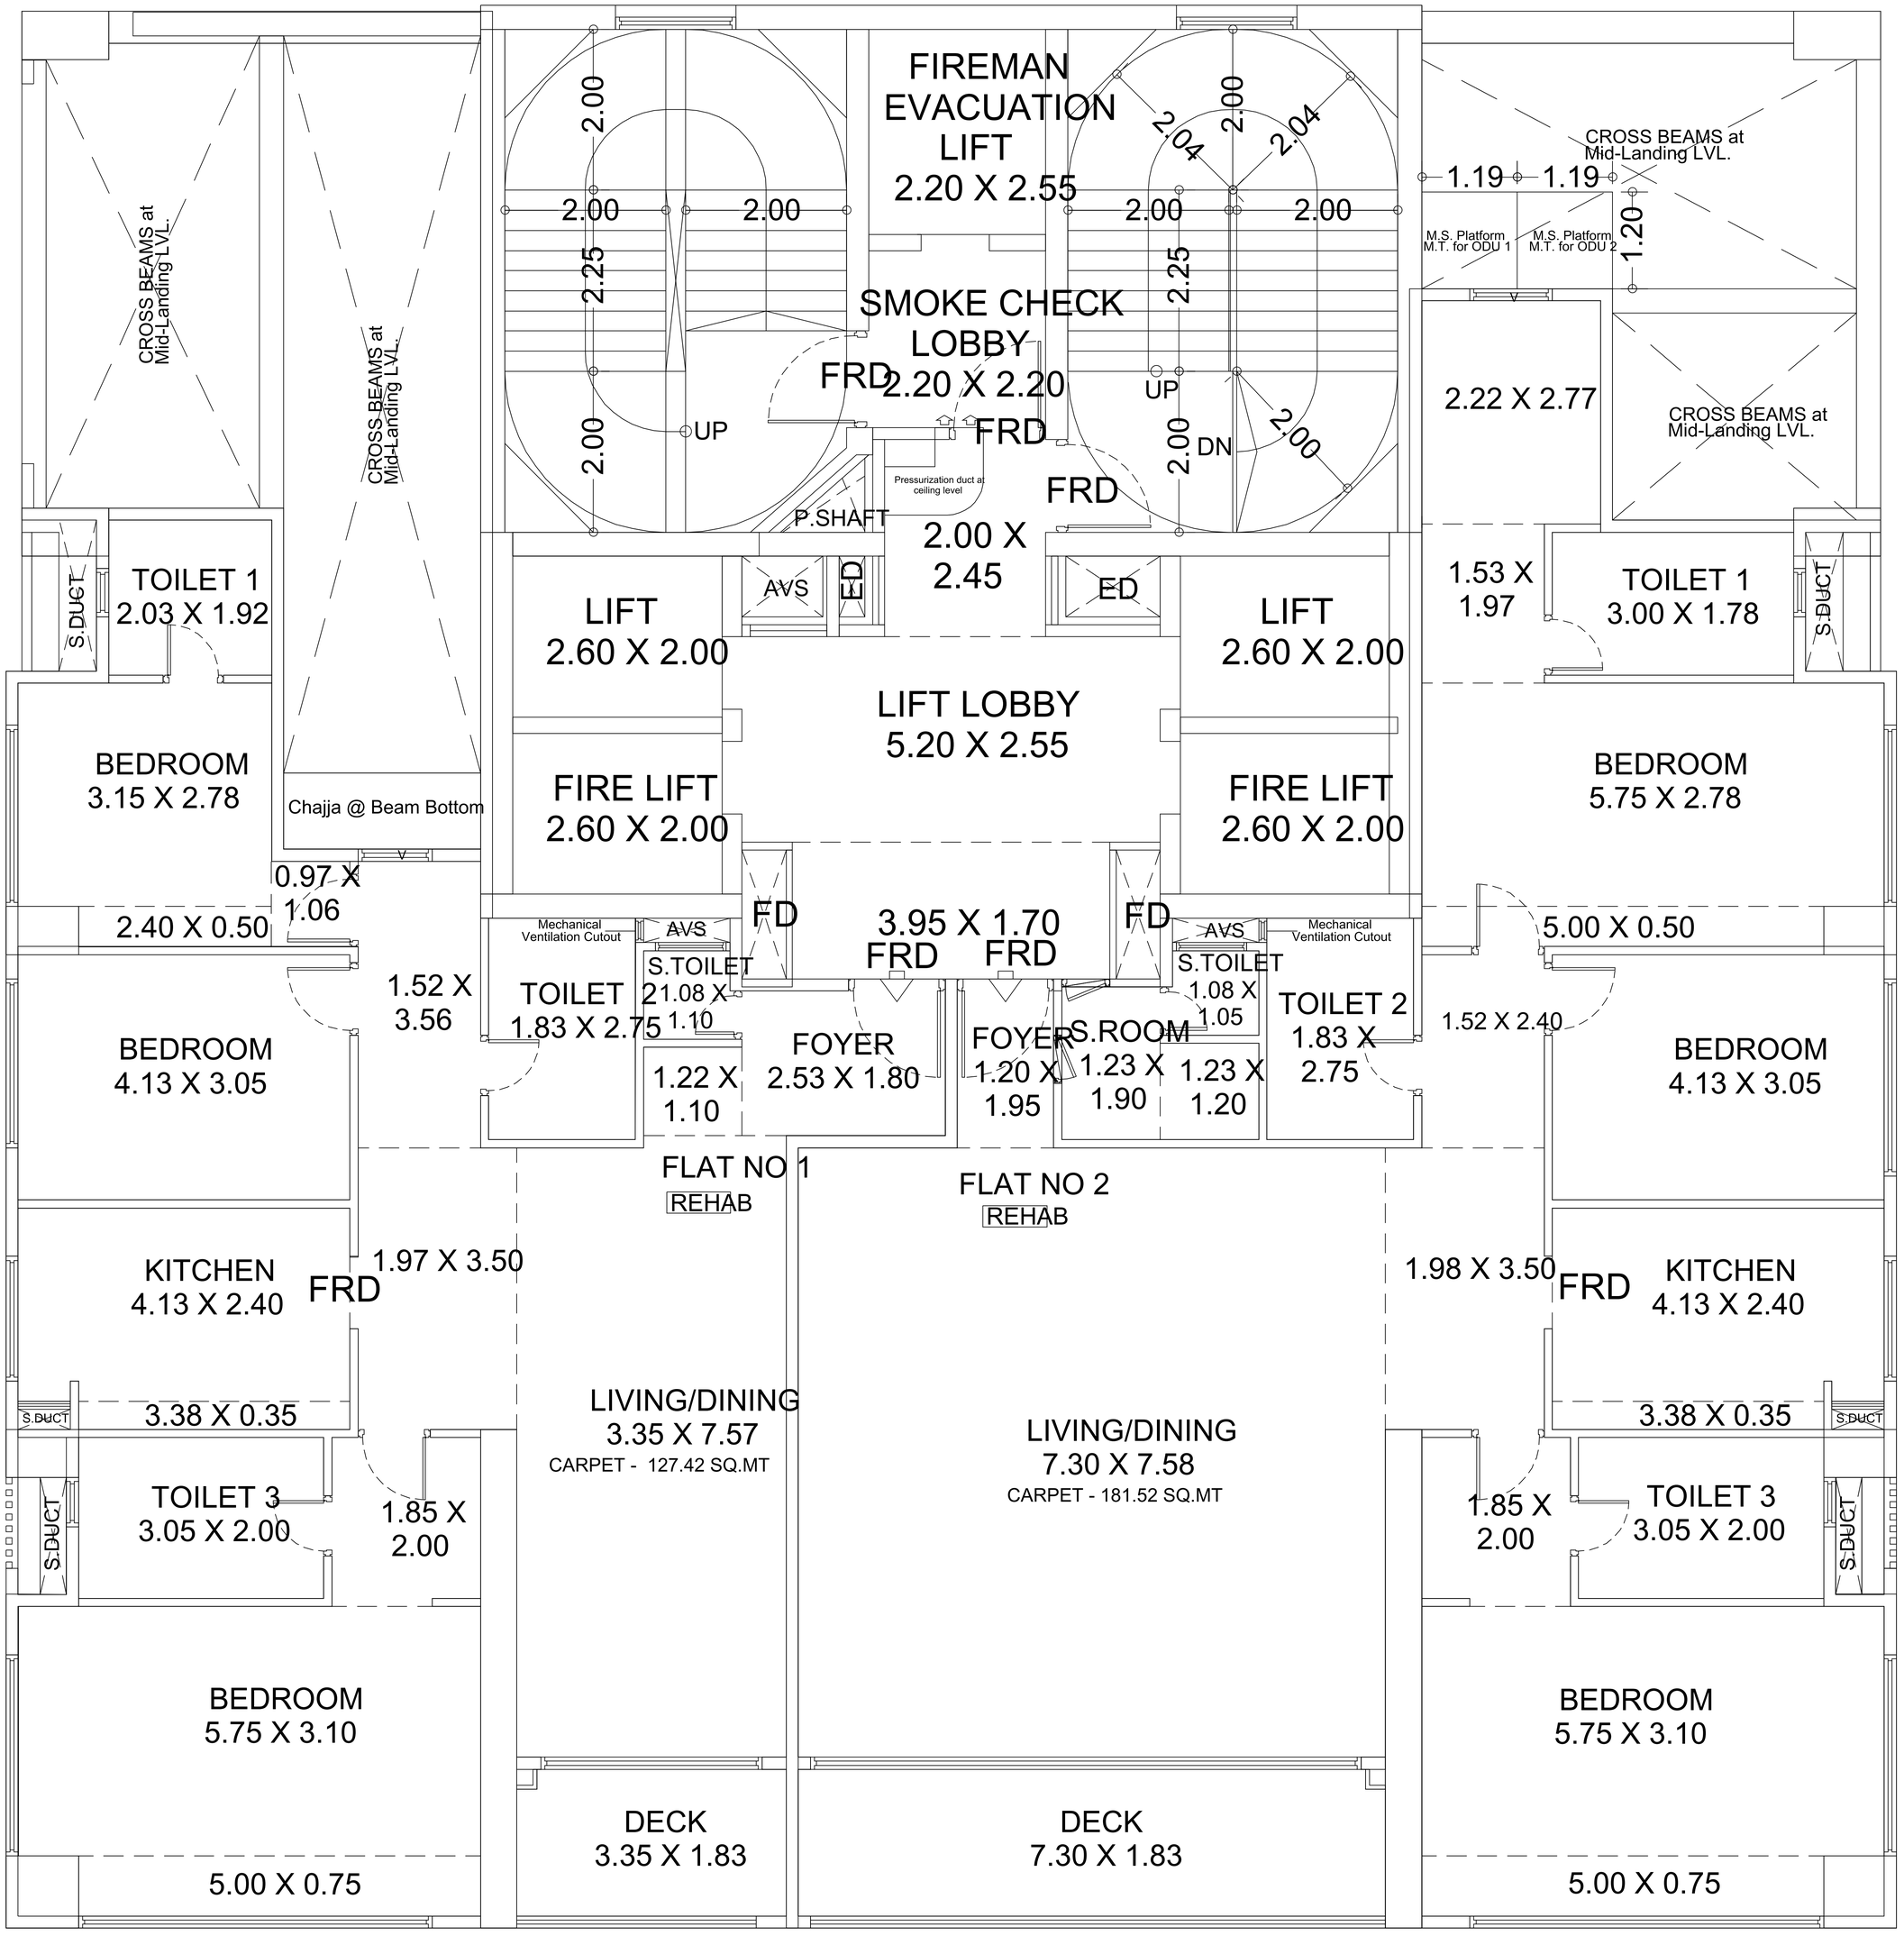

15TH FLOOR PLAN


14TH FLOOR PLAN

SCALE - 1:100

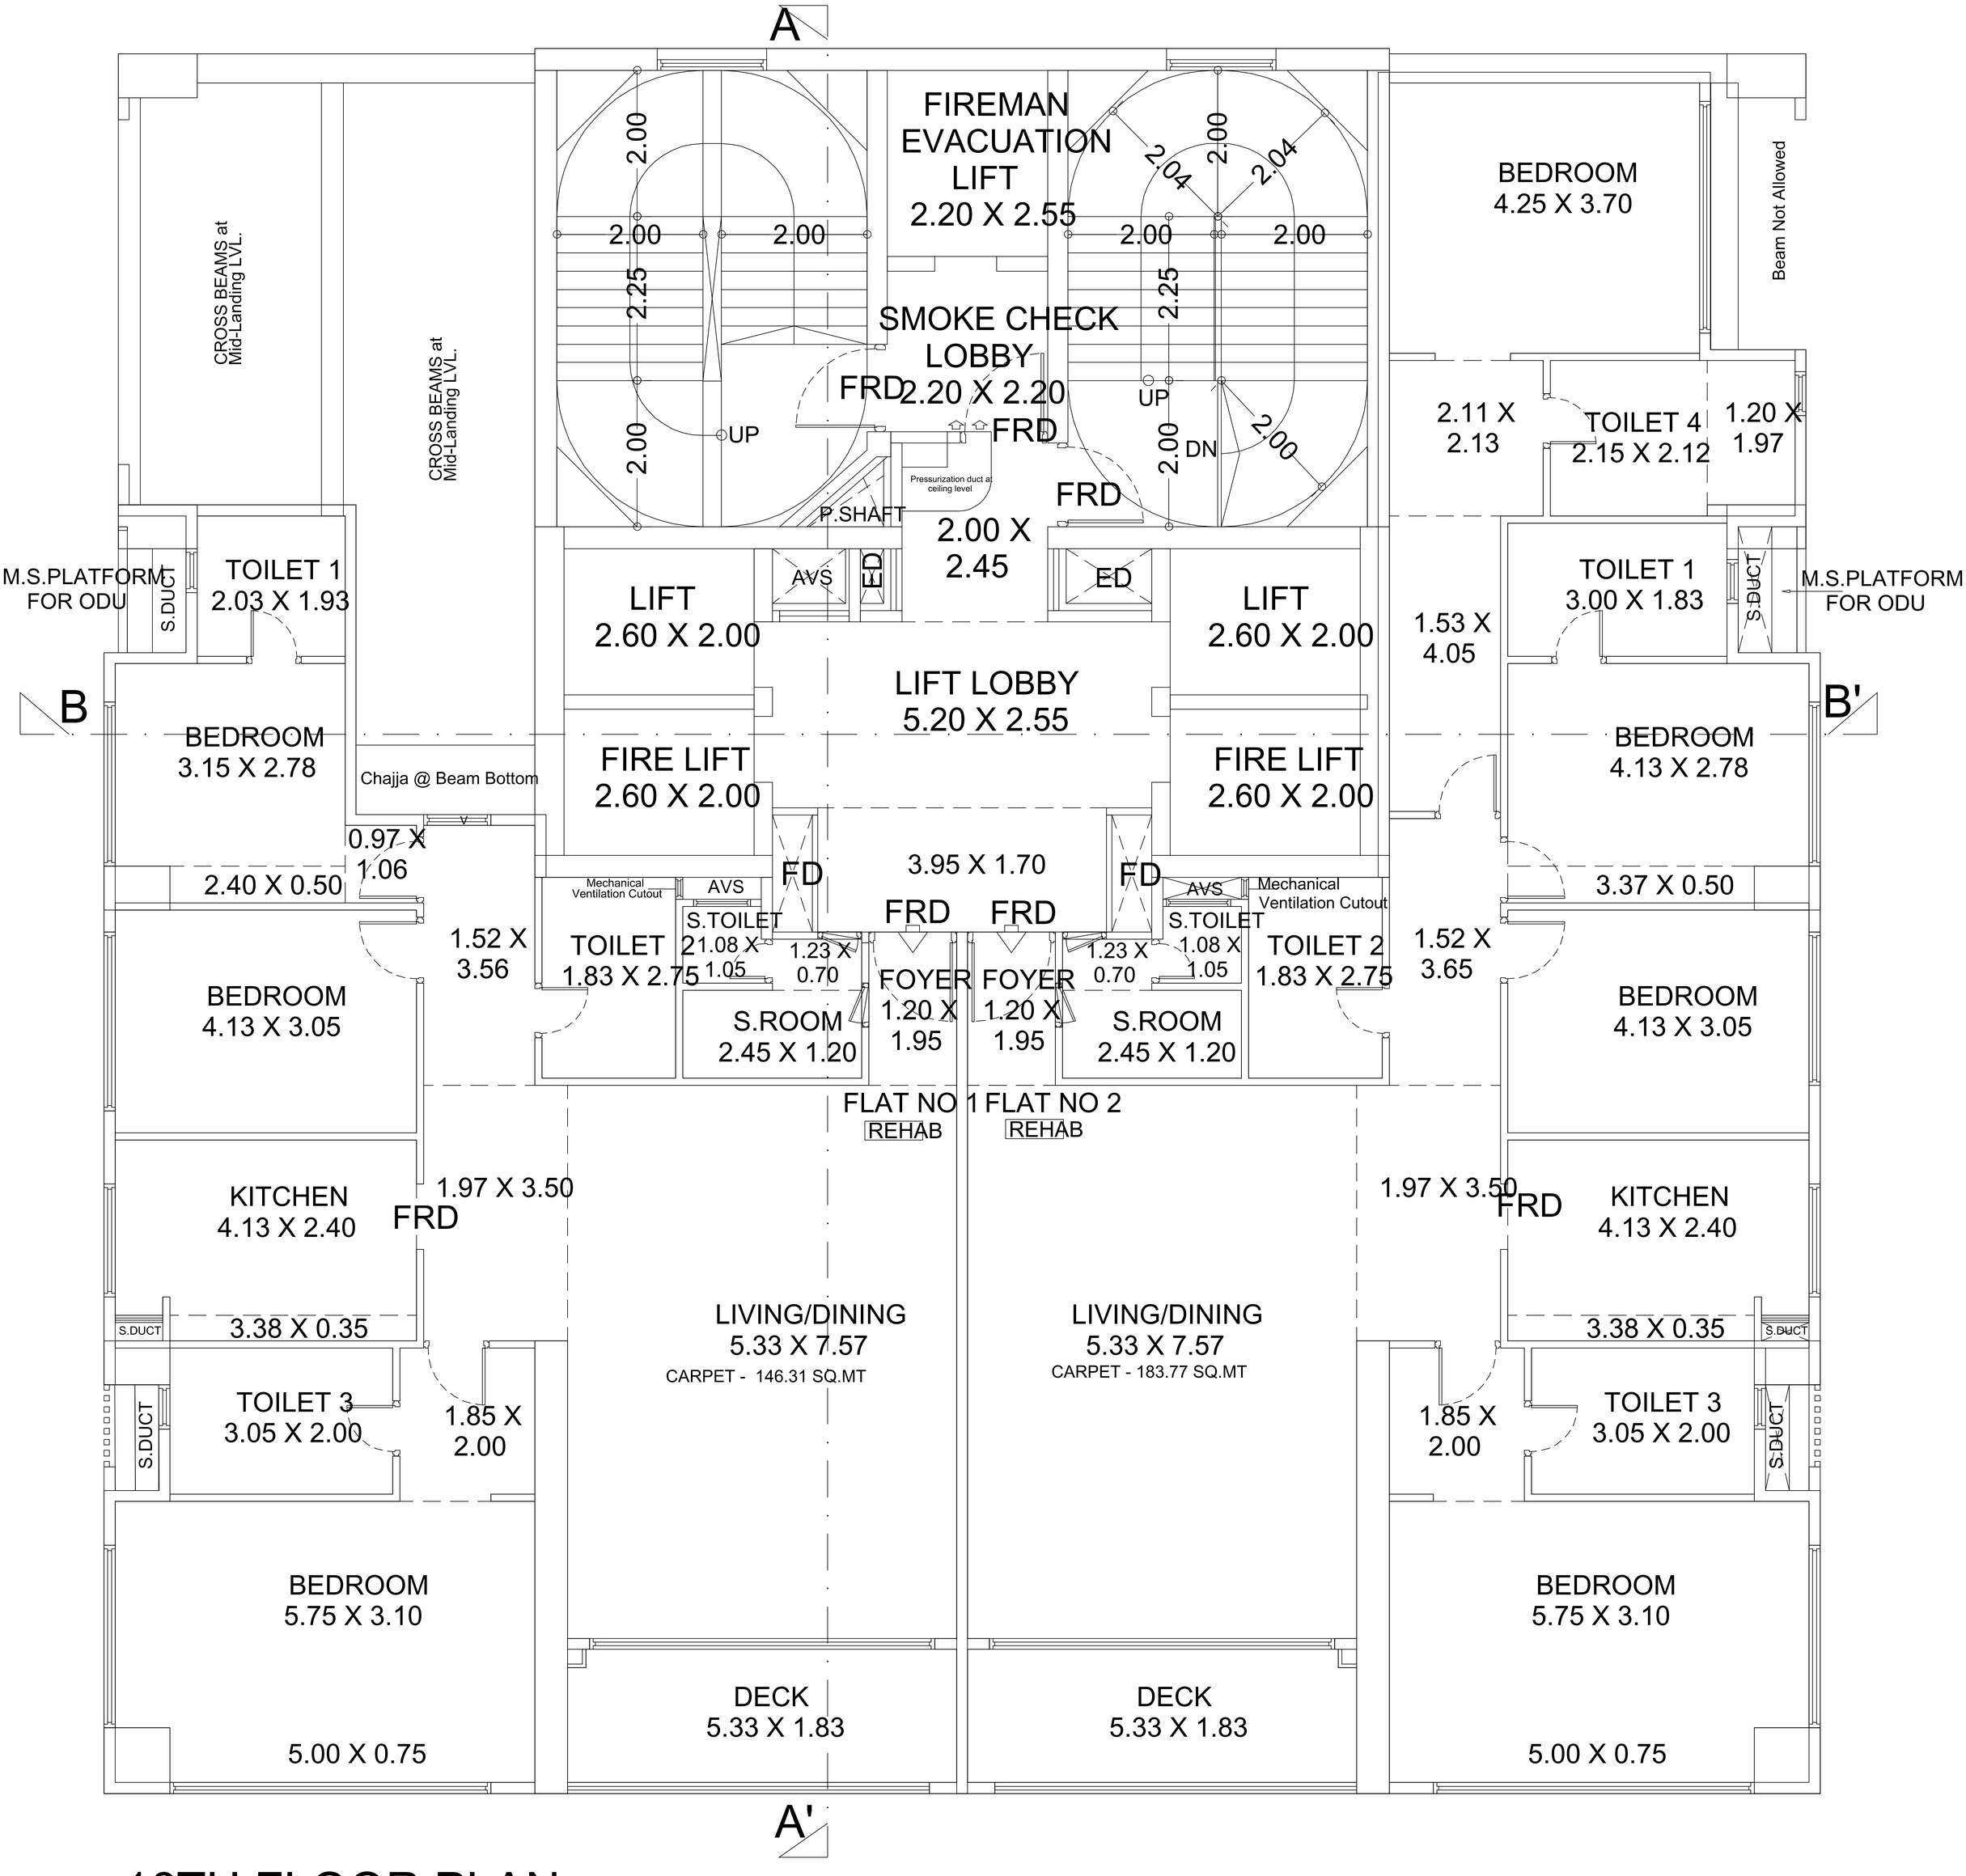


16TH FLOOR PLAN

SCALE - 1:100

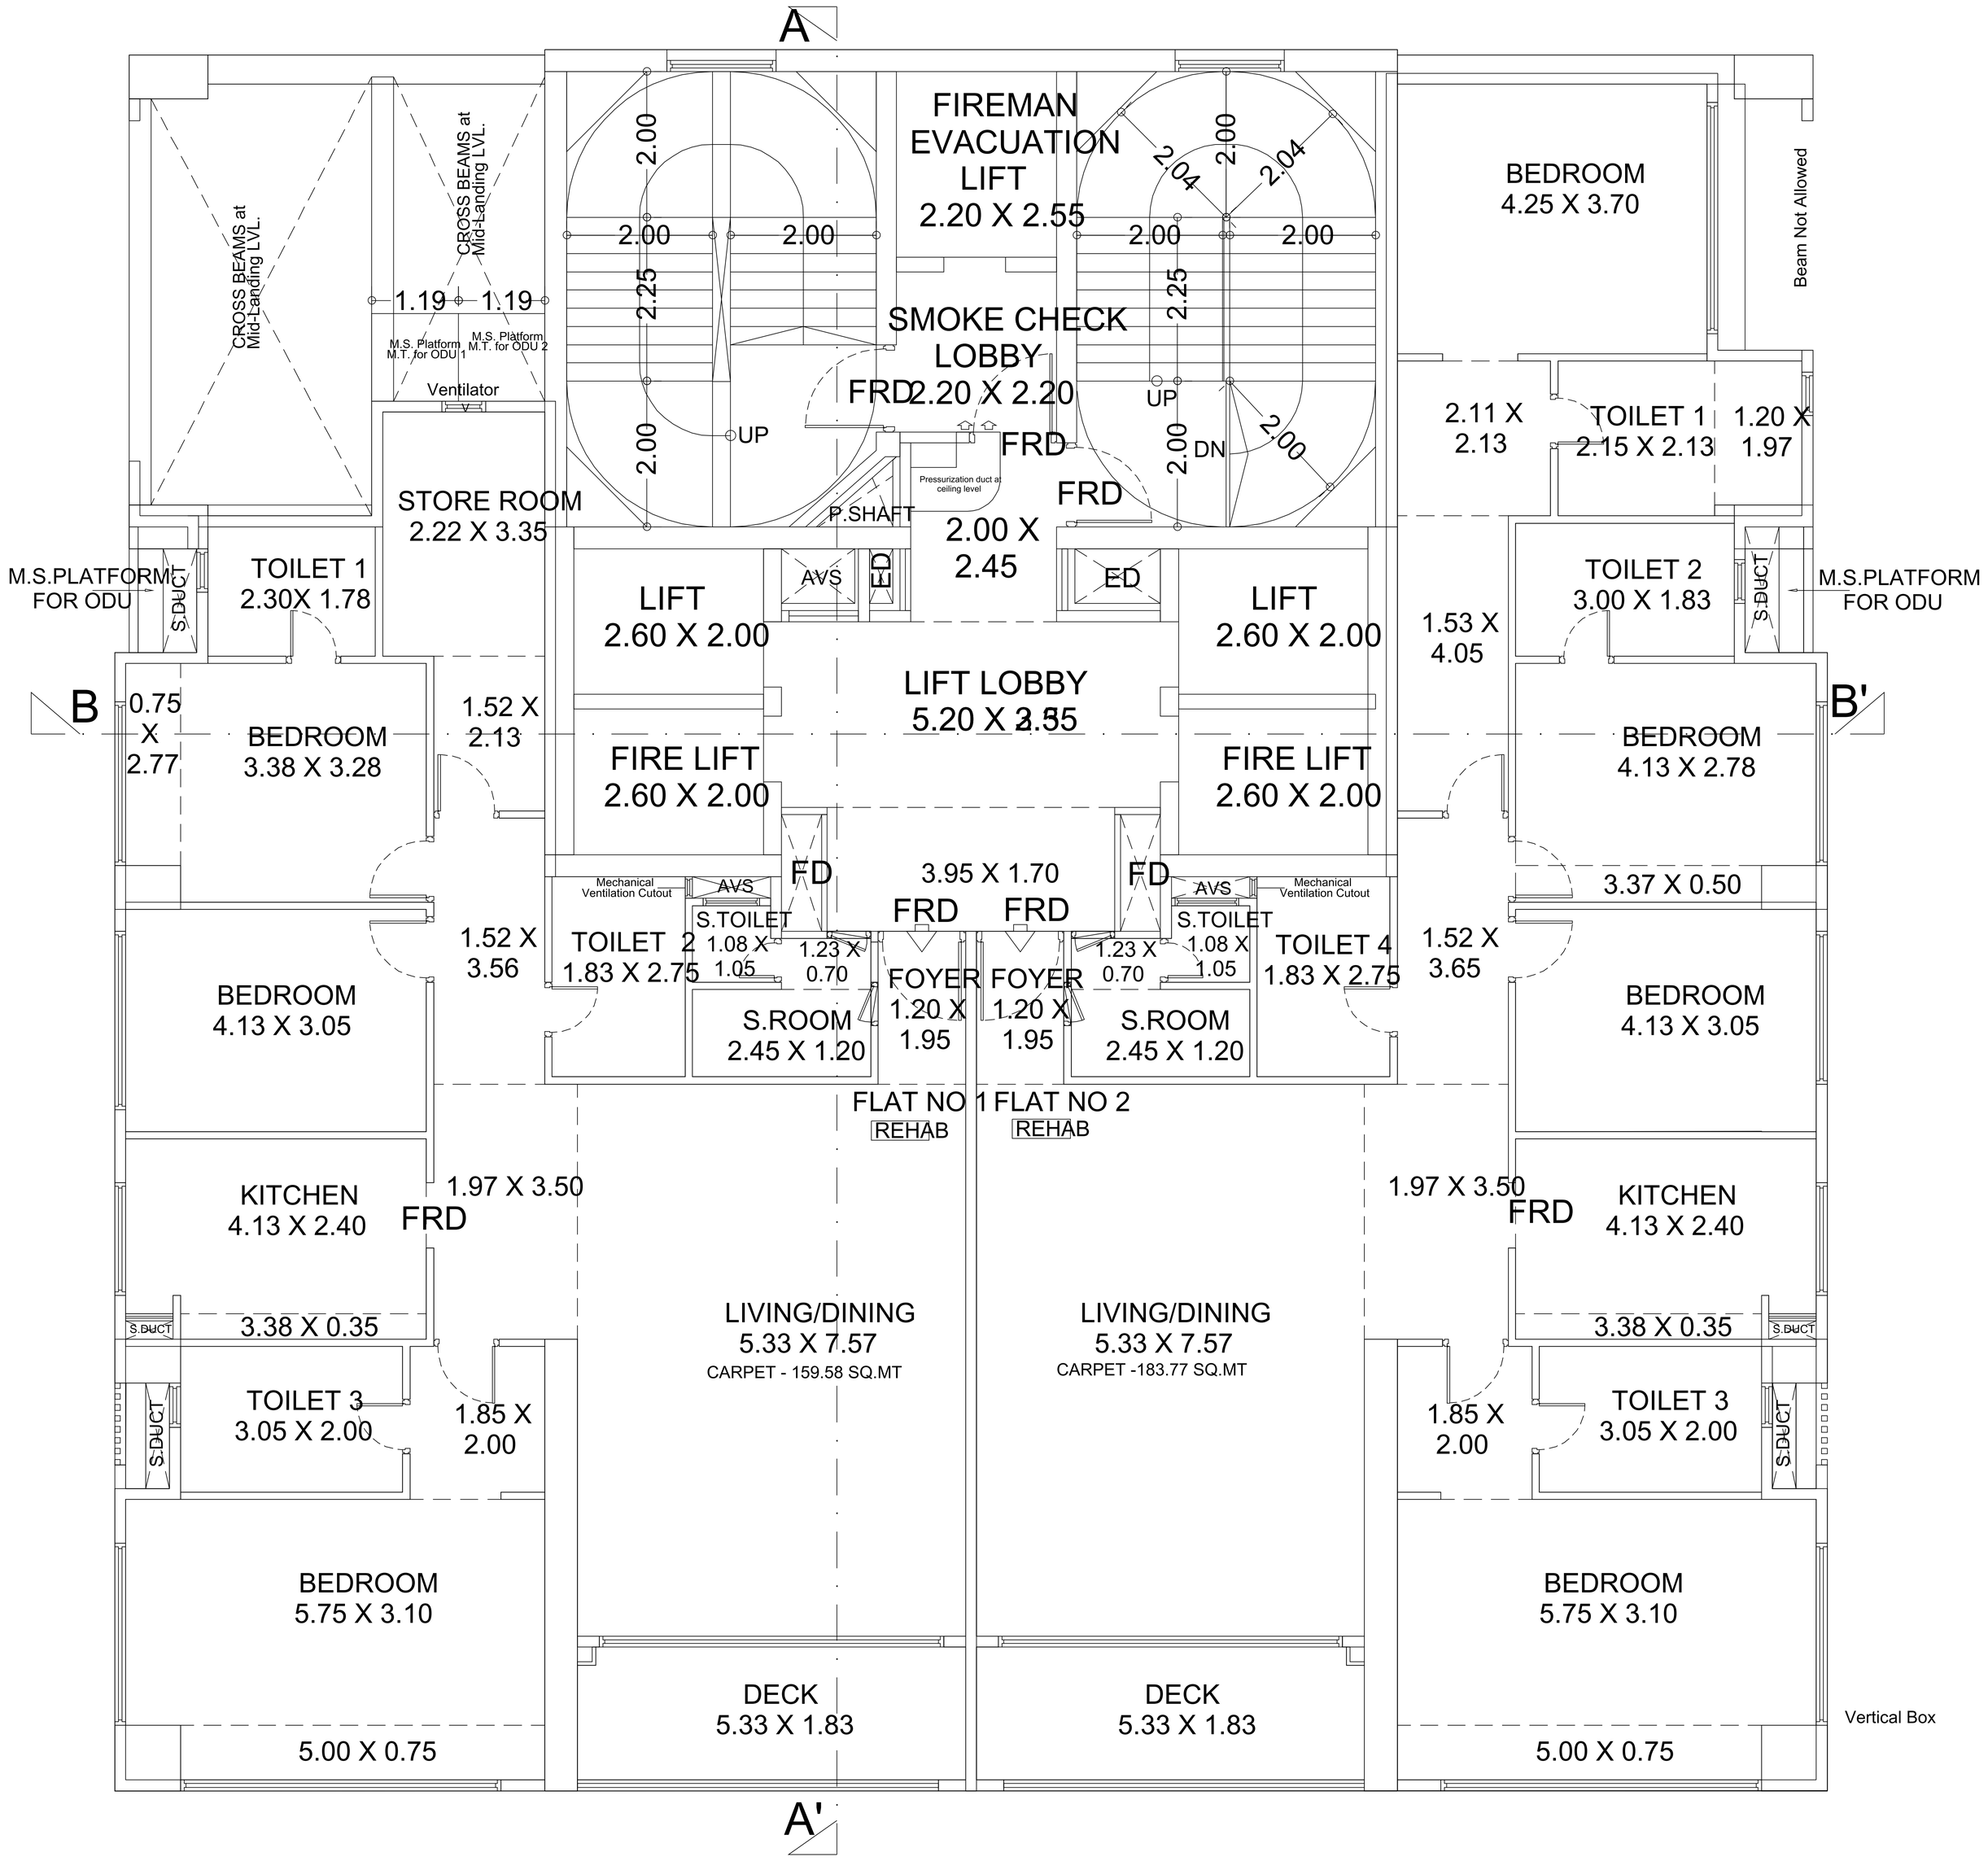

17TH FLOOR PLAN


SCALE - 1:100

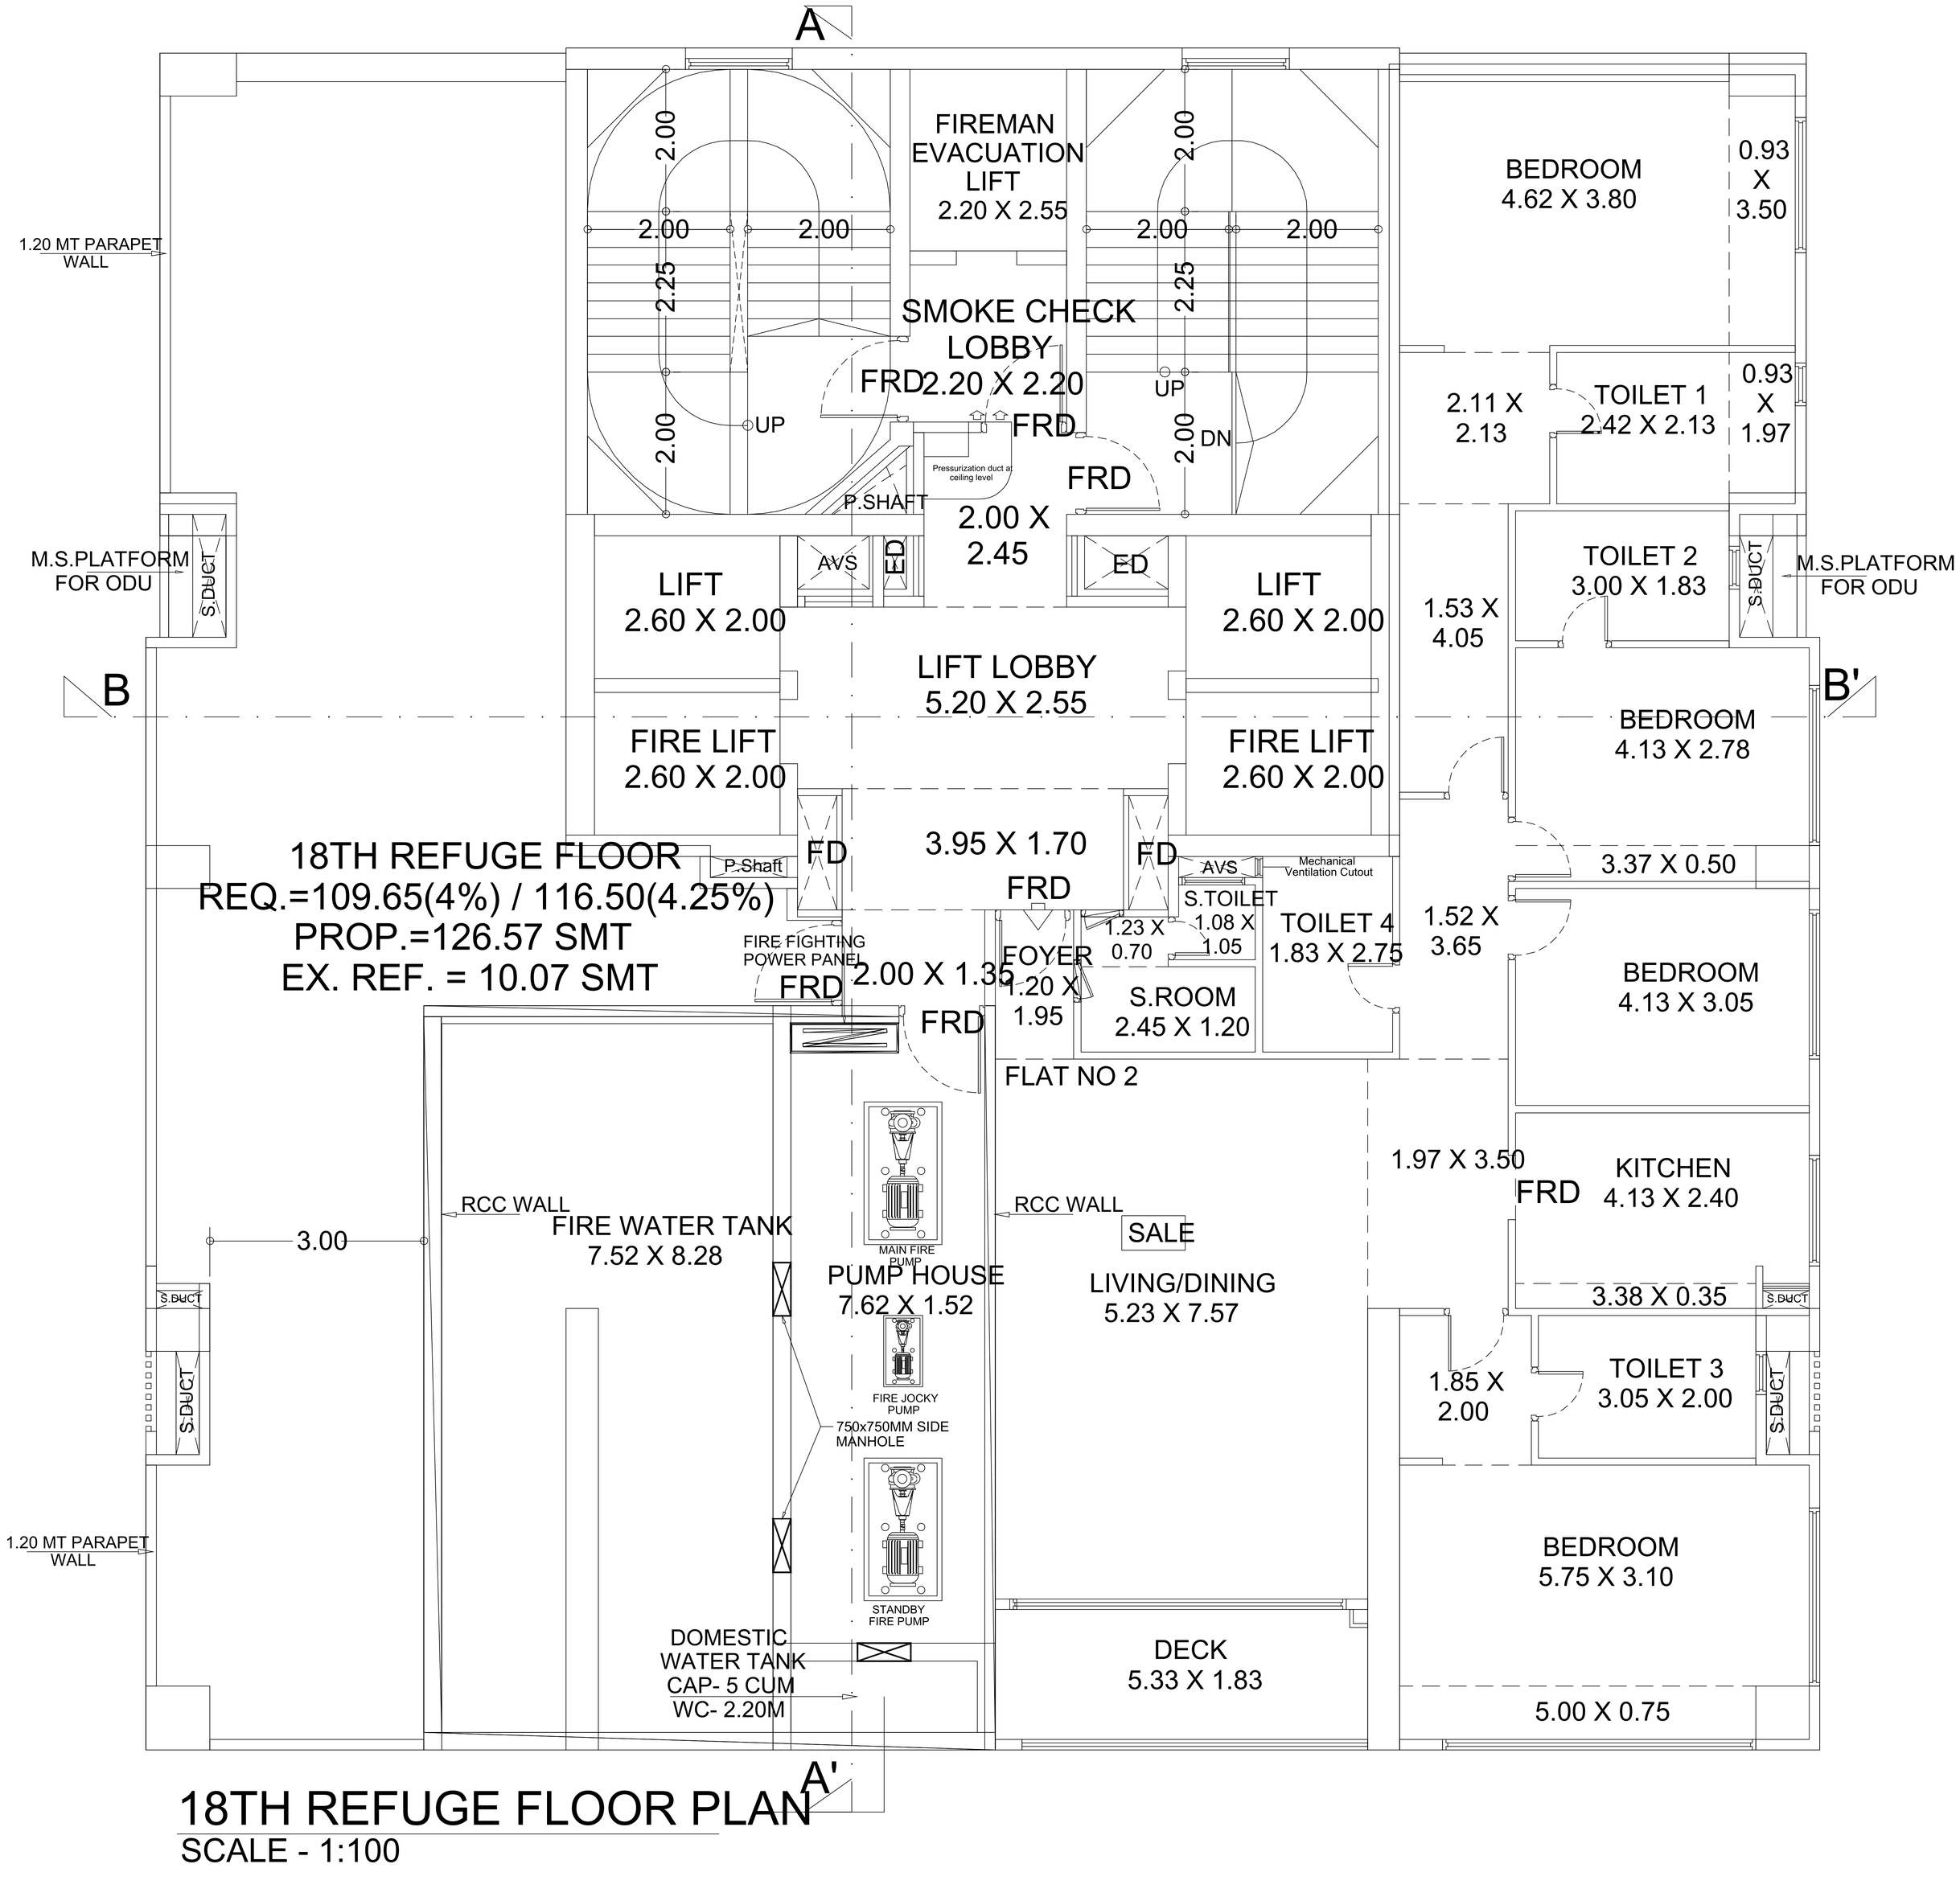

18TH REFUGE FLOOR
REQ.=109.65(4%) / 116.50(4.25%)
PROP.=126.57 SMT
EX. REF. = 10.07 SMT


18TH REFUGE FLOOR PLAN

SCALE - 1:100

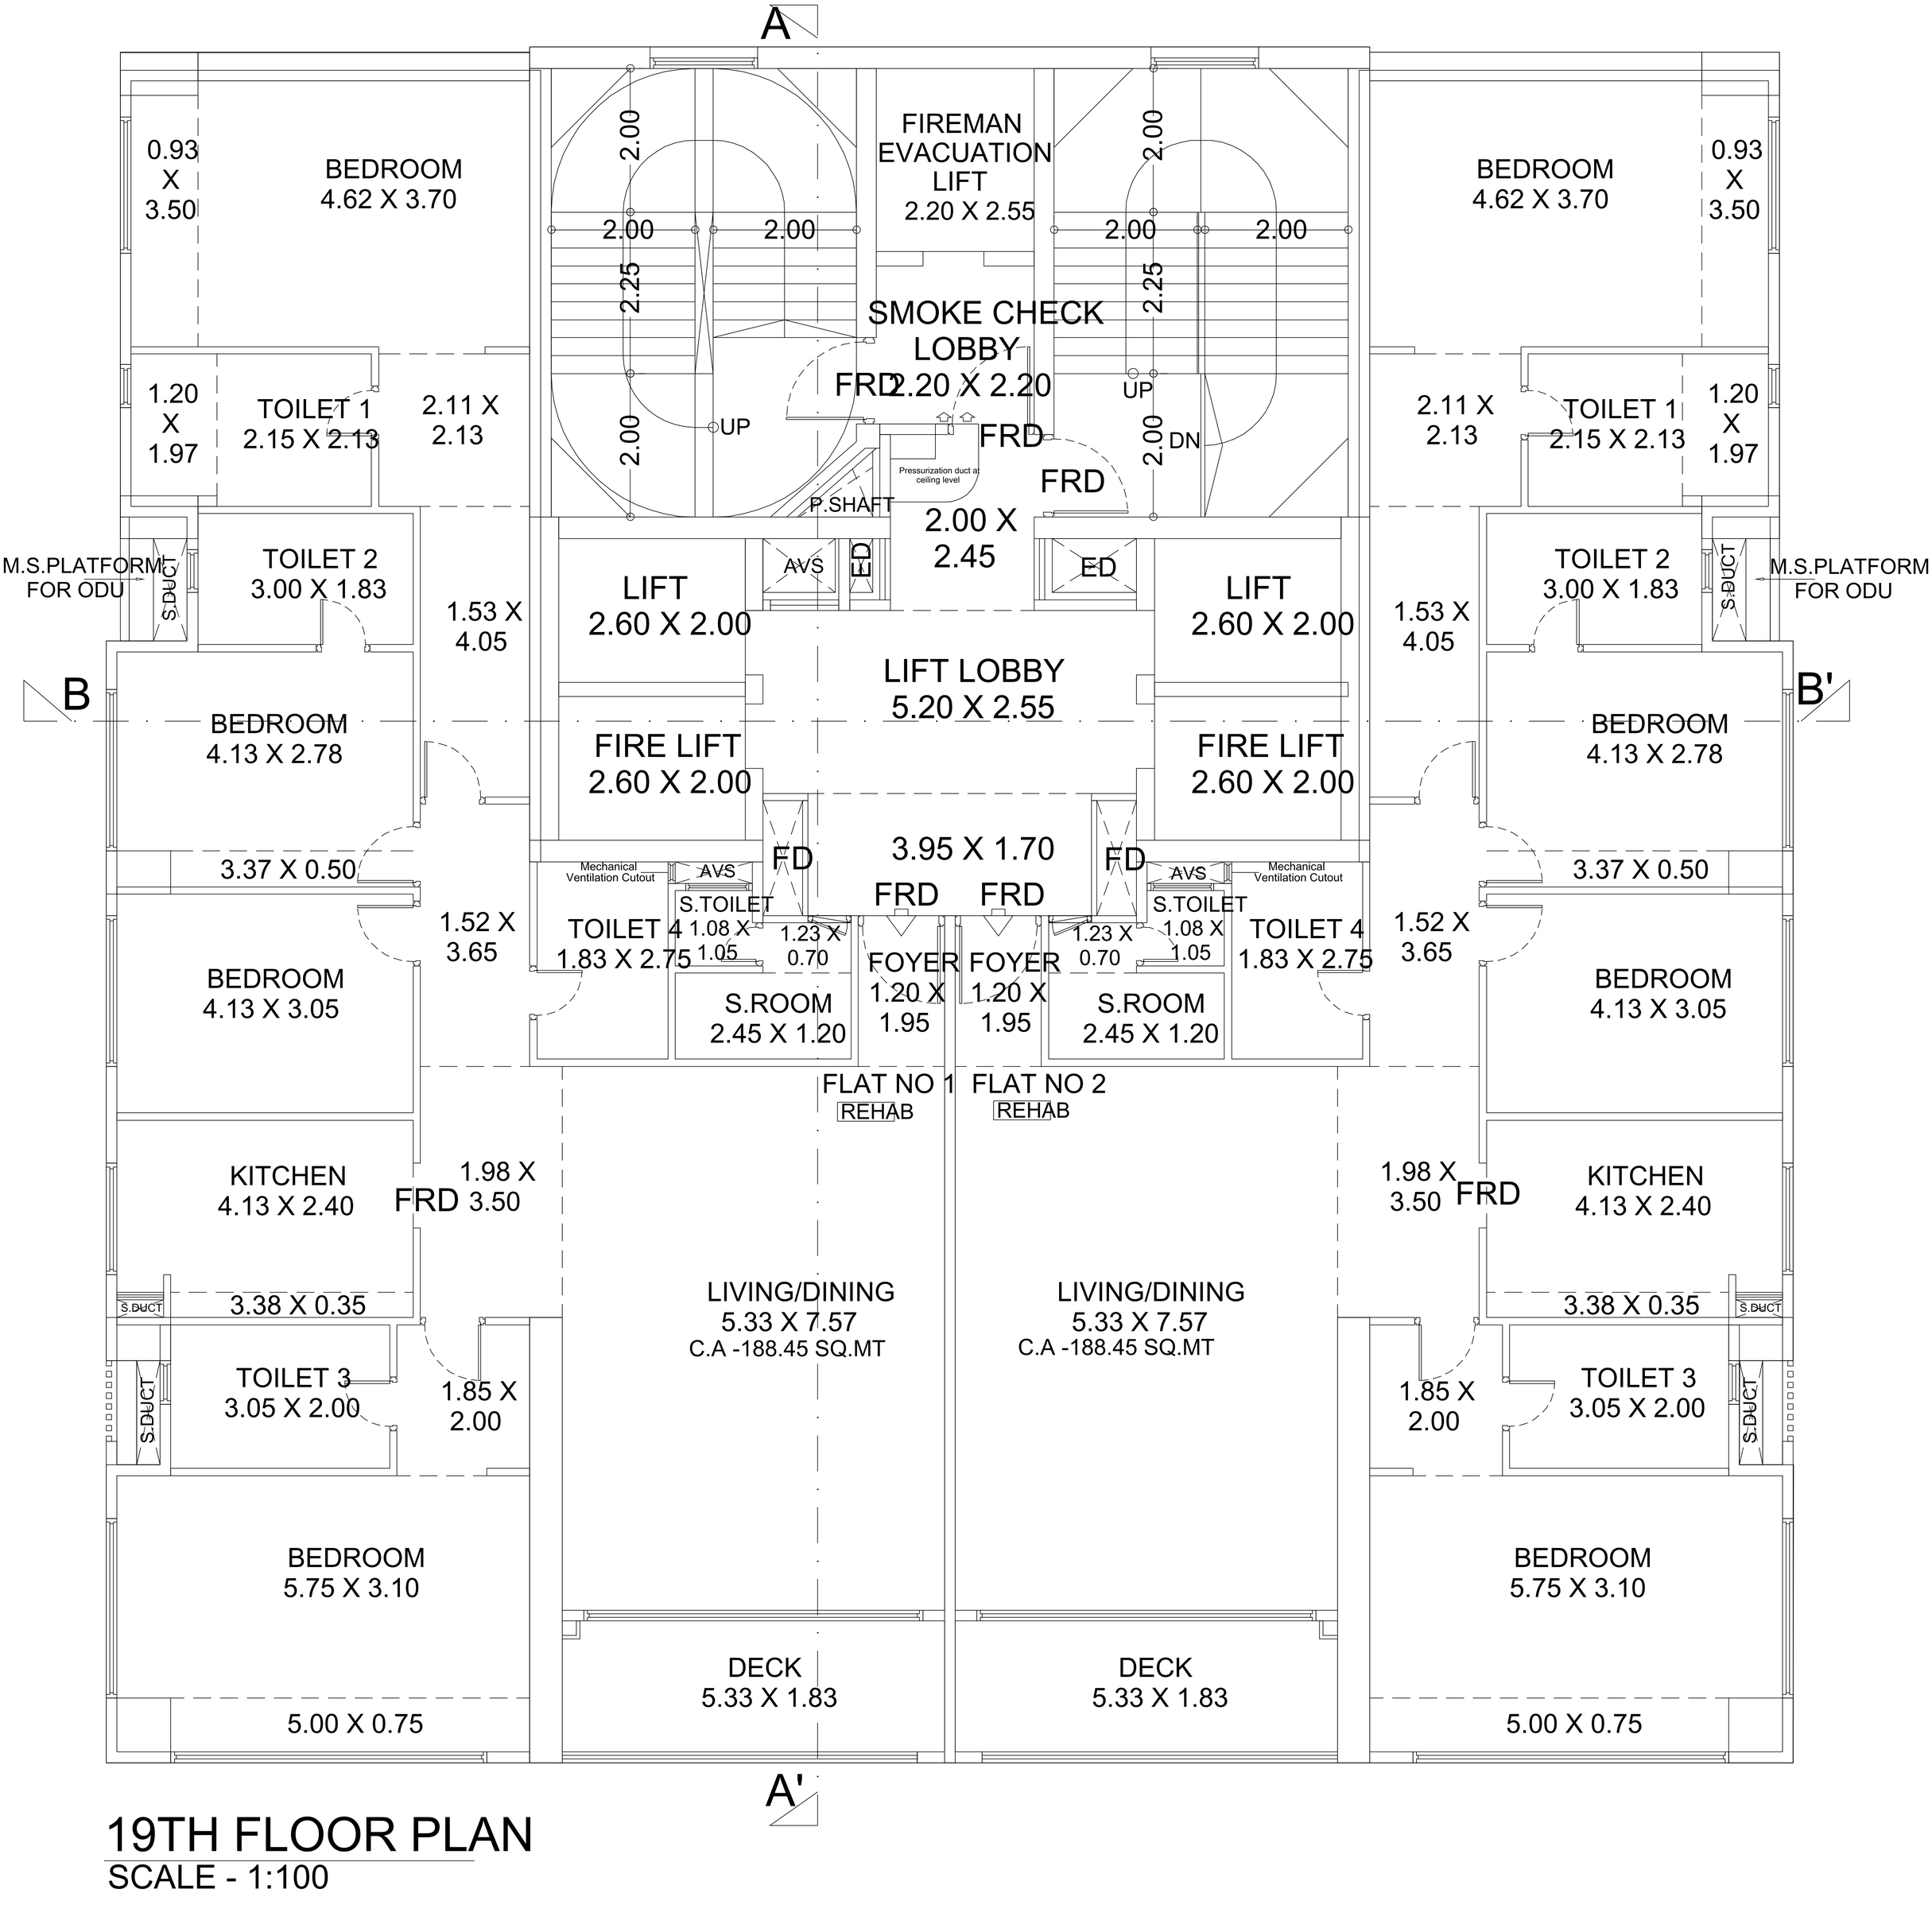

19TH FLOOR PLAN

SCALE - 1:100

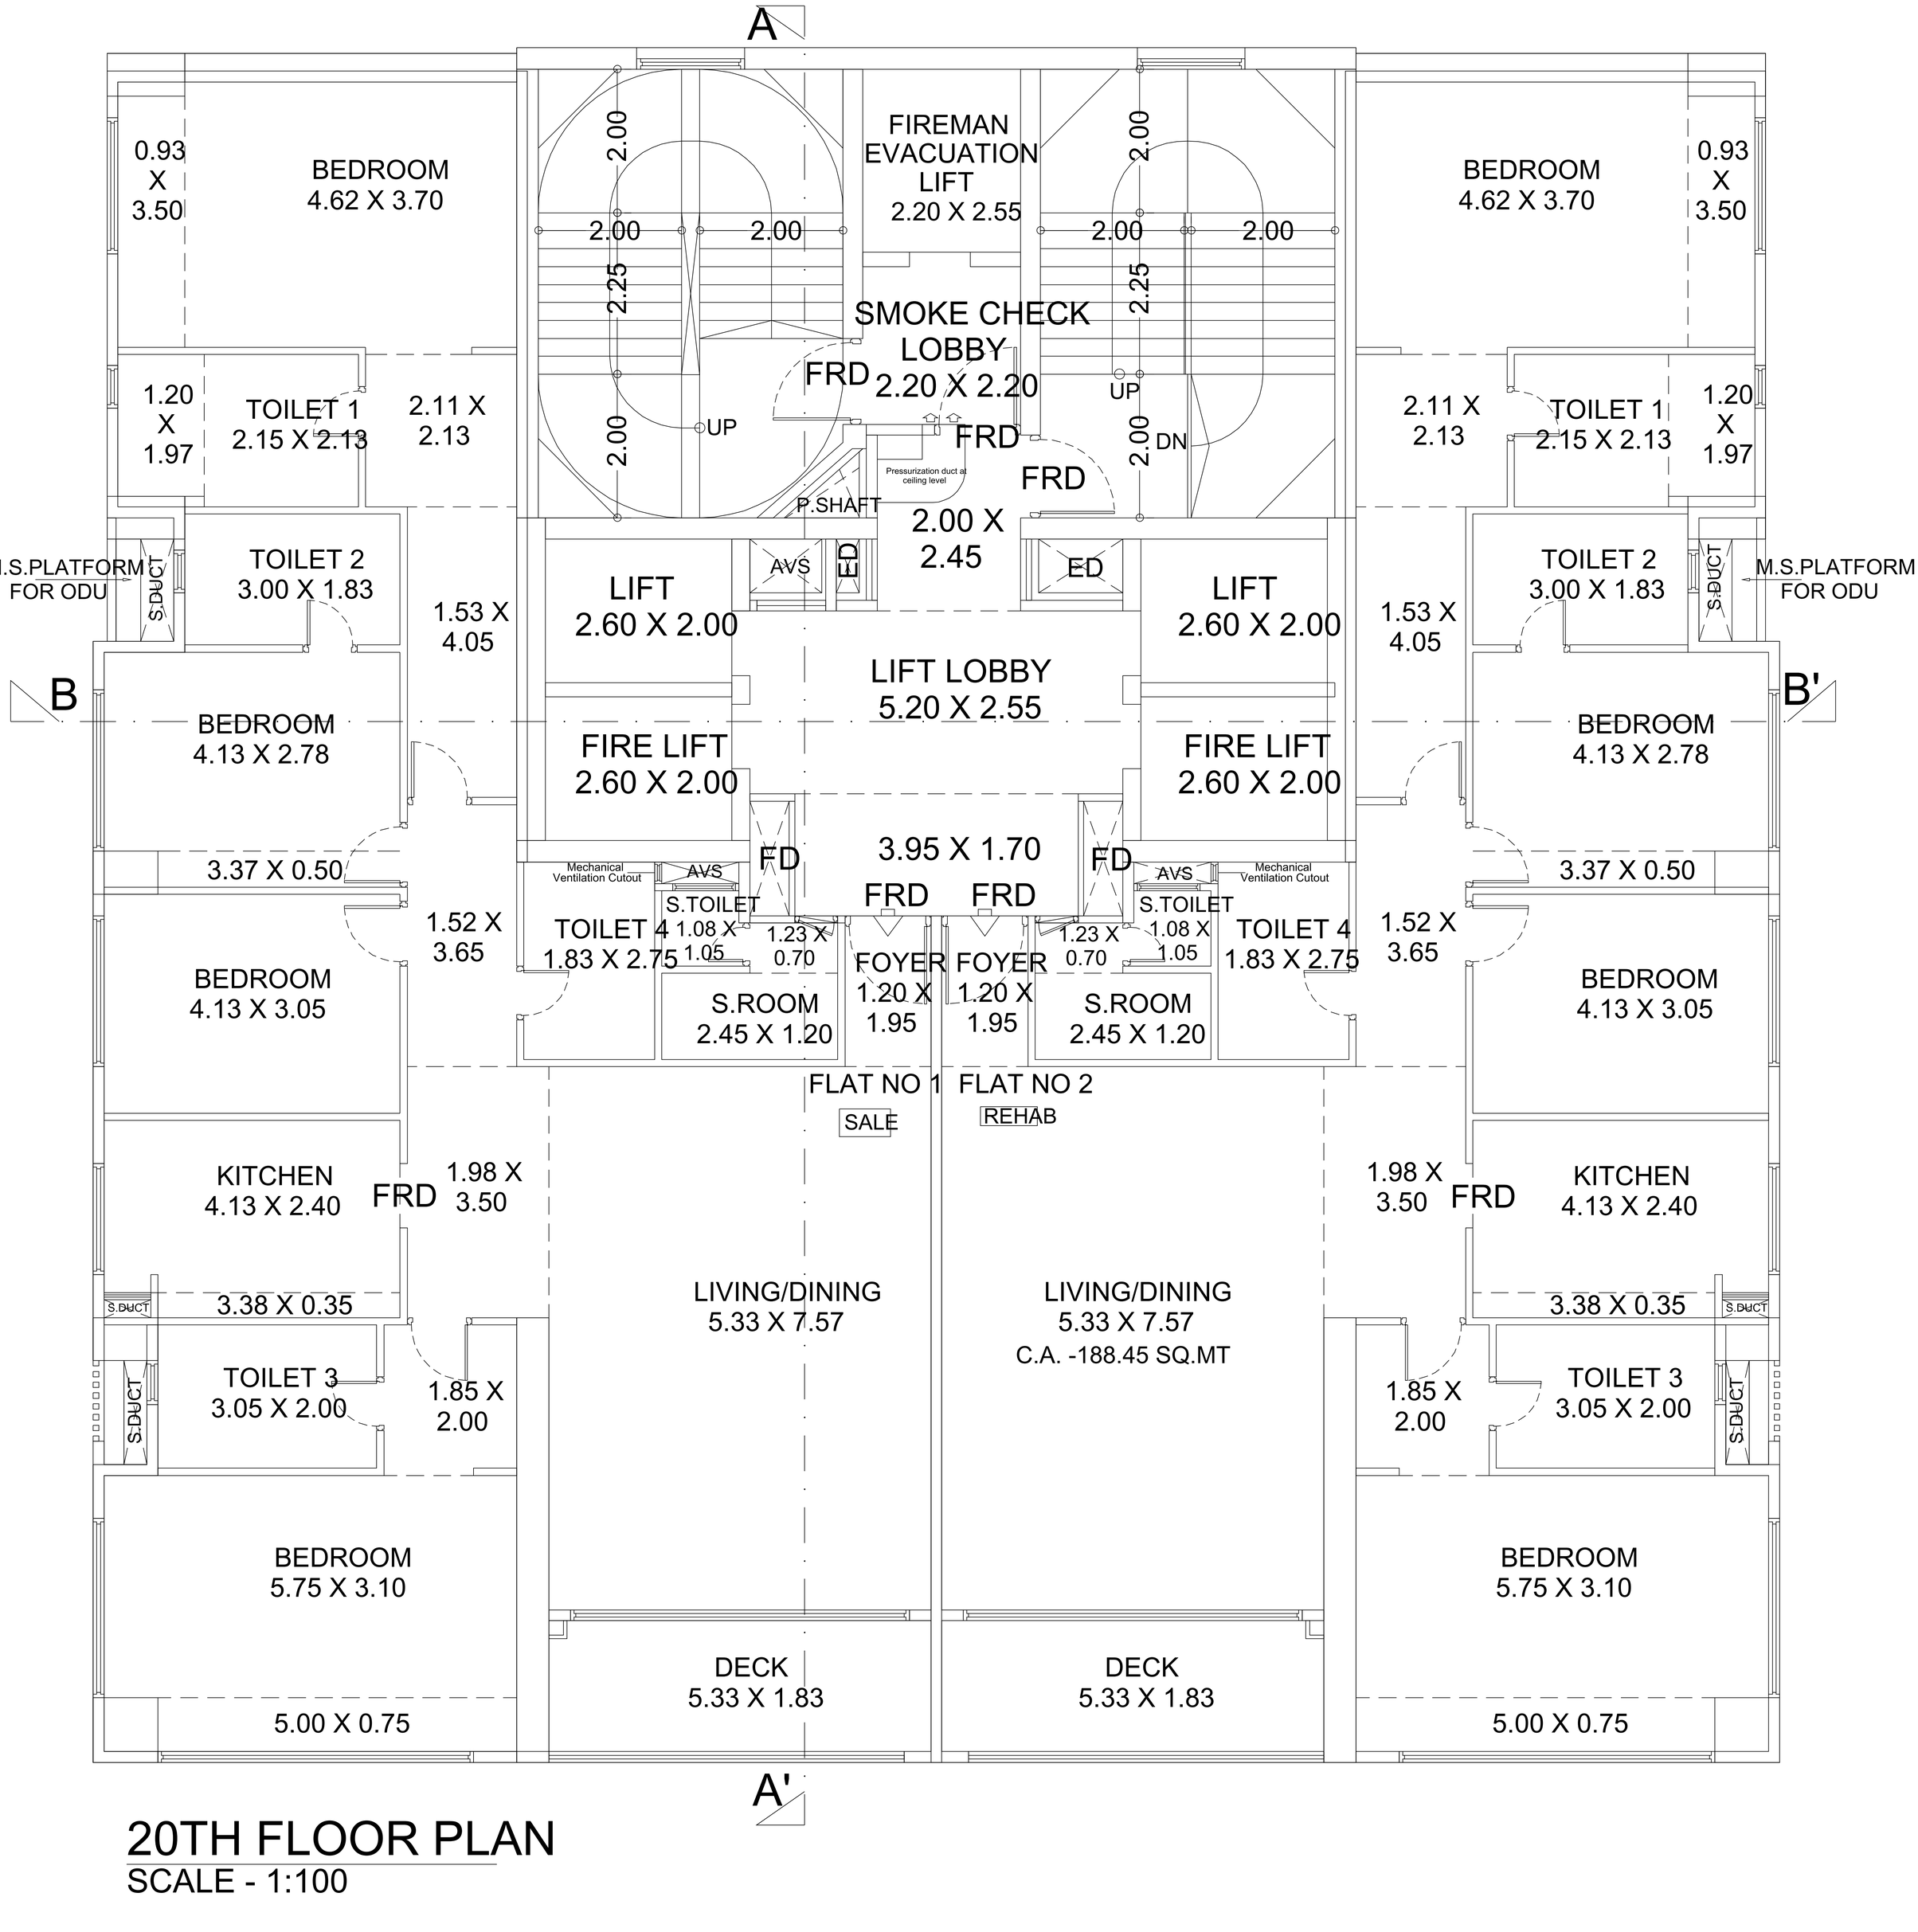

20TH FLOOR PLAN

SCALE - 1:100

A

0.93 X 3.50

BEDROOM 4.62 X 3.70

FIREMAN EVACUATION LIFT 2.20 X 2.55

2.00

2.00

2.00

2.25

2.00

2.00

2.00

2.25

2.00

SMOKE CHECK LOBBY 2.20 X 2.20

FRD

UP

FRD

UP

DN

Pressurization duct at ceiling level

FRD

P.SHAFT

2.00 X 2.45

BEDROOM 4.62 X 3.70

0.93 X 3.50

1.20 X 1.97

TOILET 1 2.15 X 2.13

2.11 X 2.13

2.11 X 2.13

TOILET 1 2.15 X 2.13

1.20 X 1.97

M.S.PLATFORM FOR ODU

S.DUCT

TOILET 2 3.00 X 1.83

AVS

ED

ED

TOILET 2 3.00 X 1.83

S.DUCT

M.S.PLATFORM FOR ODU

1.53 X 4.05

LIFT 2.60 X 2.00

LIFT 2.60 X 2.00

1.53 X 4.05

B

LIFT LOBBY 5.20 X 2.55

B'

BEDROOM 4.13 X 2.78

FIRE LIFT 2.60 X 2.00

FIRE LIFT 2.60 X 2.00

BEDROOM 4.13 X 2.78

3.37 X 0.50

Mechanical Ventilation Cutout

AVS

FD

3.95 X 1.70

FD

AVS

Mechanical Ventilation Cutout

3.37 X 0.50

FRD

FRD

S.TOILET

S.TOILET

1.52 X 3.65

TOILET 4 1.83 X 2.75

1.08 X 1.05

1.23 X 0.70

FOYER 1.20 X 1.95

FOYER 1.20 X 1.95

1.23 X 0.70

1.08 X 1.05

TOILET 4 1.83 X 2.75

1.52 X 3.65

BEDROOM 4.13 X 3.05

S.ROOM 2.45 X 1.20

S.ROOM 2.45 X 1.20

BEDROOM 4.13 X 3.05

FLAT NO 1

FLAT NO 2

KITCHEN 4.13 X 2.40

FRD

1.98 X 3.50

SALE

LIVING/DINING 5.33 X 7.57

SALE

LIVING/DINING 5.33 X 7.57

1.98 X 3.50

FRD

KITCHEN 4.13 X 2.40

3.38 X 0.35

S.DUCT

S.DUCT

3.38 X 0.35

S.DUCT

TOILET 3 3.05 X 2.00

1.85 X 2.00

1.85 X 2.00

TOILET 3 3.05 X 2.00

S.DUCT

BEDROOM 5.75 X 3.10

DECK 5.33 X 1.83

DECK 5.33 X 1.83

BEDROOM 5.75 X 3.10


5.00 X 0.75

5.00 X 0.75

A'


21ST TO 23RD TYPICAL FLOOR PLAN

SCALE - 1:100

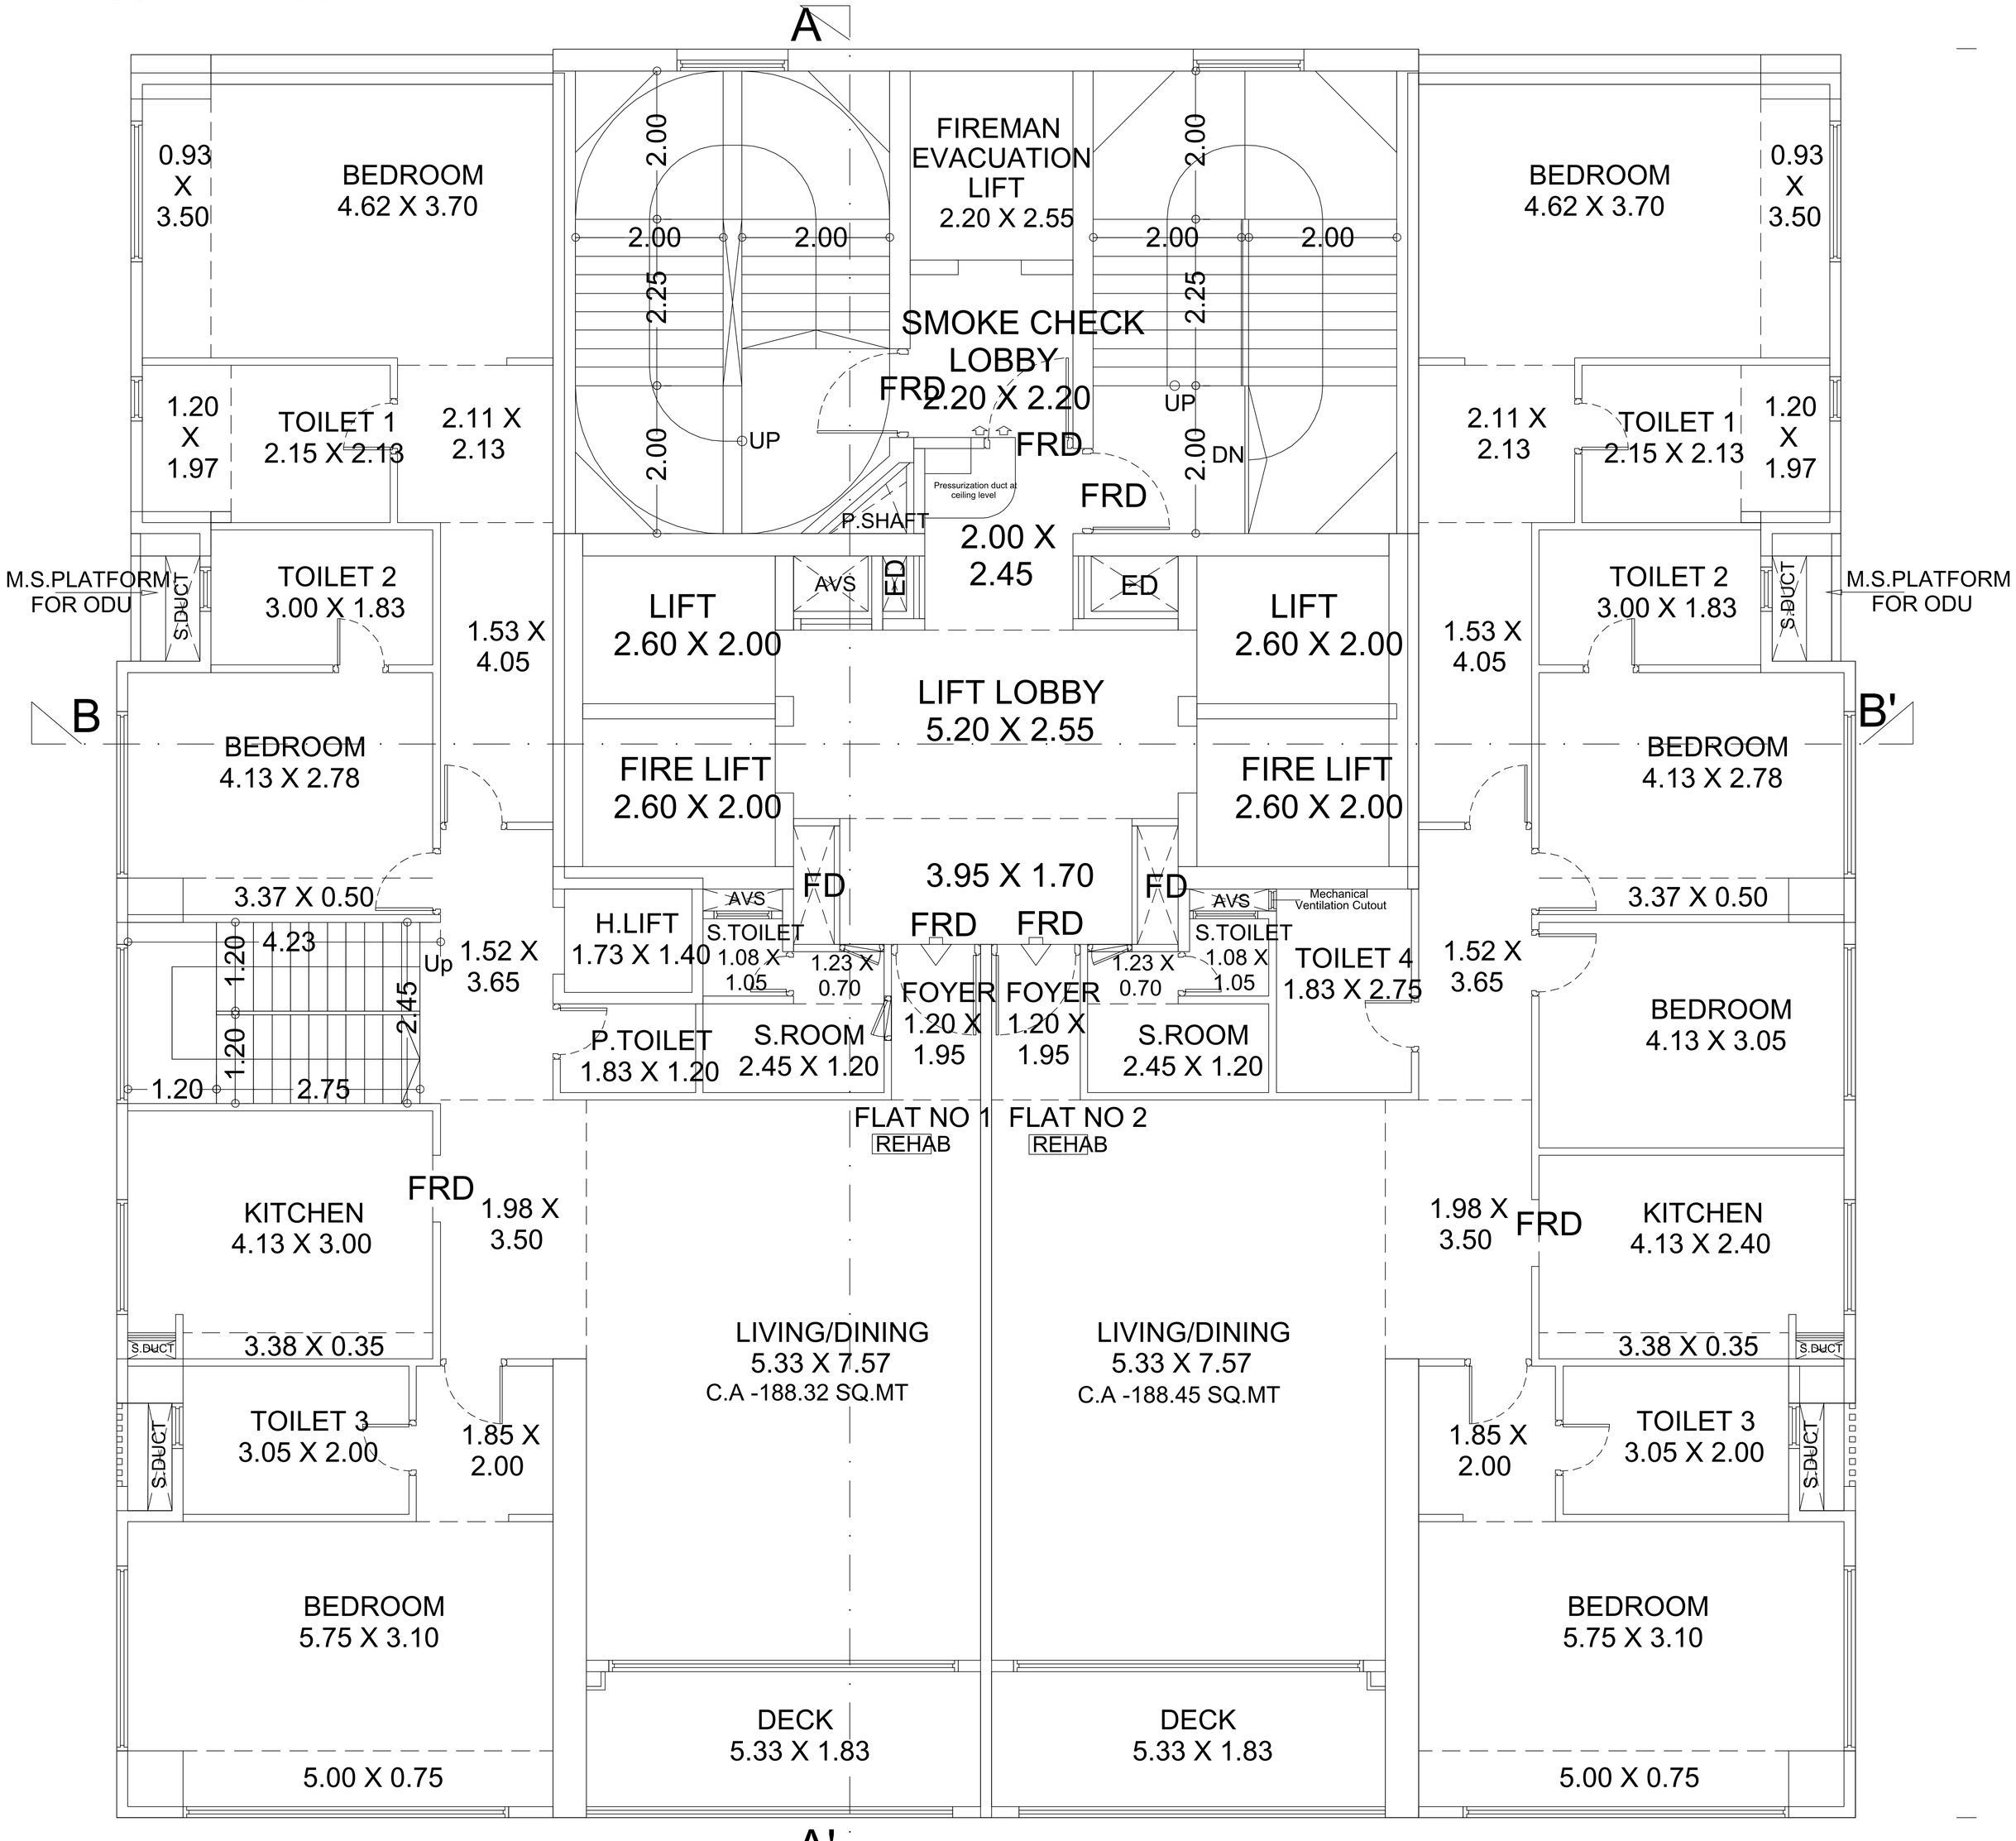


24TH (LOWER DUPLEX)FLOOR PLAN

SCALE - 1:100

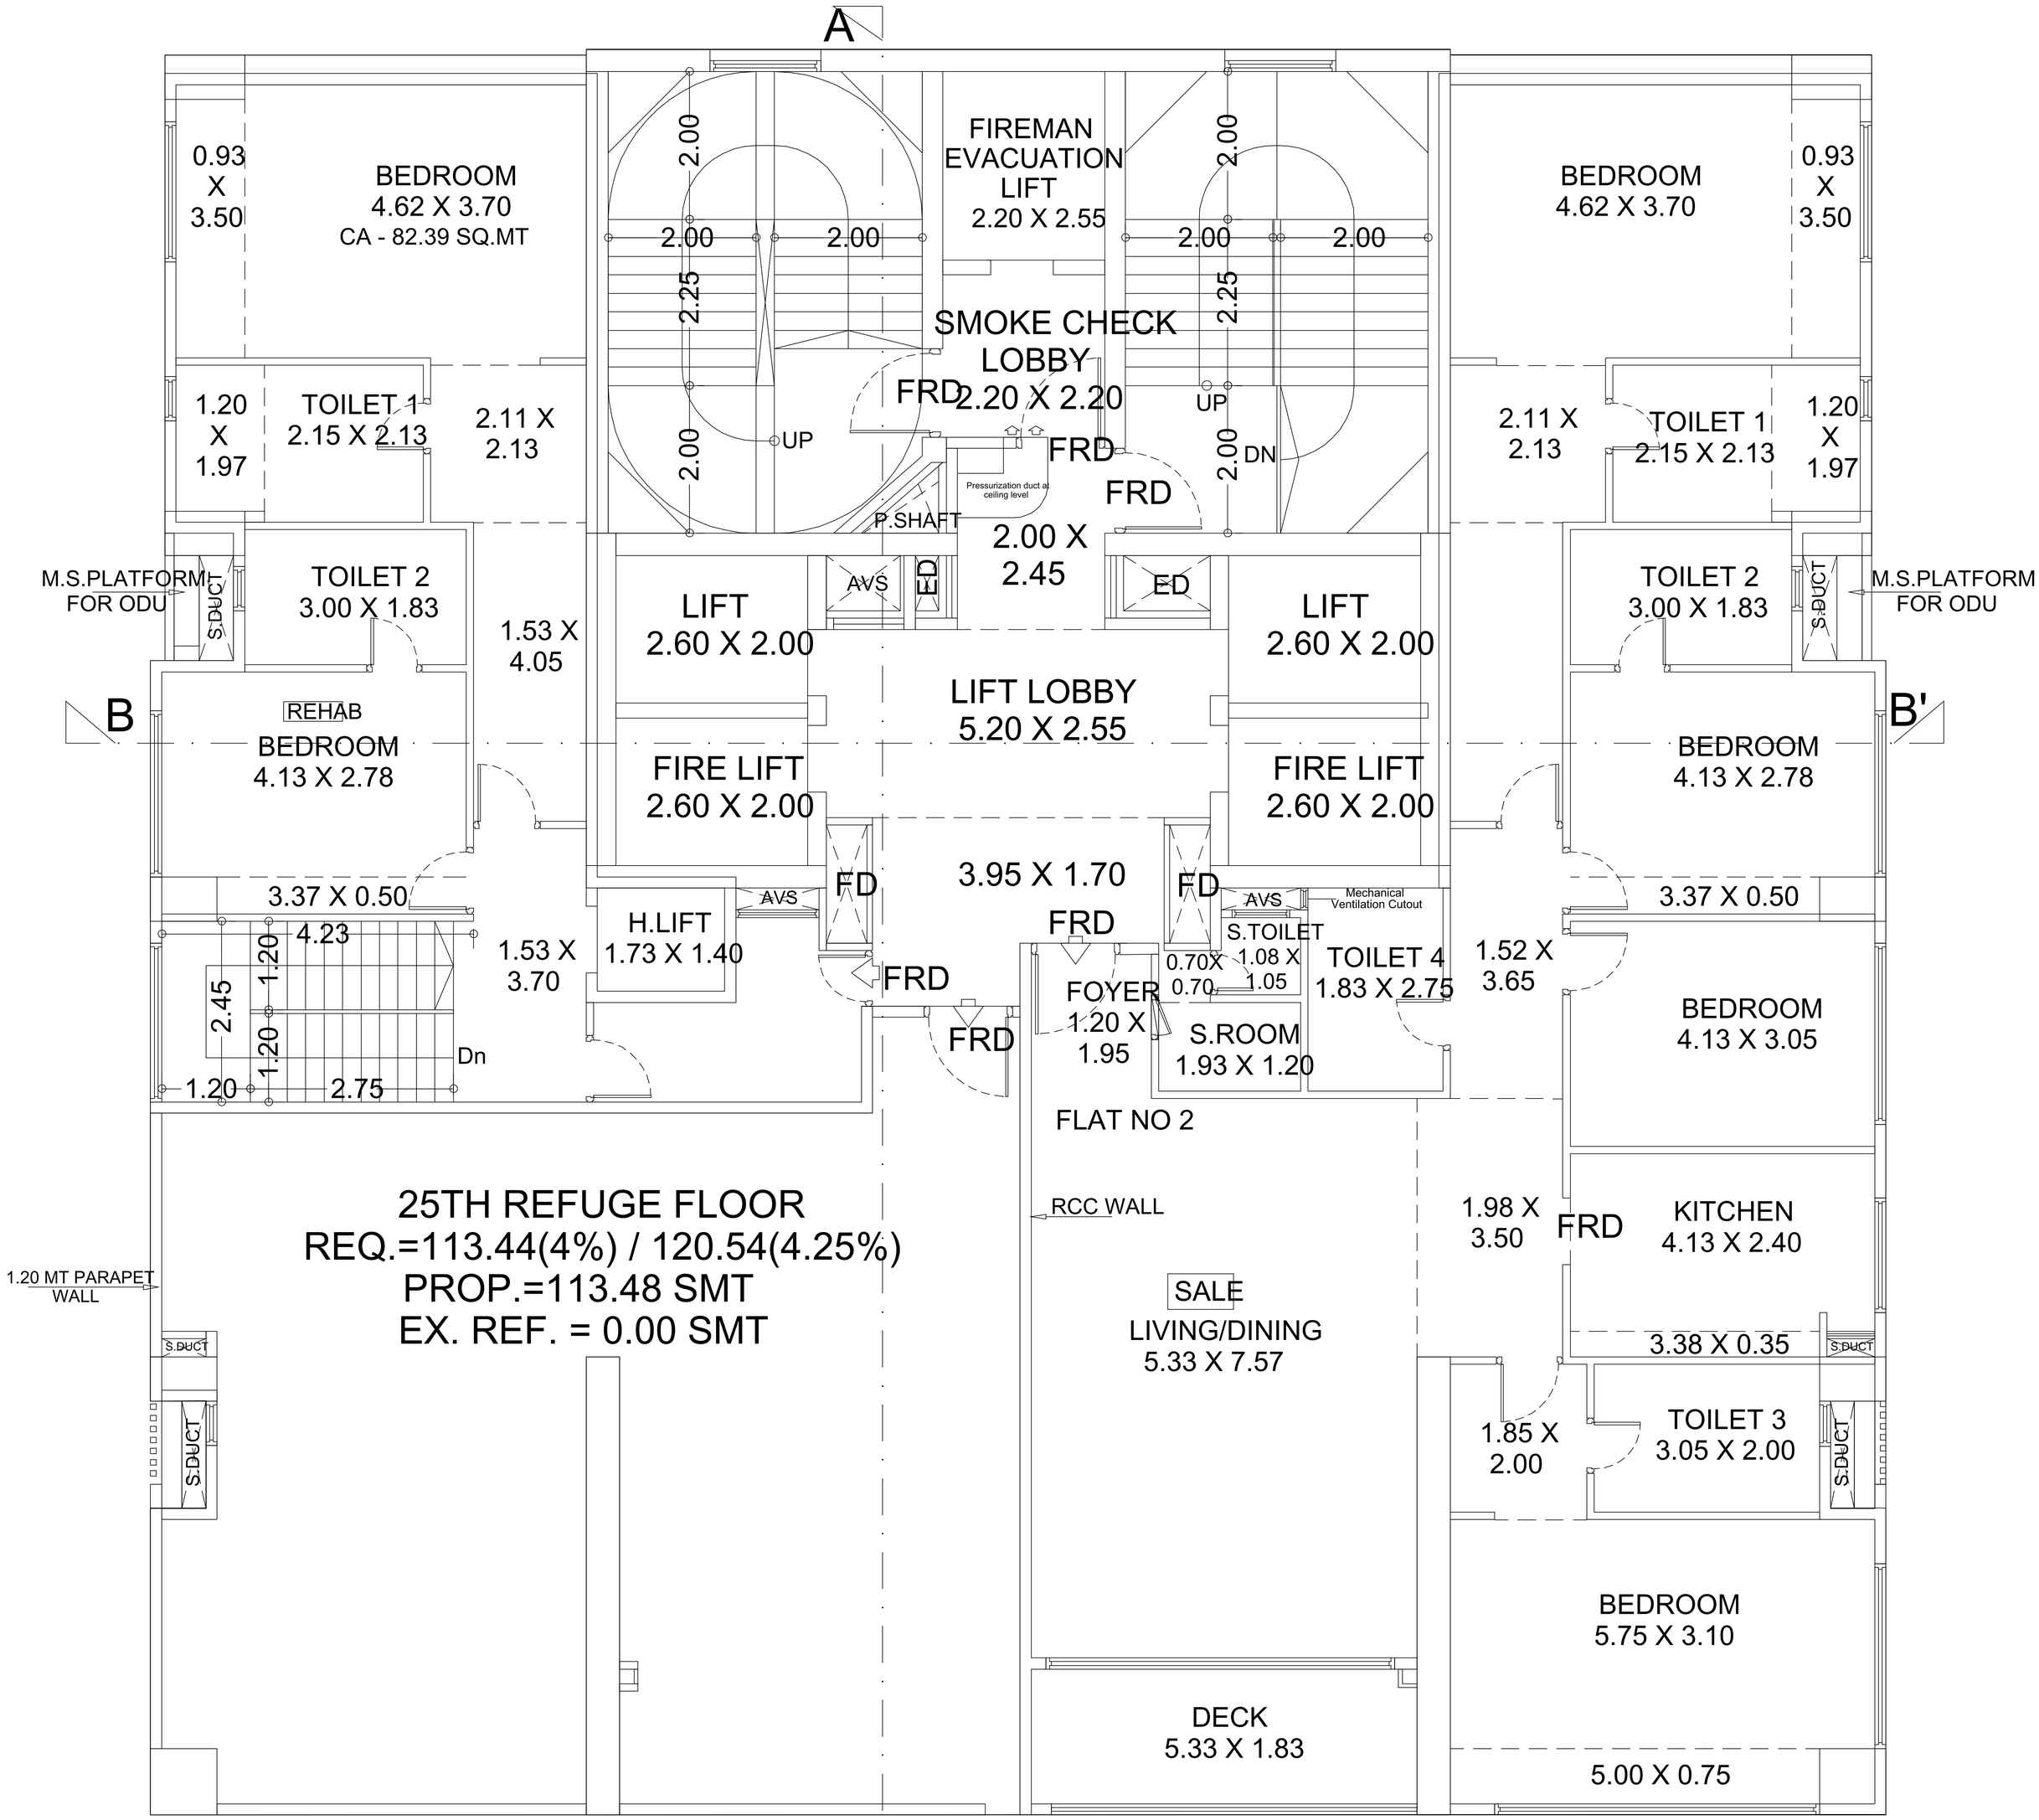


25TH REFUGE(UPPER DUPLEX)FLOOR PLAN

SCALE - 1:100

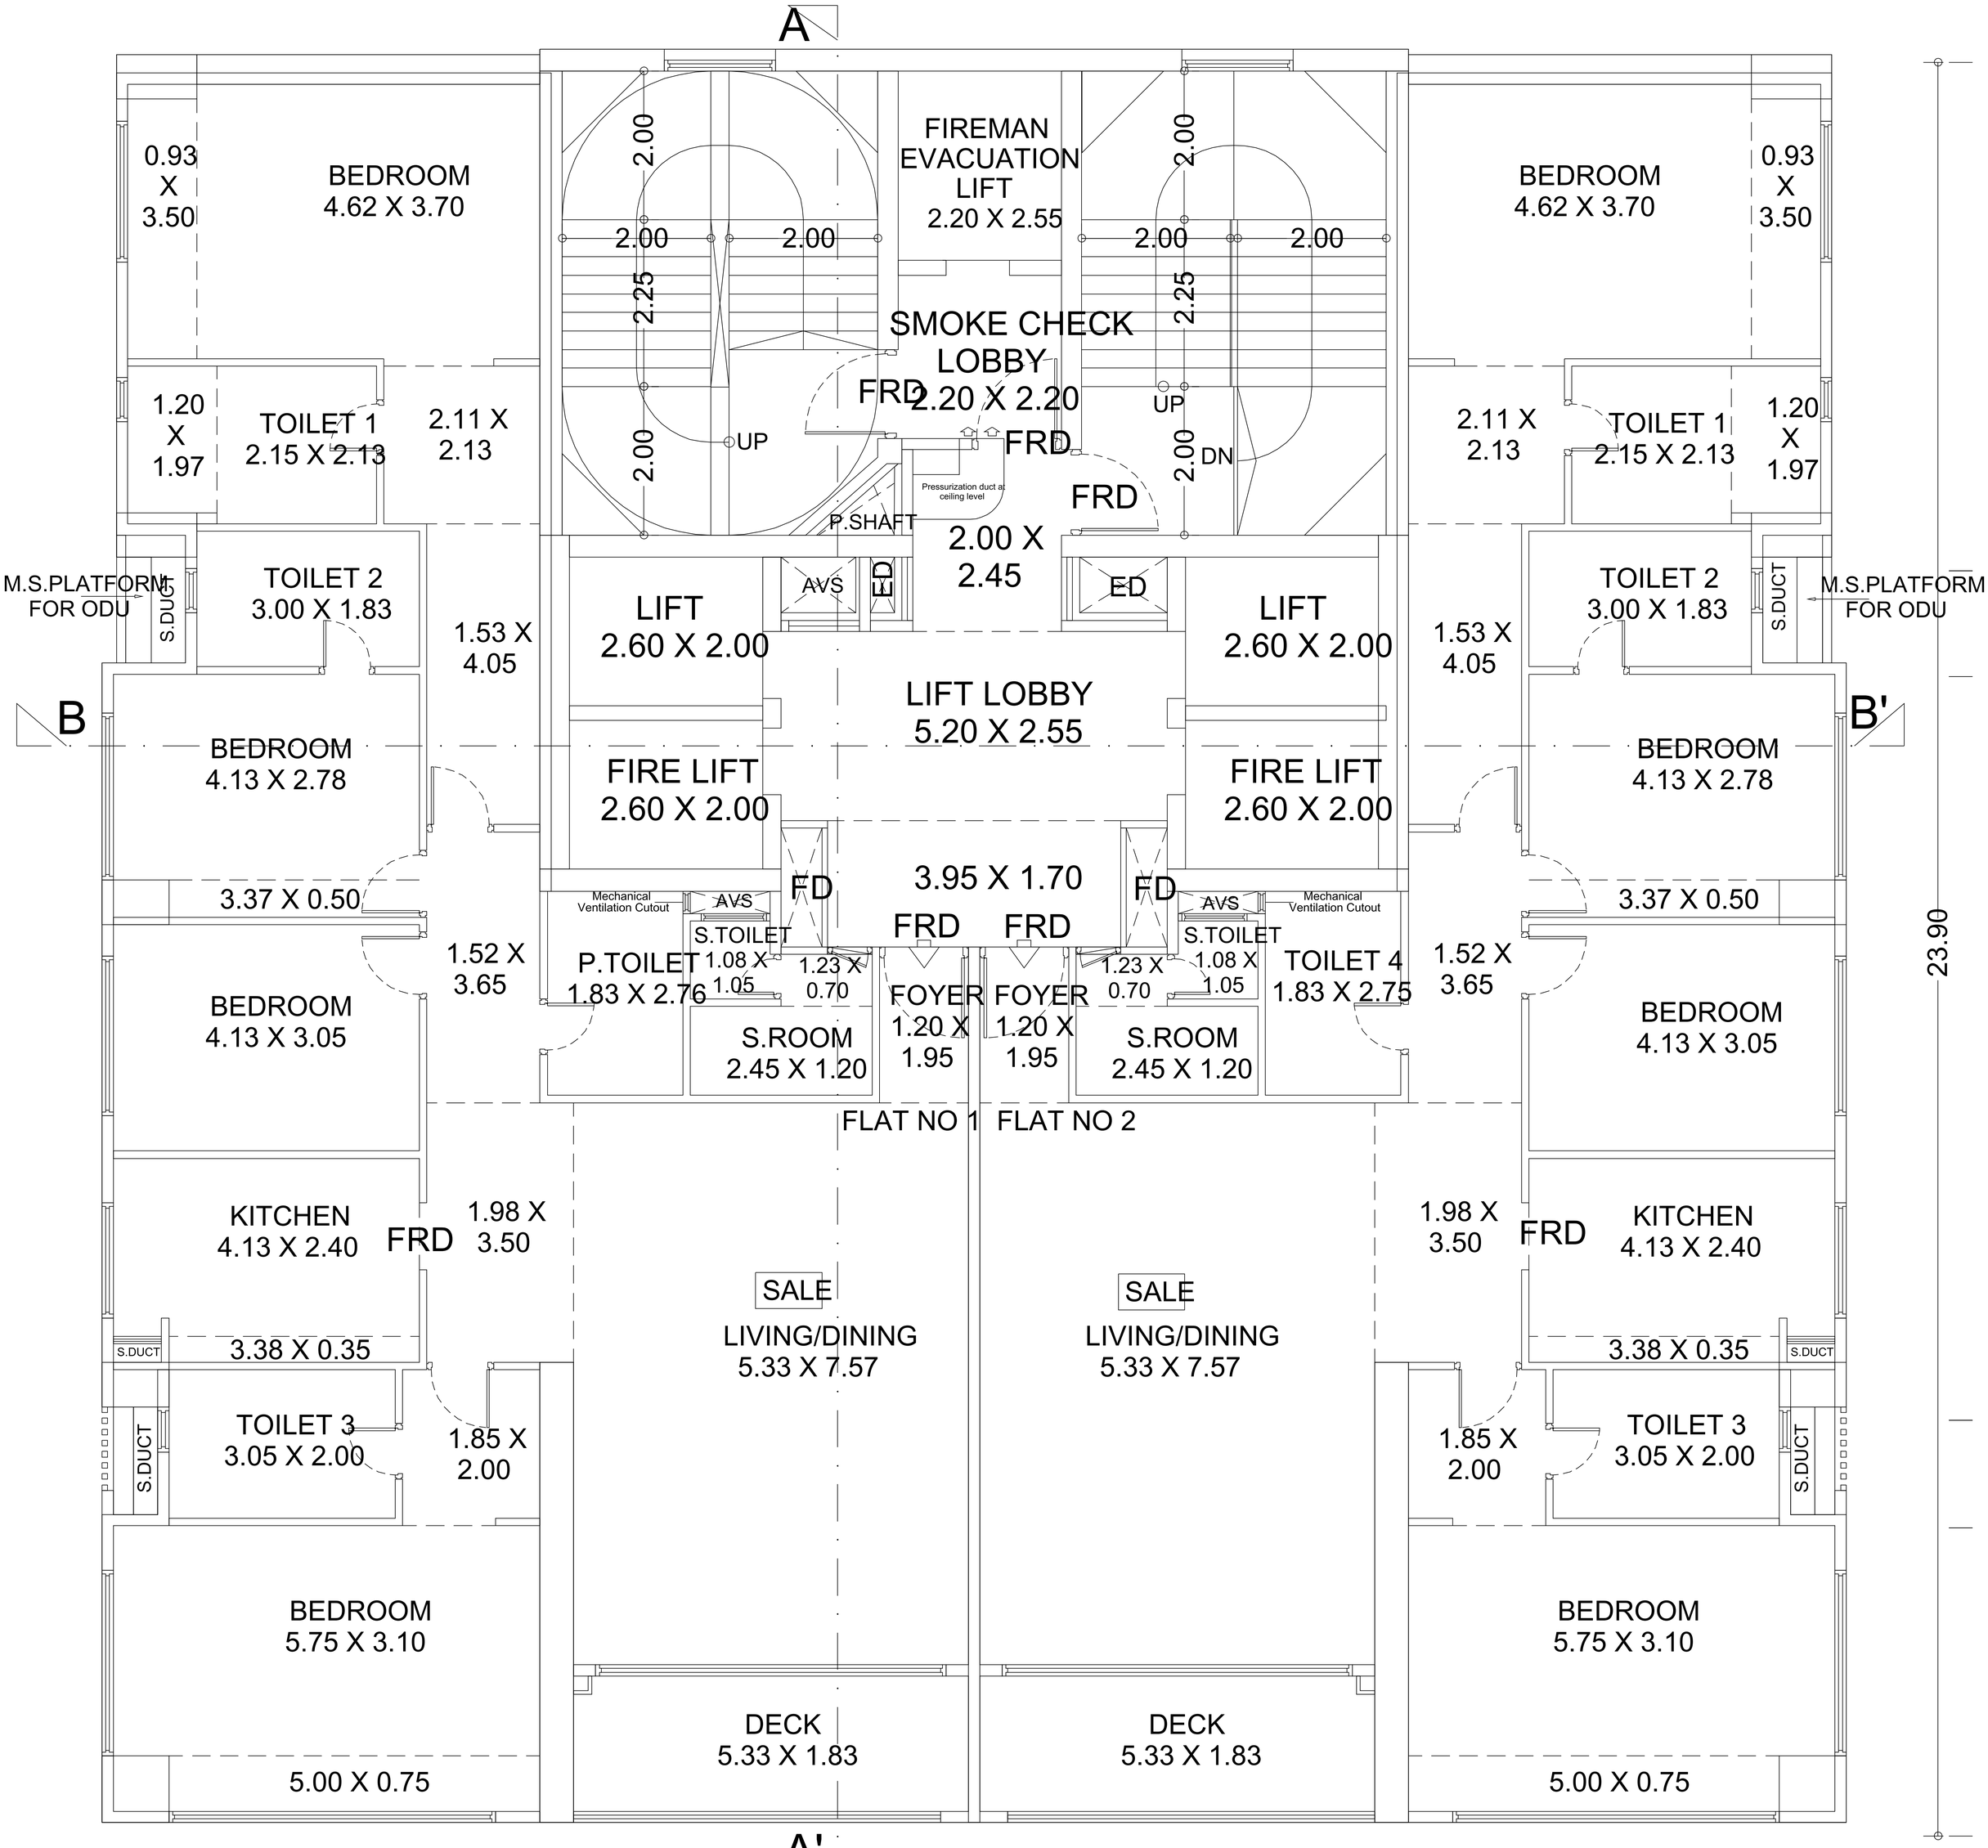


26TH TO 30TH,33RD & 34TH TYPICAL FLOOR PLAN

SCALE - 1:100

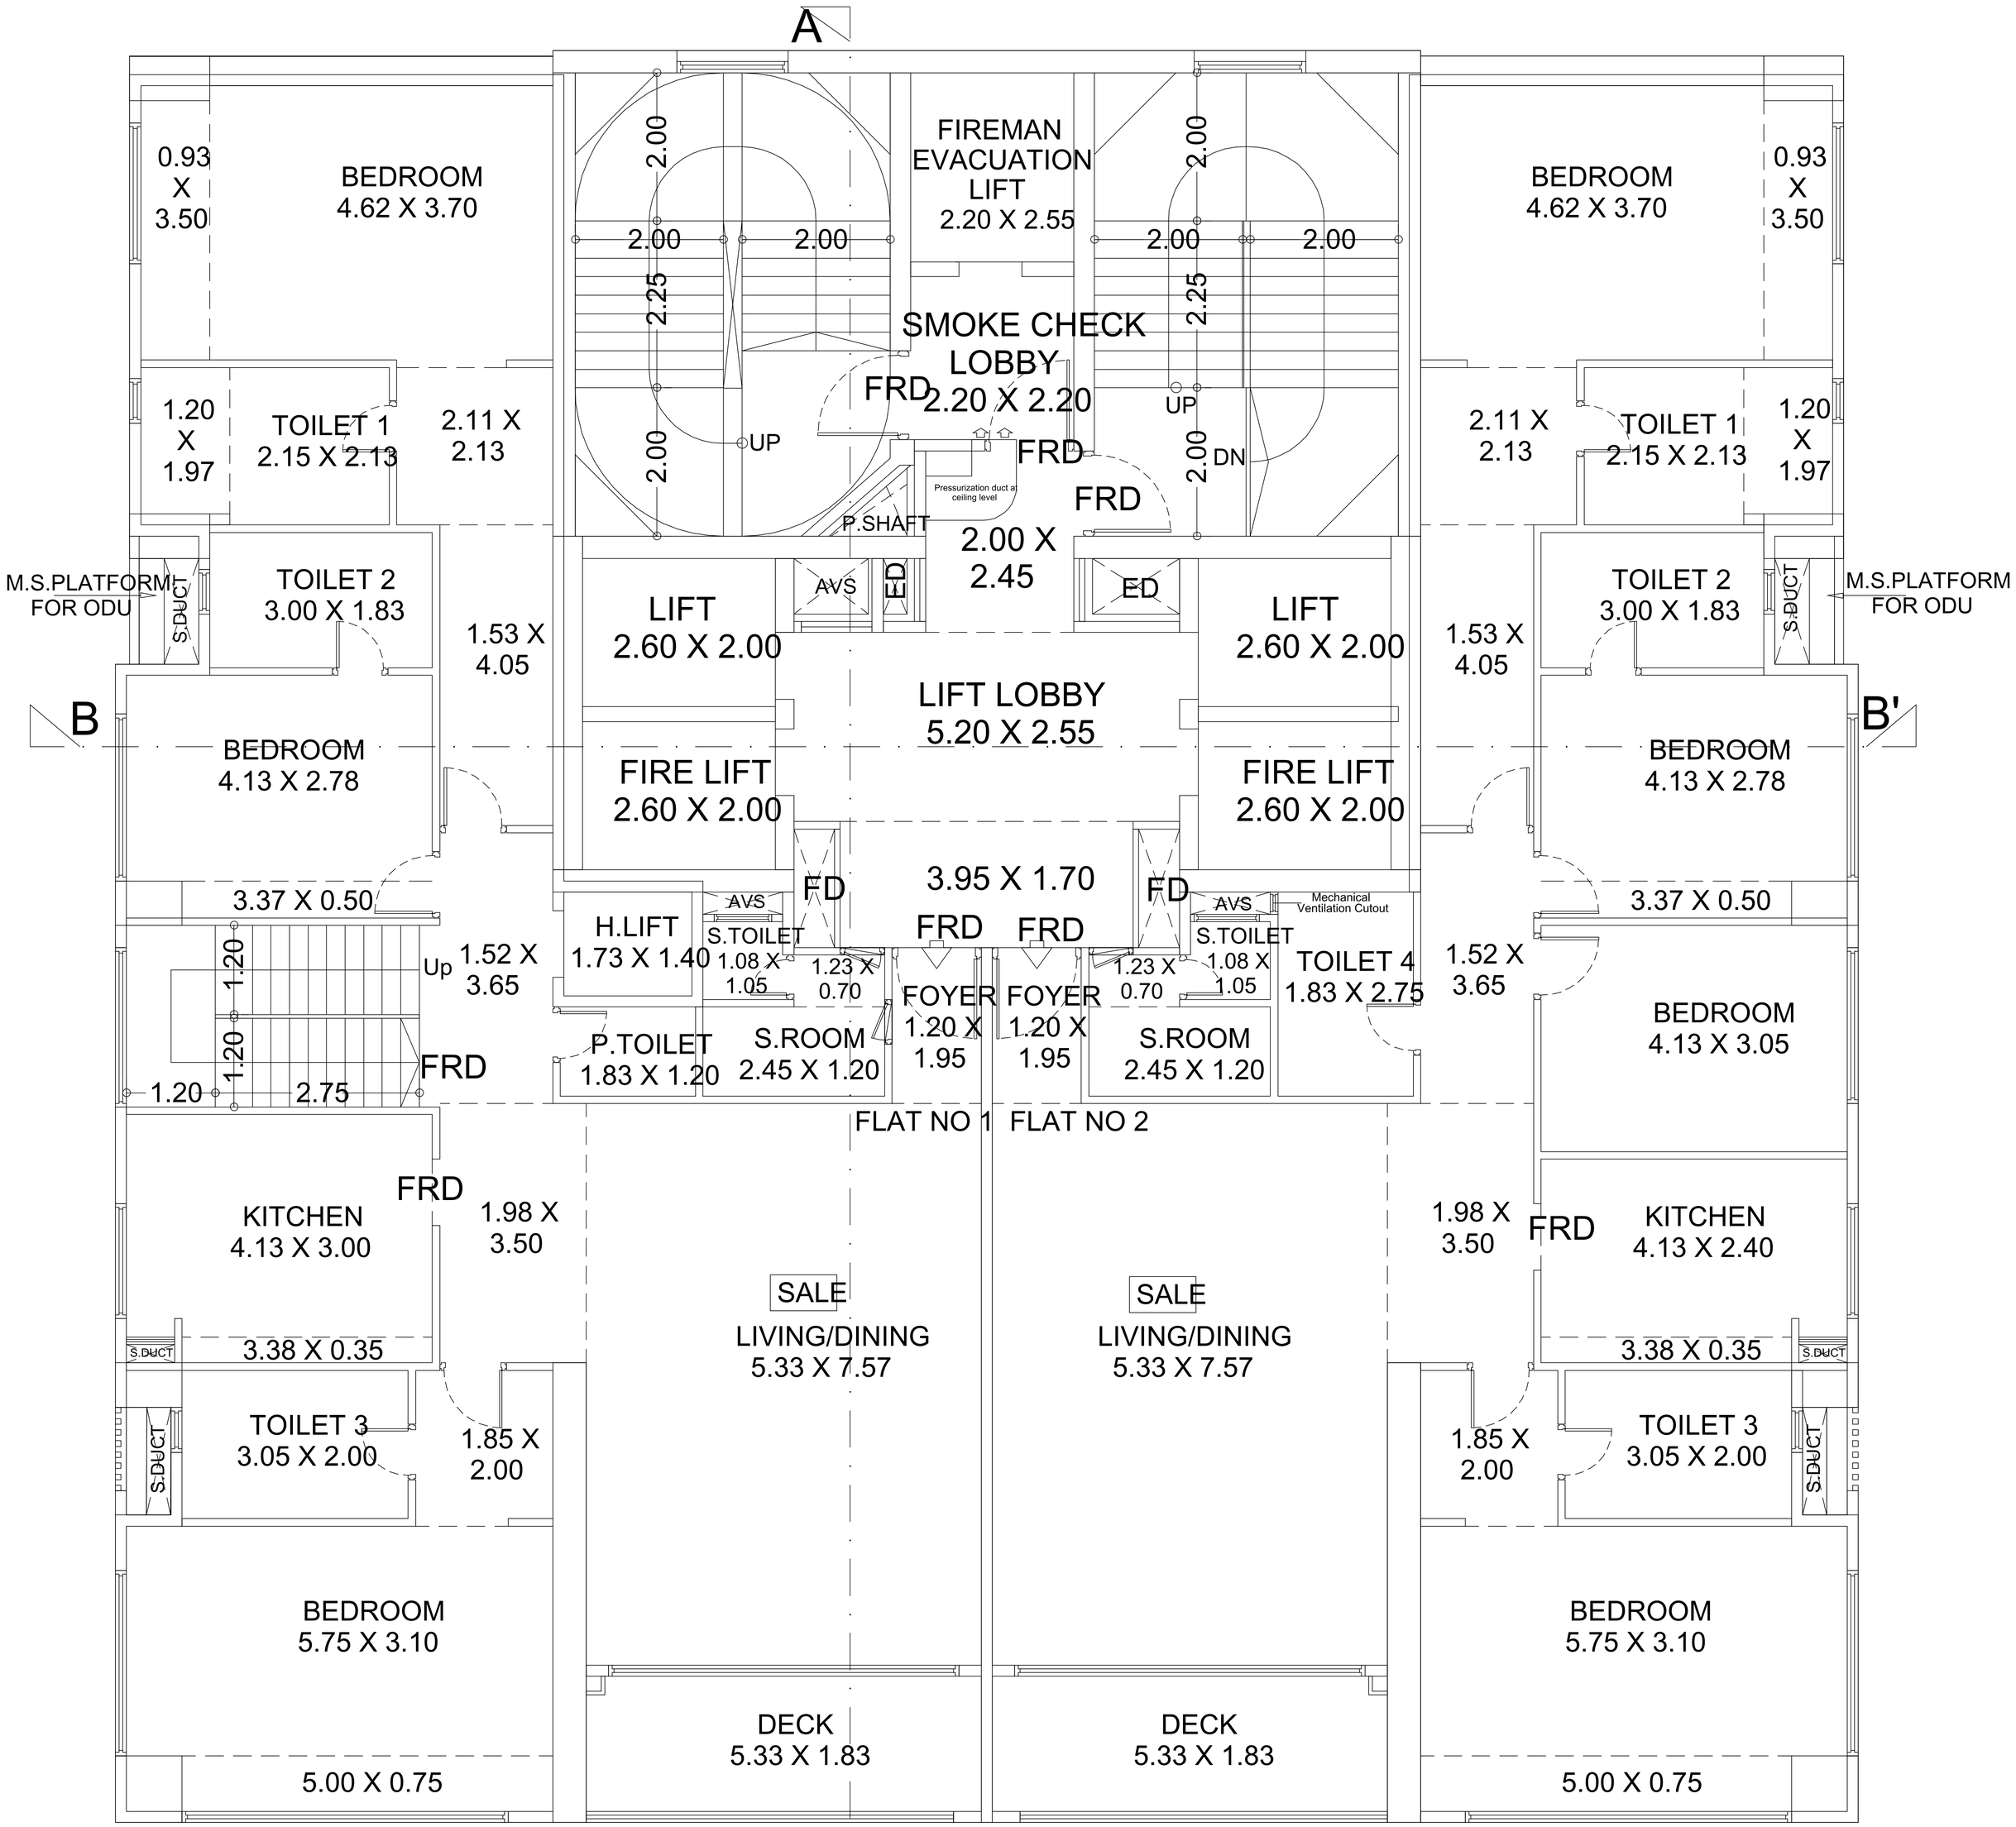

31ST (LOWER DUPLEX) FLOOR PLAN

SCALE - 1:100

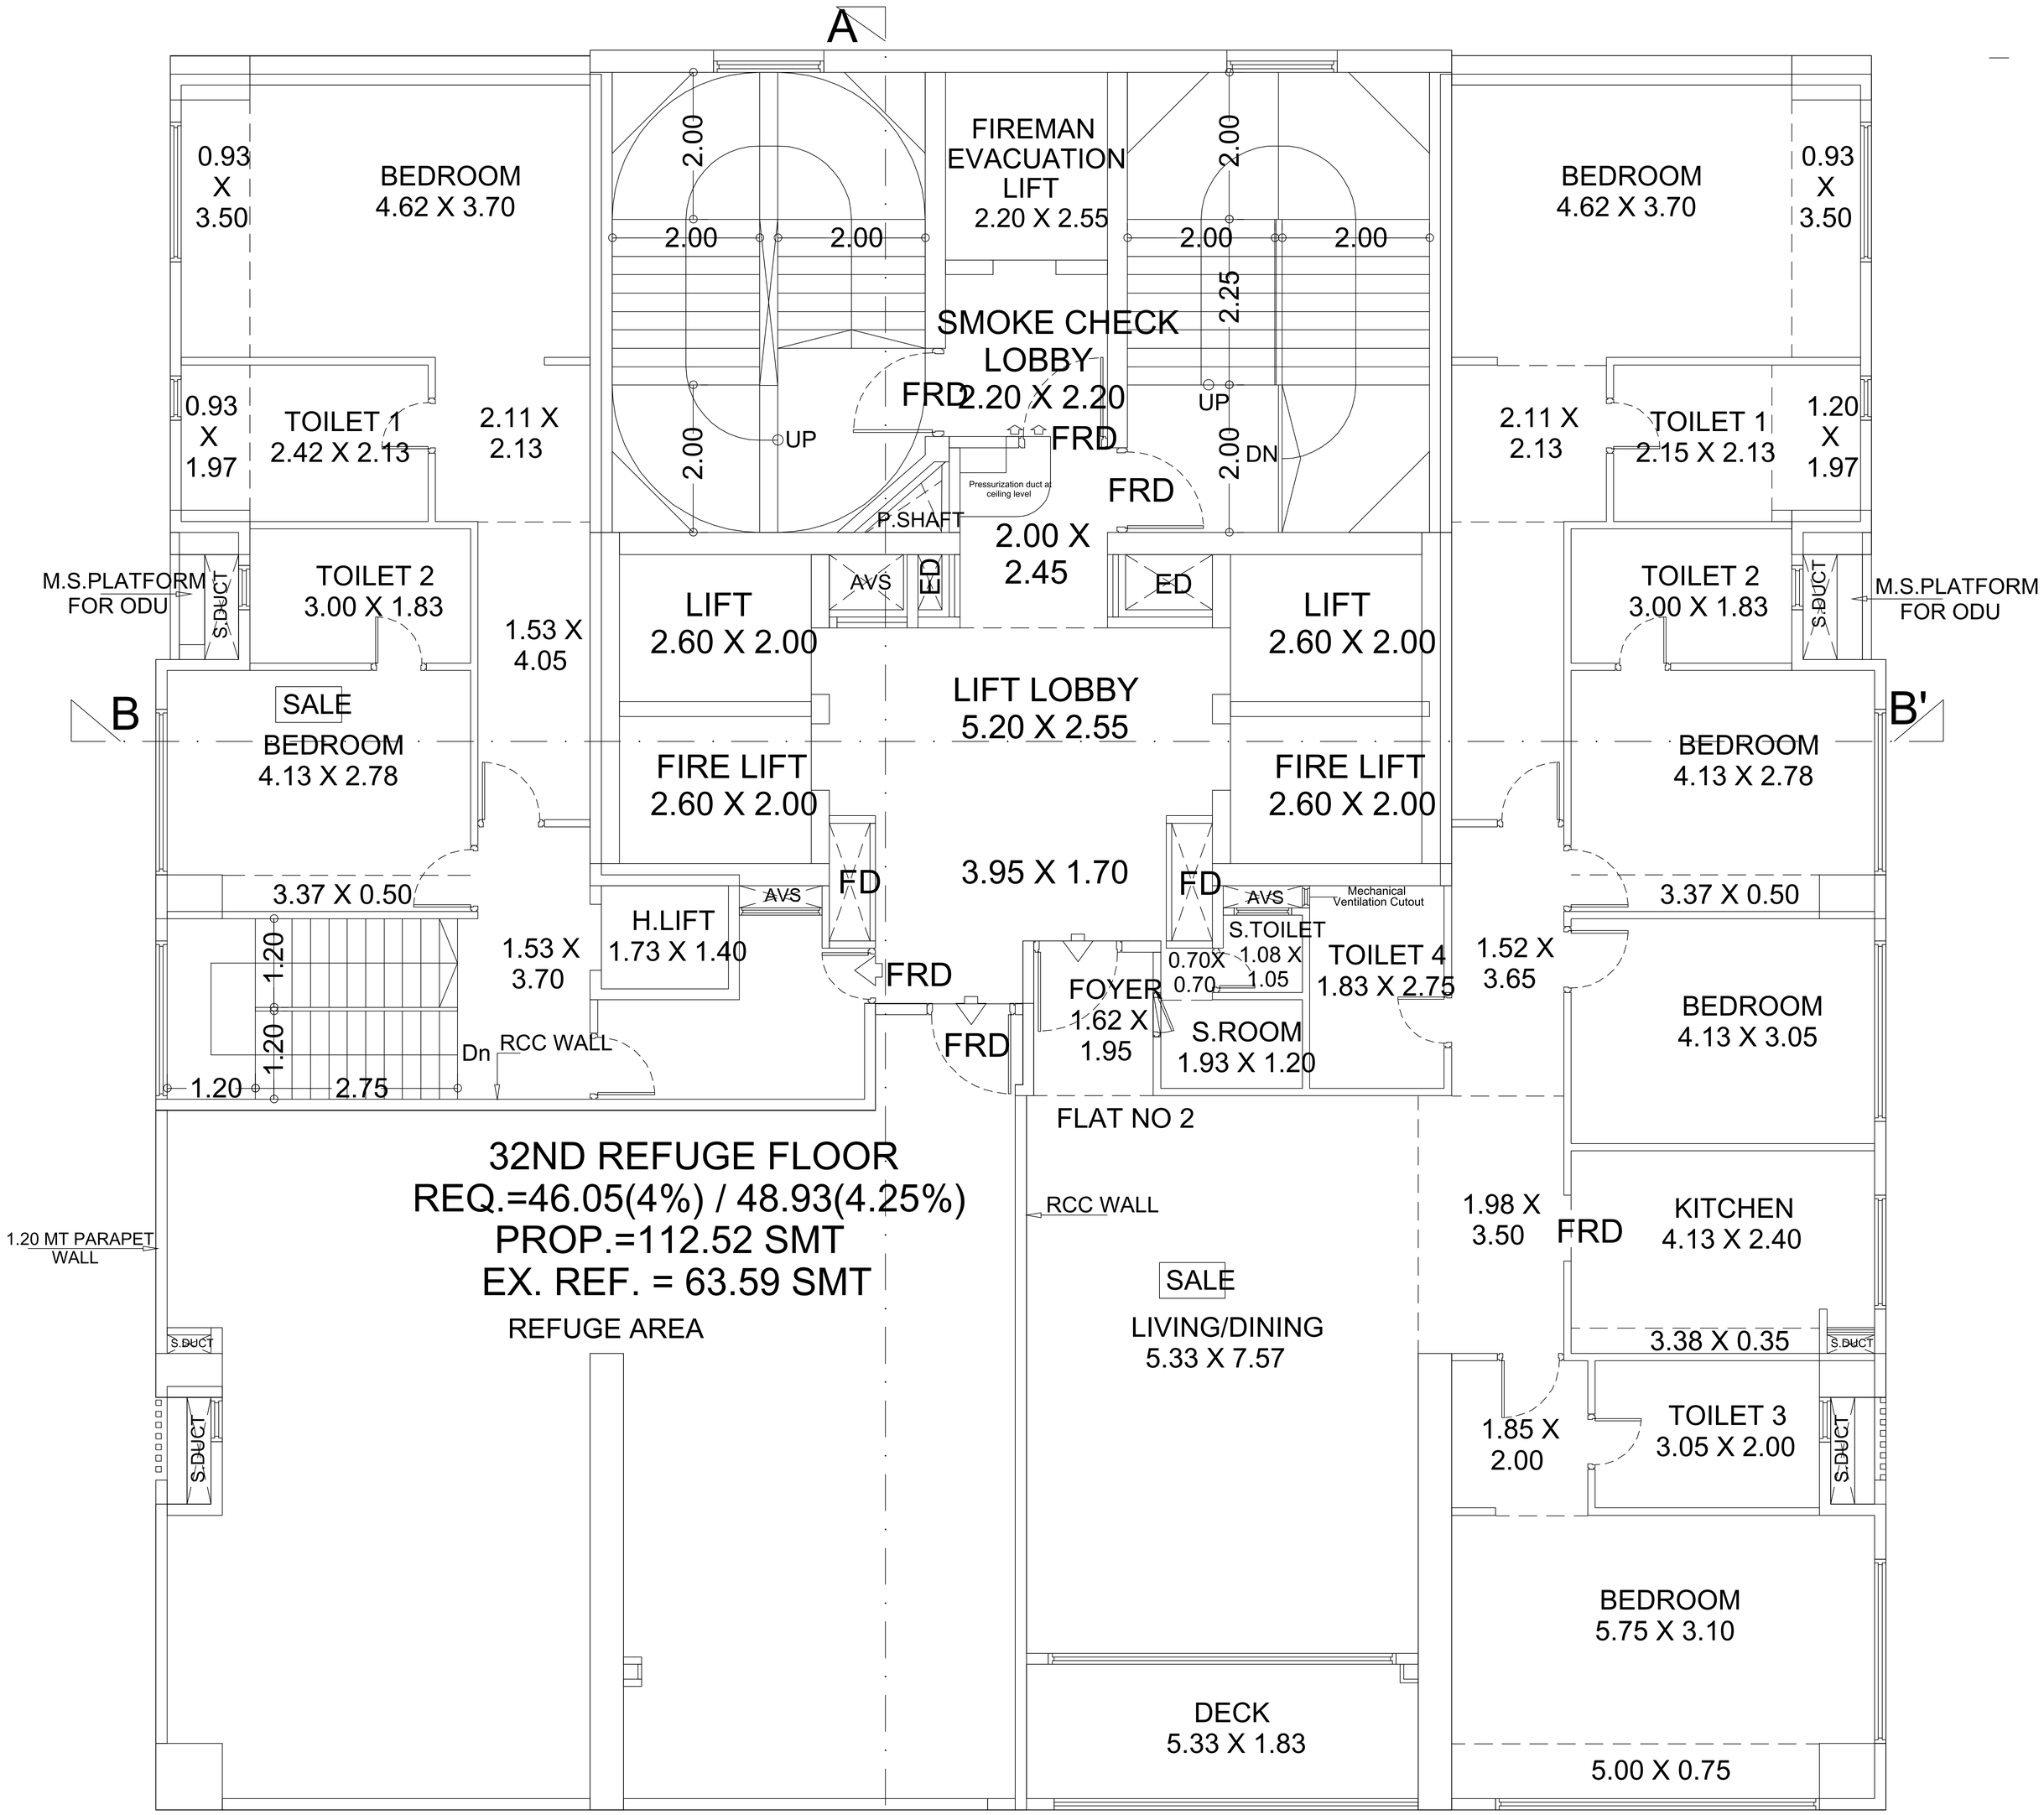

32ND (UPPER DUPLEX)REFUGE FLOOR PLAN

SCALE - 1:100