ADDITIONAL LOS

LOS15

SCALE :- 1:100

TOWER -10

TOWER -11

TOWER -12

TOWER -13

1.20 MTR.HT. PARAPET WALL

LEISURE POOL

25M LAP POOL

KIDS POOL

JACUZZI

POOL DECK

WATER PLAY

PA

F'

G

H'

S'

FITNESS CENTER
8.95 x 6.22

FITNESS CENTER
(6.20 + 1.47) / 2 x 6.09

HER TOILET
5.24 x 2.63

HIS TOILET
5.24 x 2.28


LOBBY AREA
4.24 x 3.36 Avg


LIFT
2.23 x 2.05

DN UP

- 3.85 LVL

1ST PODIUM FLOOR PLAN

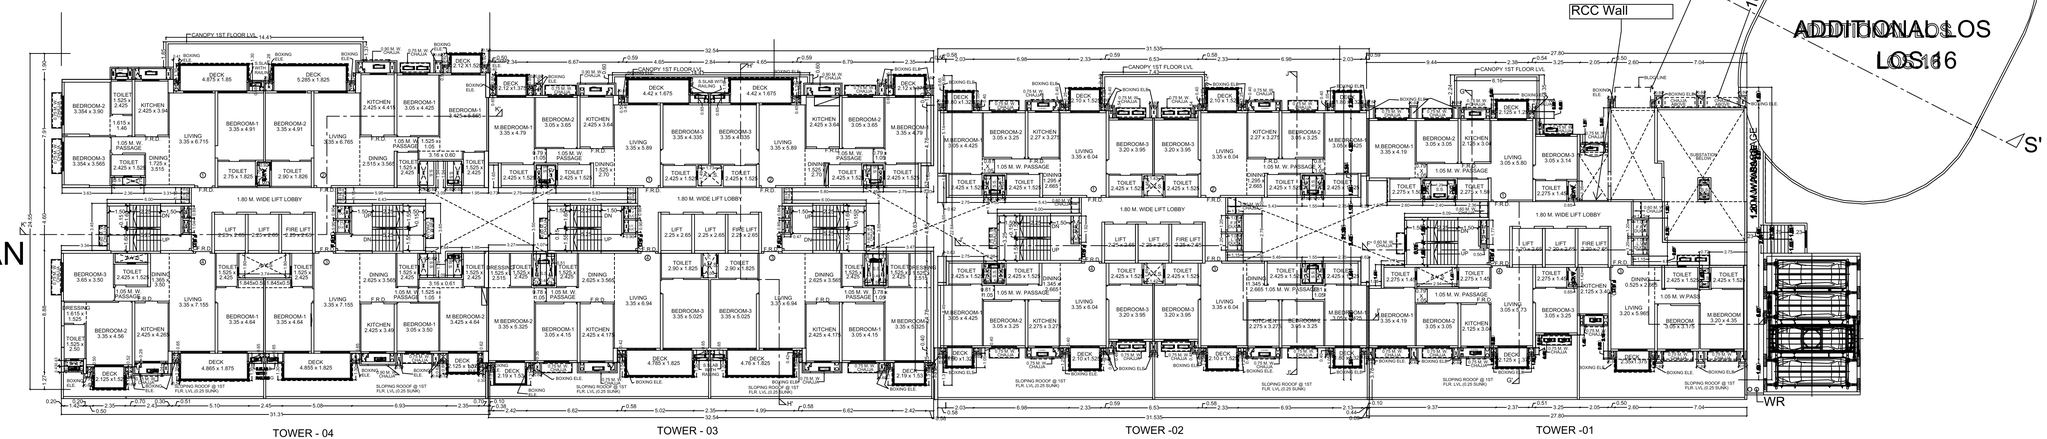


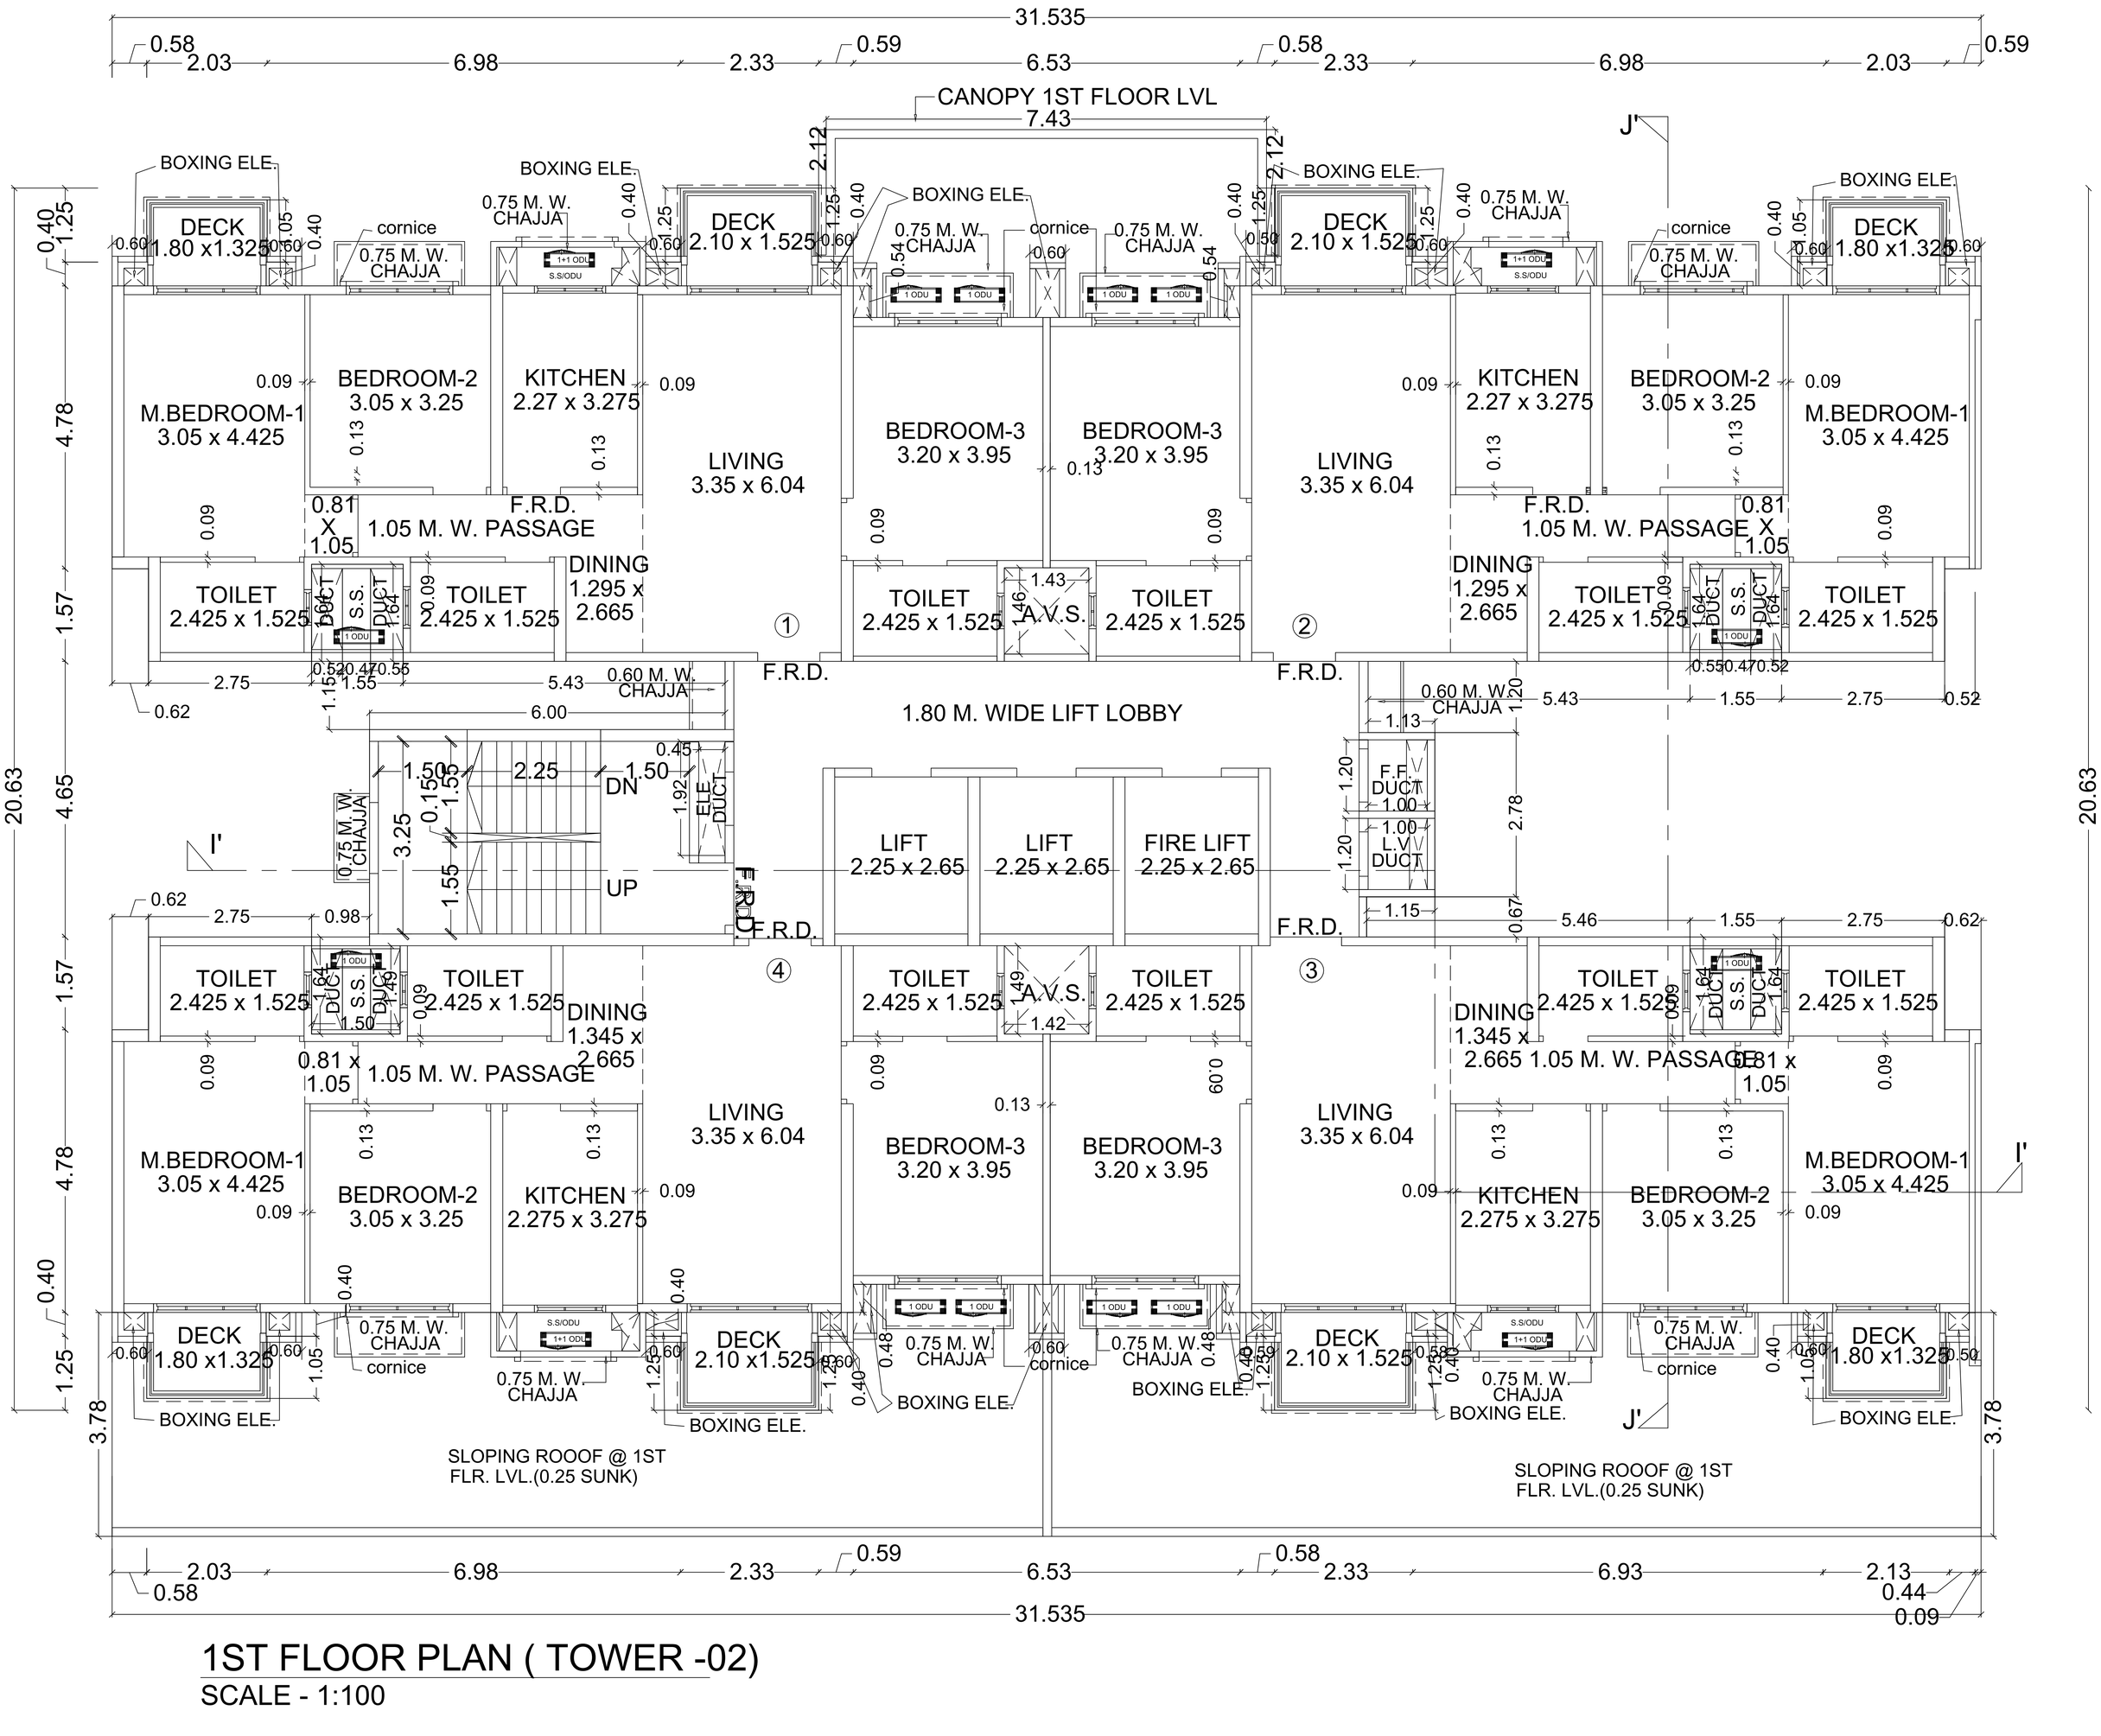

1ST FLOOR PLAN (TOWER -02)


SCALE - 1:100

SCALE - 1:100

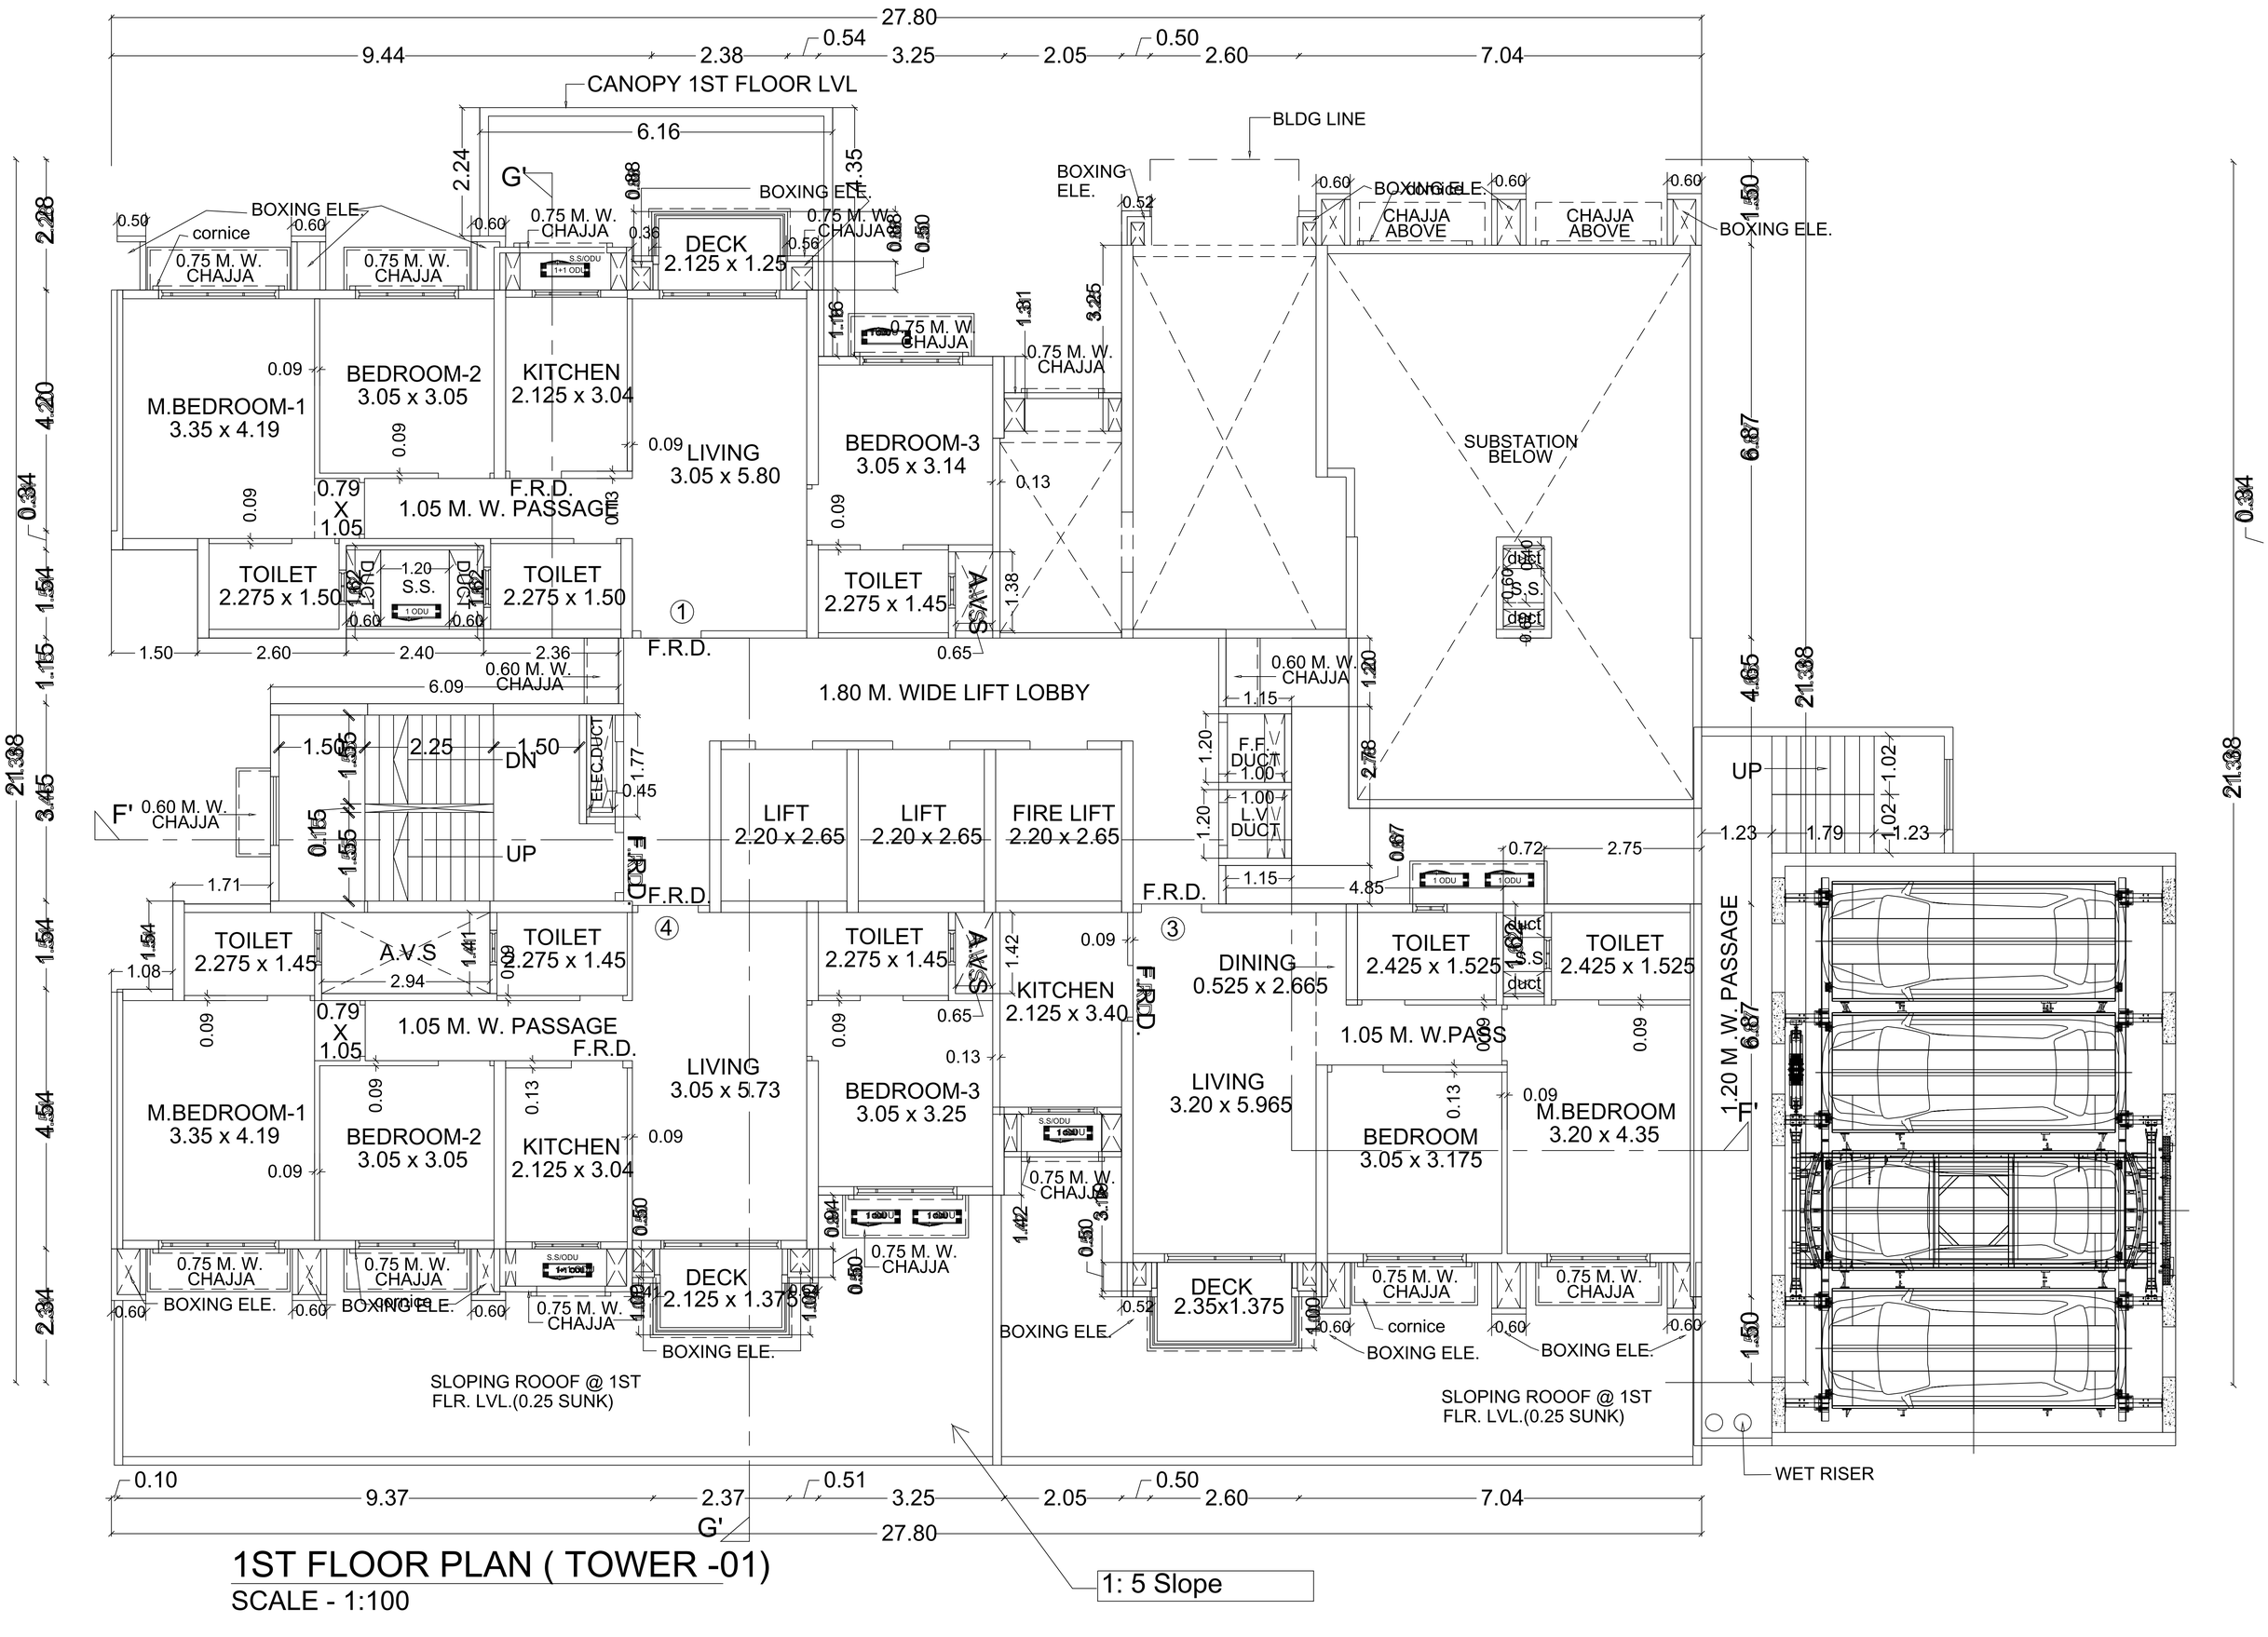

1ST FLOOR PLAN (TOWER -01)


SCALE - 1:100

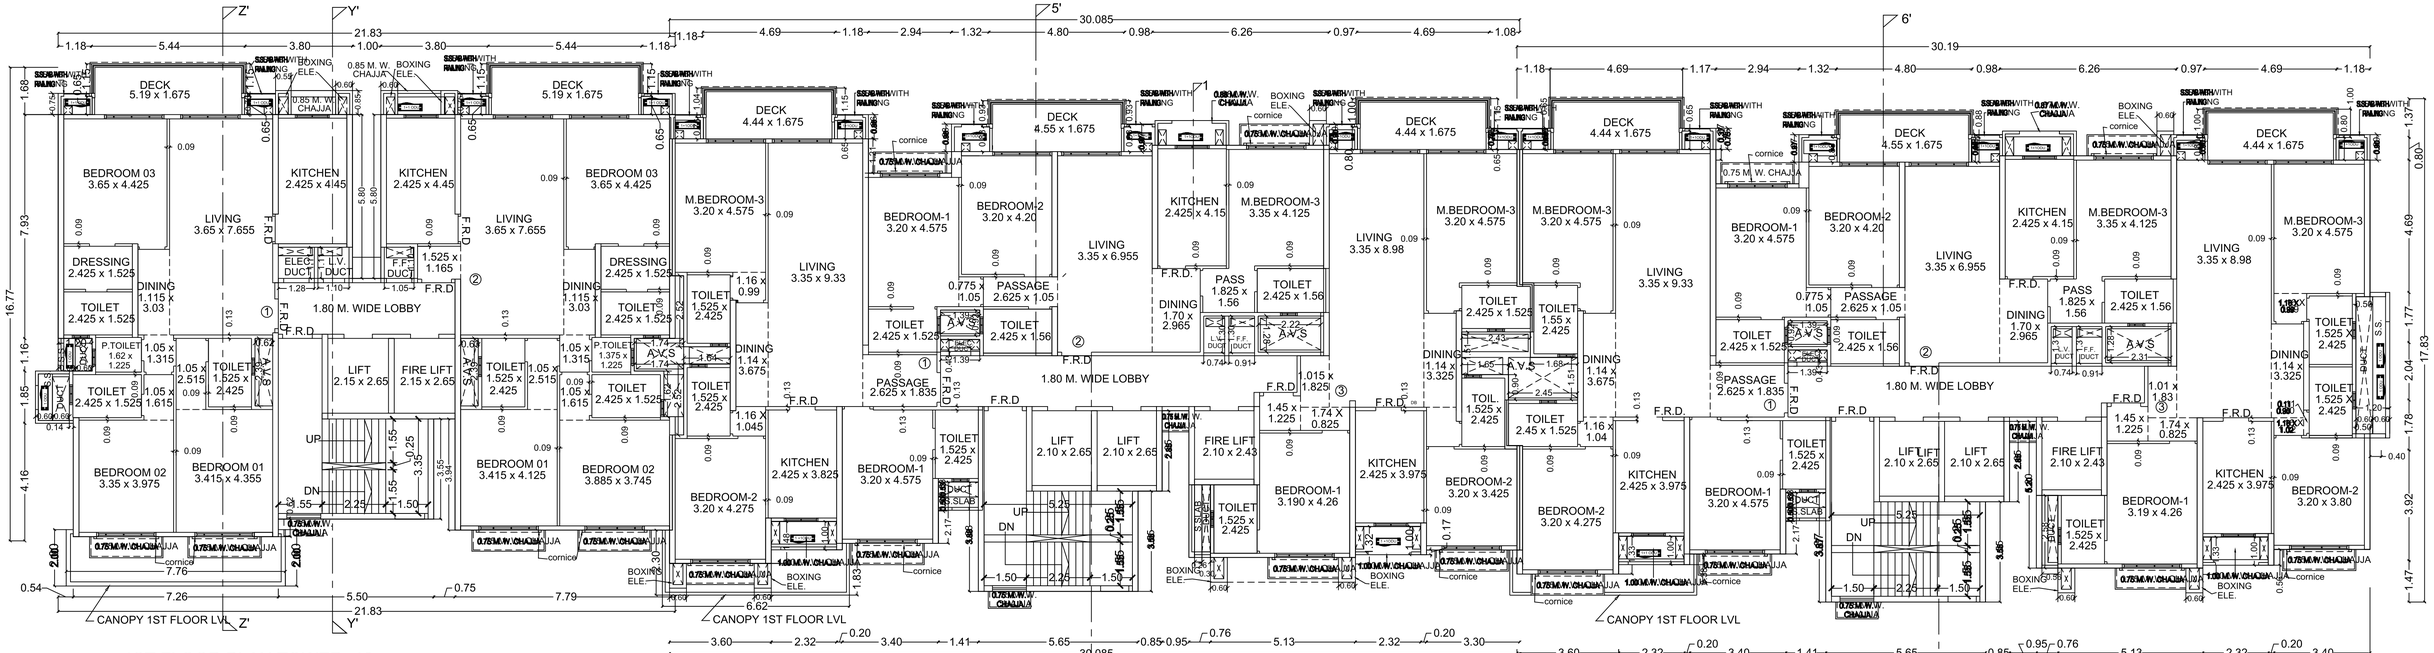

1ST FLOOR PLAN TOWER -12
SCALE - 1:100

1ST FLOOR PLAN TOWER -13
SCALE - 1:100


1ST FLOOR PLAN TOWER -14
SCALE - 1:100

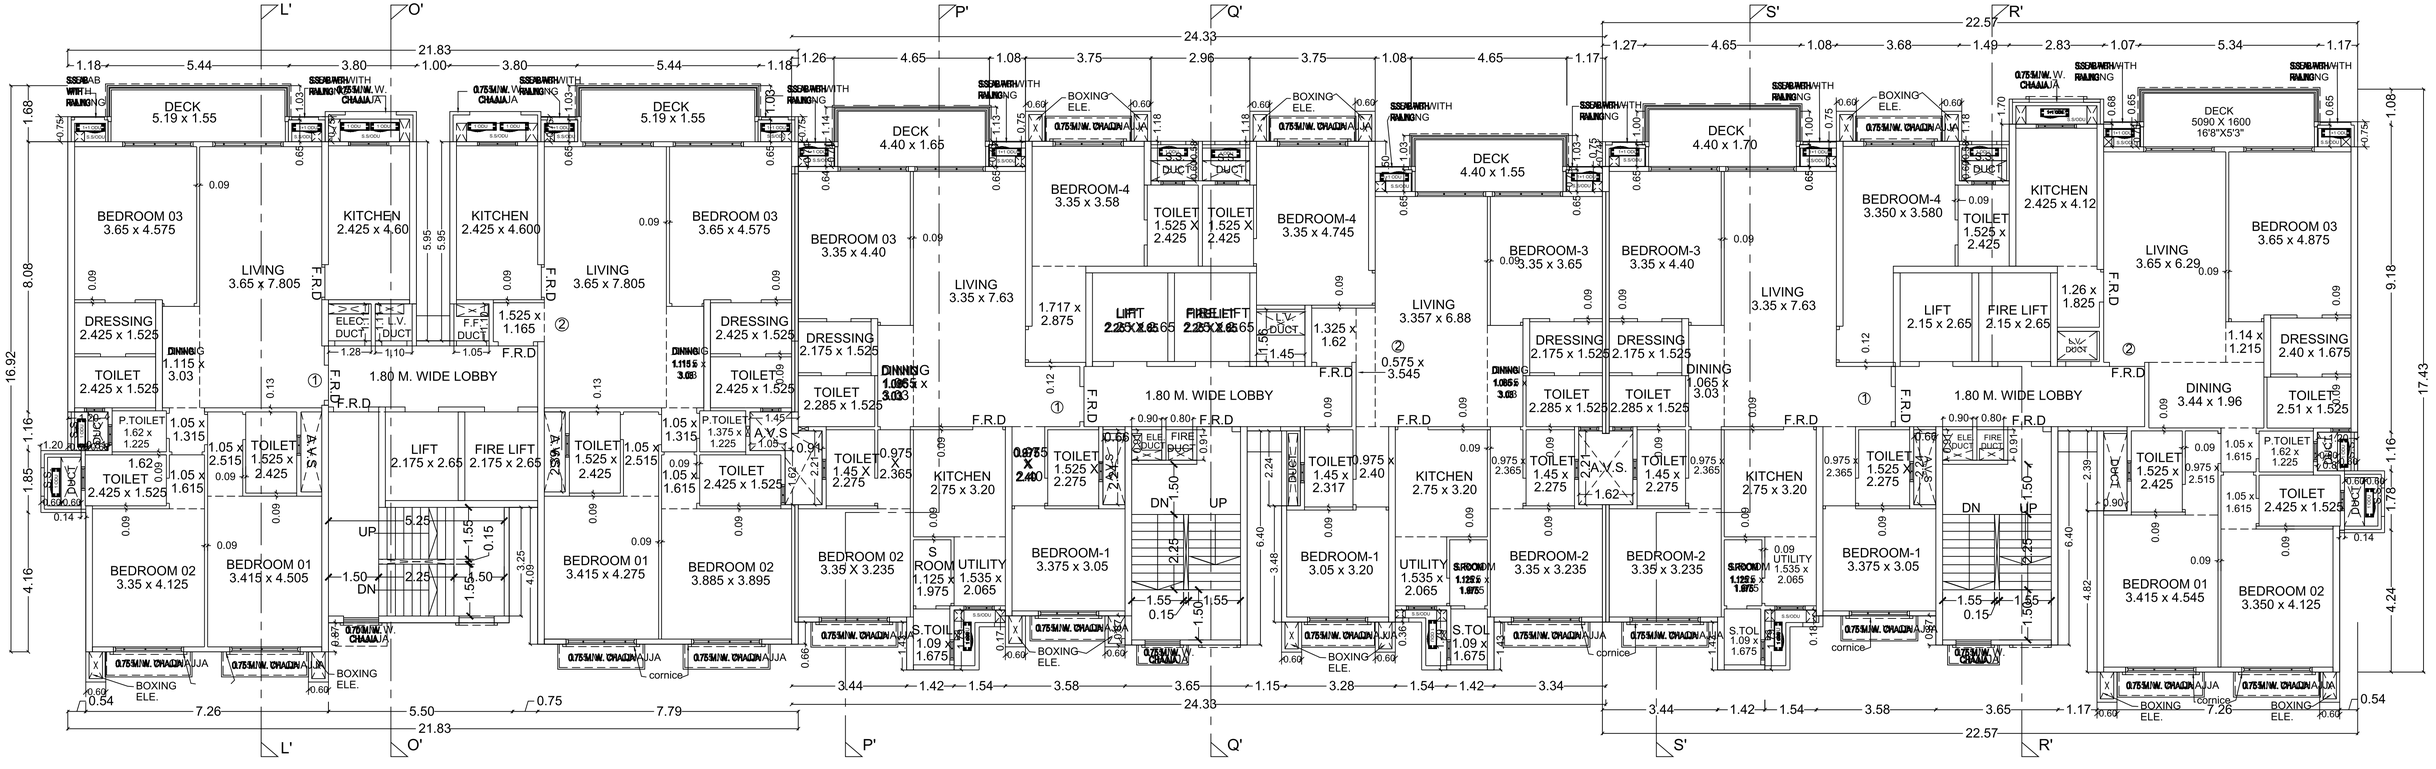

1ST FLOOR PLAN TOWER -06
SCALE - 1:100


1ST FLOOR PLAN TOWER -07
SCALE - 1:100

1ST FLOOR PLAN TOWER -08
SCALE - 1:100

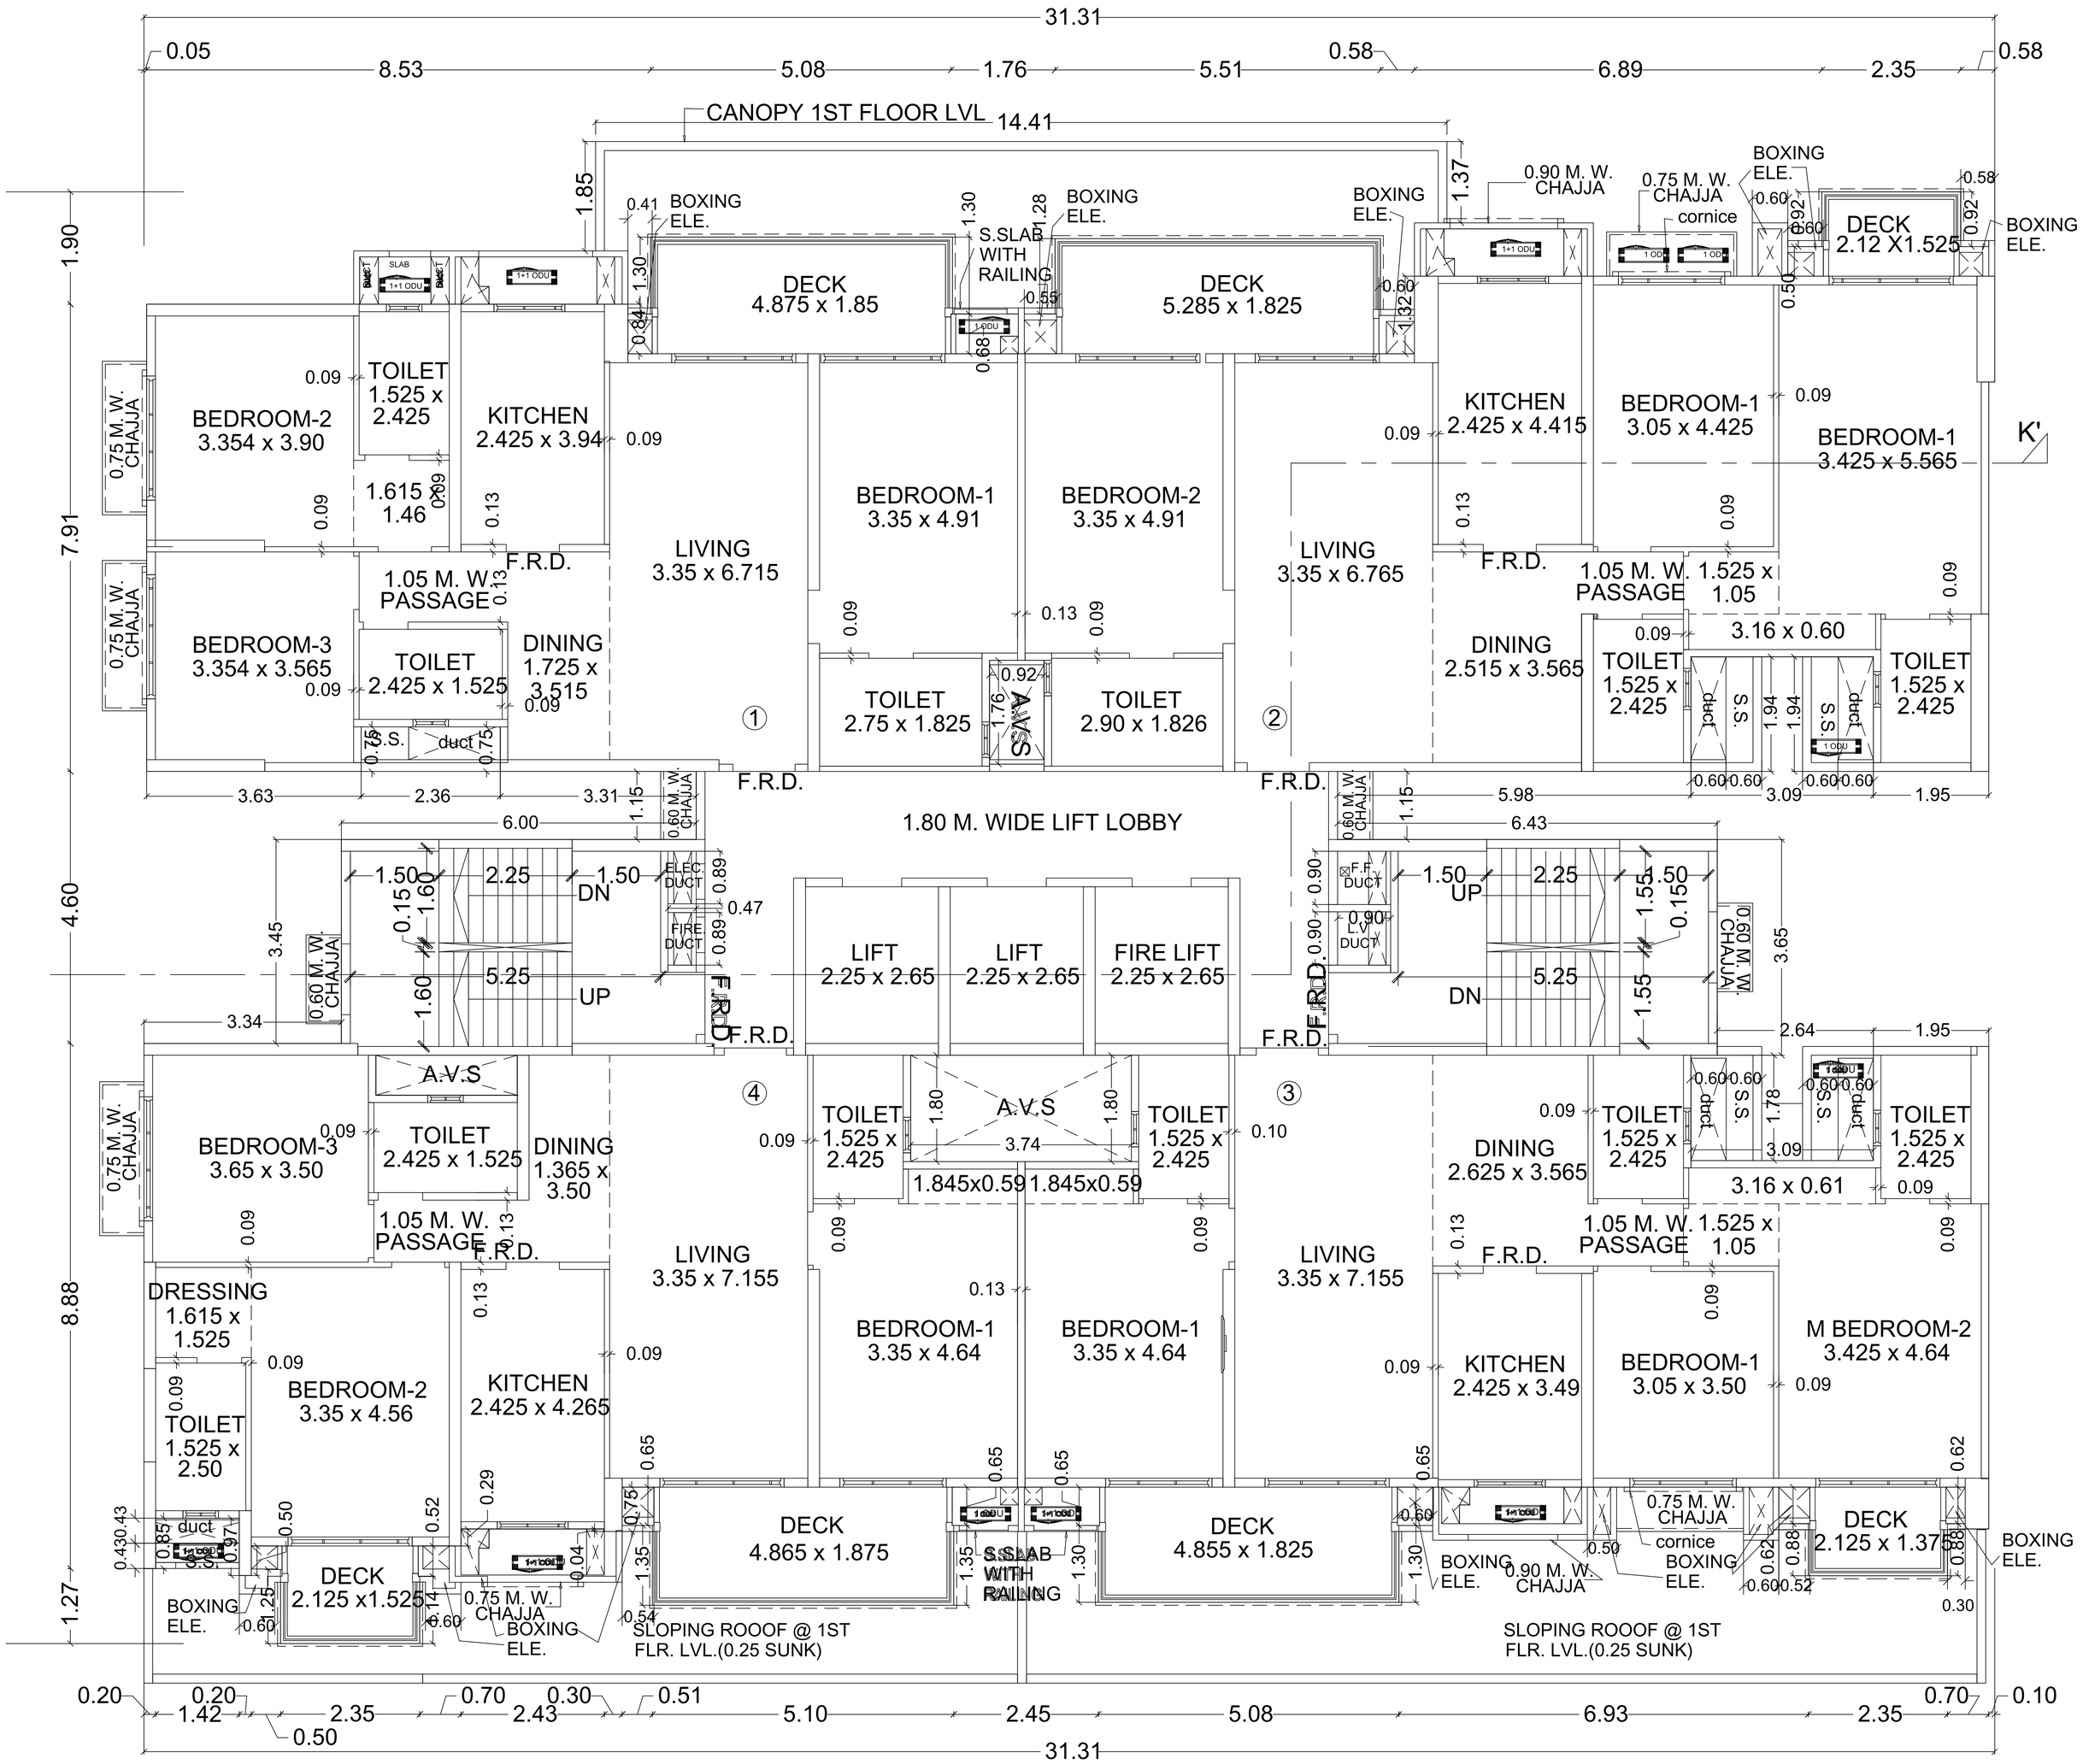

1ST FLOOR PLAN TOWER - 04


SCALE - 1:100

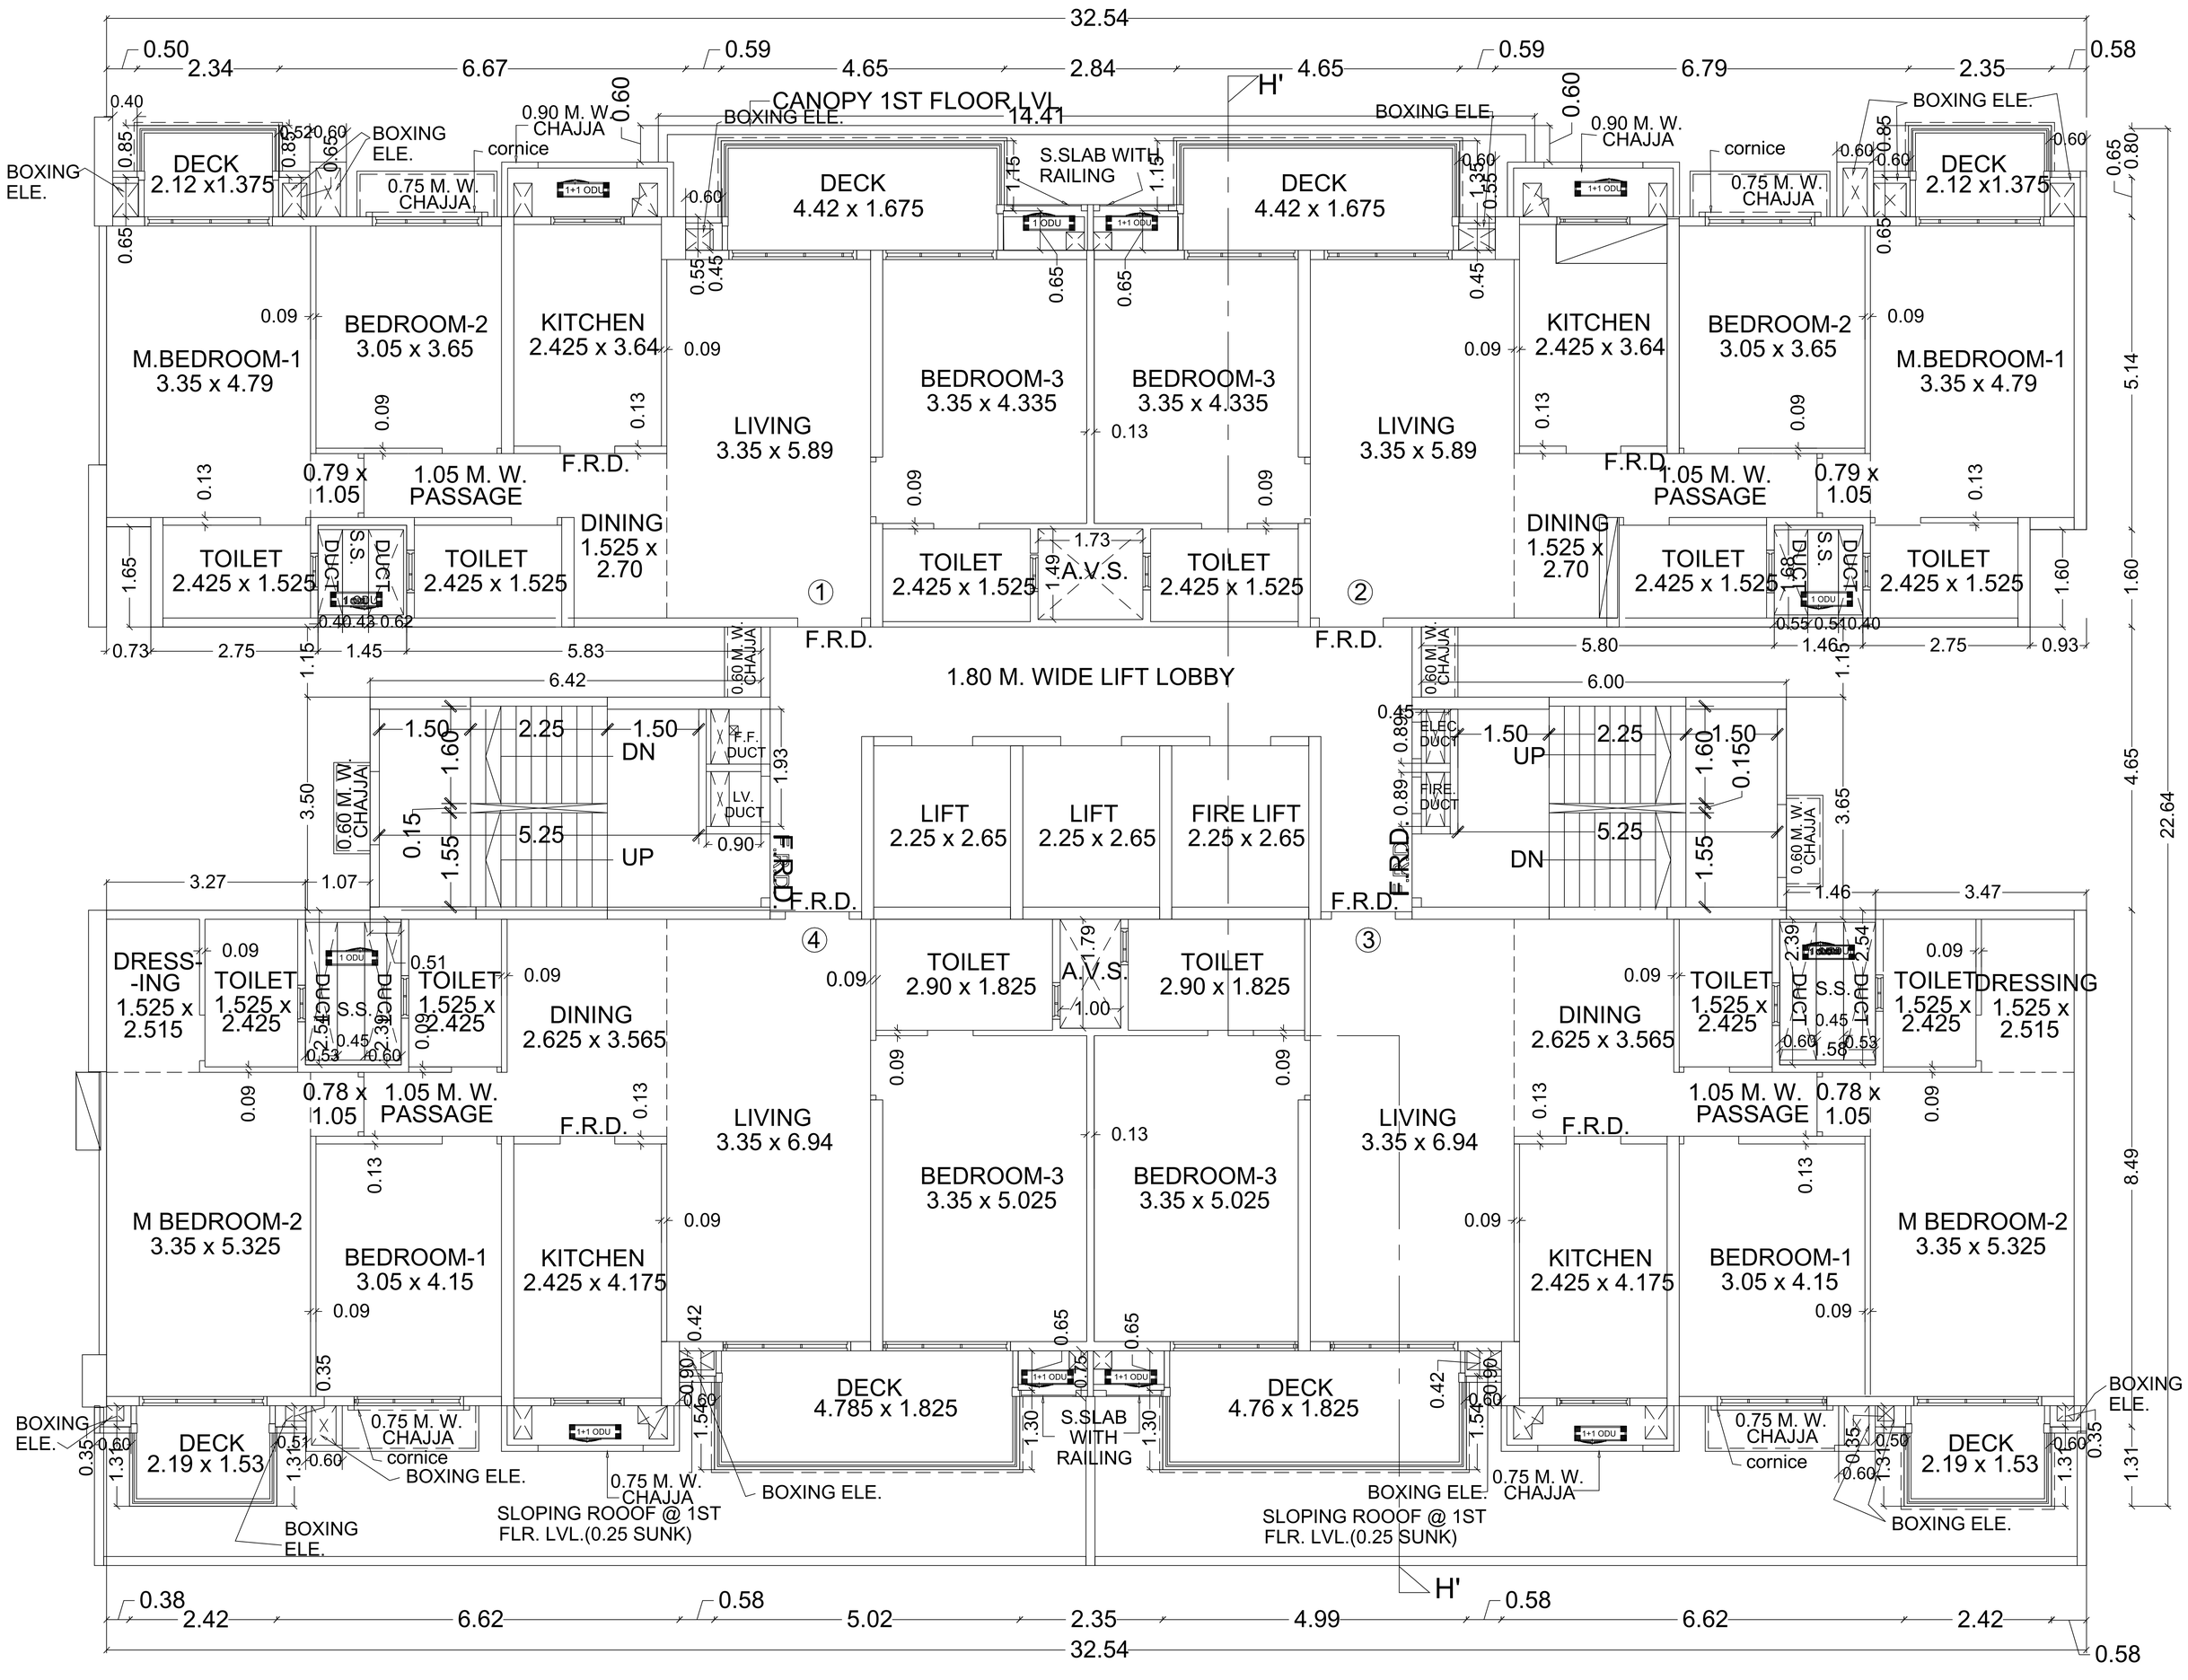

1ST FLOOR PLAN TOWER - 03


SCALE - 1:100

SCALE - 1:100

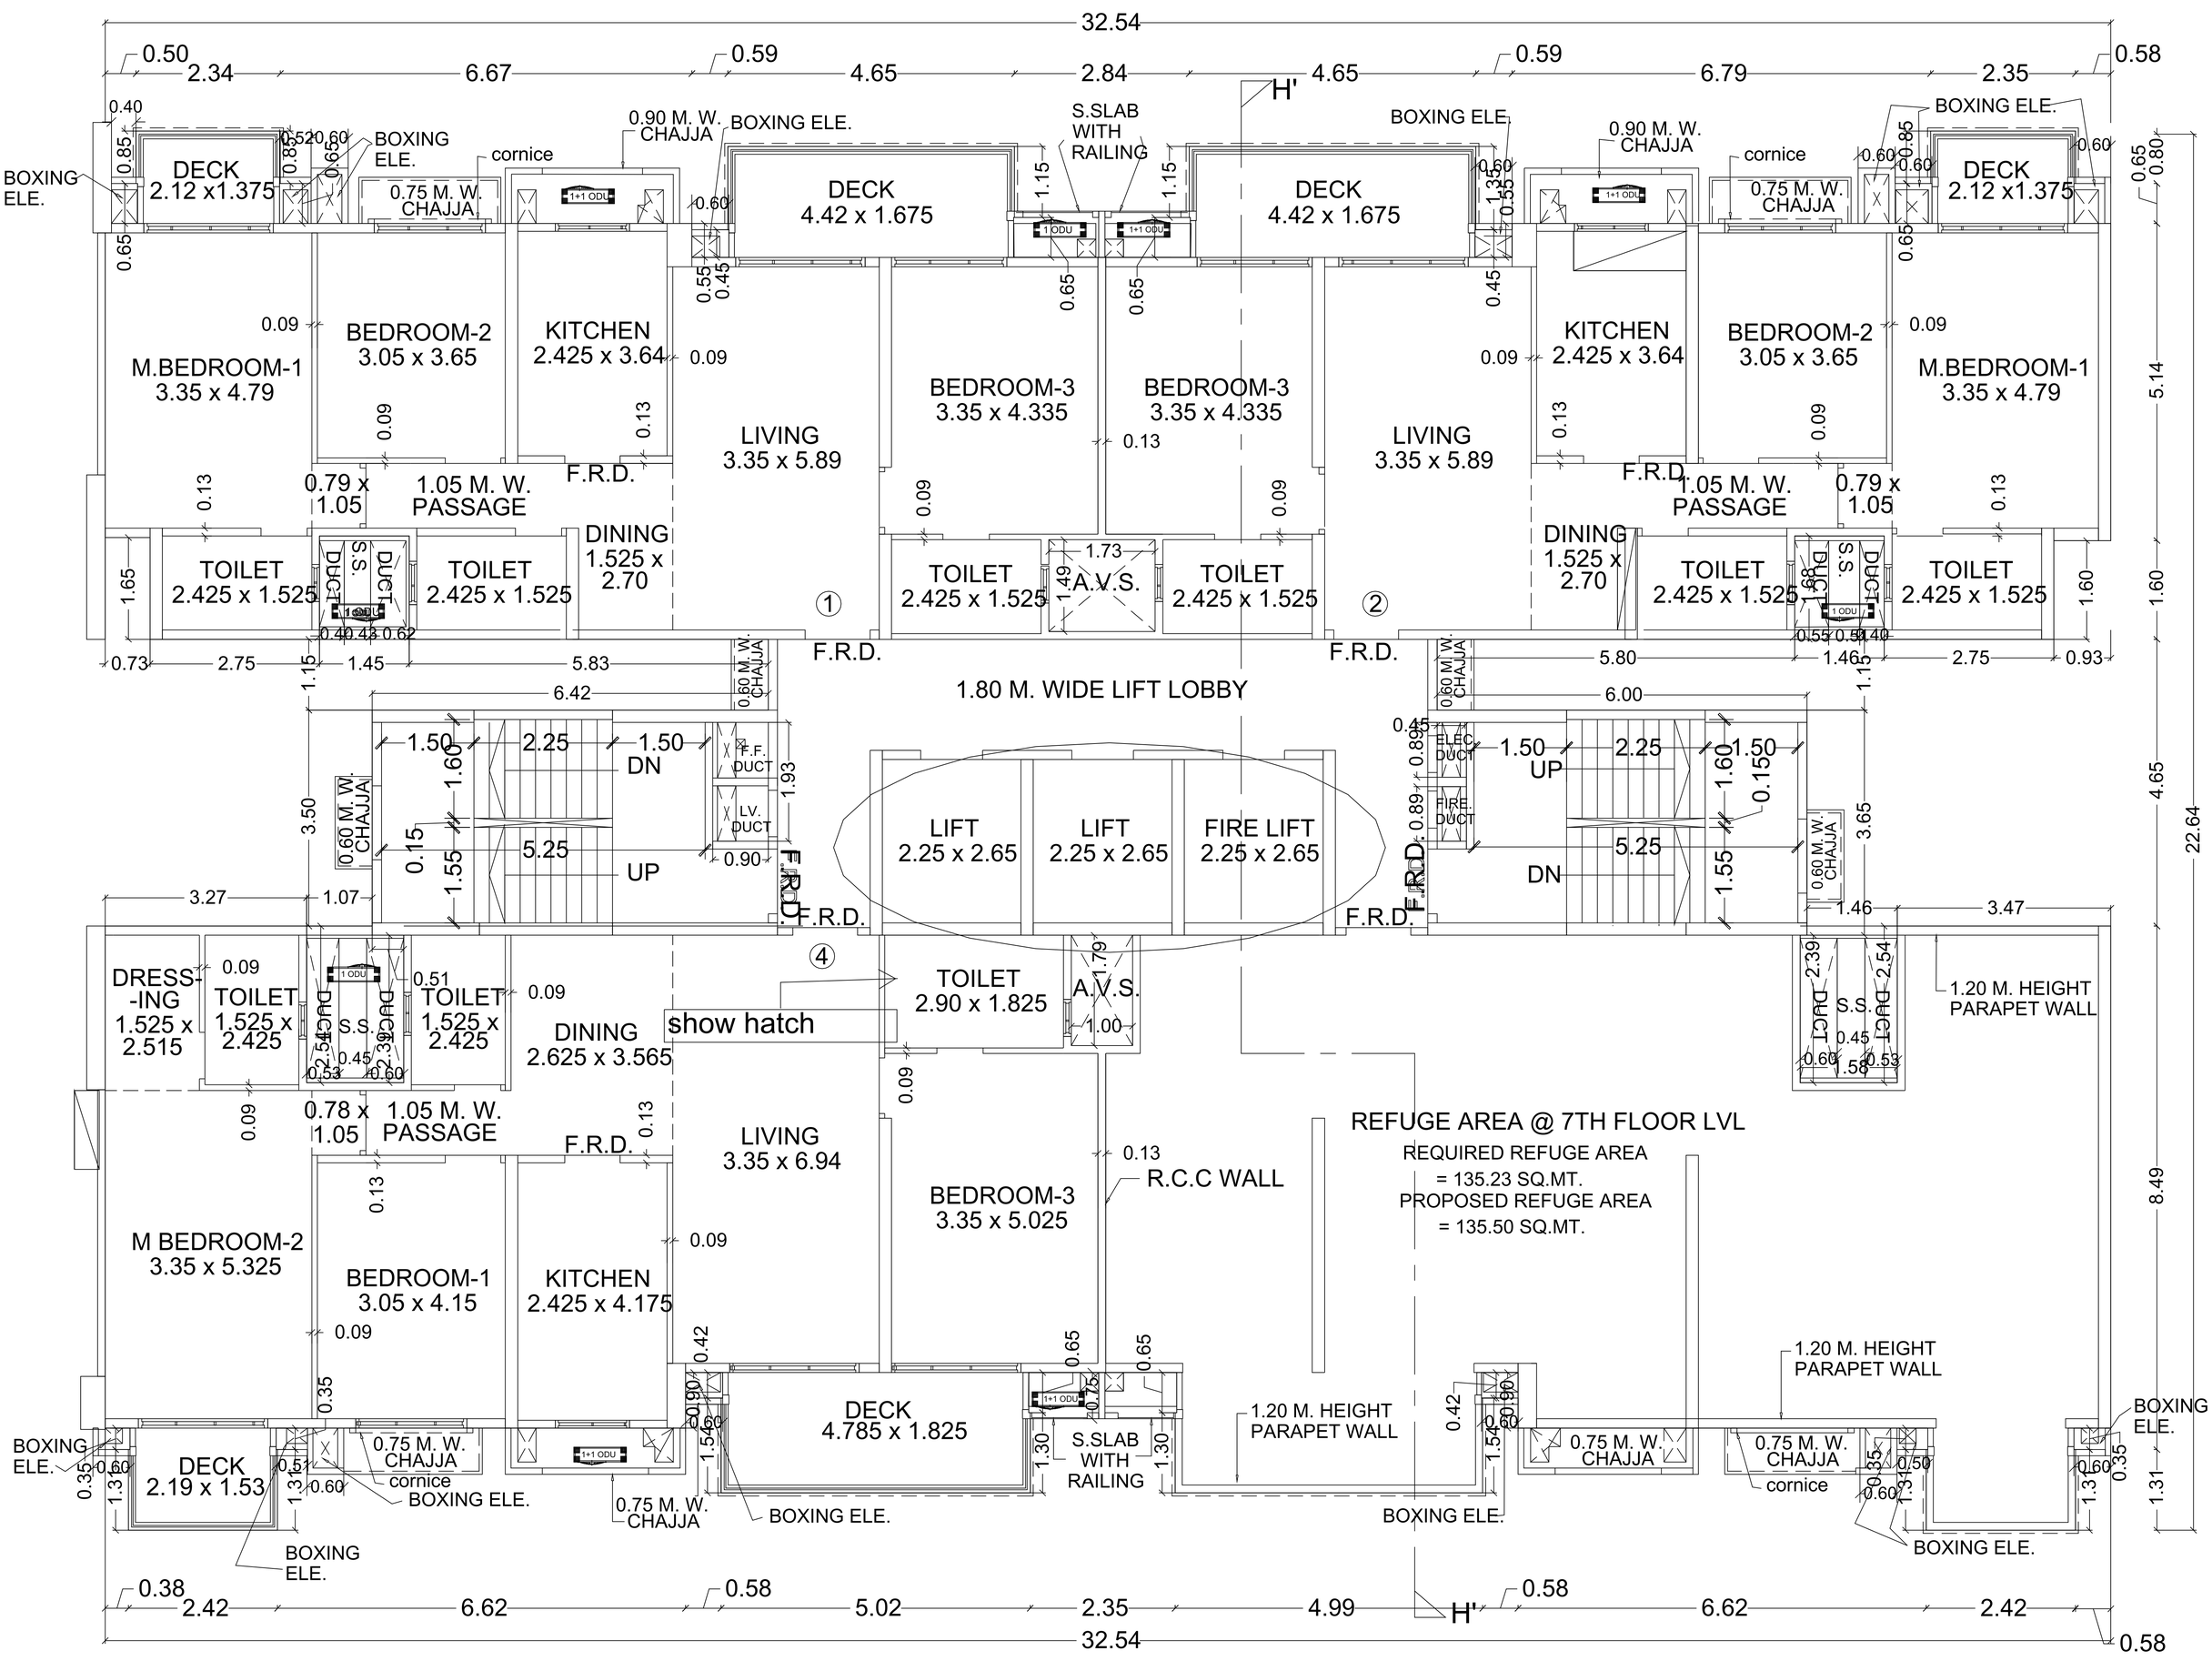


7TH REFUGE FLOOR PLAN (TOWER-03)

SCALE - 1:100

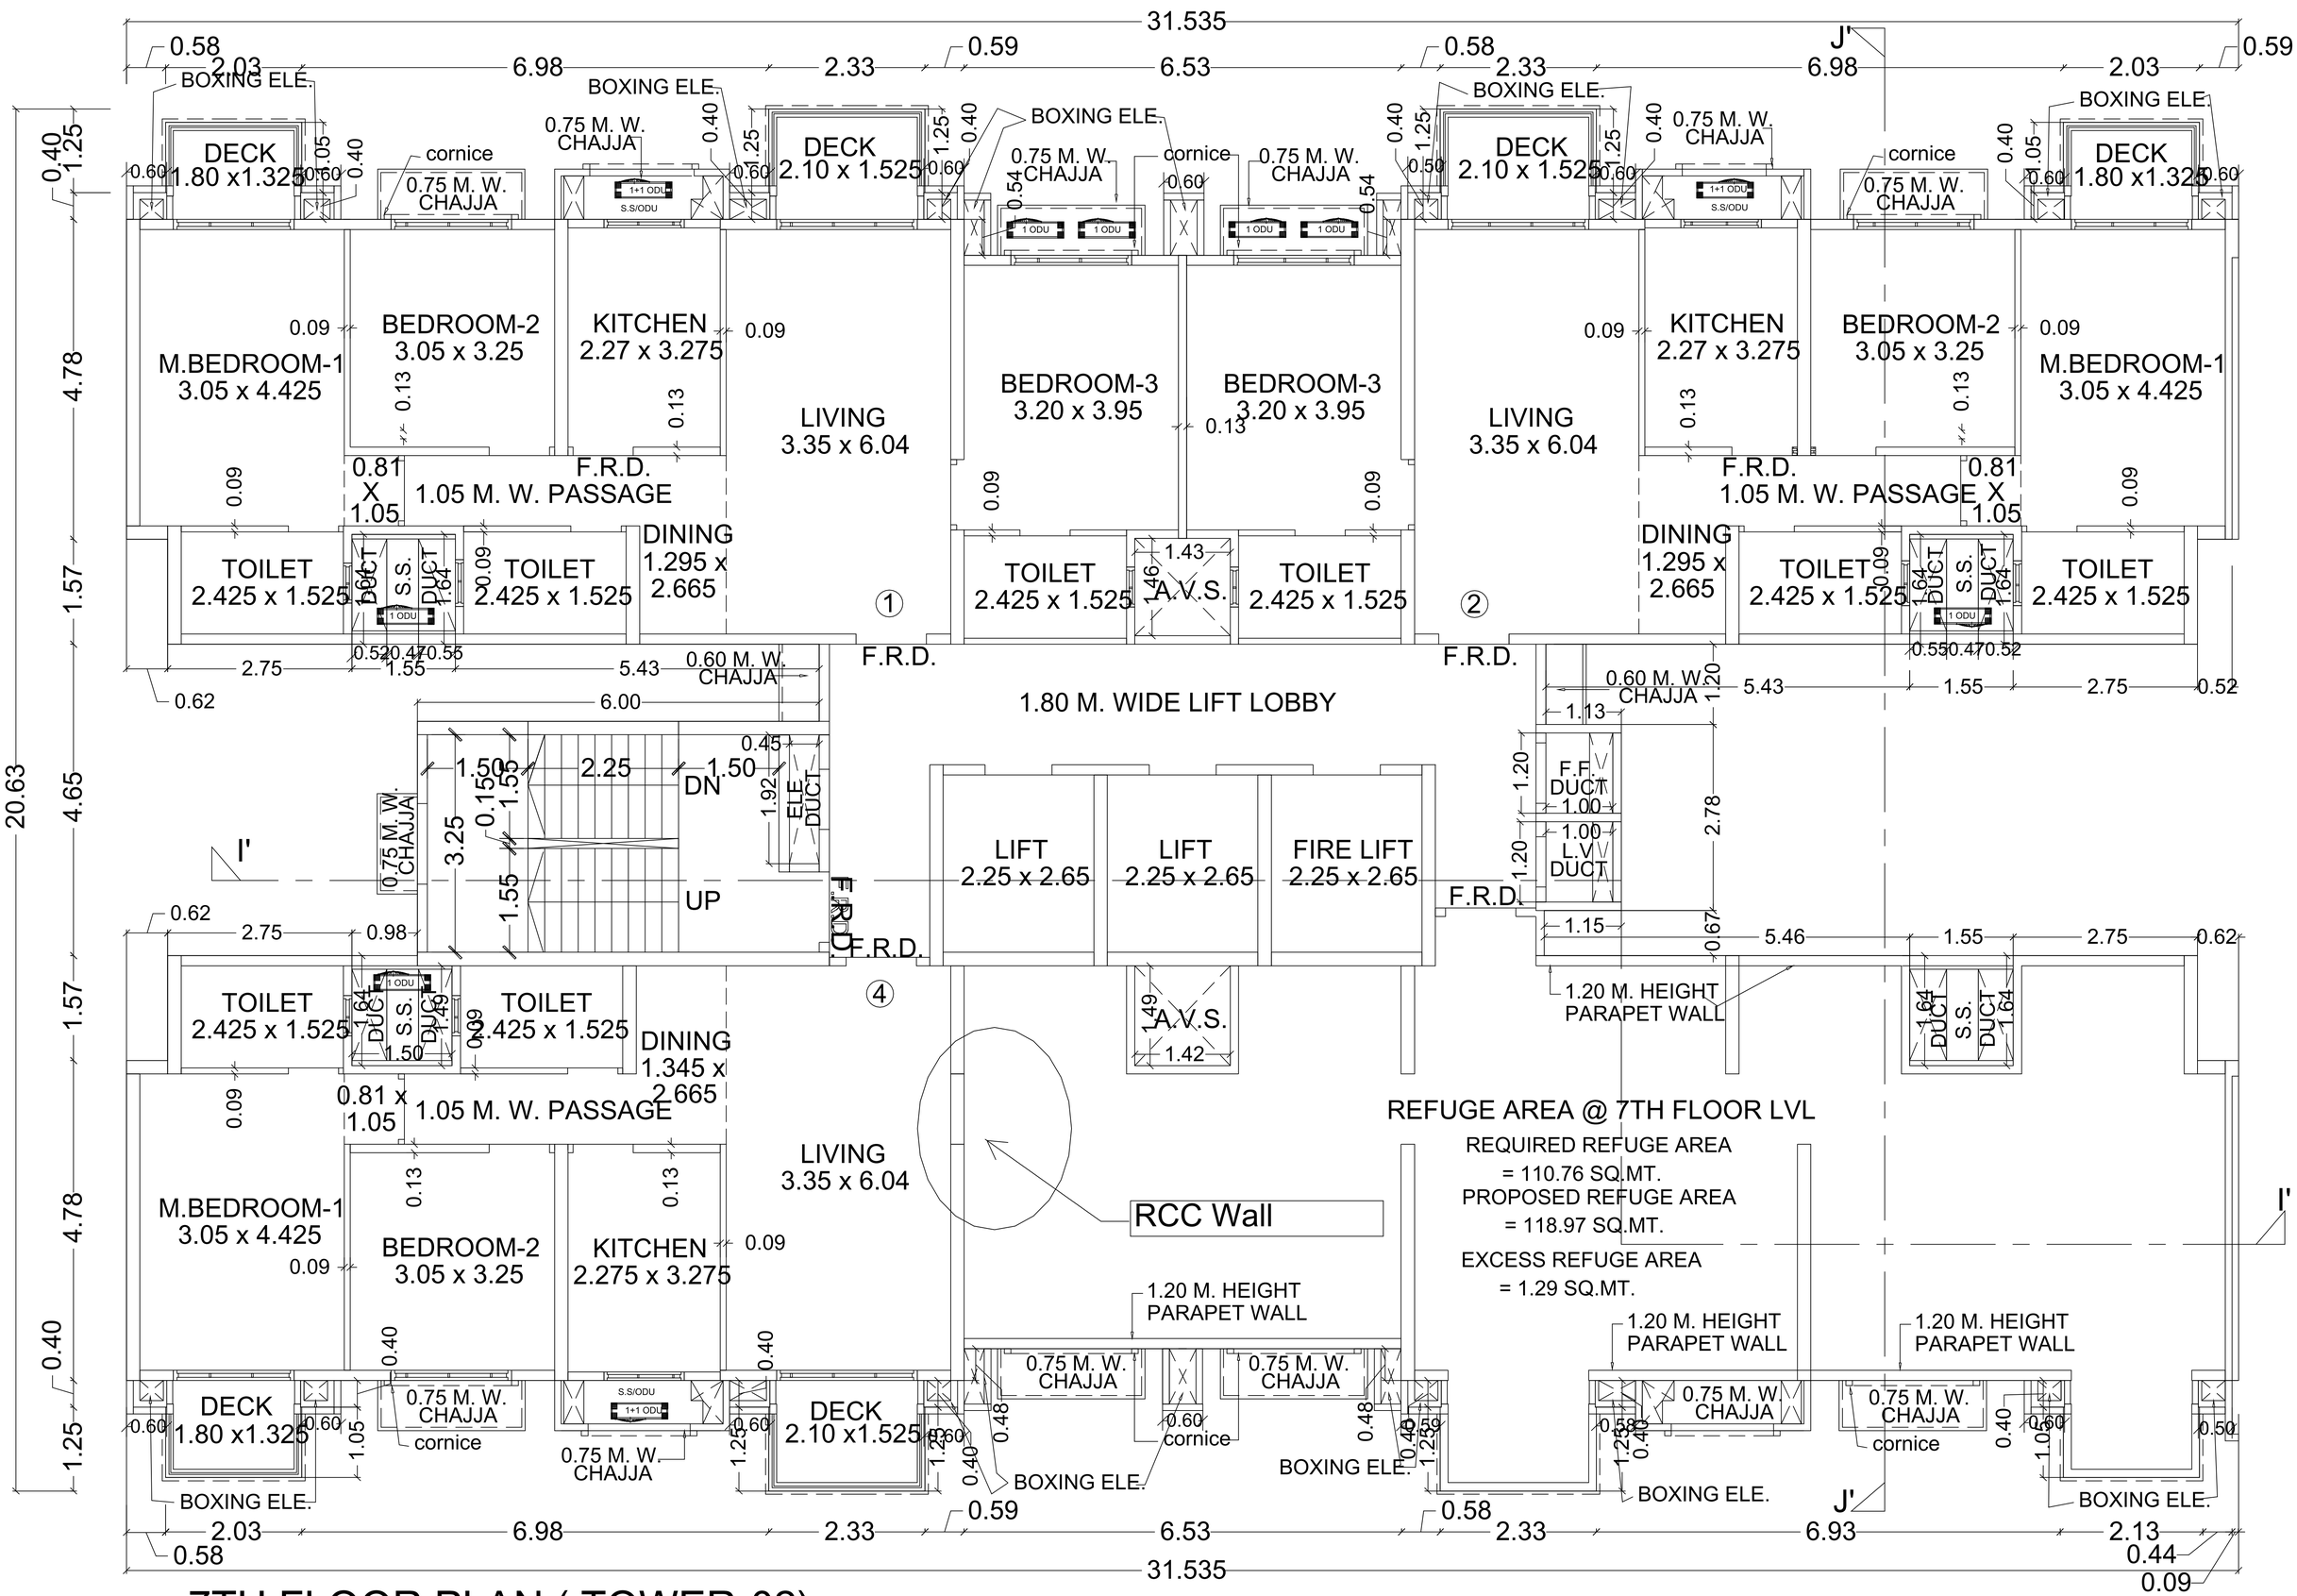

7TH FLOOR PLAN (TOWER-02)


SCALE - 1:100

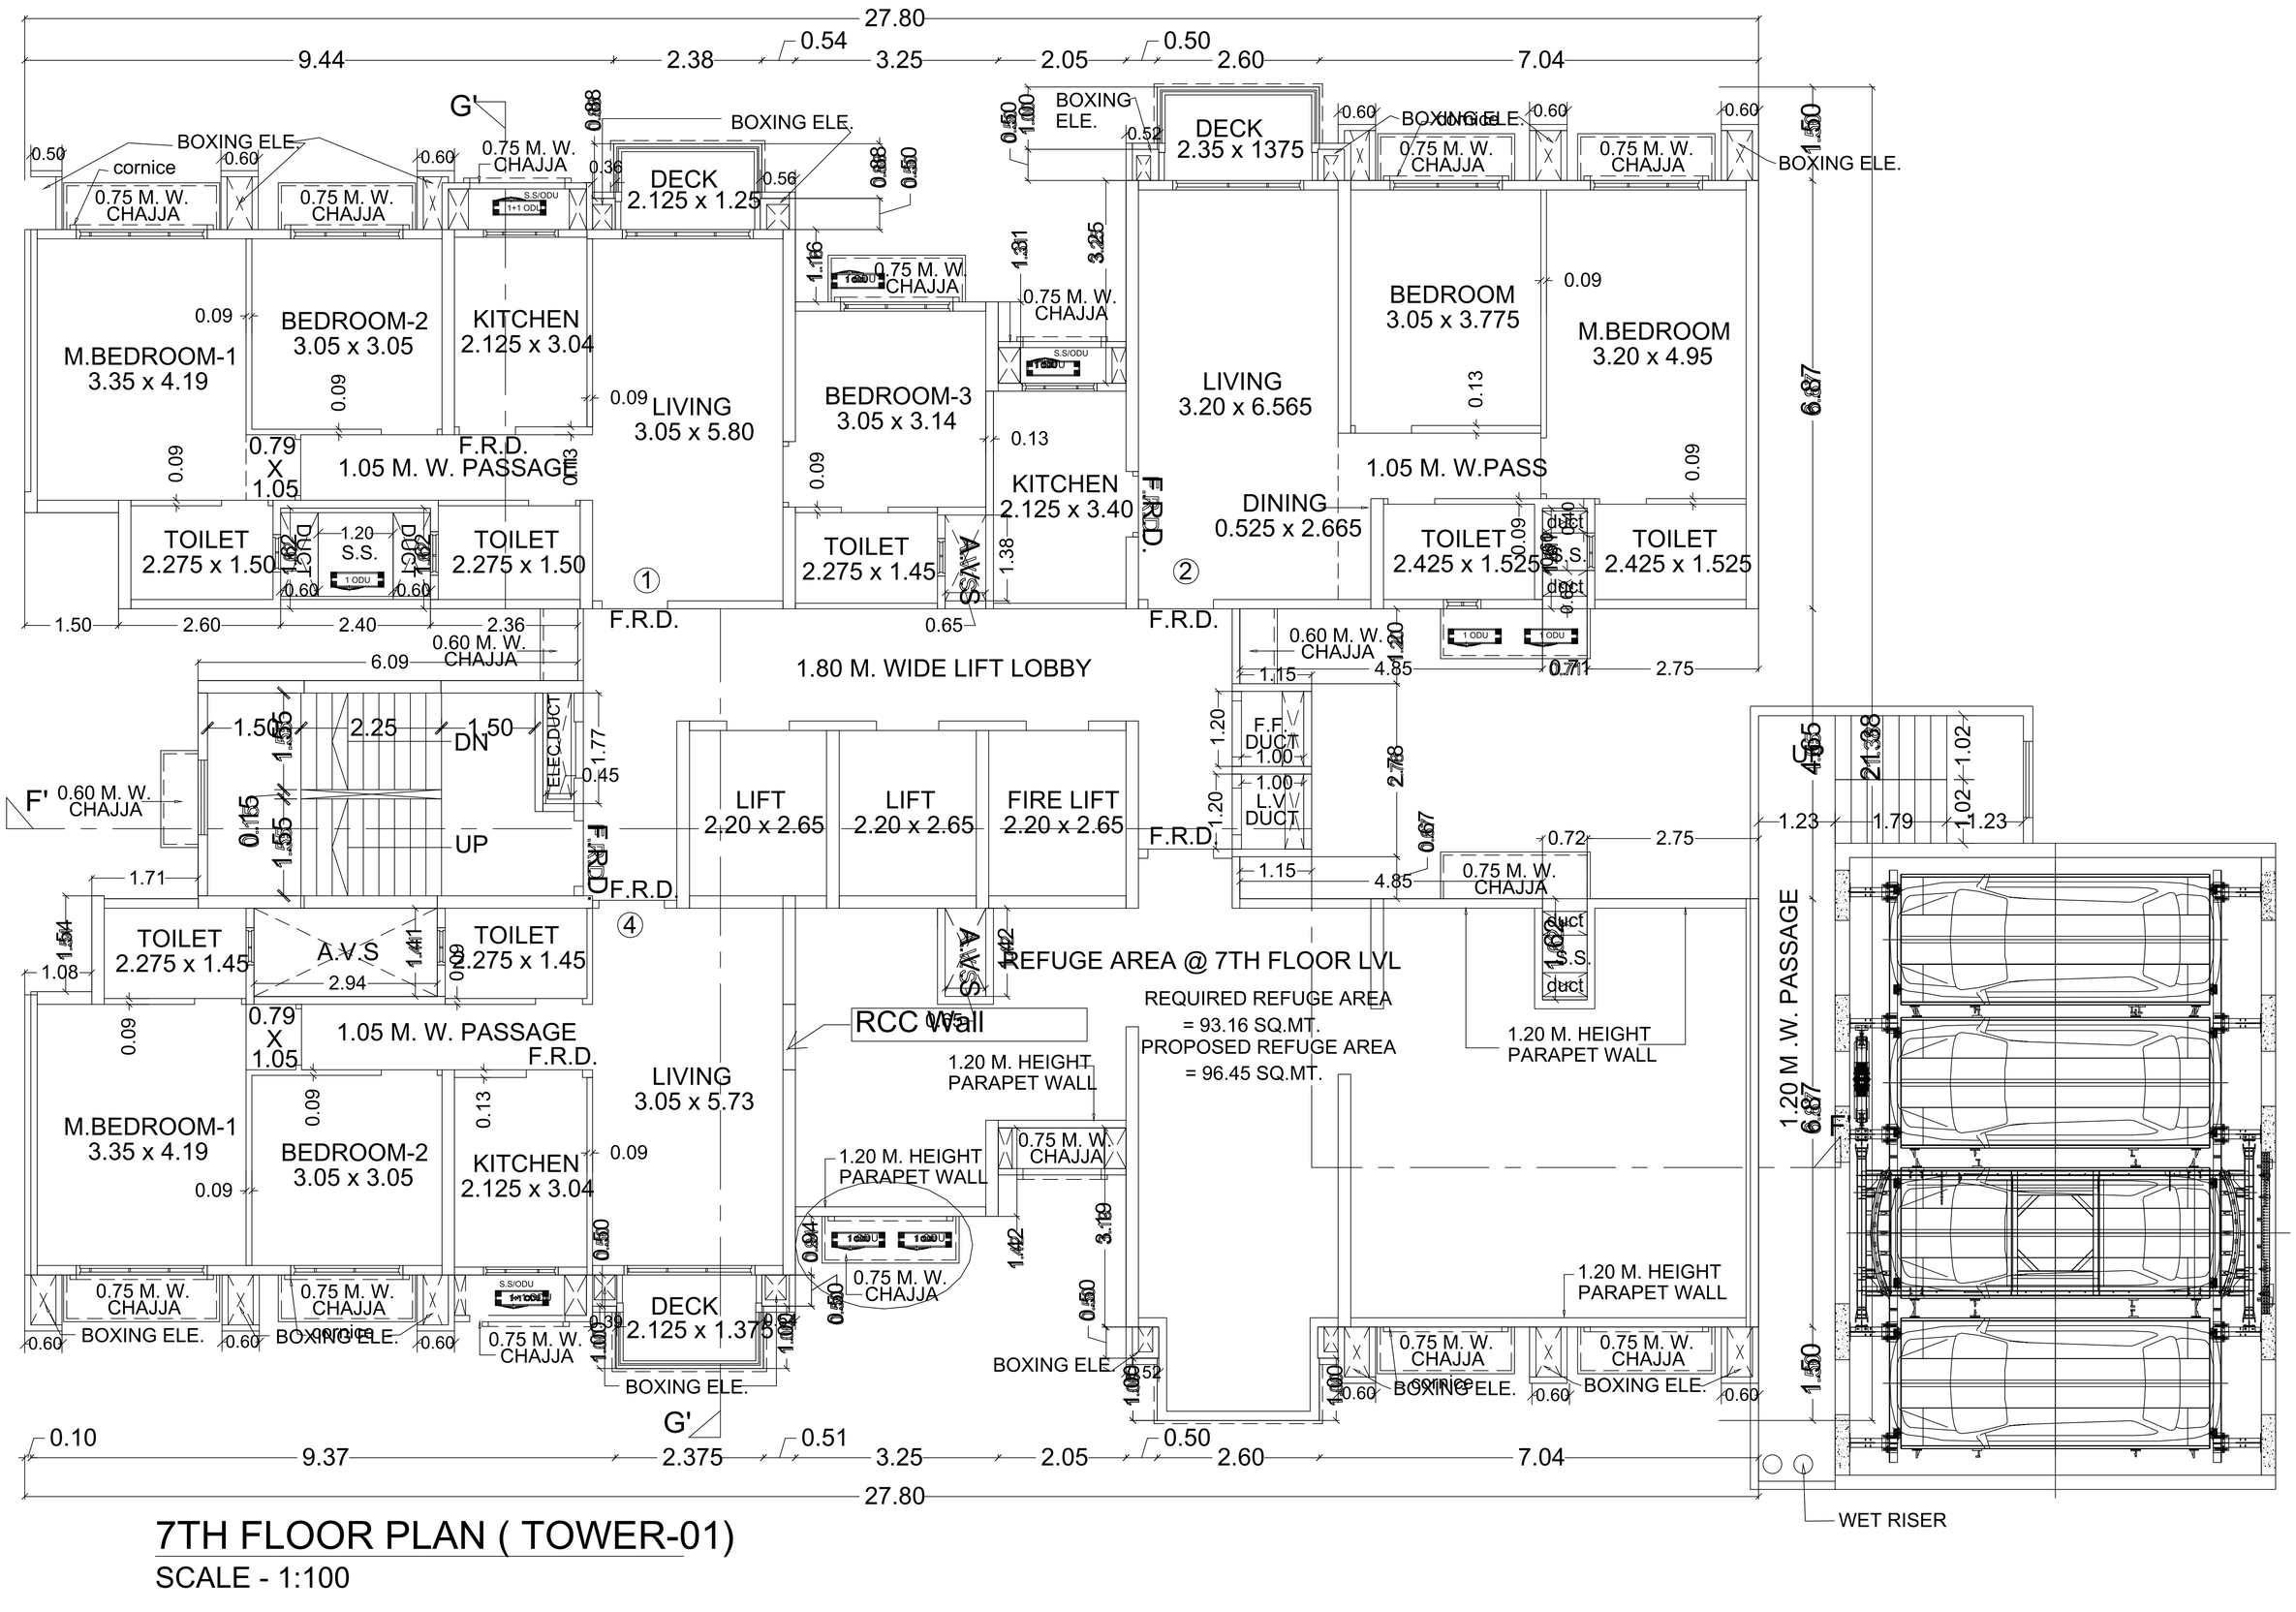

7TH FLOOR PLAN (TOWER-01)


SCALE - 1:100

(TOWER- 2)

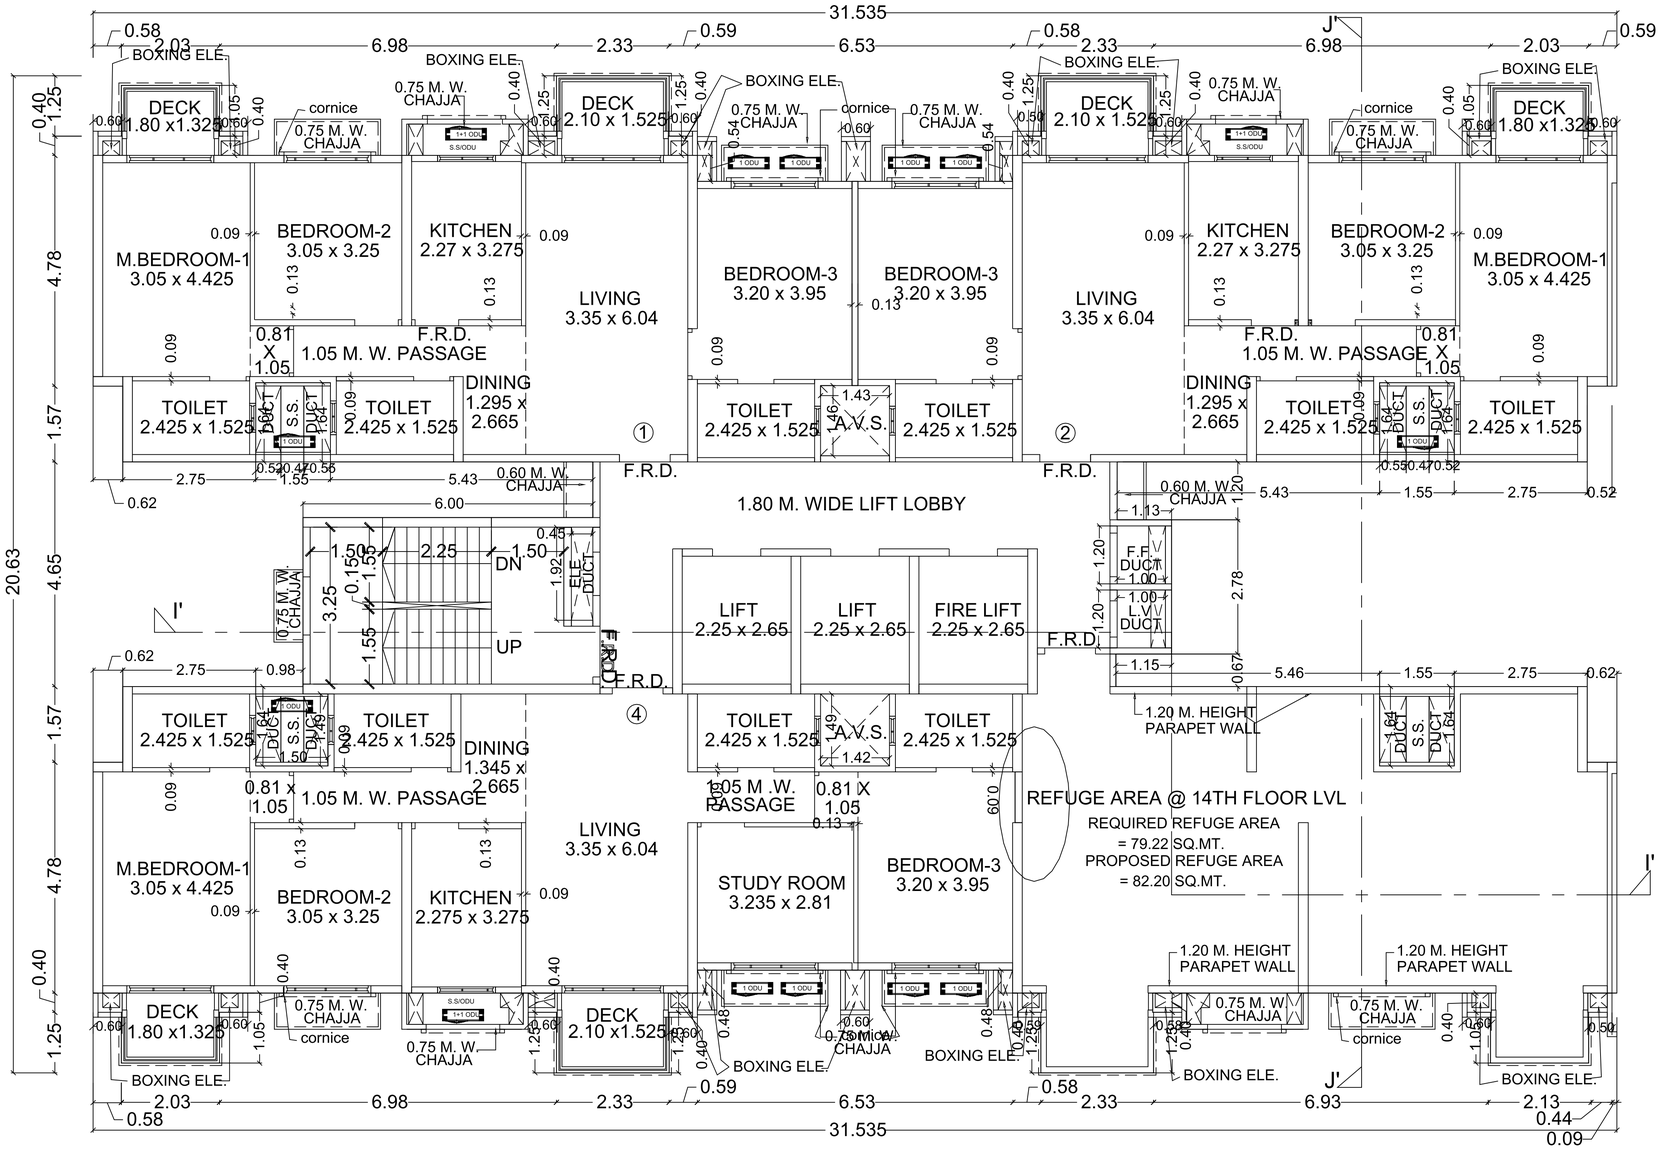


14TH FLOOR PLAN (TOWER-02)

SCALE - 1:100

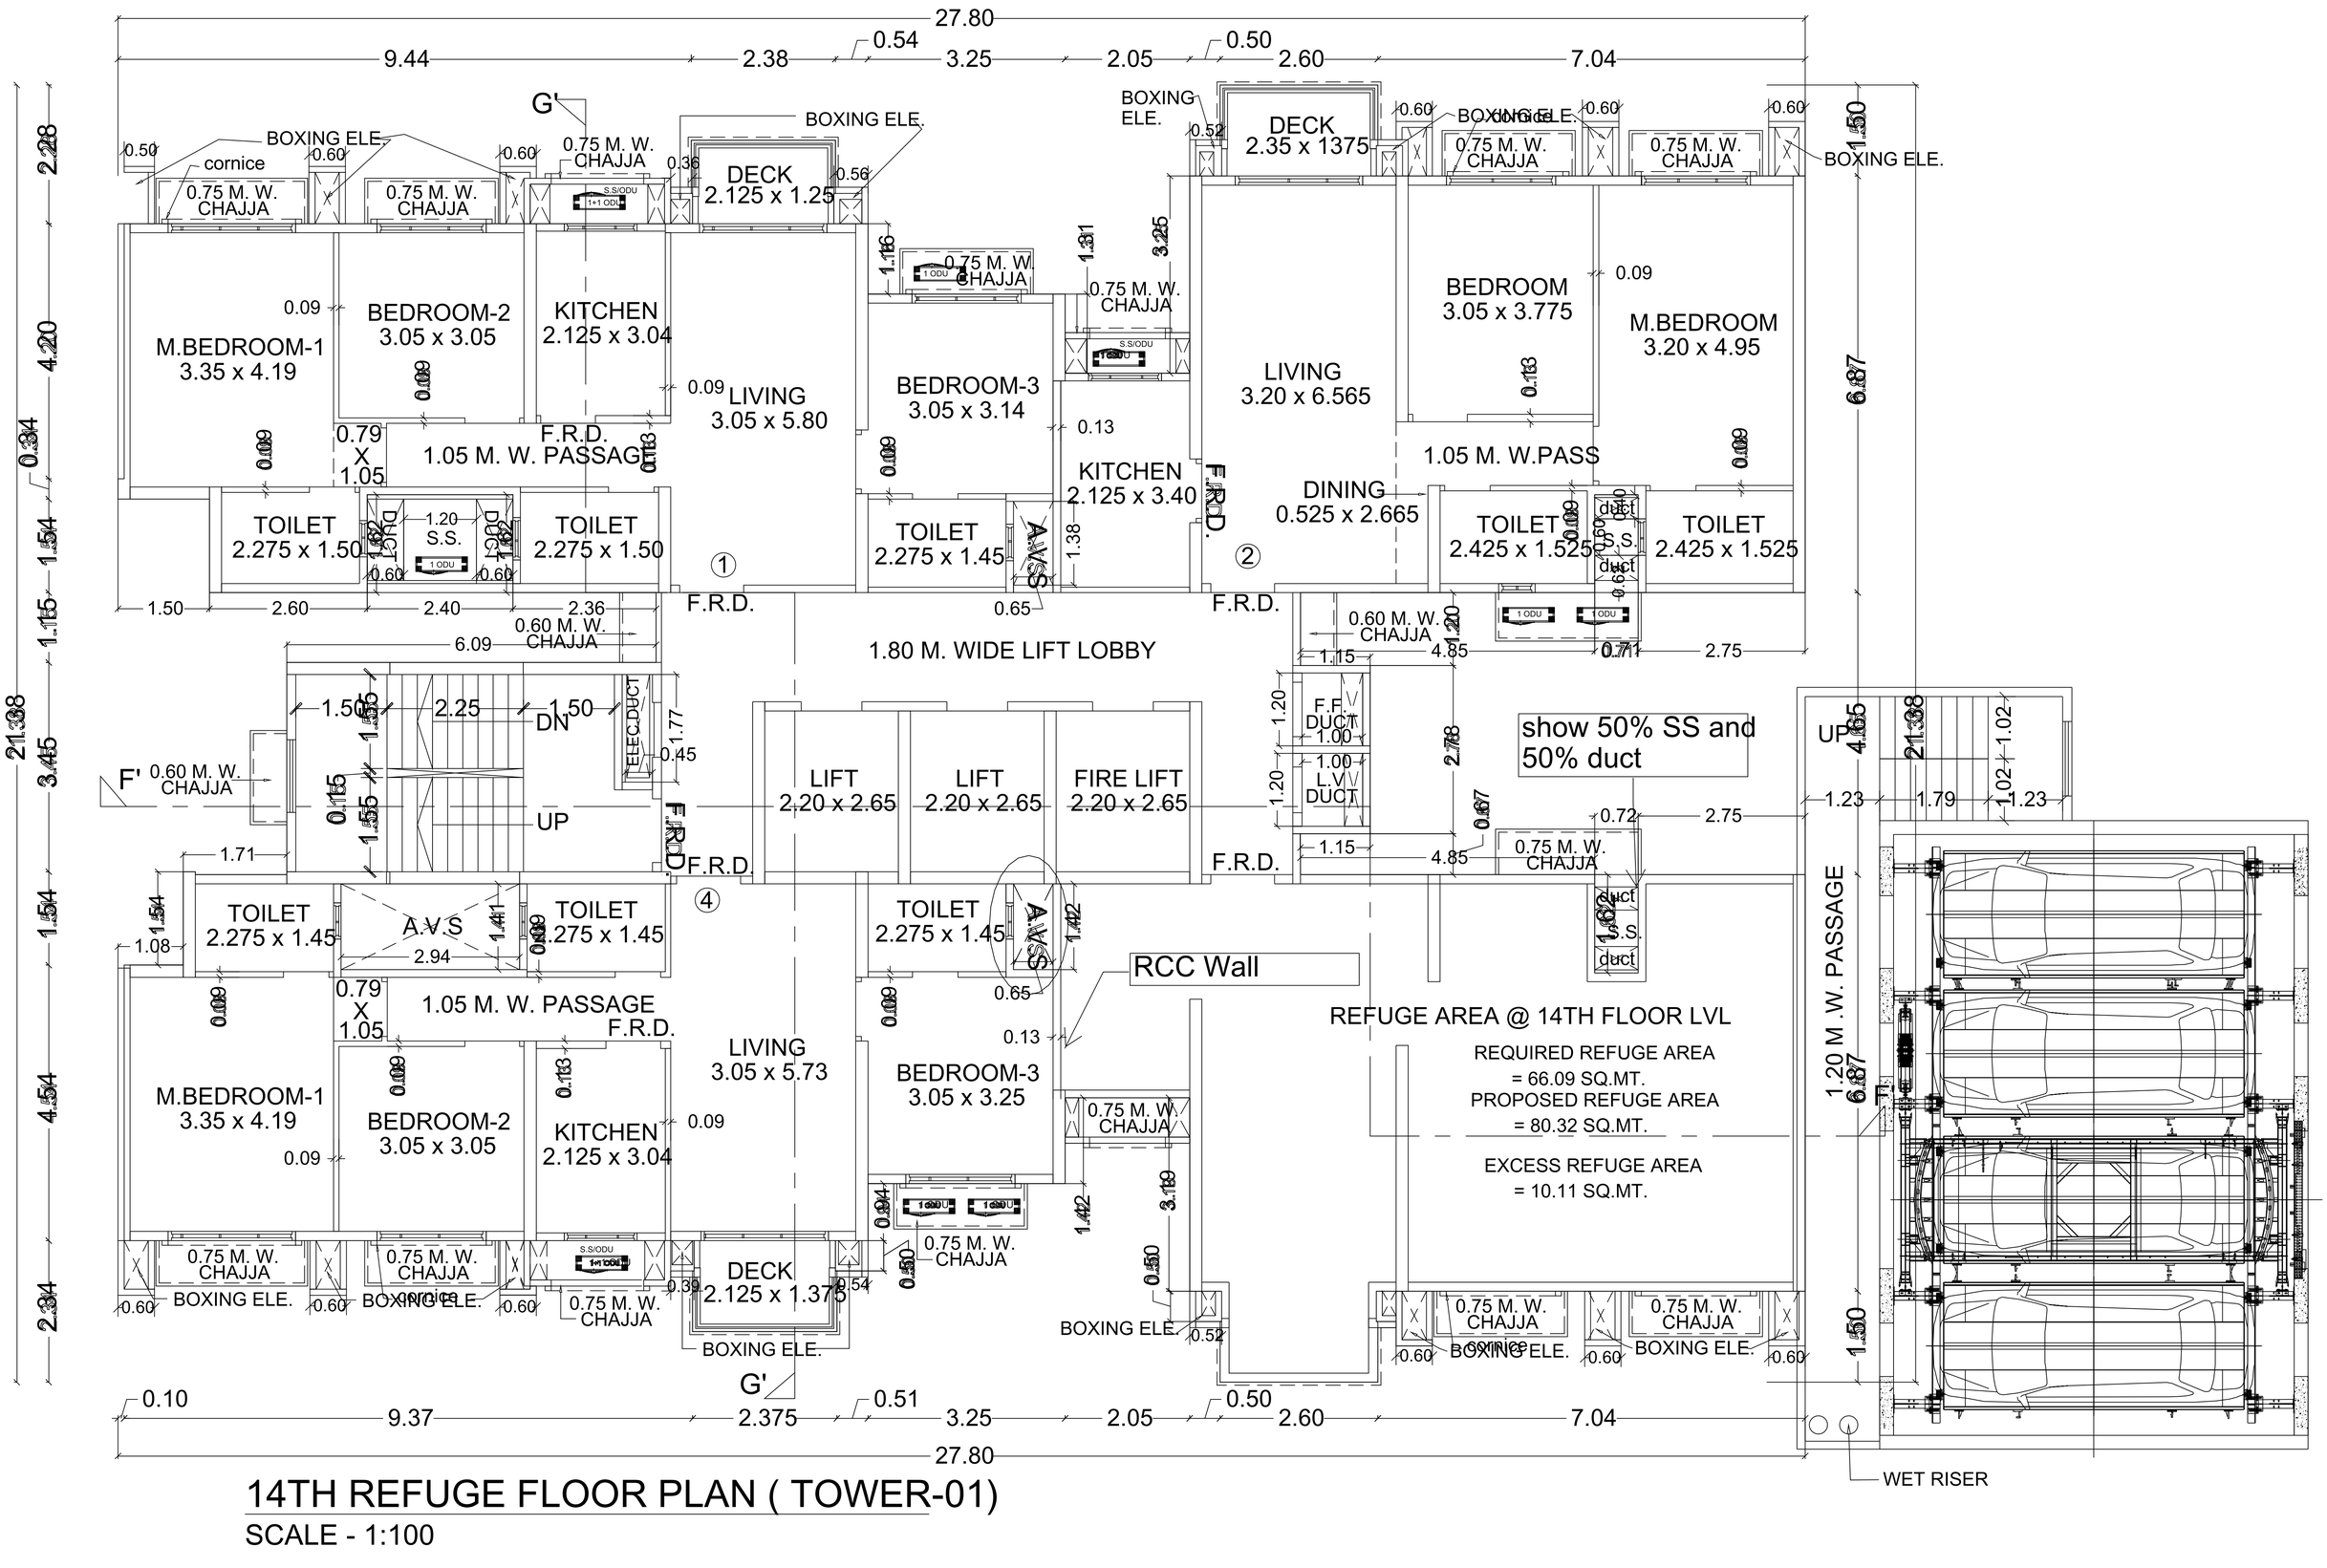


14TH REFUGE FLOOR PLAN (TOWER-01)

SCALE - 1:100

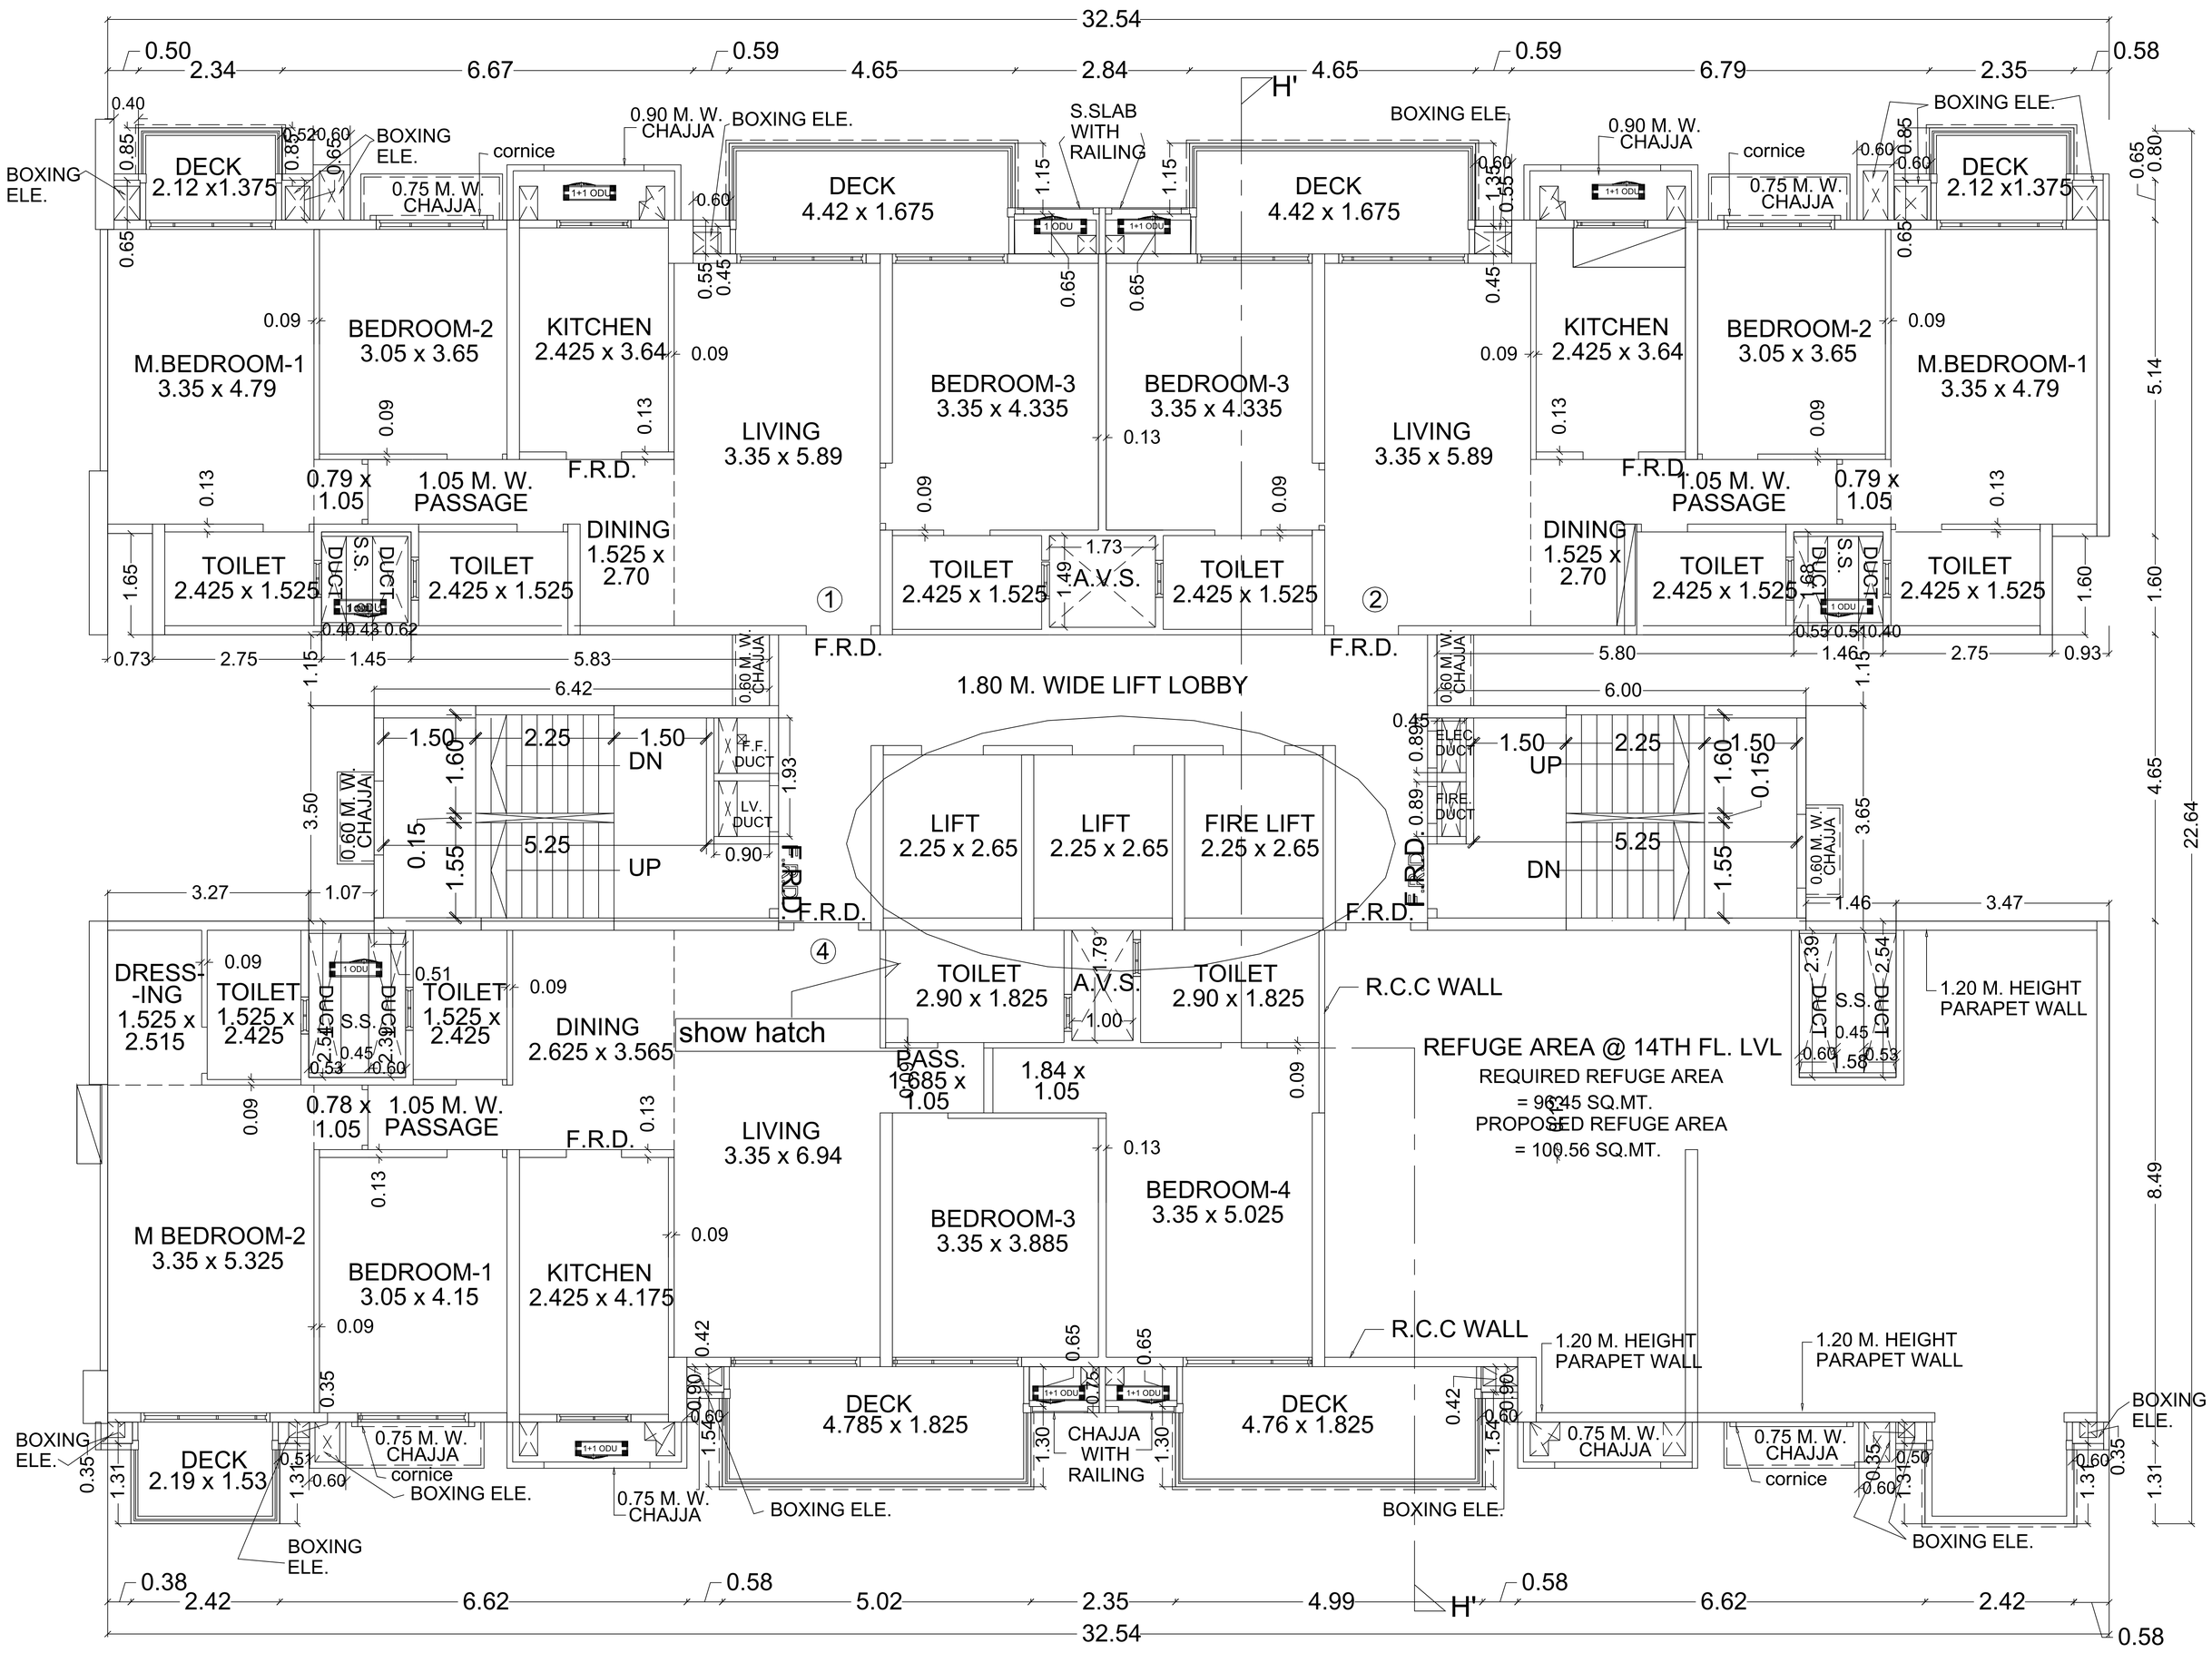

14TH REFUGE FLOOR PLAN (TOWER-03)

SCALE - 1:100

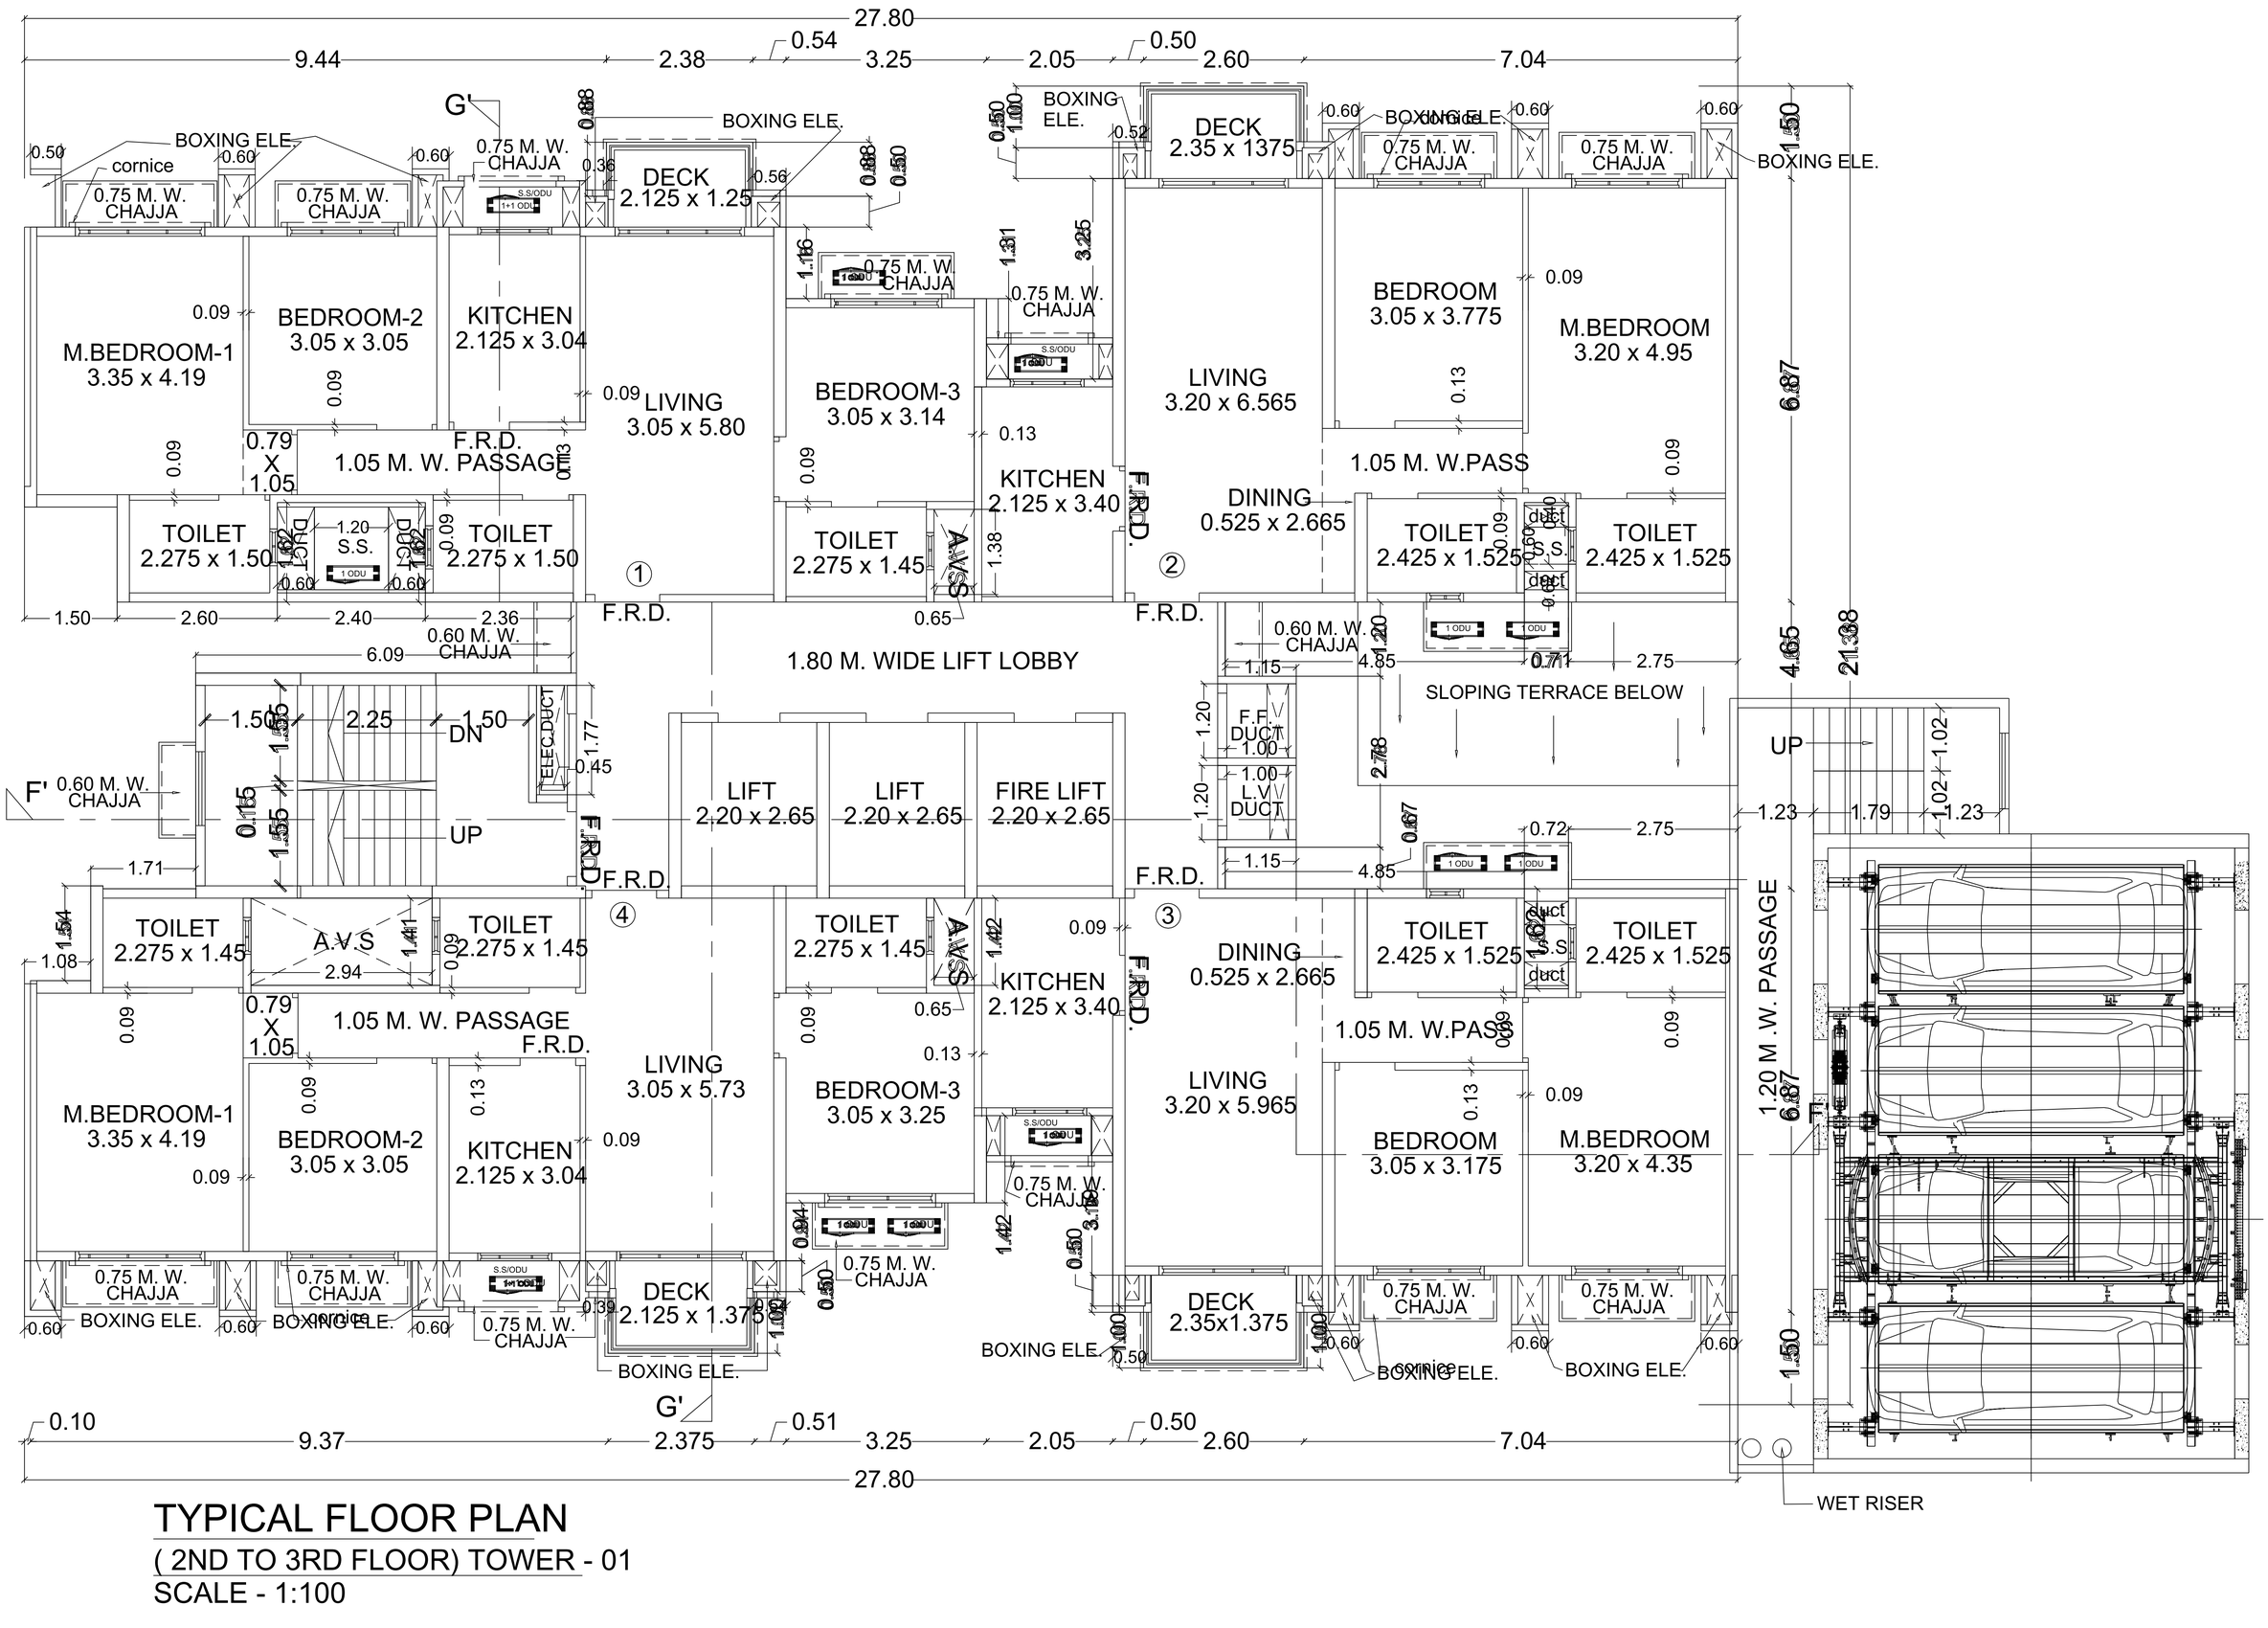

TYPICAL FLOOR PLAN

(2ND TO 3RD FLOOR) TOWER - 01

SCALE - 1:100