

SCALE - 1:100

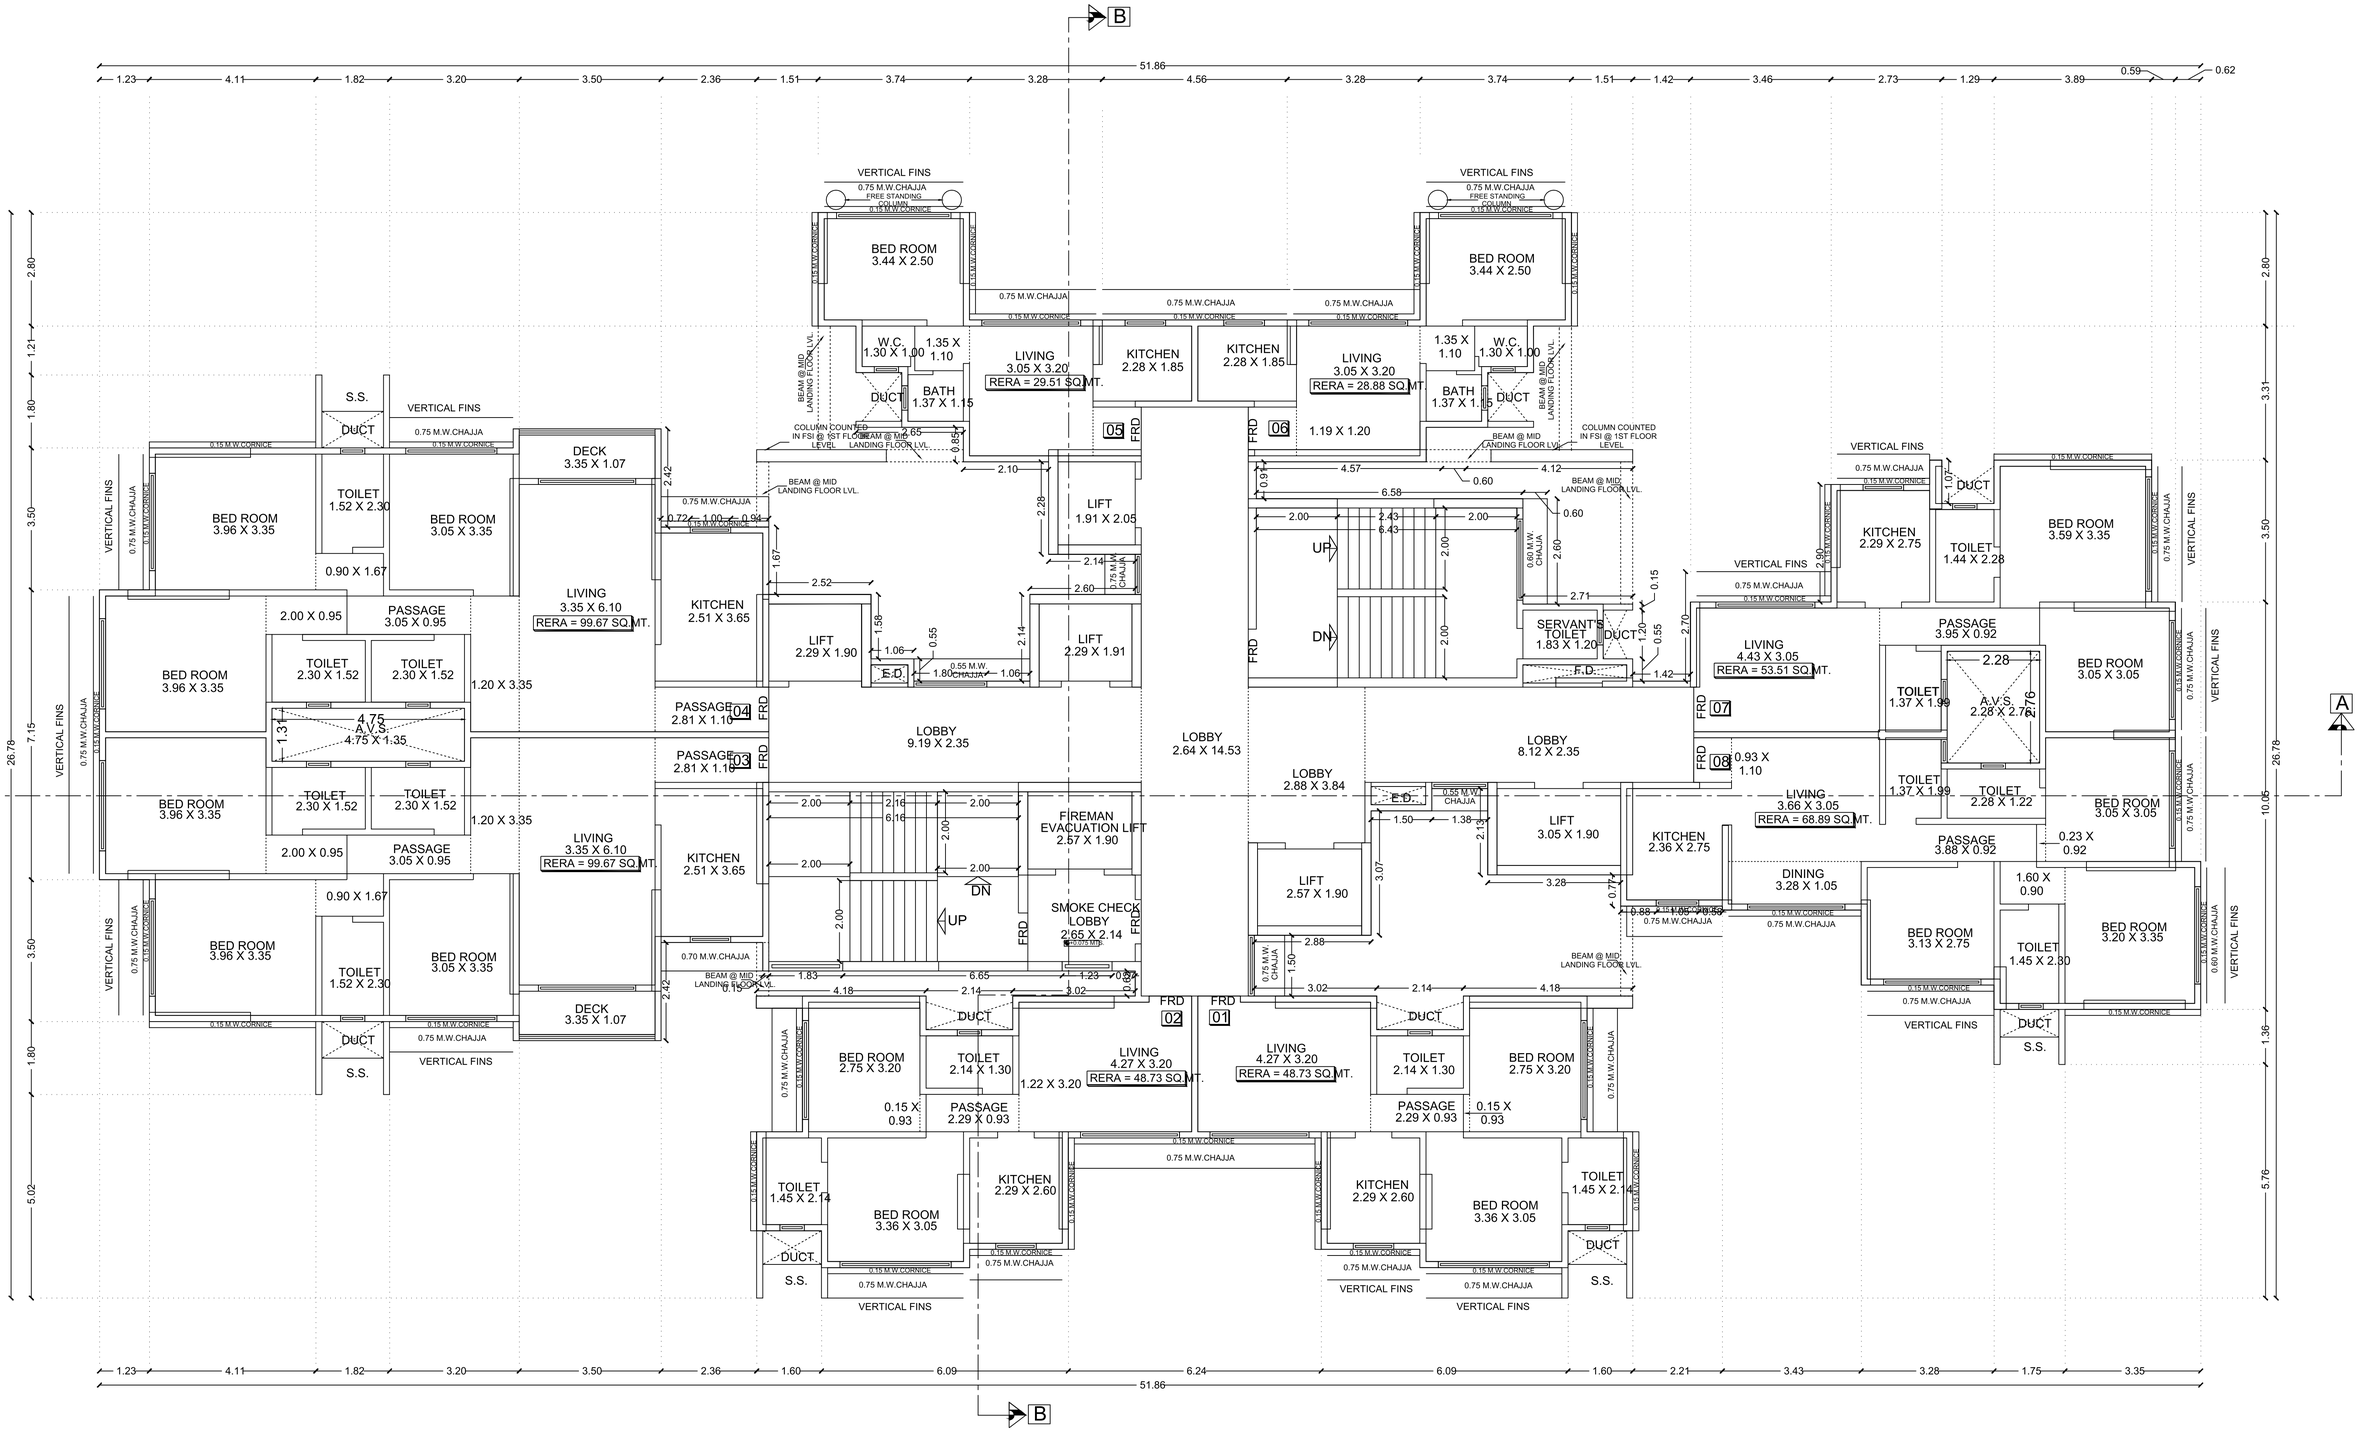


1ST FLOOR PLAN

SCALE - 1:100


SCALE - 1:100

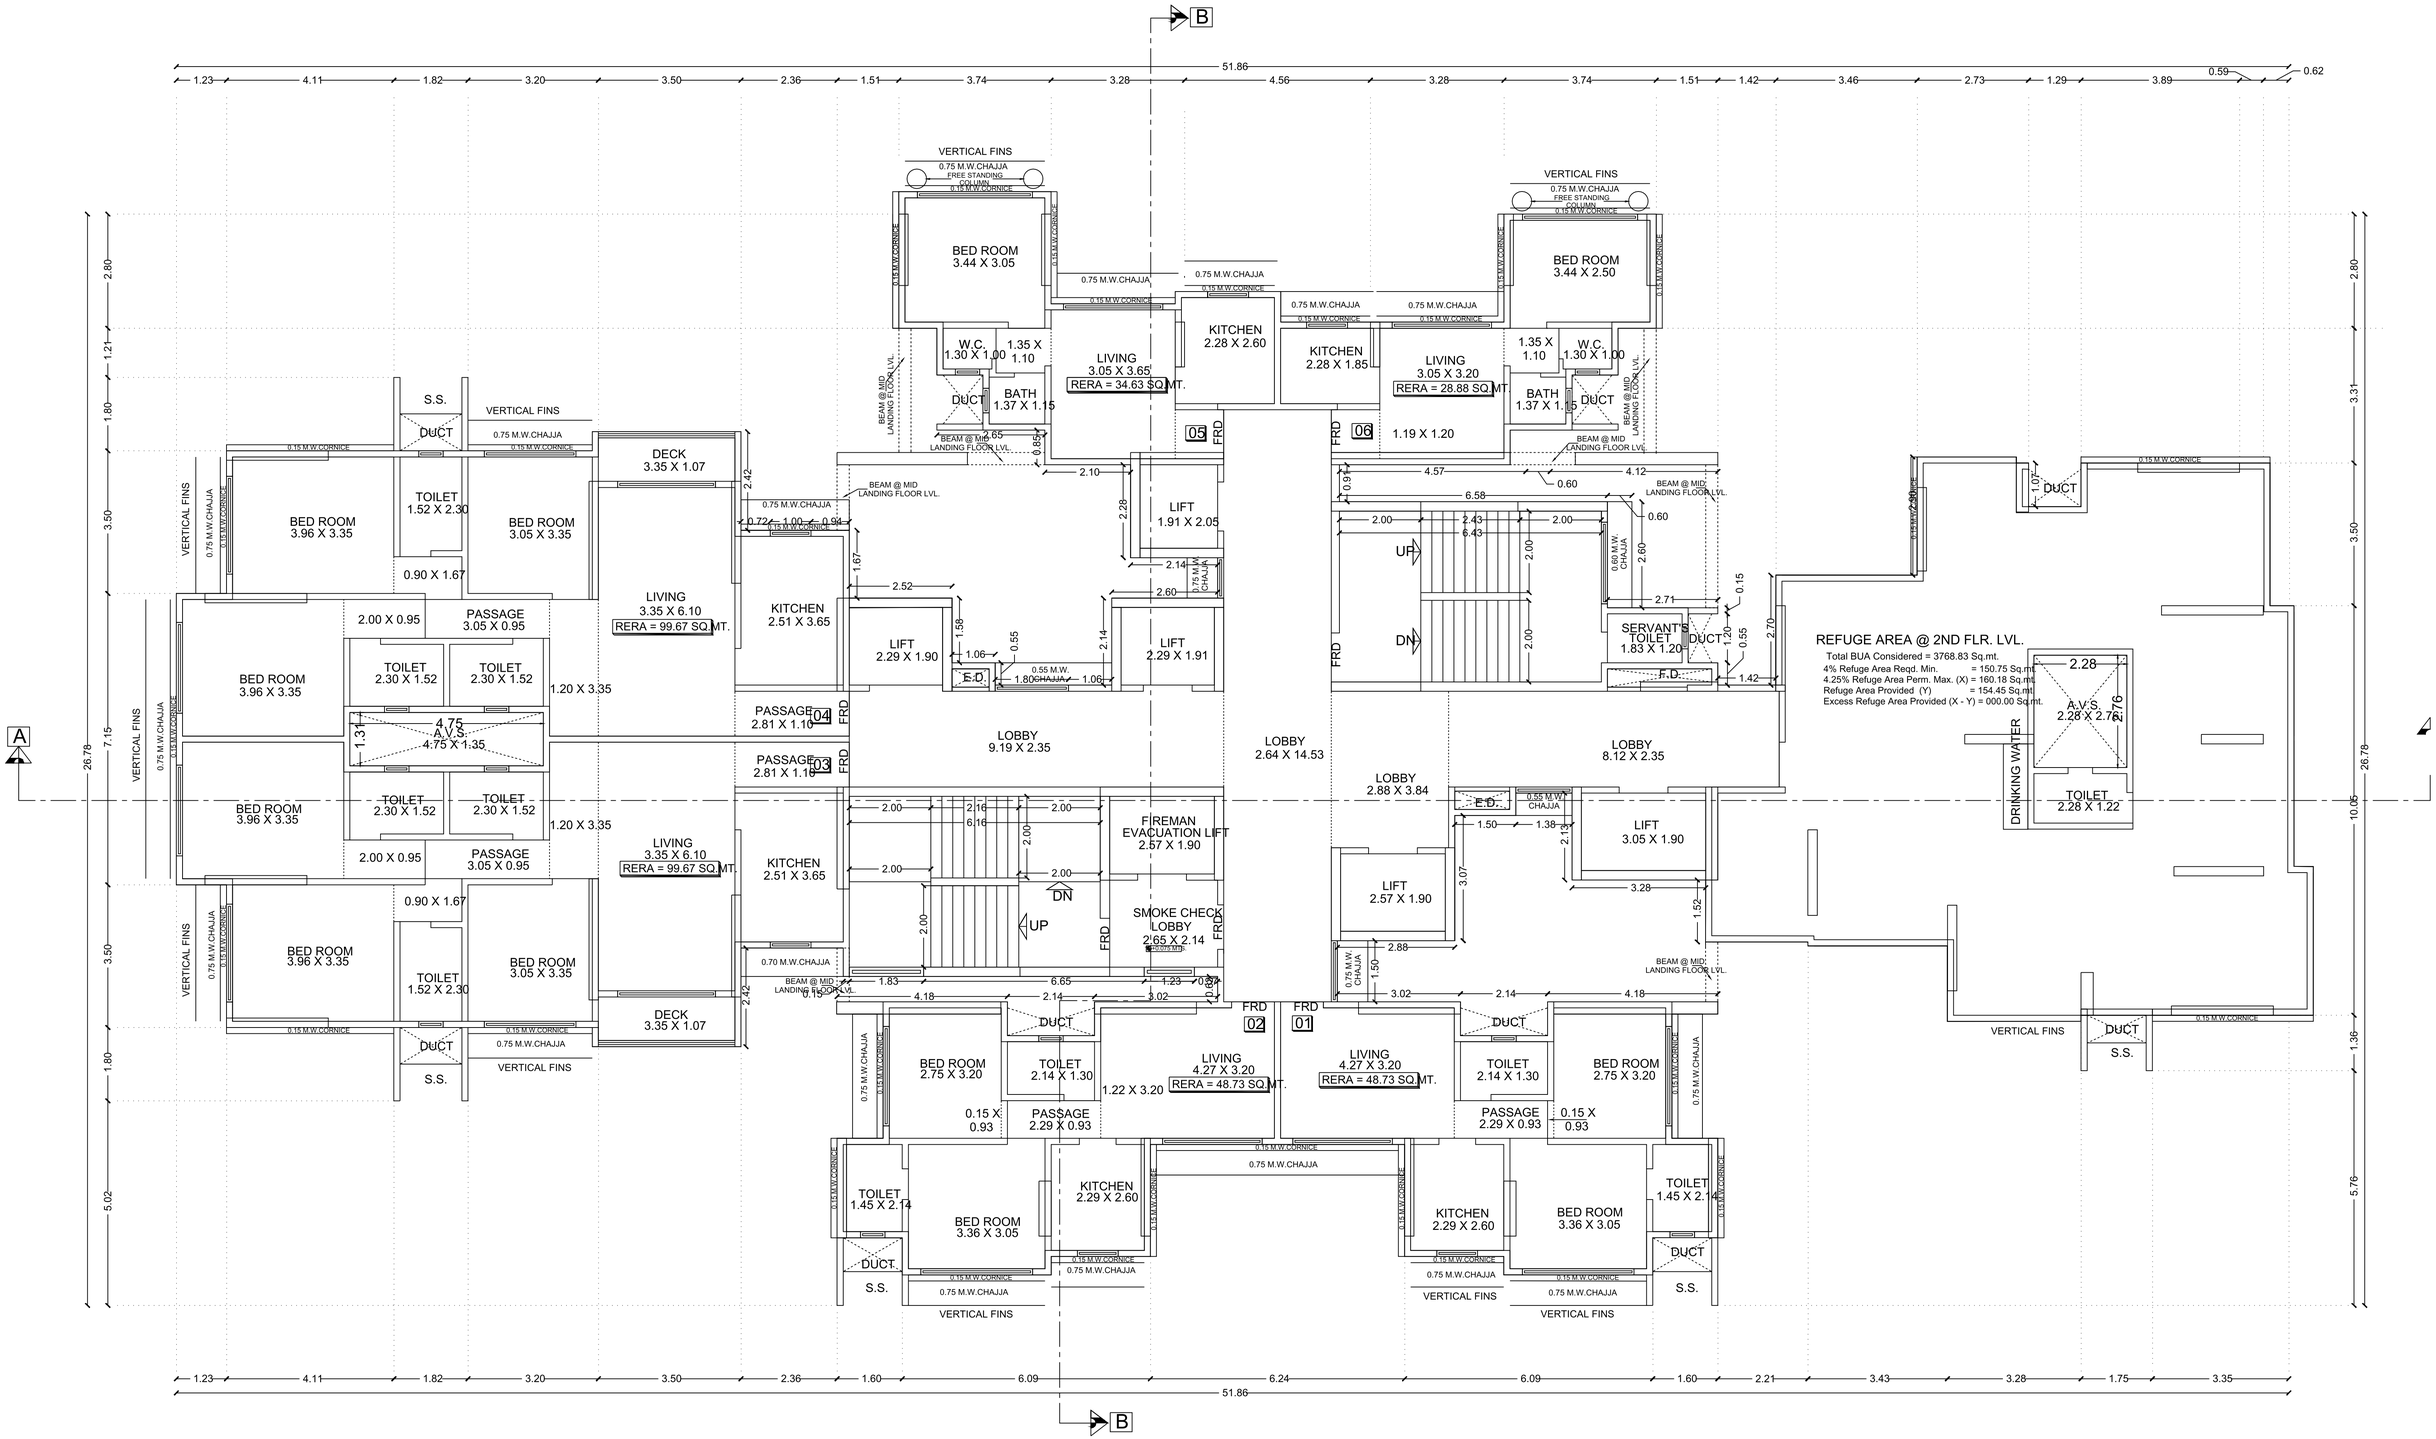

2ND REFUGE FLOOR PLAN

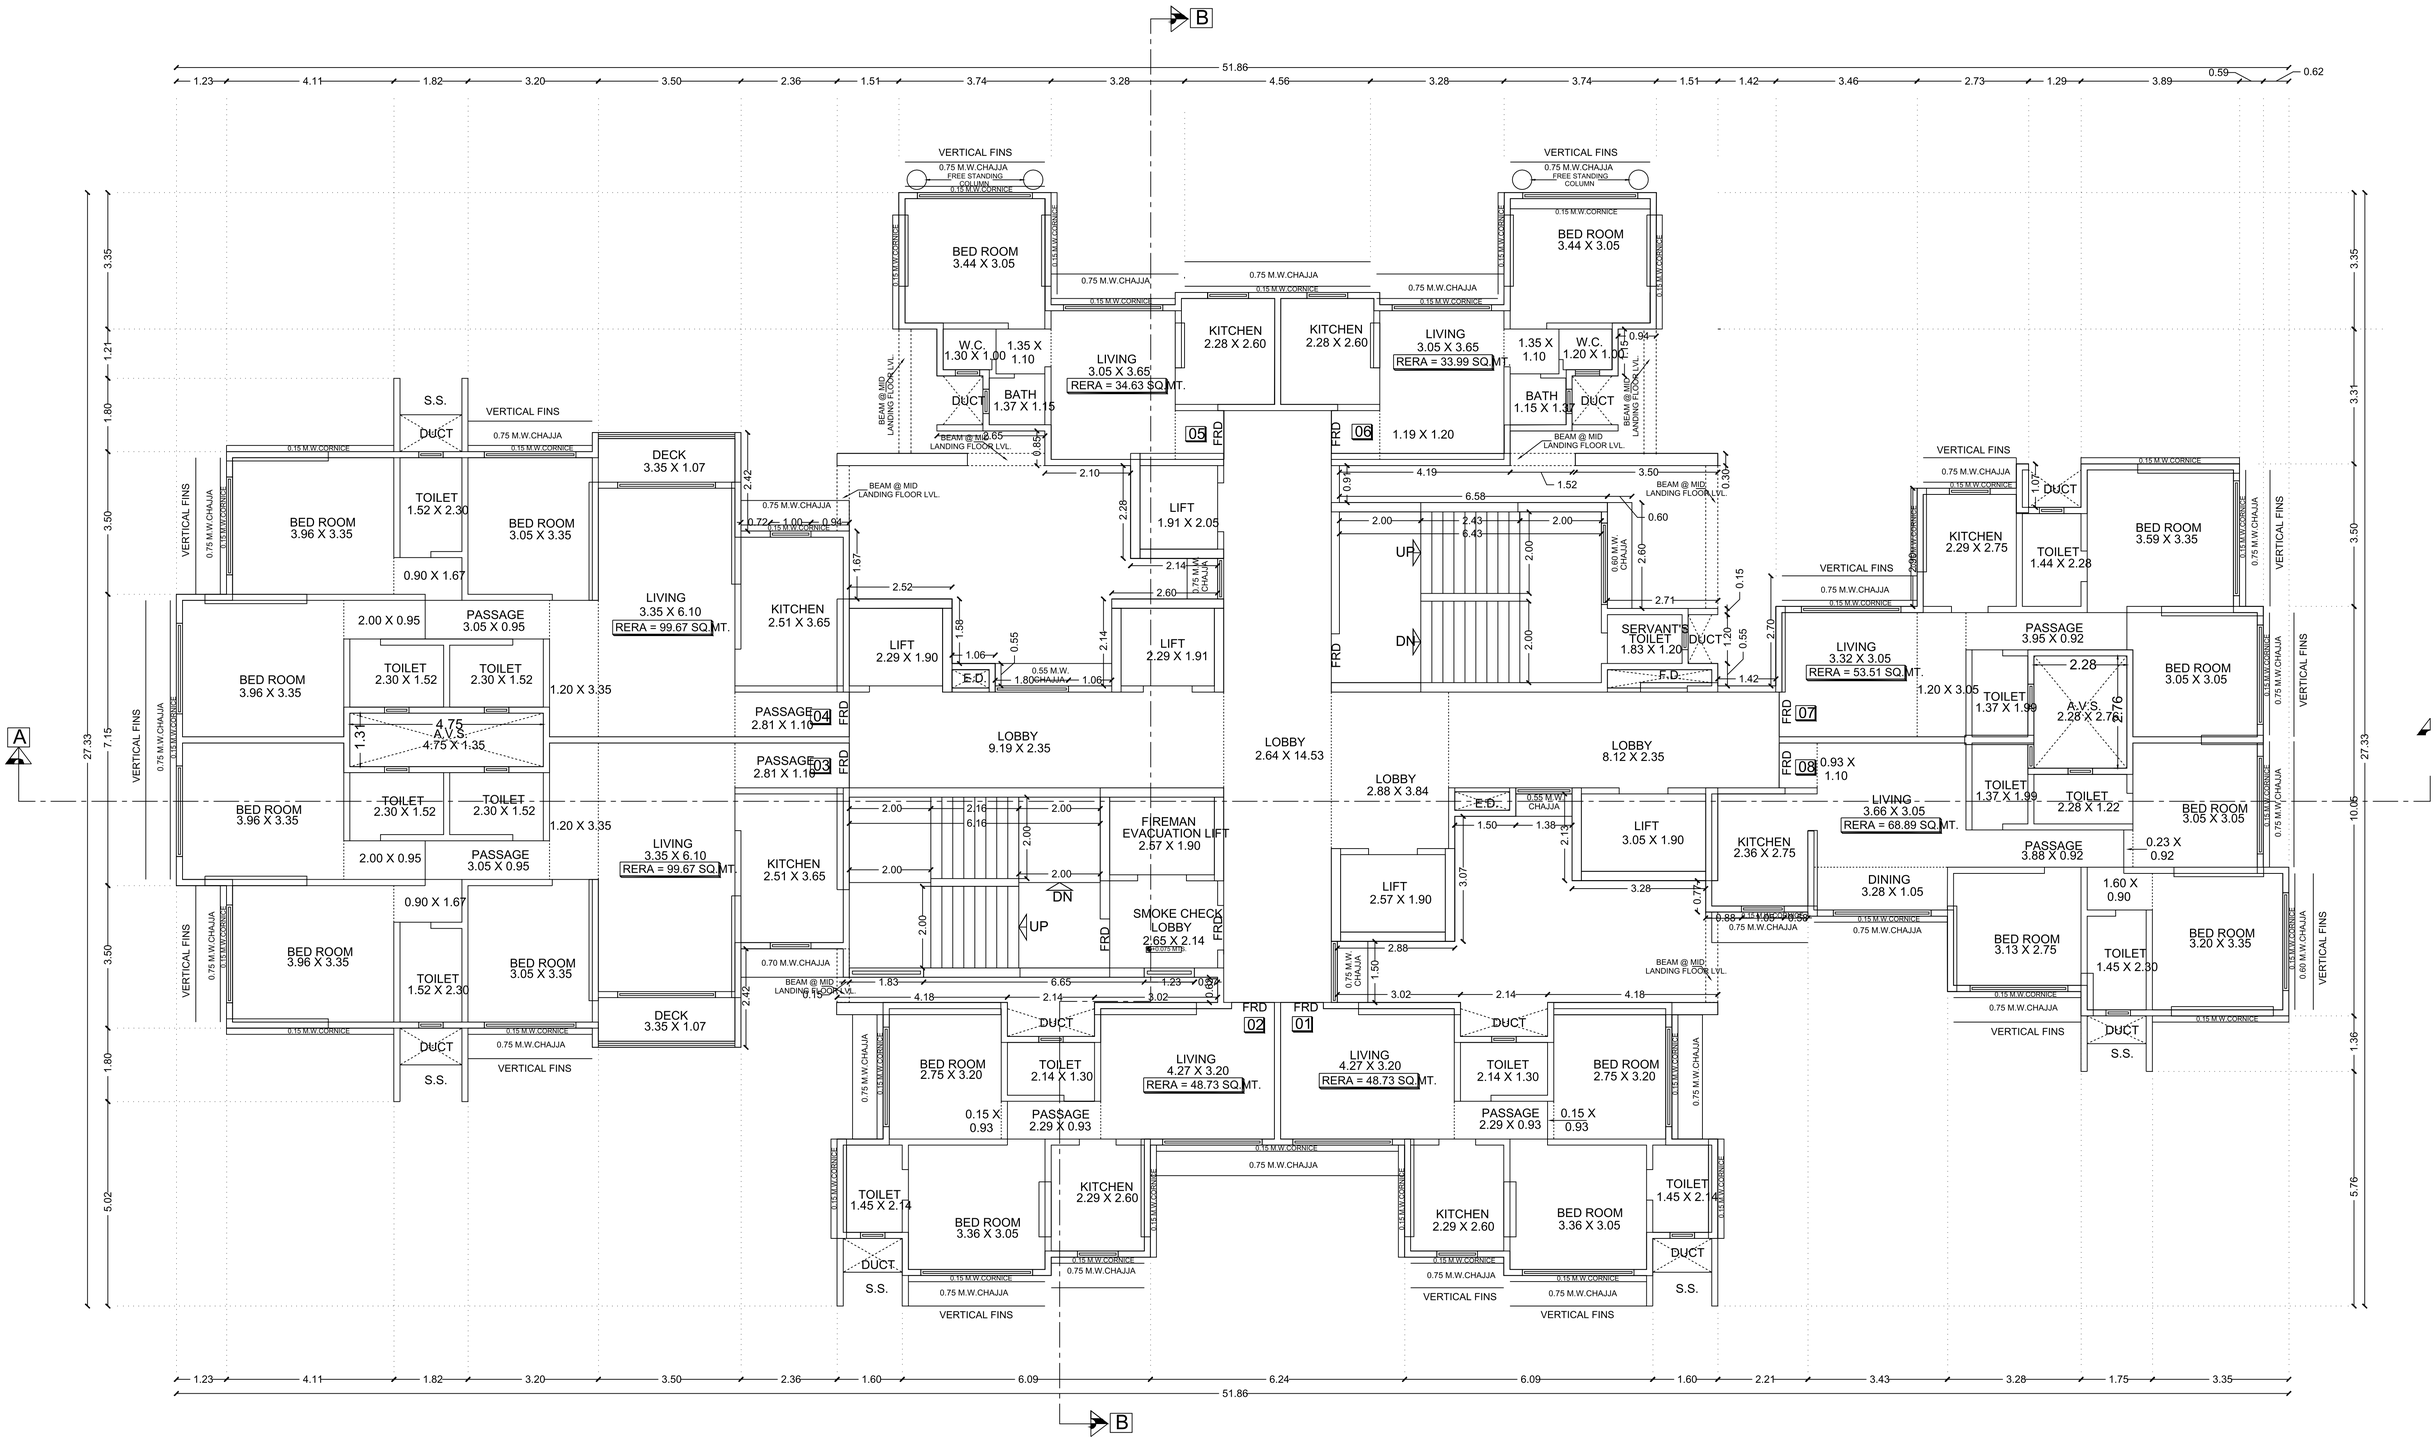


3RD FLOOR PLAN

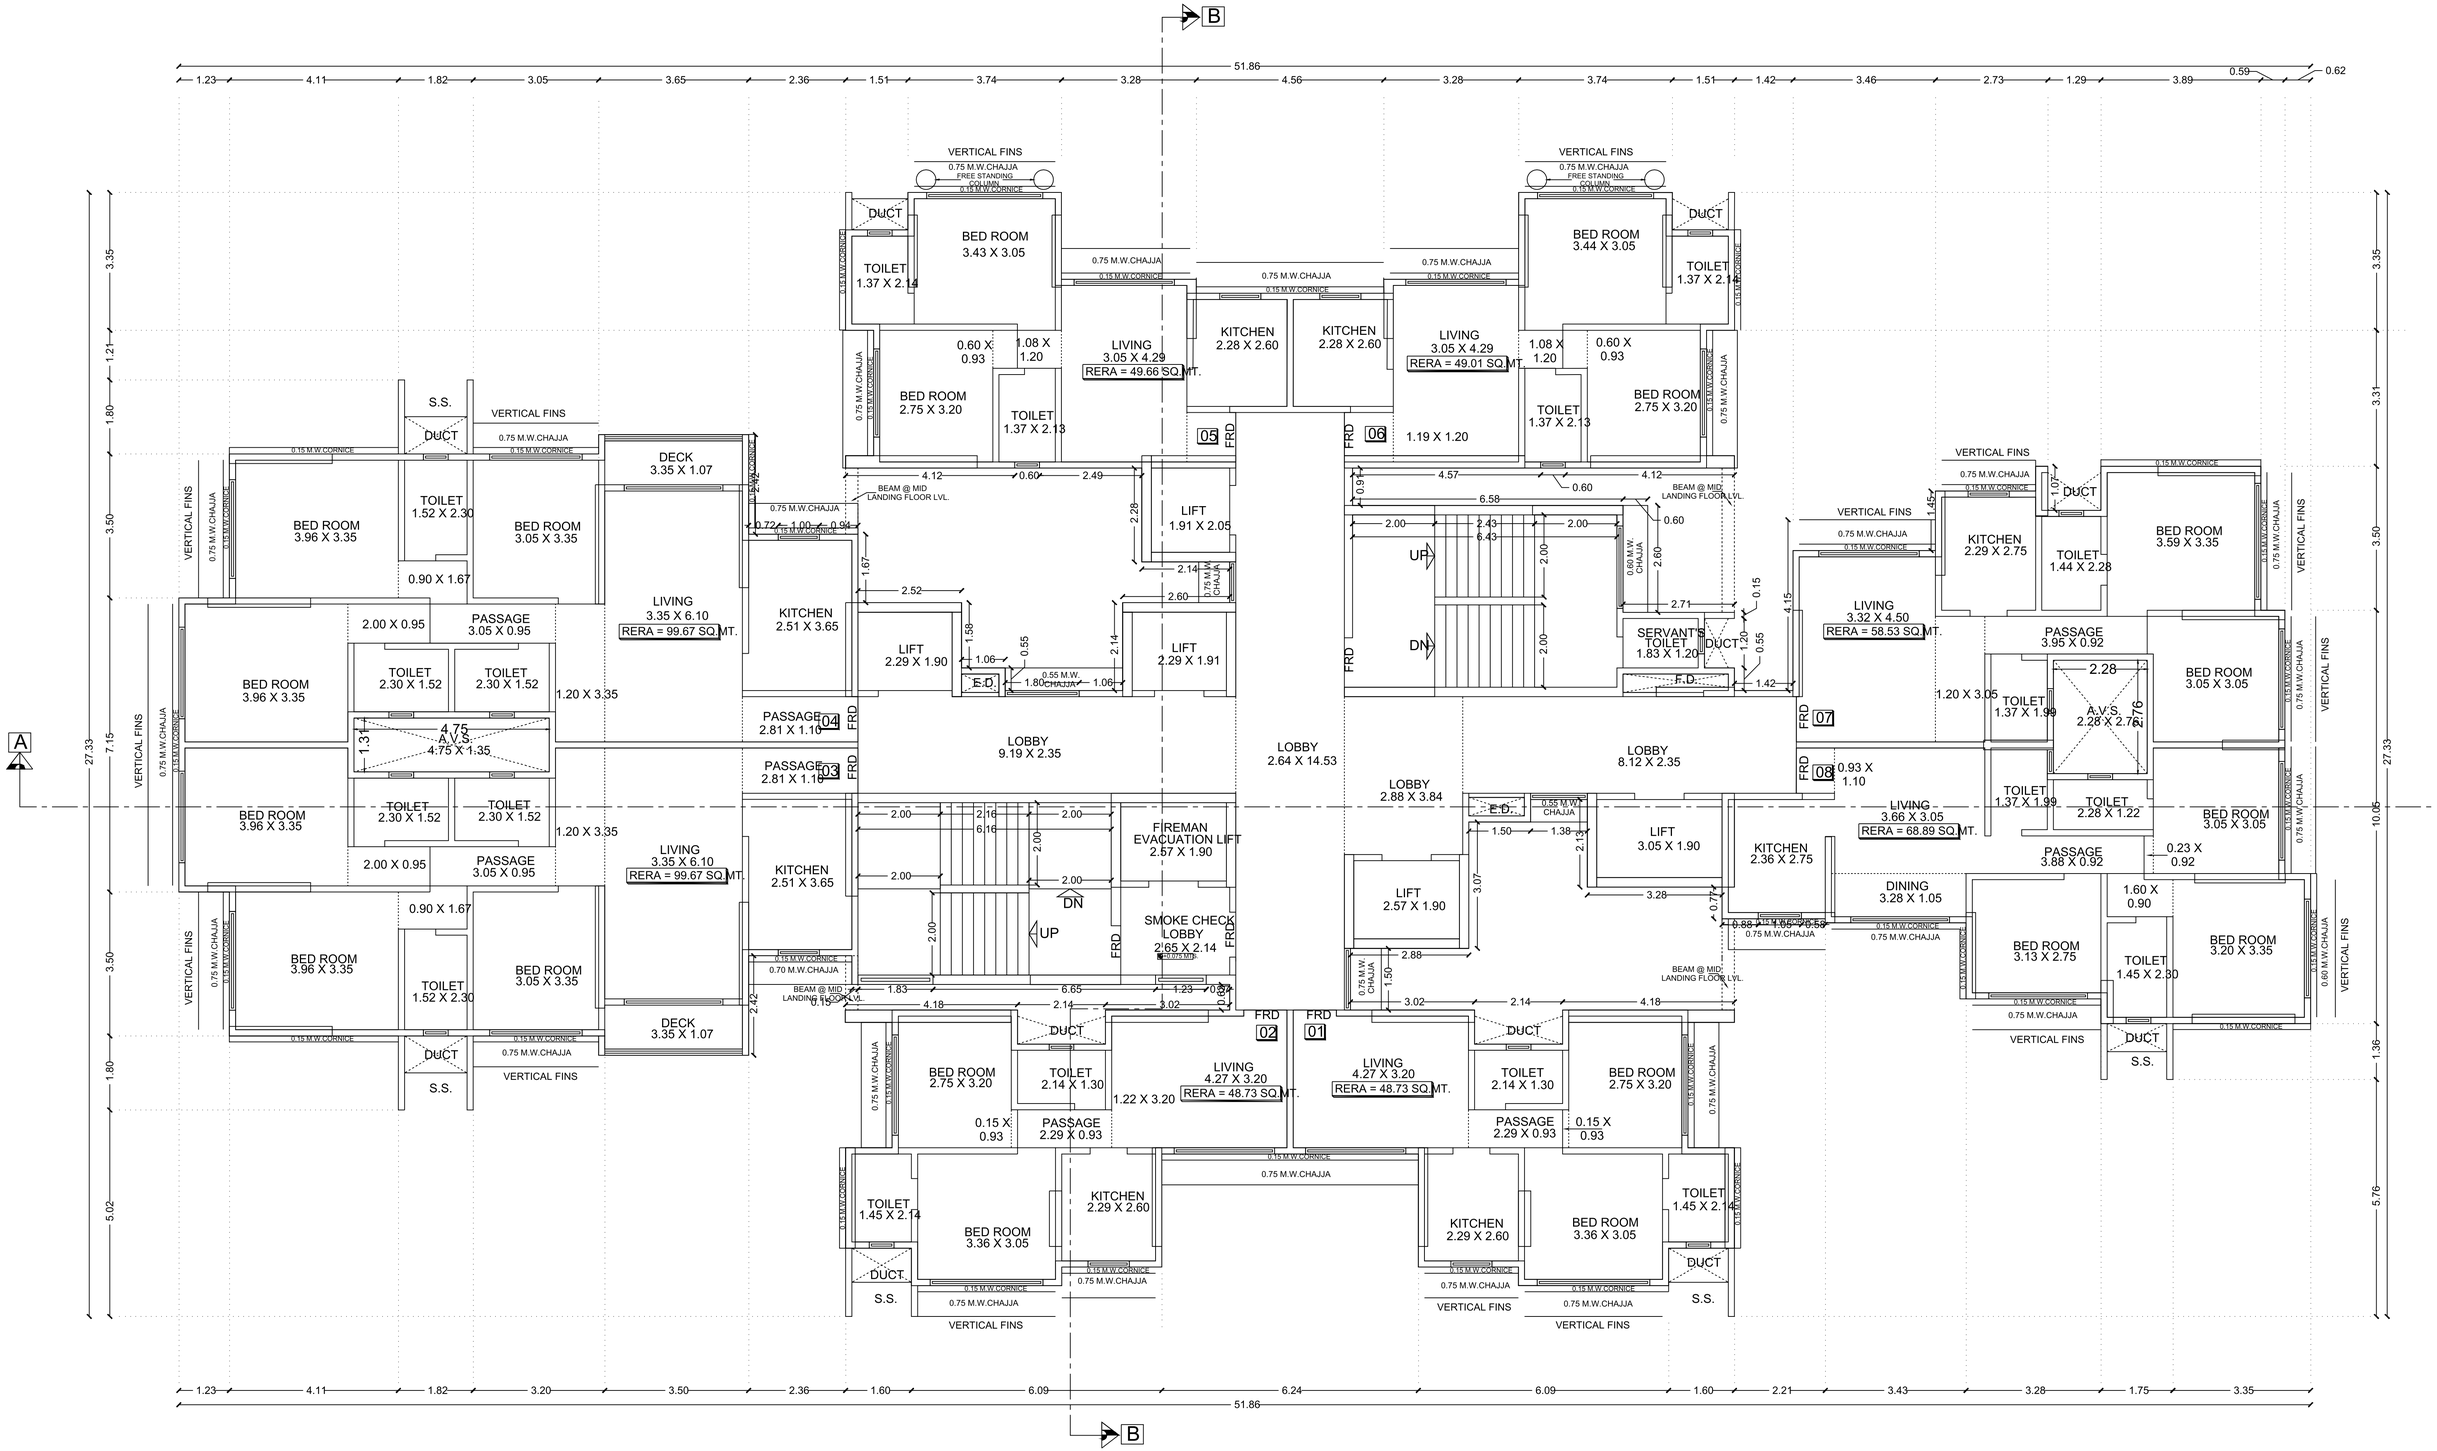

4TH TO 8TH, 10TH & 11TH FLOOR PLAN


SCALE - 1:100

SCALE - 1:100

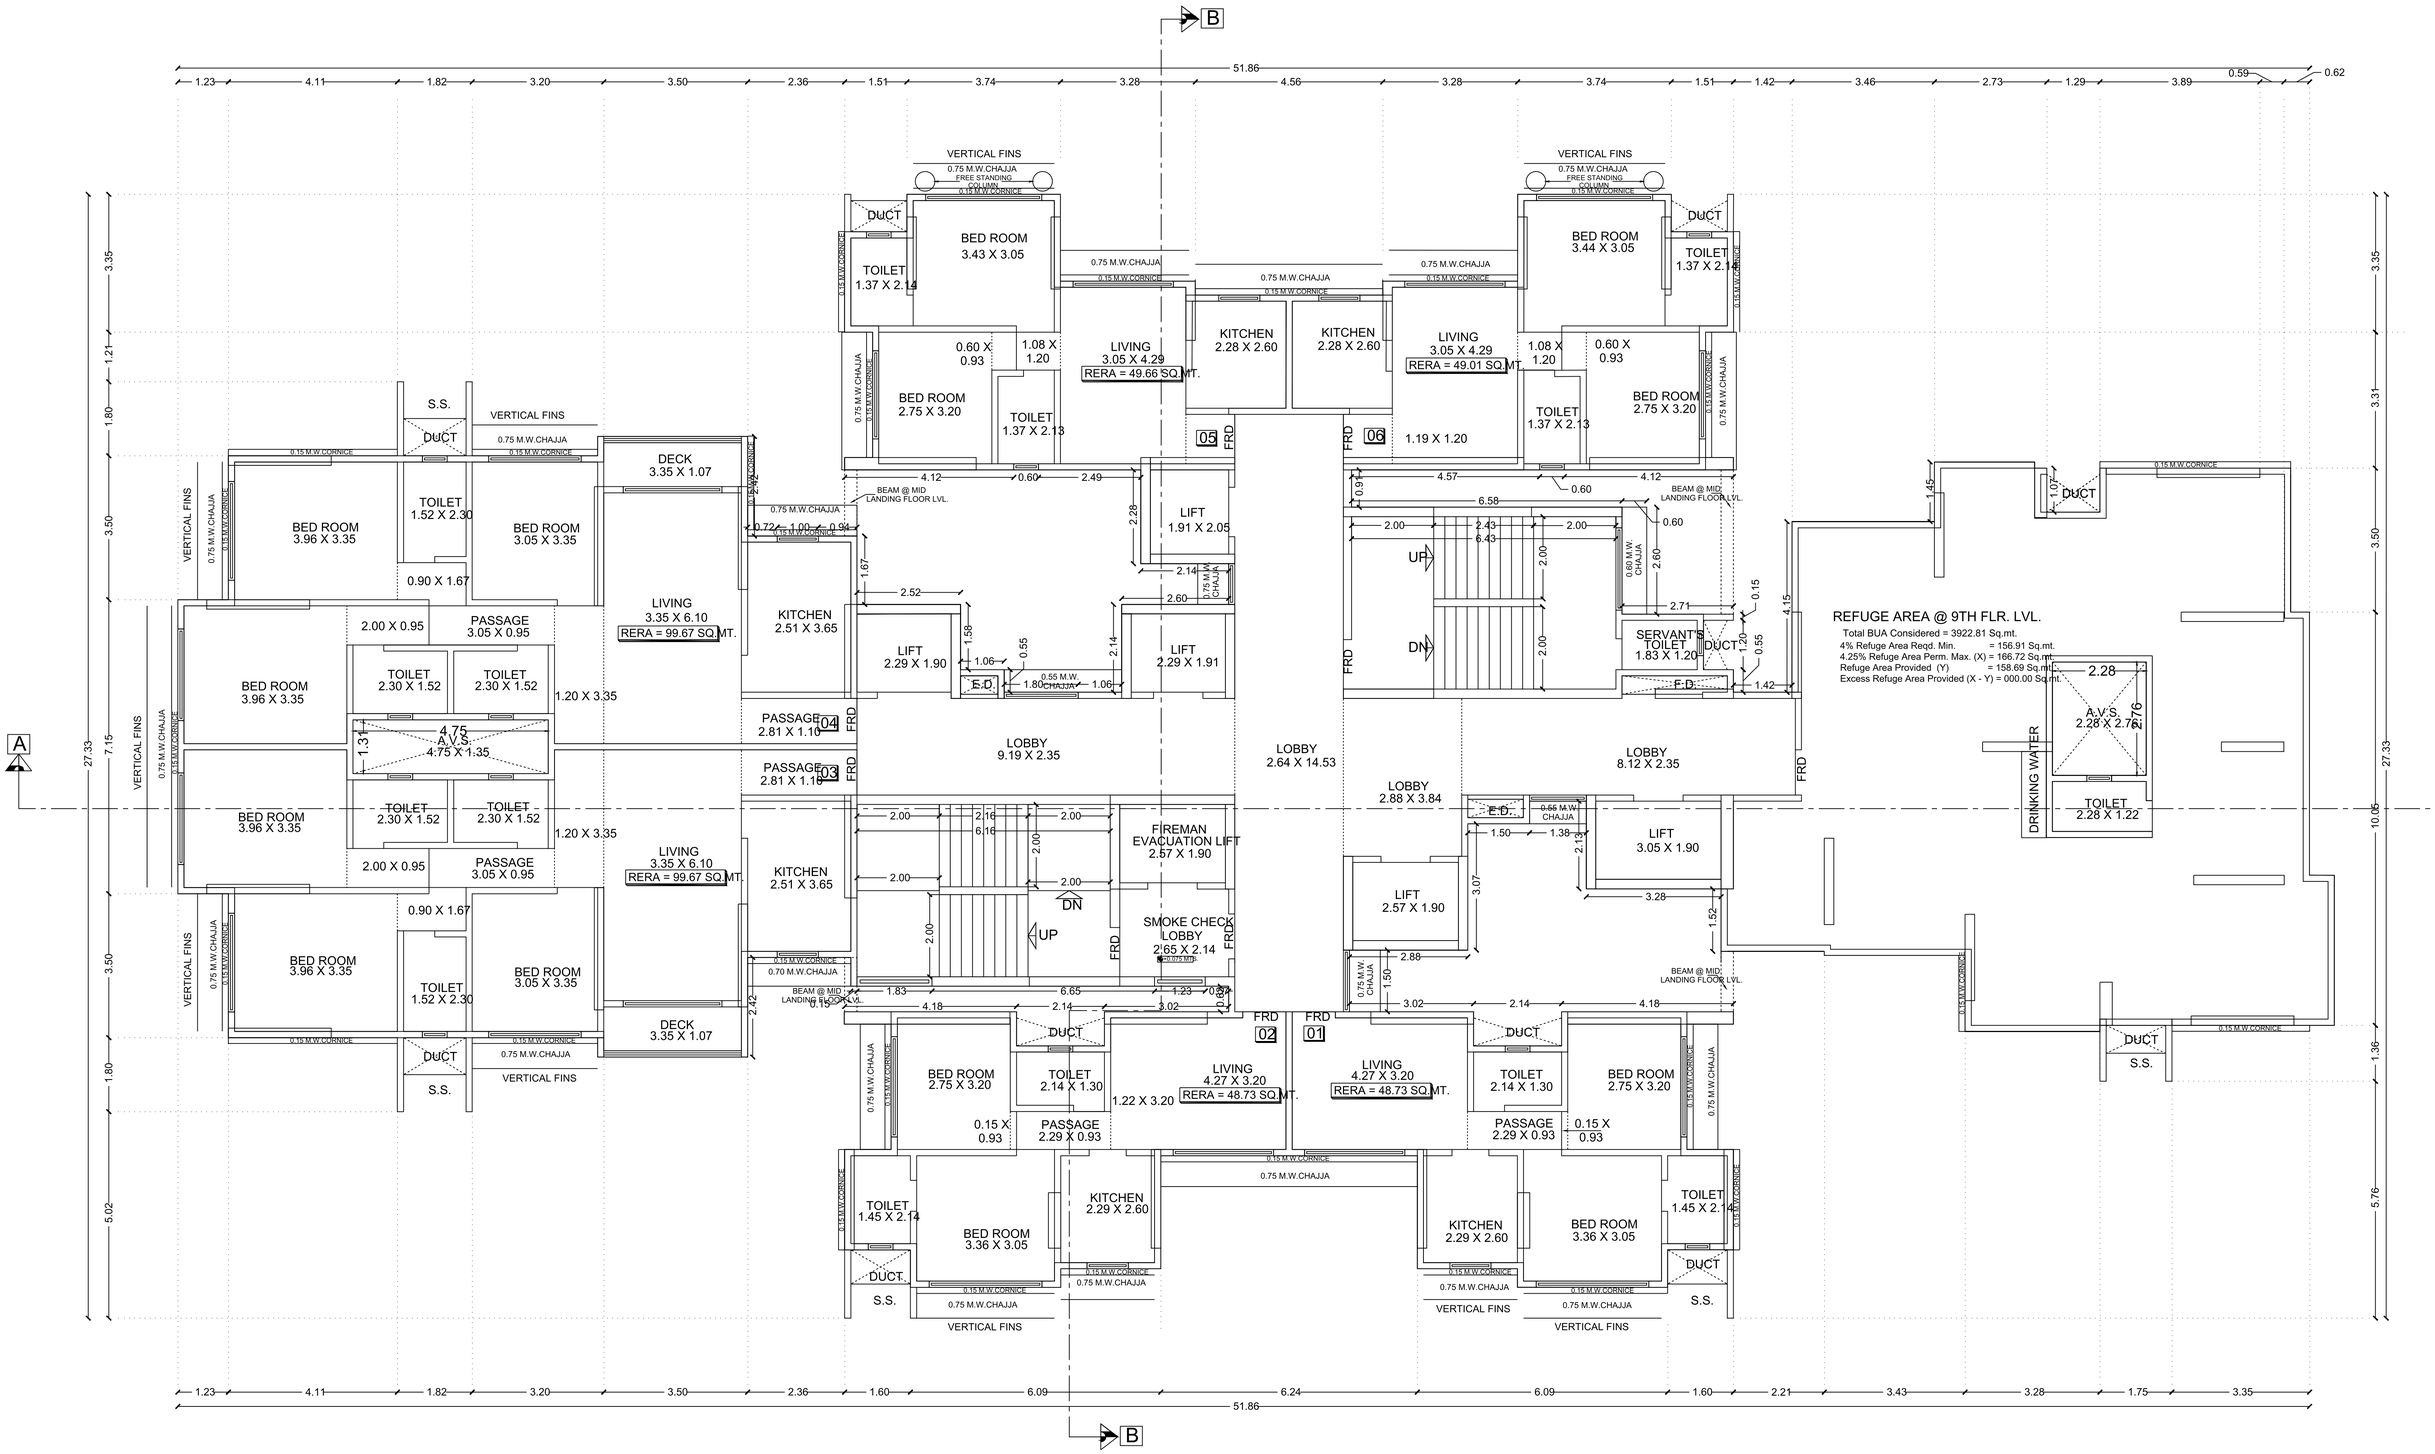


9TH REFUGE FLOOR PLAN

SCALE - 1:100

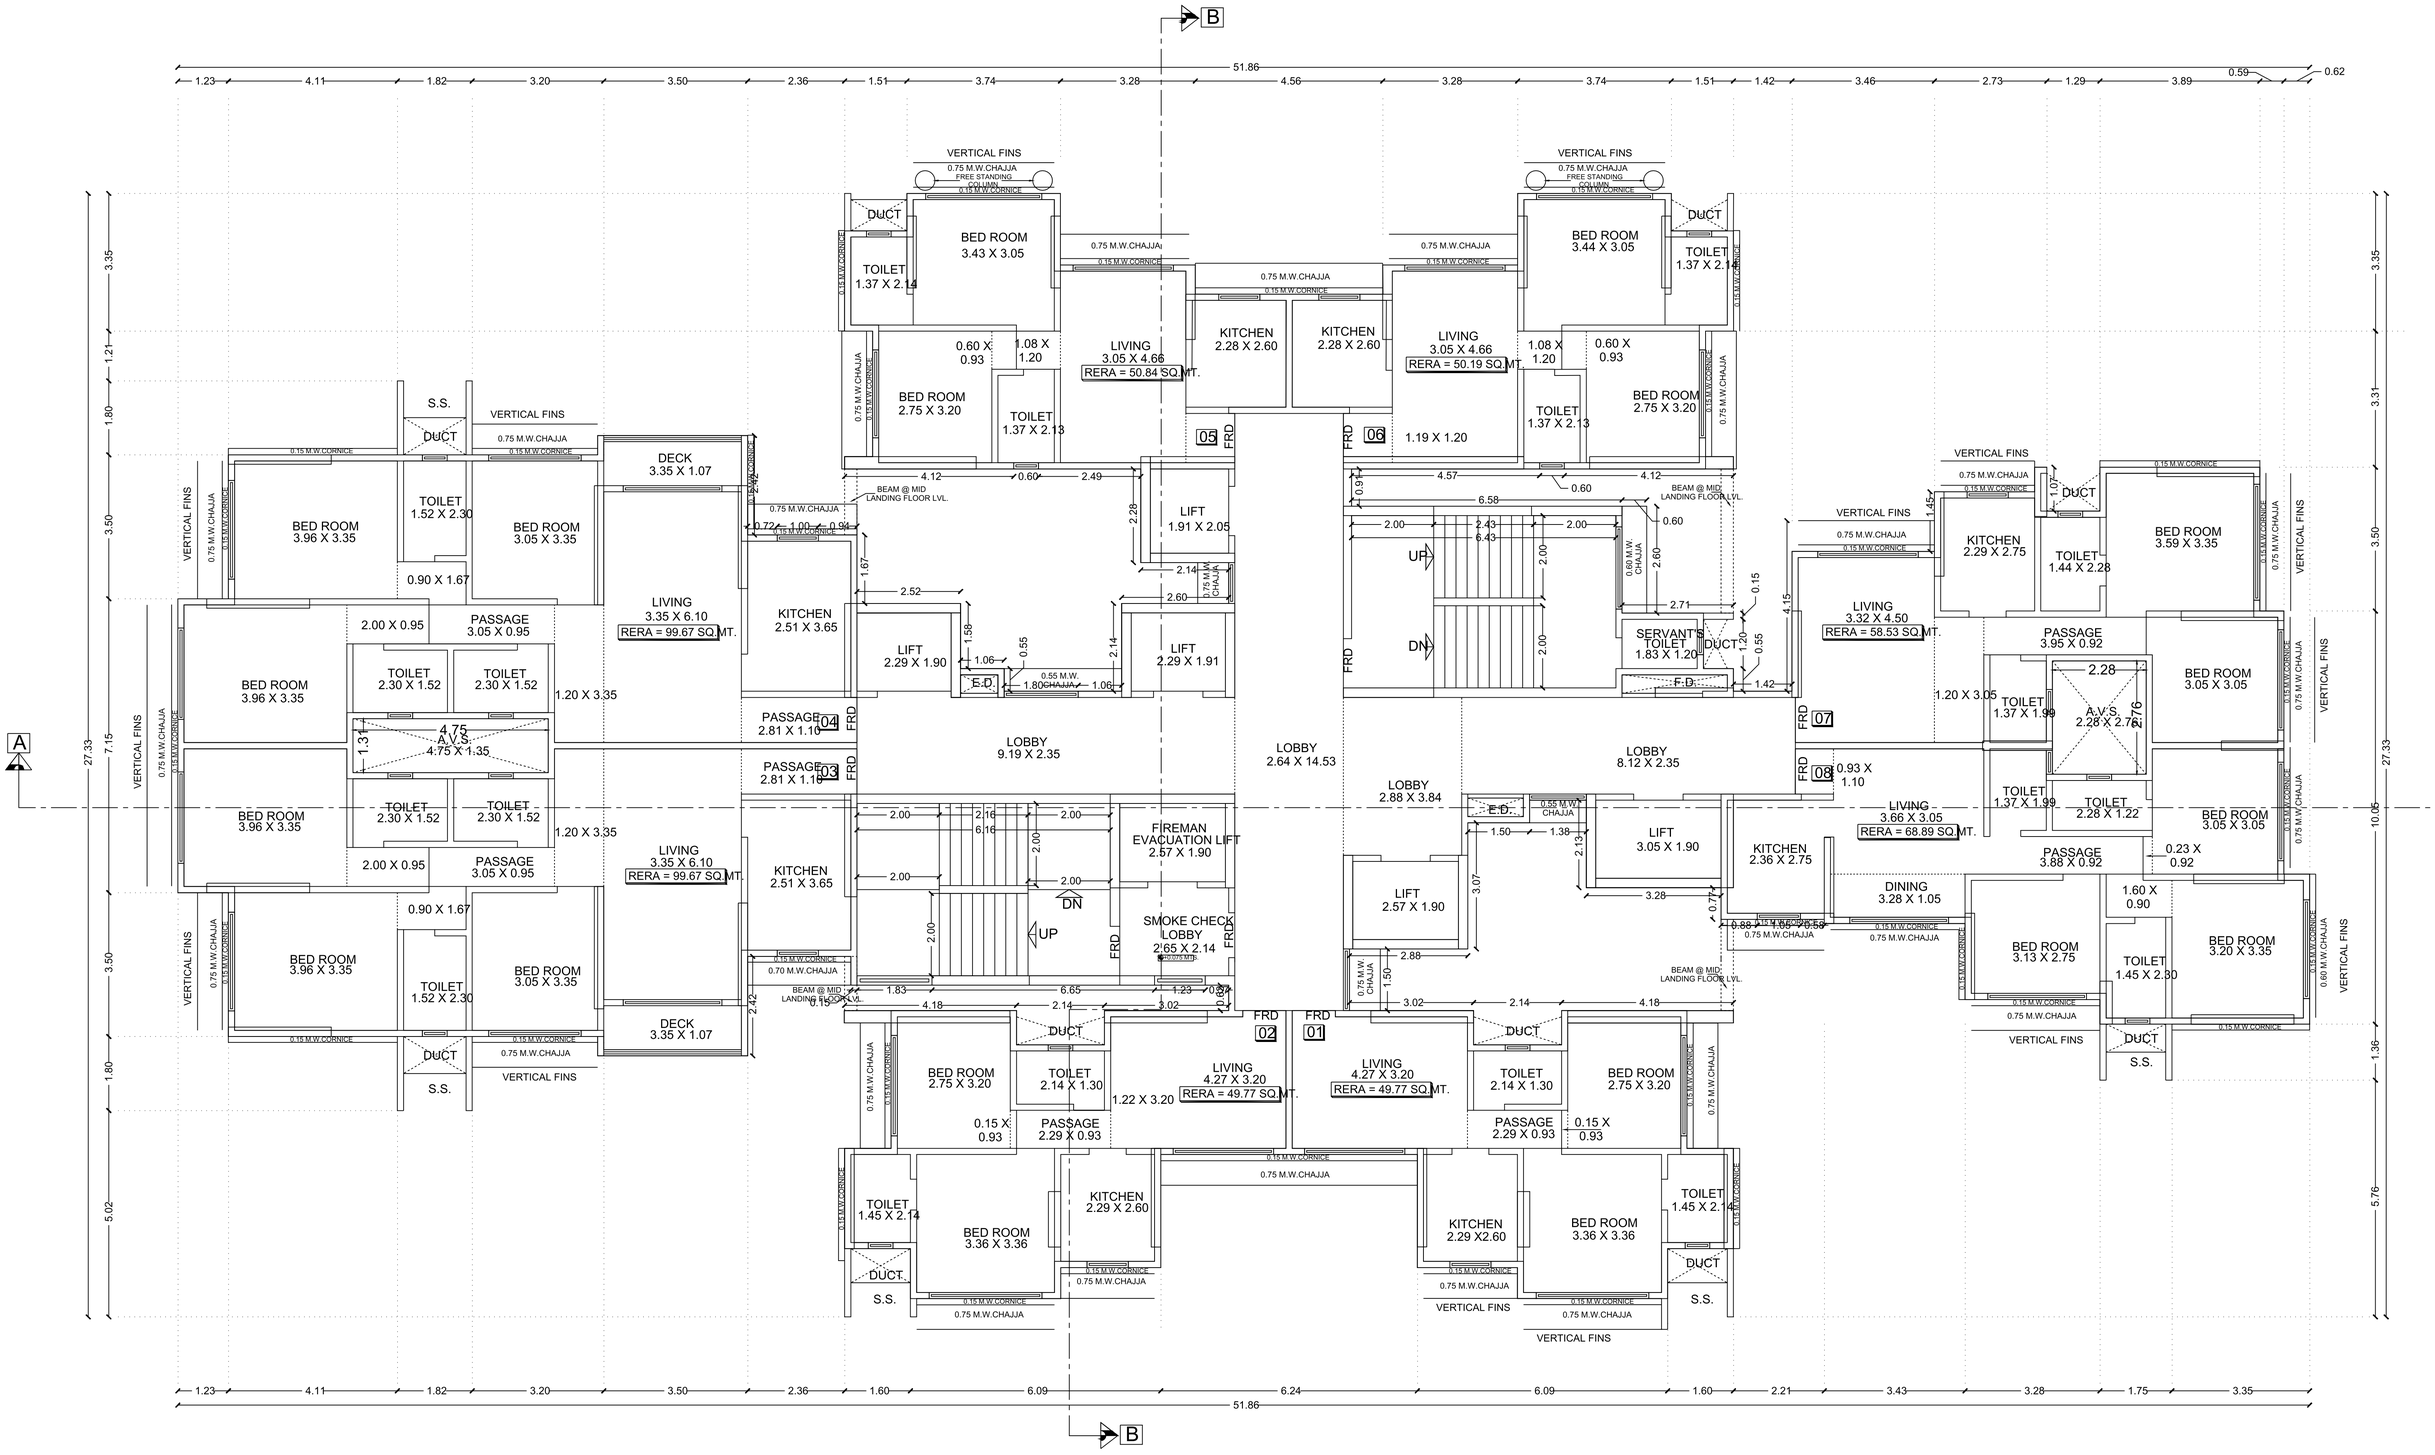


12TH & 13TH FLOOR PLAN

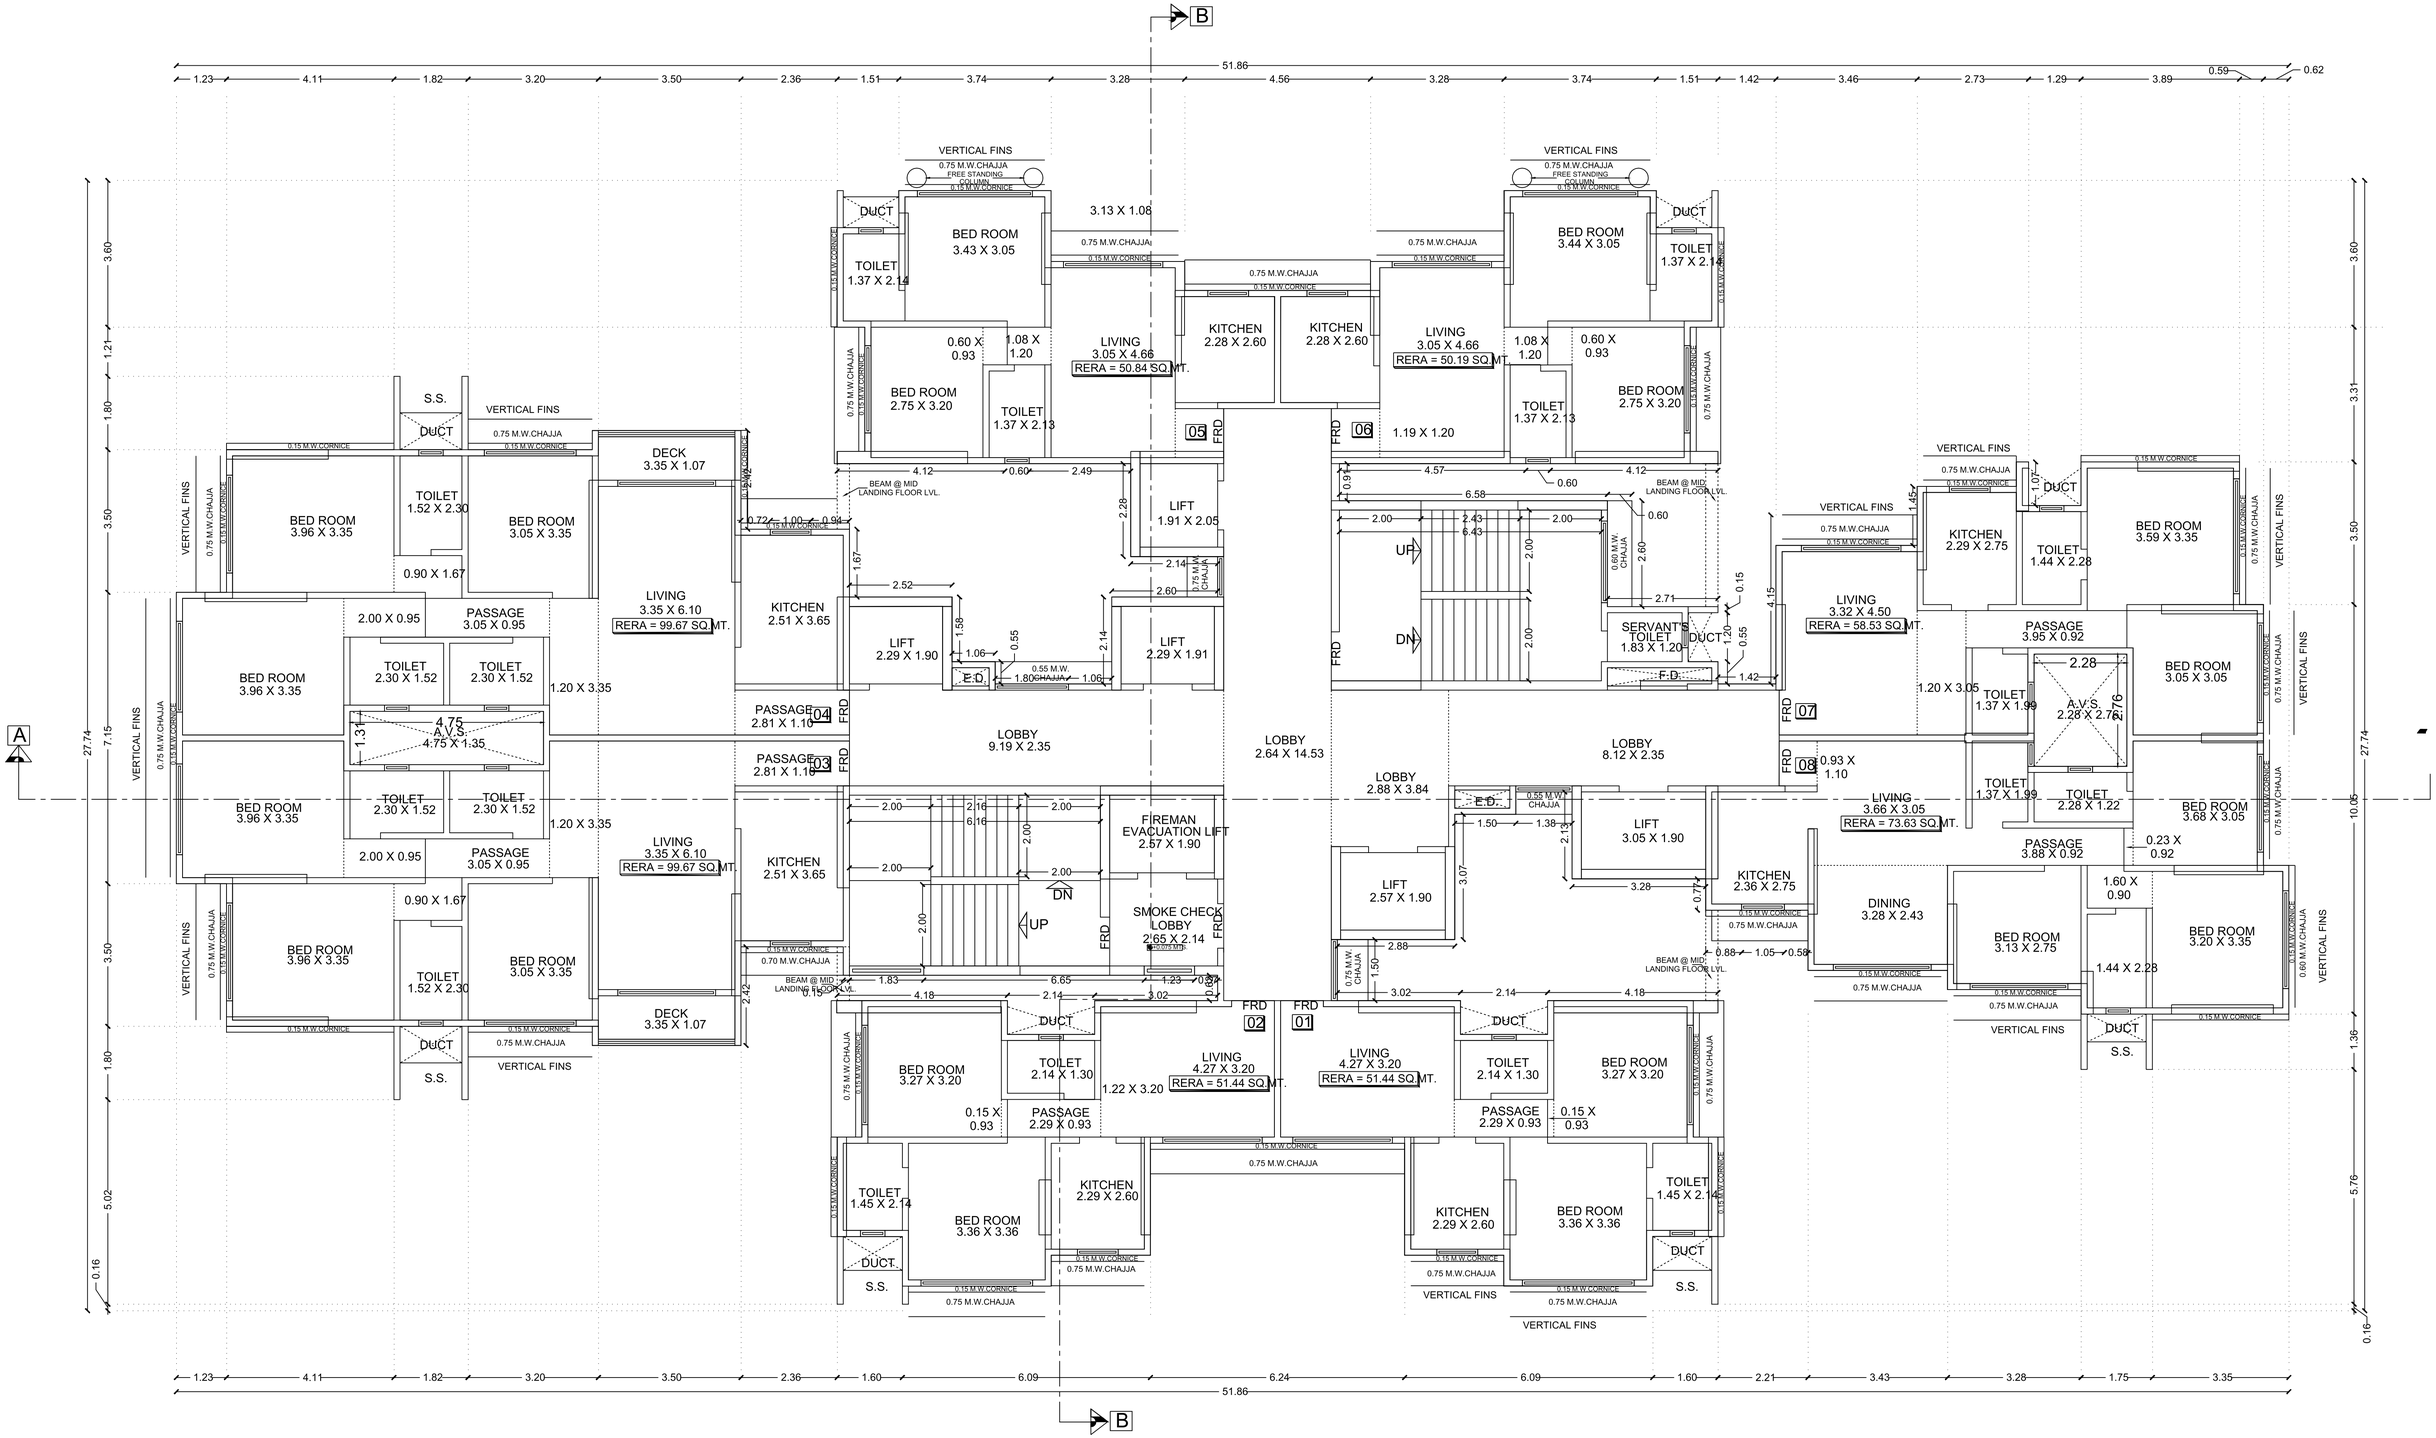

14TH FLOOR PLAN


SCALE - 1:100

SCALE - 1:100

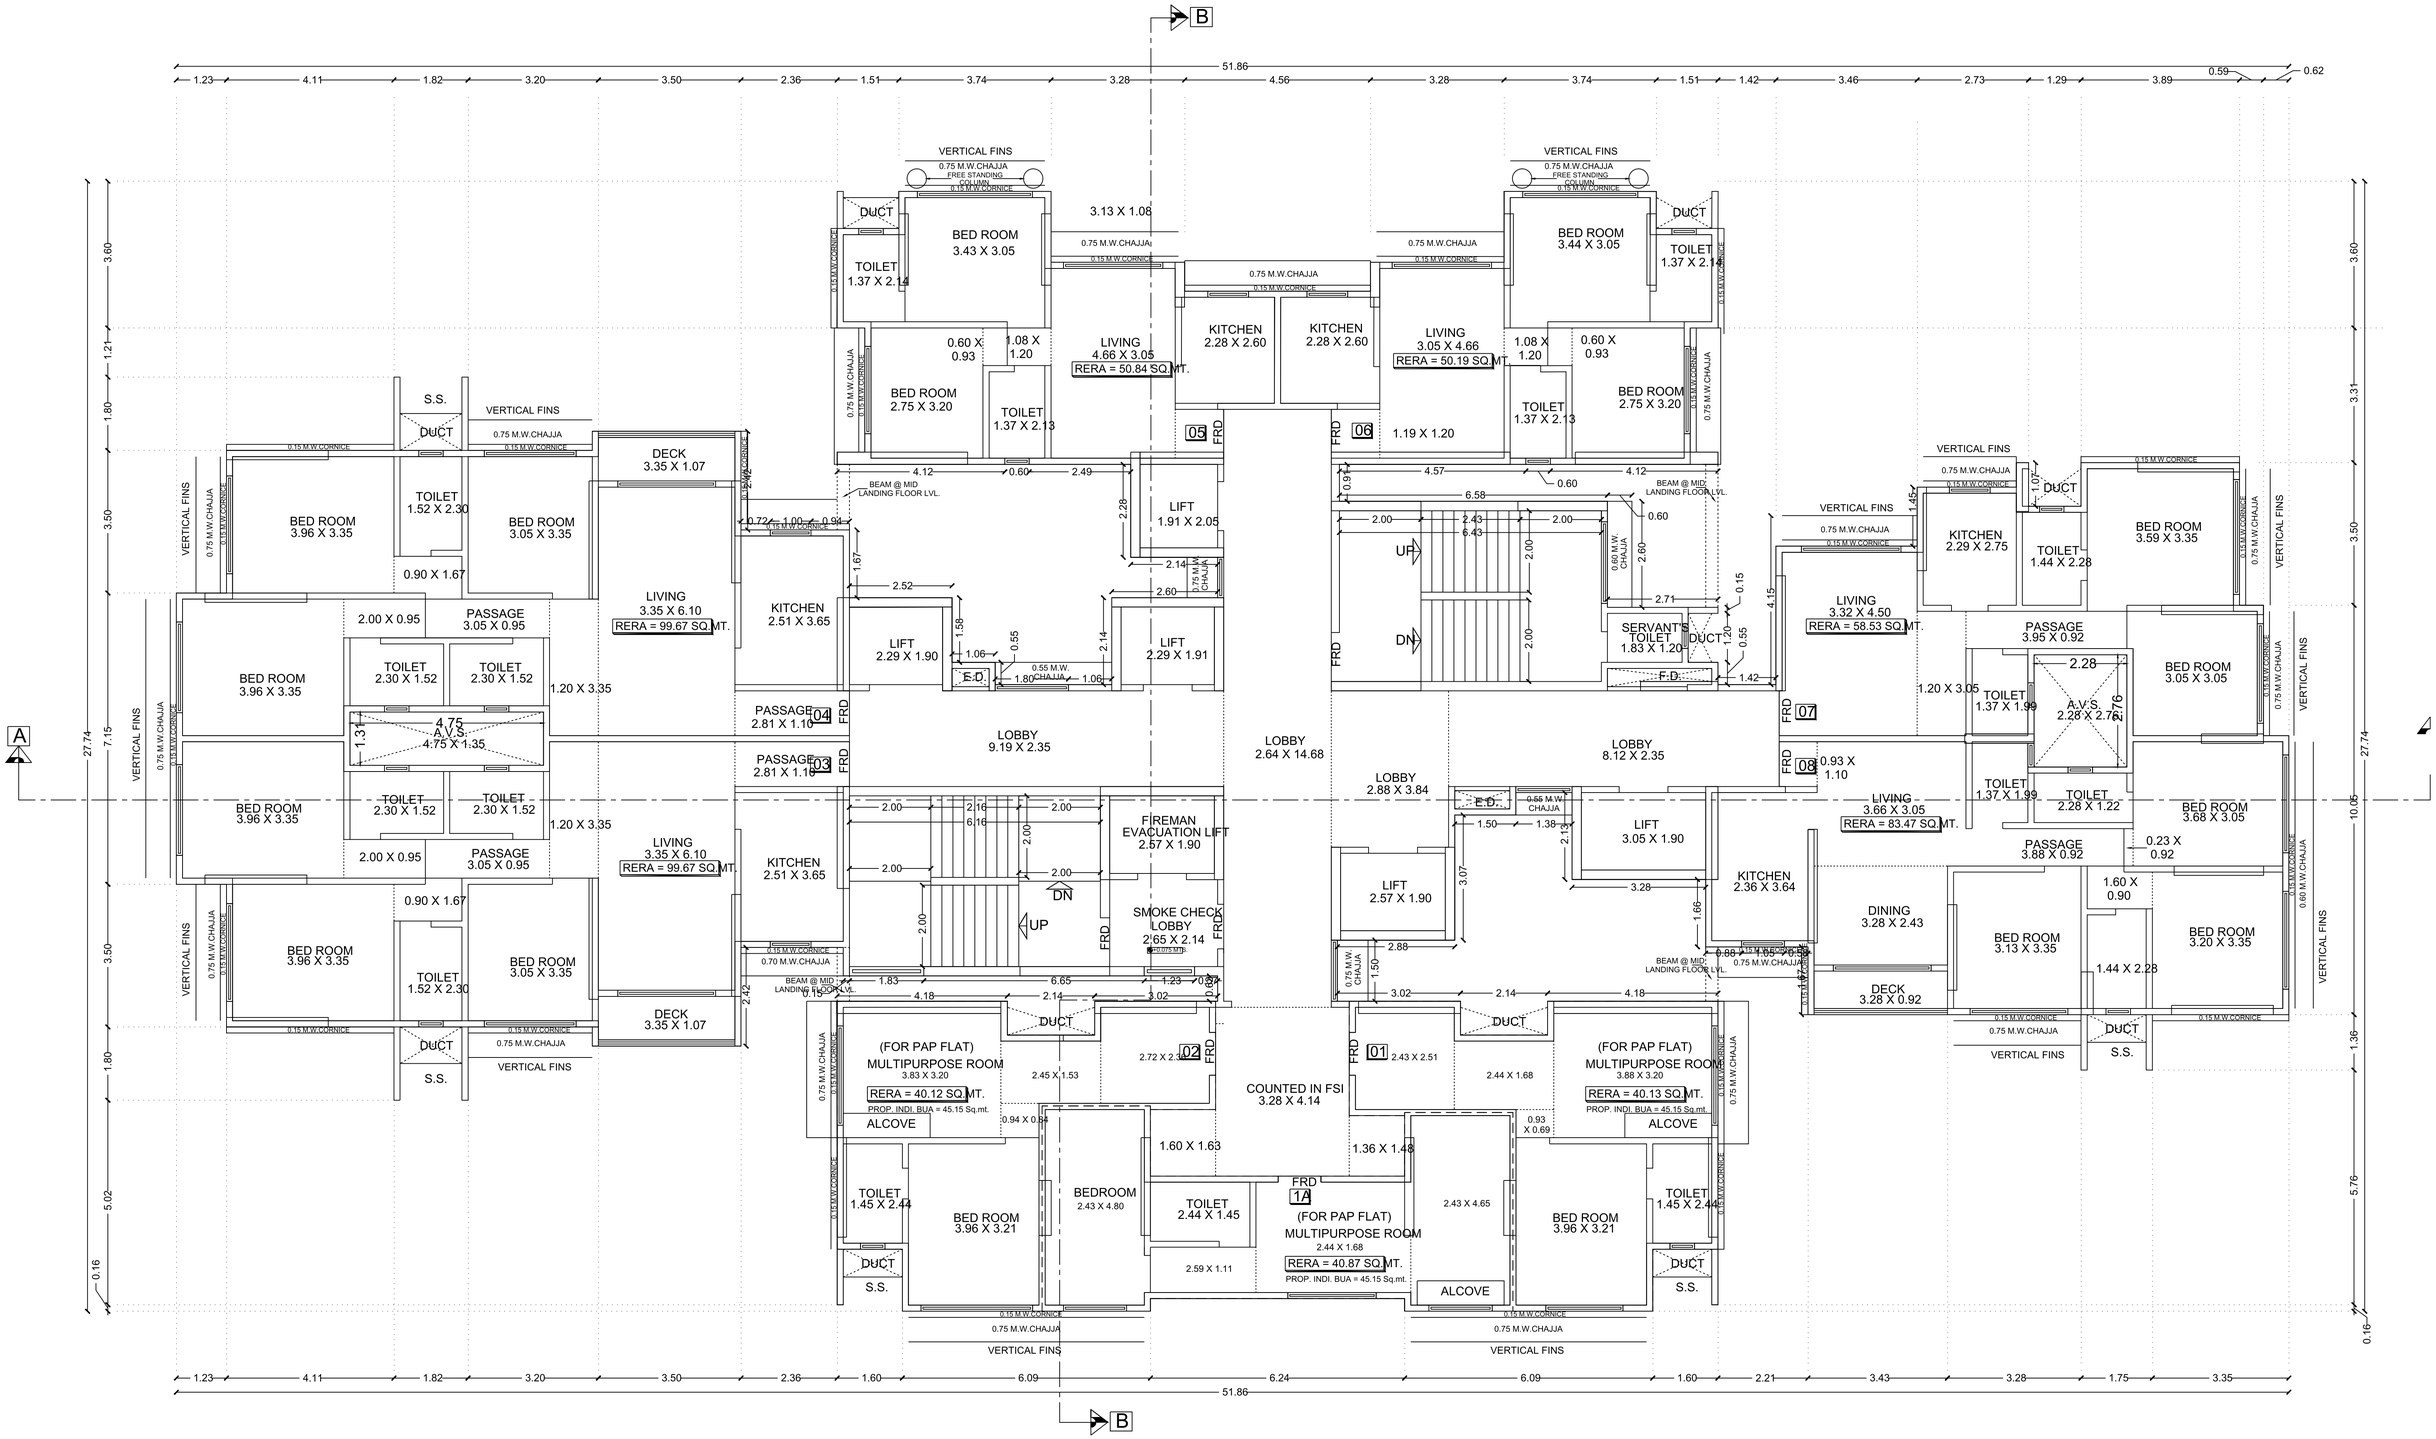


15TH FLOOR PLAN

SCALE - 1:100

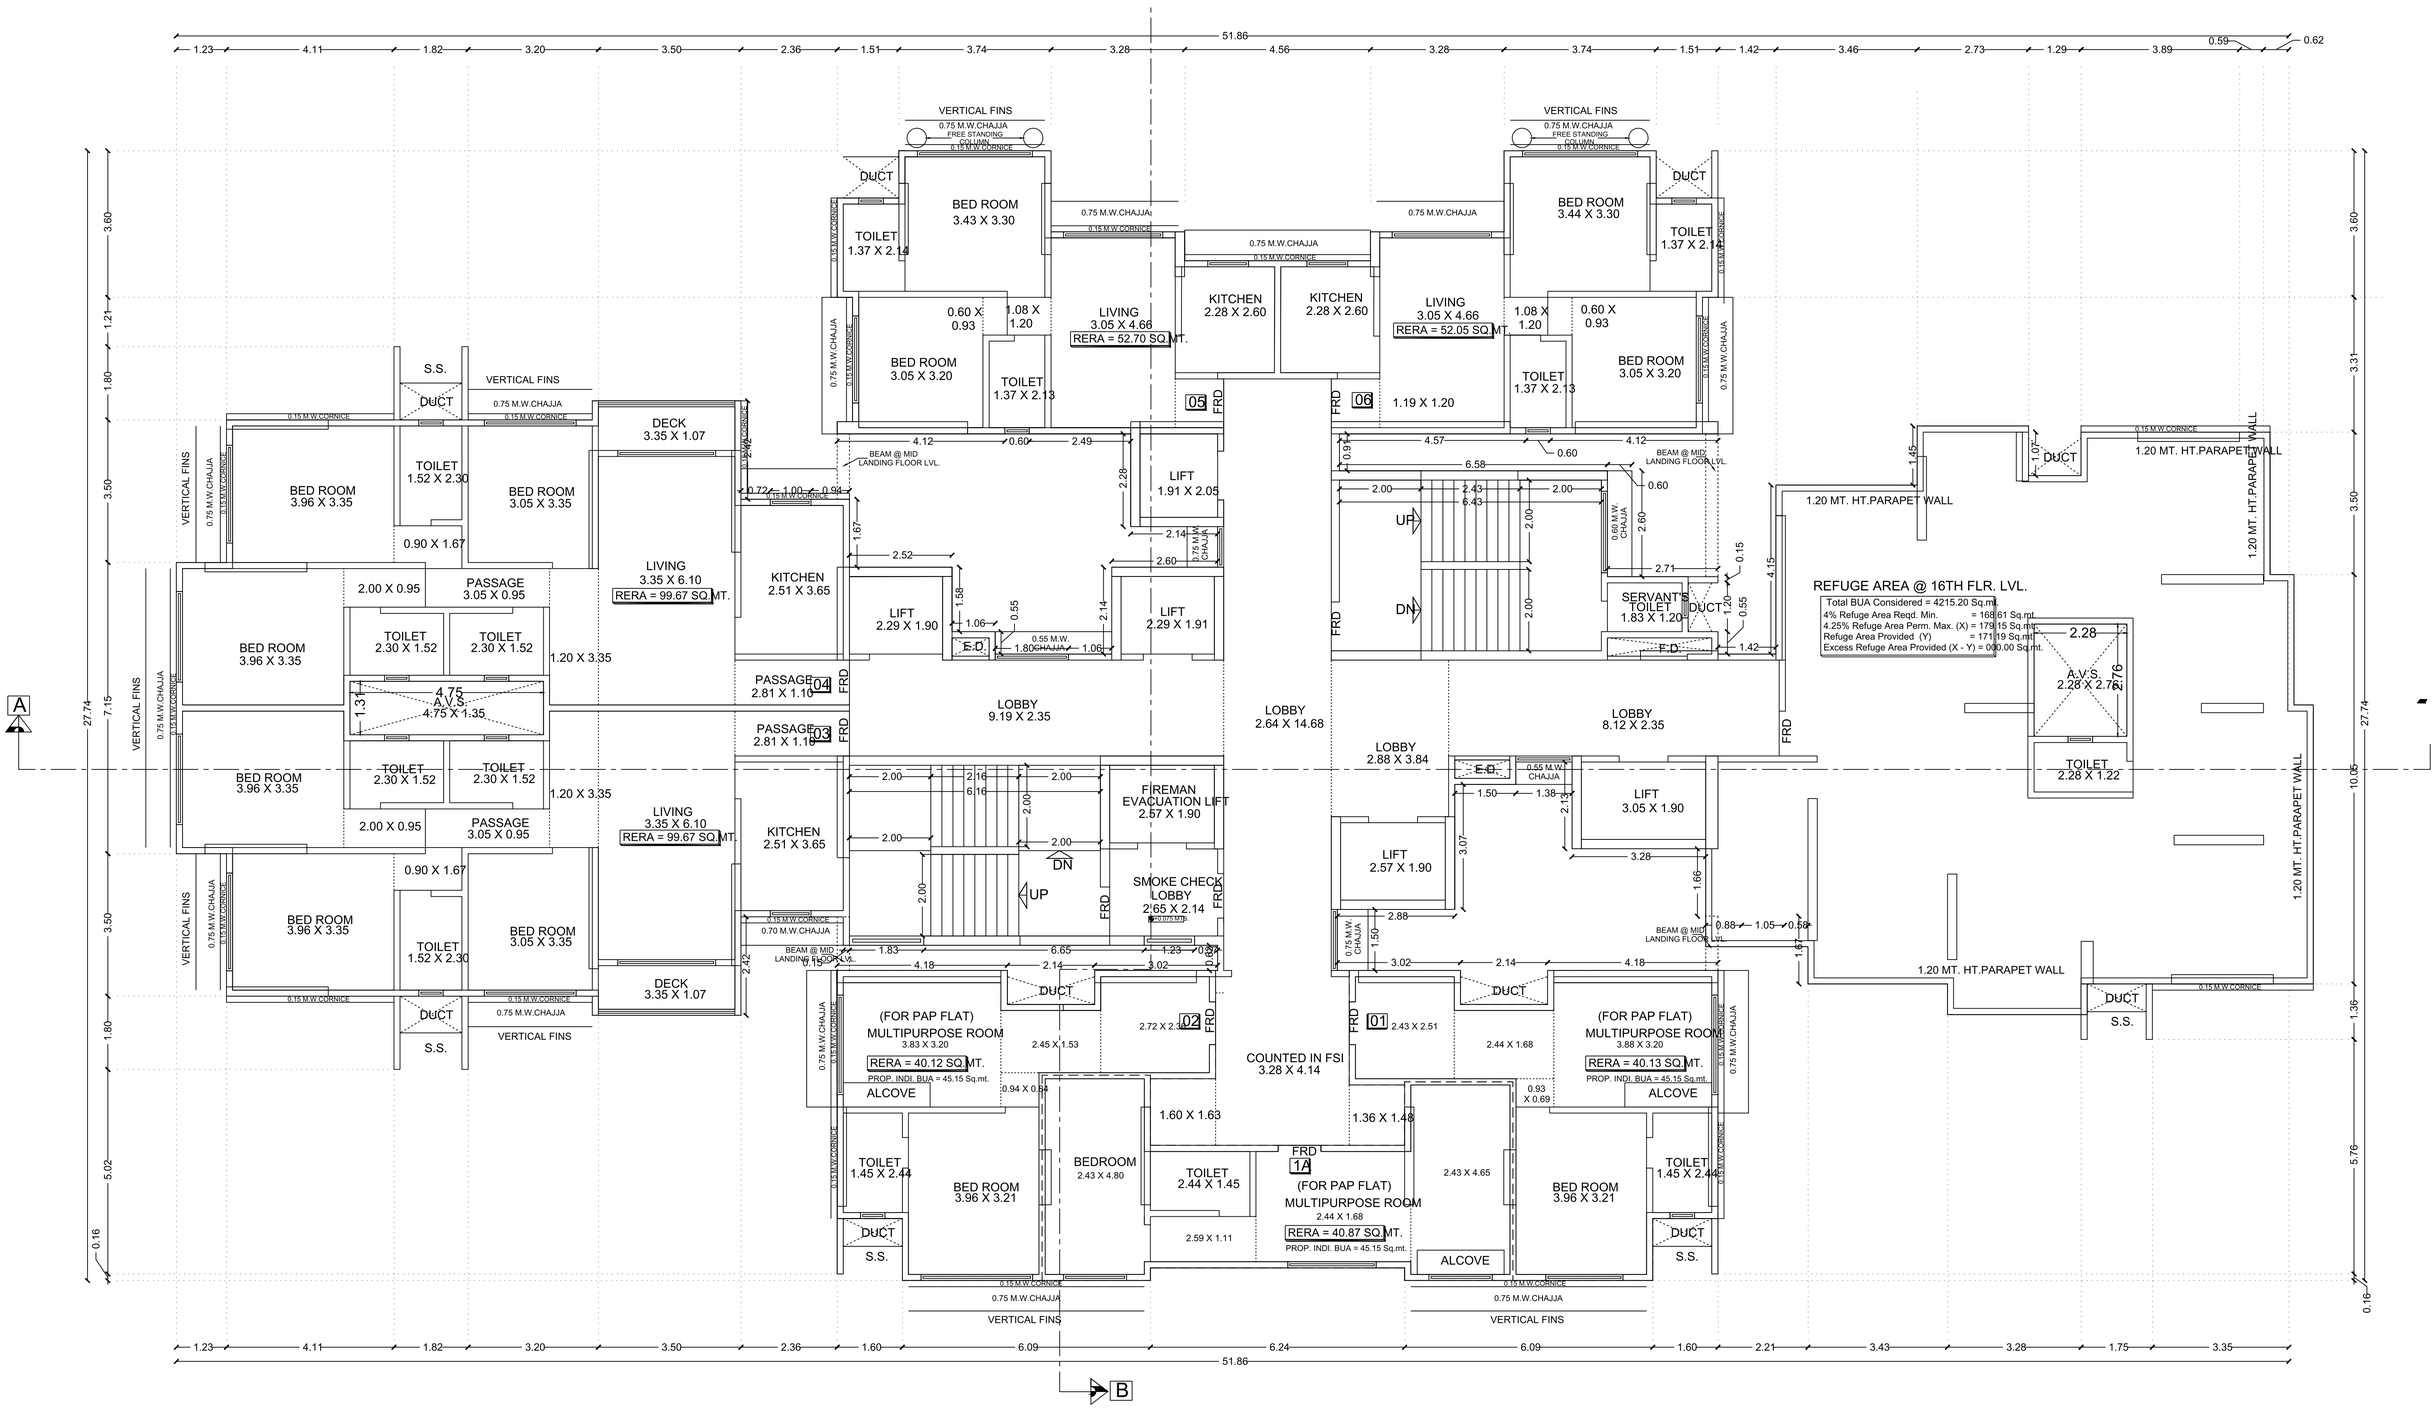


16TH REFUGE FLOOR PLAN

SCALE - 1:100

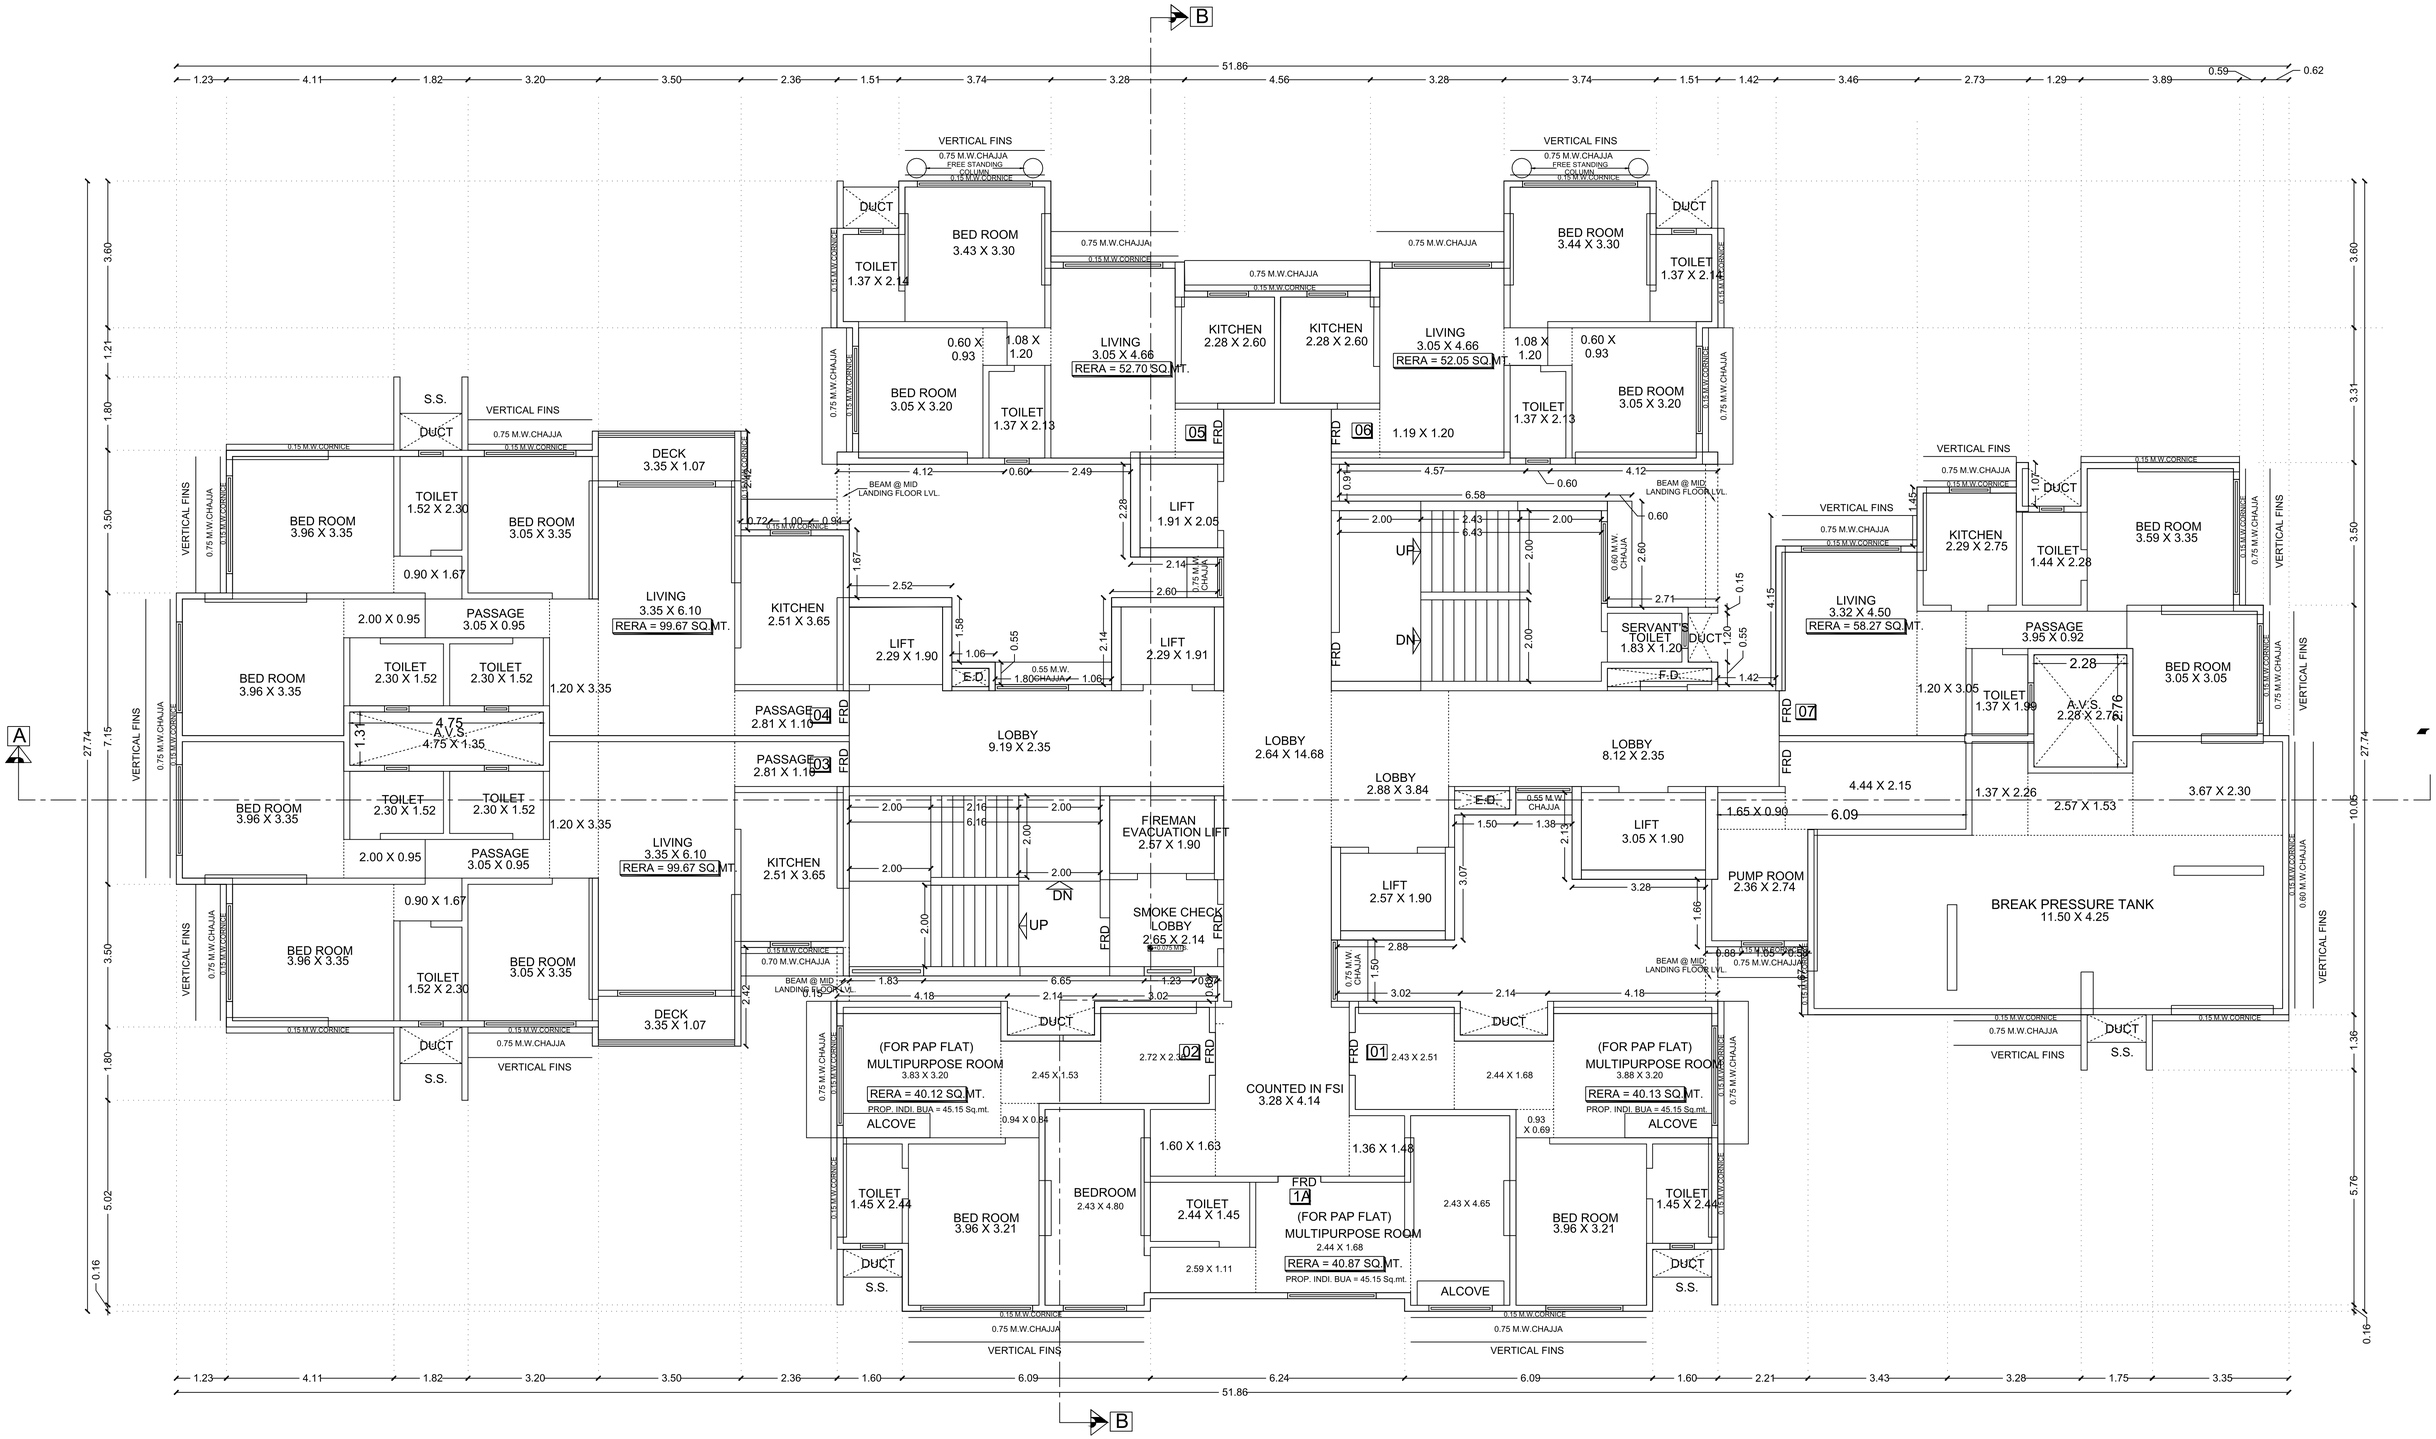


17TH FLOOR PLAN

SCALE - 1:100

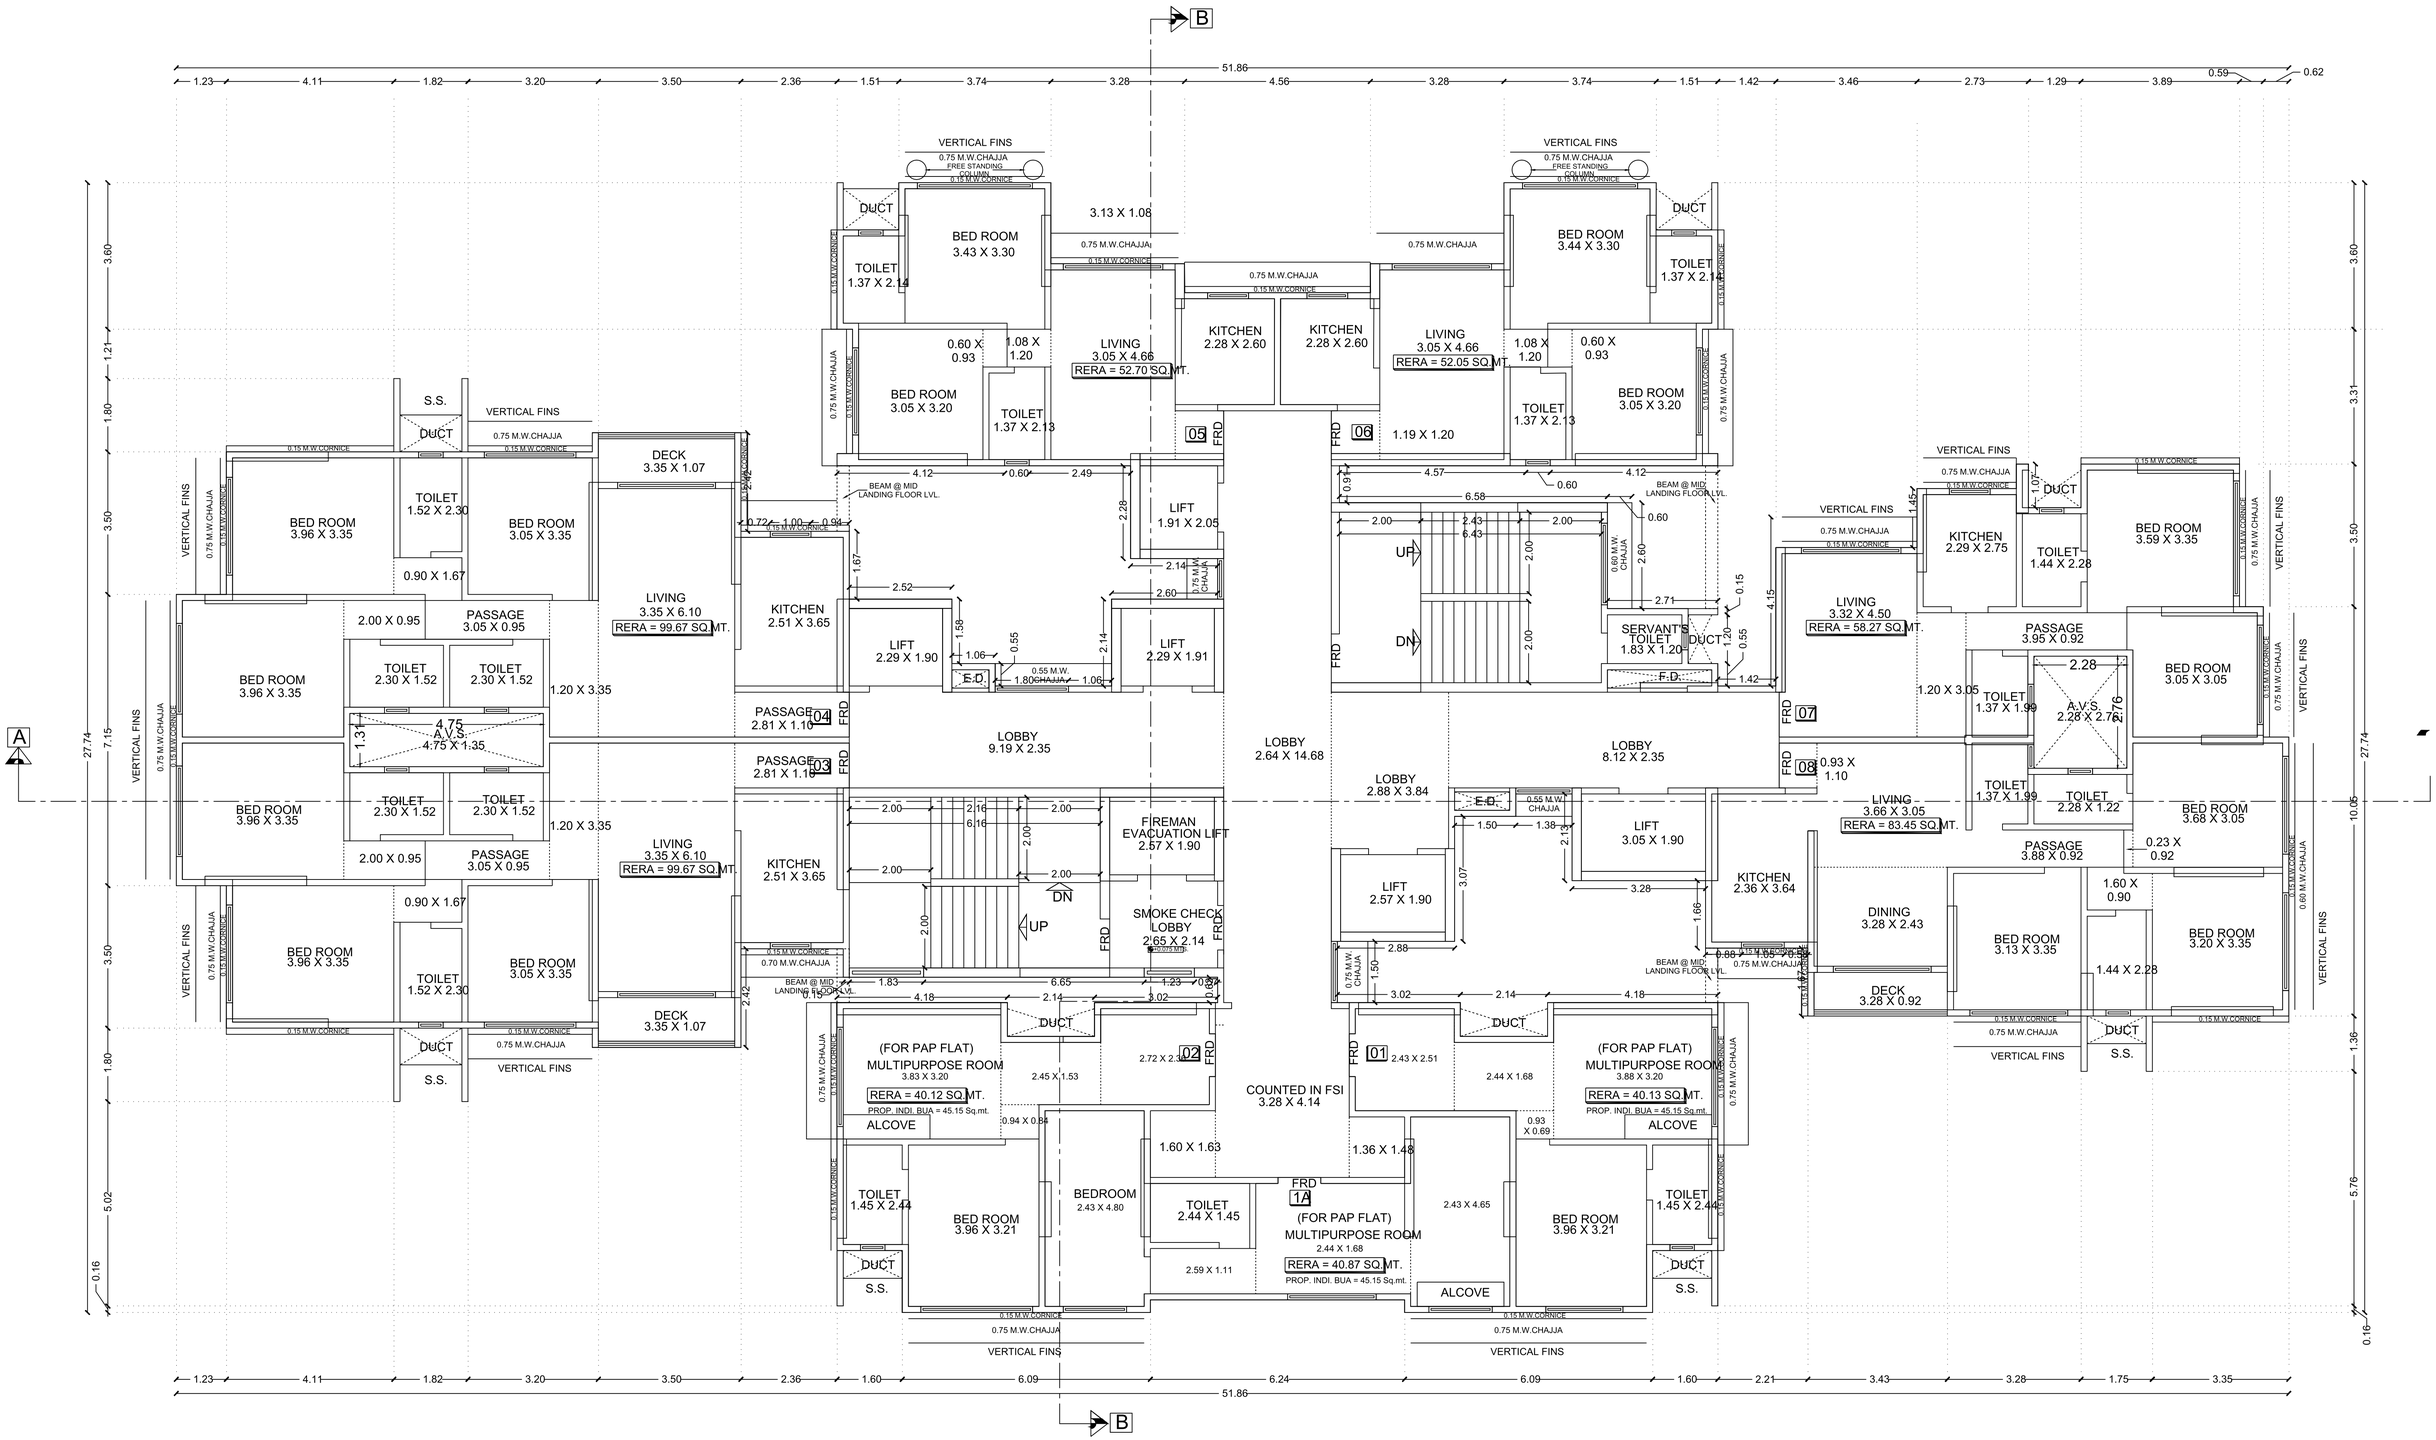


18TH TO 22ND FLOOR PLAN

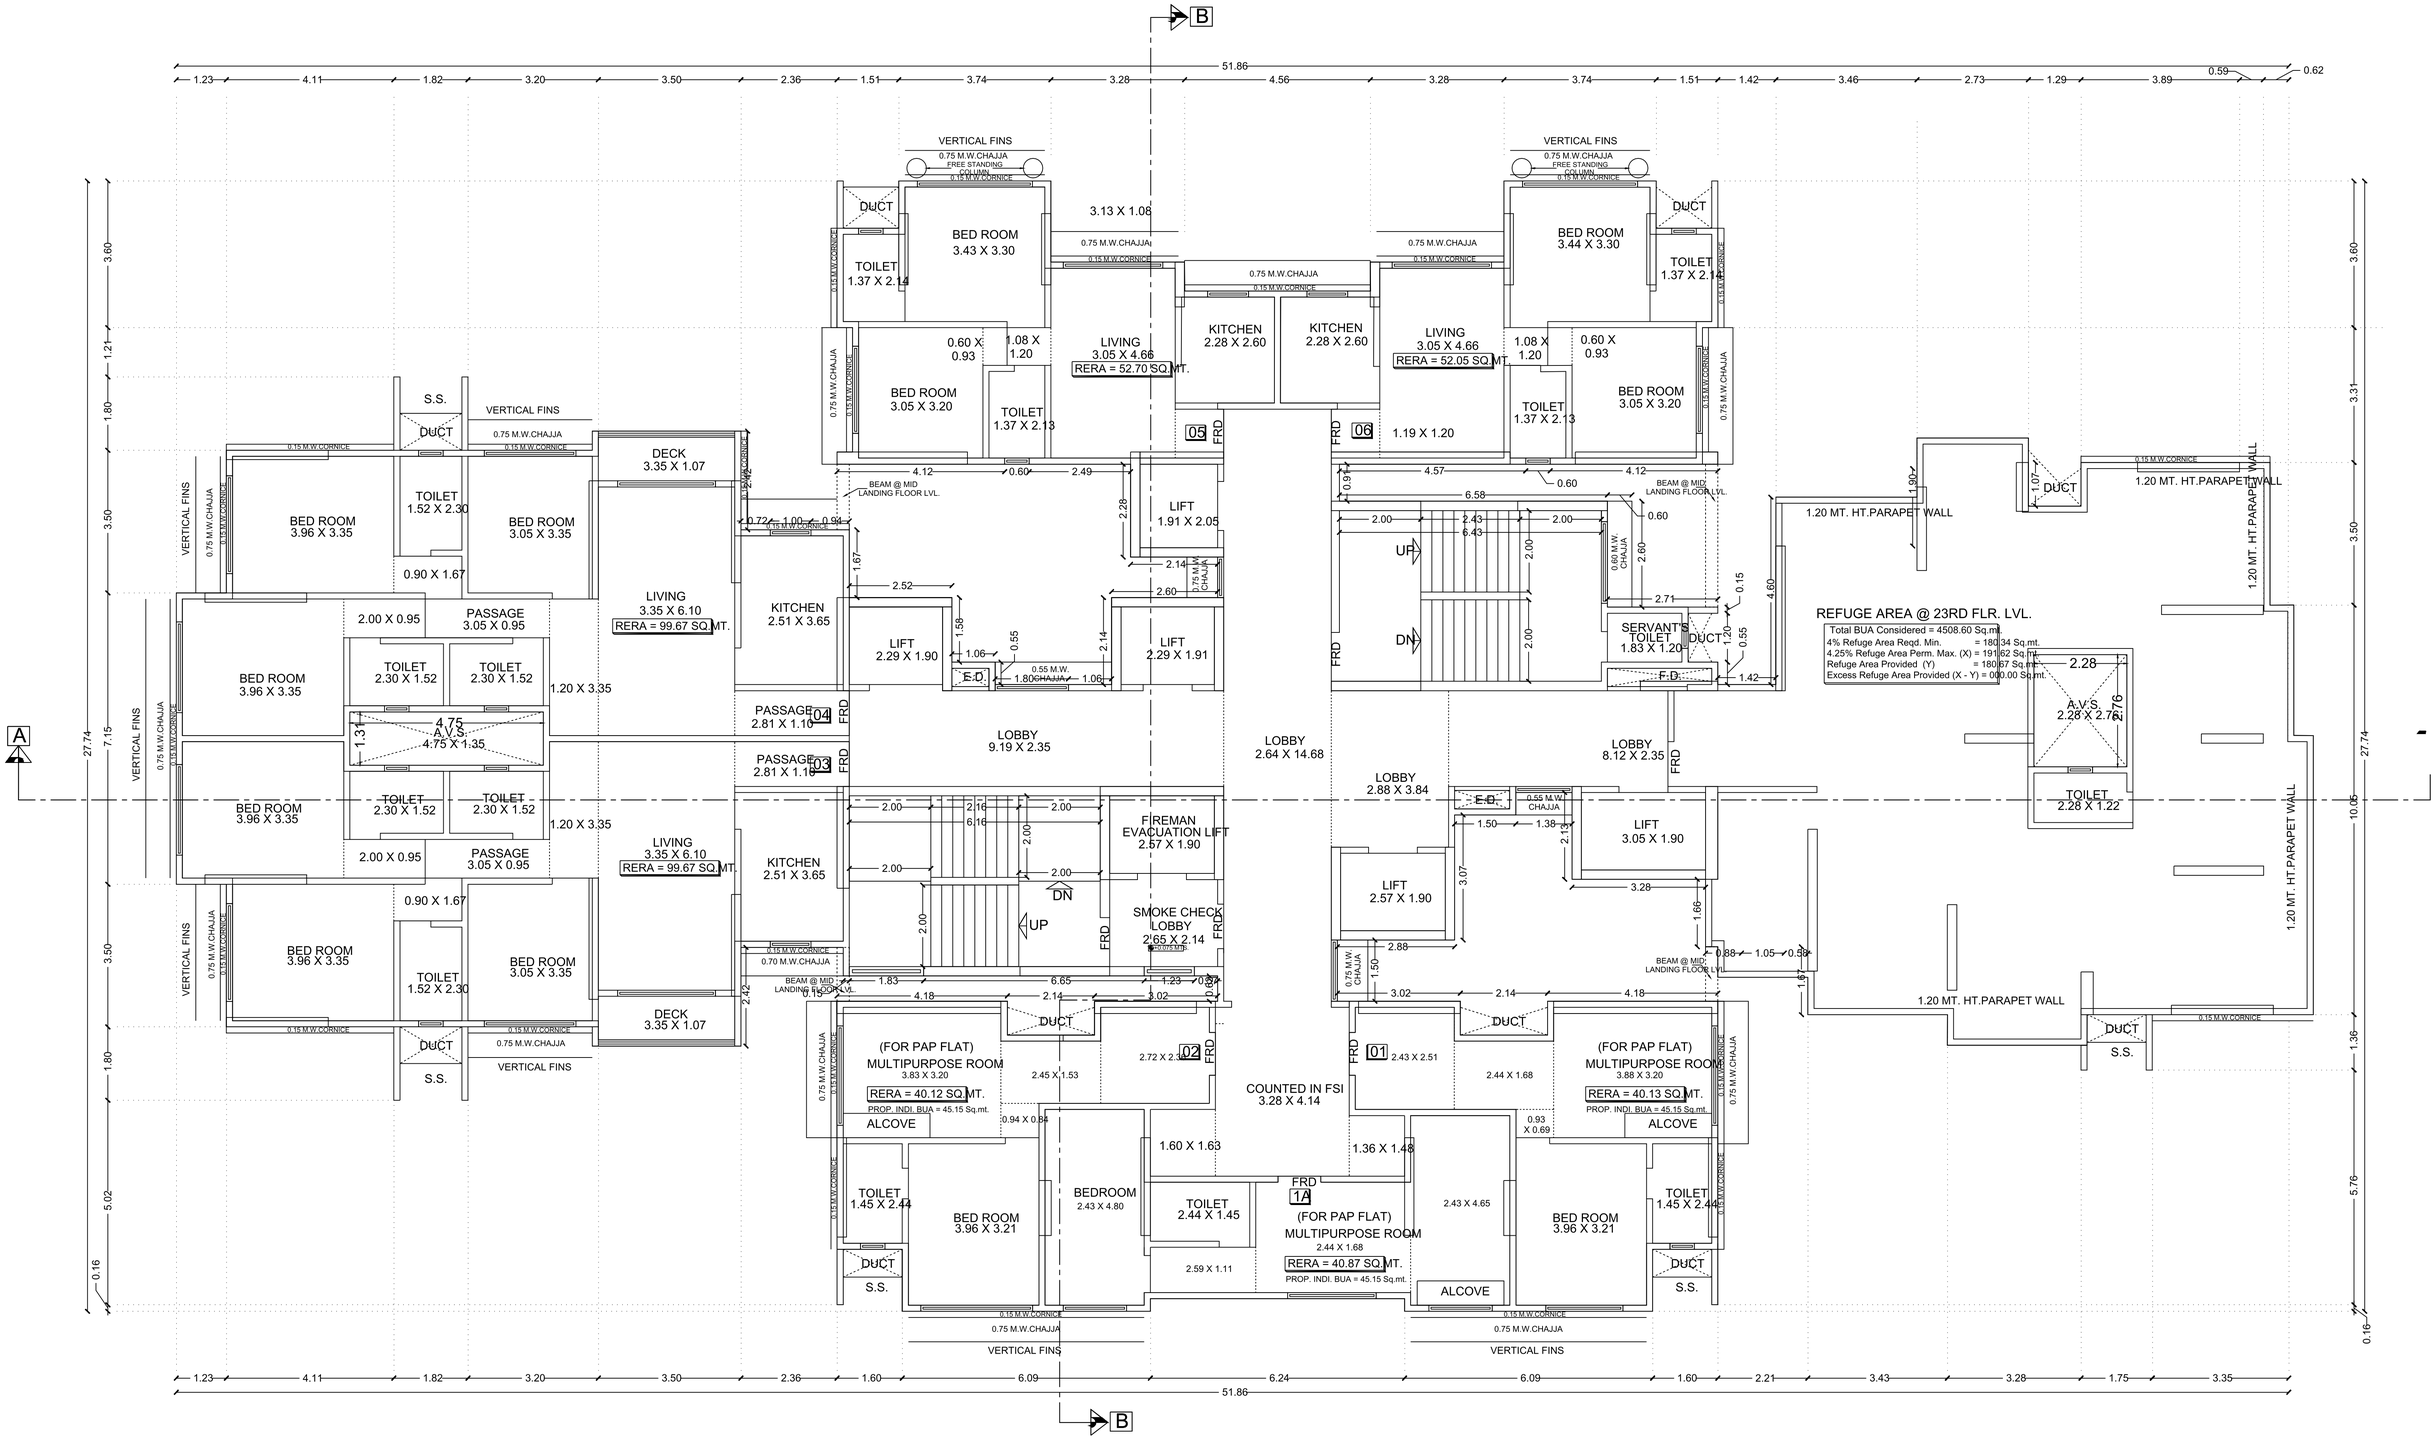

23RD REFUGE FLOOR PLAN

SCALE - 1:100

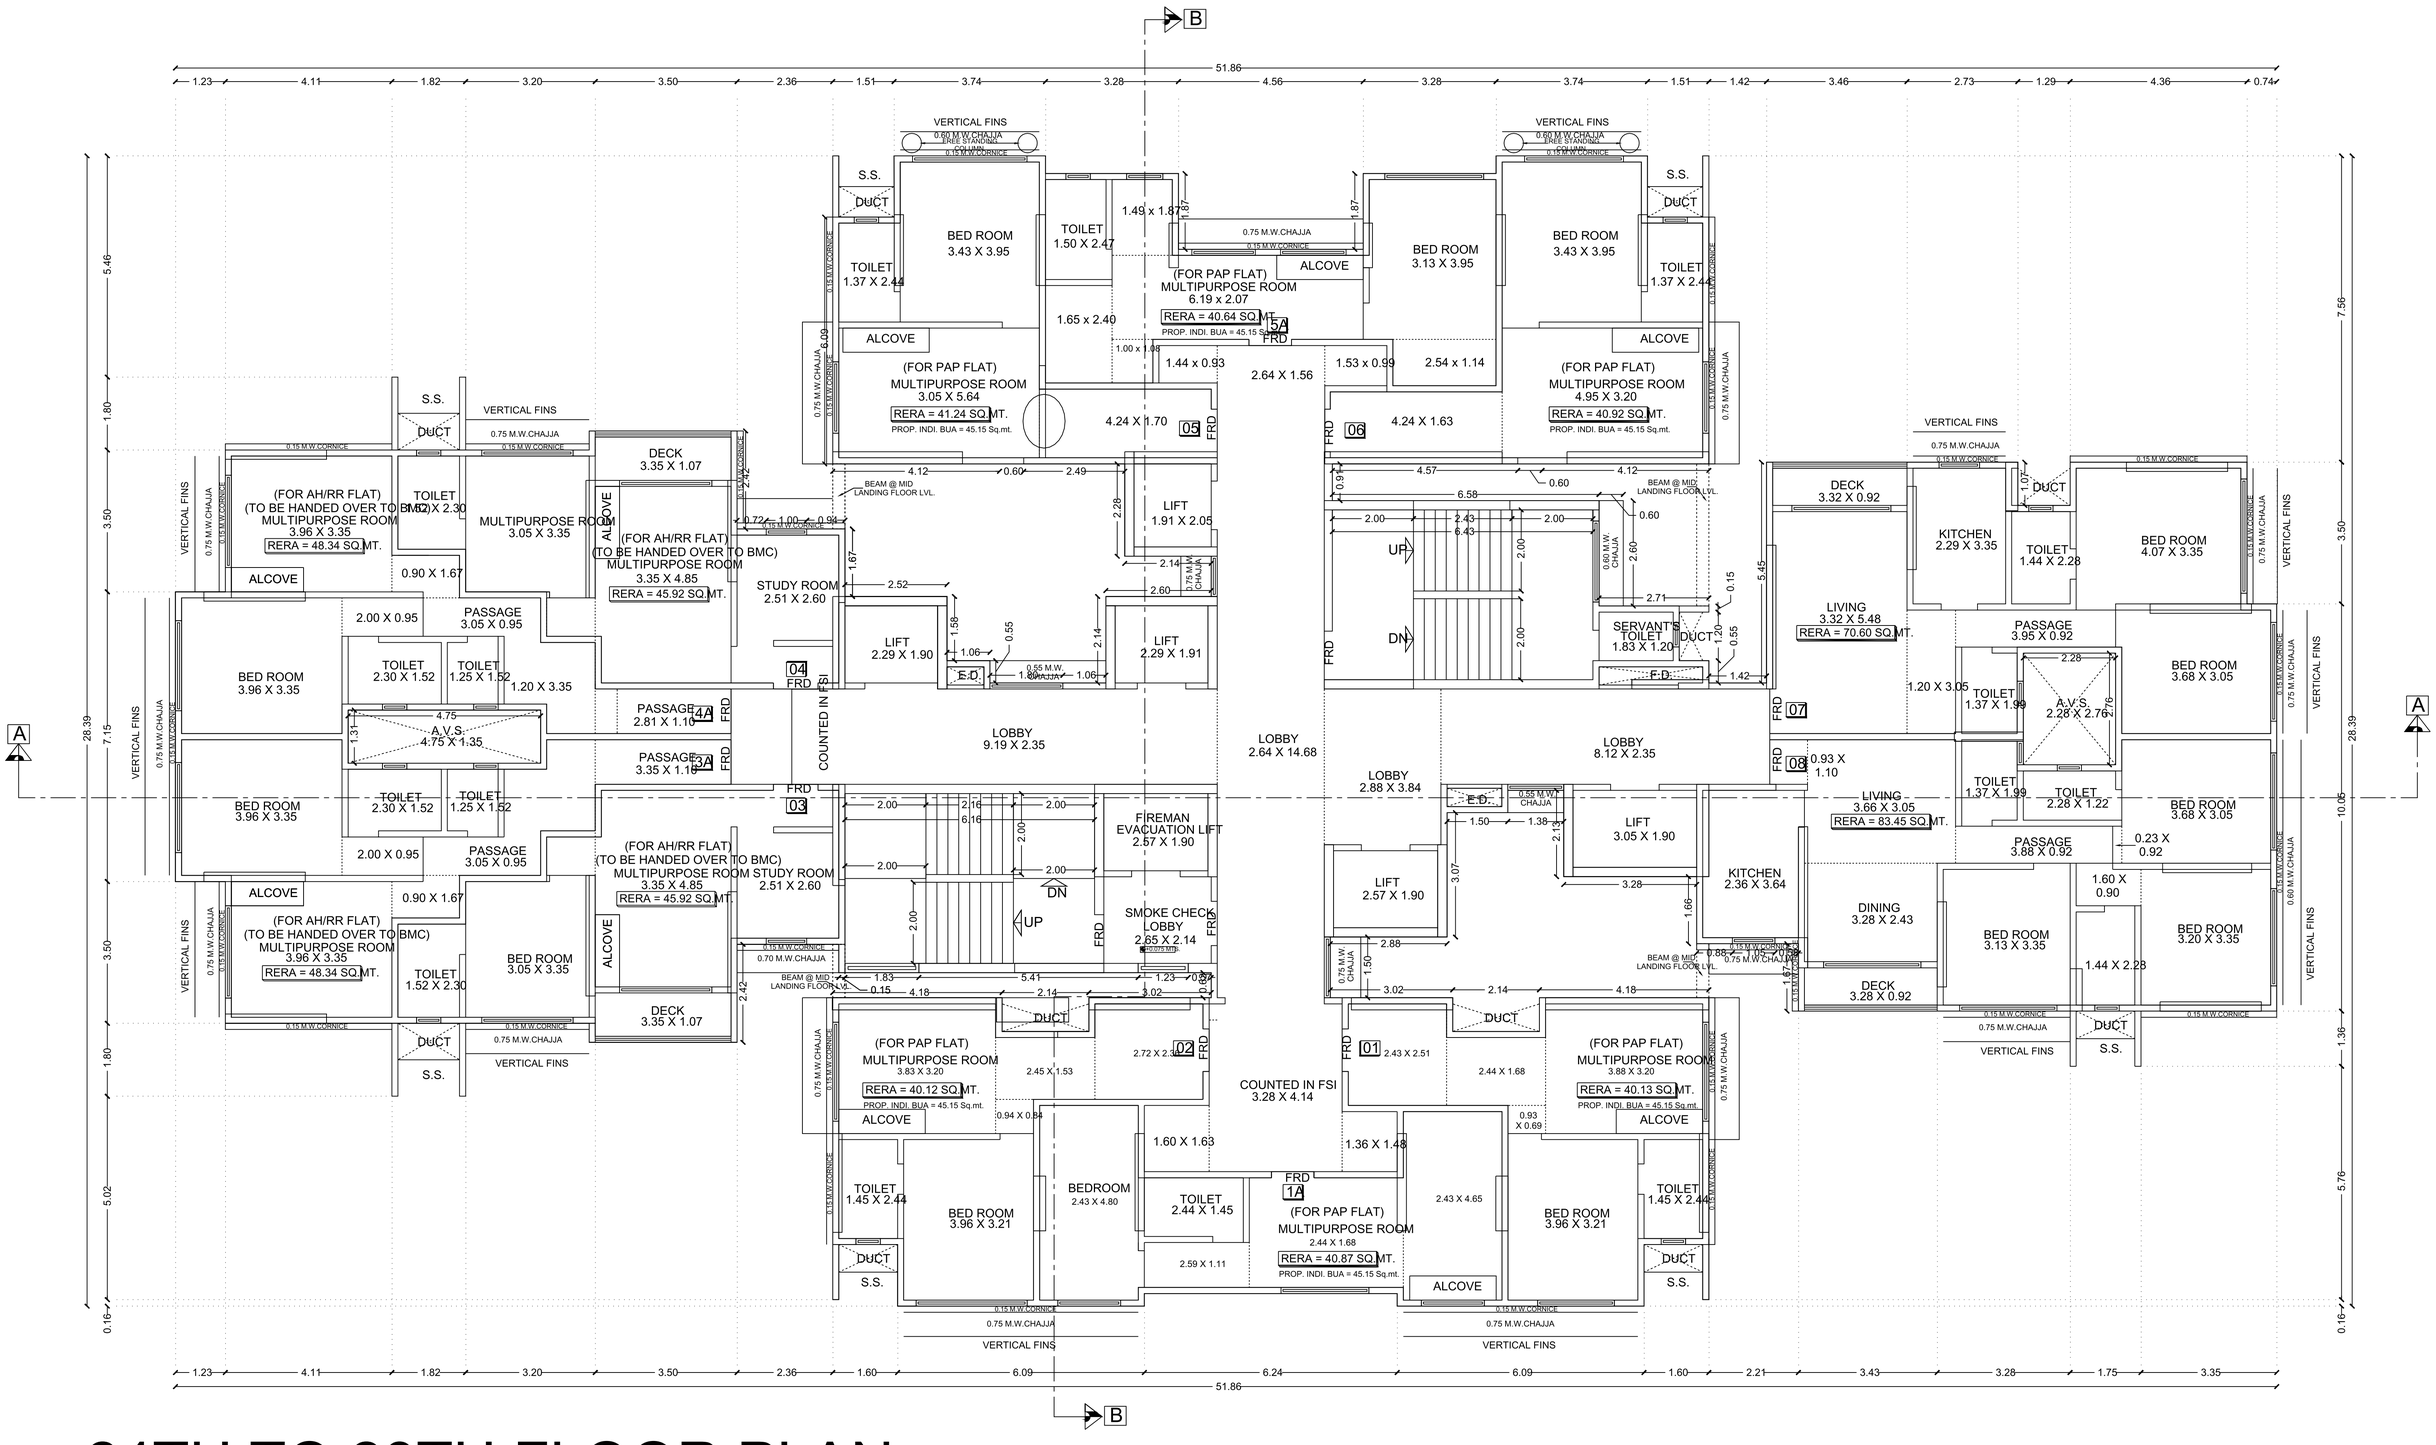


24TH TO 28TH FLOOR PLAN

SCALE - 1:100

29TH, 31ST & 32ND TYPICAL FLOOR PLAN

SCALE - 1:100

SCALE - 1:100

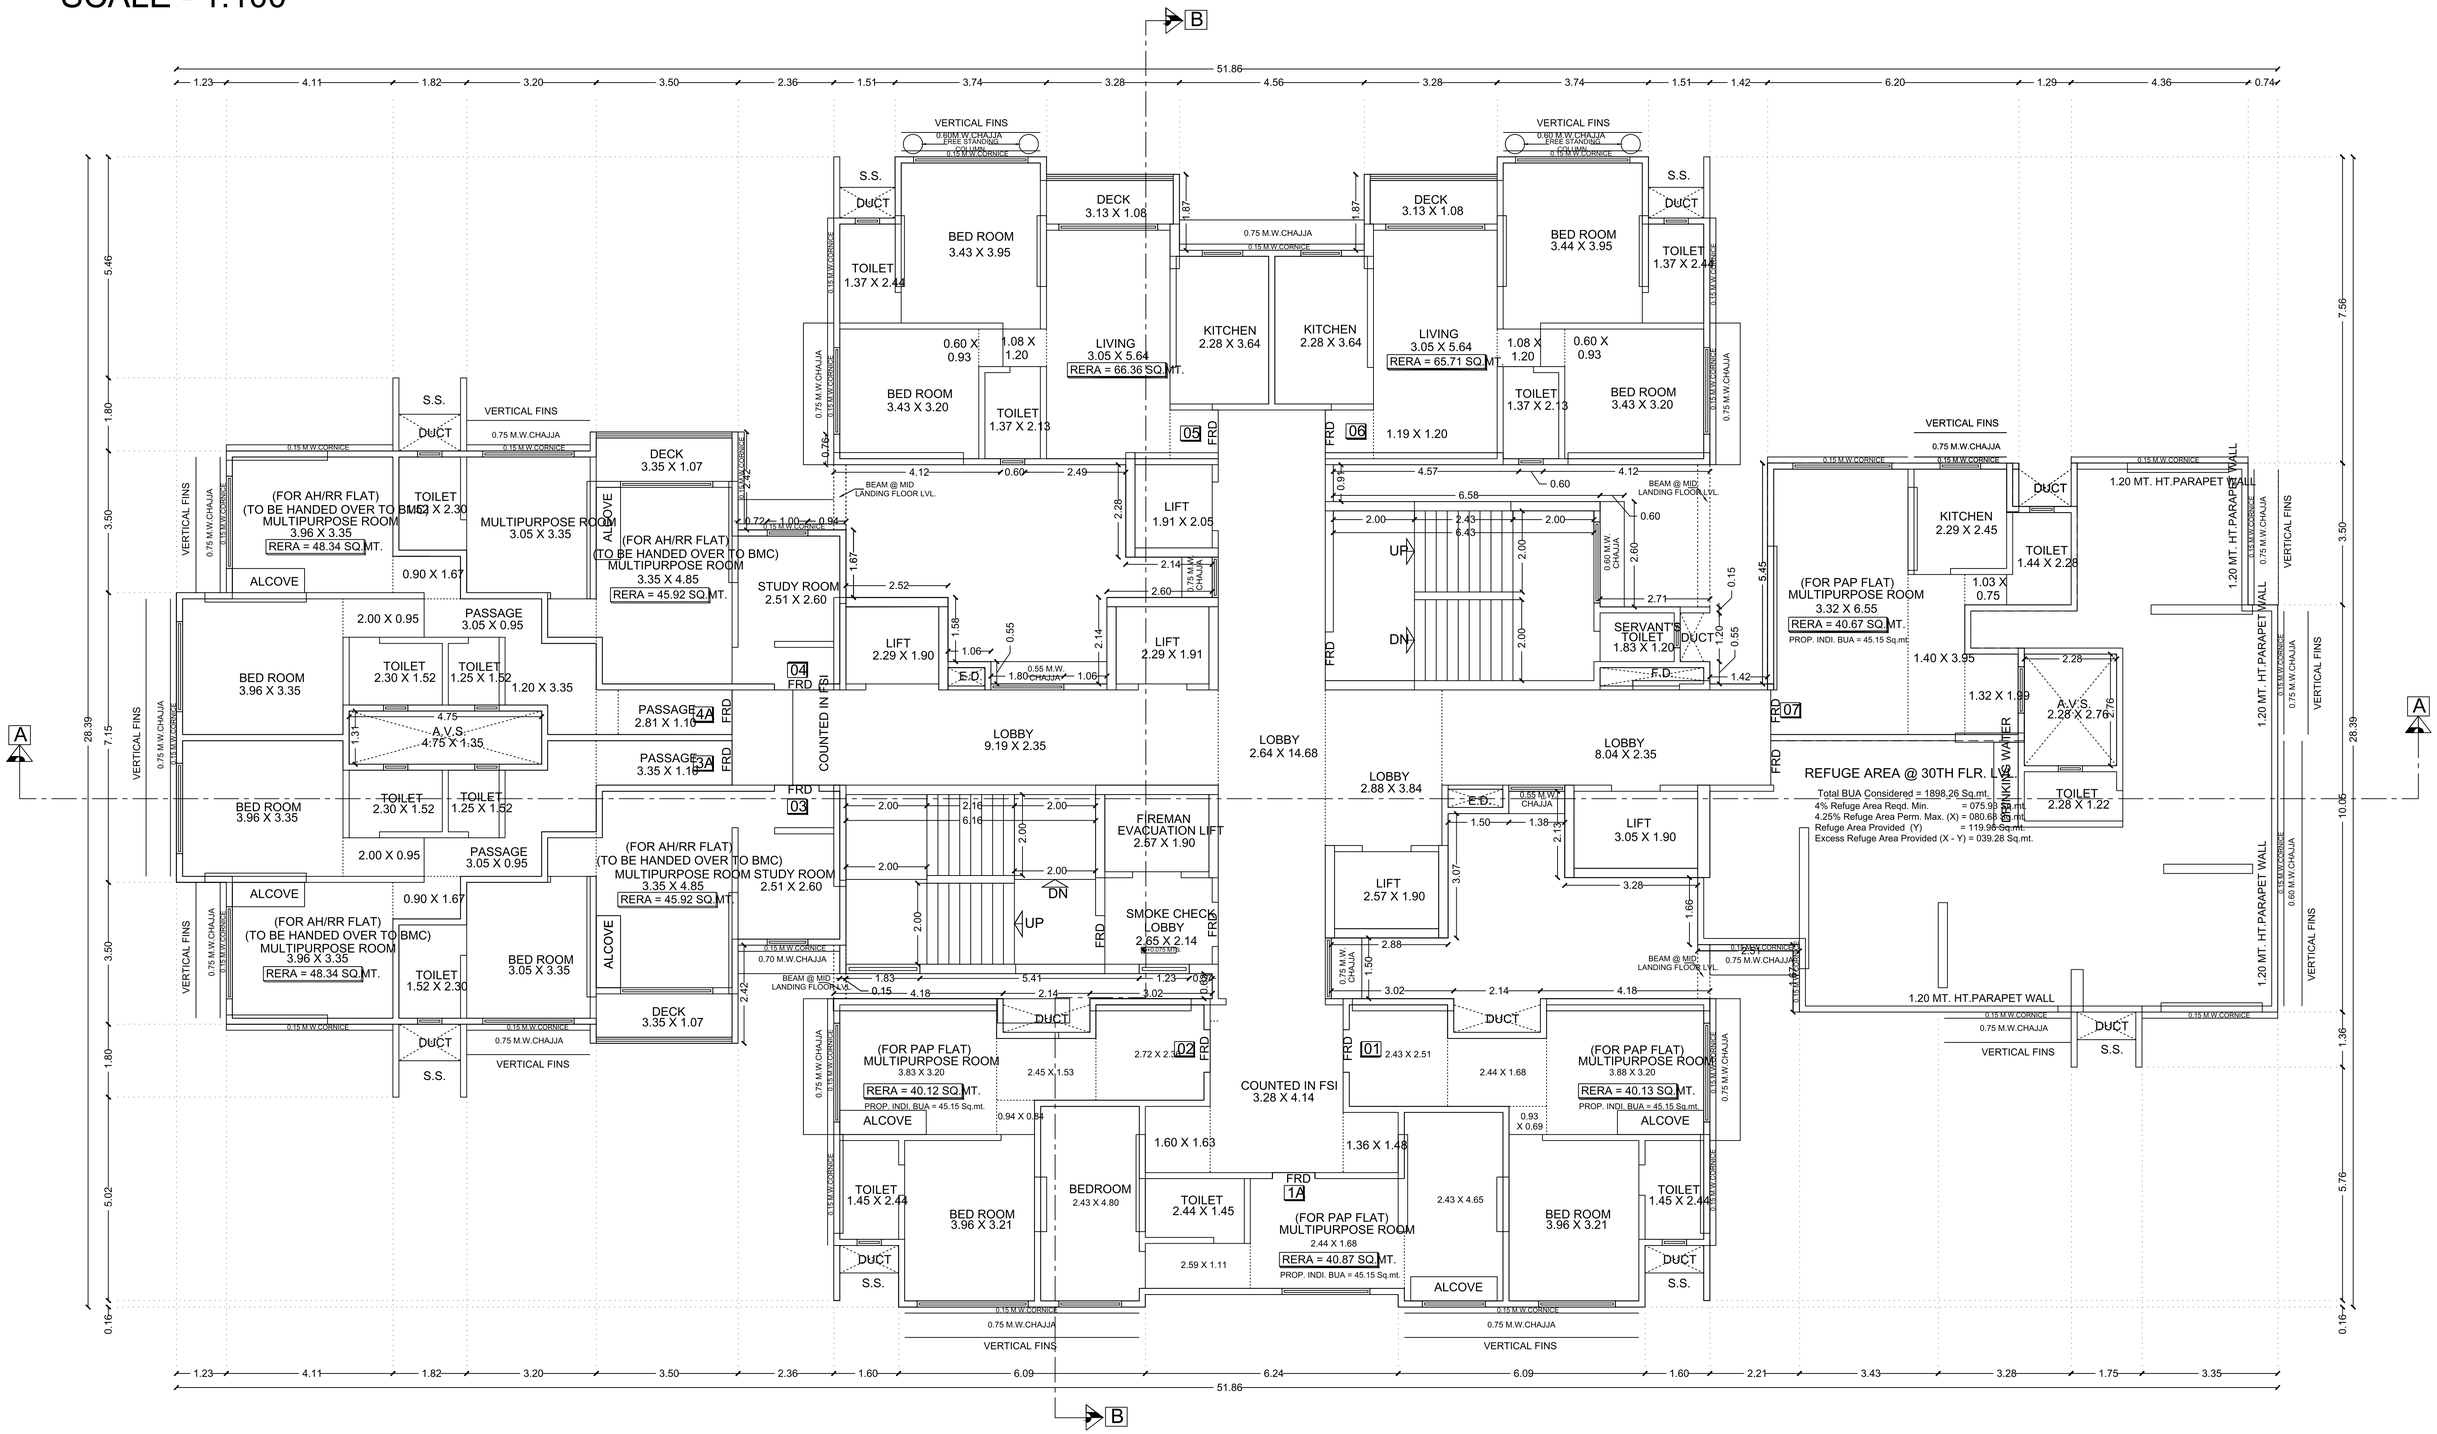

30TH REFUGE FLOOR PLAN

SCALE - 1:100