
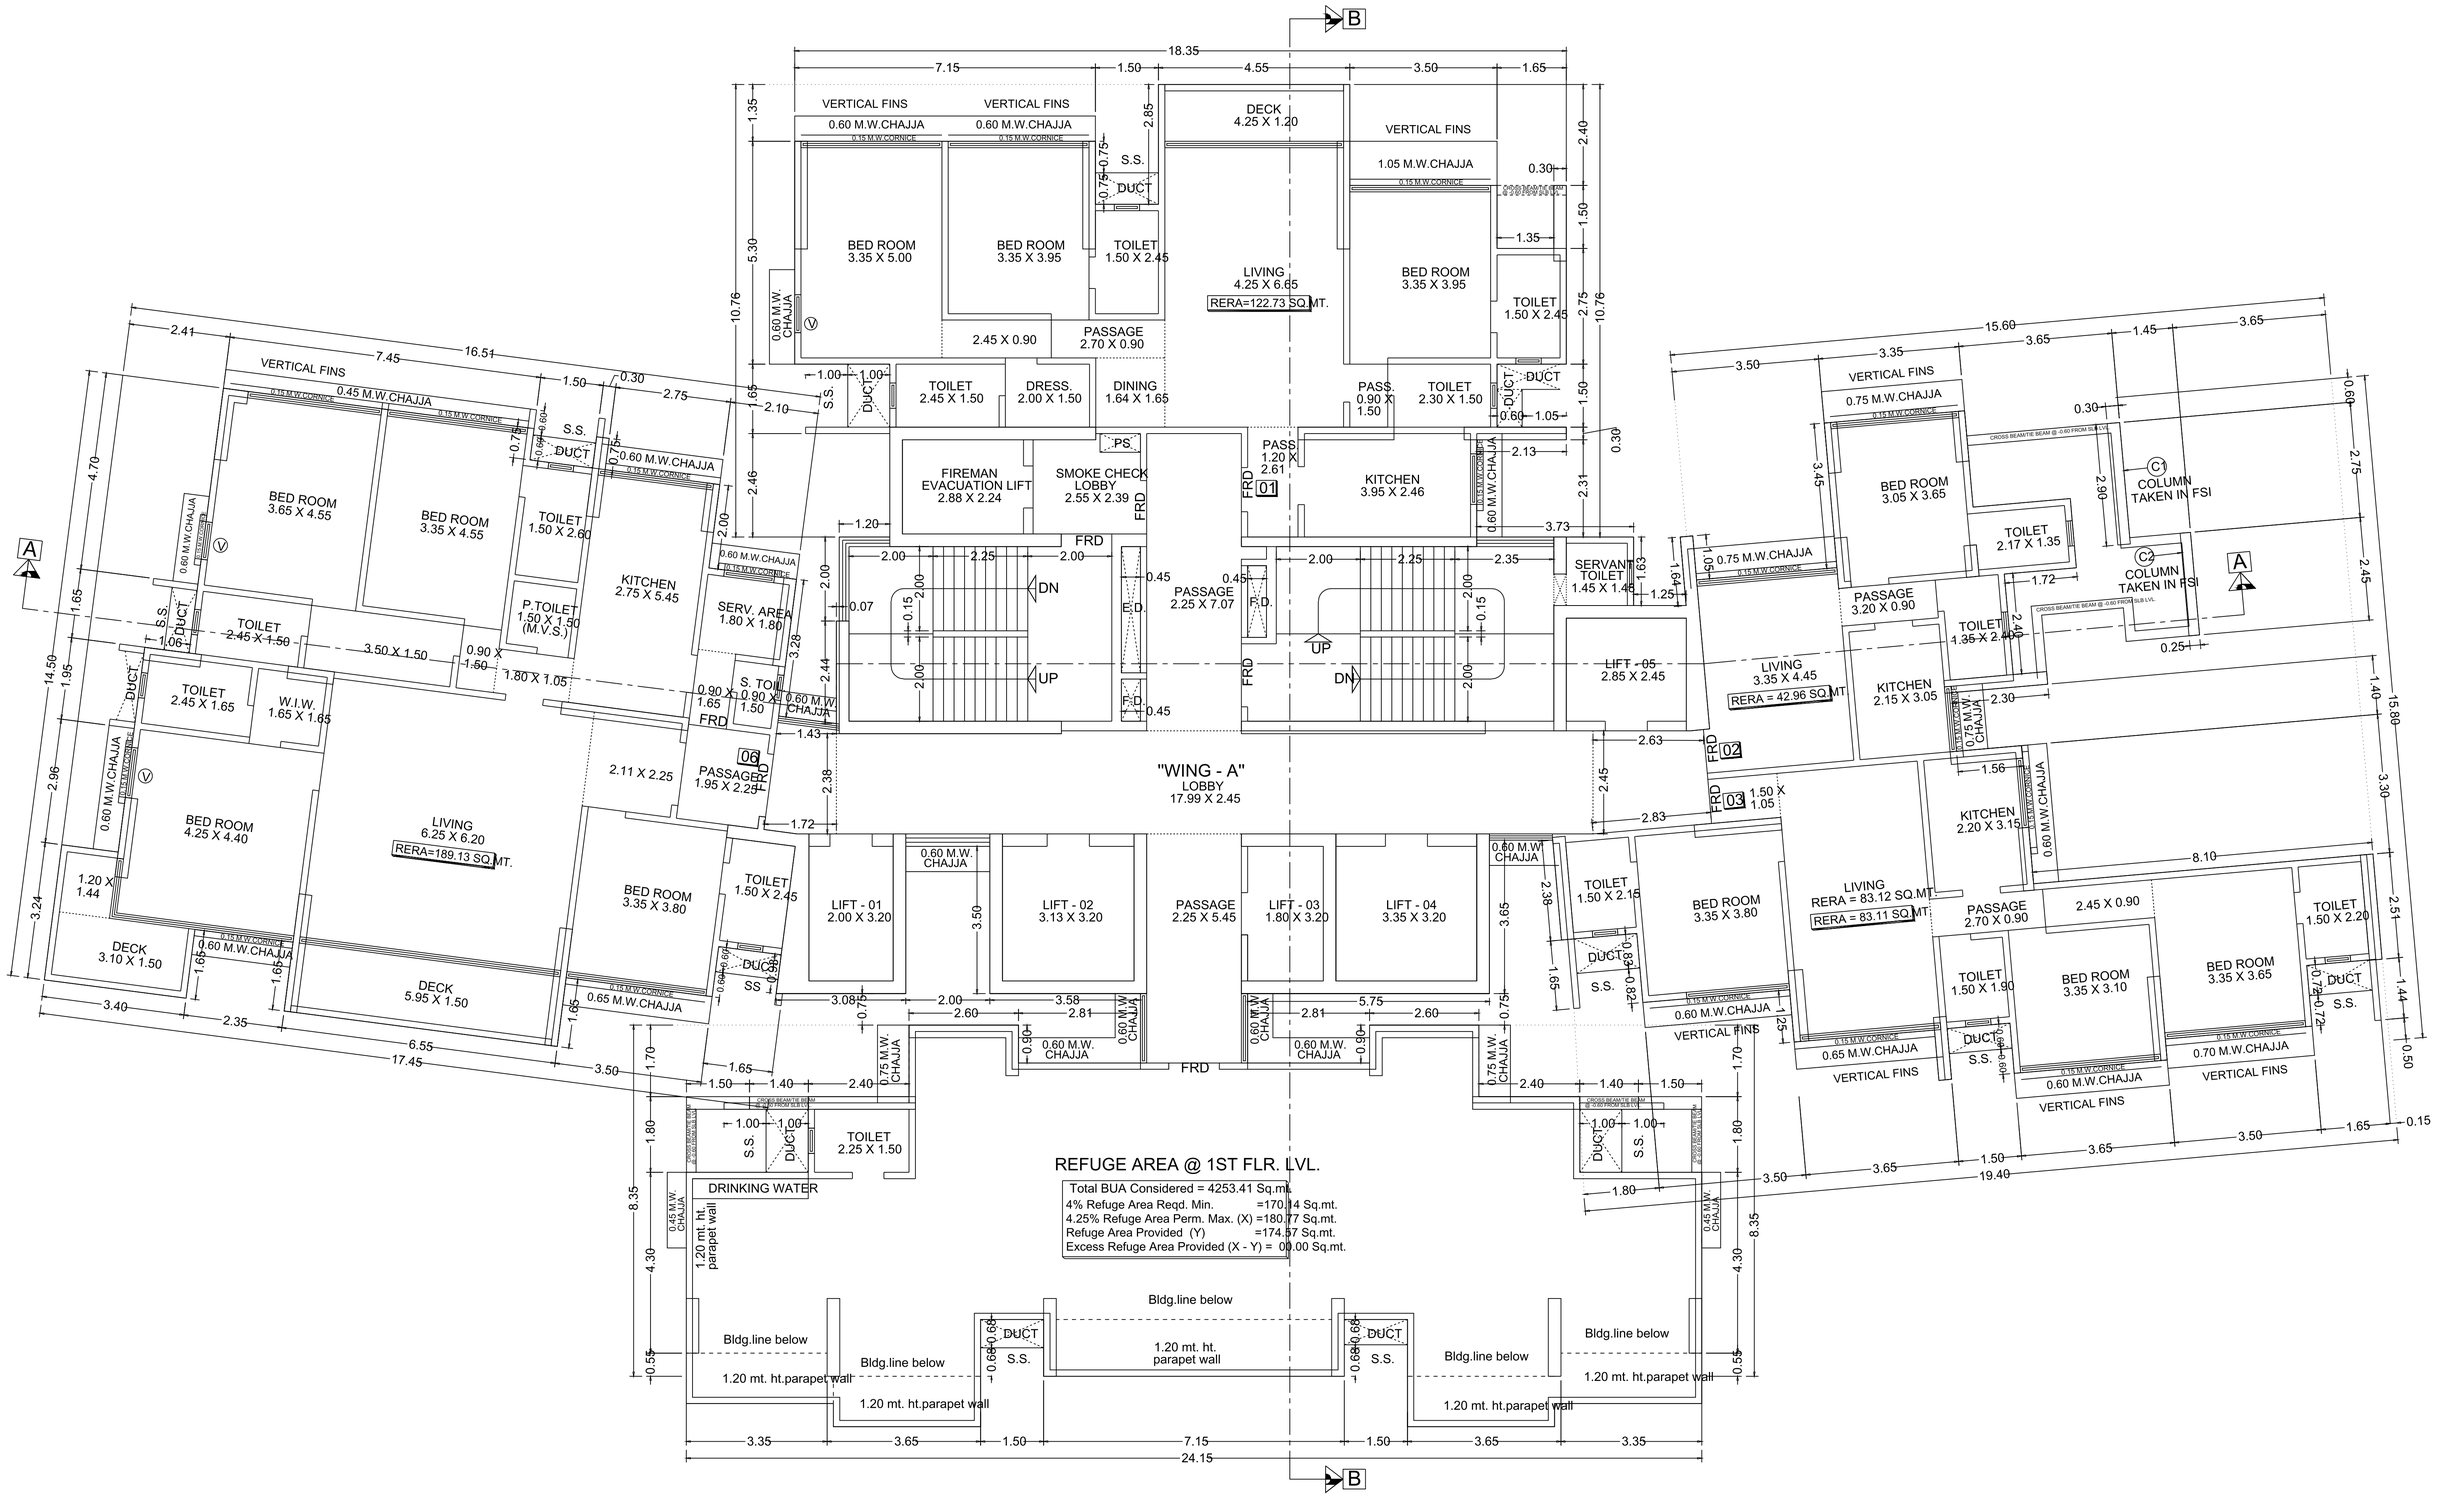



1ST REFUGE FLOOR PLAN (WING - A)

SCALE - 1:100

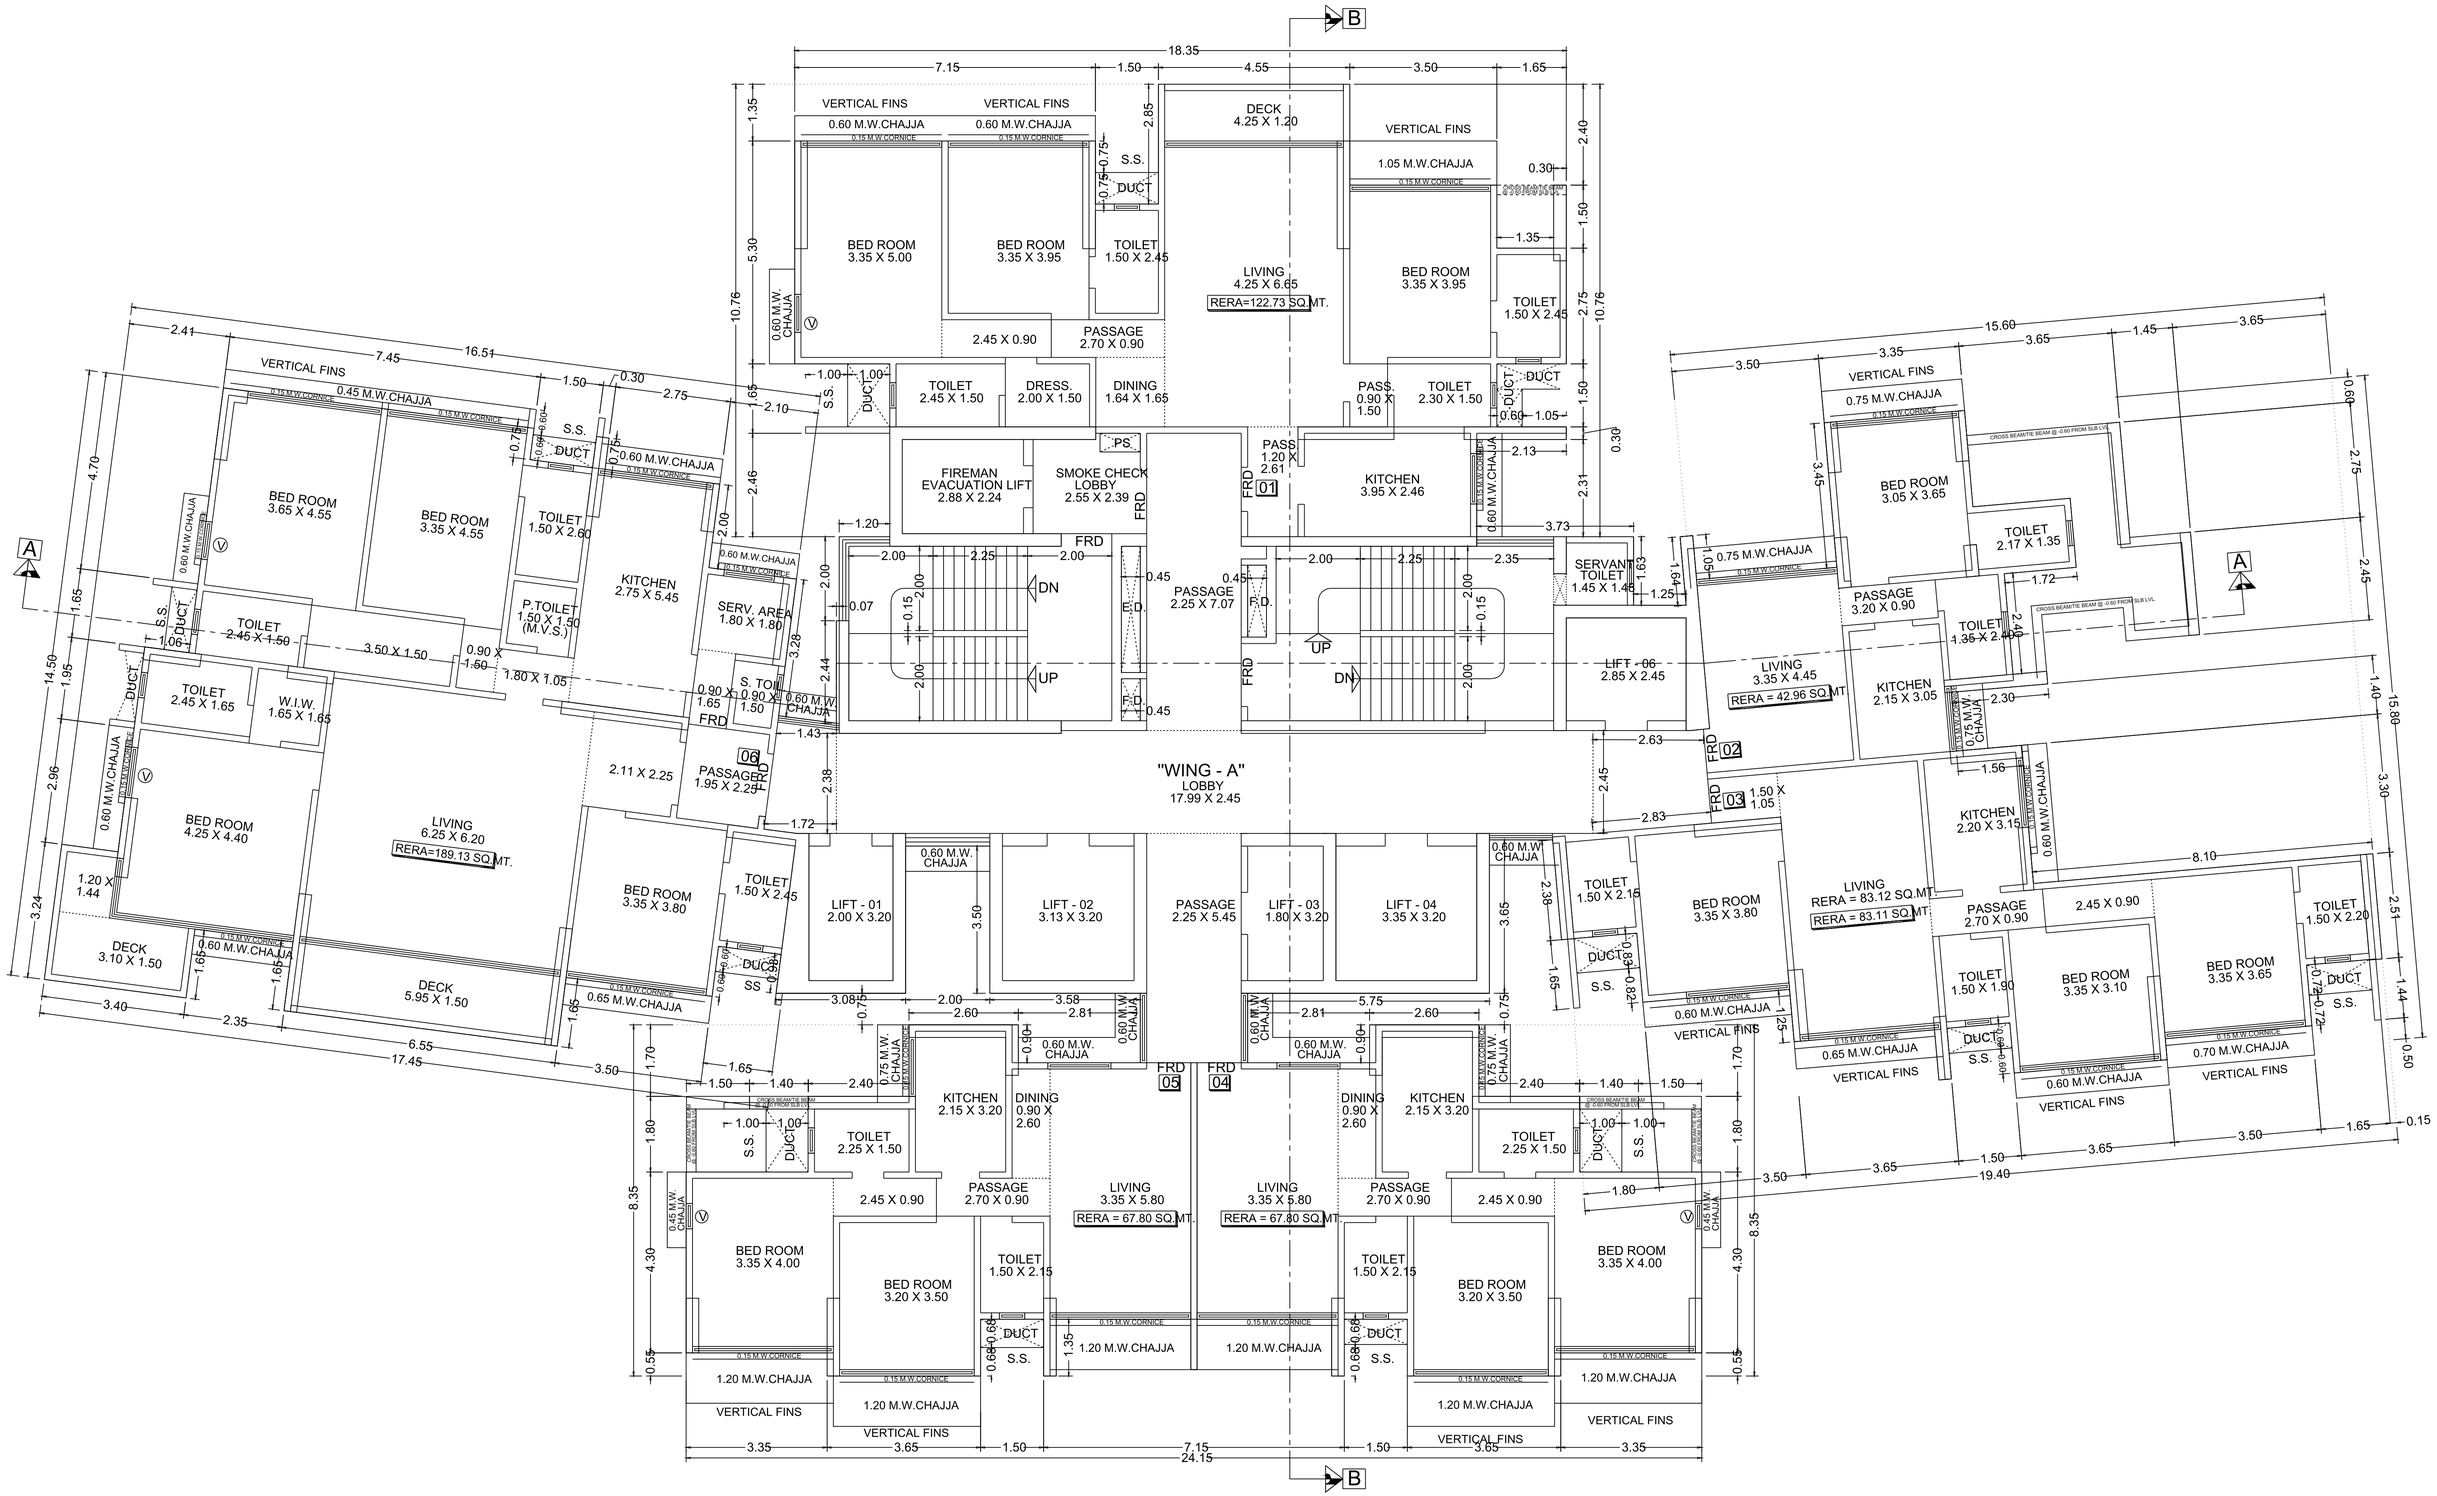

2ND FLOOR PLAN (WING - A)


SCALE - 1:100

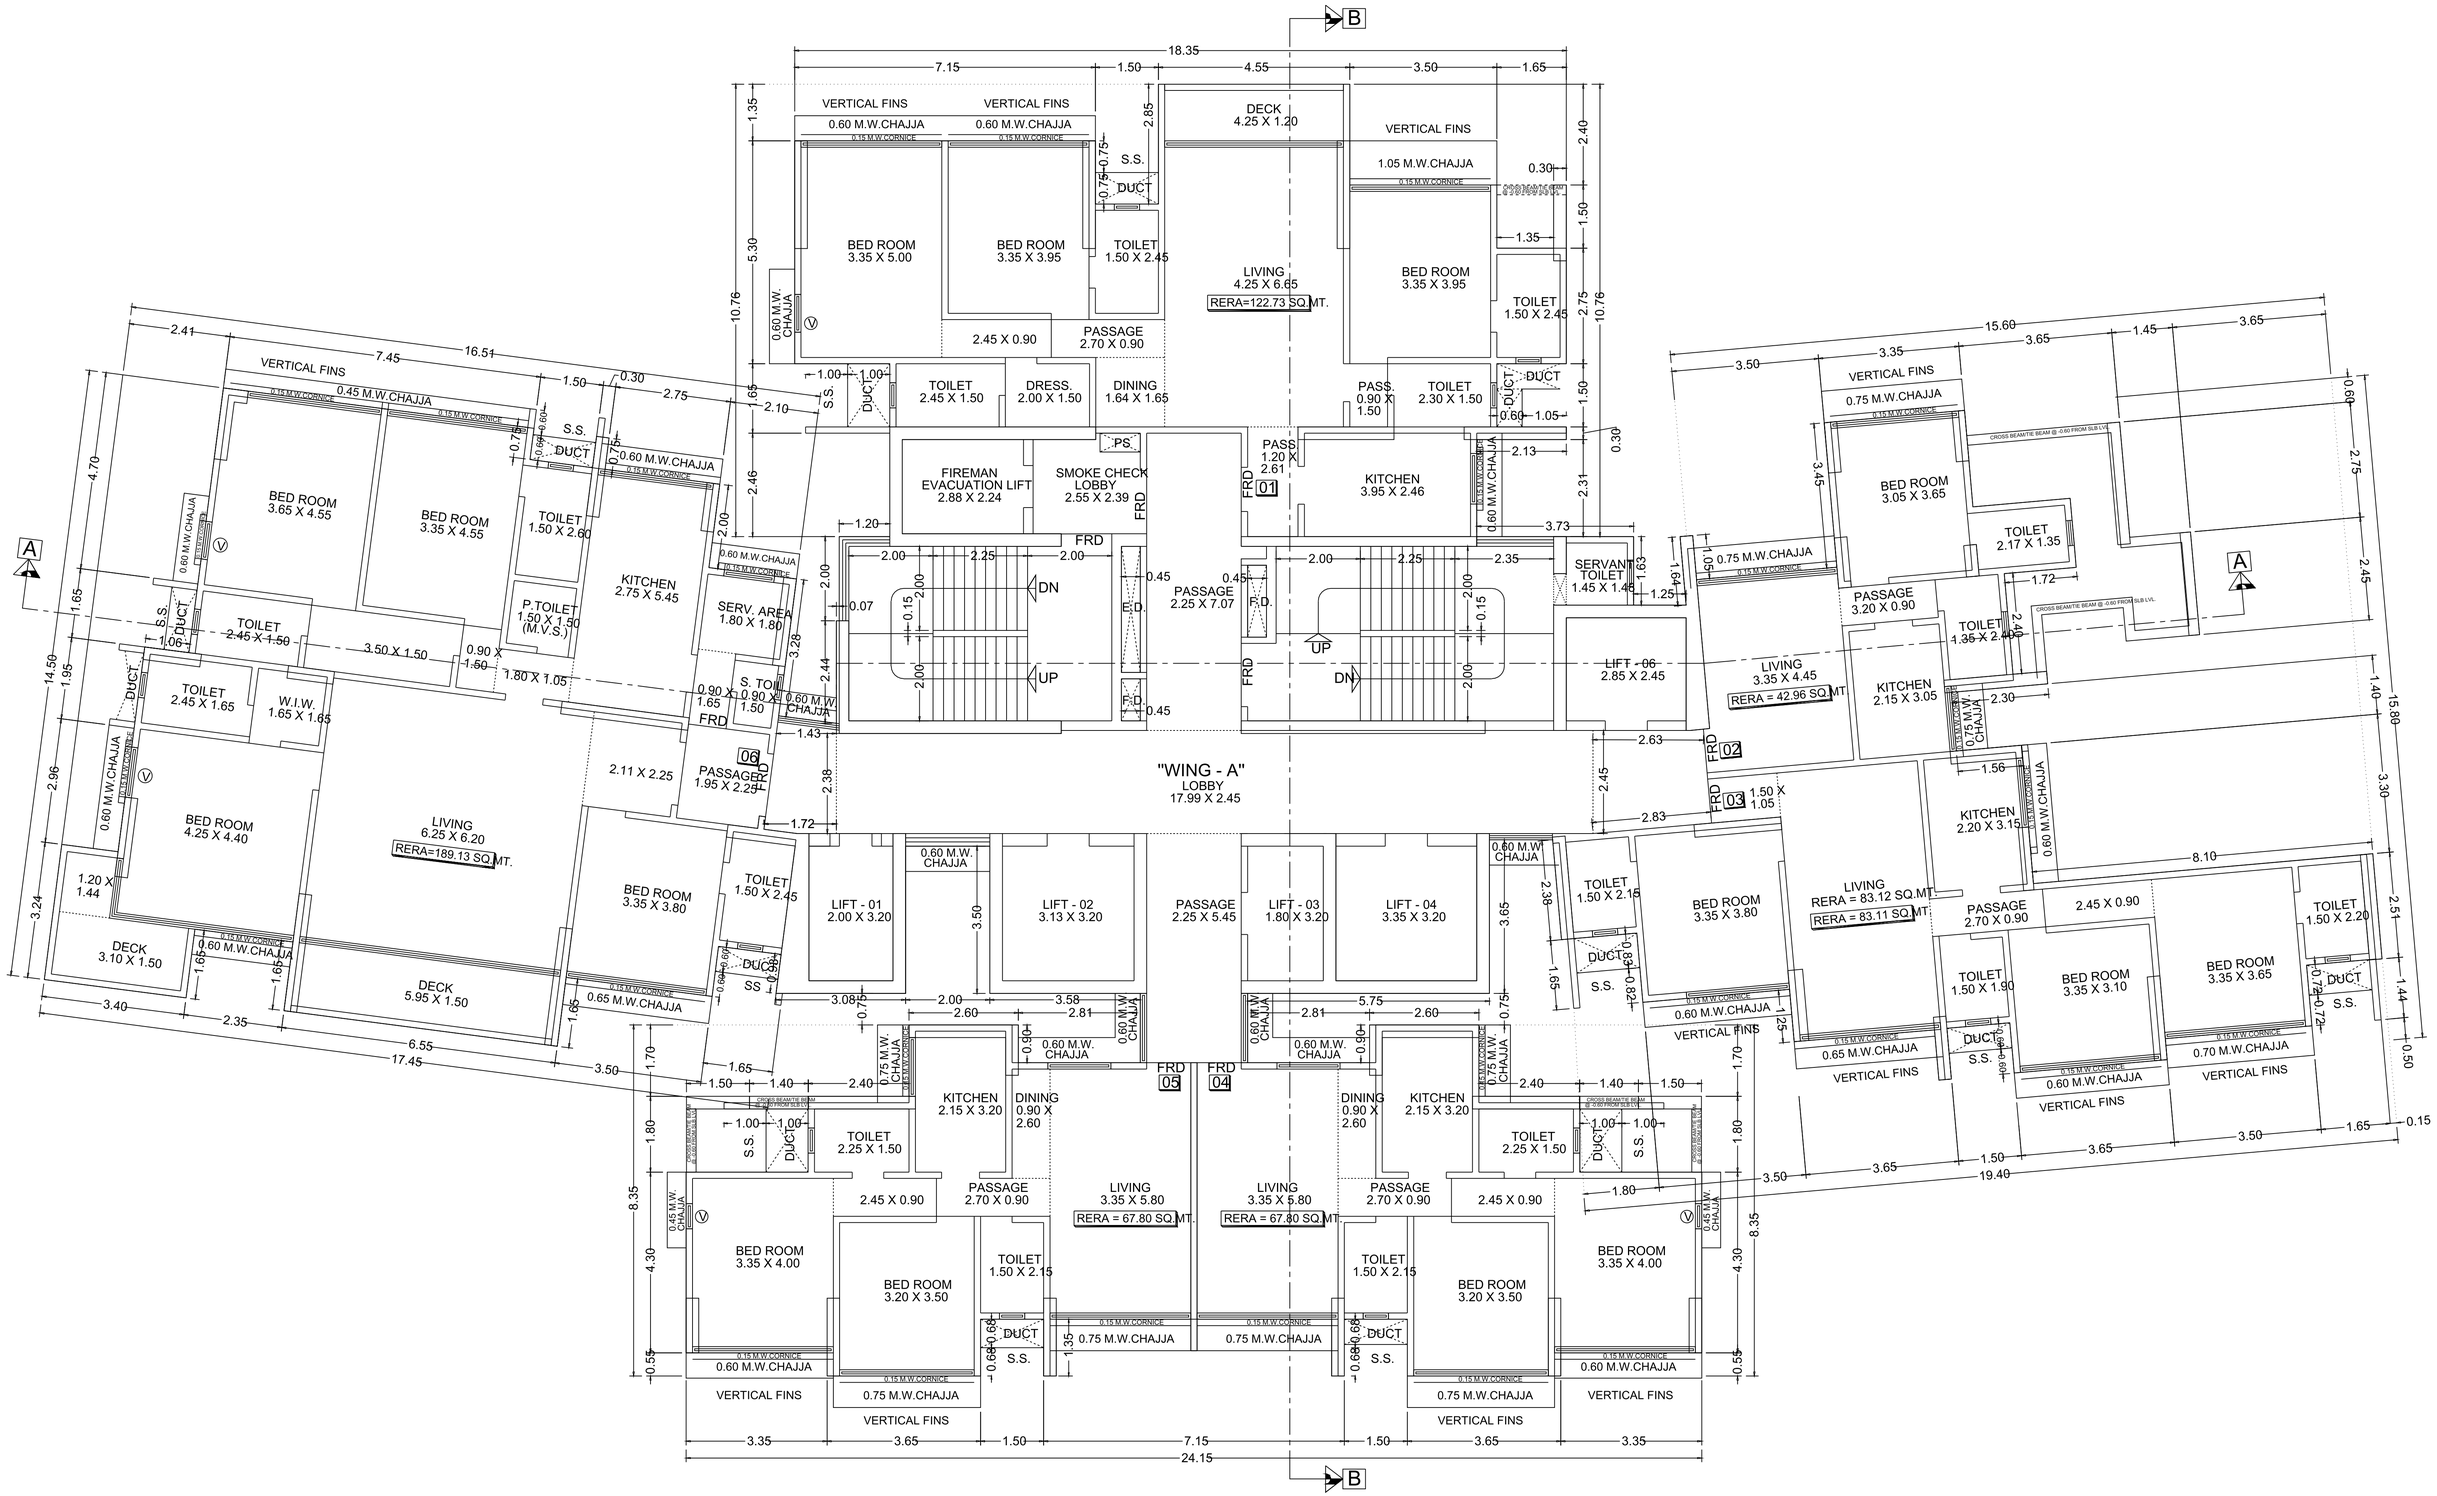

3RD & 4TH FLOOR PLAN (WING - A)


SCALE - 1:100

SCALE - 1:100

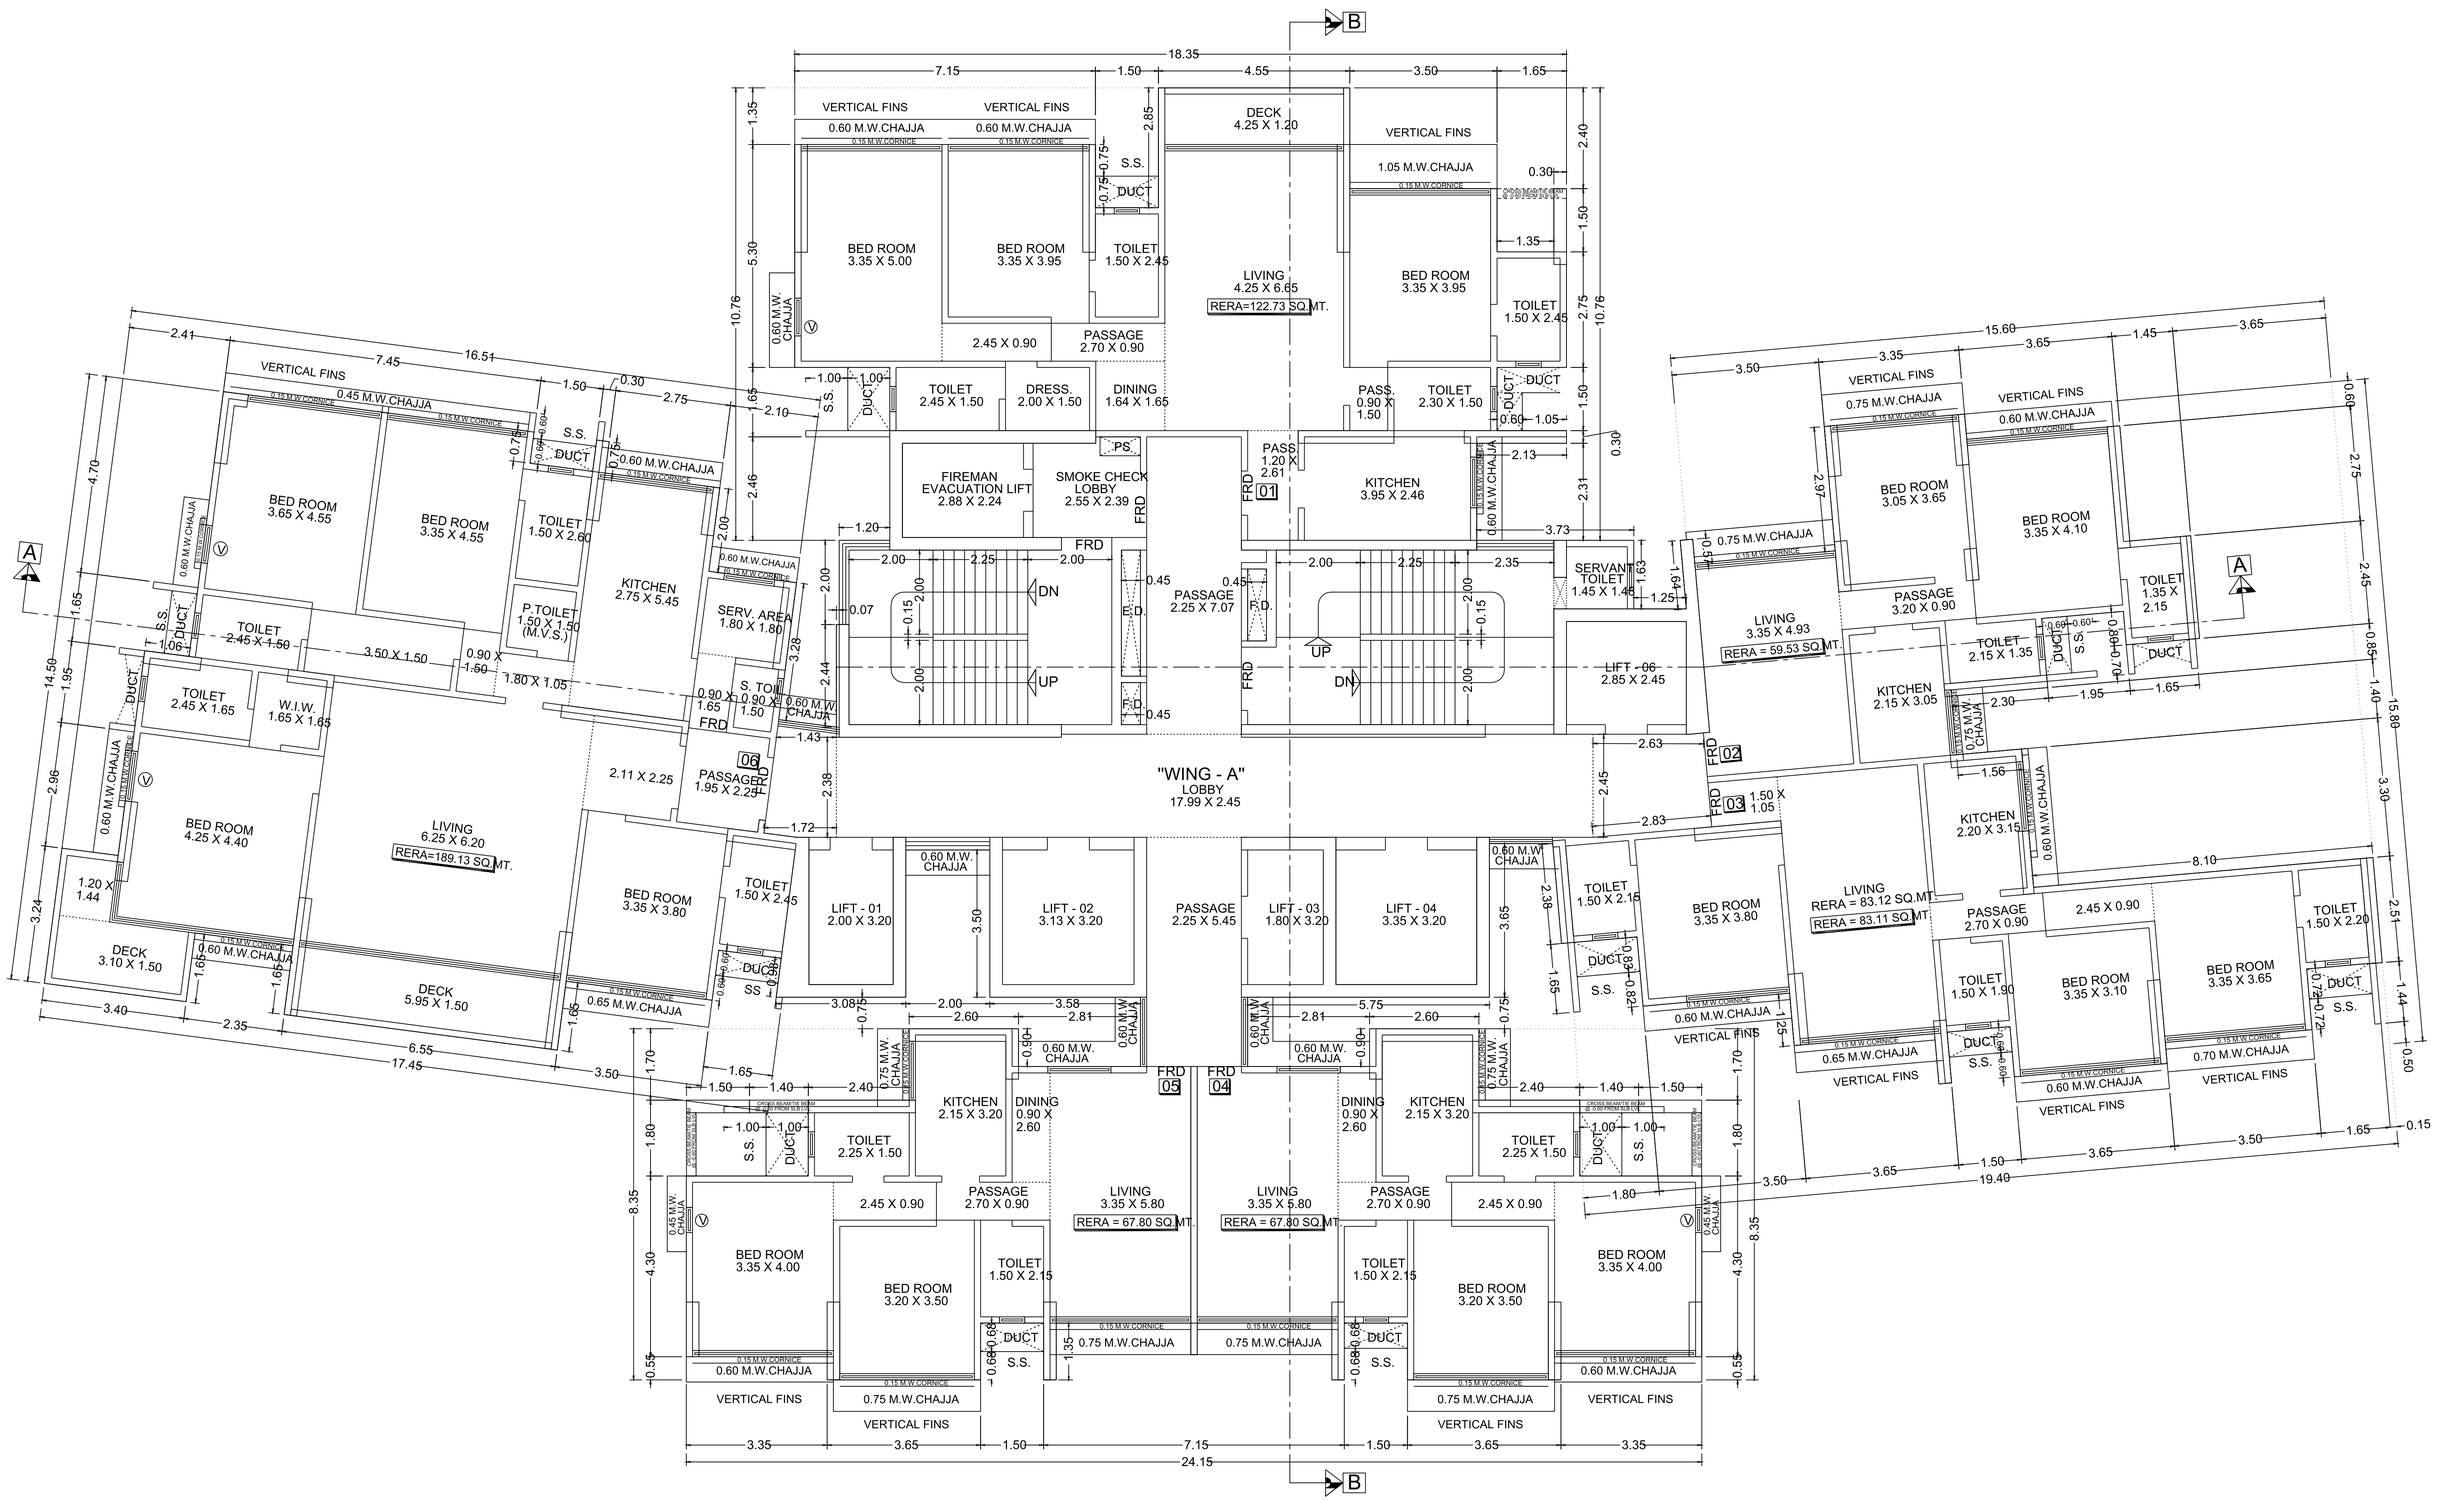

5TH & 6TH FLOOR PLAN (WING - A)


SCALE - 1:100

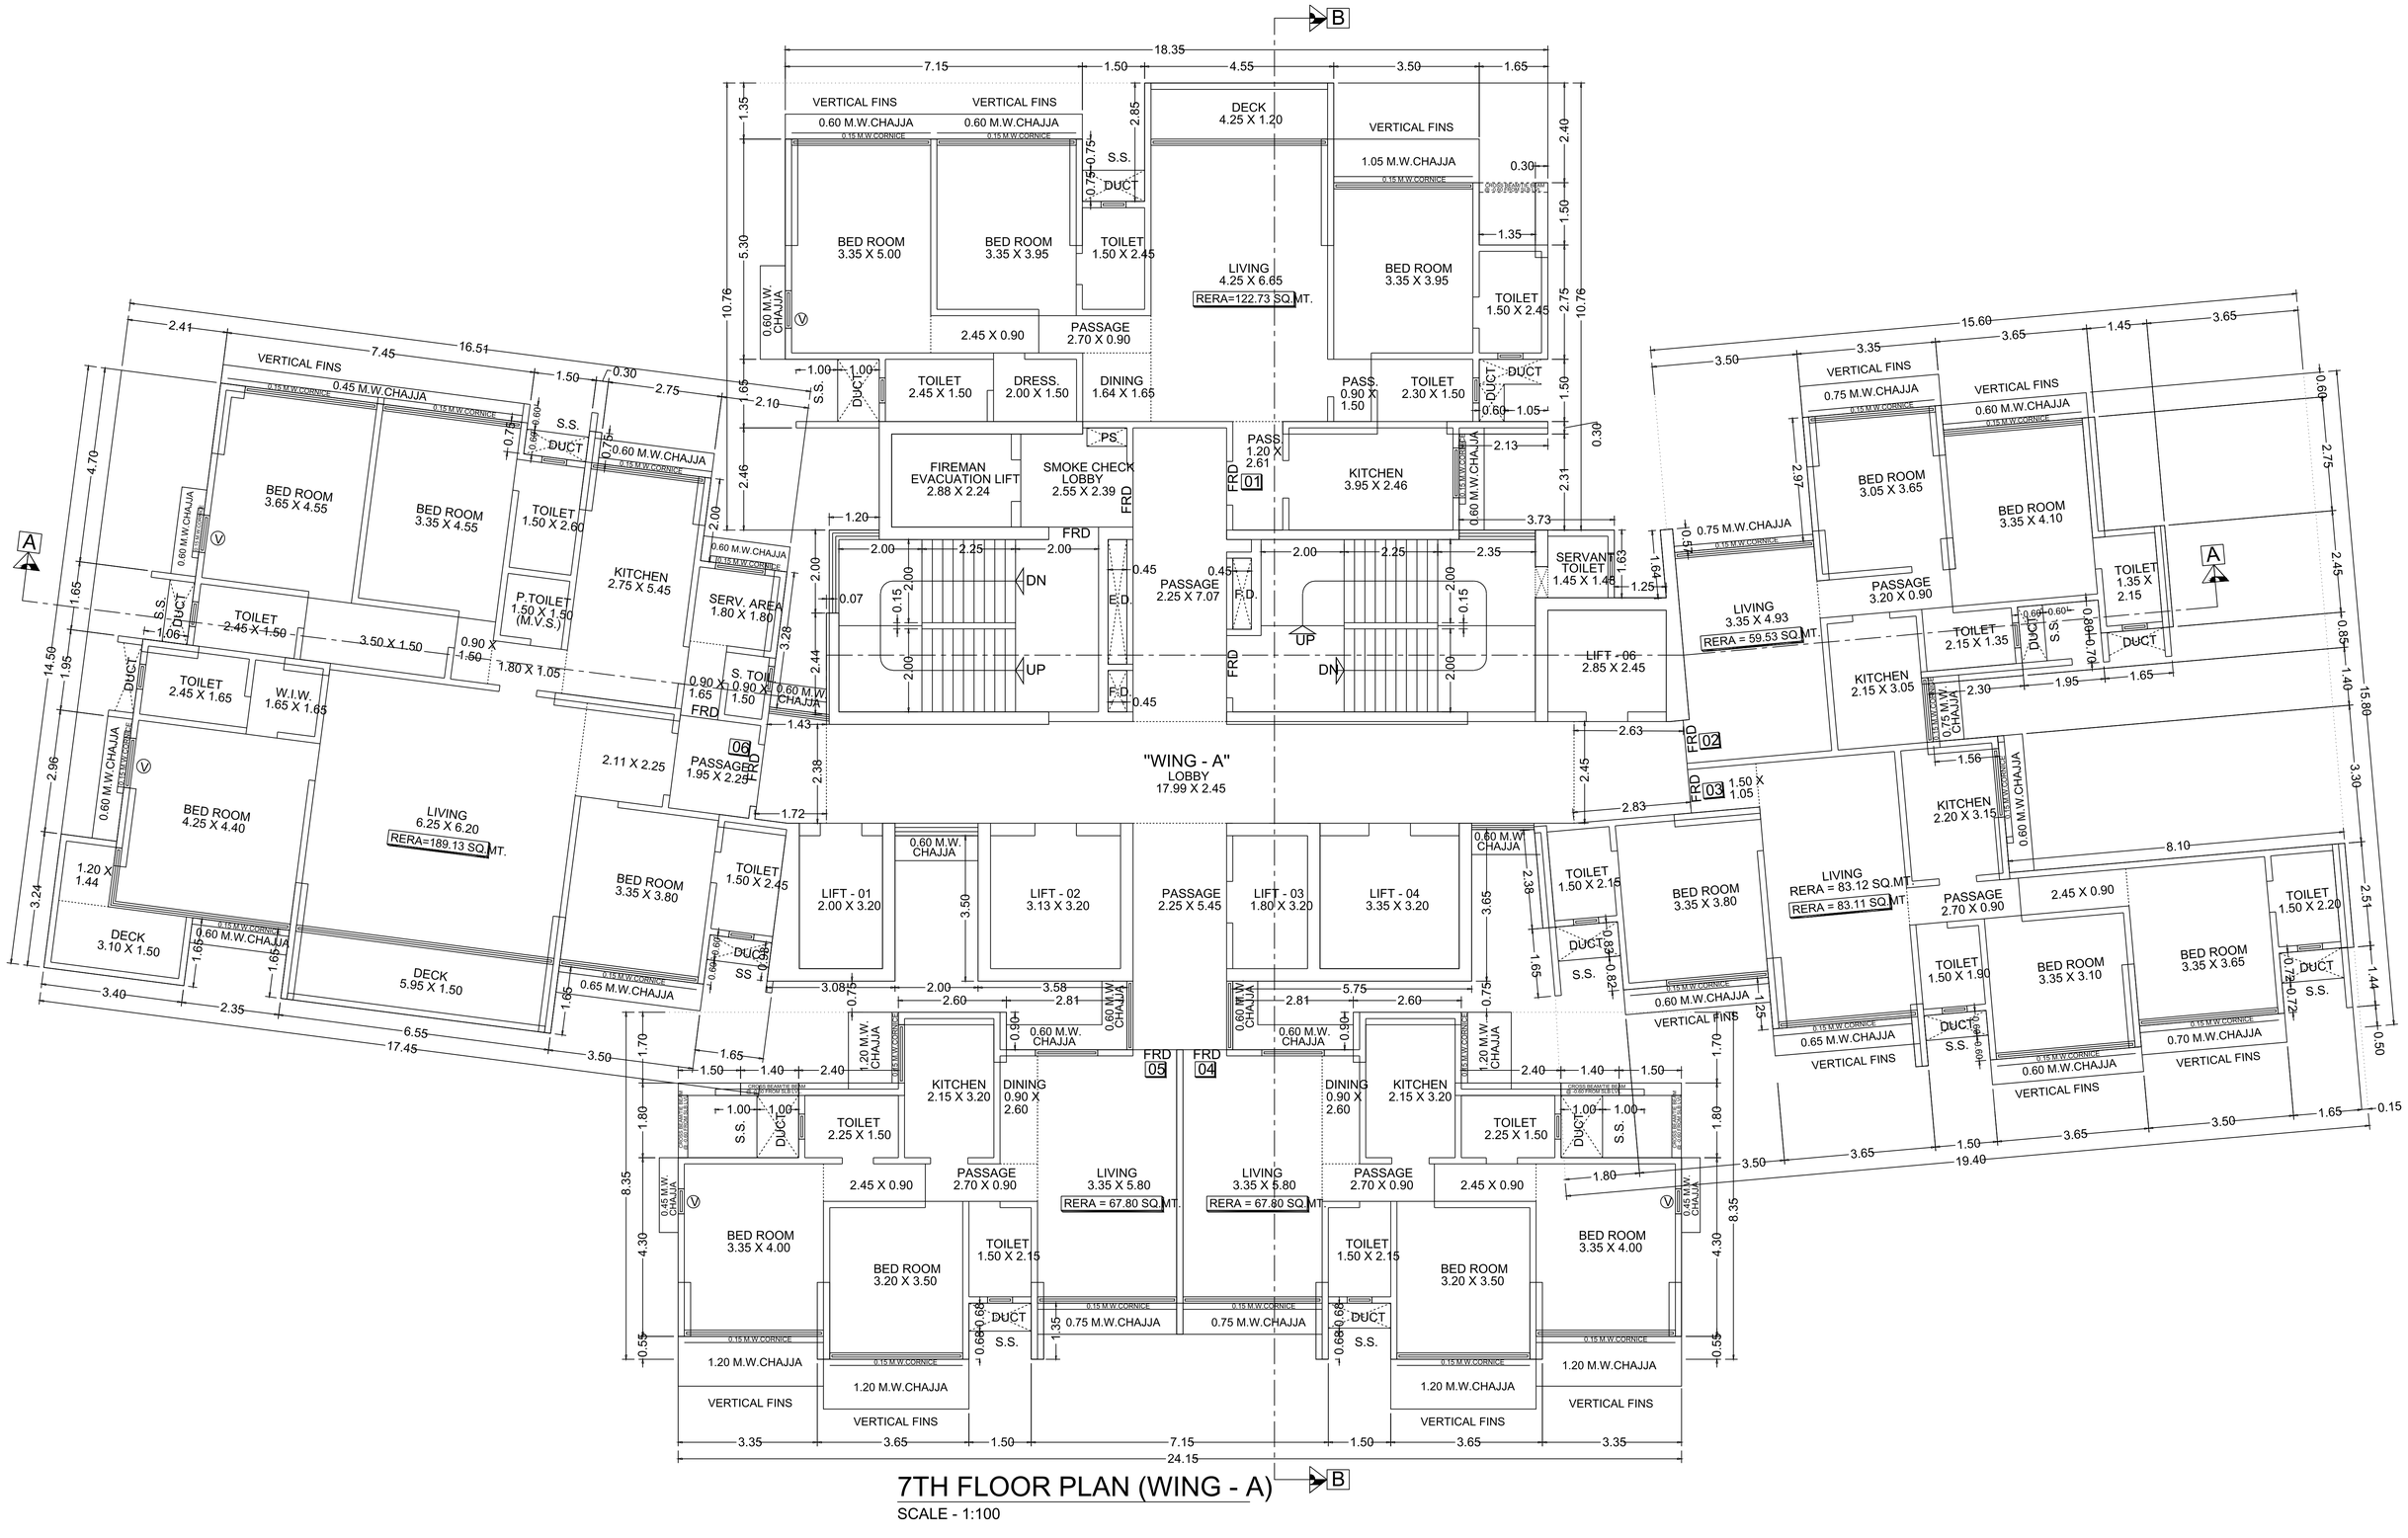

7TH FLOOR PLAN (WING - A)


SCALE - 1:100

SCALE - 1:100

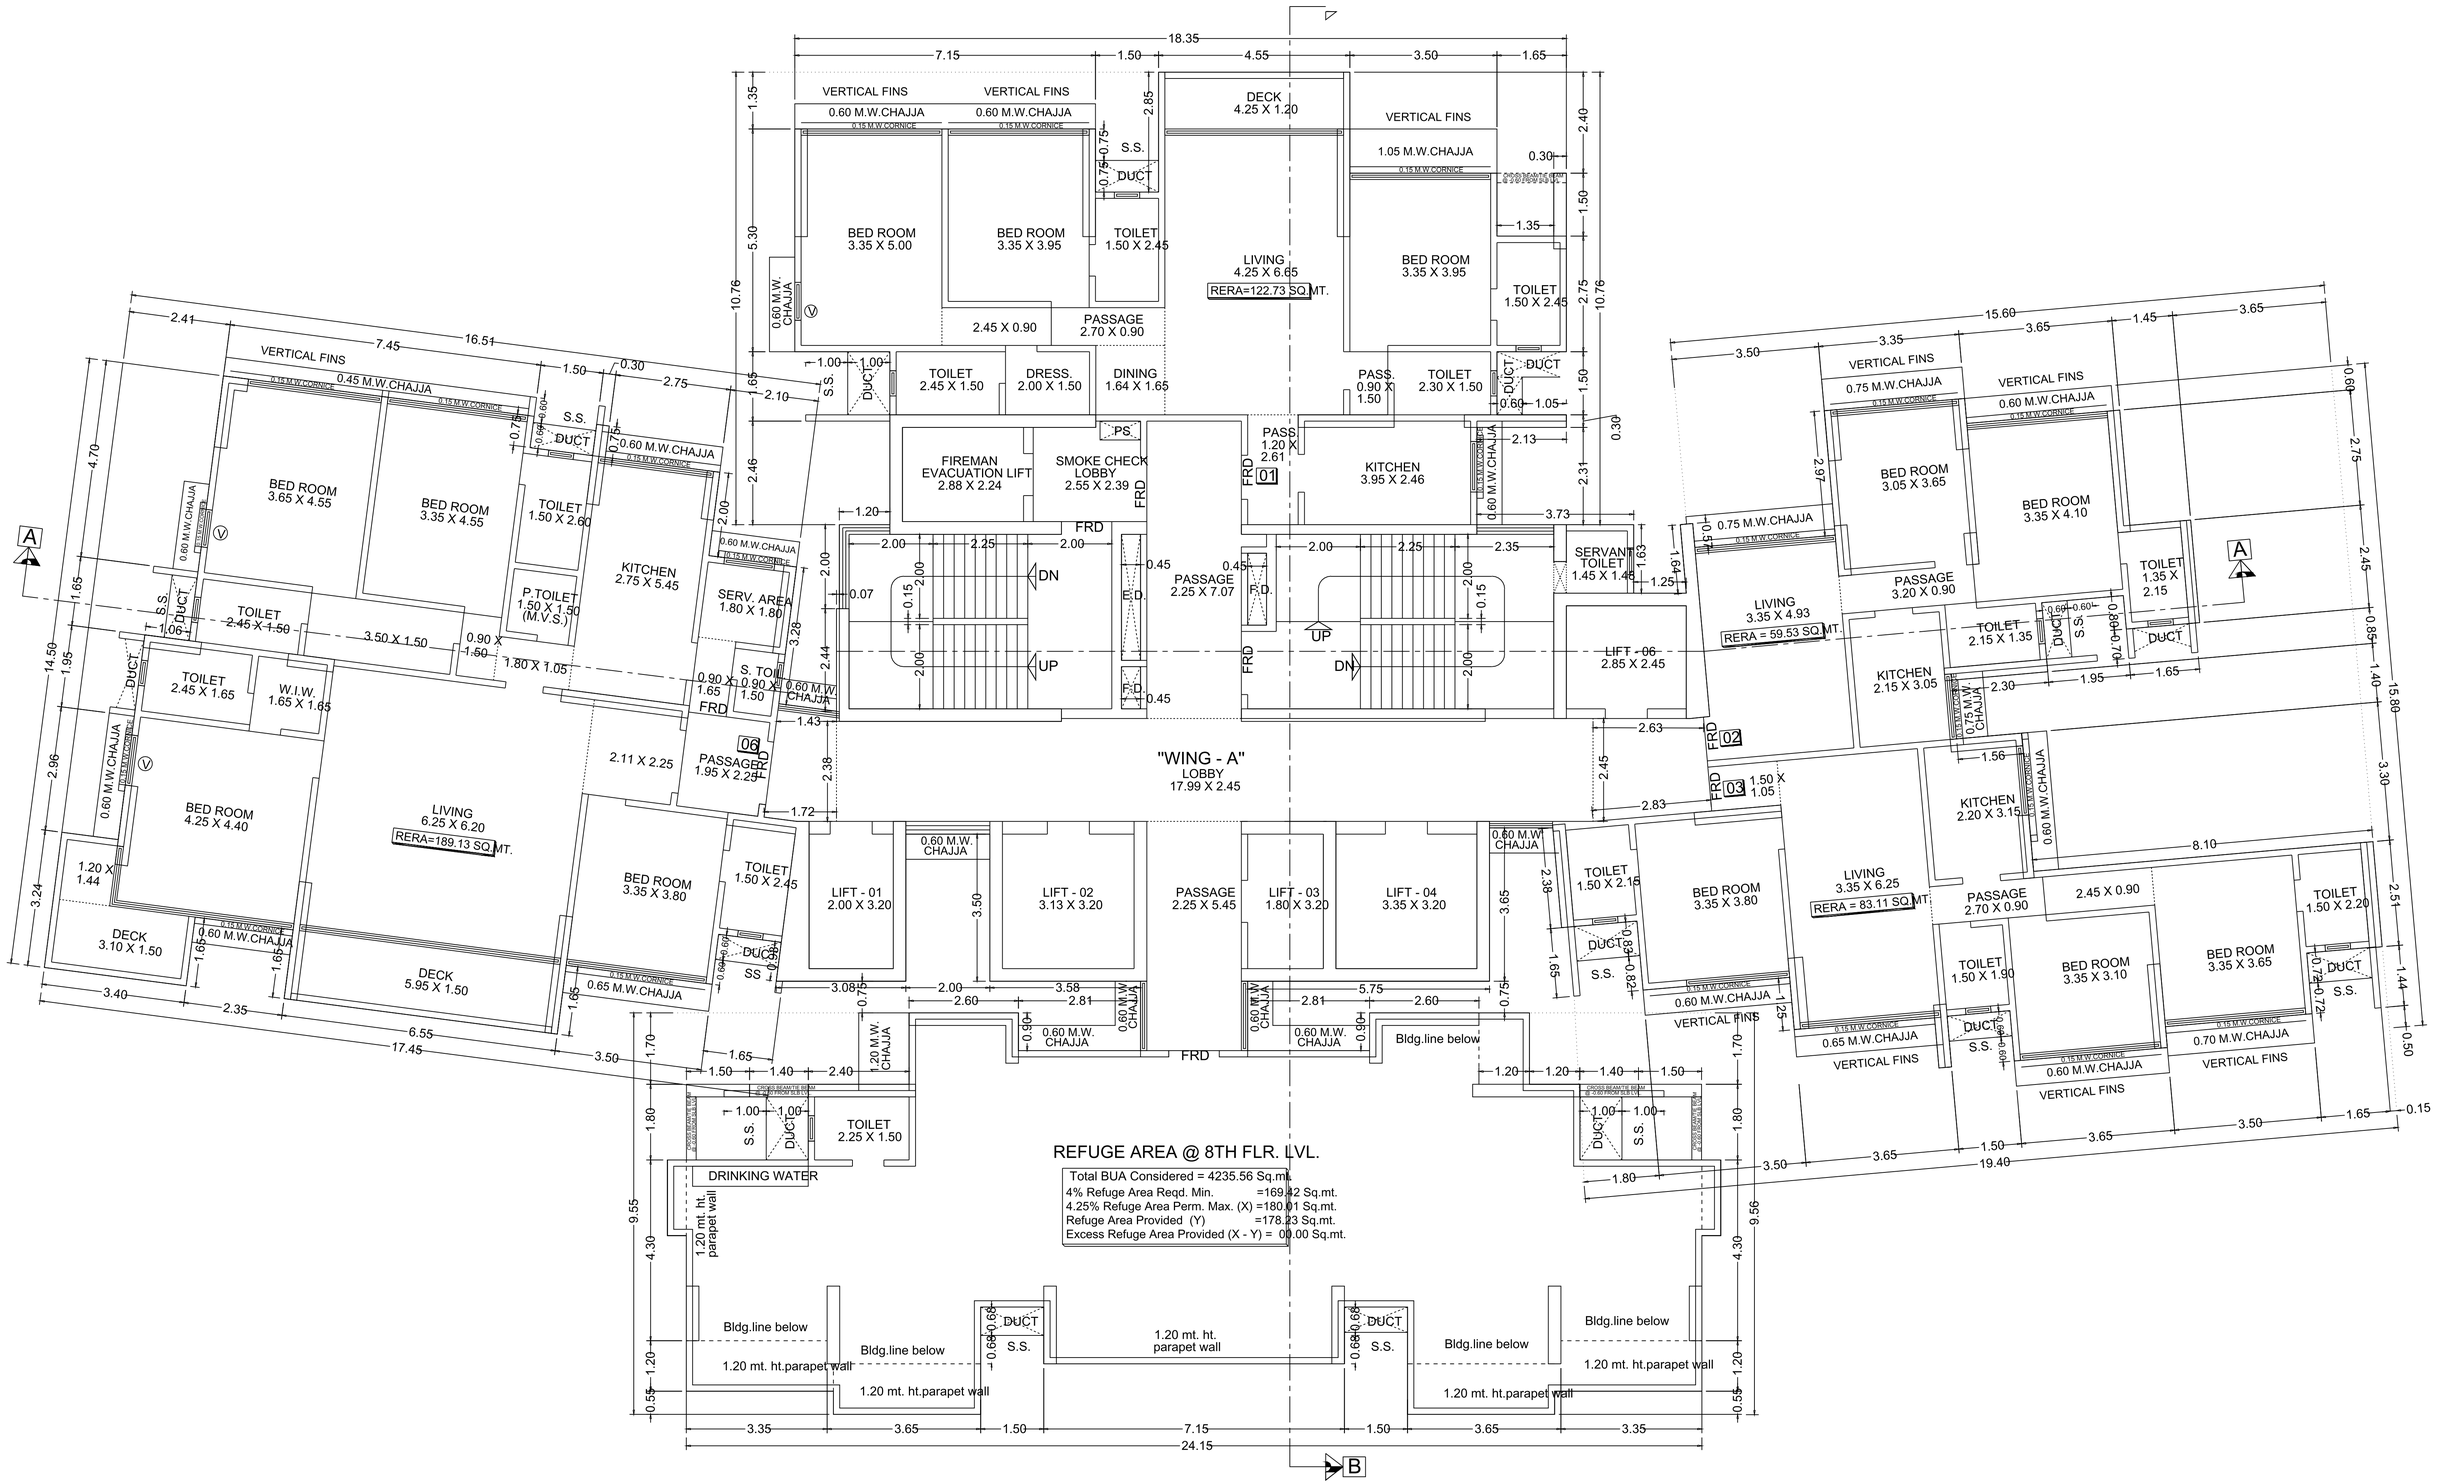

8TH REFUGE FLOOR PLAN (WING - A)


SCALE - 1:100

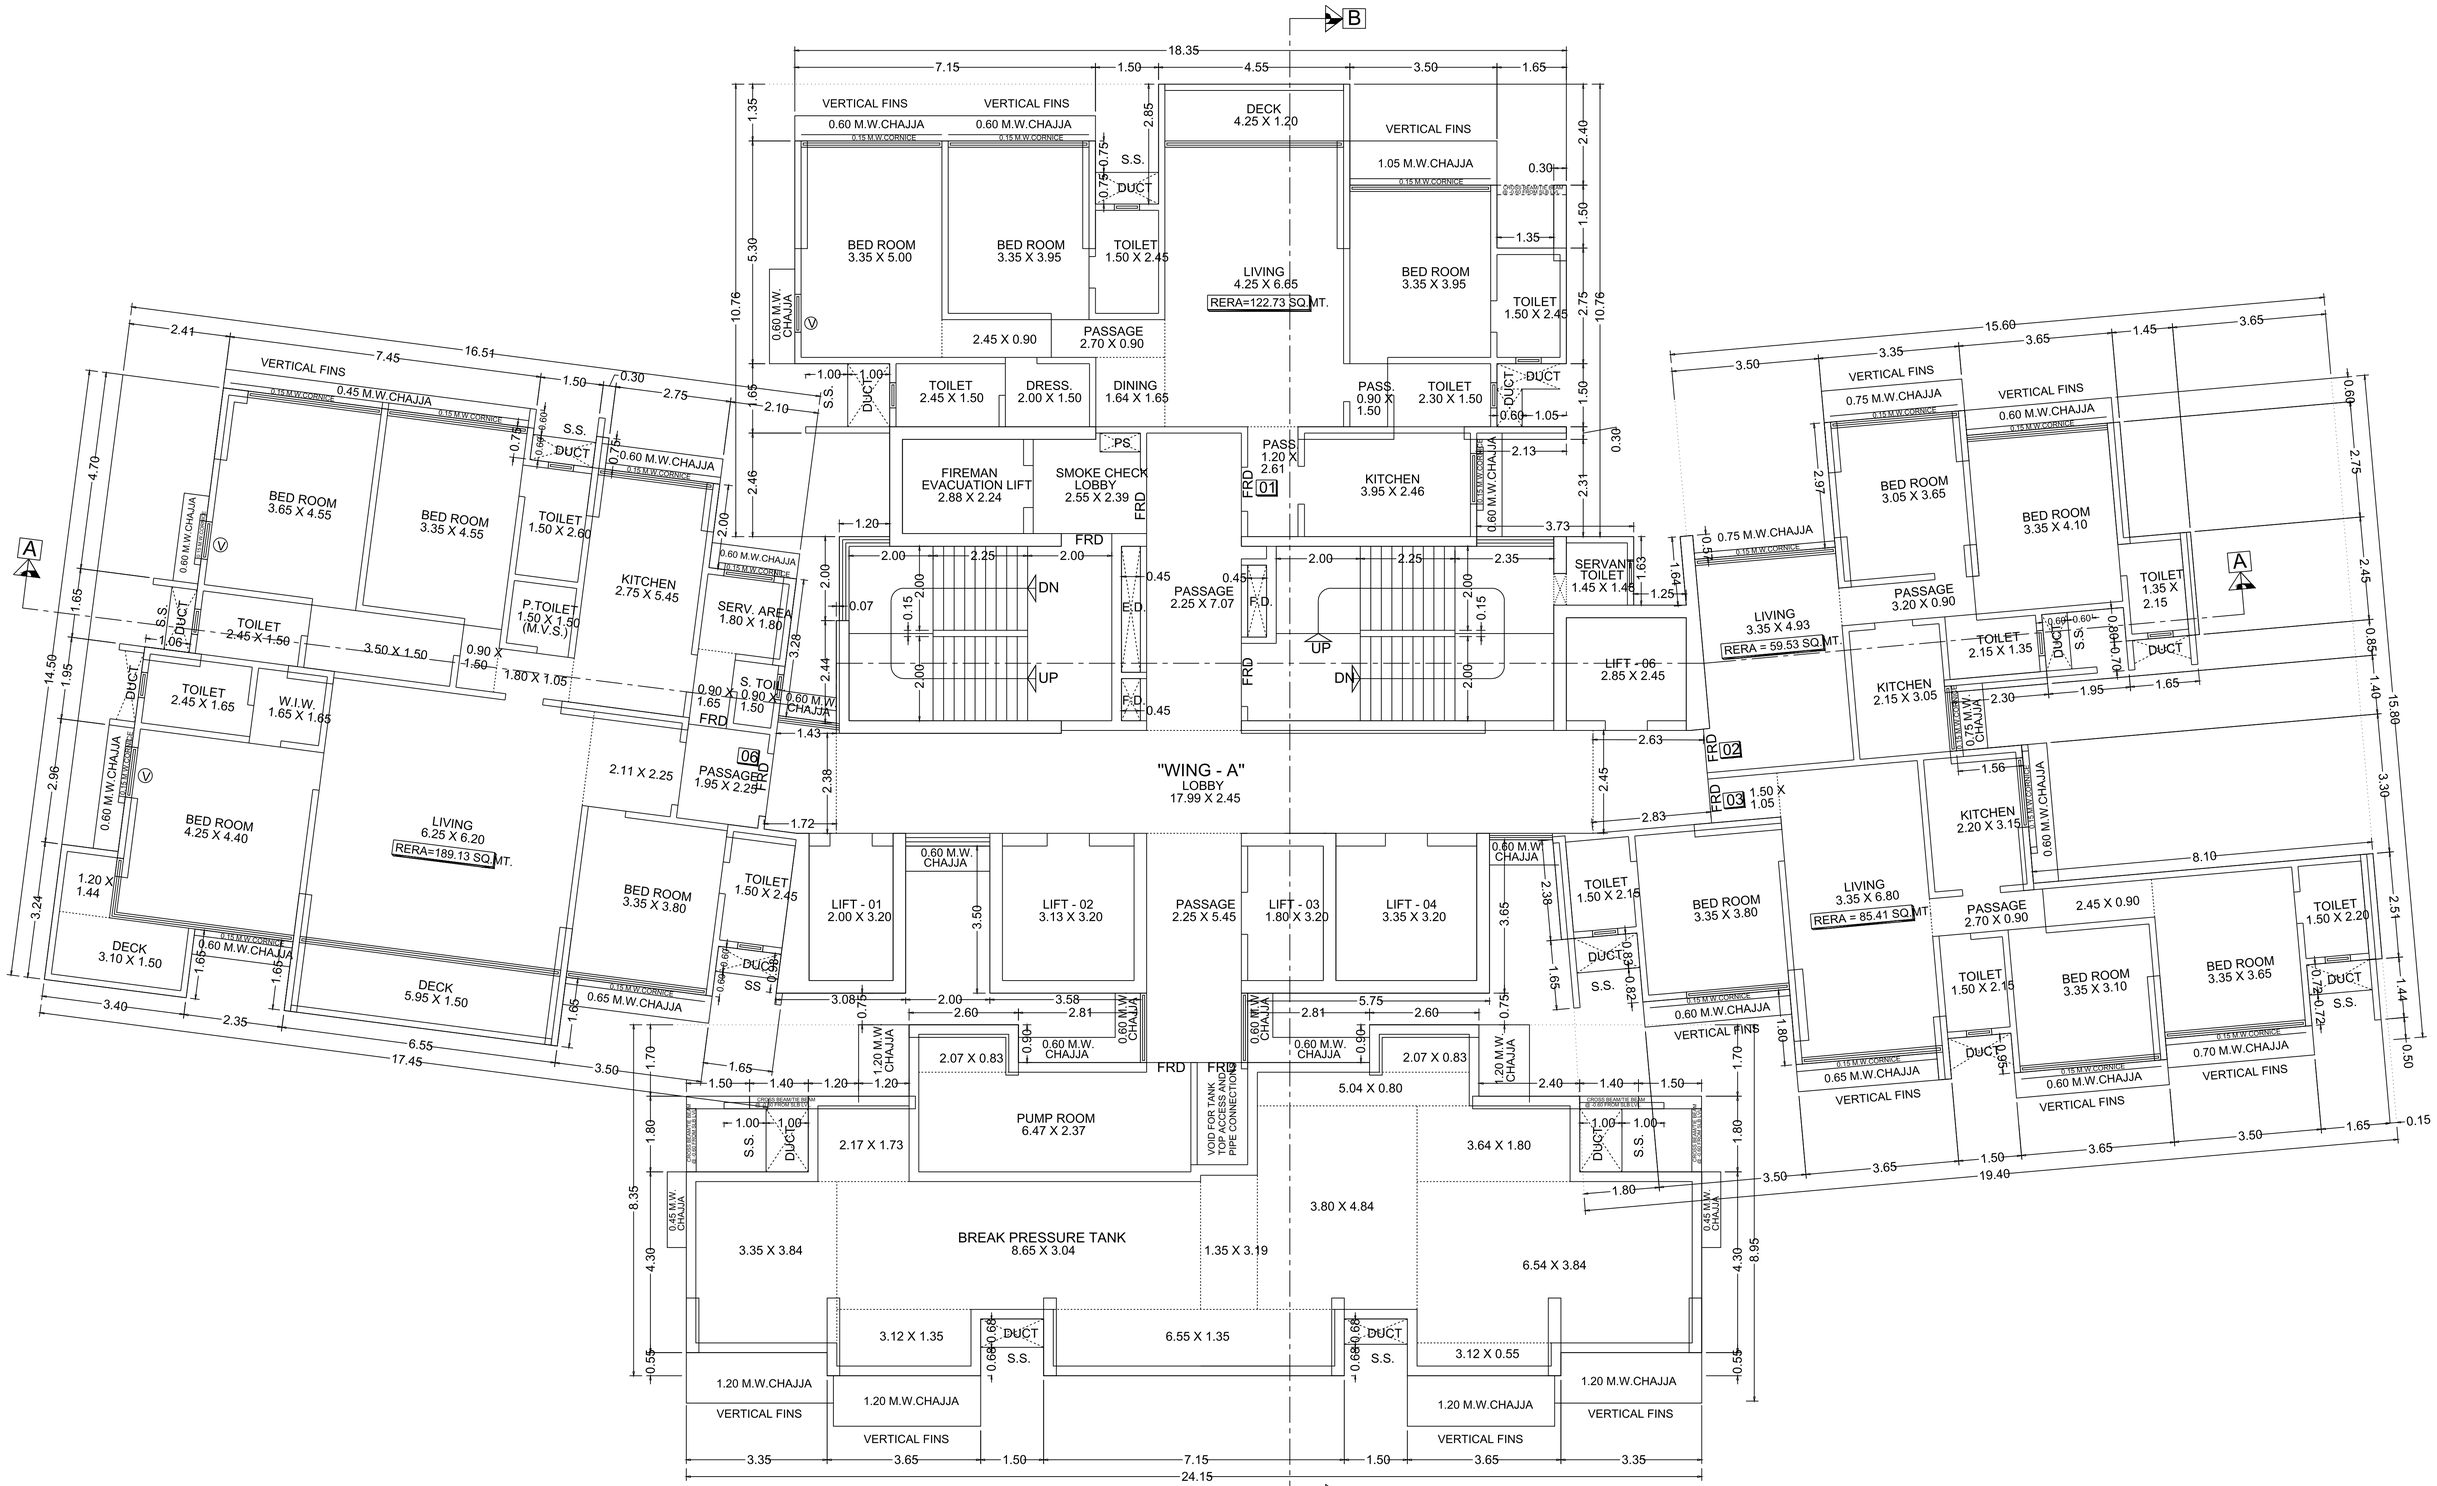

9TH BREAK PRESSURE TANK FLOOR PLAN (WING - A)

SCALE - 1:100

SCALE - 1:100

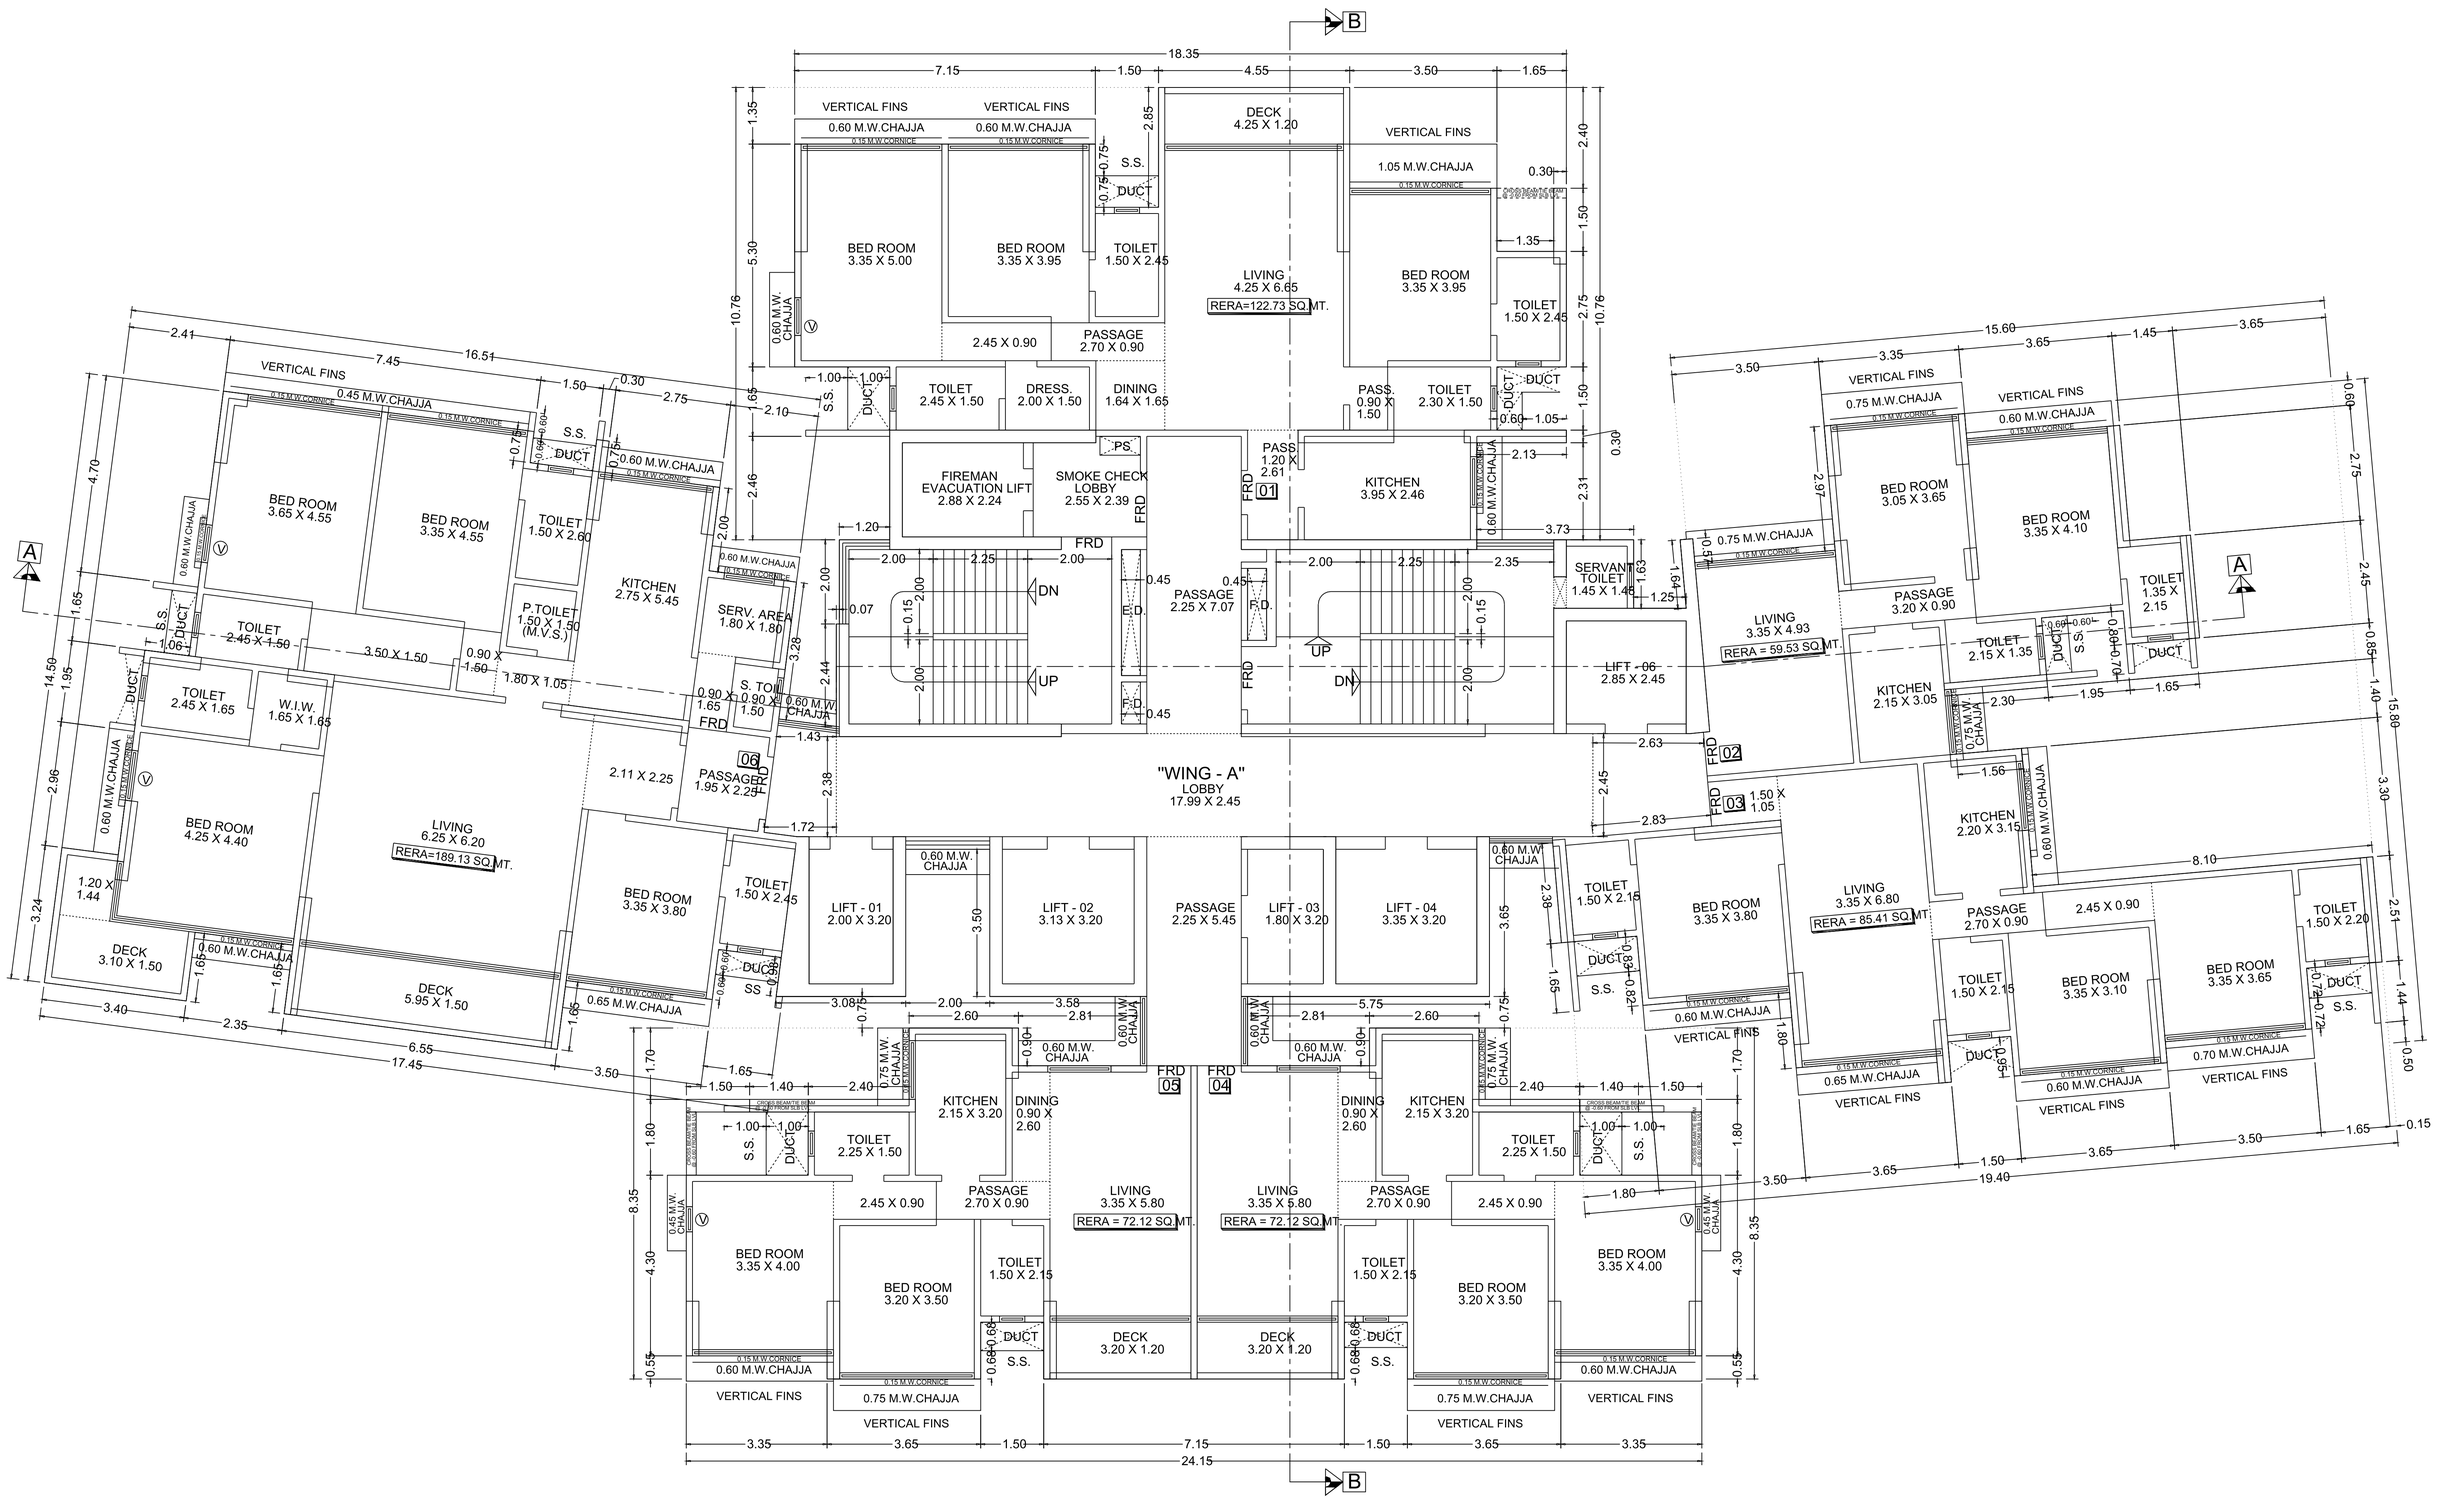

10TH TO 13TH FLOOR PLAN (WING - A)

SCALE - 1:100

14TH FLOOR PLAN (WING - A)

SCALE - 1:100

"WING - A"
LOBBY
17.99 X 2.45

BED ROOM 3.35 X 5.00
BED ROOM 3.35 X 3.95
TOILET 1.50 X 2.45
LIVING 4.25 X 6.65
RERA=122.73 SQ.MT.
DECK 4.25 X 1.20
BED ROOM 3.35 X 3.95
TOILET 1.50 X 2.45
PASSAGE 2.70 X 0.90
2.45 X 0.90
TOILET 2.45 X 1.50
DRESS. 2.00 X 1.50
DINING 1.64 X 1.65
PASS. 0.90 X 1.50
TOILET 2.30 X 1.50
FIREMAN EVACUATION LIFT 2.88 X 2.24
SMOKE CHECK LOBBY 2.55 X 2.39
PASS. 1.20 X 2.61
KITCHEN 3.95 X 2.46
PASSAGE 2.25 X 7.07
SERVANT TOILET 1.45 X 1.46
LIFT - 06 2.85 X 2.45
LIFT - 01 2.00 X 3.20
LIFT - 02 3.13 X 3.20
PASSAGE 2.25 X 5.45
LIFT - 03 1.80 X 3.20
LIFT - 04 3.35 X 3.20
BED ROOM 3.65 X 4.55
BED ROOM 3.35 X 4.55
TOILET 1.50 X 2.60
KITCHEN 2.75 X 5.45
P.TOILET 1.50 X 1.50 (M.V.S.)
SERV. AREA 1.80 X 1.80
TOILET 2.45 X 1.50
3.50 X 1.50
0.90 X 1.50
1.80 X 1.05
S. TOILET 0.90 X 1.65
0.90 X 1.50
TOILET 2.45 X 1.65
W.I.W. 1.65 X 1.65
PASSAGE 1.95 X 2.25
2.11 X 2.25
BED ROOM 4.25 X 4.40
LIVING 6.25 X 6.20
RERA=189.13 SQ.MT.
1.20 X 1.44
DECK 3.10 X 1.50
DECK 5.95 X 1.50
BED ROOM 3.35 X 3.80
TOILET 1.50 X 2.45
KITCHEN 2.15 X 3.20
DINING 0.90 X 2.60
TOILET 2.25 X 1.50
BED ROOM 3.35 X 4.00
BED ROOM 3.20 X 3.50
TOILET 1.50 X 2.15
LIVING 3.35 X 5.80
RERA = 72.12 SQ.MT.
DECK 3.20 X 1.20
BED ROOM 3.05 X 3.65
BED ROOM 3.35 X 4.10
TOILET 1.35 X 2.15
LIVING 3.35 X 4.93
RERA = 59.53 SQ.MT.
PASSAGE 3.20 X 0.90
TOILET 2.15 X 1.35
KITCHEN 2.15 X 3.05
KITCHEN 2.20 X 3.15
LIVING 3.35 X 6.80
RERA = 85.41 SQ.MT.
PASSAGE 2.70 X 0.90
2.45 X 0.90
TOILET 1.50 X 2.15
BED ROOM 3.35 X 3.10
BED ROOM 3.35 X 3.65
TOILET 1.50 X 2.20
BED ROOM 3.35 X 3.80
TOILET 1.50 X 2.15
1.50 X 1.05

0.60 M.W.CHAJJA
0.15 M.W.CORNICE
VERTICAL FINS
0.45 M.W.CHAJJA
1.05 M.W.CHAJJA
0.75 M.W.CHAJJA
0.65 M.W.CHAJJA
0.70 M.W.CHAJJA
S.S.
DUCT
FRD
PS.
W.D.
DN
UP
CROSS BEAM TIE BEAM @ 0.600 FROM SLB LVL
0.60 M.W. CHAJJA
1.20 M.W.CHAJJA
0.30
0.60 M.W.CHAJJA
0.15 M.W.CORNICE
0.60 M.W.CHAJJA
0.15 M.W.CORNICE
0.60 M.W.CHAJJA
0.15 M.W.CORNICE

15TH REFUGE FLOOR PLAN (WING - A)

SCALE - 1:100

"WING - A"
LOBBY
17.99 X 2.45

BED ROOM 3.65 X 4.55
BED ROOM 3.35 X 4.55
TOILET 1.50 X 2.60
KITCHEN 2.75 X 5.45
P.TOILET 1.50 X 1.50 (M.V.S.)
SERV. AREA 1.80 X 1.80
TOILET 2.45 X 1.50
TOILET 2.45 X 1.65
W.I.W. 1.65 X 1.65
BED ROOM 4.25 X 4.40
LIVING 6.25 X 6.20
RERA=189.13 SQ.MT.
DECK 3.10 X 1.50
DECK 5.95 X 1.50
BED ROOM 3.35 X 3.80
TOILET 1.50 X 2.45
PASSAGE 1.95 X 2.25
2.11 X 2.25
TOILET 2.25 X 1.50
DRINKING WATER
FIREMAN EVACUATION LIFT 2.88 X 2.24
SMOKE CHECK LOBBY 2.55 X 2.39
PASSAGE 2.25 X 7.07
LIFT - 01 2.00 X 3.20
LIFT - 02 3.13 X 3.20
PASSAGE 2.25 X 5.45
LIFT - 03 1.80 X 3.20
LIFT - 04 3.35 X 3.20
LIFT - 06 2.85 X 2.45
SERVANT TOILET 1.45 X 1.46
KITCHEN 3.95 X 2.46
PASS. 1.20 X 2.61
PASS. 0.90 X 1.50
TOILET 2.30 X 1.50
BED ROOM 3.35 X 3.95
TOILET 1.50 X 2.45
LIVING 4.25 X 6.65
RERA=122.73 SQ.MT.
DECK 4.25 X 1.20
BED ROOM 3.35 X 3.95
TOILET 1.50 X 2.45
2.45 X 0.90
PASSAGE 2.70 X 0.90
TOILET 2.45 X 1.50
DRESS. 2.00 X 1.50
DINING 1.64 X 1.65
1.50 X 1.05
TOILET 2.15 X 2.15
BED ROOM 3.35 X 3.80
LIVING 3.35 X 6.80
RERA = 85.41 SQ.MT.
PASSAGE 2.70 X 0.90
2.45 X 0.90
TOILET 1.50 X 2.15
BED ROOM 3.35 X 3.10
BED ROOM 3.35 X 3.65
TOILET 1.50 X 2.20
KITCHEN 2.20 X 3.15
1.50 X 1.05
BED ROOM 3.05 X 3.65
BED ROOM 3.35 X 4.10
PASSAGE 3.20 X 0.90
TOILET 1.35 X 2.15
LIVING 3.35 X 4.93
RERA = 59.53 SQ.MT.
TOILET 2.15 X 1.35
KITCHEN 2.15 X 3.05

VERTICAL FINS
0.60 M.W.CHAJJA
0.15 M.W.CORNICE
0.45 M.W.CHAJJA
0.75 M.W.CHAJJA
1.05 M.W.CHAJJA
0.65 M.W.CHAJJA
0.70 M.W.CHAJJA
0.60 M.W. CHAJJA
DUCT
S.S.
FRD
UP
DN
Bldg.line below
1.20 mt. ht. parapet wall
1.20 mt. ht.parapet wall
CROSS BEAM T/E BEAM @ 0.600 FROM SLB LVL

REFUGE AREA @ 15TH FLR. LVL.

Total BUA Considered = 4447.70 Sq.mt.
4% Refuge Area Reqd. Min. =177.91 Sq.mt.
4.25% Refuge Area Perm. Max. (X) =189.03 Sq.mt.
Refuge Area Provided (Y) =180.27 Sq.mt.
Excess Refuge Area Provided (X - Y) = 00.00 Sq.mt.

16TH FLOOR PLAN (WING - A)


SCALE - 1:100


"WING - A"
LOBBY
17.99 X 2.45

BED ROOM 3.35 X 5.00
BED ROOM 3.35 X 3.95
TOILET 1.50 X 2.45
LIVING 4.25 X 6.65
RERA=122.73 SQ.MT.
DECK 4.25 X 1.20
BED ROOM 3.35 X 3.95
TOILET 1.50 X 2.45
PASSAGE 2.70 X 0.90
2.45 X 0.90
TOILET 2.45 X 1.50
DRESS. 2.00 X 1.50
DINING 1.64 X 1.65
PASS. 0.90 X 1.50
TOILET 2.30 X 1.50
FIREMAN EVACUATION LIFT 2.88 X 2.24
SMOKE CHECK LOBBY 2.55 X 2.39
PASS. 1.20 X 2.61
KITCHEN 3.95 X 2.46
PASSAGE 2.25 X 7.07
SERVANT TOILET 1.45 X 1.46
LIFT - 06 2.85 X 2.45
BED ROOM 3.65 X 4.55
BED ROOM 3.35 X 4.55
TOILET 1.50 X 2.60
KITCHEN 2.75 X 5.45
P.TOILET 1.50 X 1.50 (M.V.S.)
SERV. AREA 1.80 X 1.80
TOILET 2.45 X 1.50
3.50 X 1.50
0.90 X 1.50
1.80 X 1.05
TOILET 2.45 X 1.65
W.I.W. 1.65 X 1.65
S. TOILET 0.90 X 1.65
0.90 X 1.50
2.11 X 2.25
PASSAGE 1.95 X 2.25
BED ROOM 4.25 X 4.40
LIVING 6.25 X 6.20
RERA=189.13 SQ.MT.
1.20 X 1.44
DECK 3.10 X 1.50
DECK 5.95 X 1.50
BED ROOM 3.35 X 3.80
TOILET 1.50 X 2.45
LIFT - 01 2.00 X 3.20
LIFT - 02 3.13 X 3.20
PASSAGE 2.25 X 5.45
LIFT - 03 1.80 X 3.20
LIFT - 04 3.35 X 3.20
TOILET 1.50 X 2.15
BED ROOM 3.35 X 3.80
KITCHEN 2.15 X 3.20
DINING 0.90 X 2.60
TOILET 2.25 X 1.50
2.45 X 0.90
PASSAGE 2.70 X 0.90
LIVING 3.35 X 5.80
RERA = 72.12 SQ.MT.
BED ROOM 3.35 X 4.00
BED ROOM 3.20 X 3.50
TOILET 1.50 X 2.15
DECK 3.20 X 1.20
BED ROOM 3.05 X 3.65
BED ROOM 3.35 X 4.10
LIVING 3.35 X 5.45
RERA = 61.35 SQ.MT.
PASSAGE 3.20 X 0.90
TOILET 1.35 X 2.15
KITCHEN 2.15 X 3.05
TOILET 2.15 X 1.35
LIVING 3.35 X 6.80
RERA = 85.41 SQ.MT.
PASSAGE 2.70 X 0.90
6.17 X 10.15(AVG.)
2.45 X 0.90
TOILET 1.50 X 2.15
BED ROOM 3.35 X 3.10
BED ROOM 3.35 X 3.65
TOILET 1.50 X 2.20
KITCHEN 2.20 X 3.15
1.50 X 1.05
DUCT
S.S.
0.60 M.W.CHAJJA
0.15 M.W.CORNICE
VERTICAL FINS
0.45 M.W.CHAJJA
0.75 M.W.CHAJJA
1.05 M.W.CHAJJA
0.65 M.W.CHAJJA
0.70 M.W.CHAJJA
CROSS BEAM TIE BEAM @ 0.00 FROM W.B.T.L.
FRD
01
02
03
04
05
06
UP
DN
P.D.
PS
V
A
B

17TH & 18TH FLOOR PLAN (WING - A)

SCALE - 1:100

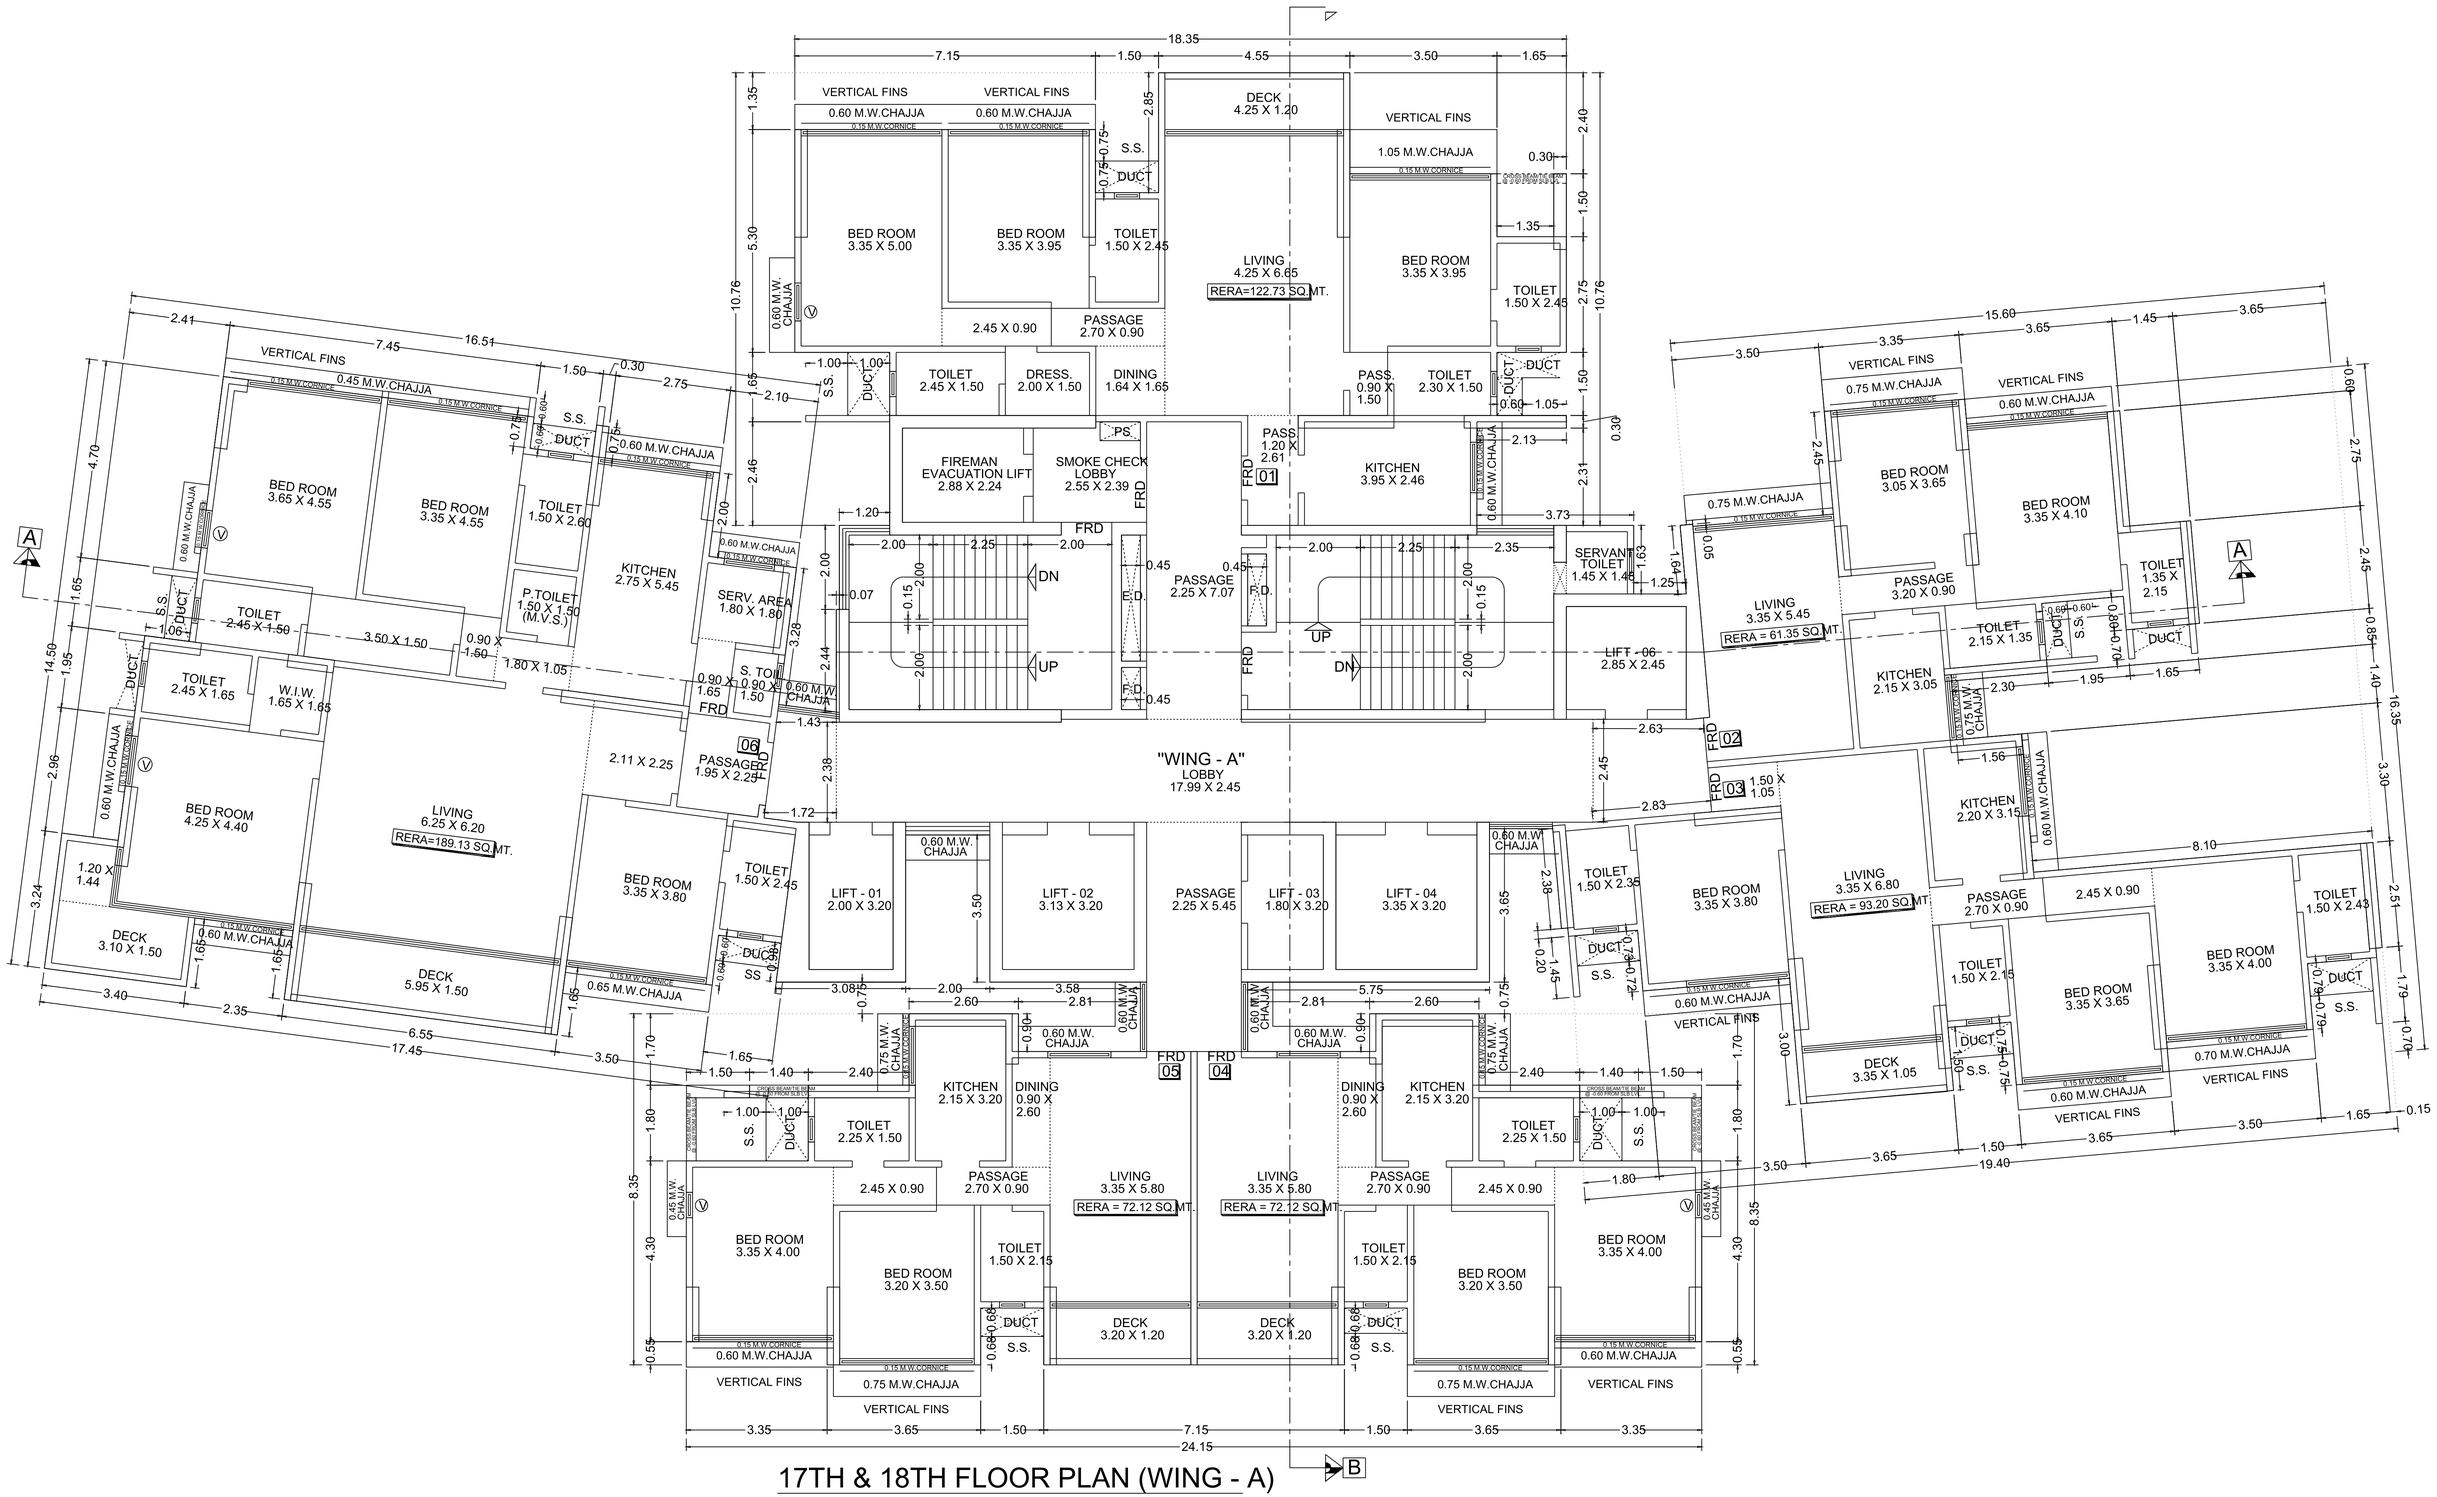

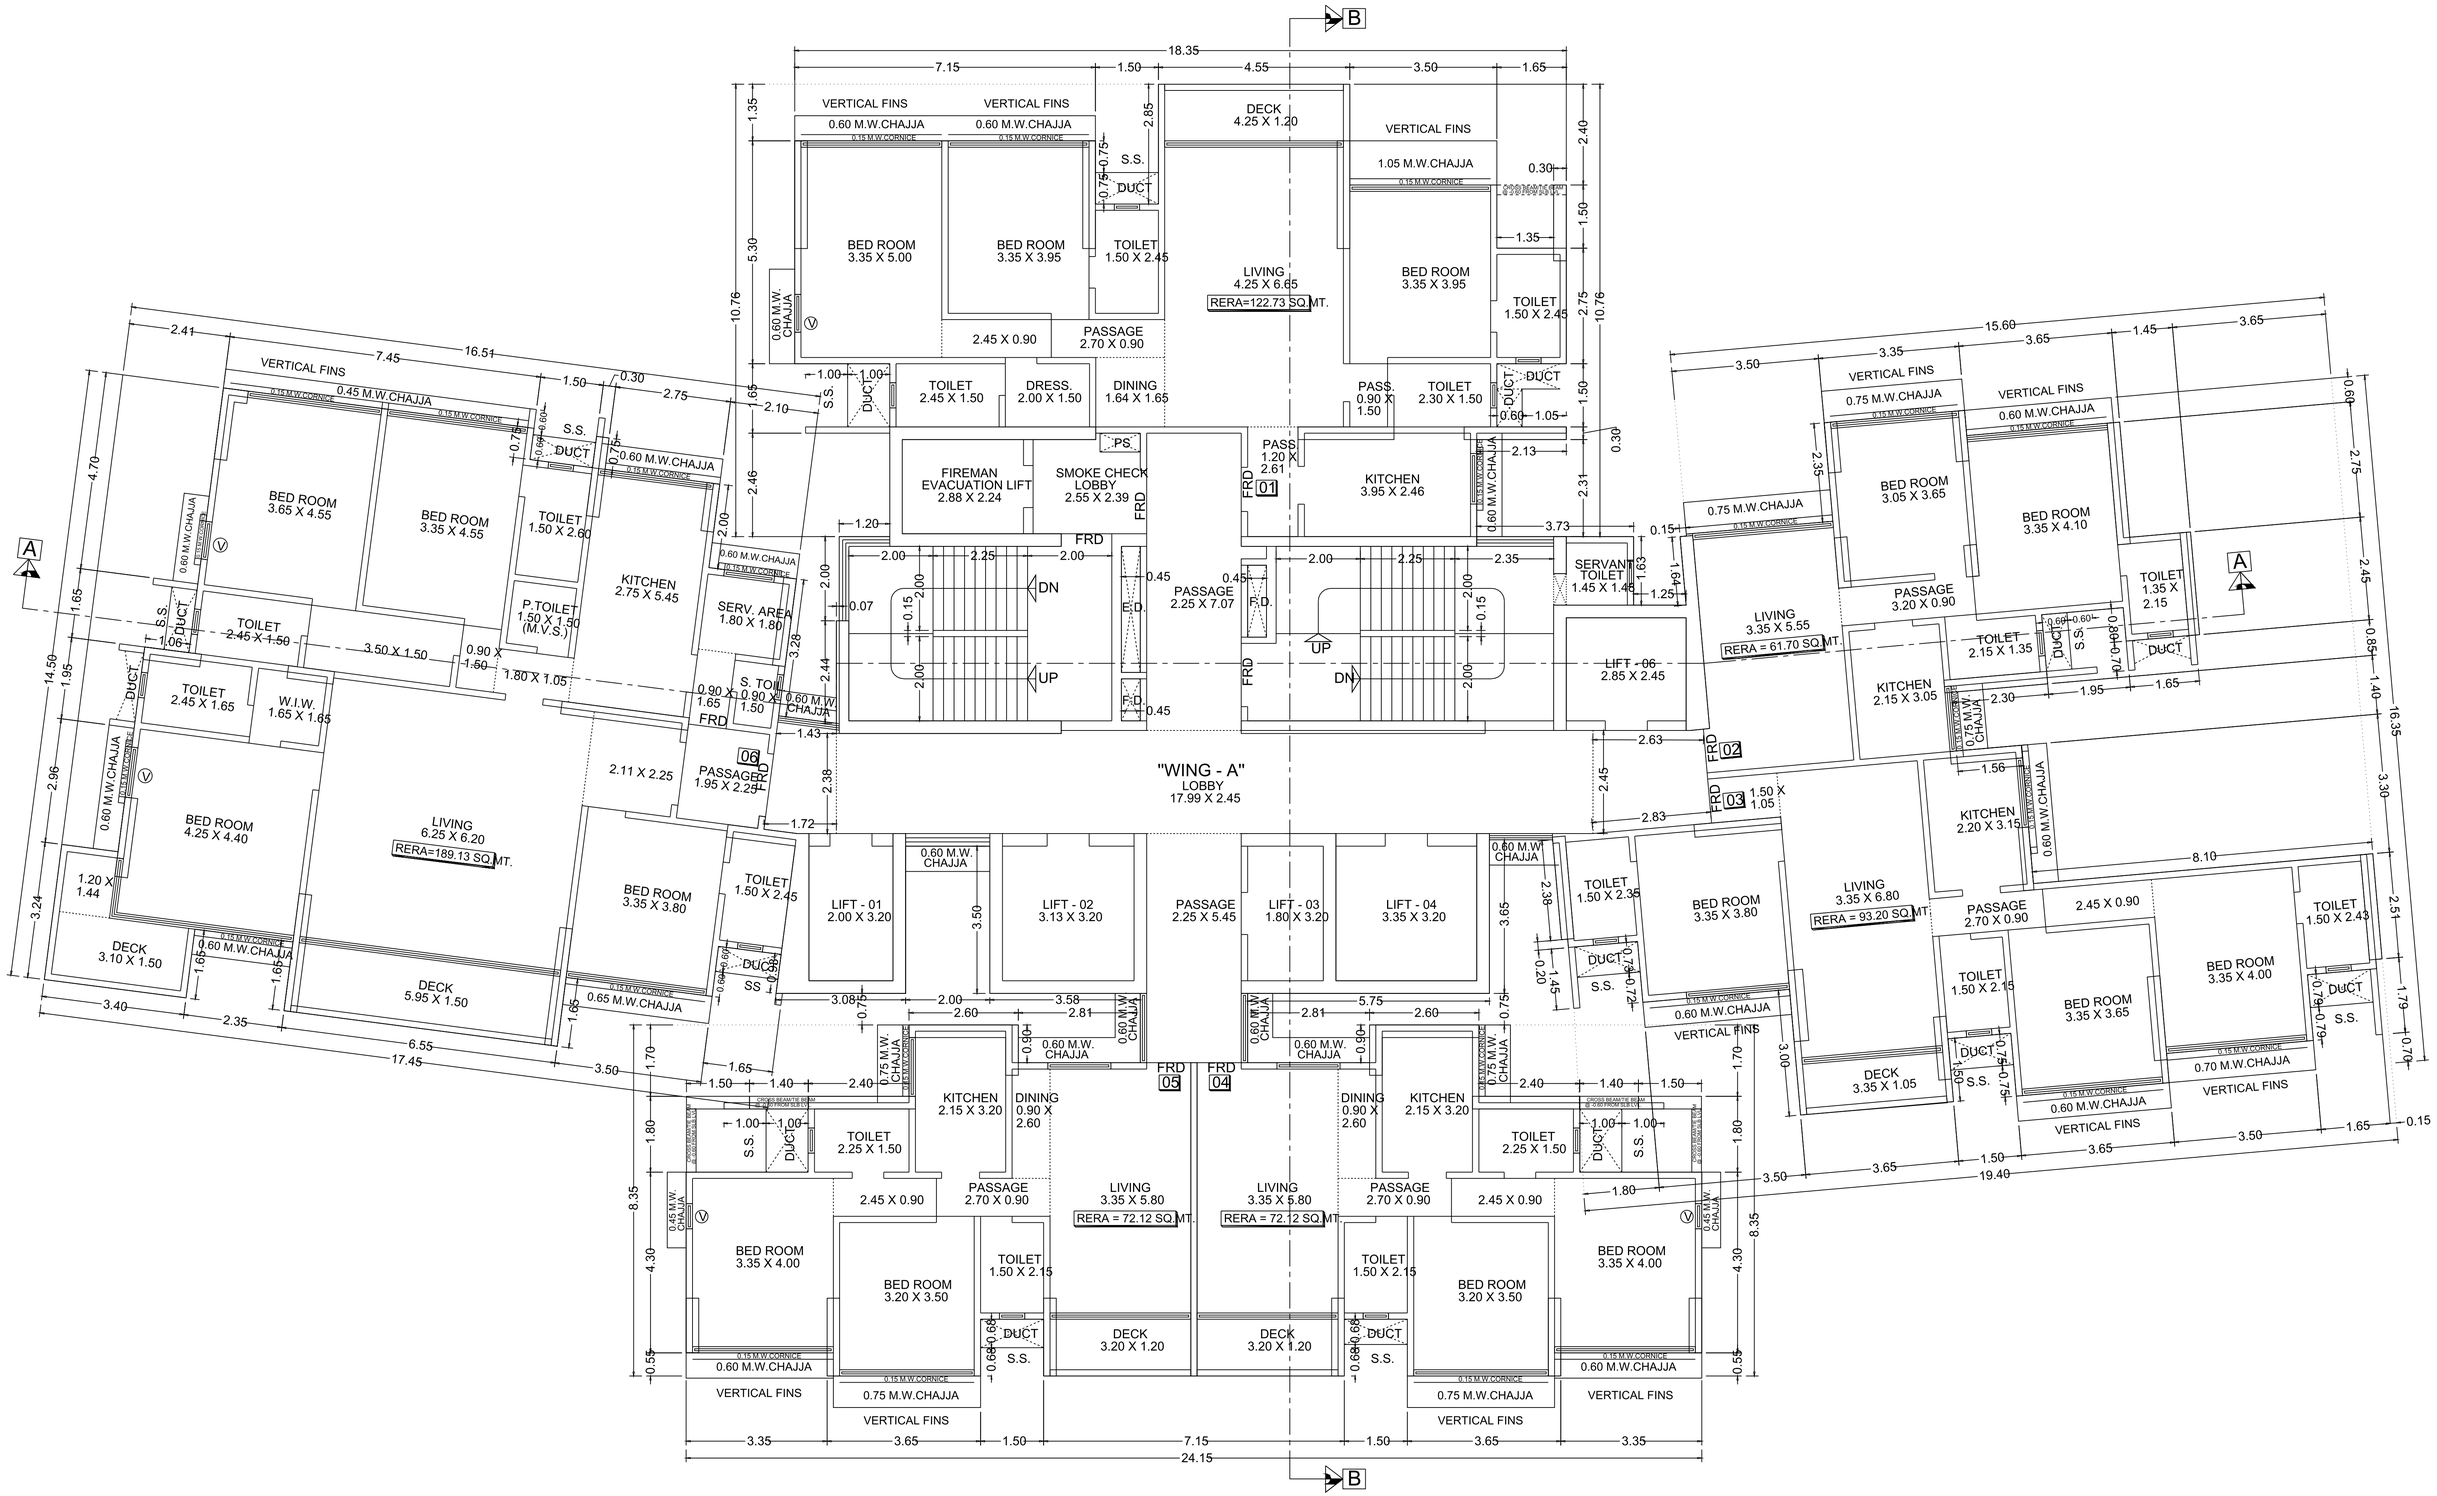


19TH, 20TH, 24TH & 25TH FLOOR PLAN (WING - A)

SCALE - 1:100

21ST & 23RD FLOOR FLOOR PLAN (WING - A)

SCALE - 1:100

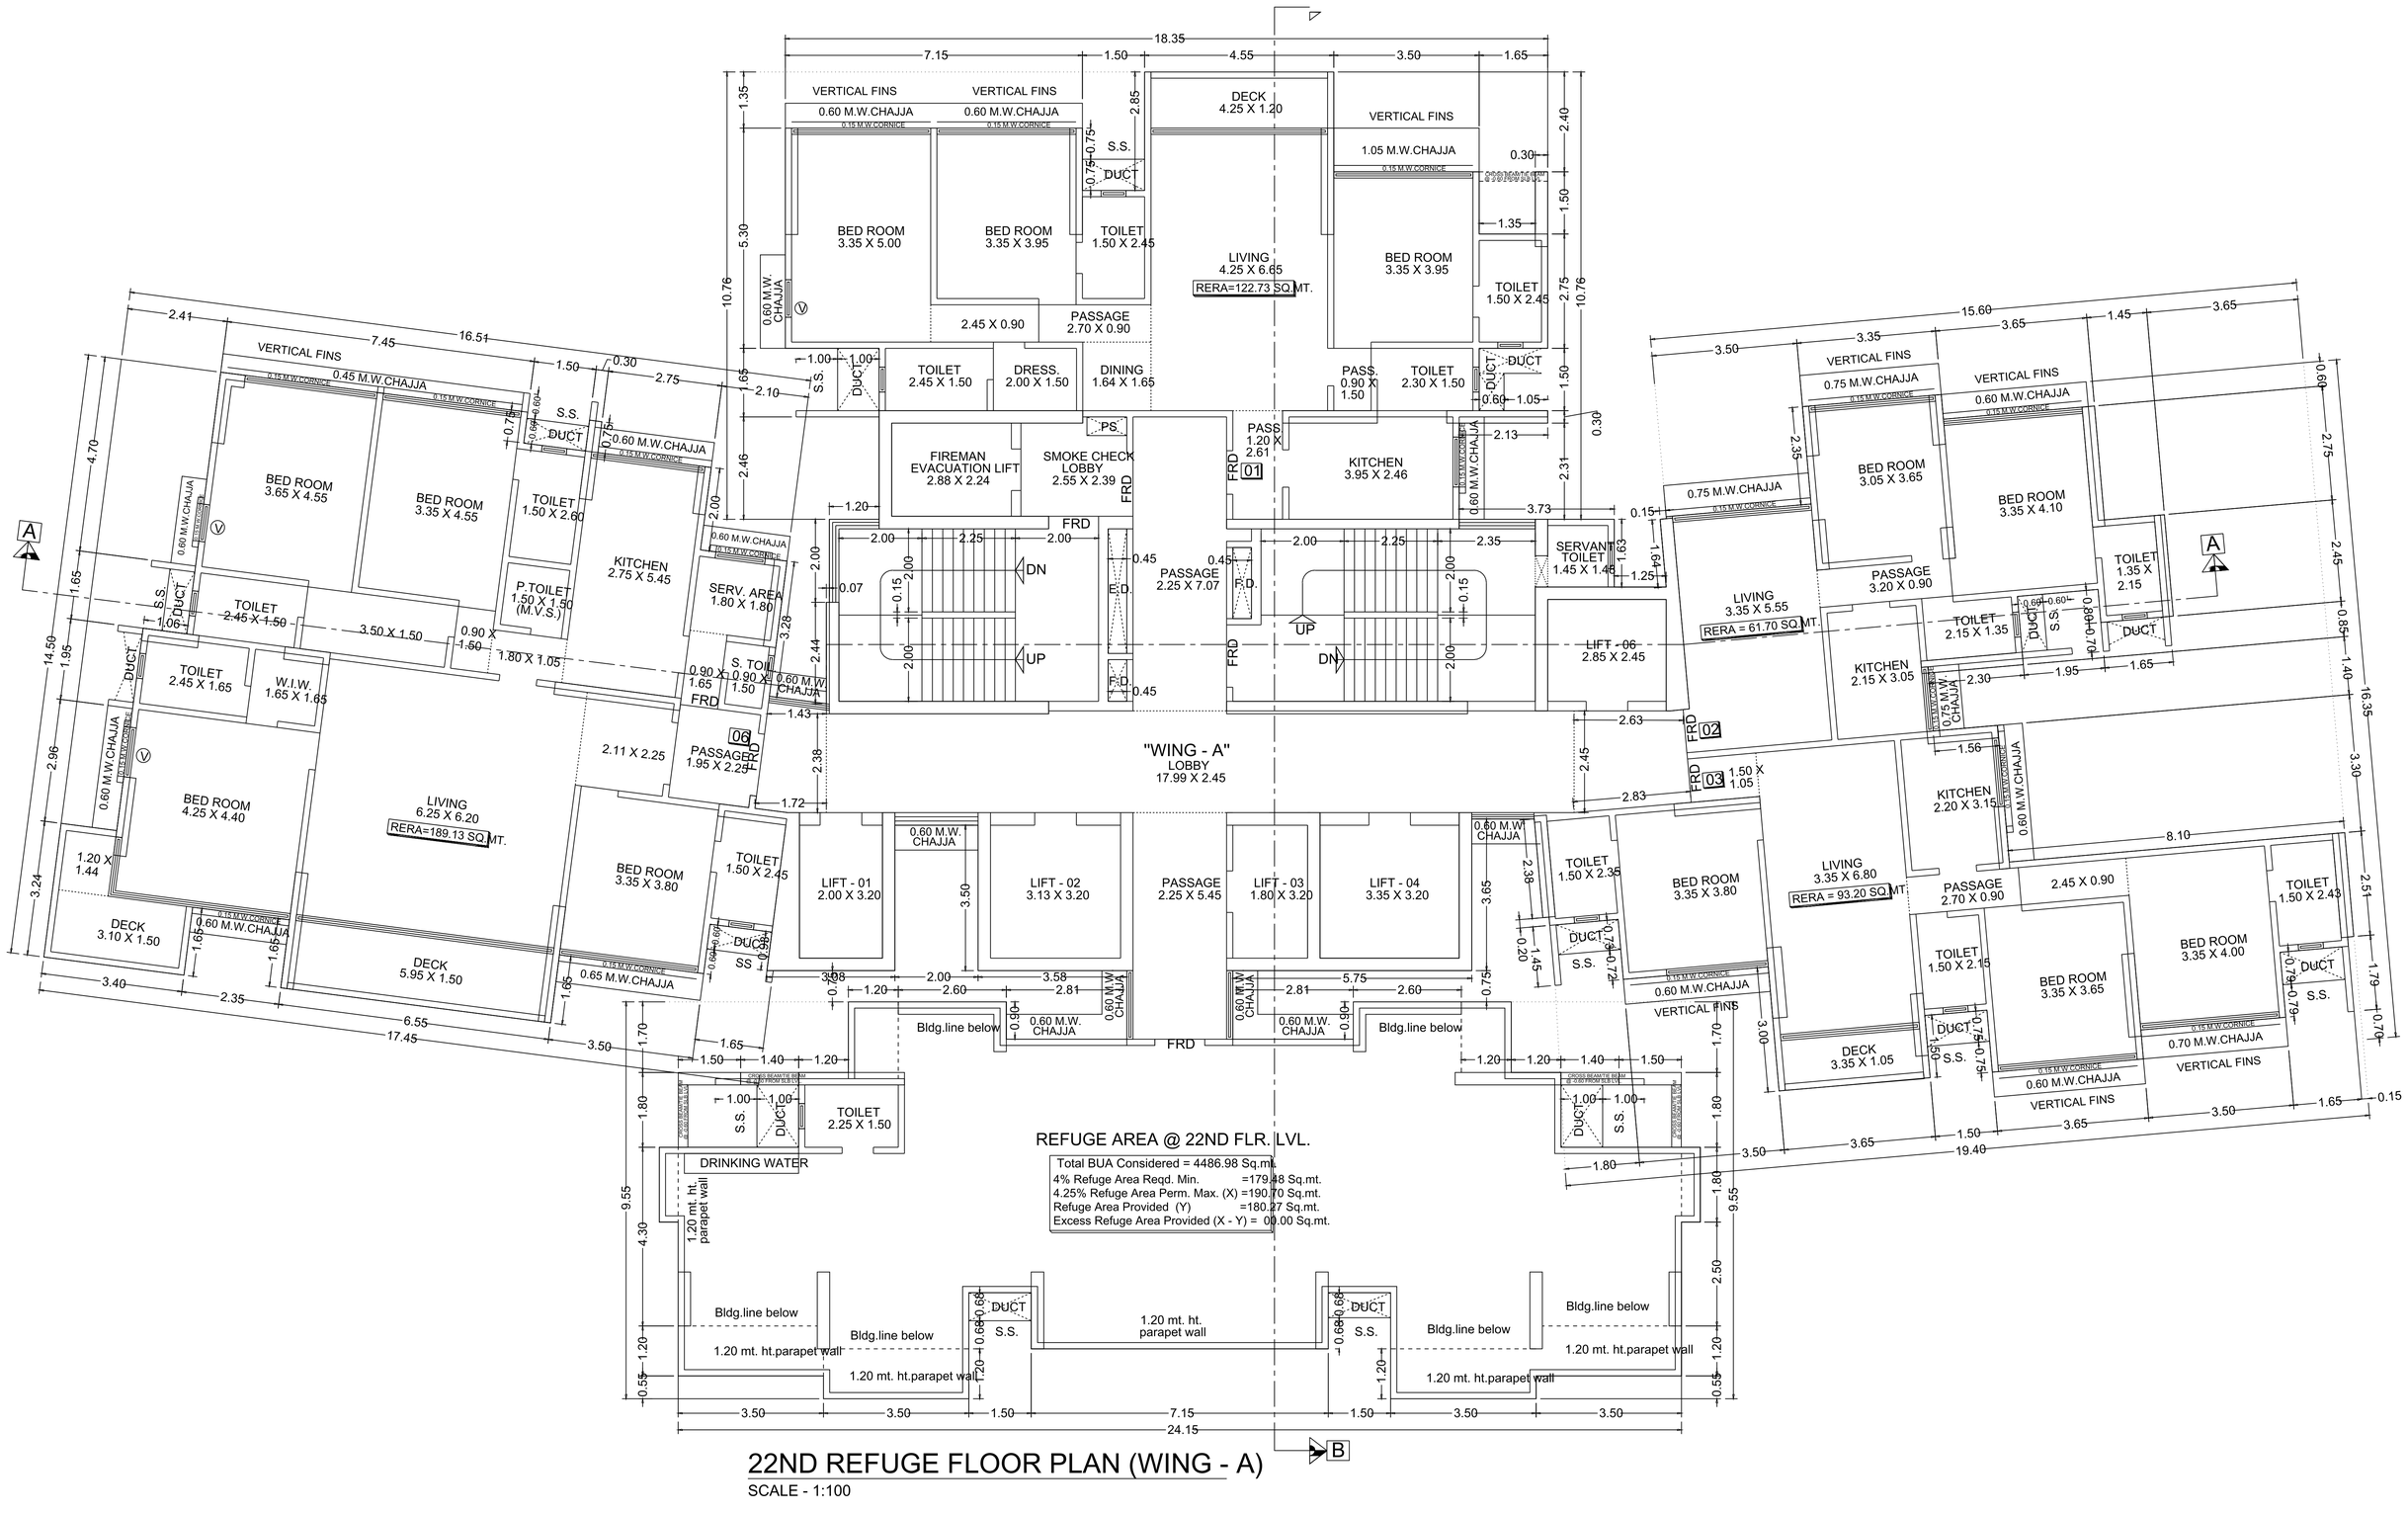

22ND REFUGE FLOOR PLAN (WING - A)

SCALE - 1:100