

ADDITIONAL LOS
LOS 15.5

SCALE :- 1:100


1ST PODIUM FLOOR PLAN

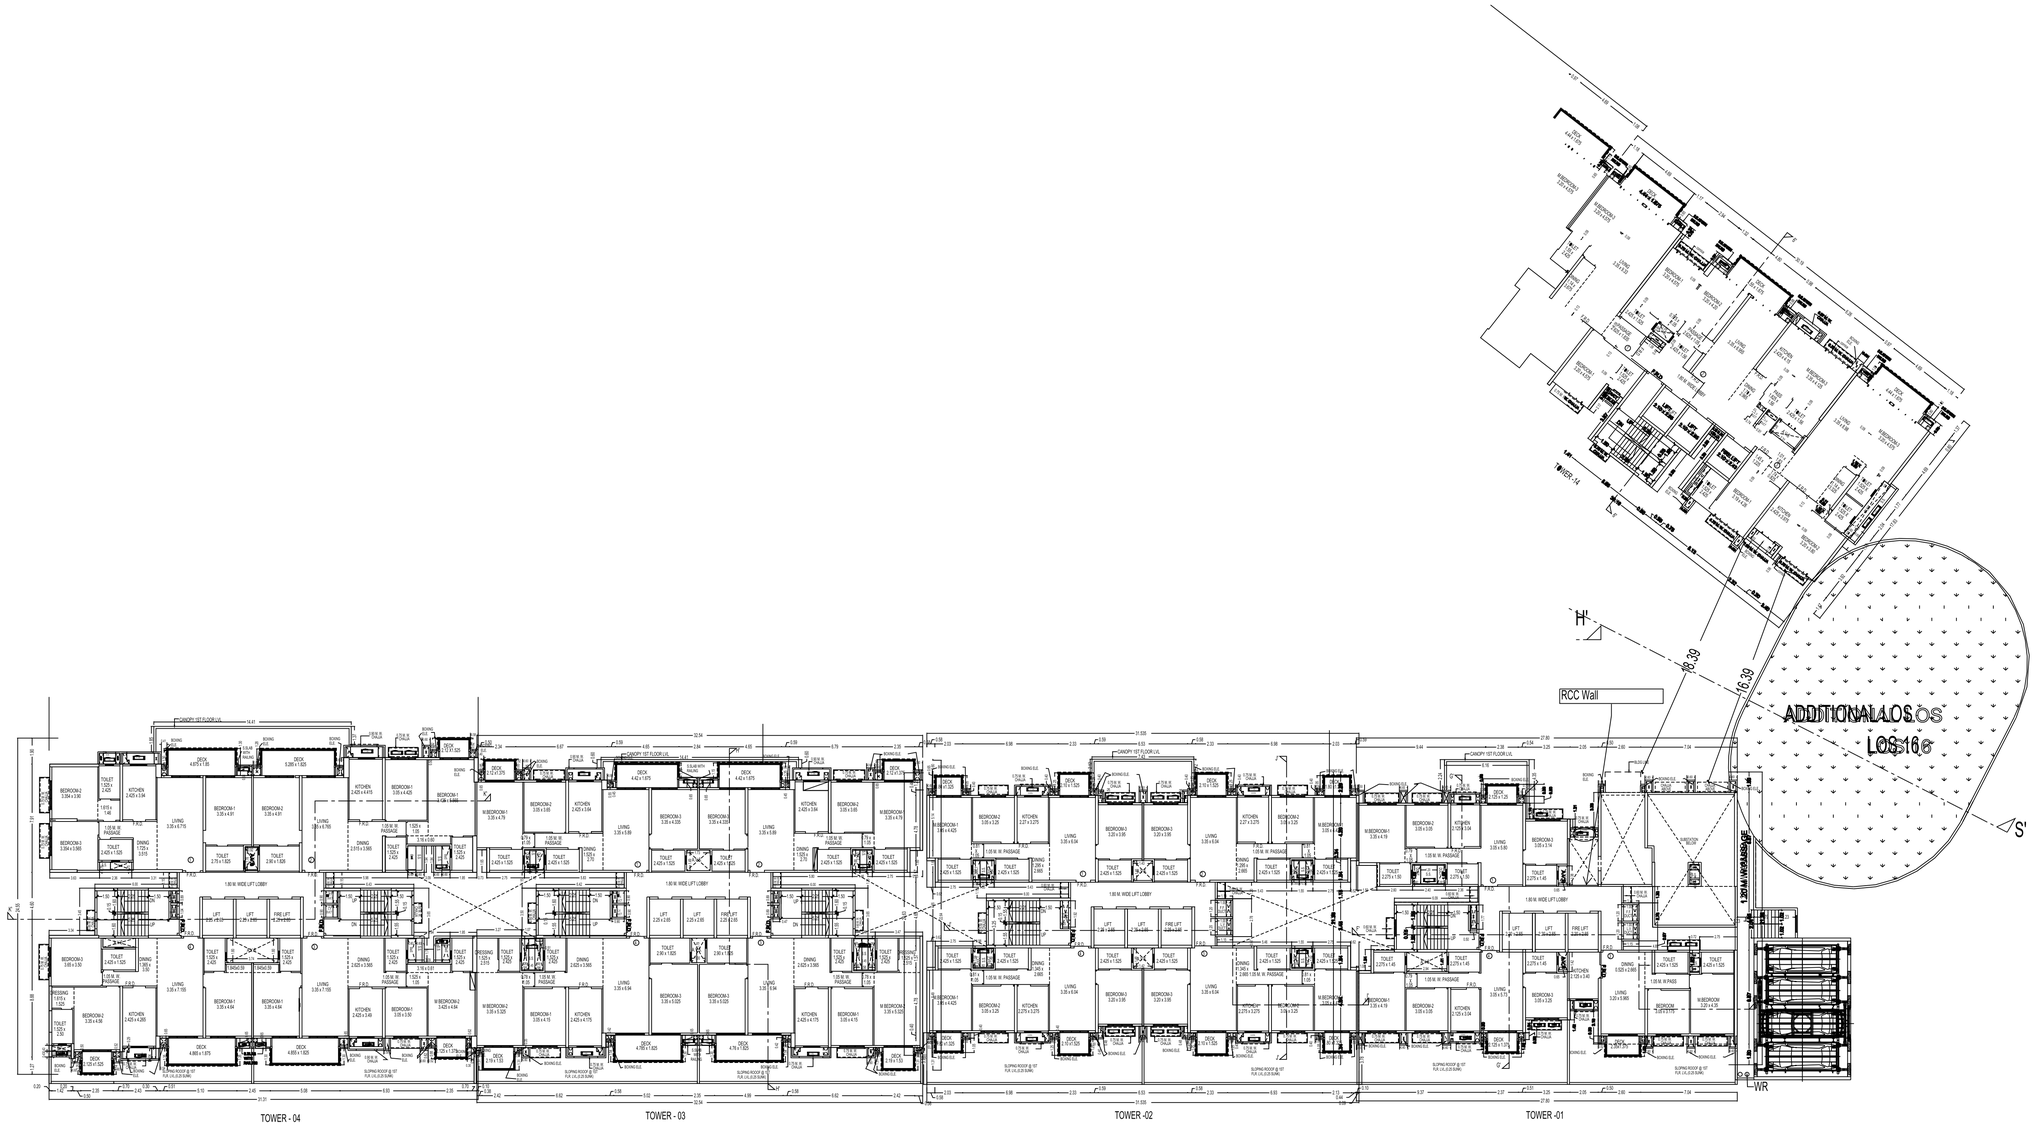

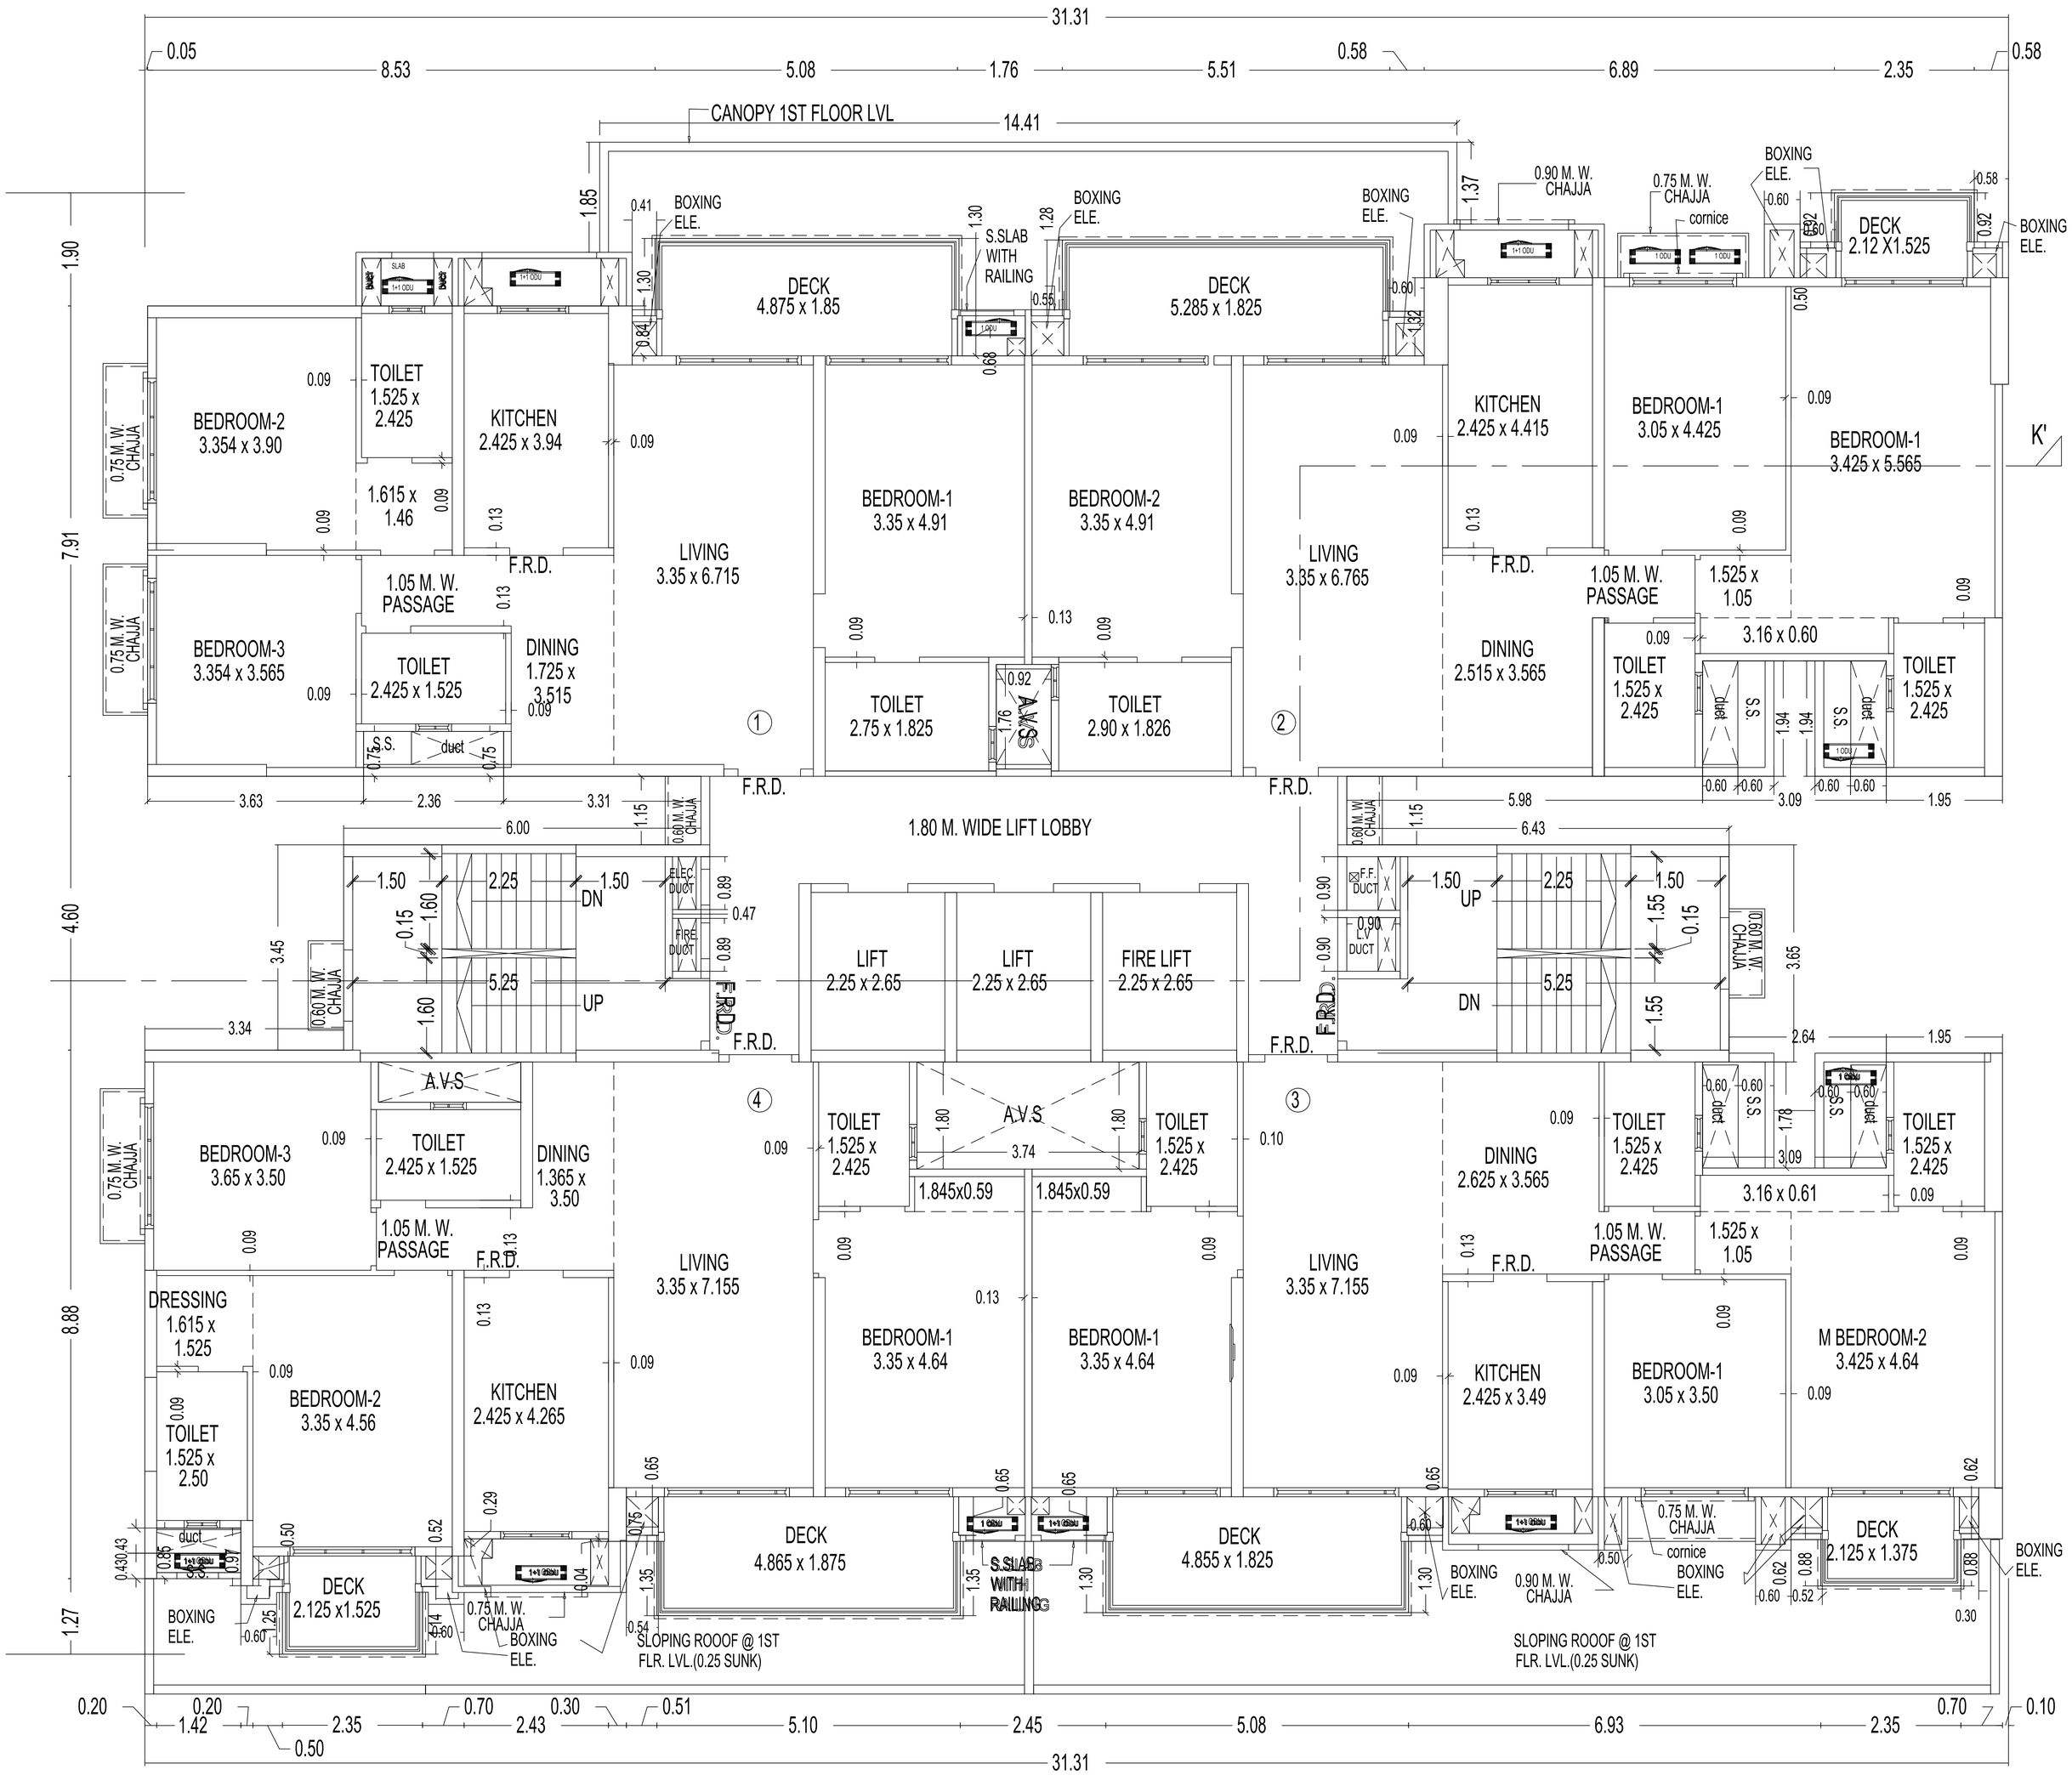


1ST FLOOR PLAN TOWER - 04


SCALE - 1:100

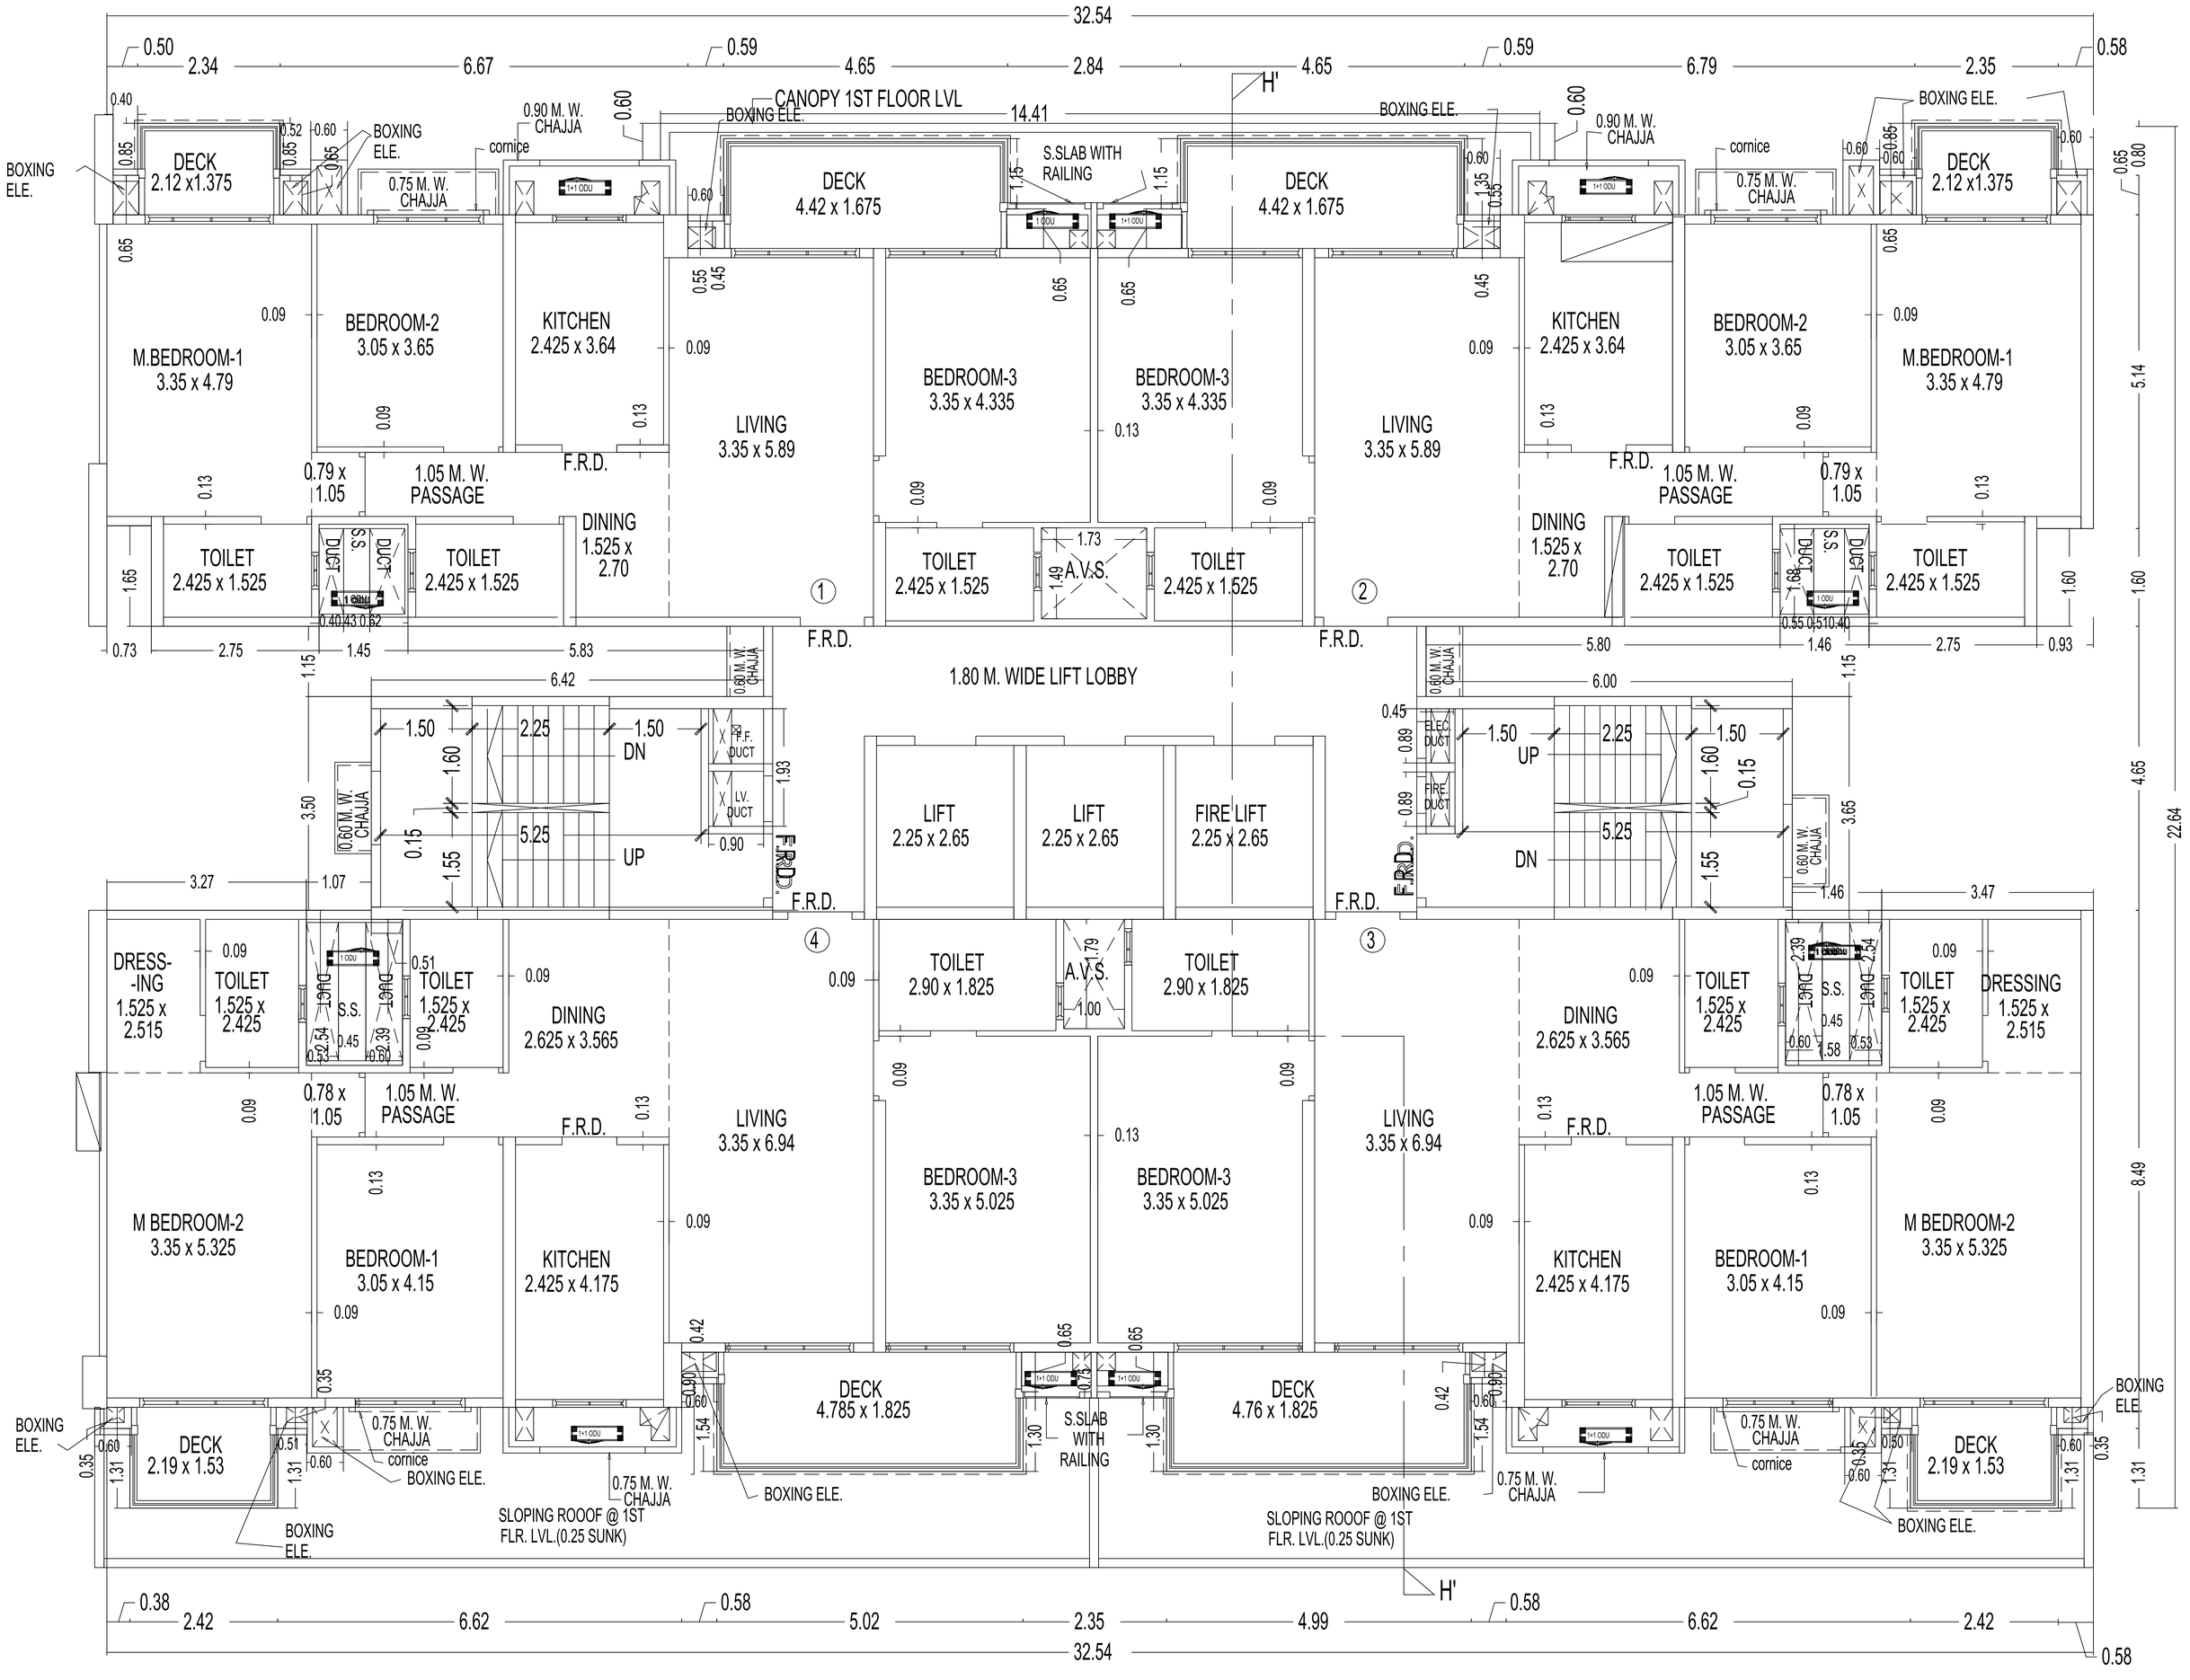

1ST FLOOR PLAN TOWER - 03

SCALE - 1:100

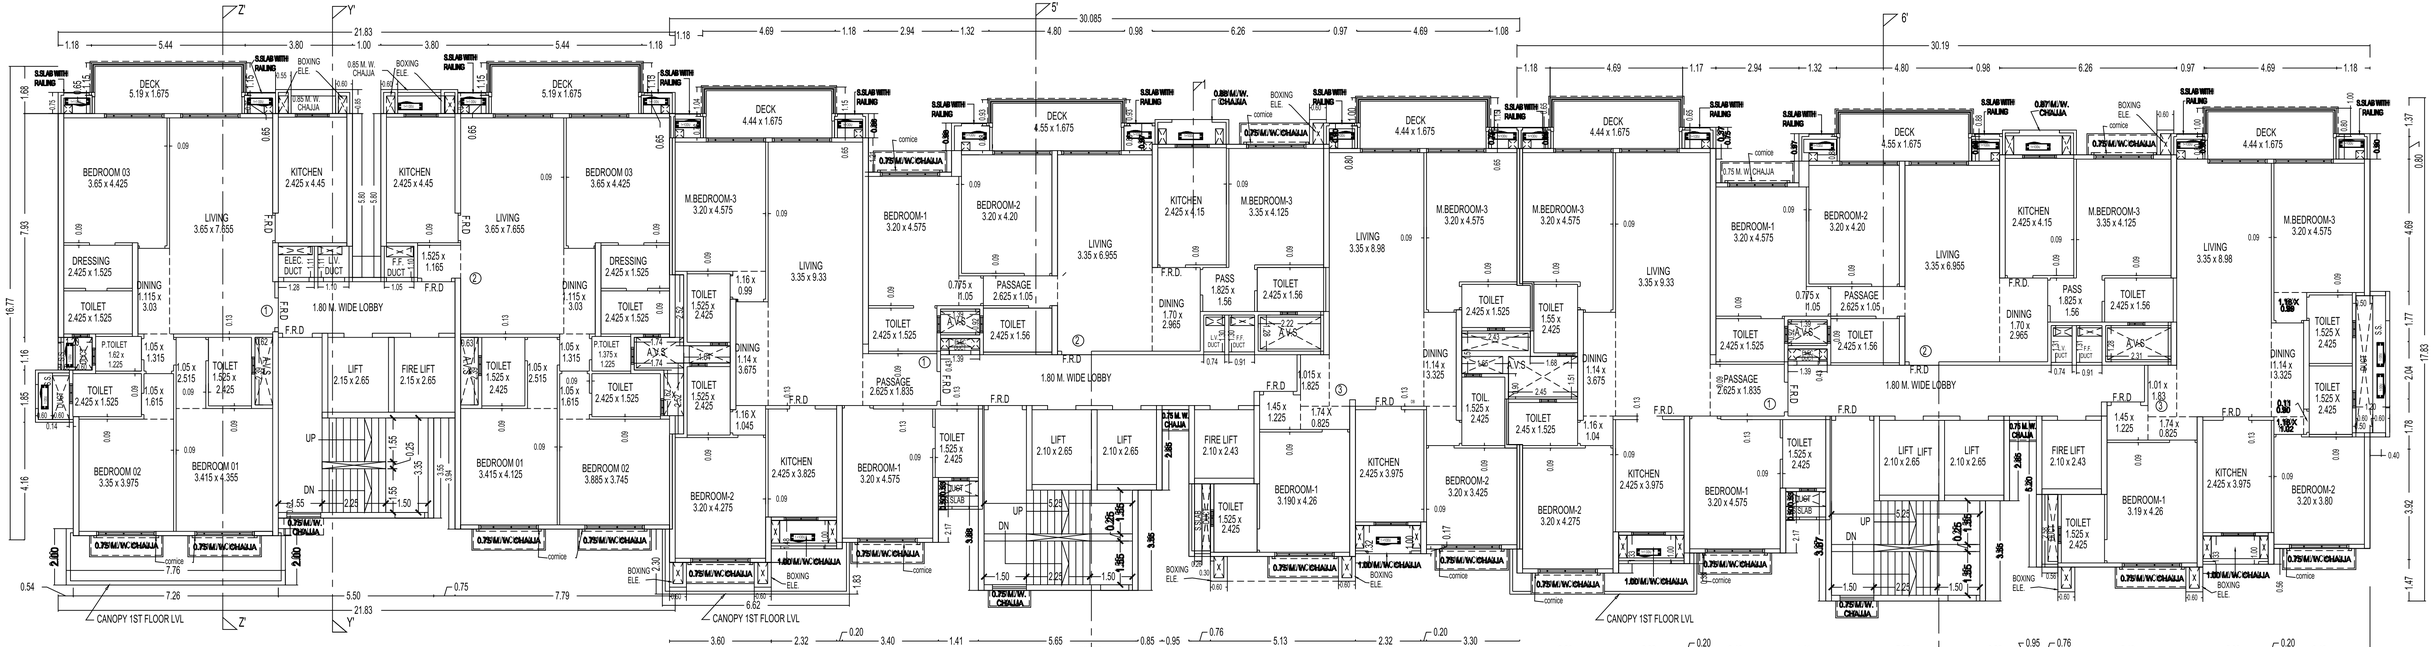
1ST FLOOR PLAN TOWER -12
SCALE - 1:100
1ST FLOOR PLAN TOWER -13
SCALE - 1:100
1ST FLOOR PLAN TOWER -14
SCALE - 1:100
1.80 M. WIDE LOBBY
CANOPY 1ST FLOOR LVL
F.R.D
S.SLAB WITH RAILING
BOXING ELE.
0.75 M. W. CHAJJA
0.85 M. W. CHAJJA
DECK 5.19 x 1.675
DECK 4.44 x 1.675
DECK 4.55 x 1.675
BEDROOM 03 3.65 x 4.425
LIVING 3.65 x 7.655
KITCHEN 2.425 x 4.45
DRESSING 2.425 x 1.525
TOILET 2.425 x 1.525
P.TOILET 1.62 x 1.225
BEDROOM 02 3.35 x 3.975
BEDROOM 01 3.415 x 4.355
BEDROOM 02 3.885 x 3.745
BEDROOM 01 3.415 x 4.125
LIFT 2.15 x 2.65
FIRE LIFT 2.15 x 2.65
M.BEDROOM-3 3.20 x 4.575
LIVING 3.35 x 9.33
BEDROOM-2 3.20 x 4.275
KITCHEN 2.425 x 3.825
BEDROOM-1 3.20 x 4.575
BEDROOM-2 3.20 x 4.20
LIVING 3.35 x 6.955
PASSAGE 2.625 x 1.835
LIFT 2.10 x 2.65
FIRE LIFT 2.10 x 2.43
BEDROOM-1 3.190 x 4.26
KITCHEN 2.425 x 4.15
M.BEDROOM-3 3.35 x 4.125
LIVING 3.35 x 8.98
KITCHEN 2.425 x 3.975
BEDROOM-2 3.20 x 3.425
BEDROOM-2 3.20 x 4.275
BEDROOM-1 3.20 x 4.575
M.BEDROOM-3 3.20 x 4.575
LIVING 3.35 x 9.33
LIFT LIFT 2.10 x 2.65
LIFT 2.10 x 2.65
BEDROOM-1 3.19 x 4.26
BEDROOM-2 3.20 x 3.80

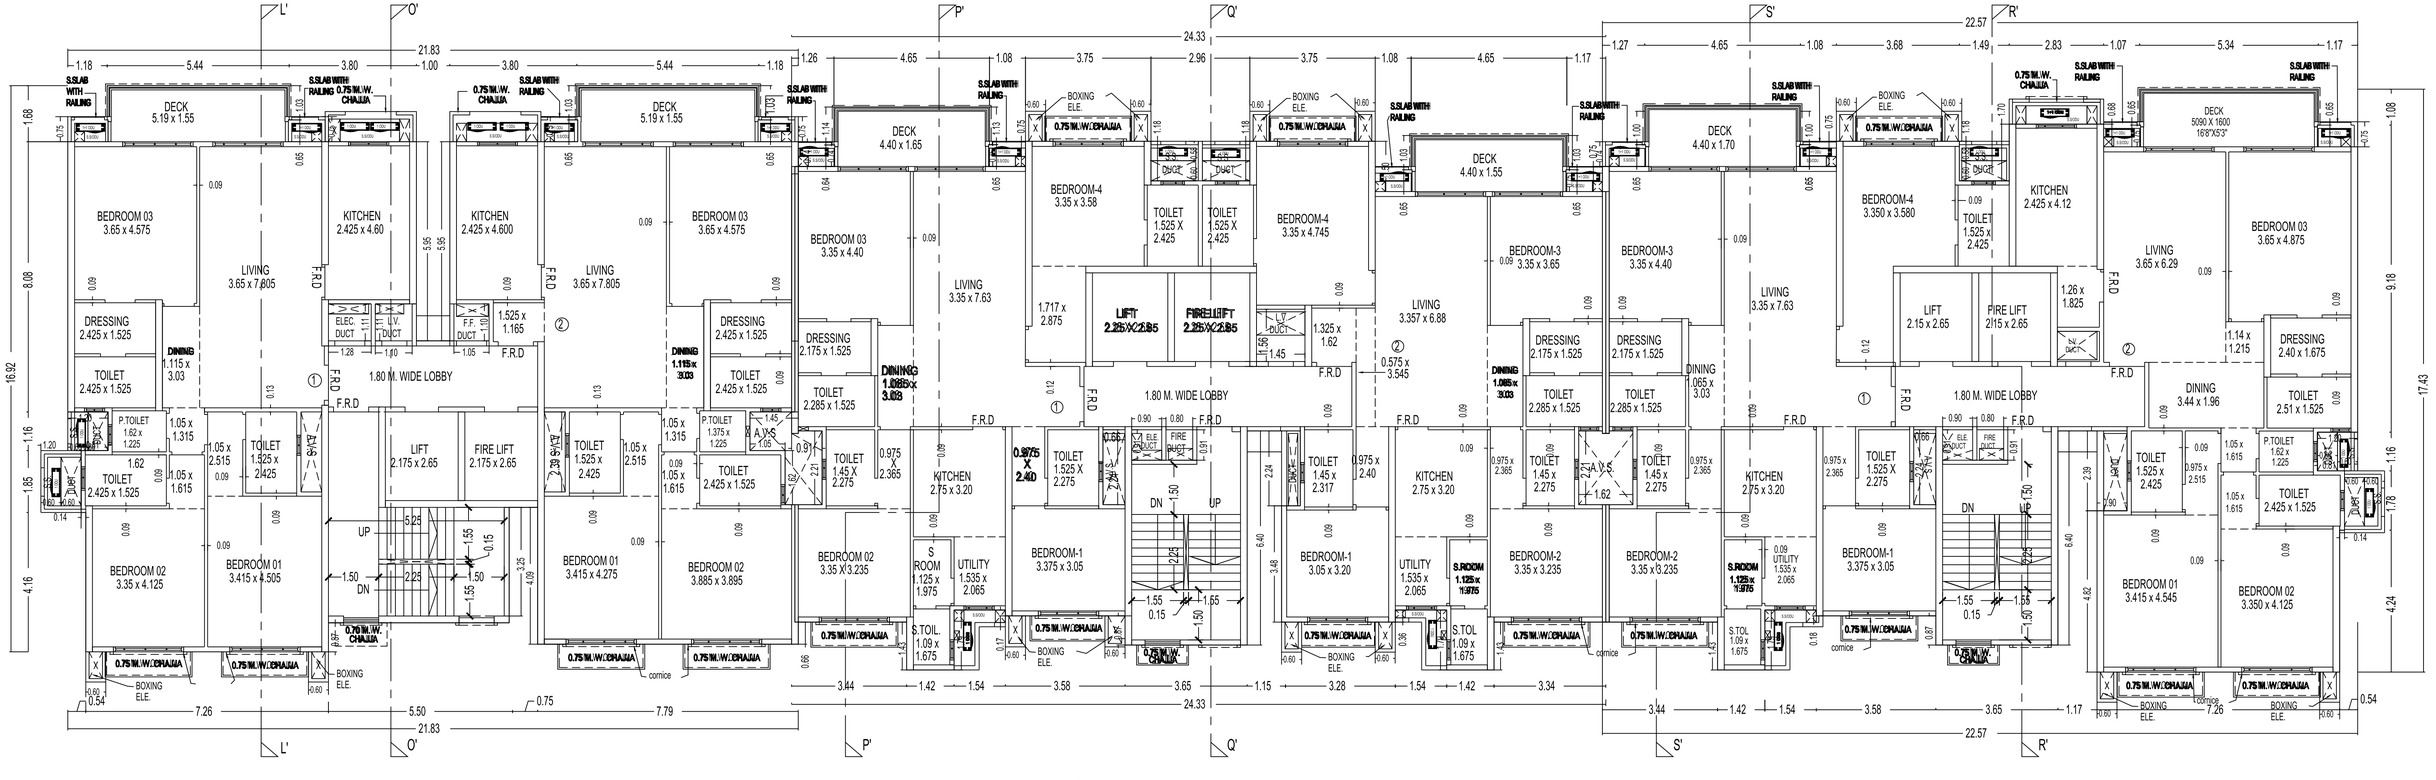

1ST FLOOR PLAN TOWER -06

SCALE - 1:100


1ST FLOOR PLAN TOWER -07

SCALE - 1:100

1ST FLOOR PLAN TOWER -08


SCALE - 1:100

SCALE - 1:100

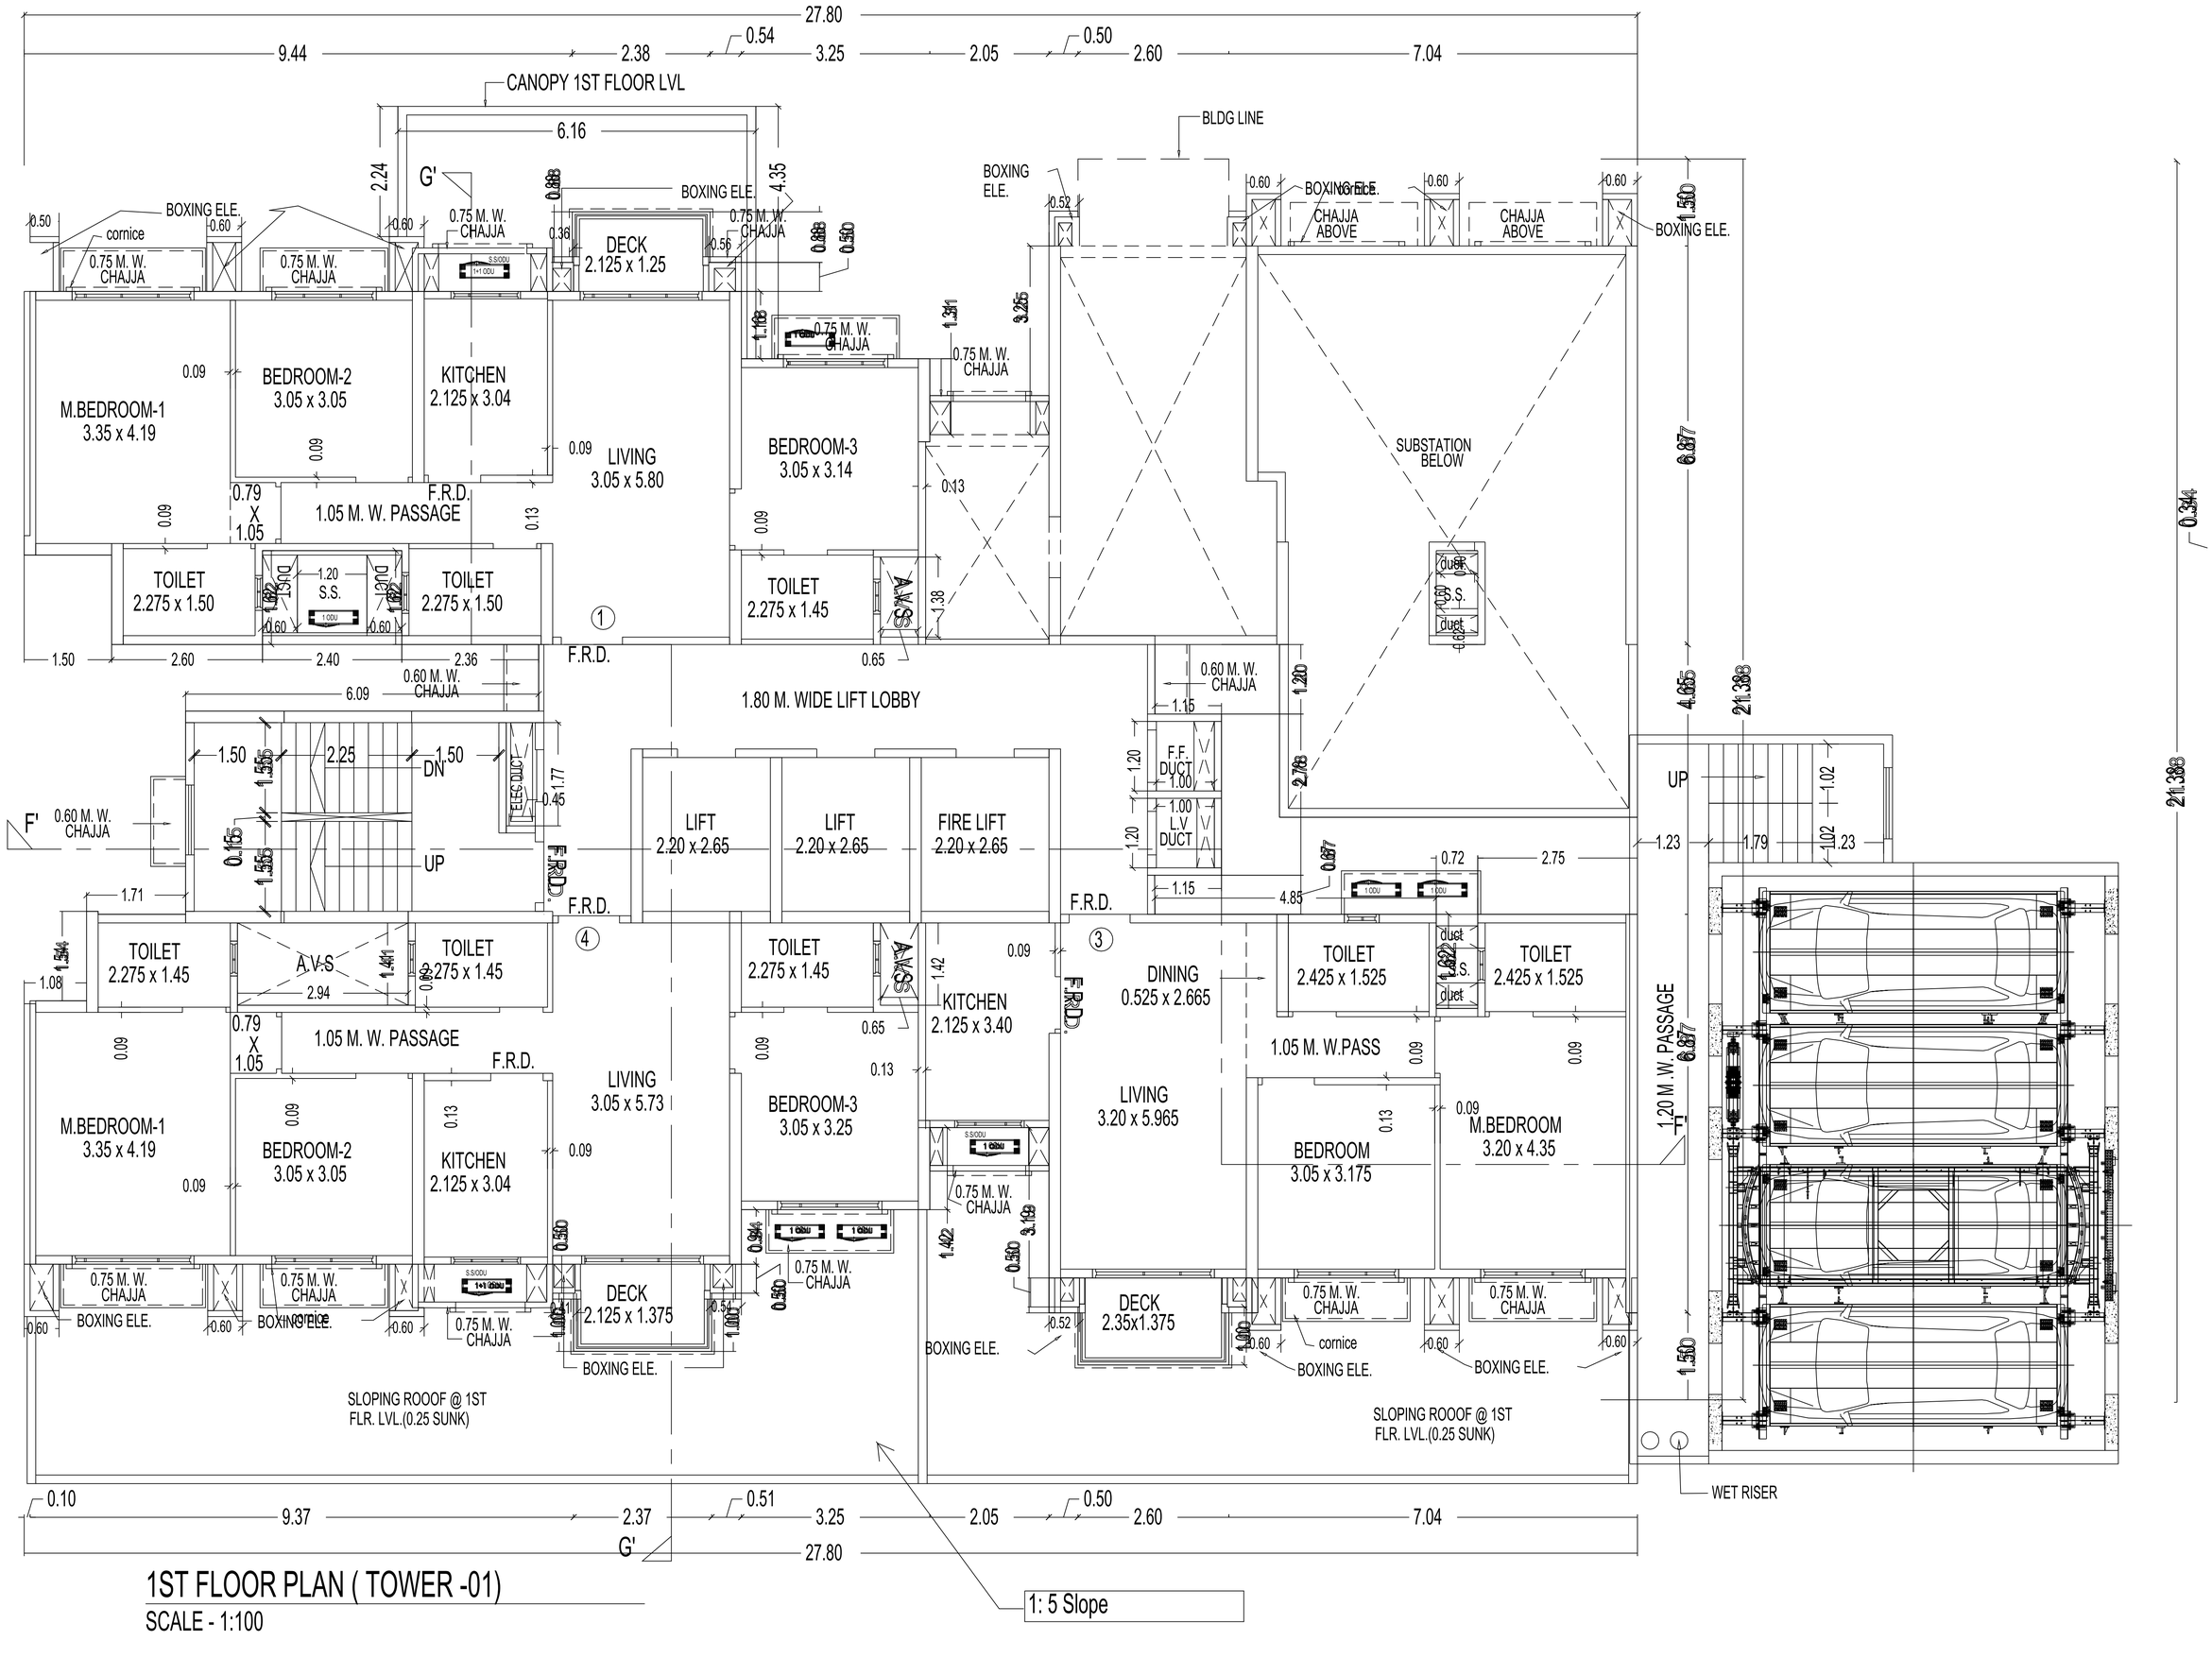

1ST FLOOR PLAN (TOWER -01)


SCALE - 1:100

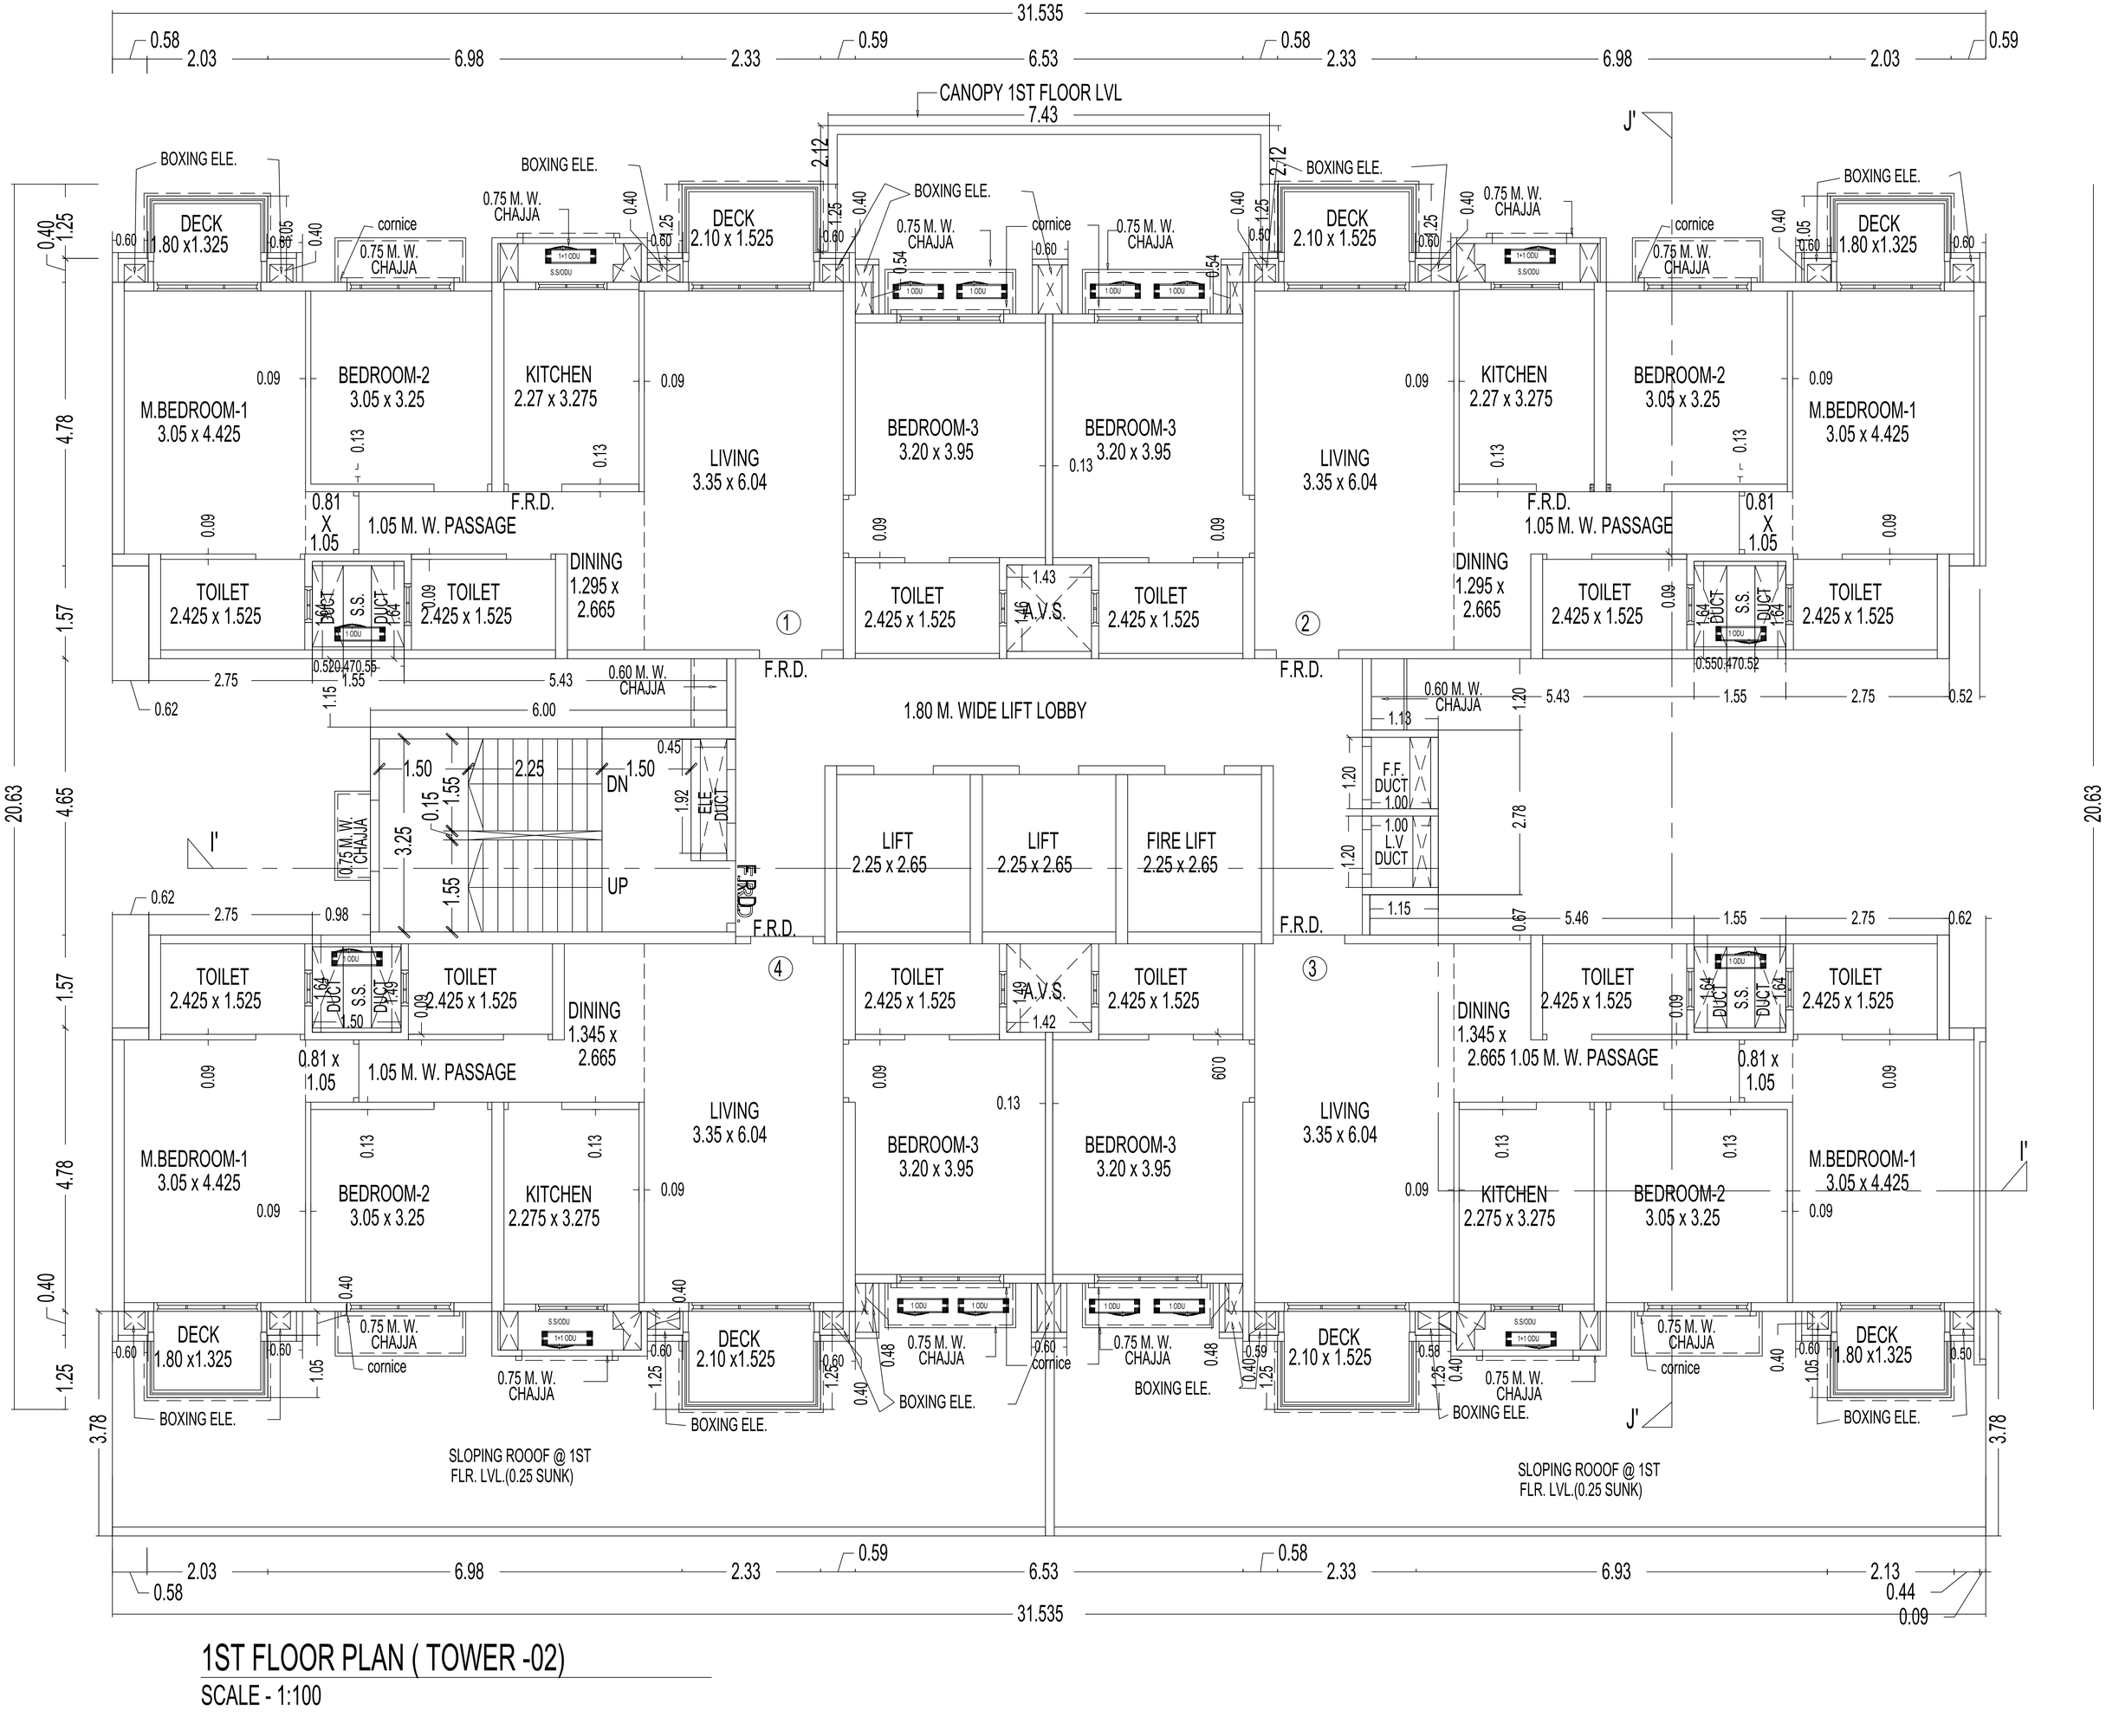

1ST FLOOR PLAN (TOWER -02)


SCALE - 1:100

SCALE - 1:100

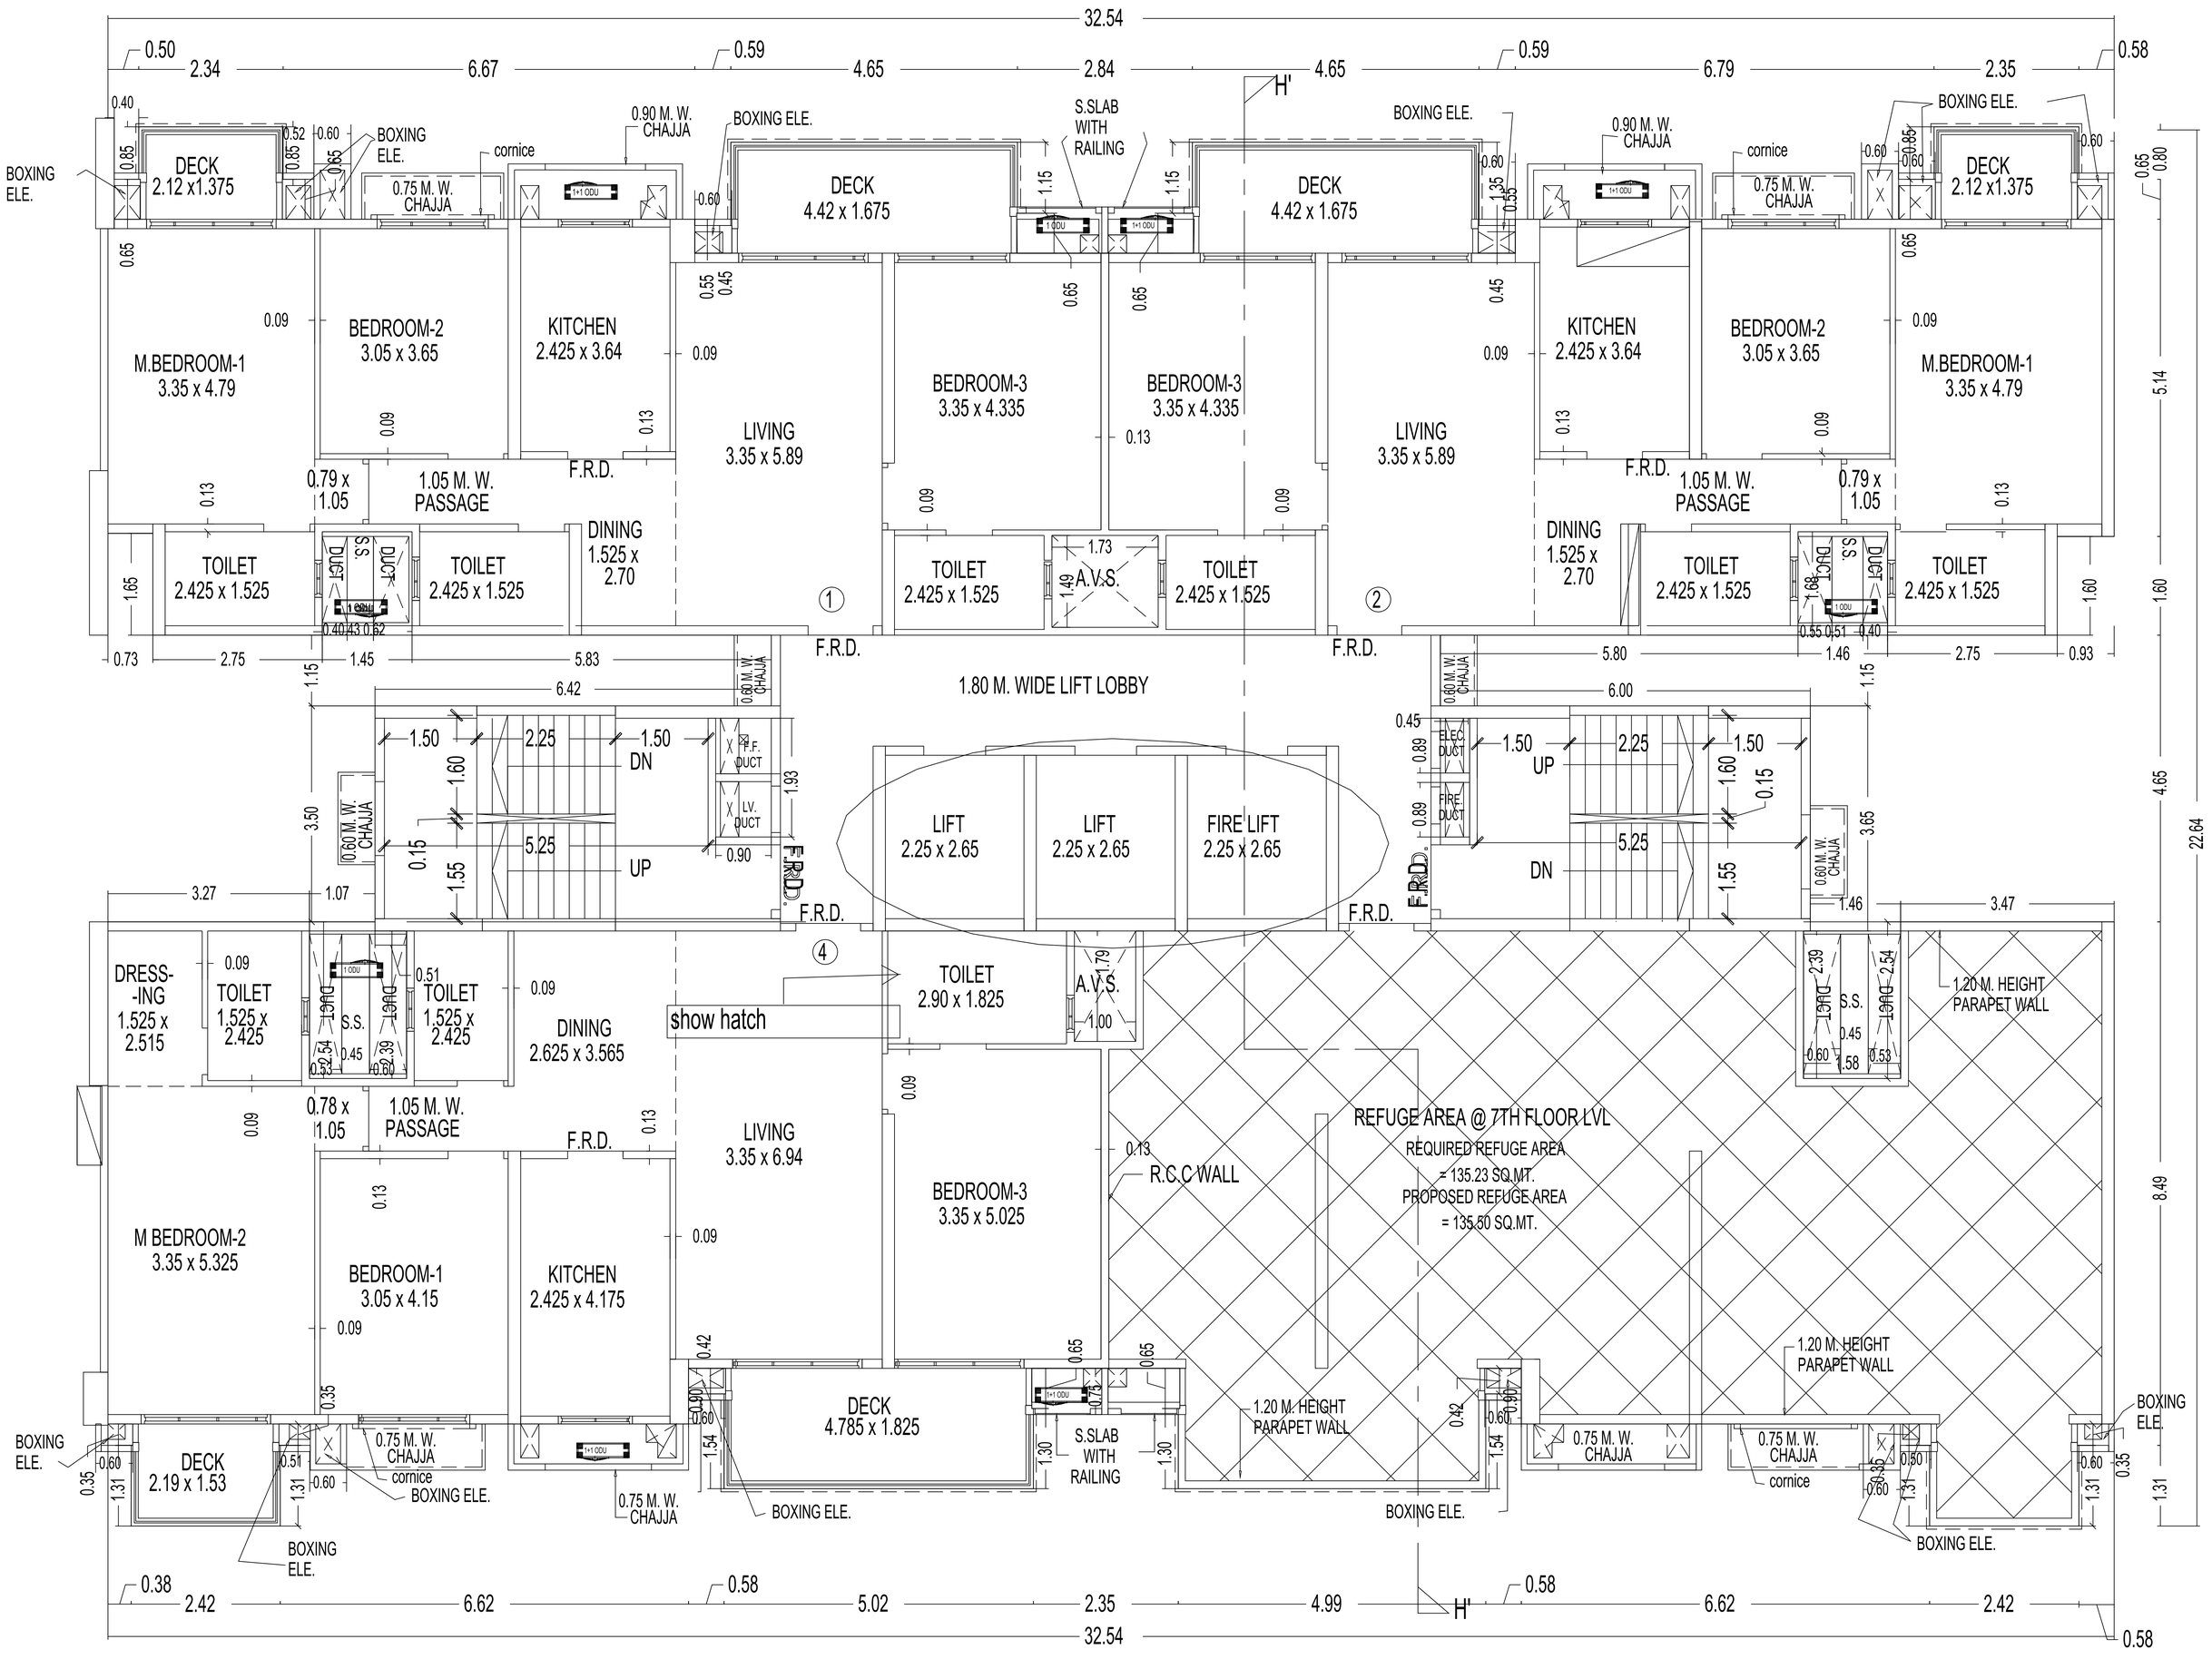


7TH REFUGE FLOOR PLAN (TOWER-03)

SCALE - 1:100

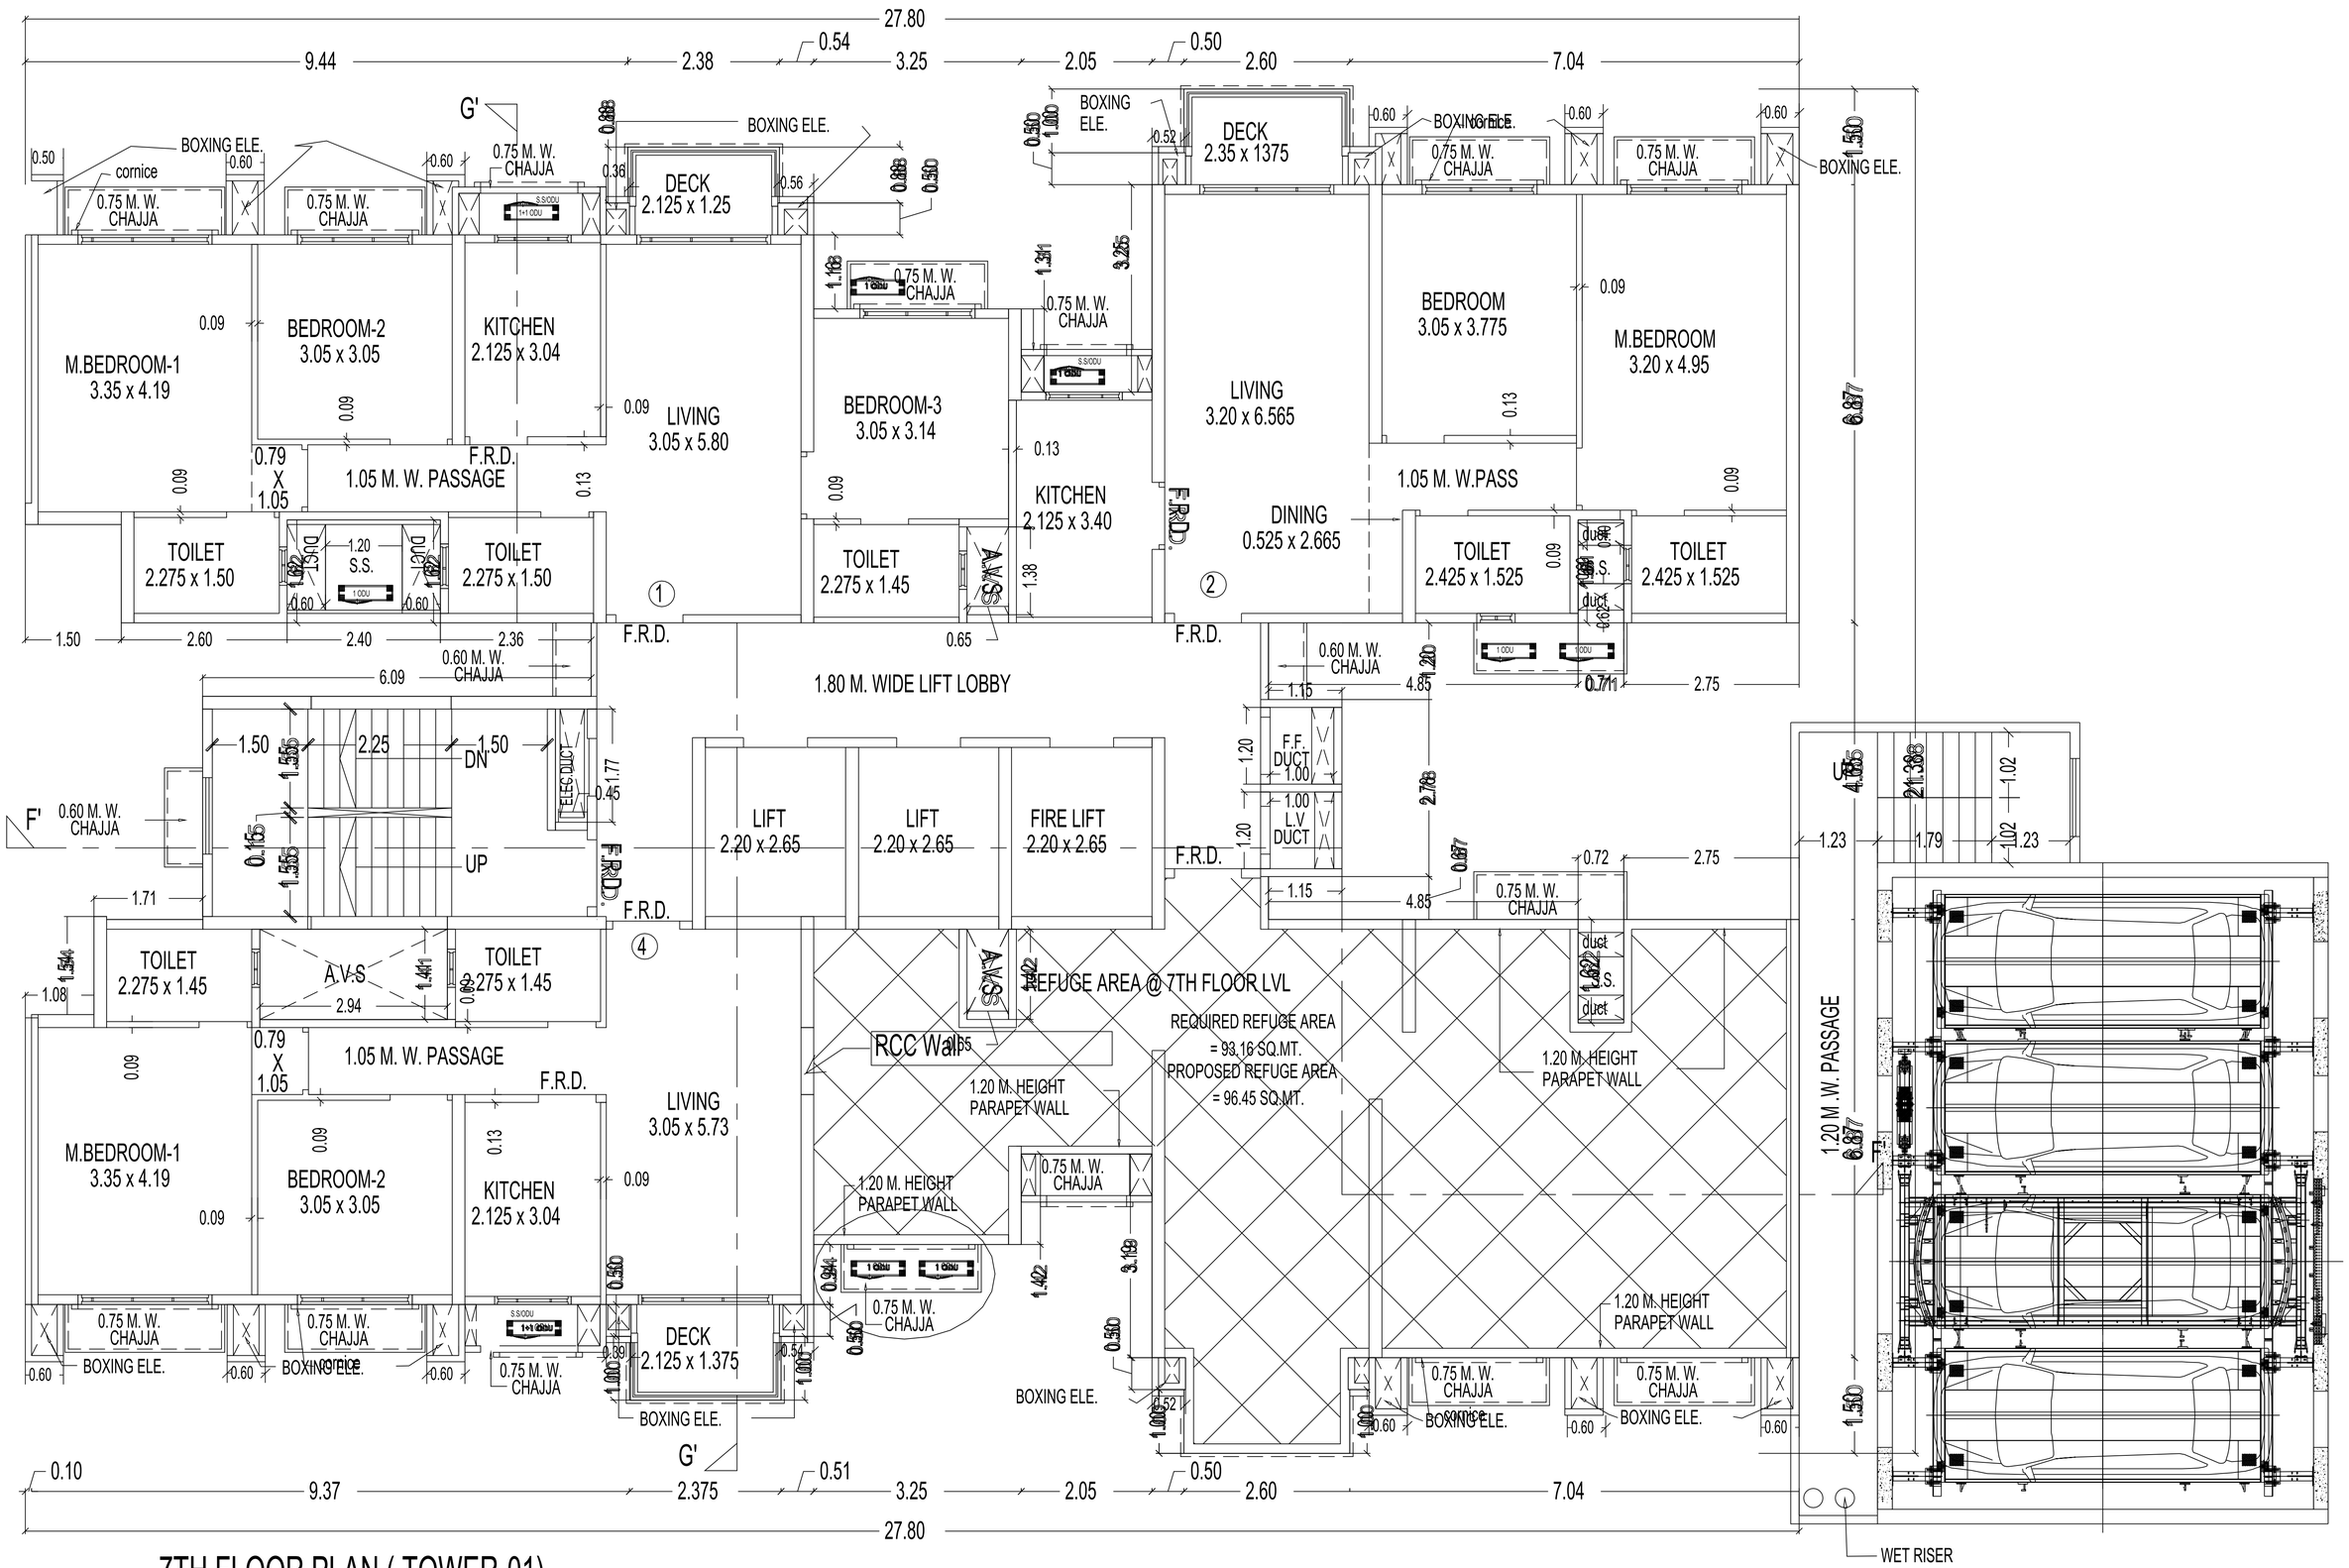


7TH FLOOR PLAN (TOWER-01)

SCALE - 1:100

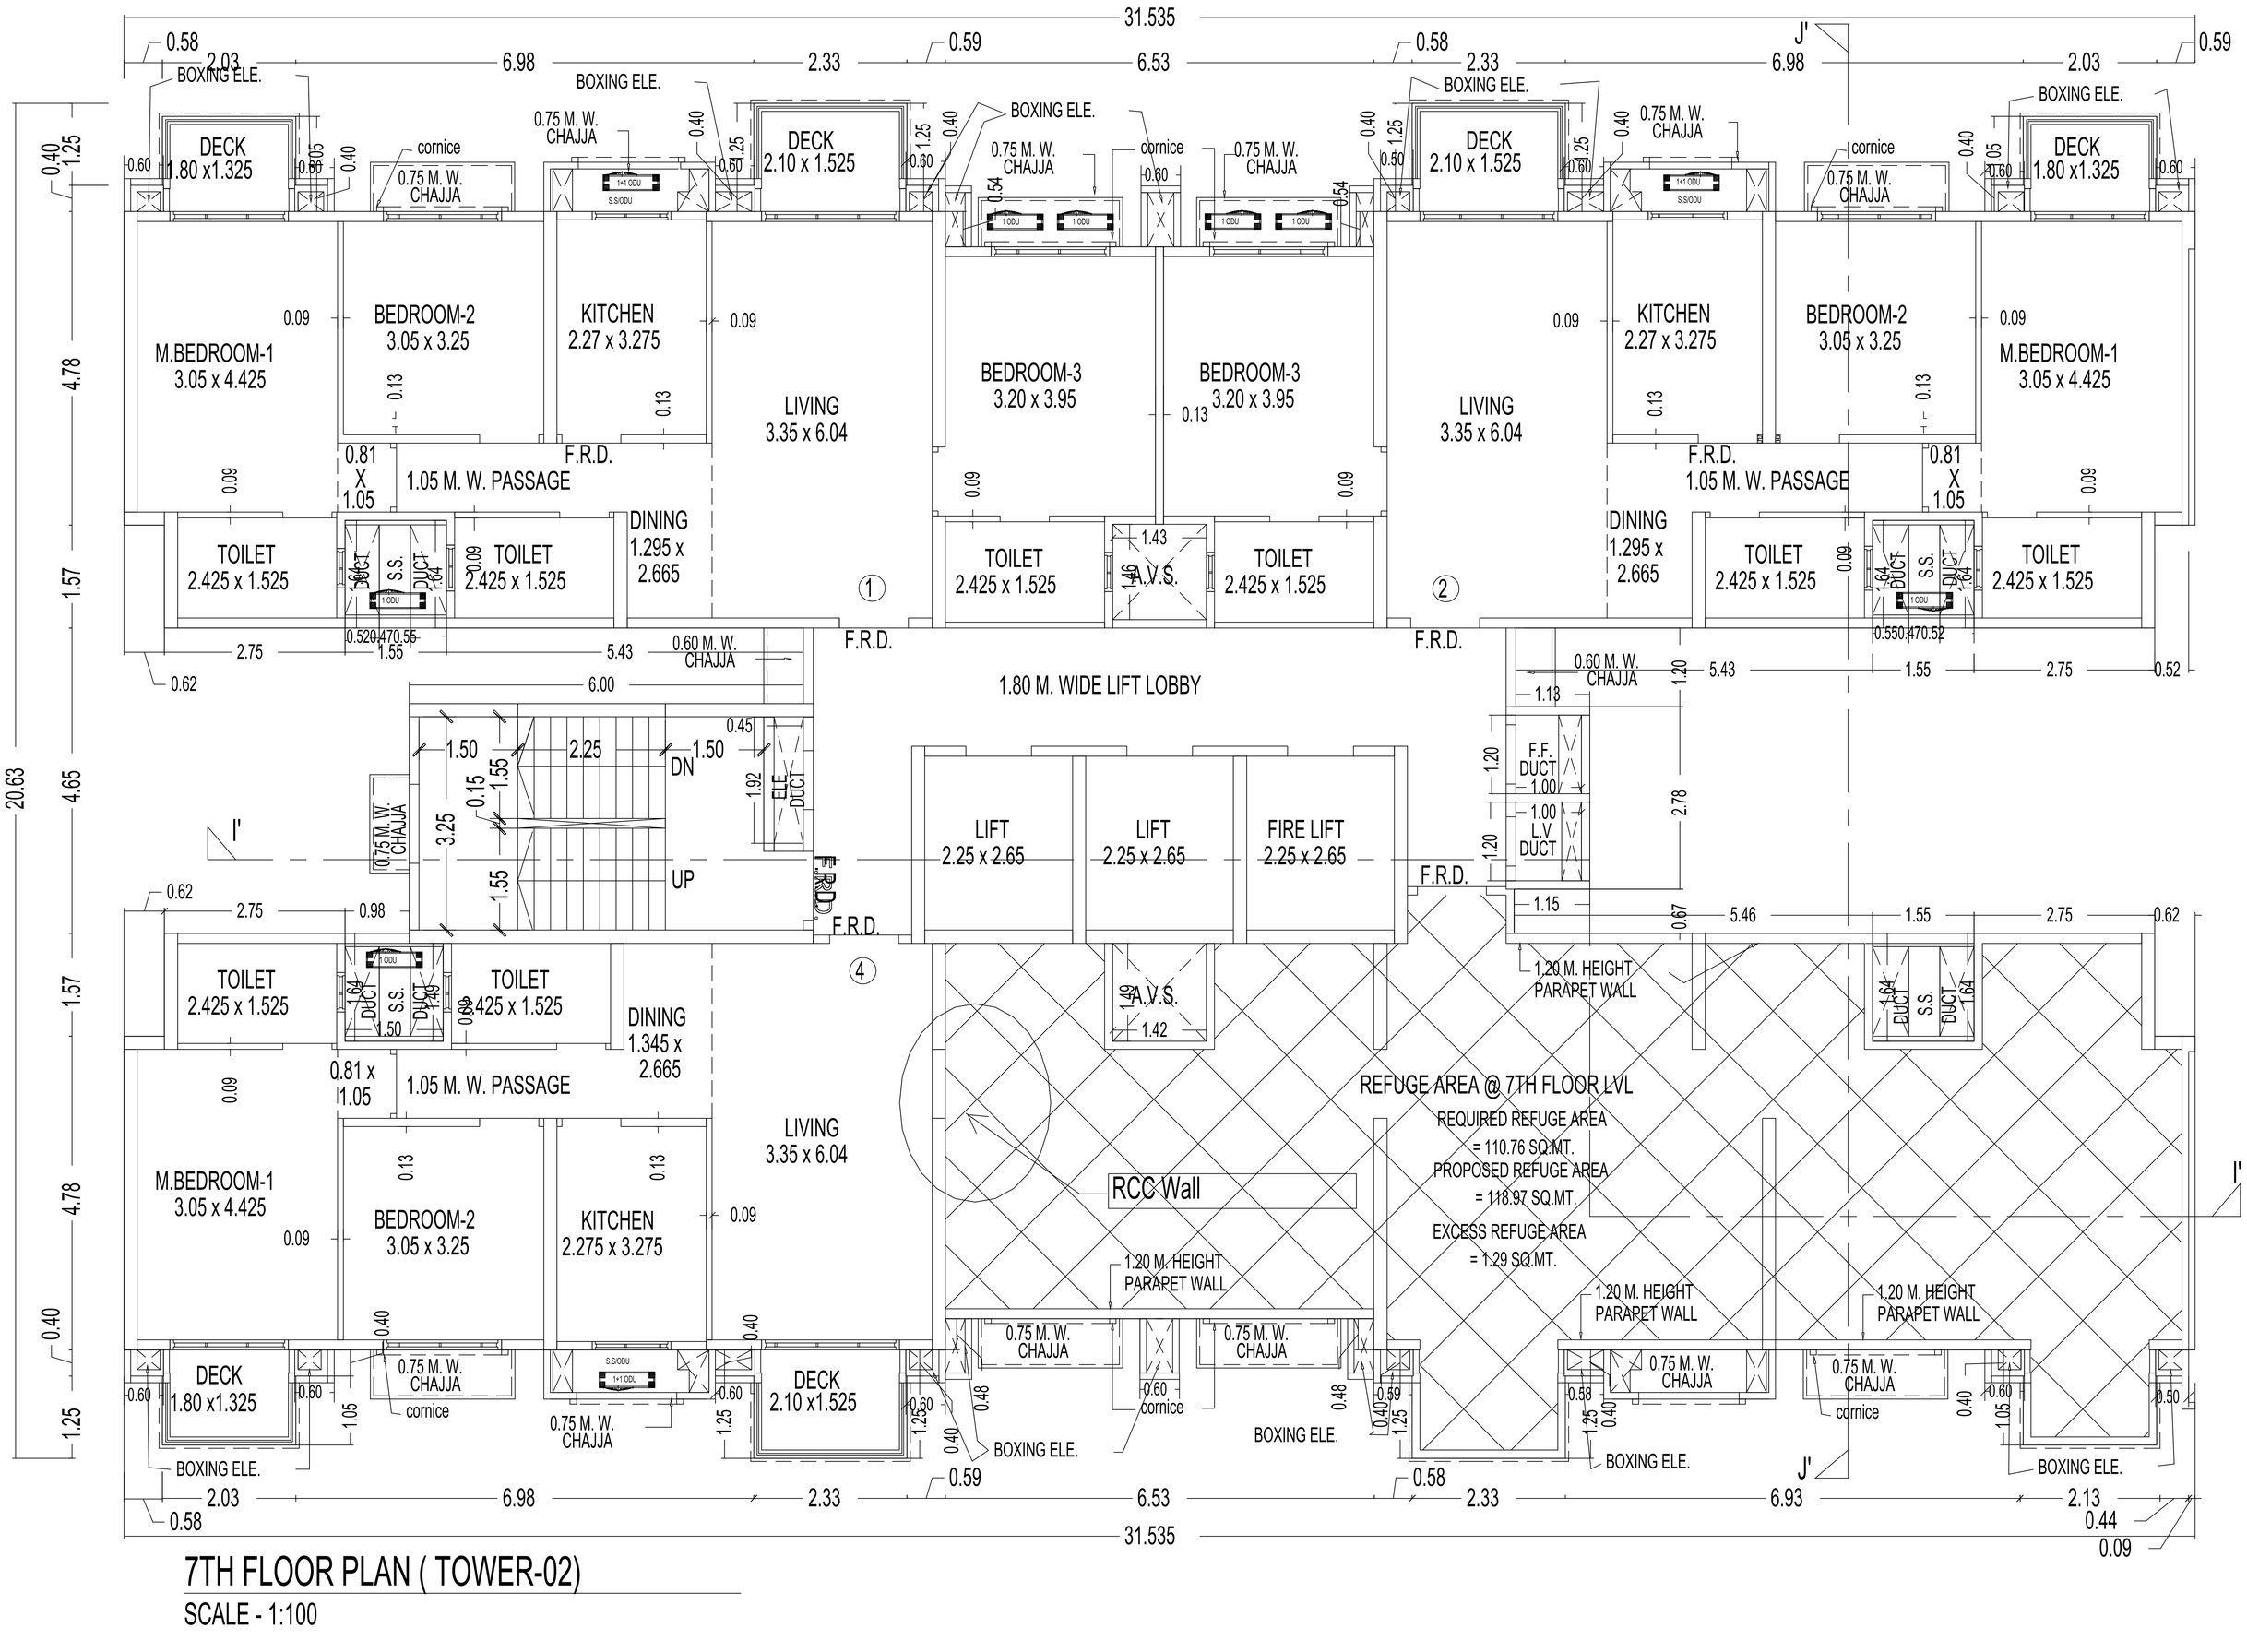


7TH FLOOR PLAN (TOWER-02)

SCALE - 1:100

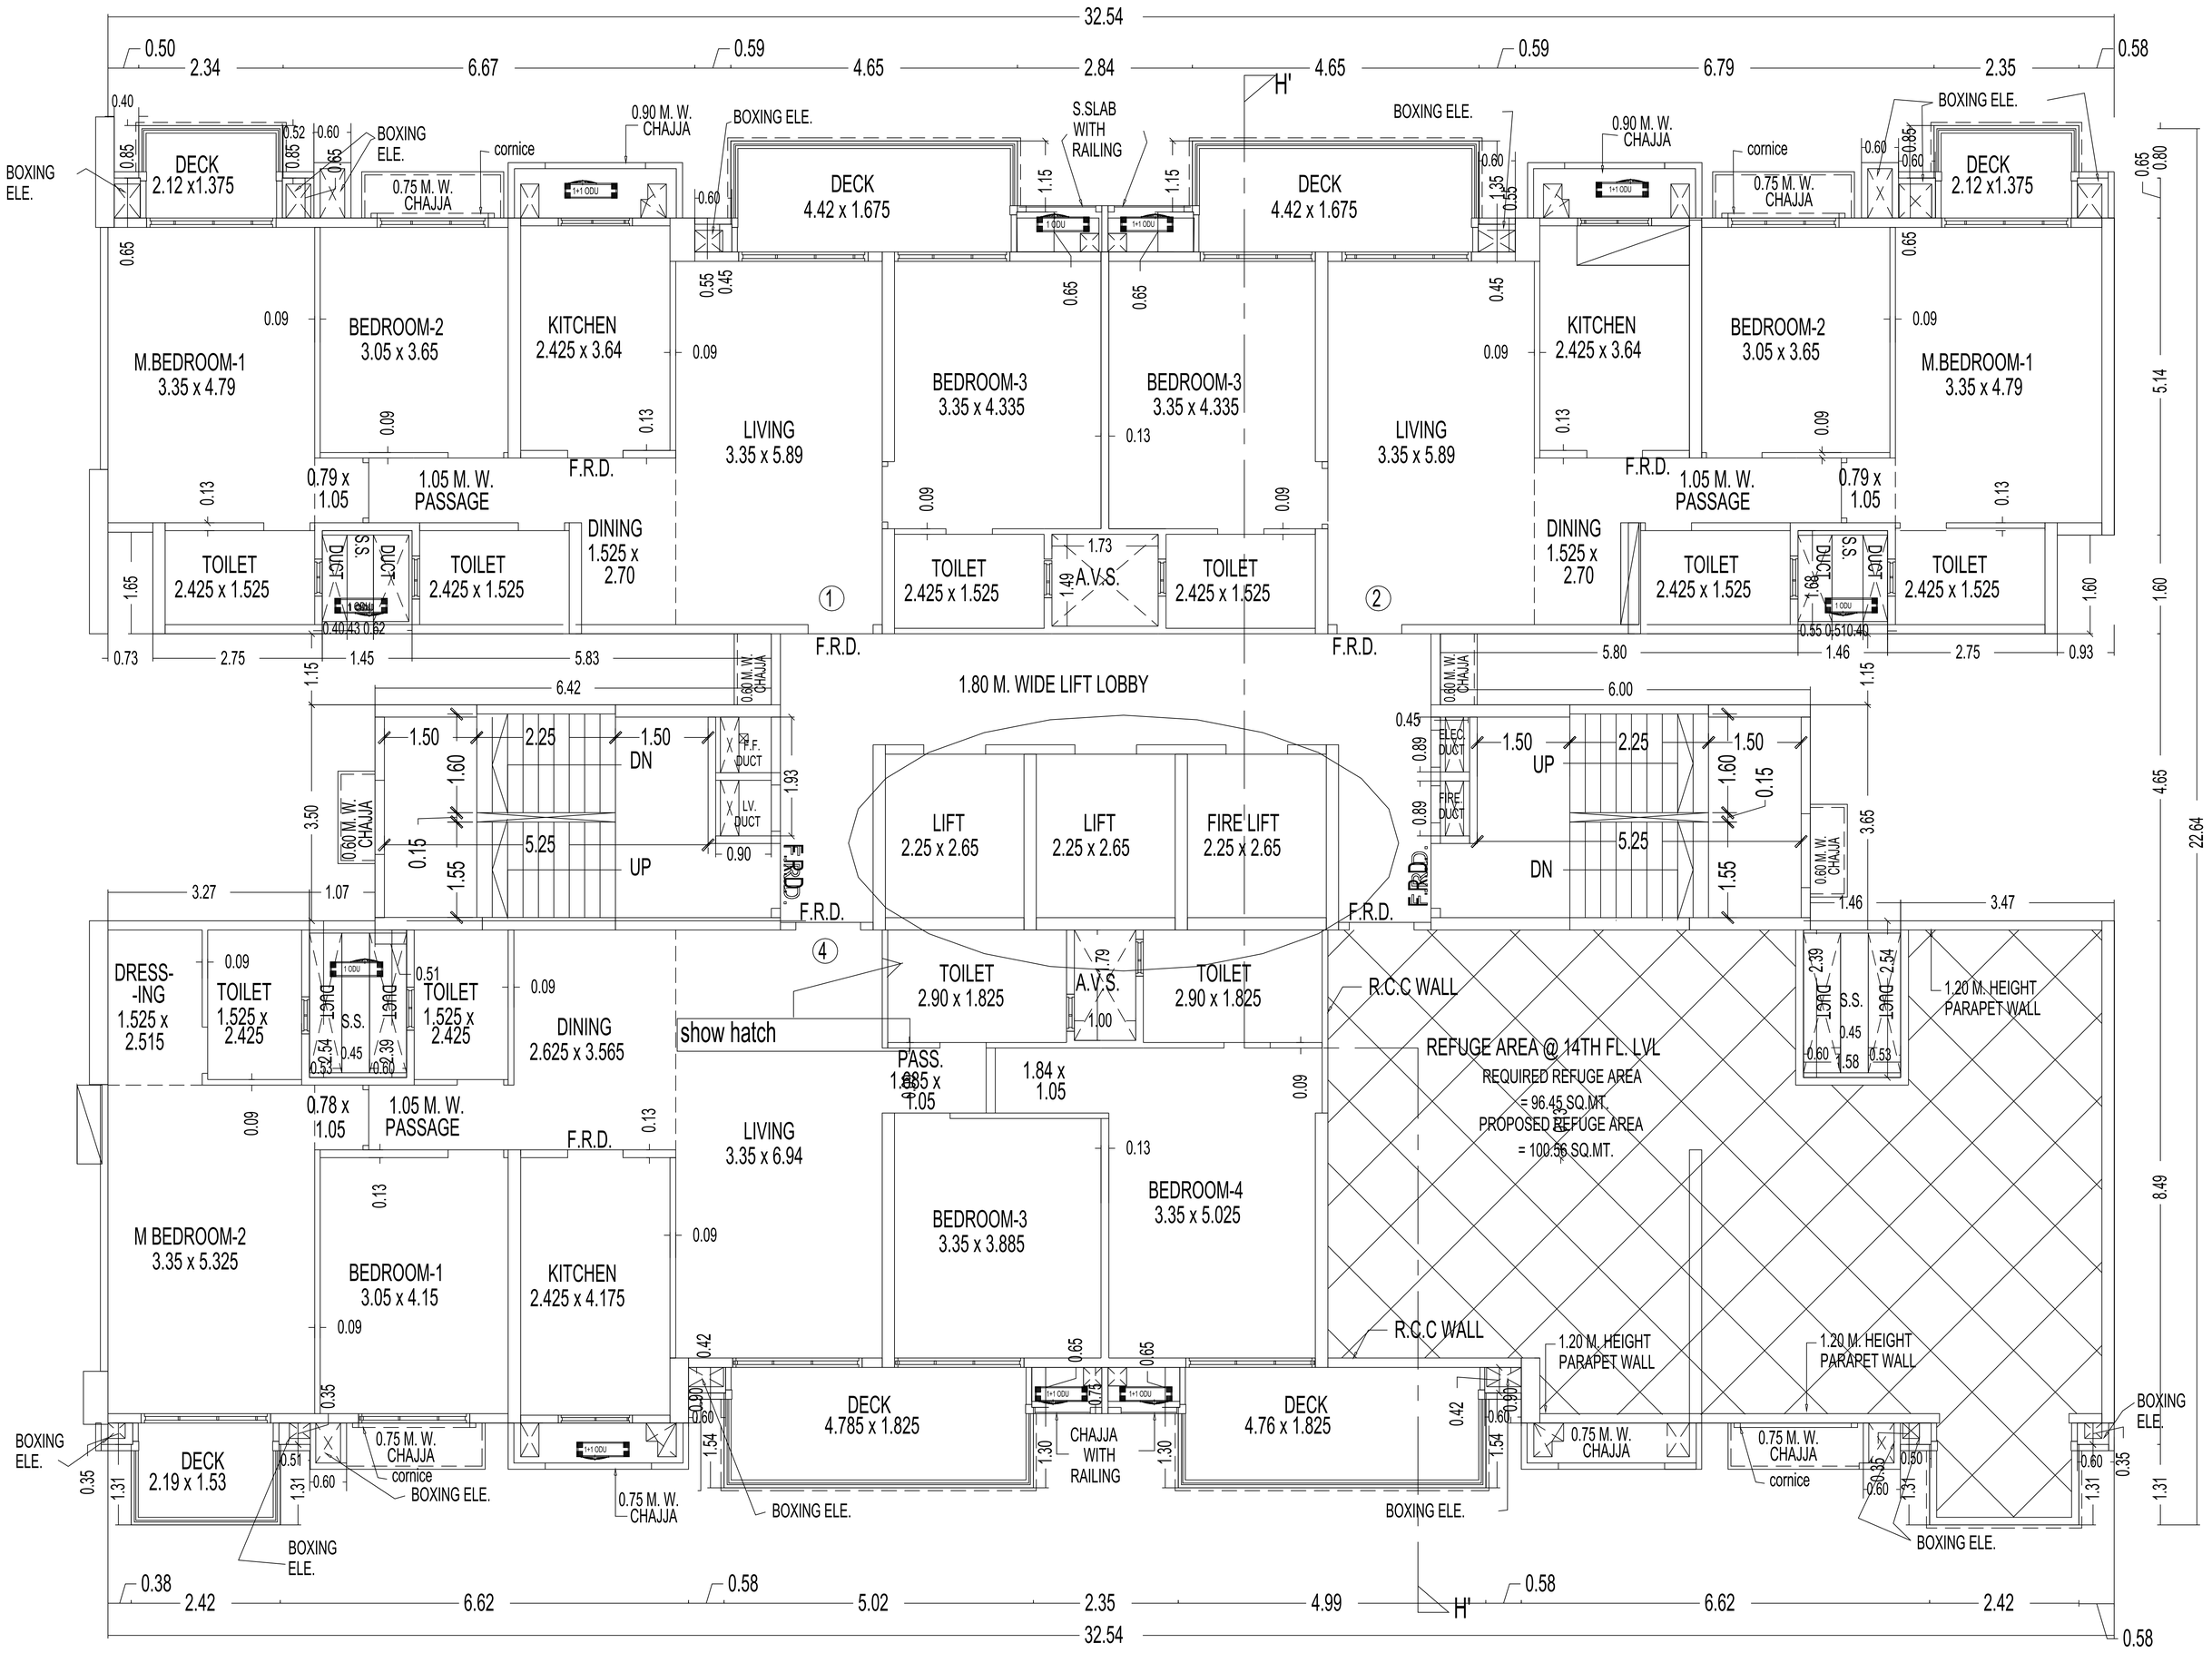

14TH REFUGE FLOOR PLAN (TOWER-03)


SCALE - 1:100

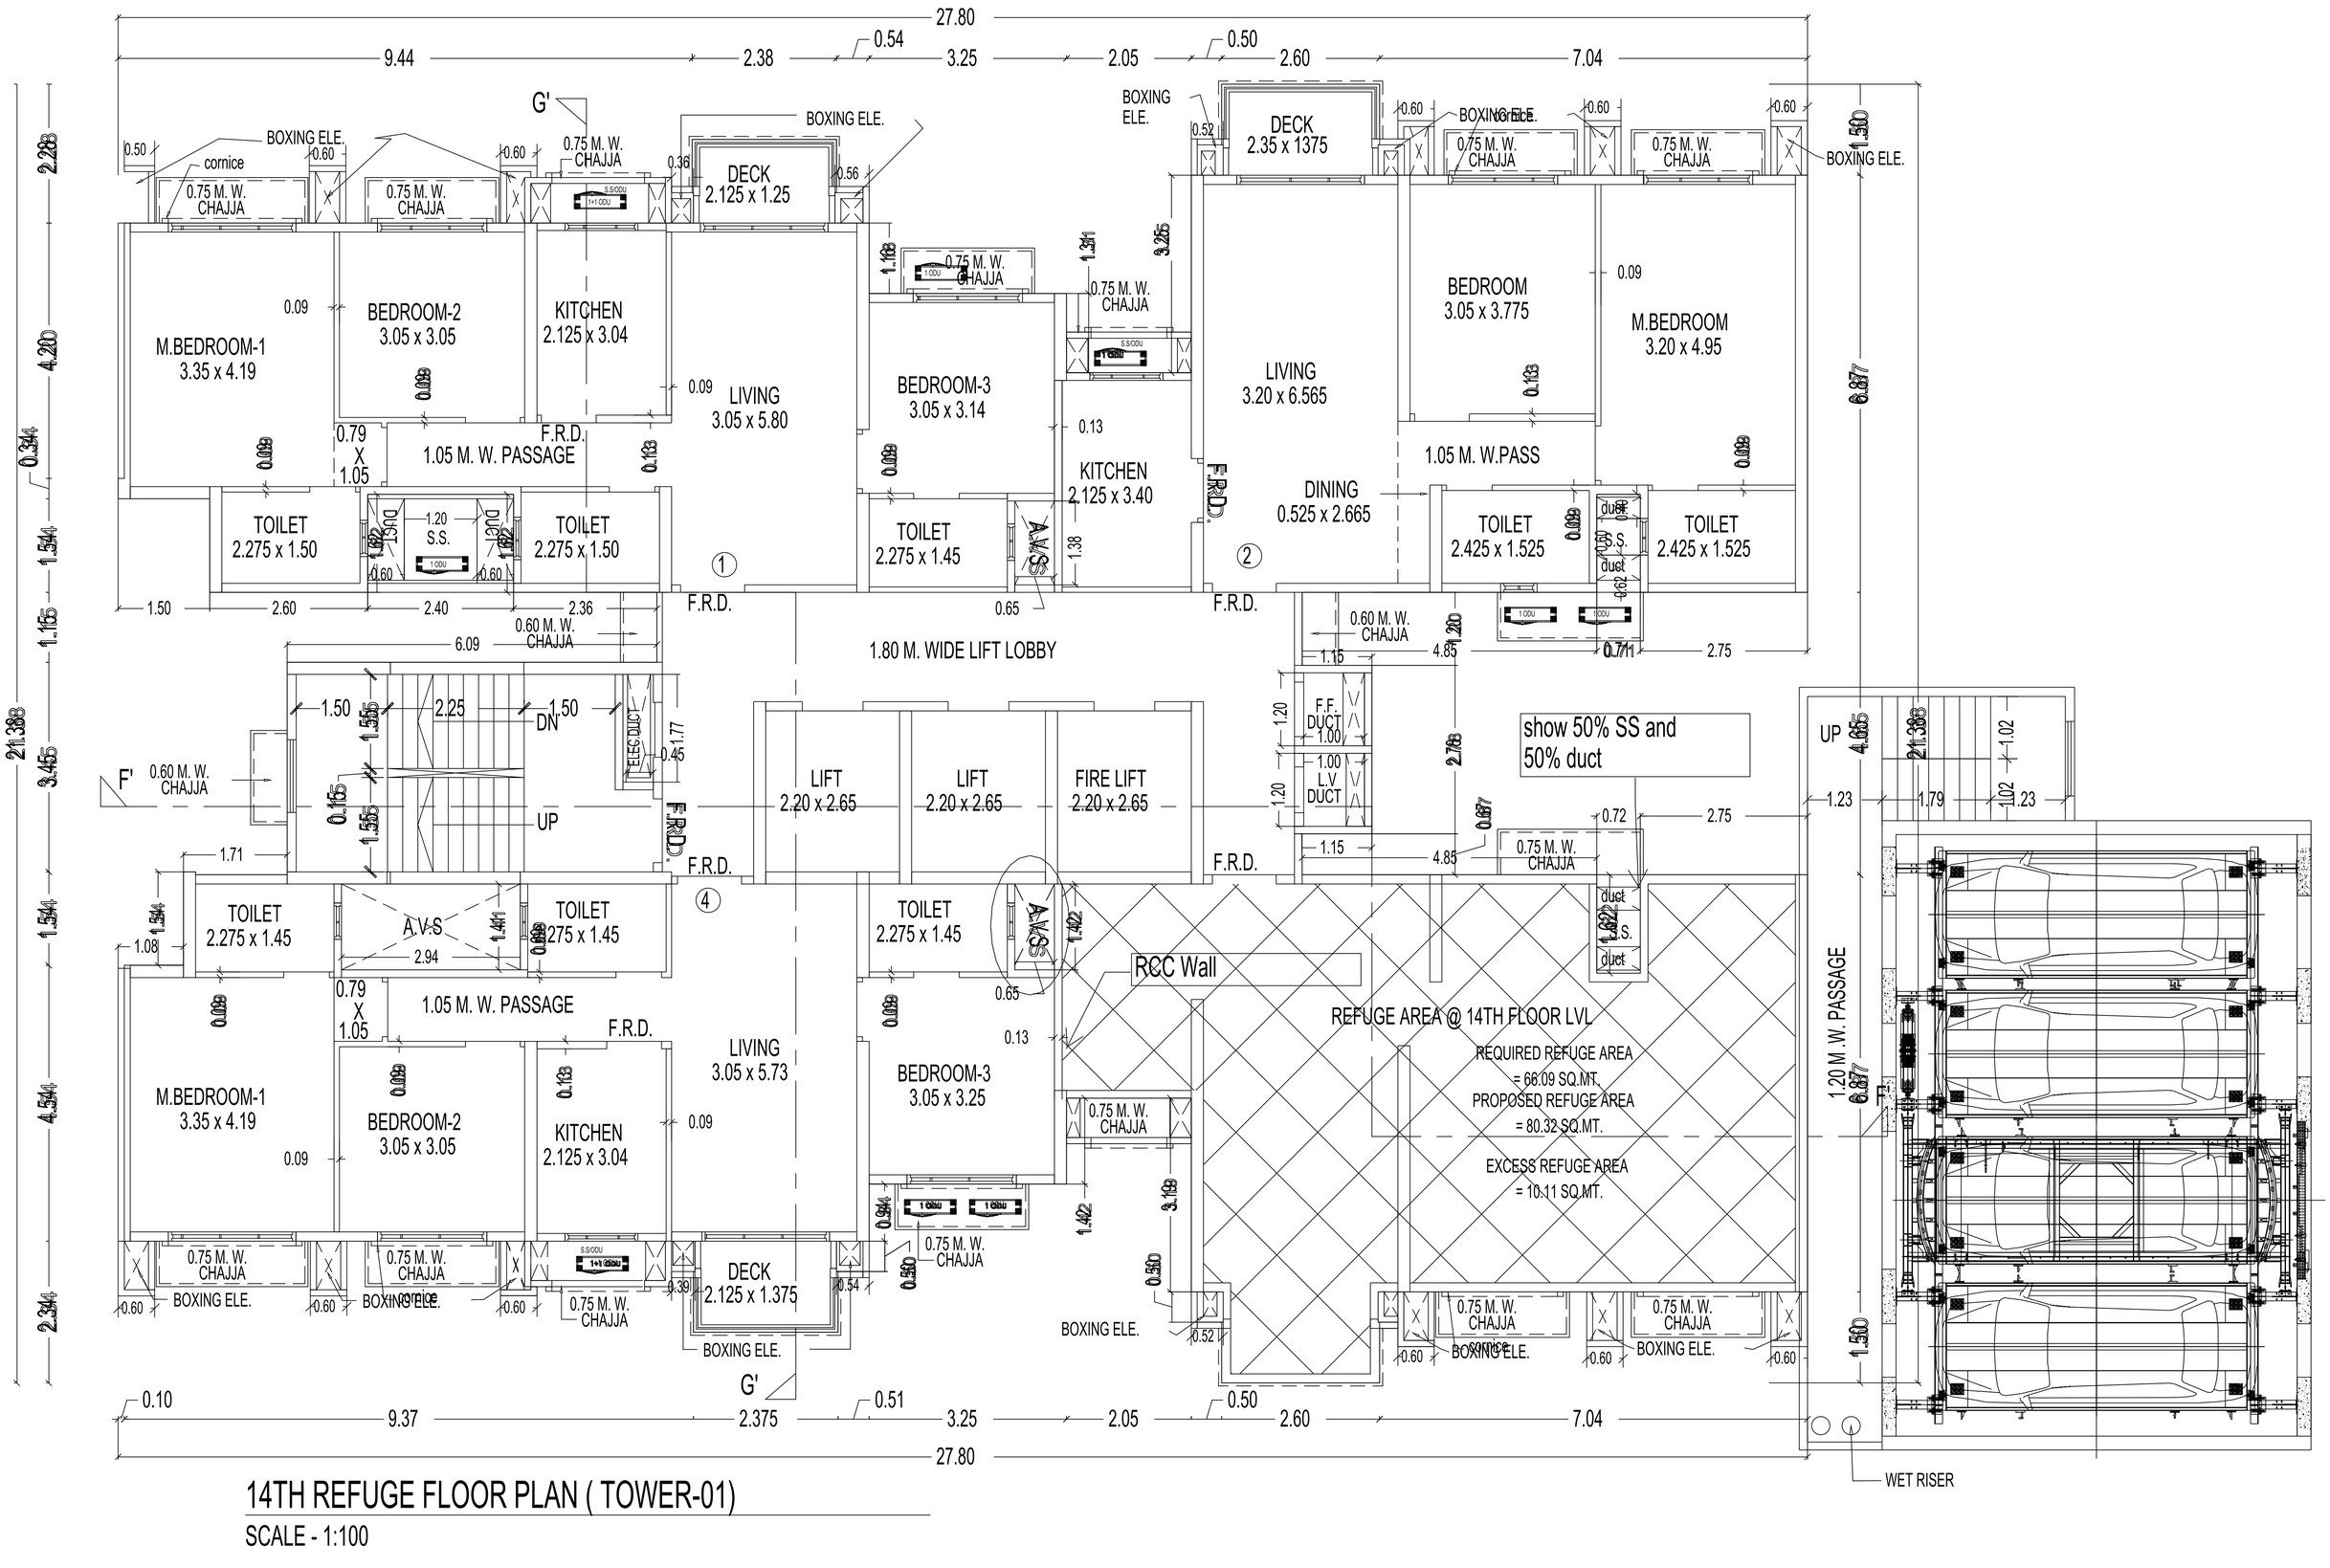

14TH REFUGE FLOOR PLAN (TOWER-01)


SCALE - 1:100

(TOWER- 2)

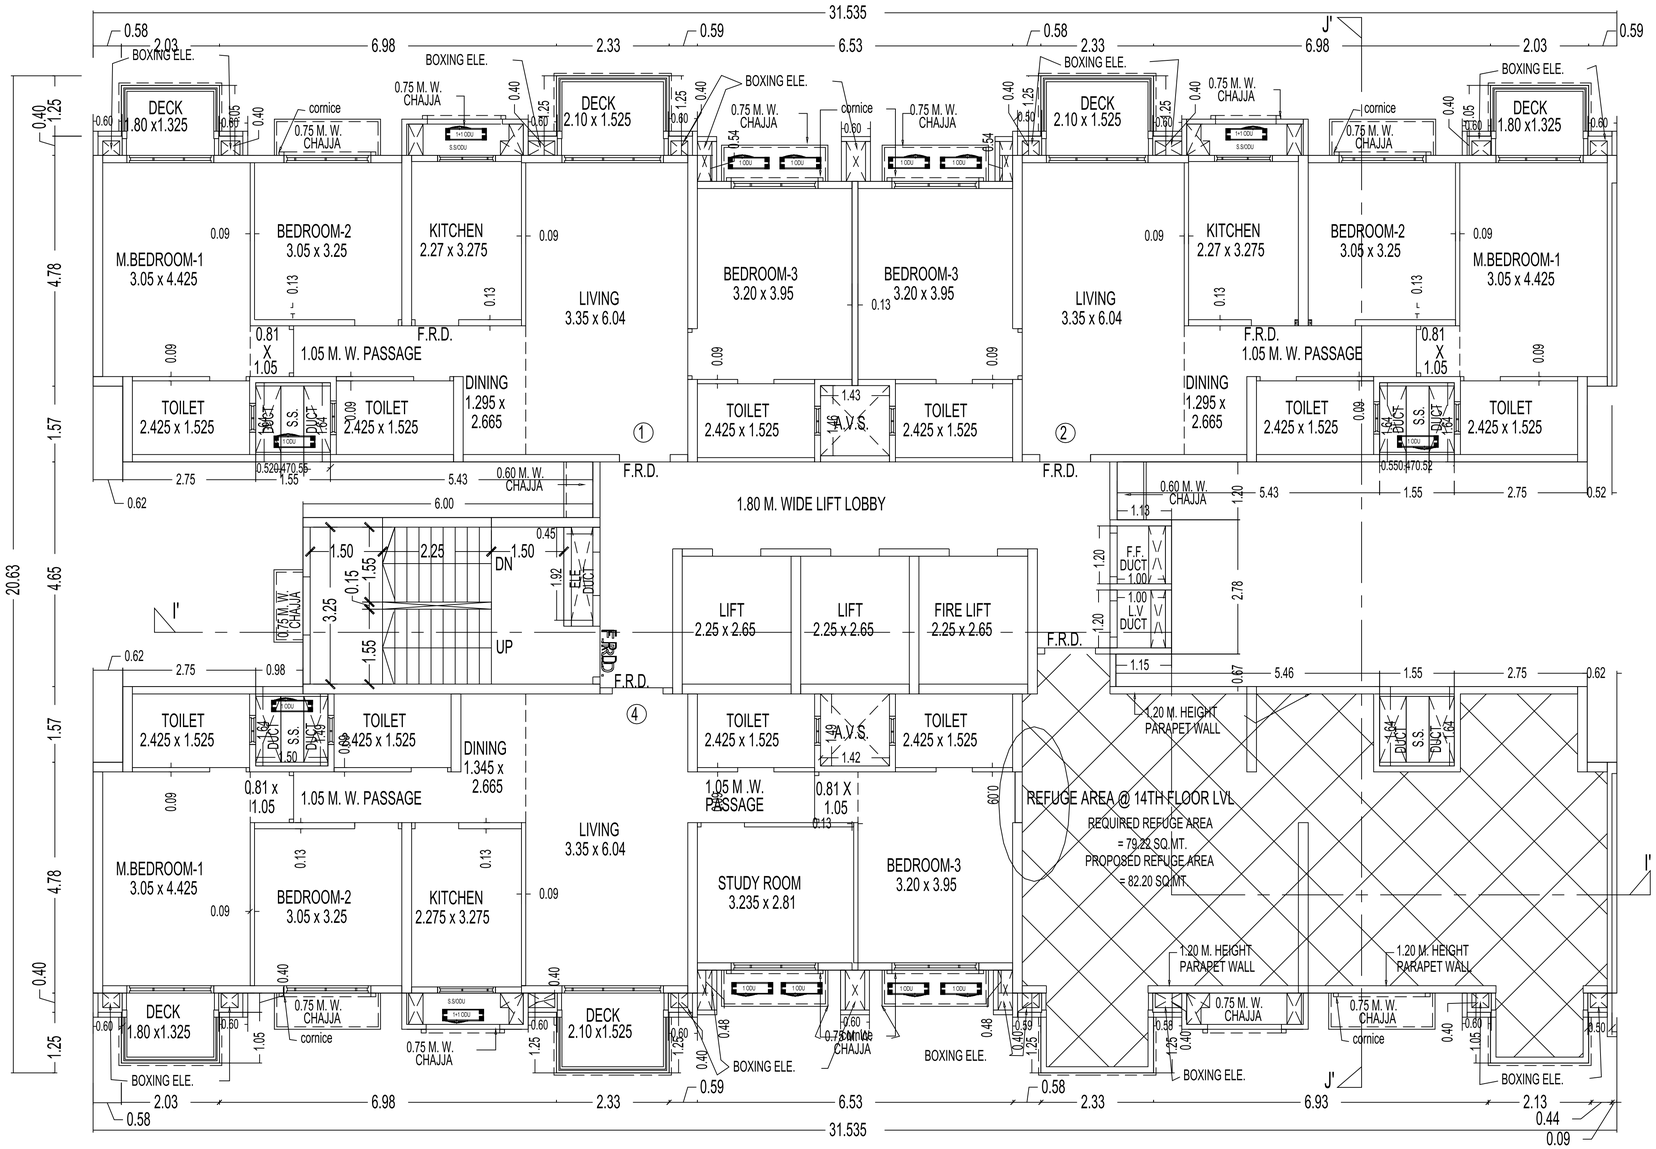

14TH FLOOR PLAN (TOWER-02)

SCALE - 1:100

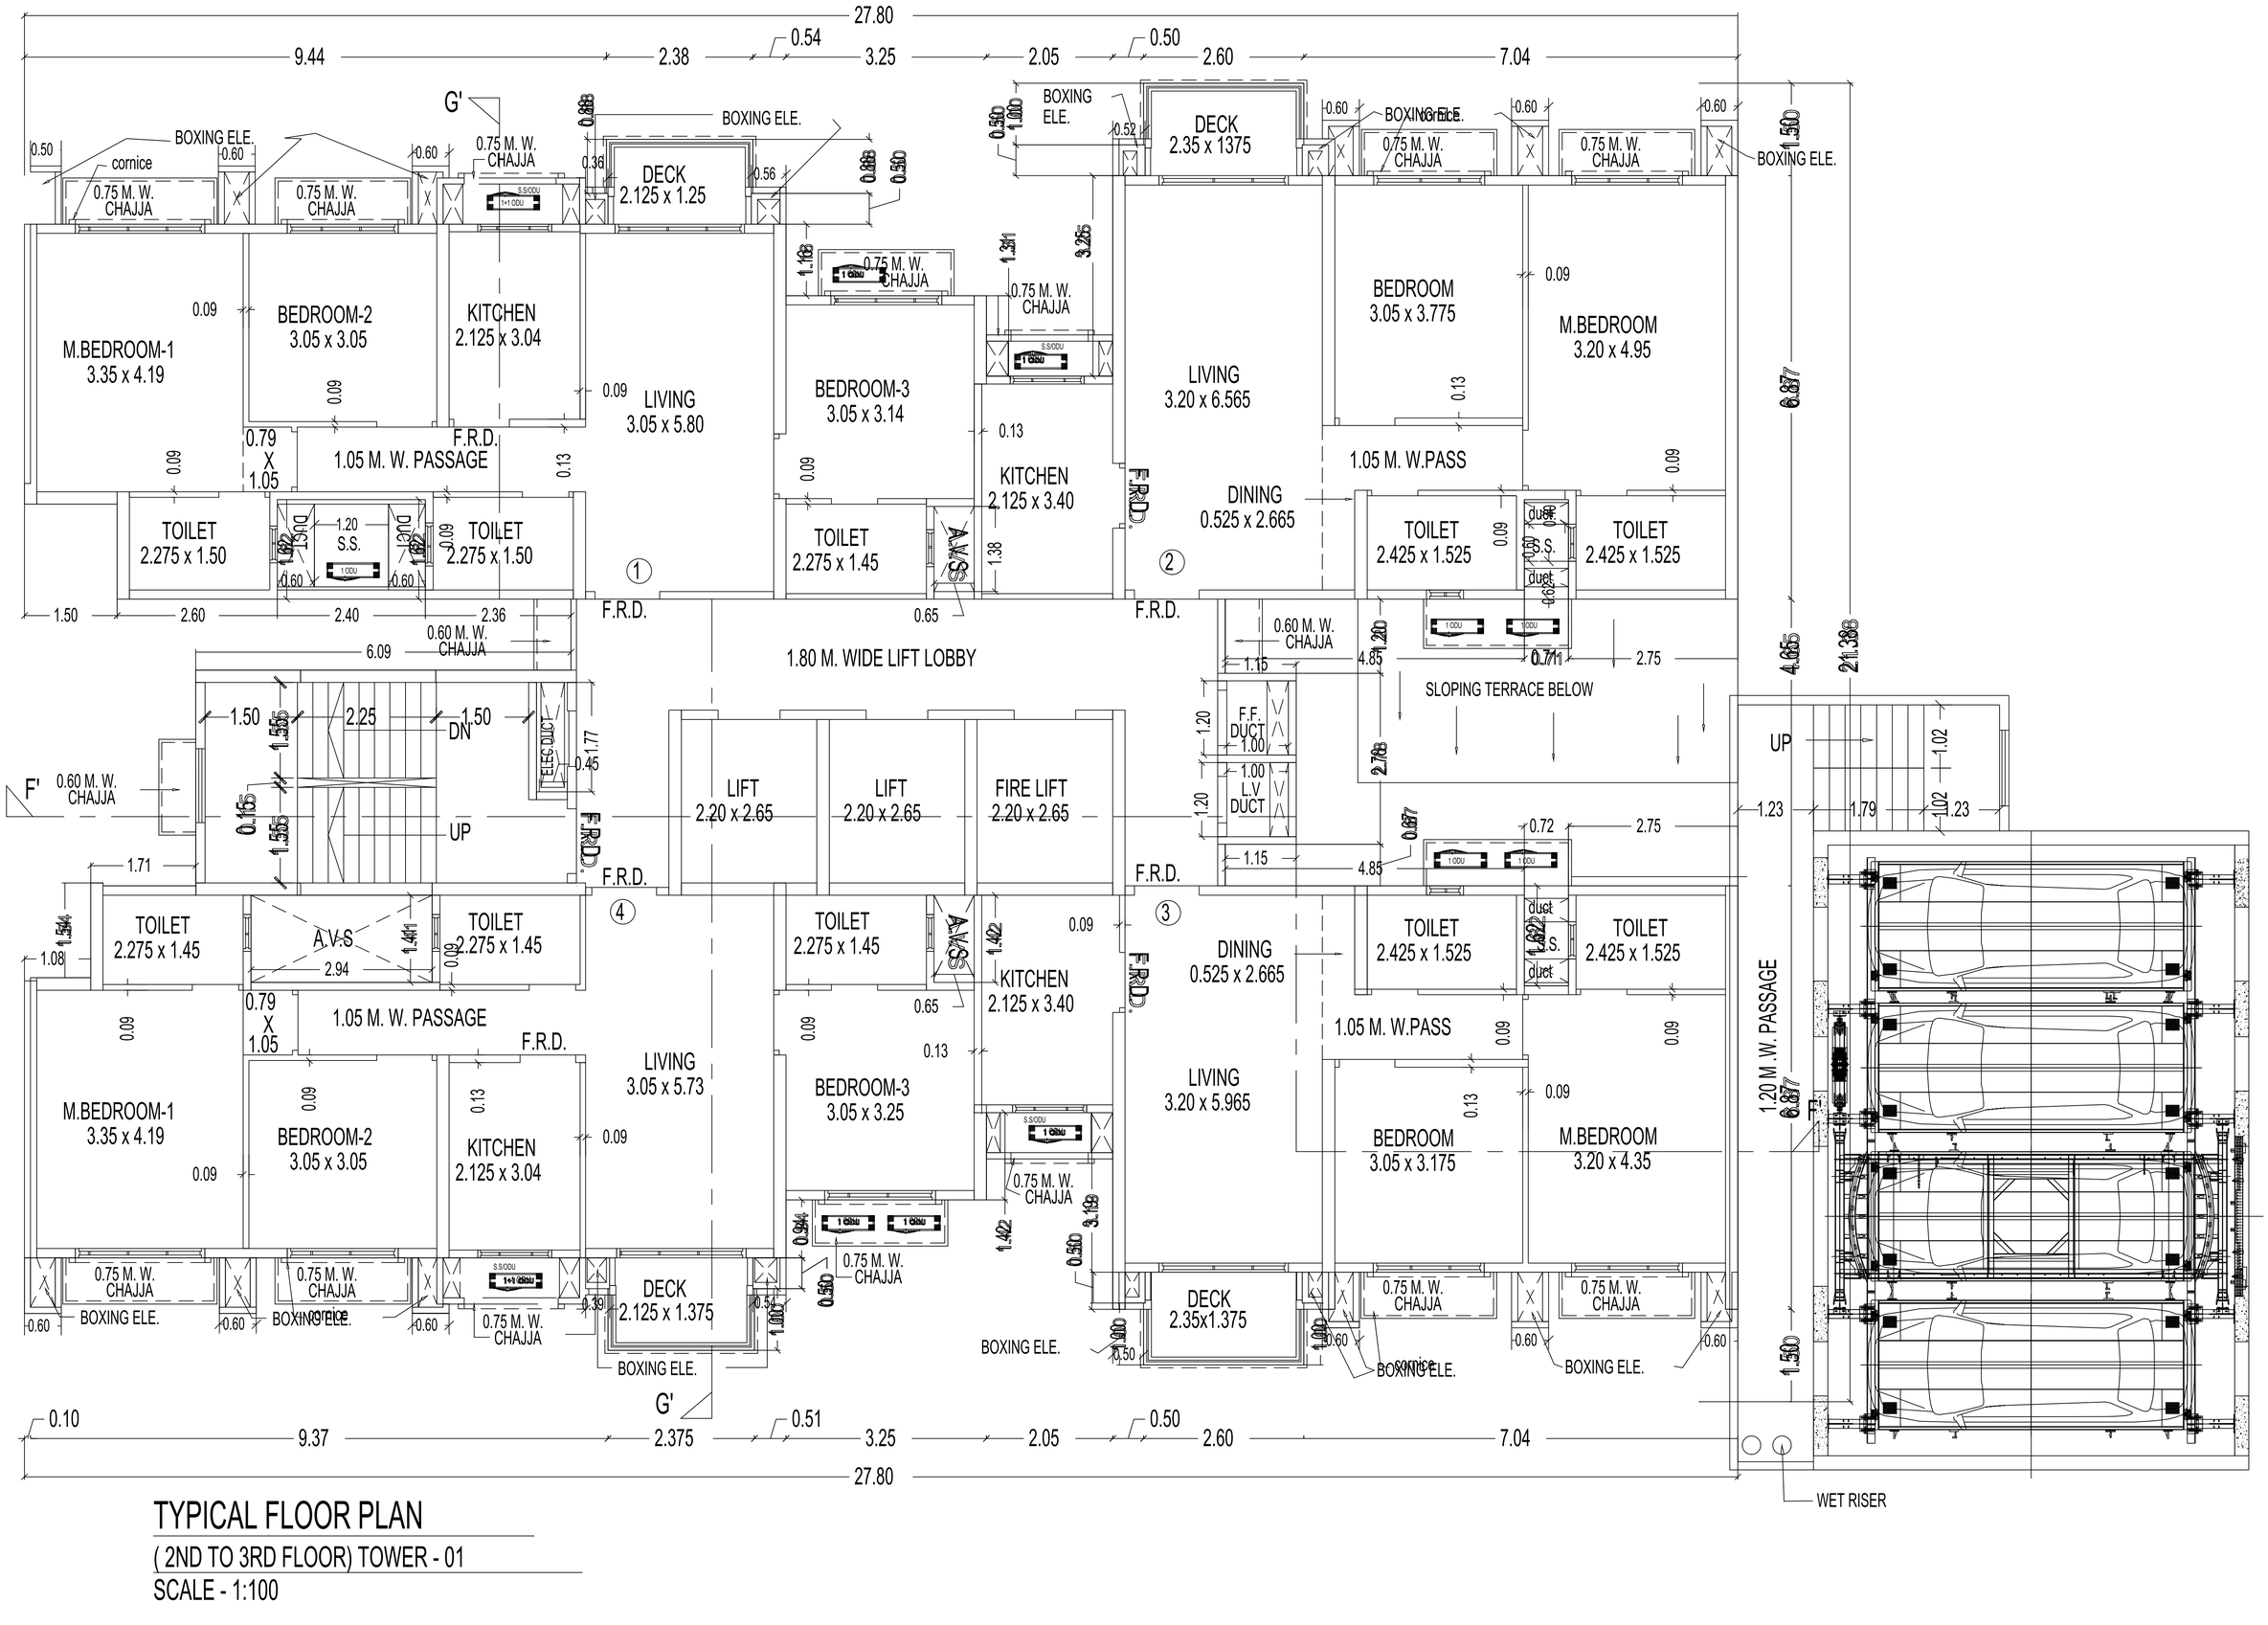

TYPICAL FLOOR PLAN

(2ND TO 3RD FLOOR) TOWER - 01

SCALE - 1:100