


WEST
<< 9.00 MT. WIDE ROAD >>
<< 9.00 MT. WIDE ROAD >>
<< 9.00 MT. WIDE ROAD >>
NORTH
SOUTH
EAST
<< 18.30 MT. WIDE ROAD >>
<< 18.30 MT. WIDE ROAD >>
PROPOSED GYM
PROPOSED SWIMMING POOL
PROPOSED FITNESS CENTER
PROPOSED FITNESS CENTER


SCALE - 1:100

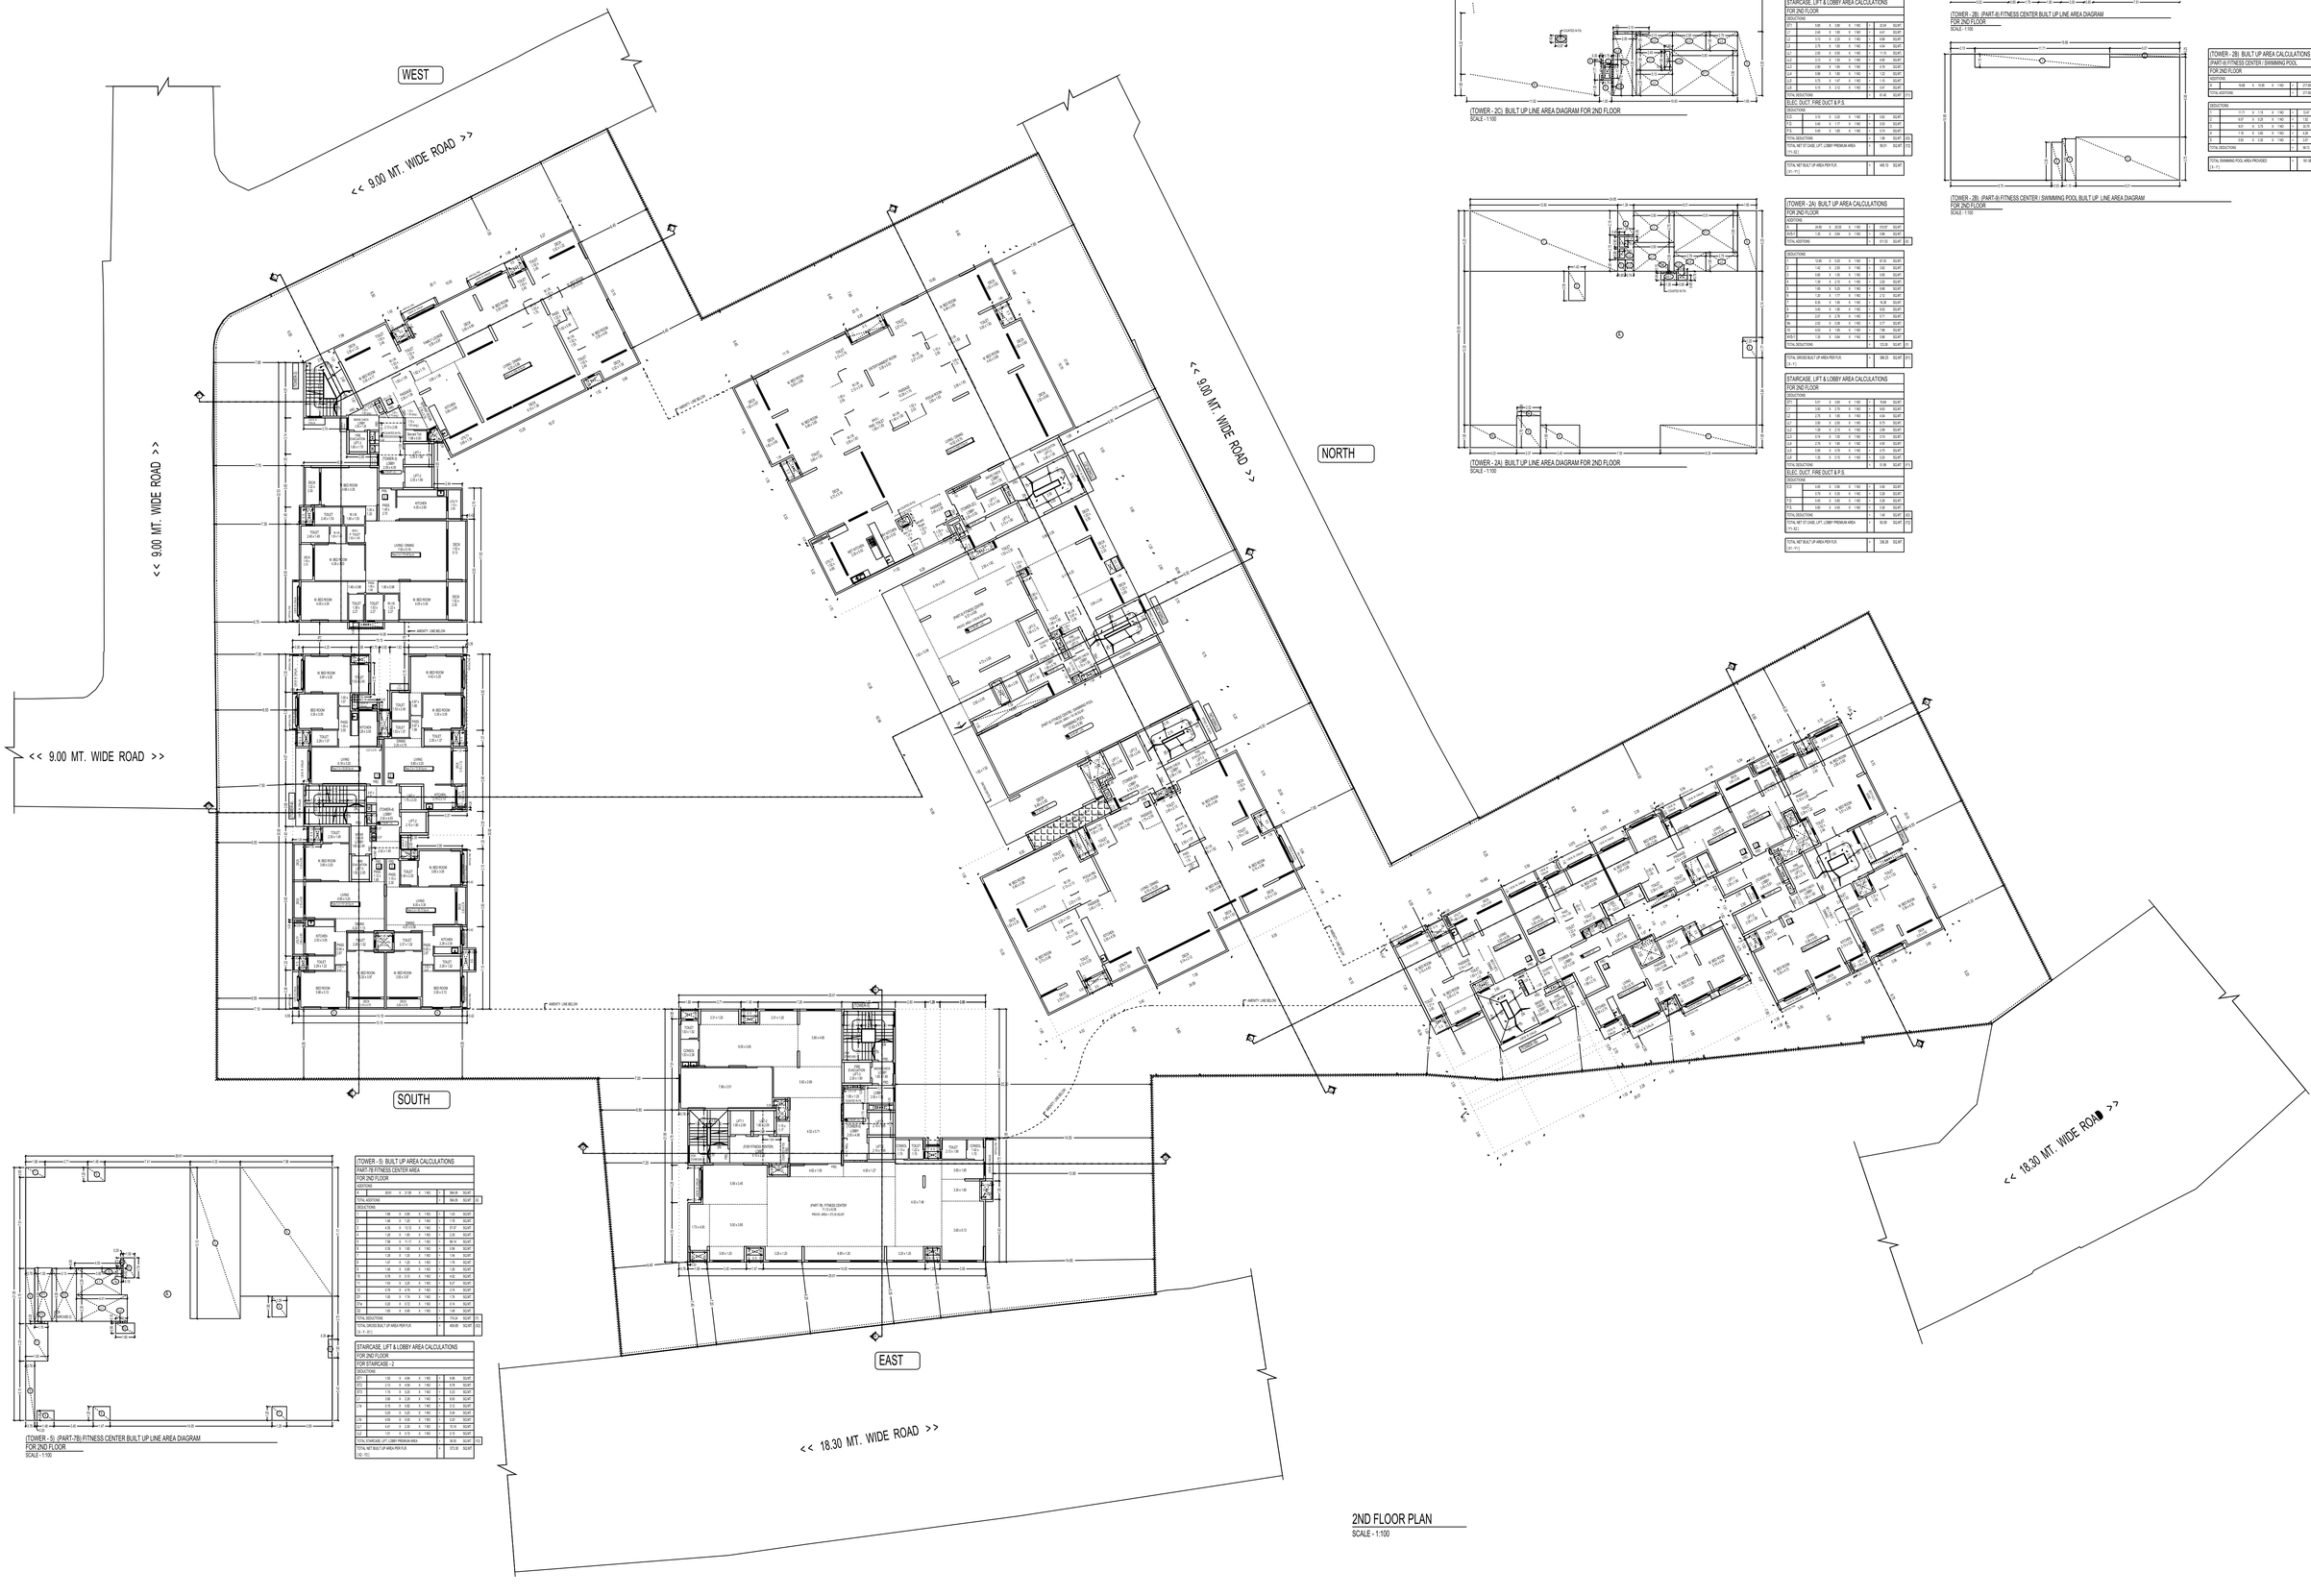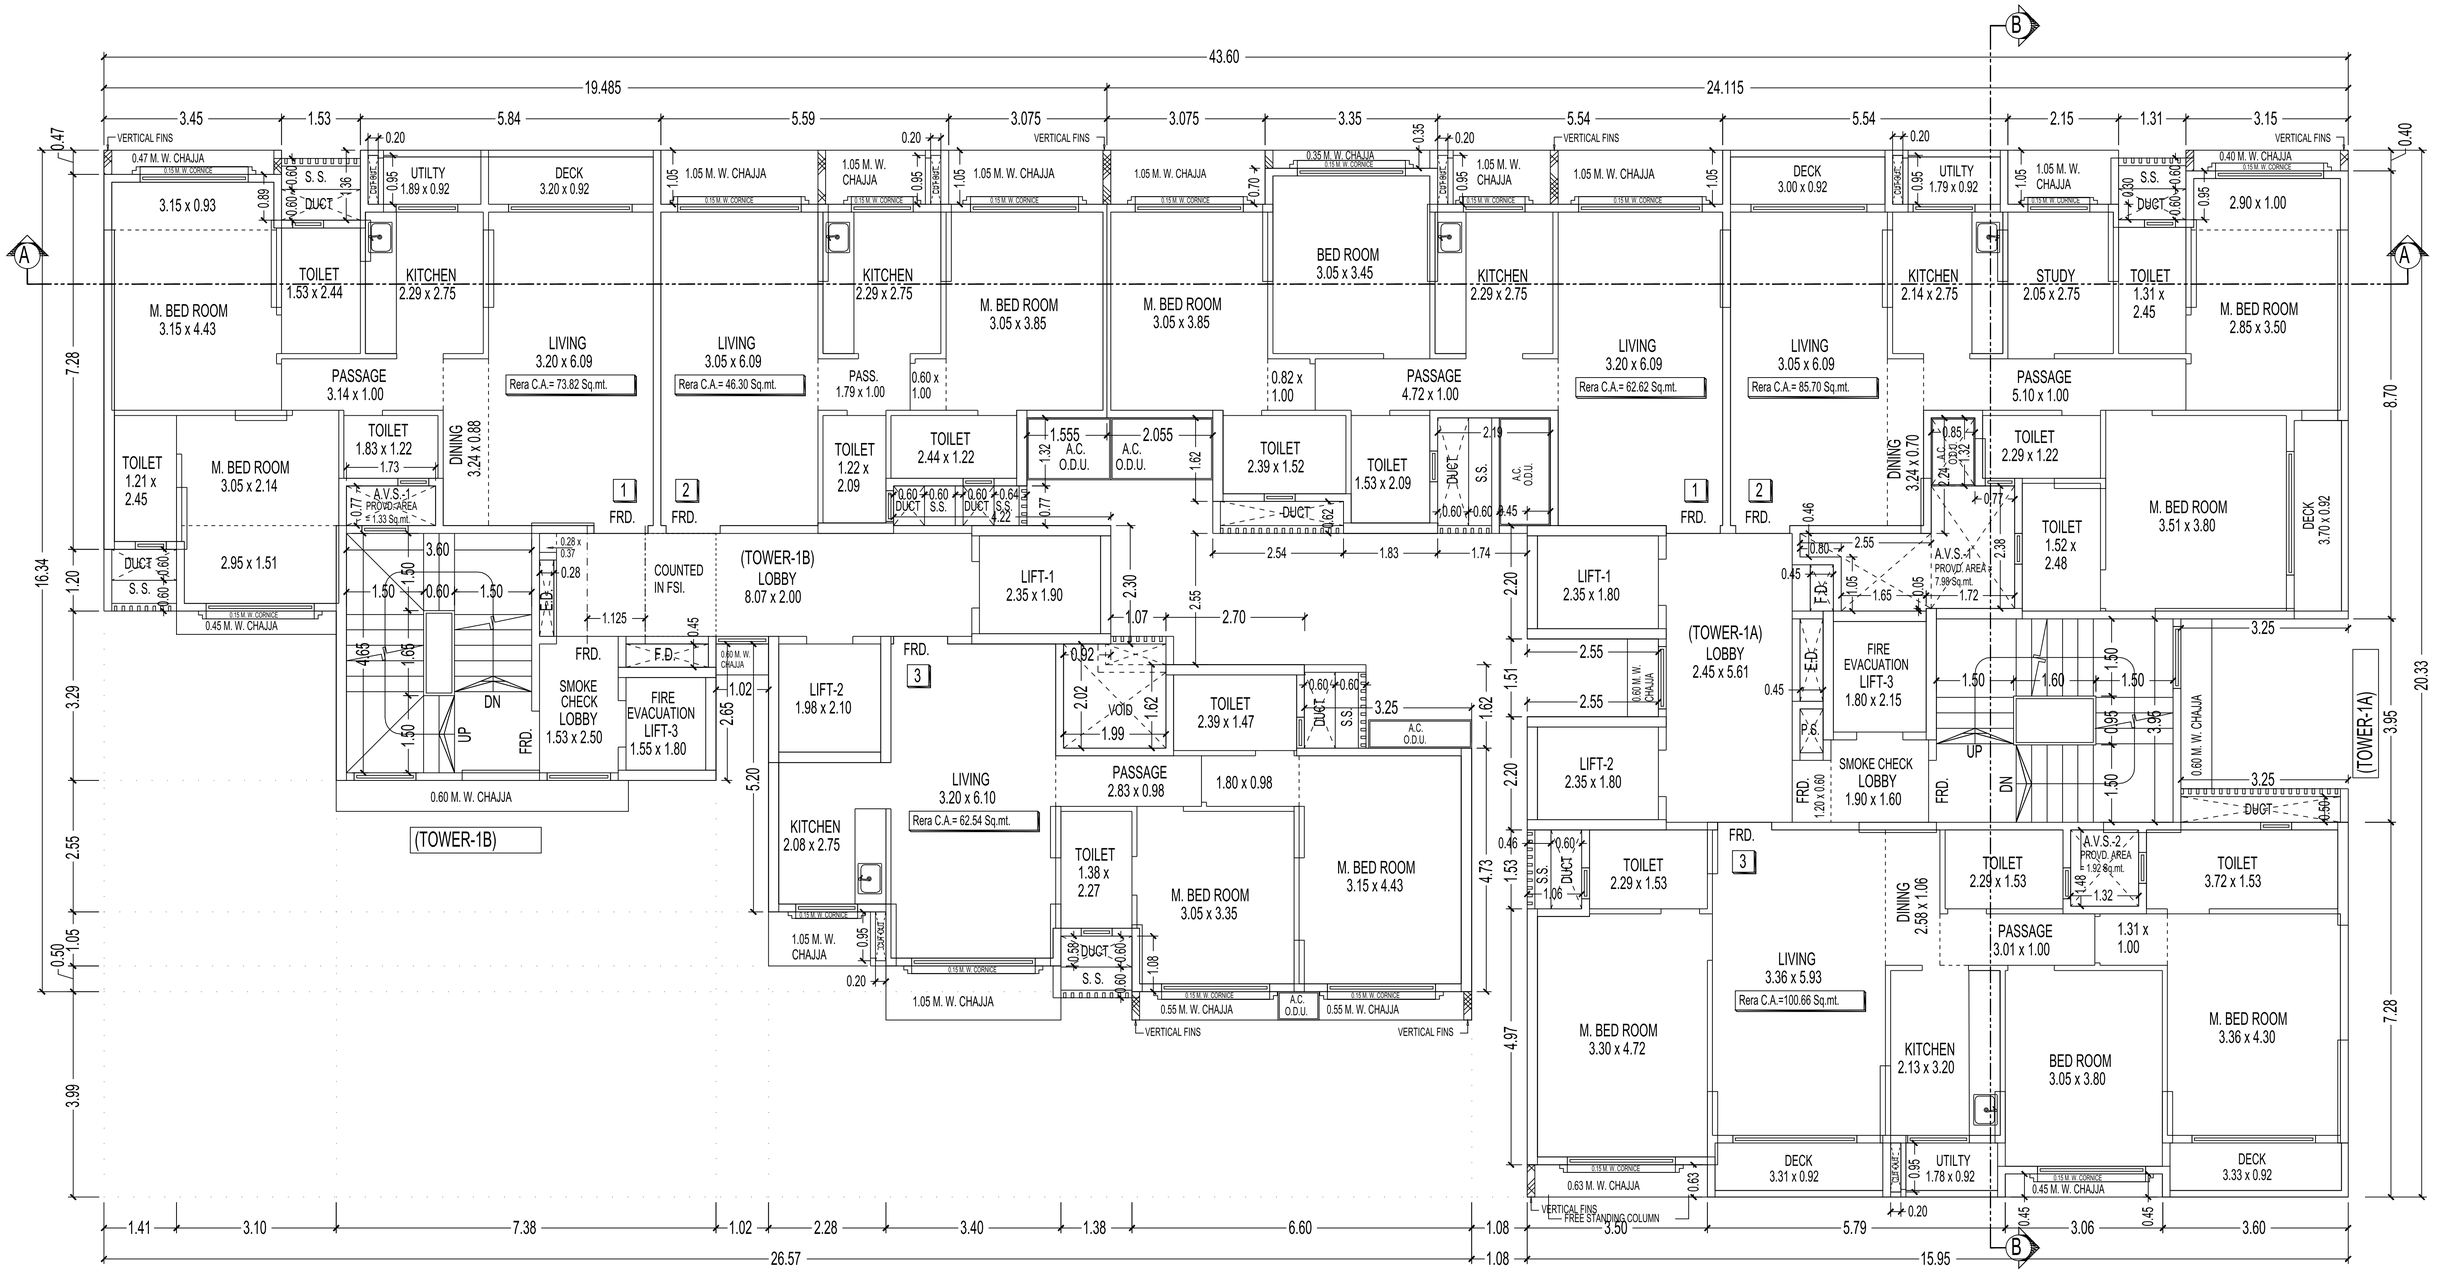


(TOWER-1A & 1B) 3RD FLOOR PLAN

SCALE - 1:100

SCALE - 1:100

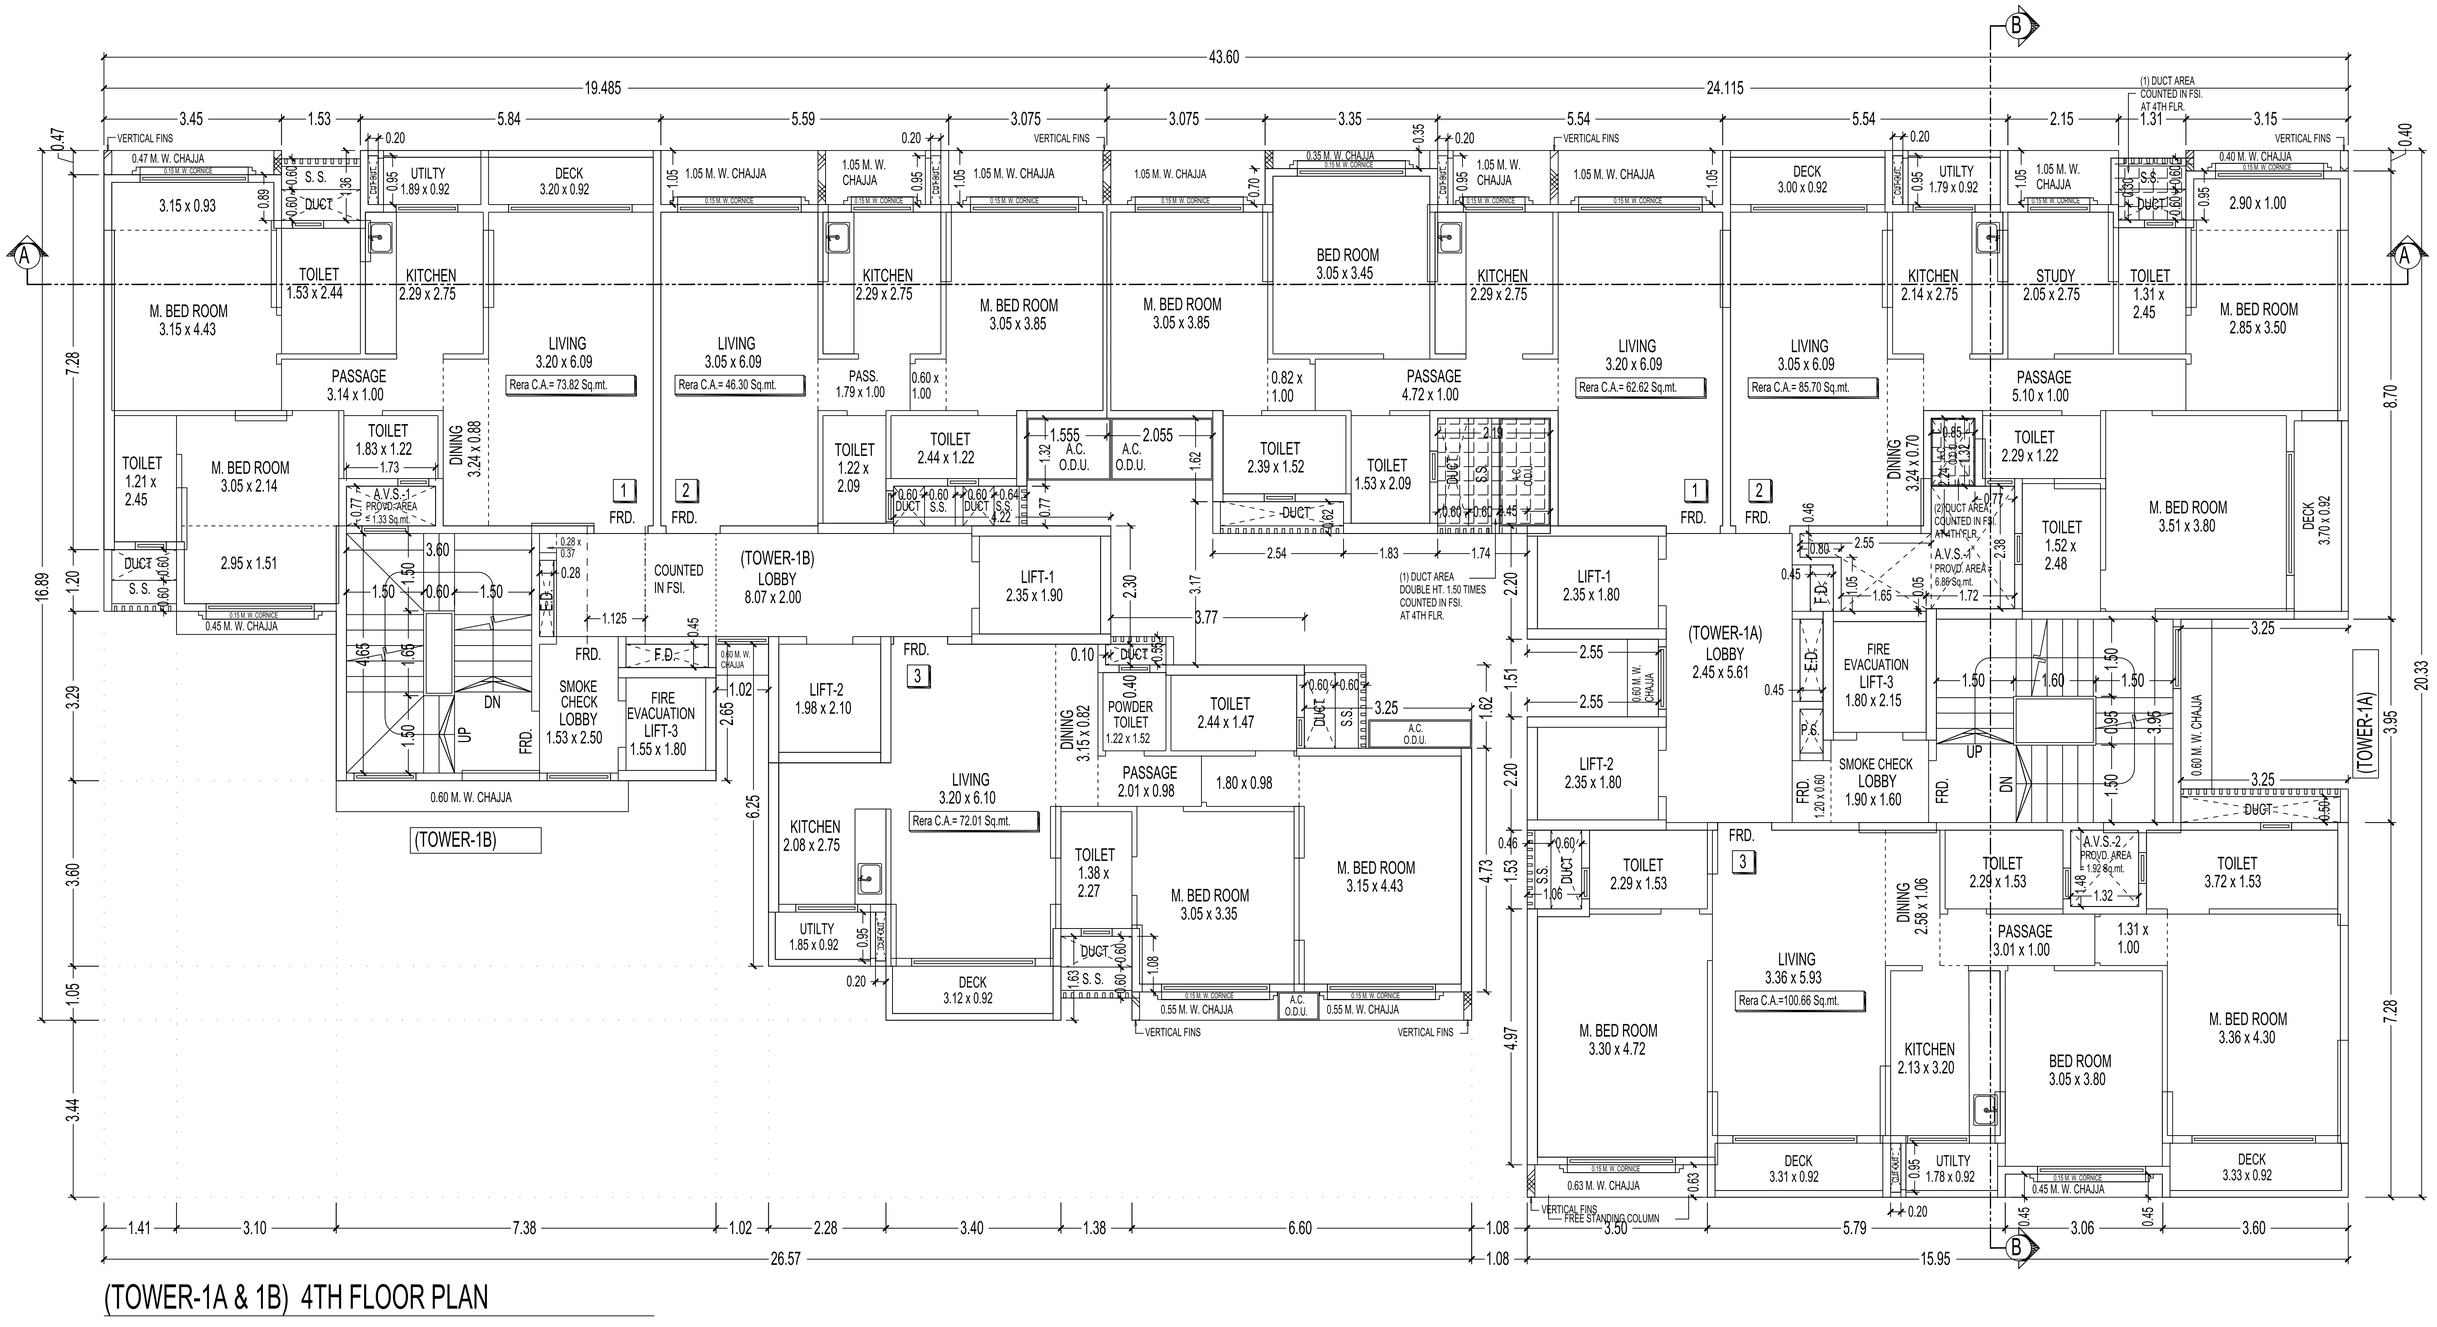


(TOWER-1A & 1B) 4TH FLOOR PLAN

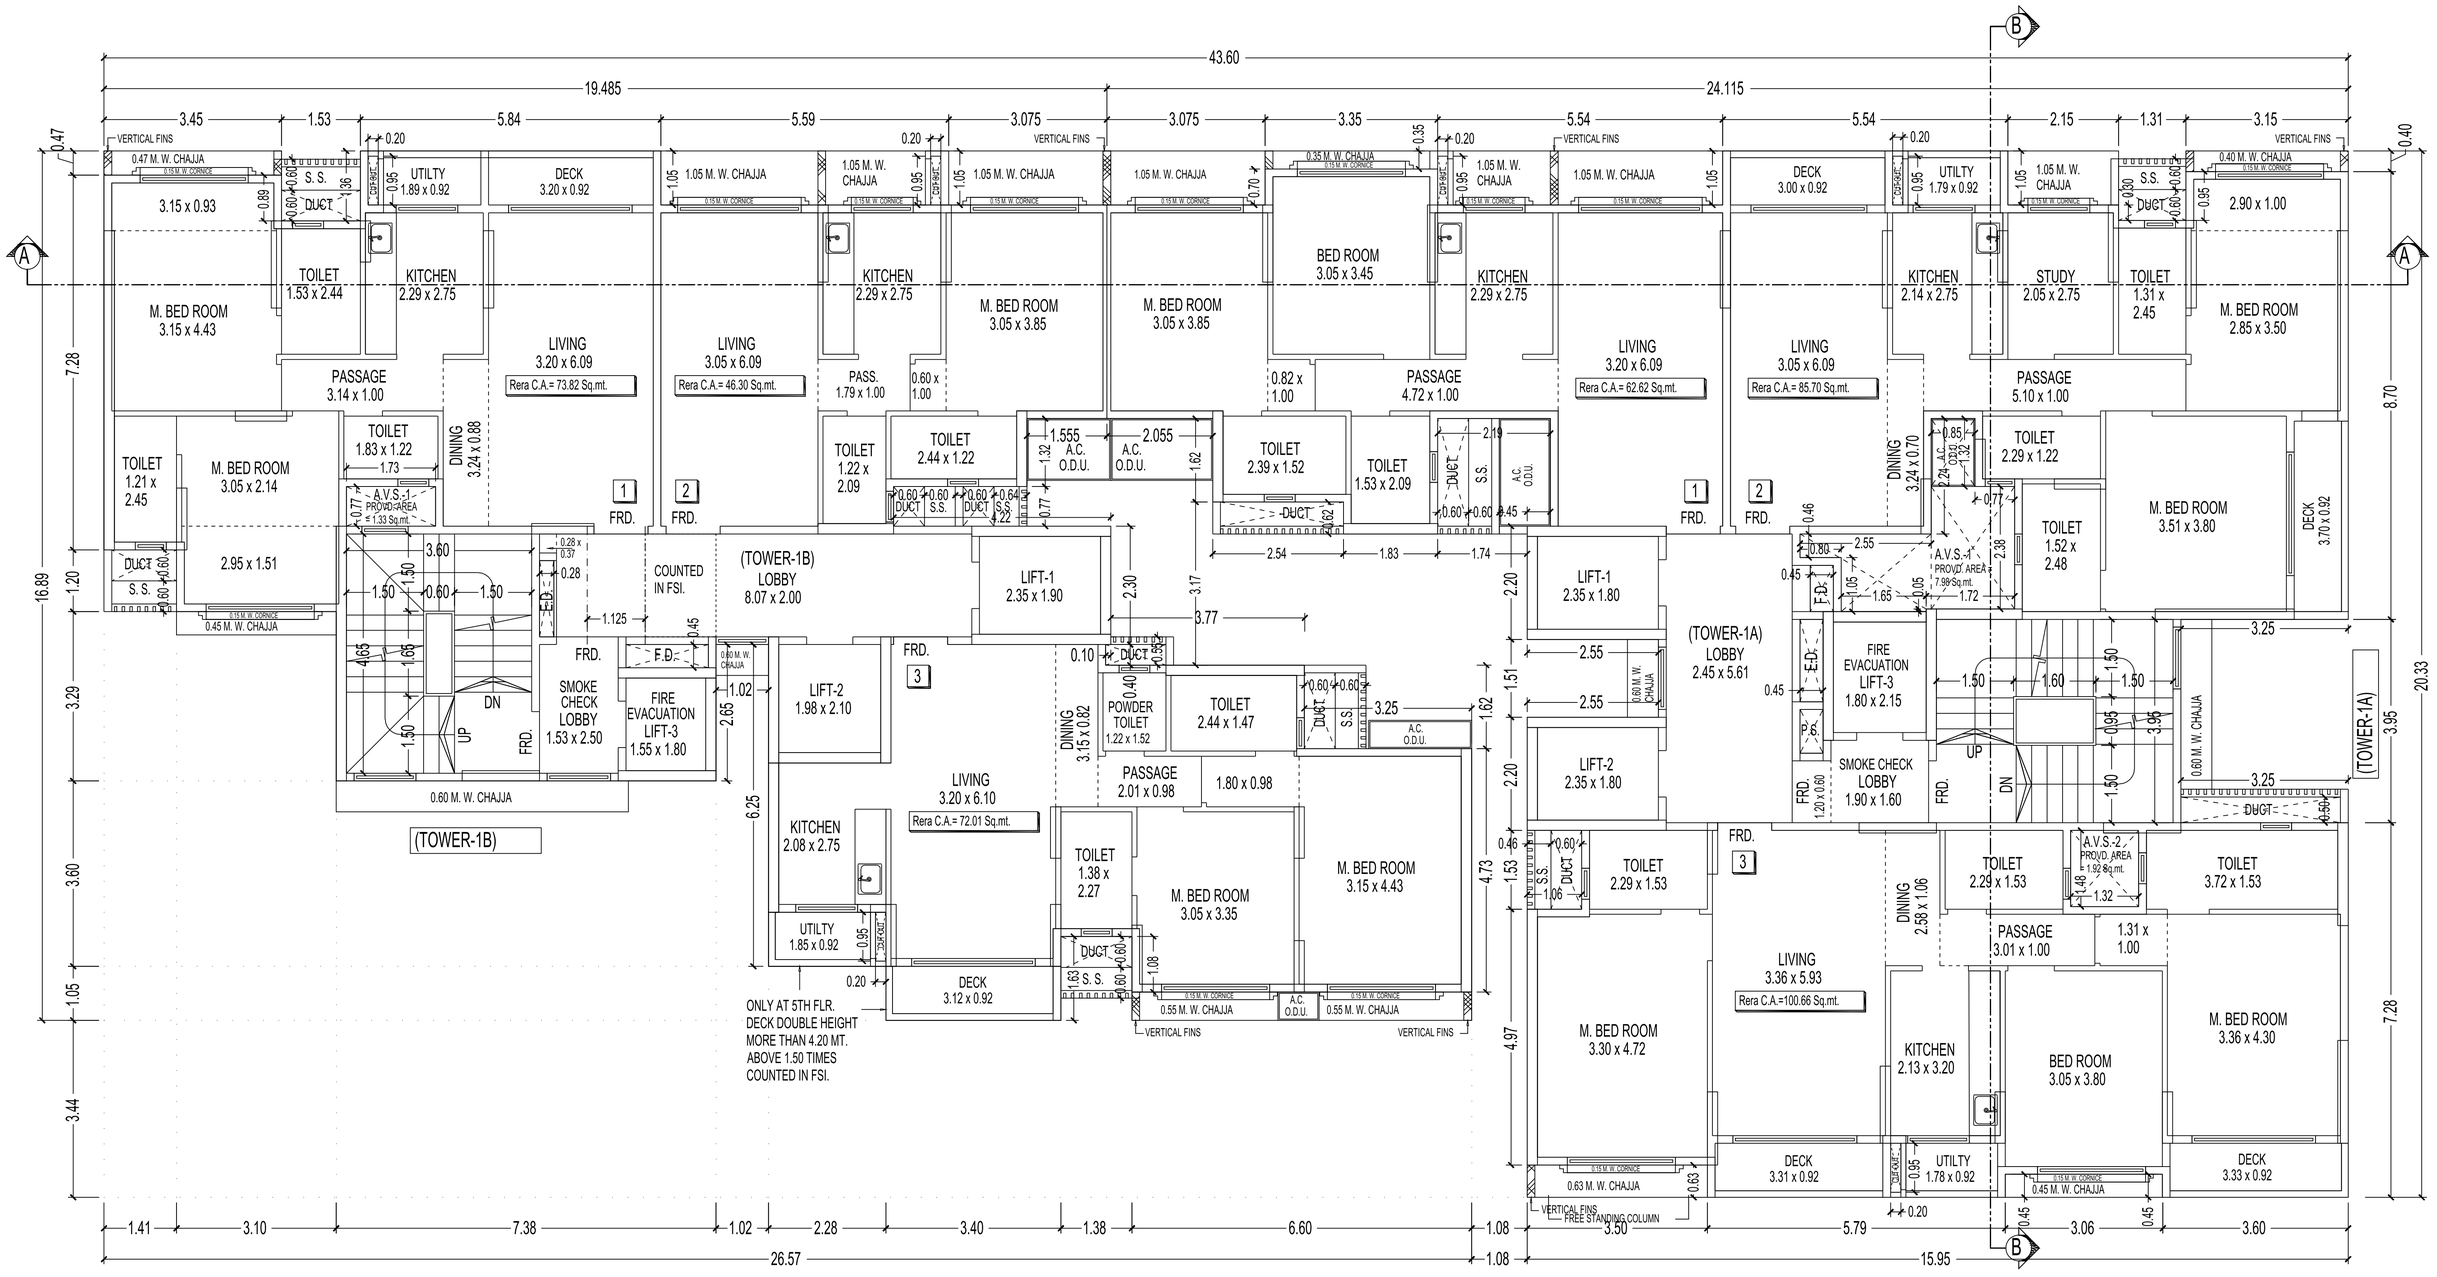

(TOWER-1A & 1B) 5TH FLOOR PLAN


SCALE - 1:100

SCALE - 1:100

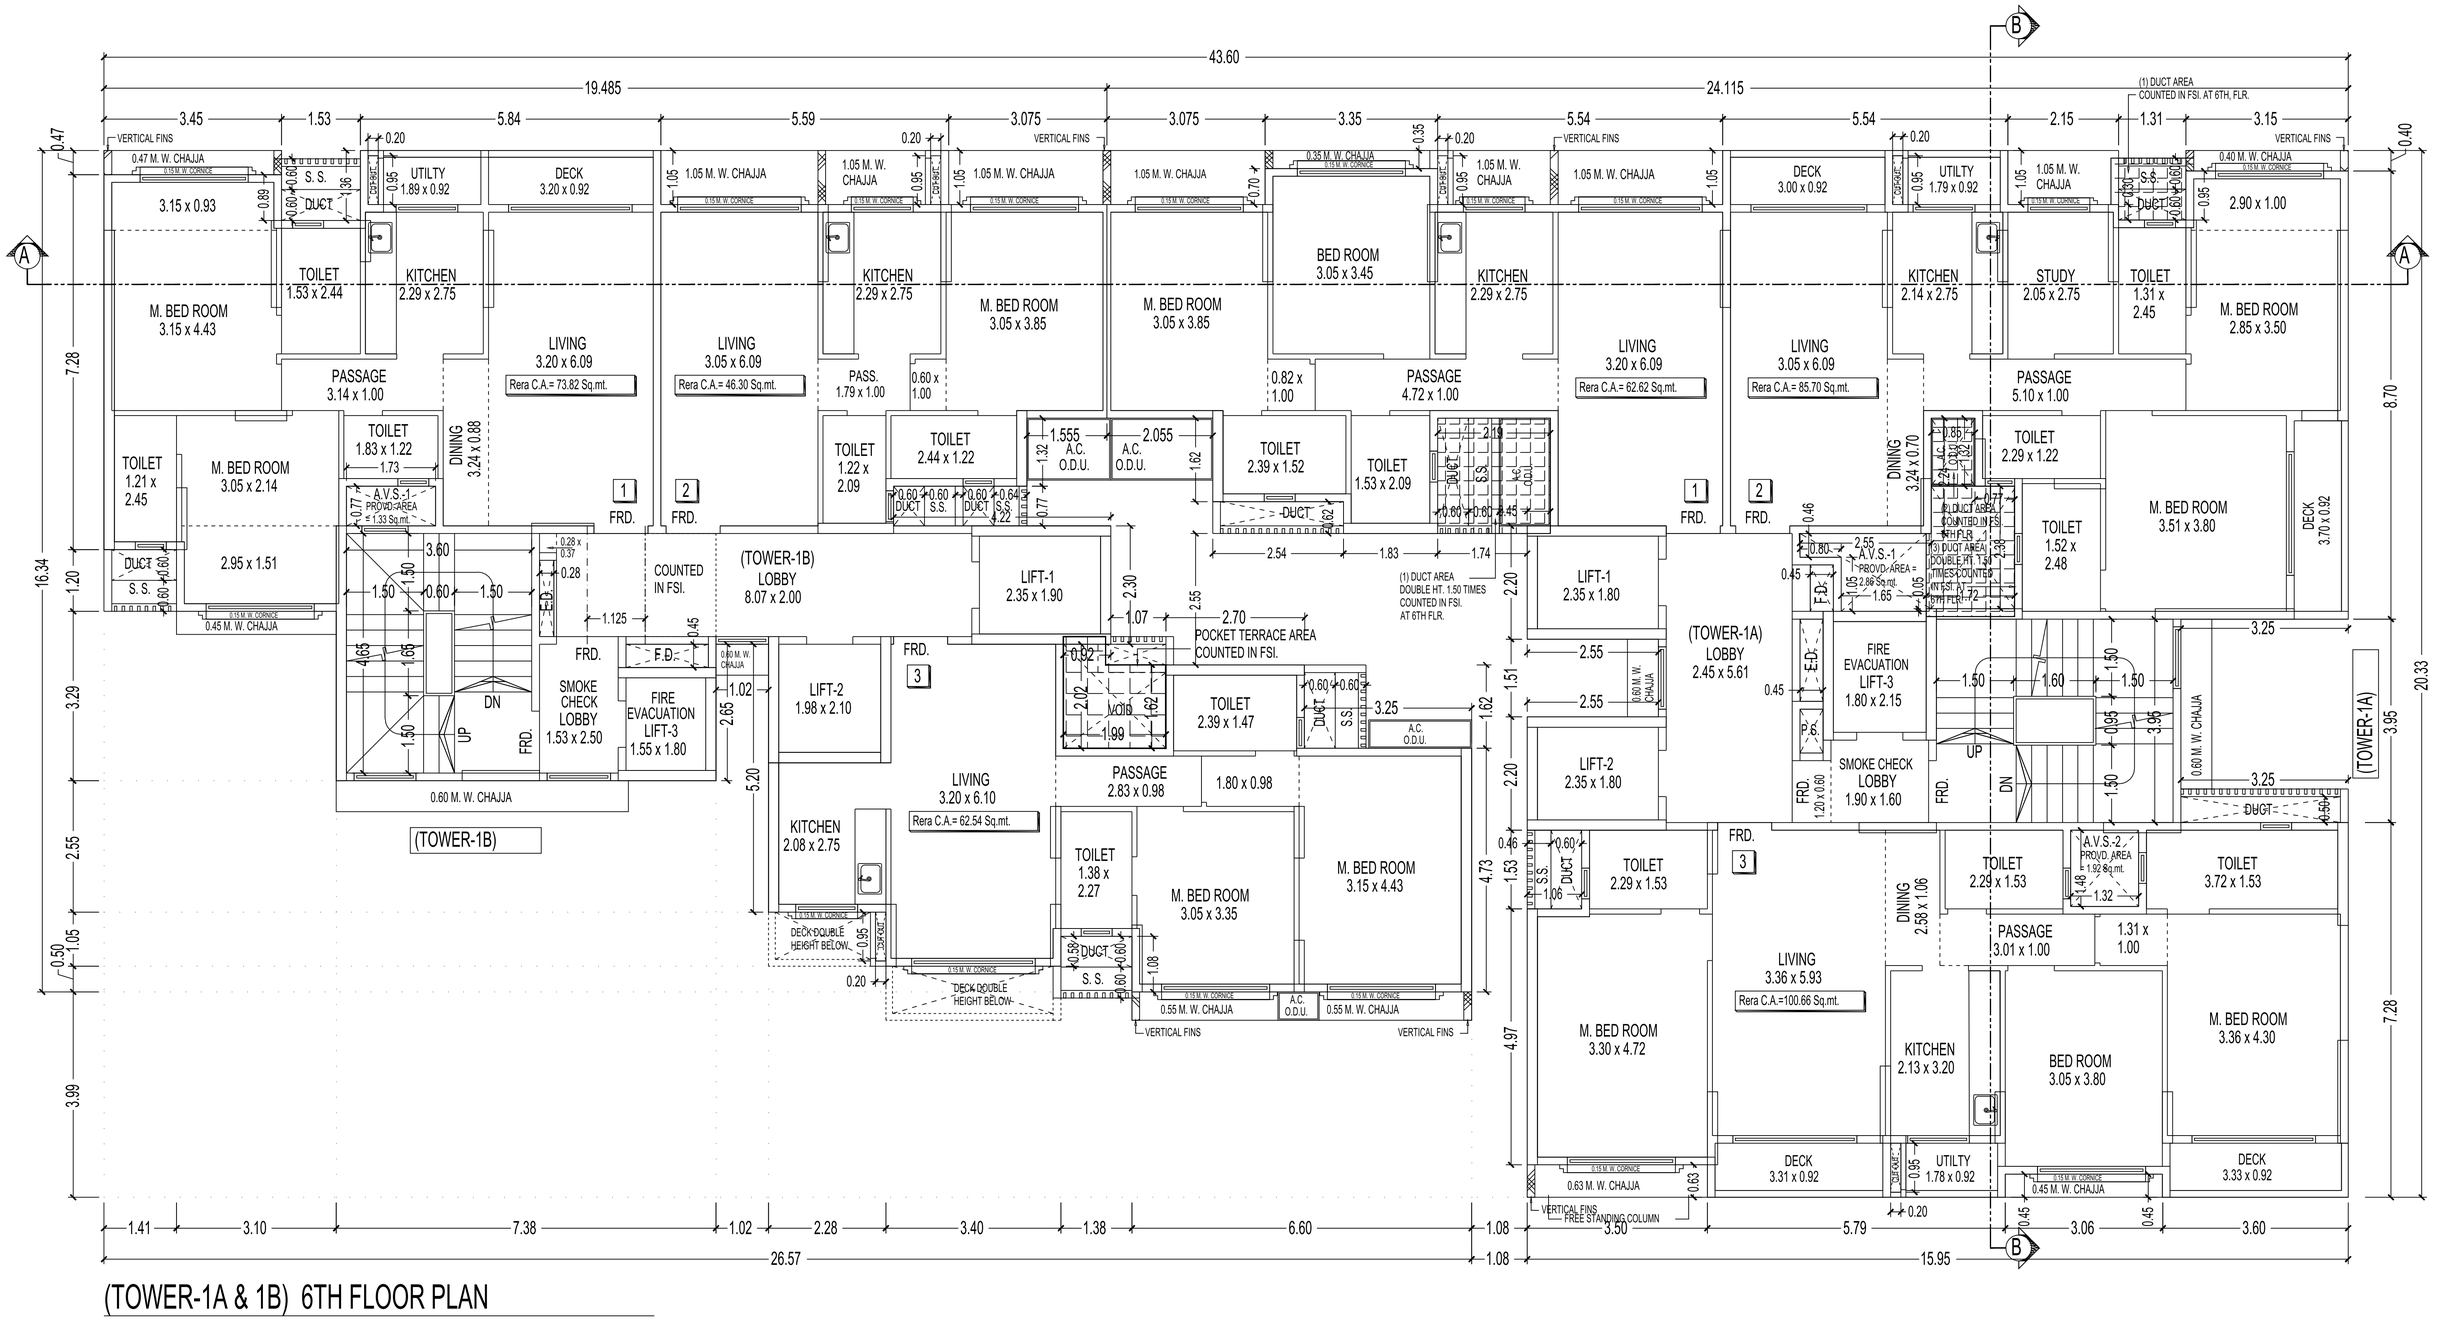

(TOWER-1A & 1B) 6TH FLOOR PLAN


SCALE - 1:100

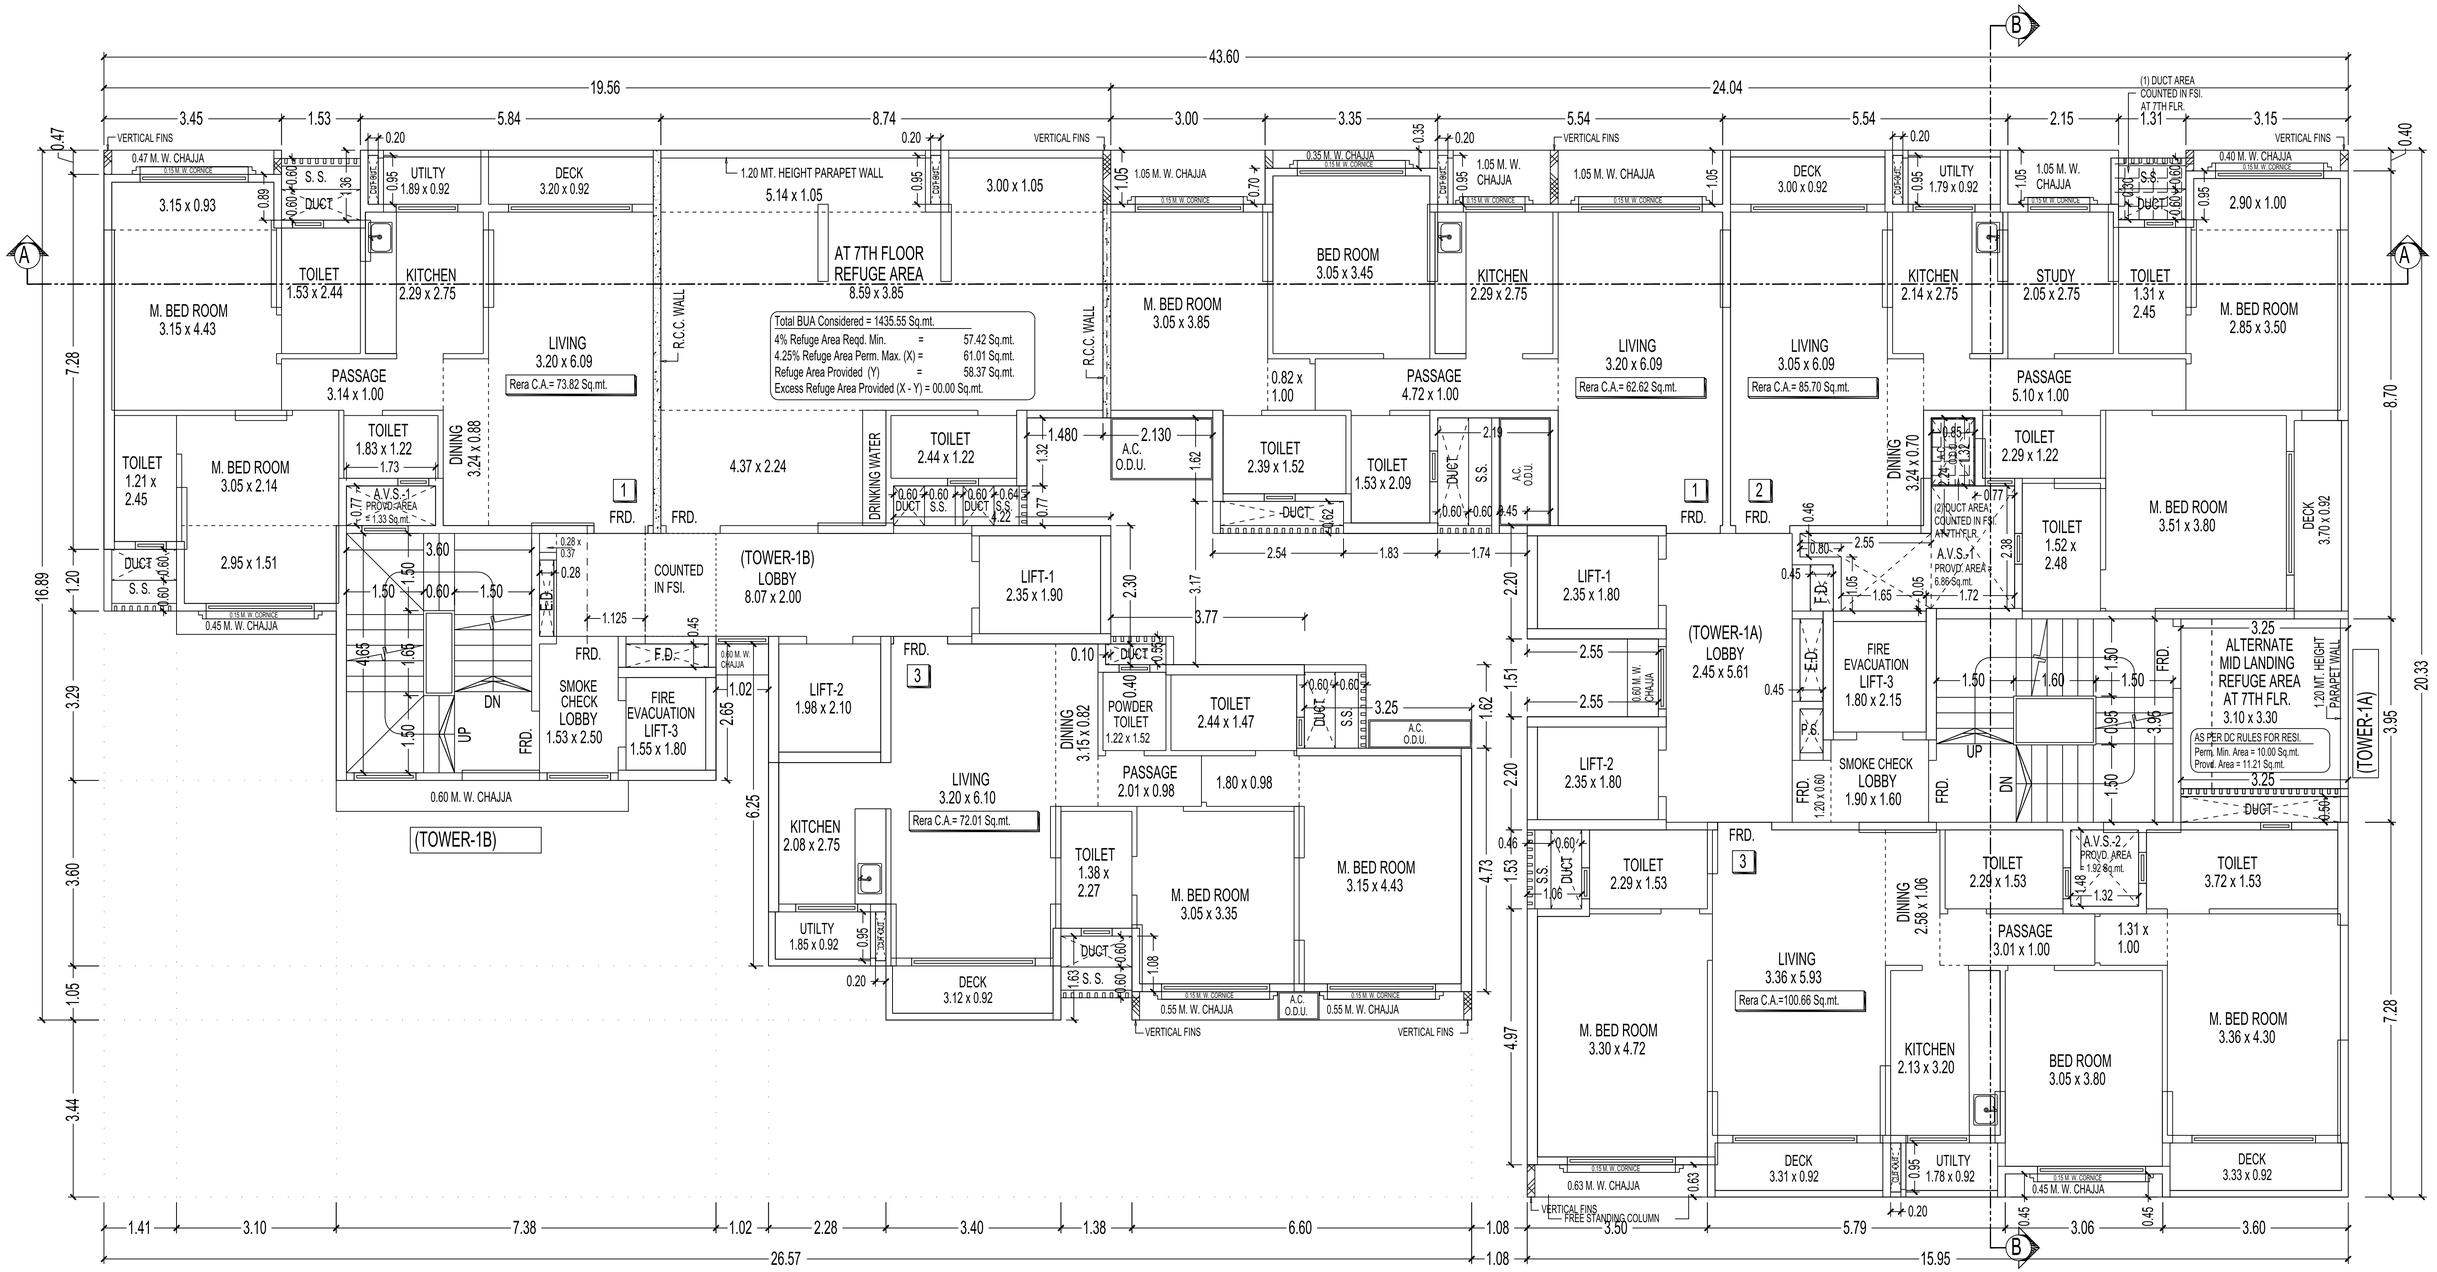


(TOWER-1A & 1B) 7TH REFUGE FLOOR PLAN

SCALE - 1:100

SCALE - 1:100

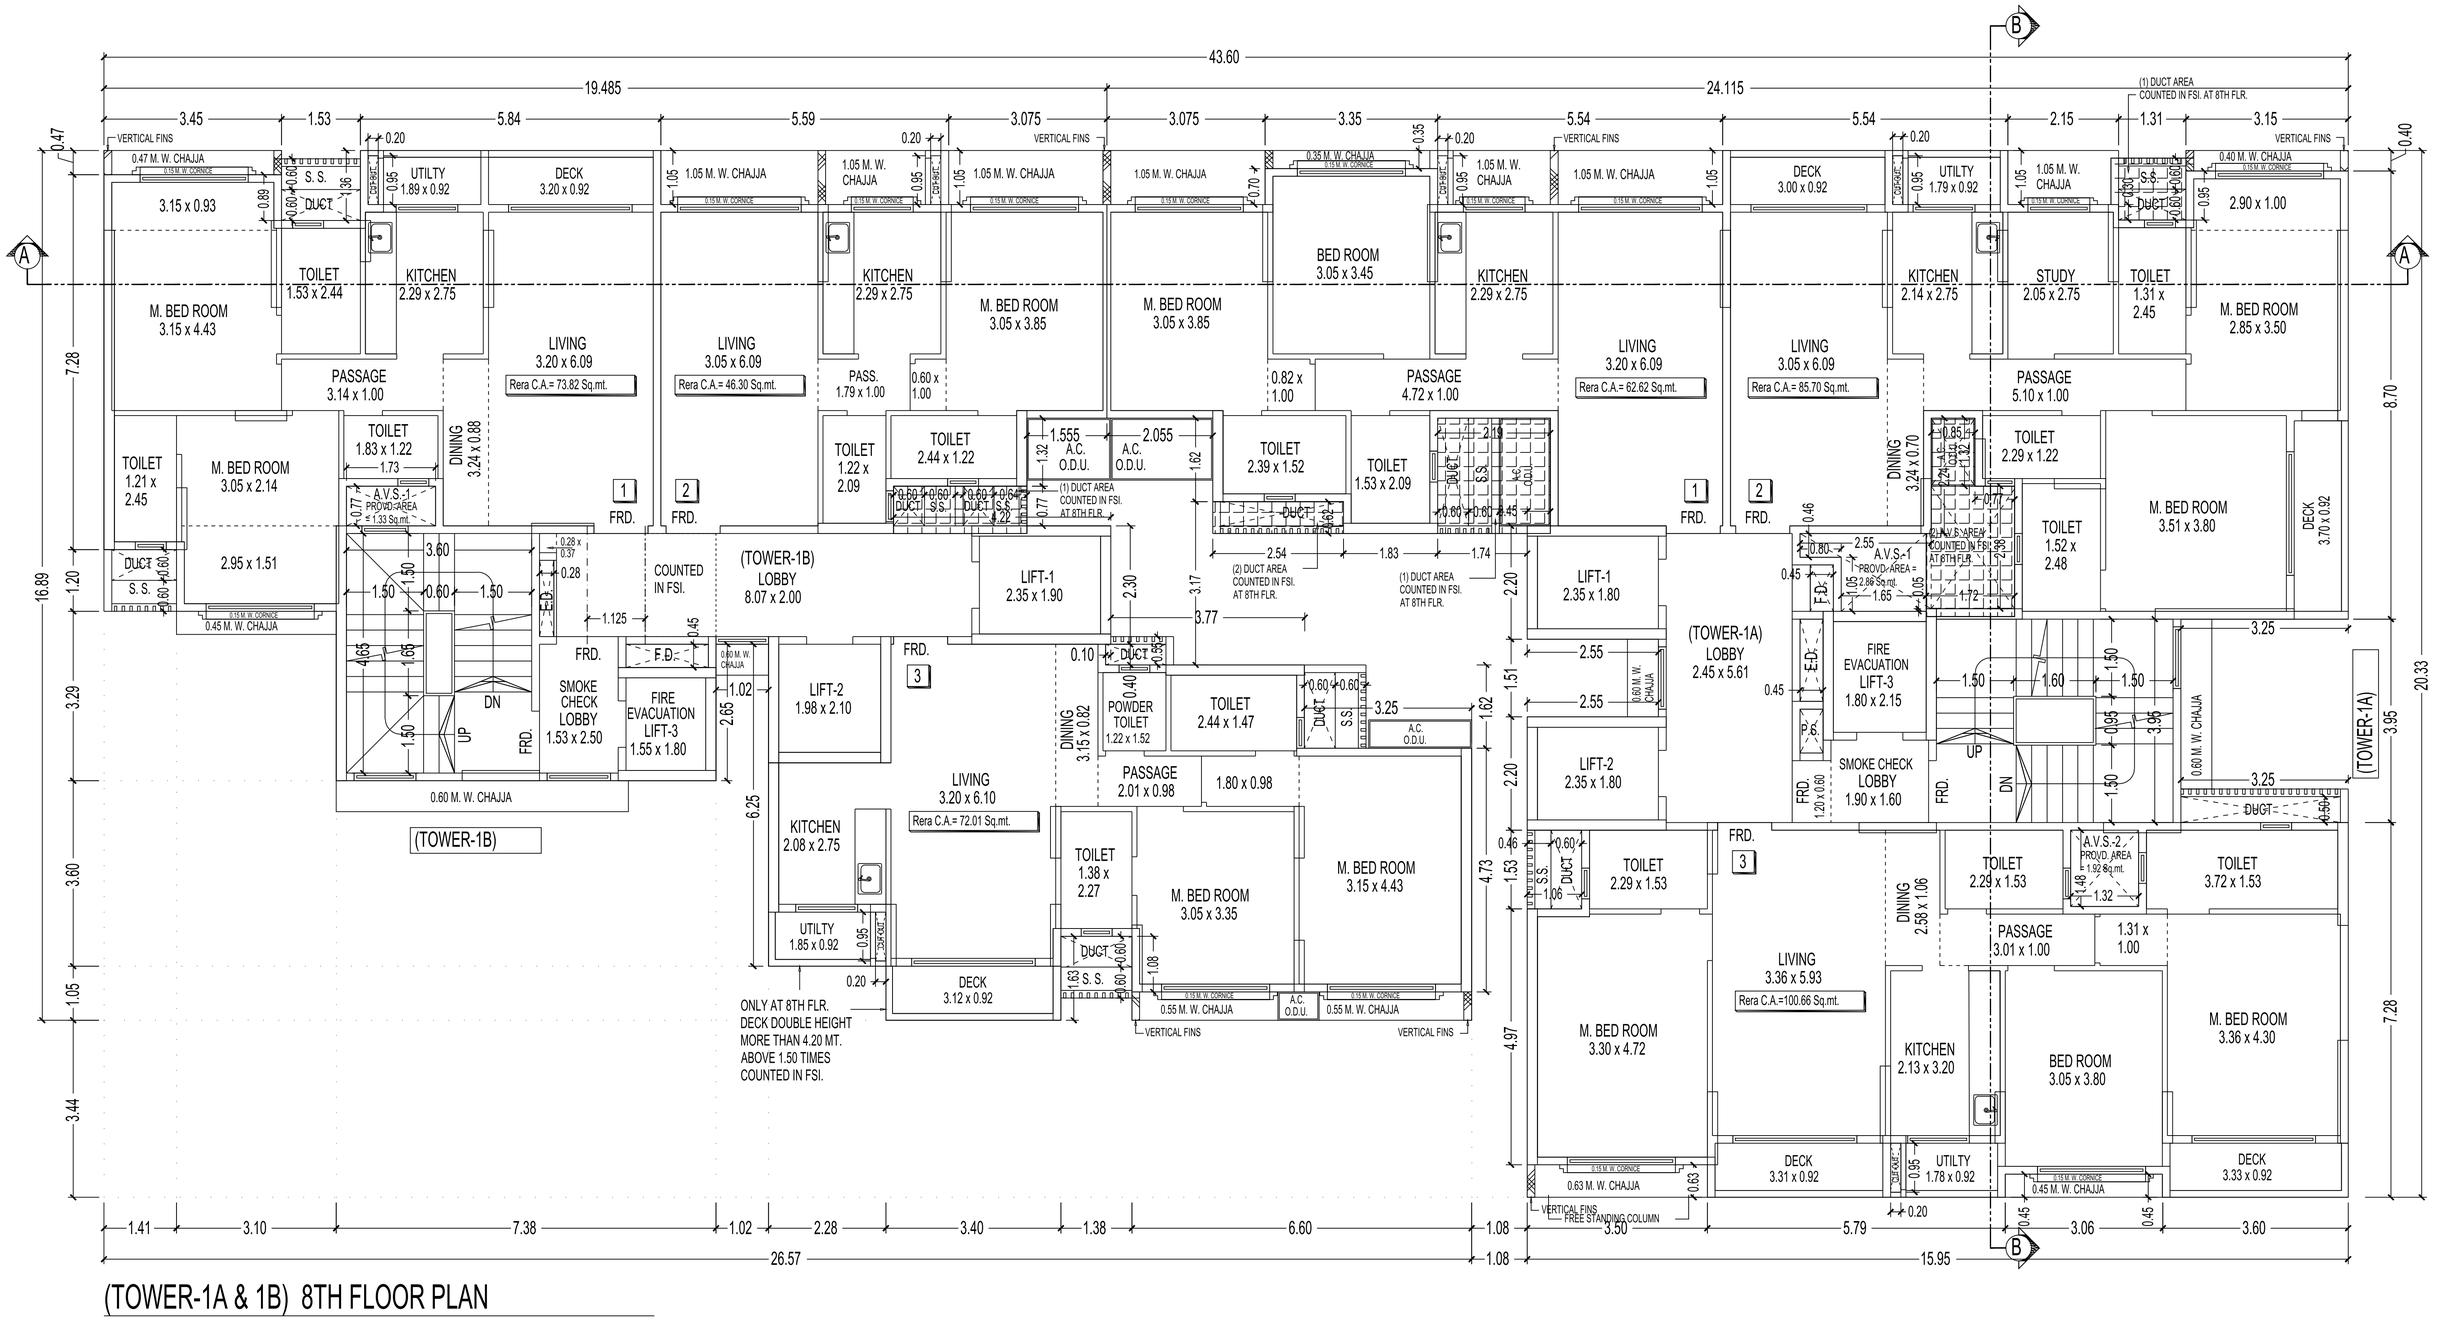


(TOWER-1A & 1B) 8TH FLOOR PLAN

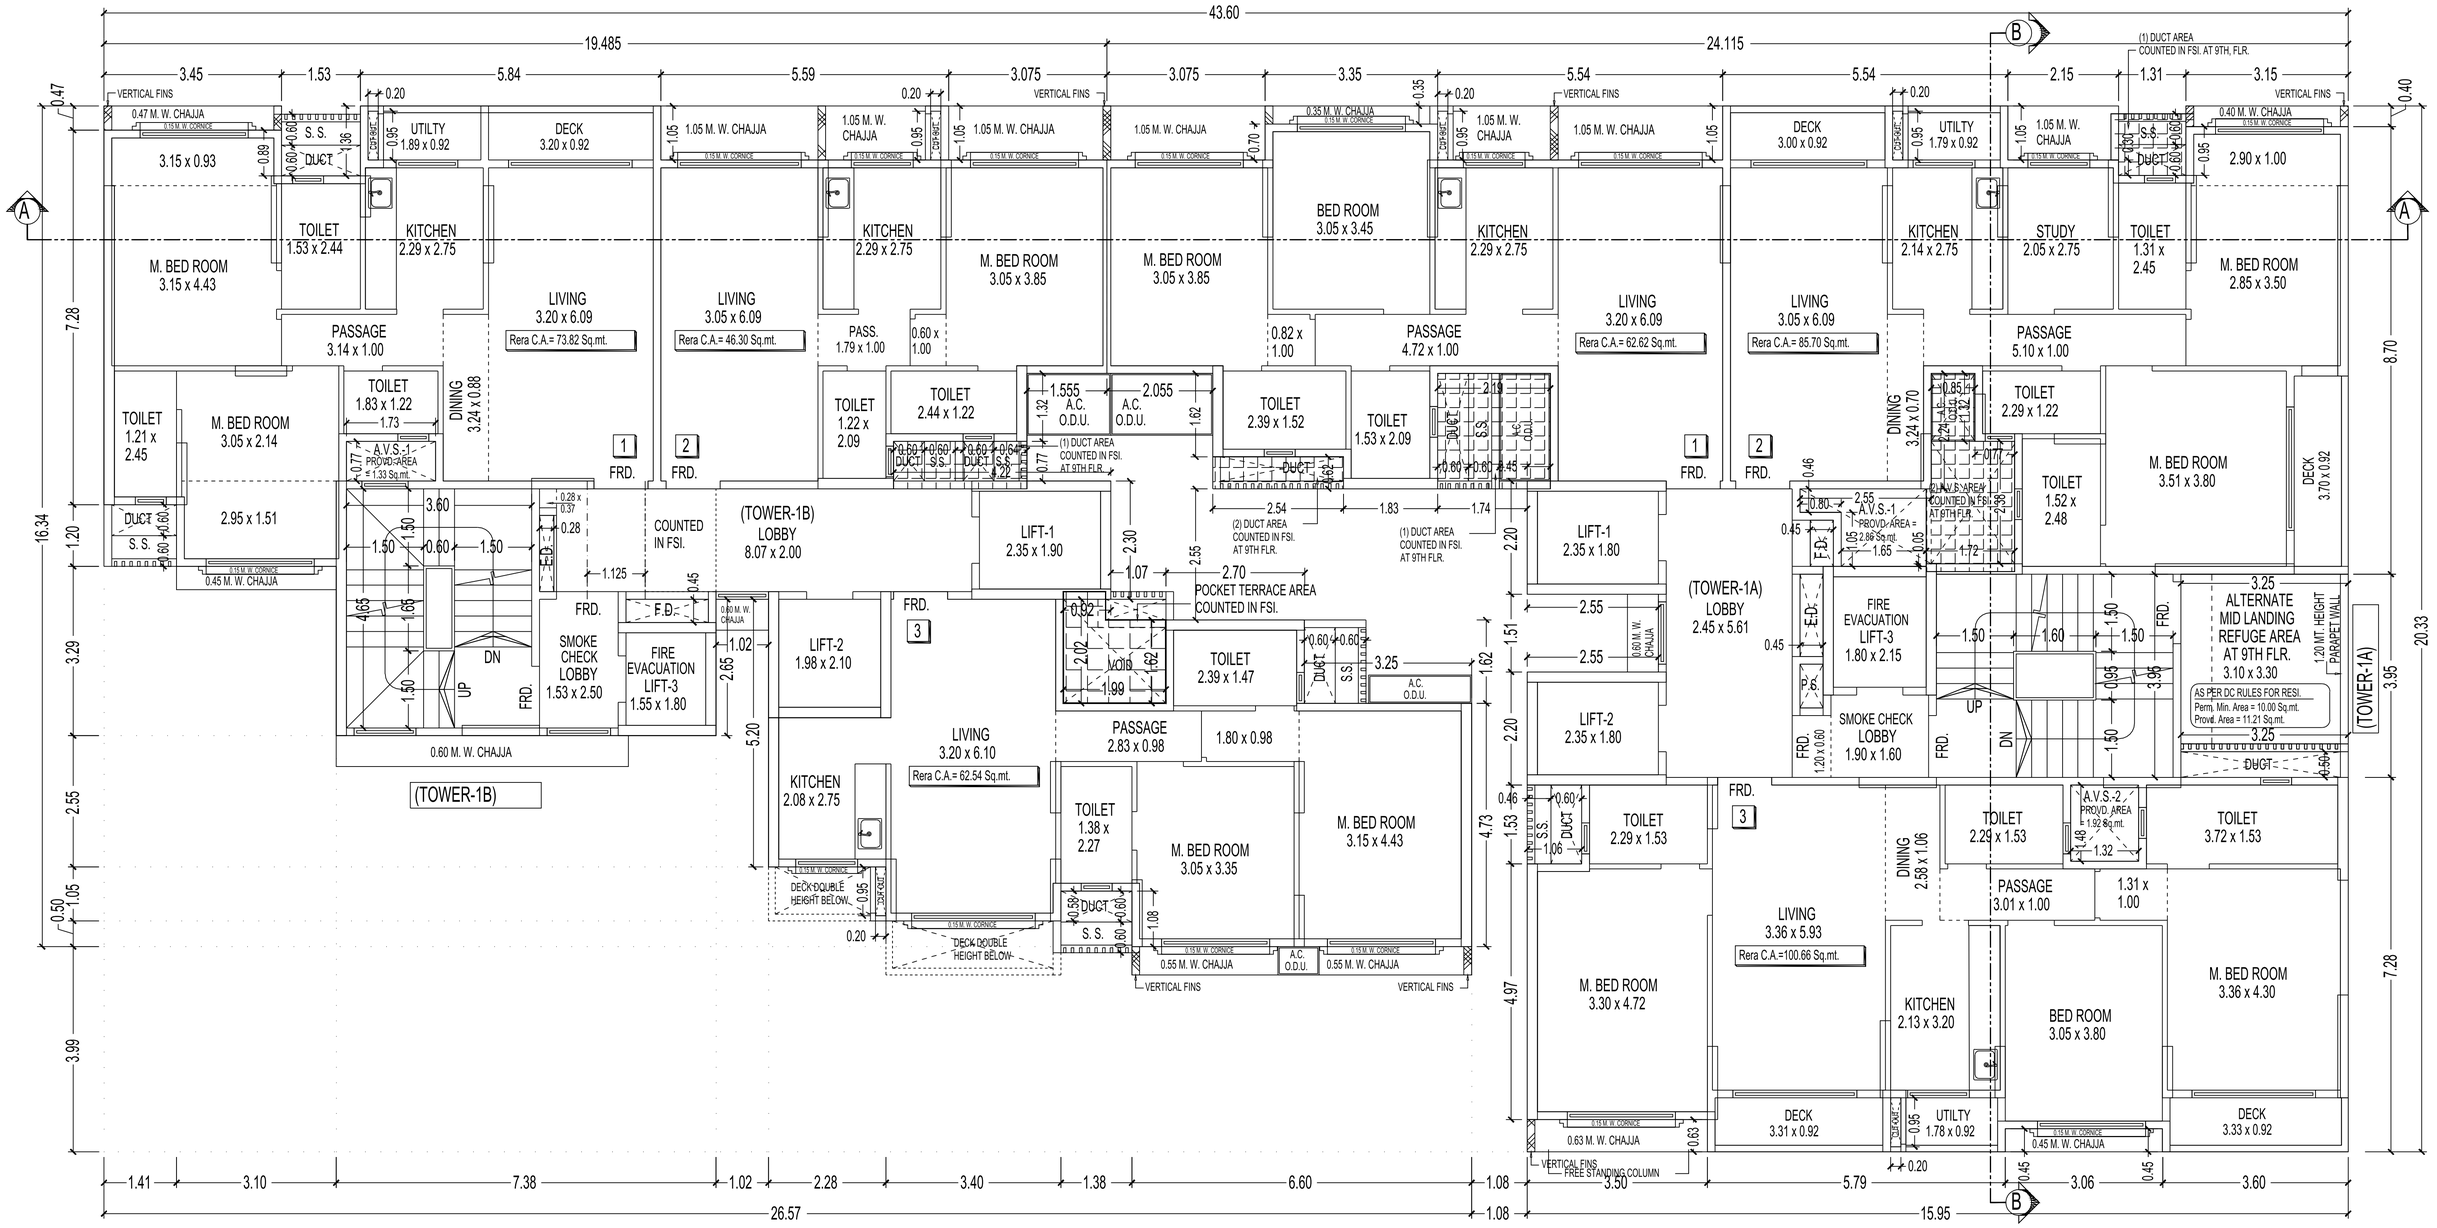

(TOWER-1A & 1B) 9TH FLOOR PLAN


SCALE - 1:100

SCALE - 1:100

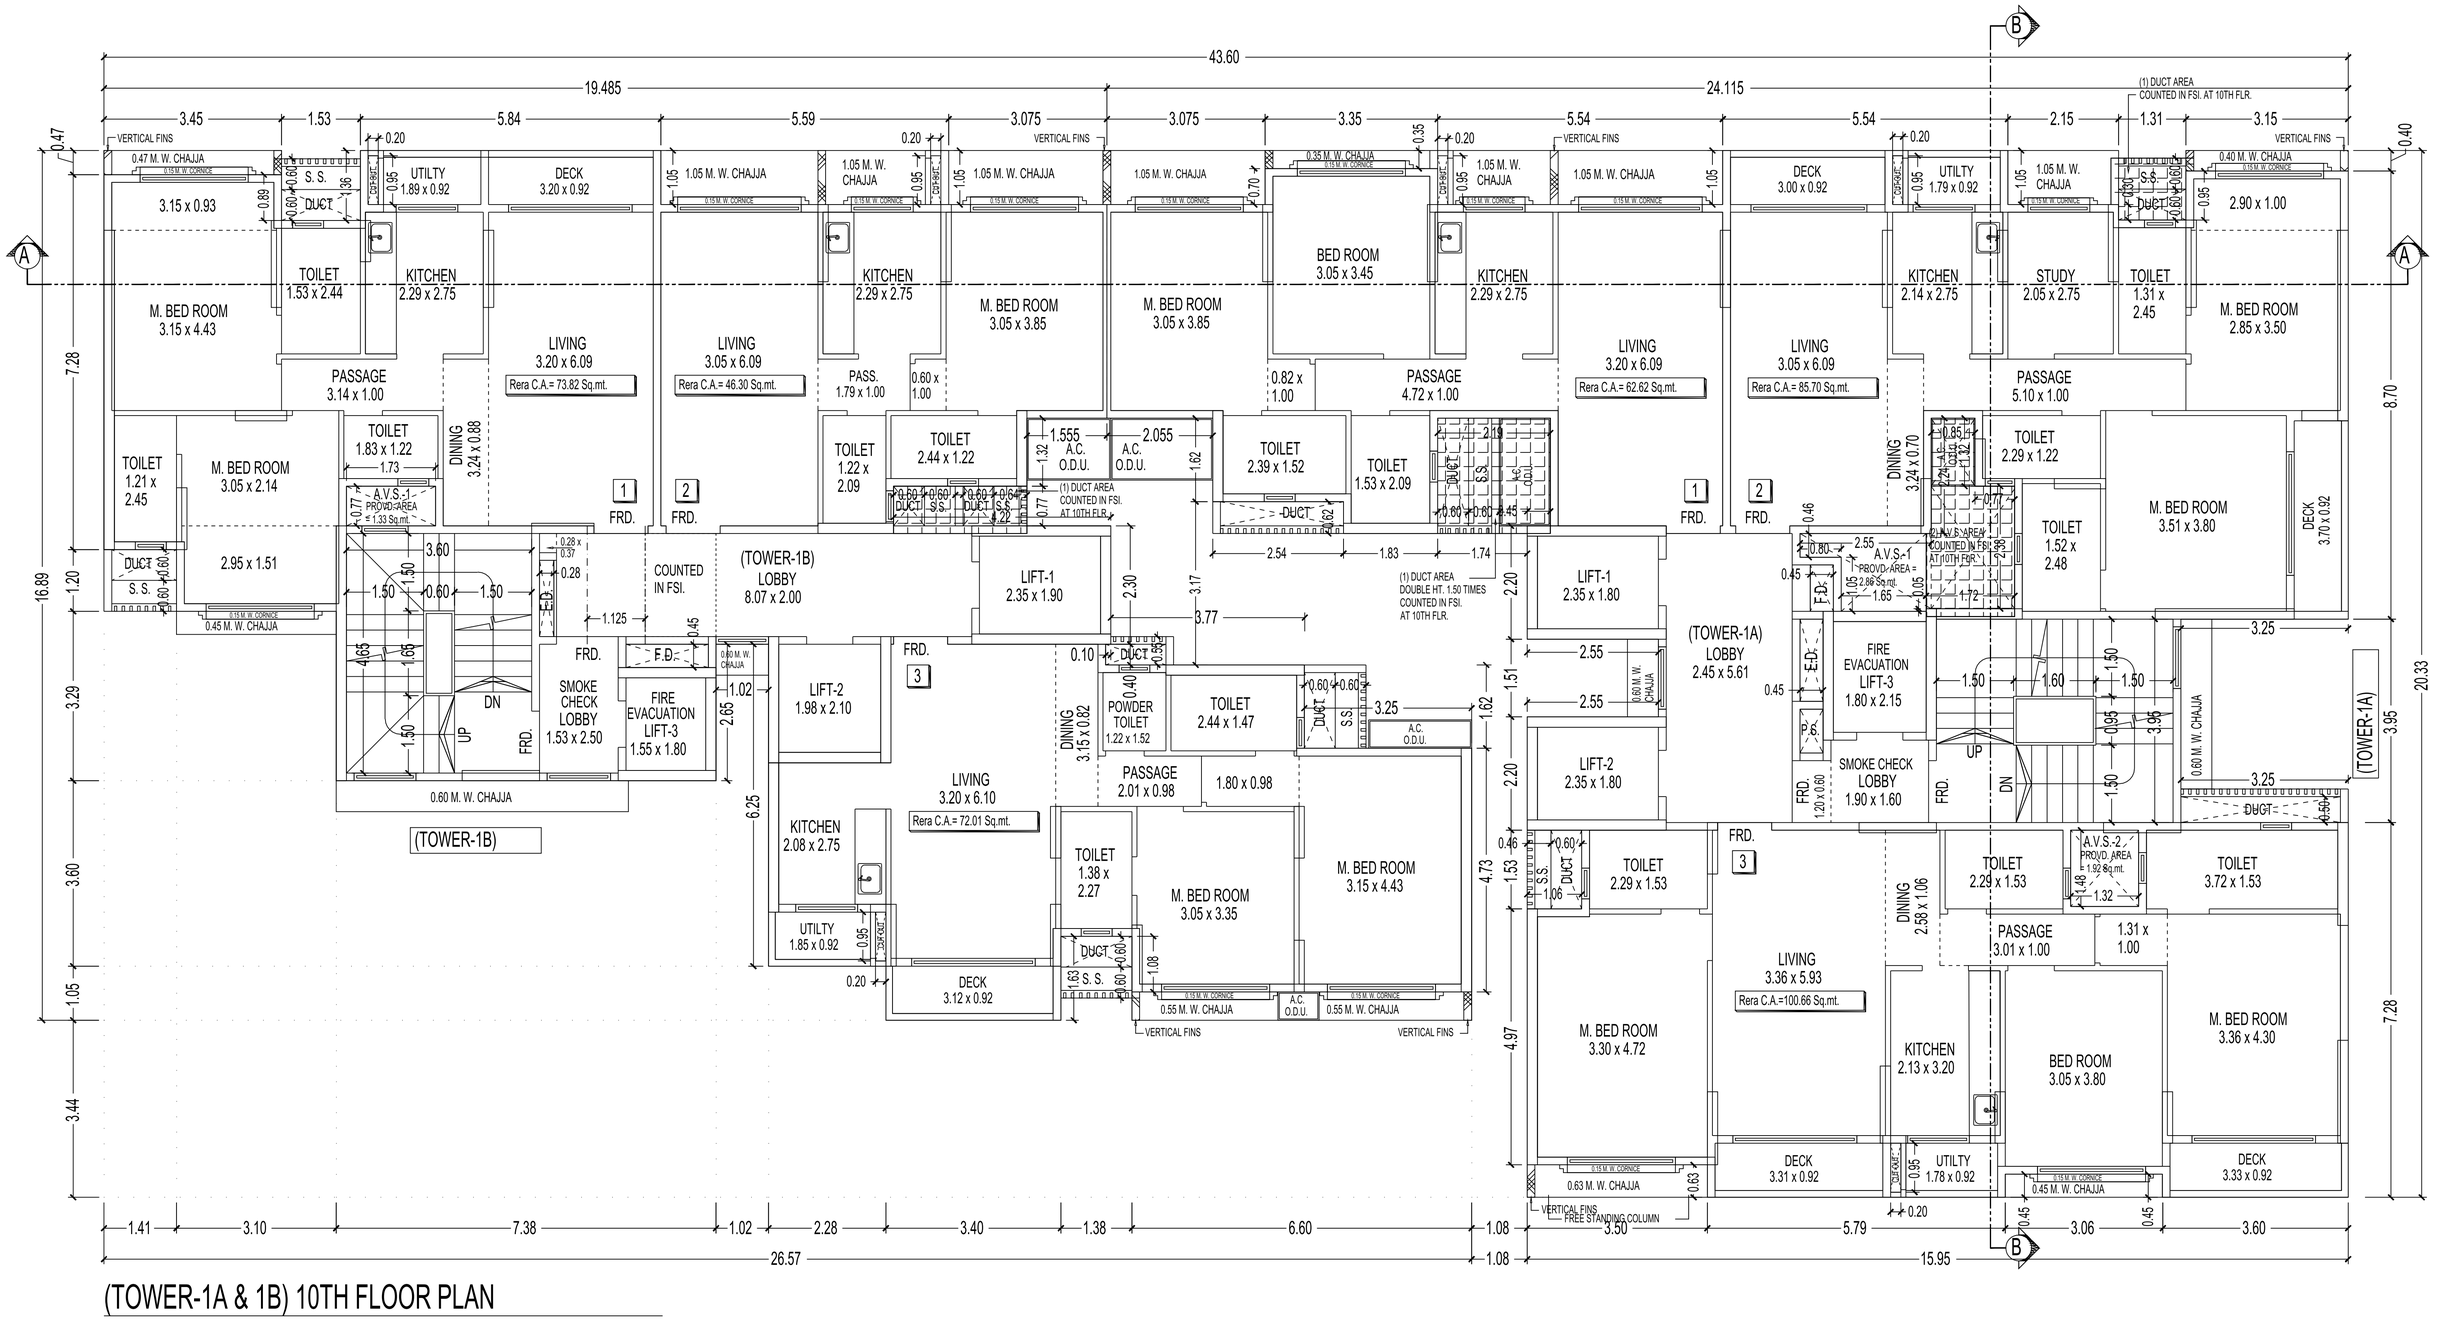

(TOWER-1A & 1B) 10TH FLOOR PLAN


SCALE - 1:100

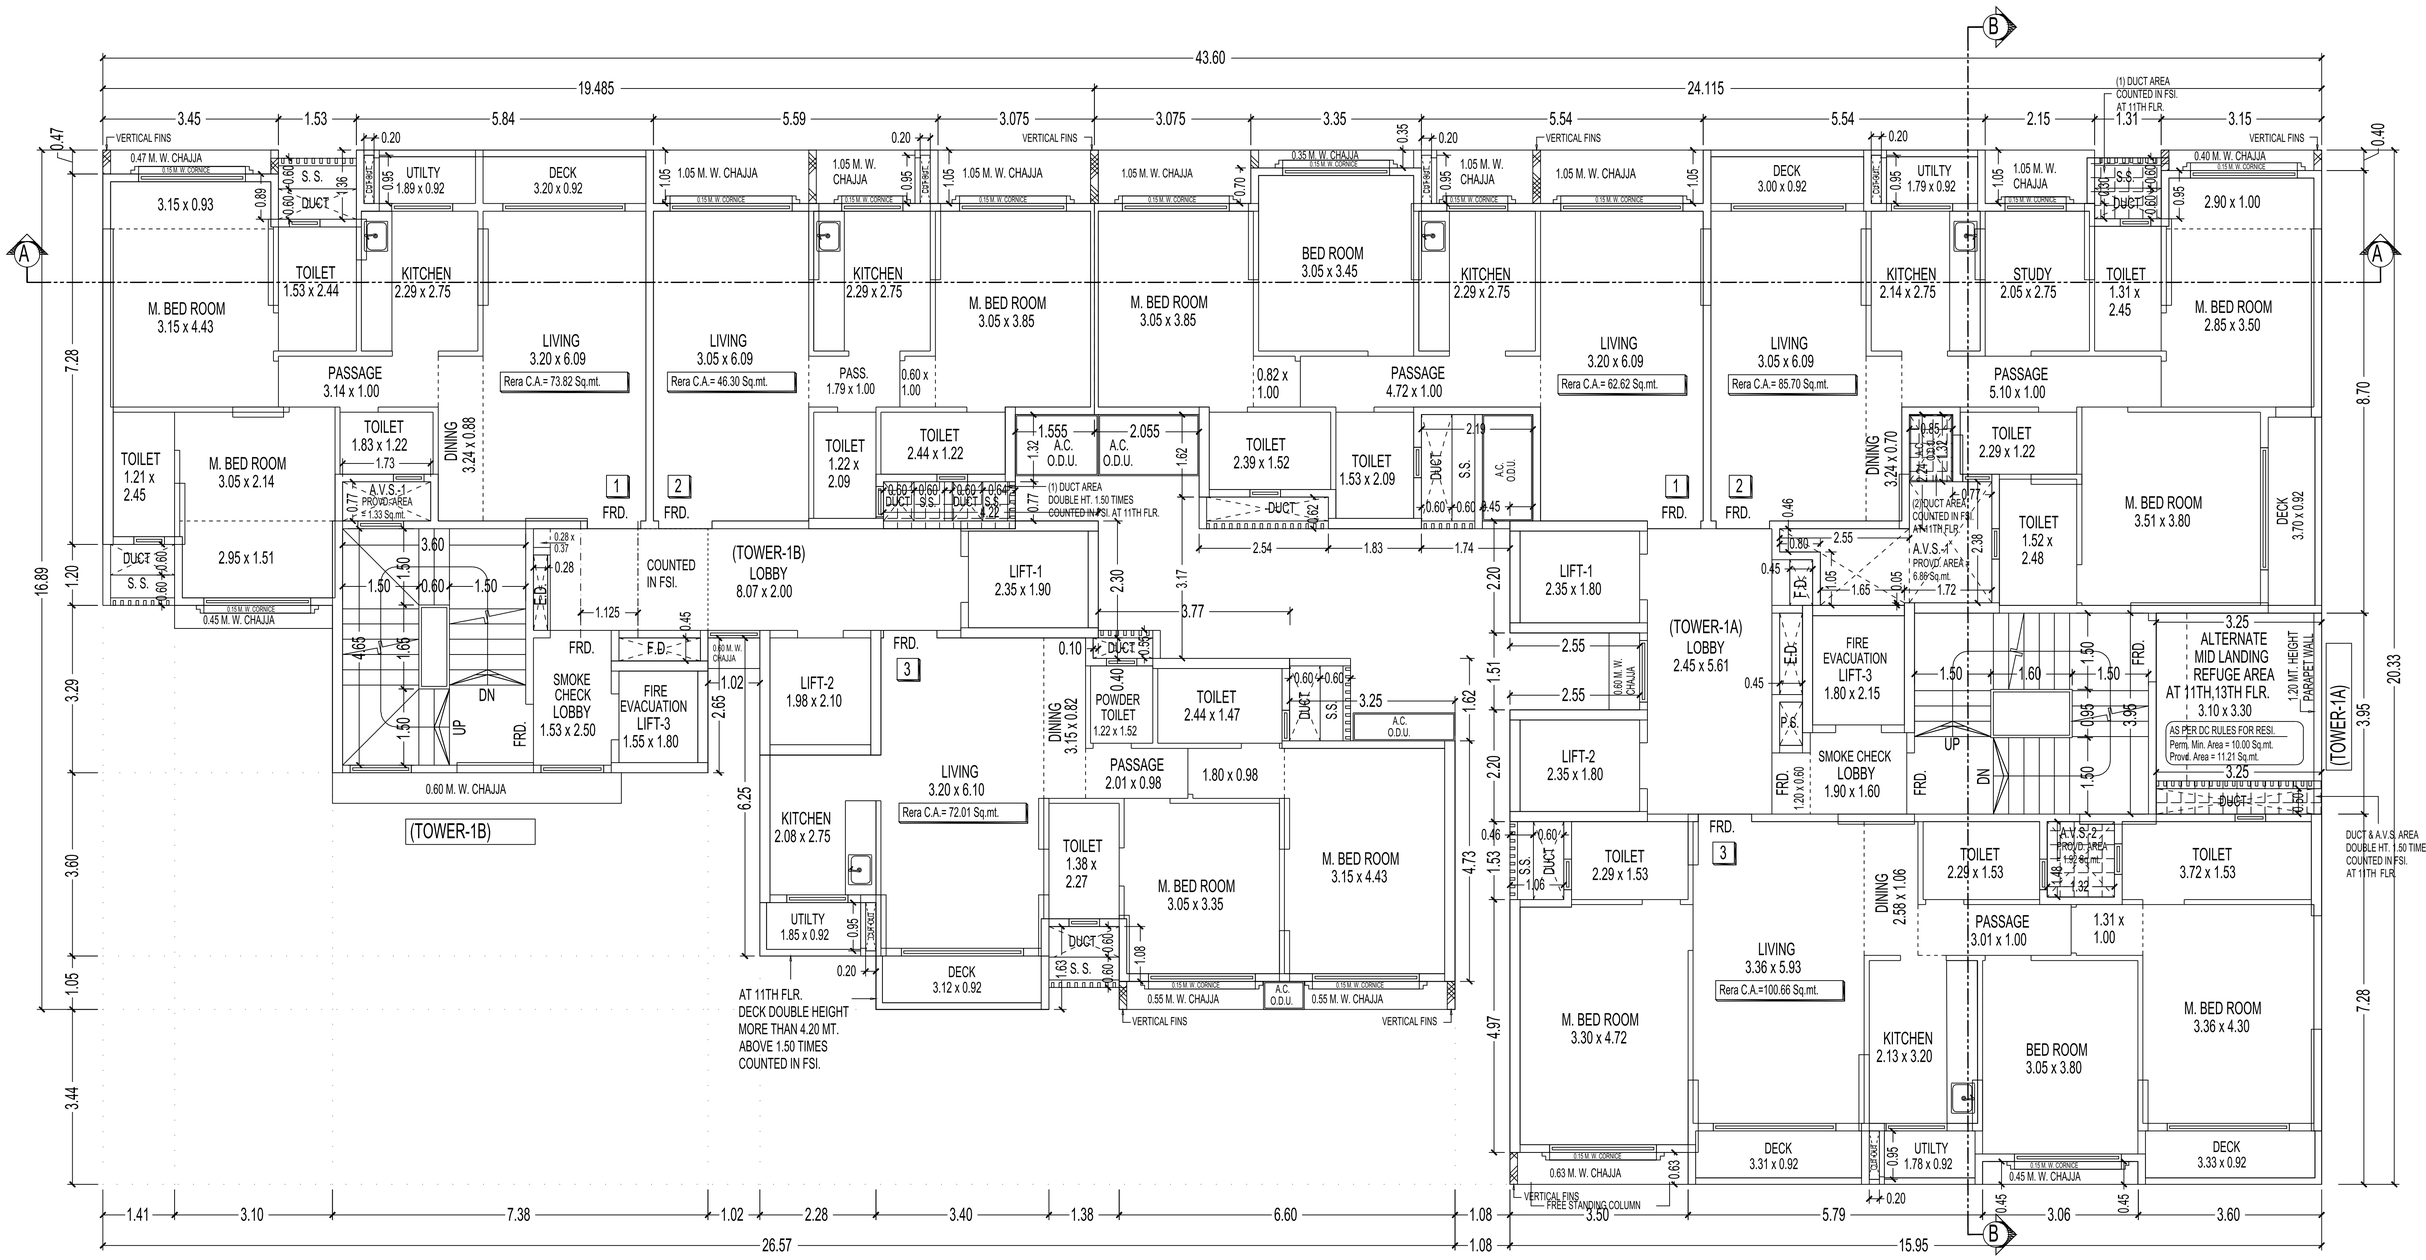

(TOWER-1A & 1B) 11TH FLOOR PLAN


SCALE - 1:100

SCALE - 1:100

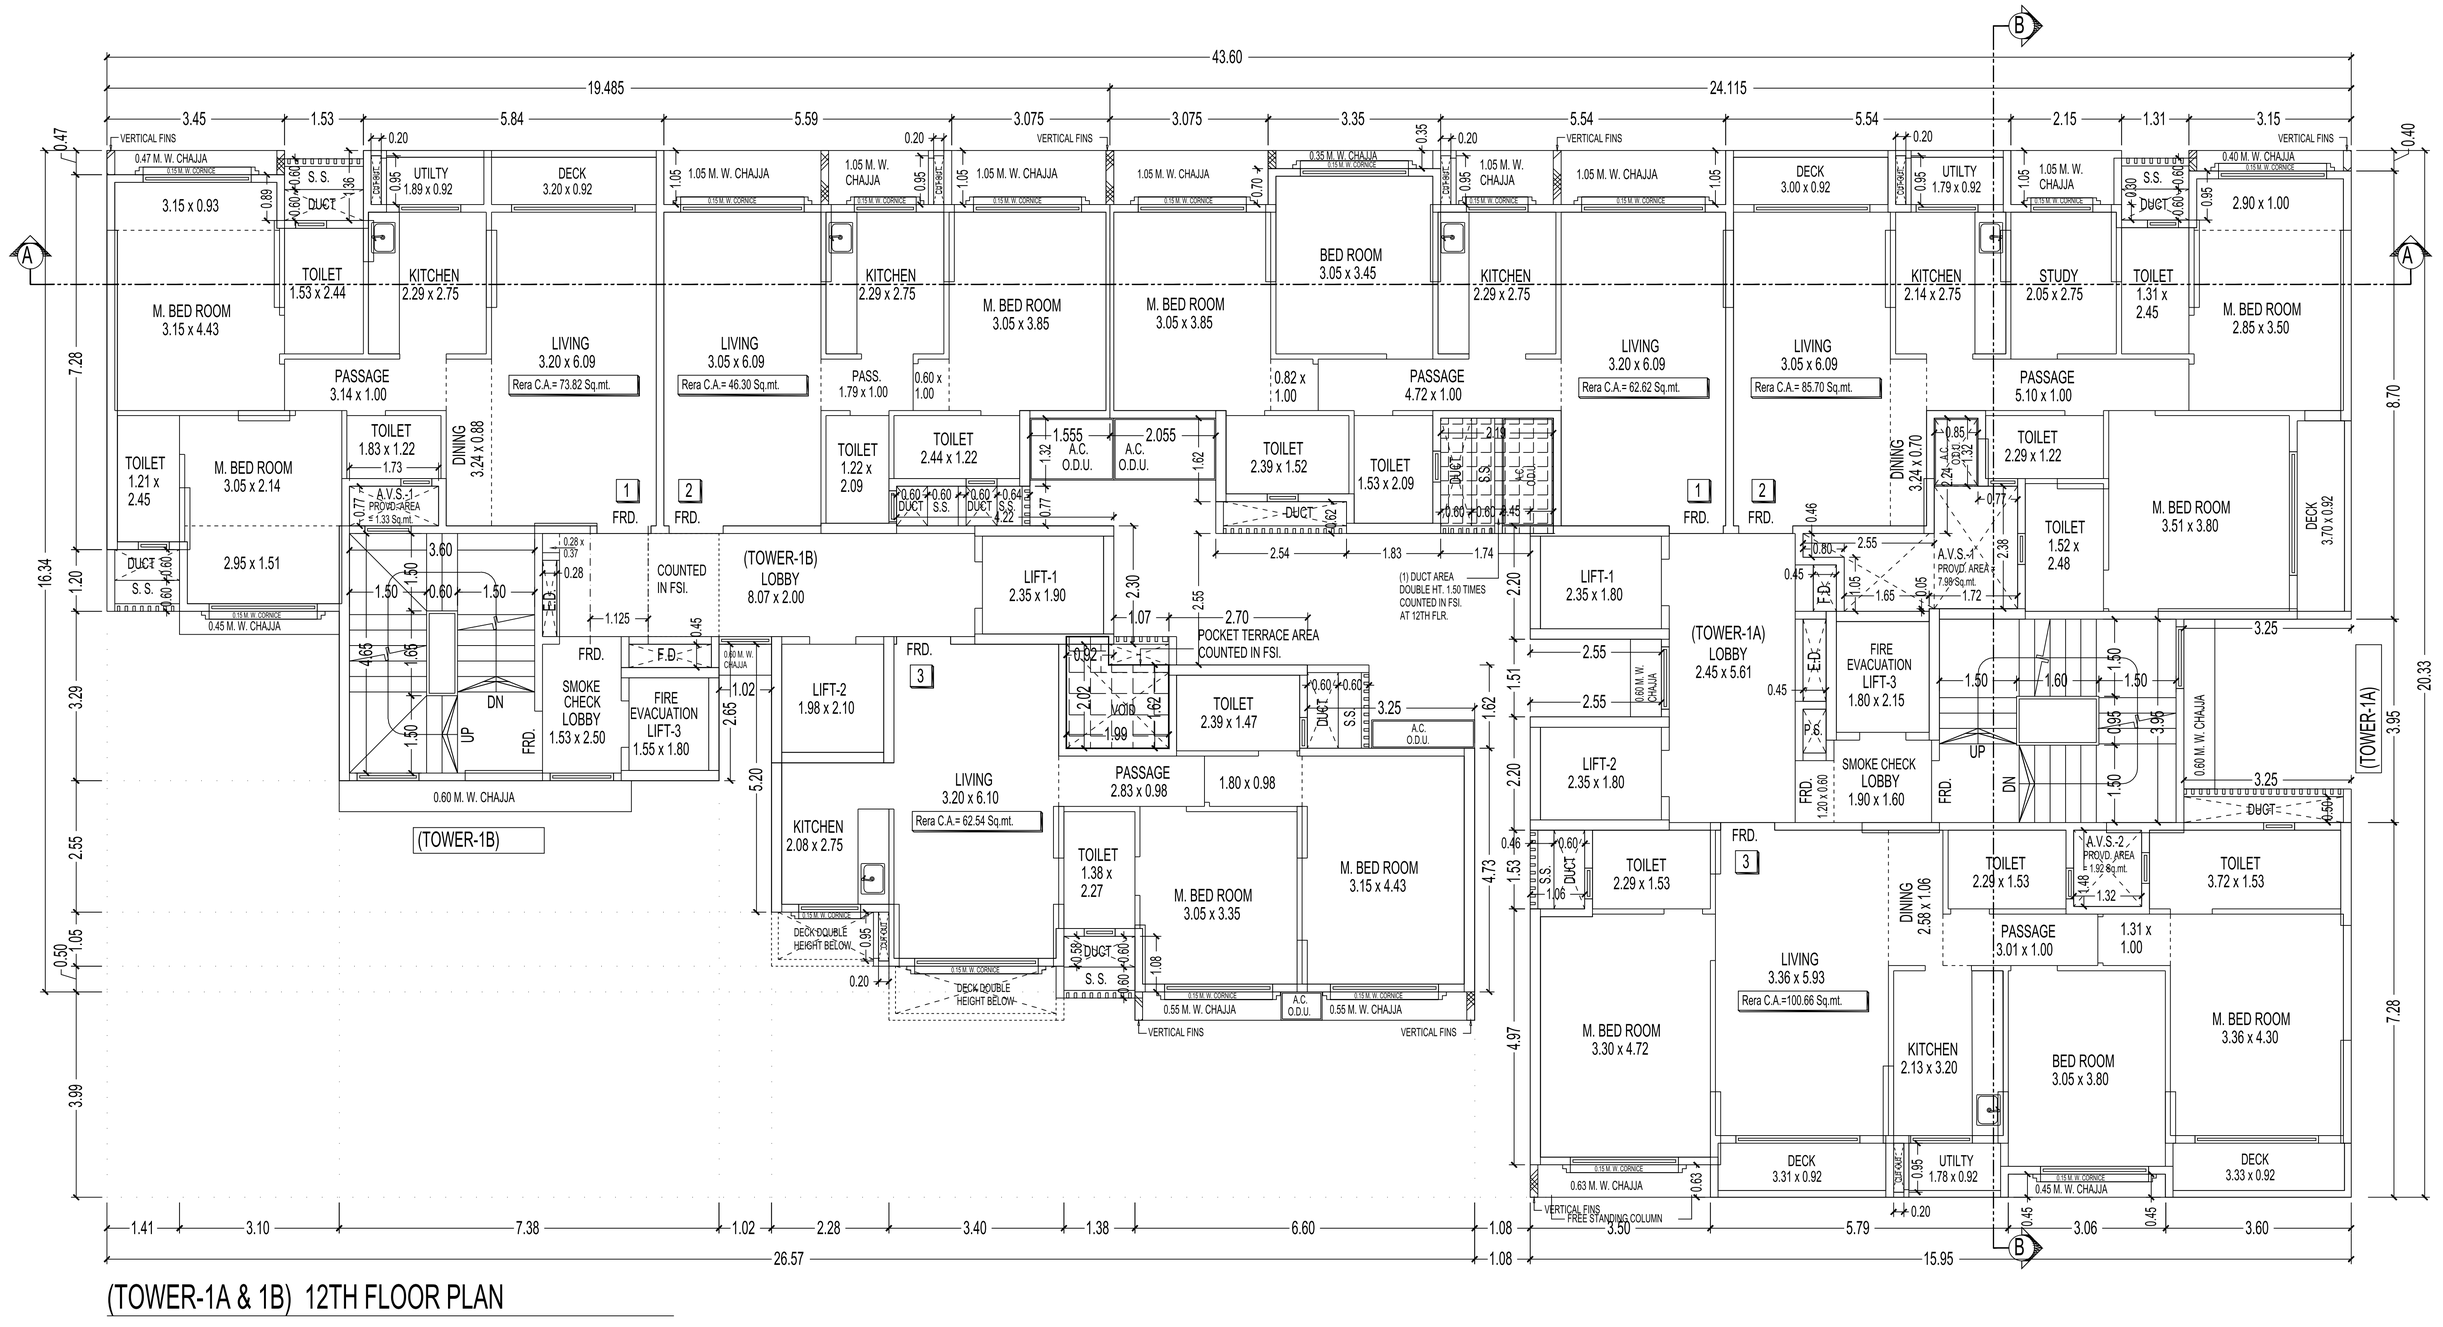

(TOWER-1A & 1B) 12TH FLOOR PLAN

SCALE - 1:100

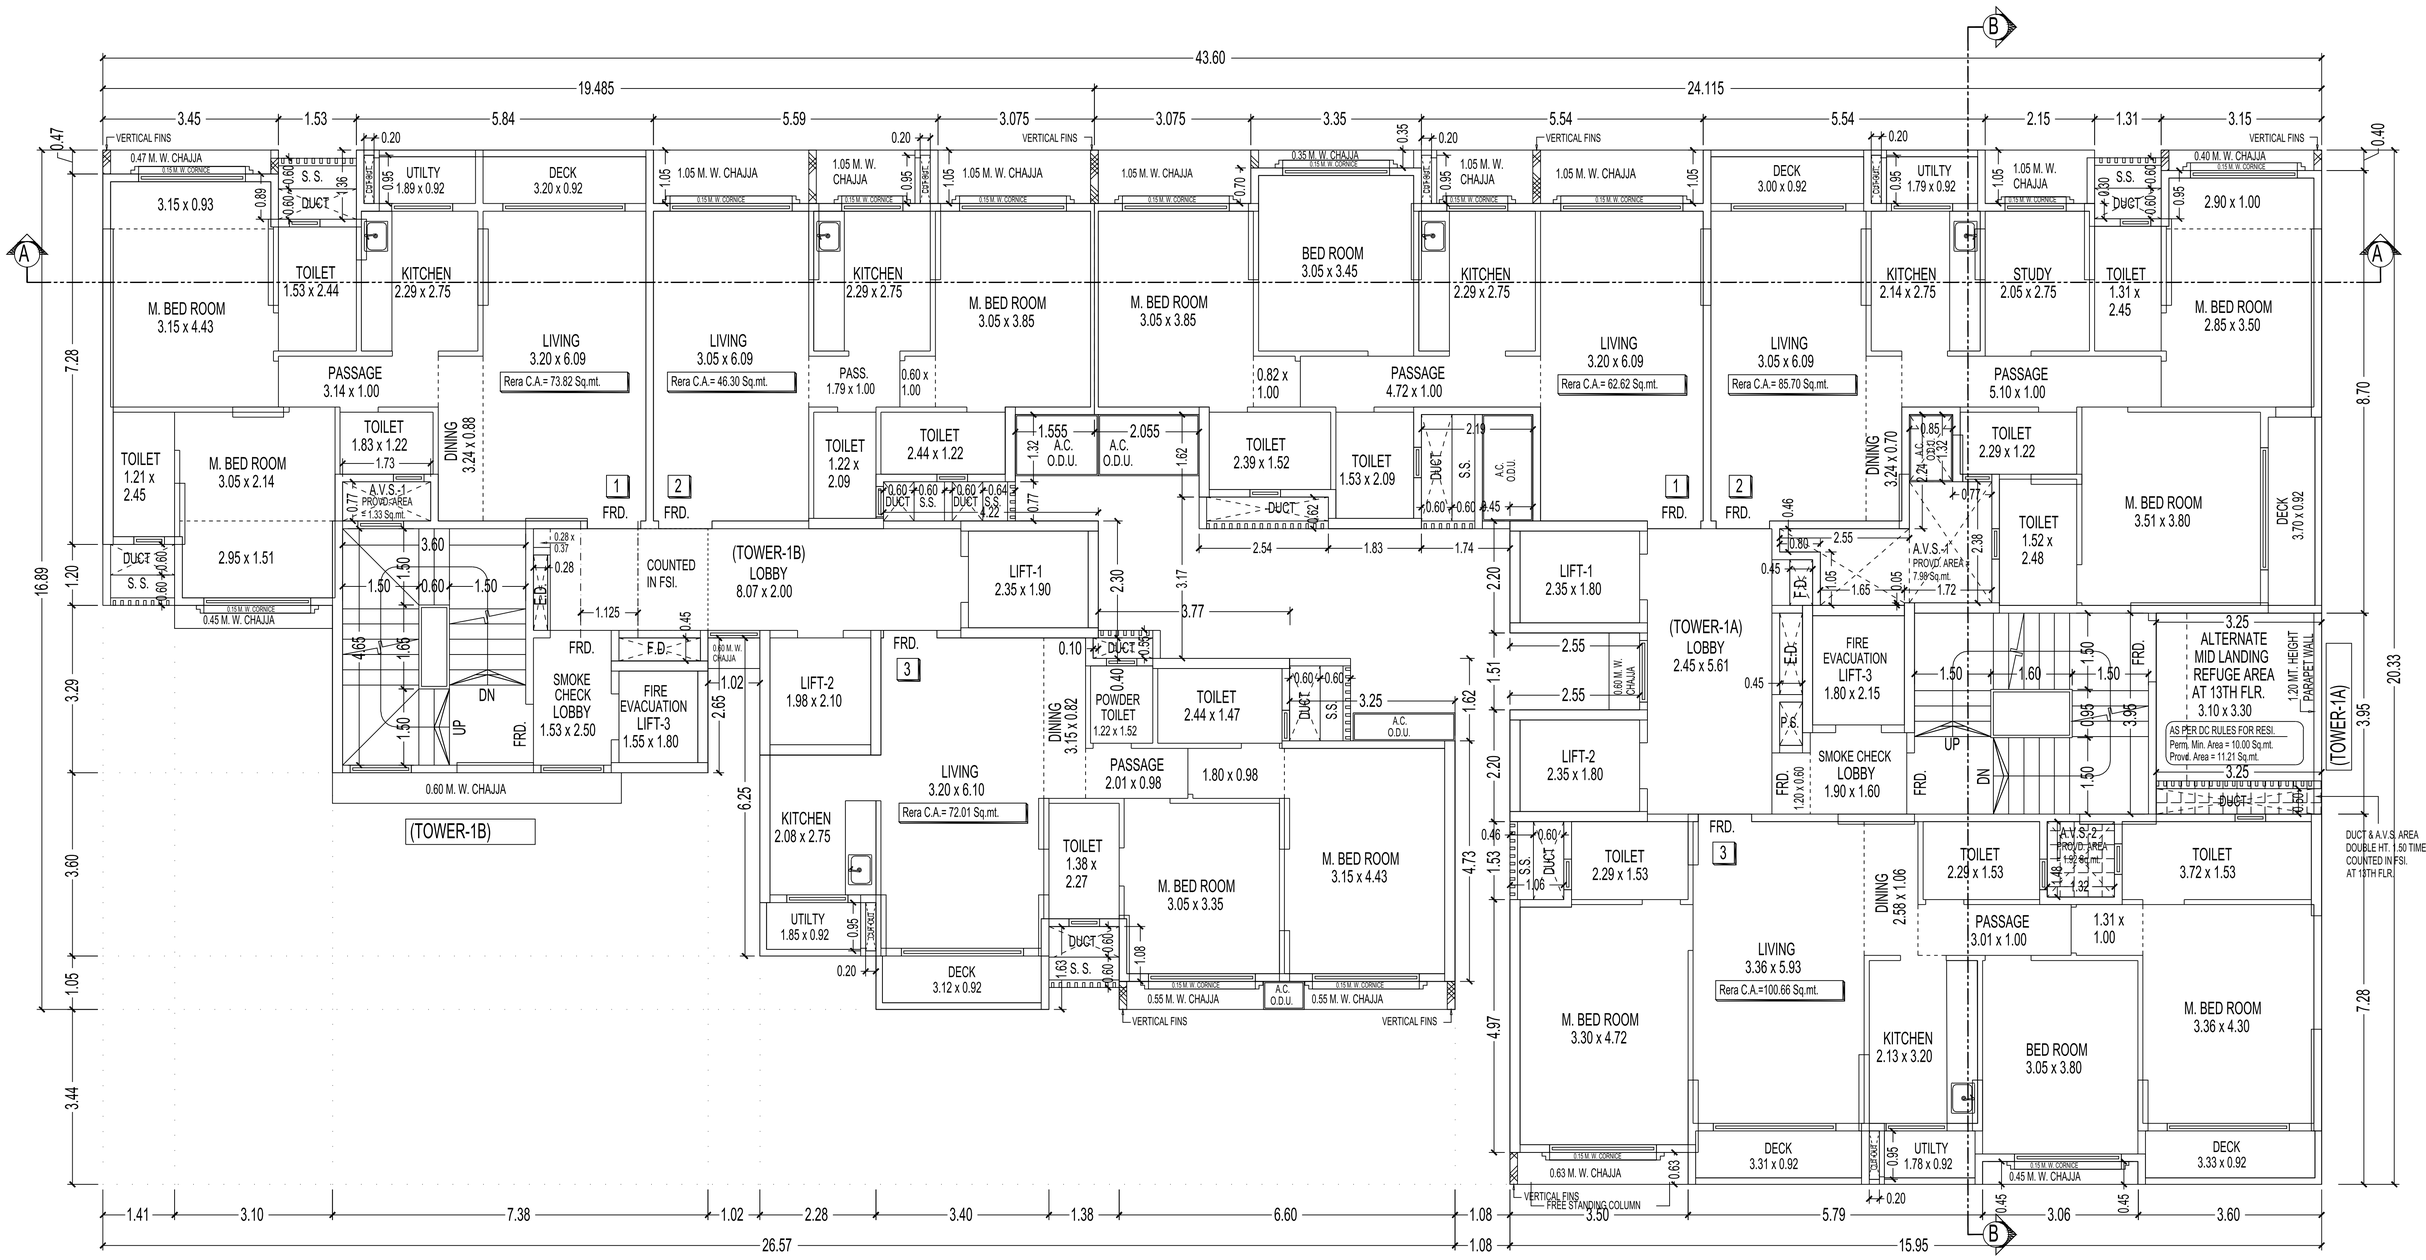


(TOWER-1A & 1B) 13TH FLOOR PLAN

SCALE - 1:100

FOR 14TH REFUGE FLOOR

SCALE - 1:100


SCALE - 1:100

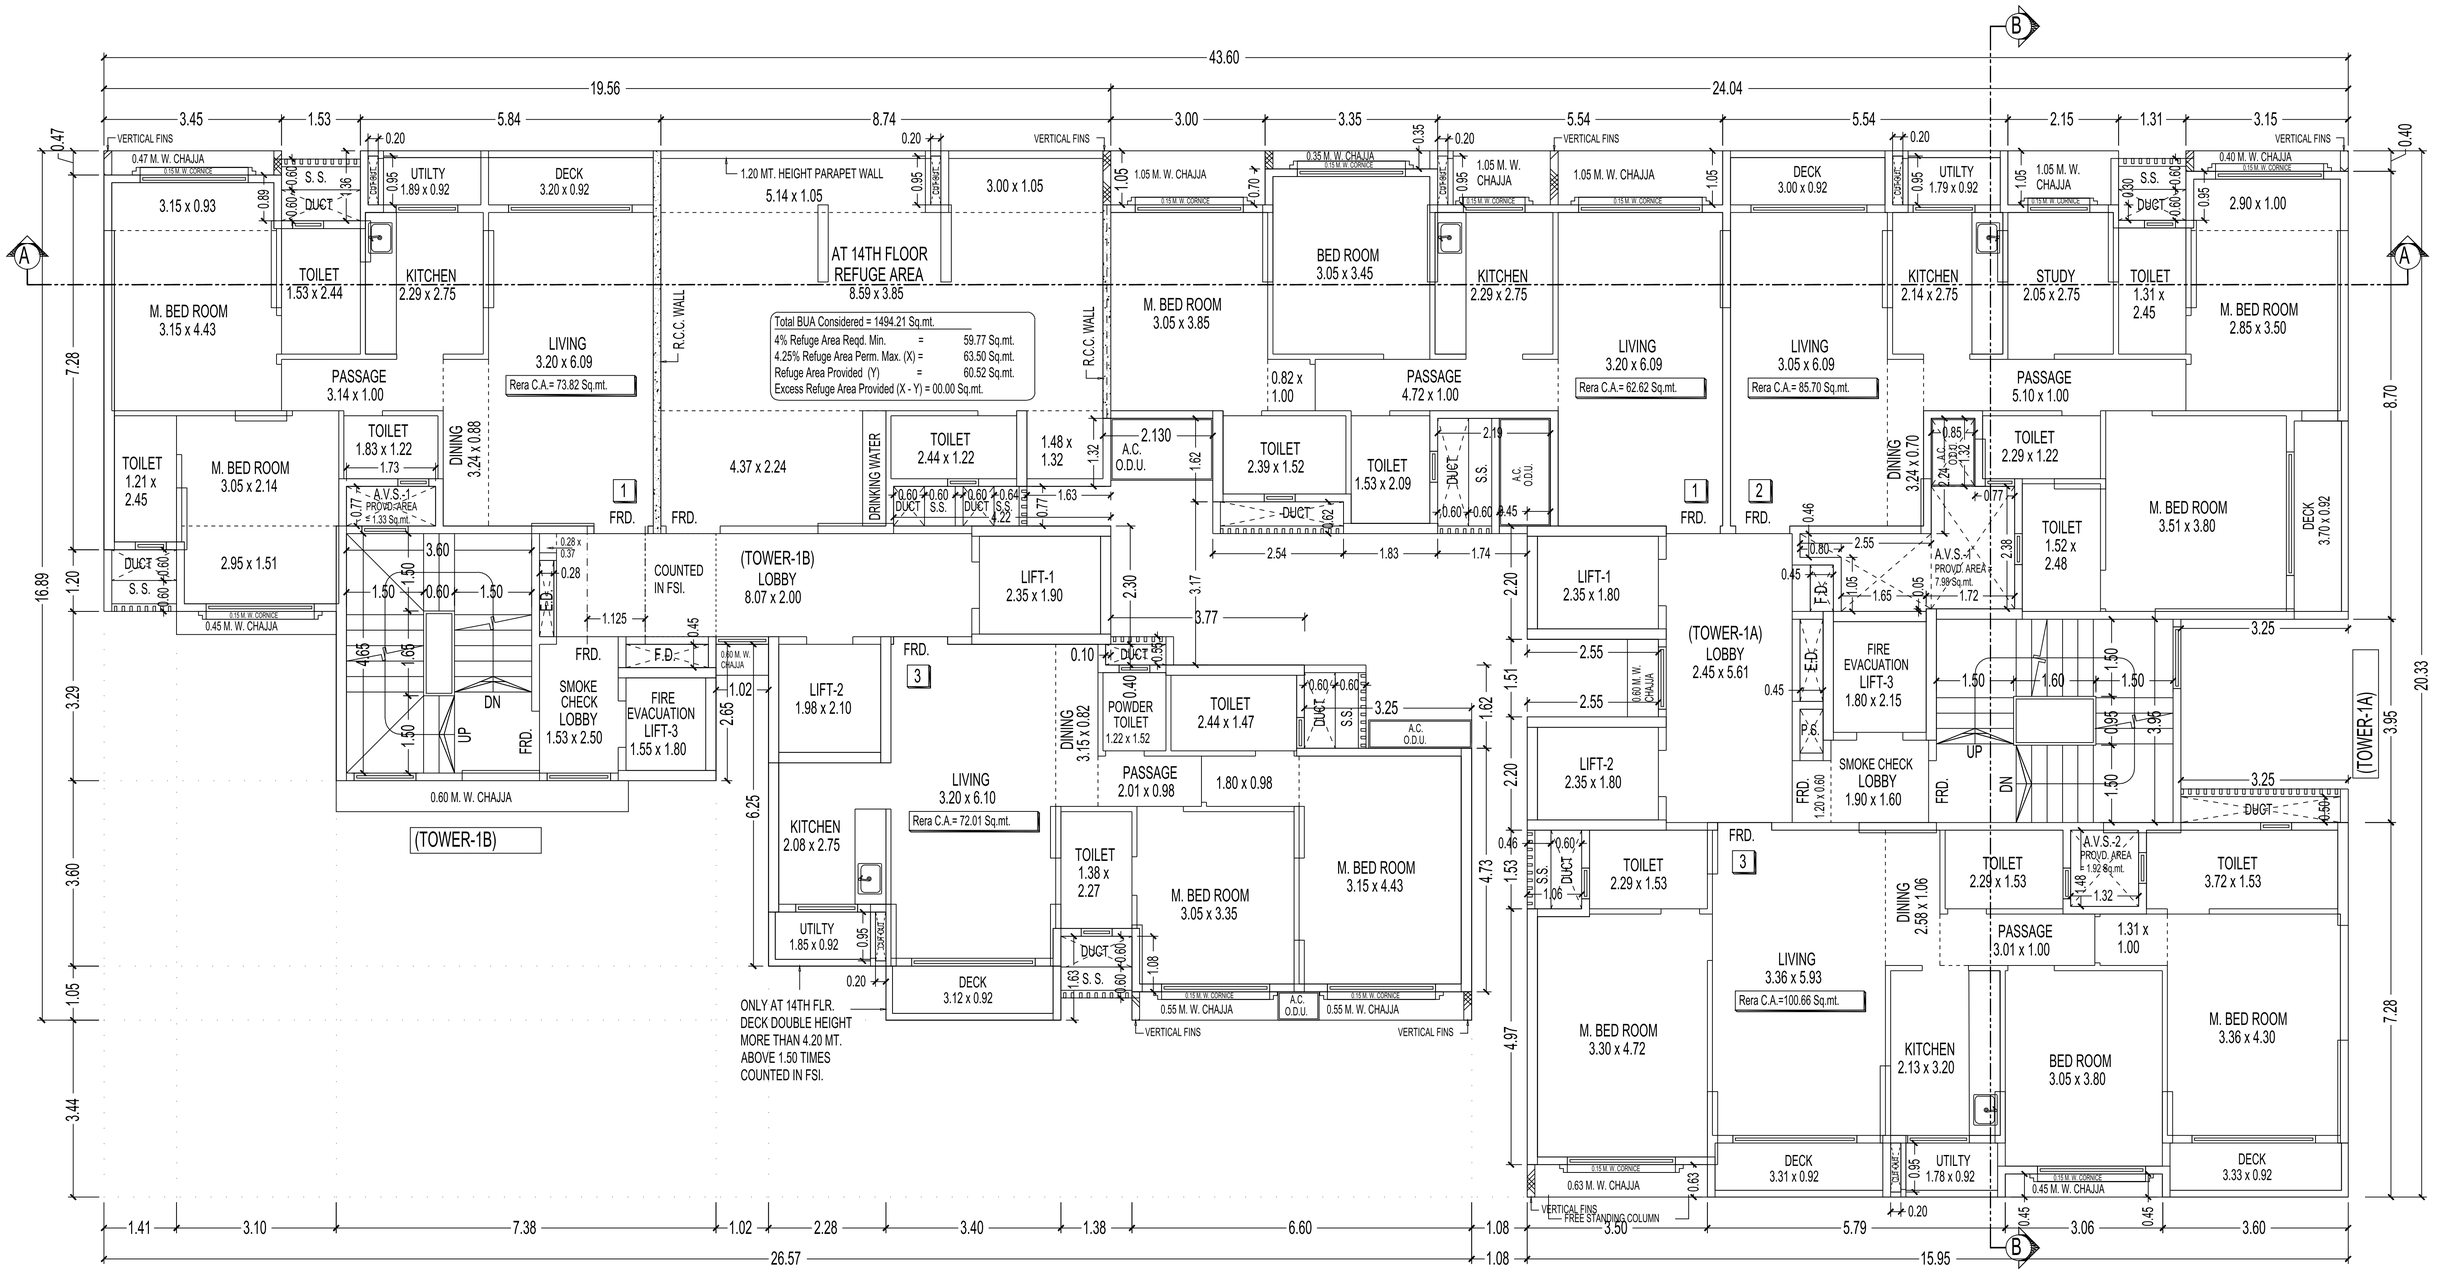

(TOWER-1A & 1B) 14TH REFUGE FLOOR PLAN


SCALE - 1:100

SCALE - 1:100

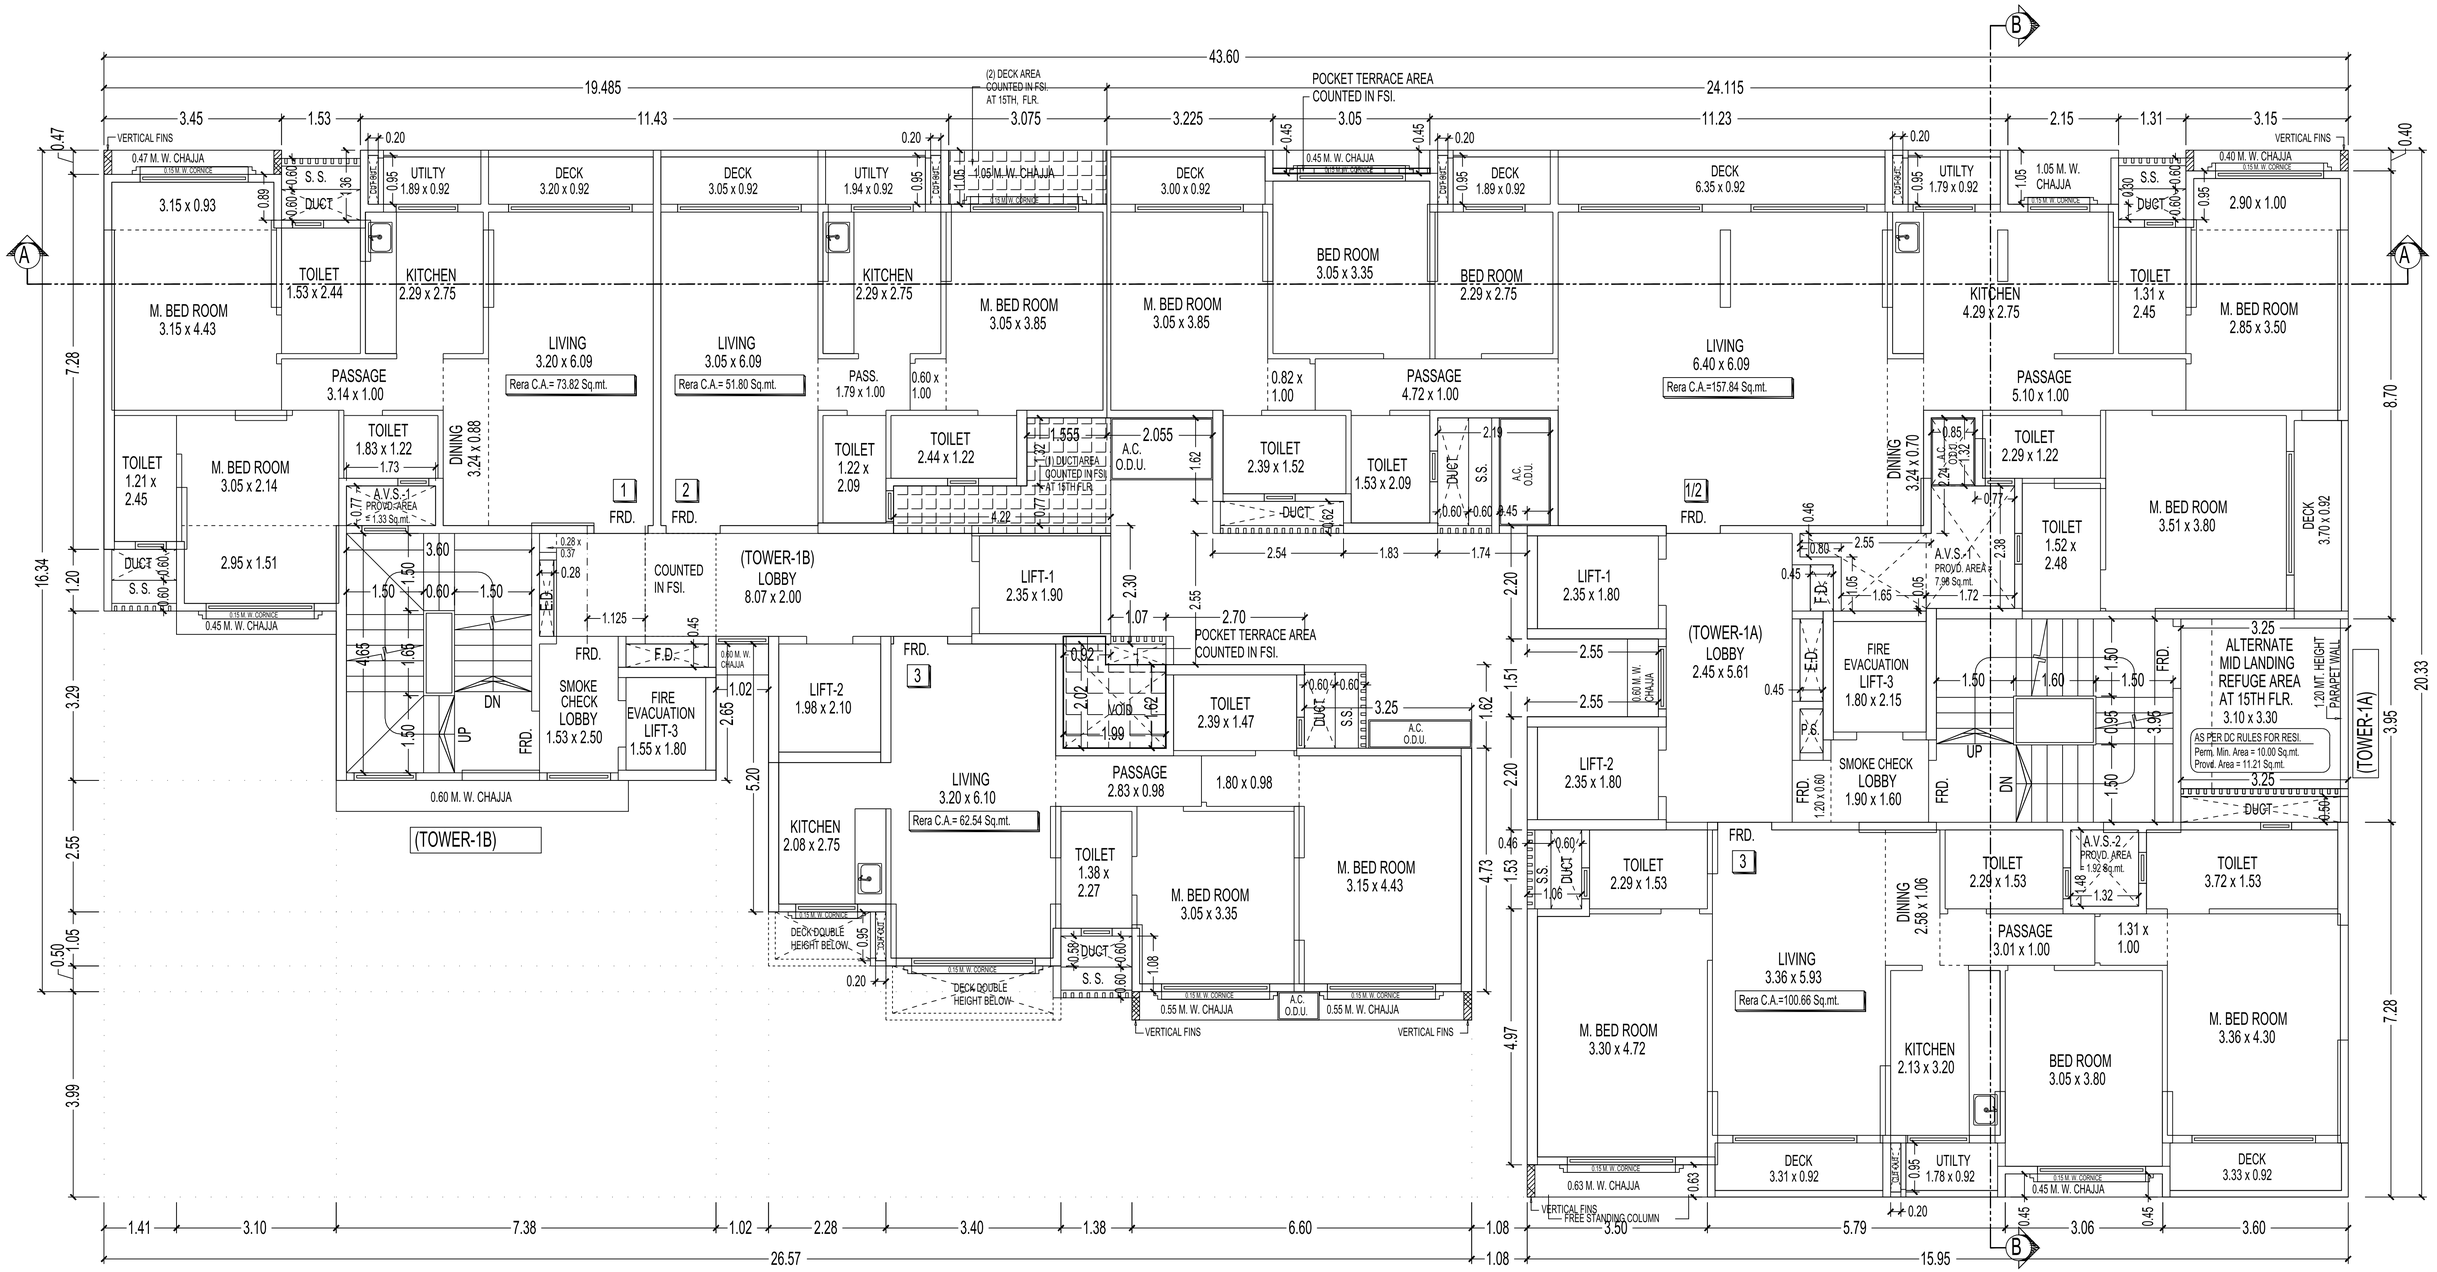

(TOWER-1A & 1B) 15TH FLOOR PLAN

SCALE - 1:100

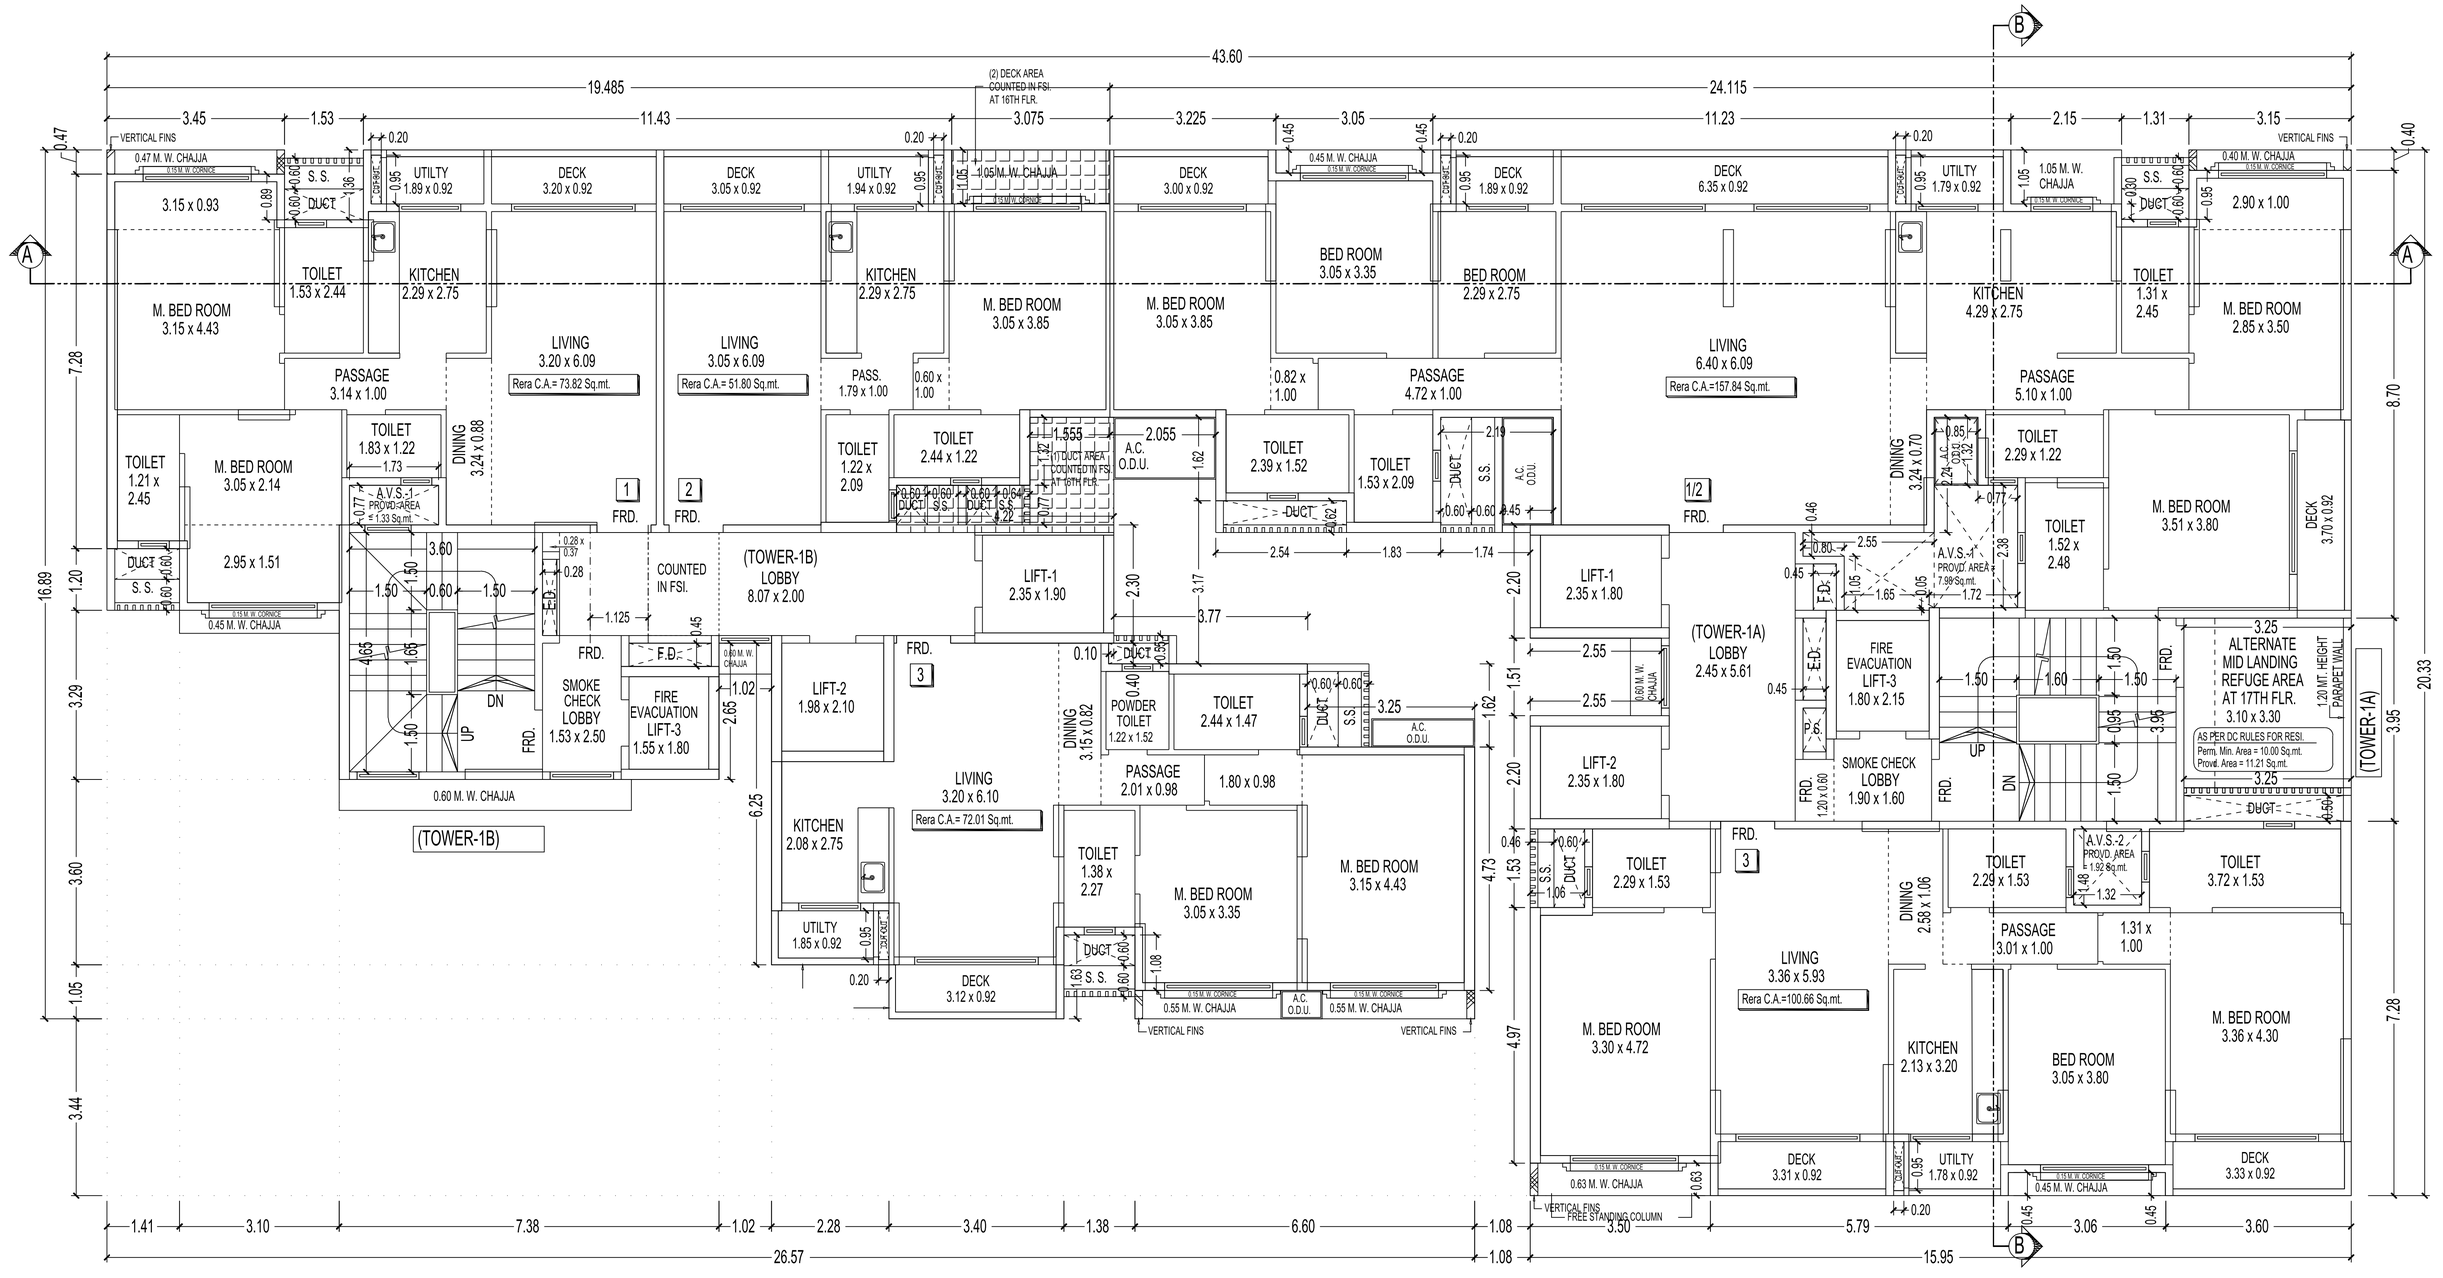

(TOWER-1A & 1B) 16TH FLOOR PLAN