4TH FLOOR PLAN

SCALE :- 1:100

WING - A

WING - B

REHAB LIVING 3.35 x 4.27 R.A.=68.29 SQ.MT.

REHAB LIVING 3.05 x 5.01 R.A.=52.78 SQ.MT.

REHAB LIVING 3.15 x 5.06 R.A.=57.90 SQ.MT.

REHAB LIVING 3.08 x 4.41 R.A.=52.10 SQ.MT.

REHAB LIVING 4.00 x 3.05 R.A.=34.07 SQ.MT.

AH TO BMC LIVING 3.05 x 4.27 R.A.=56.48 SQ.MT.

AH TO BMC LIVING 3.05 x 4.27 R.A.=56.48 SQ.MT.

AH TO BMC LIVING 6.17 x 2.69 R.A.=55.44 SQ.MT.

LOBBY 13.83 x 1.80

LOBBY 5.71 x 2.12

SMOKE CHECK LOBBY 1.88 x 1.50

SMOKE CHECK LOBBY 1.70 x 2.08

FIREMAN EVACUATION LIFT 1.80 x 1.80

FIREMAN EVACUATION LIFT 1.82 x 3.02

LIFT 4.56 x 2.00

LIFT 3.47 x 1.85

LIFT 2.25 x 1.80

LIFT 1.85 x 2.30

BED ROOM 3.04 x 3.21

BED ROOM 3.05 x 3.05

BED ROOM 3.15 x 2.43

BED ROOM 3.05 x 3.31

BED ROOM 2.85 x 2.75

BED ROOM 3.05 x 3.10

BED ROOM 3.05 x 3.65

BED ROOM 3.10 x 3.70

BED ROOM 3.05 x 2.64

BED ROOM 3.00 x 3.05

BED ROOM 3.35 x 3.05

BED ROOM 3.97 x 3.15

BED ROOM 3.75 x 2.62

BED ROOM 5.17 x 2.46

KITCHEN 2.43 x 2.43

KITCHEN 2.13 x 2.75

KITCHEN 2.28 x 3.10

KITCHEN 2.18 x 2.64

KITCHEN 3.00 x 2.20

KITCHEN 2.28 x 3.35

KITCHEN 3.10 x 2.62

TOILET 2.13 x 1.37

TOILET 2.22 x 1.22

TOILET 2.02 x 1.37

TOILET 2.28 x 1.25

TOILET 2.28 x 1.22

TOILET 2.43 x 1.22

TOILET 1.22 x 2.13

TOILET 2.13 x 1.22

TOILET 1.22 x 1.87

3.71 x 0.92

2.12 x 2.39

4.31 x 0.92

0.92 x 2.24

0.92 x 2.16

4.66 x 0.92

0.92 x 1.47

3.95 x 0.92

0.53 x 1.67

1.22 x 0.55

3.60 x 0.92

2.23 x 1.03

2.13 x 1.17

2.20 x 2.46

0.75 MT. W. CHAJJA

0.67 MT. W. CHAJJA

1.13 MT. W. CHAJJA

0.30 MT. W. CHAJJA

0.45 MT. W. CHAJJA

0.68 MT. W. CHAJJA

0.69 MT. W. CHAJJA

0.15 MT. W. CHAJJA

0.75 MT. W. CHAJJA

O.D.U.

FINS

F.R.D.

E.D.

M.S. PLATFORM

S.S.

W.R.

UP

COLUMN

VERTICAL BOXING

WING - A

WING - B

BED ROOM 3.05 x 3.05
BED ROOM 3.15 x 2.43
KITCHEN 2.43 x 2.43
BED ROOM 3.05 x 3.96
BED ROOM 2.85 x 3.28
KITCHEN 2.13 x 3.28
KITCHEN 2.28 x 3.10
BED ROOM 3.05 x 3.10
BED ROOM 3.05 x 3.65
BED ROOM 3.04 x 3.21
BED ROOM 3.65 x 3.05
BED ROOM 3.23 x 3.05
KITCHEN 3.23 x 2.20
BED ROOM 3.97 x 3.15
BED ROOM 3.35 x 3.05
KITCHEN 2.28 x 3.35
KITCHEN 3.10 x 2.62
BED ROOM 3.75 x 2.62
BED ROOM 5.17 x 2.46
KITCHEN 2.18 x 2.64
BED ROOM 3.05 x 2.64
BED ROOM 3.10 x 3.70

TOILET 2.13 x 1.37
TOILET 2.13 x 1.37
TOILET 2.22 x 1.22
TOILET 2.22 x 1.22
TOILET 2.28 x 1.25
TOILET 2.28 x 1.22
TOILET 2.02 x 1.37
TOILET 1.22 x 2.13
TOILET 2.43 x 1.22
TOILET 1.22 x 2.13
TOILET 2.13 x 1.22
TOILET 1.22 x 2.13
TOILET 2.13 x 1.37
TOILET 1.22 x 1.87
TOILET 2.13 x 1.22
TOILET 1.22 x 2.13
TOILET 2.13 x 1.22
TOILET 1.22 x 2.13

REHAB
LIVING
3.35 x 4.27
R.A.=68.29 SQ.MT.

REHAB
LIVING
3.05 x 5.14
R.A.=57.92 SQ.MT.

REHAB
LIVING
3.15 x 5.06
R.A.=57.90 SQ.MT.

REHAB
LIVING
3.08 x 4.41
R.A.=52.10 SQ.MT.

REHAB
LIVING
4.87 x 3.05
R.A.=57.91 SQ.MT.

AH TO BMC
LIVING
3.05 x 4.27
R.A.=56.48 SQ.MT.

AH TO BMC
LIVING
3.05 x 4.27
R.A.=56.48 SQ.MT.

AH TO BMC
LIVING
6.17 x 2.69
R.A.=55.44 SQ.MT.

LIFT 4.56 x 2.00
LIFT 2.25 x 1.80
LIFT 3.47 x 1.85
LIFT 1.85 x 2.30

FIREMAN EVACUATION LIFT 1.92 x 3.02
FIREMAN EVACUATION LIFT 1.80 x 1.80

LOBBY 13.83 x 1.80
SMOKE CHECK LOBBY 1.88 x 1.50
SMOKE CHECK LOBBY 1.70 x 2.08
LOBBY 5.71 x 2.12

STAIRCASE UP

M.S. PLATFORM

S.S.

W.R.

F.R.D.

E.D.

FINS

O.D.U.


0.75 MT. W. CHAJJA
0.85 MT. W. CHAJJA
0.30 MT. W. CHAJJA
0.45 MT. W. CHAJJA
1.20 MT. W. CHAJJA
0.60 MT. W. CHAJJA
0.68 MT. W. CHAJJA

COLUMN

5TH FLOOR PLAN

SCALE :- 1:100

B

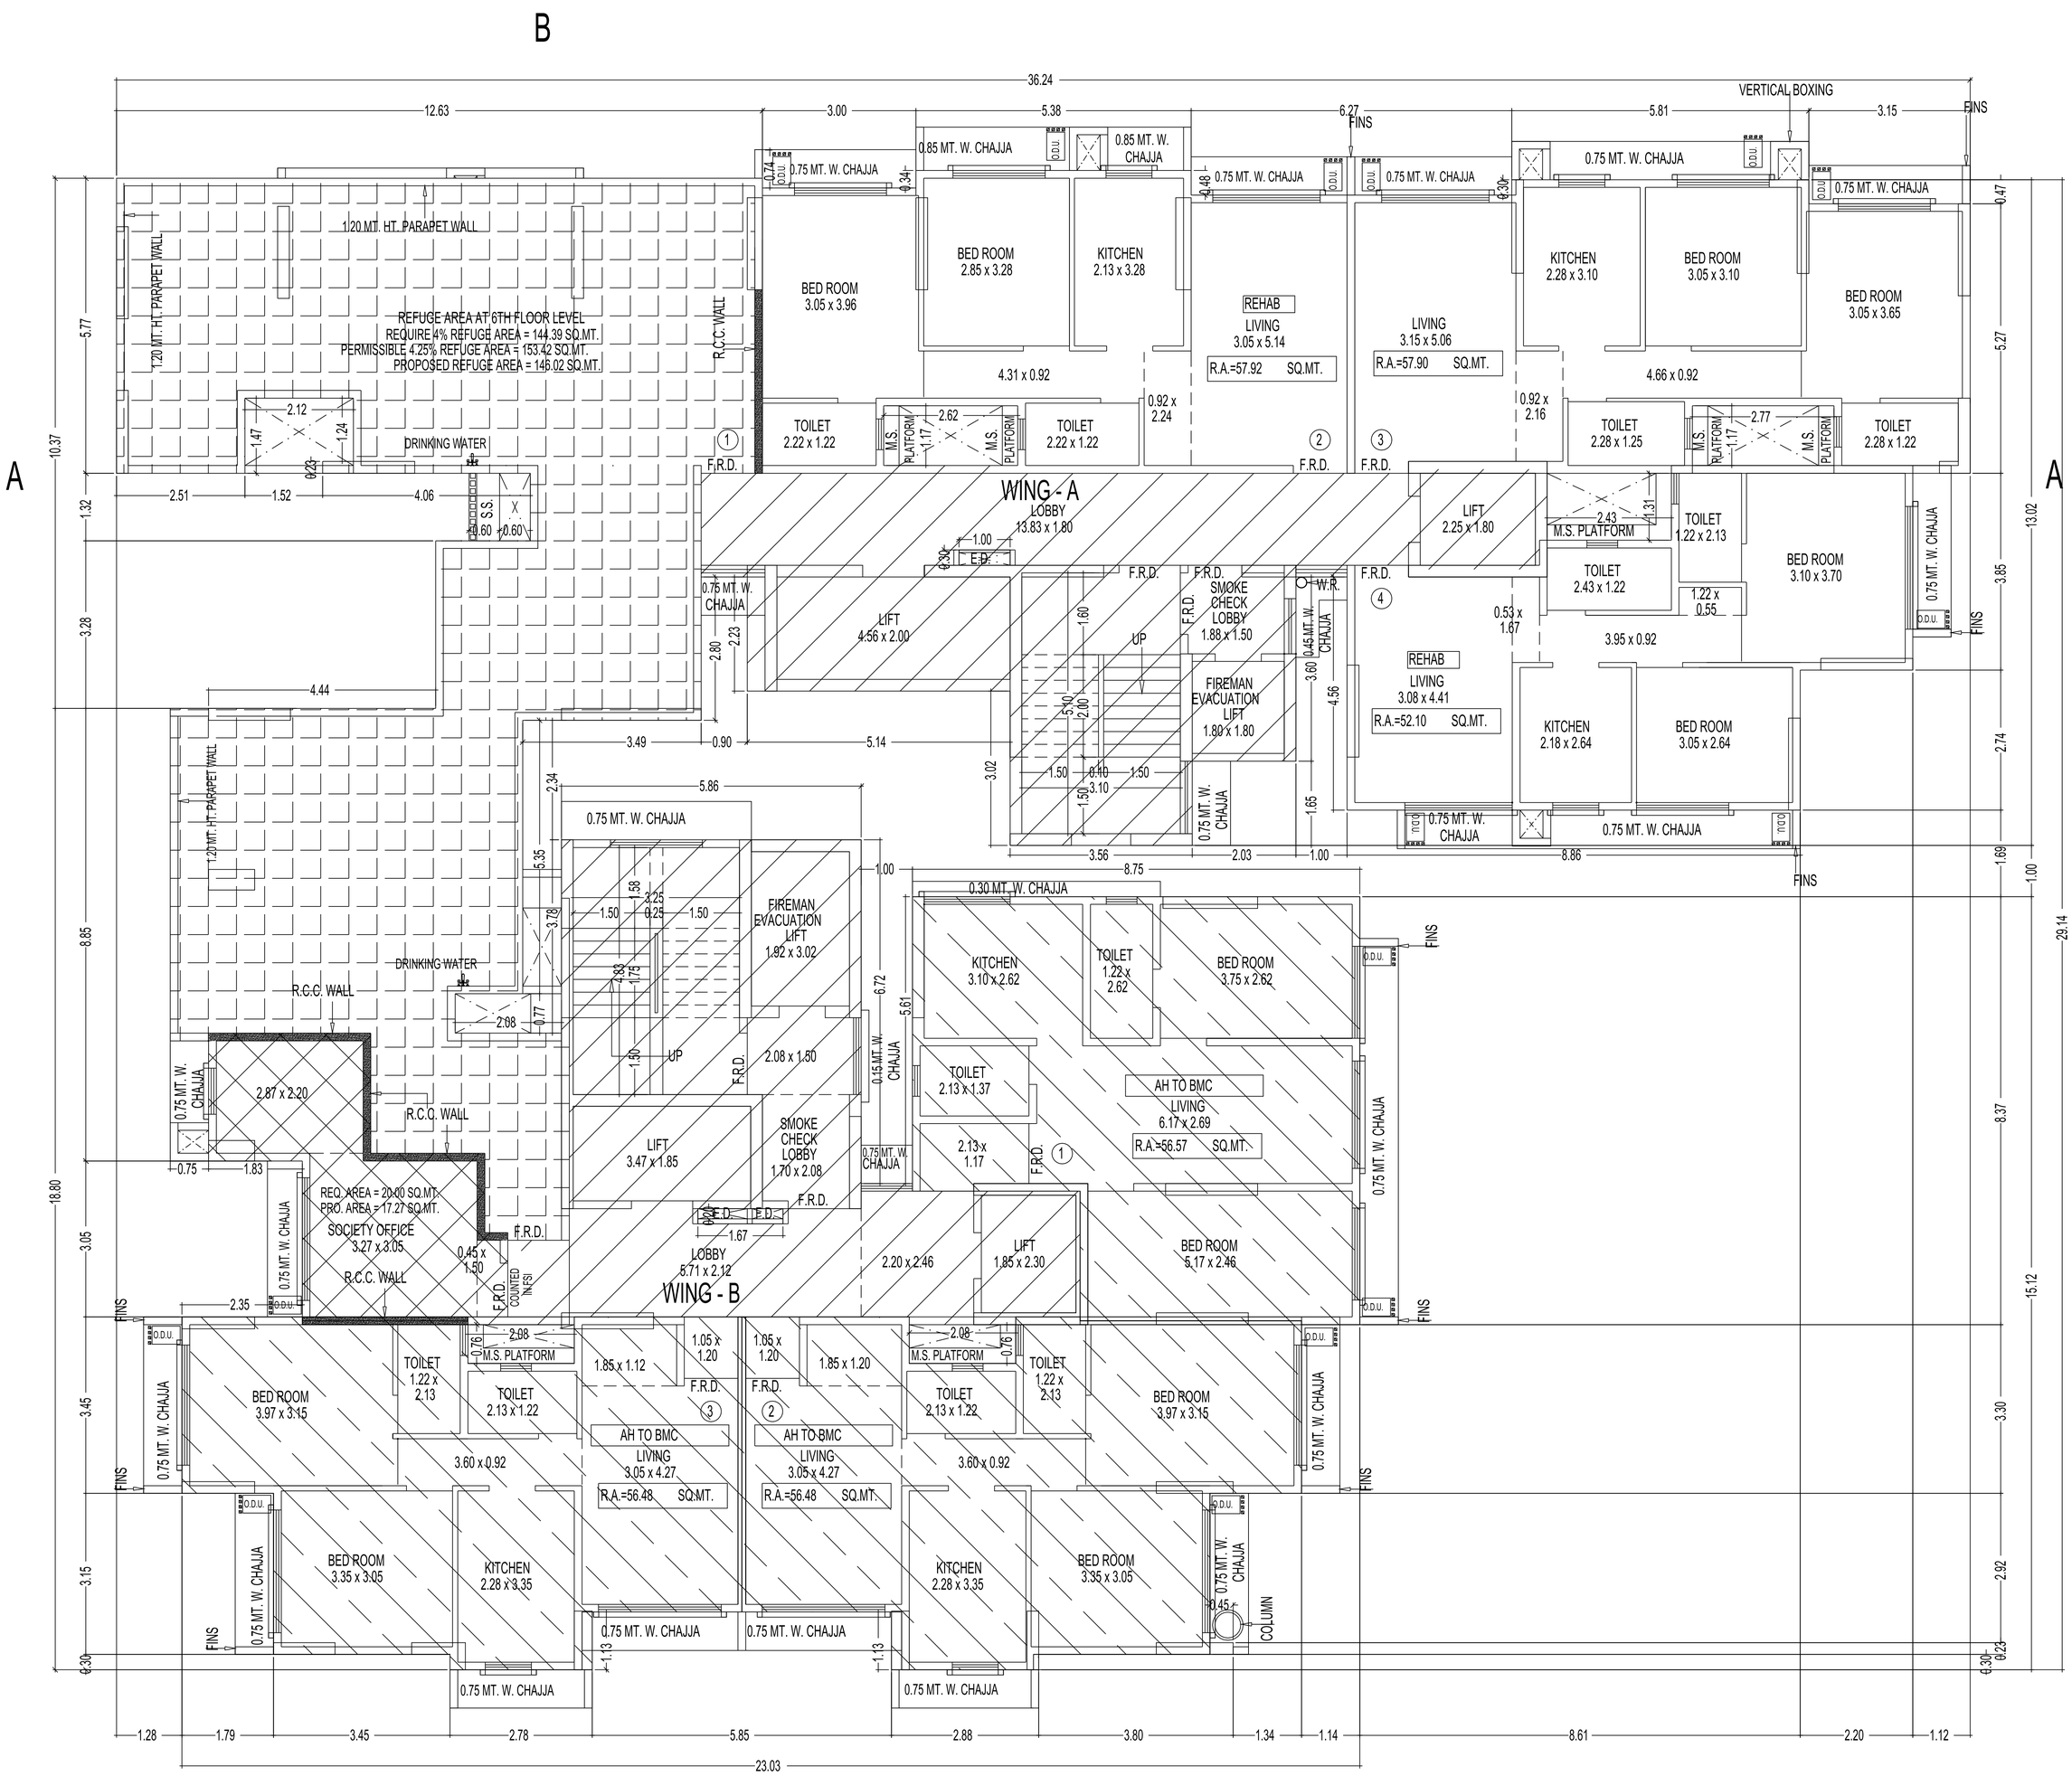

6TH FLOOR PLAN

SCALE :- 1:100

B

B

A

WING - A

WING - B

BED ROOM 3.05 x 3.05
BED ROOM 3.15 x 2.43
KITCHEN 2.43 x 2.43
BED ROOM 3.05 x 3.96
BED ROOM 2.85 x 3.28
KITCHEN 2.13 x 3.28
BED ROOM 3.05 x 3.65
KITCHEN 2.28 x 3.10
BED ROOM 3.05 x 3.10
REHAB LIVING 3.35 x 4.27 R.A.=68.29 SQ.MT.
REHAB LIVING 3.05 x 5.14 R.A.=57.92 SQ.MT.
REHAB LIVING 3.15 x 5.06 R.A.=57.90 SQ.MT.
REHAB LIVING 3.08 x 4.41 R.A.=52.10 SQ.MT.
TOILET 2.13 x 1.37
TOILET 2.22 x 1.22
TOILET 2.28 x 1.25
TOILET 2.28 x 1.22
TOILET 2.02 x 1.37
TOILET 1.22 x 2.13
TOILET 2.43 x 1.22
LOBBY 13.83 x 1.80
LIFT 4.56 x 2.00
LIFT 2.25 x 1.80
SMOKE CHECK LOBBY 1.88 x 1.50
FIREMAN EVACUATION LIFT 1.80 x 1.80
BED ROOM 3.04 x 3.21
BED ROOM 3.10 x 3.70
BED ROOM 4.52 x 3.05
BED ROOM 3.50 x 3.05
KITCHEN 3.50 x 2.20
TOILET 1.22 x 2.13
TOILET 2.13 x 1.22
FIREMAN EVACUATION LIFT 1.92 x 3.02
KITCHEN 3.10 x 2.62
TOILET 1.22 x 2.62
BED ROOM 3.75 x 2.62
TOILET 2.13 x 1.37
AH TO BMC
LIVING 6.17 x 2.69 R.A.=56.57 SQ.MT.
LIFT 3.47 x 1.85
SMOKE CHECK LOBBY 1.70 x 2.08
LIFT 1.85 x 2.30
BED ROOM 5.17 x 2.46
LIVING 4.92 x 3.05 R.A.=62.26 SQ.MT.
LOBBY 5.71 x 2.12
BED ROOM 3.97 x 3.15
BED ROOM 3.35 x 3.05
KITCHEN 2.28 x 3.35
REHAB LIVING 3.05 x 5.47 R.A.=57.92 SQ.MT.
0.75 MT. W. CHAJJA
0.85 MT. W. CHAJJA
0.30 MT. W. CHAJJA
0.60 MT. W. CHAJJA
1.20 MT. W. CHAJJA
0.45 MT. W. CHAJJA
0.15 MT. W. CHAJJA
O.D.U.
FINS
F.R.D.
M.S. PLATFORM
S.S.
E.D.
W.P.
UP
VERTICAL BOXING
COLUMN

7TH FLOOR PLAN

SCALE :- 1:100

B

8TH FLOOR PLAN

SCALE :- 1:100

WING - A

WING - B

REHAB LIVING 3.35 x 5.23 R.A.=82.47 SQ.MT.

REHAB LIVING 3.05 x 5.14 R.A.=57.92 SQ.MT.

REHAB LIVING 3.15 x 5.06 R.A.=57.90 SQ.MT.

REHAB LIVING 3.08 x 4.41 R.A.=52.10 SQ.MT.

REHAB LIVING 3.05 x 6.25 R.A.=62.31 SQ.MT.

REHAB LIVING 3.05 x 5.47 R.A.=57.92 SQ.MT.

AH TO BMC LIVING 6.17 x 2.89 R.A.=56.57 SQ.MT.

LIVING 4.92 x 3.05 R.A.=62.26 SQ.MT.

9TH FLOOR PLAN

SCALE :- 1:100

WING - A

WING - B

LOBBY 13.83 x 1.80

LOBBY 5.71 x 2.12

REHAB LIVING 3.35 x 5.23 R.A.=82.47 SQ.MT.

REHAB LIVING 3.05 x 5.62 R.A.=62.34 SQ.MT.

REHAB LIVING 3.15 x 5.36 R.A.=62.25 SQ.MT.

REHAB LIVING 3.08 x 4.41 R.A.=52.10 SQ.MT.

REHAB LIVING 3.05 x 6.25 R.A.=62.31 SQ.MT.

REHAB LIVING 3.05 x 5.47 R.A.=57.92 SQ.MT.

LIVING 4.92 x 3.05 R.A.=62.26 SQ.MT.

AH TO BMC LIVING 6.17 x 2.69 R.A.=56.57 SQ.MT.

LIFT 4.56 x 2.00

LIFT 2.25 x 1.80

LIFT 3.47 x 1.85

LIFT 1.85 x 2.30

FIREMAN EVACUATION LIFT 1.80 x 1.80

FIREMAN EVACUATION LIFT 1.82 x 3.02

SMOKE CHECK LOBBY 1.88 x 1.50

SMOKE CHECK LOBBY 1.70 x 2.08

BED ROOM 3.05 x 3.65

BED ROOM 3.15 x 3.35

KITCHEN 2.43 x 3.35

BED ROOM 3.05 x 4.30

BED ROOM 2.85 x 3.28

KITCHEN 2.13 x 3.28

KITCHEN 2.28 x 3.10

BED ROOM 3.05 x 3.10

BED ROOM 3.05 x 4.12

BED ROOM 4.14 x 3.21

BED ROOM 3.10 x 3.70

KITCHEN 2.18 x 2.64

BED ROOM 3.05 x 2.64

BED ROOM 4.52 x 3.05

BED ROOM 3.50 x 3.05

KITCHEN 3.50 x 2.20

KITCHEN 3.10 x 2.62

BED ROOM 3.75 x 2.62

BED ROOM 4.27 x 3.15

BED ROOM 3.97 x 3.15

BED ROOM 3.65 x 3.05

KITCHEN 2.28 x 3.35

BED ROOM 3.35 x 3.05

TOILET 2.13 x 1.37

TOILET 2.22 x 1.22

TOILET 2.28 x 1.25

TOILET 2.28 x 1.22

TOILET 2.43 x 1.22

TOILET 1.22 x 2.13

TOILET 2.13 x 1.22

TOILET 1.22 x 2.62

0.75 MT. W. CHAJJA

0.80 MT. W. CHAJJA

0.30 MT. W. CHAJJA

0.60 MT. W. CHAJJA

1.20 MT. W. CHAJJA

0.45 MT. W. CHAJJA

0.15 MT. W. CHAJJA

O.D.U.

M.S. PLATFORM

F.R.D.

E.D.

S.S.

W.R.

UP

FINS

VERTICAL BOXING

COLUMN

B

A

B

A

WING - A

WING - B

BED ROOM 3.15 x 3.35
KITCHEN 2.43 x 3.35
BED ROOM 3.05 x 3.65
REHAB LIVING 3.35 x 5.23 R.A.=82.47 SQ.MT.
BED ROOM 3.05 x 4.30
BED ROOM 2.85 x 3.28
KITCHEN 2.13 x 3.28
REHAB LIVING 3.05 x 5.62 R.A.=62.34 SQ.MT.
REHAB LIVING 3.15 x 5.36 R.A.=62.25 SQ.MT.
KITCHEN 2.28 x 3.10
BED ROOM 3.05 x 3.10
BED ROOM 3.05 x 4.12
TOILET 2.13 x 1.37
TOILET 2.22 x 1.22
TOILET 2.28 x 1.25
TOILET 2.28 x 1.22
LIFT 4.56 x 2.00
LIFT 2.25 x 1.80
LOBBY 13.83 x 1.80
SMOKE CHECK LOBBY 1.88 x 1.50
FIREMAN EVACUATION LIFT 1.80 x 1.80
BED ROOM 4.14 x 3.21
BED ROOM 4.52 x 3.05
BED ROOM 3.10 x 3.70
TOILET 2.43 x 1.22
TOILET 1.22 x 2.13
REHAB LIVING 3.08 x 4.41 R.A.=52.10 SQ.MT.
KITCHEN 2.18 x 2.64
BED ROOM 3.05 x 2.64
BED ROOM 3.50 x 3.05
KITCHEN 3.50 x 2.20
TOILET 1.22 x 2.13
TOILET 2.13 x 1.22
FIREMAN EVACUATION LIFT 1.92 x 3.02
LIFT 3.47 x 1.85
SMOKE CHECK LOBBY 1.70 x 2.08
KITCHEN 3.10 x 2.62
TOILET 1.22 x 2.62
BED ROOM 3.75 x 2.62
TOILET 2.13 x 1.37
AH TO BMC LIVING 6.17 x 2.69 R.A.=56.57 SQ.MT.
LIFT 1.85 x 2.30
BED ROOM 5.17 x 2.46
LIVING 4.92 x 3.05 R.A.=62.26 SQ.MT.
BED ROOM 4.27 x 3.15
REHAB LIVING 3.05 x 6.25 R.A.=62.31 SQ.MT.
KITCHEN 2.28 x 3.35
BED ROOM 3.65 x 3.05
COLUMN

10TH FLOOR PLAN

SCALE :- 1:100

B

A

WING - A

WING - B

BED ROOM 3.15 x 3.35
KITCHEN 2.43 x 3.35
BED ROOM 3.05 x 3.65
REHAB
LIVING 3.35 x 5.23
R.A.=82.47 SQ.MT.
TOILET 2.13 x 1.37
TOILET 2.13 x 1.37
TOILET 2.13 x 1.37
BED ROOM 4.14 x 3.21
BED ROOM 3.05 x 4.30
BED ROOM 2.85 x 3.28
KITCHEN 2.13 x 3.28
REHAB
LIVING 3.05 x 5.62
R.A.=62.33 SQ.MT.
TOILET 2.22 x 1.22
TOILET 2.22 x 1.22
LOBBY 13.83 x 1.80
LIFT 4.56 x 2.00
SMOKE CHECK LOBBY 1.88 x 1.50
FIREMAN EVACUATION LIFT 1.80 x 1.80
REHAB
LIVING 3.15 x 5.36
R.A.=62.25 SQ.MT.
KITCHEN 2.28 x 3.10
BED ROOM 3.05 x 3.10
BED ROOM 3.05 x 4.12
TOILET 2.28 x 1.25
TOILET 2.28 x 1.22
LIFT 2.25 x 1.80
TOILET 2.43 x 1.22
TOILET 1.22 x 2.13
BED ROOM 3.10 x 3.70
LIVING 3.08 x 4.41
R.A.=52.10 SQ.MT.
KITCHEN 2.18 x 2.64
BED ROOM 3.05 x 2.64
BED ROOM 4.52 x 3.05
BED ROOM 3.50 x 3.05
KITCHEN 3.50 x 2.20
TOILET 1.22 x 2.13
TOILET 2.13 x 1.22
LIFT 3.47 x 1.85
FIREMAN EVACUATION LIFT 1.92 x 3.02
SMOKE CHECK LOBBY 1.70 x 2.08
KITCHEN 3.10 x 2.62
TOILET 1.22 x 2.62
BED ROOM 3.75 x 2.62
TOILET 2.13 x 1.37
AH TO BMC
LIVING 6.17 x 2.69
R.A.=56.57 SQ.MT.
LOBBY 5.71 x 2.12
LIFT 1.85 x 2.30
BED ROOM 5.17 x 2.46
LIVING 4.92 x 3.05
R.A.=62.26 SQ.MT.
BED ROOM 4.27 x 3.15
TOILET 1.22 x 2.13
TOILET 2.13 x 1.22
LIVING 3.05 x 6.25
R.A.=62.31 SQ.MT.
BED ROOM 3.65 x 3.05
KITCHEN 2.28 x 3.35
COLUMN

11TH FLOOR PLAN

SCALE :- 1:100

B

A


WING - A

WING - B

BED ROOM 3.15 x 3.35
KITCHEN 2.43 x 3.35
BED ROOM 3.05 x 3.65
LIVING 3.35 x 5.23
R.A.=82.47 SQ.MT.
BED ROOM 3.05 x 4.30
BED ROOM 2.85 x 3.28
KITCHEN 2.13 x 3.28
LIVING 3.05 x 5.62
R.A.=62.33 SQ.MT.
REHAB
LIVING 3.15 x 5.36
R.A.=62.25 SQ.MT.
KITCHEN 2.28 x 3.10
BED ROOM 3.05 x 3.10
BED ROOM 3.05 x 4.12
TOILET 2.13 x 1.37
TOILET 2.22 x 1.22
TOILET 2.28 x 1.25
TOILET 2.28 x 1.22
LOBBY 13.83 x 1.80
LIFT 4.56 x 2.00
LIFT 2.25 x 1.80
SMOKE CHECK LOBBY 1.88 x 1.50
FIREMAN EVACUATION LIFT 1.80 x 1.80
BED ROOM 4.14 x 3.21
BED ROOM 4.52 x 3.05
BED ROOM 3.50 x 3.05
KITCHEN 3.50 x 2.20
TOILET 1.22 x 2.13
TOILET 2.13 x 1.22
FIREMAN EVACUATION LIFT 1.92 x 3.02
LIFT 3.47 x 1.85
SMOKE CHECK LOBBY 1.70 x 2.08
LIVING 4.92 x 3.05
R.A.=62.26 SQ.MT.
LOBBY 5.71 x 2.12
KITCHEN 3.10 x 2.62
TOILET 1.22 x 2.62
BED ROOM 3.75 x 2.62
TOILET 2.13 x 1.37
AH TO BMC
LIVING 6.17 x 2.69
R.A.=56.57 SQ.MT.
LIFT 1.85 x 2.30
BED ROOM 5.17 x 2.46
BED ROOM 4.27 x 3.15
BED ROOM 3.65 x 3.05
KITCHEN 2.28 x 3.35
LIVING 3.05 x 6.25
R.A.=62.31 SQ.MT.
KITCHEN 2.18 x 2.64
BED ROOM 3.05 x 2.64
BED ROOM 3.10 x 3.70
LIVING 3.08 x 4.41
R.A.=52.10 SQ.MT.

12TH FLOOR PLAN


SCALE :- 1:100

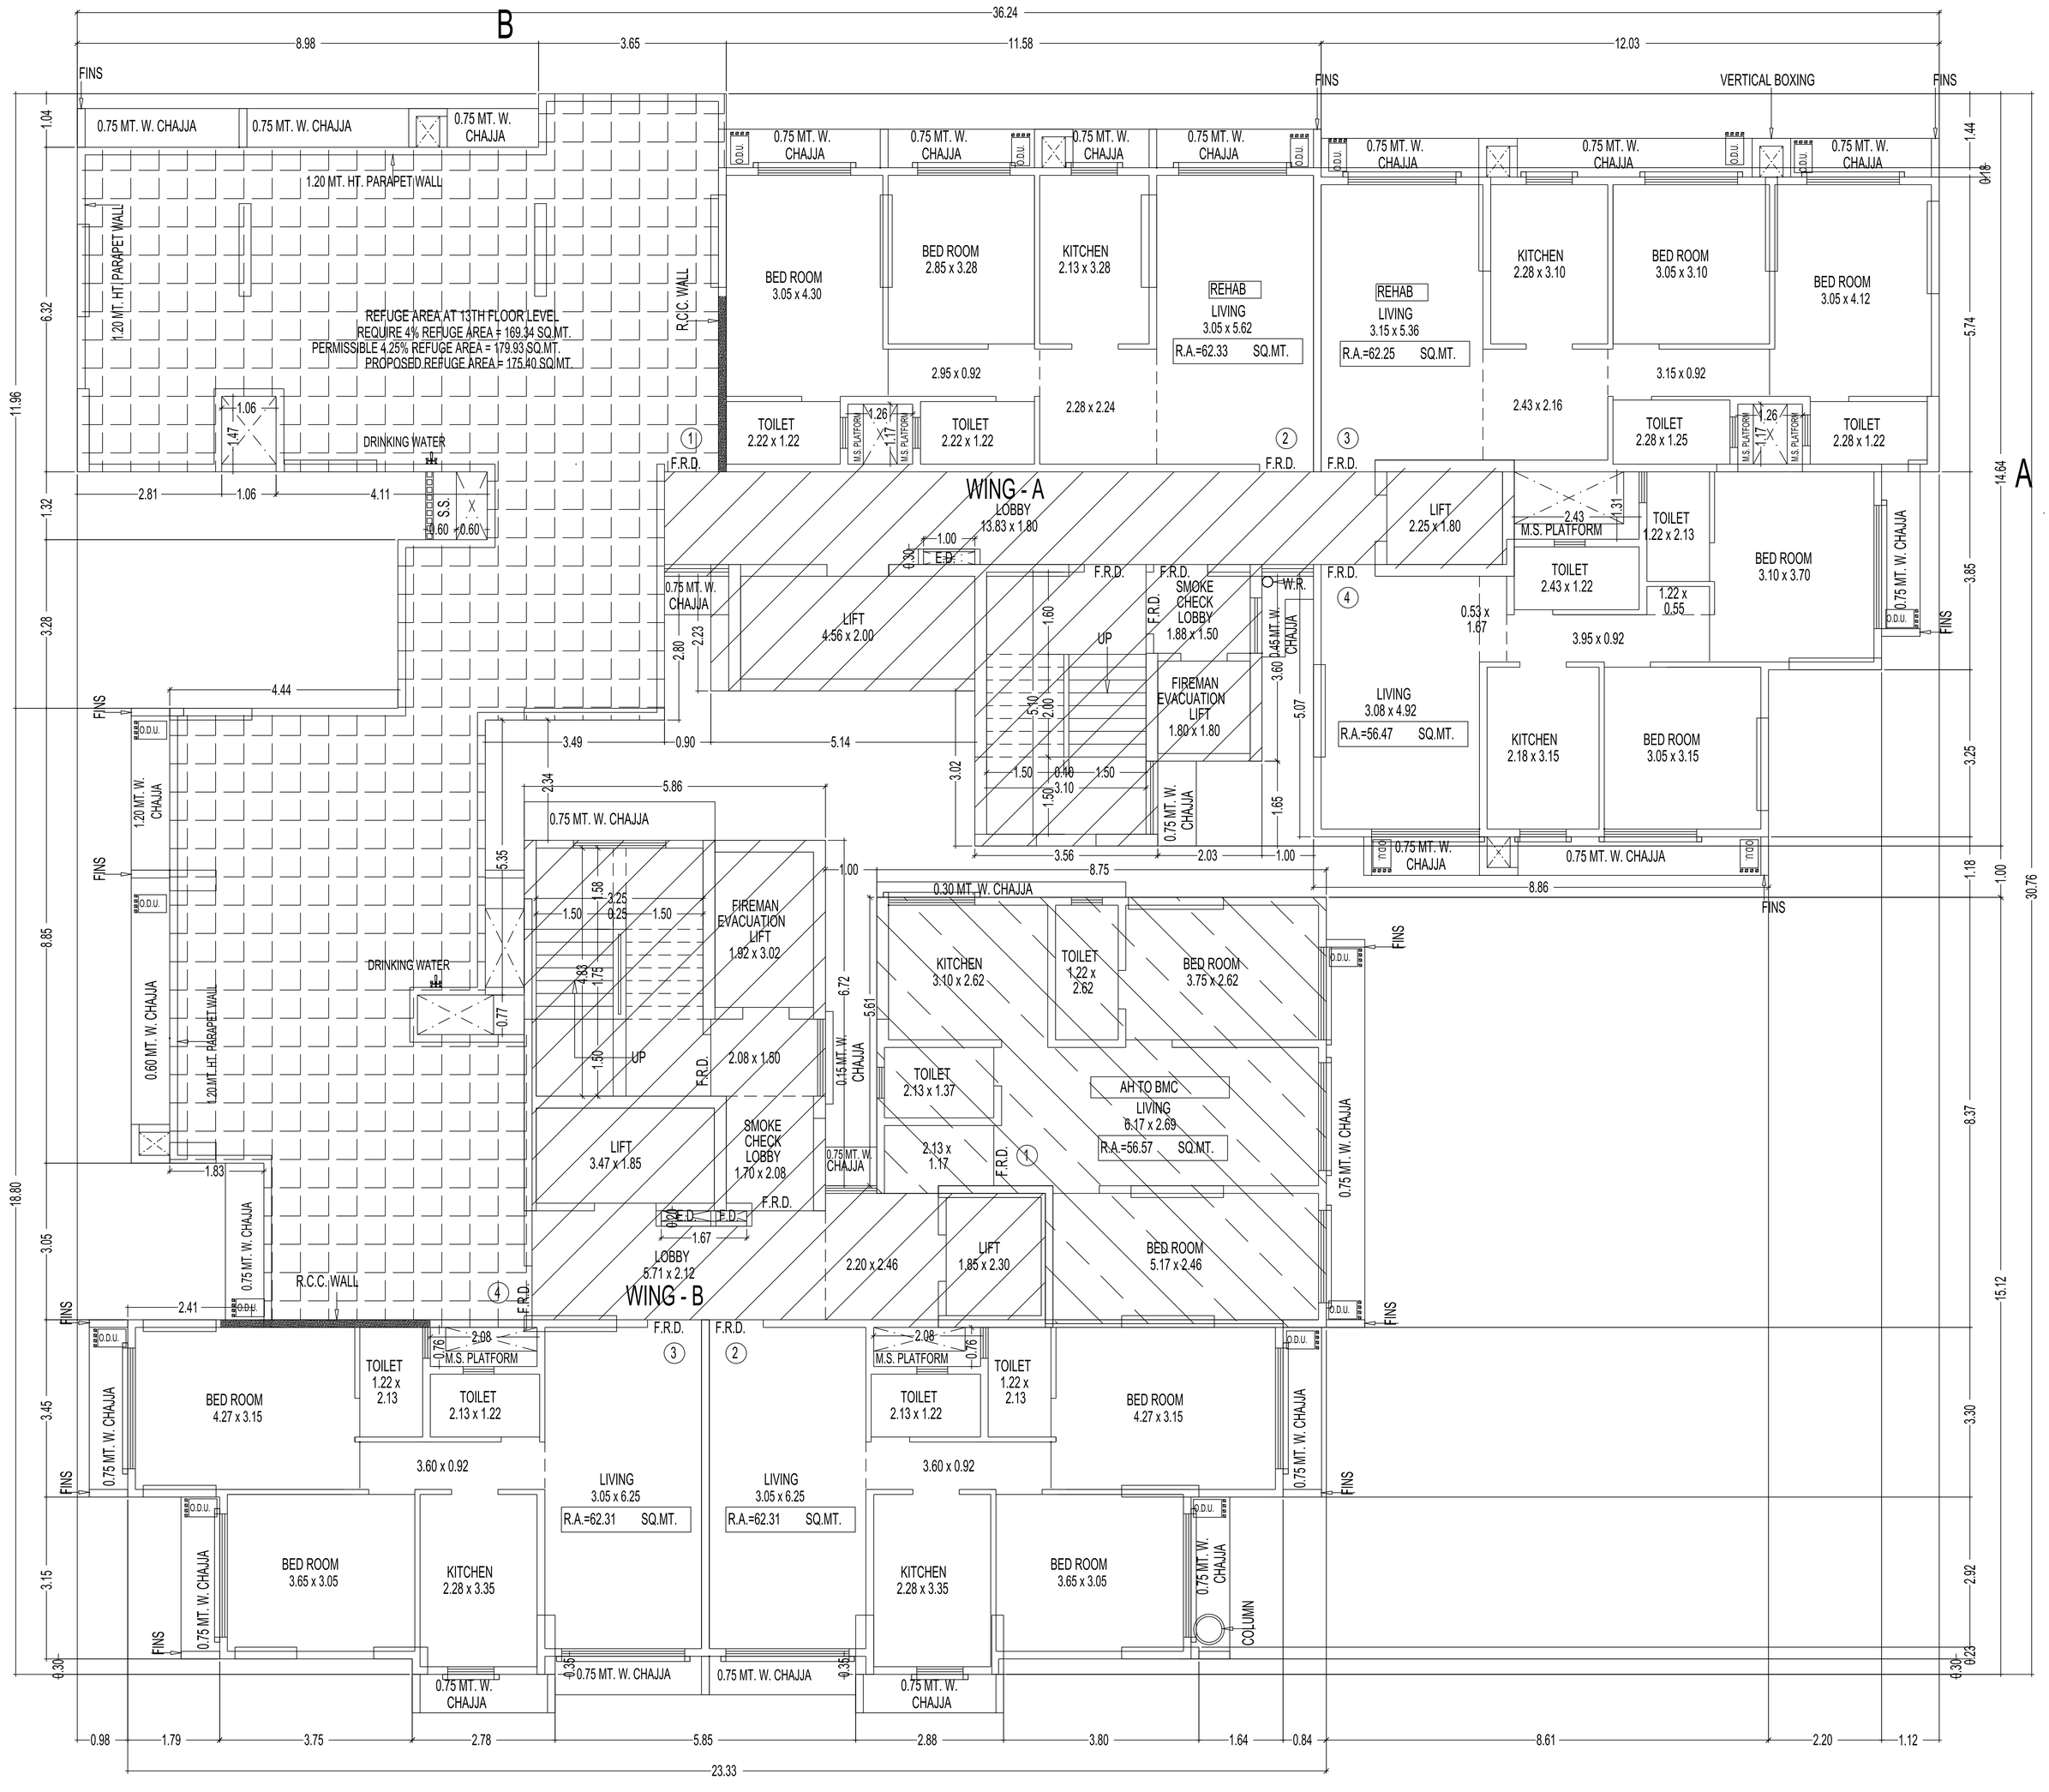

13TH FLOOR PLAN

SCALE :- 1:100

B

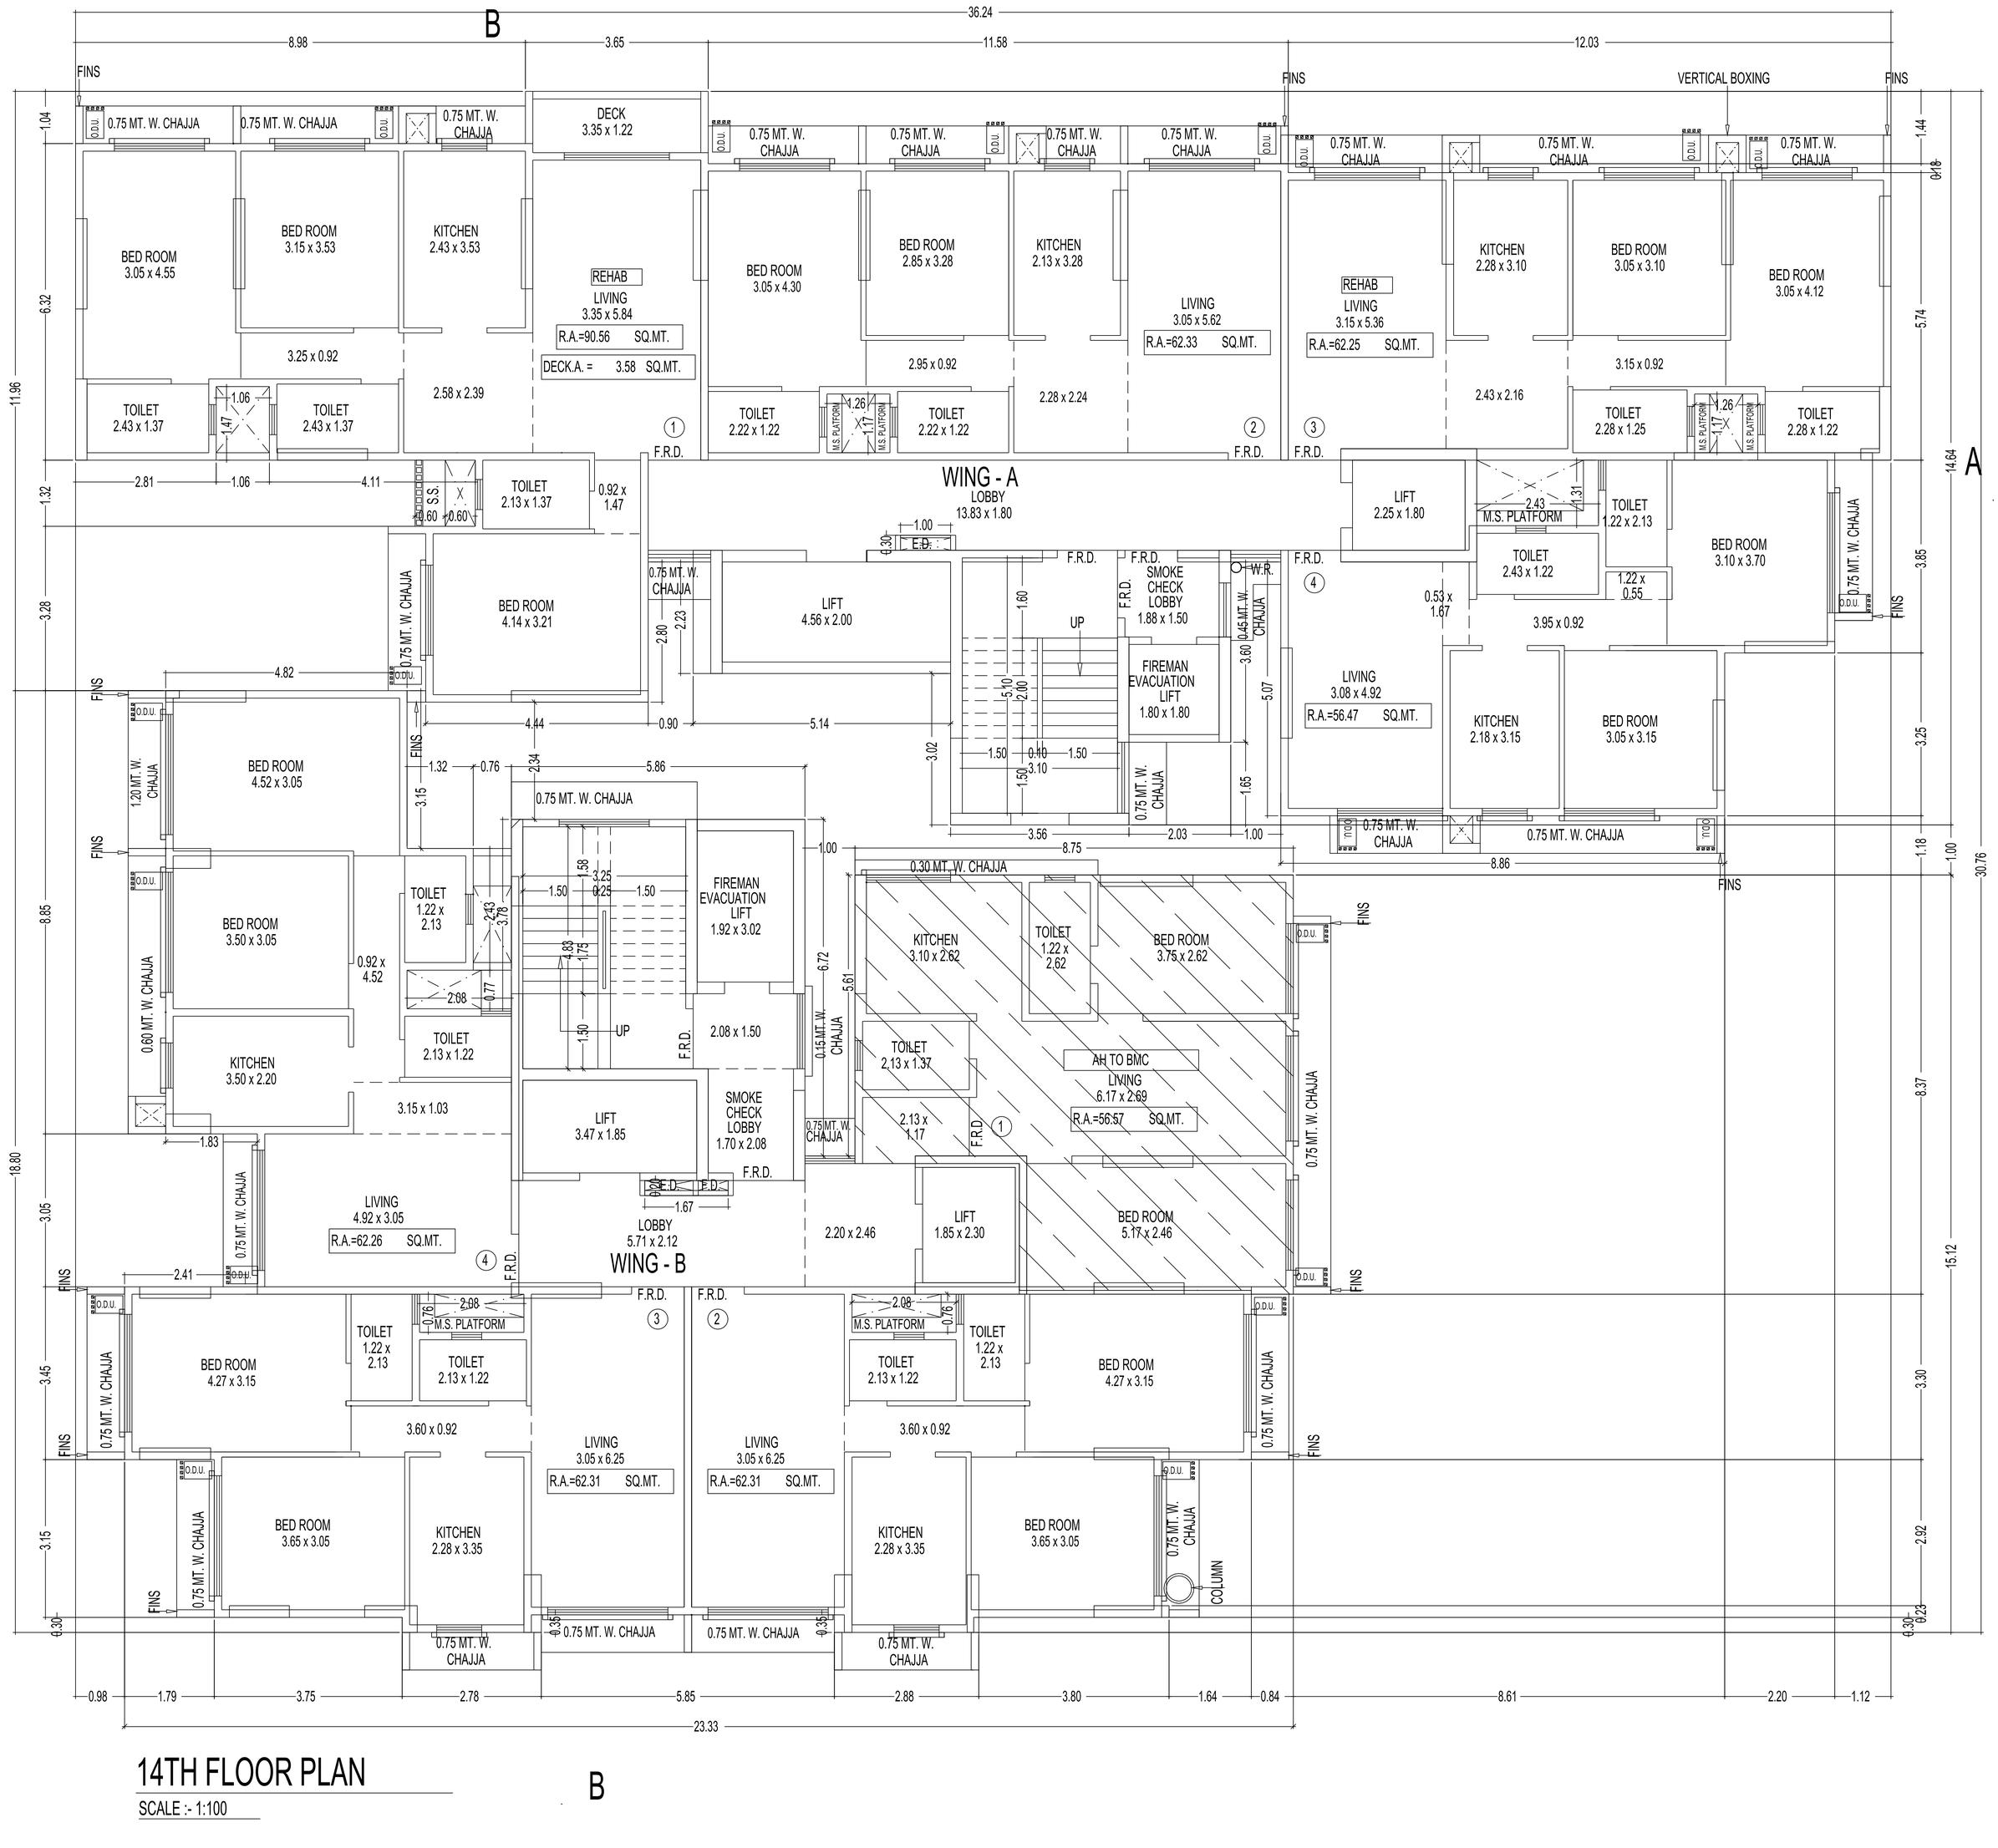


14TH FLOOR PLAN

SCALE :- 1:100

15TH FLOOR PLAN

SCALE :- 1:100

B

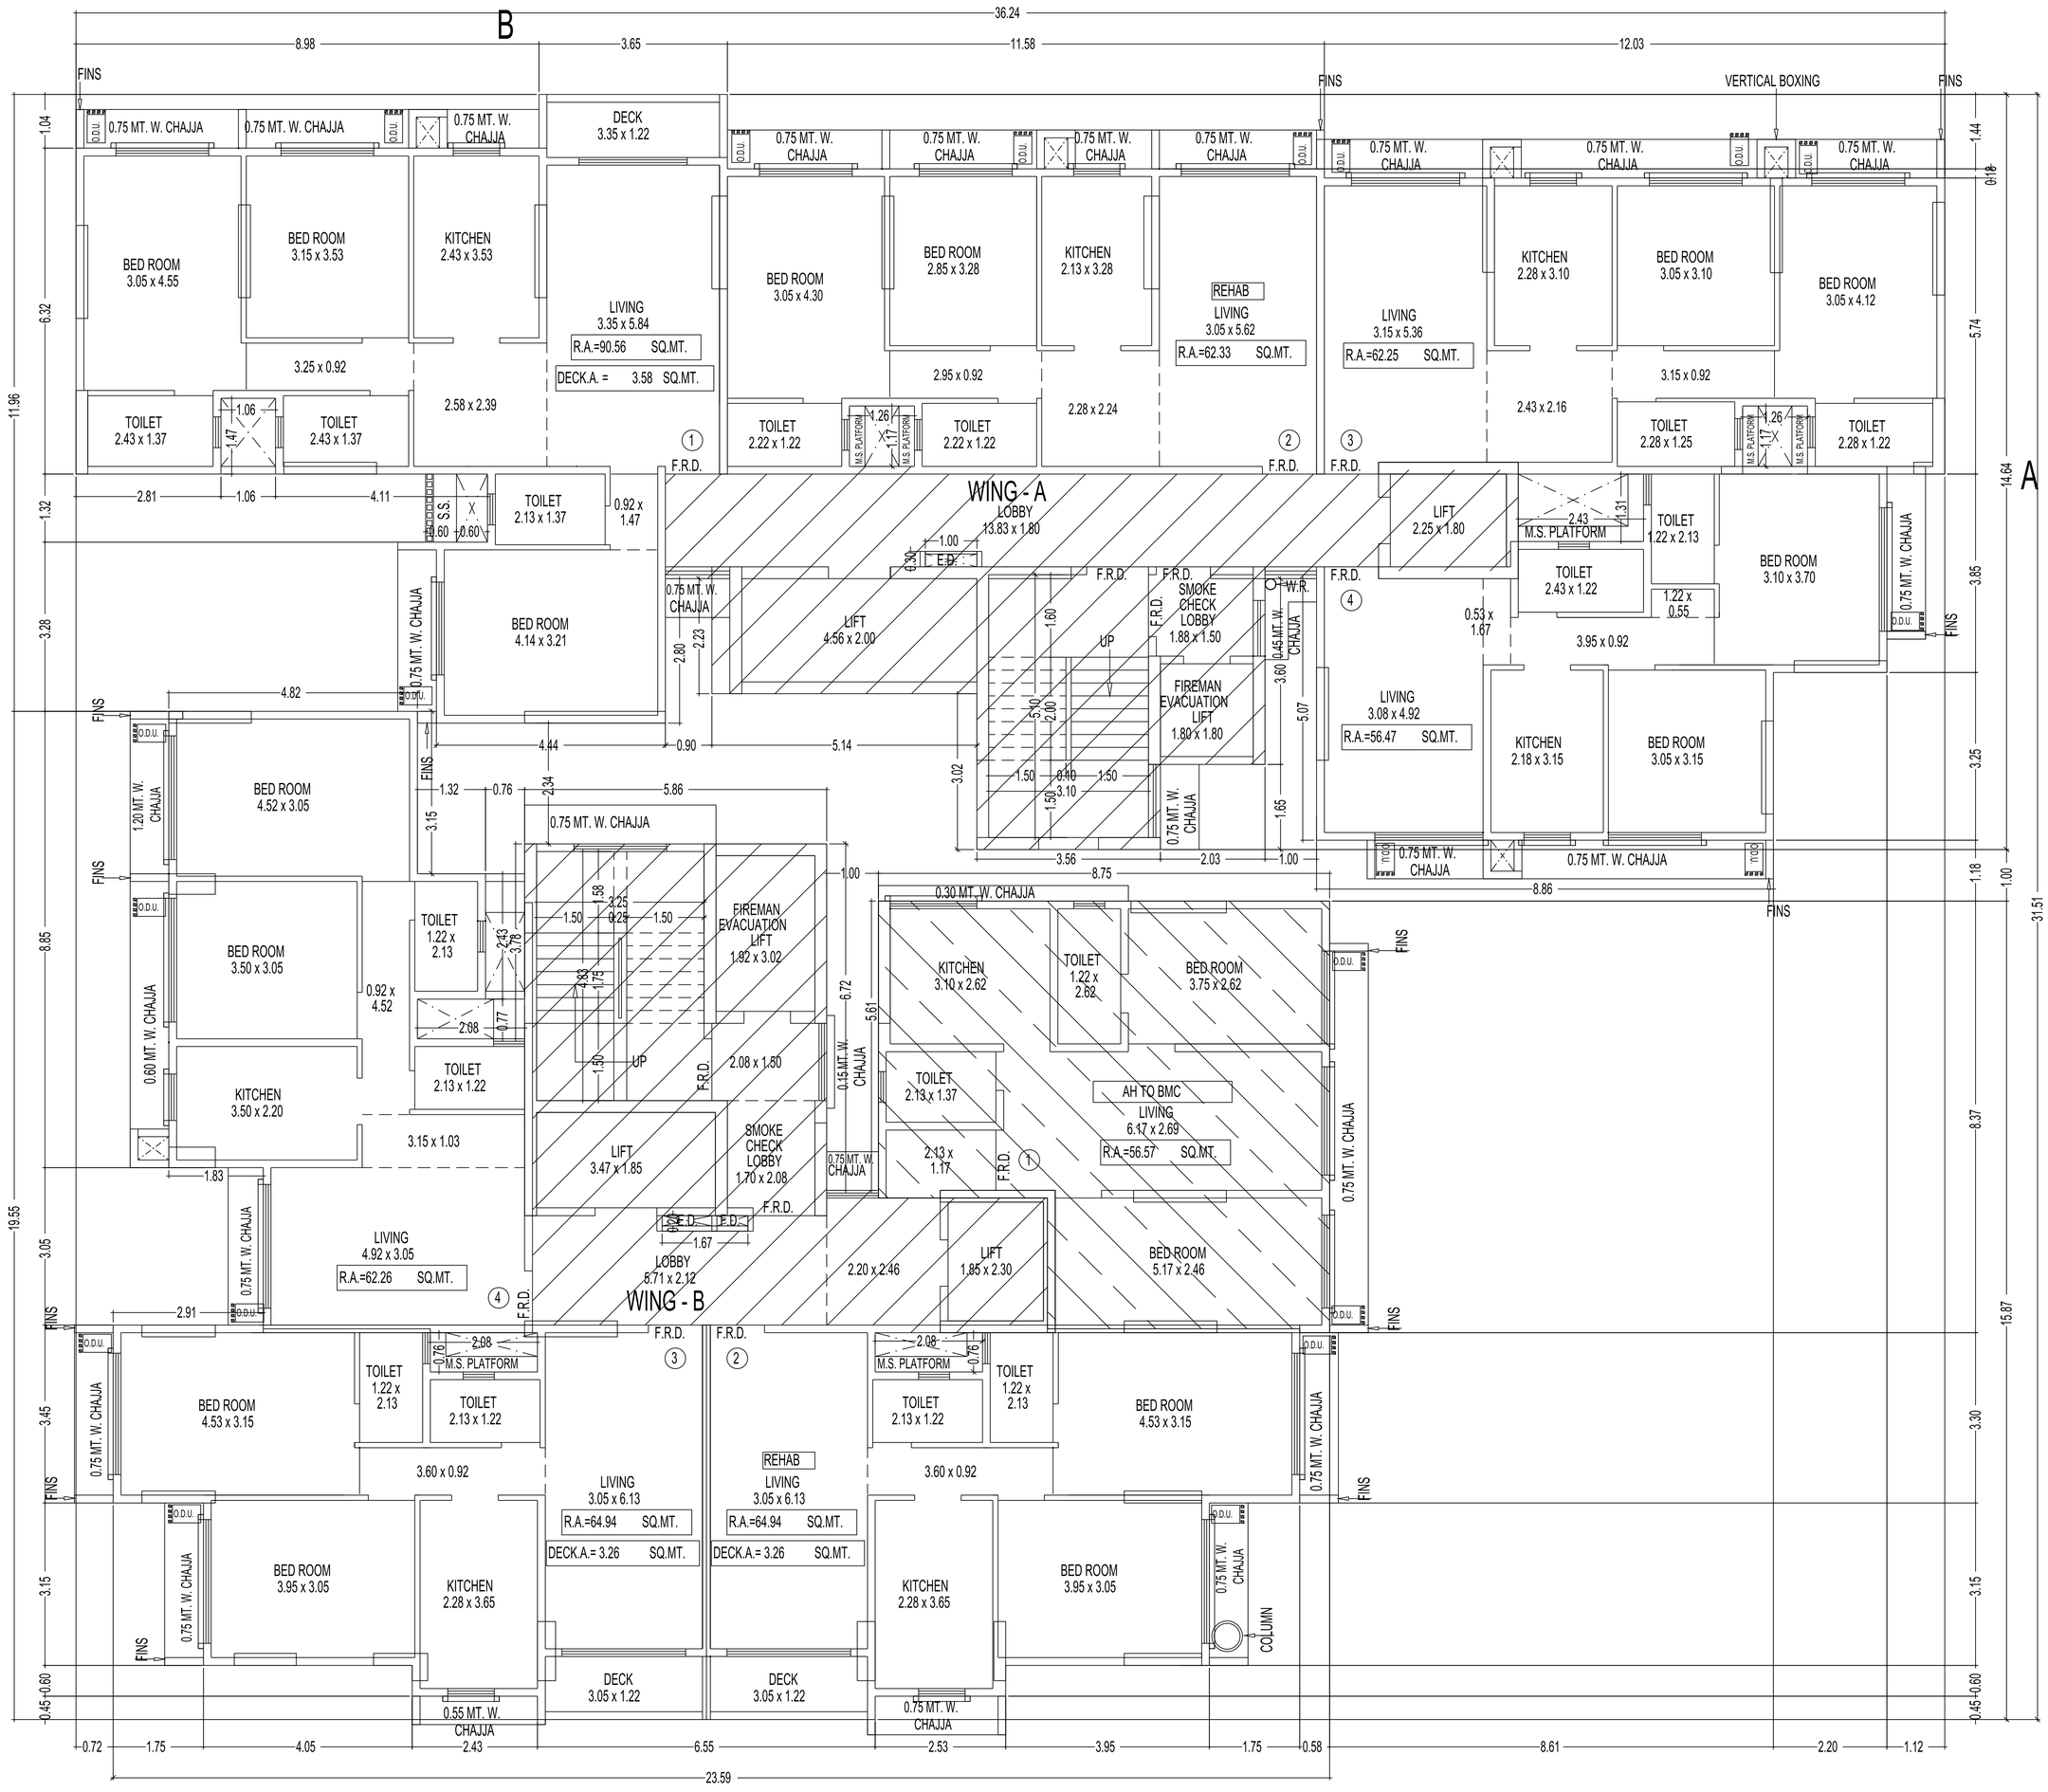

16TH FLOOR PLAN

SCALE :- 1:100

B

EXISTING 18.30 MT. WIDE SANT DNYANESHWAR ROAD

WEST

SOUTH

NORTH

EAST

AREA IN ADVERSE POSSESSION

WING - A

WING - B

L.O.S AREA = 202.64 SQ.MT.

17TH TO 19TH FLOOR PLAN

SCALE :- 1:100

B

FINS

CHAJJA BELOW


CHAJJA

FINS

FINS

0.75 MT. W. CHAJJA

0.75 MT. W. CHAJJA

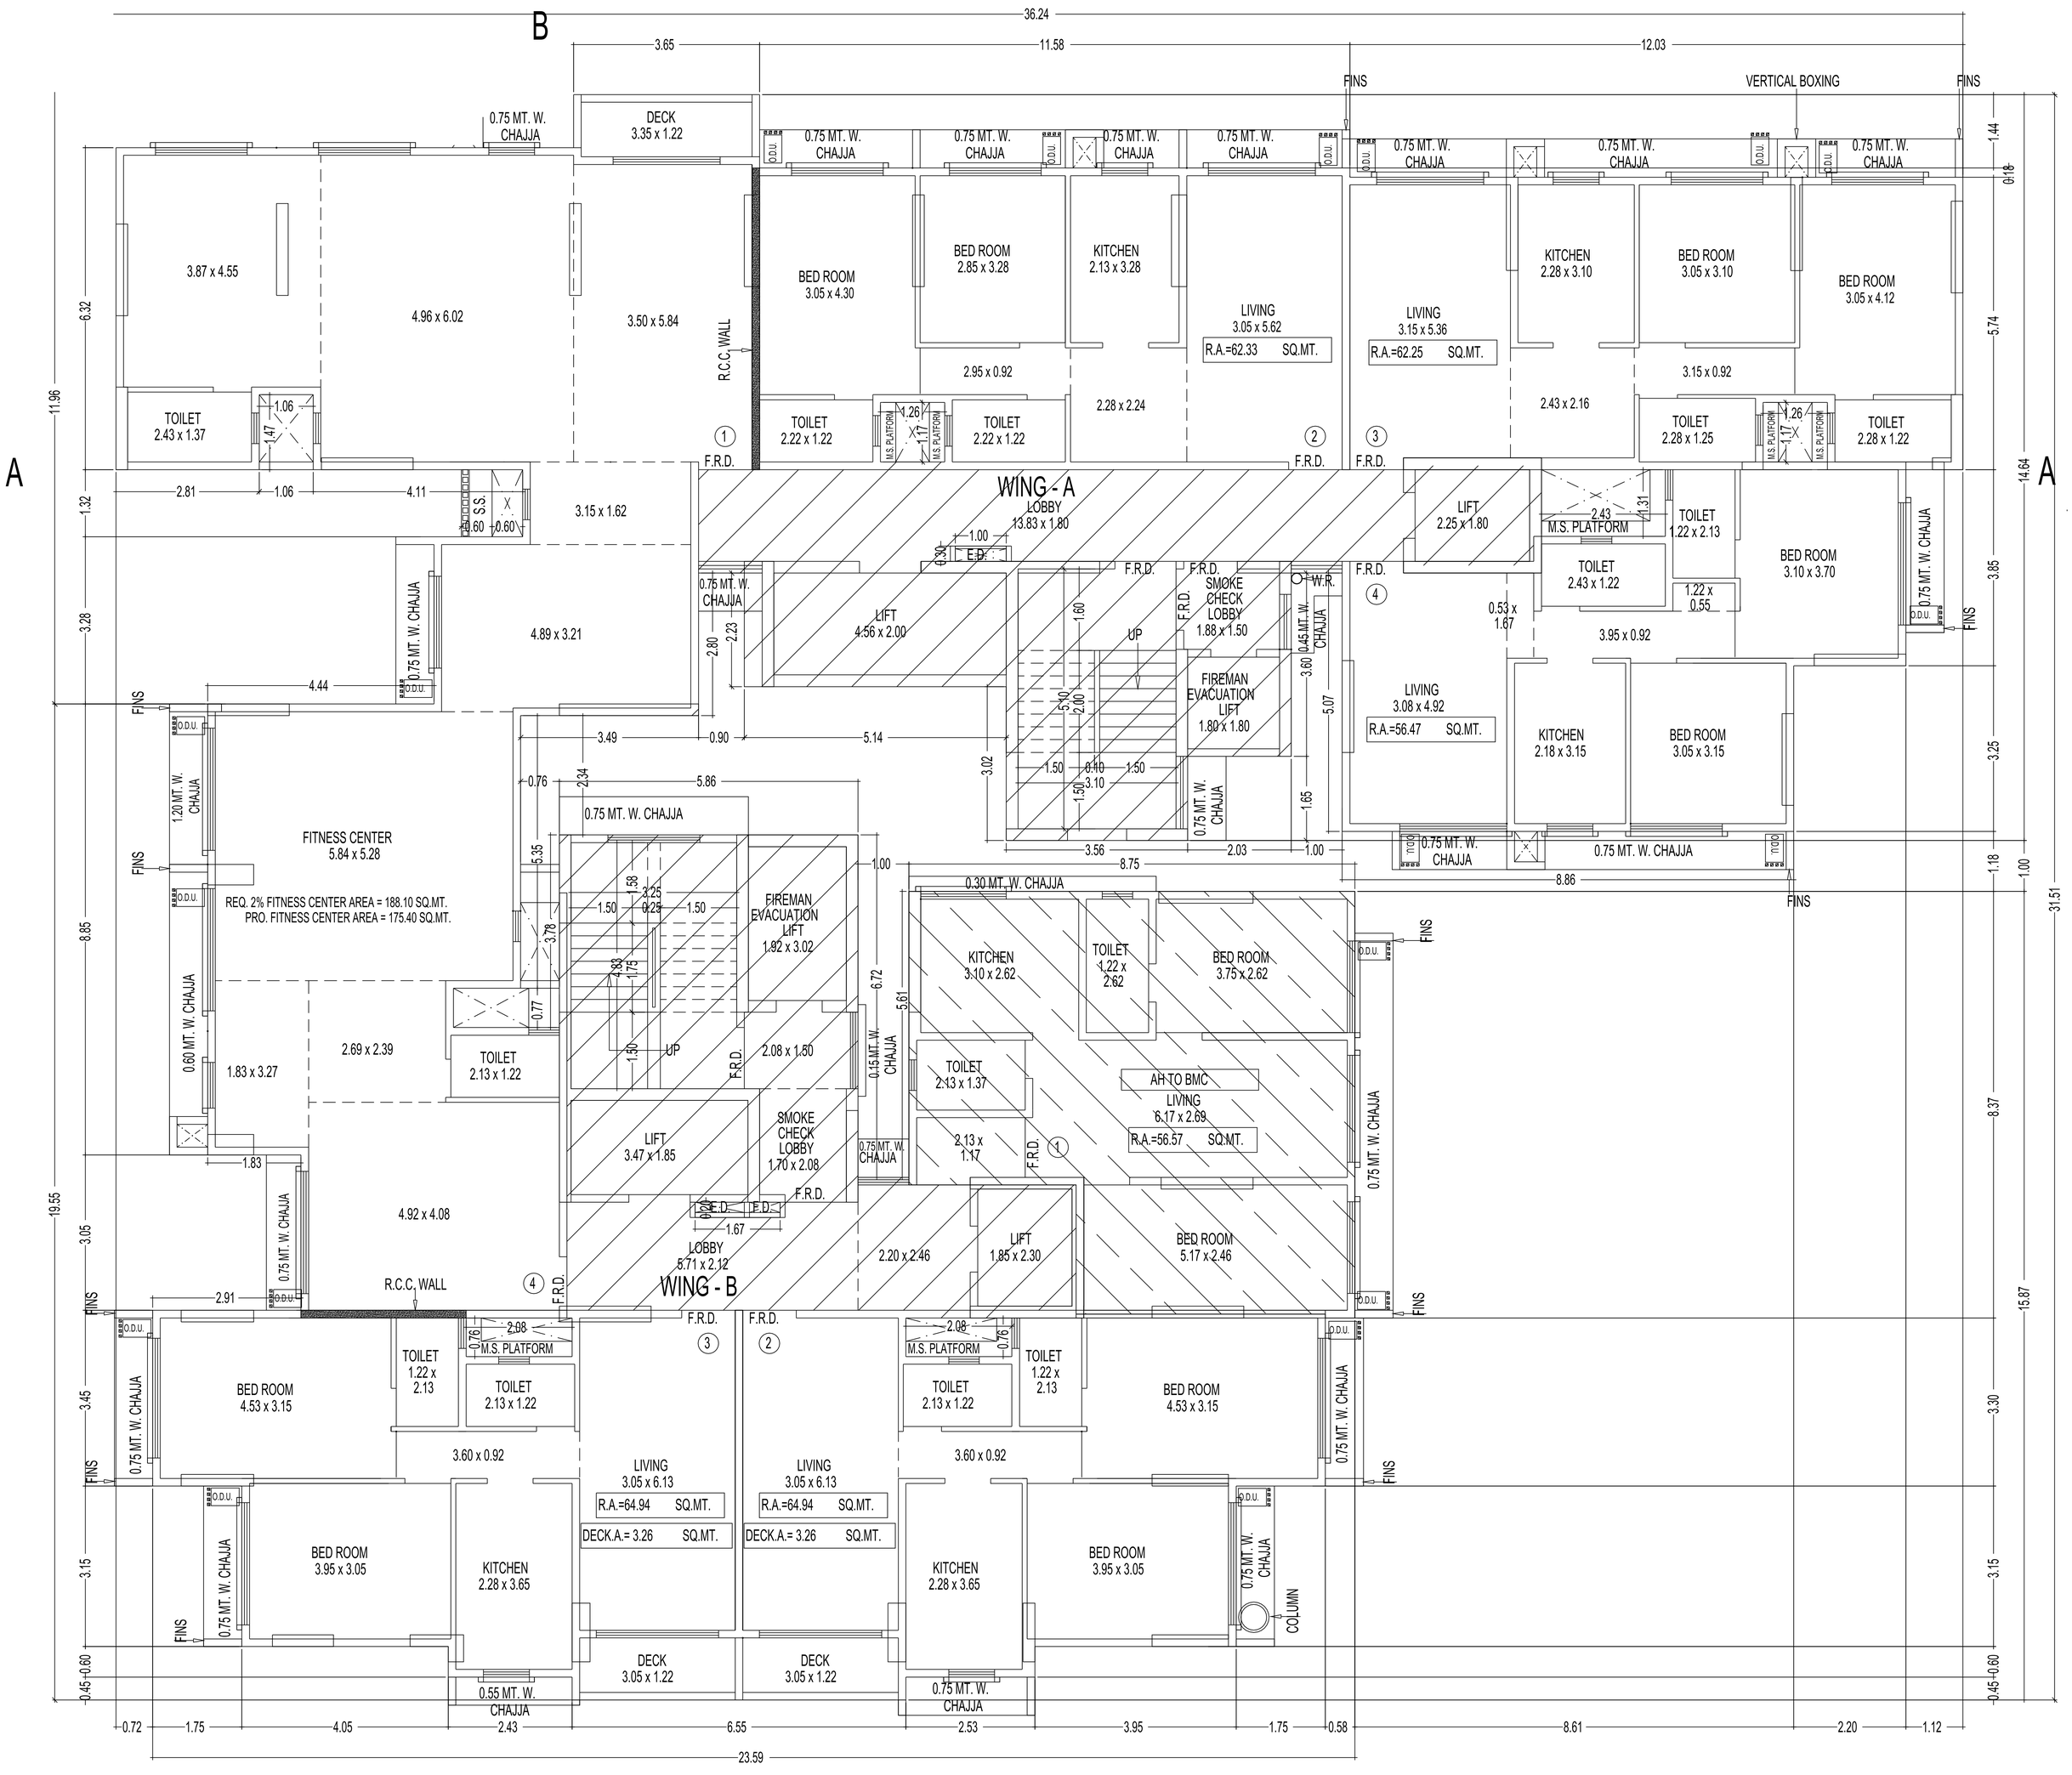

20TH FLOOR PLAN

SCALE :- 1:100

B