
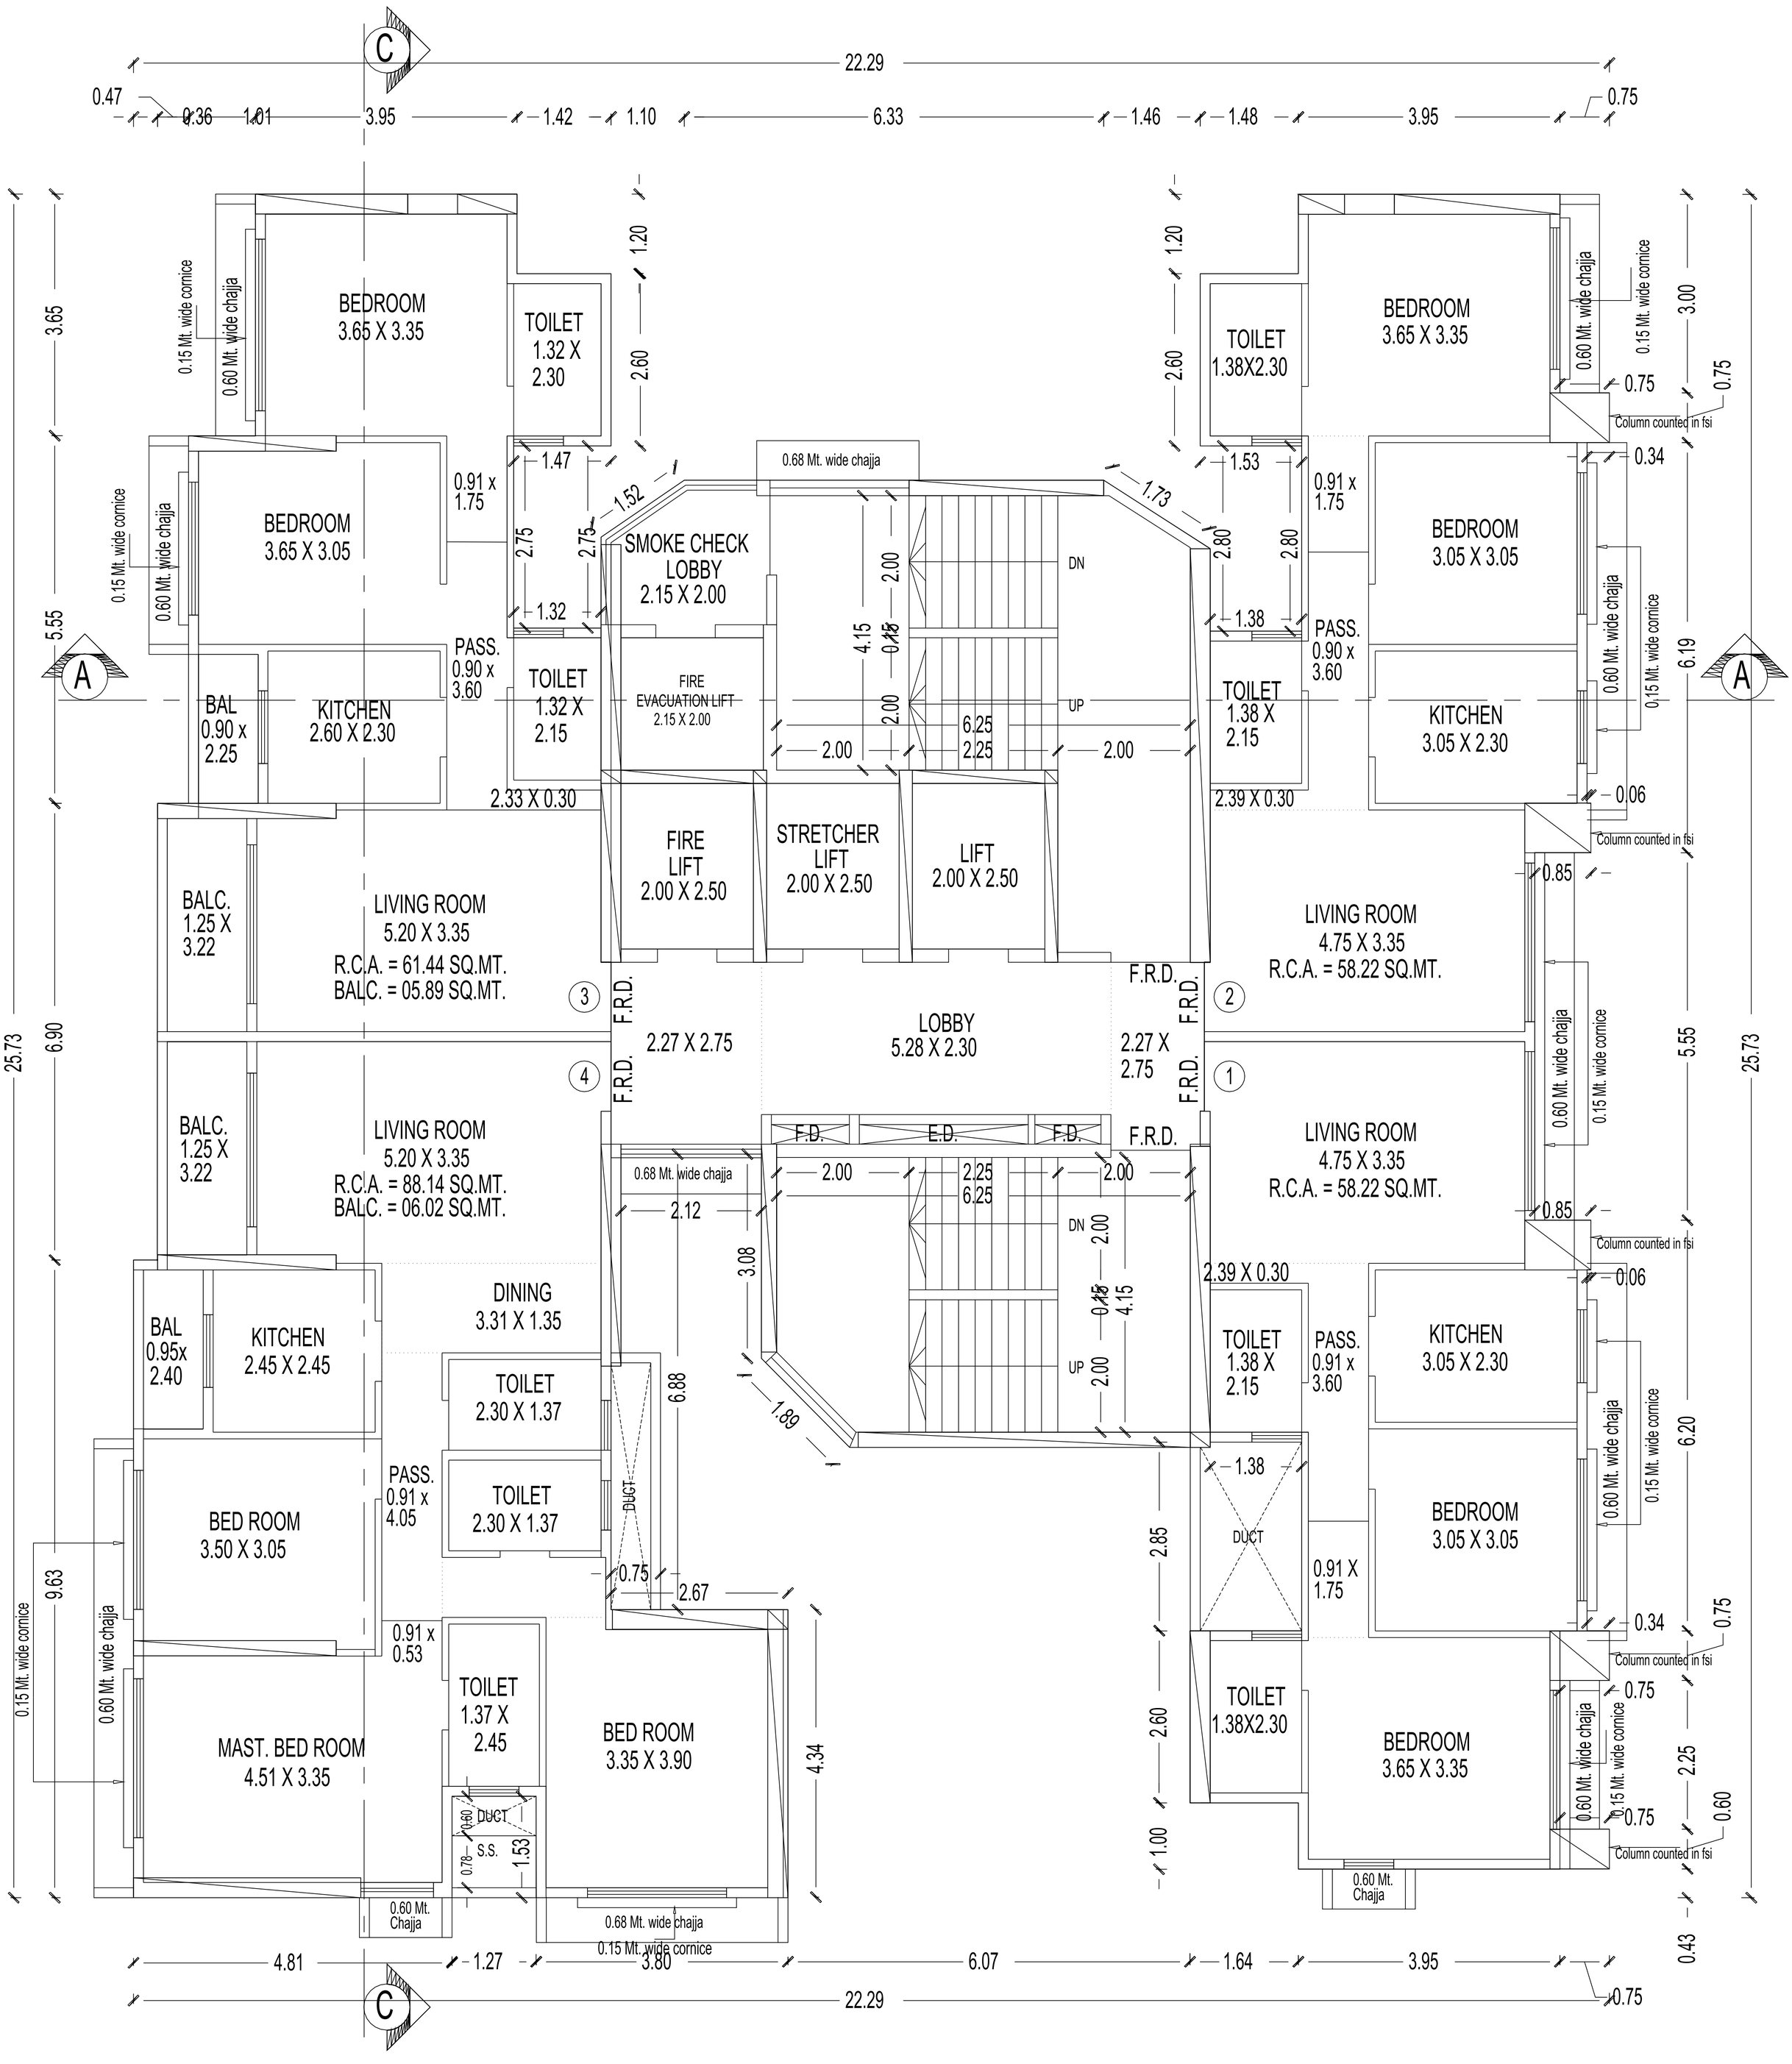


1ST, 2ND, 4TH TO 9TH 11TH TO 16TH FLOOR PLAN

SCALE :- 1:100

WING - A

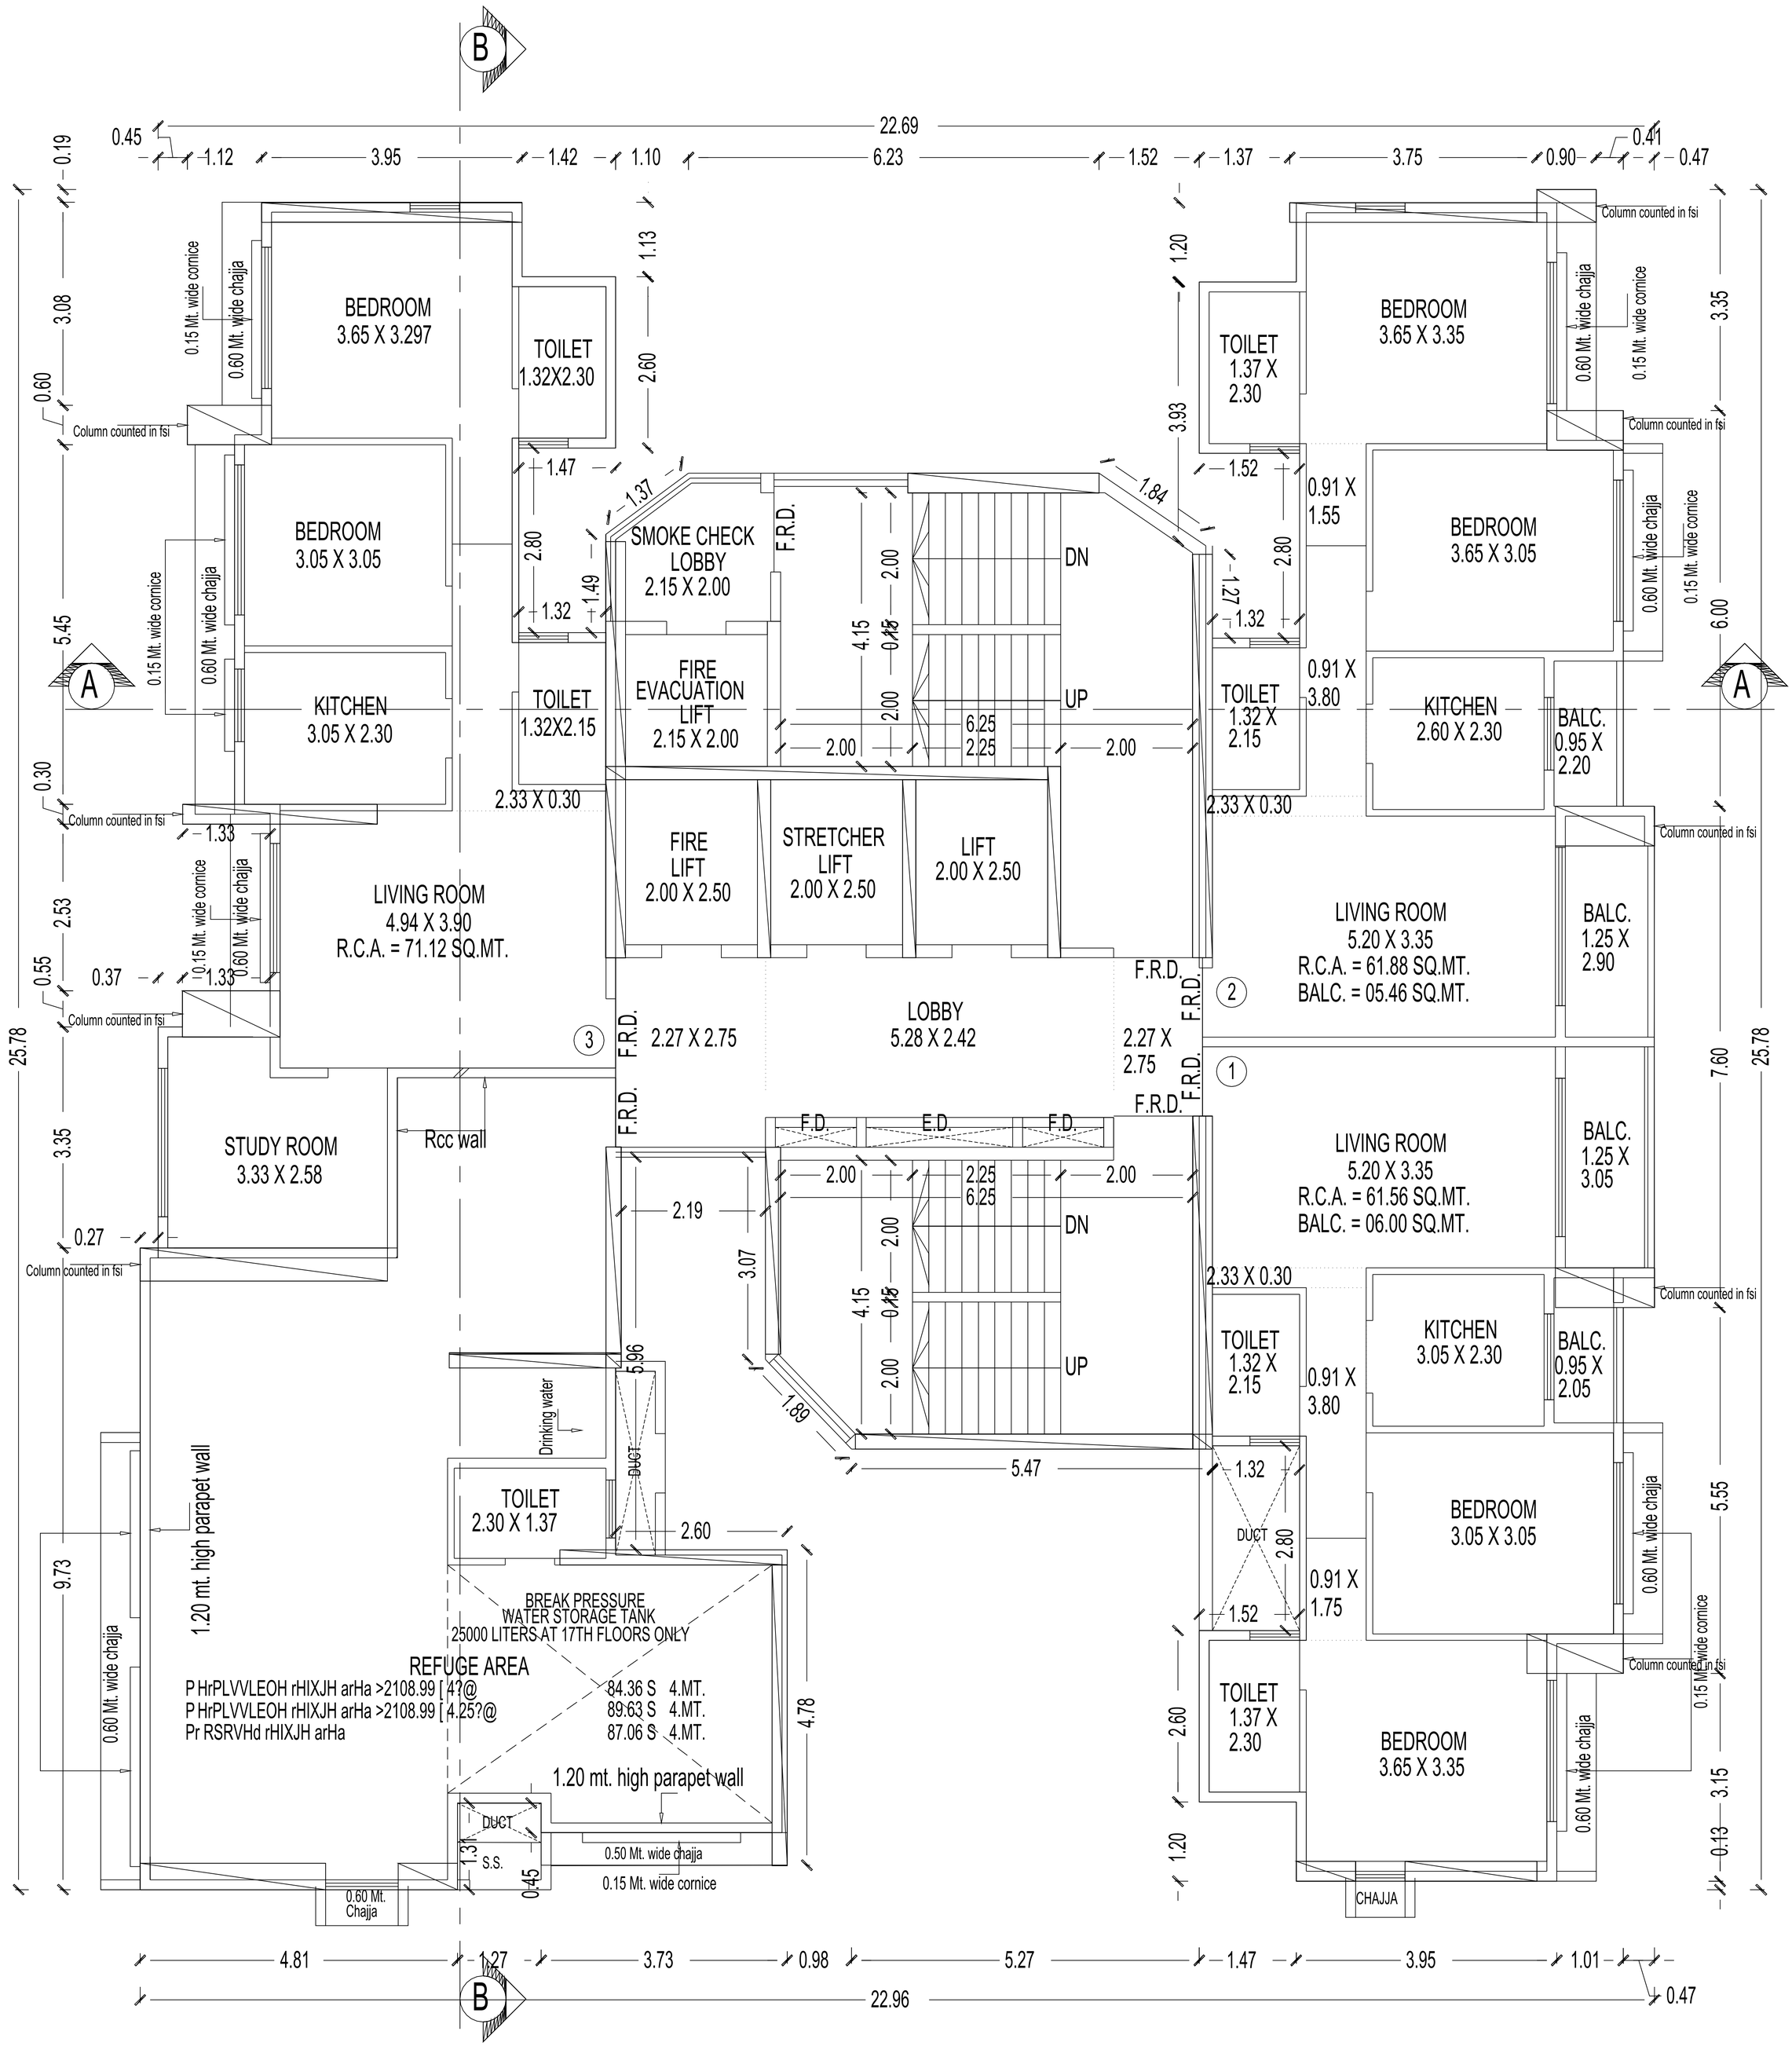

3RD &10TH (REFUGE) FLOOR PLAN

SCALE :- 1:100

WING - B

P HrPLVVLEOH rHIXJH arHa >2051.86 [4?@ 82.07 S 4.MT.
P HrPLVVLEOH rHIXJH arHa >2051.86 [4.25?@ 87.20 S 4.MT.
Pr RSRVHd rHIXJH arHa 82.95 S 4.MT.

3RD & 10TH (REFUGE) FLOOR PLAN

SCALE :- 1:100 WING - A

BREAK PRESSURE
WATER STORAGE TANK
25000 LITERS AT 17TH FLOORS ONLY

1.20 mt. high parapet wall

1.20 mt. high parapet wall

1.20 mt. high parapet wall

1.50 mt. high parapet wall

1.50 mt. high parapet wall

1.50 mt. high parapet wall

SMOKE CHECK
LOBBY
2.15 X 2.00

Drinking water

FIRE
EVACUATION LIFT
2.15 X 2.00

FIRE
LIFT
2.00 X 2.50

STRETCHER
LIFT
2.00 X 2.50

LIFT
2.00 X 2.50

DUCT

DUCT

DN

UP

DN

UP

0.68 Mt. wide chajja

0.68 Mt. wide chajja

REFUGE AREA

P HrPLVVLEOH rHIXJH arHa >1341.88 [4?@	53.68 S	4.MT.
P HrPLVVLEOH rHIXJH arHa >1341.88 [4.25?@	57.03 S	4.MT.
Pr RSRVHd rHIXJH arHa	82.95 S	4.MT.
C RXQWHd LQ FSI rHIXJH arHa	25.92 S	4.MT.

Rcc wall

F.R.D.

F.R.D.

F.R.D.

F.R.D.

F.R.D.

F.R.D.

F.R.D.

F.D.

F.D.

F.D.

2.27 X 2.75

LOBBY
5.28 X 2.30

2.27 X
2.75

TOILET
1.38X2.30

BEDROOM
3.65 X 3.35

0.60 Mt. wide chajja

0.15 Mt. wide cornice

Column counted in fsi

PASS.
0.90 x
3.60

BEDROOM
3.05 X 3.05

TOILET
1.38 X
2.15

KITCHEN
3.05 X 2.30

2.39 X 0.30

Column counted in fsi

LIVING ROOM
4.75 X 3.35
R.C.A. = 58.22 SQ.MT.

0.91 x
1.75

LIVING ROOM
4.75 X 3.35
R.C.A. = 58.22 SQ.MT.

2.39 X 0.30

Column counted in fsi

TOILET
1.38 X
2.15

PASS.
0.91 x
3.60

KITCHEN
3.05 X 2.30

DUCT

BEDROOM
3.05 X 3.05

0.91 X
1.75

TOILET
1.38X2.30

BEDROOM
3.65 X 3.35

0.60 Mt.
Chajja

Column counted in fsi

Column counted in fsi

TERRACE OPEN TO SKY @ 17TH FLOOR

BELOW CHAJJA

BELOW
CHAJJA

BELOW CHAJJA

S.S.

22.29

22.29

17TH (REFUGE) FLOOR PLAN


SCALE :- 1:100

WING - A

17TH (REFUGE) FLOOR PLAN


SCALE :- 1:100

WING - B

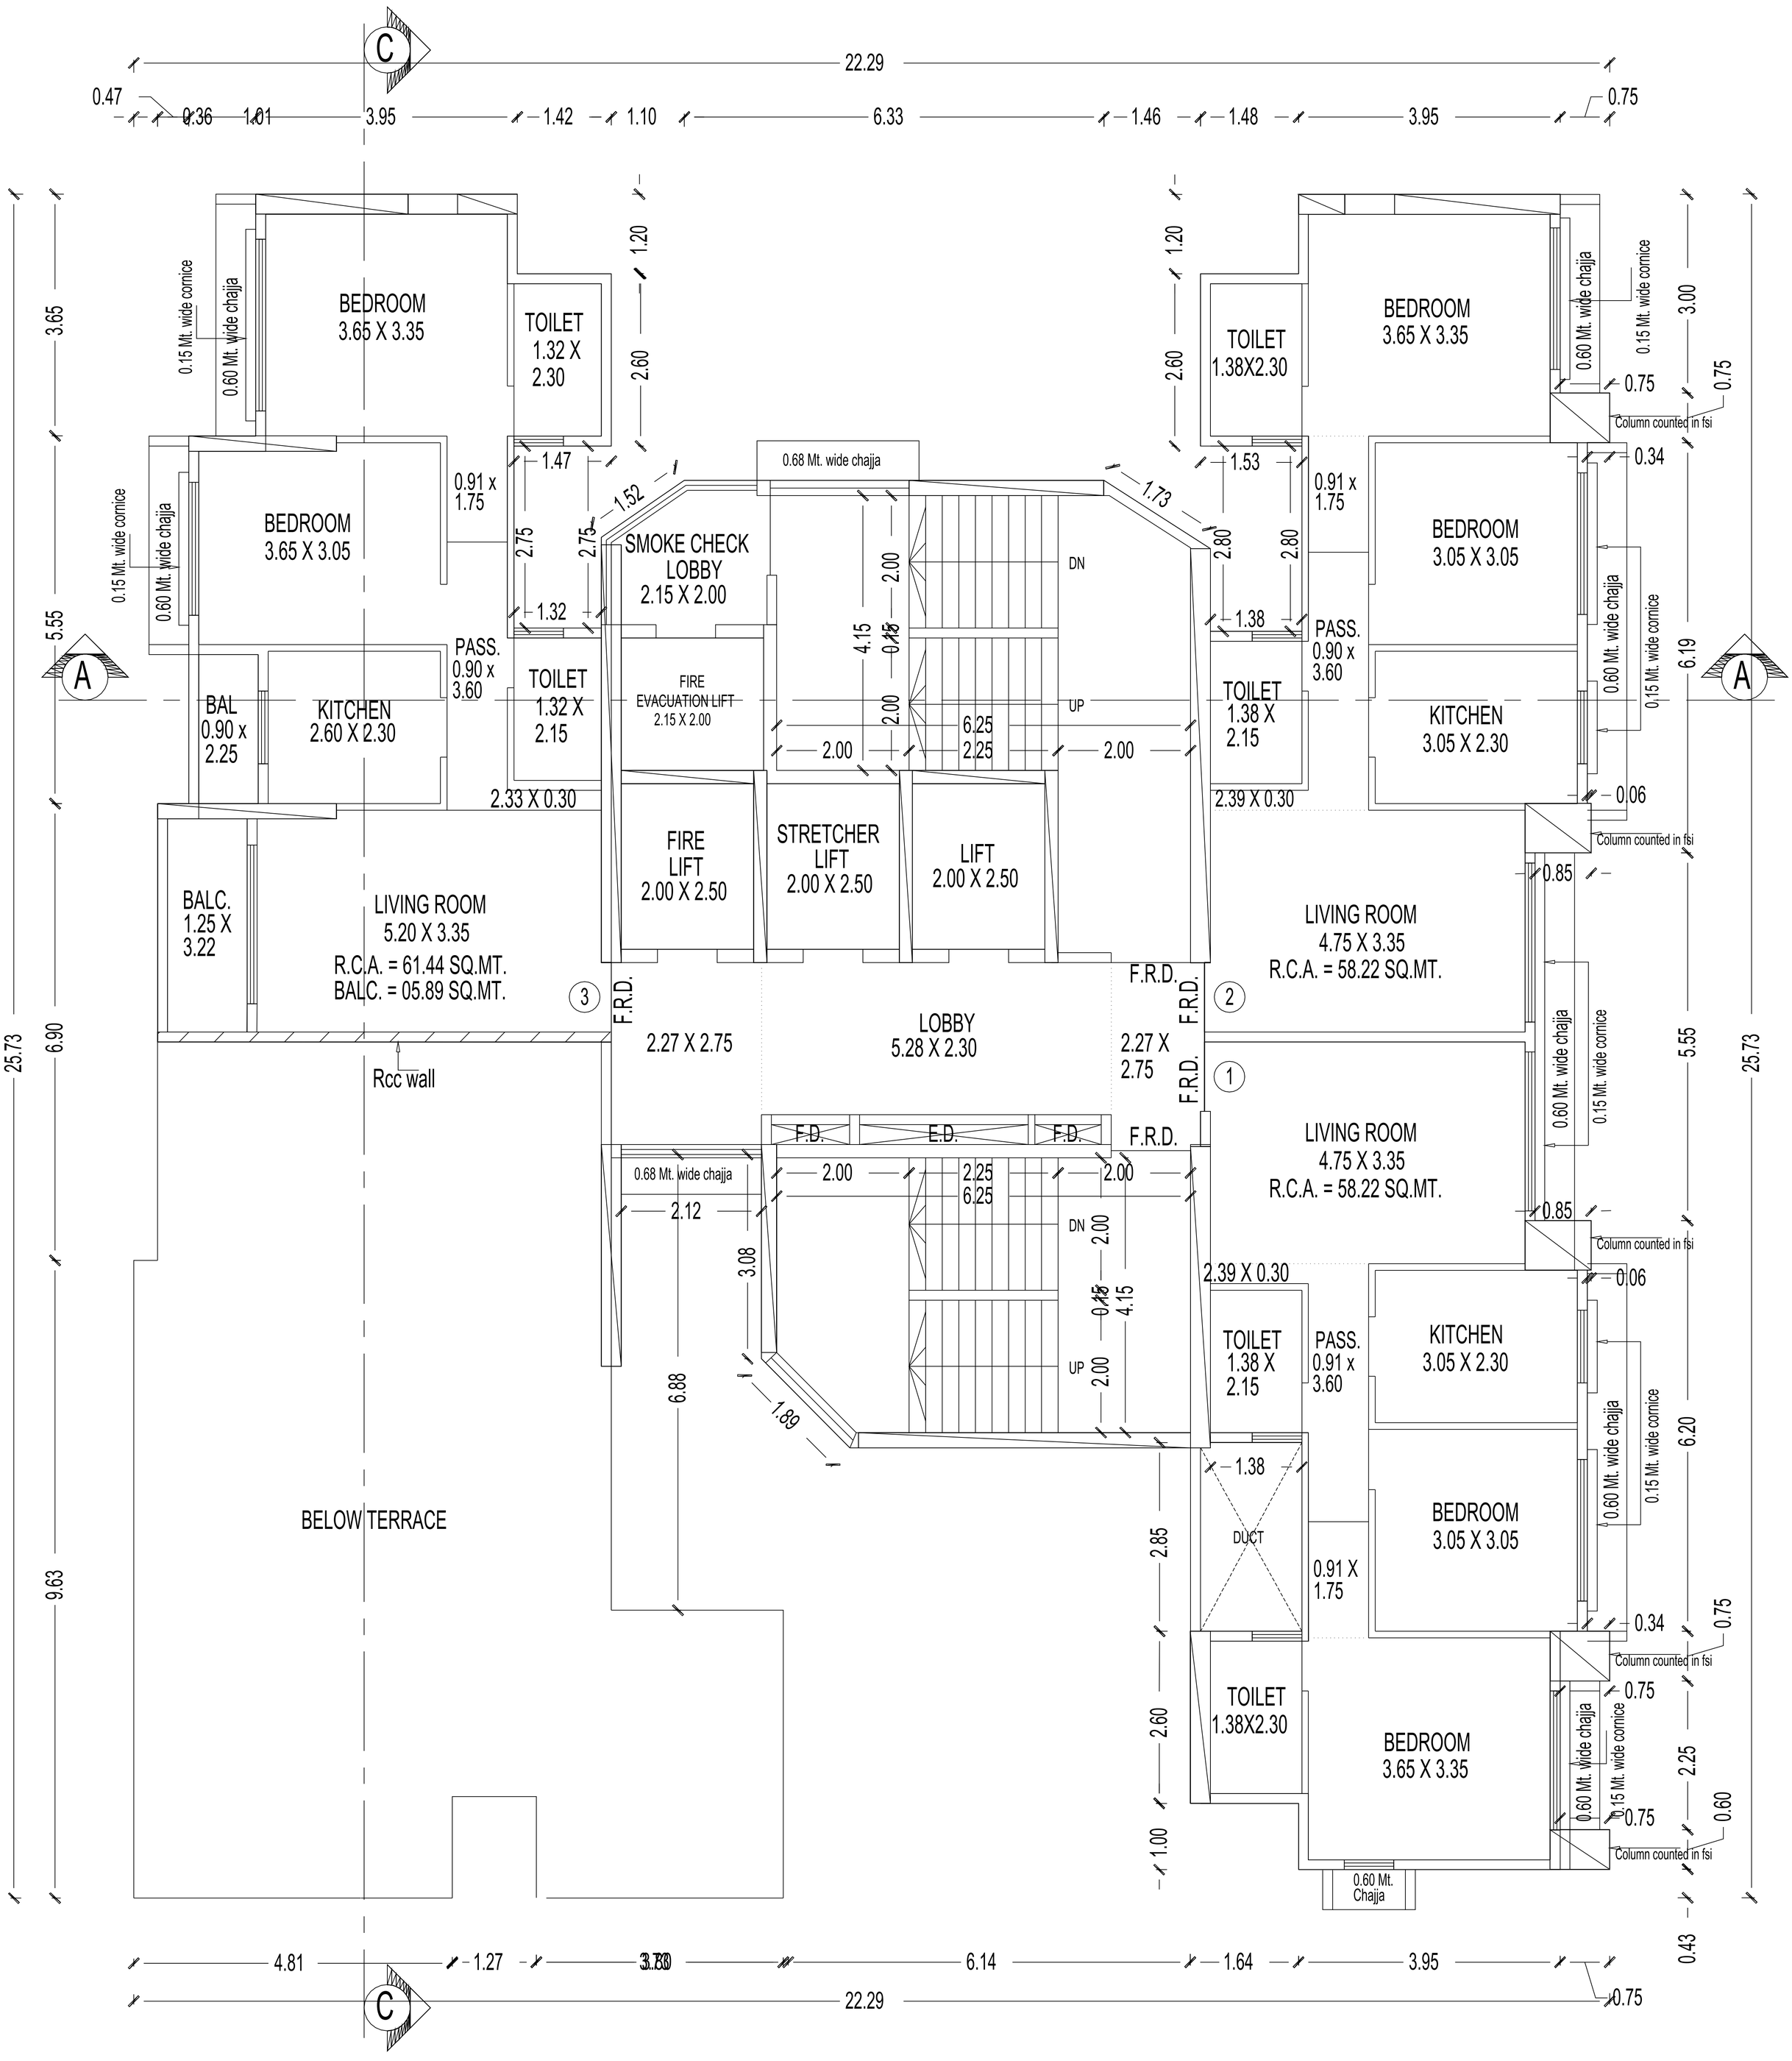

18TH FLOOR PLAN

SCALE :- 1:100 WING - A

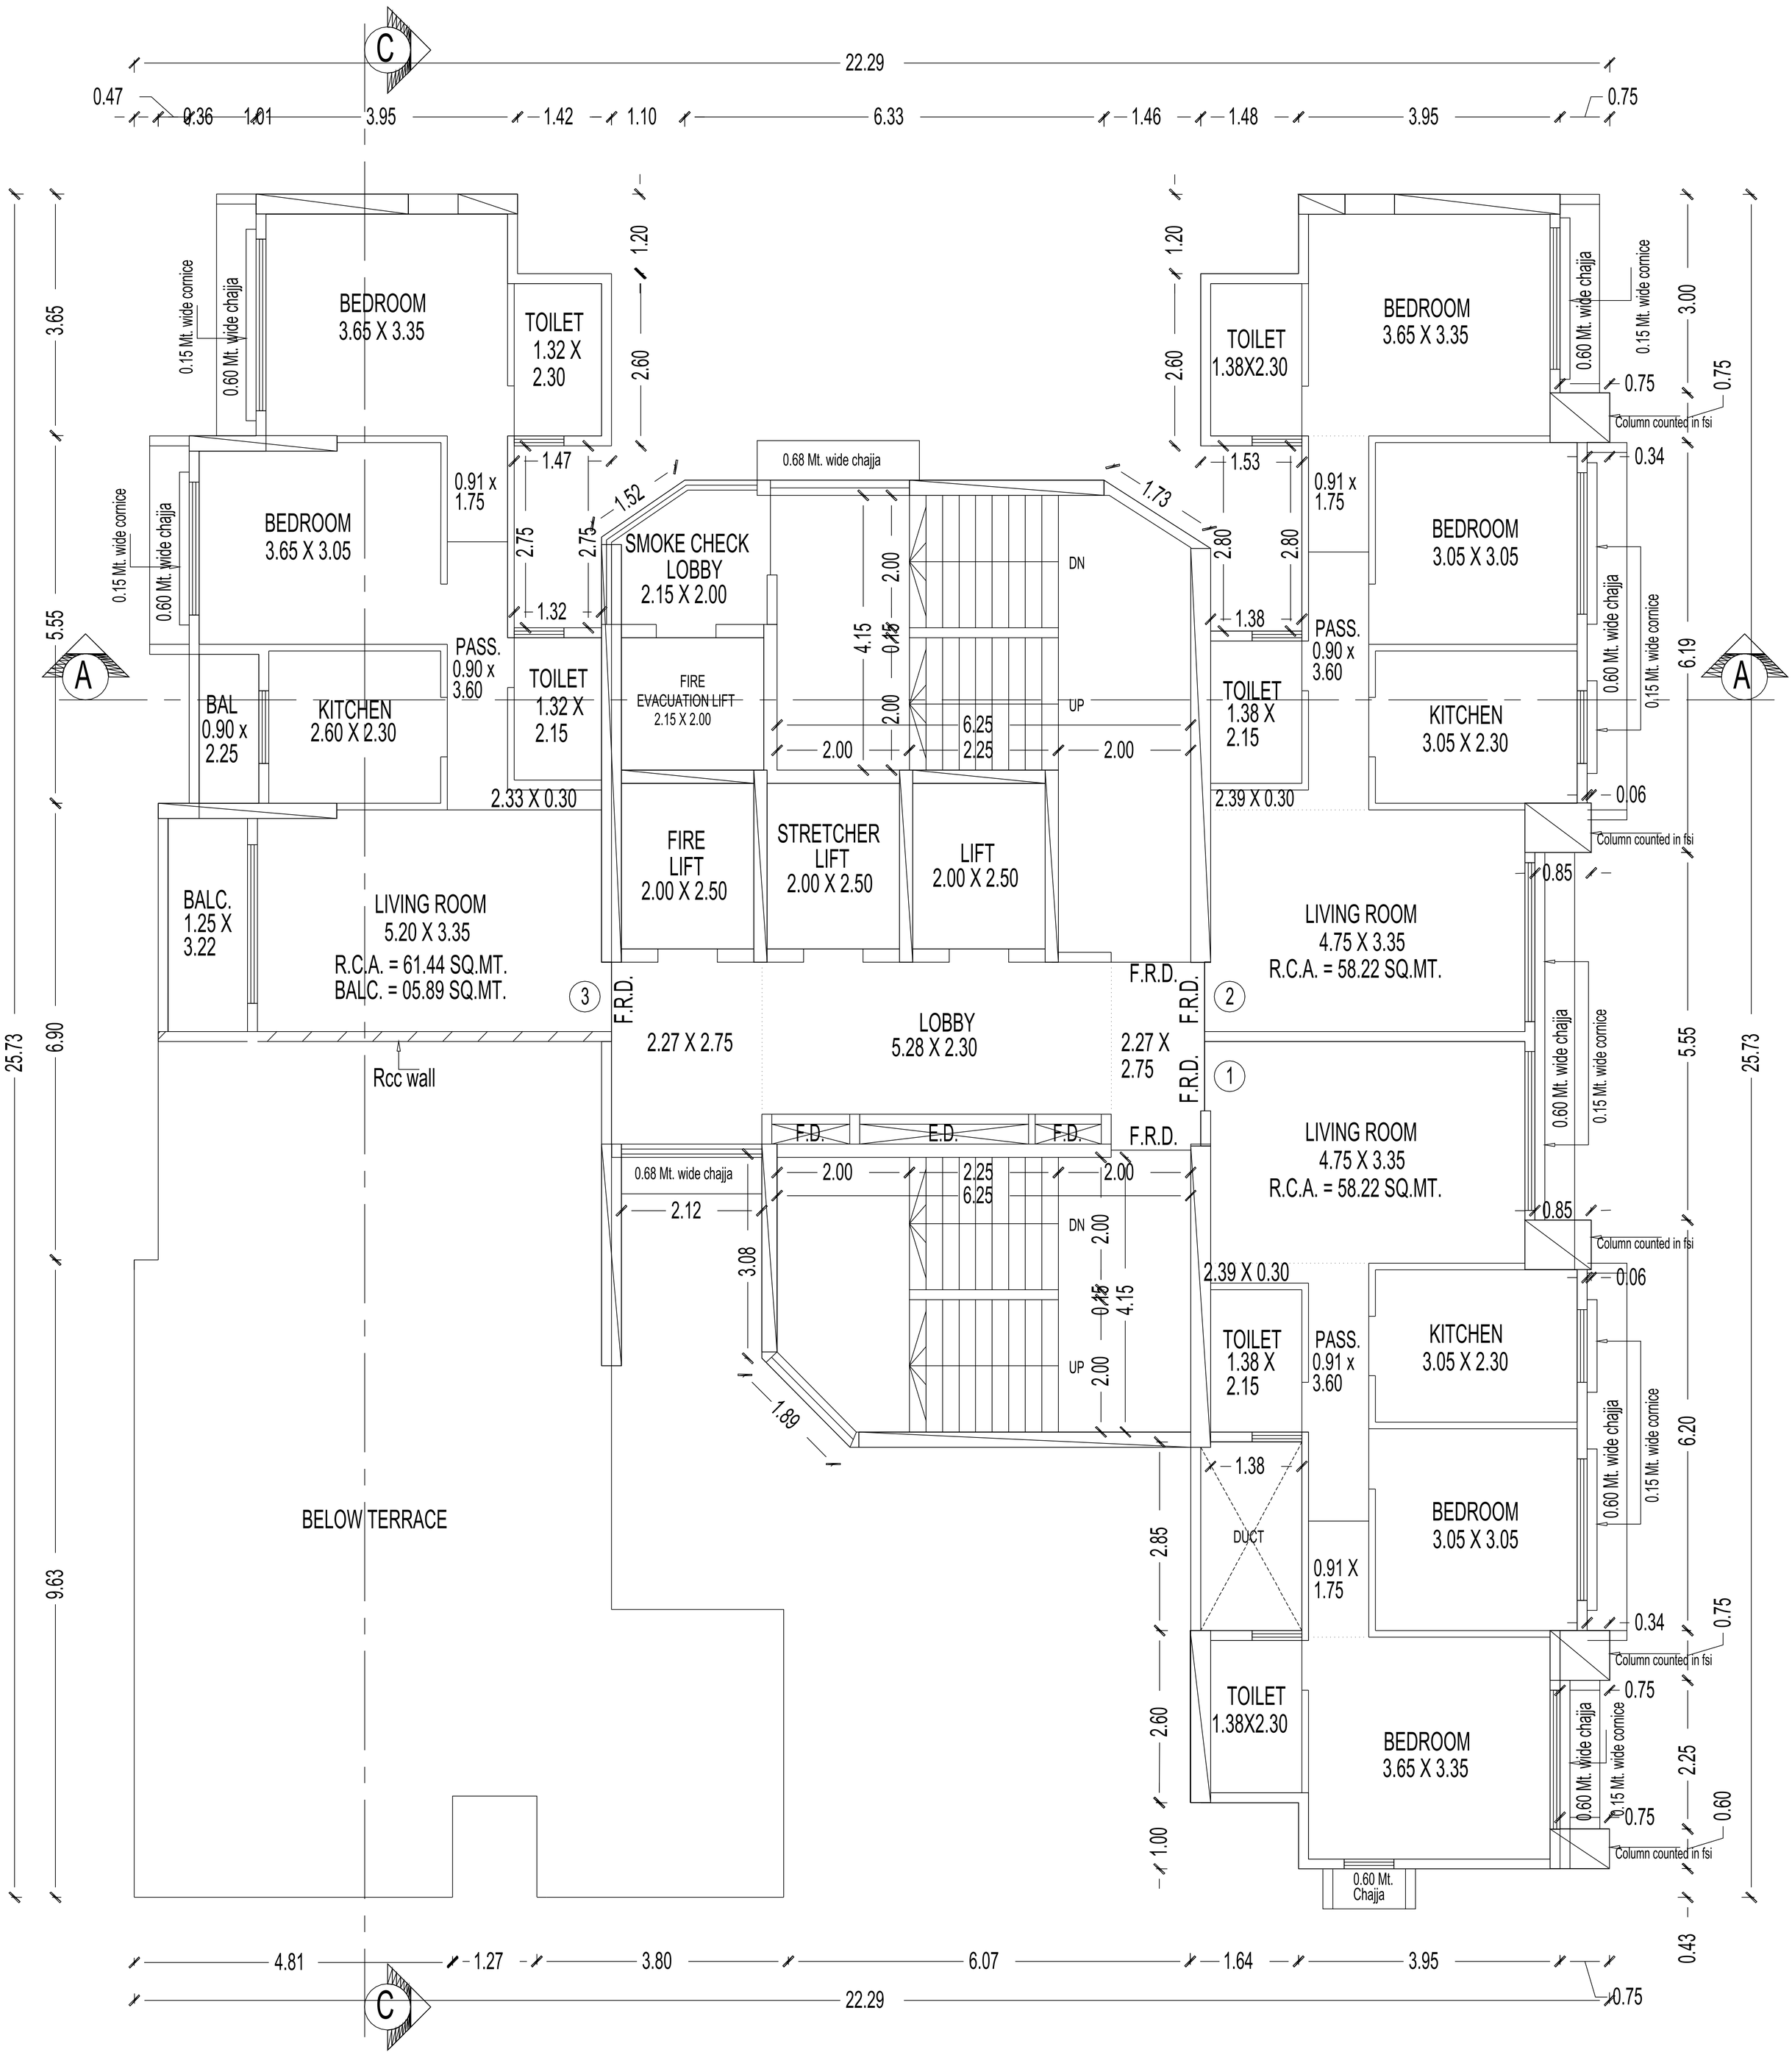

19TH TO 23RD FLOOR PLAN

SCALE :- 1:100

WING - A


22ND FLOOR PLAN

SCALE :- 1:100 WING - B

SHEET NO. 08 /18


FILE NO- P-20375/2024/(1007)/P/S Ward/PAHADI GOREGAON-W

NORTH

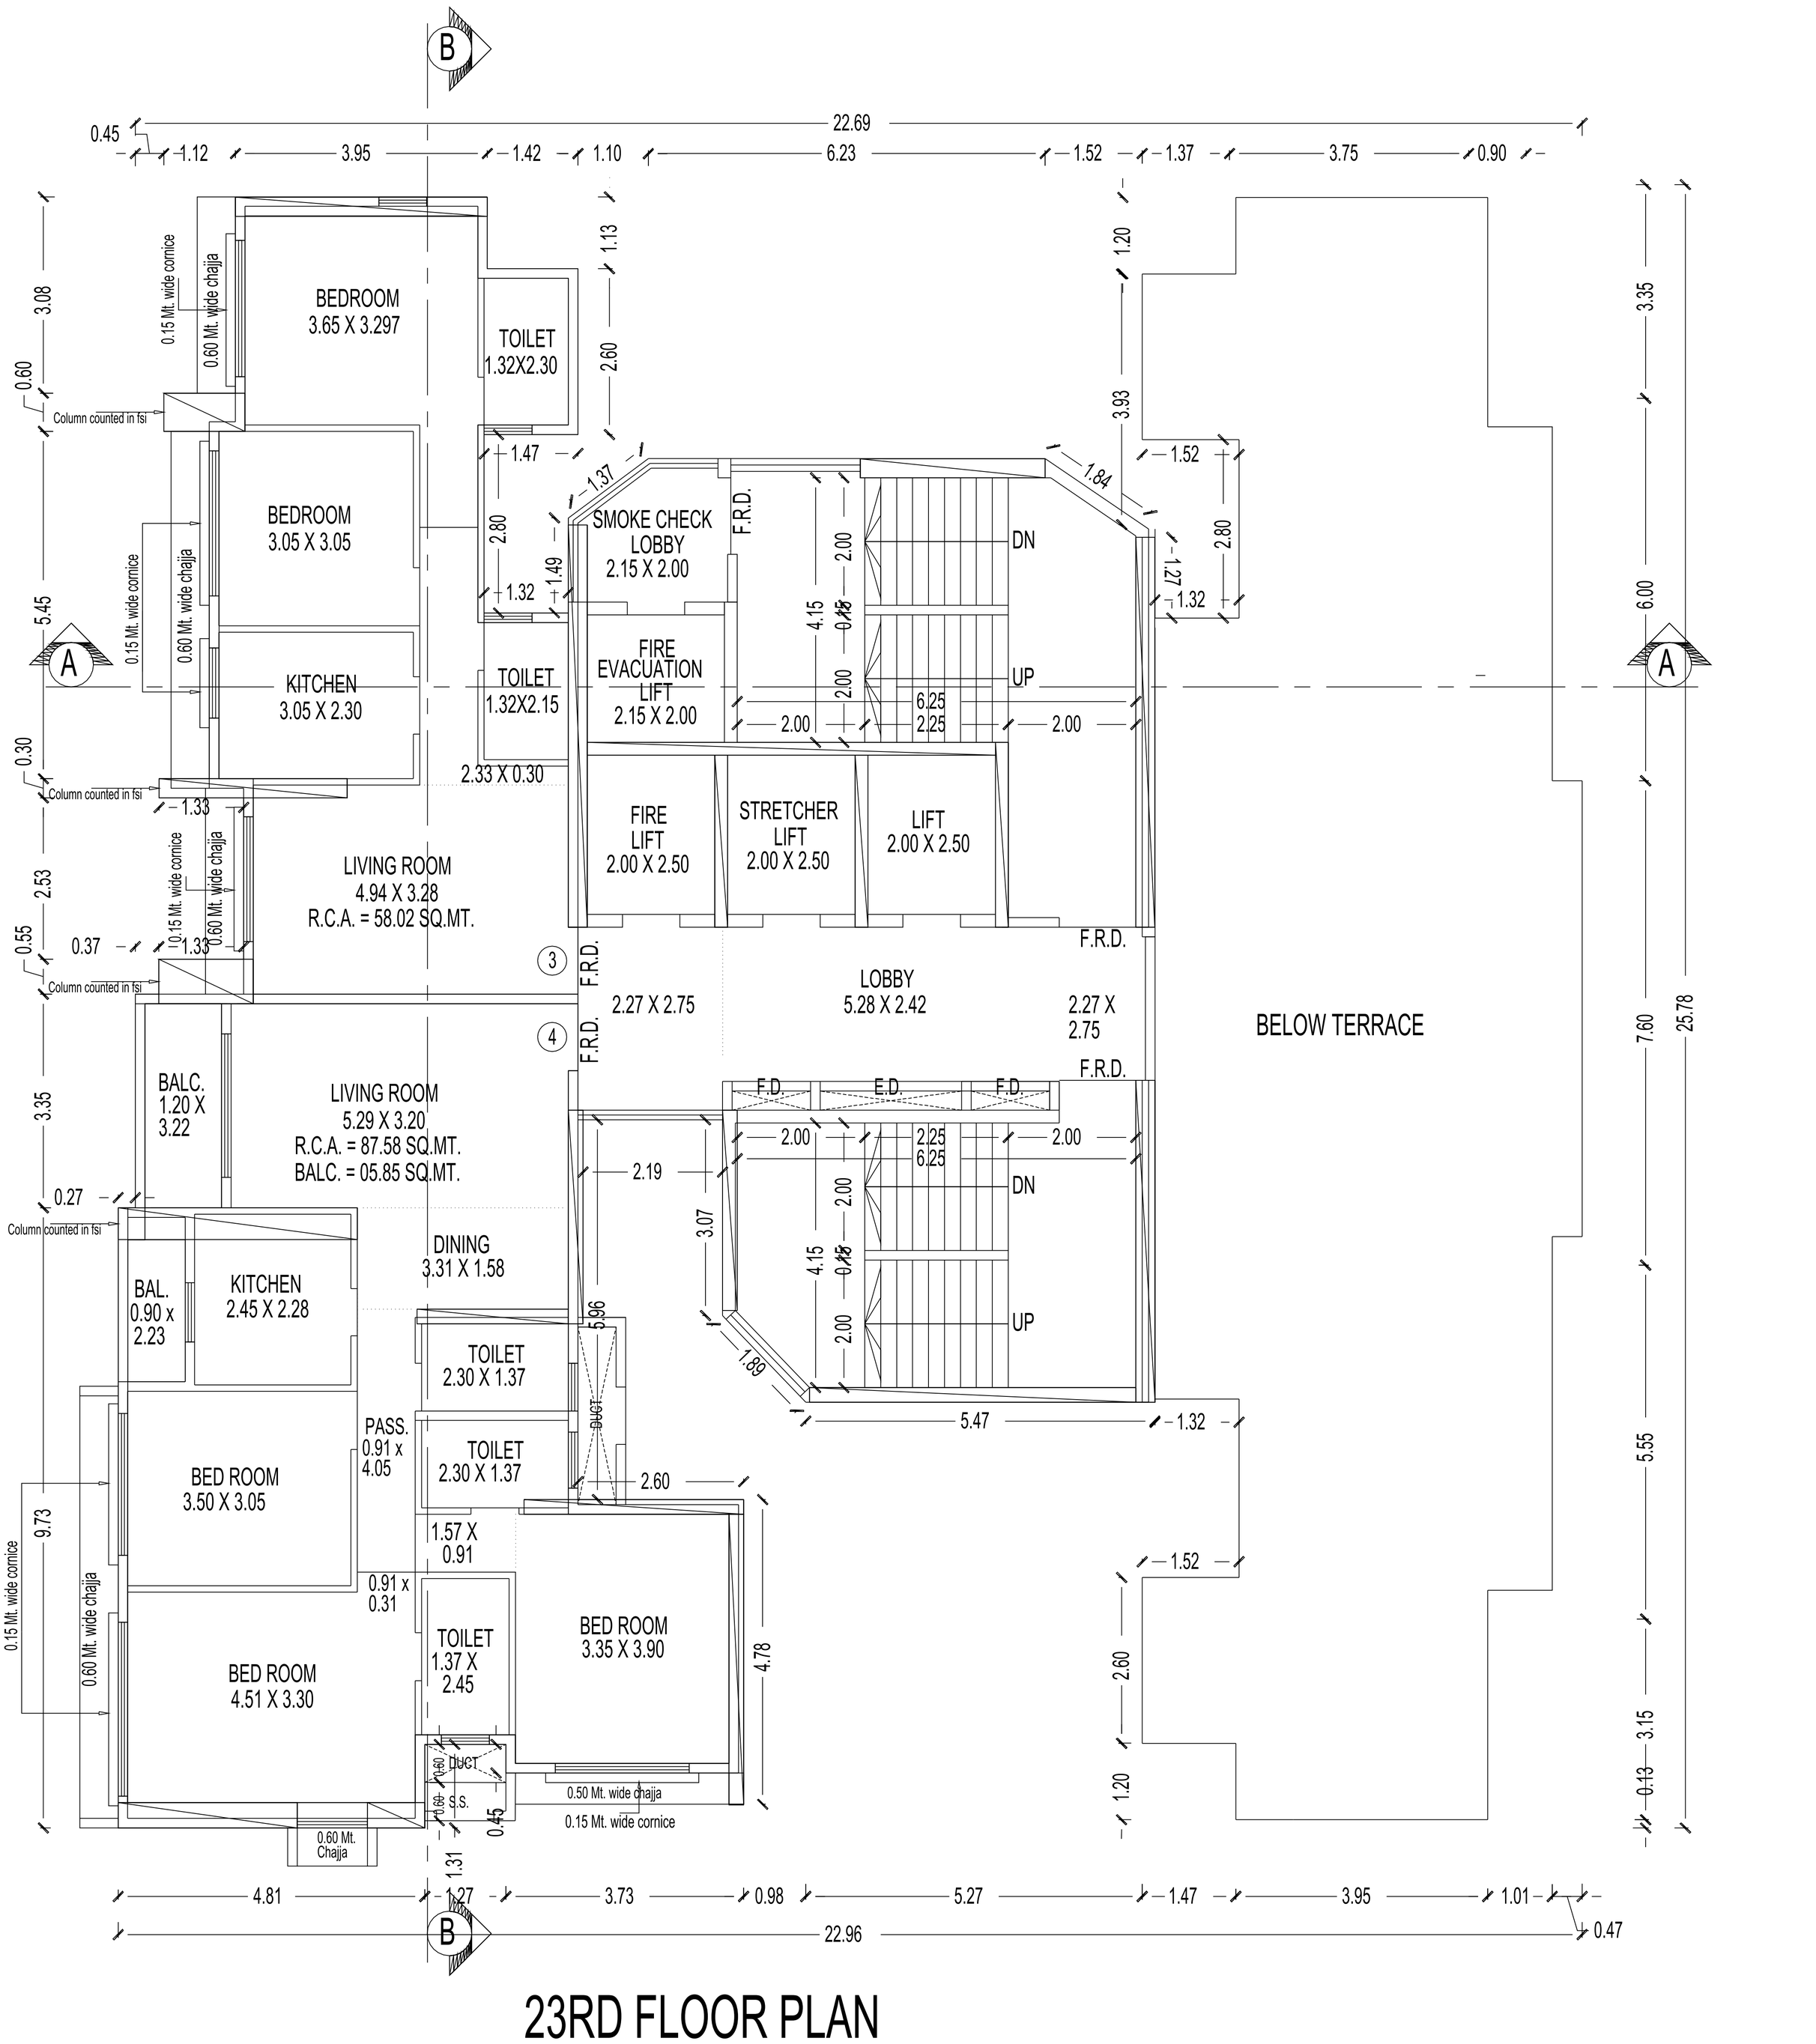

23RD FLOOR PLAN


SCALE :- 1:100 WING - B

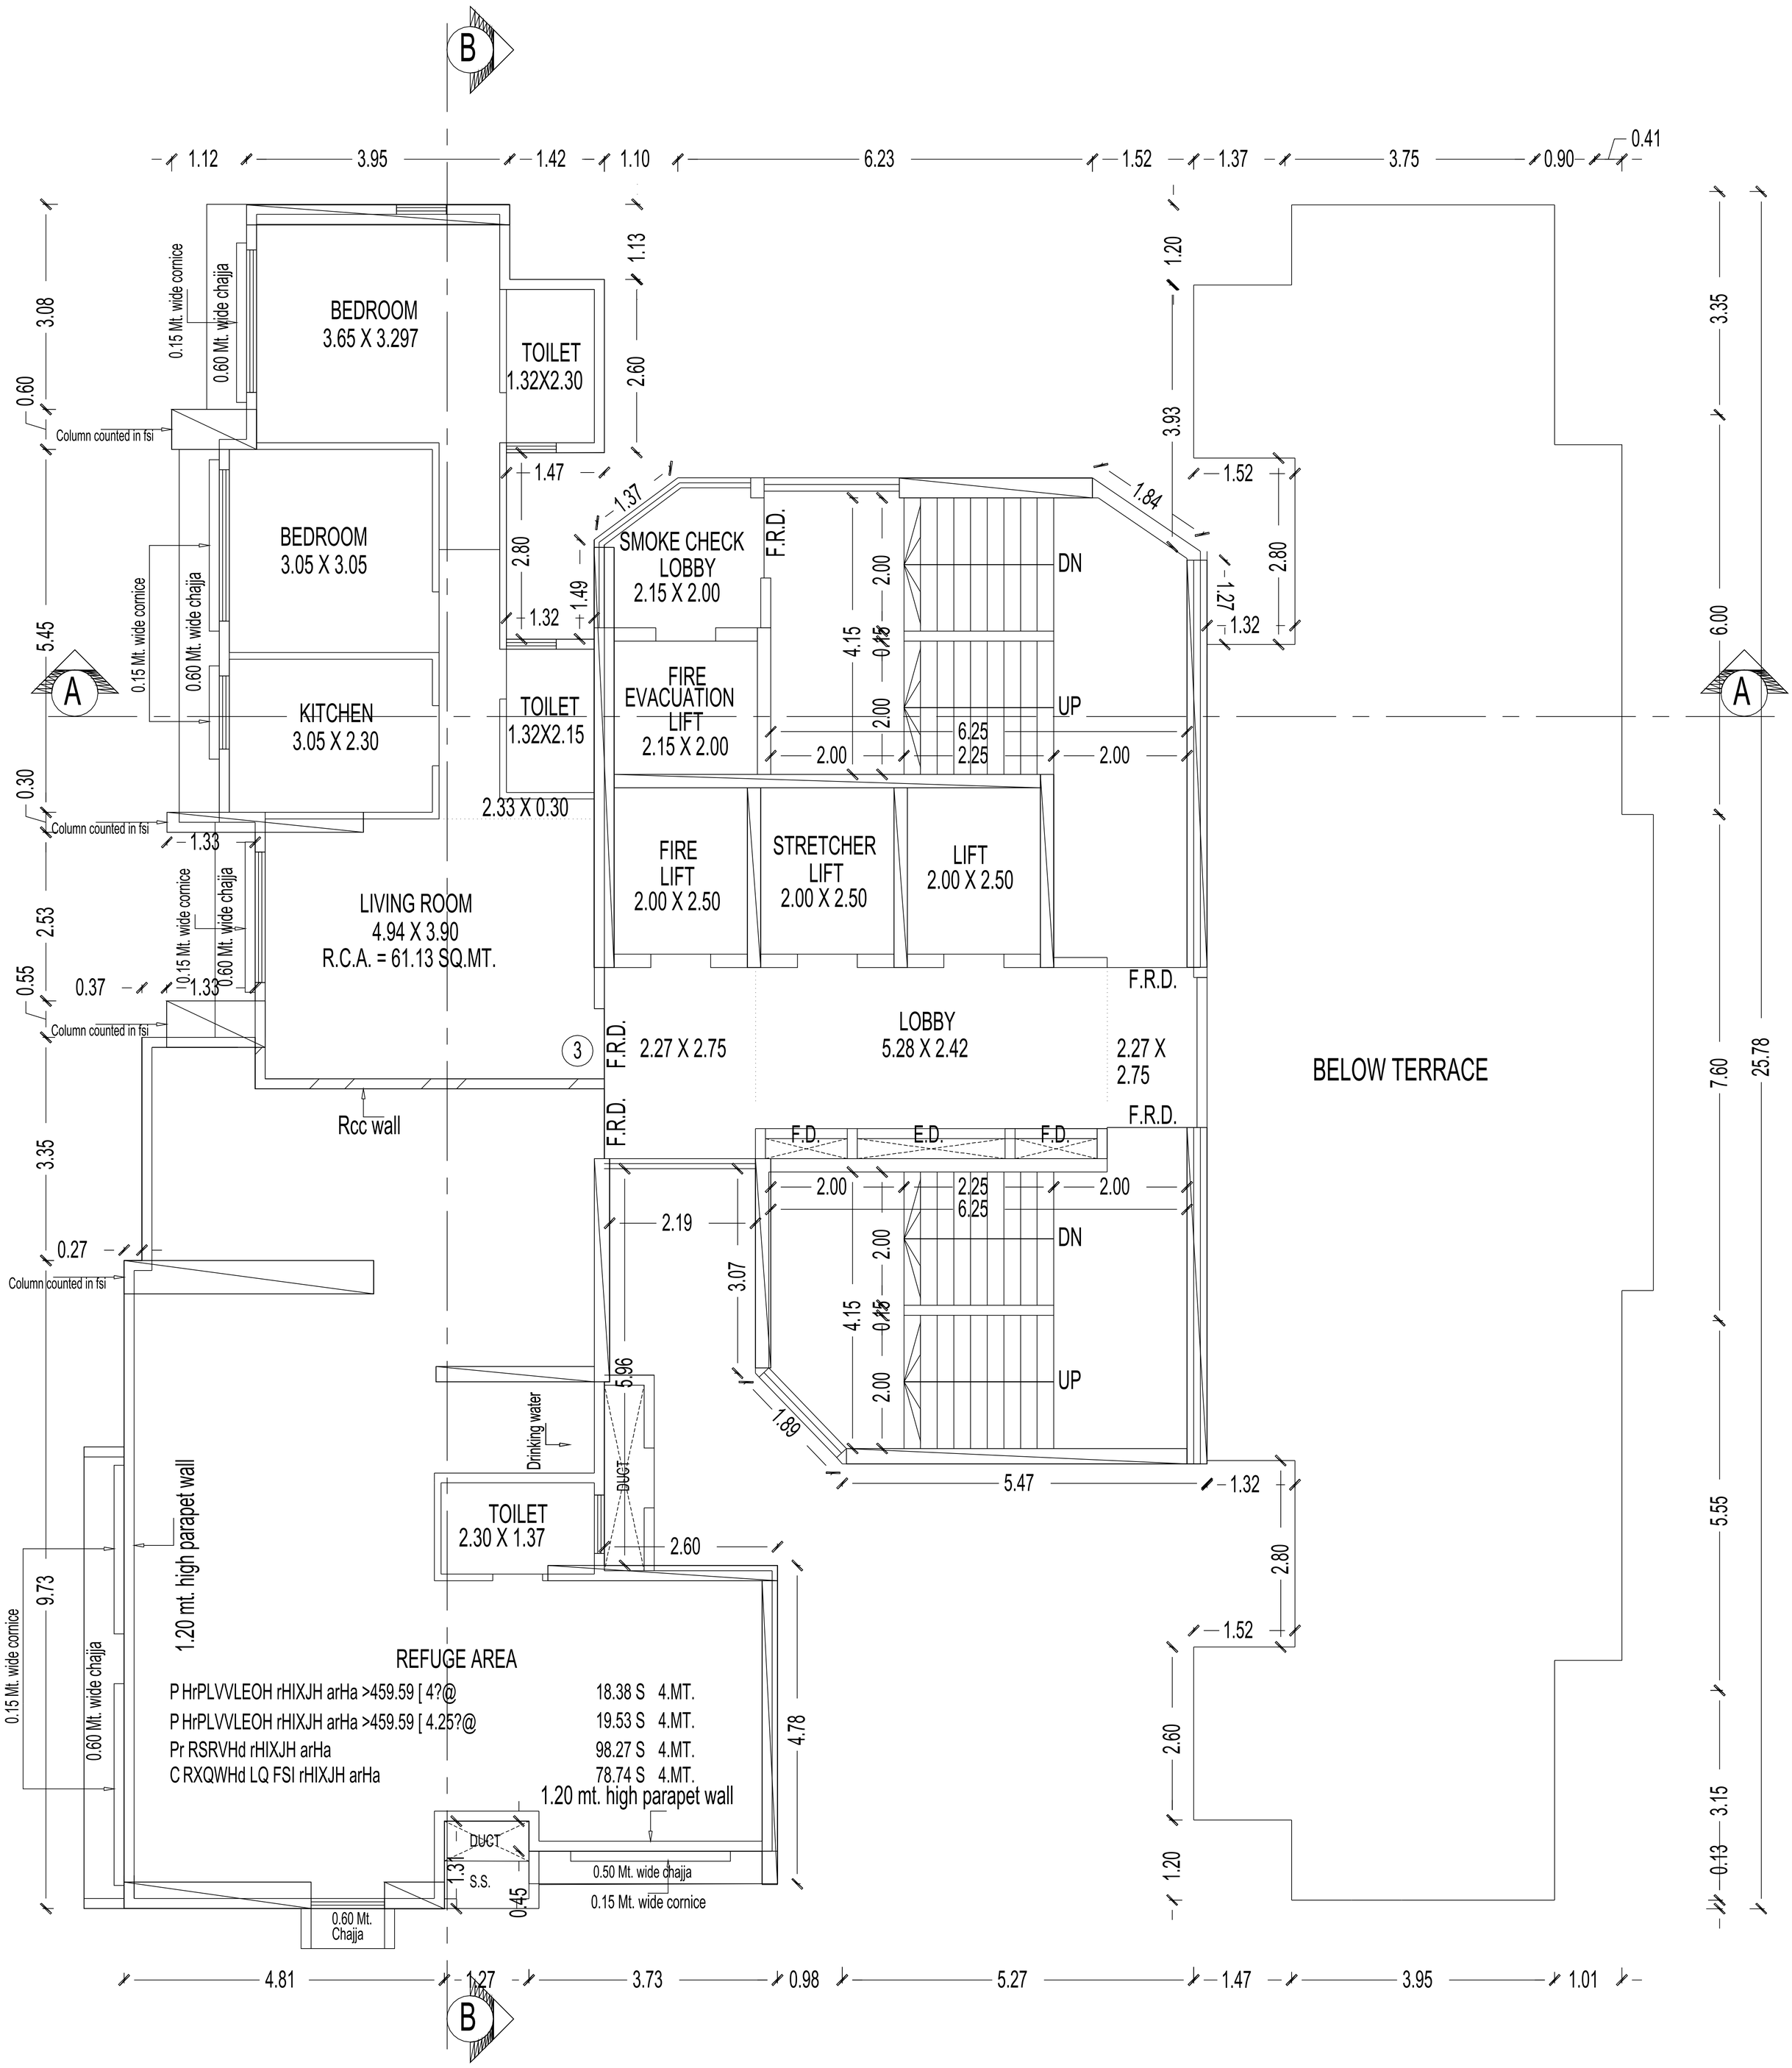

24TH (REFUGE) FLOOR PLAN

SCALE :- 1:100

WING - B

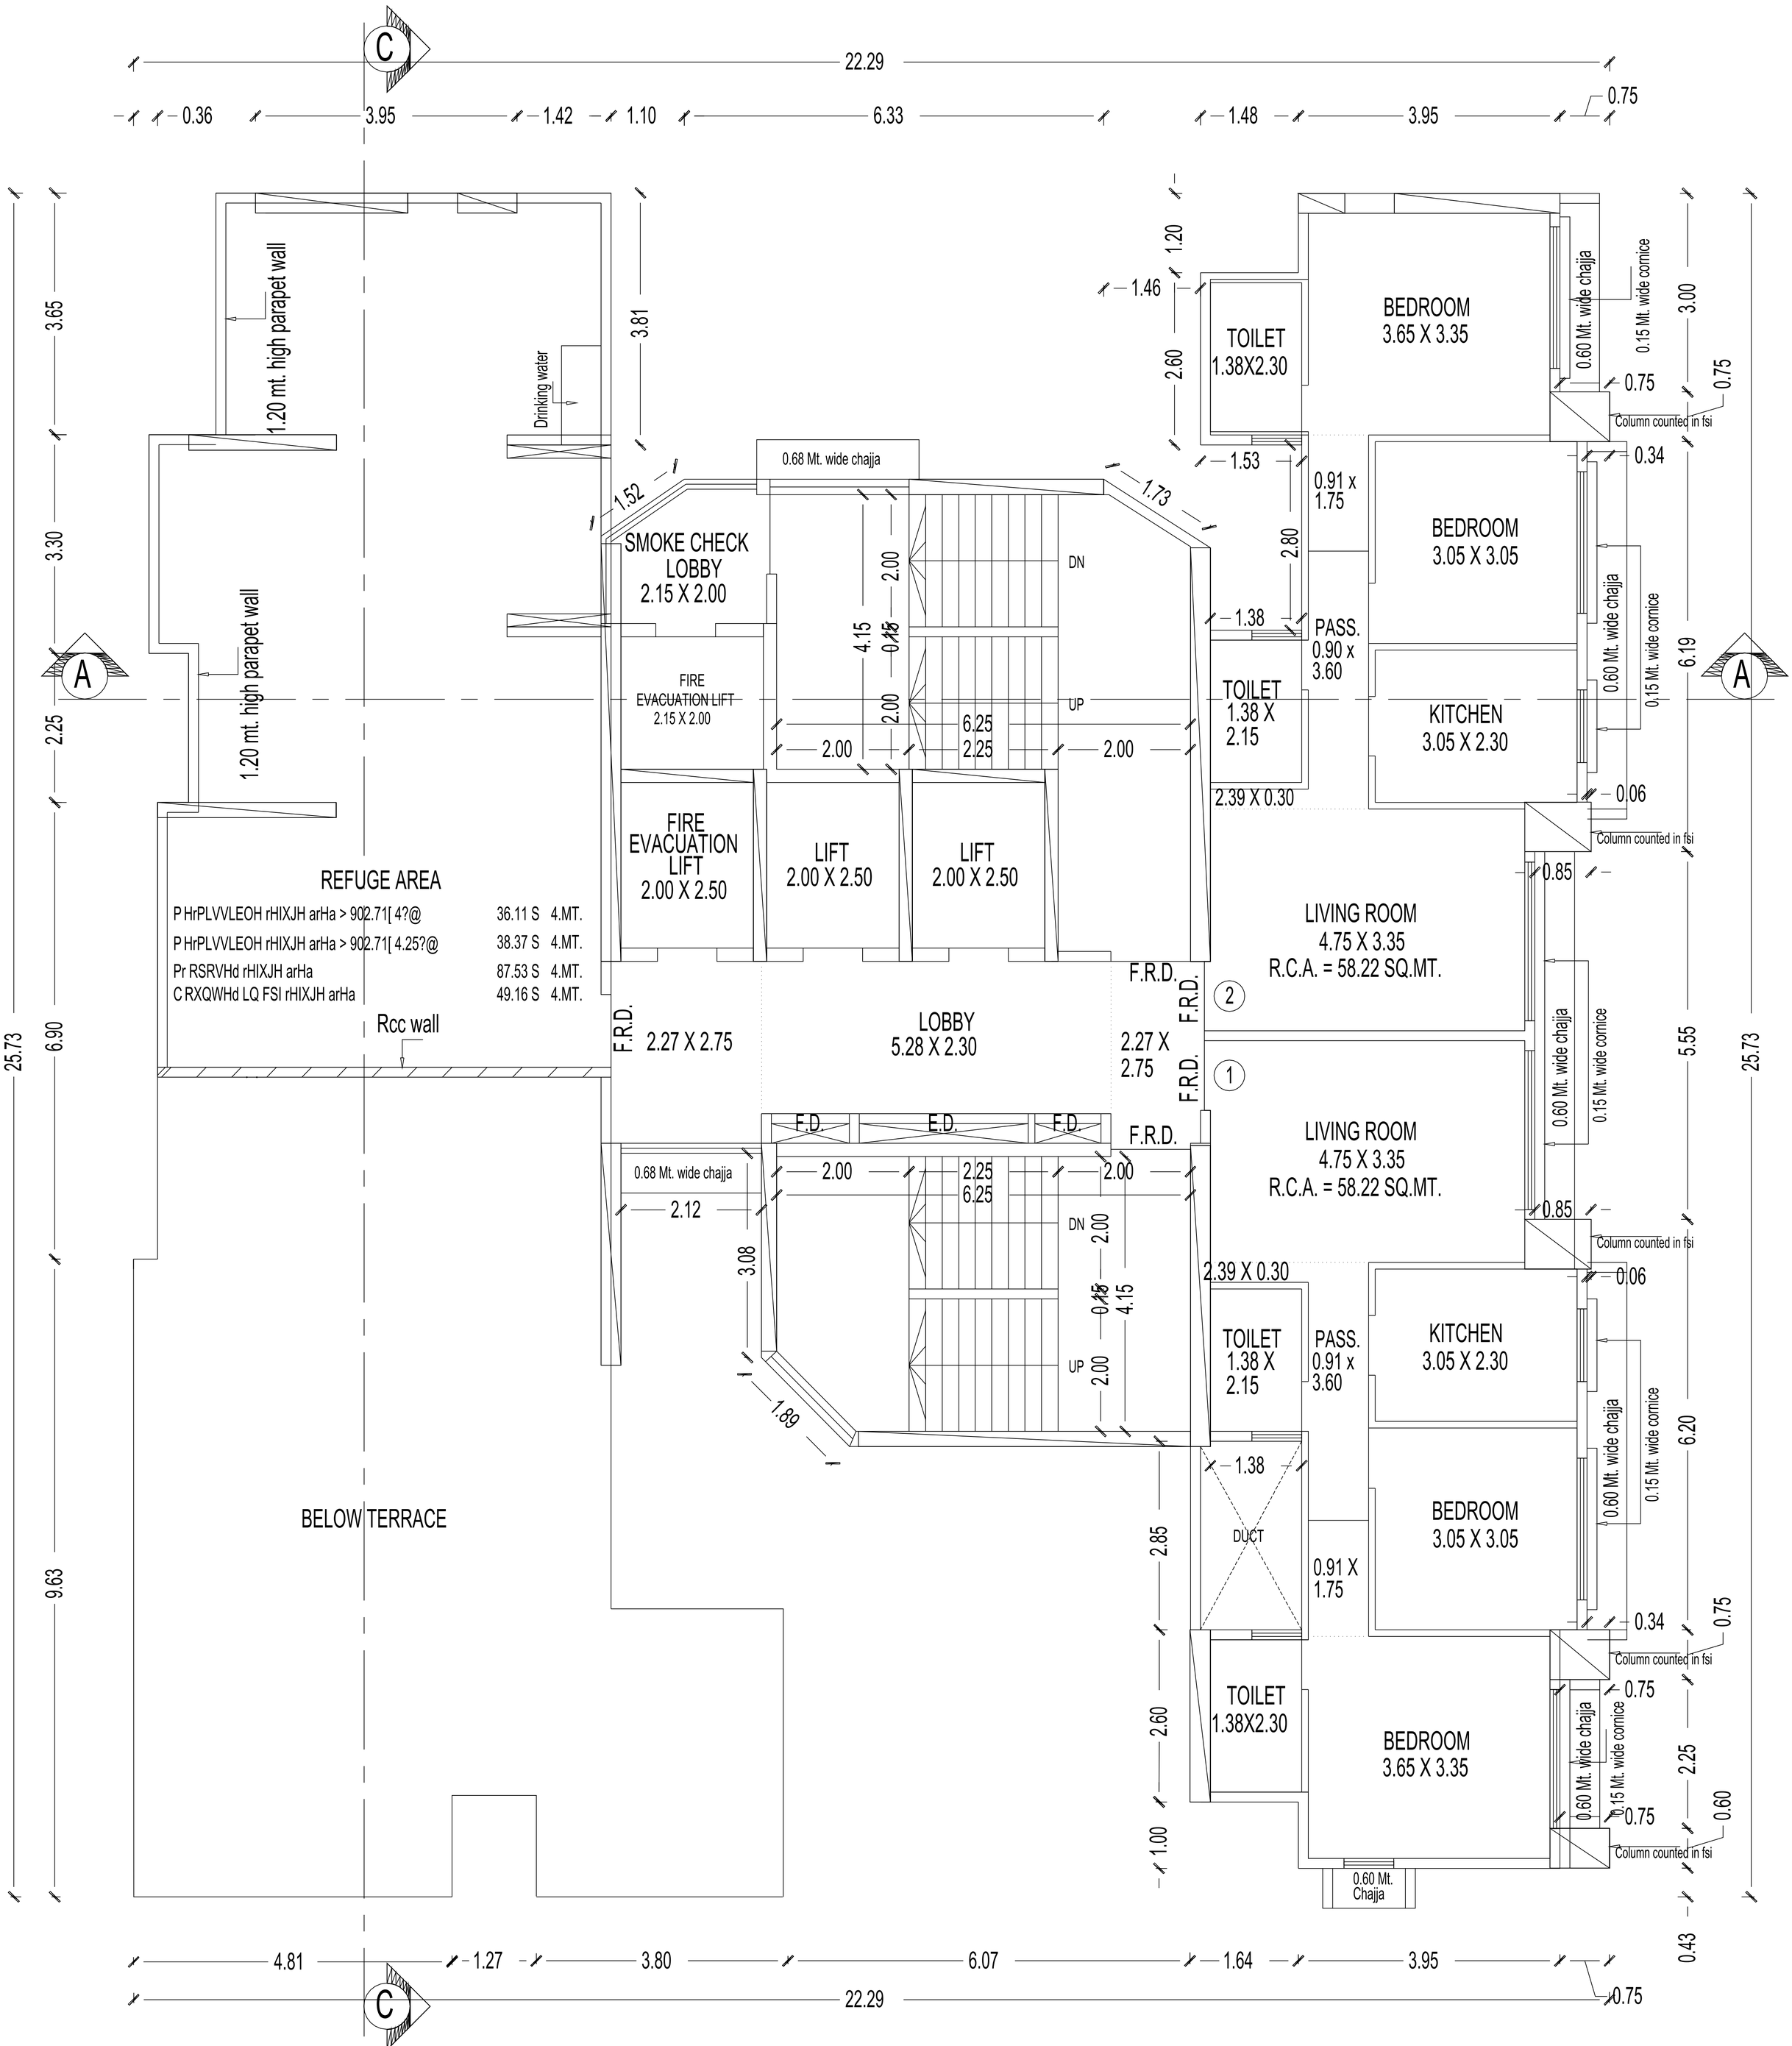

24TH (REFUGE) FLOOR PLAN

SCALE :- 1:100 WING - A


25TH FLOOR PLAN

SCALE :- 1:100 WING - B

SHEET NO. 07 /18


FILE NO- P-20375/2024/(1007)/P/S Ward/PAHADI GOREGAON-W

NORTH

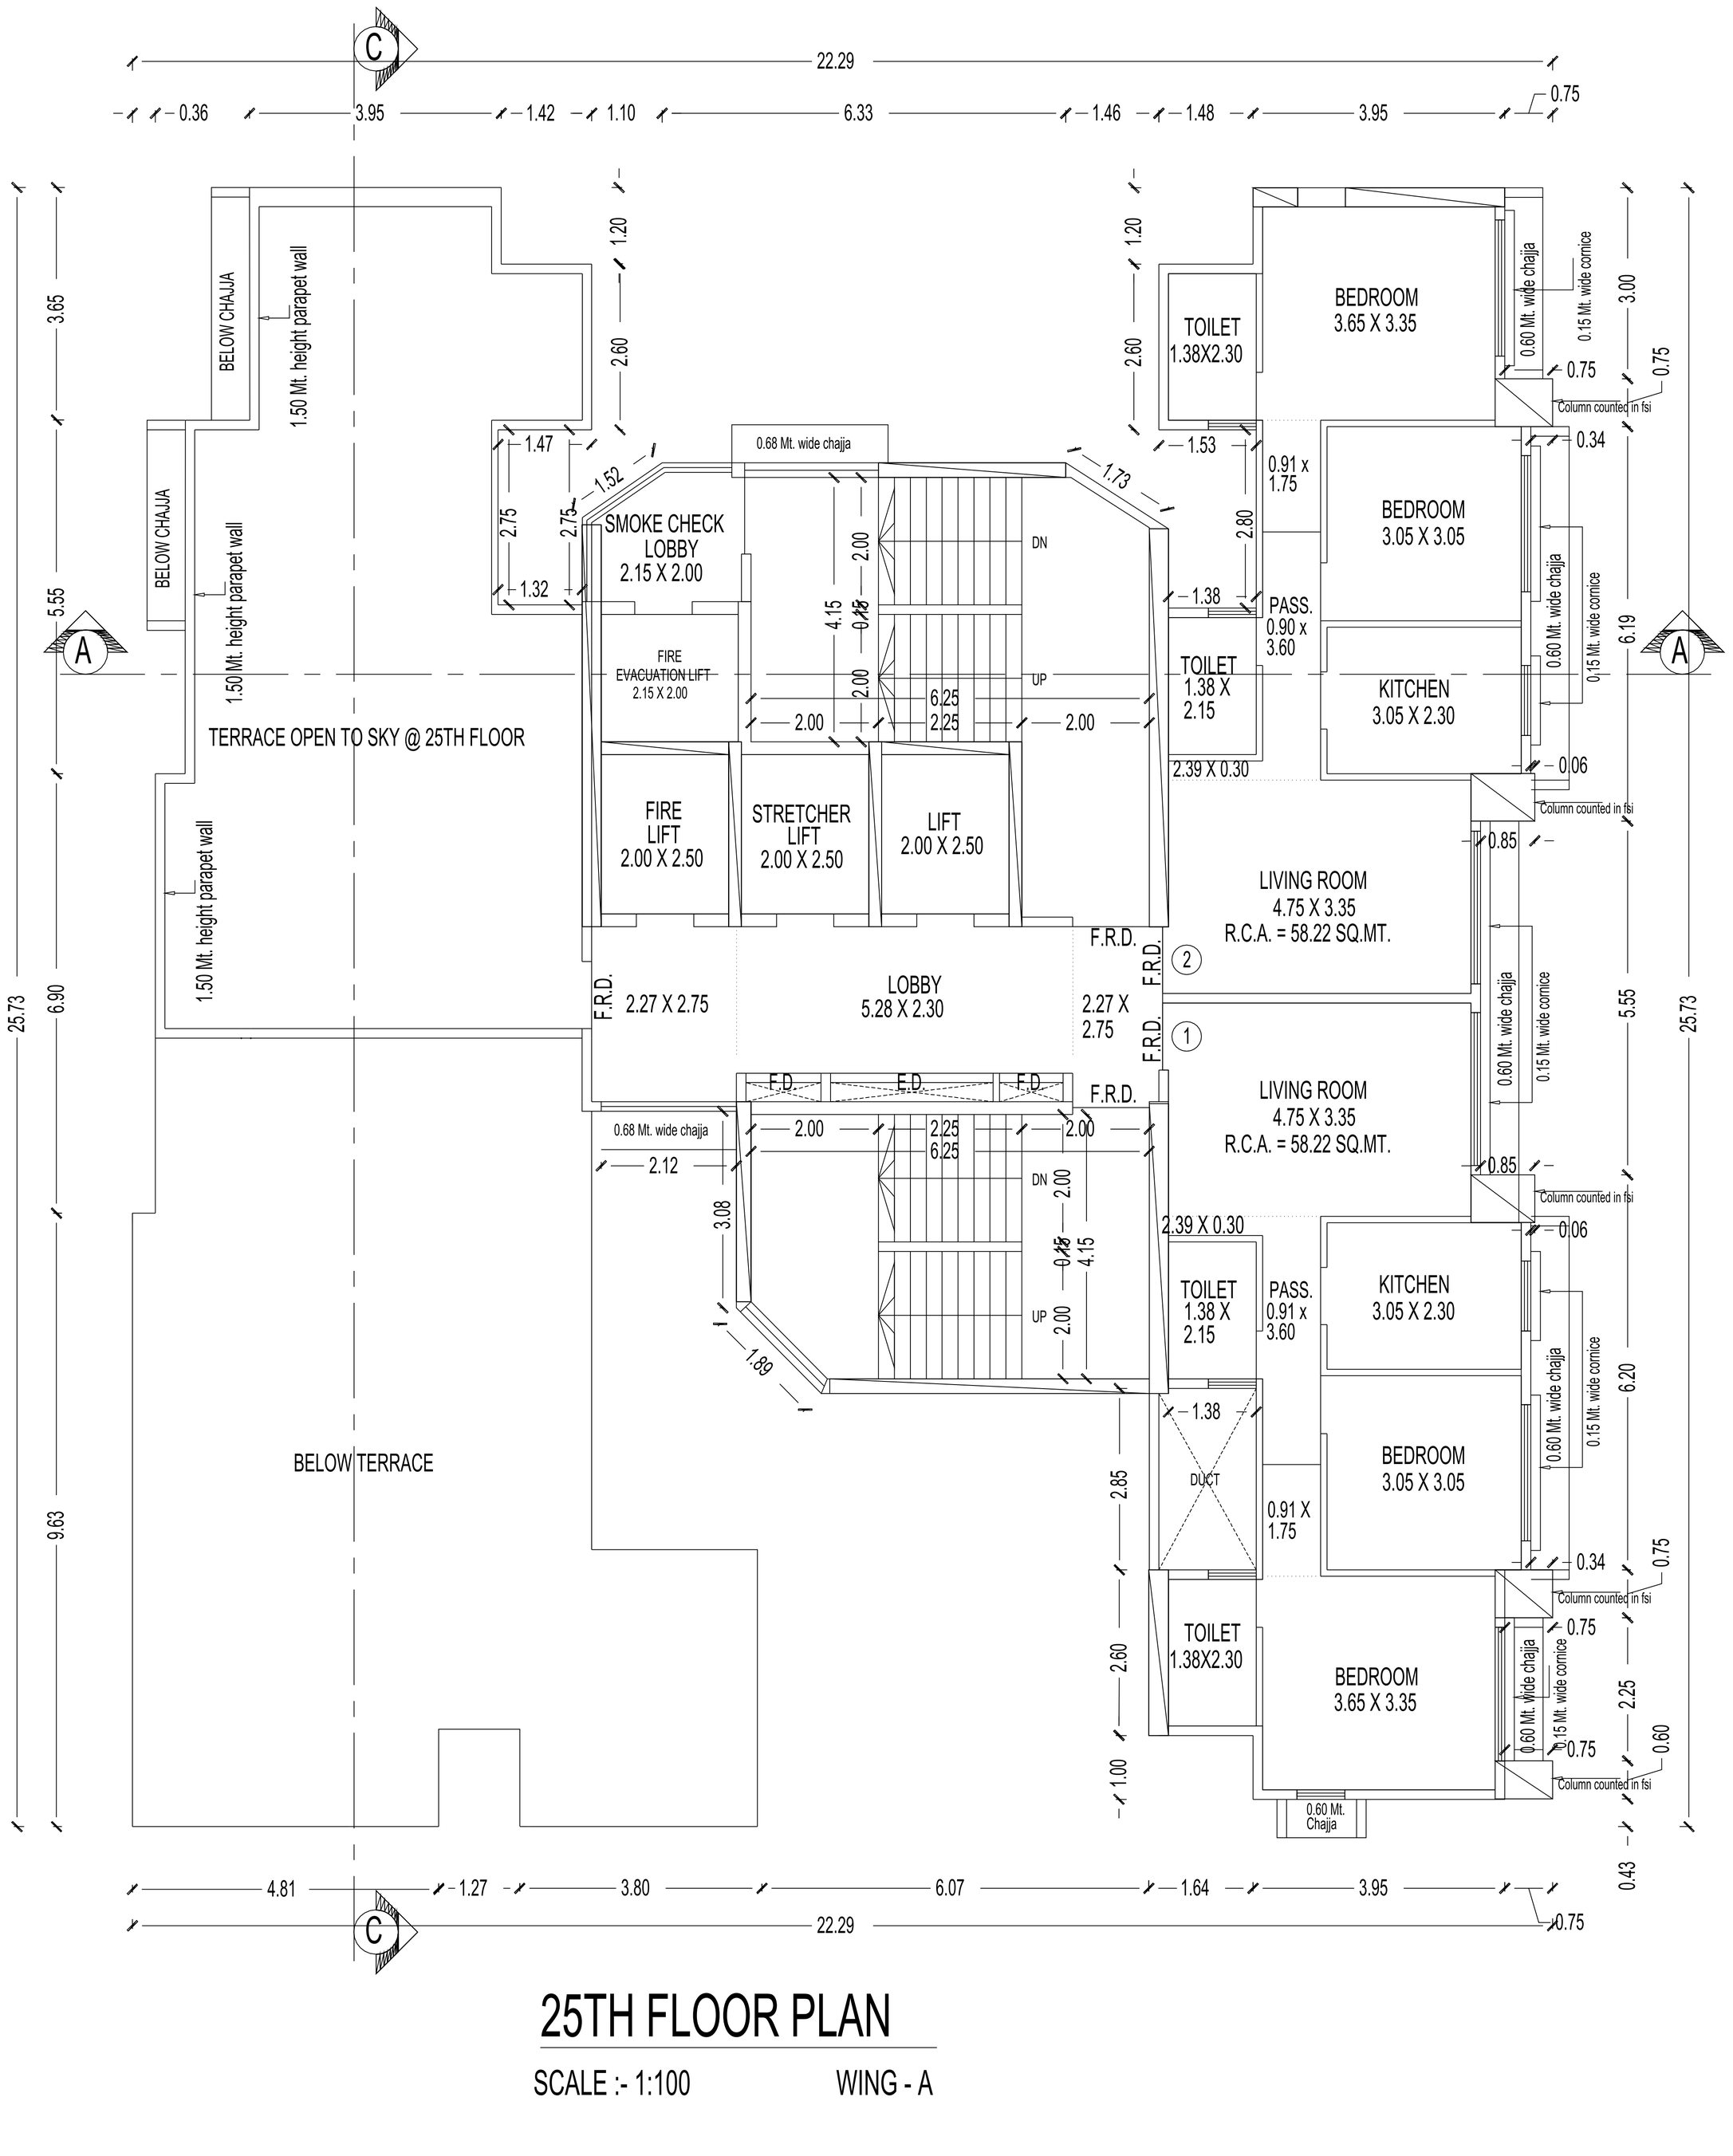

25TH FLOOR PLAN


SCALE :- 1:100 WING - A

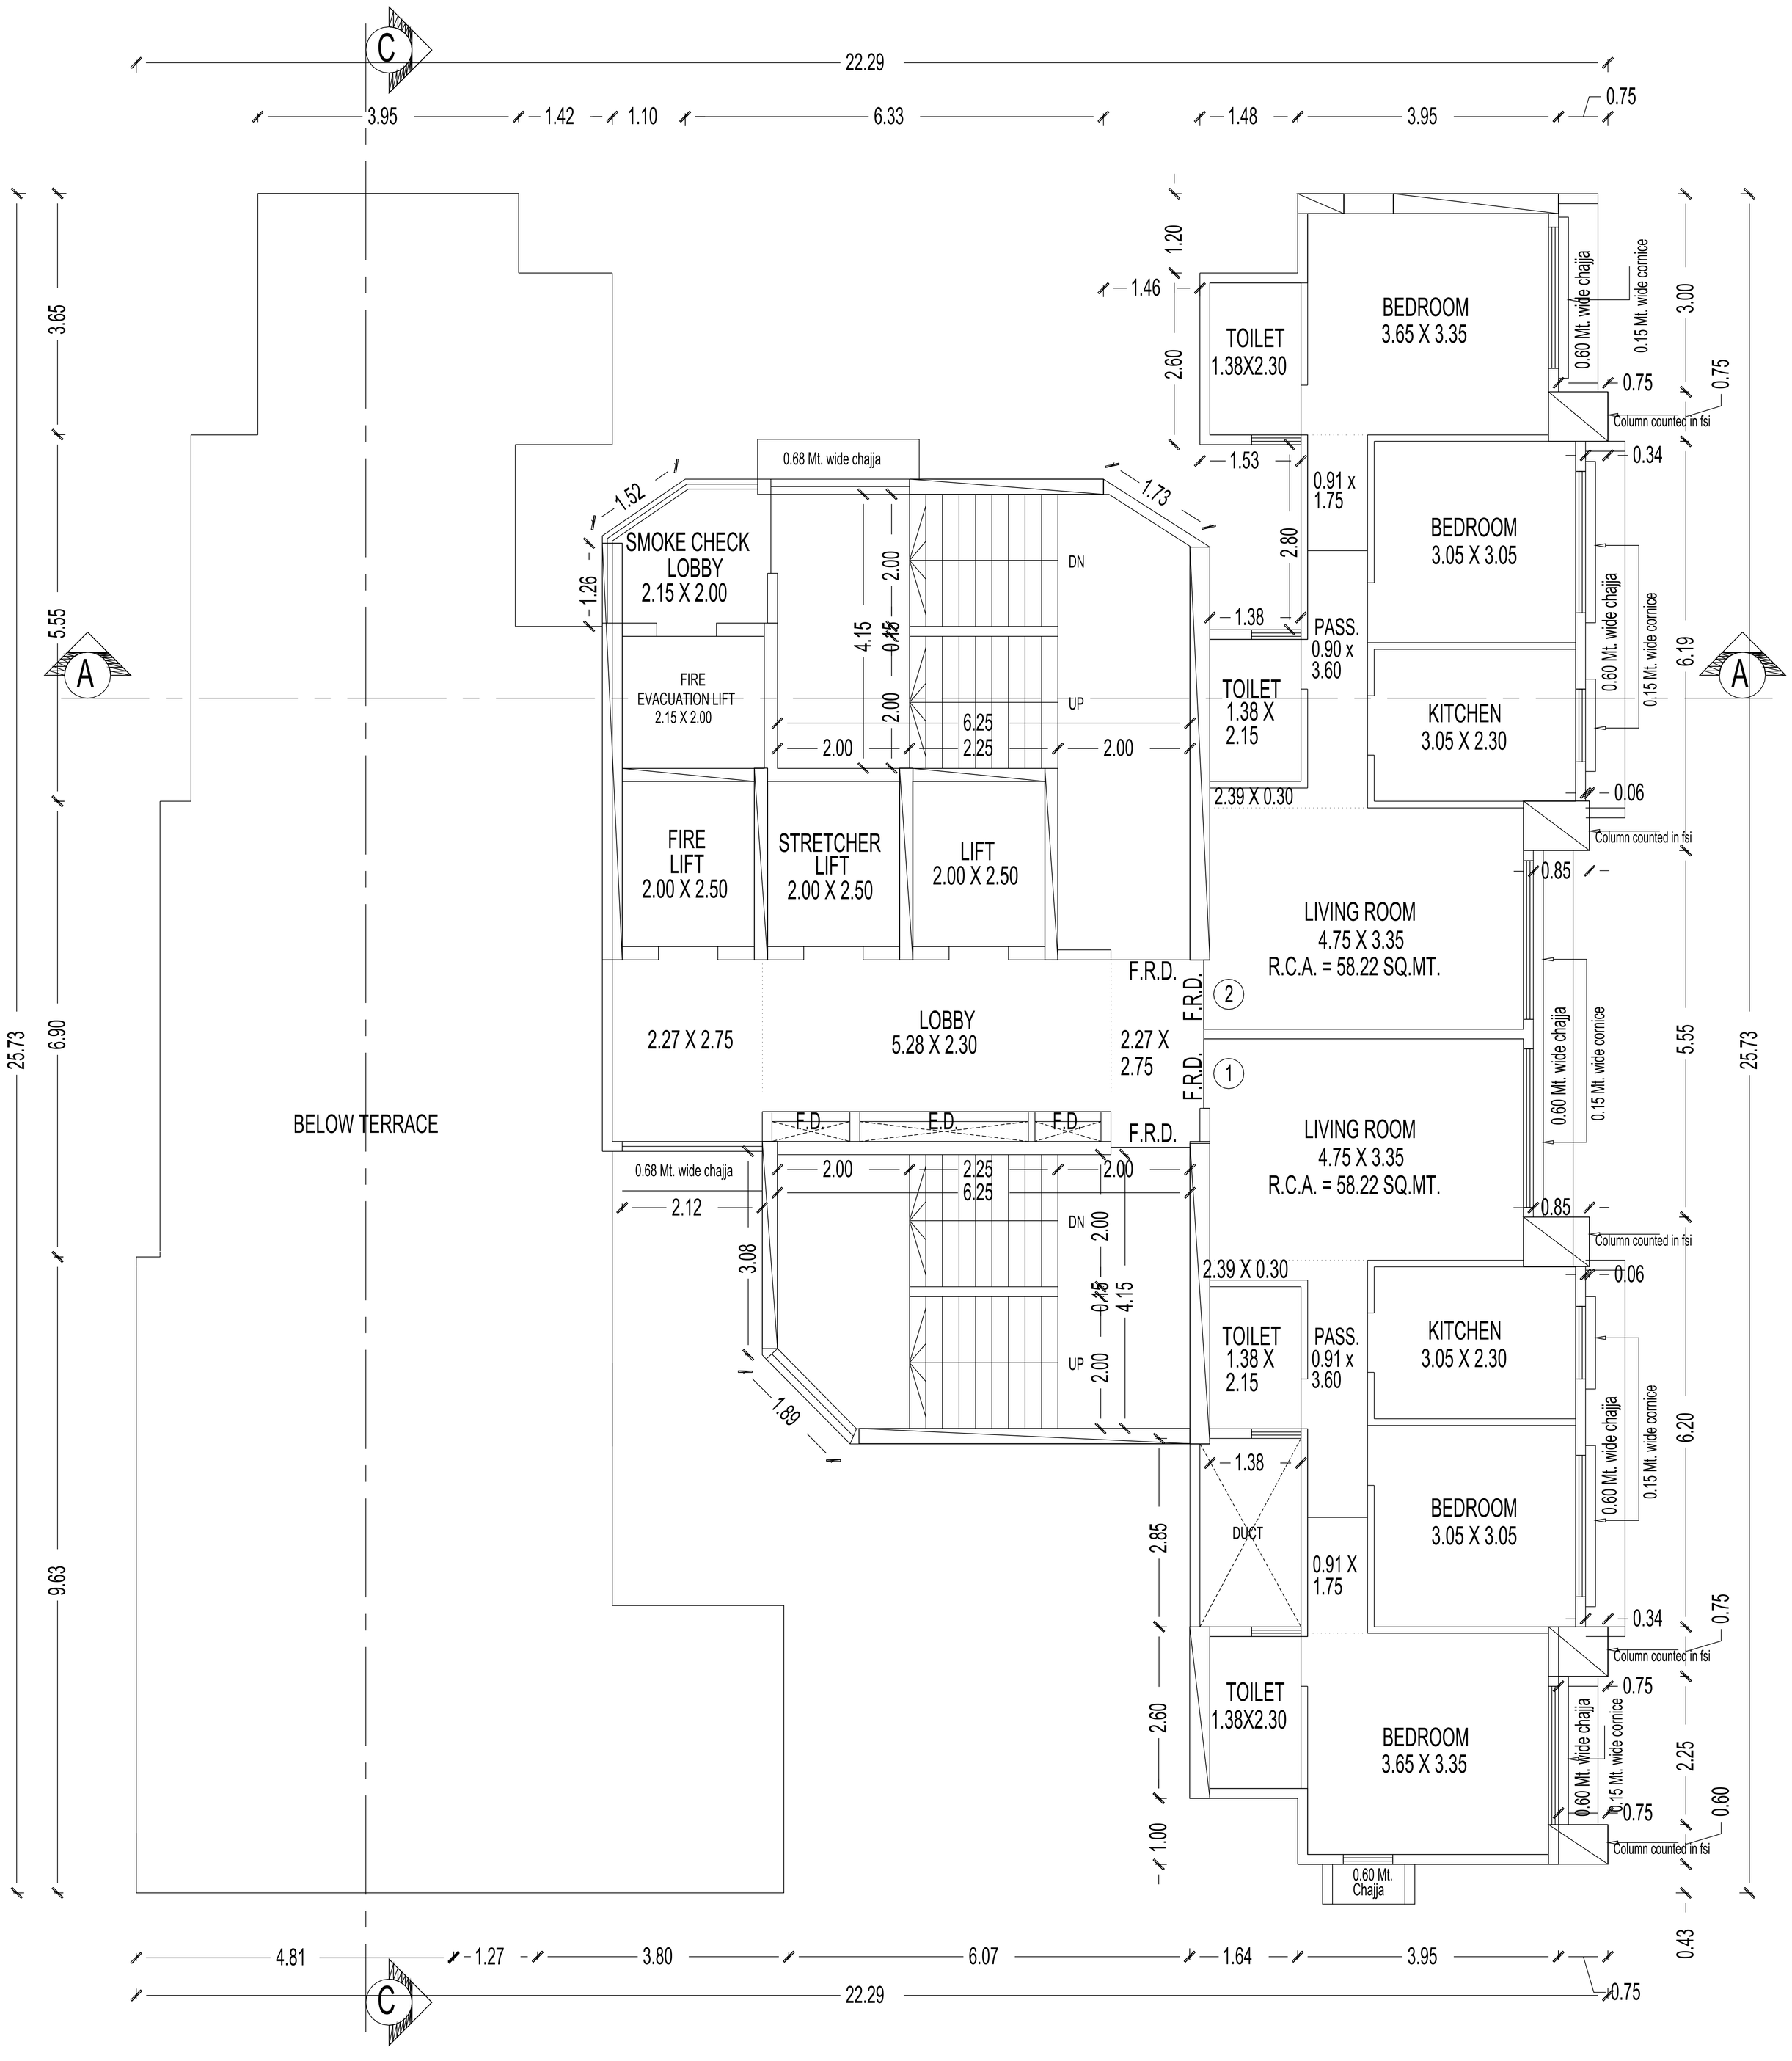

26TH TO 30TH FLOOR PLAN

SCALE :- 1:100

WING - A

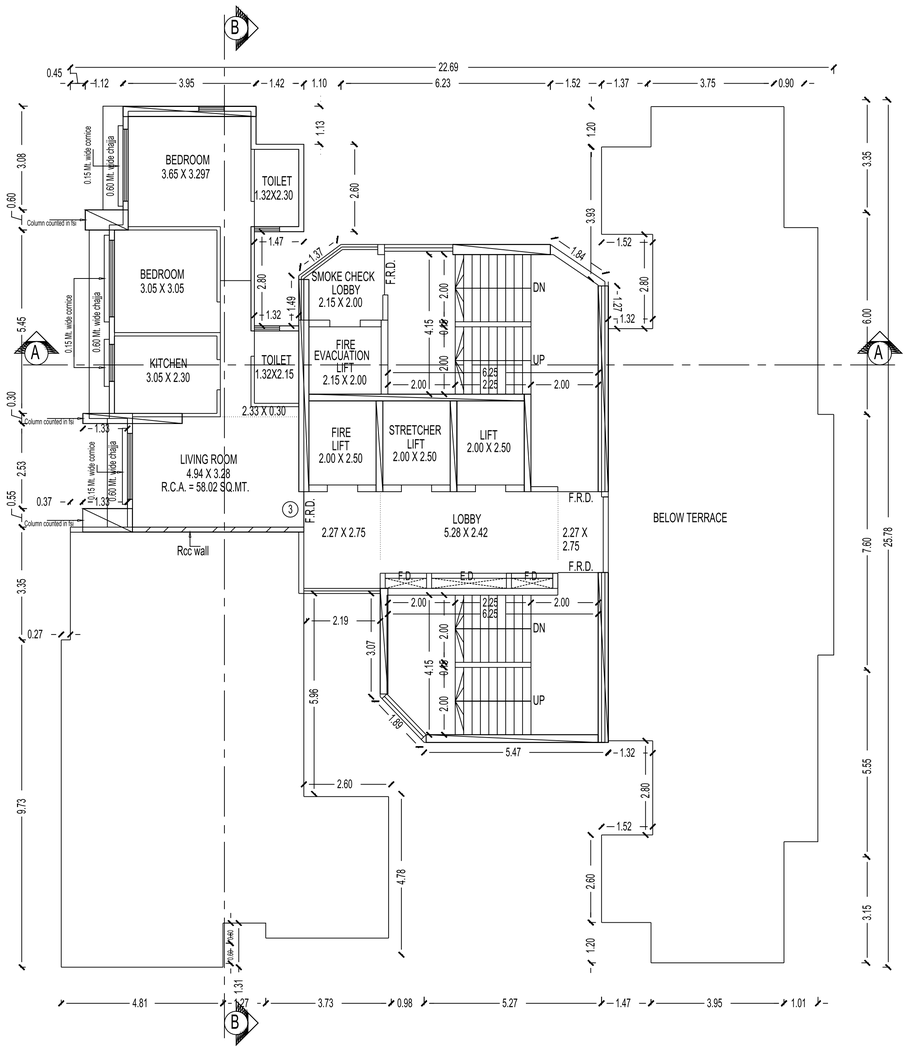

26TH TO 30TH FLOOR PLAN

SCALE :- 1:100 WING - B