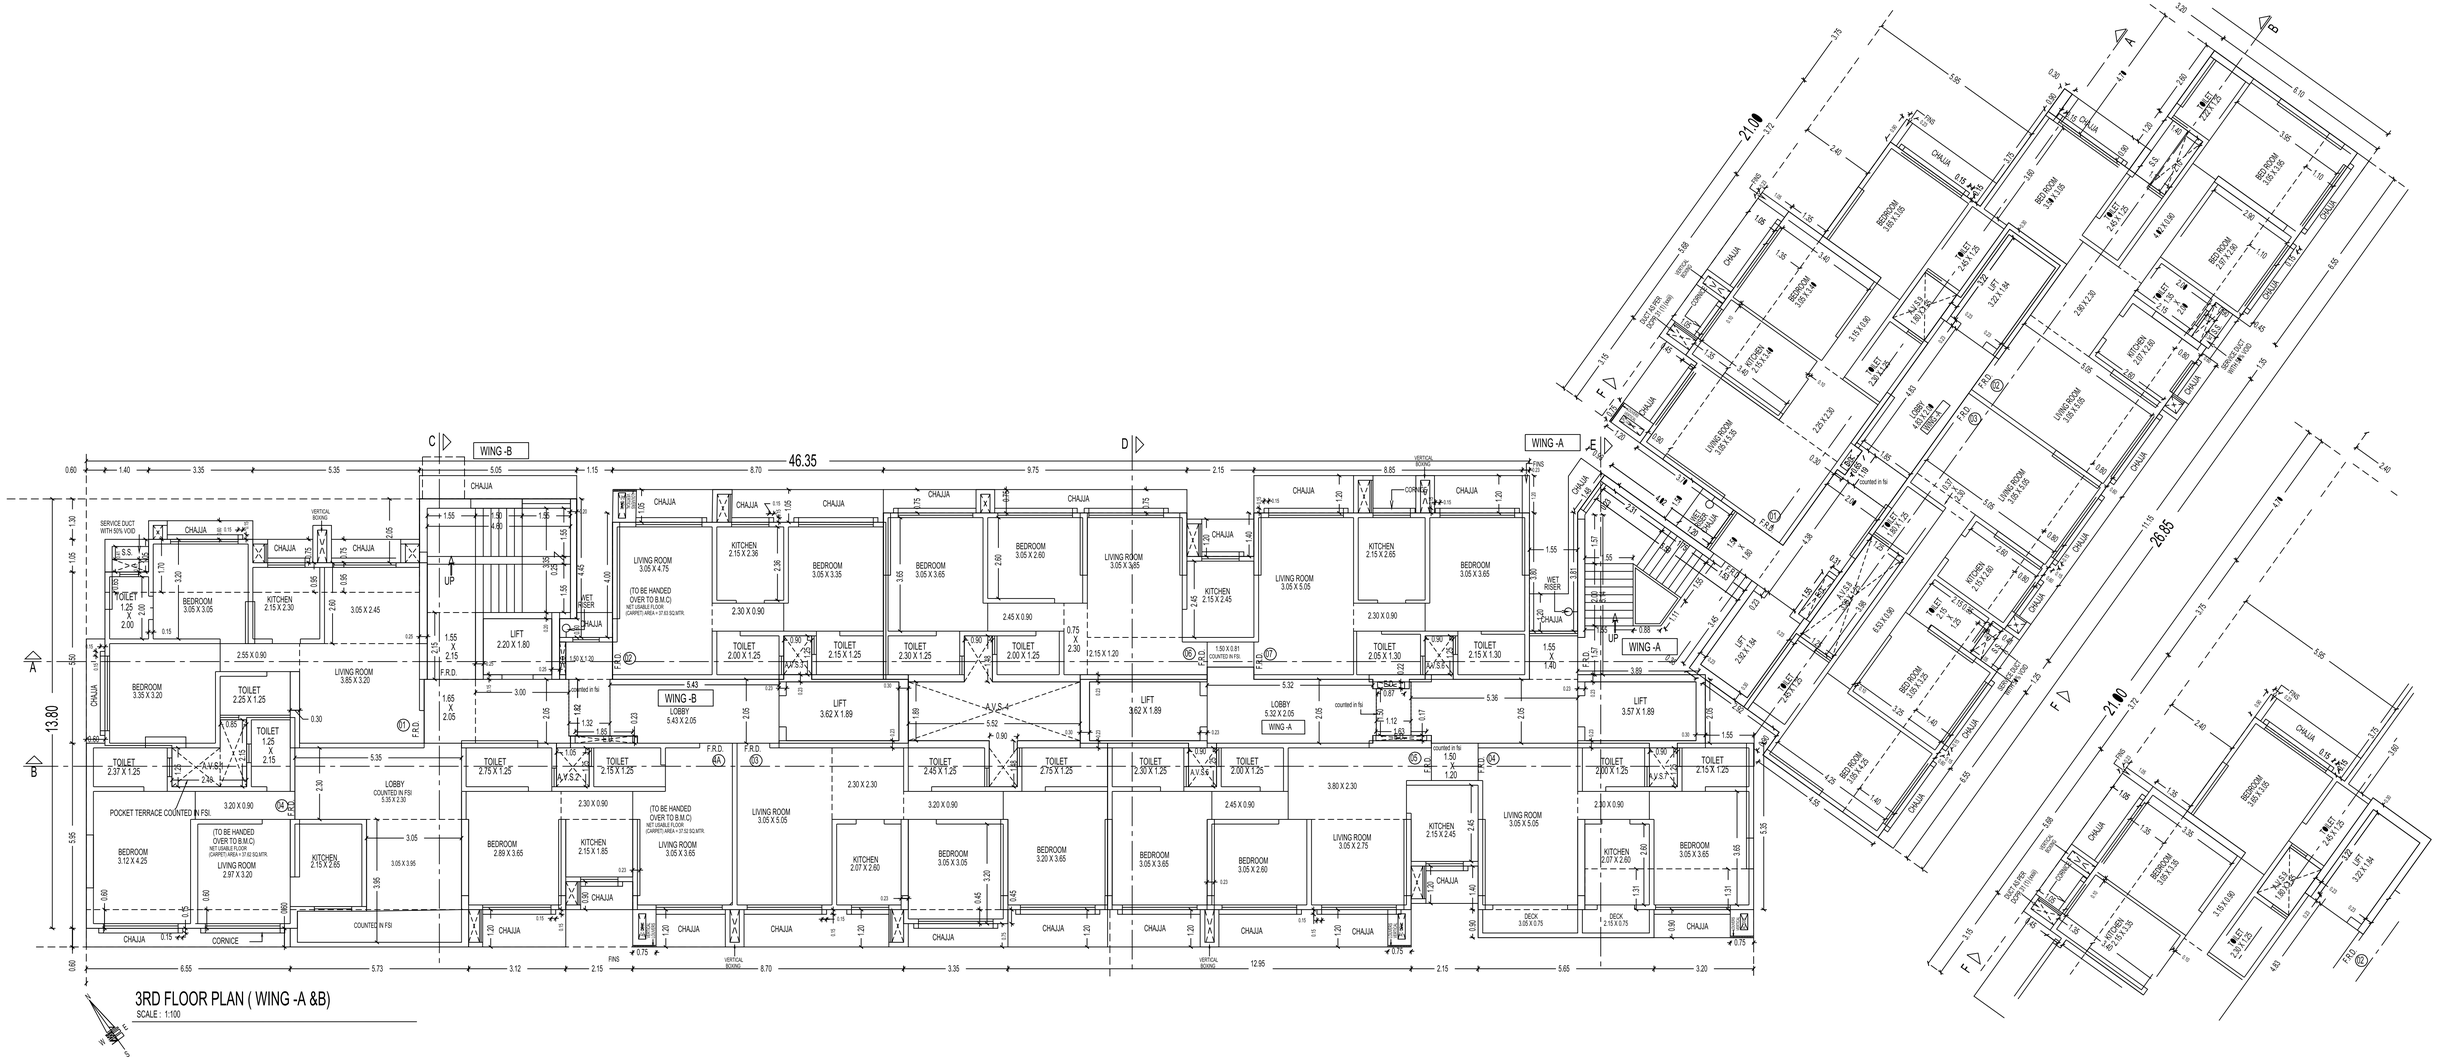
WING -B
WING -A
46.35
26.85
21.00
13.80
UP
LIFT
LOBBY
WET RISER
CHAJJA
CORNICE
FINS
VERTICAL BOXING
SERVICE DUCT WITH 50% VOID
POCKET TERRACE COUNTED IN FSI.
COUNTED IN FSI
(TO BE HANDED OVER TO B.M.C) NOT USABLE FLOOR (CARPET) AREA = 37.82 SQ.MTR.
LIVING ROOM 3.05 X 4.75
KITCHEN 2.15 X 2.30
BEDROOM 3.05 X 3.35
BEDROOM 3.05 X 3.65
BEDROOM 3.05 X 2.60
LIVING ROOM 3.05 X 3.65
KITCHEN 2.15 X 2.45
LIVING ROOM 3.05 X 5.05
KITCHEN 2.15 X 2.65
BEDROOM 3.05 X 3.65
BEDROOM 3.35 X 3.20
LIVING ROOM 3.65 X 3.20
BEDROOM 3.12 X 4.25
LIVING ROOM 2.97 X 3.20
KITCHEN 2.15 X 2.65
BEDROOM 2.89 X 3.65
KITCHEN 2.15 X 1.85
LIVING ROOM 3.05 X 3.65
LIVING ROOM 3.05 X 5.05
KITCHEN 2.07 X 2.60
BEDROOM 3.05 X 3.05
BEDROOM 3.20 X 3.65
BEDROOM 3.05 X 3.65
BEDROOM 3.05 X 2.60
LIVING ROOM 3.05 X 2.75
KITCHEN 2.15 X 2.45
LIVING ROOM 3.05 X 5.05
KITCHEN 2.07 X 2.60
BEDROOM 3.05 X 3.65
DECK 3.05 X 0.75
DECK 2.15 X 0.75
3RD FLOOR PLAN (WING -A &B)
SCALE : 1:100

4TH FLOOR PLAN (WING -A &B)

SCALE : 1:100

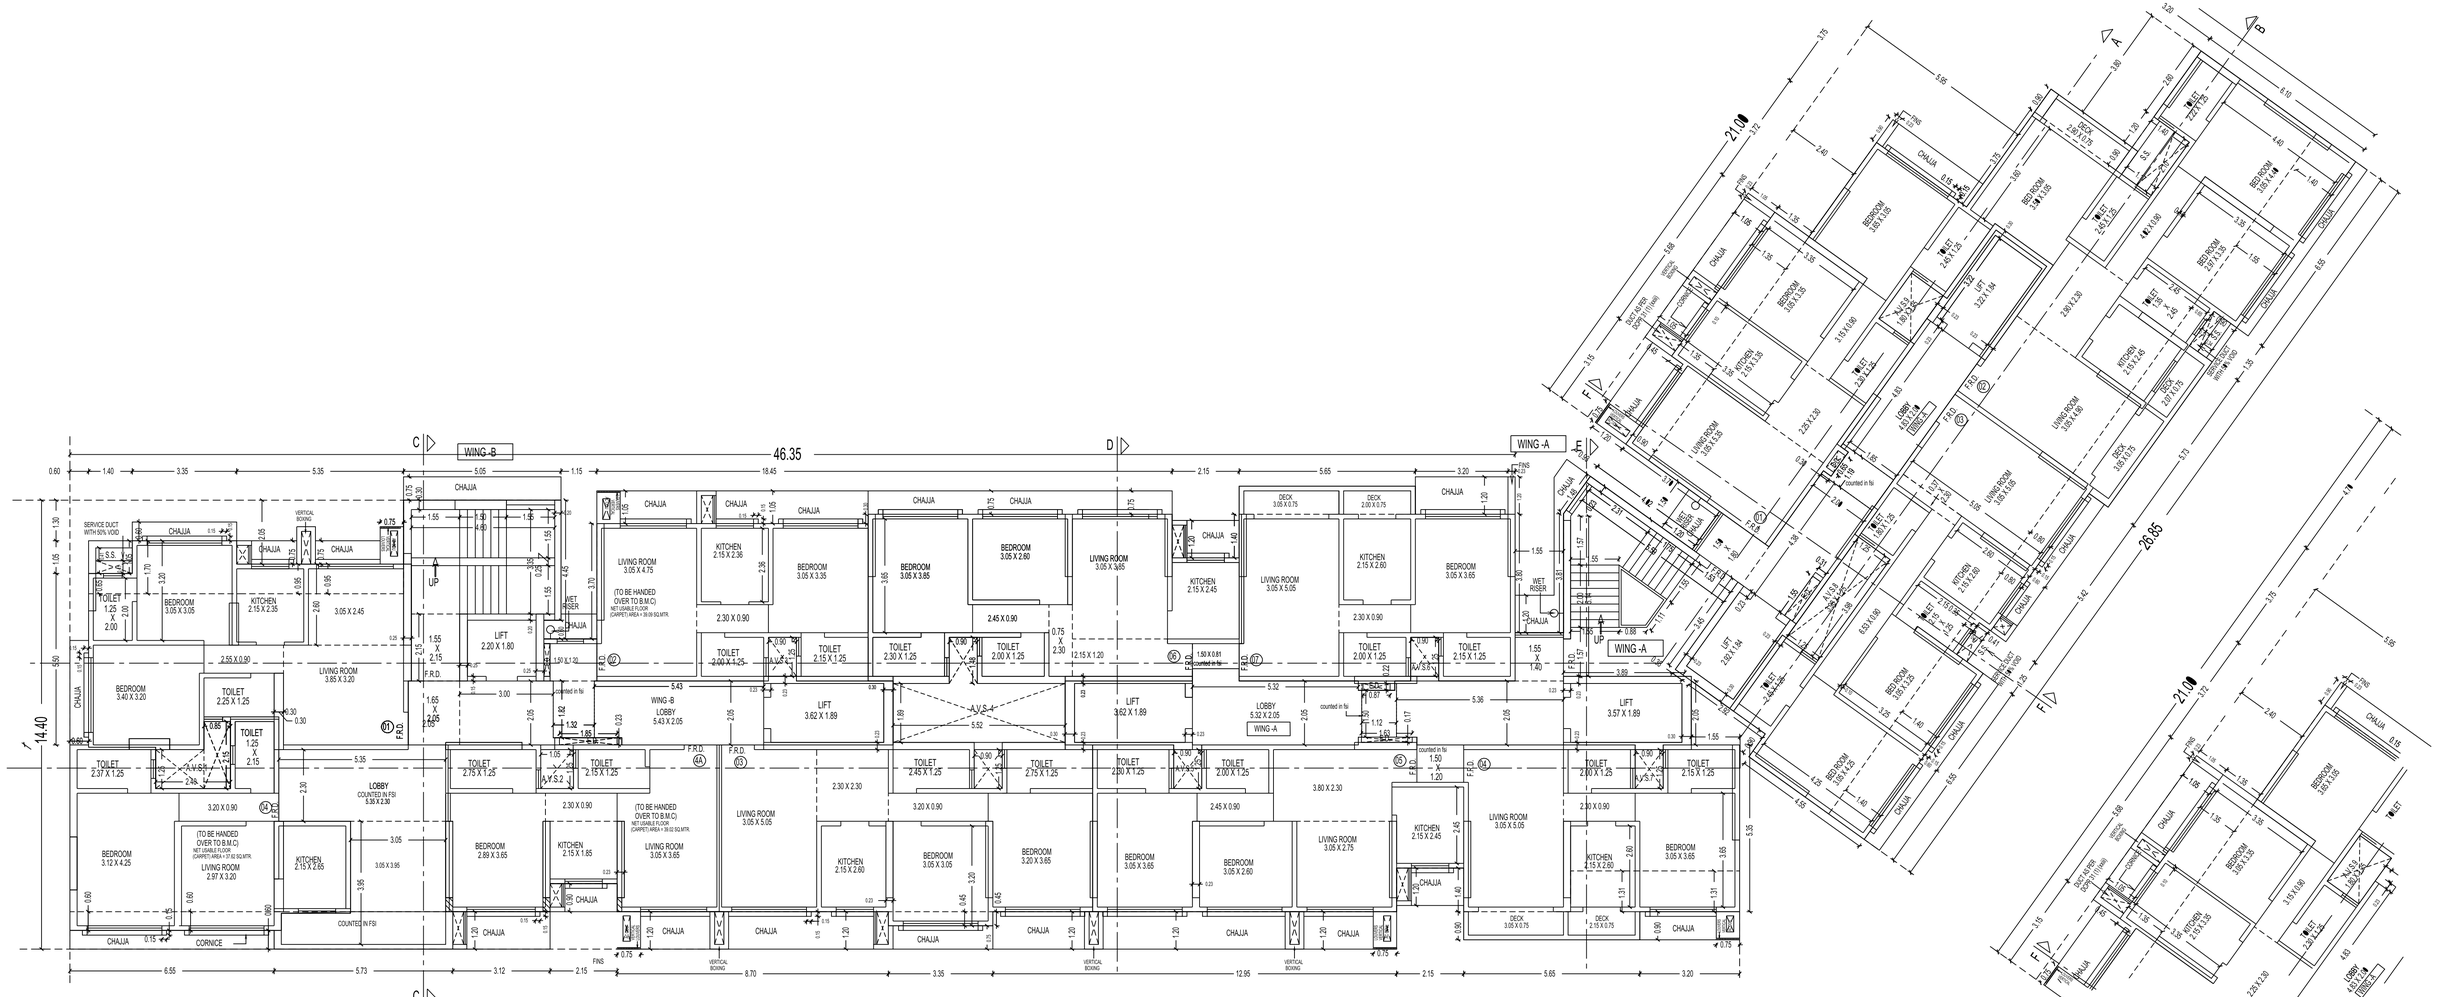

5TH FLOOR PLAN (WING - A&B)

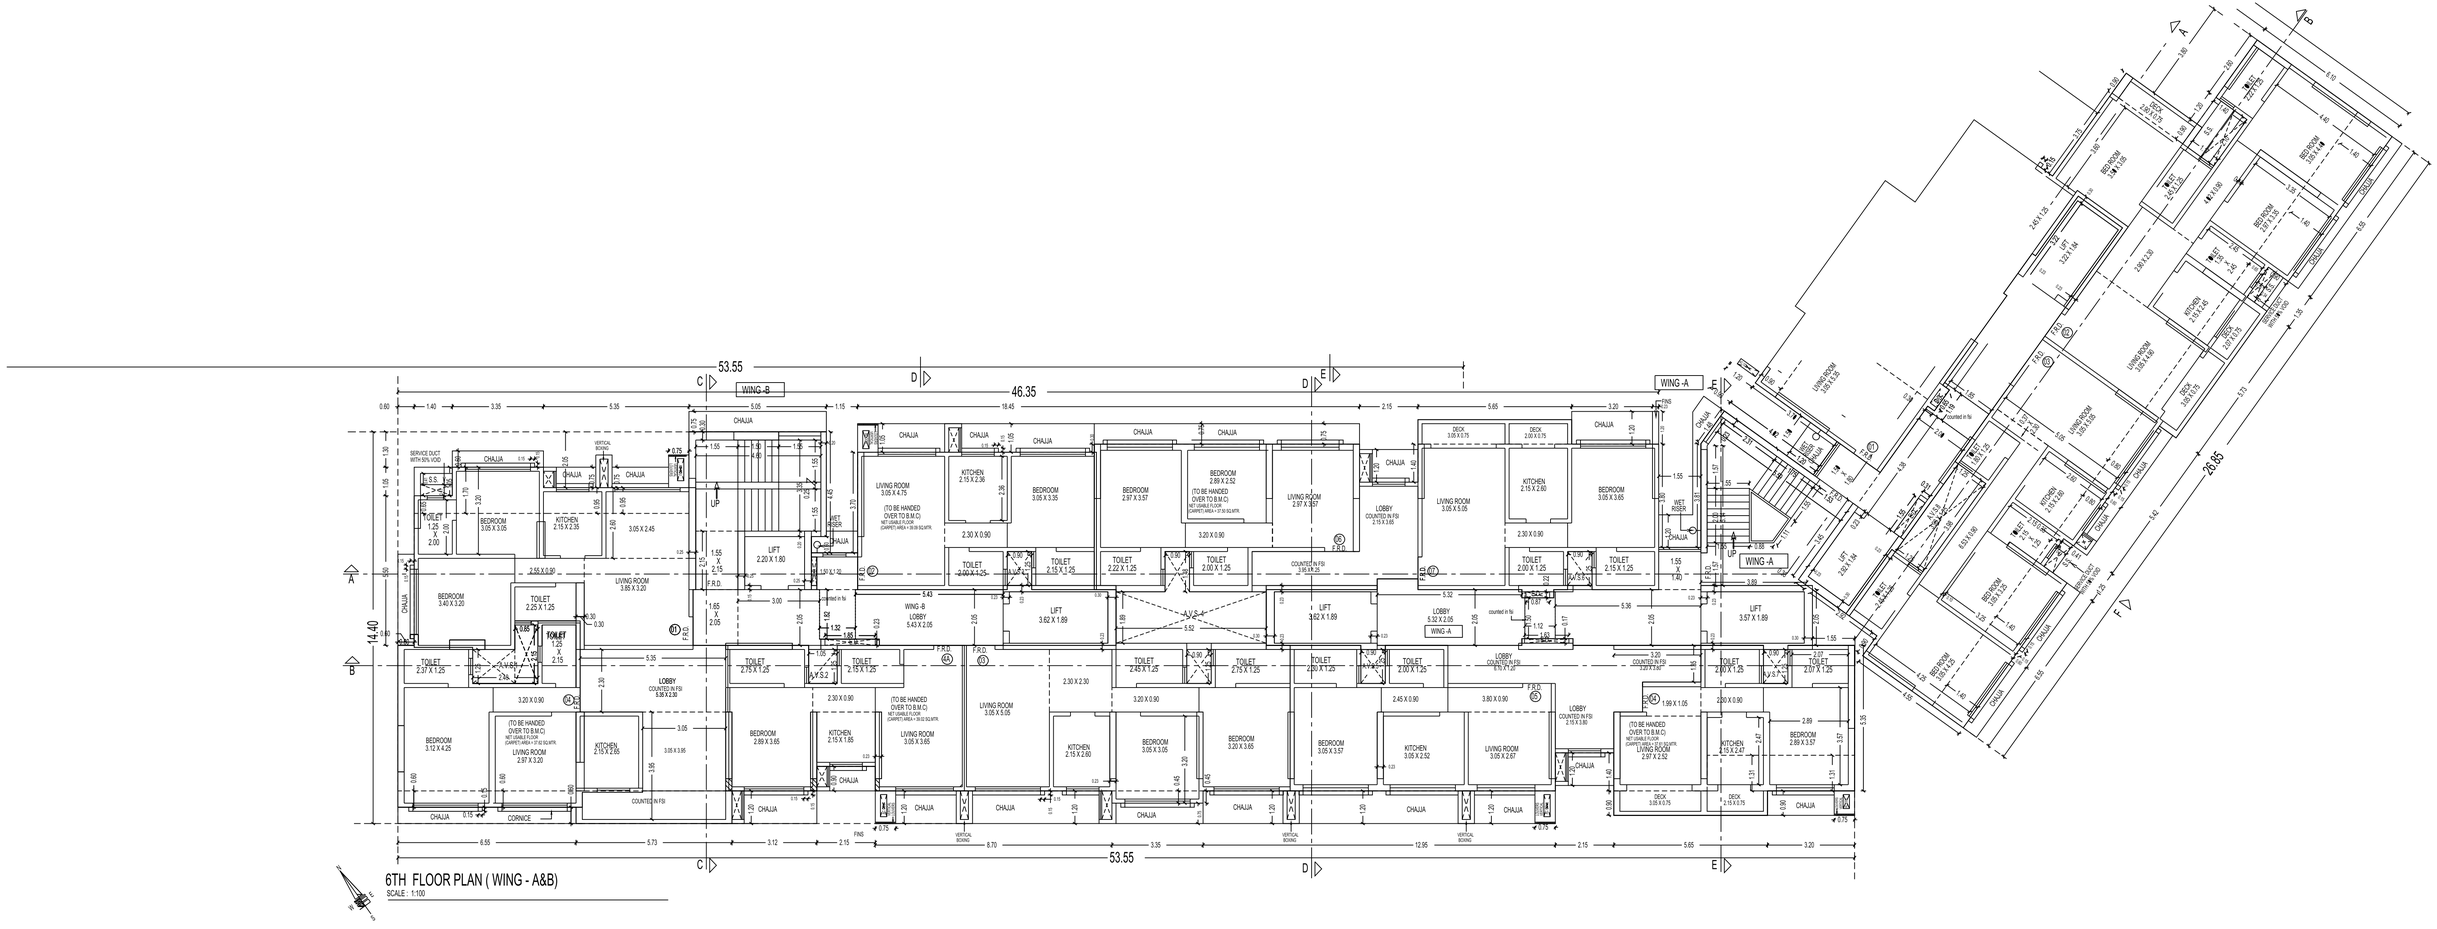
WING-B
WING-A
53.55
46.35
26.85
14.40
LIFT
LOBBY
LIVING ROOM
BEDROOM
KITCHEN
TOILET
CHAJJA
UP
6TH FLOOR PLAN (WING - A&B)
SCALE : 1:100

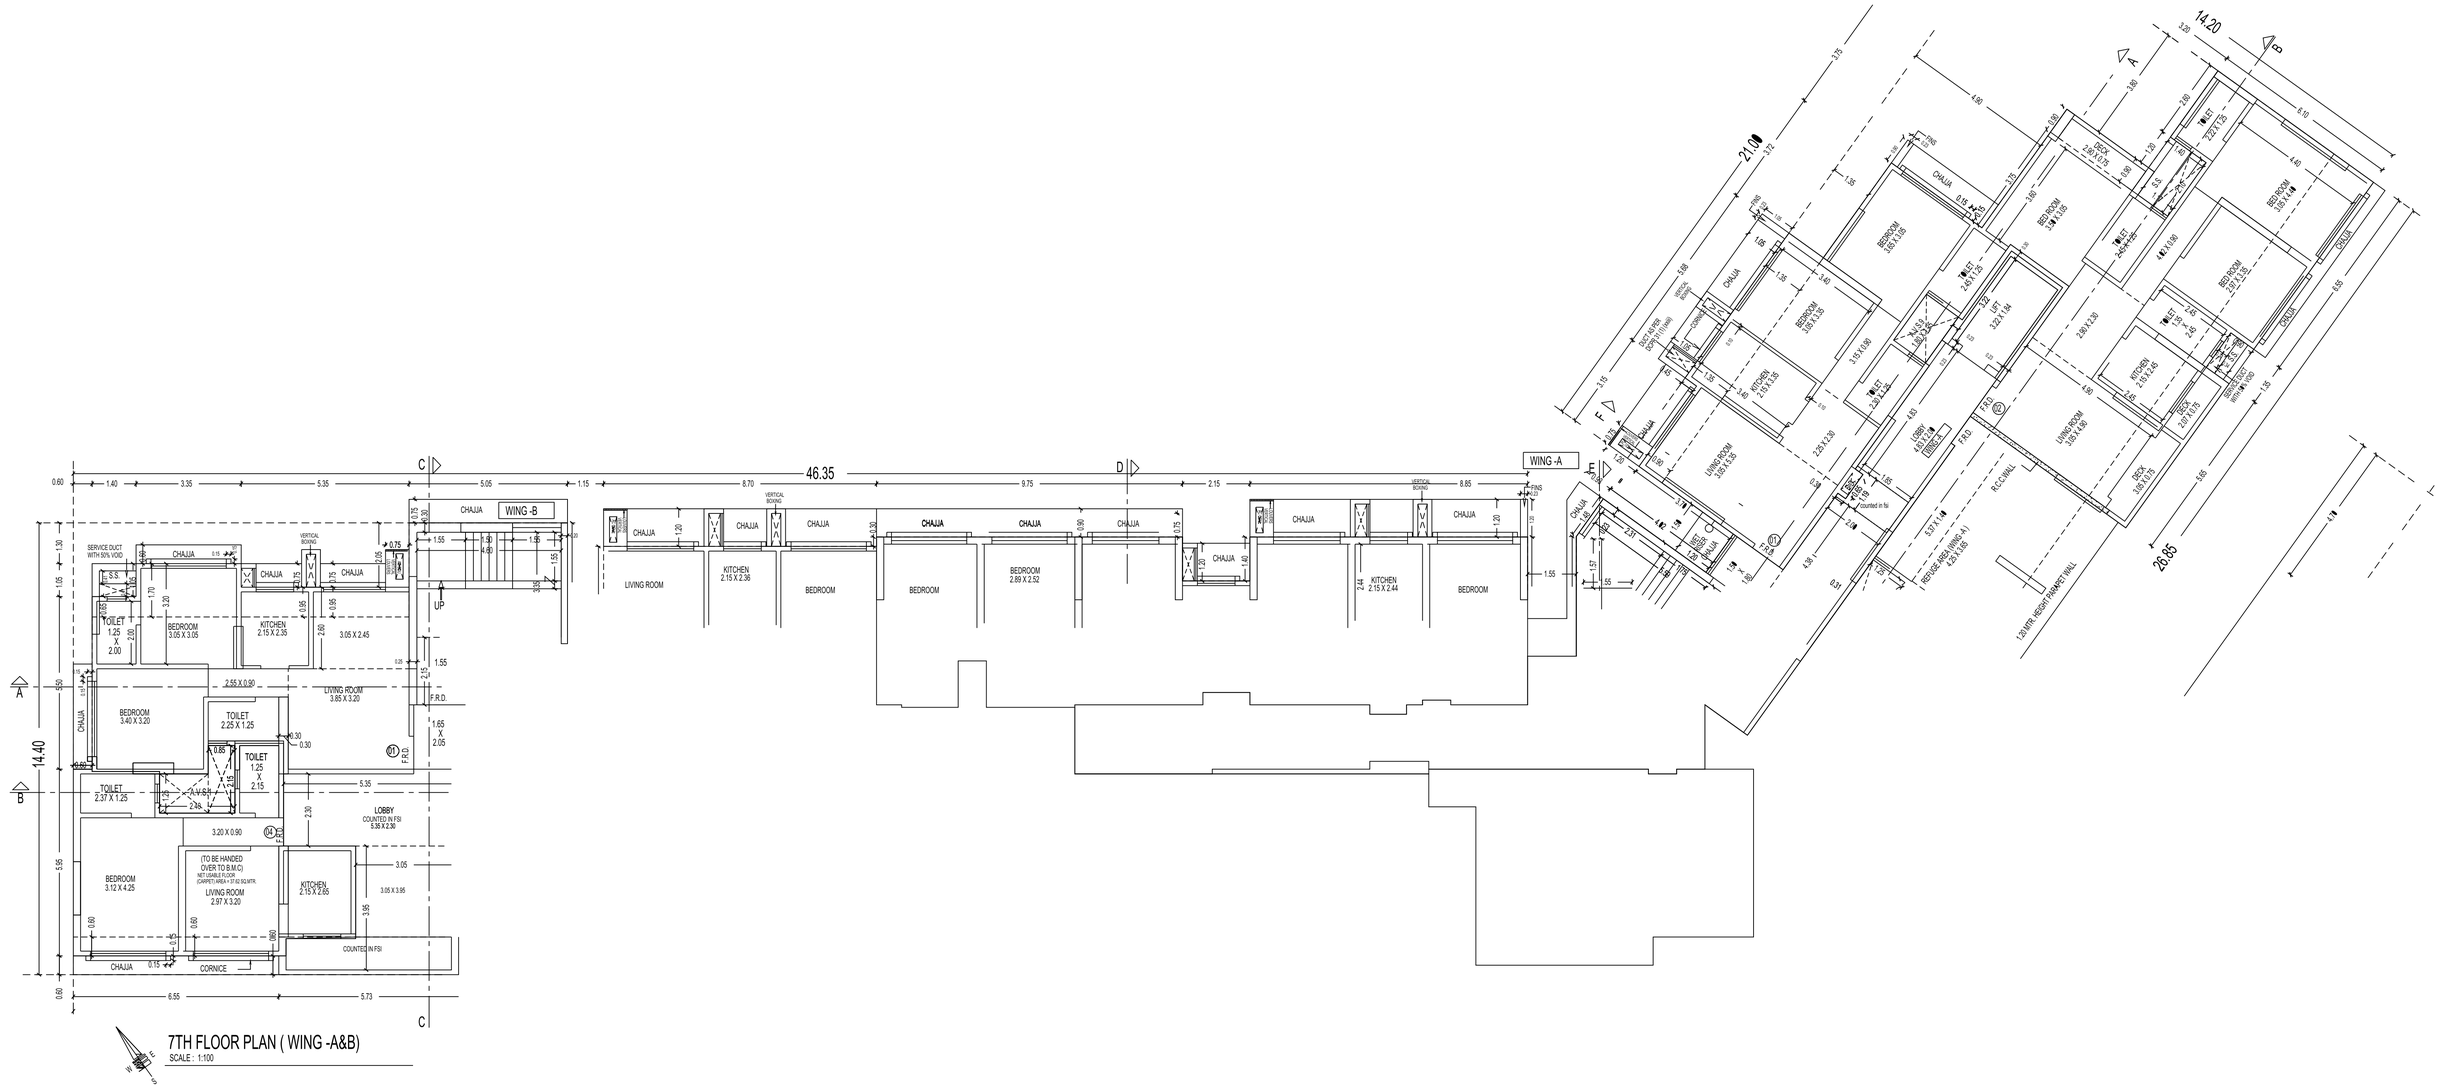
WING -B
WING -A
46.35
14.40
21.00
14.20
26.85
LIVING ROOM
KITCHEN 2.15 X 2.36
BEDROOM
BEDROOM 2.89 X 2.52
KITCHEN 2.15 X 2.44
BEDROOM
BEDROOM 3.40 X 3.20
TOILET 2.25 X 1.25
TOILET 2.37 X 1.25
TOILET 1.25 X 2.00
BEDROOM 3.05 X 3.05
KITCHEN 2.15 X 2.35
3.05 X 2.45
LIVING ROOM 3.85 X 3.20
TOILET 1.25 X 2.15
BEDROOM 3.12 X 4.25
(TO BE HANDED OVER TO B.M.C) NET USABLE FLOOR (CARPET) AREA = 37.62 SQ.MTR.
LIVING ROOM 2.97 X 3.20
KITCHEN 2.15 X 2.65
LOBBY COUNTED IN FSI 5.35 X 2.30
COUNTED IN FSI
CHAJJA
CORNICE
SERVICE DUCT WITH 50% VOID
VERTICAL BOXING
F.R.D.
UP
7TH FLOOR PLAN (WING -A&B)
SCALE : 1:100

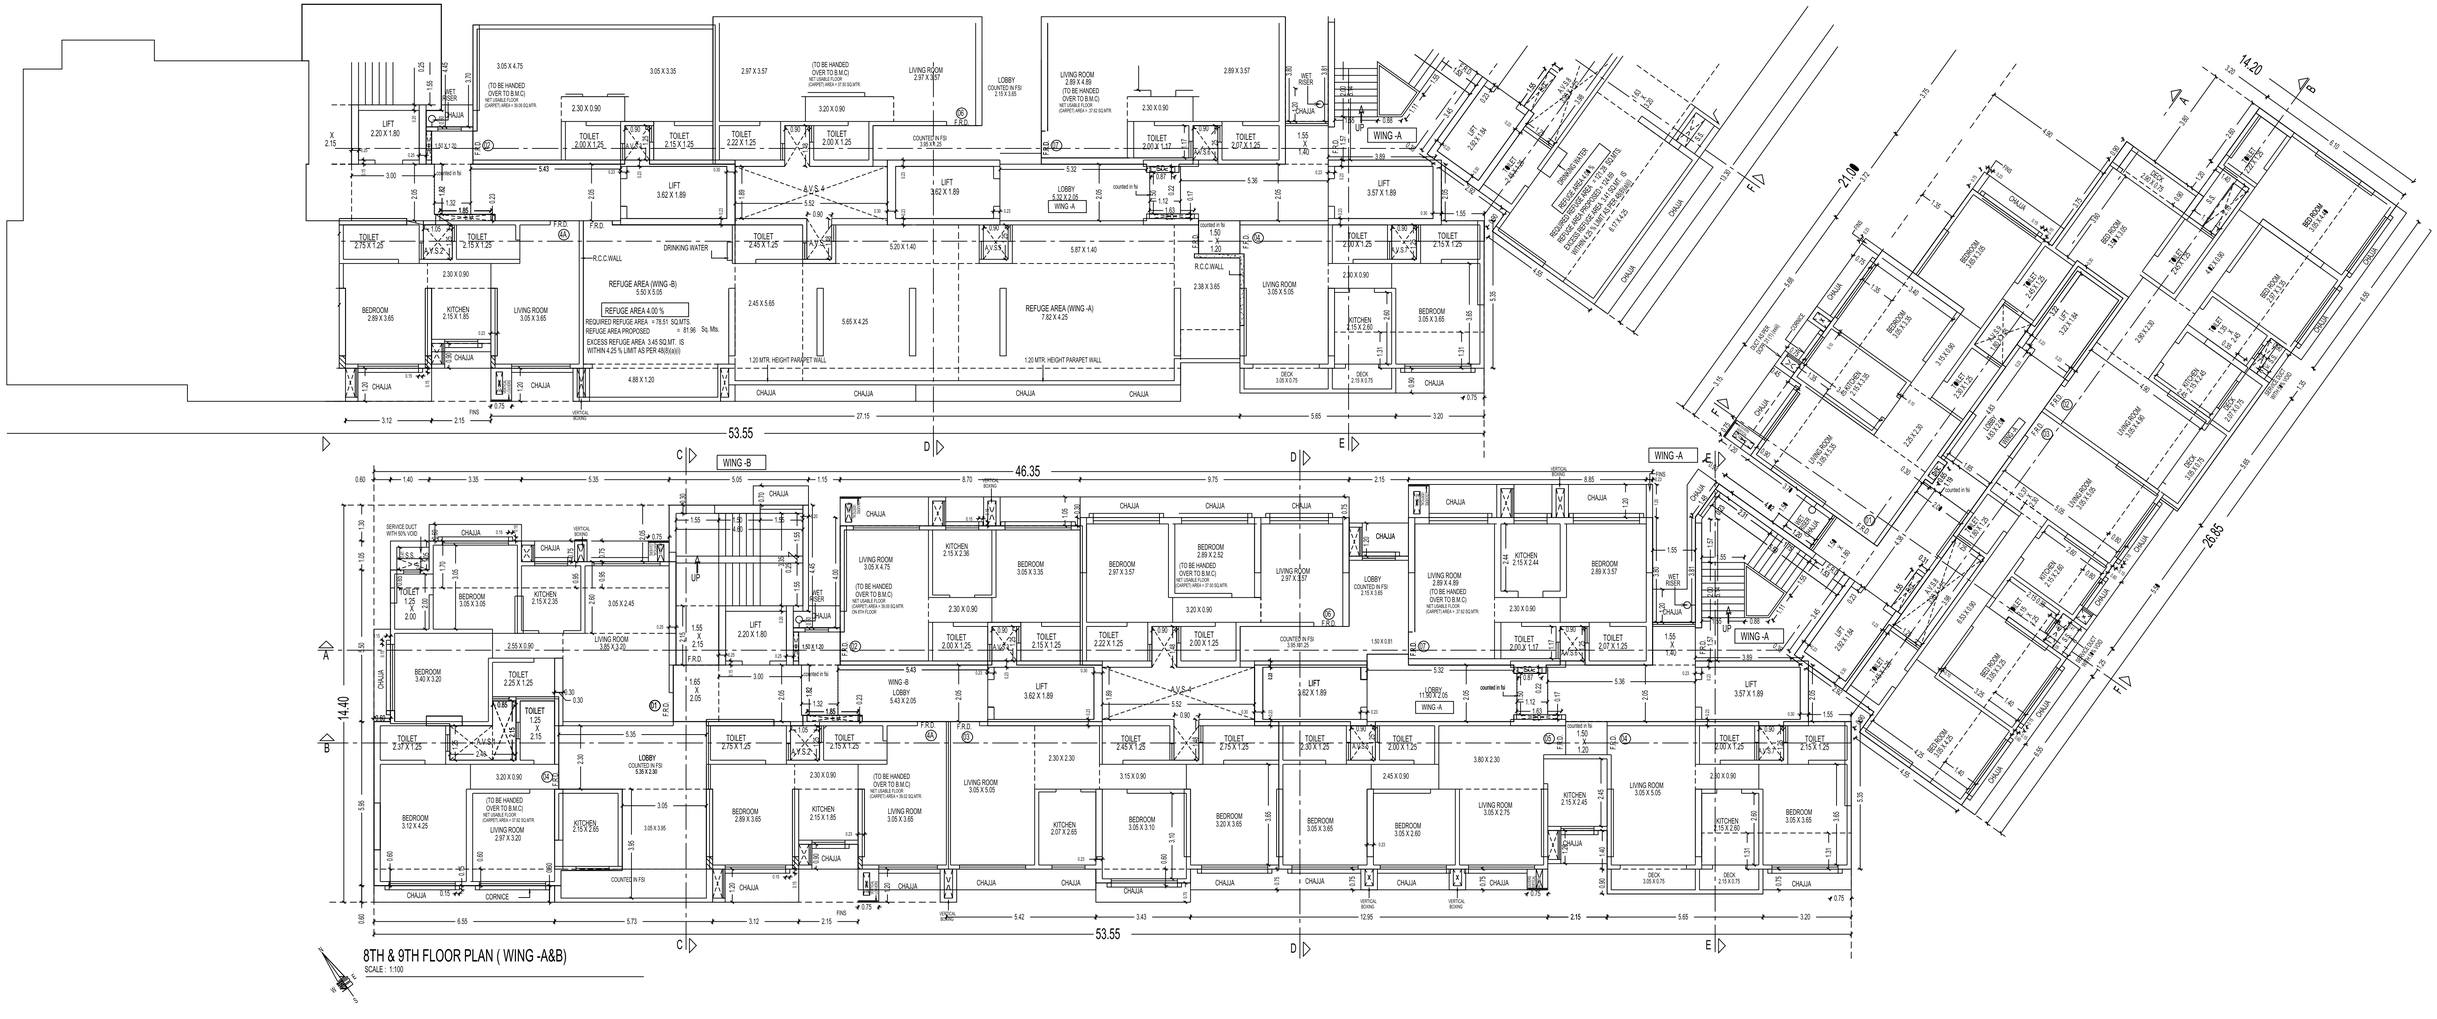
WING -B
WING -A
REFUGE AREA (WING -B)
5.50 X 5.05
REFUGE AREA 4.00 %
REQUIRED REFUGE AREA = 78.51 SQ.MTS.
REFUGE AREA PROPOSED = 81.96 Sq. Mts.
EXCESS REFUGE AREA 3.45 SQ.MT. IS WITHIN 4.25 % LIMIT AS PER 48(6)(a)(i)
REFUGE AREA (WING -A)
7.82 X 4.25
1.20 MTR. HEIGHT PARAPET WALL
DRINKING WATER
R.C.C.WALL
LIFT
LOBBY
LIVING ROOM
BEDROOM
KITCHEN
TOILET
CHAJJA
DECK
53.55
46.35
14.40
26.05
14.20
21.00
8TH & 9TH FLOOR PLAN (WING -A&B)
SCALE : 1:100

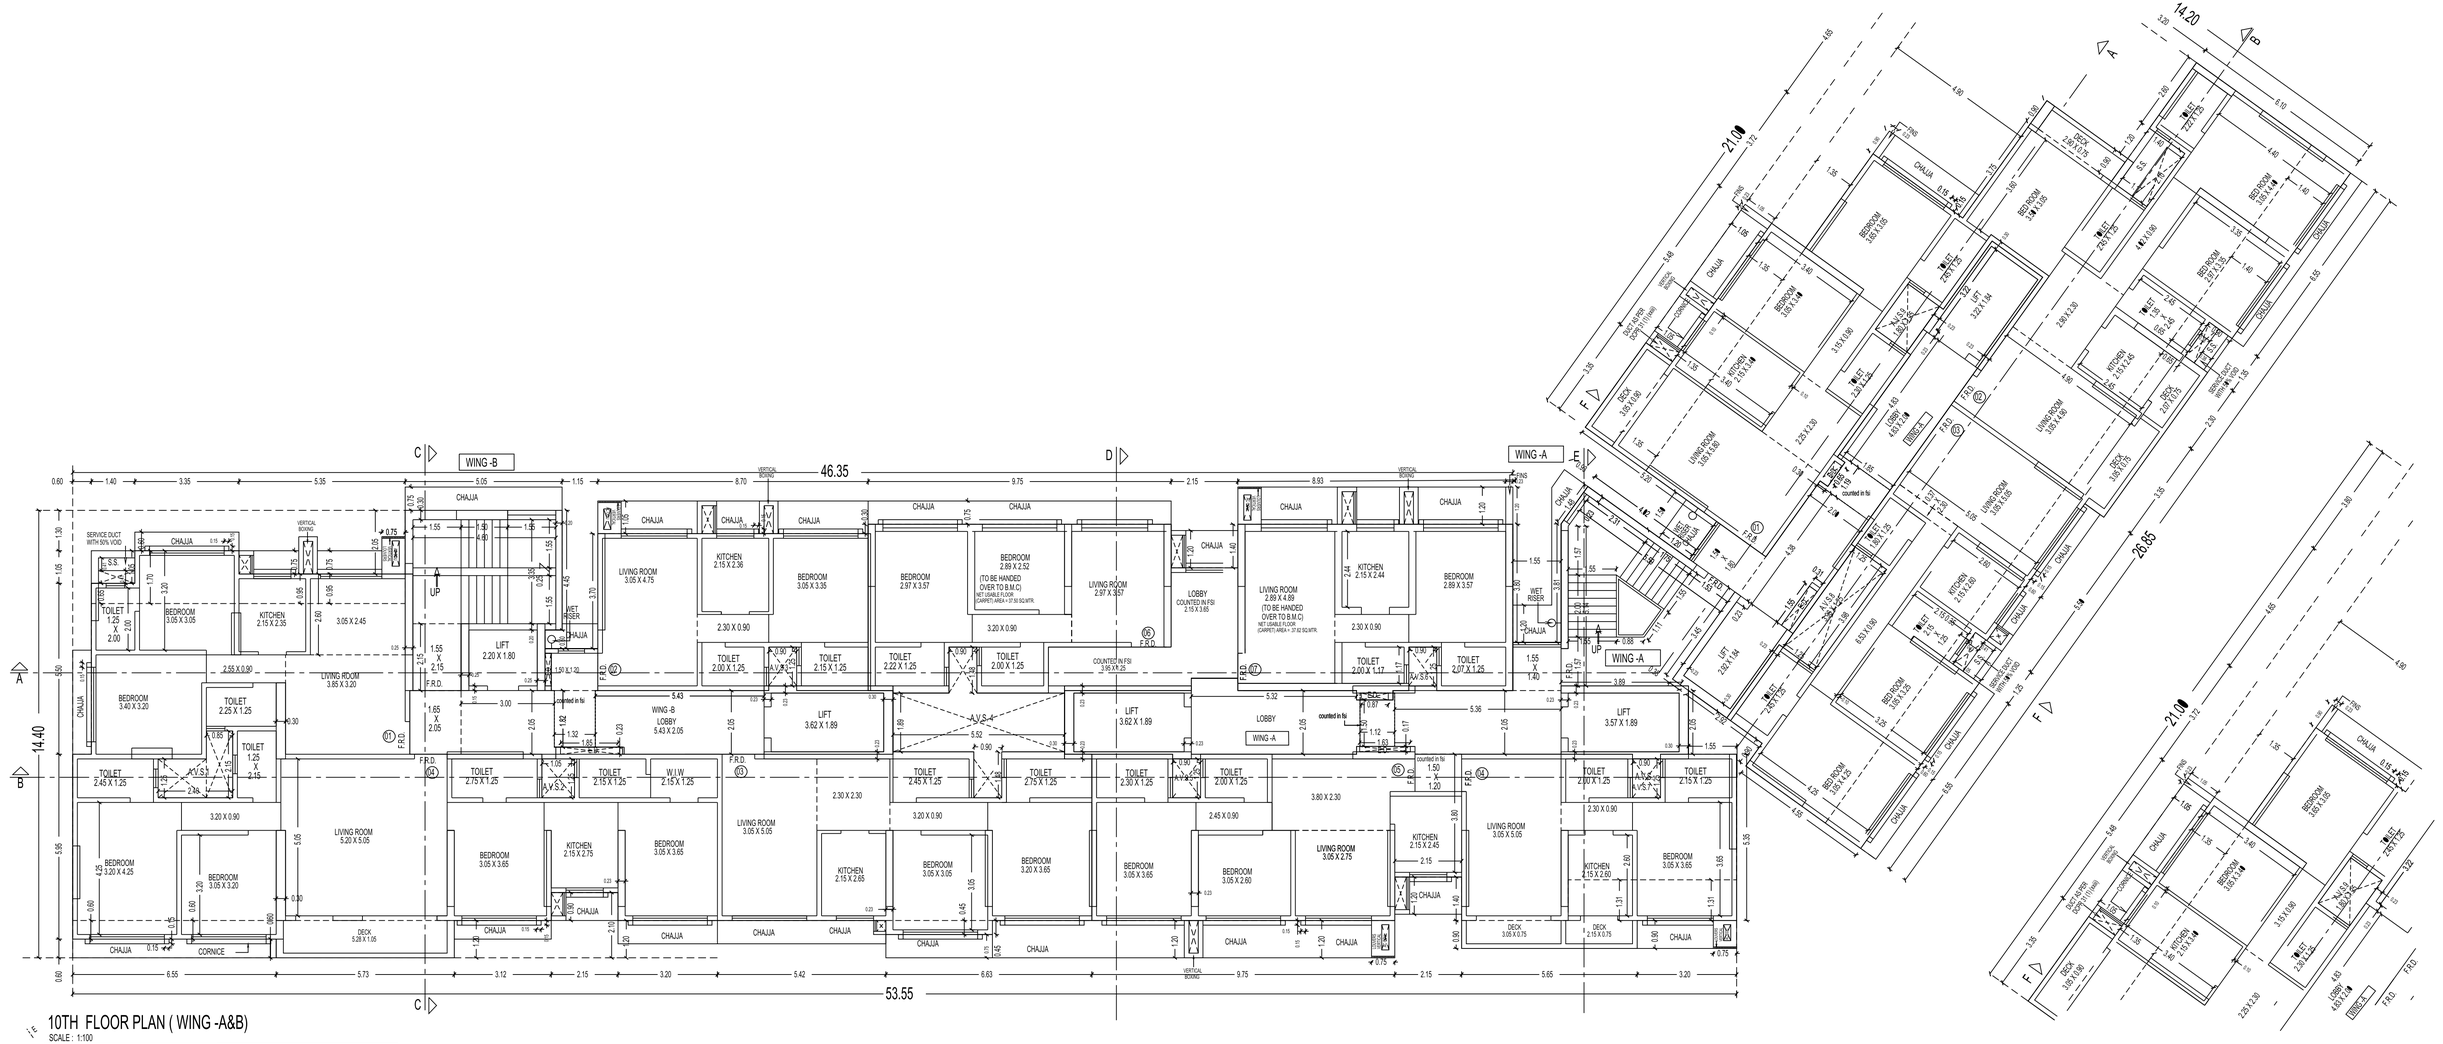

10TH FLOOR PLAN (WING -A&B)

SCALE : 1:100

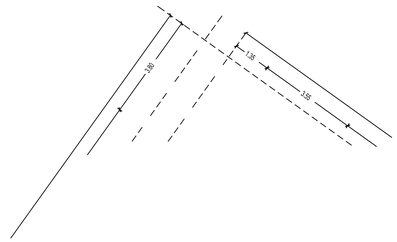

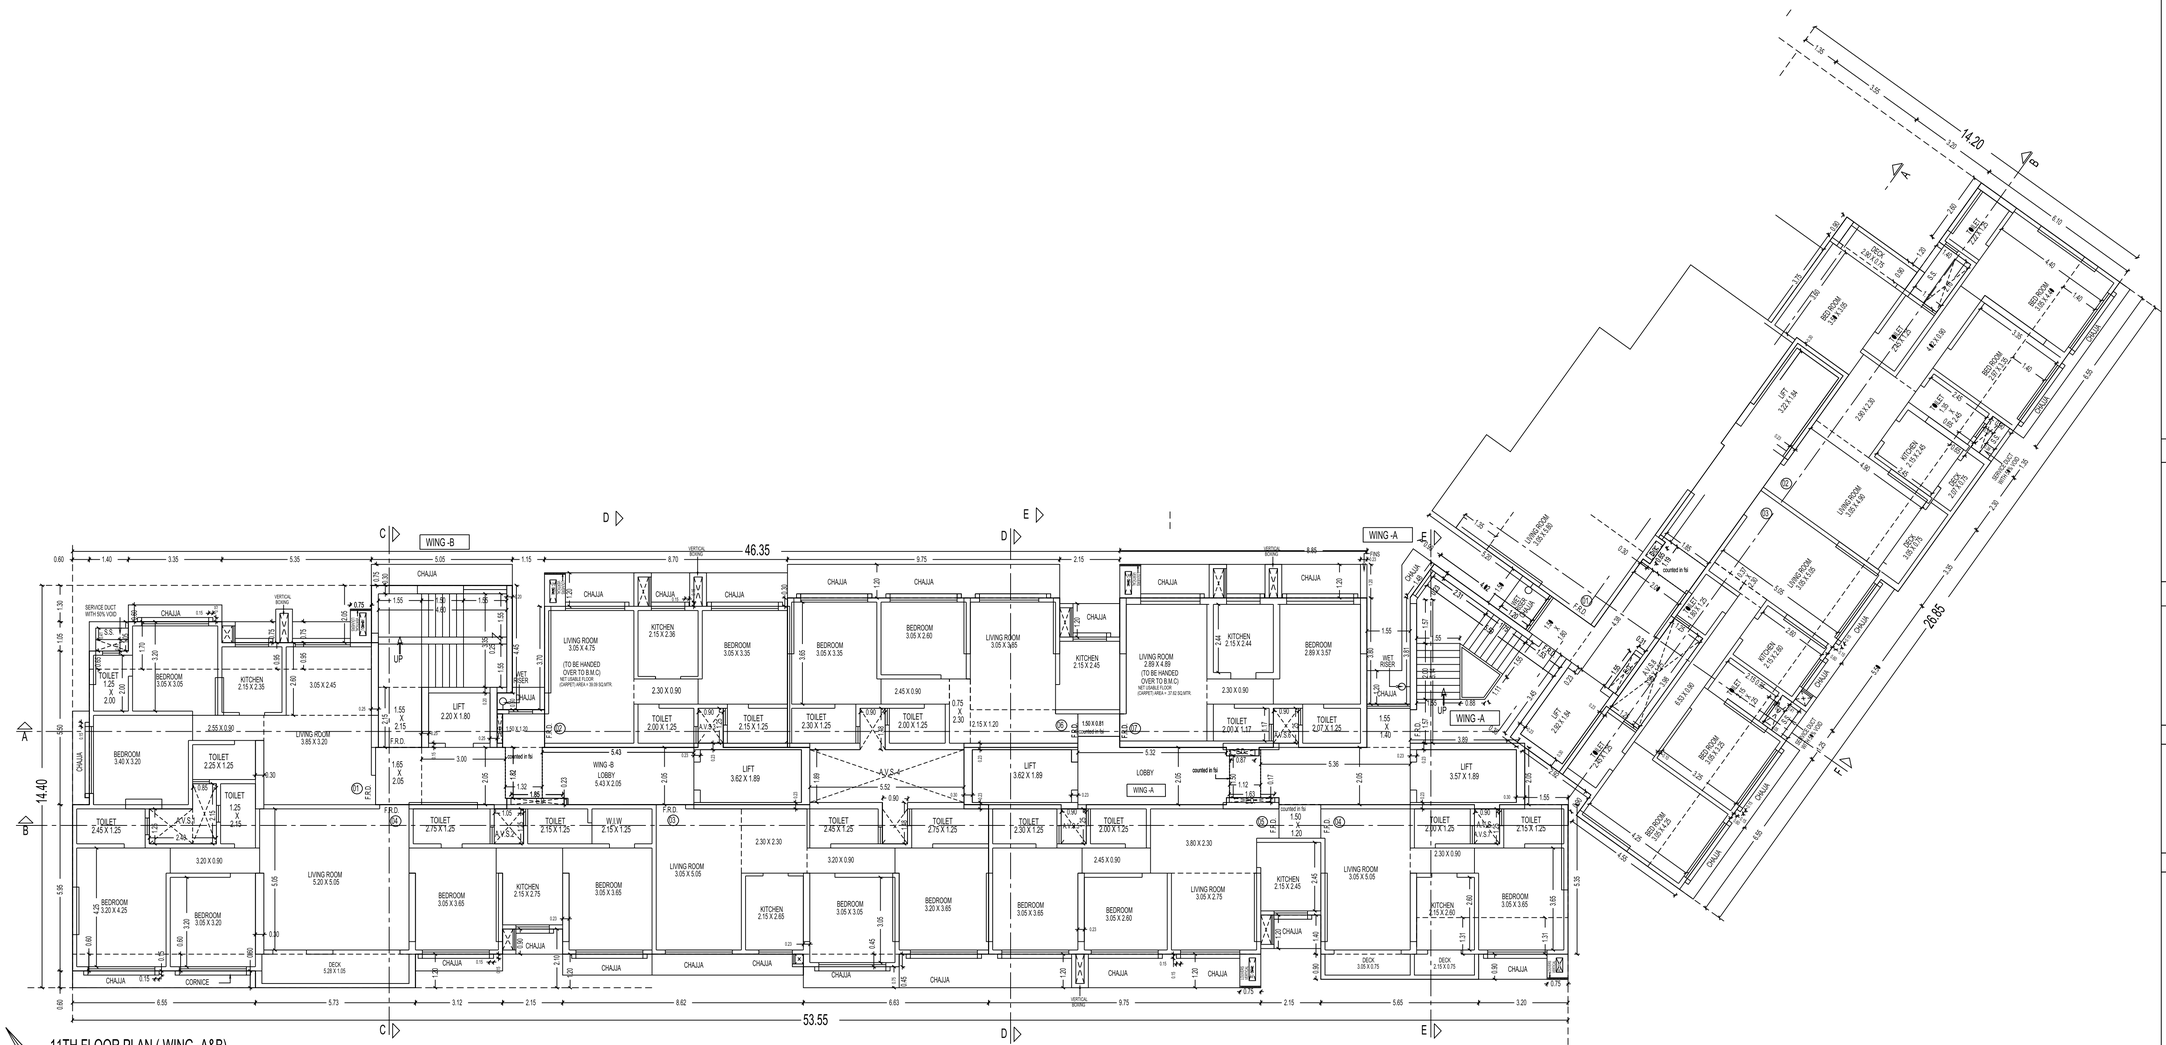

STAMP & DATE OF APPROVAL OF PLAN

THIS CANCELS APPROVAL TO THE PREVIOUS PLANS SANCTIONED UNDER AUTODCR NO. P- 23225/2024/(896) /WARD/MULUND-E/337/1/NEW - DATED 27-12 -2024

APPROVED SUBJECT TO THE CONDITIONS MENTIONED IN THIS OFFICE LETTER NO. P- 23225/2024/(896) /T WARD/MULUND-E/337/1/NEW

PRAVIN VISHNU THORAT

E.E.B.P. (E.S.)-II

SWATI NIKHIL PARBAT

S.E.(B.P.) S / W

SHRUTI VINOD NARVEKAR

A.E.B.P. (S & T)

CONTENTS OF SHEET

- 7TH TO 11TH FLOOR PLAN

NAME OF THE OWNER

Harsheel Mansukh Satra

Mr. HARSHEEL MANSUKH SATRA
H.S.PROPERTY DEVELOPERS C.A.TO OWNER
NEETA APARTMENT BUILDING 1 CHS LTD
A 102 / 03,SHIV SIDDHI CHSL,ABOVE APNA SAHAKARI BANK G.V. SCHEME,RAOD NO.1,
MULUND (E) MUMBAI -400081

DESCRIPTION OF PROPOSAL

PROPOSED REDEVELOPMENT ON PLOT BEARING C.T.S NO. 896 / 1 OF VILLAGE MULUND (E) AT HUTATMA CHAPEKAR BANDHU MARG.

NAME & SIGN OF ARCHITECT

RAMJIBHAI POPATBHAI ASUNDARIA

R. P. ASUNDARIA

ARCHITECT

236,2ND FLOOR, AVIOR,
NIRMAL GALAXY, NEAR DEEP MANDIR
CINEMA,L.B.S.MARG,MULUND (W)
MUMBAI - 400080

SHEET : 6 / 17

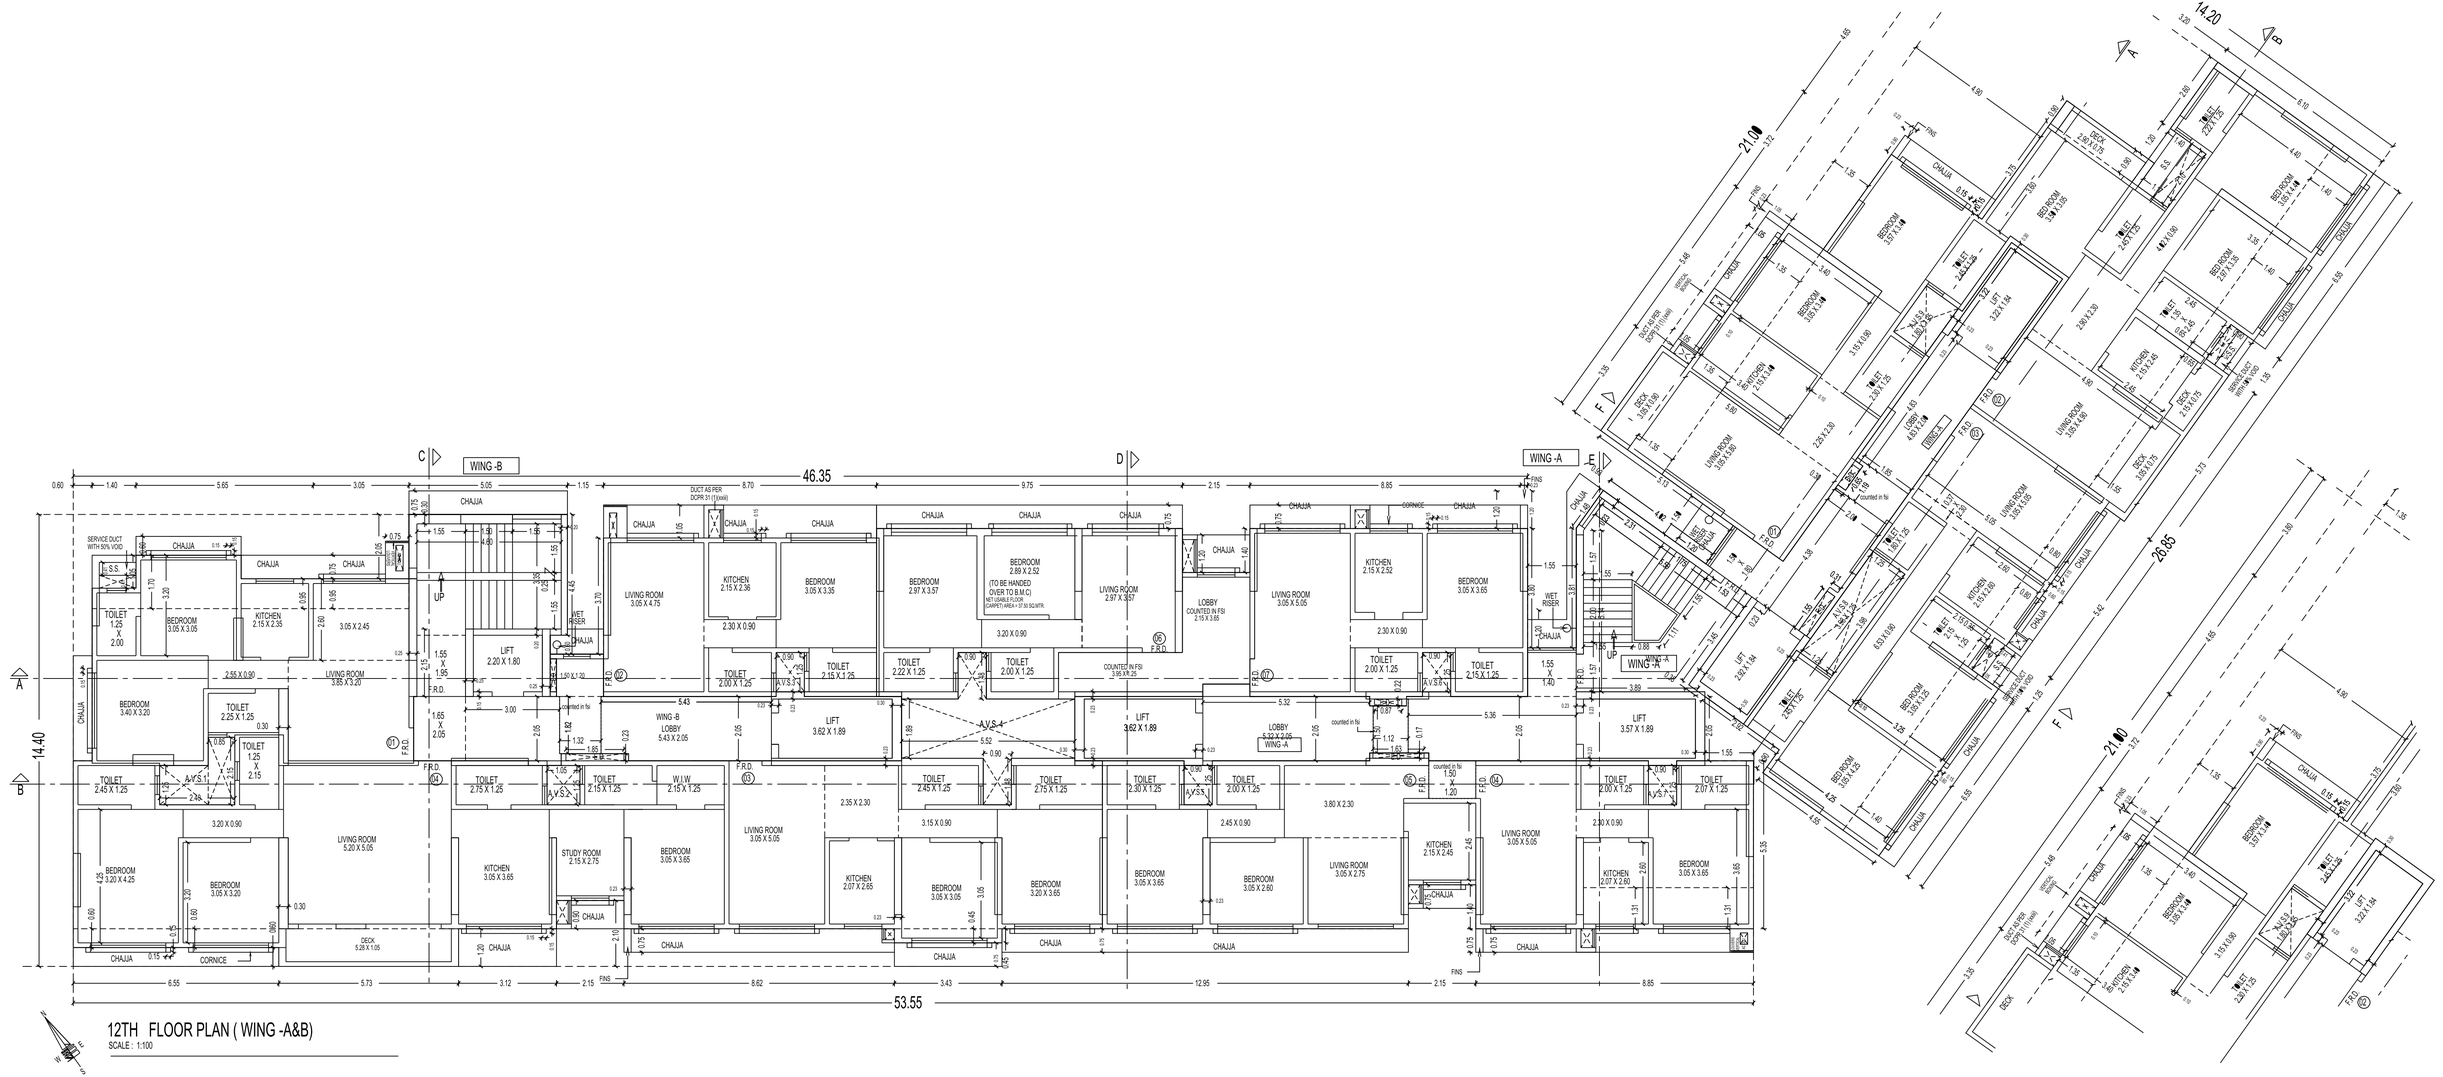

12TH FLOOR PLAN (WING -A&B)

SCALE : 1:100

13TH FLOOR PLAN (WING -A&B)

SCALE : 1:100

14TH FLOOR PLAN (WING -A&B)

SCALE : 1:100

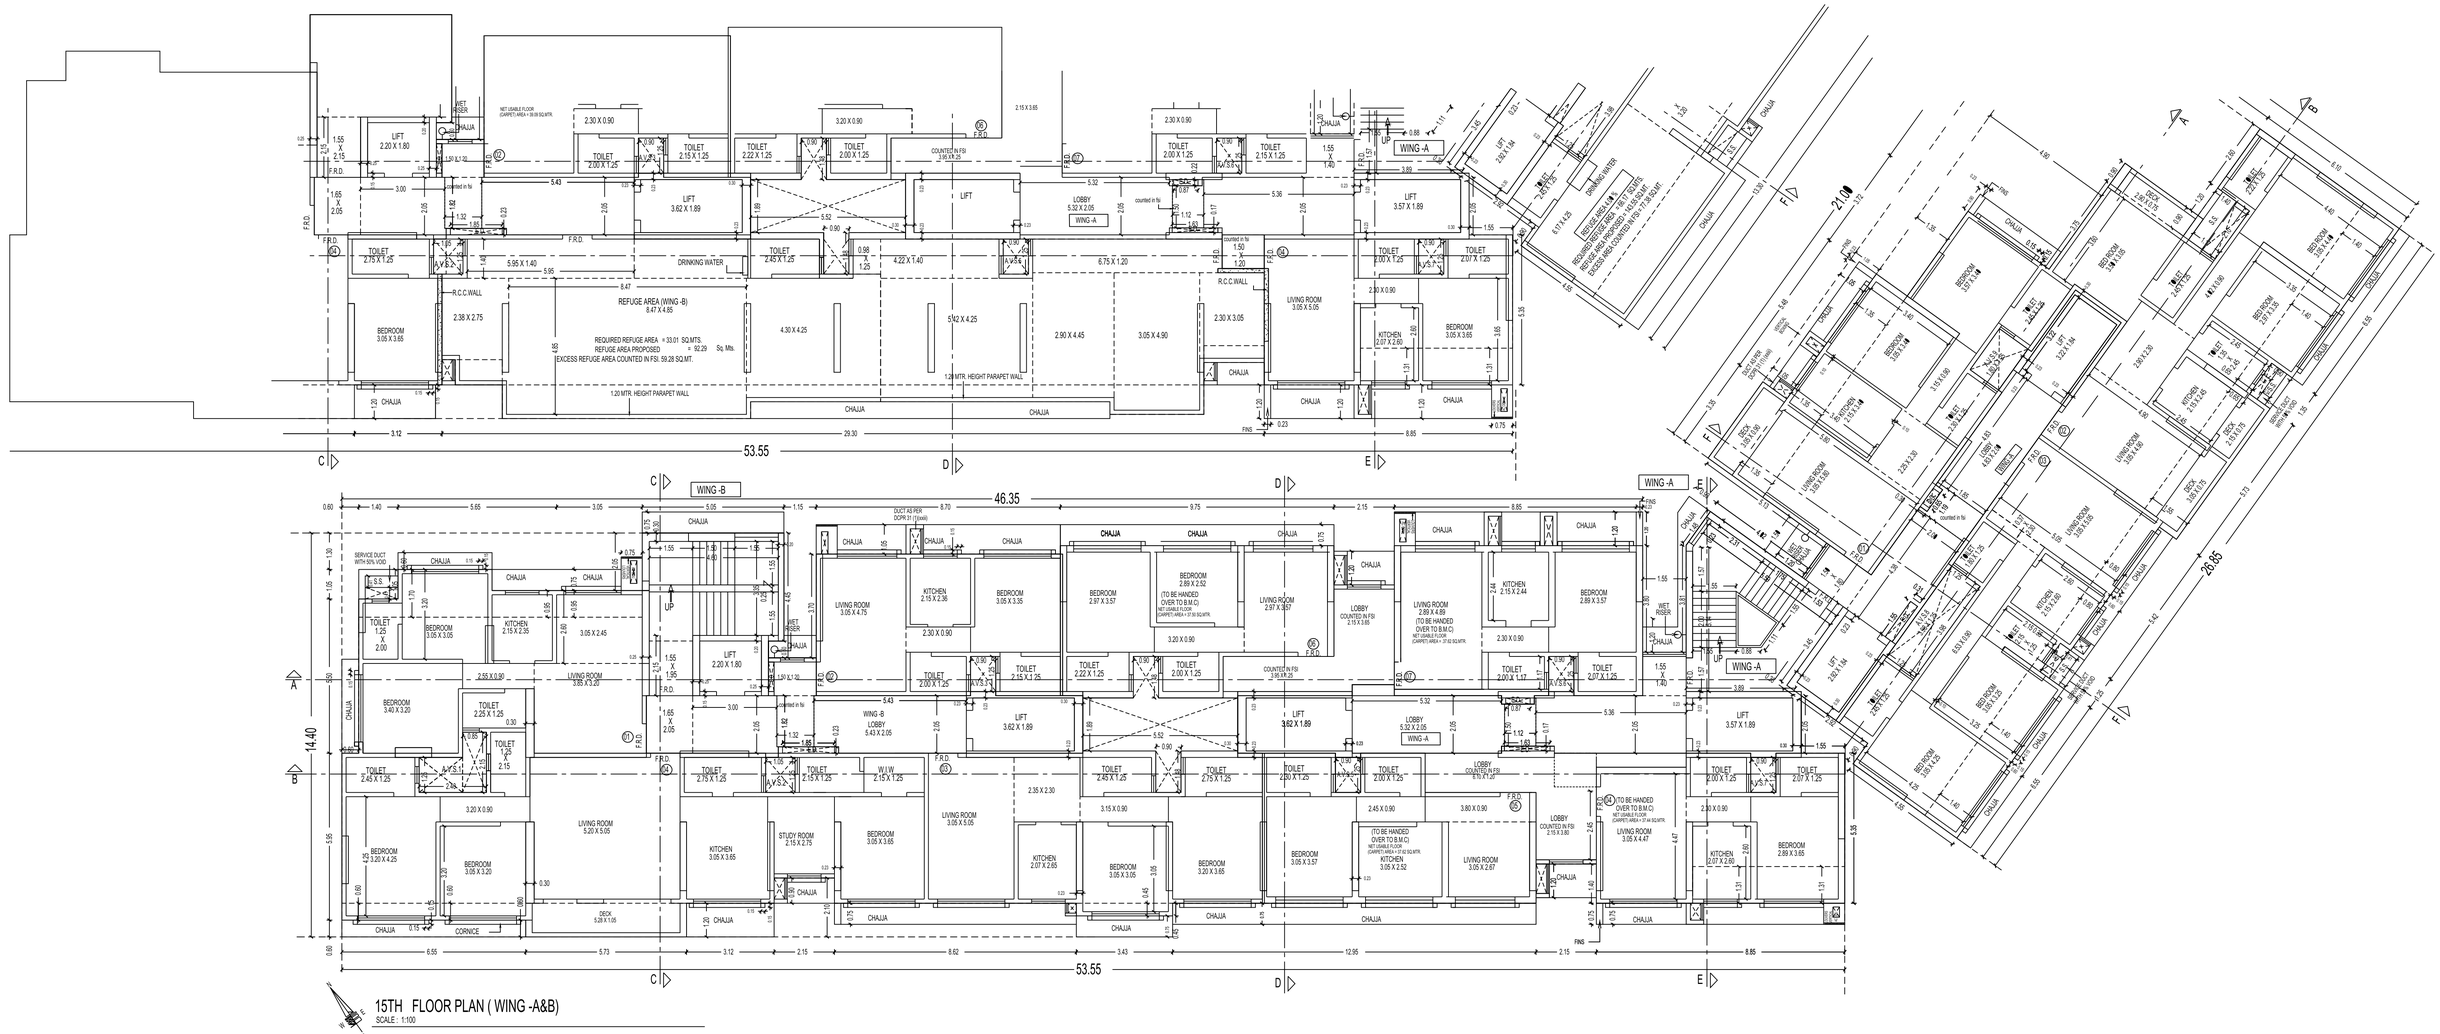

15TH FLOOR PLAN (WING -A&B)

SCALE : 1:100

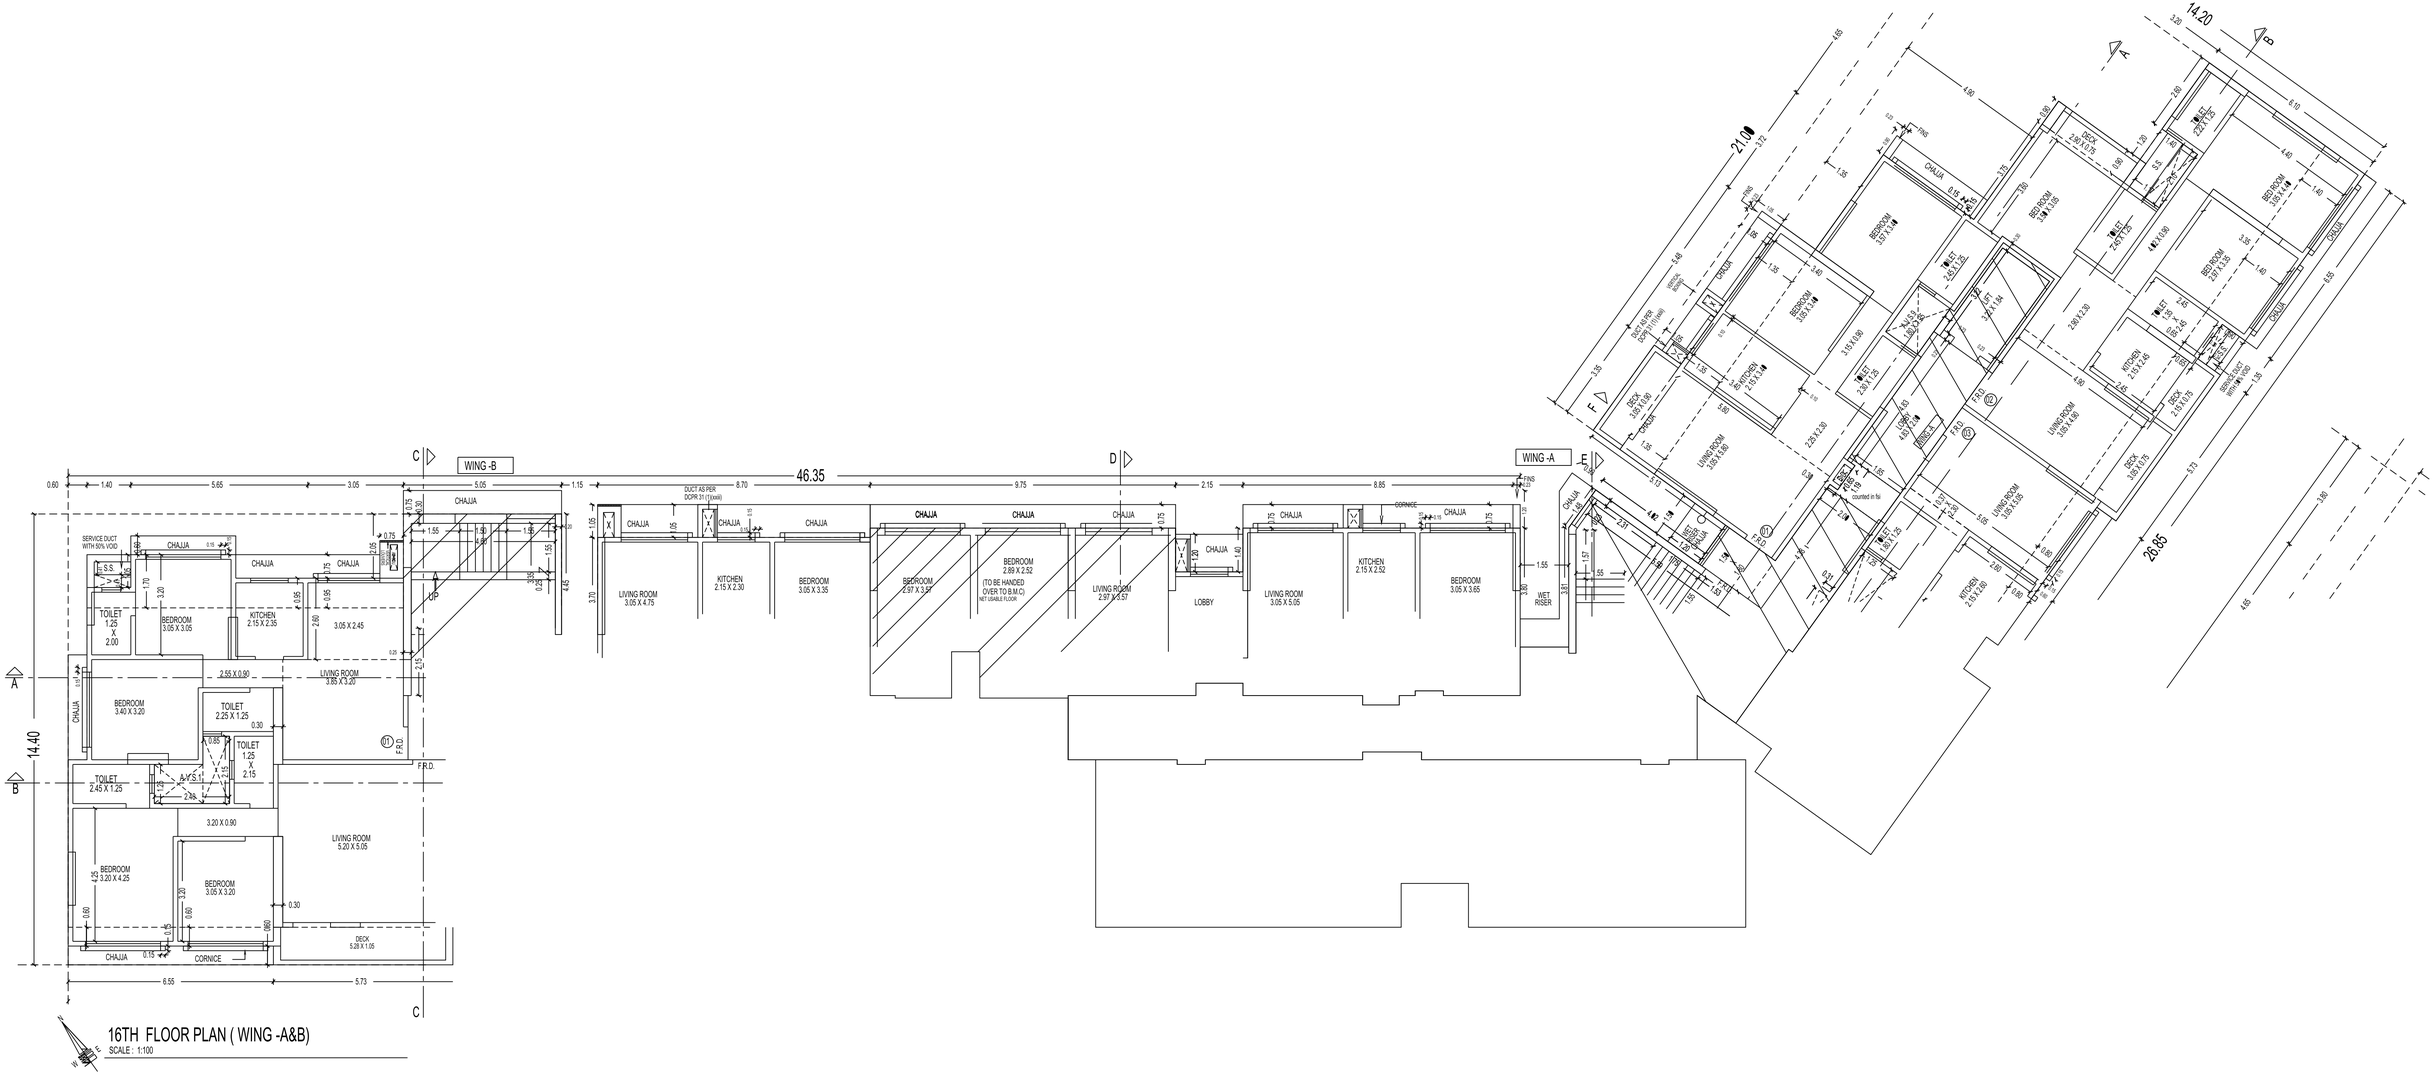
WING -B
WING -A
46.35
14.40
21.00
14.20
26.85
16TH FLOOR PLAN (WING -A&B)
SCALE : 1:100

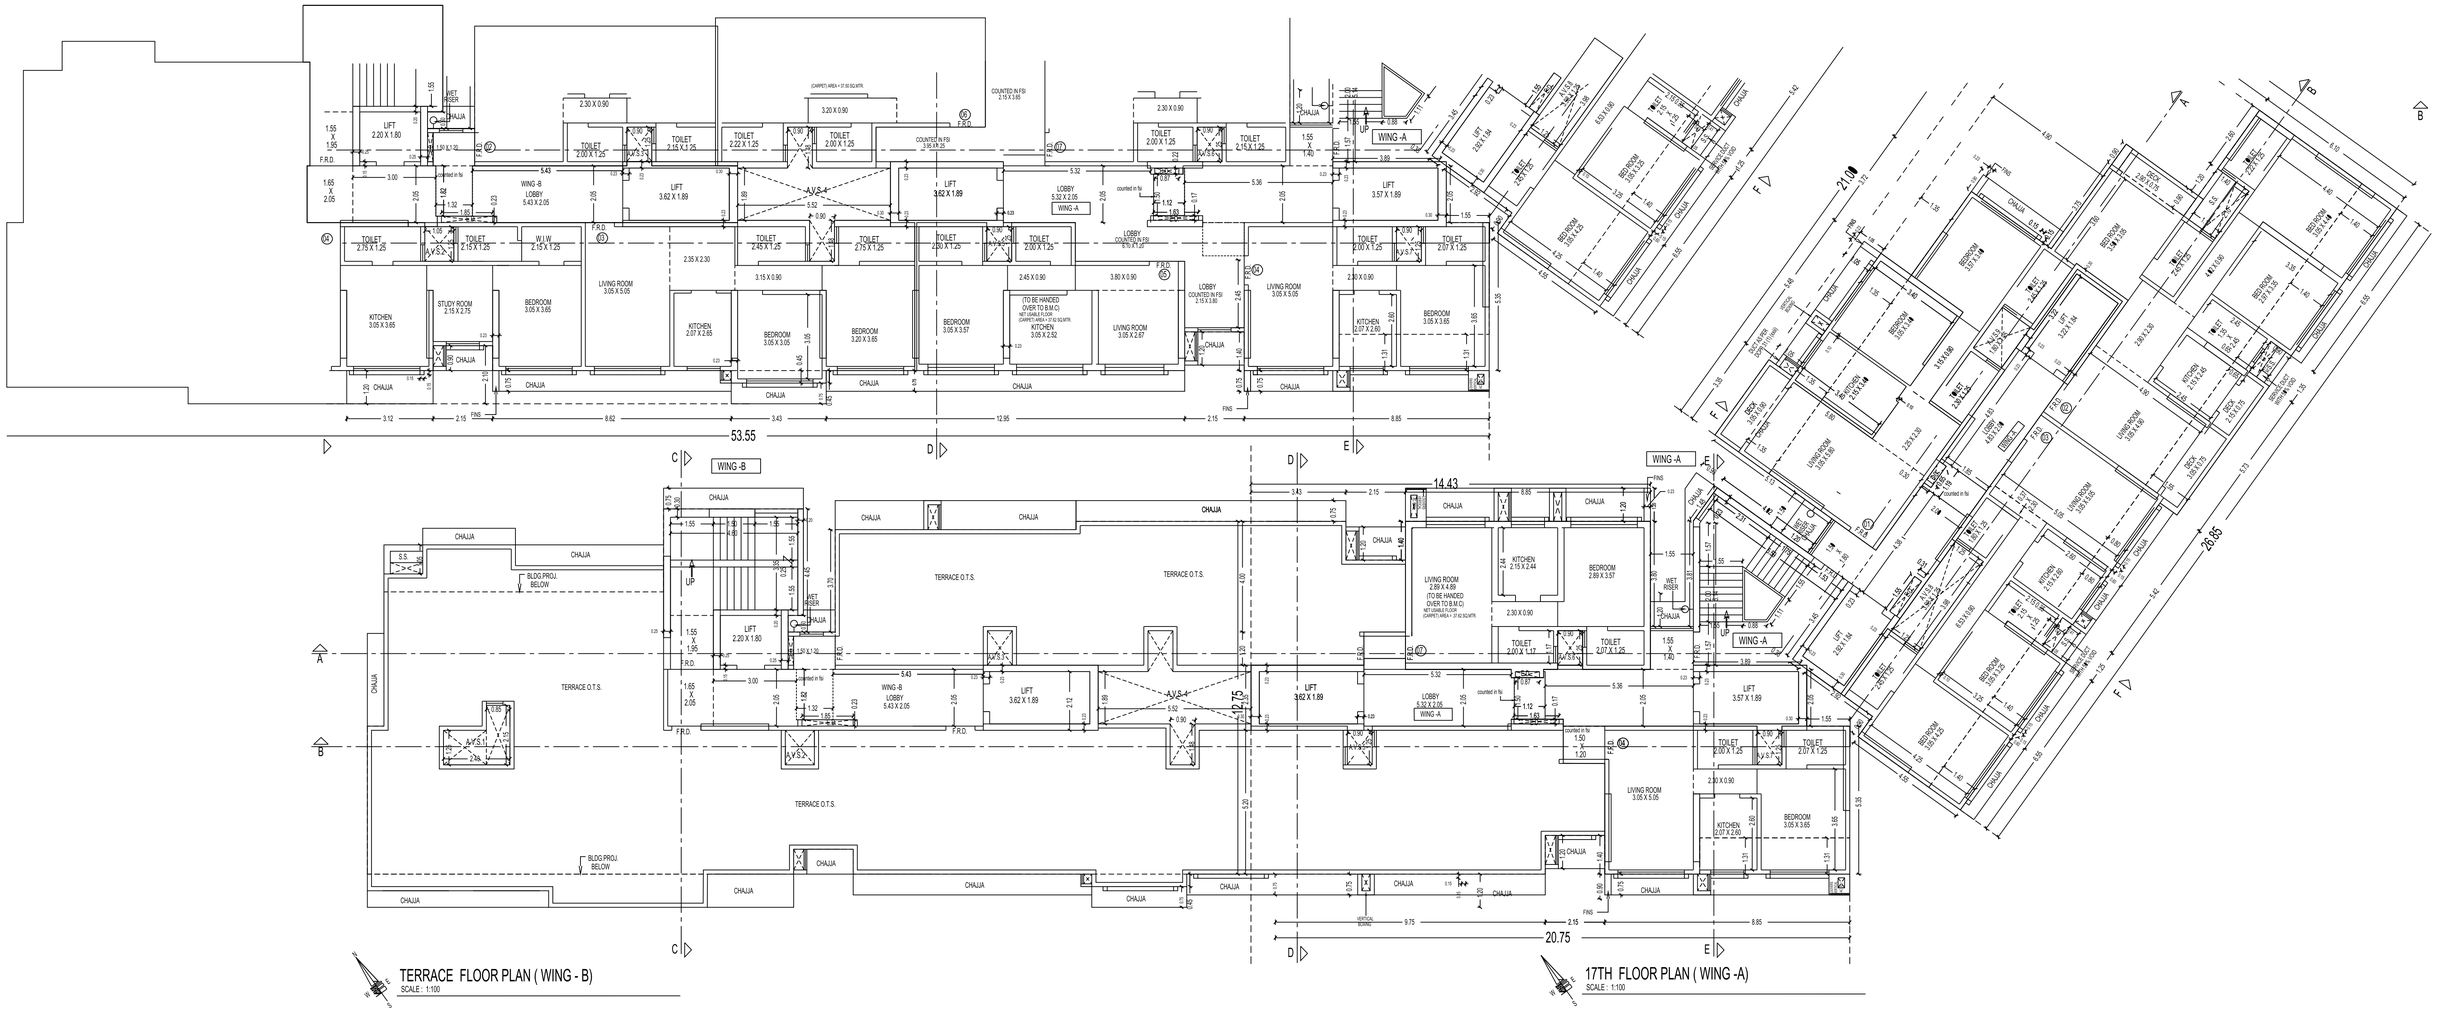
WING-B
WING-A
LIFT 2.20 X 1.80
LIFT 3.62 X 1.89
LIFT 3.57 X 1.89
WET RISER
LOBBY 5.43 X 2.05
LOBBY 5.32 X 2.05
LIVING ROOM 3.05 X 5.05
KITCHEN 3.05 X 3.65
STUDY ROOM 2.15 X 2.75
BEDROOM 3.05 X 3.65
KITCHEN 2.07 X 2.65
BEDROOM 3.05 X 3.05
BEDROOM 3.20 X 3.65
BEDROOM 3.05 X 3.57
KITCHEN 3.05 X 2.52
LIVING ROOM 3.05 X 2.67
KITCHEN 2.07 X 2.60
BEDROOM 3.05 X 3.65
TOILET 2.75 X 1.25
TOILET 2.15 X 1.25
W.I.W 2.15 X 1.25
TOILET 2.22 X 1.25
TOILET 2.00 X 1.25
TOILET 2.15 X 1.25
TOILET 2.45 X 1.25
TOILET 2.75 X 1.25
TOILET 2.00 X 1.25
TOILET 2.07 X 1.25
CHAJJA
F.R.D.
UP
DN
S.S.
BLDG.PROJ. BELOW
TERRACE O.T.S.
LIVING ROOM 2.89 X 4.69
KITCHEN 2.15 X 2.44
BEDROOM 2.89 X 3.57
TOILET 2.00 X 1.17
TOILET 2.07 X 1.25
53.55
14.43
20.75
26.85
TERRACE FLOOR PLAN (WING - B)
SCALE : 1:100
17TH FLOOR PLAN (WING -A)
SCALE : 1:100