

SCALE:-1:100

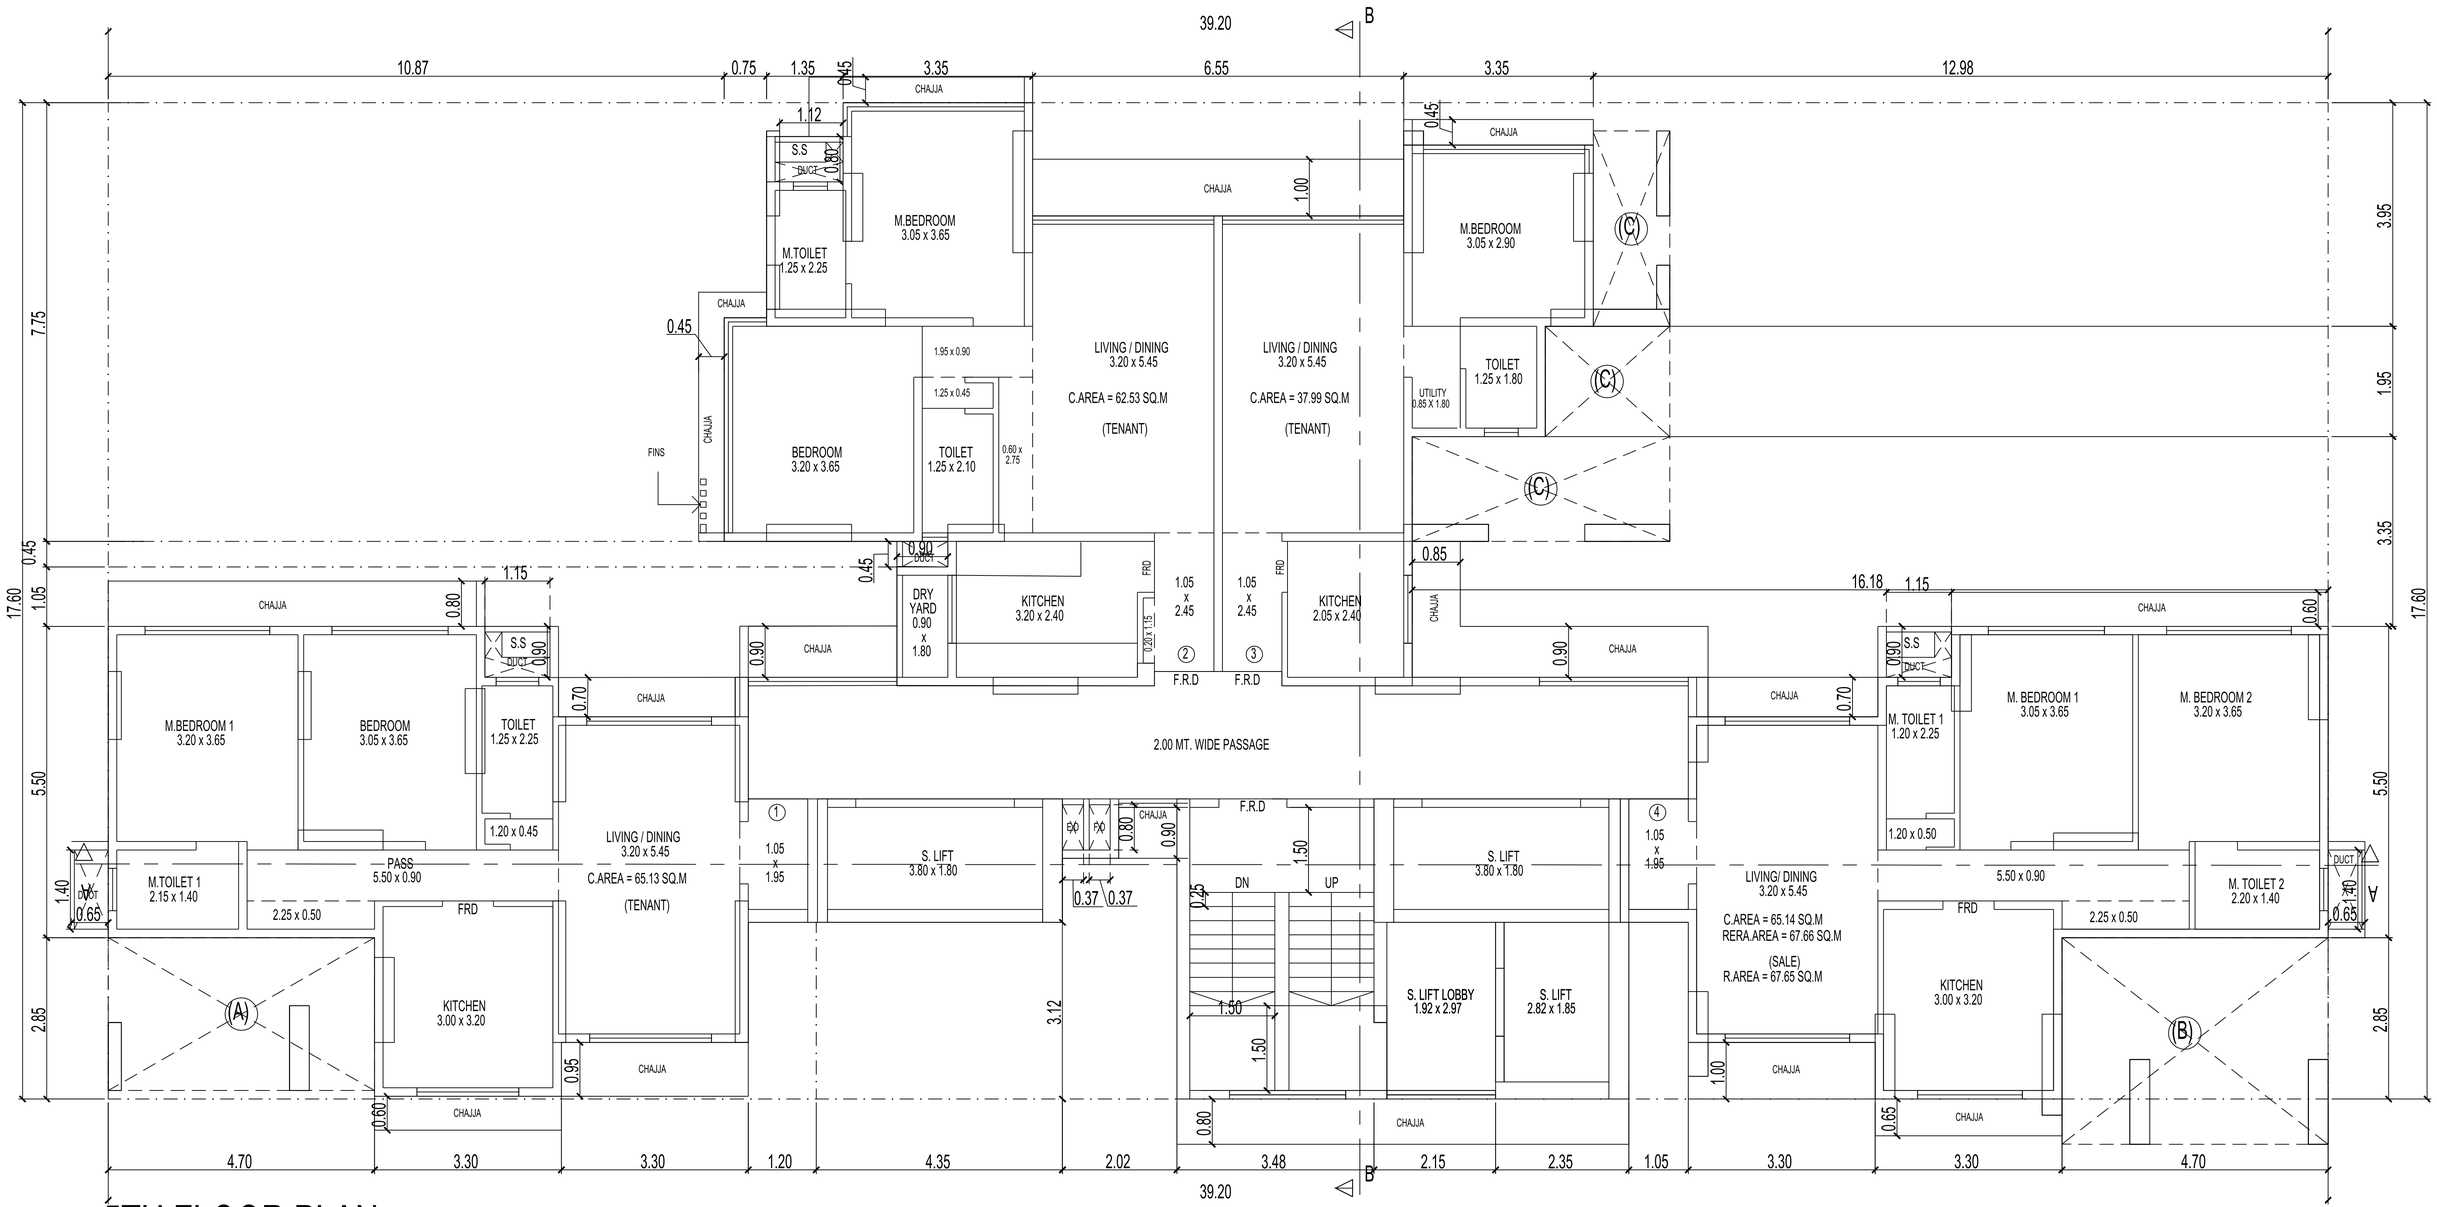


5TH FLOOR PLAN

SCALE:-1:100

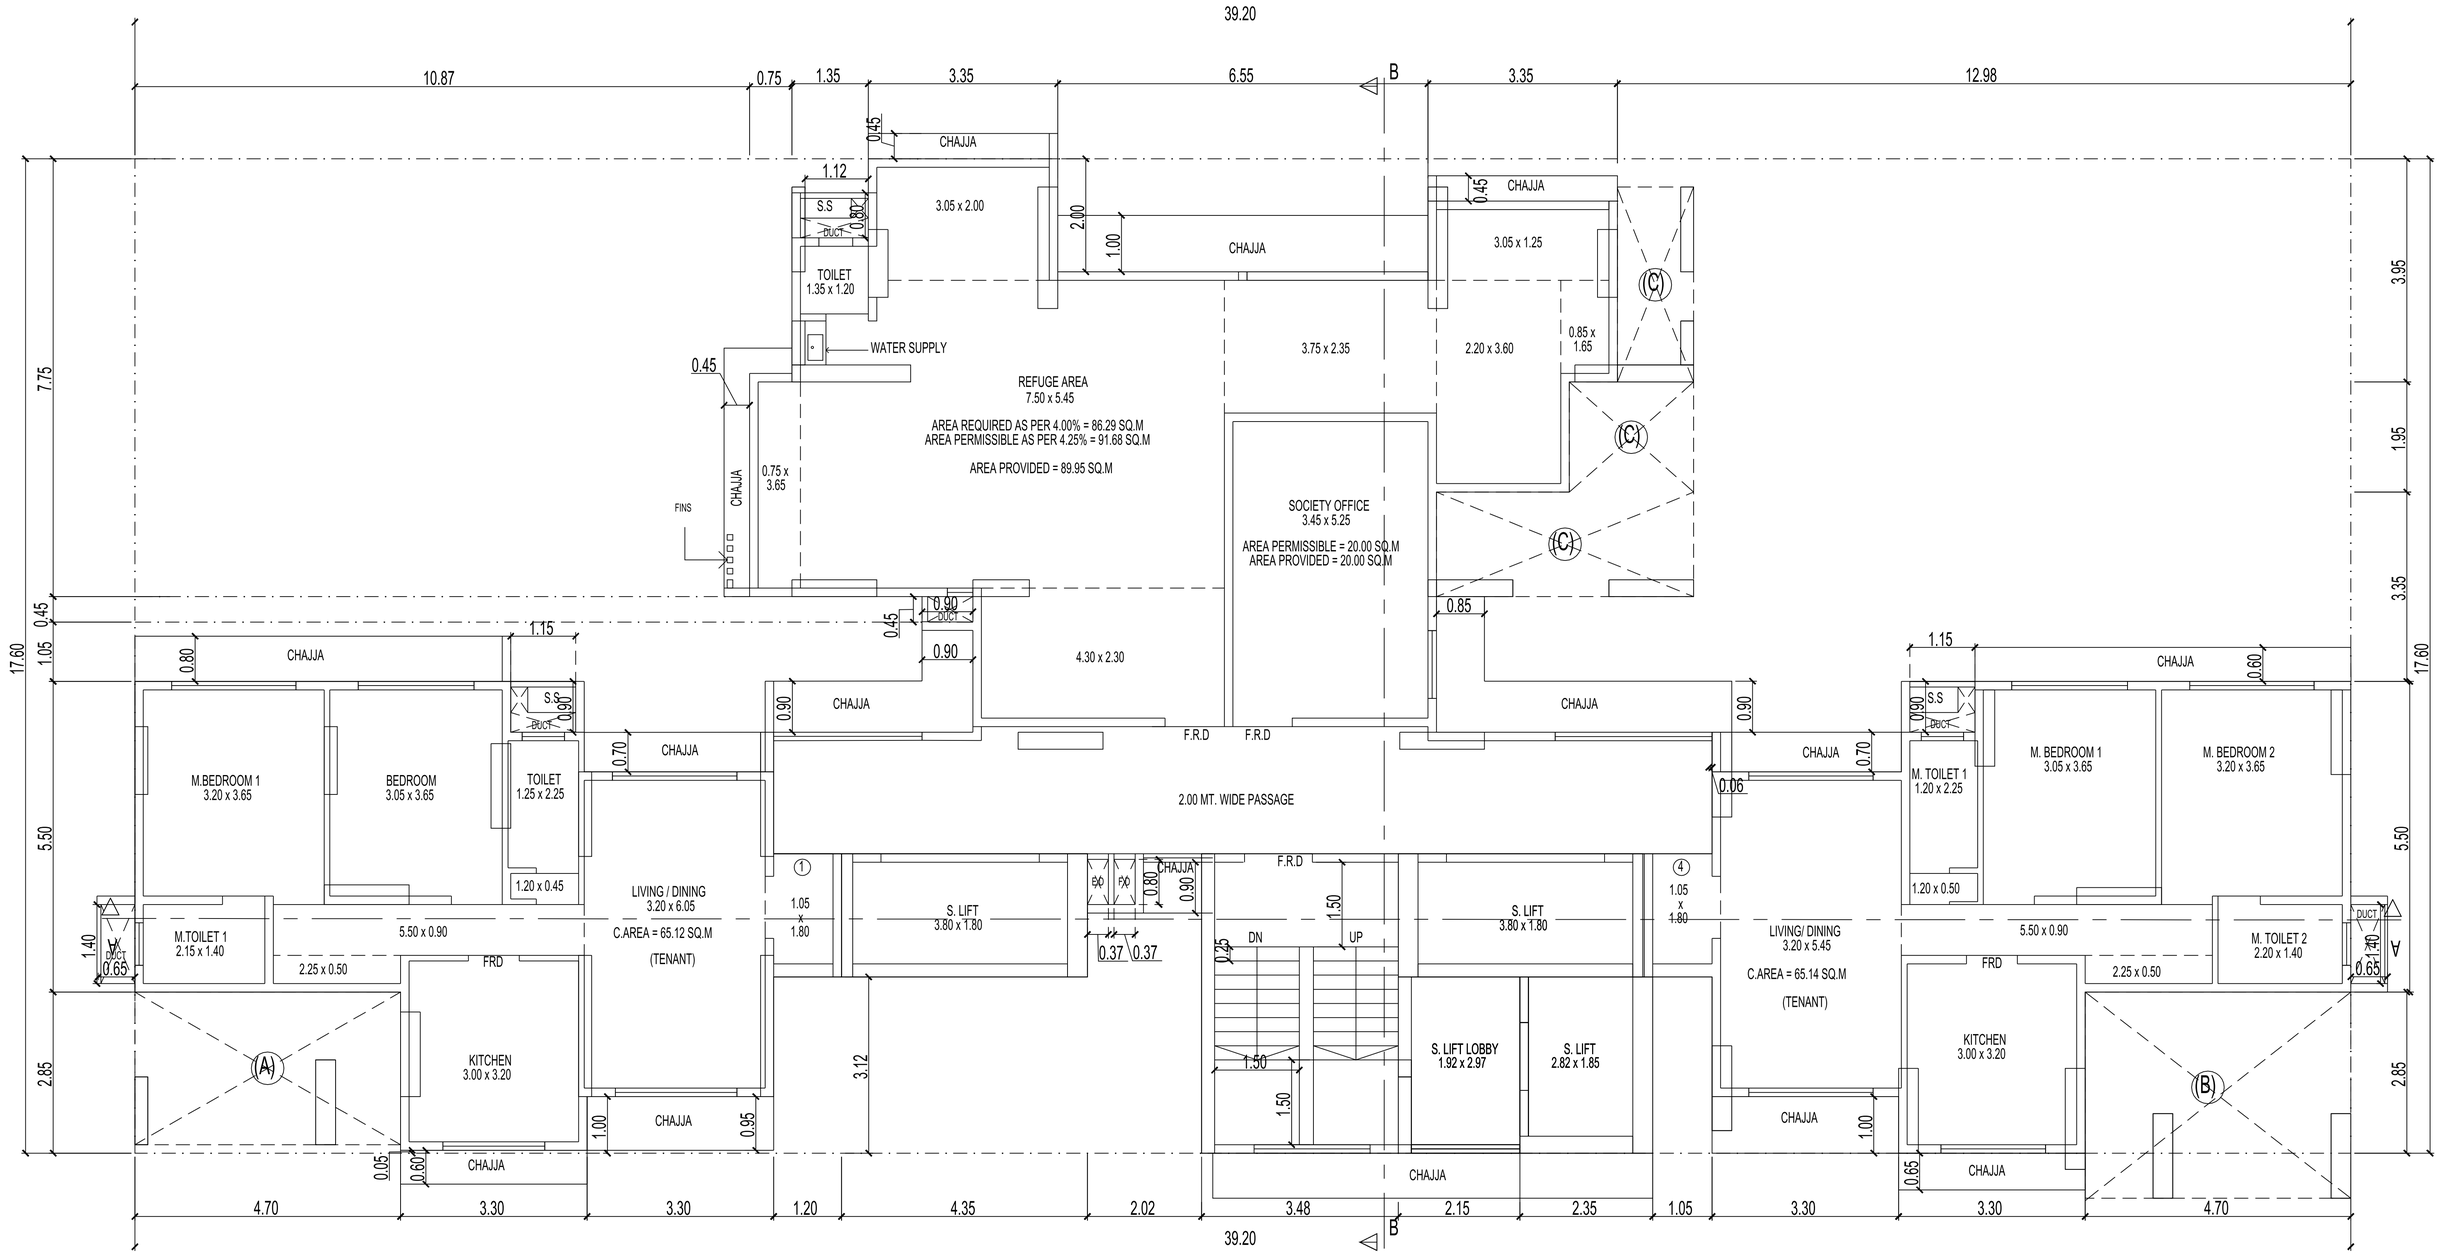


6TH FLOOR PLAN (REFUGE)

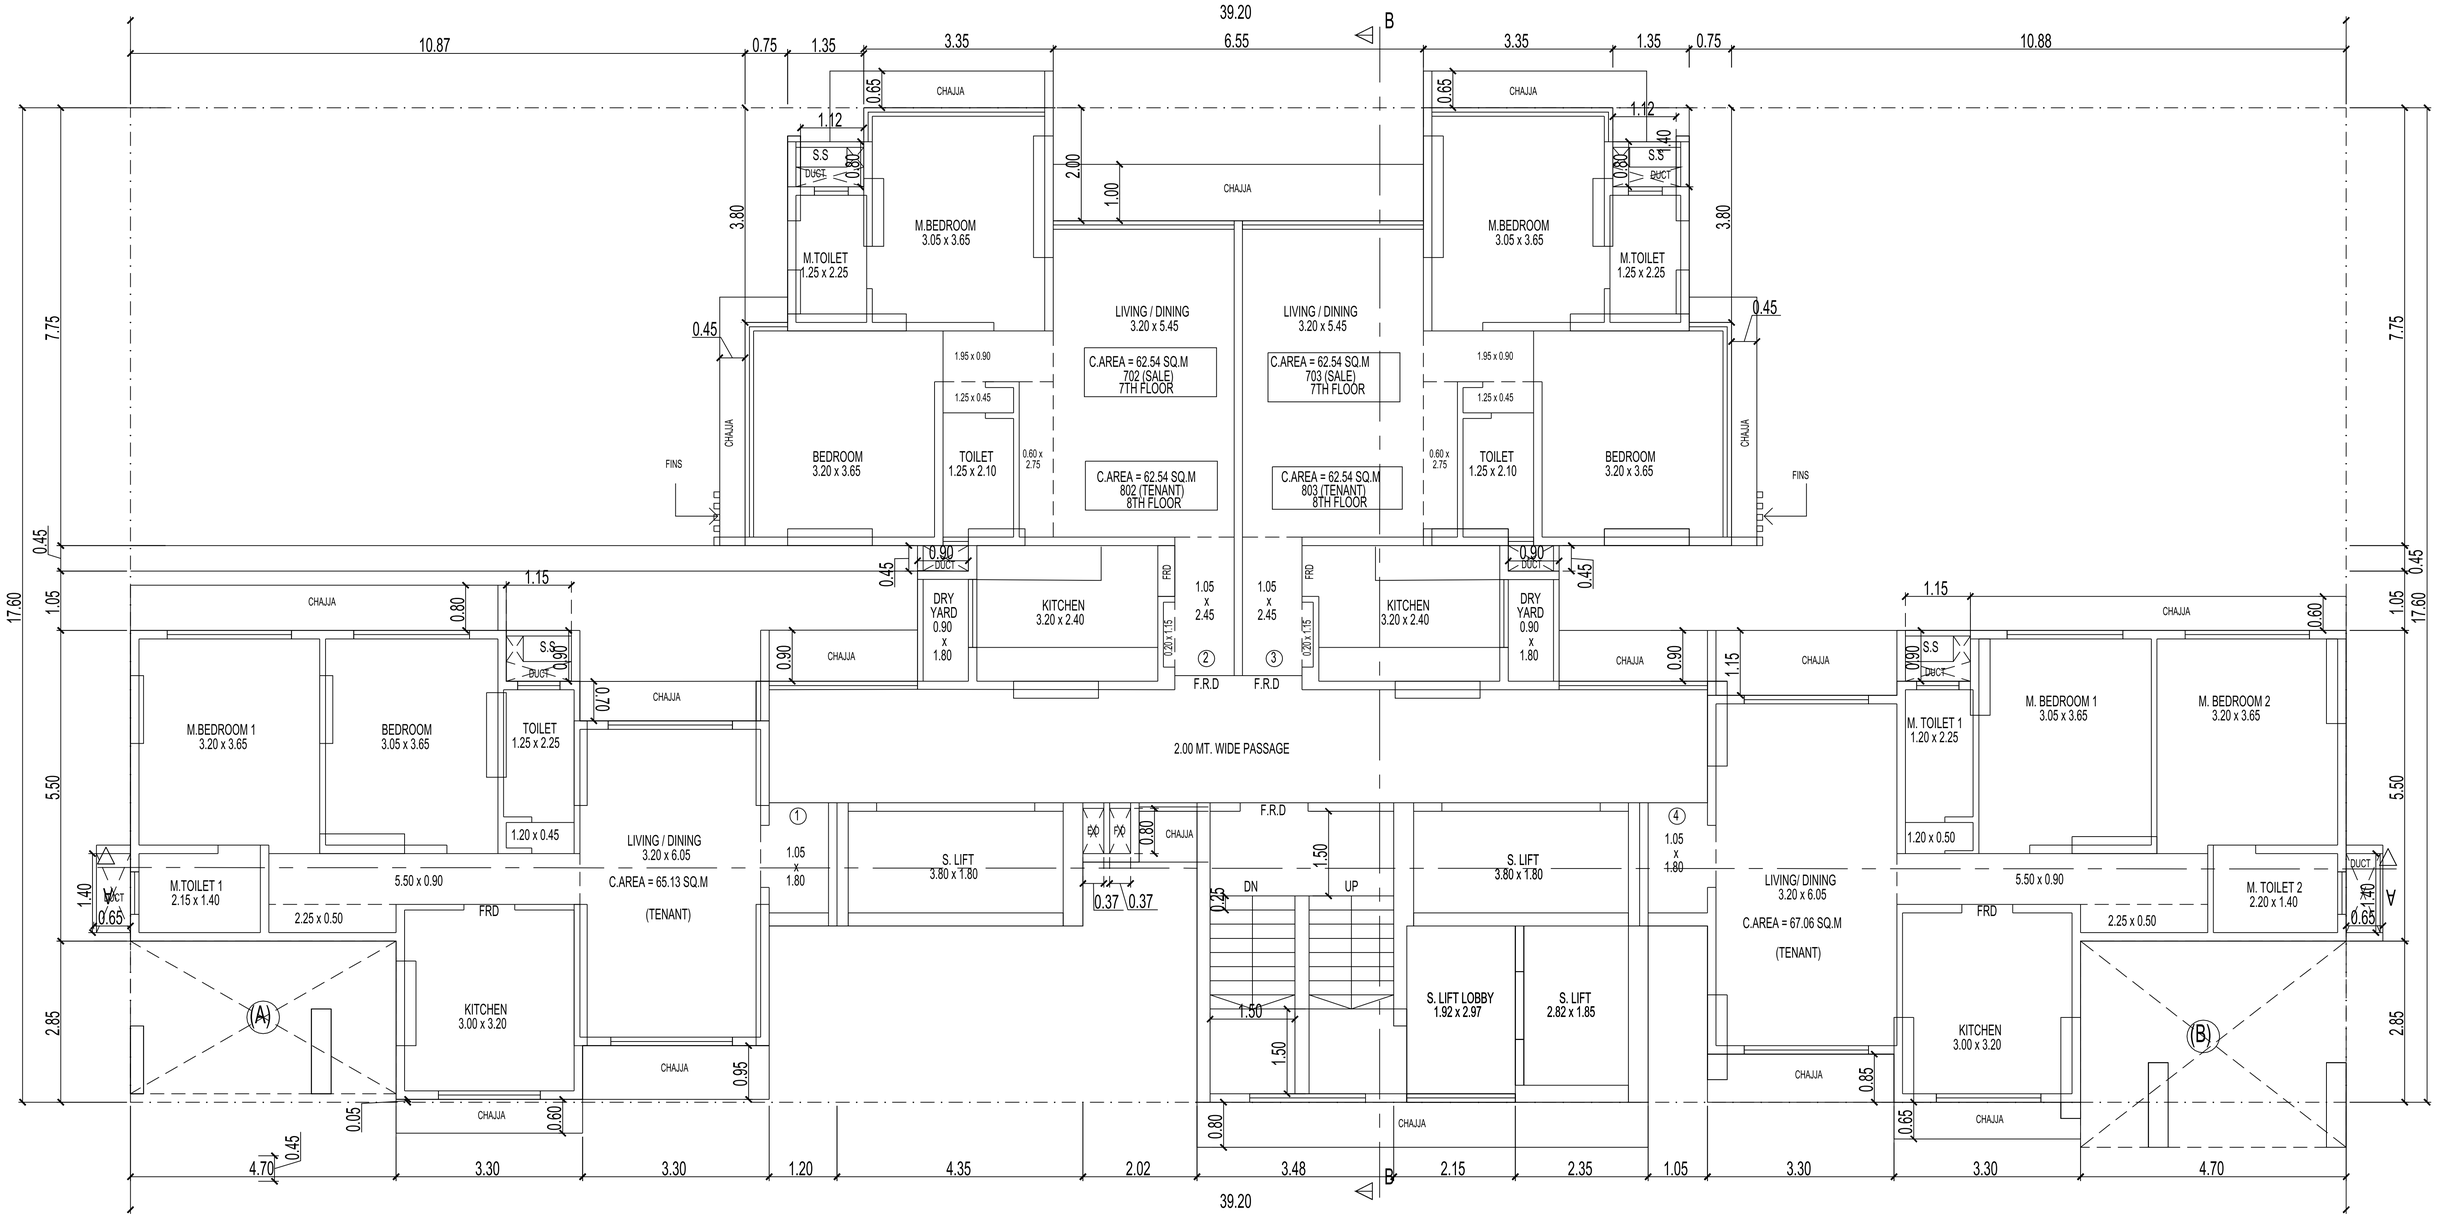

7TH & 8TH FLOOR PLAN


SCALE:-1:100

NOTE:- 702 & 703 - SALE FLATS
802 & 803 - REHAB FLATS

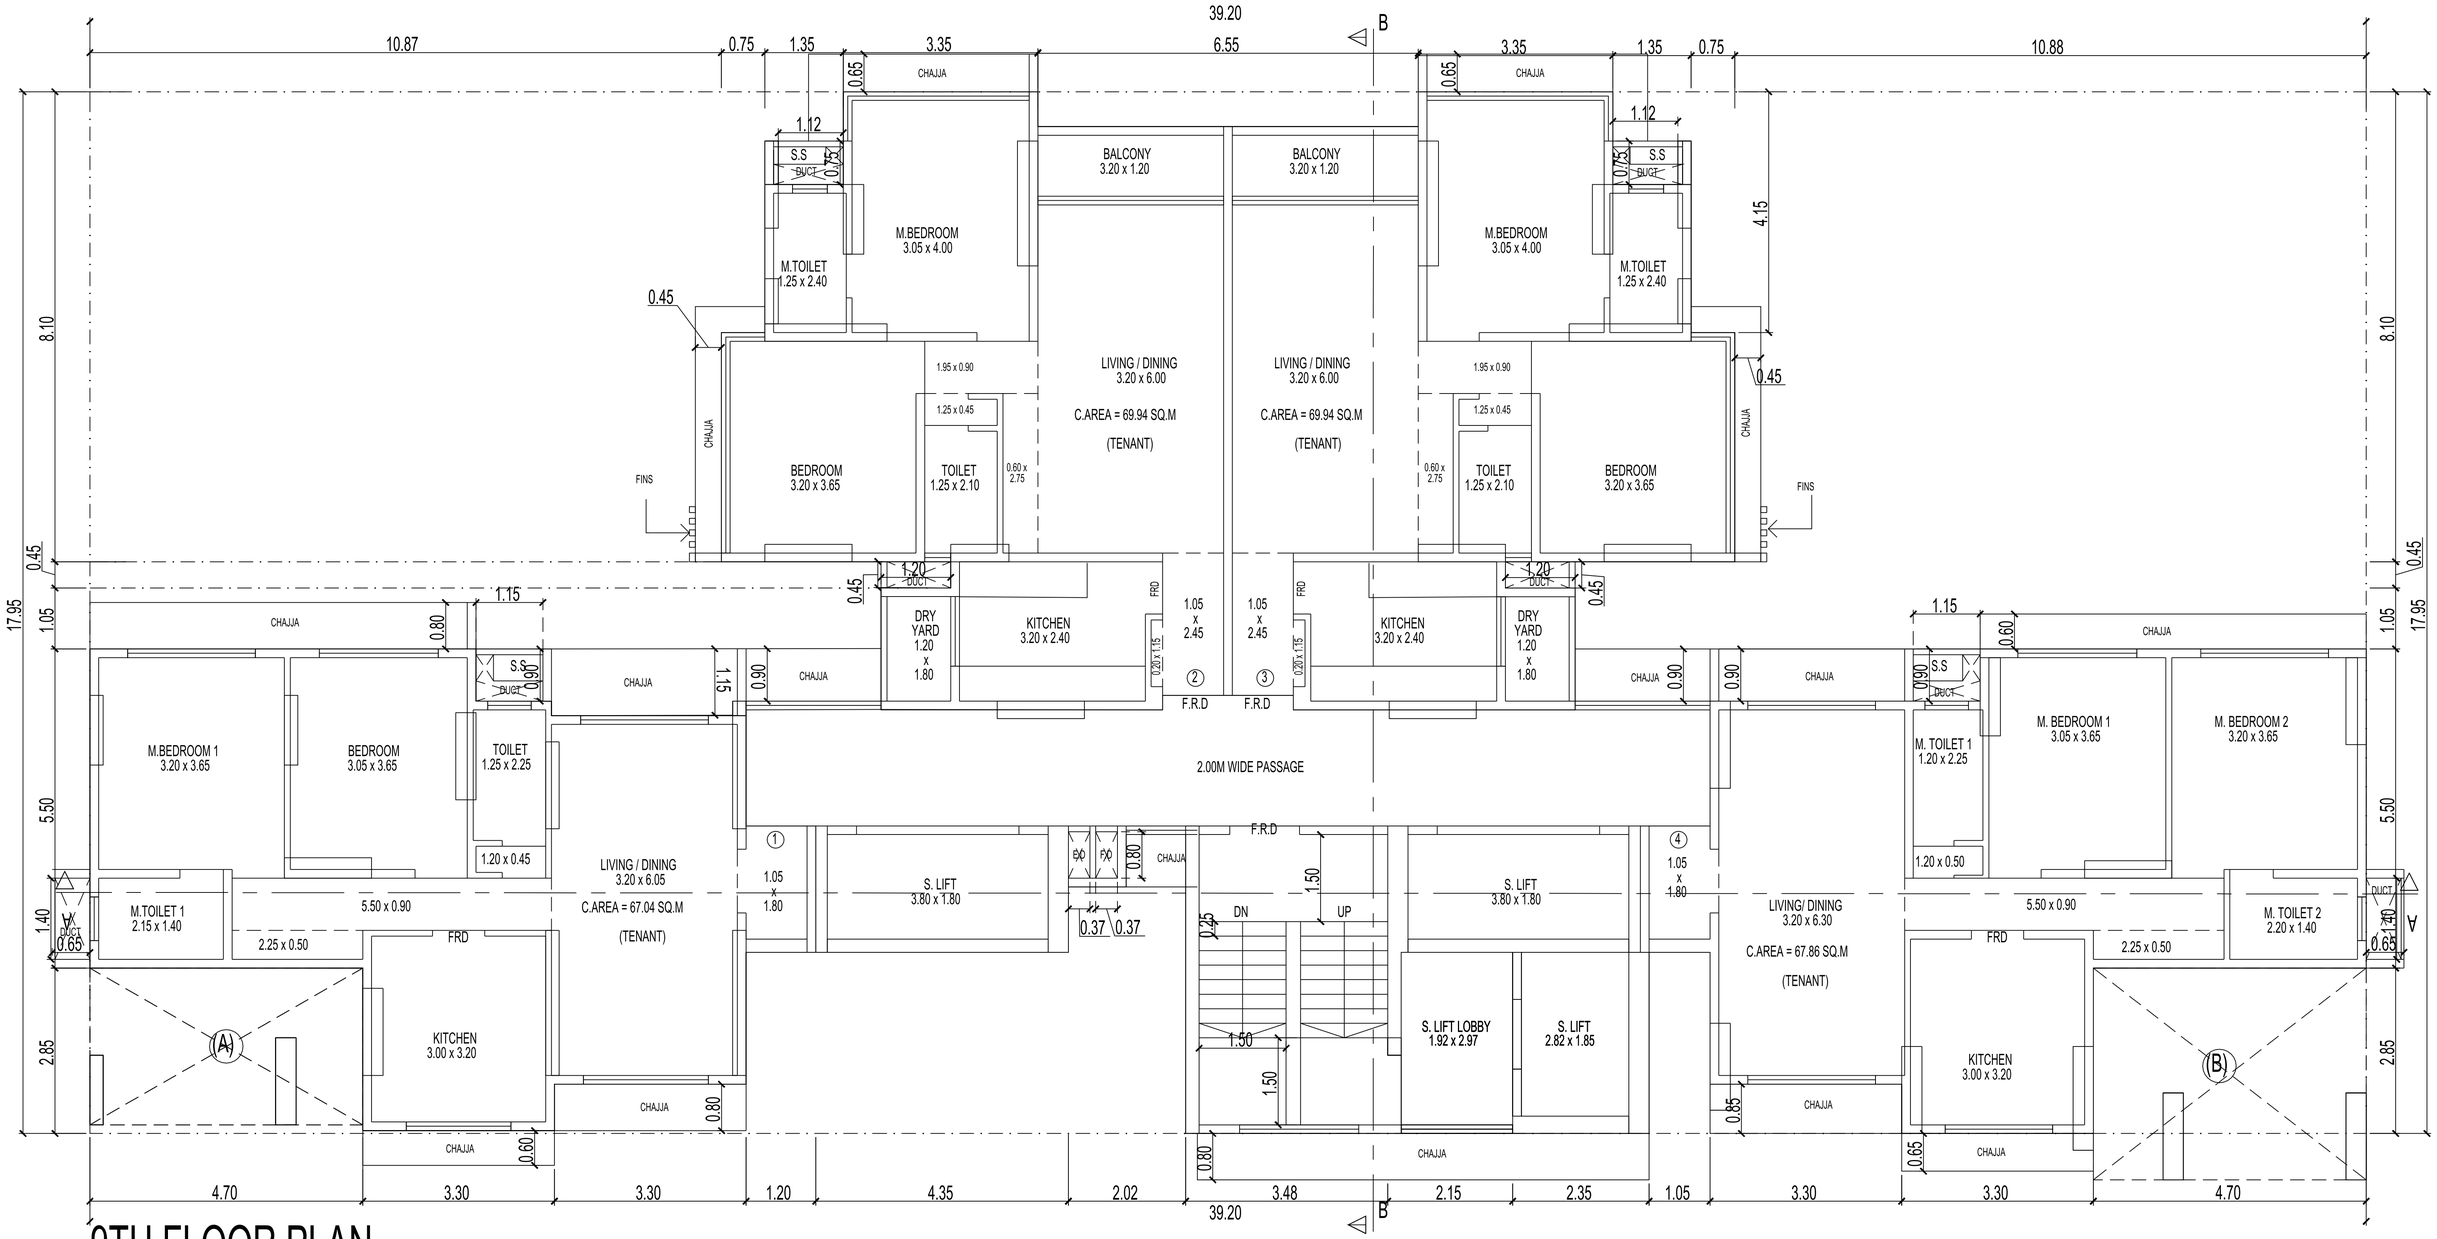


9TH FLOOR PLAN

SCALE:-1:100

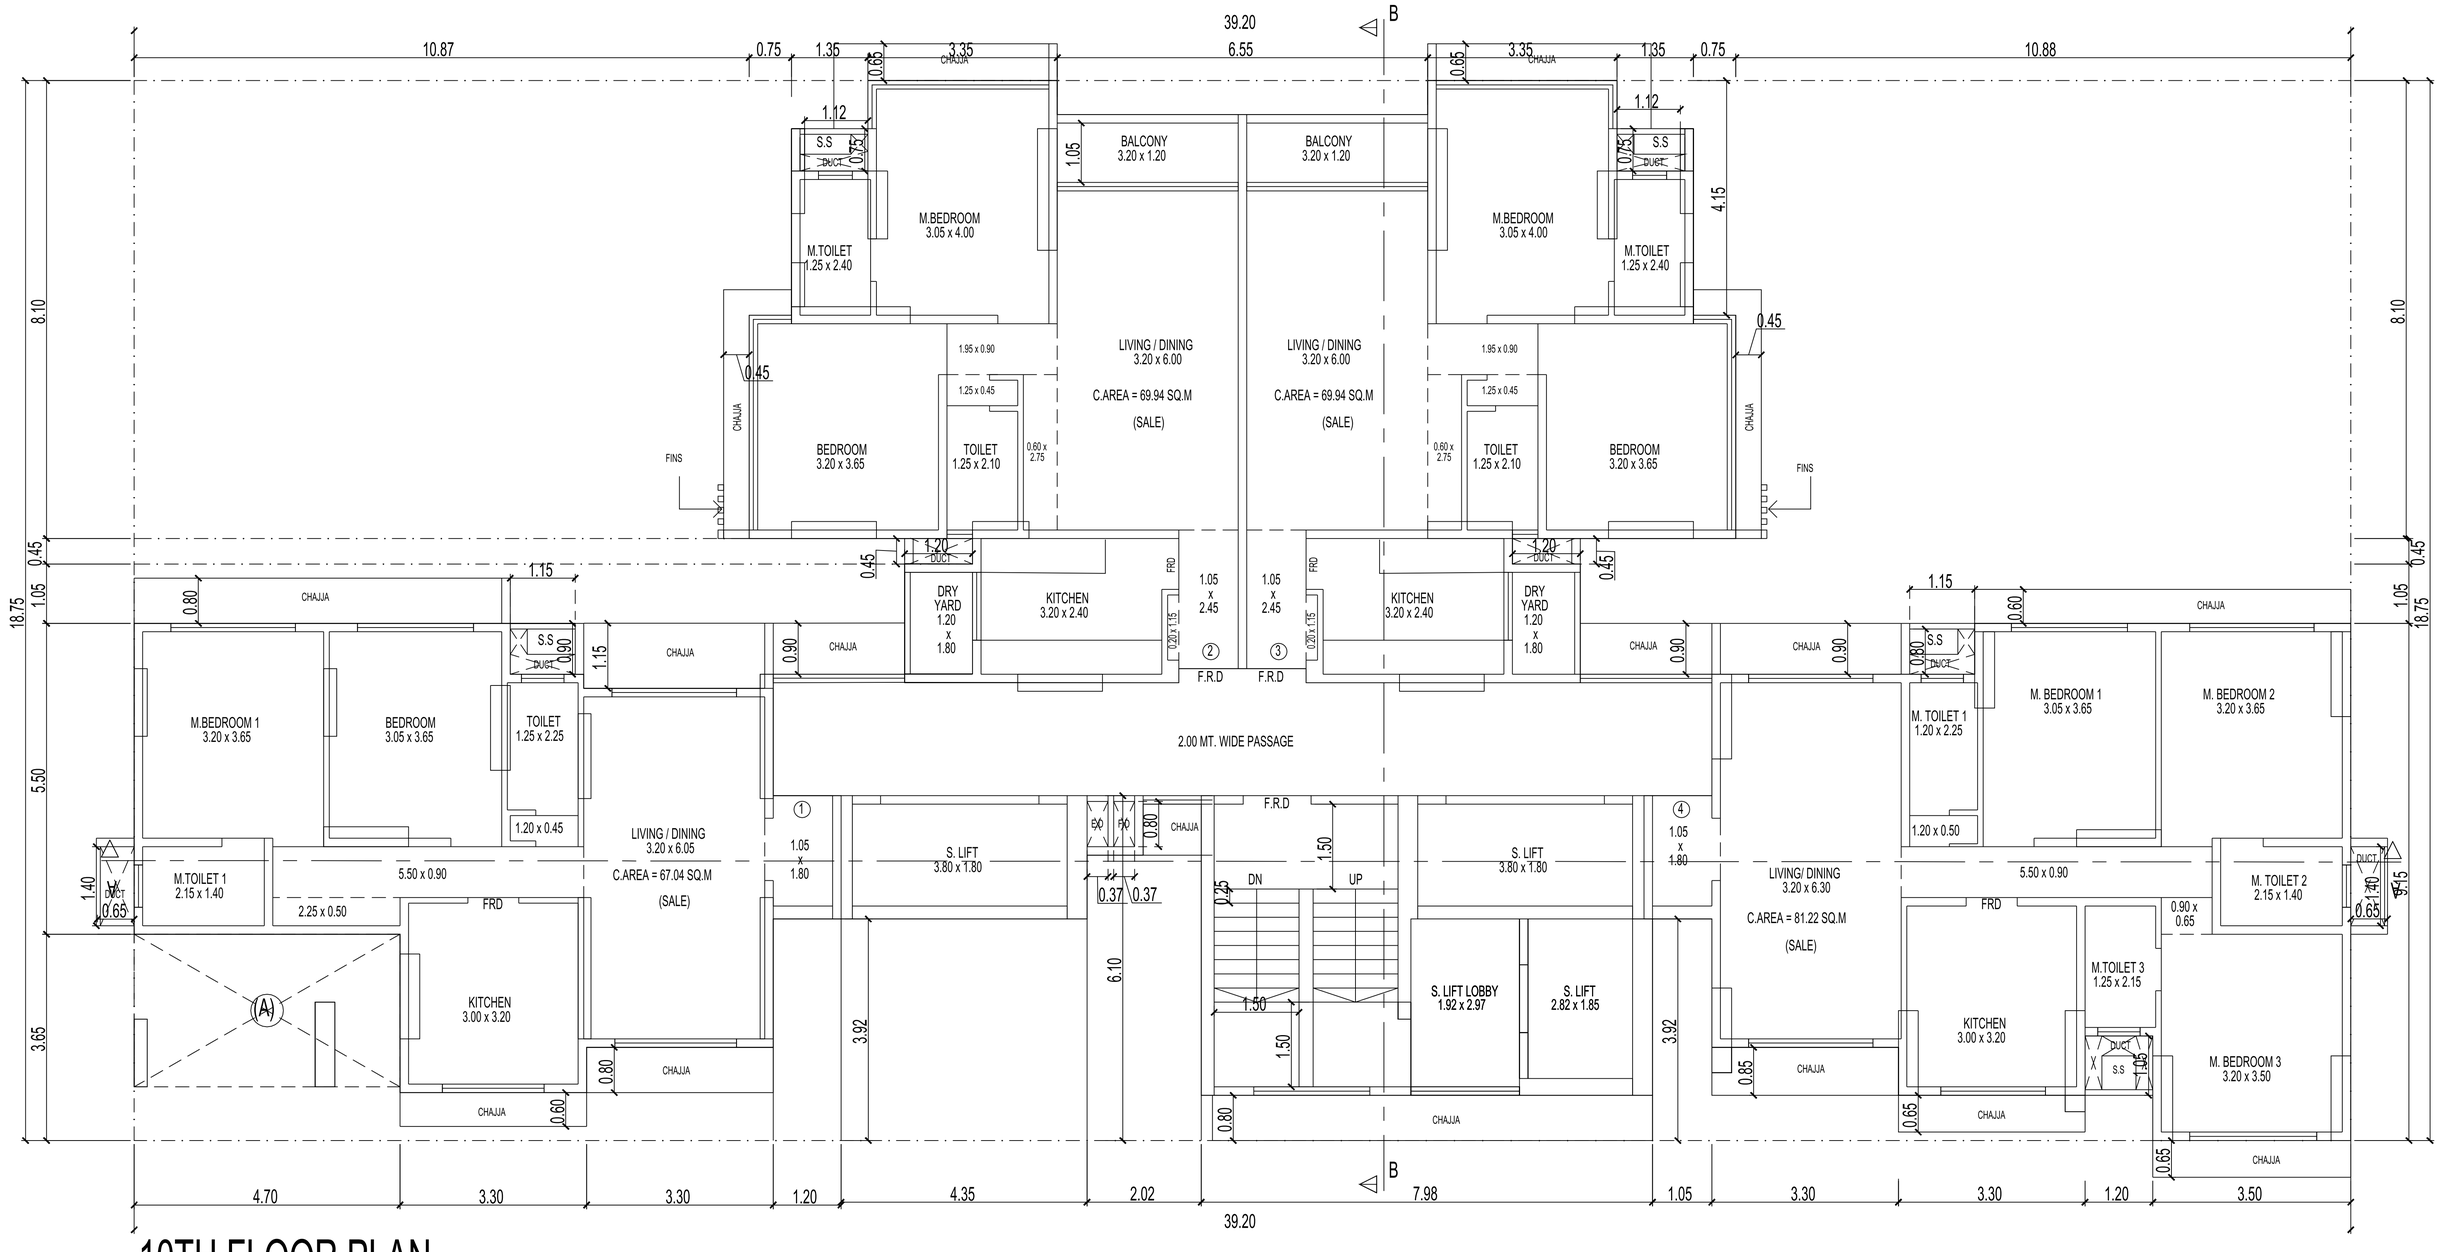


10TH FLOOR PLAN

SCALE:-1:100

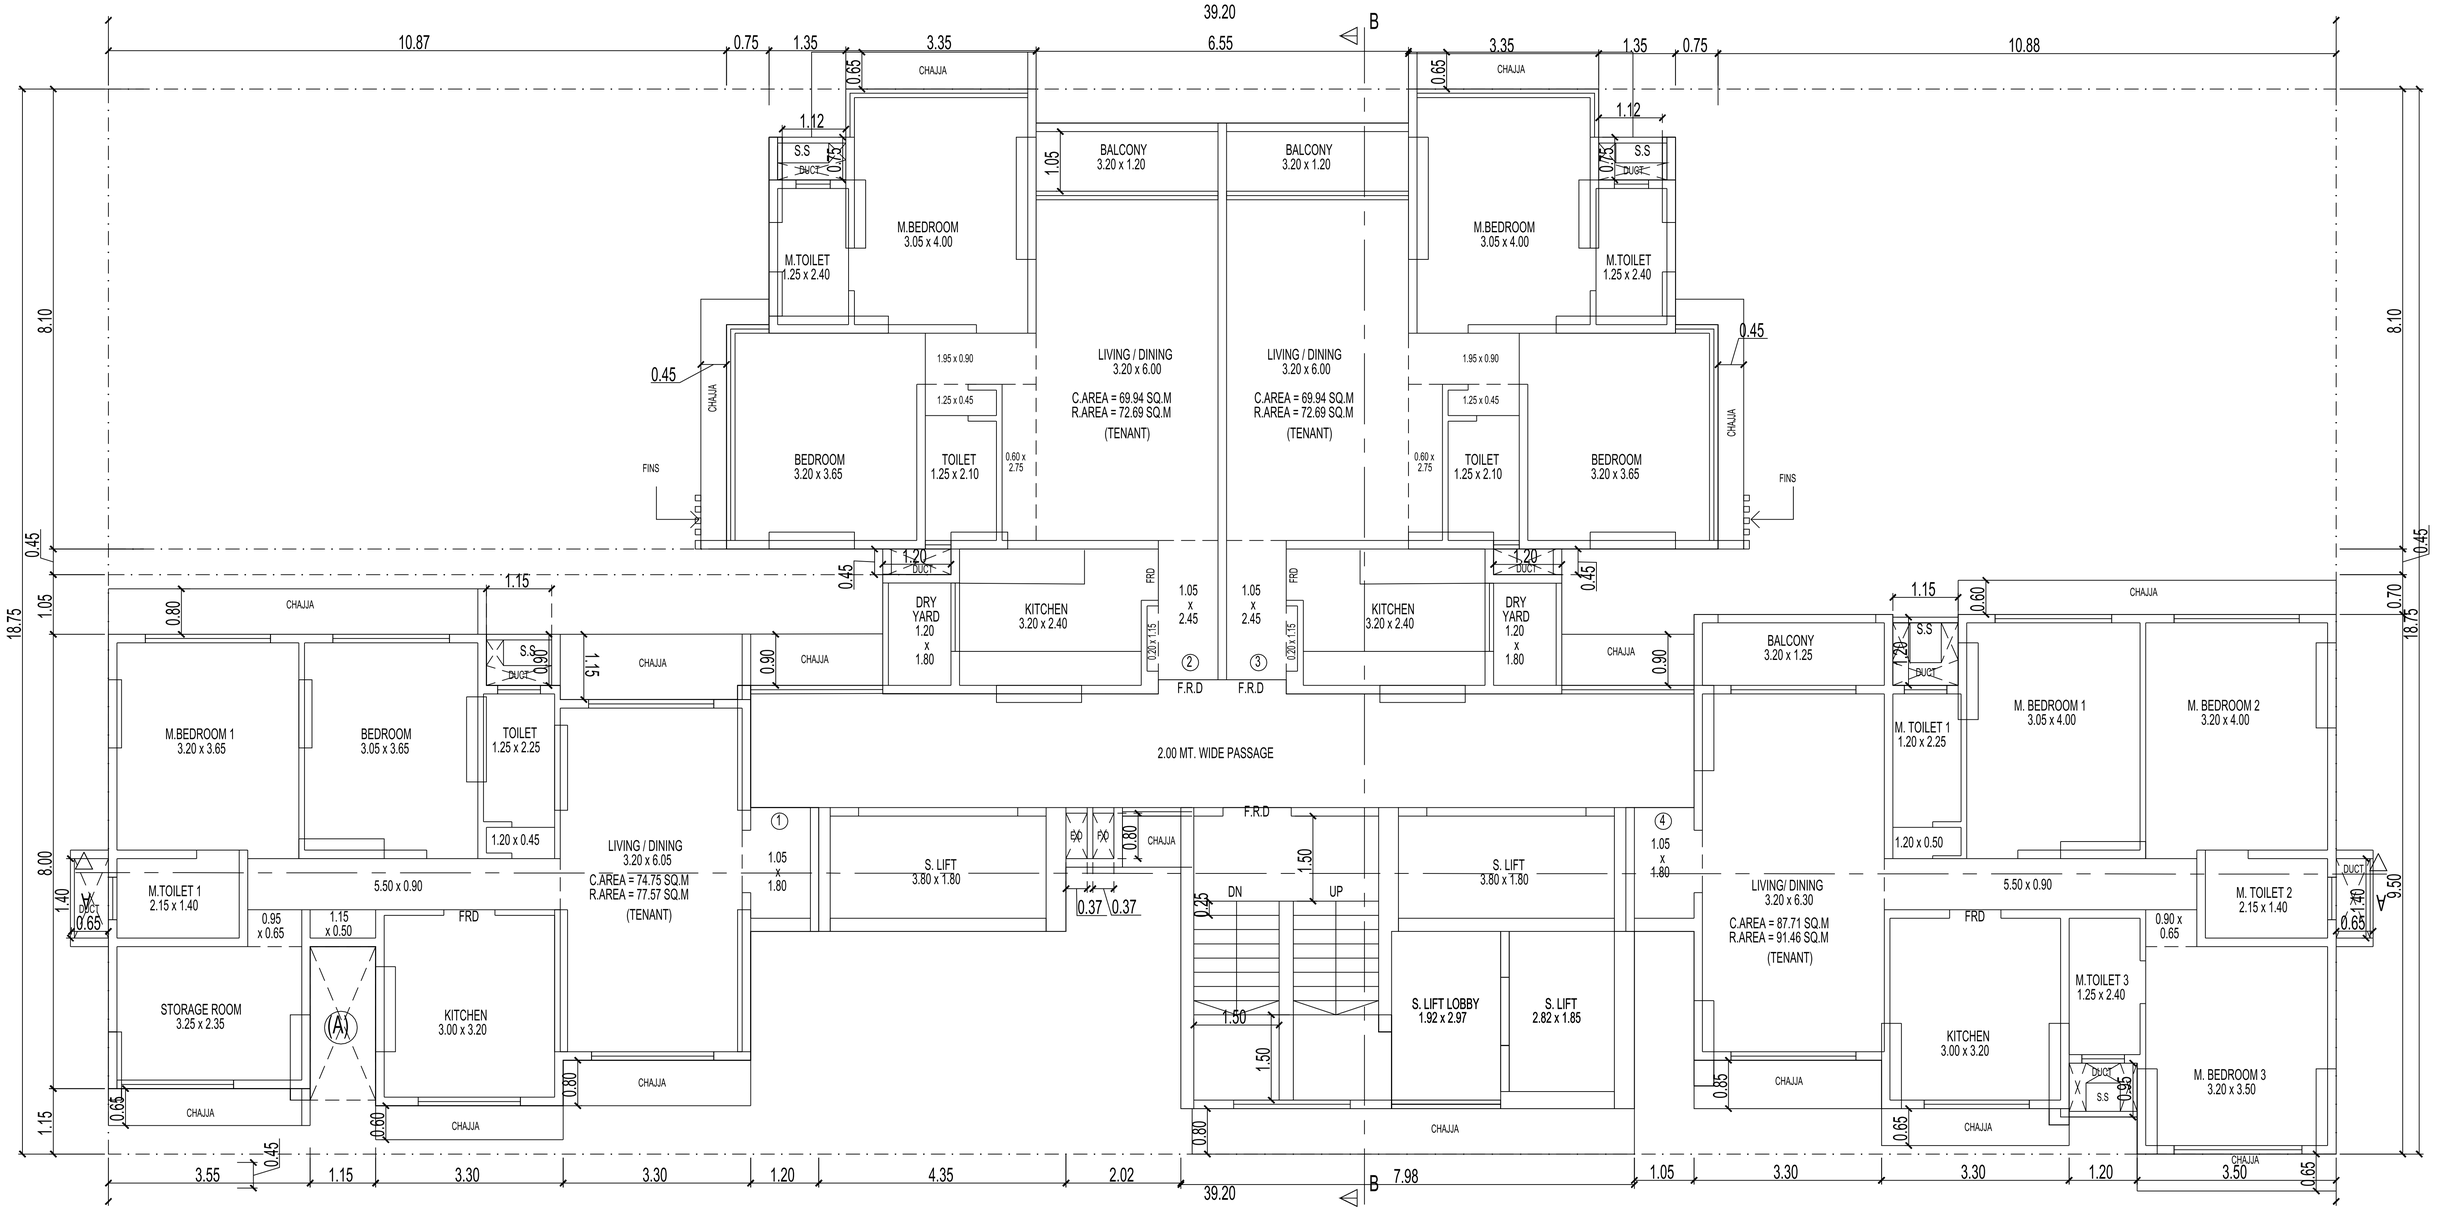

39.20
B
10.87
0.75
1.35
3.35
6.55
3.35
1.35
0.75
10.88
CHAJJA
0.65
1.12
S.S
DUCT
0.75
BALCONY
3.20 x 1.20
1.05
M.BEDROOM
3.05 x 4.00
M.TOILET
1.25 x 2.40
0.45
CHAJJA
FINS
1.95 x 0.90
1.25 x 0.45
LIVING / DINING
3.20 x 6.00
C.AREA = 69.94 SQ.M
R.AREA = 72.69 SQ.M
(TENANT)
BEDROOM
3.20 x 3.65
TOILET
1.25 x 2.10
0.60 x
2.75
8.10
18.75
1.20
DUCT
DRY
YARD
1.20
x
1.80
KITCHEN
3.20 x 2.40
FRD
1.05
x
2.45
0.20 x 1.15
2
3
F.R.D
2.00 MT. WIDE PASSAGE
1.15
0.80
0.90
1.15
M.BEDROOM 1
3.20 x 3.65
BEDROOM
3.05 x 3.65
TOILET
1.25 x 2.25
1.20 x 0.45
LIVING / DINING
3.20 x 6.05
C.AREA = 74.75 SQ.M
R.AREA = 77.57 SQ.M
(TENANT)
1
1.05
x
1.80
S. LIFT
3.80 x 1.80
50
50
0.80
0.37
0.37
1.50
0.25
DN
UP
1.50
1.50
S. LIFT LOBBY
1.92 x 2.97
S. LIFT
2.82 x 1.85
4
1.05
x
1.80
BALCONY
3.20 x 1.25
1.28
M. BEDROOM 1
3.05 x 4.00
M. BEDROOM 2
3.20 x 4.00
M. TOILET 1
1.20 x 2.25
1.20 x 0.50
LIVING/ DINING
3.20 x 6.30
C.AREA = 87.71 SQ.M
R.AREA = 91.46 SQ.M
(TENANT)
M. TOILET 2
2.15 x 1.40
0.70
9.50
M.TOILET 1
2.15 x 1.40
5.50 x 0.90
0.95
x 0.65
1.15
x 0.50
FRD
STORAGE ROOM
3.25 x 2.35
A
KITCHEN
3.00 x 3.20
0.90 x
0.65
M.TOILET 3
1.25 x 2.40
M. BEDROOM 3
3.20 x 3.50
1.40
1.15
3.55
1.15
3.30
3.30
1.20
4.35
2.02
7.98
1.05
3.30
3.30
1.20
3.50
0.65
39.20

SCALE:-1:100

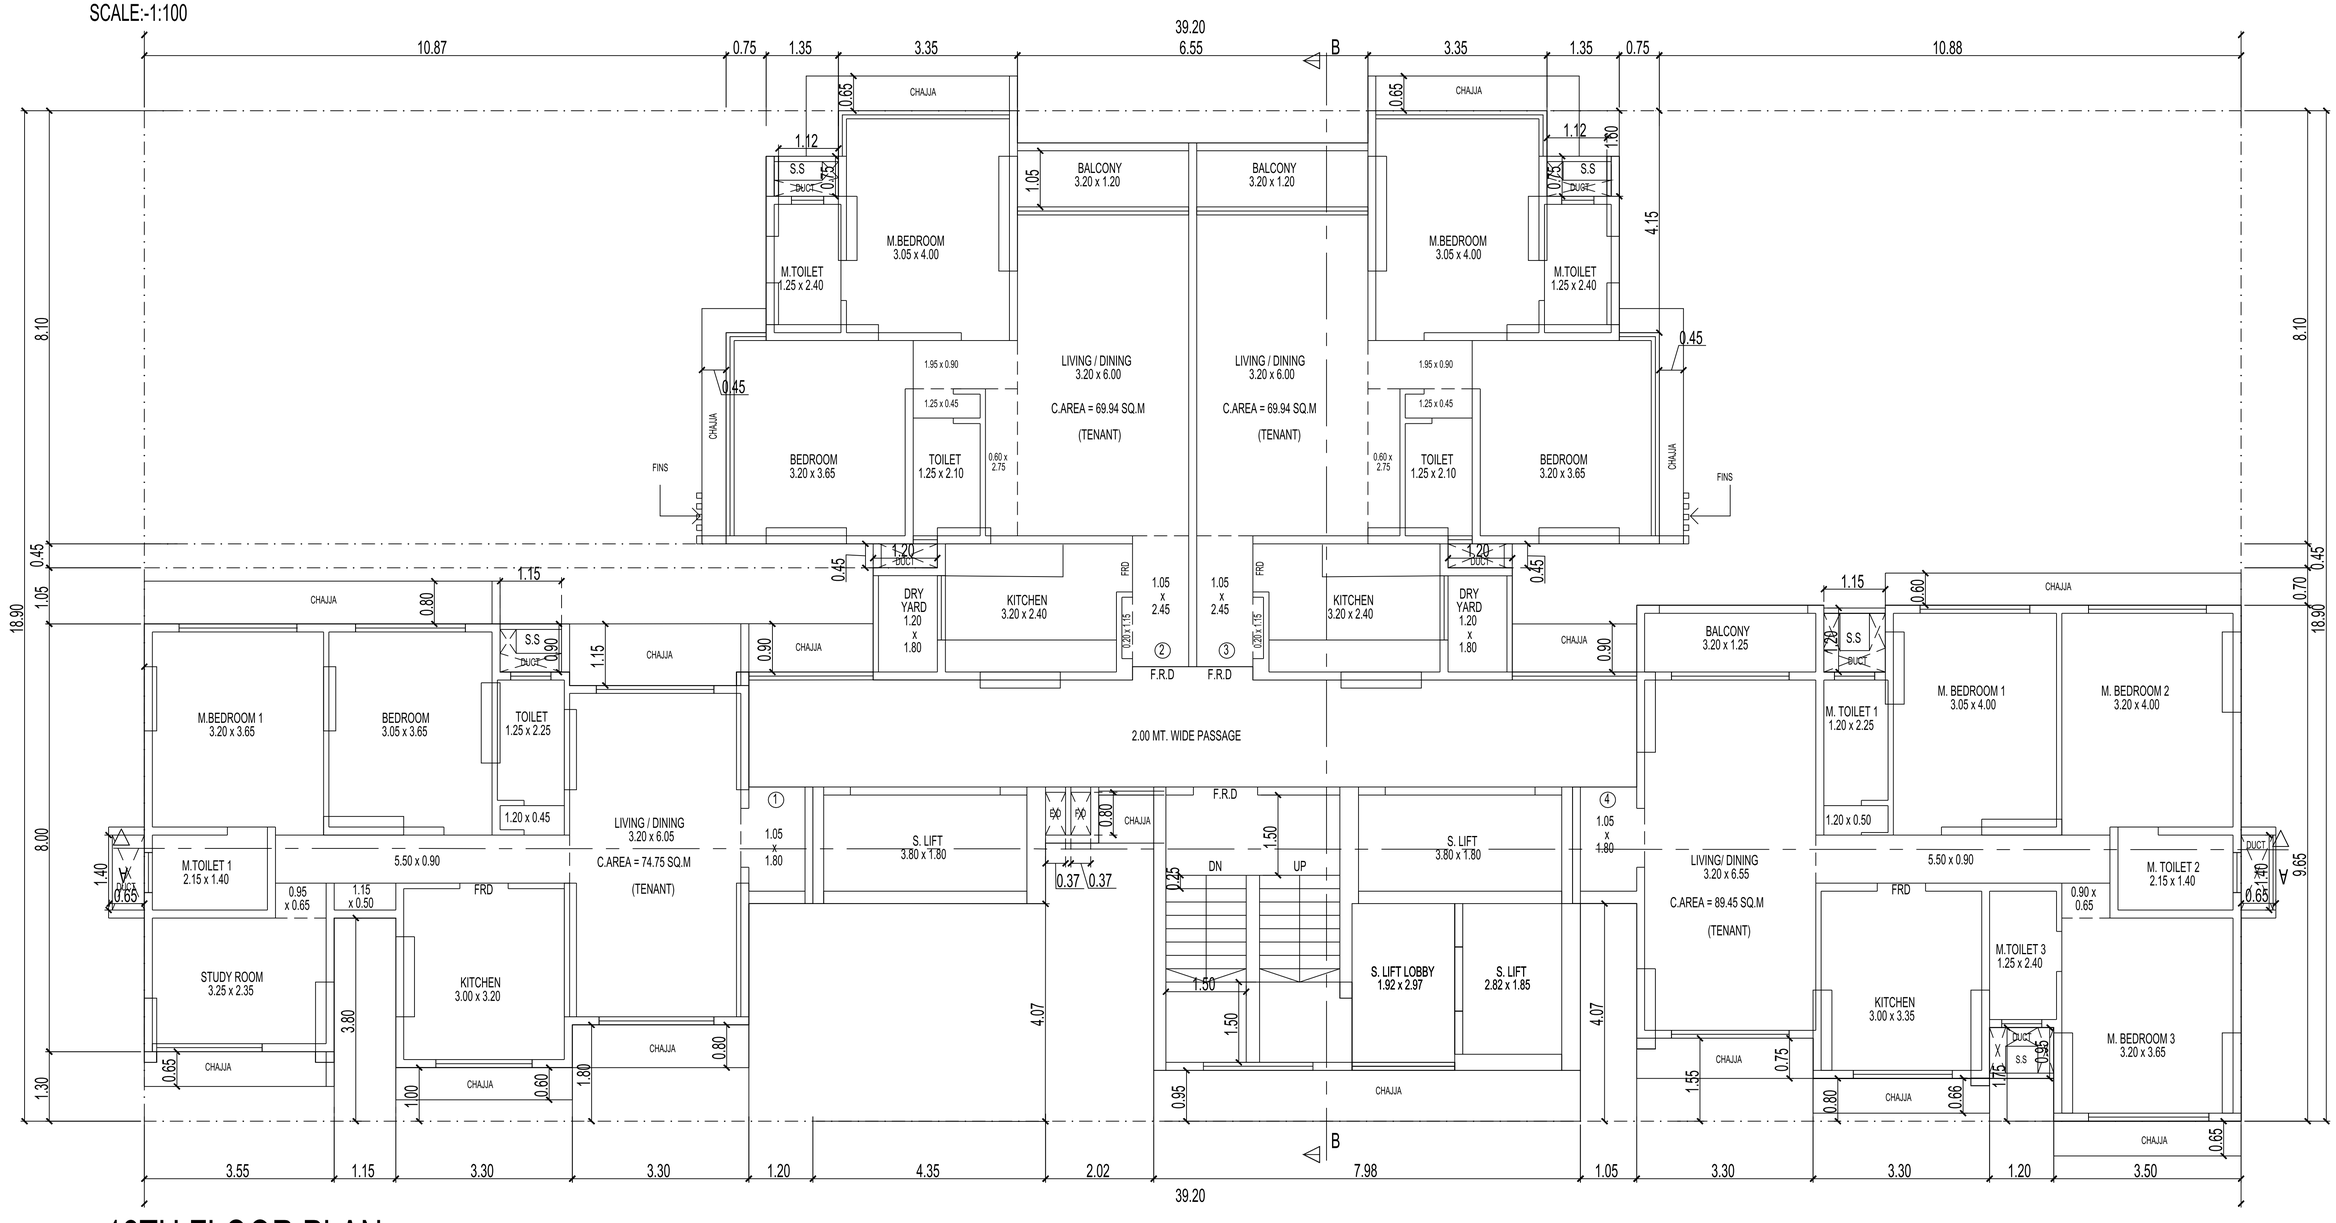


12TH FLOOR PLAN

SCALE:-1:100

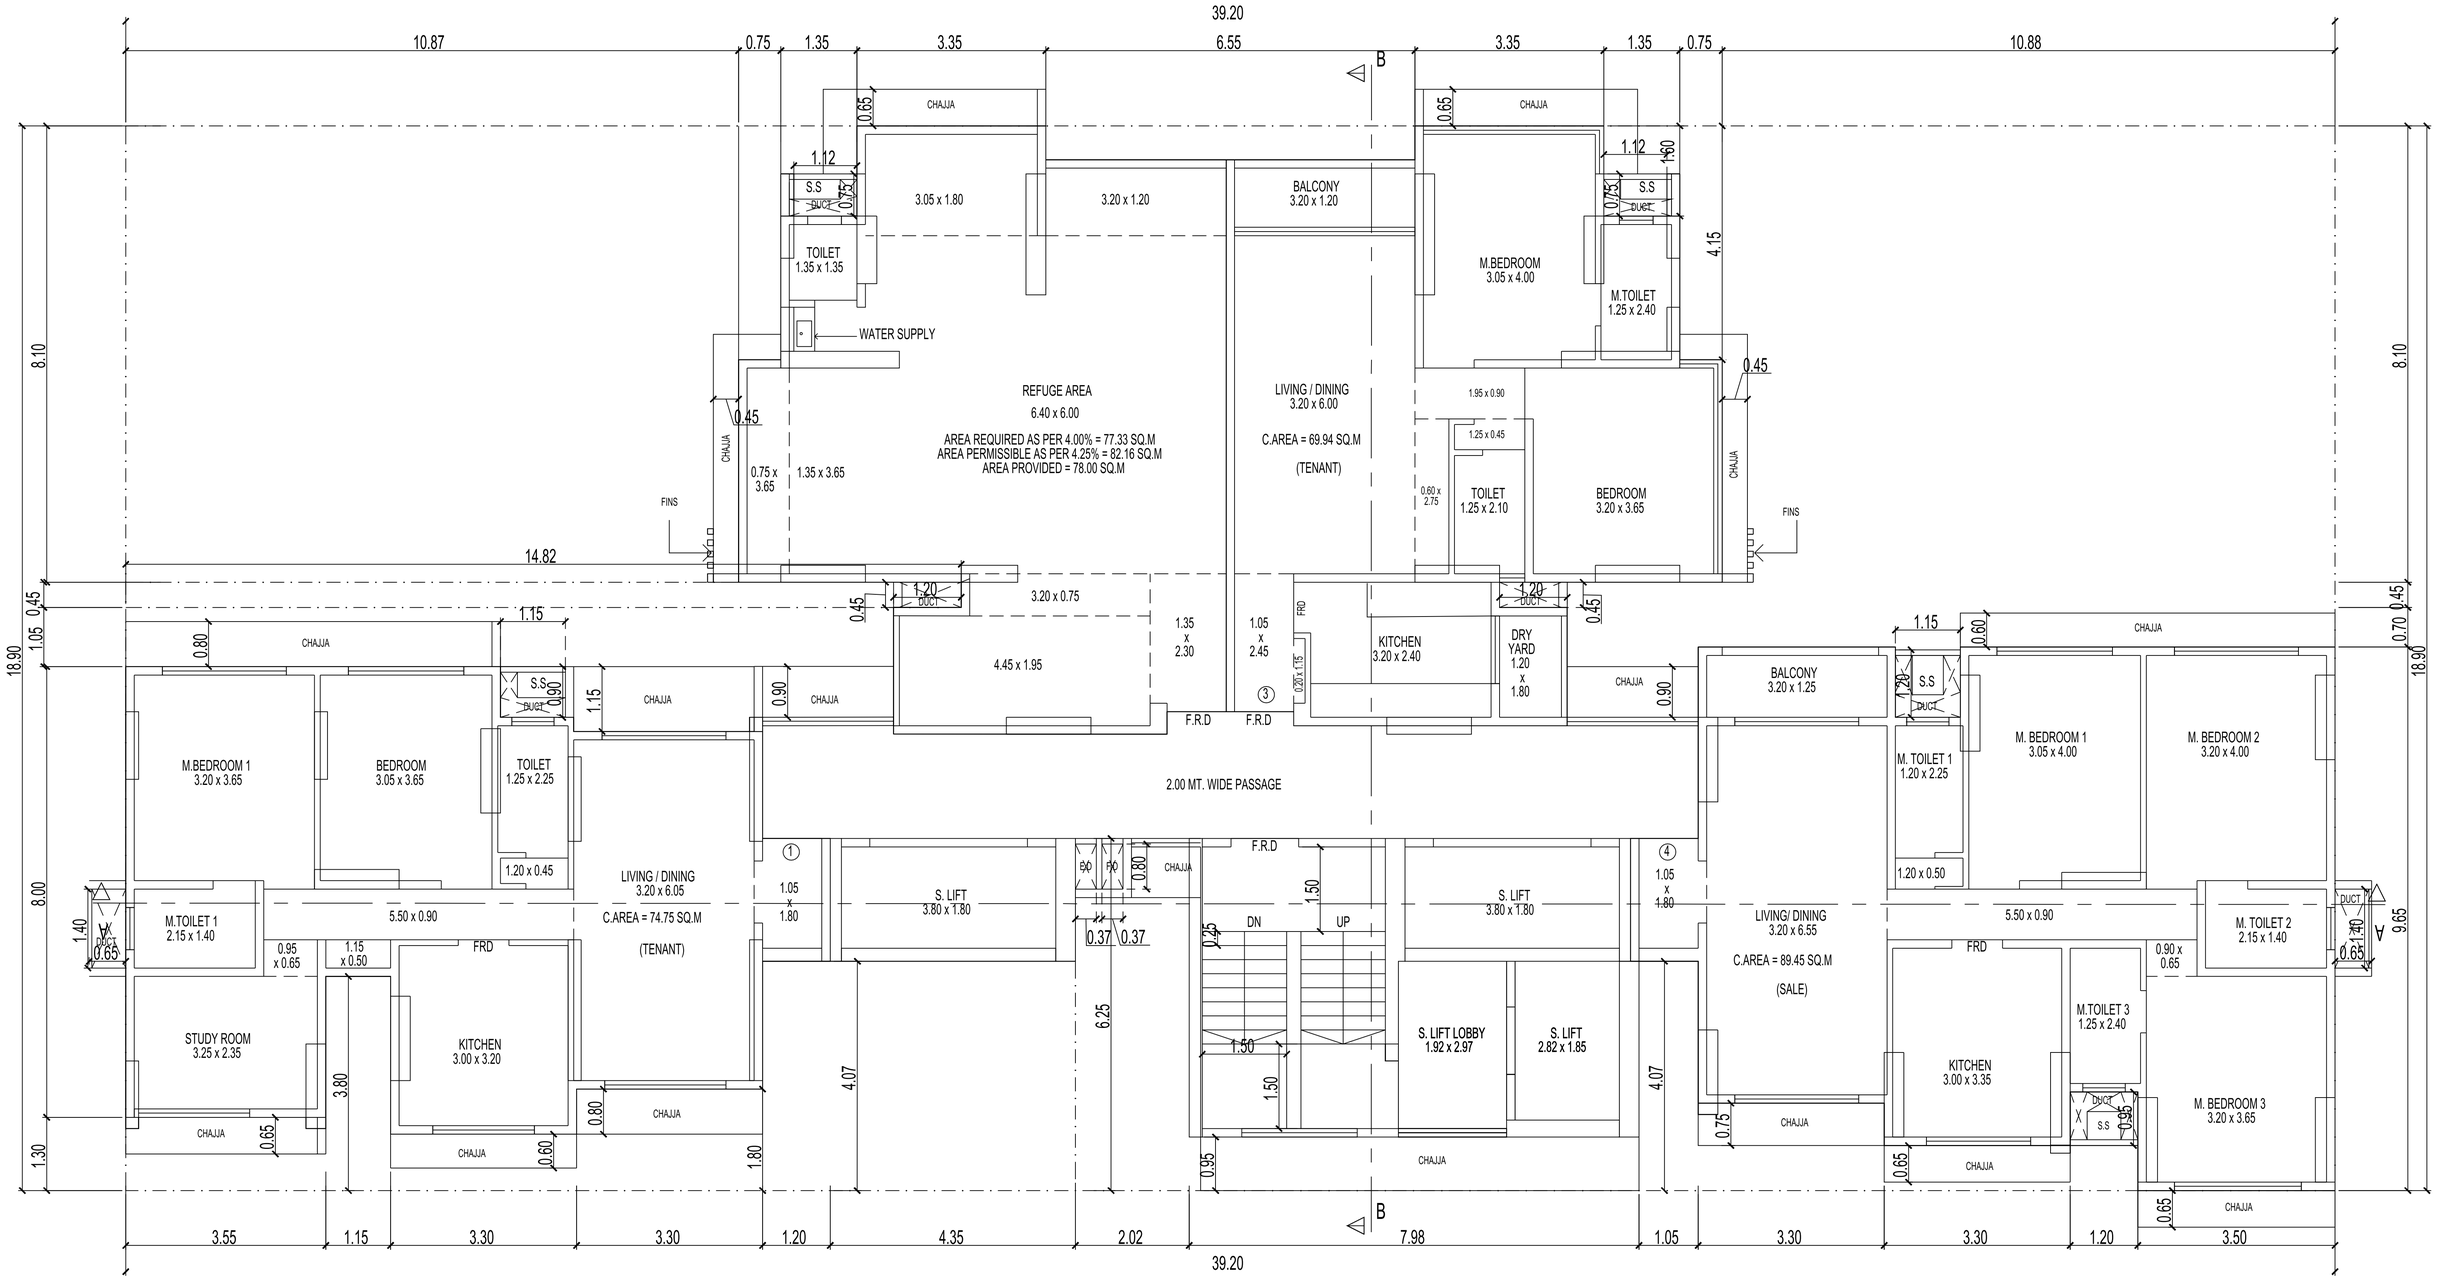


13TH FLOOR PLAN

SCALE:-1:100

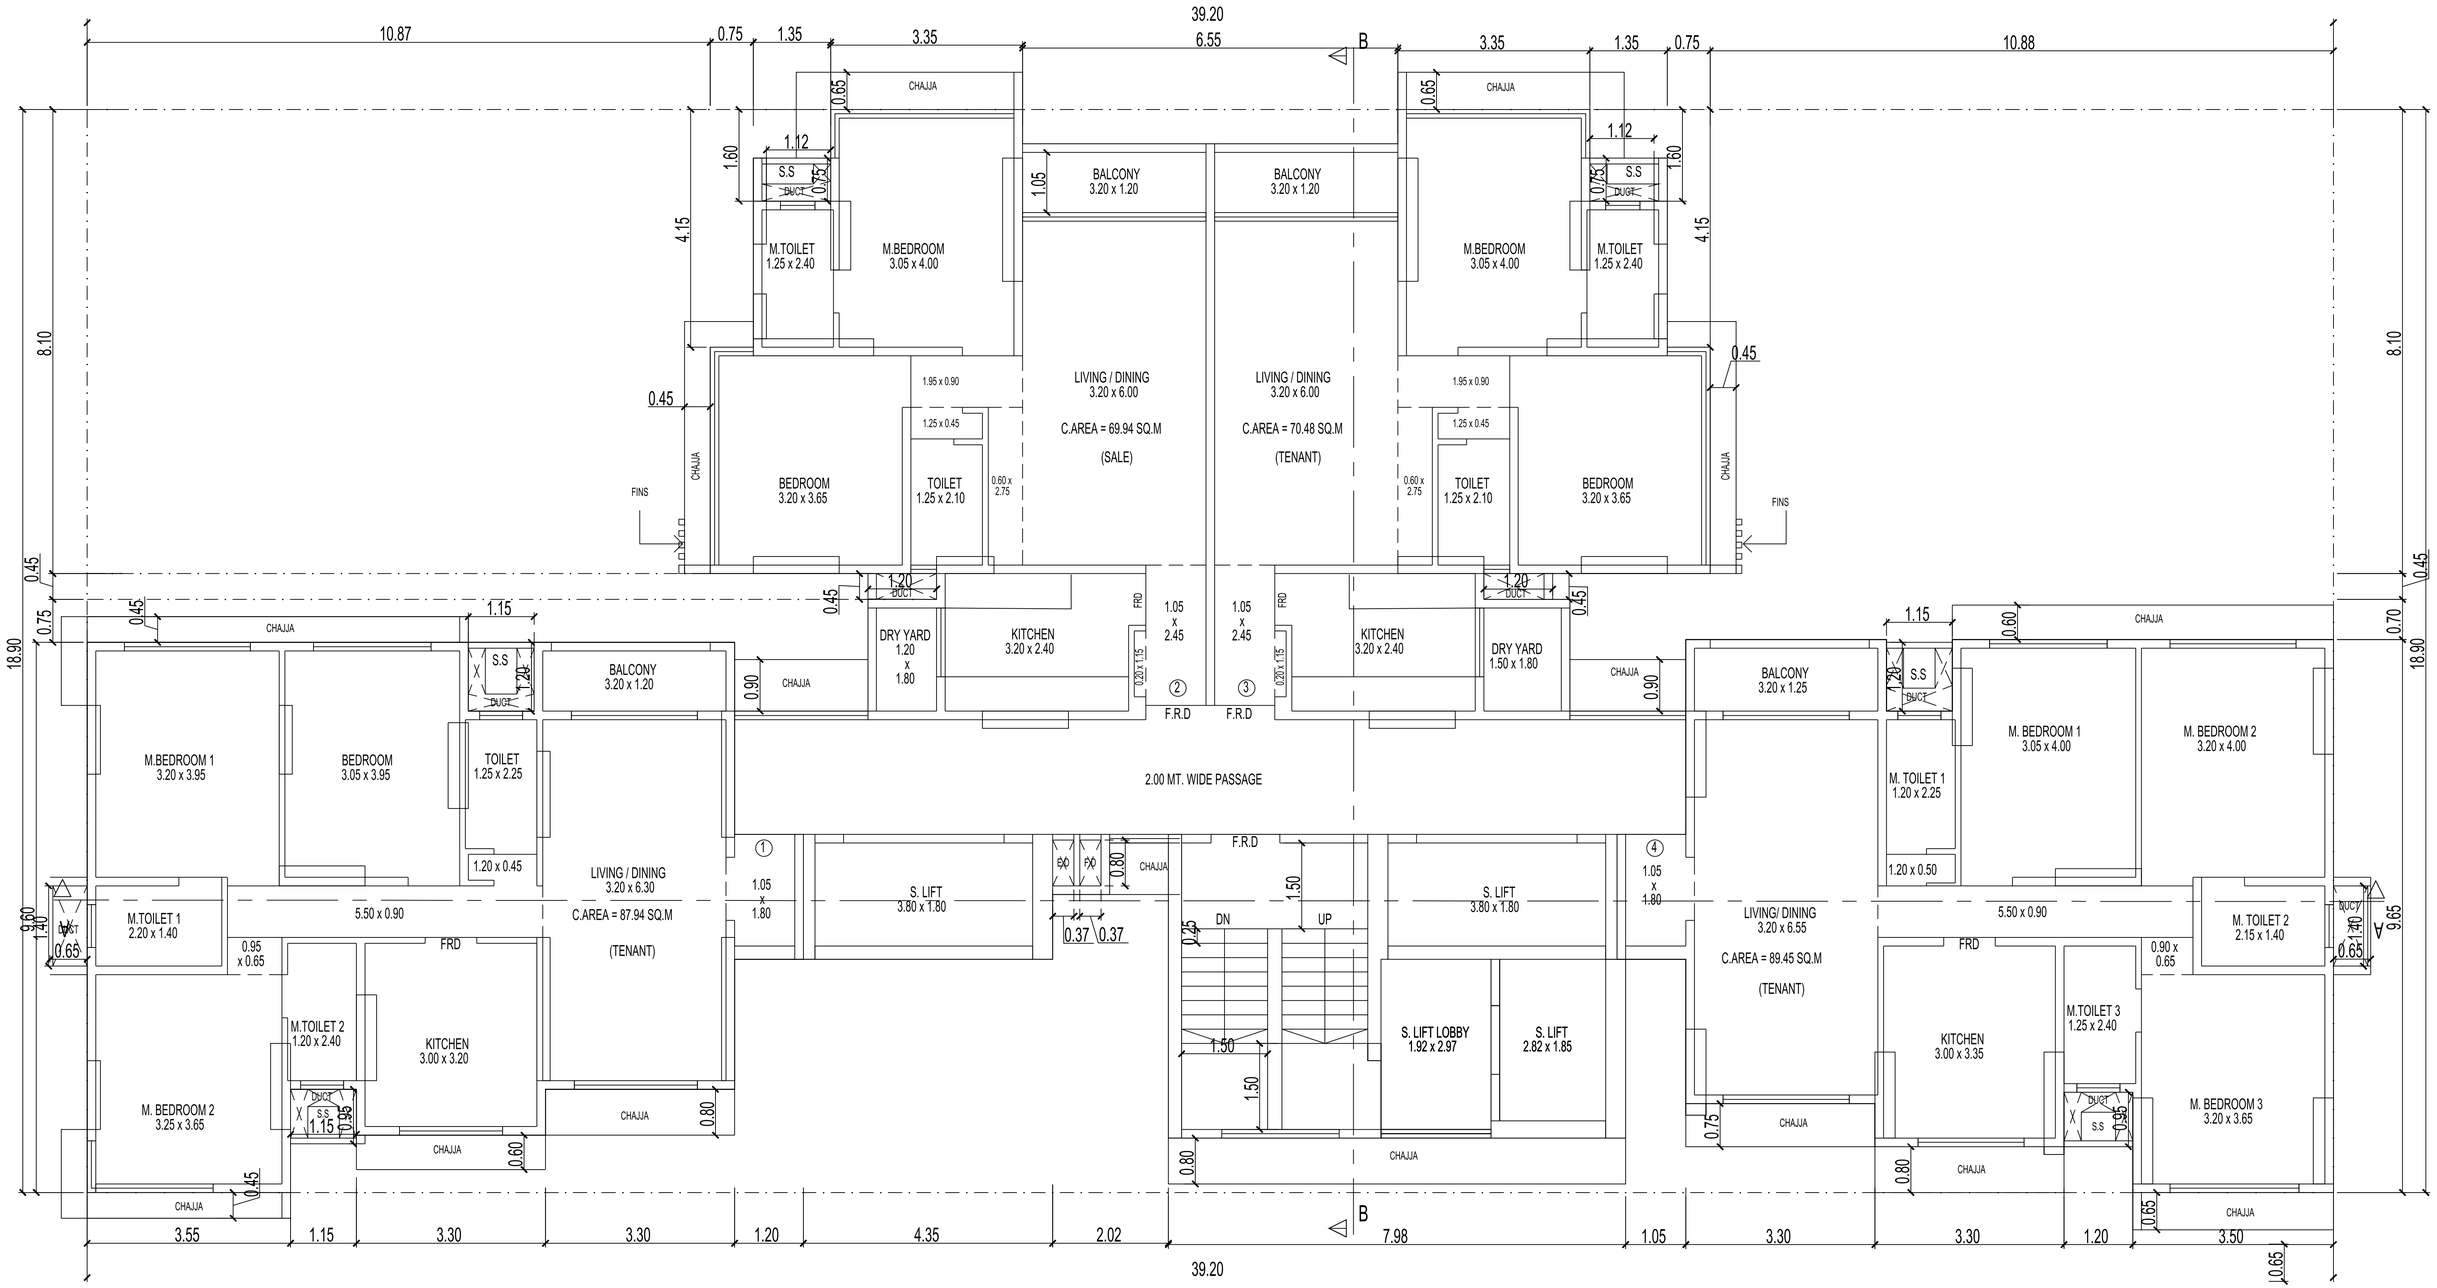


14TH FLOOR PLAN

SCALE:-1:100

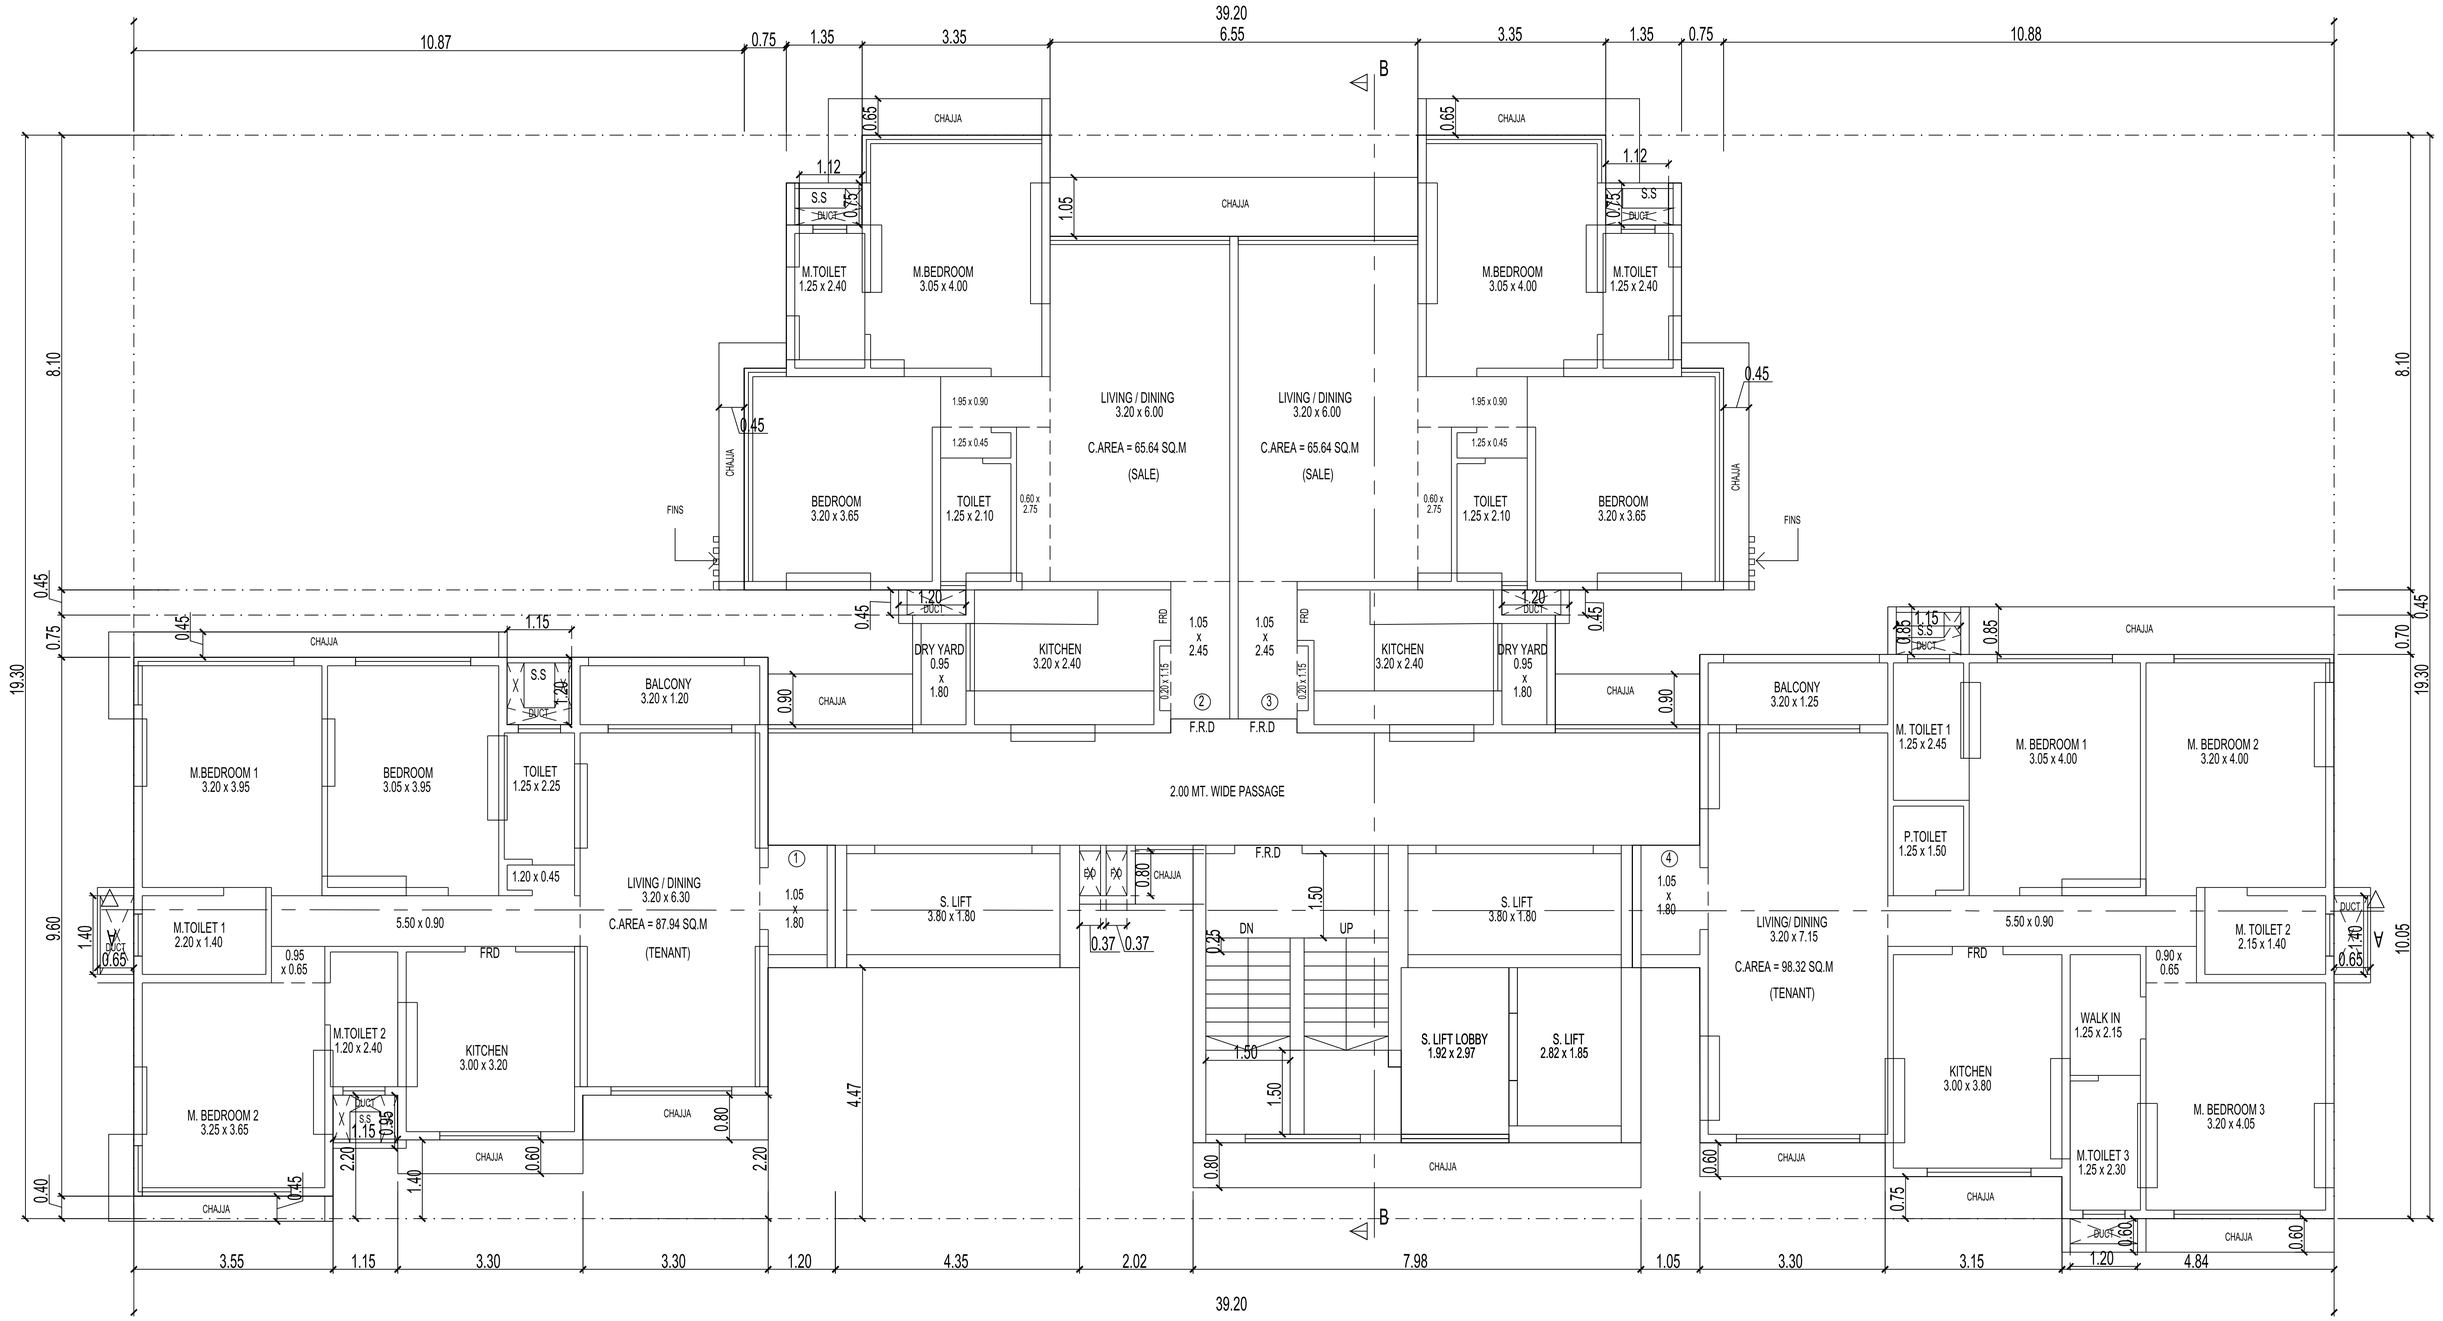

15TH FLOOR PLAN

SCALE:-1:100

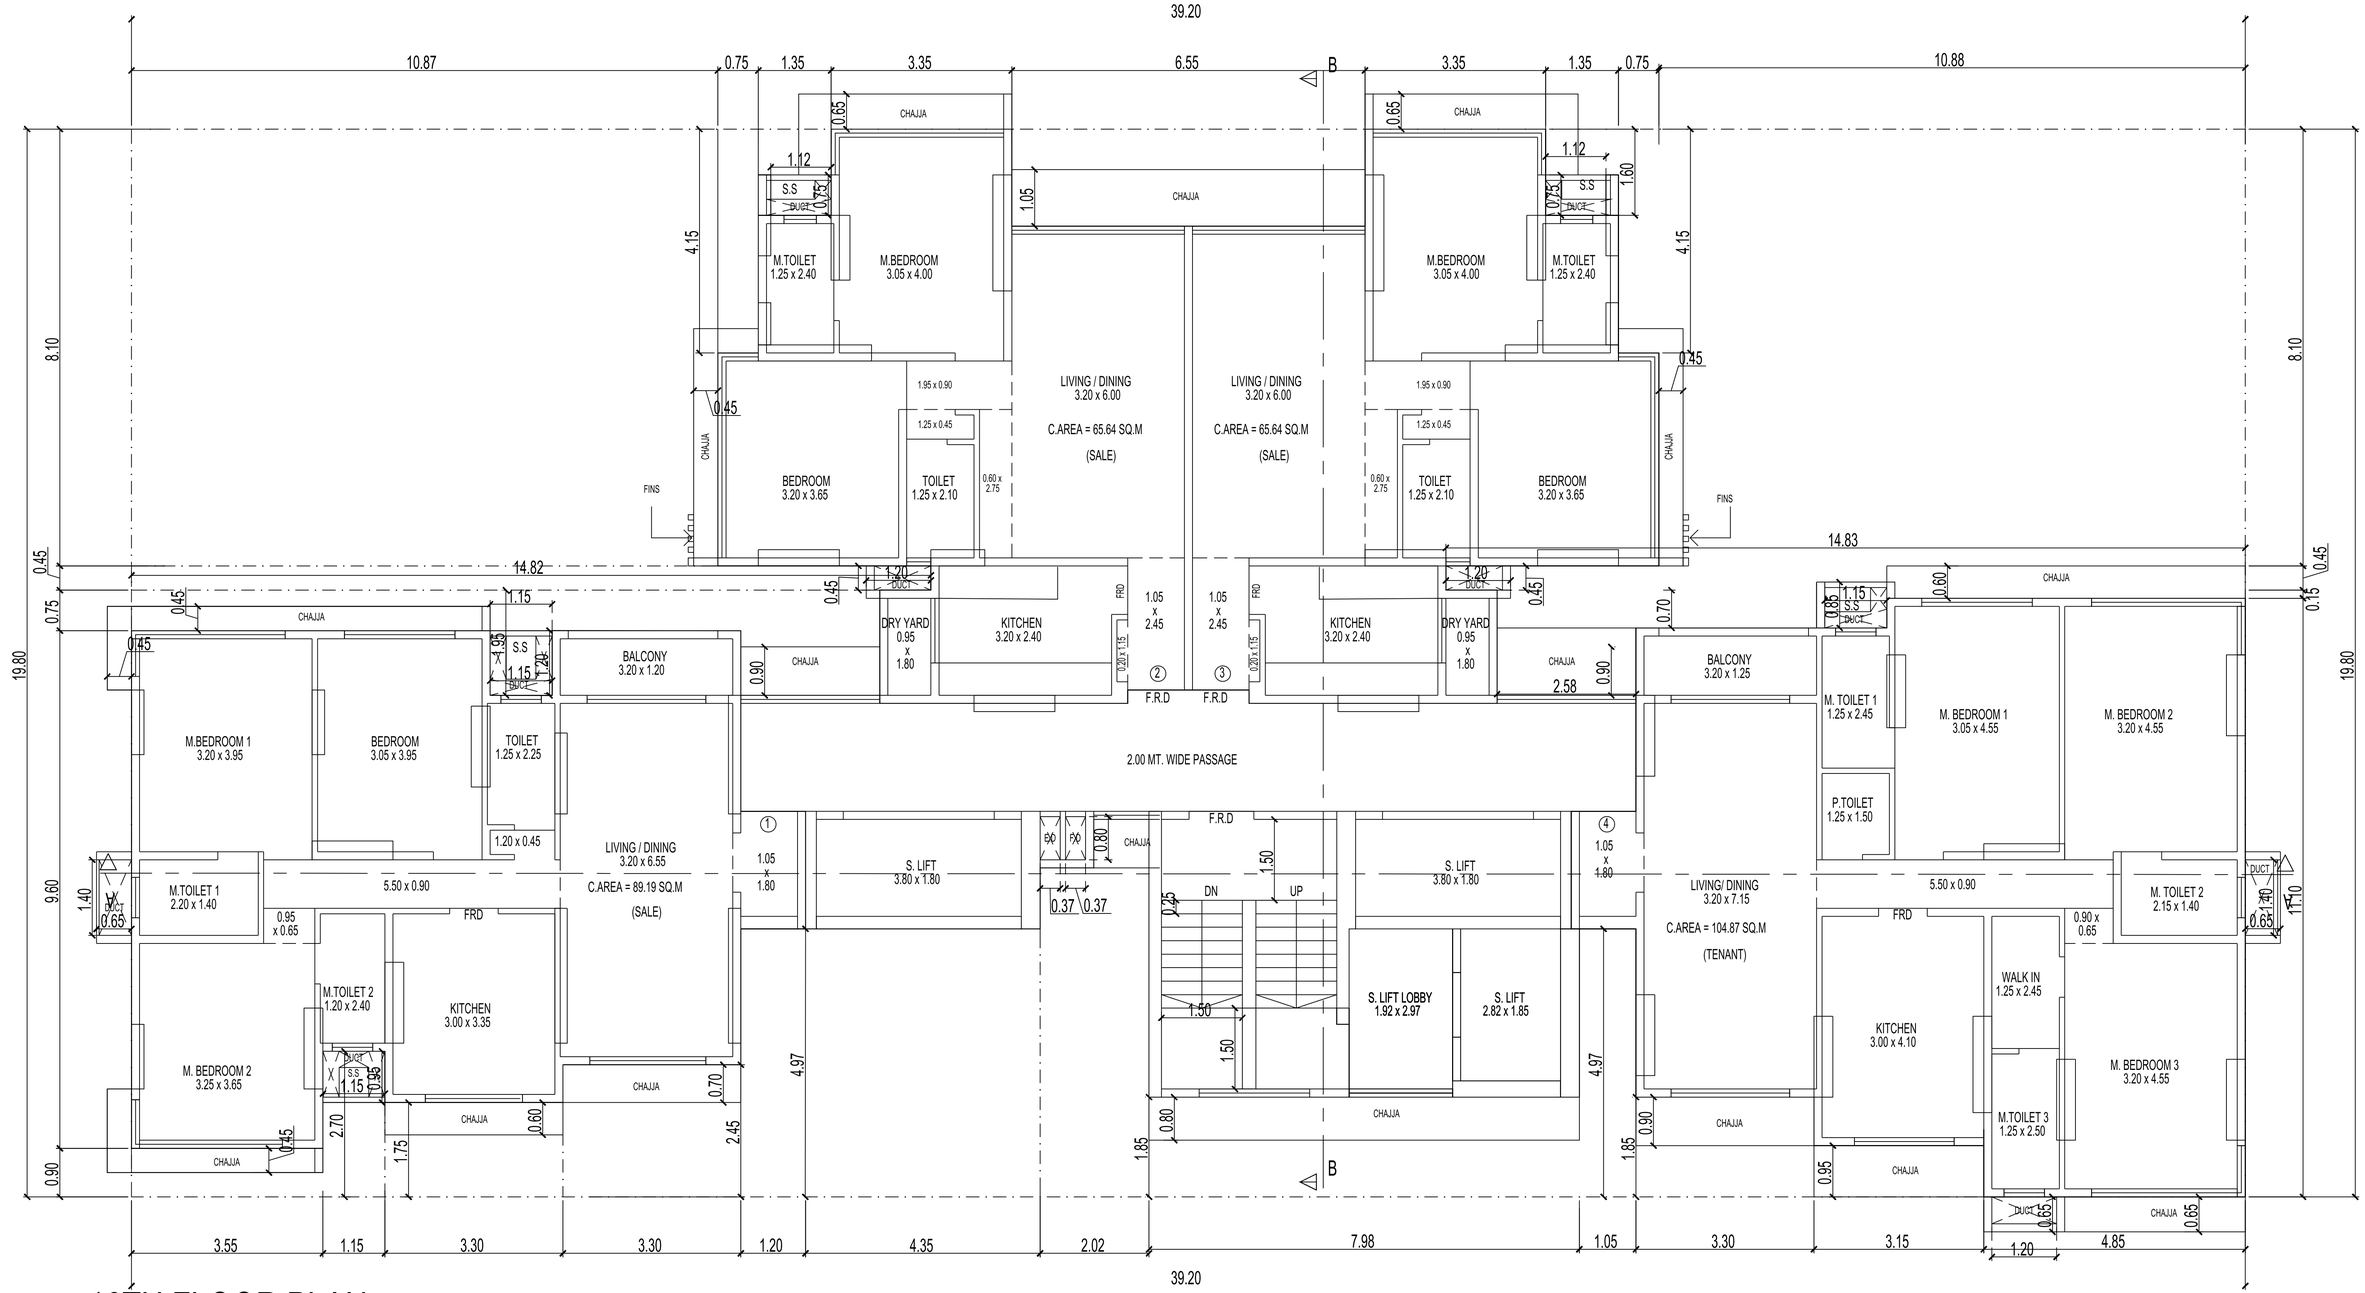

16TH FLOOR PLAN

SCALE:-1:100

17TH FLOOR PLAN

18TH FLOOR PLAN

SCALE:-1:100

39.20

B

DUCT

DUCT

18TH FLOOR BUILDING LINE

ELEVATIONAL TREATMENT @4.50M FROM TERRACE FLOOR LVL WITH 60% OPENING

ELEVATIONAL TREATMENT @4.50M FROM TERRACE FLOOR LVL WITH 60% OPENING

TERRACE GARDEN OPEN TO SKY

9.80

11.15

DUCT

DUCT

DUCT

CHAJJA

0.45

20.45

11.15 X S.S 1.20

DUCT

0.90

ROOF OVER BALCONY

F.R.D

CHAJJA

M.BEDROOM 1
3.20 x 3.95

BEDROOM
3.05 x 3.95

TOILET
1.25 x 2.25

1.20 x 0.45

2.00 MT. WIDE PASSAGE

2.00

ELEVATIONAL TREATMENT @4.50M FROM TERRACE FLOOR LVL WITH 60% OPENING

9.60

1.40

DUCT

0.65

M.TOILET 1
2.20 x 1.40

5.50 x 0.90

LIVING / DINING
3.20 x 6.55
C.AREA = 85.35 SQ.M
(SALE)

1.05 x 1.80

1

S. LIFT
3.80 x 1.80

FD

FD

0.37 0.37

CHAJJA

0.80

0.90

F.R.D

0.25

DN

UP

1.50

S. LIFT
3.80 x 1.80

F.R.D

DUCT

1.40

0.60

0.95 x 0.65

FRD

M.TOILET 2
1.20 x 2.40

KITCHEN
3.00 x 3.35

TERRACE GARDEN OPEN TO SKY

7.30

M. BEDROOM 2
3.25 x 3.65

DUCT X S.S 0.95

0.70

CHAJJA

1.50

1.50

S. LIFT LOBBY
1.92 x 2.97

S. LIFT
2.82 x 1.85

1.15

0.60

CHAJJA

0.80

CHAJJA

1.05

CHAJJA

0.45

B

DUCT

3.55 1.15 3.30 3.30 1.20 4.35 2.02 7.83 12.50

39.20

19TH FLOOR PLAN