
TOTAL DUCT AREA PER FL. (TYPICAL FLOOR)	=	5.49


NET BUILT UP AREA [X1 - (Y2+Y3)]	=	163.01 SQ.MT.

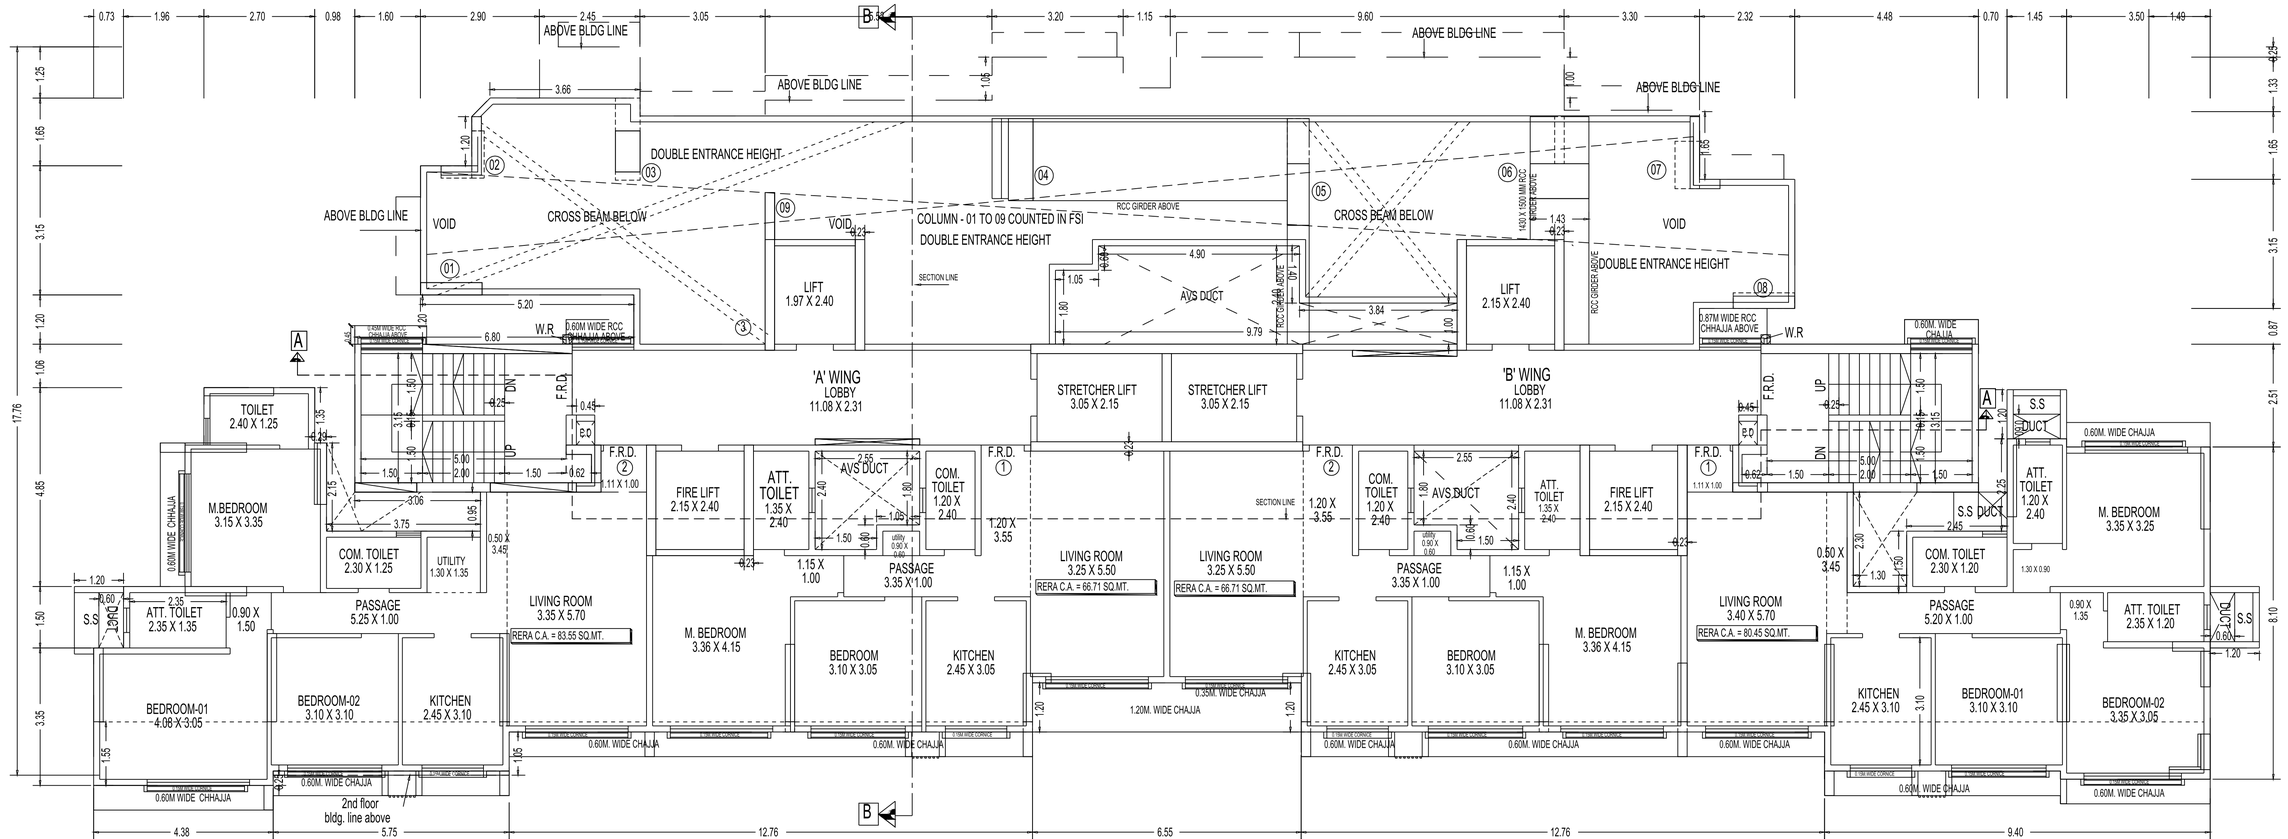

1st FLOOR PLAN


SCALE 1:100

NET BUILT UP AREA
[X1 - (Y2+Y3)]

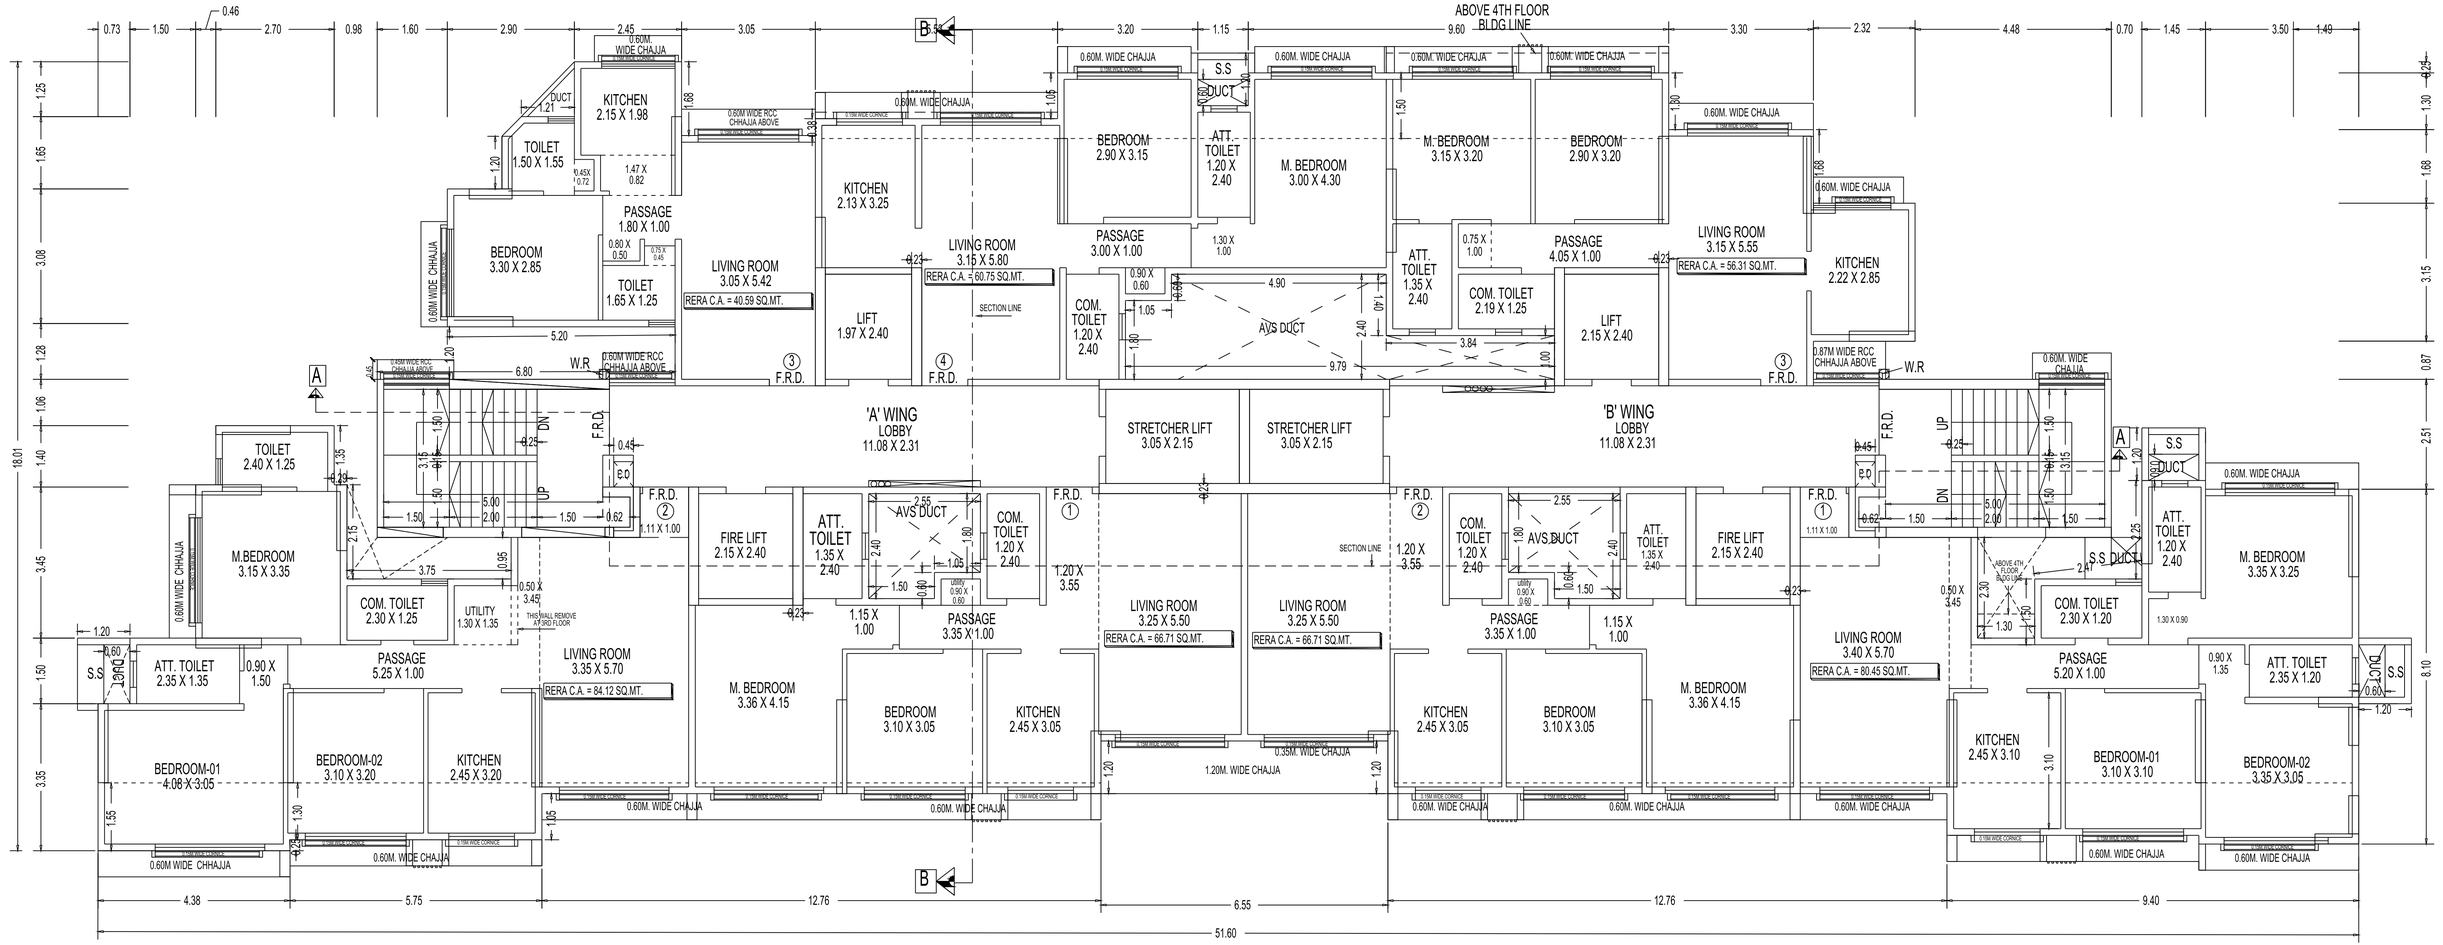


2nd & 3RD FLOOR PLAN


SCALE 1:100

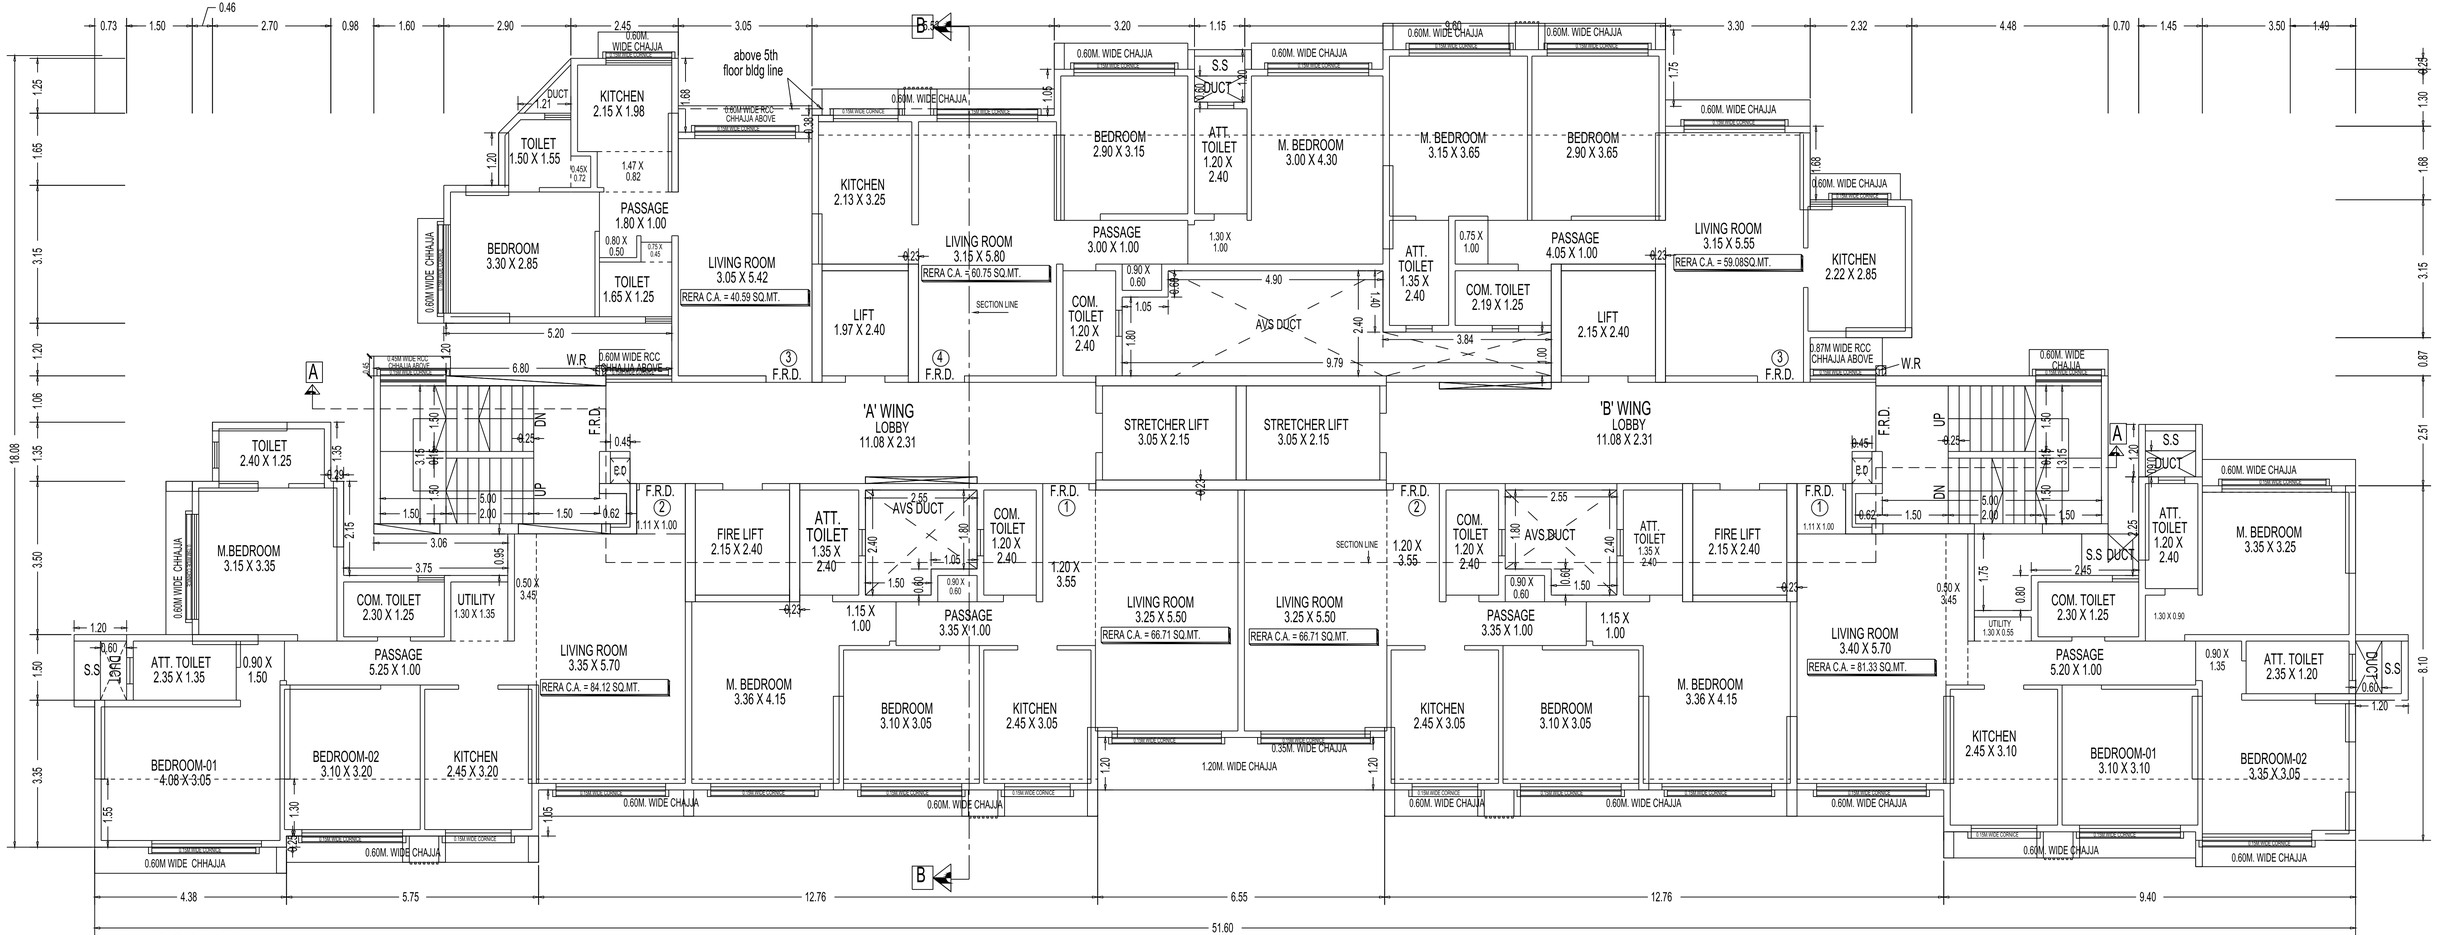

4th FLOOR PLAN


SCALE 1:100

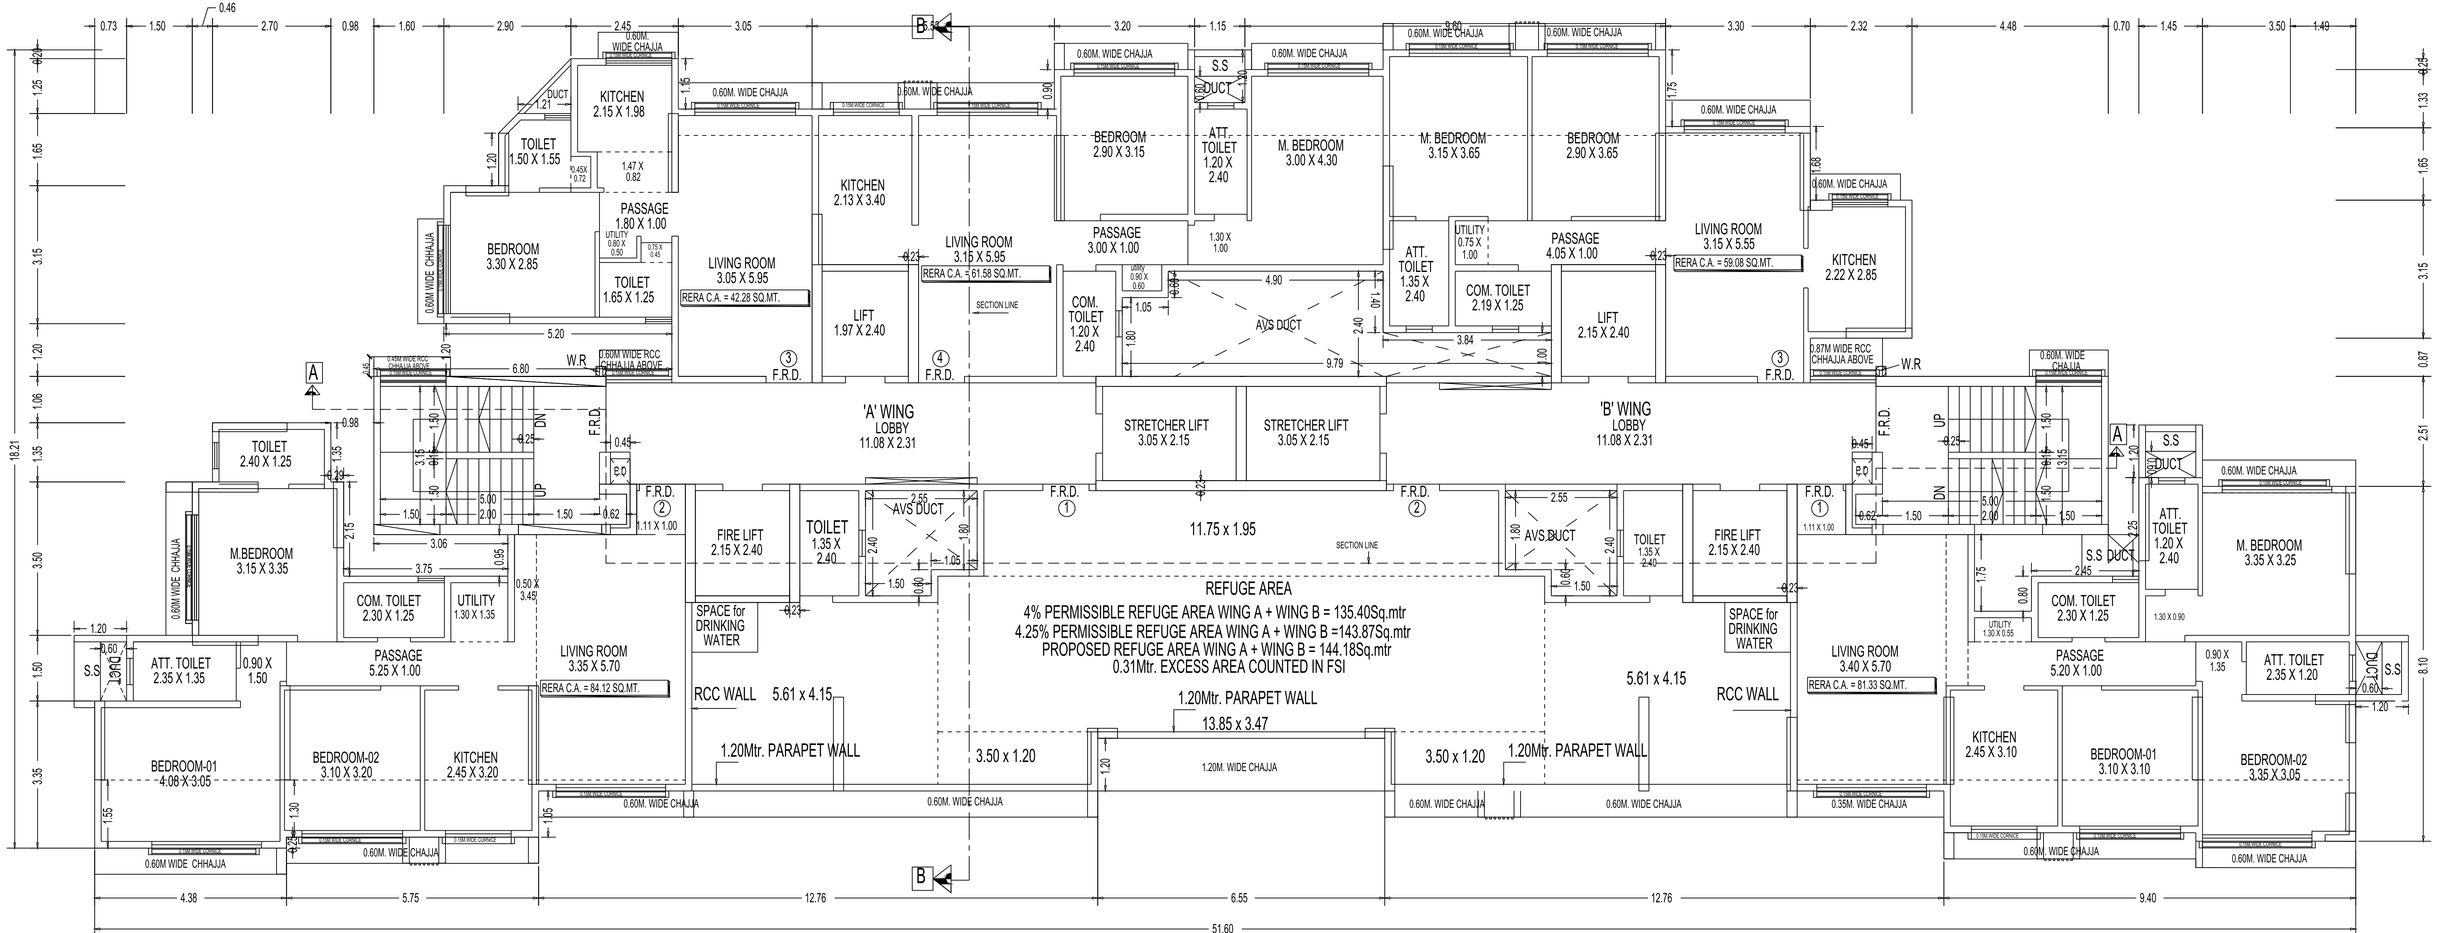
KITCHEN 2.15 X 1.98
TOILET 1.50 X 1.55
BEDROOM 3.30 X 2.85
PASSAGE 1.80 X 1.00
TOILET 1.65 X 1.25
LIVING ROOM 3.05 X 5.95
RERA C.A. = 42.28 SQ.MT.
KITCHEN 2.13 X 3.40
LIFT 1.97 X 2.40
LIVING ROOM 3.15 X 5.95
RERA C.A. = 61.58 SQ.MT.
BEDROOM 2.90 X 3.15
PASSAGE 3.00 X 1.00
ATT. TOILET 1.20 X 2.40
M. BEDROOM 3.00 X 4.30
COM. TOILET 1.20 X 2.40
AVS DUCT
M. BEDROOM 3.15 X 3.65
BEDROOM 2.90 X 3.65
ATT. TOILET 1.35 X 2.40
COM. TOILET 2.19 X 1.25
PASSAGE 4.05 X 1.00
LIFT 2.15 X 2.40
LIVING ROOM 3.15 X 5.55
RERA C.A. = 59.08 SQ.MT.
KITCHEN 2.22 X 2.85
'A' WING LOBBY 11.08 X 2.31
STRETCHER LIFT 3.05 X 2.15
STRETCHER LIFT 3.05 X 2.15
'B' WING LOBBY 11.08 X 2.31
TOILET 2.40 X 1.25
M.BEDROOM 3.15 X 3.35
COM. TOILET 2.30 X 1.25
UTILITY 1.30 X 1.35
PASSAGE 5.25 X 1.00
ATT. TOILET 2.35 X 1.35
LIVING ROOM 3.35 X 5.70
RERA C.A. = 84.12 SQ.MT.
FIRE LIFT 2.15 X 2.40
TOILET 1.35 X 2.40
AVS DUCT
11.75 x 1.95
SECTION LINE
REFUGE AREA
4% PERMISSIBLE REFUGE AREA WING A + WING B = 135.40Sq.mtr
4.25% PERMISSIBLE REFUGE AREA WING A + WING B =143.87Sq.mtr
PROPOSED REFUGE AREA WING A + WING B = 144.18Sq.mtr
0.31Mtr. EXCESS AREA COUNTED IN FSI
SPACE for DRINKING WATER
RCC WALL 5.61 x 4.15
1.20Mtr. PARAPET WALL
13.85 x 3.47
3.50 x 1.20
1.20M. WIDE CHAJJA
5.61 x 4.15
RCC WALL
1.20Mtr. PARAPET WALL
3.50 x 1.20
SPACE for DRINKING WATER
FIRE LIFT 2.15 X 2.40
TOILET 1.35 X 2.40
AVS DUCT
TOILET 2.40 X 1.25
M.BEDROOM 3.35 X 3.25
COM. TOILET 2.30 X 1.25
ATT. TOILET 1.20 X 2.40
PASSAGE 5.20 X 1.00
LIVING ROOM 3.40 X 5.70
RERA C.A. = 81.33 SQ.MT.
ATT. TOILET 2.35 X 1.20
BEDROOM-01 4.08 X 3.05
BEDROOM-02 3.10 X 3.20
KITCHEN 2.45 X 3.20
KITCHEN 2.45 X 3.10
BEDROOM-01 3.10 X 3.10
BEDROOM-02 3.35 X 3.05
0.60M. WIDE CHAJJA
0.60M WIDE CHHAJJA
0.87M WIDE RCC CHHAJJA ABOVE
W.R
F.R.D.
UP
DN
S.S DUCT
A
B
4.38
5.75
12.76
6.55
12.76
9.40
51.60
18.21
5th FLOOR PLAN (REFUGE)
SCALE 1:100

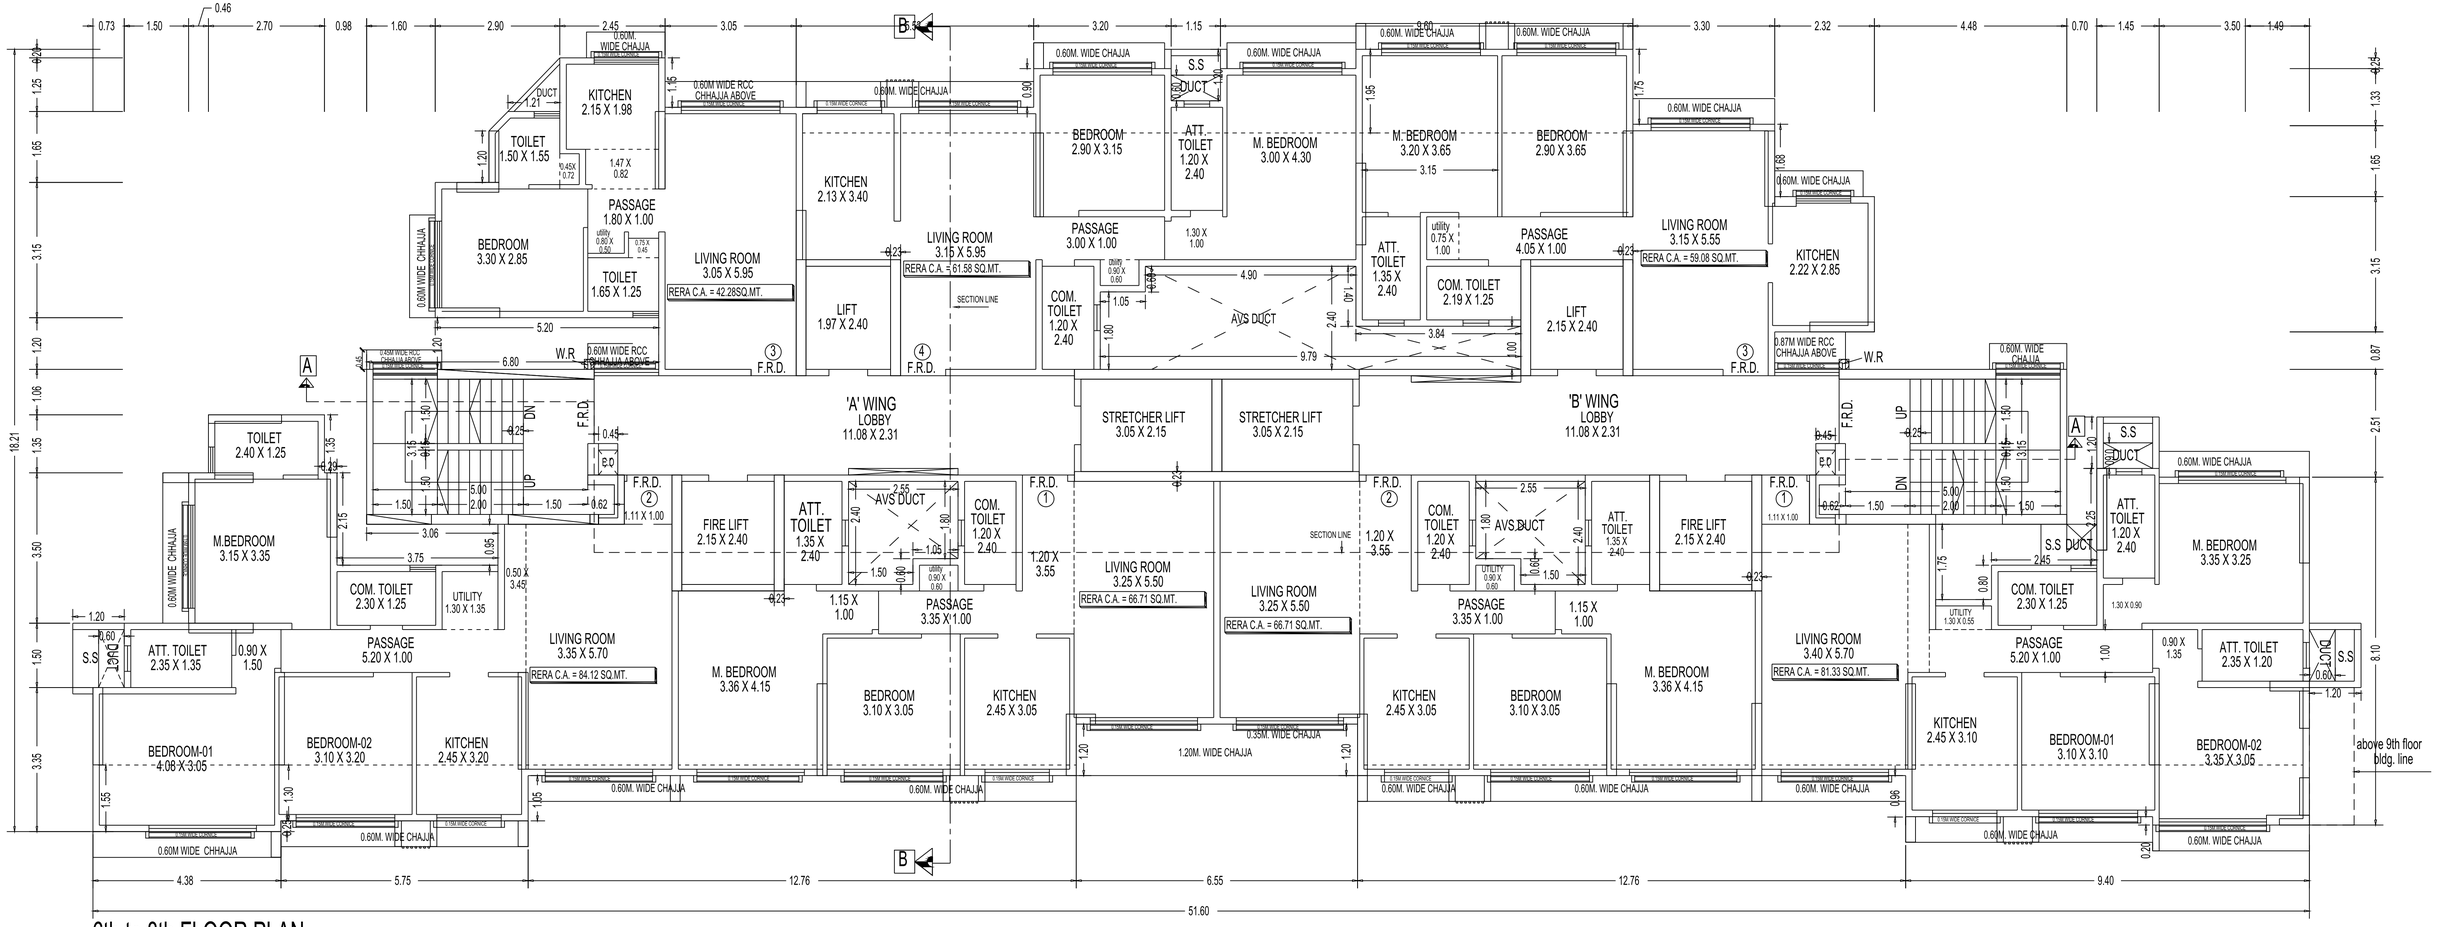


6th to 8th FLOOR PLAN

SCALE 1:100

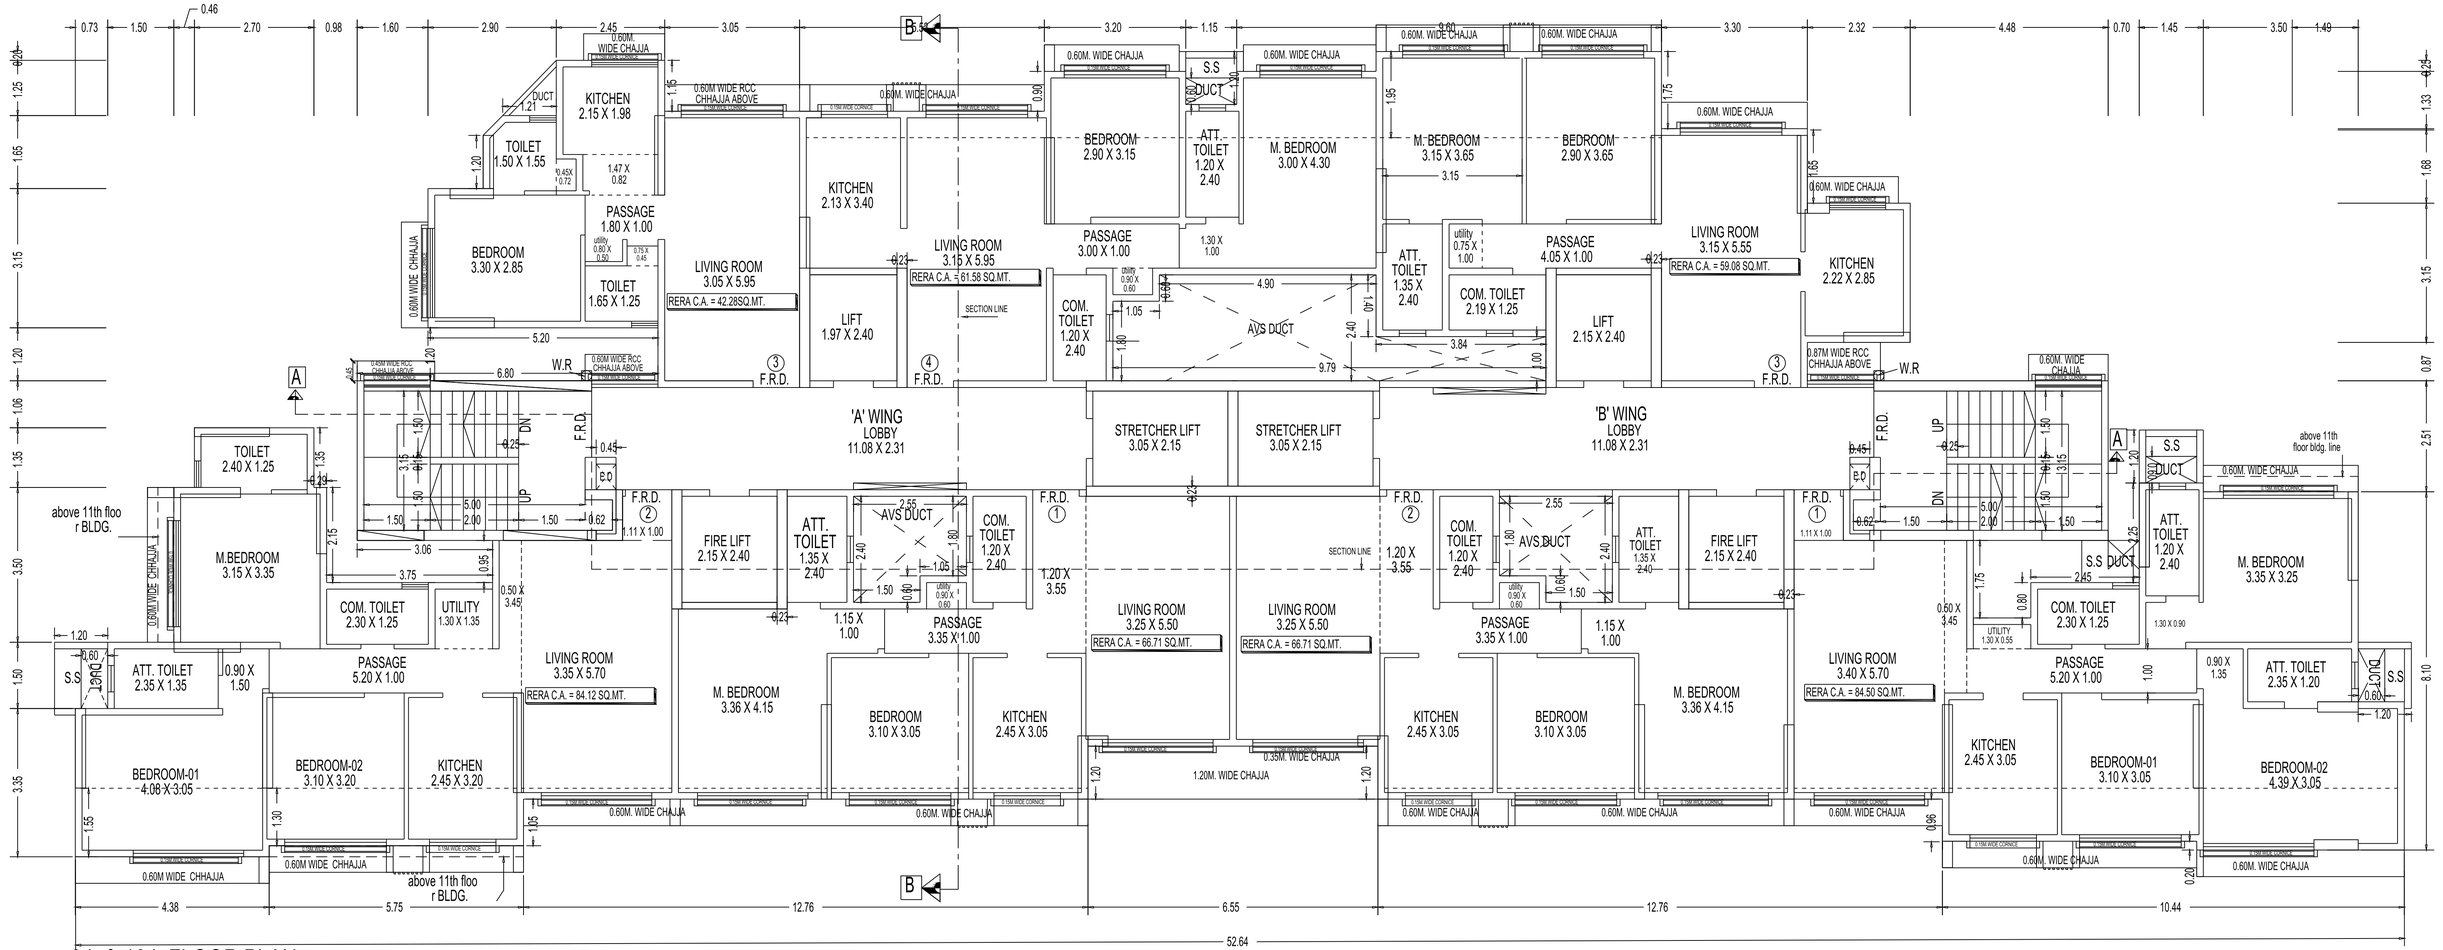


9th & 10th FLOOR PLAN

SCALE 1:100

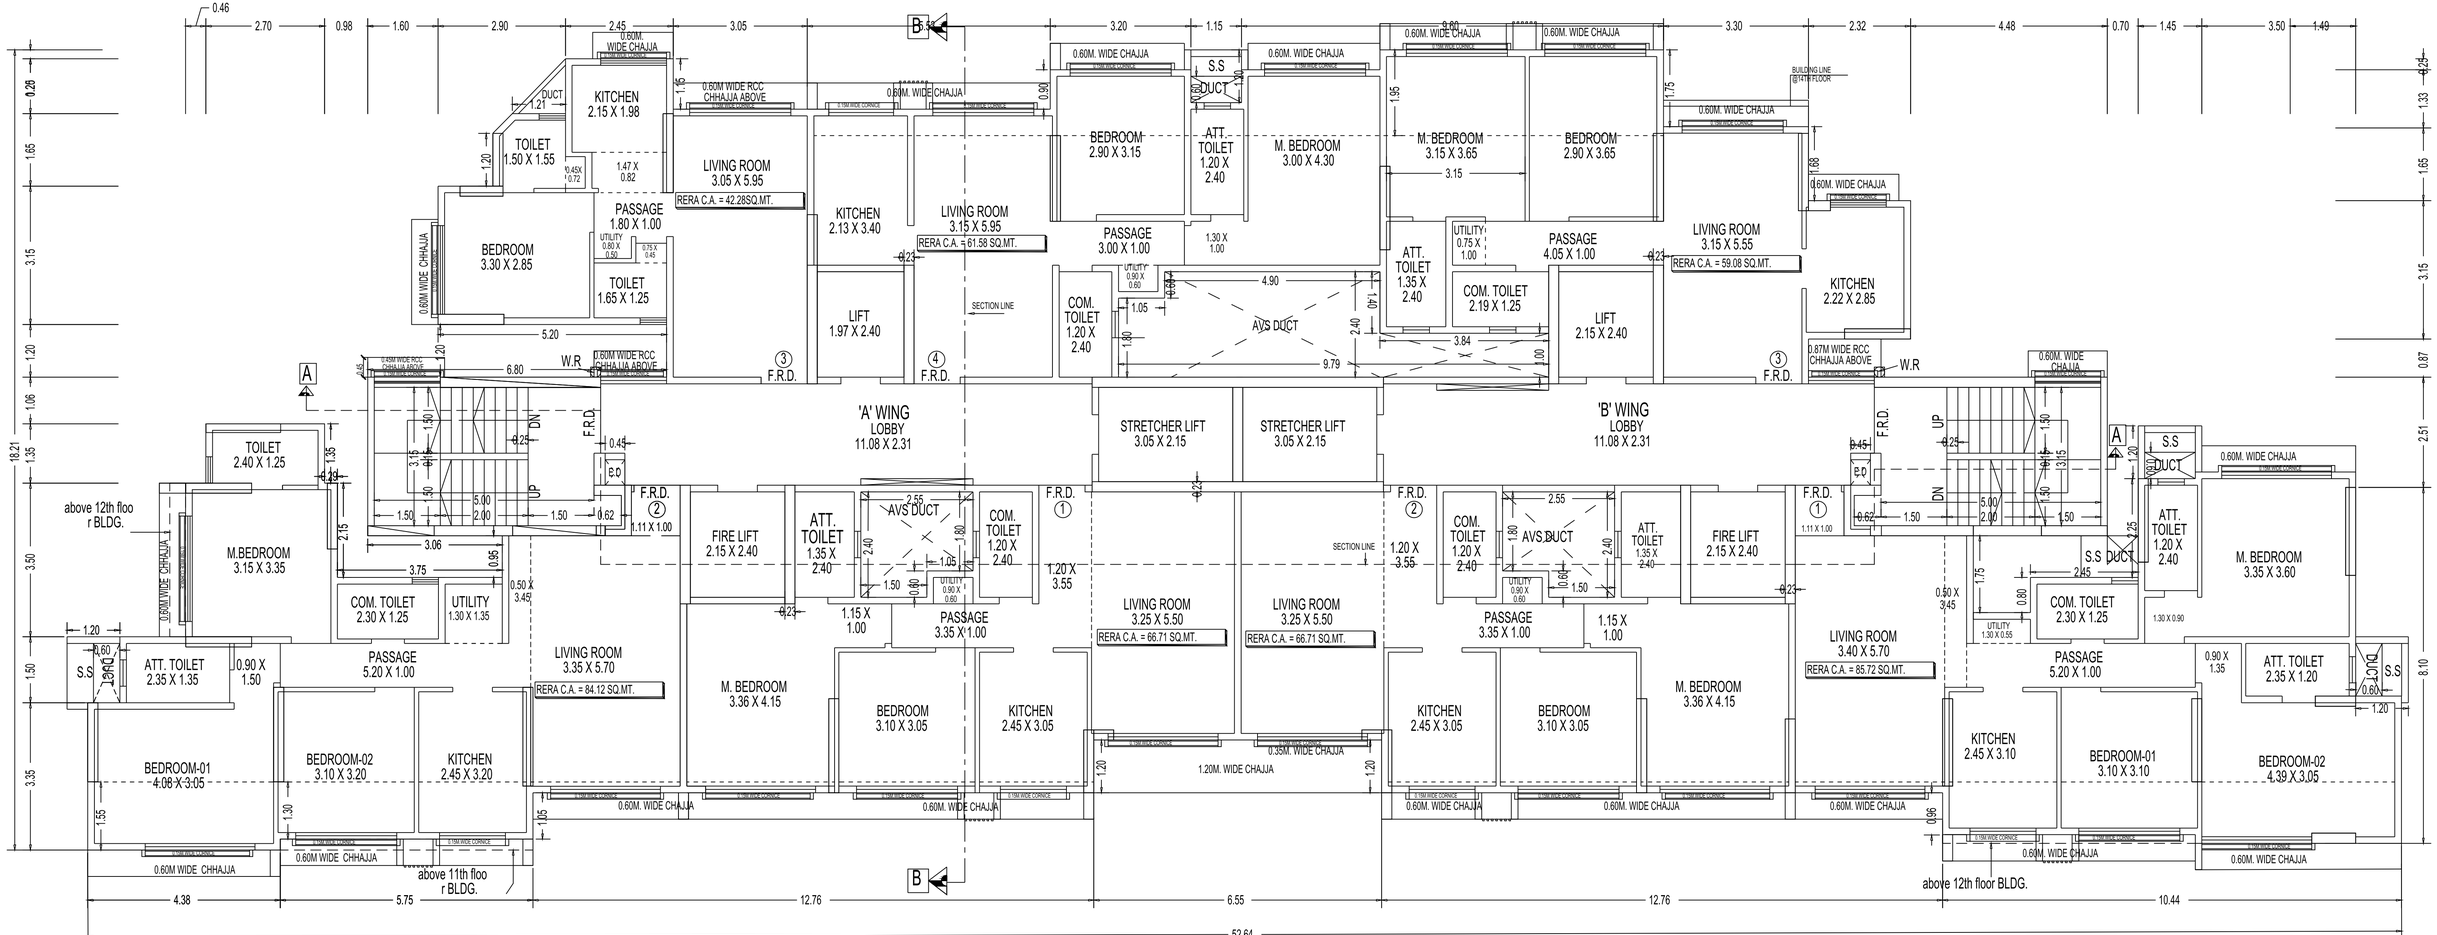


11th FLOOR PLAN

SCALE 1:100

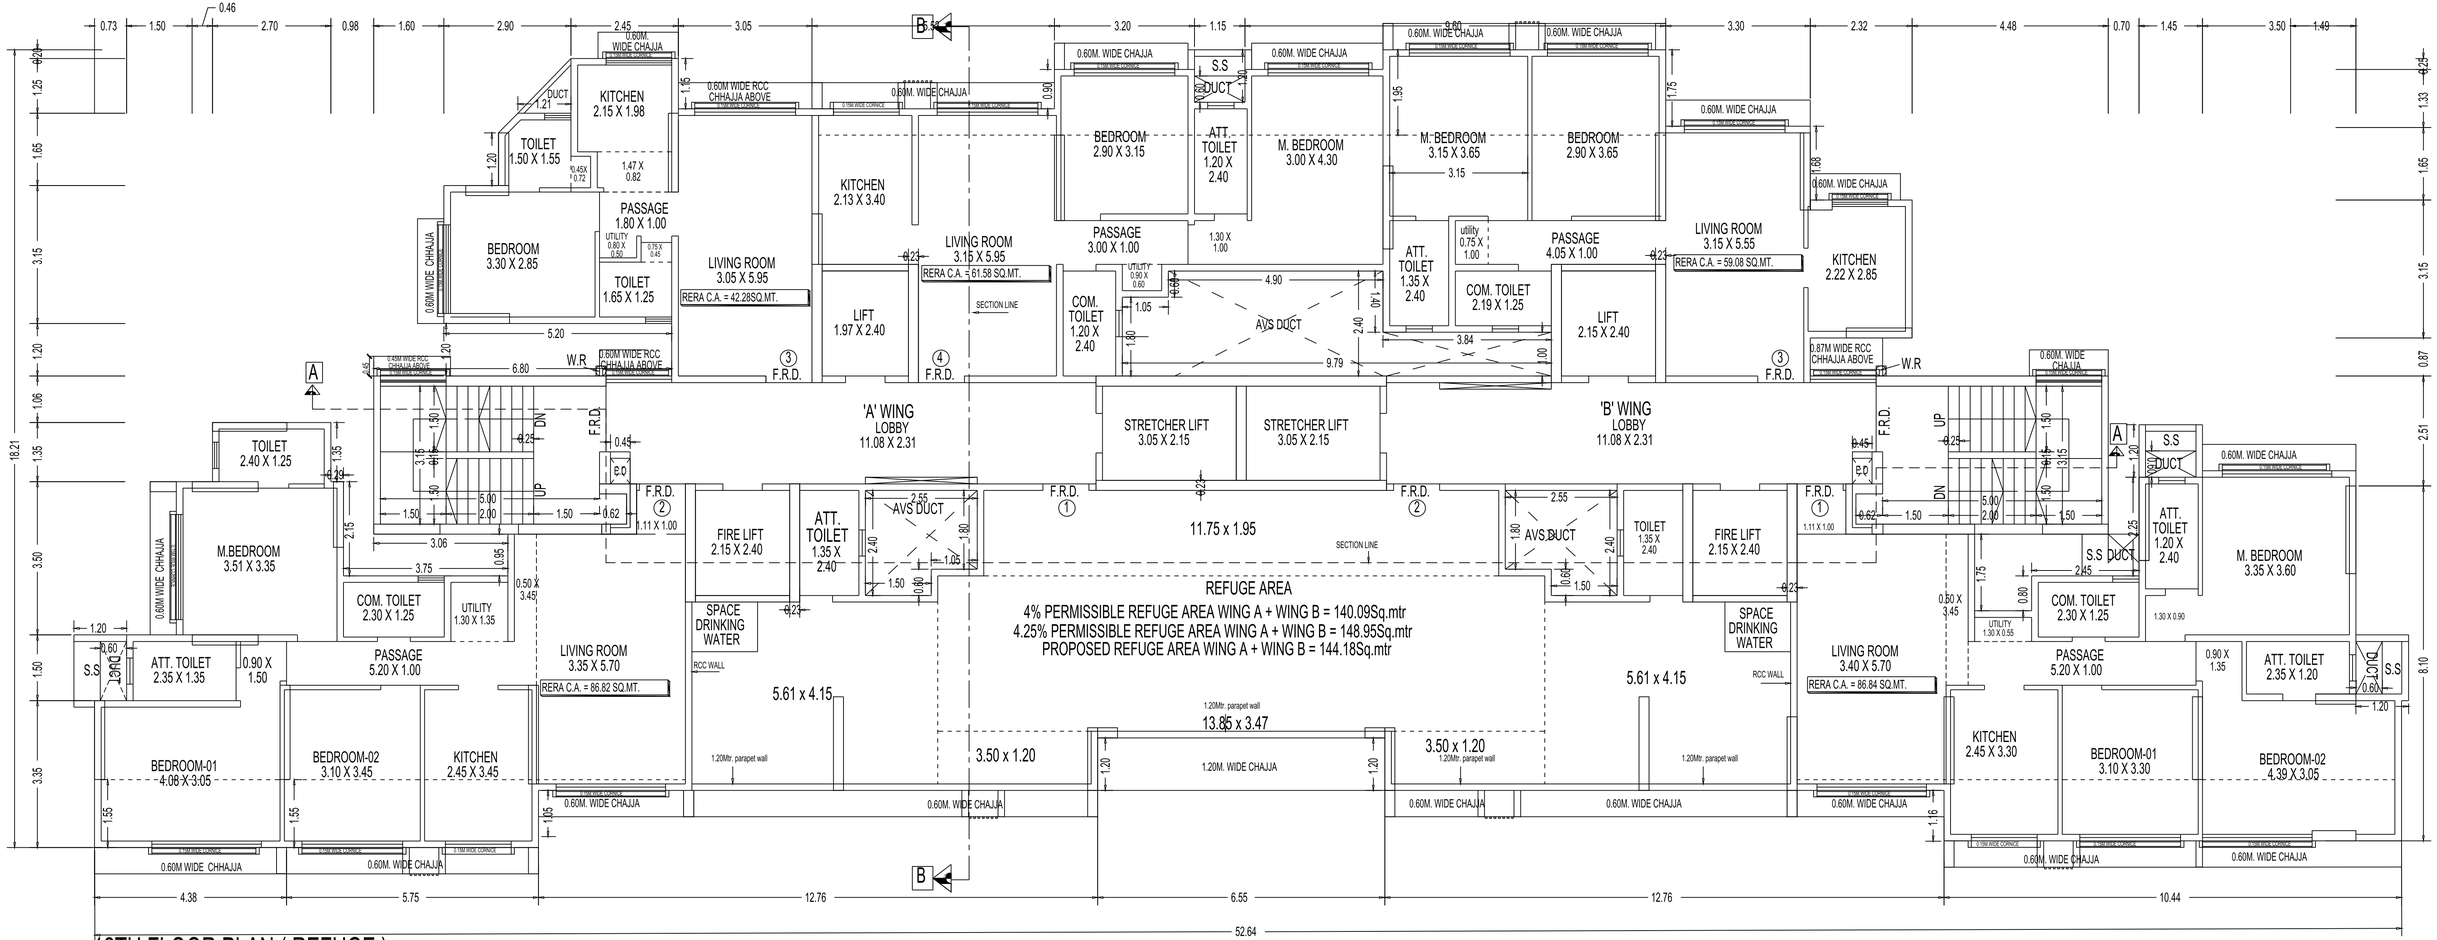

12TH FLOOR PLAN (REFUGE)


SCALE 1:100

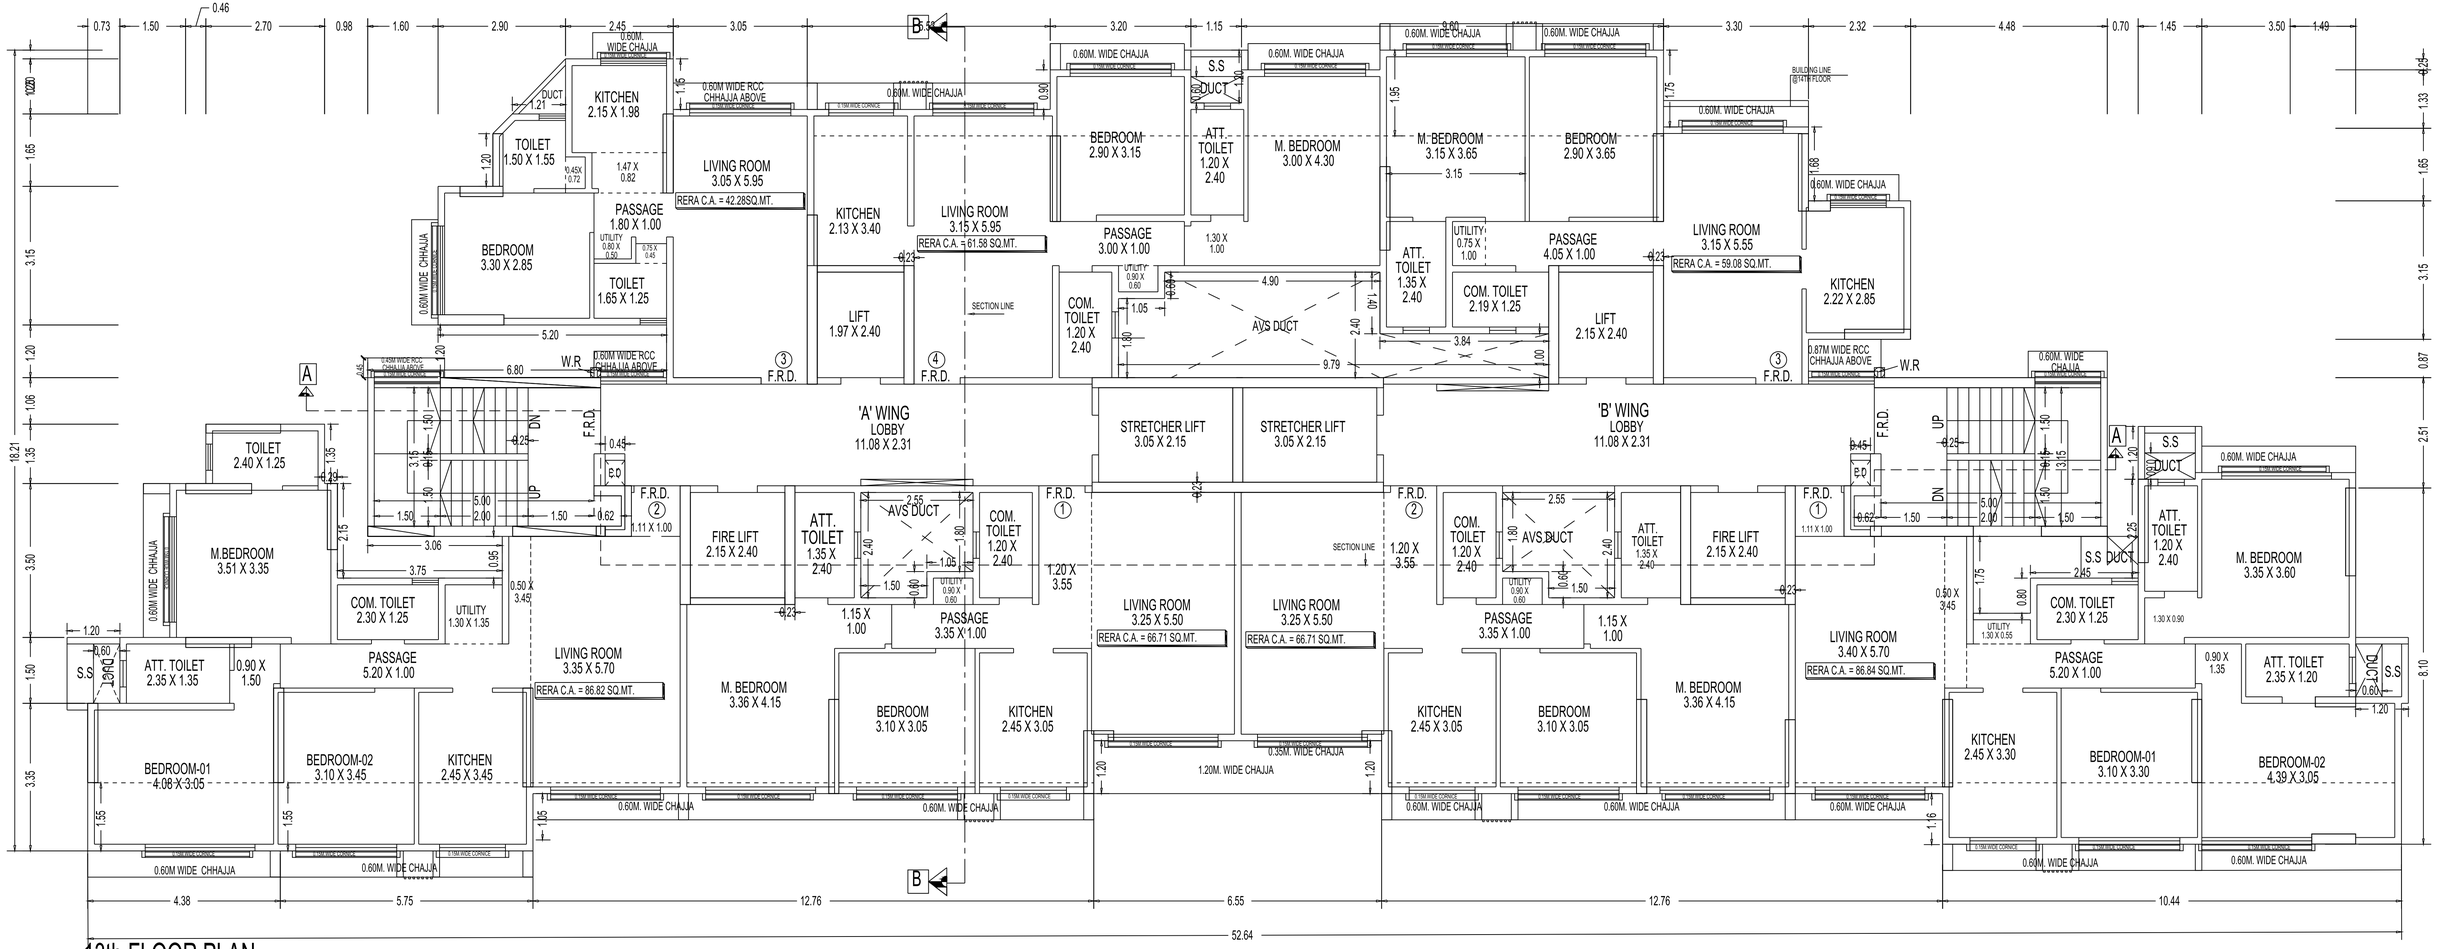

13th FLOOR PLAN


SCALE 1:100

SCALE 1:100

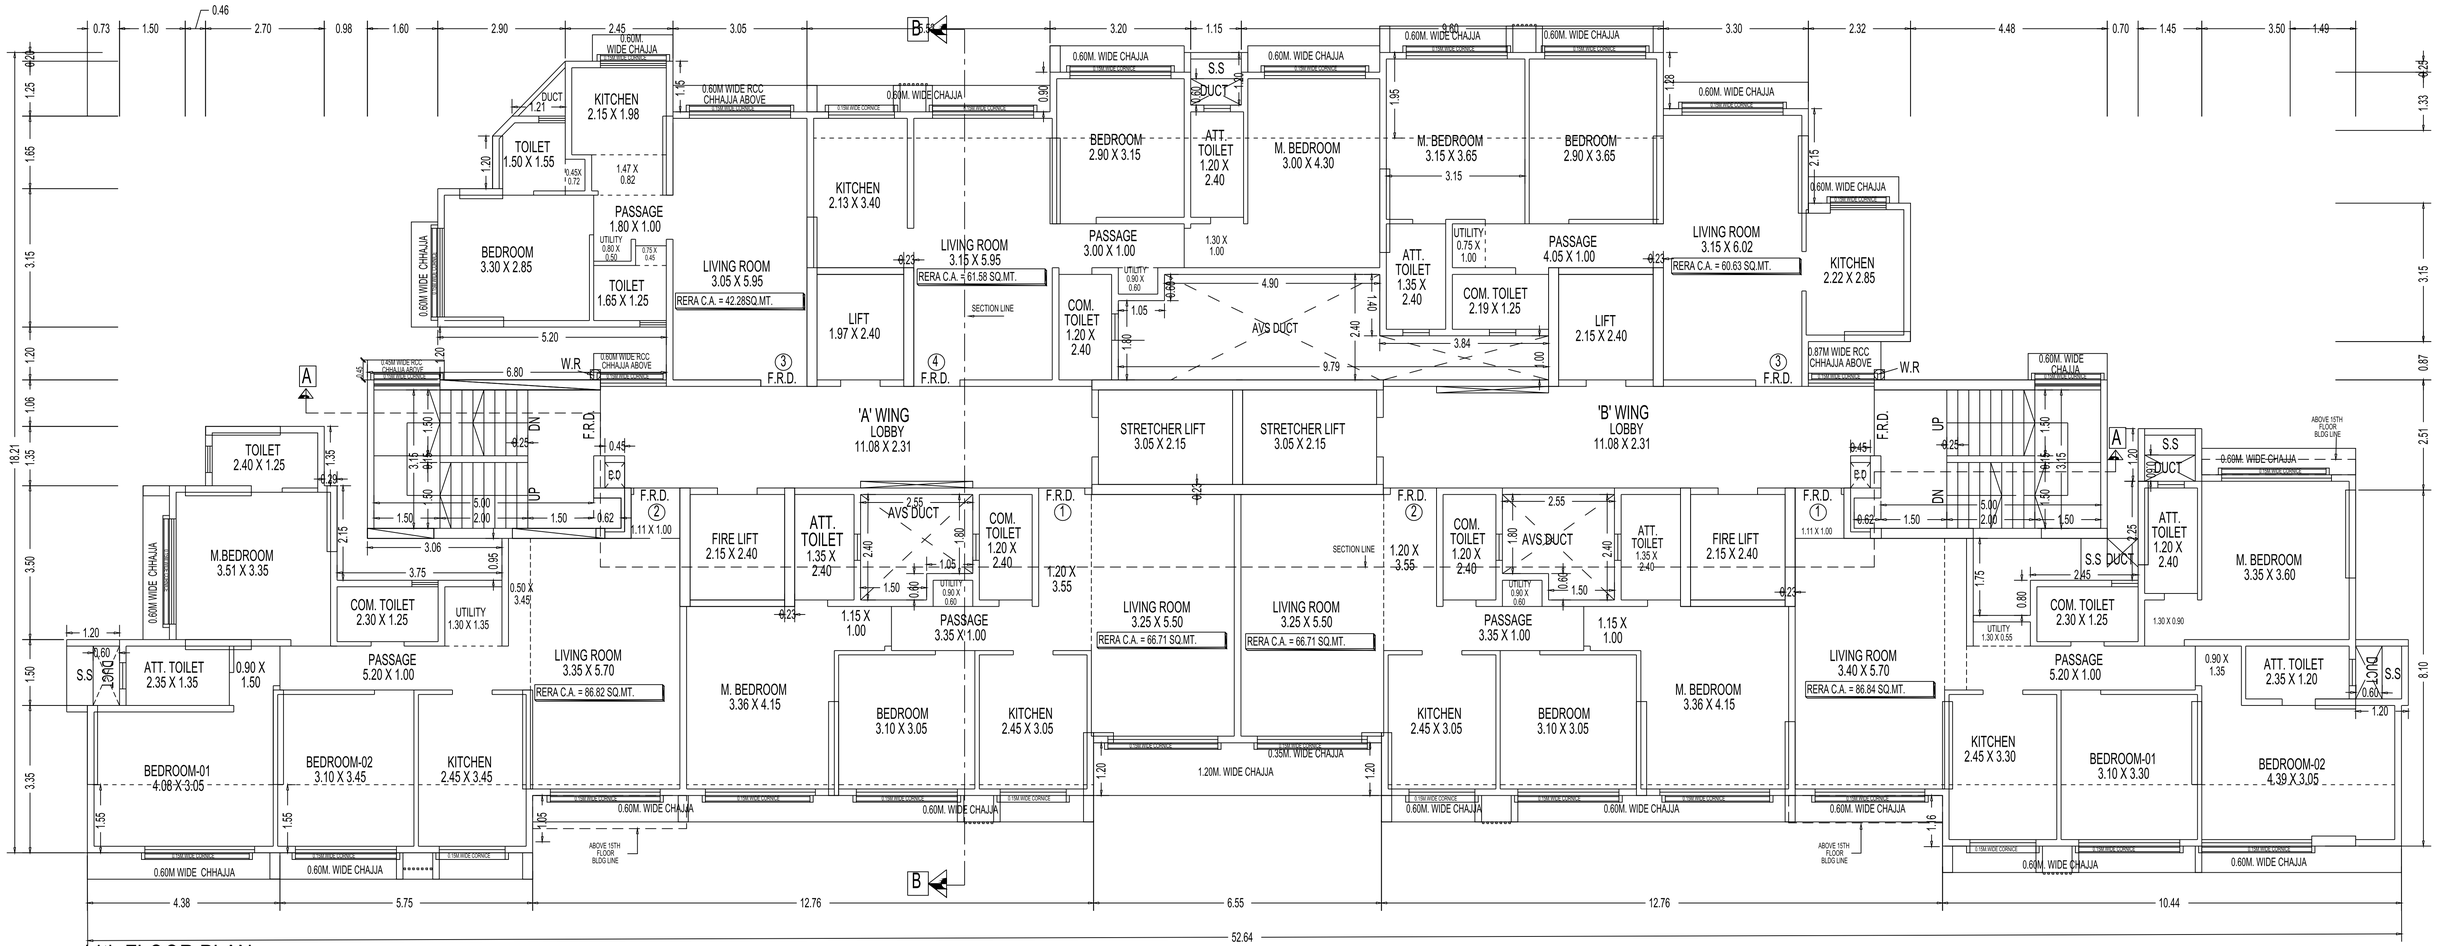


14th FLOOR PLAN

SCALE 1:100

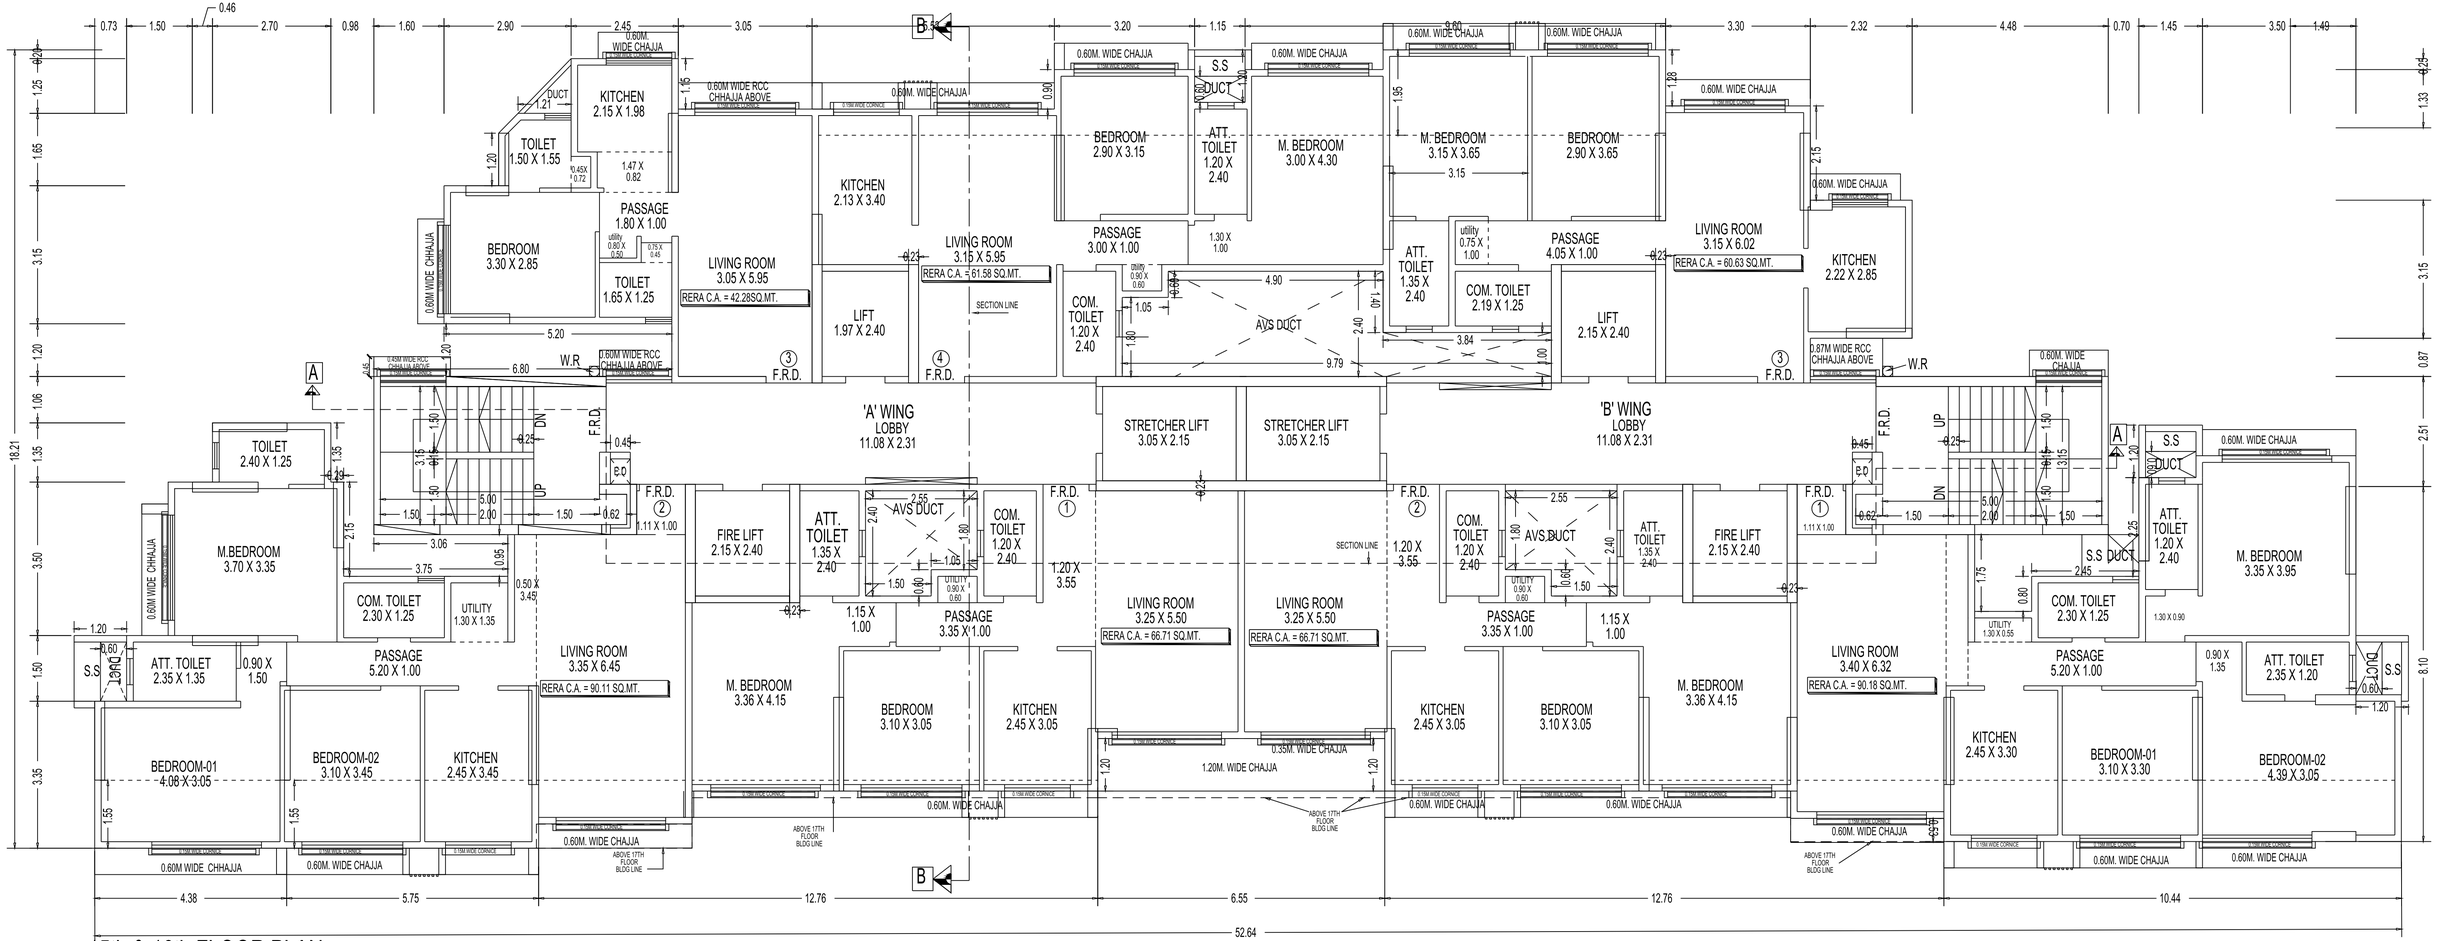

15th & 16th FLOOR PLAN


SCALE 1:100

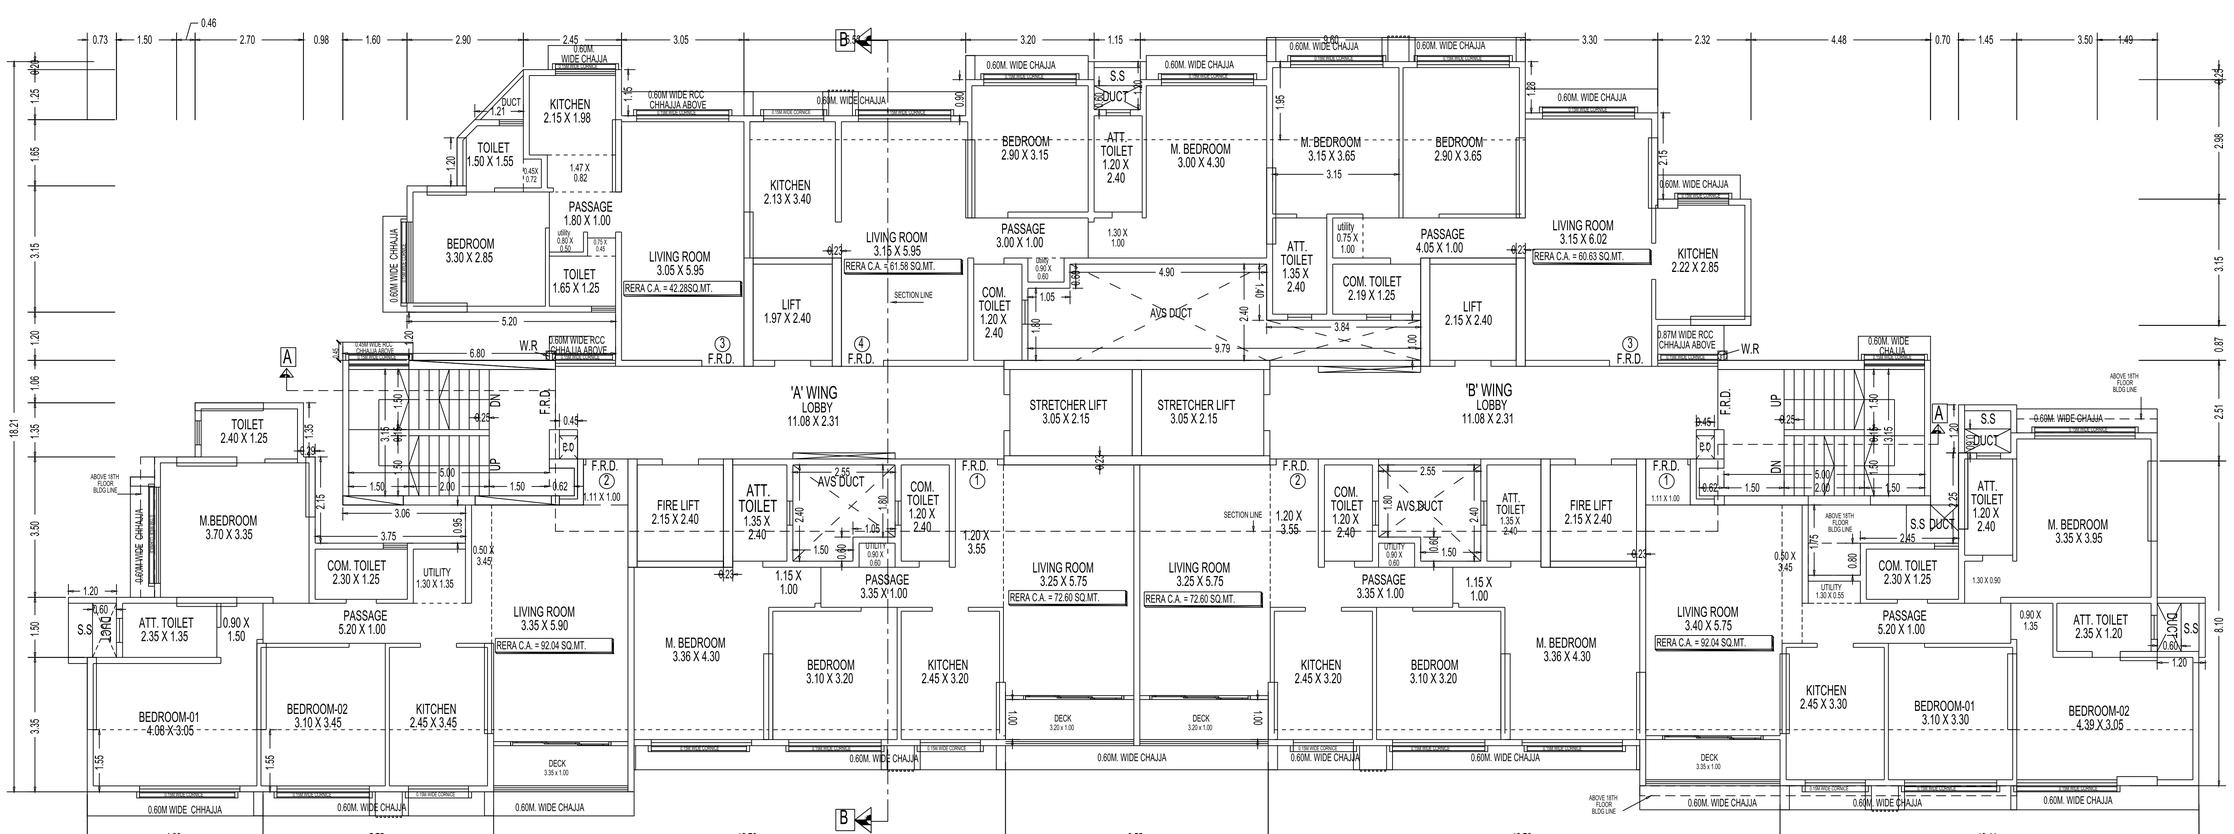


[X1 - (Y2+Y3)]

D1
D2
D3
TOTAL DUCT AREA PER FL. (TYPICAL FLOOR)

NET BUILT UP AREA
[X1 - (Y2+Y3)]

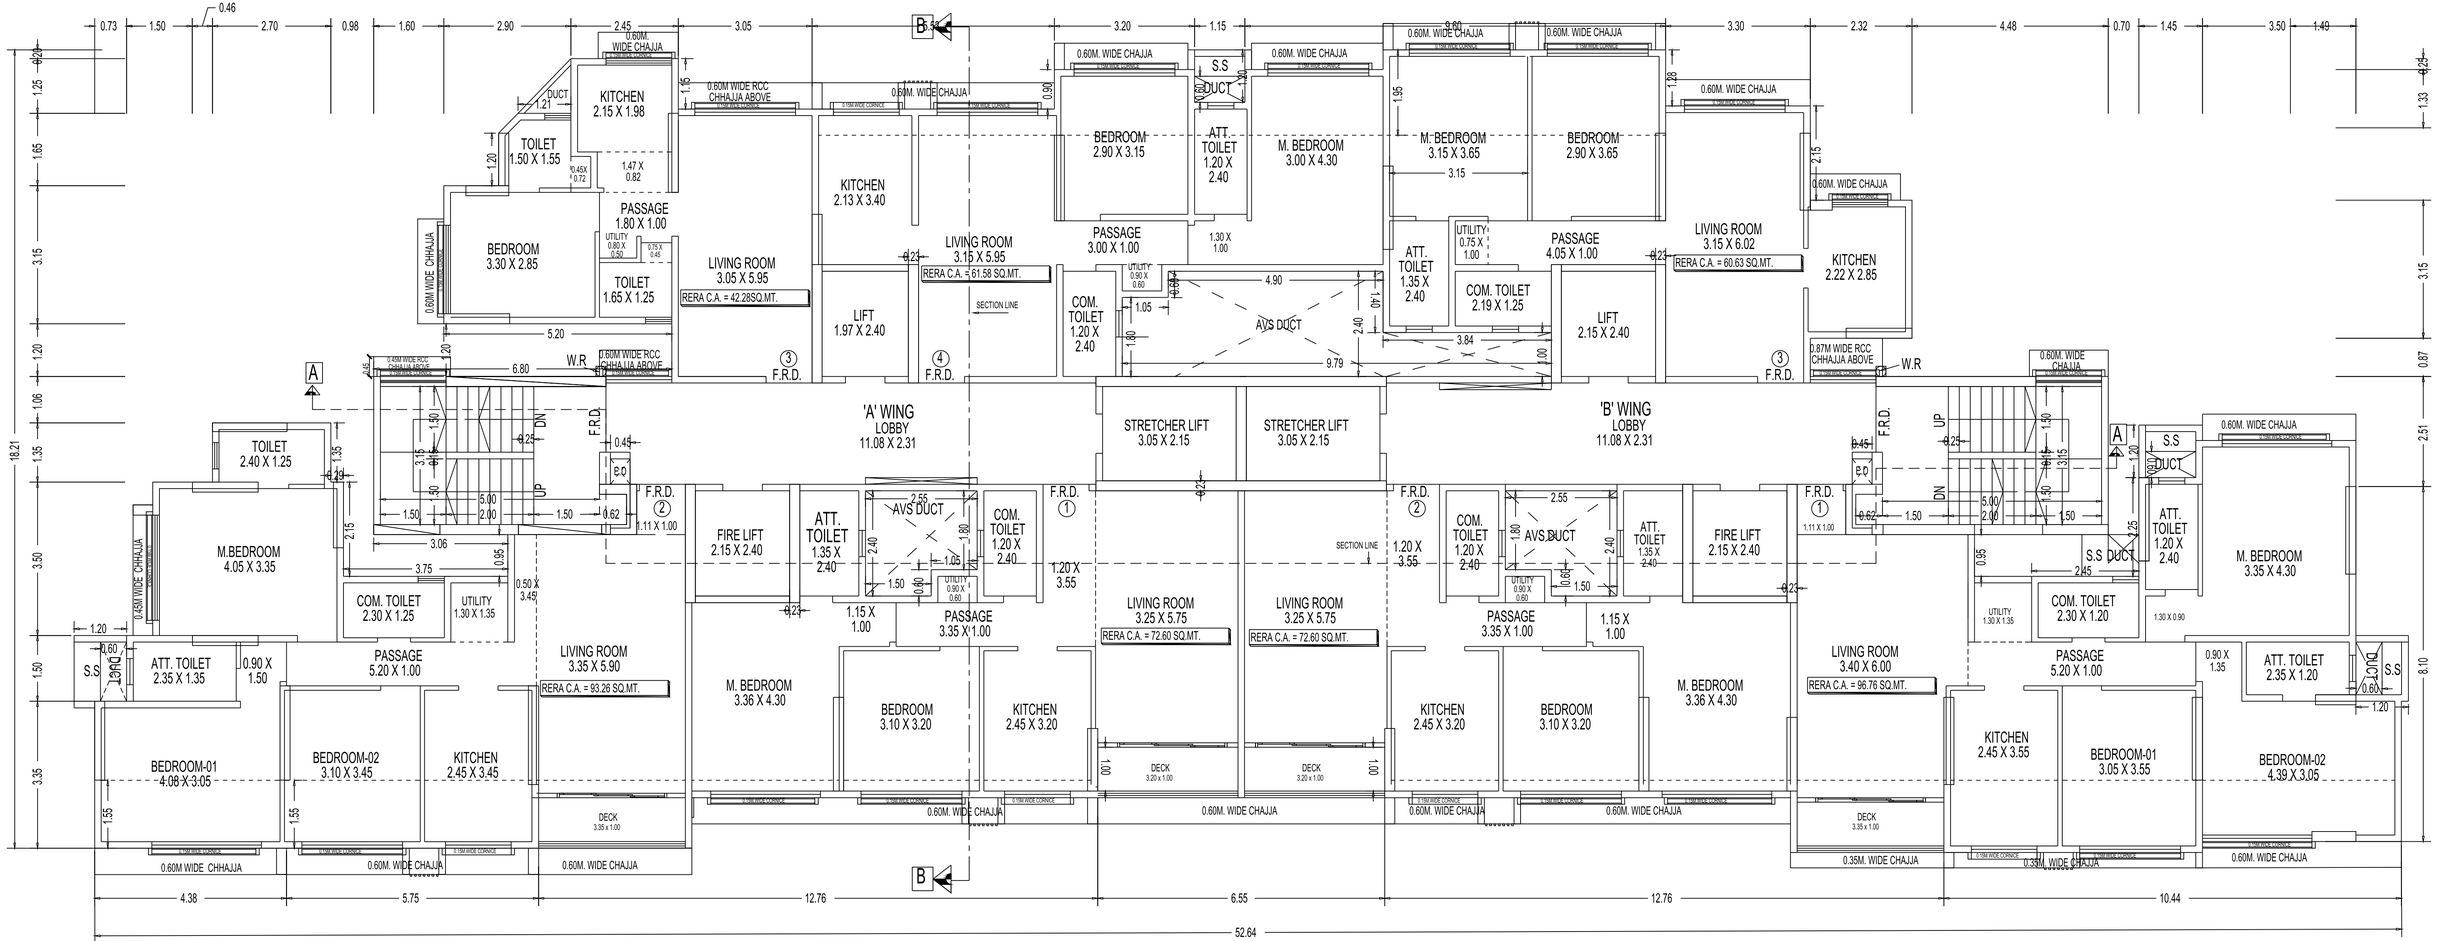

18th FLOOR PLAN
SCALE 1:100

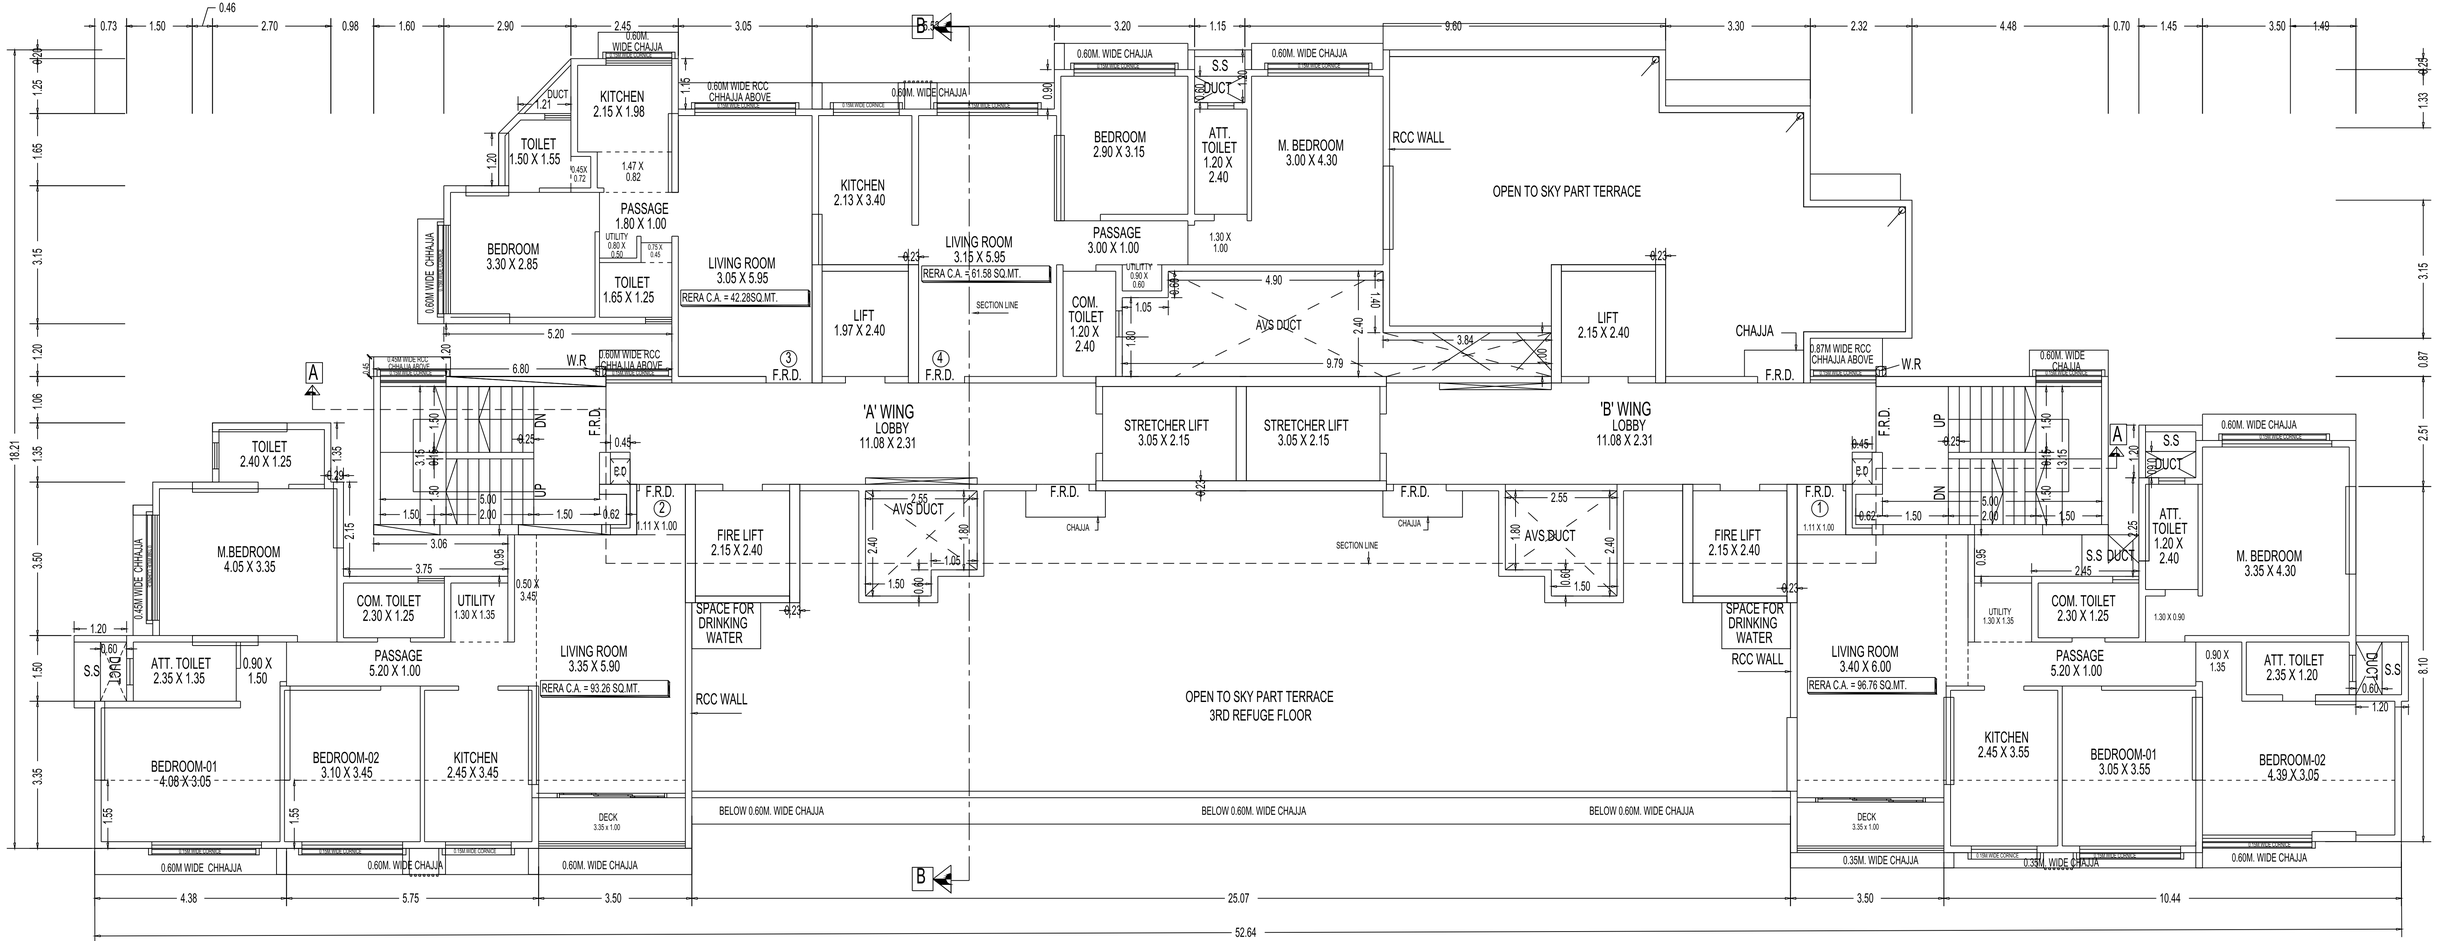
KITCHEN 2.15 X 1.98
TOILET 1.50 X 1.55
PASSAGE 1.80 X 1.00
BEDROOM 3.30 X 2.85
TOILET 1.65 X 1.25
LIVING ROOM 3.05 X 5.95
RERA C.A. = 42.28SQ.MT.
KITCHEN 2.13 X 3.40
LIFT 1.97 X 2.40
LIVING ROOM 3.15 X 5.95
RERA C.A. = 61.58 SQ.MT.
BEDROOM 2.90 X 3.15
PASSAGE 3.00 X 1.00
ATT. TOILET 1.20 X 2.40
M. BEDROOM 3.00 X 4.30
RCC WALL
OPEN TO SKY PART TERRACE
COM. TOILET 1.20 X 2.40
AVS DUCT
LIFT 2.15 X 2.40
'A' WING LOBBY 11.08 X 2.31
STRETCHER LIFT 3.05 X 2.15
STRETCHER LIFT 3.05 X 2.15
'B' WING LOBBY 11.08 X 2.31
TOILET 2.40 X 1.25
M.BEDROOM 4.05 X 3.35
COM. TOILET 2.30 X 1.25
UTILITY 1.30 X 1.35
PASSAGE 5.20 X 1.00
ATT. TOILET 2.35 X 1.35
LIVING ROOM 3.35 X 5.90
RERA C.A. = 93.26 SQ.MT.
FIRE LIFT 2.15 X 2.40
SPACE FOR DRINKING WATER
RCC WALL
OPEN TO SKY PART TERRACE
3RD REFUGE FLOOR
LIVING ROOM 3.40 X 6.00
RERA C.A. = 96.76 SQ.MT.
PASSAGE 5.20 X 1.00
KITCHEN 2.45 X 3.55
BEDROOM-01 3.05 X 3.55
BEDROOM-02 4.39 X 3.05
ATT. TOILET 2.35 X 1.20
M. BEDROOM 3.35 X 4.30
COM. TOILET 2.30 X 1.25
BEDROOM-01 4.08 X 3.05
BEDROOM-02 3.10 X 3.45
KITCHEN 2.45 X 3.45
DECK 3.35 X 1.00
BELOW 0.60M. WIDE CHAJJA
SECTION LINE
F.R.D.
W.R
DUCT
CHAJJA
52.64
19th FLOOR PLAN
SCALE 1:100