

SCALE:-1:100

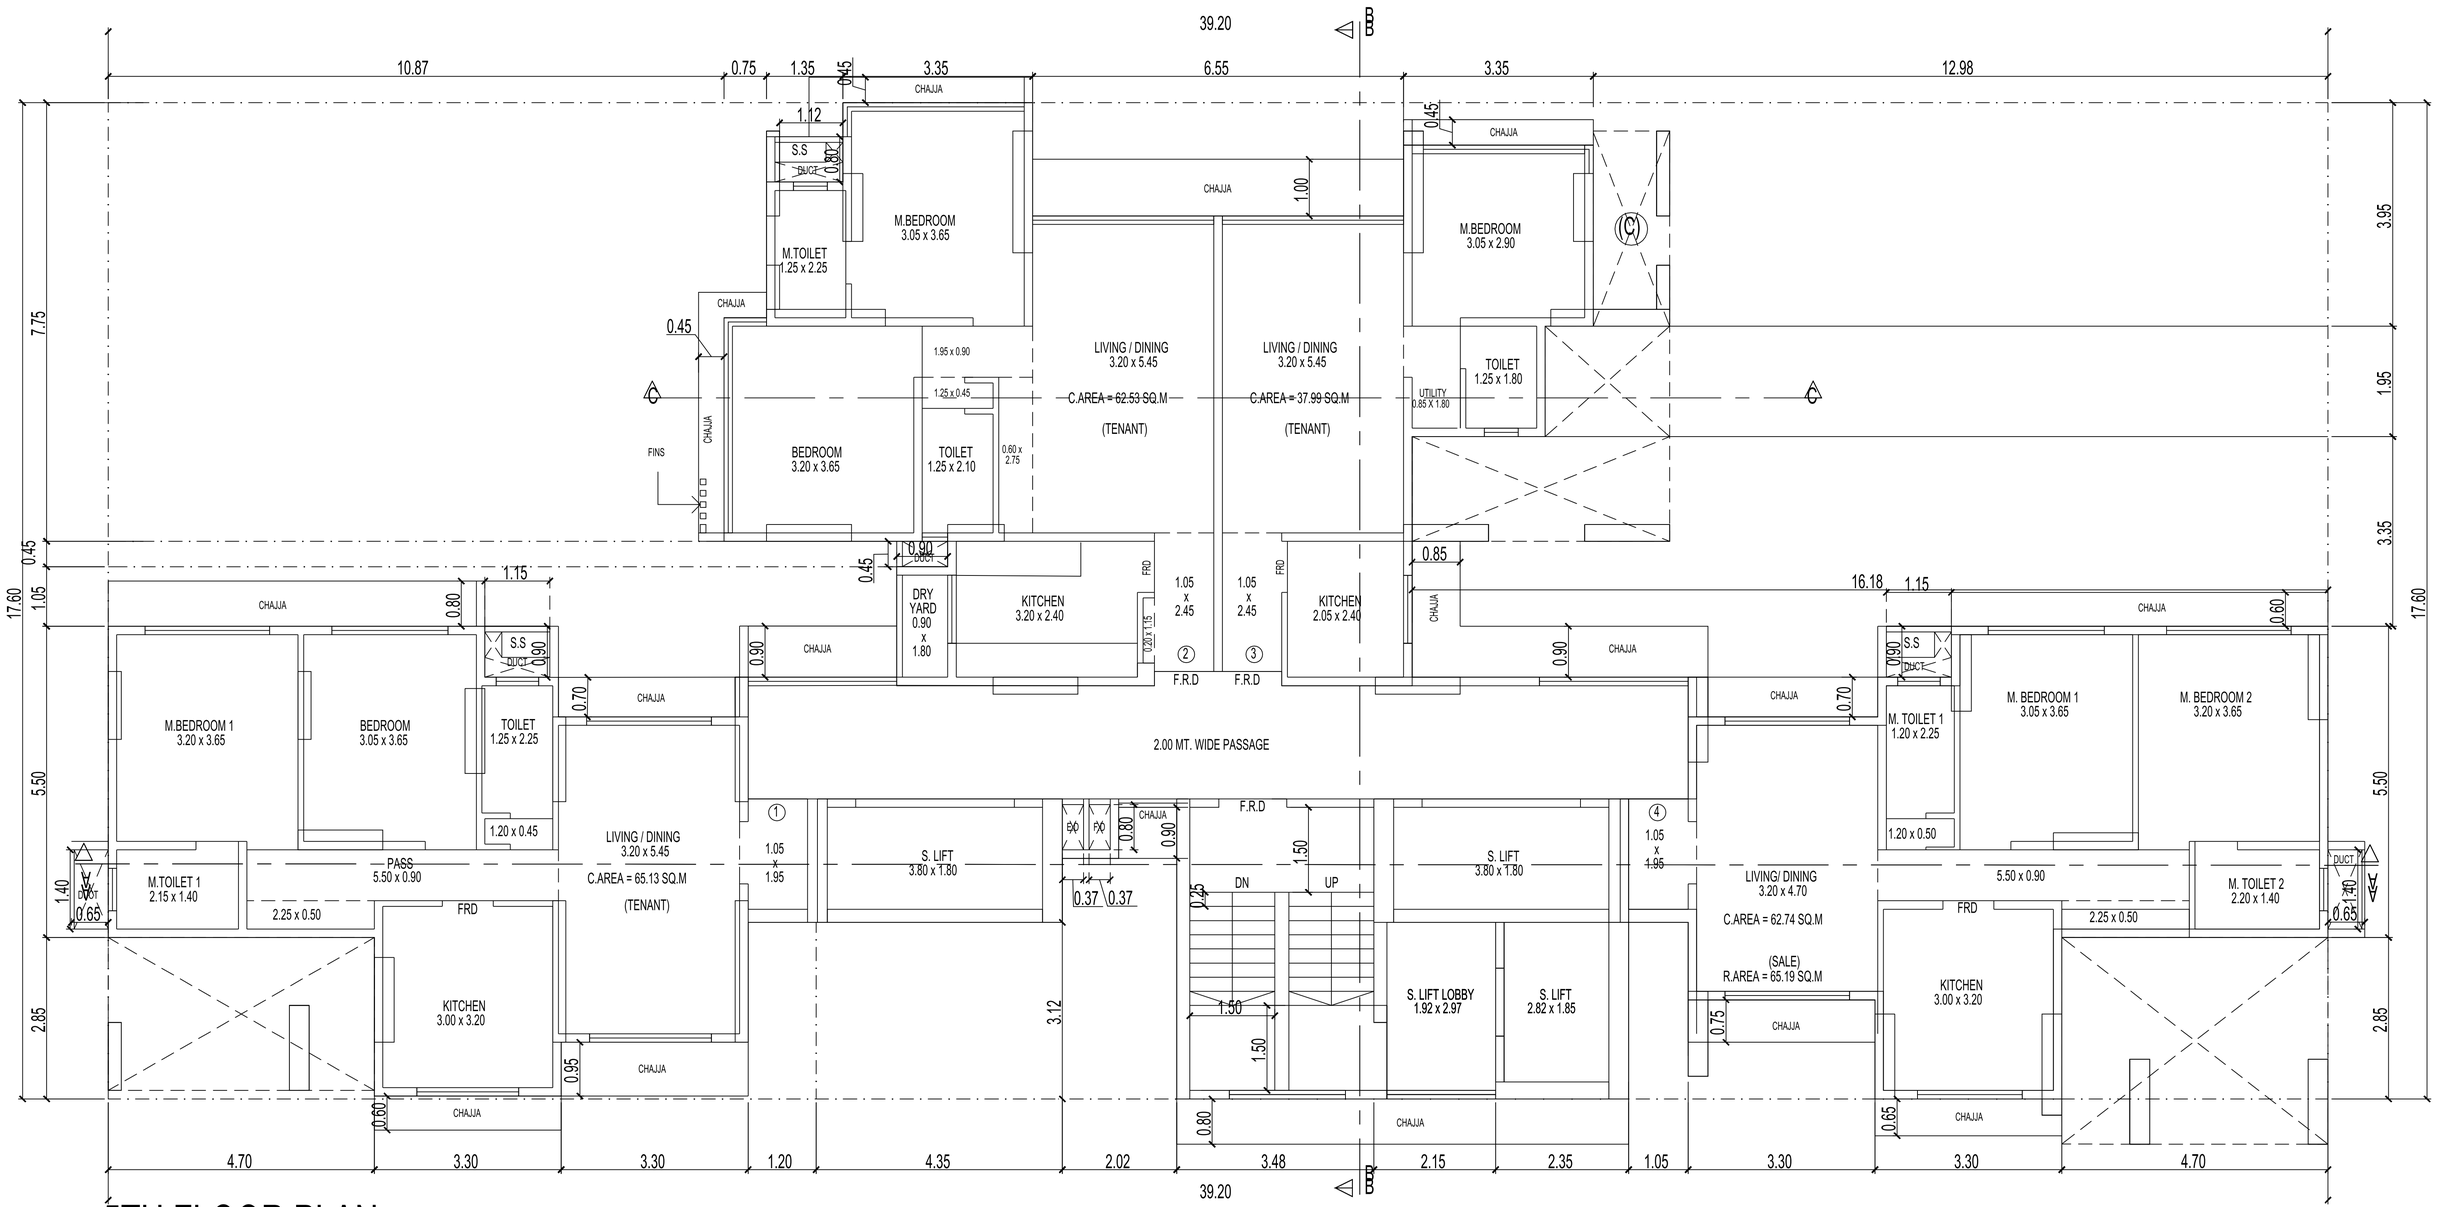


5TH FLOOR PLAN

SCALE:-1:100

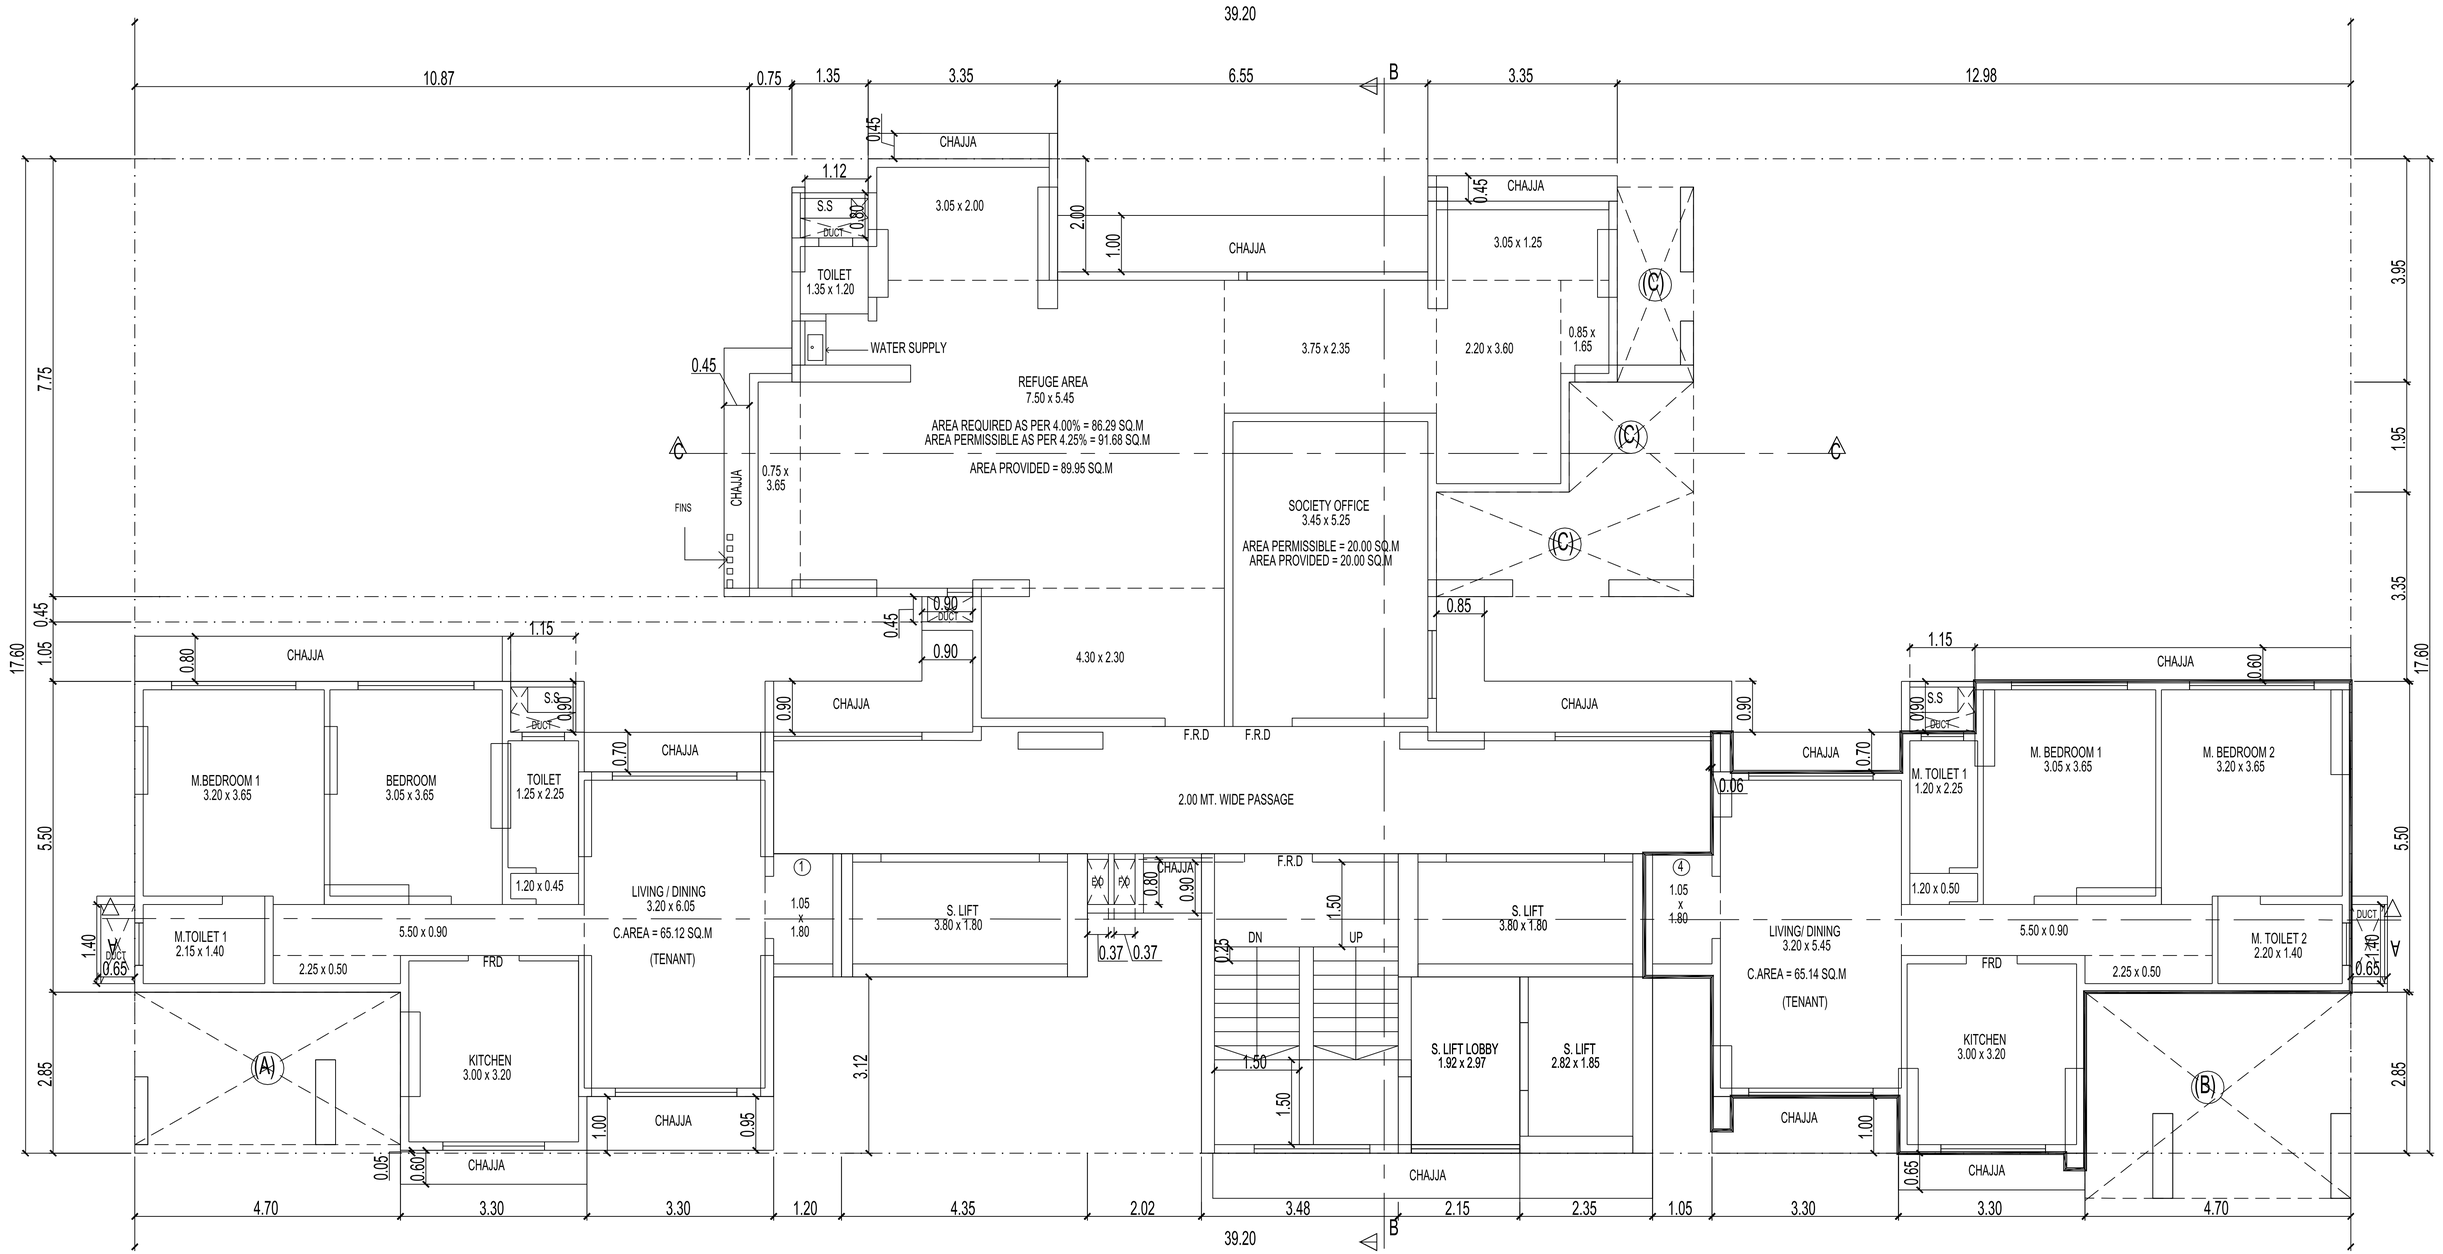


6TH FLOOR PLAN (REFUGE)

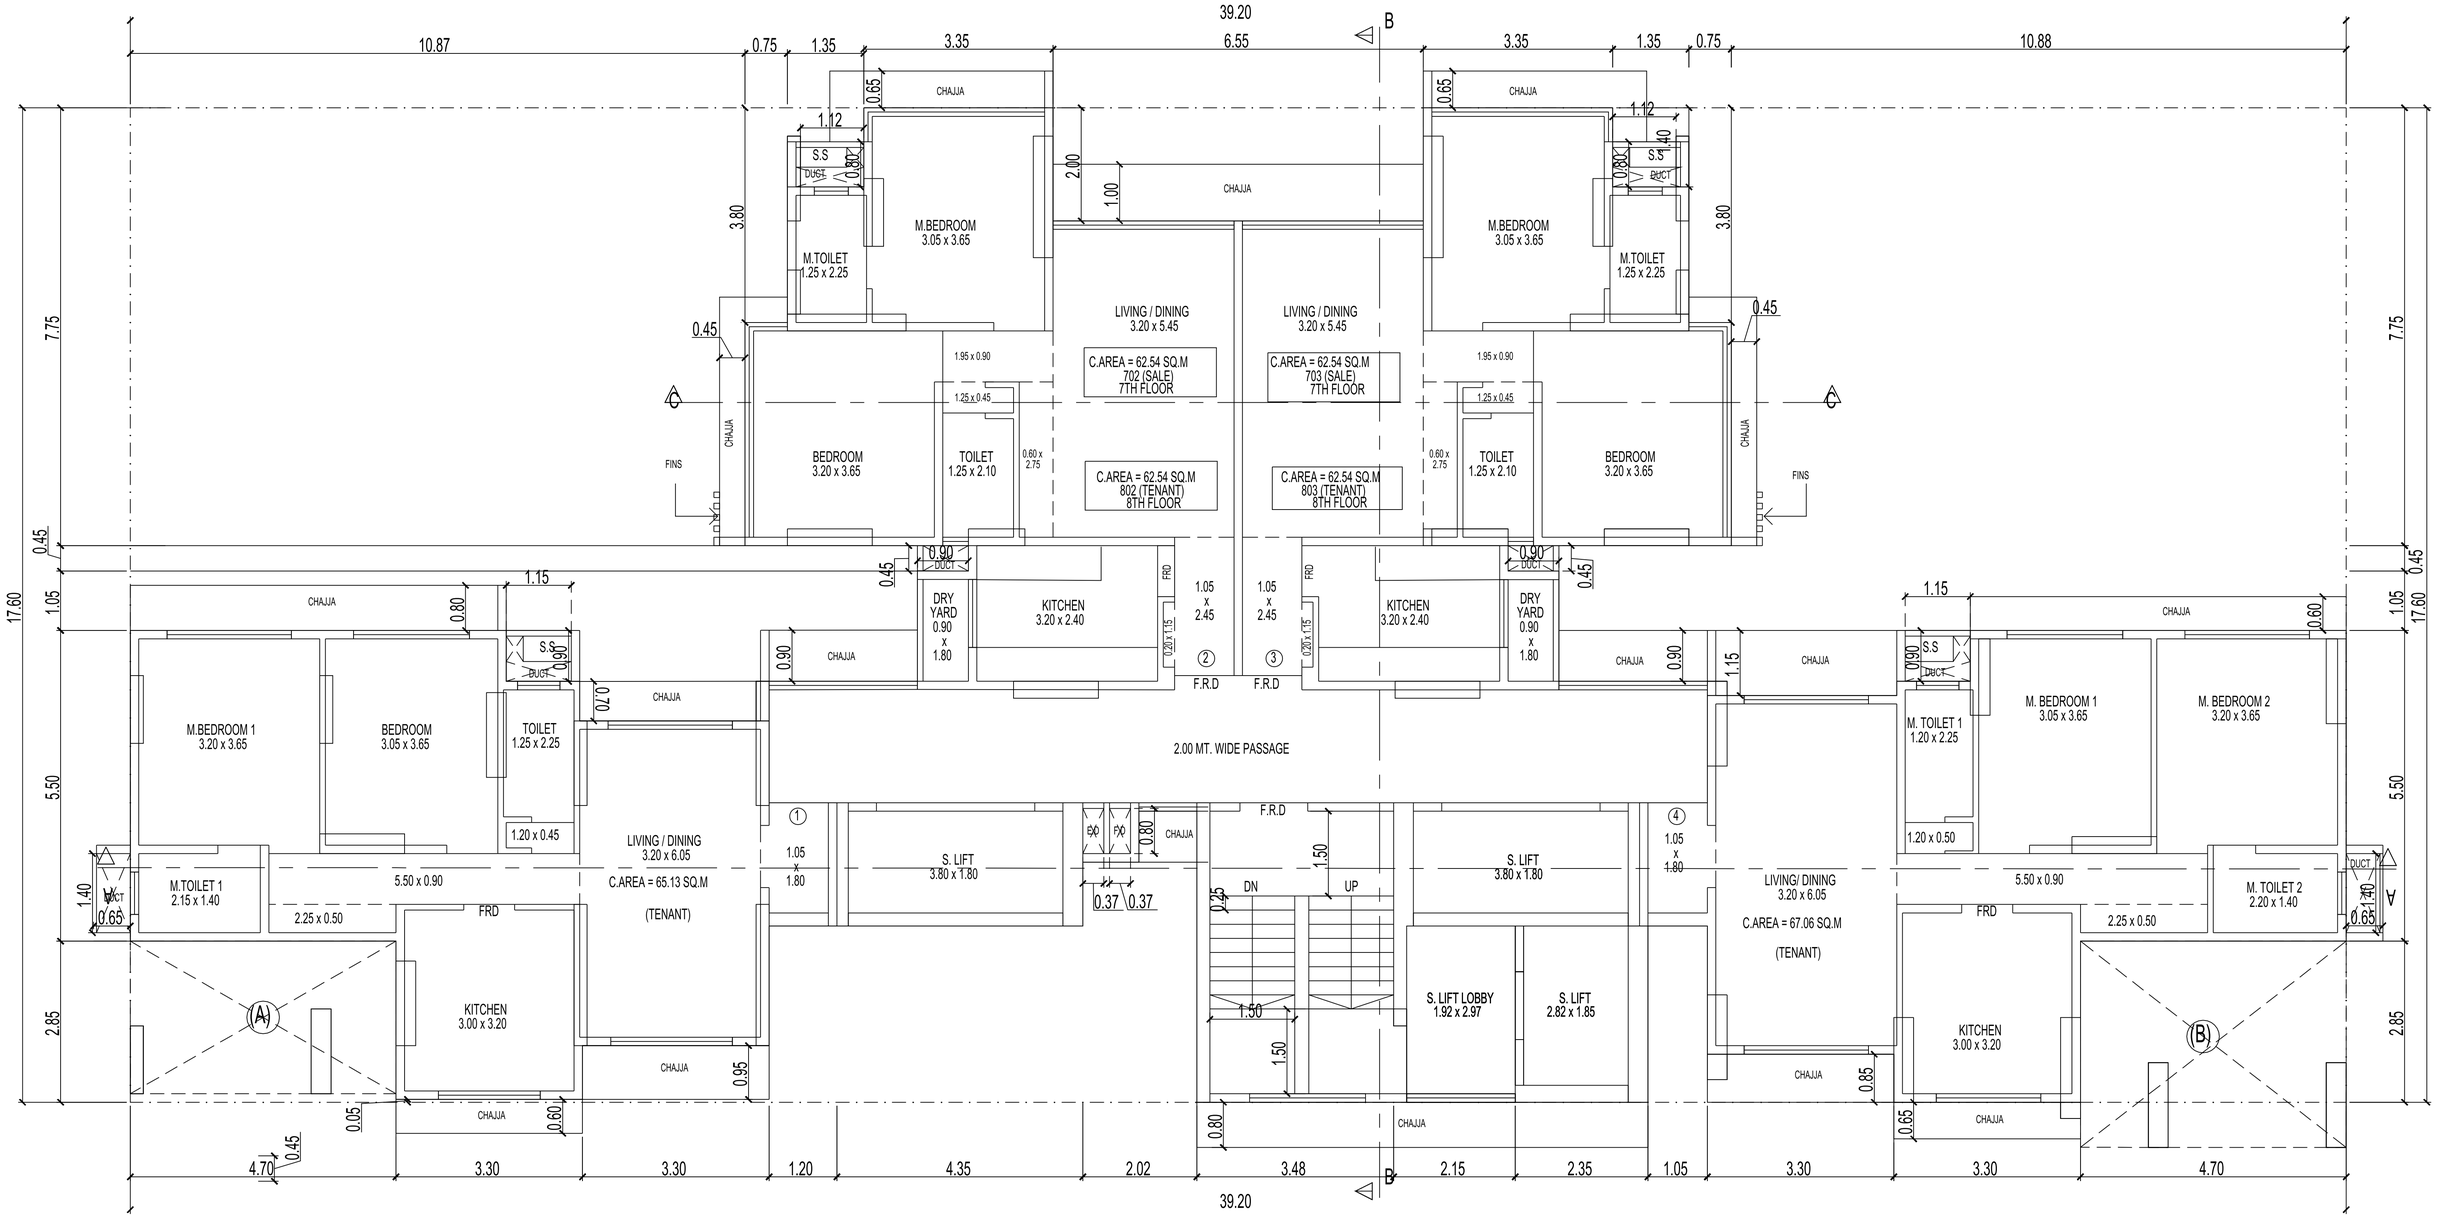

7TH & 8TH FLOOR PLAN


SCALE:-1:100

NOTE:- 702 & 703 - SALE FLATS
802 & 803 - REHAB FLATS

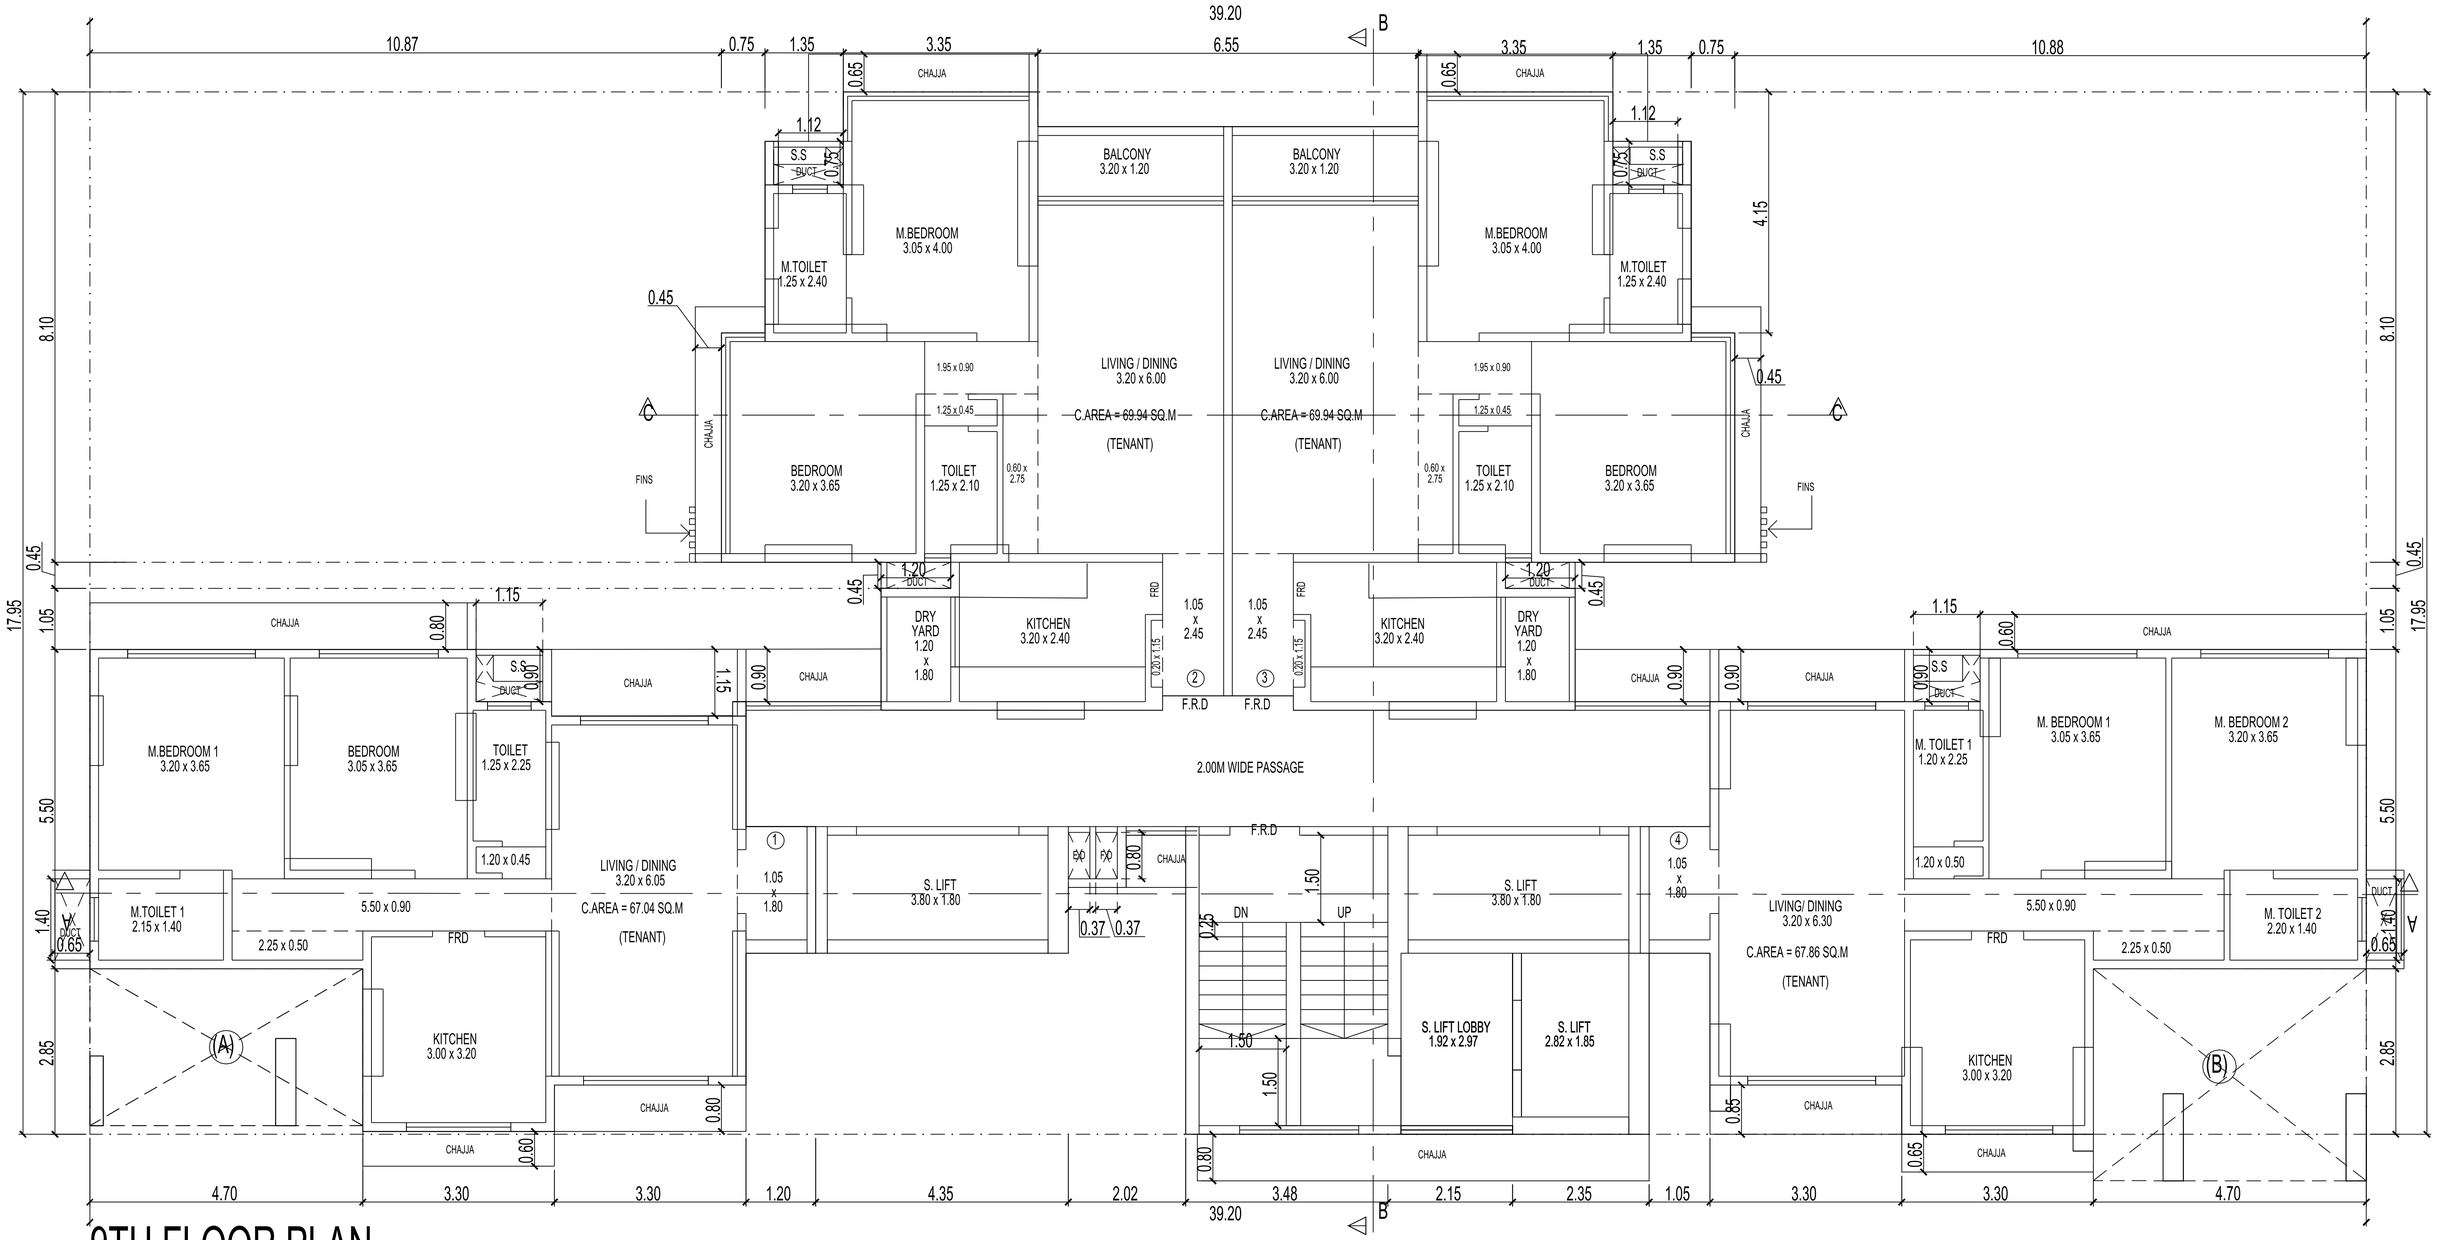


9TH FLOOR PLAN

SCALE:-1:100

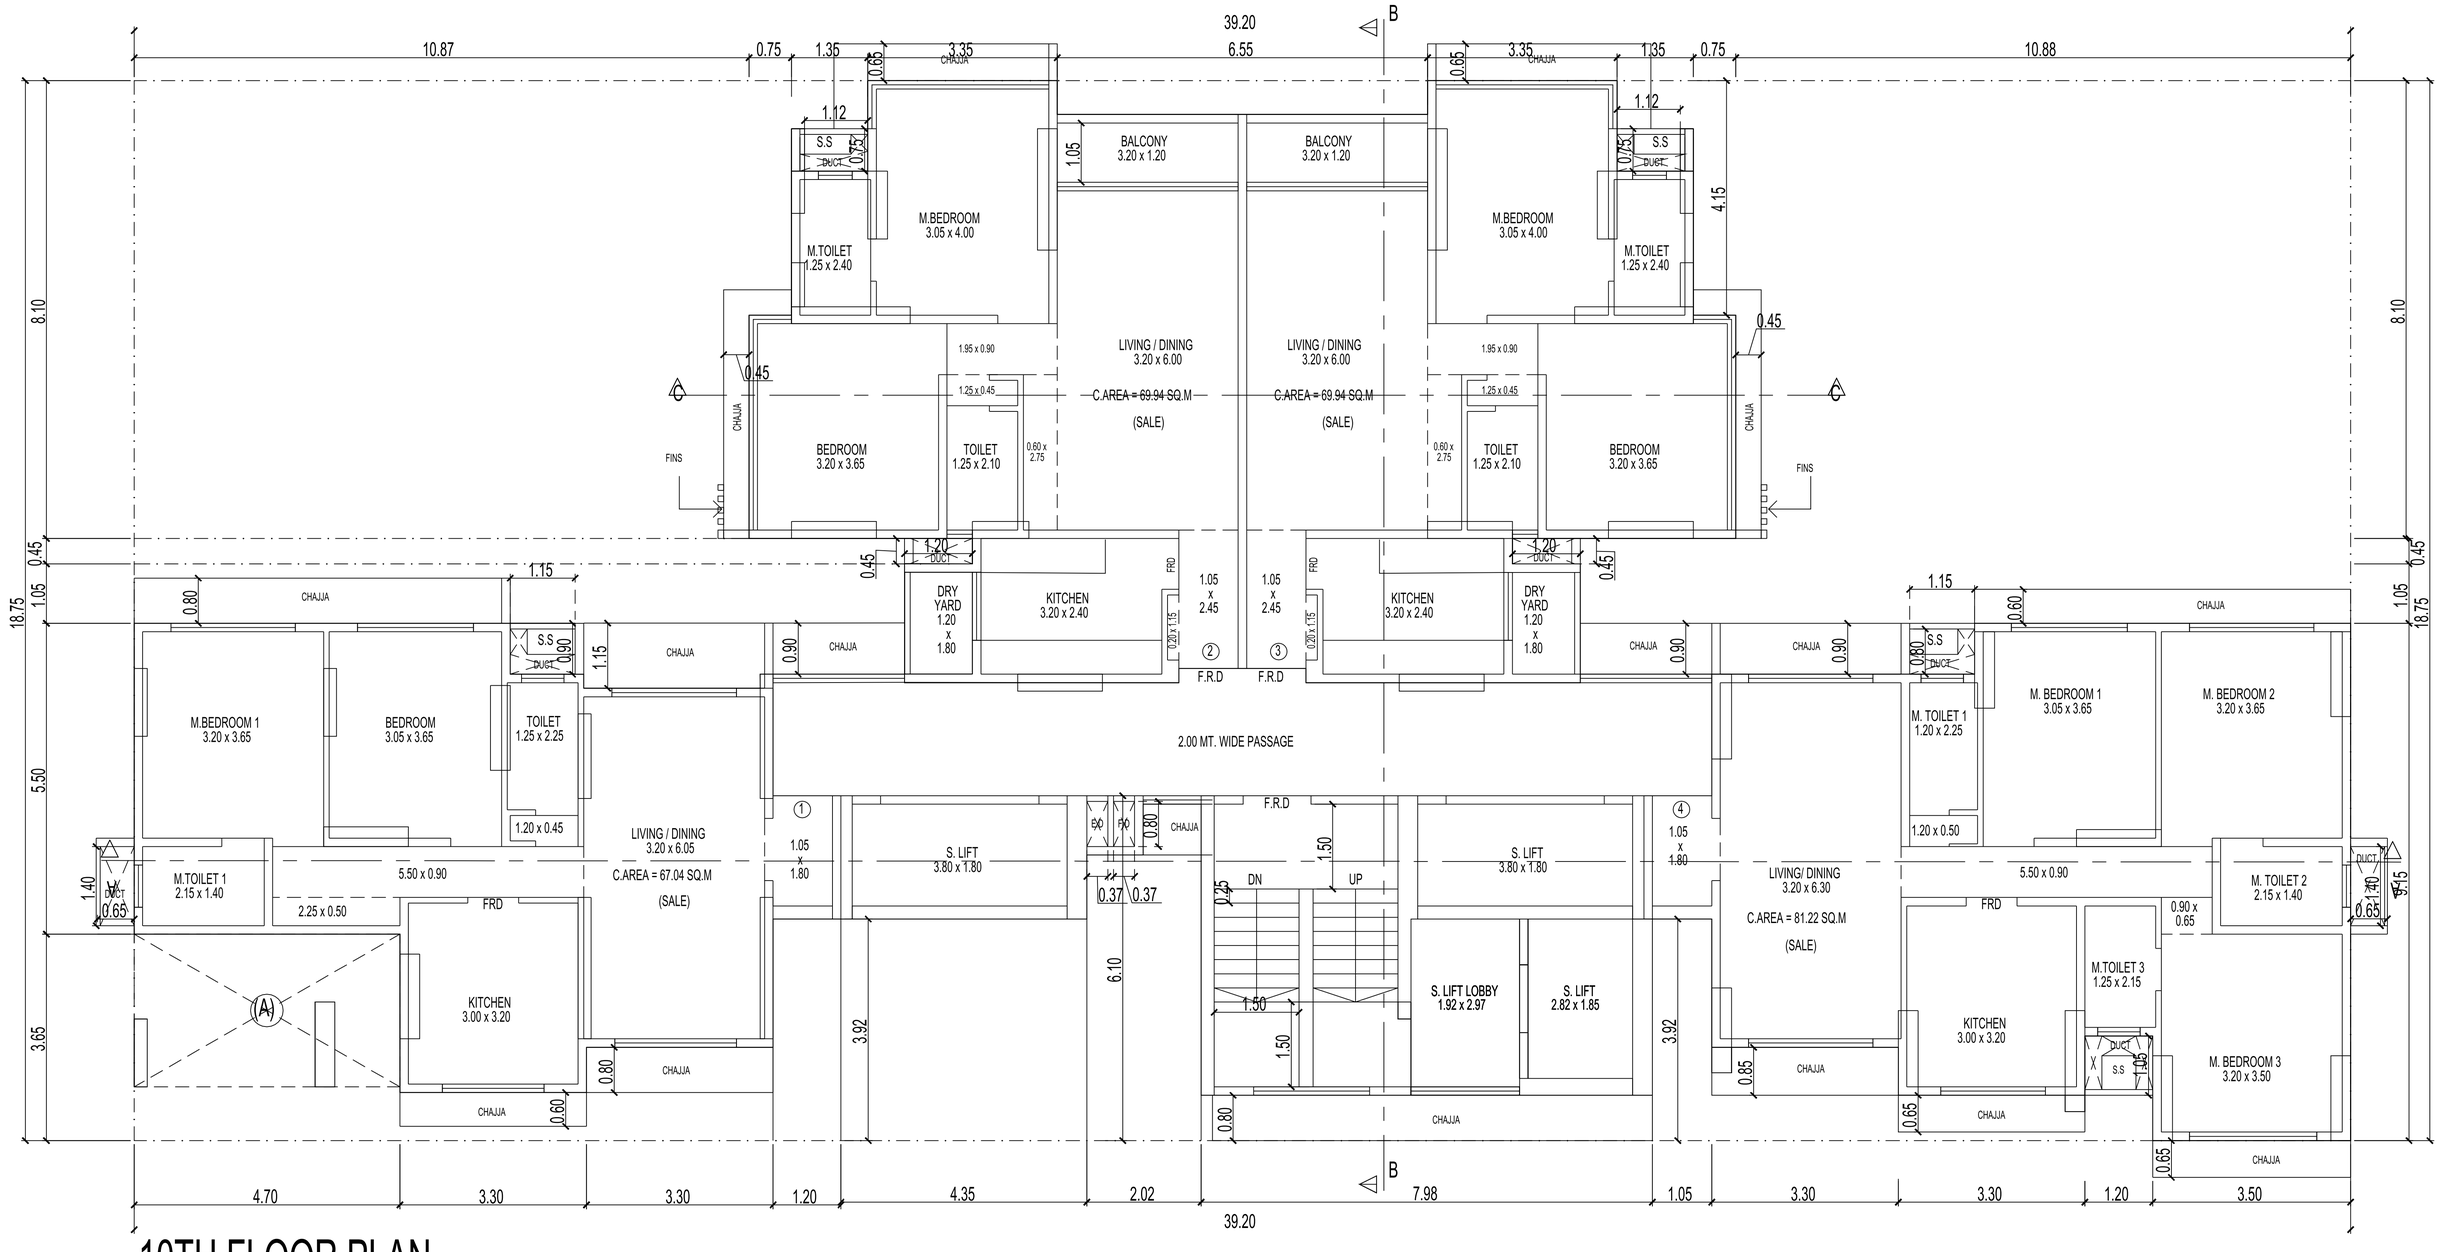


10TH FLOOR PLAN

SCALE:-1:100

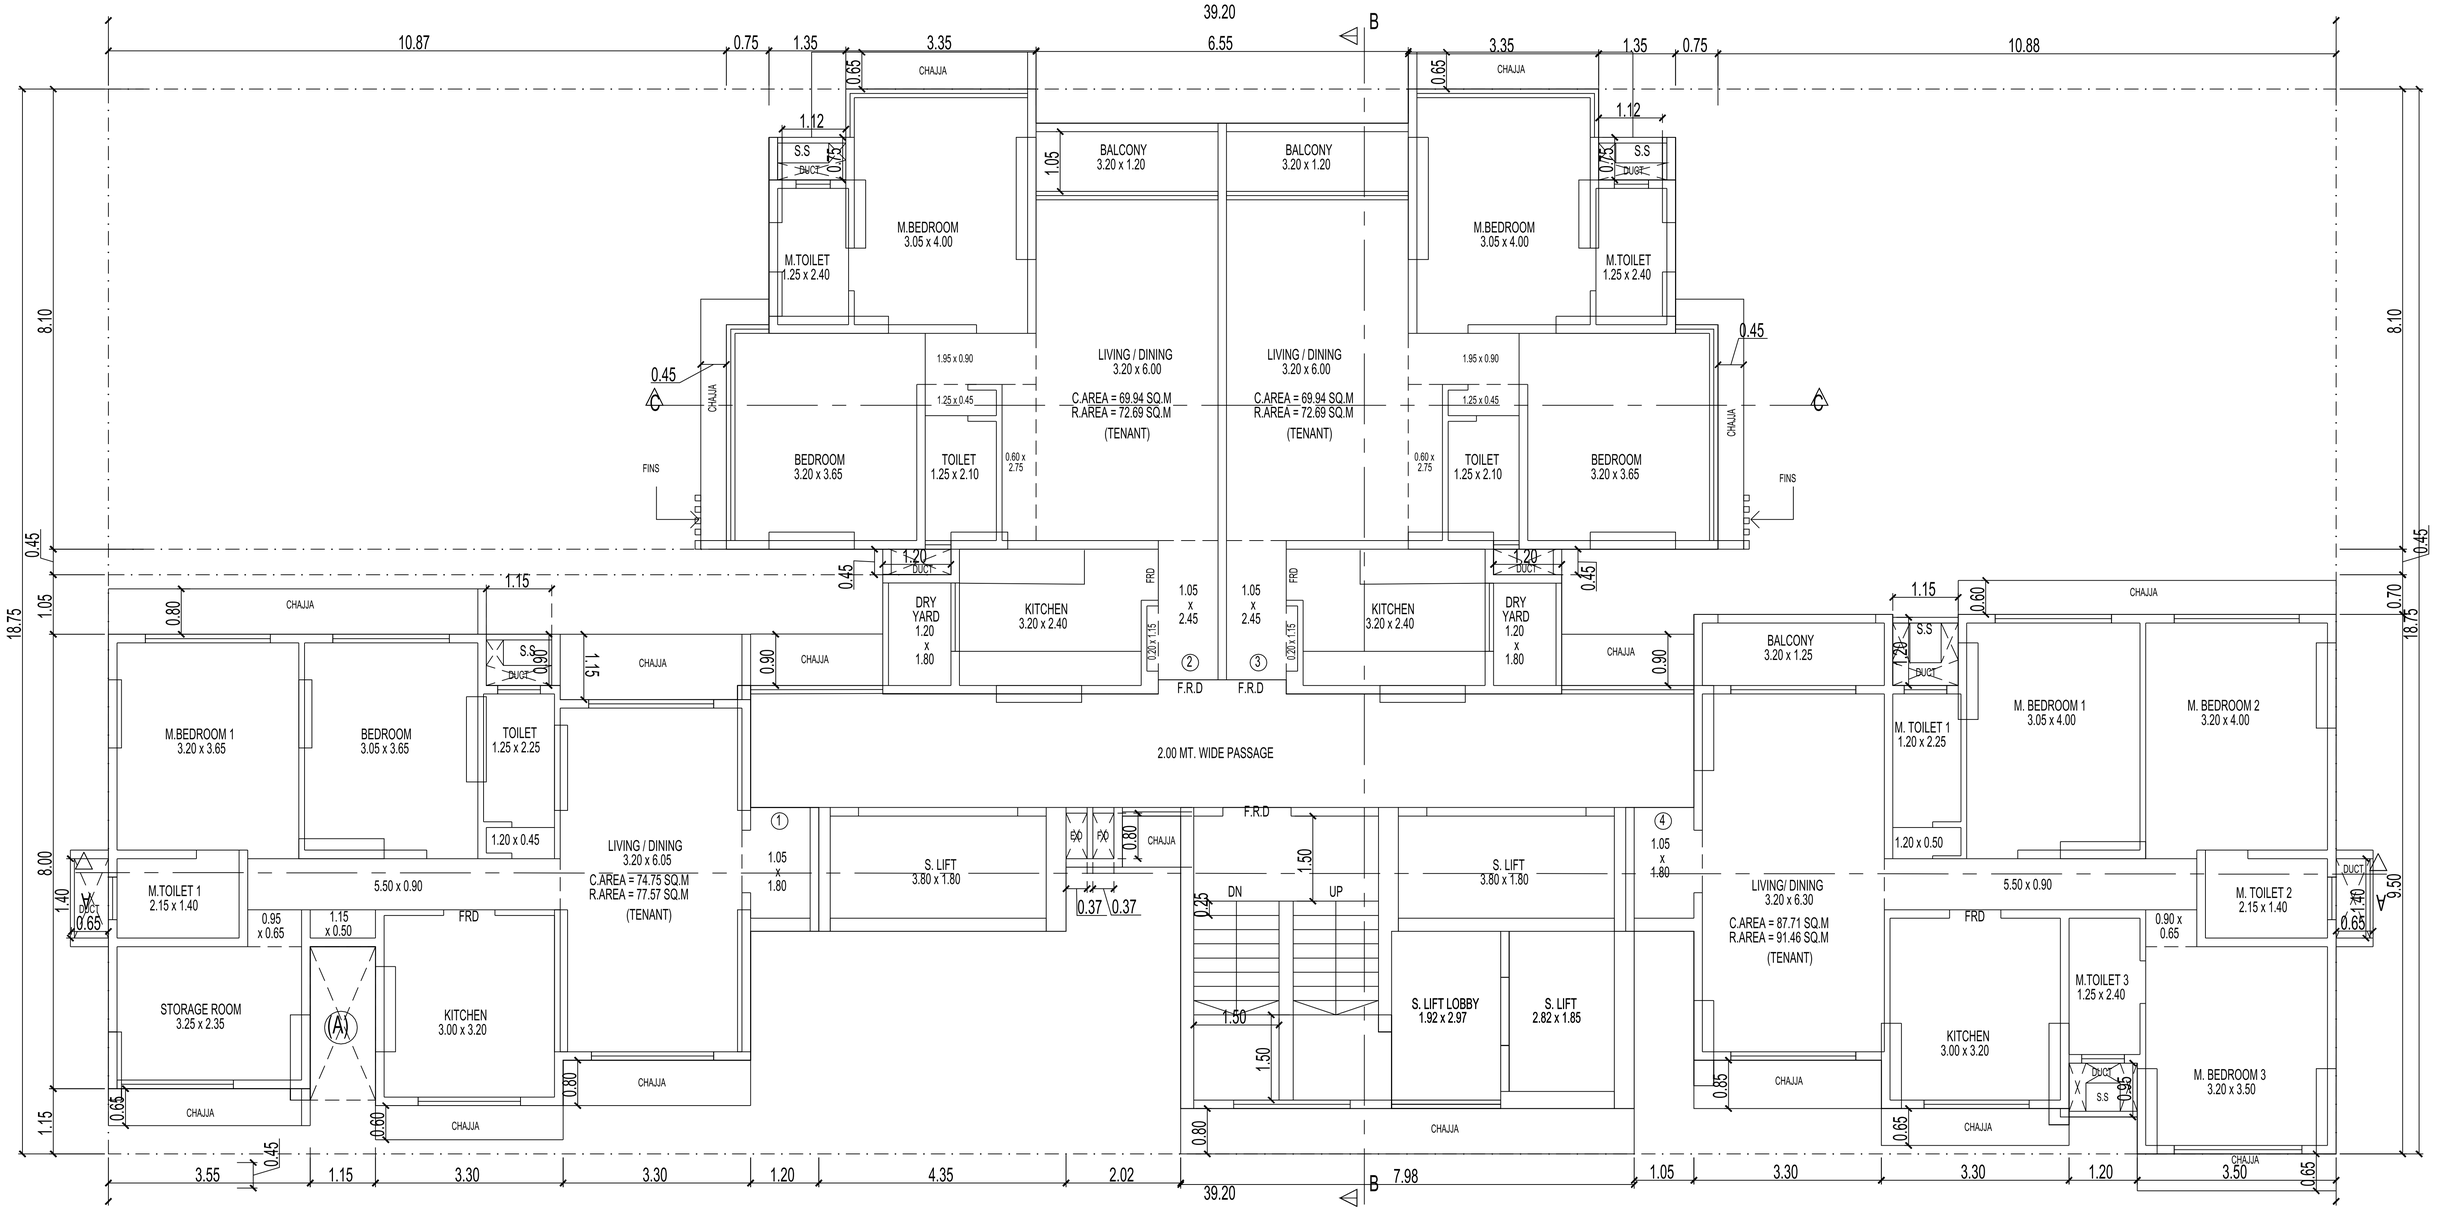

39.20
B
10.87
0.75
1.35
3.35
6.55
3.35
1.35
0.75
10.88
CHAJJA
0.65
1.12
S.S
DUCT
0.75
BALCONY
3.20 x 1.20
1.05
M.BEDROOM
3.05 x 4.00
M.TOILET
1.25 x 2.40
LIVING / DINING
3.20 x 6.00
C.AREA = 69.94 SQ.M
R.AREA = 72.69 SQ.M
(TENANT)
1.95 x 0.90
1.25 x 0.45
0.60 x
2.75
BEDROOM
3.20 x 3.65
TOILET
1.25 x 2.10
FINS
0.45
C
8.10
1.20
DUCT
DRY
YARD
1.20
x
1.80
KITCHEN
3.20 x 2.40
FRD
1.05
x
2.45
0.20 x 1.15
F.R.D
2.00 MT. WIDE PASSAGE
1.15
0.80
0.90
M.BEDROOM 1
3.20 x 3.65
BEDROOM
3.05 x 3.65
TOILET
1.25 x 2.25
1.20 x 0.45
LIVING / DINING
3.20 x 6.05
C.AREA = 74.75 SQ.M
R.AREA = 77.57 SQ.M
(TENANT)
18.75
1.40
M.TOILET 1
2.15 x 1.40
5.50 x 0.90
0.95
x 0.65
1.15
x 0.50
STORAGE ROOM
3.25 x 2.35
KITCHEN
3.00 x 3.20
A
1.15
0.65
0.60
1
S. LIFT
3.80 x 1.80
F.R.D
0.80
0.37
0.37
0.25
DN
UP
1.50
S. LIFT LOBBY
1.92 x 2.97
S. LIFT
2.82 x 1.85
4
BALCONY
3.20 x 1.25
1.28
M. BEDROOM 1
3.05 x 4.00
M. BEDROOM 2
3.20 x 4.00
M. TOILET 1
1.20 x 2.25
1.20 x 0.50
LIVING/ DINING
3.20 x 6.30
C.AREA = 87.71 SQ.M
R.AREA = 91.46 SQ.M
(TENANT)
M. TOILET 2
2.15 x 1.40
0.90 x
0.65
M.TOILET 3
1.25 x 2.40
KITCHEN
3.00 x 3.20
M. BEDROOM 3
3.20 x 3.50
0.70
9.50
3.55
1.15
3.30
3.30
1.20
4.35
2.02
7.98
1.05
3.30
3.30
1.20
3.50
0.65
39.20

SCALE:-1:100

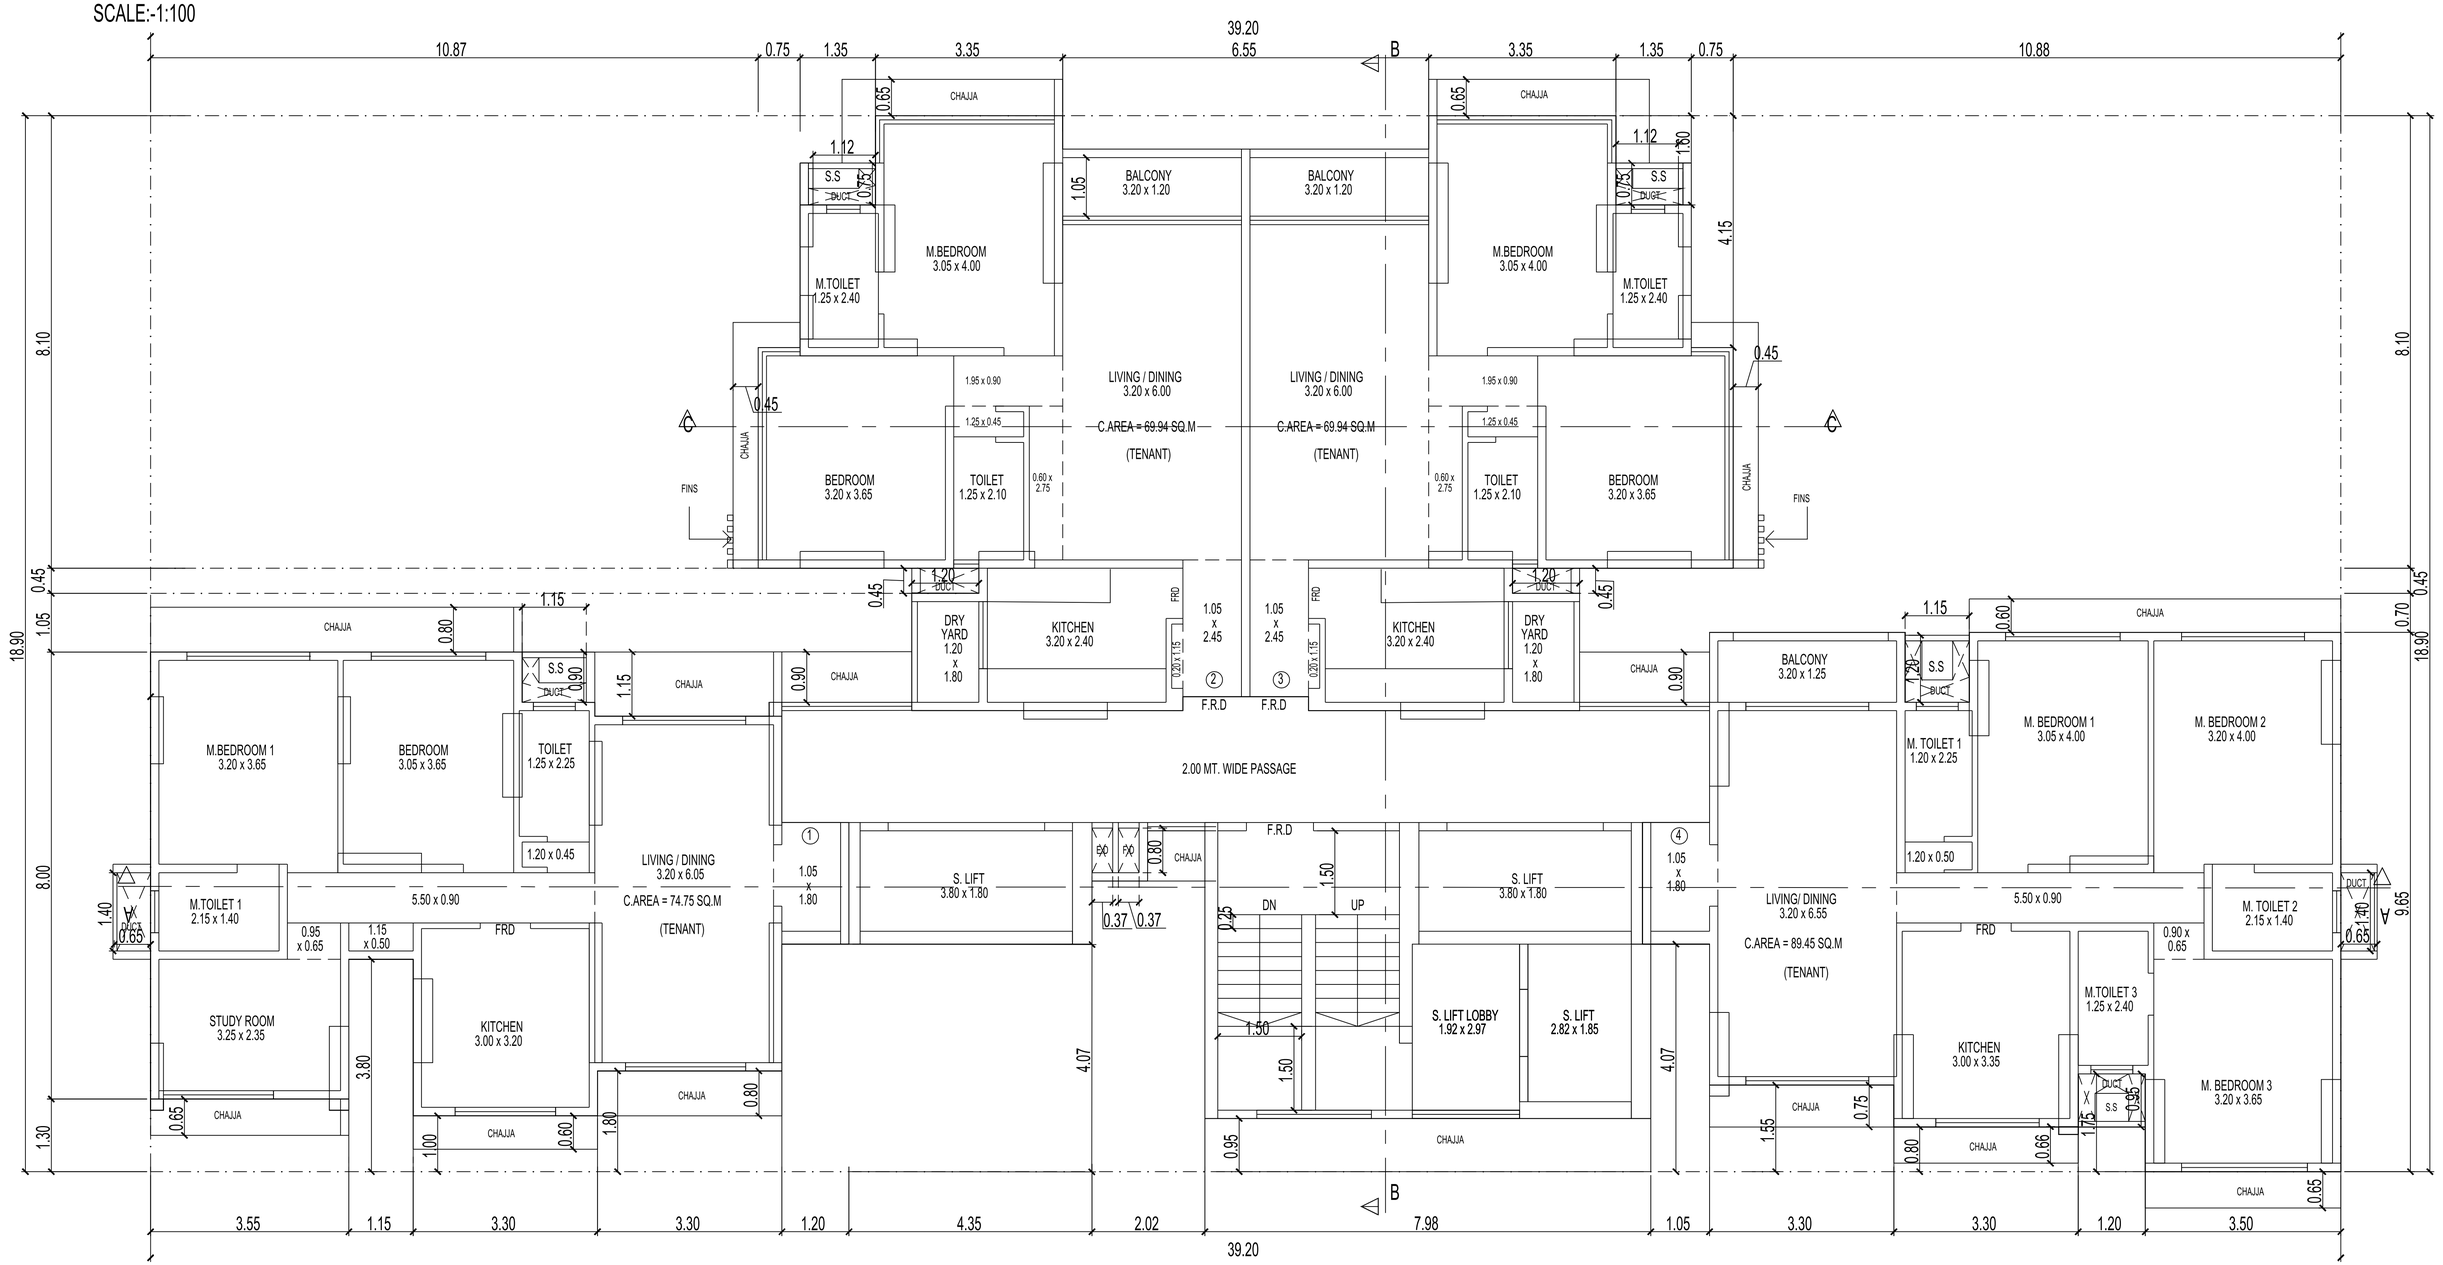


12TH FLOOR PLAN

SCALE:-1:100

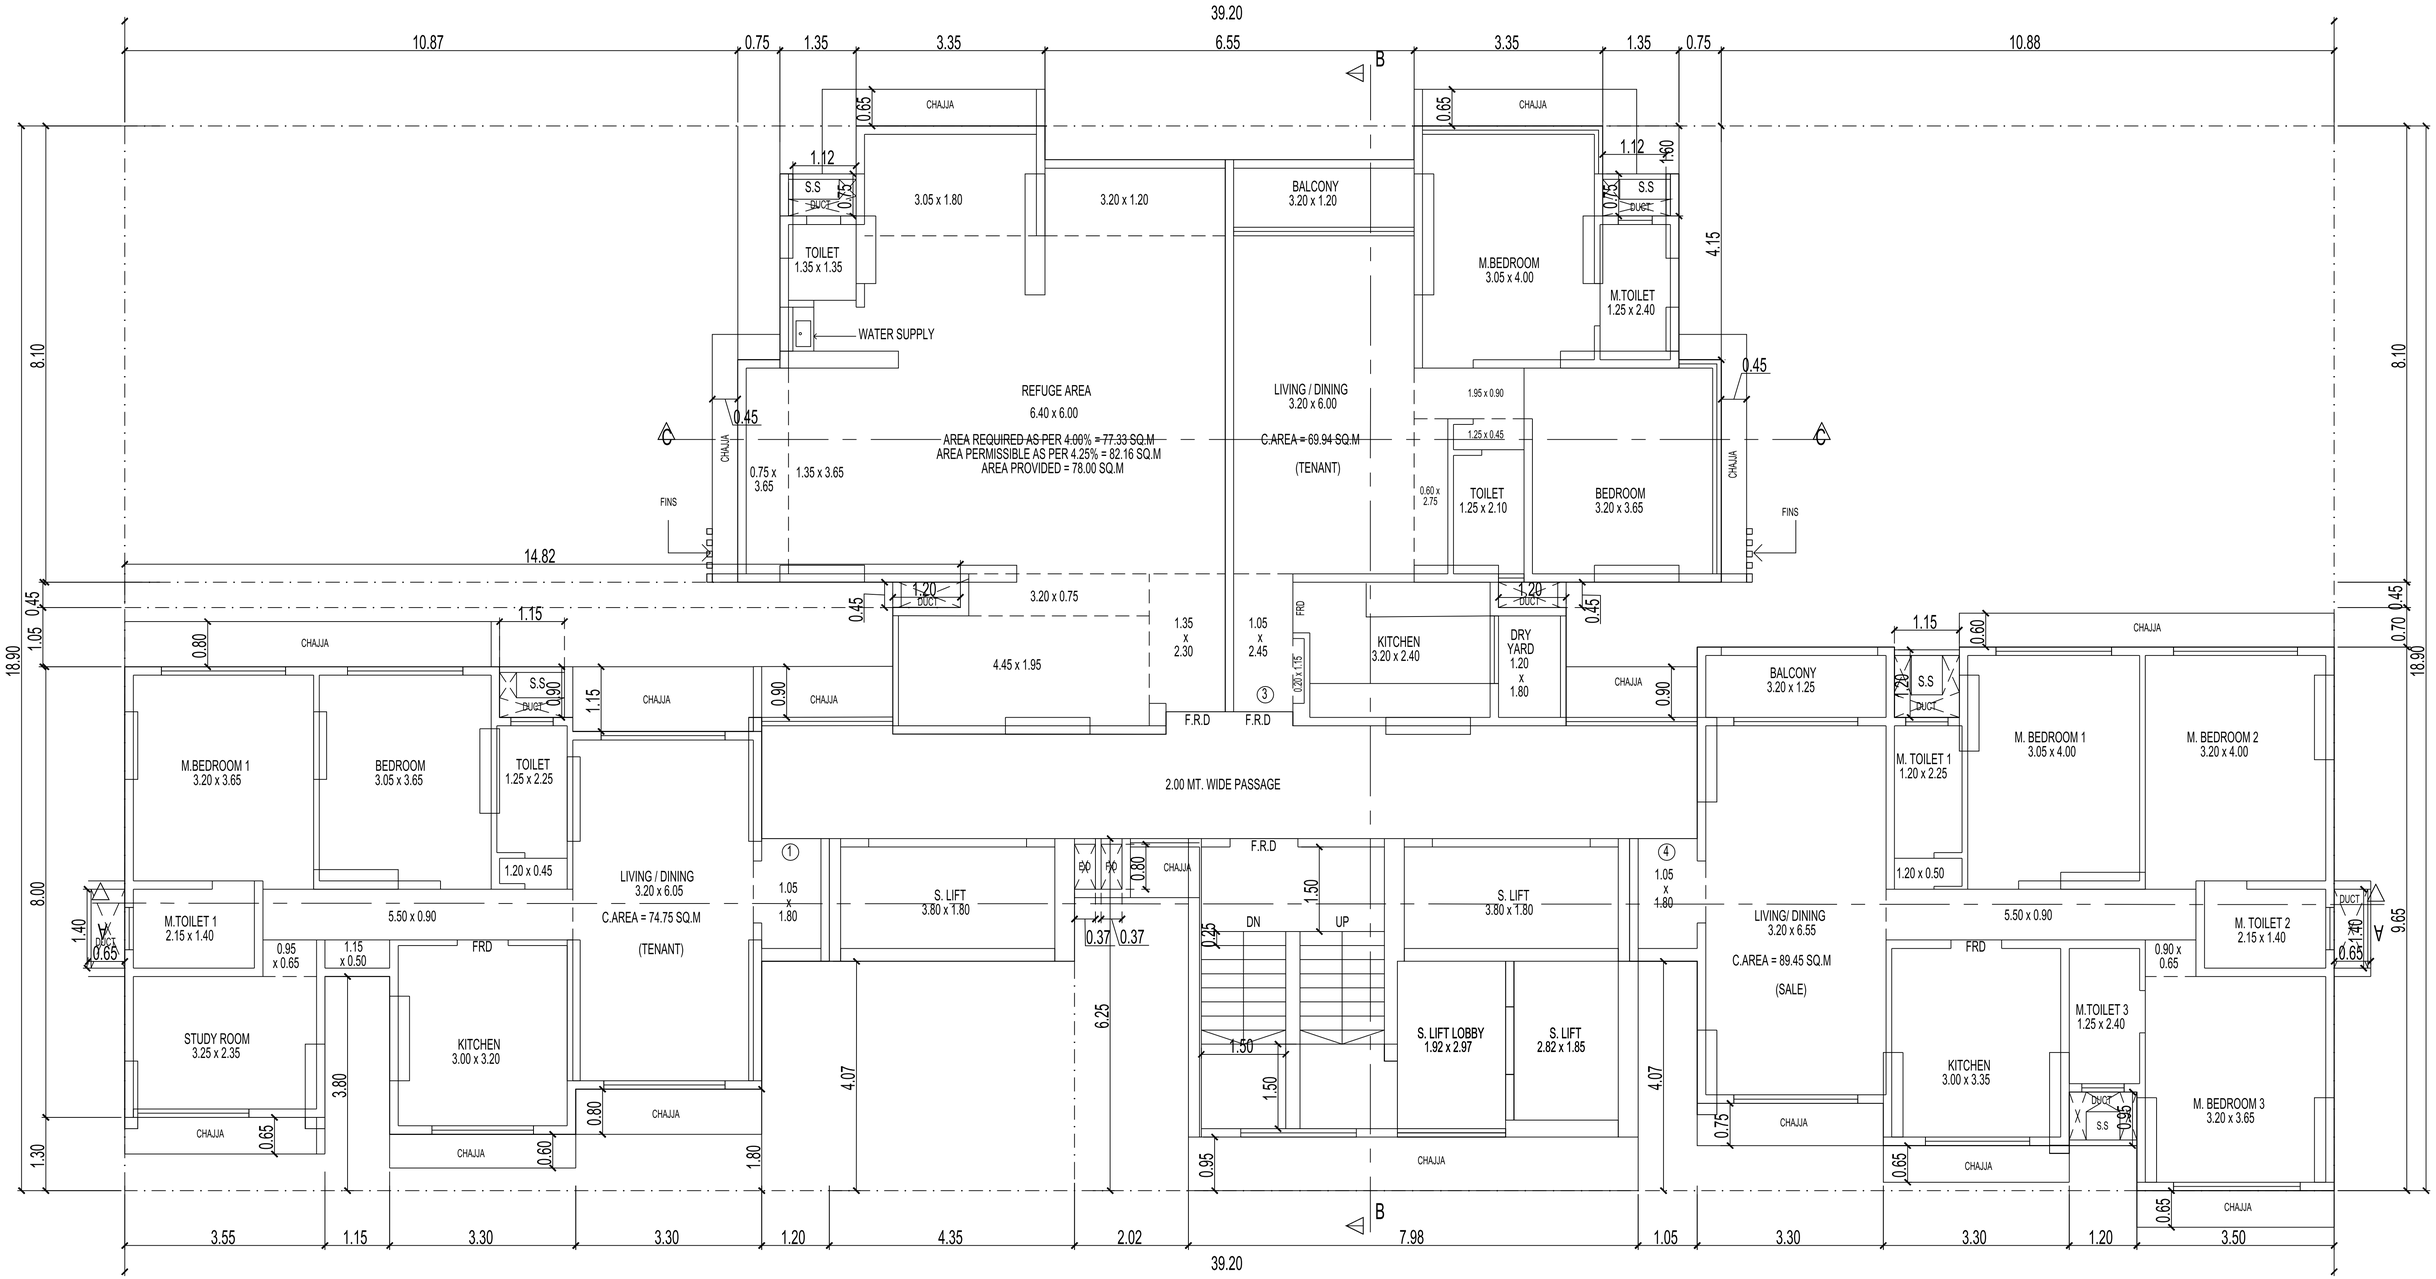


13TH FLOOR PLAN

SCALE:-1:100

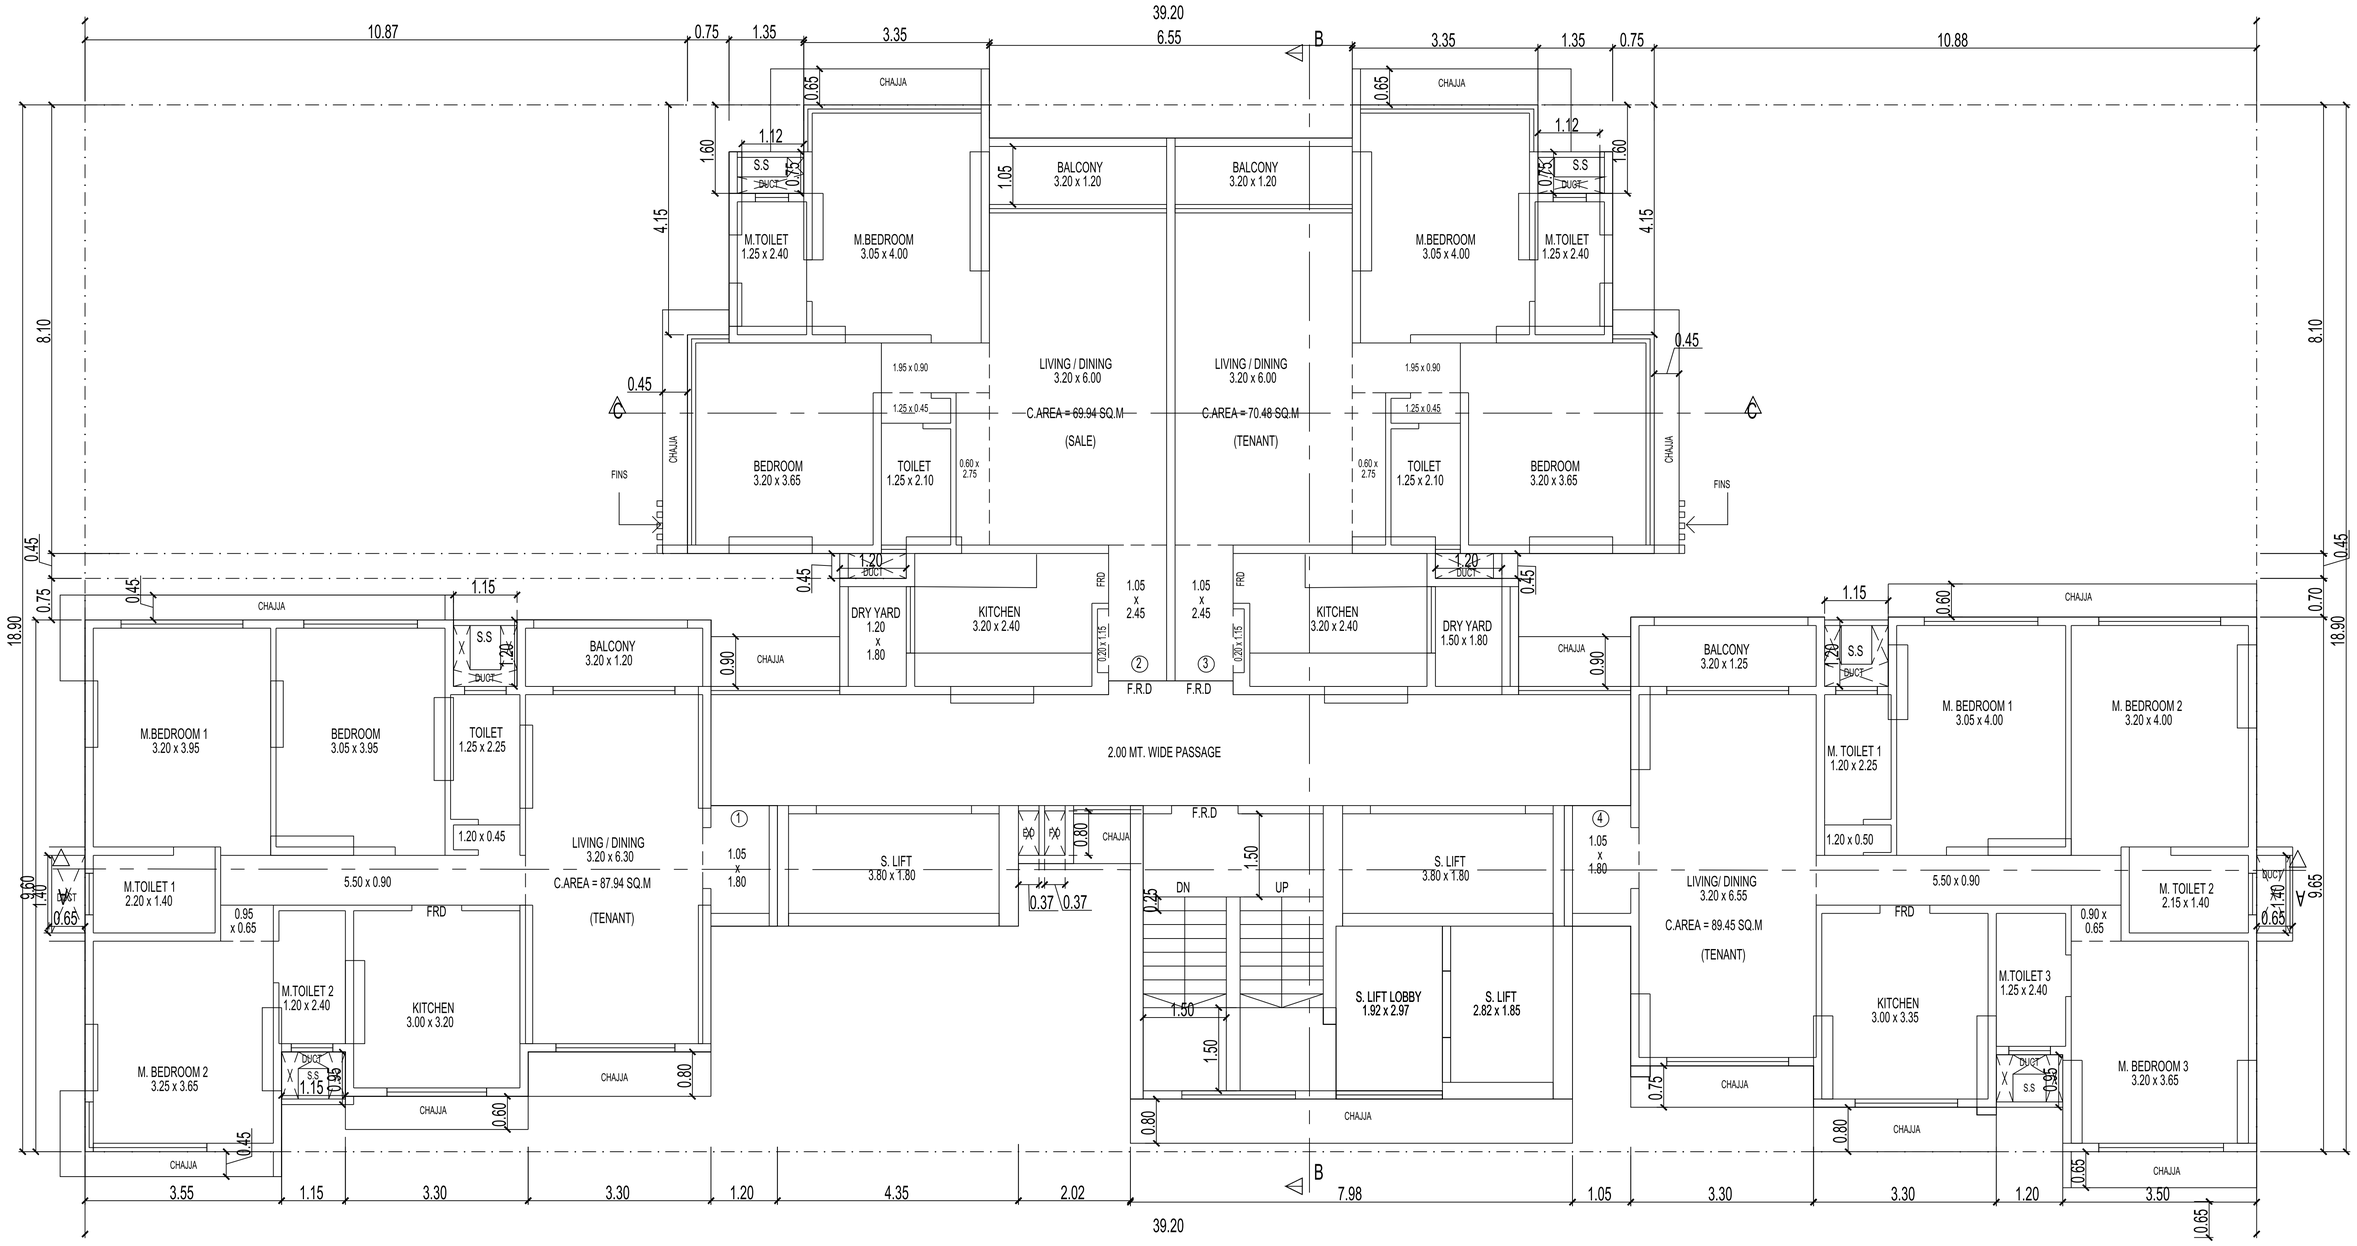


14TH FLOOR PLAN

SCALE:-1:100

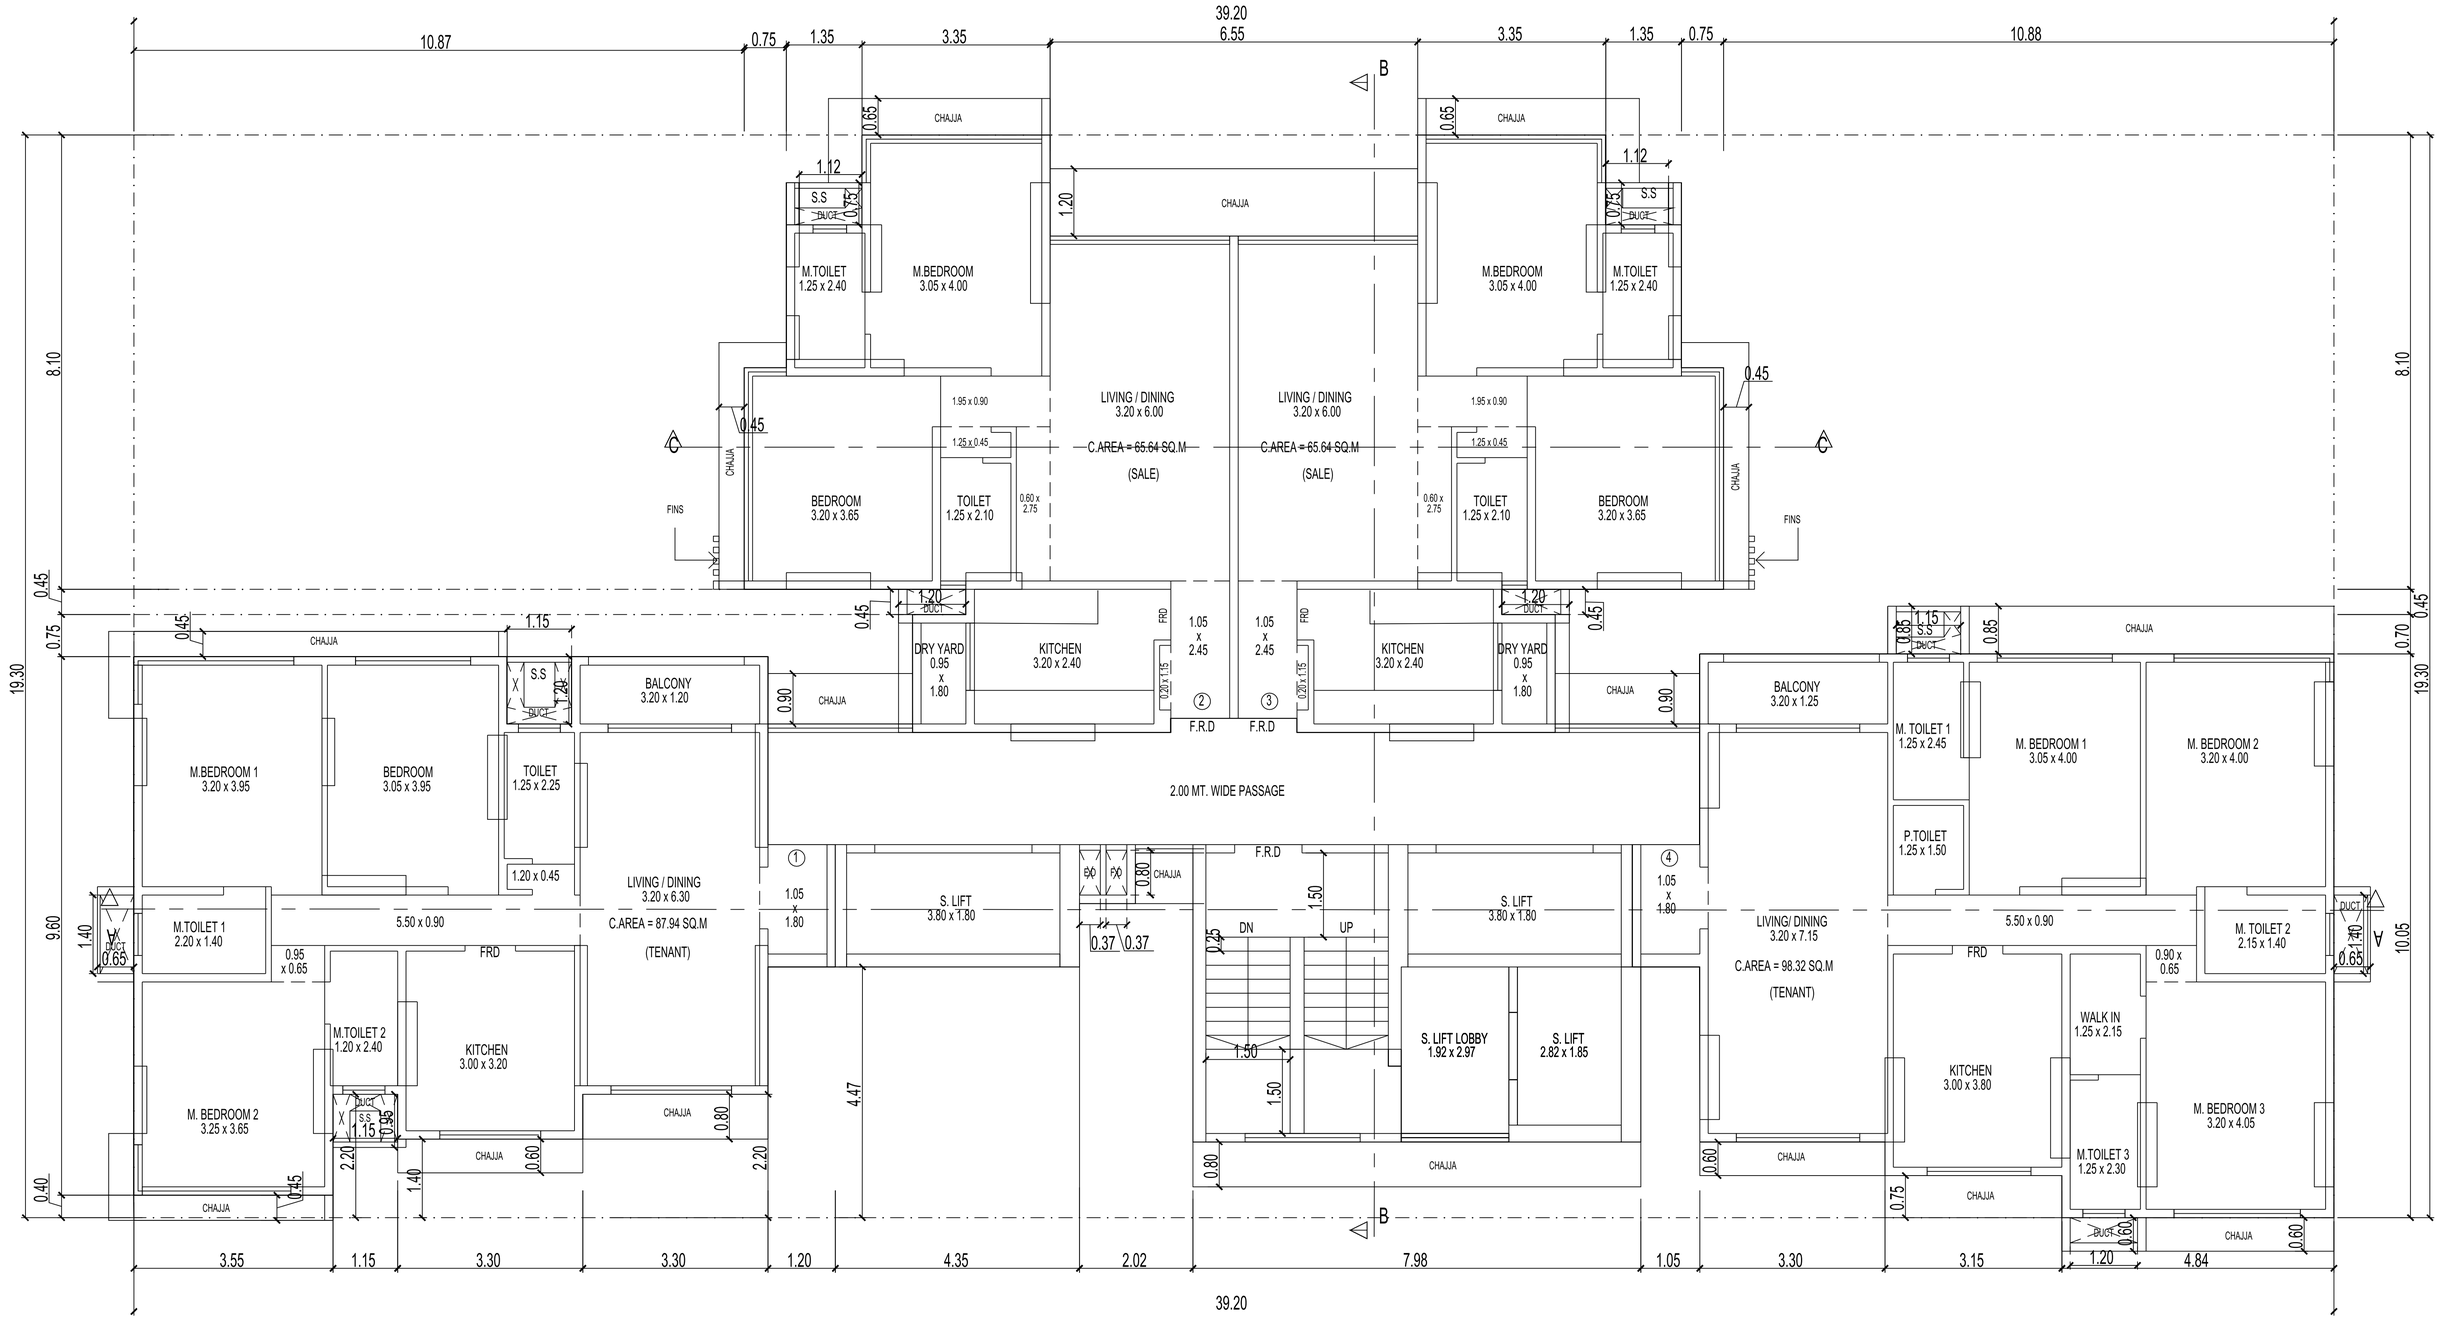

15TH FLOOR PLAN

SCALE:-1:100

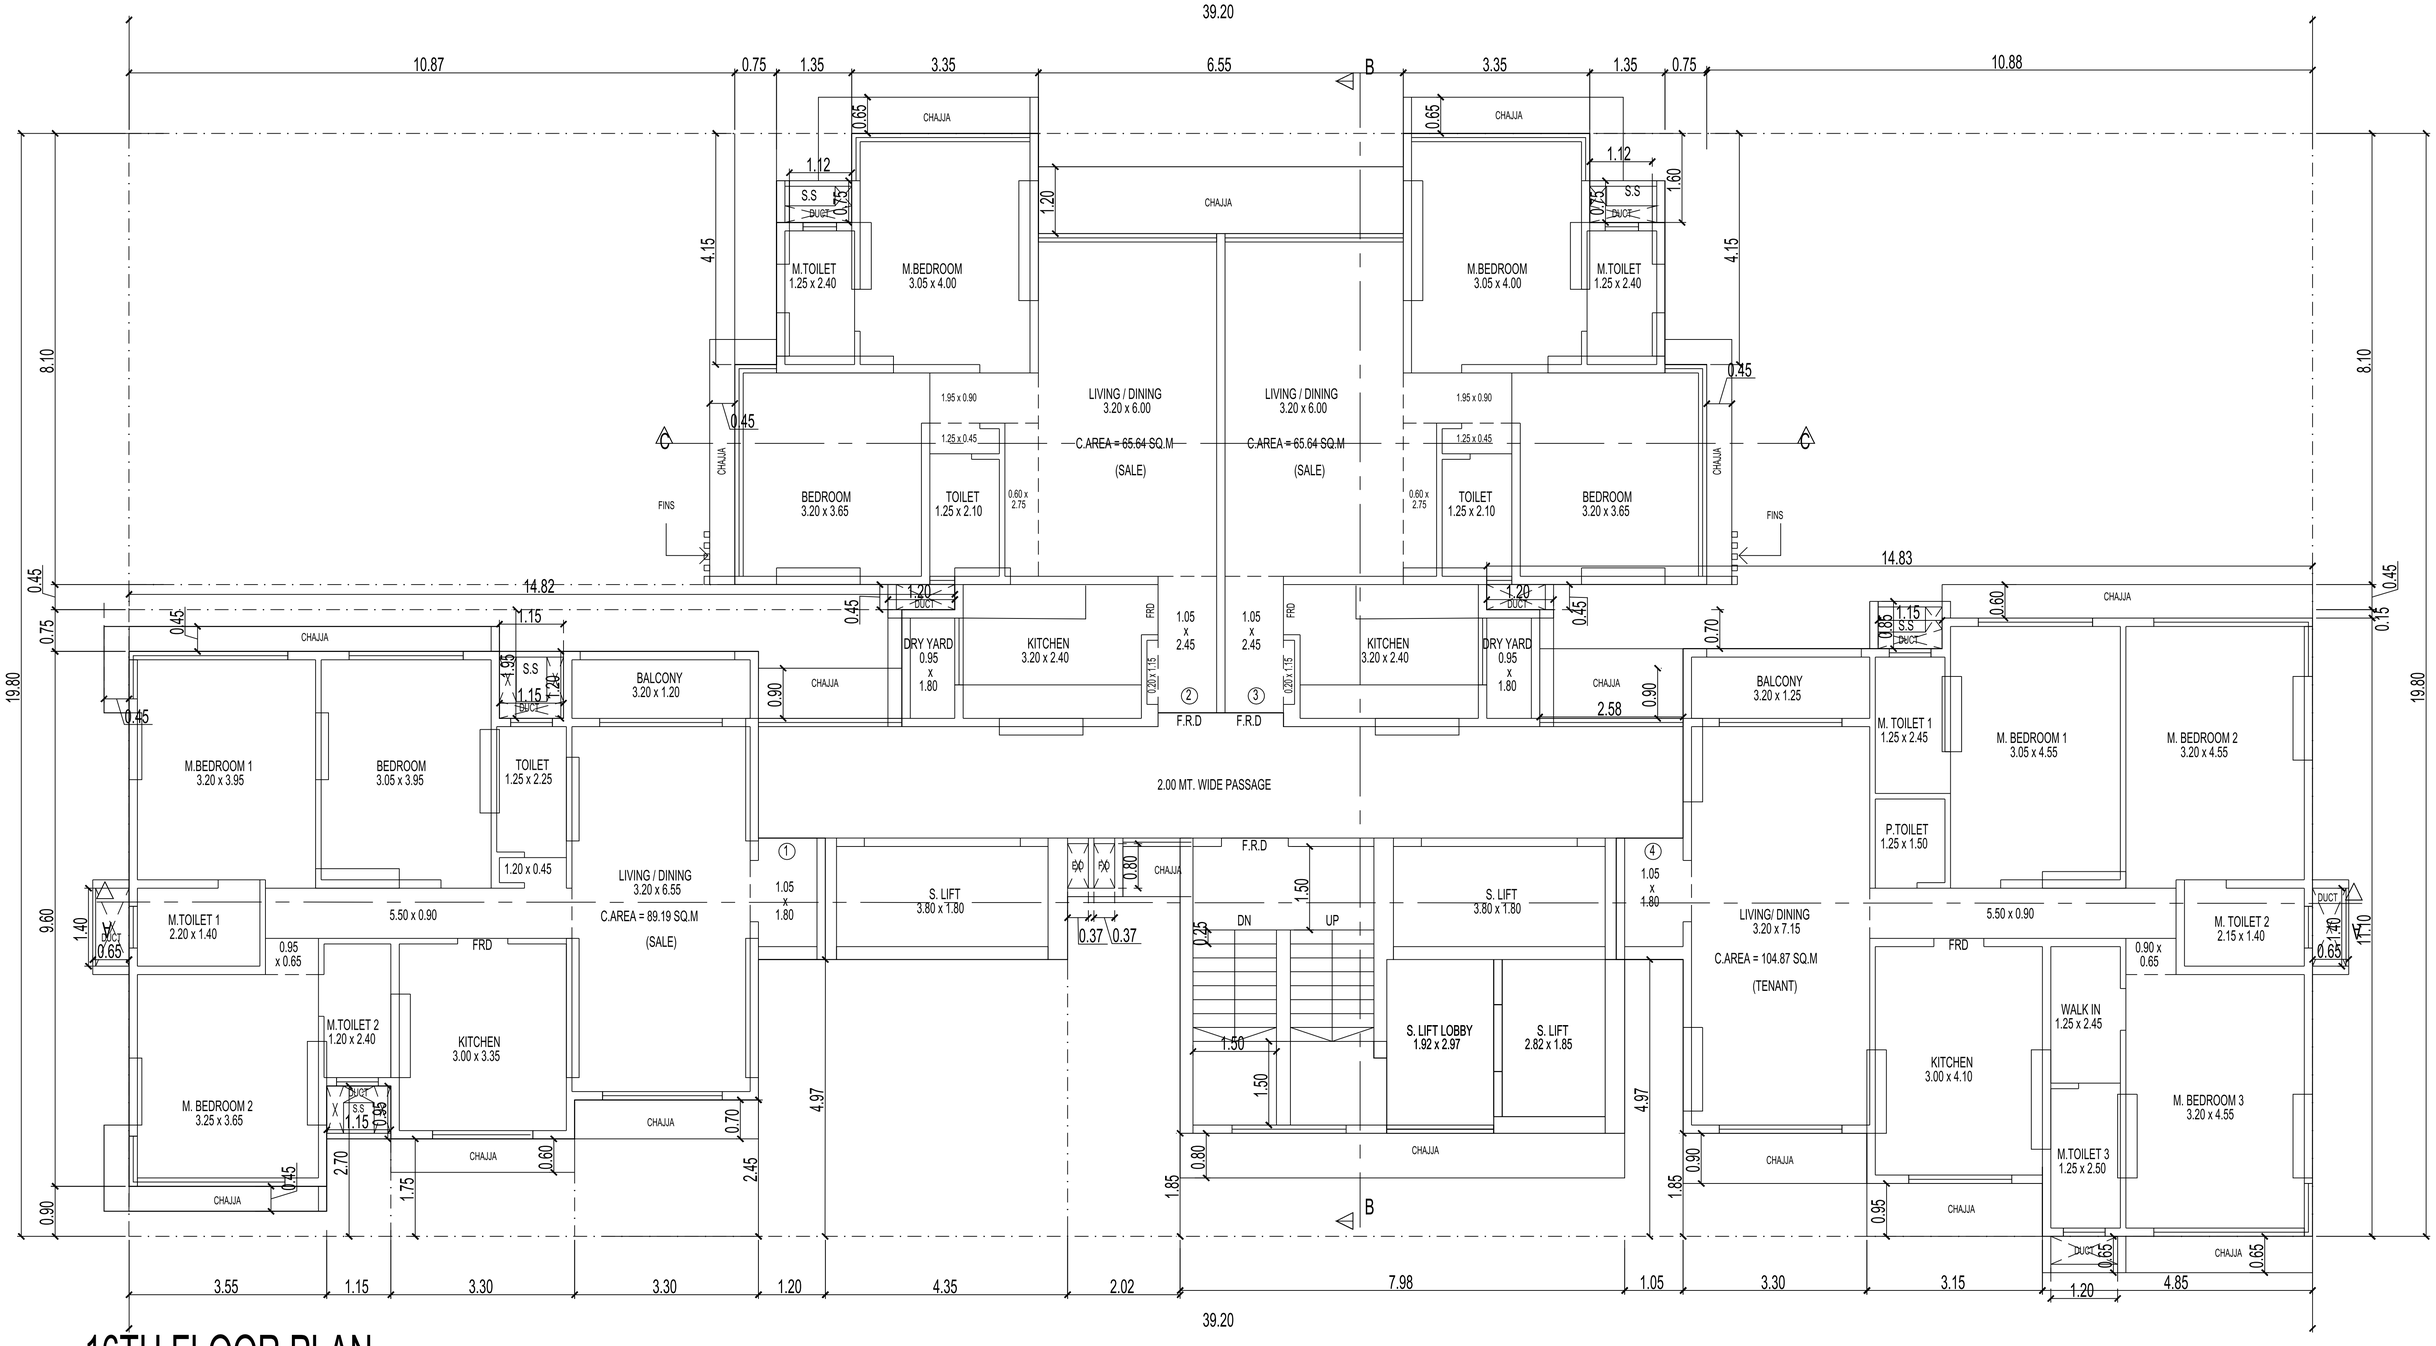

16TH FLOOR PLAN

SCALE:-1:100

17TH FLOOR PLAN

39.20

10.87 | 0.75 | 1.35 | 3.35 | 6.55 | 3.35 | 1.35 | 0.75 | 10.88

B

CHAJJA 0.65 | 1.12 S.S DUCT 0.75 | 1.20 CHAJJA | 1.12 S.S DUCT 1.60 | 0.75 CHAJJA 0.65

M.TOILET 1.25 x 2.40 | M.BEDROOM 3.05 x 4.00 | M.BEDROOM 3.05 x 4.00 | M.TOILET 1.25 x 2.40

4.15 | 4.15

8.10 | 8.10

0.45 | 0.45

C | C

CHAJJA | 1.95 x 0.90 | 1.25 x 0.45 | CHAJJA

BEDROOM 3.20 x 3.65 | TOILET 1.25 x 2.10 | 0.60 x 2.75 | LIVING / DINING 3.20 x 6.00 C.AREA = 65.64 SQ.M (SALE) | LIVING / DINING 3.20 x 6.00 C.AREA = 65.64 SQ.M (SALE) | 0.60 x 2.75 | TOILET 1.25 x 2.10 | BEDROOM 3.20 x 3.65

FINS | FINS

14.82 | 14.83

0.45 | 6.65 | 0.45 | 1.15 | 0.75 | 3.50 | 0.45 | 1.20 DUCT | 1.05 x 2.45 | 1.05 x 2.45 | 1.20 DUCT | 0.70 | 0.45 | 0.85 | 1.15 S.S DUCT | 0.60 | CHAJJA | 0.15 | 0.45

CHAJJA | 1.95 S.S 1.20 DUCT | BALCONY 3.20 x 1.20 | 0.90 CHAJJA | DRY YARD 0.95 x 1.80 | KITCHEN 3.20 x 2.40 | F.R.D 0.20 x 1.15 | F.R.D | F.R.D | KITCHEN 3.20 x 2.40 | DRY YARD 0.95 x 1.80 | CHAJJA 2.58 | 0.90 | BALCONY 3.20 x 1.25 | M. TOILET 1 1.25 x 2.45 | M. BEDROOM 1 3.05 x 4.55 | M. BEDROOM 2 3.20 x 4.55

2.00 MT. WIDE PASSAGE

19.80 | P.TOILET 1.25 x 1.50 | 19.80

M.BEDROOM 1 3.20 x 3.95 | BEDROOM 3.05 x 3.95 | TOILET 1.25 x 2.25 | 1.20 x 0.45 | LIVING / DINING 3.20 x 6.55 C.AREA = 89.19 SQ.M (TENANT) | 1 | 1.05 x 1.80 | S. LIFT 3.80 x 1.80 | 0.80 | 0.80 | CHAJJA | F.R.D | 1.50 | S. LIFT 3.80 x 1.80 | 4 | 1.05 x 1.80 | LIVING/ DINING 3.20 x 7.15 C.AREA = 104.87 SQ.M (TENANT)

9.60 | 1.40 | 5.50 x 0.90 | 5.50 x 0.90 | 1.40

DUCT 0.65 | M.TOILET 1 2.20 x 1.40 | 0.95 x 0.65 | FRD | 0.37 | 0.37 | 0.25 | DN | UP | 1.50 | 0.90 x 0.65 | M. TOILET 2 2.15 x 1.40 | DUCT 0.65

M.TOILET 2 1.20 x 2.40 | KITCHEN 3.00 x 3.35 | S.S DUCT 1.15 0.95 | S. LIFT LOBBY 1.92 x 2.97 | S. LIFT 2.82 x 1.85 | KITCHEN 3.00 x 4.10 | WALK IN 1.25 x 2.45 | M. BEDROOM 3 3.20 x 4.55

M. BEDROOM 2 3.25 x 3.65 | 4.97 | 1.50 | M.TOILET 3 1.25 x 2.50

CHAJJA | 0.45 | 2.70 | 1.75 | CHAJJA | 0.60 | 2.45 | CHAJJA 0.70 | CHAJJA 0.80 | CHAJJA 0.90 | CHAJJA 0.95

0.90

B

3.55 | 1.15 | 3.30 | 3.30 | 1.20 | 4.35 | 2.02 | 7.98 | 1.05 | 3.30 | 3.15 | DUCT 0.65 | 4.85 | CHAJJA 0.65

39.20

1.20

18TH FLOOR PLAN

SCALE:-1:100

39.20

B

DUCT

DUCT

18TH FLOOR BUILDING LINE

ELEVATIONAL TREATMENT @4.50M FROM TERRACE FLOOR LVL WITH 60% OPENING

ELEVATIONAL TREATMENT @4.50M FROM TERRACE FLOOR LVL WITH 60% OPENING

TERRACE GARDEN OPEN TO SKY

A

A

9.80

11.15

DUCT

DUCT

DUCT

CHAJJA

0.45

1.15 X 1.20 S.S DUCT

0.90

ROOF OVER BALCONY

F.R.D

CHAJJA

20.45

M.BEDROOM 1 3.20 x 3.95

BEDROOM 3.05 x 3.95

TOILET 1.25 x 2.25

2.00 MT. WIDE PASSAGE

2.00

1.20 x 0.45

LIVING / DINING 3.20 x 6.55

C.AREA = 85.35 SQ.M

(SALE)

1.05 x 1.80

1

S. LIFT 3.80 x 1.80

FD

FD

0.80

0.90

CHAJJA

F.R.D

F.R.D

ELEVATIONAL TREATMENT @4.50M FROM TERRACE FLOOR LVL WITH 60% OPENING

9.60

1.40

DUCT 0.65

M.TOILET 1 2.20 x 1.40

5.50 x 0.90

0.95 x 0.65

FRD

0.37 0.37

0.25

DN

1.50

UP

S. LIFT 3.80 x 1.80

DUCT

0.60

1.40

TERRACE GARDEN OPEN TO SKY

M.TOILET 2 1.20 x 2.40

KITCHEN 3.00 x 3.35

1.50

S. LIFT LOBBY 1.92 x 2.97

S. LIFT 2.82 x 1.85

7.30

M. BEDROOM 2 3.25 x 3.65

DUCT 0.95 S.S

0.70

CHAJJA

1.15

0.60

CHAJJA

1.50

0.80

CHAJJA

CHAJJA

B

1.05

0.45

DUCT

3.55

1.15

3.30

3.30

1.20

4.35

2.02

7.83

12.50

39.20

19TH FLOOR PLAN