

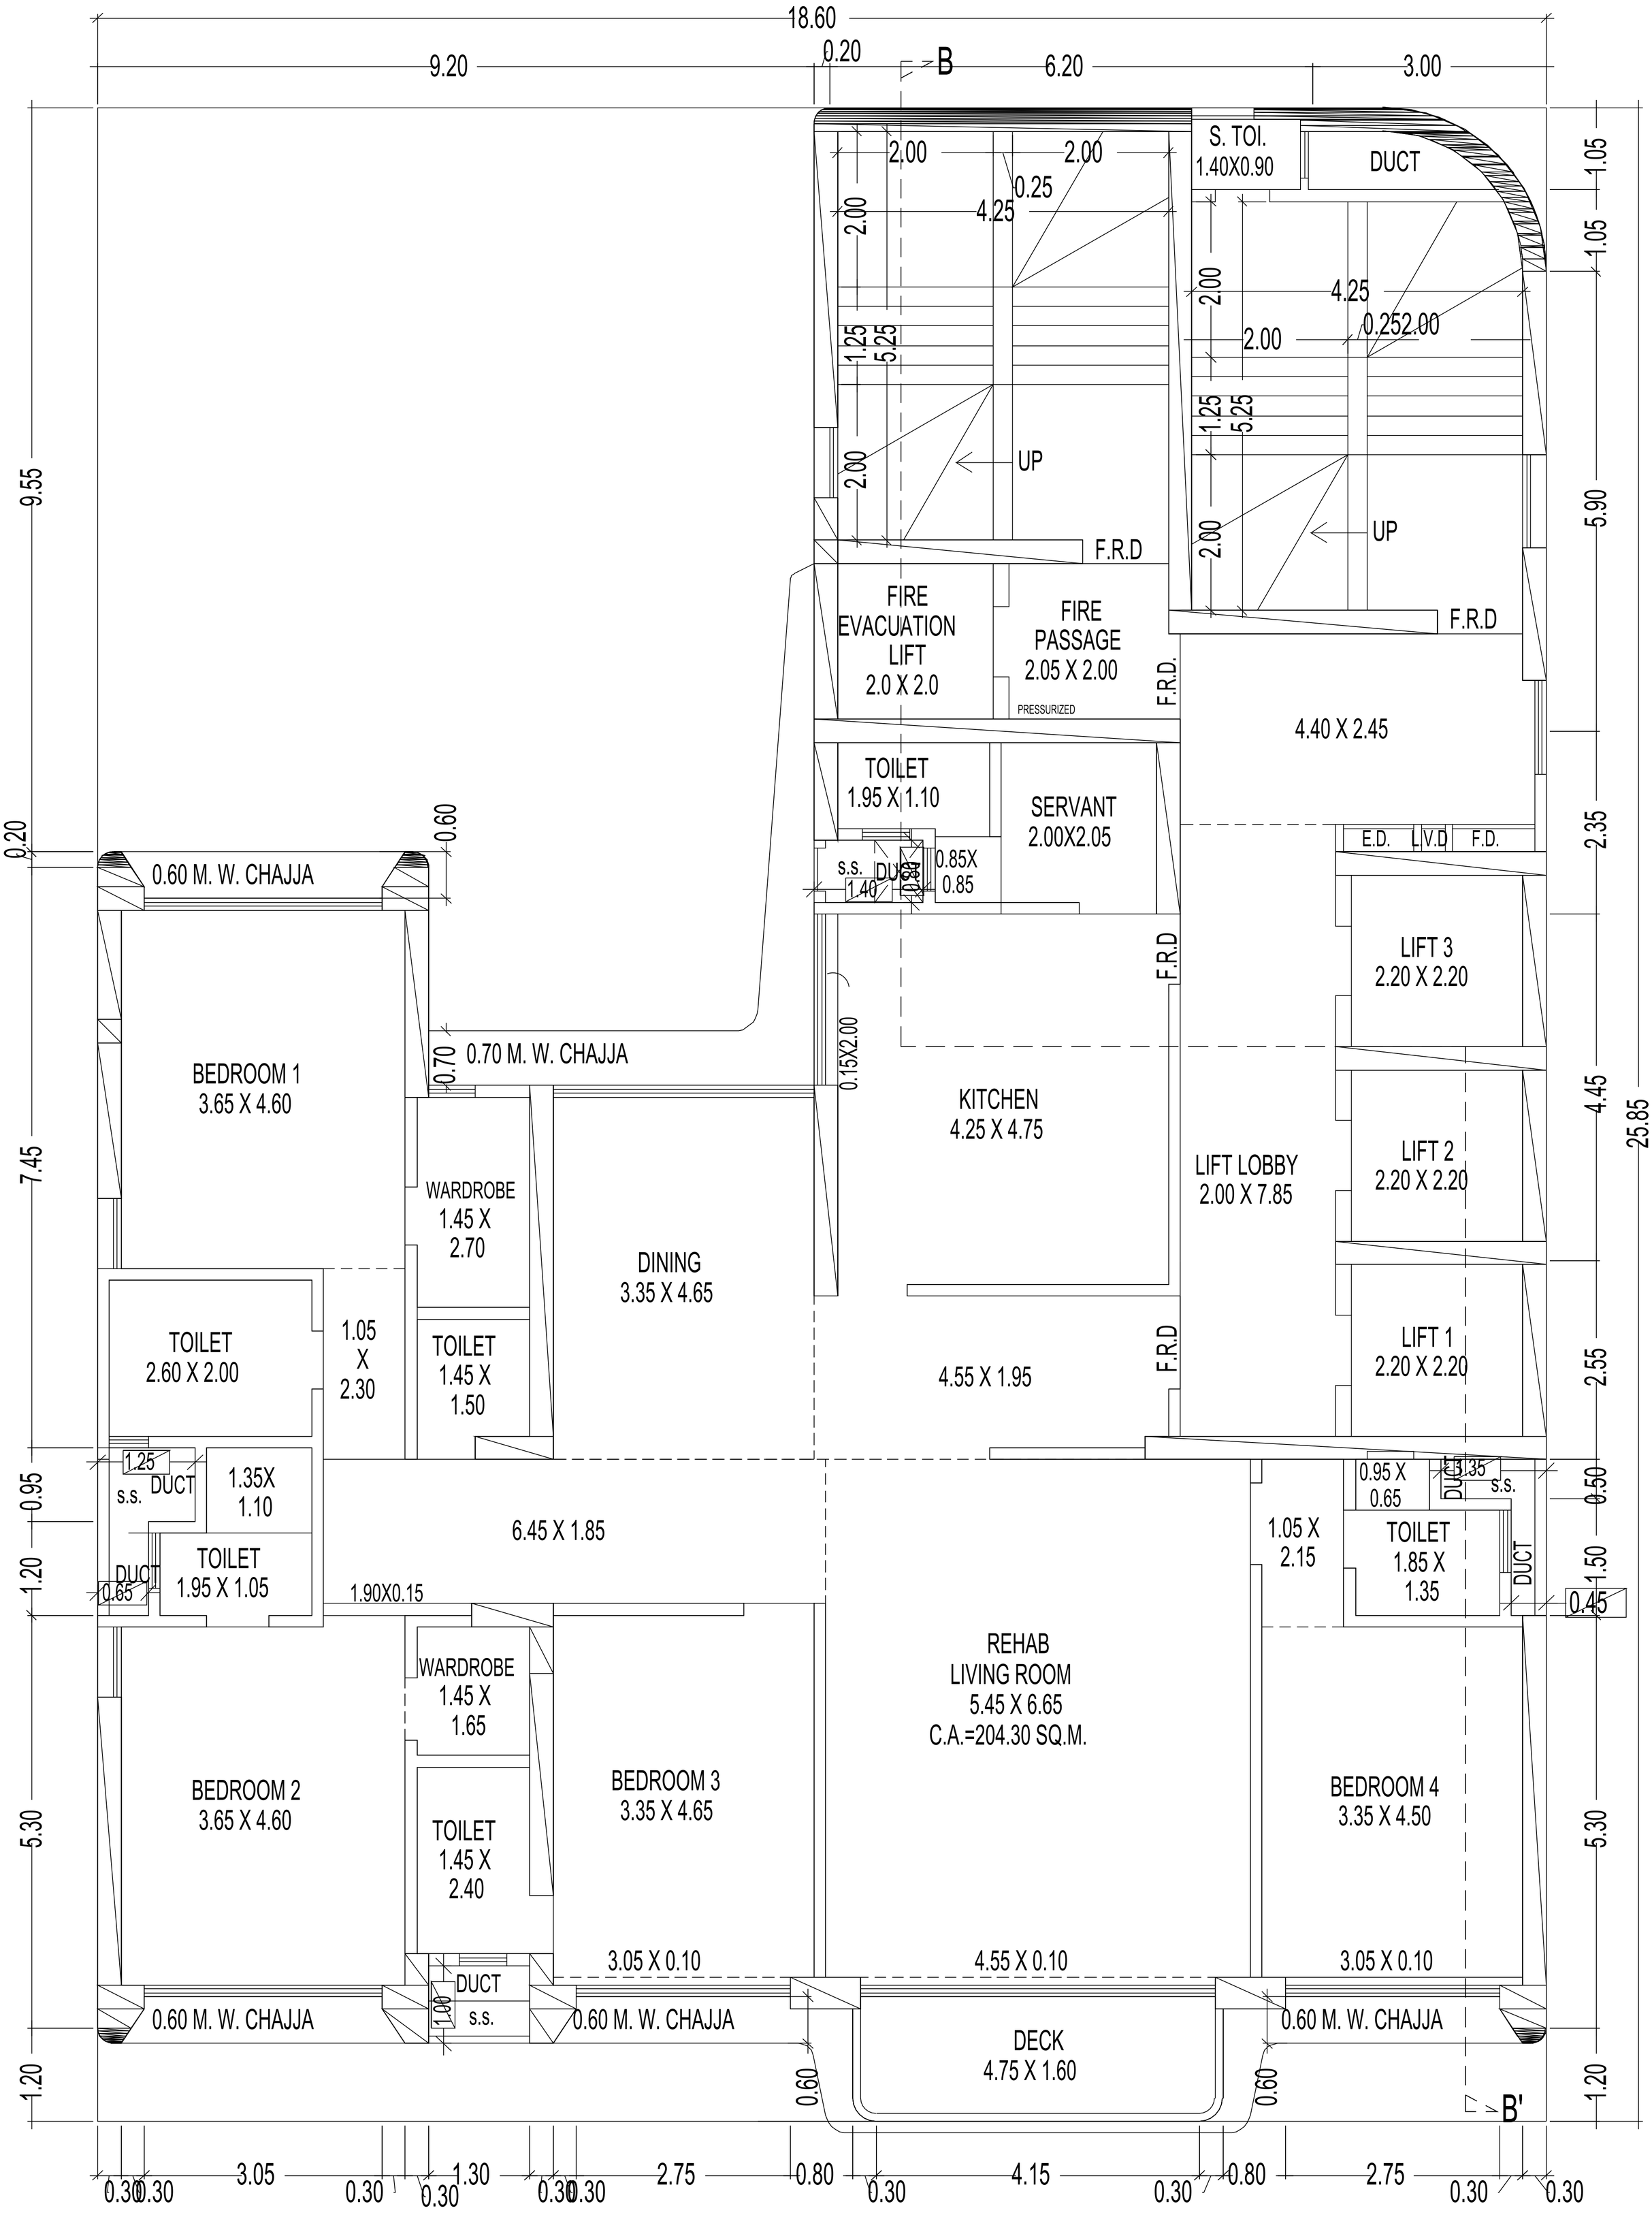


2ND FLOOR PLAN

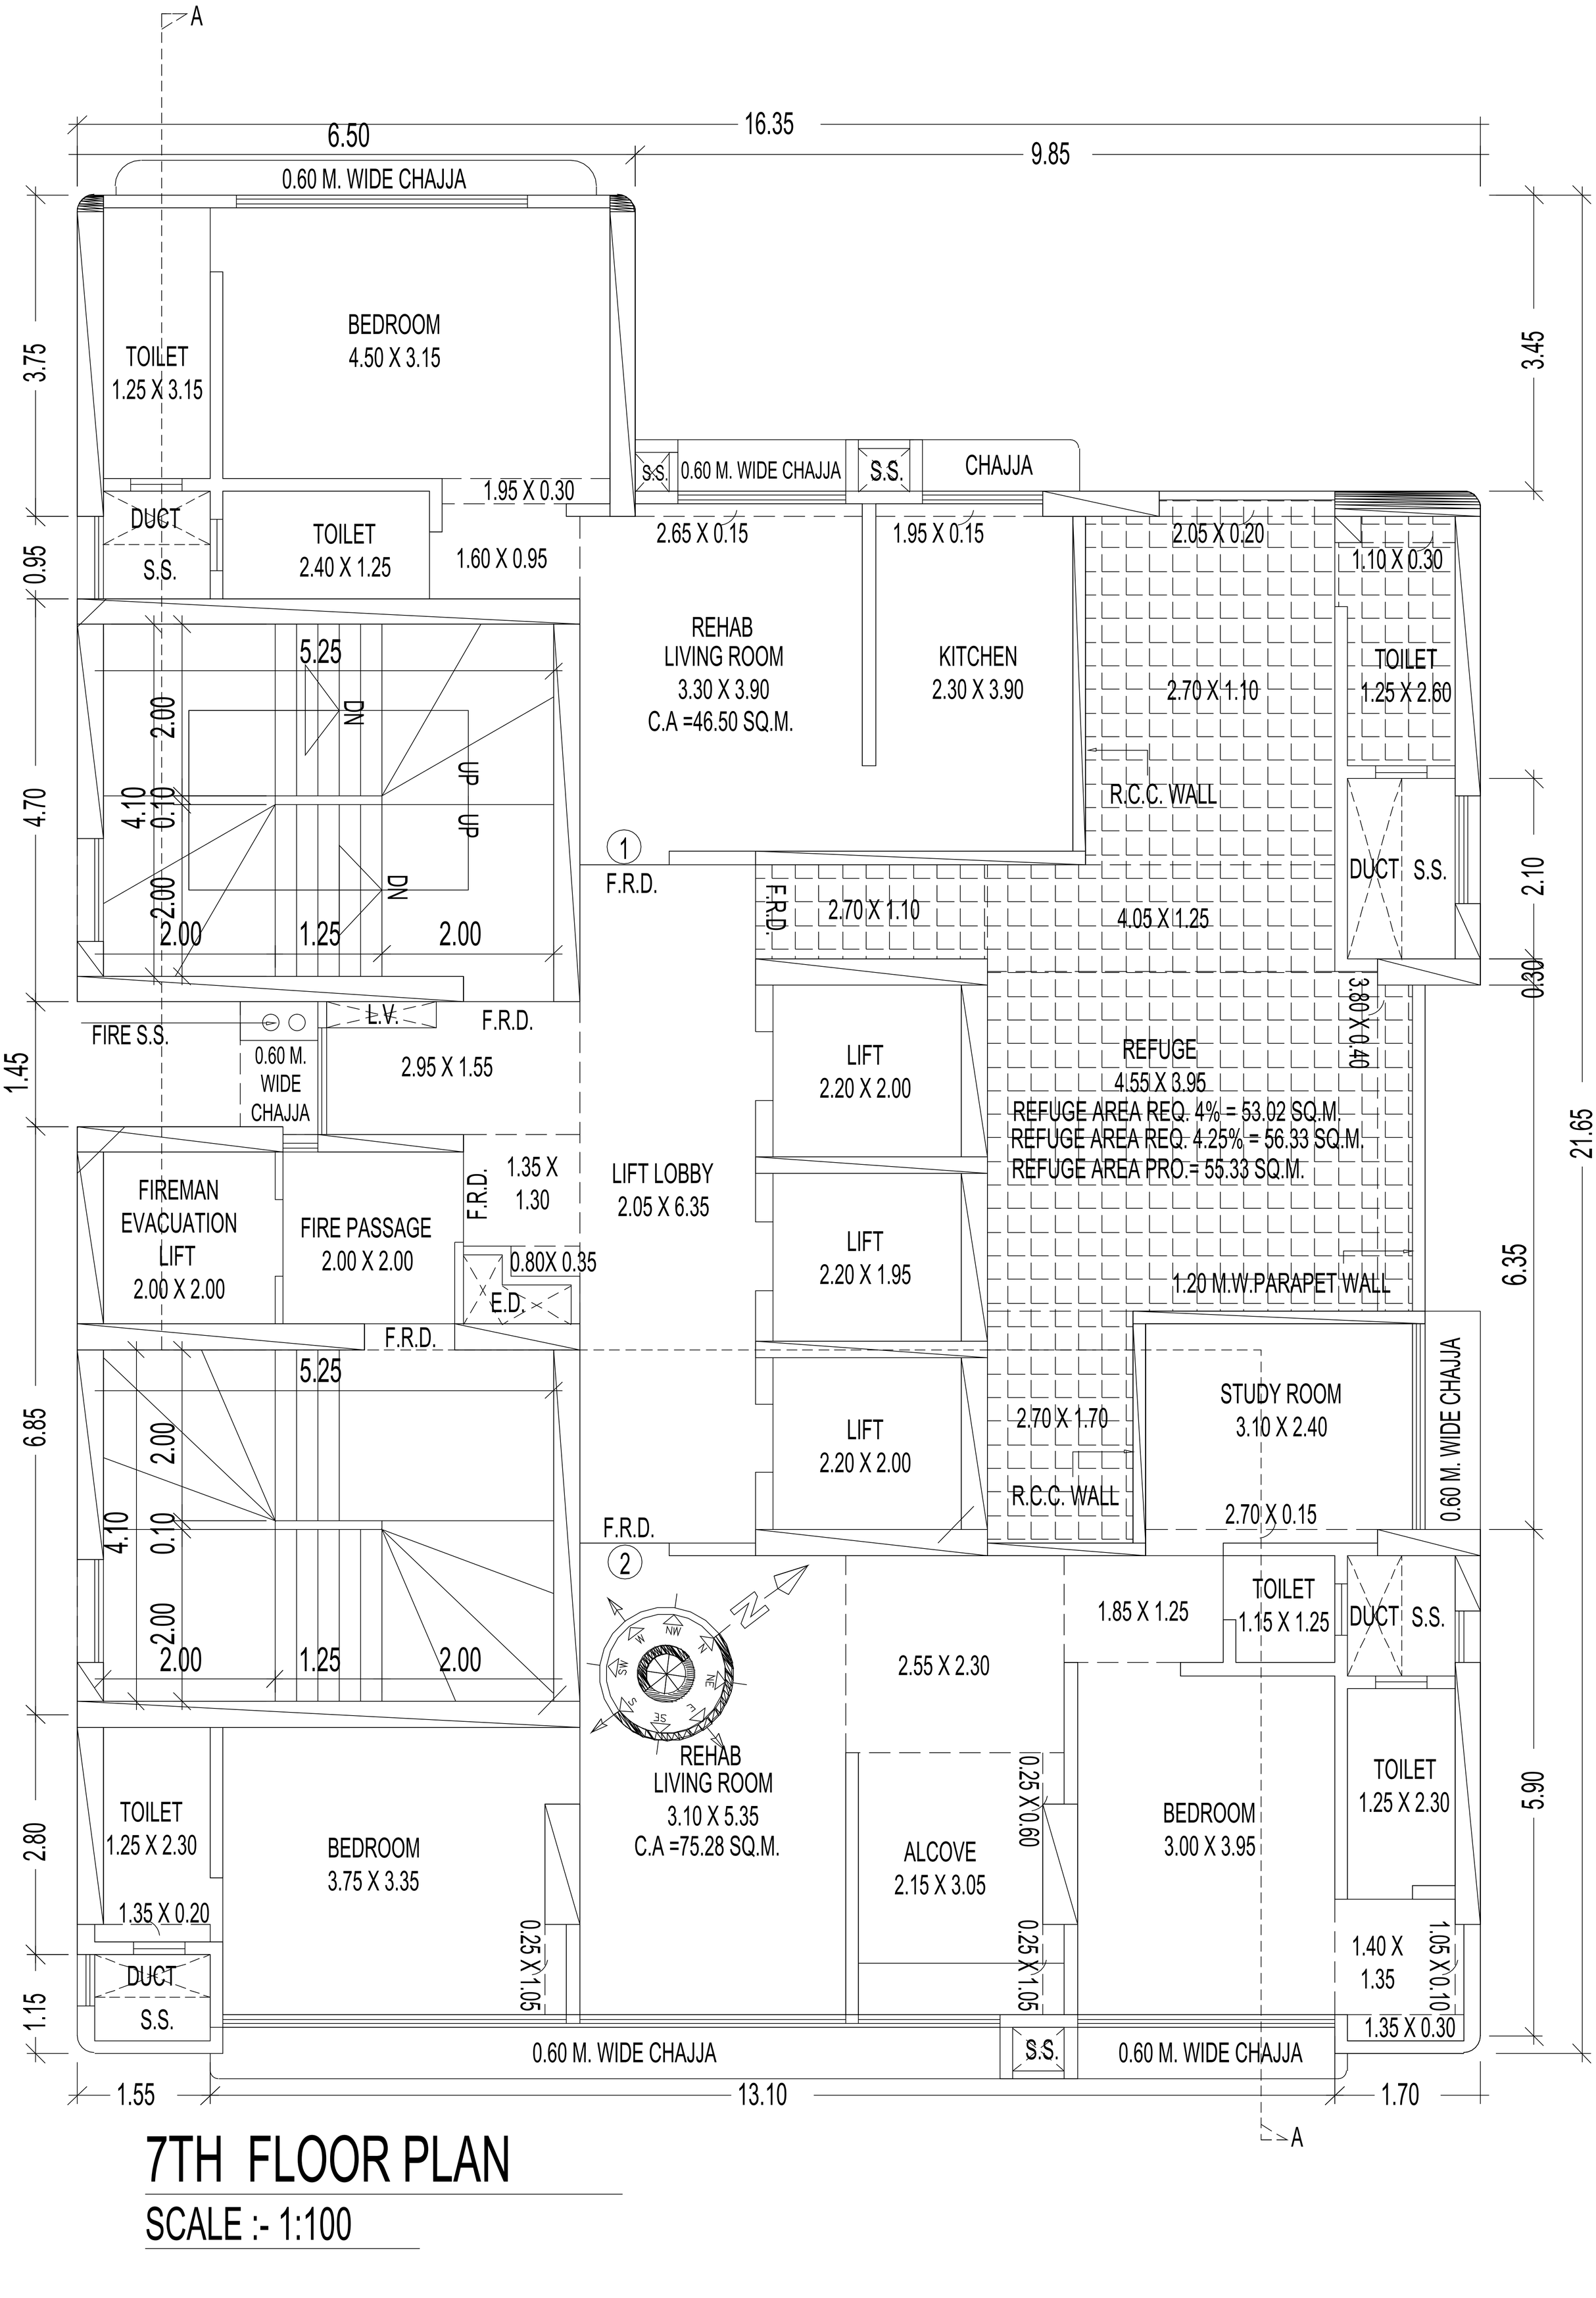


7TH FLOOR PLAN

SCALE :- 1:100

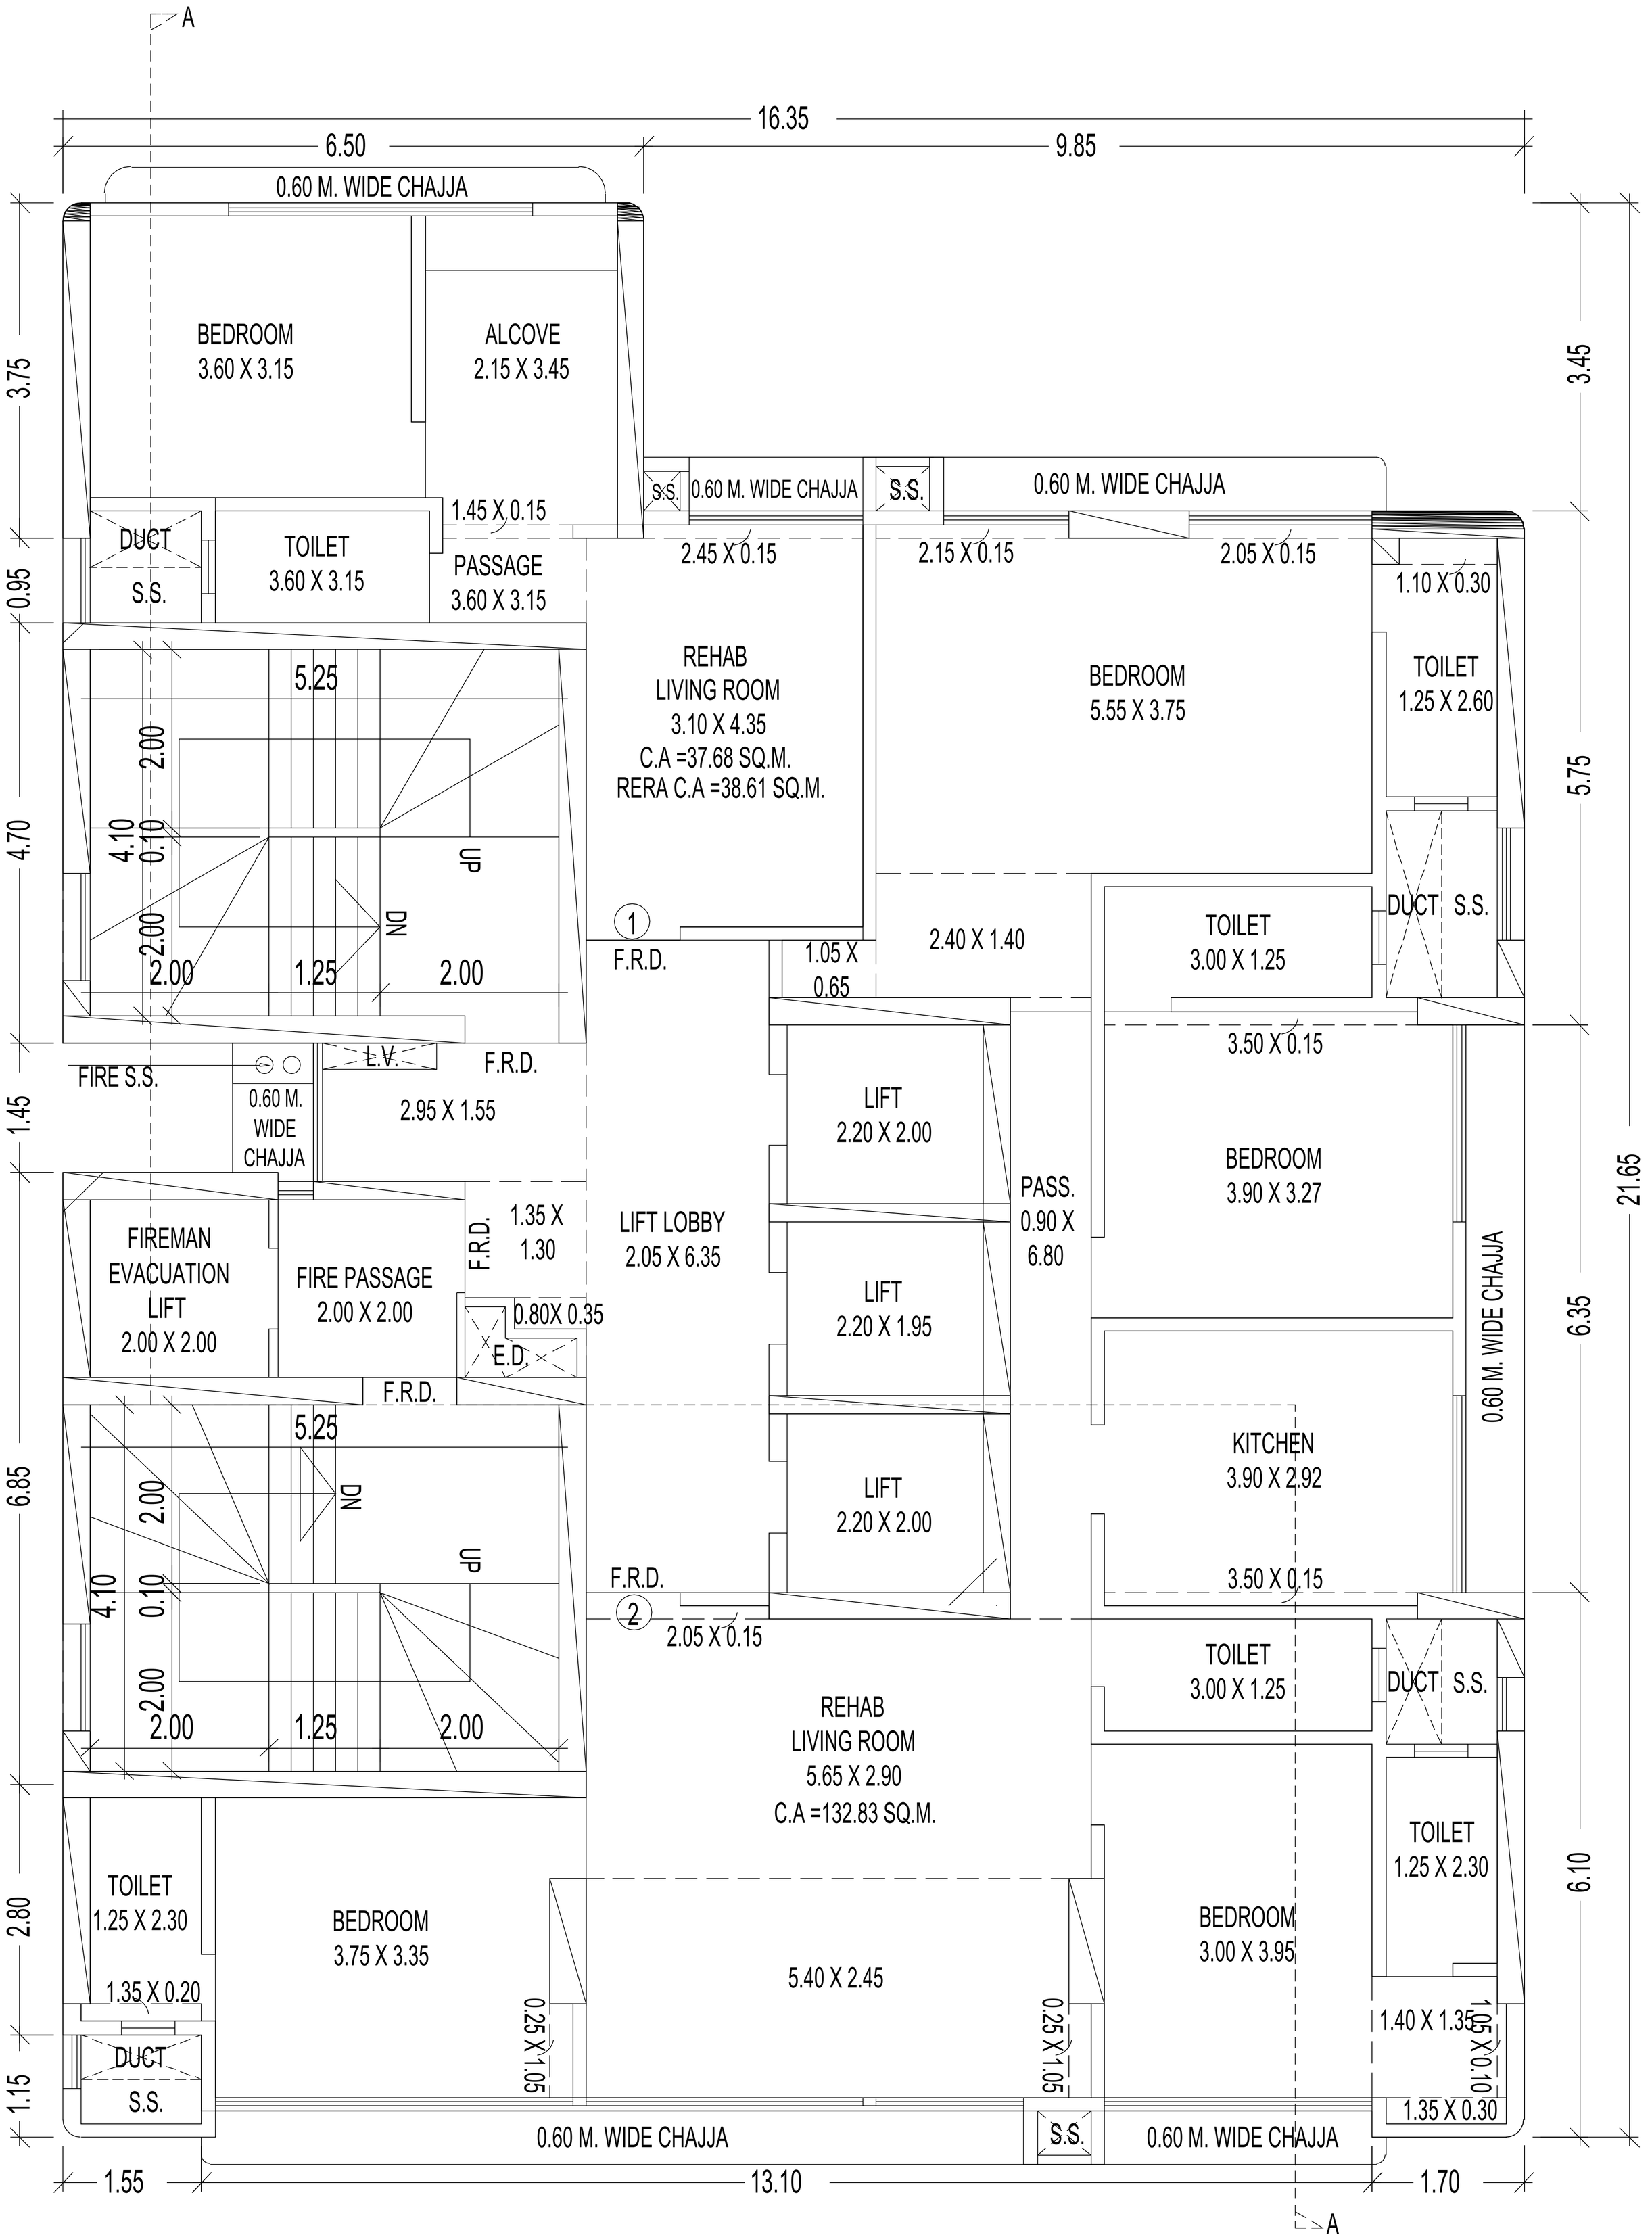

8TH T0 13TH FLOOR PLAN

SCALE :- 1:100

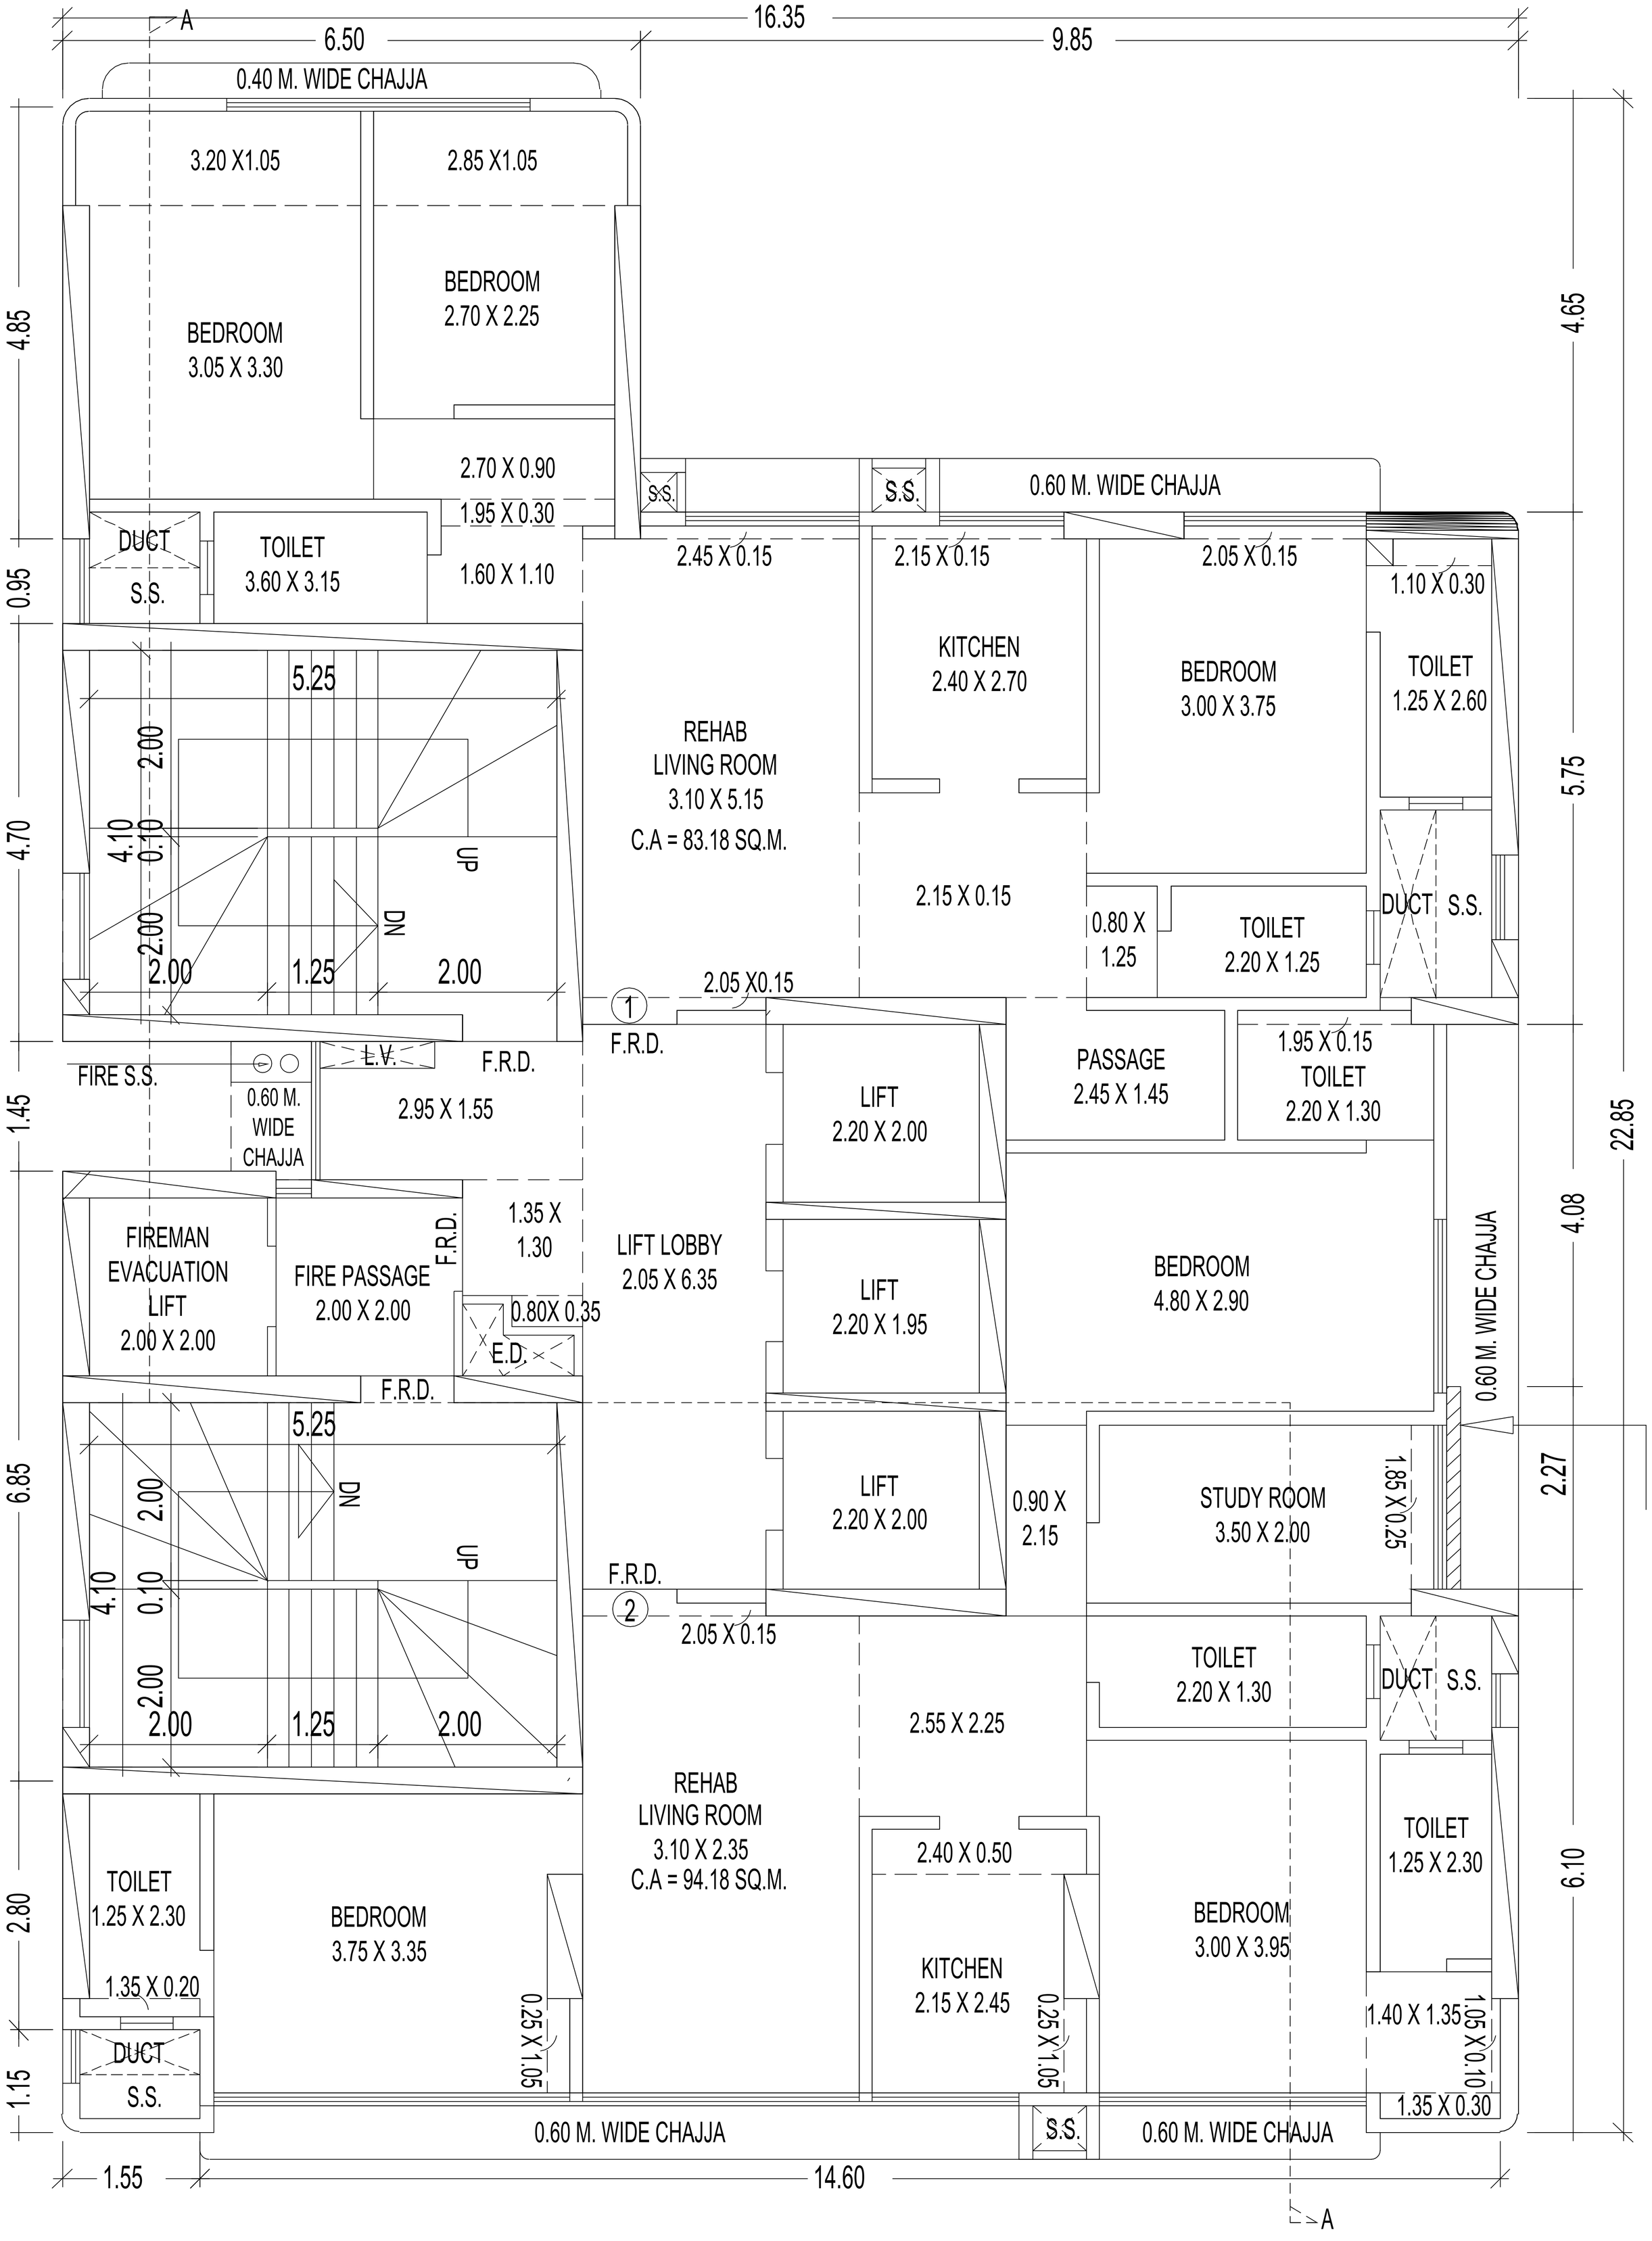


15TH TO 20TH FLOOR PLAN

SCALE :- 1:100

21ST FLOOR PLAN

SCALE :- 1:100

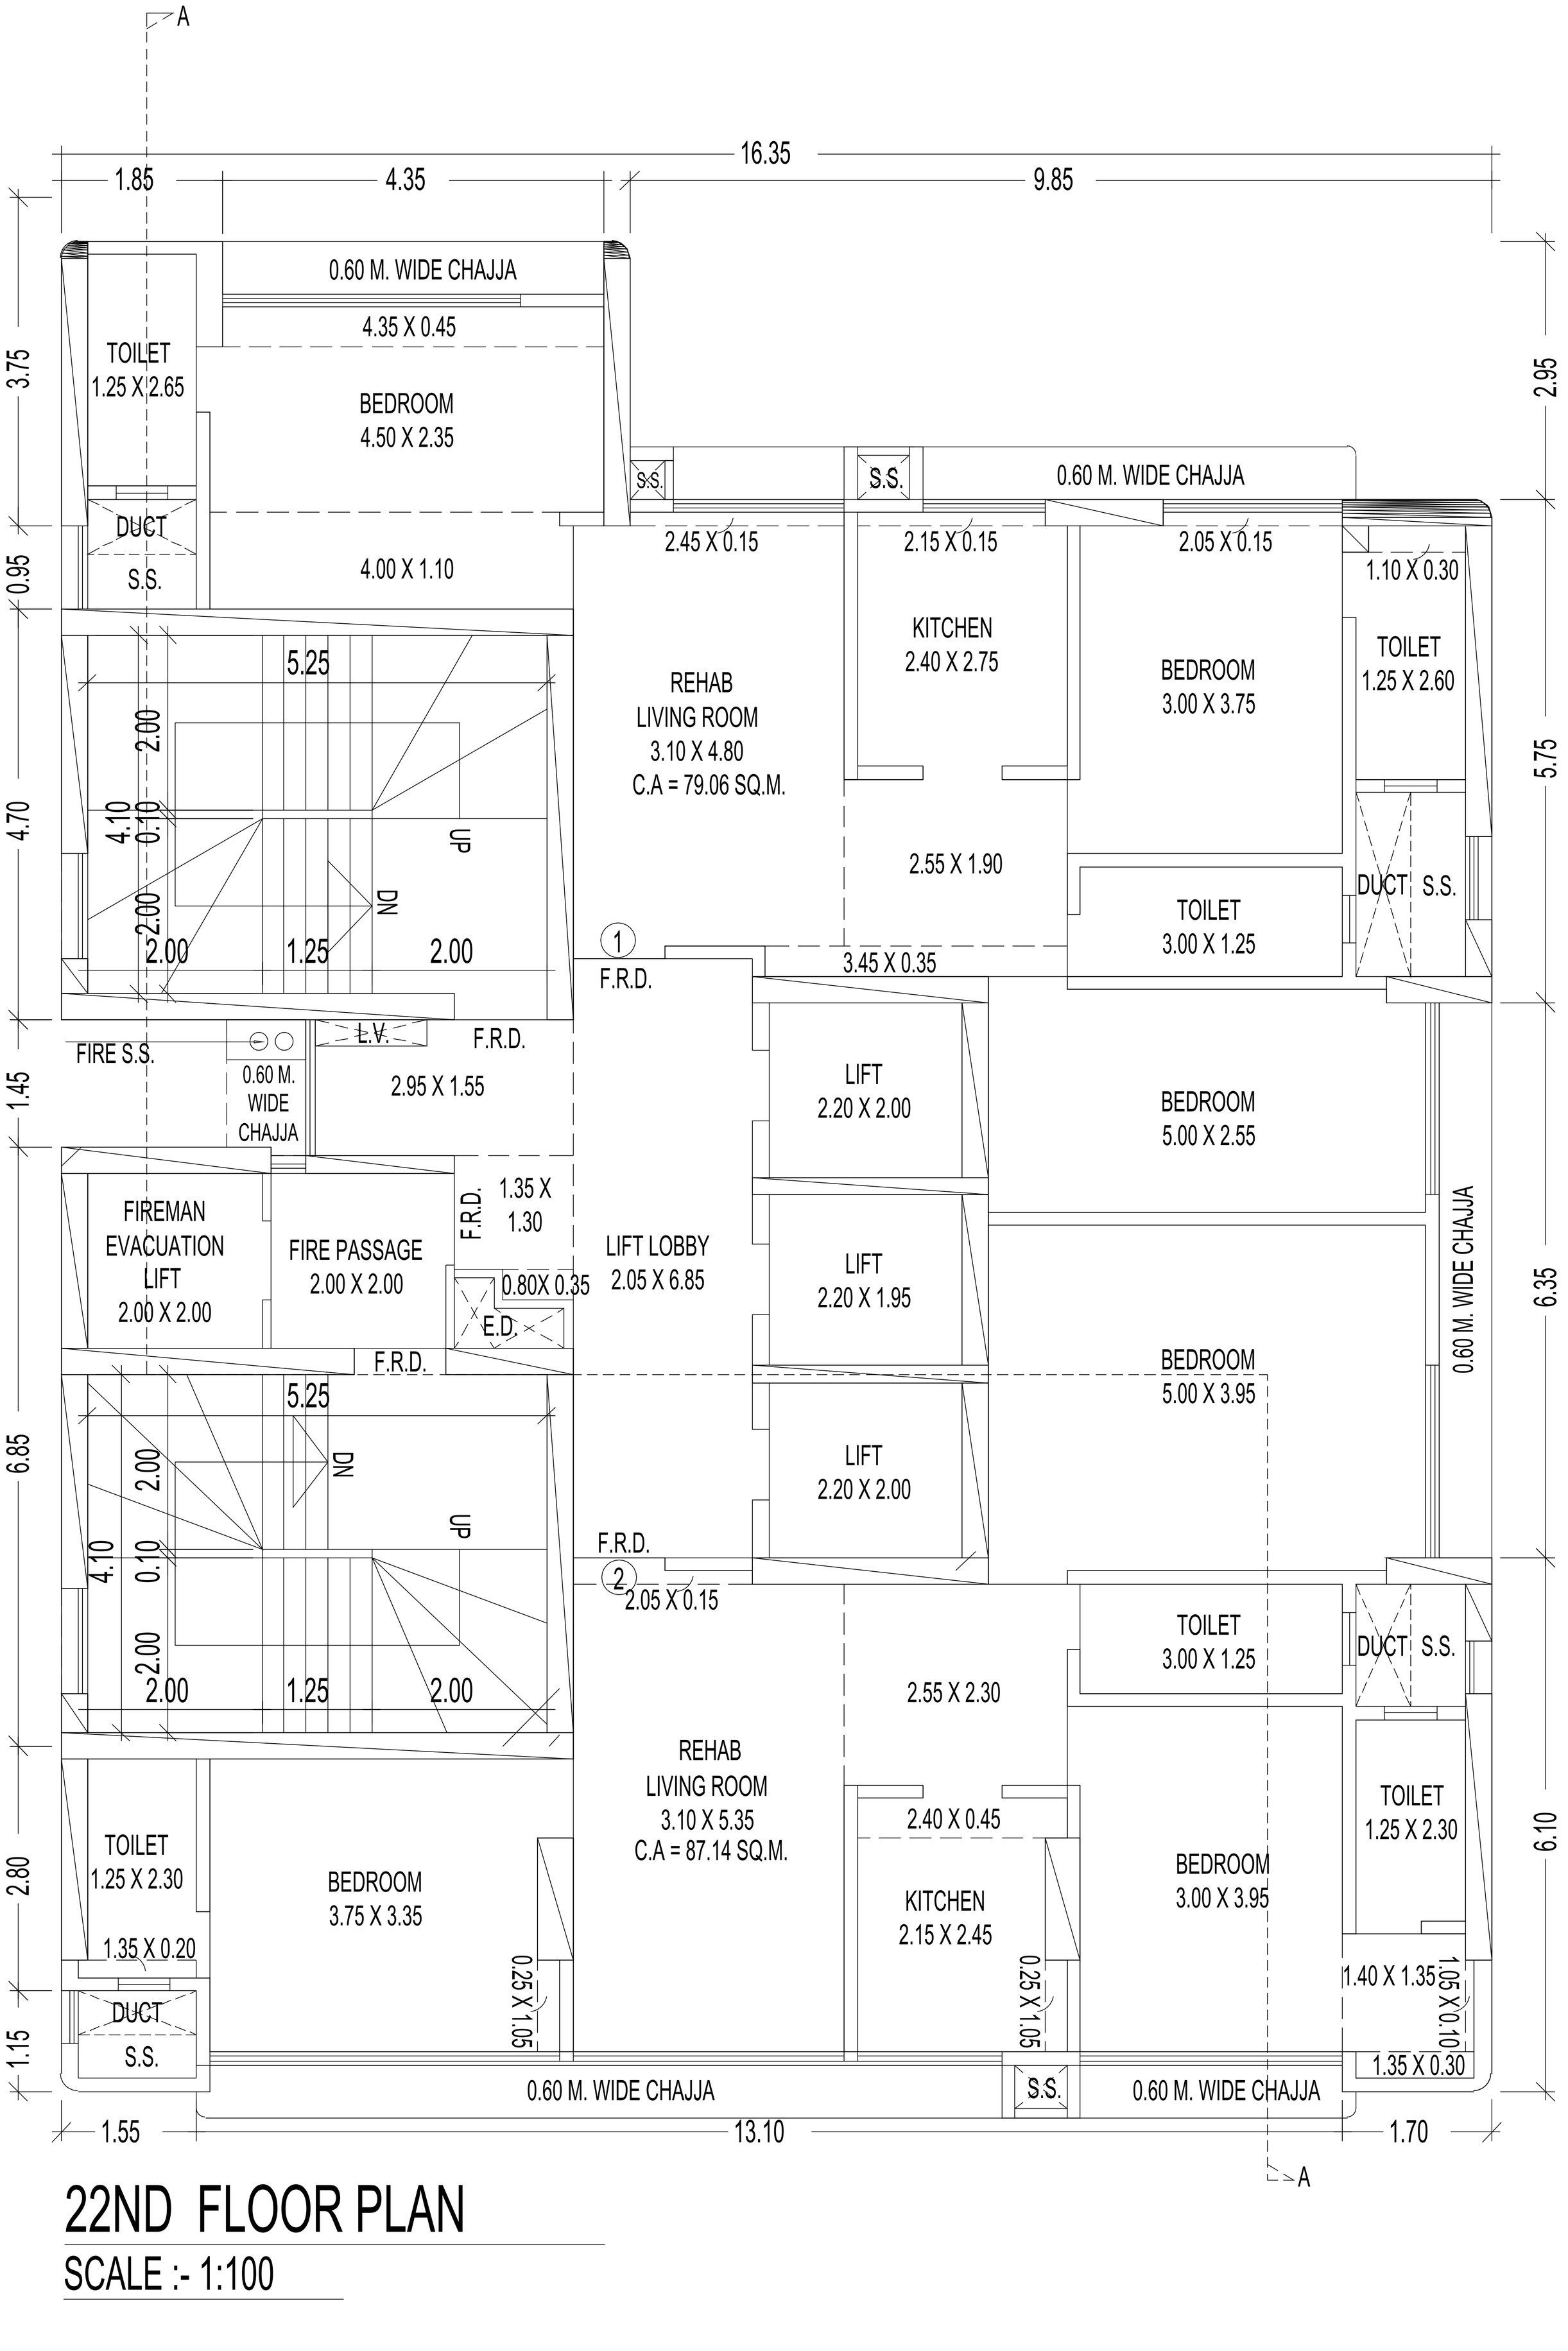

22ND FLOOR PLAN

SCALE :- 1:100

23RD TO 27TH & 29TH TO 30TH FLOOR PLAN

SCALE :- 1:100

NOTE:-FLAT NO.2501,2601,2701,2901,3001-SALE FLAT

A

1.85 | 4.35 | 9.85 | 16.35

3.75 | 0.95 | 4.70 | 1.45 | 6.85 | 2.80 | 1.15

2.95 | 5.75 | 6.35 | 21.15

0.60 M. WIDE CHAJJA

4.35 X 0.25

TOILET
1.25 X 2.65

BEDROOM
4.50 X 2.10

DUCT
S.S.

4.00 X 1.10

S.S.

S.S.

S.S.

0.60 M. WIDE CHAJJA

2.45 X 0.15

2.15 X 0.15

2.05 X 0.15

1.10 X 0.30

KITCHEN
2.40 X 2.70

TOILET
1.25 X 2.60

BEDROOM
3.00 X 3.75

5.25

2.00

4.10

0.10

2.00

2.00

1.25

2.00

SALE
LIVING ROOM
3.10 X 5.15
RERA C.A = 103.48 SQ.M.

2.55 X 2.30

TOILET
3.00 X 1.25

DUCT S.S.

1

F.R.D.

L.V.

F.R.D.

FIRE S.S.

0.60 M.
WIDE
CHAJJA

2.95 X 1.55

LIFT
2.20 X 2.00

0.90 X
3.40

BEDROOM
3.95 X 3.25

FIREMAN
EVACUATION
LIFT
2.00 X 2.00

FIRE PASSAGE
2.00 X 2.00

F.R.D.

1.35 X
1.30

LIFT LOBBY
2.05 X 7.77

0.80X 0.35

E.D.

F.R.D.

LIFT
2.20 X 1.95

0.60 M. WIDE CHAJJA

5.25

2.00

DN

UP

4.10

0.10

2.00

2.00

1.25

2.00

LIFT
2.20 X 2.00

STUDY ROOM
5.00 X 3.25

R.C.C. WALL

F.R.D.

6.60 X 1.12

DUCT S.S.

F.R.D.

2

1.00 X
0.87

REFUGE
7.65 X 1.77
REFUGE AREA REQ. 4% = 51.17 SQ.M.
REFUGE AREA REQ. 4.25% = 54.36 SQ.M.
REFUGE AREA PRO.= 54.31 SQ.M.

1.92 X 0.90

TOILET
1.25 X 2.30

TOILET
1.25 X 2.30

SOCIETY OFFICE
3.22 X 3.35
C.A = 16.82 SQ.M.

0.37X
1.25

R.C.C. WALL

1.15 X
2.30

3.00 X 1.40

1.35 X 0.20

4.25 X 2.45

1.40 X 1.35

1.05 X 0.10

0.77 X
1.05

1.20 M.W.PARAPET WALL

3.40 X 1.05

DUCT
S.S.

S.S.

1.35 X 0.30

1.55 | 13.10 | 1.70

A

28TH FLOOR PLAN


SCALE :- 1:100



31ST TO 34TH & 36TH TO 38TH FLOOR PLAN


SCALE :- 1:100

SCALE : 1:100

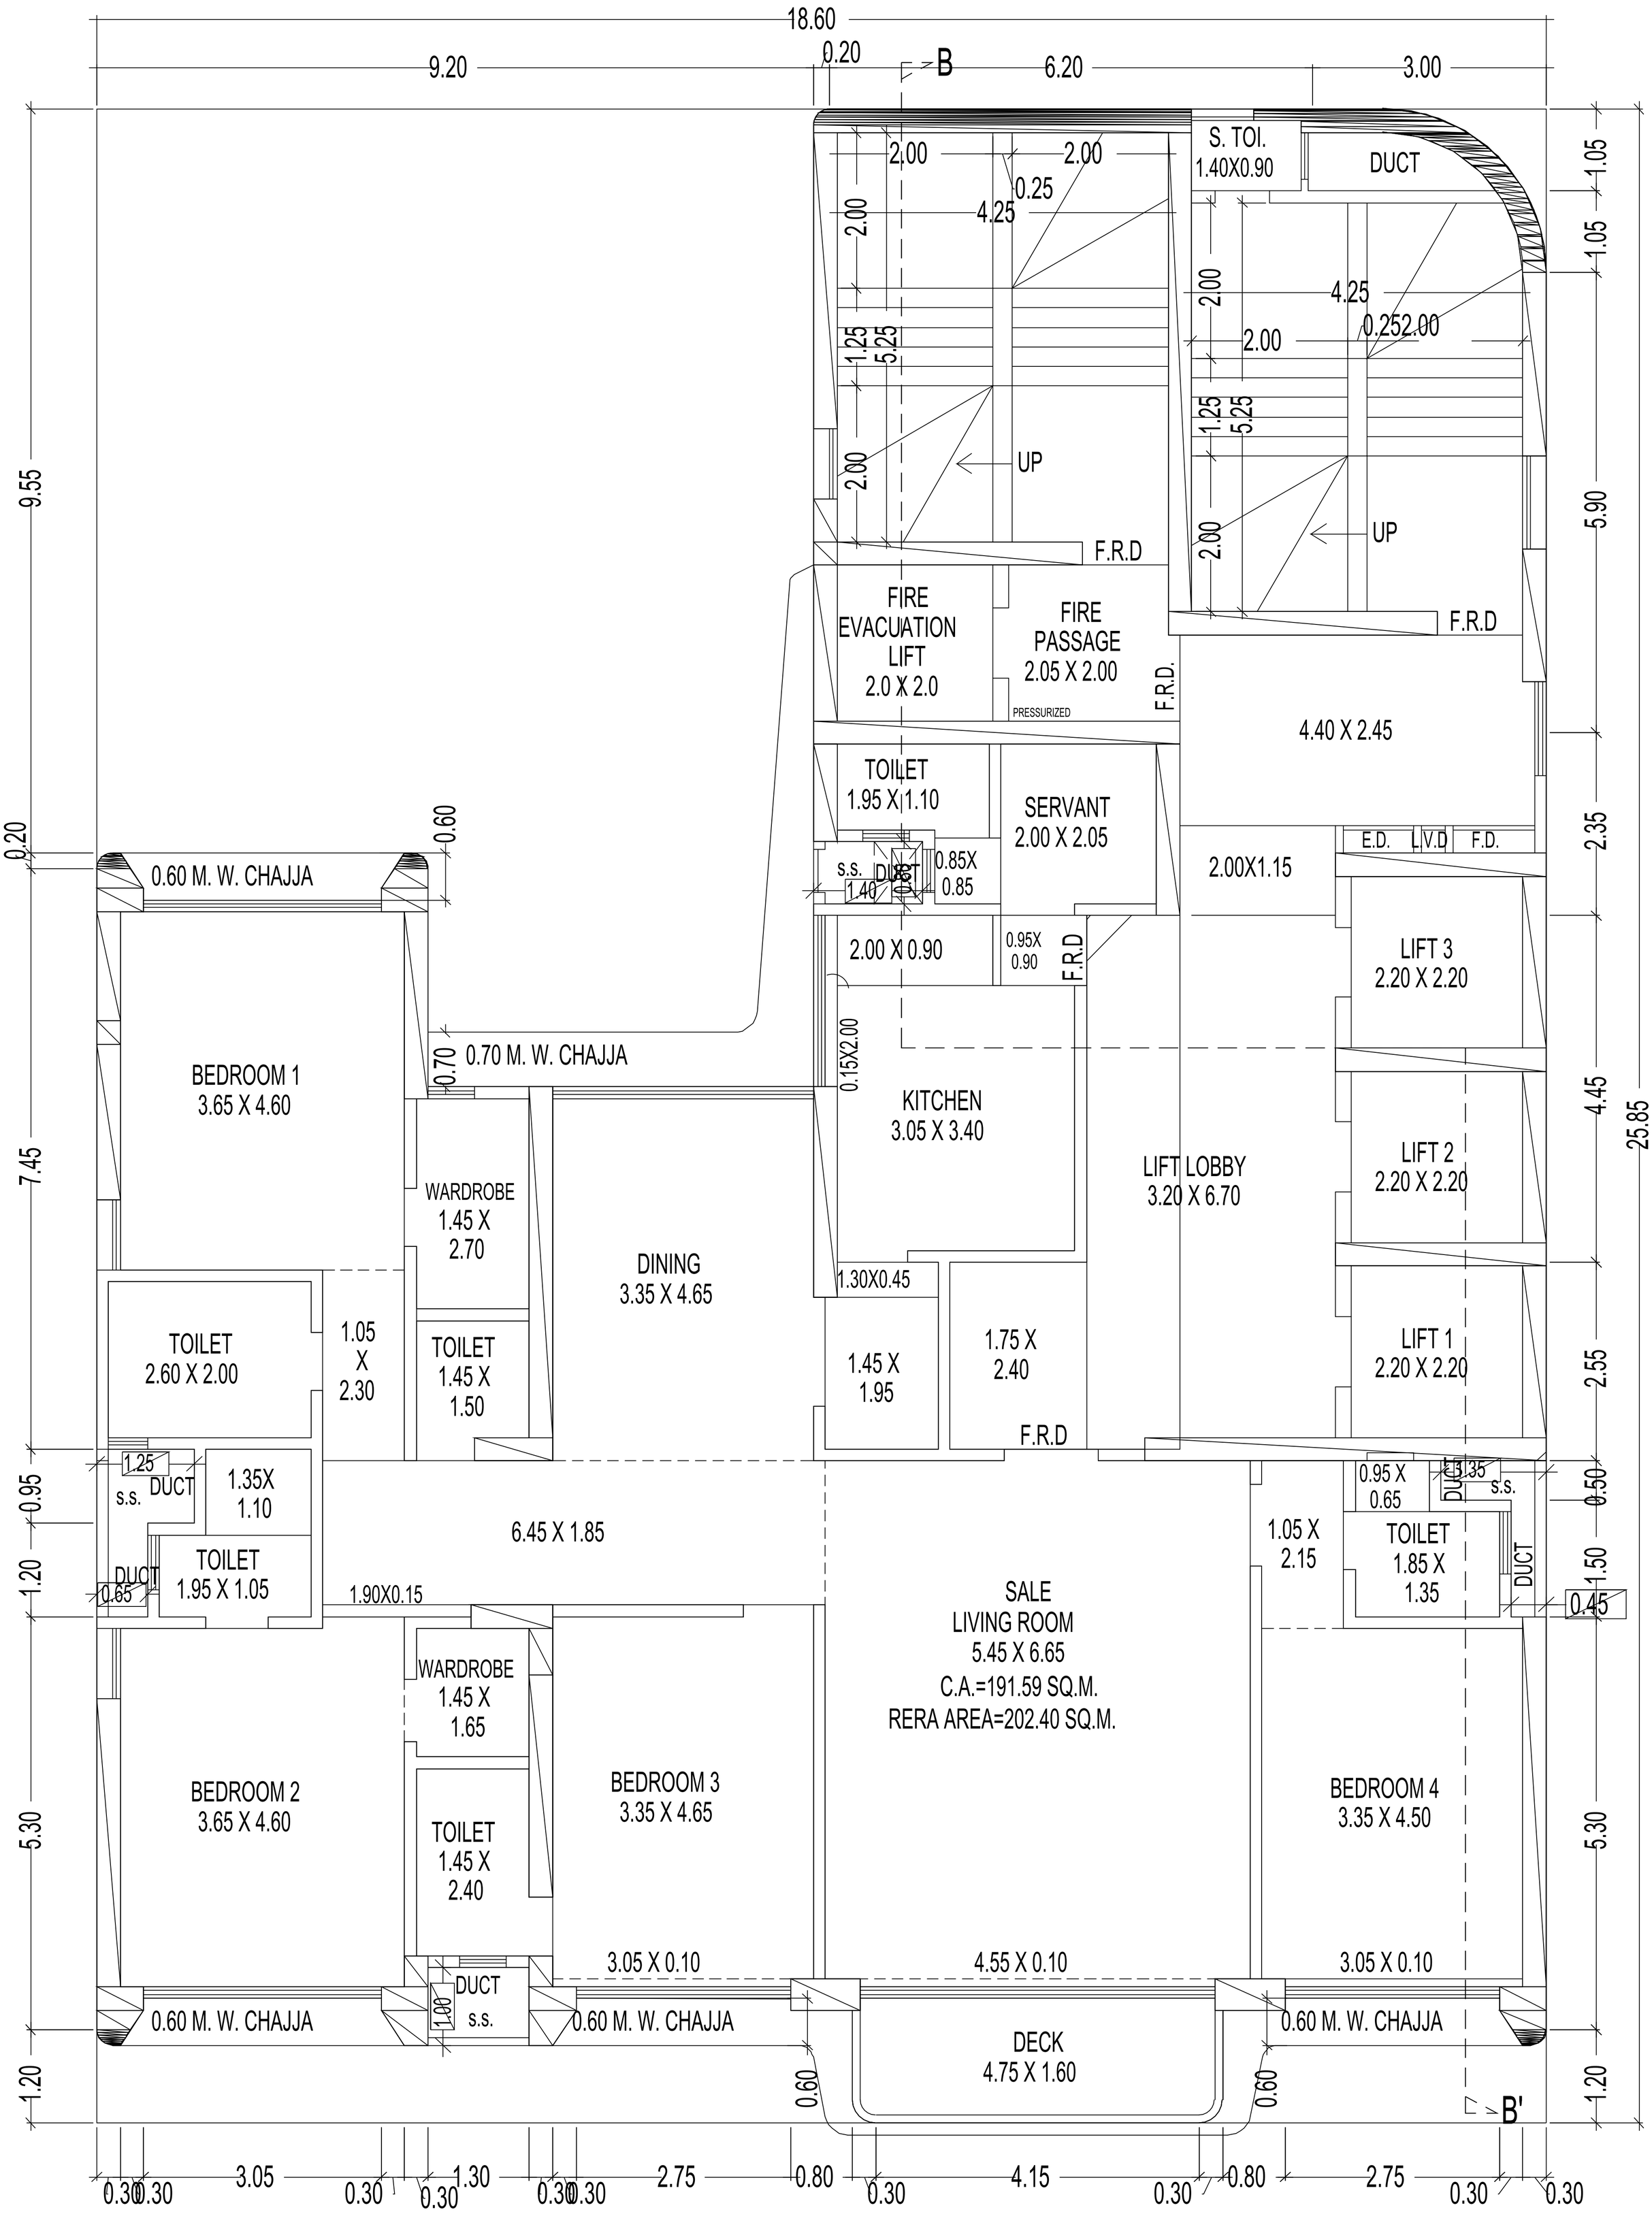

3RD TO 6TH,8TH TO 13TH,15TH TO 20TH,22ND TO 27TH,29TH TO 34TH,36TH TO 41ST,43RD ,44TH & 50TH FLOOR PLAN


SCALE : 1:100

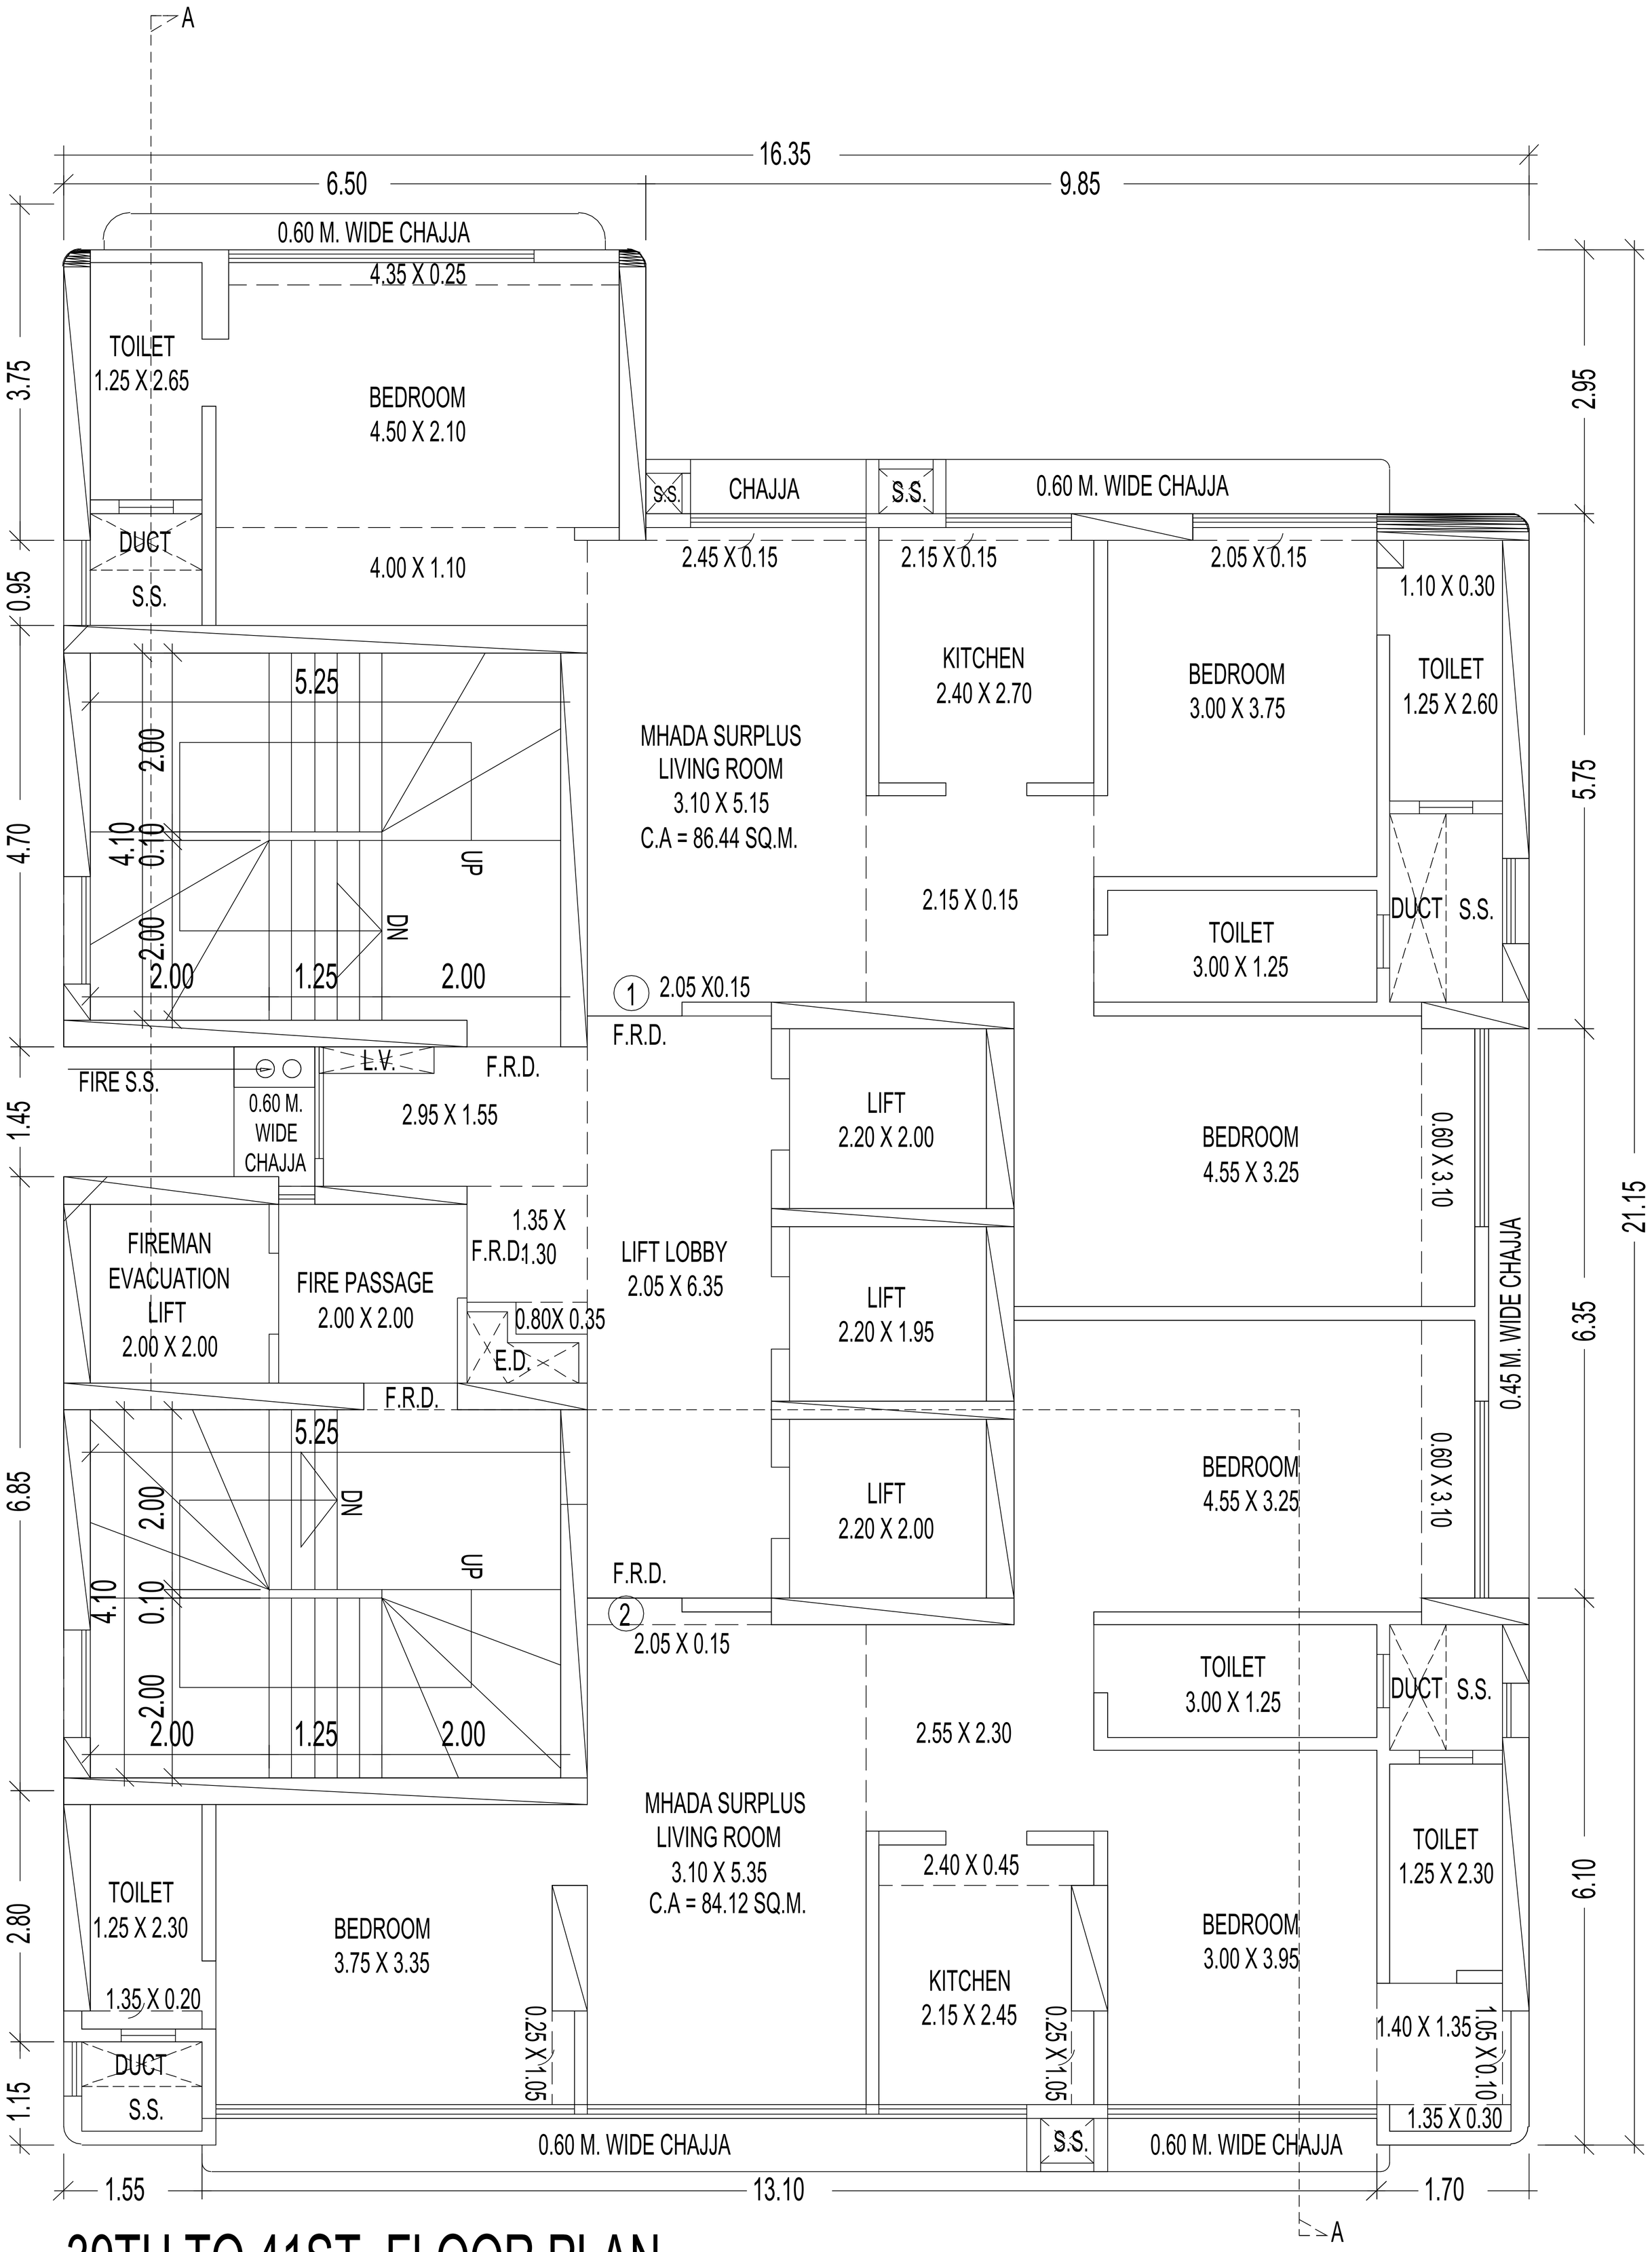

39TH TO 41ST FLOOR PLAN


SCALE :- 1:100

NOTE:-FLAT NO.3902,4101,4102-SALE FLAT

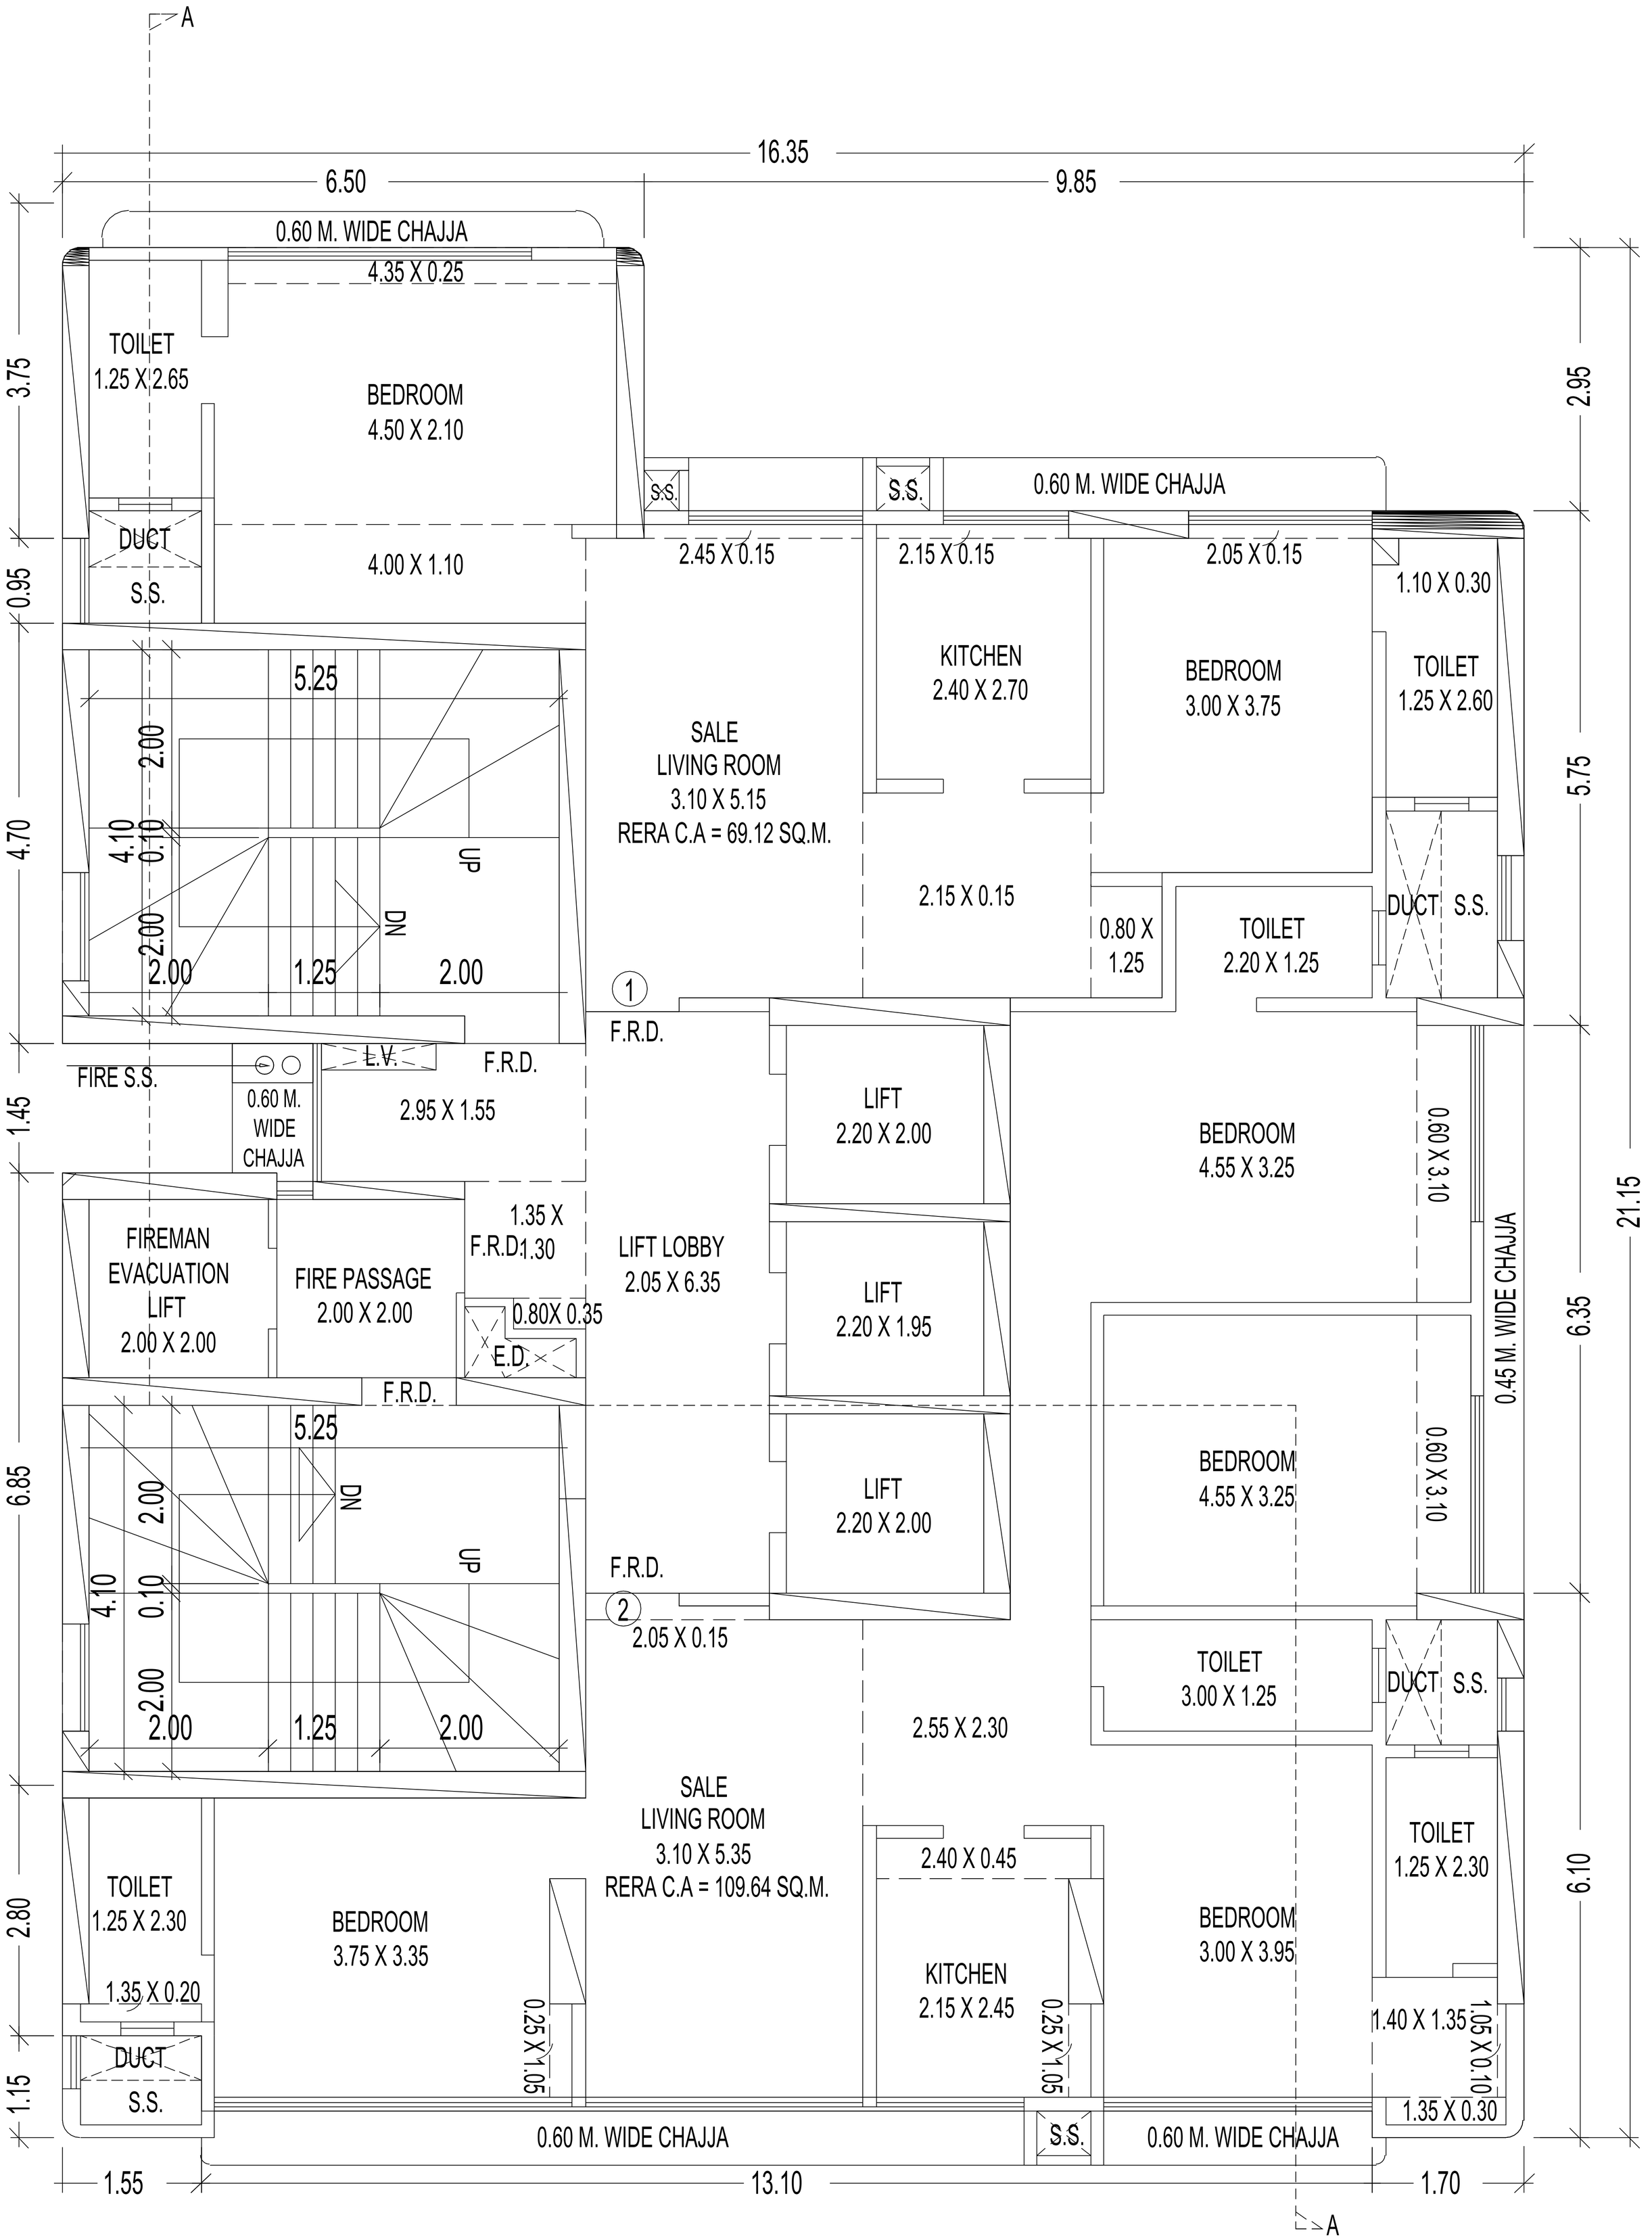


42ND FLOOR PLAN

SCALE :- 1:100

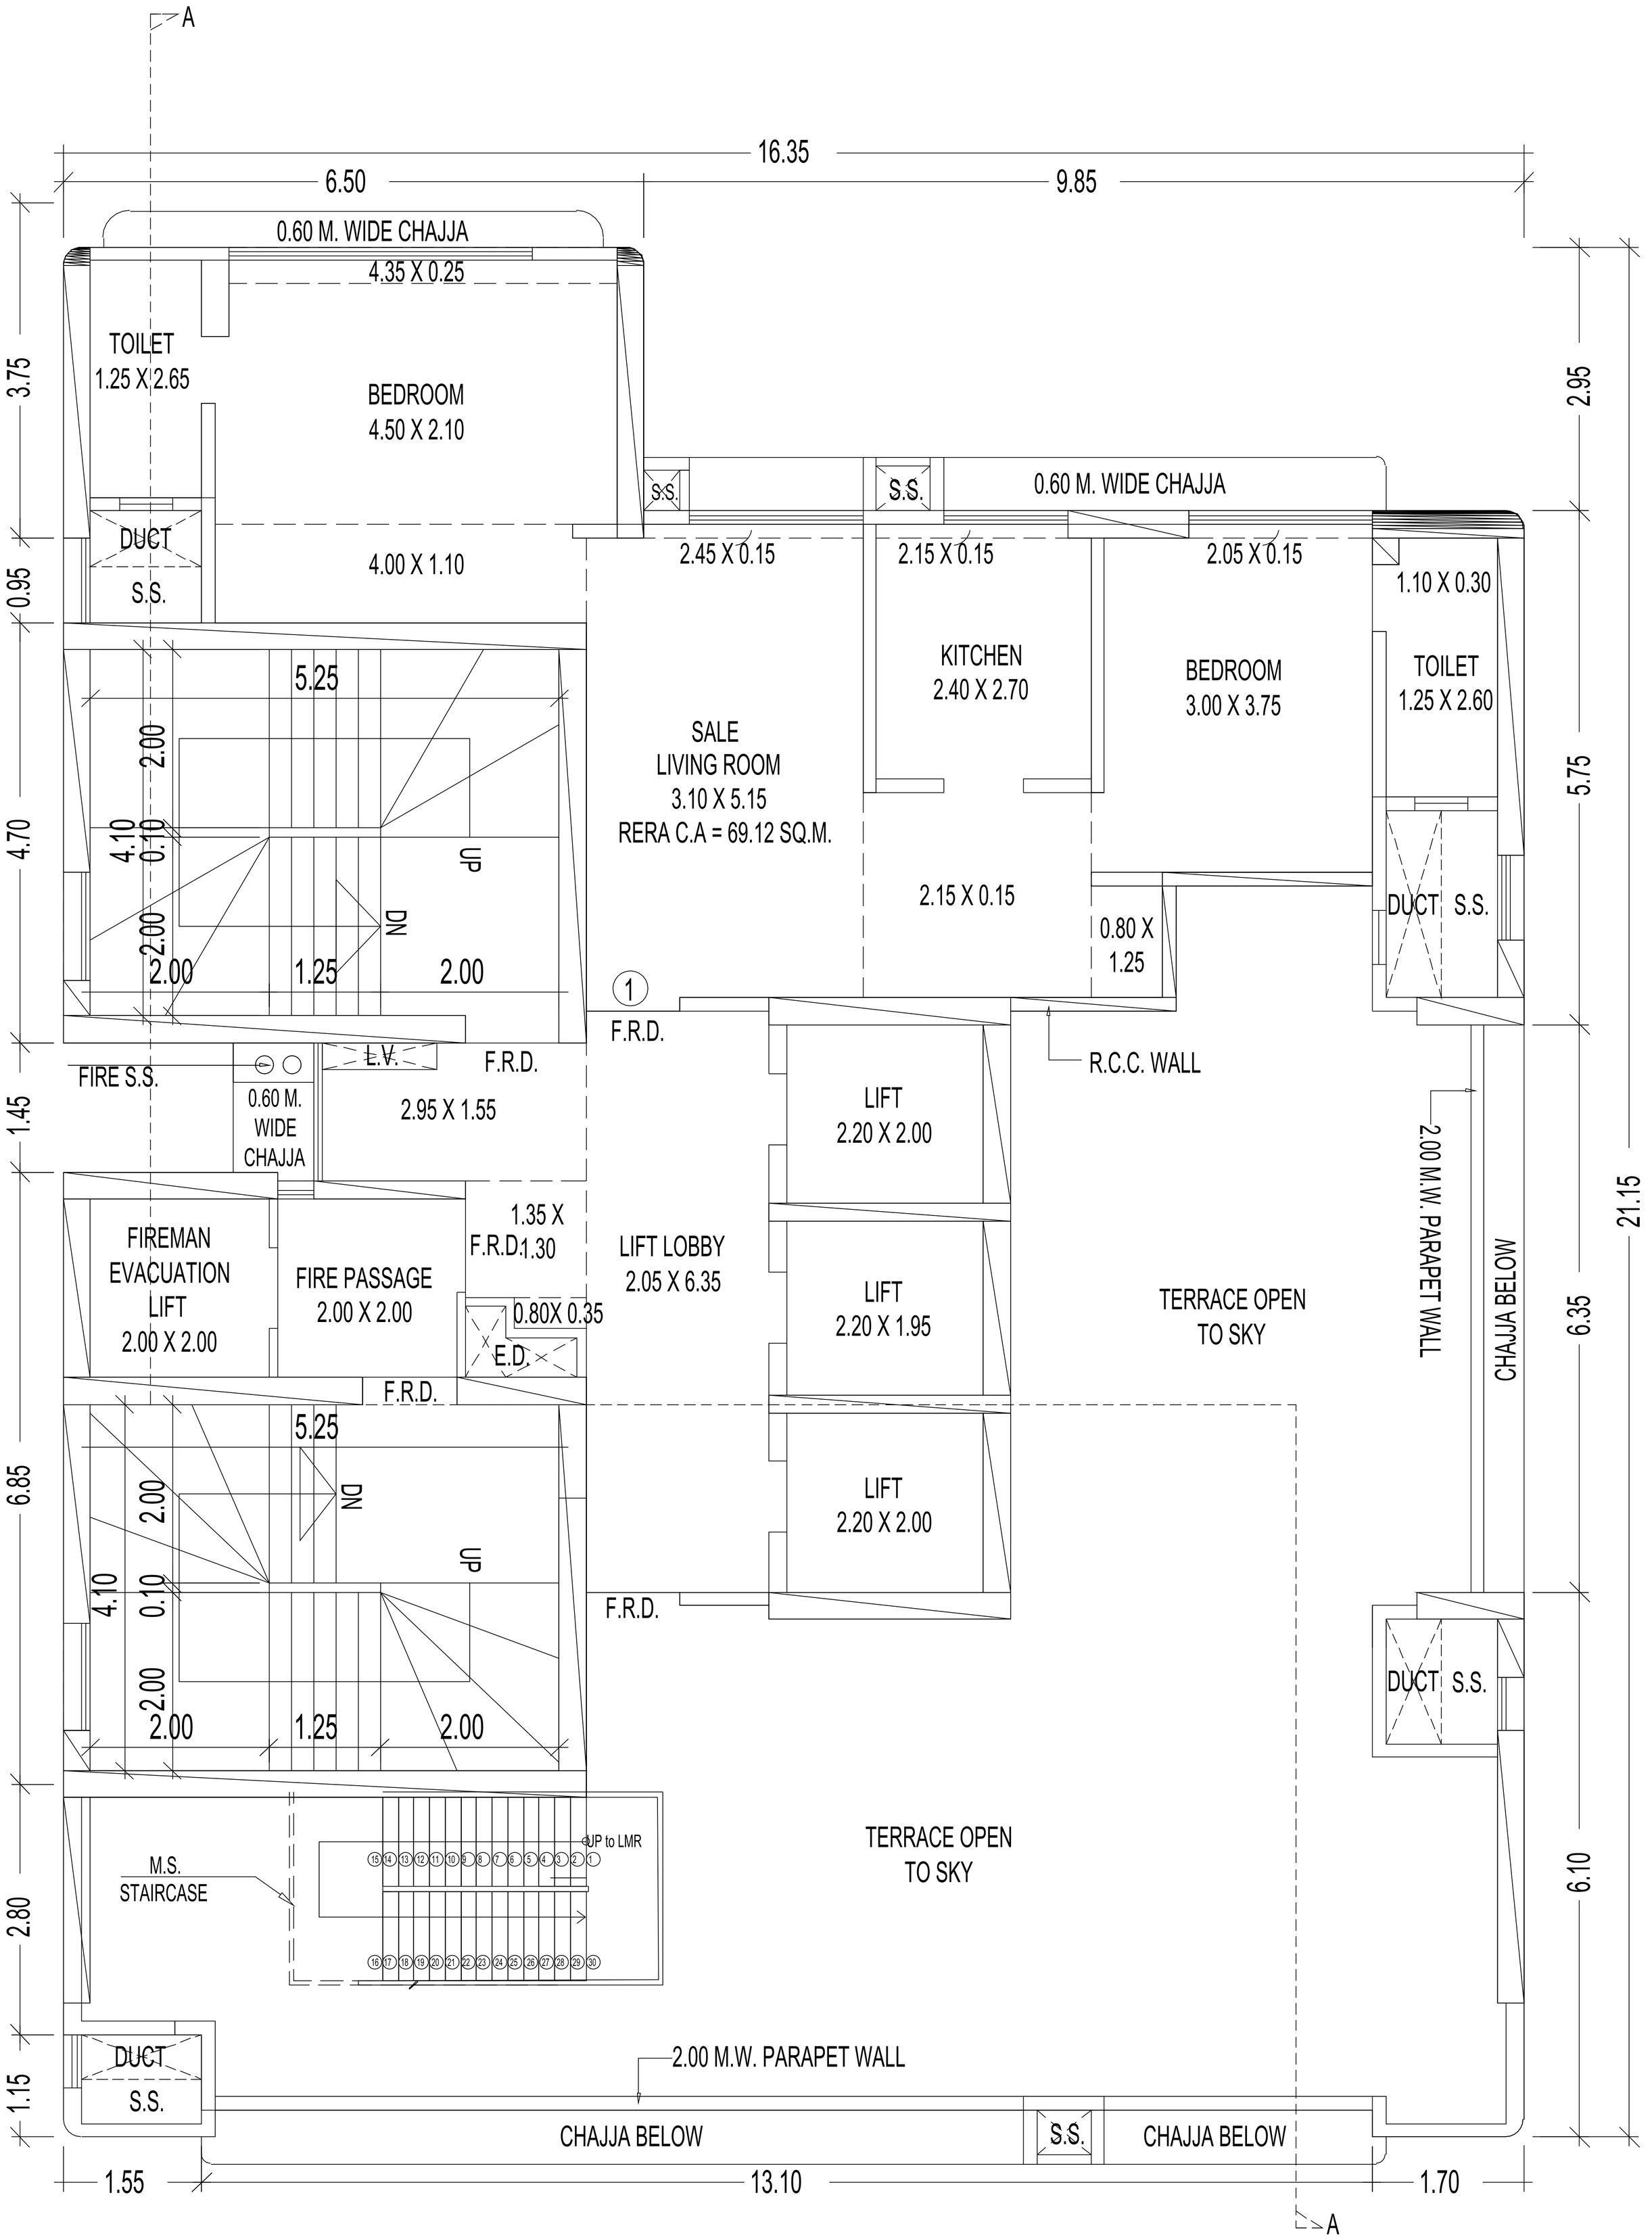

43RD FLOOR PLAN

SCALE :- 1:100

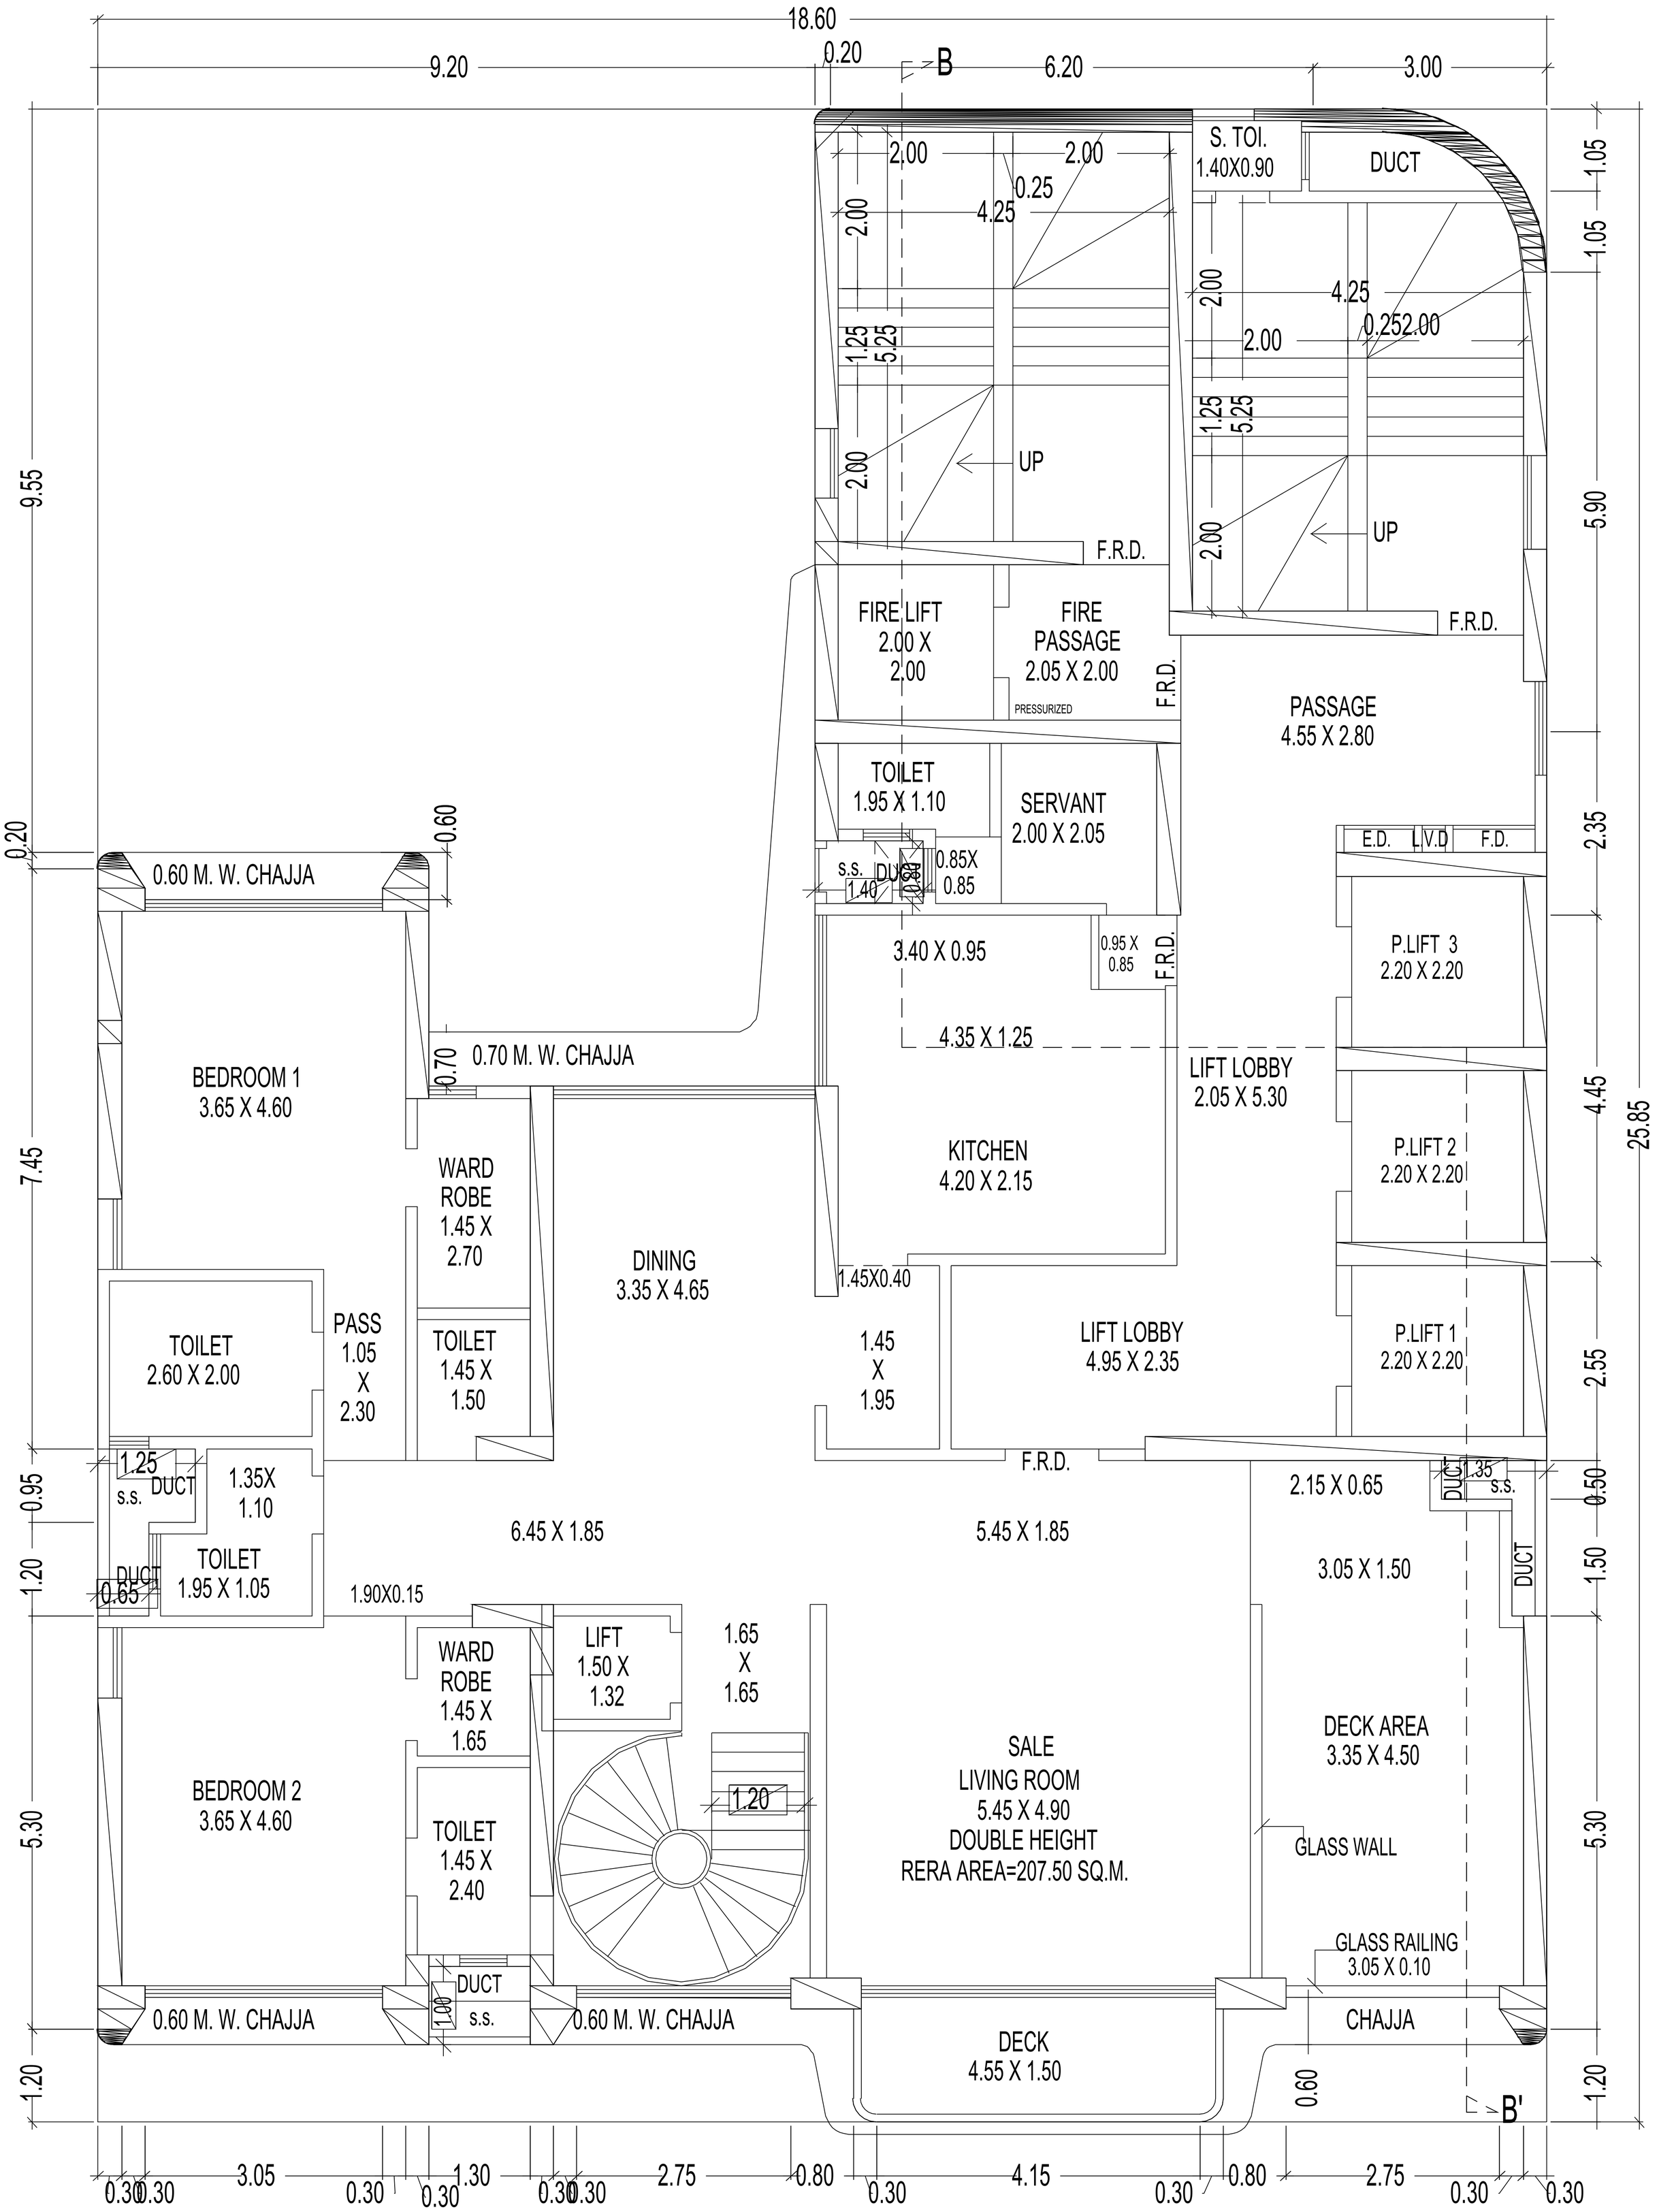

45TH,47TH,51ST DUPLEX FLOOR PLAN(LOWER PLAN)