
2ND FLOOR LINE AREA DIAGRAM

SCALE - 1: 100

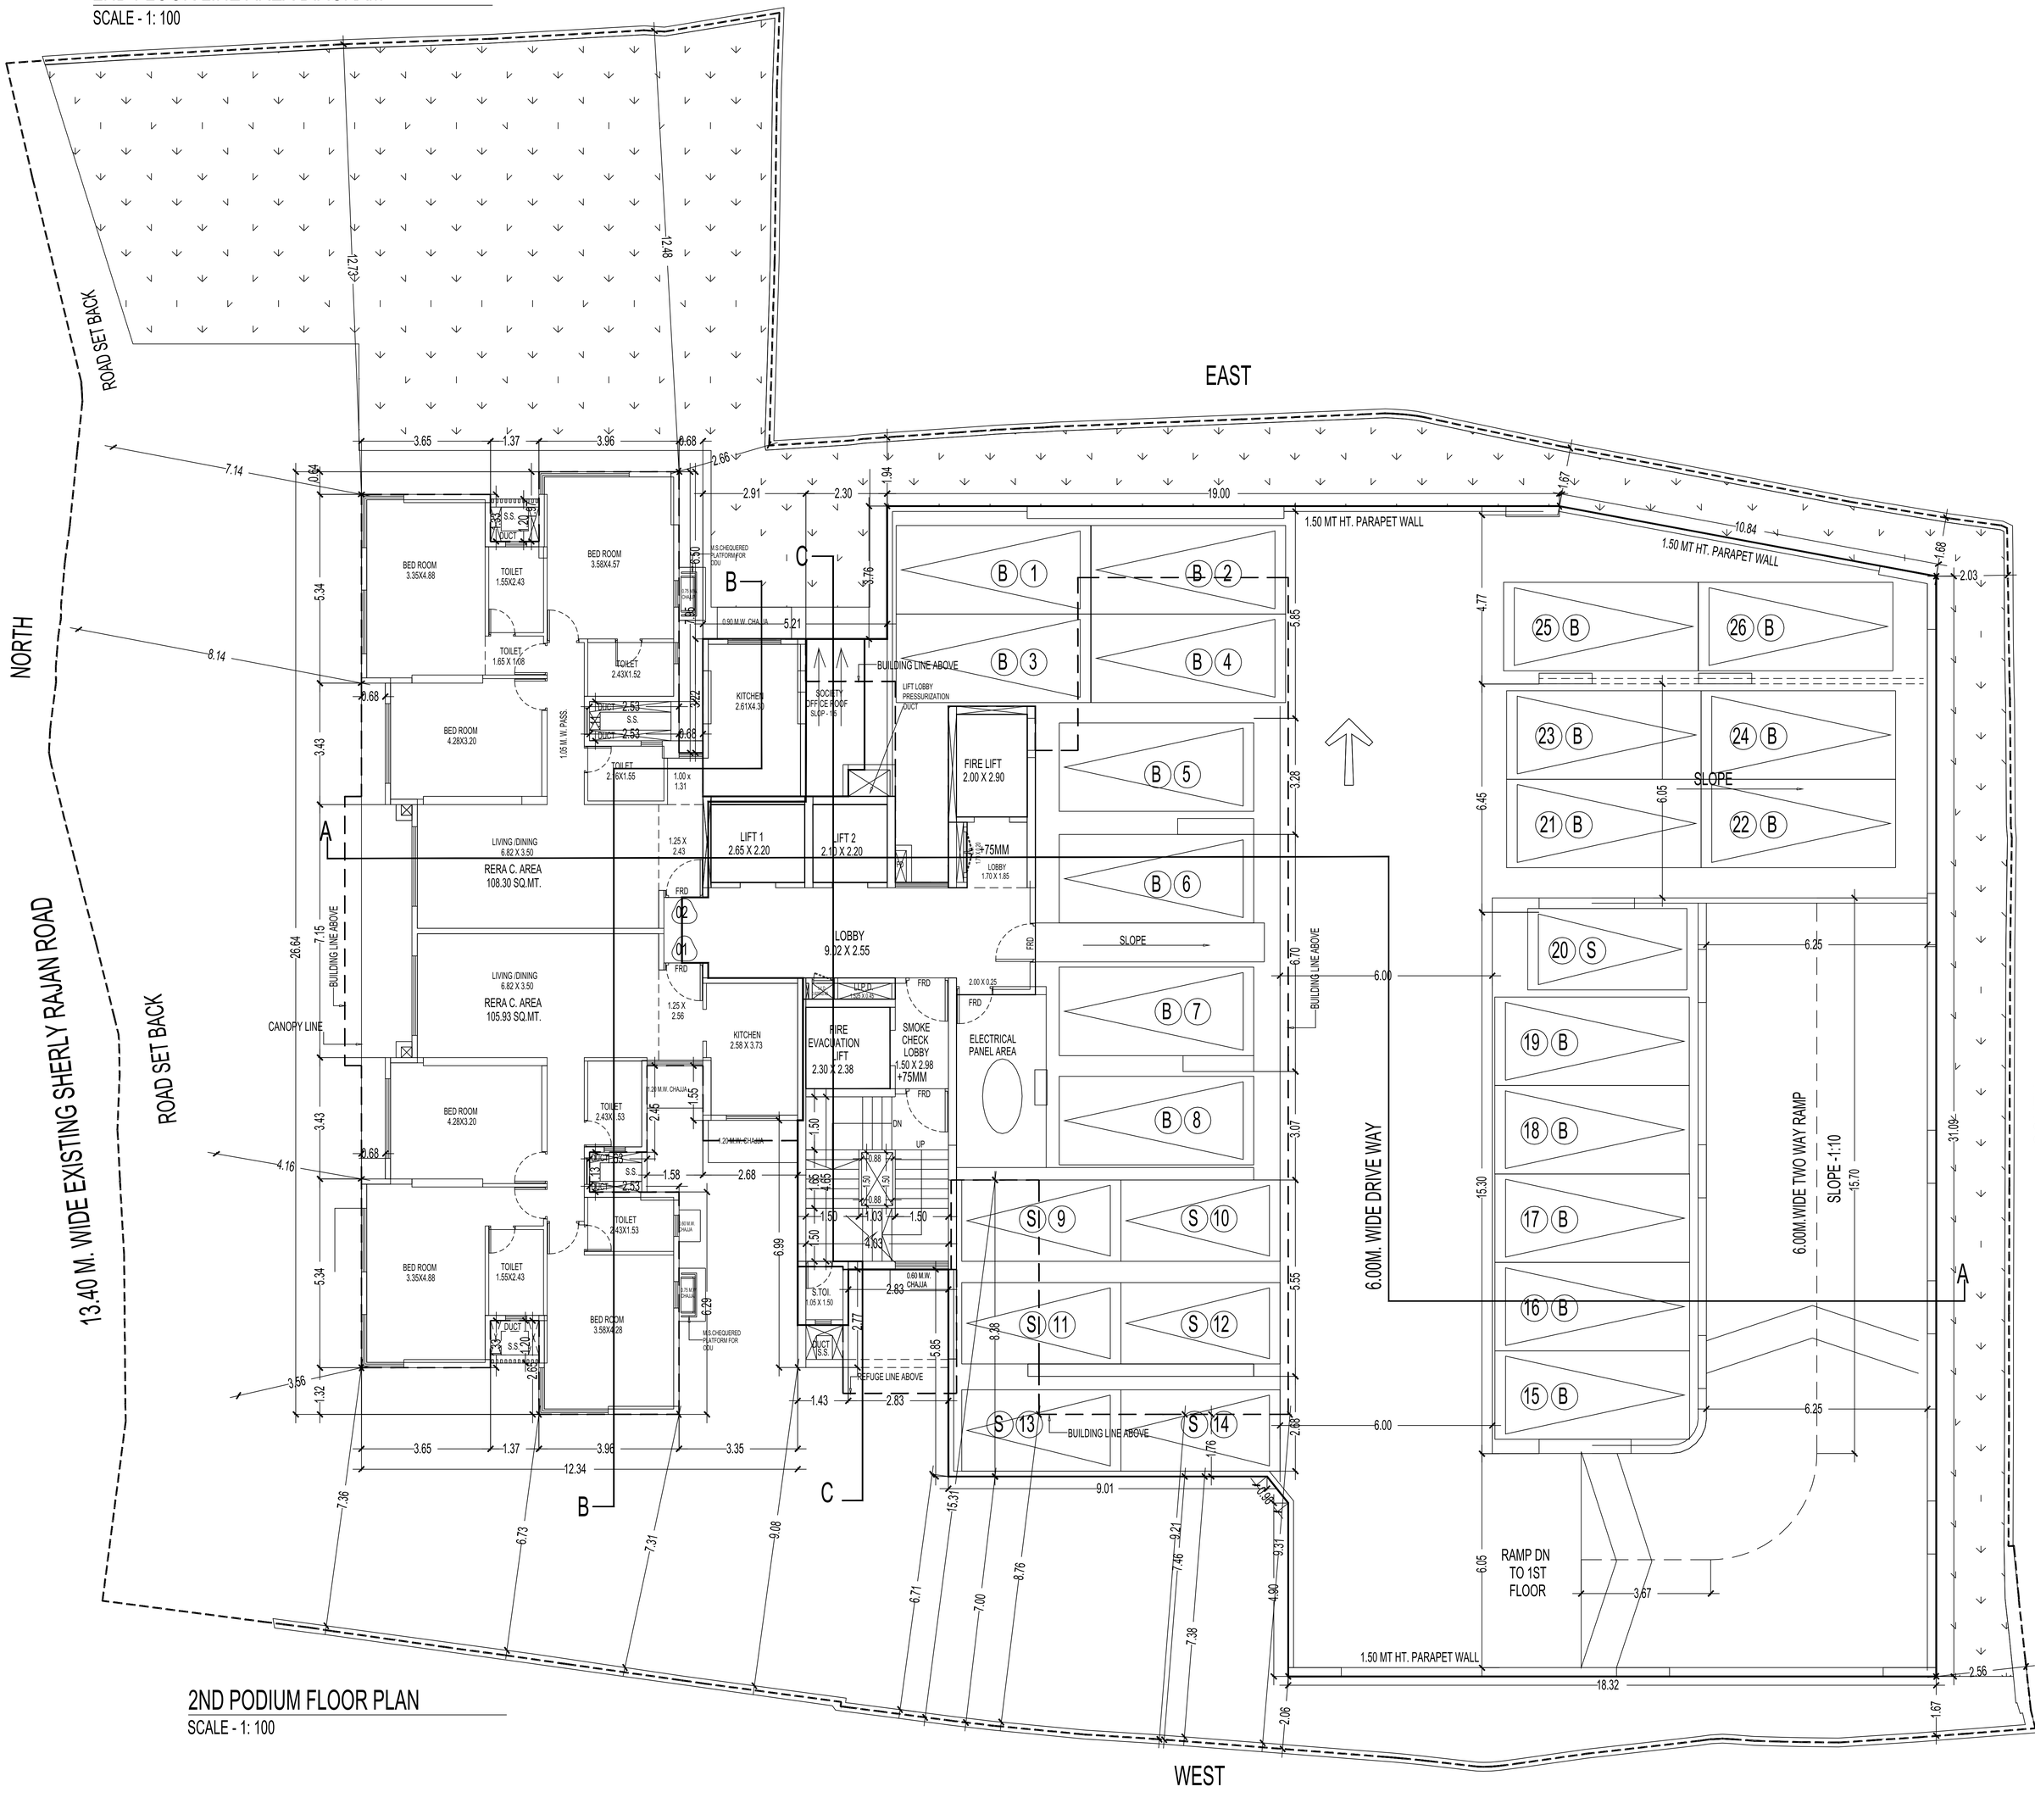

2ND PODIUM FLOOR PLAN

SCALE - 1: 100


LIFT WELL AREA DIAGRAM
@ 4TH & 5TH FLOOR
SCALE - 1: 100
L4
2.38
2.30
EAST
WEST
NORTH
SOUTH
ROAD SET BACK
13.40 M. WIDE SHERLY RAJAN ROAD
additional LOS should be in appropriate colour
BUILDING LINE ABOVE
REFUGE LINE ABOVE
BED ROOM 3.35 X 4.88
BED ROOM 3.58X4.57
BED ROOM 4.28 X 3.20
TOILET 1.55X2.43
TOILET 2.43X1.52
KITCHEN 2.61X4.30
LIFT 1 2.65 X 2.20
LIFT 2 2.10 X 2.20
FIRE LIFT 2.00 X 2.90
LOBBY 9.02 X 2.55
LOBBY 1.70 X 1.85
RERA C. AREA 110.81 SQ.MT.
LIVING /DINING 8.08X3.65
LIVING /DINING 8.08X3.35
RERA C. AREA 105.97 SQ.MT.
KITCHEN 2.58 X 3.73
FIRE EVACUATION LIFT 2.30 X 2.38
SMOKE CHECK LOBBY 1.50 X 2.98 +75MM
KITCHEN 2.46X3.05
KITCHEN 1.85X2.13
BED ROOM 2.58X3.21
TOILET 1.35 X 2.13
LIVING /DINING 3.25X3.05
RERA C. AREA 27.66 SQ.MT.
LIVING/DINING 6.10X3.05
RERA C. AREA 67.34 SQ.MT.
BED ROOM 3.35X3.15
BED ROOM 3.30X4.28
TOILET 1.35X2.13
TOILET 2.15X1.52
FITNESS CENTER ROOF
SLOP - 1:5
COLUMN COUNTED IN FSI
BEAM
M.S.CHEQUERED PLATFORM FOR ODU
0.75 M.W. CHAJJA
0.60 M.W. CHAJJA
0.90 M.W. CHAJJA
1.05 M. W. PASS.
1.13 M. W. PASS.
DUCT
S.S.
FRD
LIFT
UP
DN
TIE BEAM @ MIDLANDING LEVEL
BUILDING LINE ABOVE
REFUGE LINE ABOVE
4TH FLOOR PLAN
SCALE - 1: 100

5TH FLOOR LINE AREA DIAGRAM

SCALE - 1: 100

SCALE - 1: 100

Show elevation features in drawing as mentioned in Indicatieve report

NORTH

SOUTH

EAST

WEST

13.40 M. WIDE SHERLY RAJAN ROAD

ROAD SET BACK

ROAD SET BACK

RERA C. AREA 110.81 SQ.MT.

RERA C. AREA 105.97 SQ.MT.

RERA C. AREA 41.53 SQ.MT.

RERA C. AREA 67.34 SQ.MT.

LIFT 1 2.65 X 2.20

LIFT 2 2.10 X 2.20

FIRE LIFT 2.00 X 2.90

LOBBY 9.02 X 2.55

FIRE EVACUATION LIFT 2.30 X 2.38

SMOKE CHECK LOBBY 1.50 X 2.98 +75MM

BUILDING LINE ABOVE

COLUMN COUNTED IN FSI

BEAM AT FLOOR LVL

REFUGE LINE ABOVE

TIE BEAM @ MIDLANDING LEVEL

M.S.CHEQUERED PLATFORM FOR ODU

0.60 M.W. CHAJJA

0.75 M.W. CHAJJA

0.90 M.W. CHAJJA

1.05 M. W. PASS.

1.13 M. W. PASS.

5TH FLOOR PLAN

SCALE - 1: 100




6TH FLOOR PLAN

SCALE - 1: 100

LIFT WELL AREA DIAGRAM


@ 6TH TO 9TH FLOOR

SCALE - 1: 100

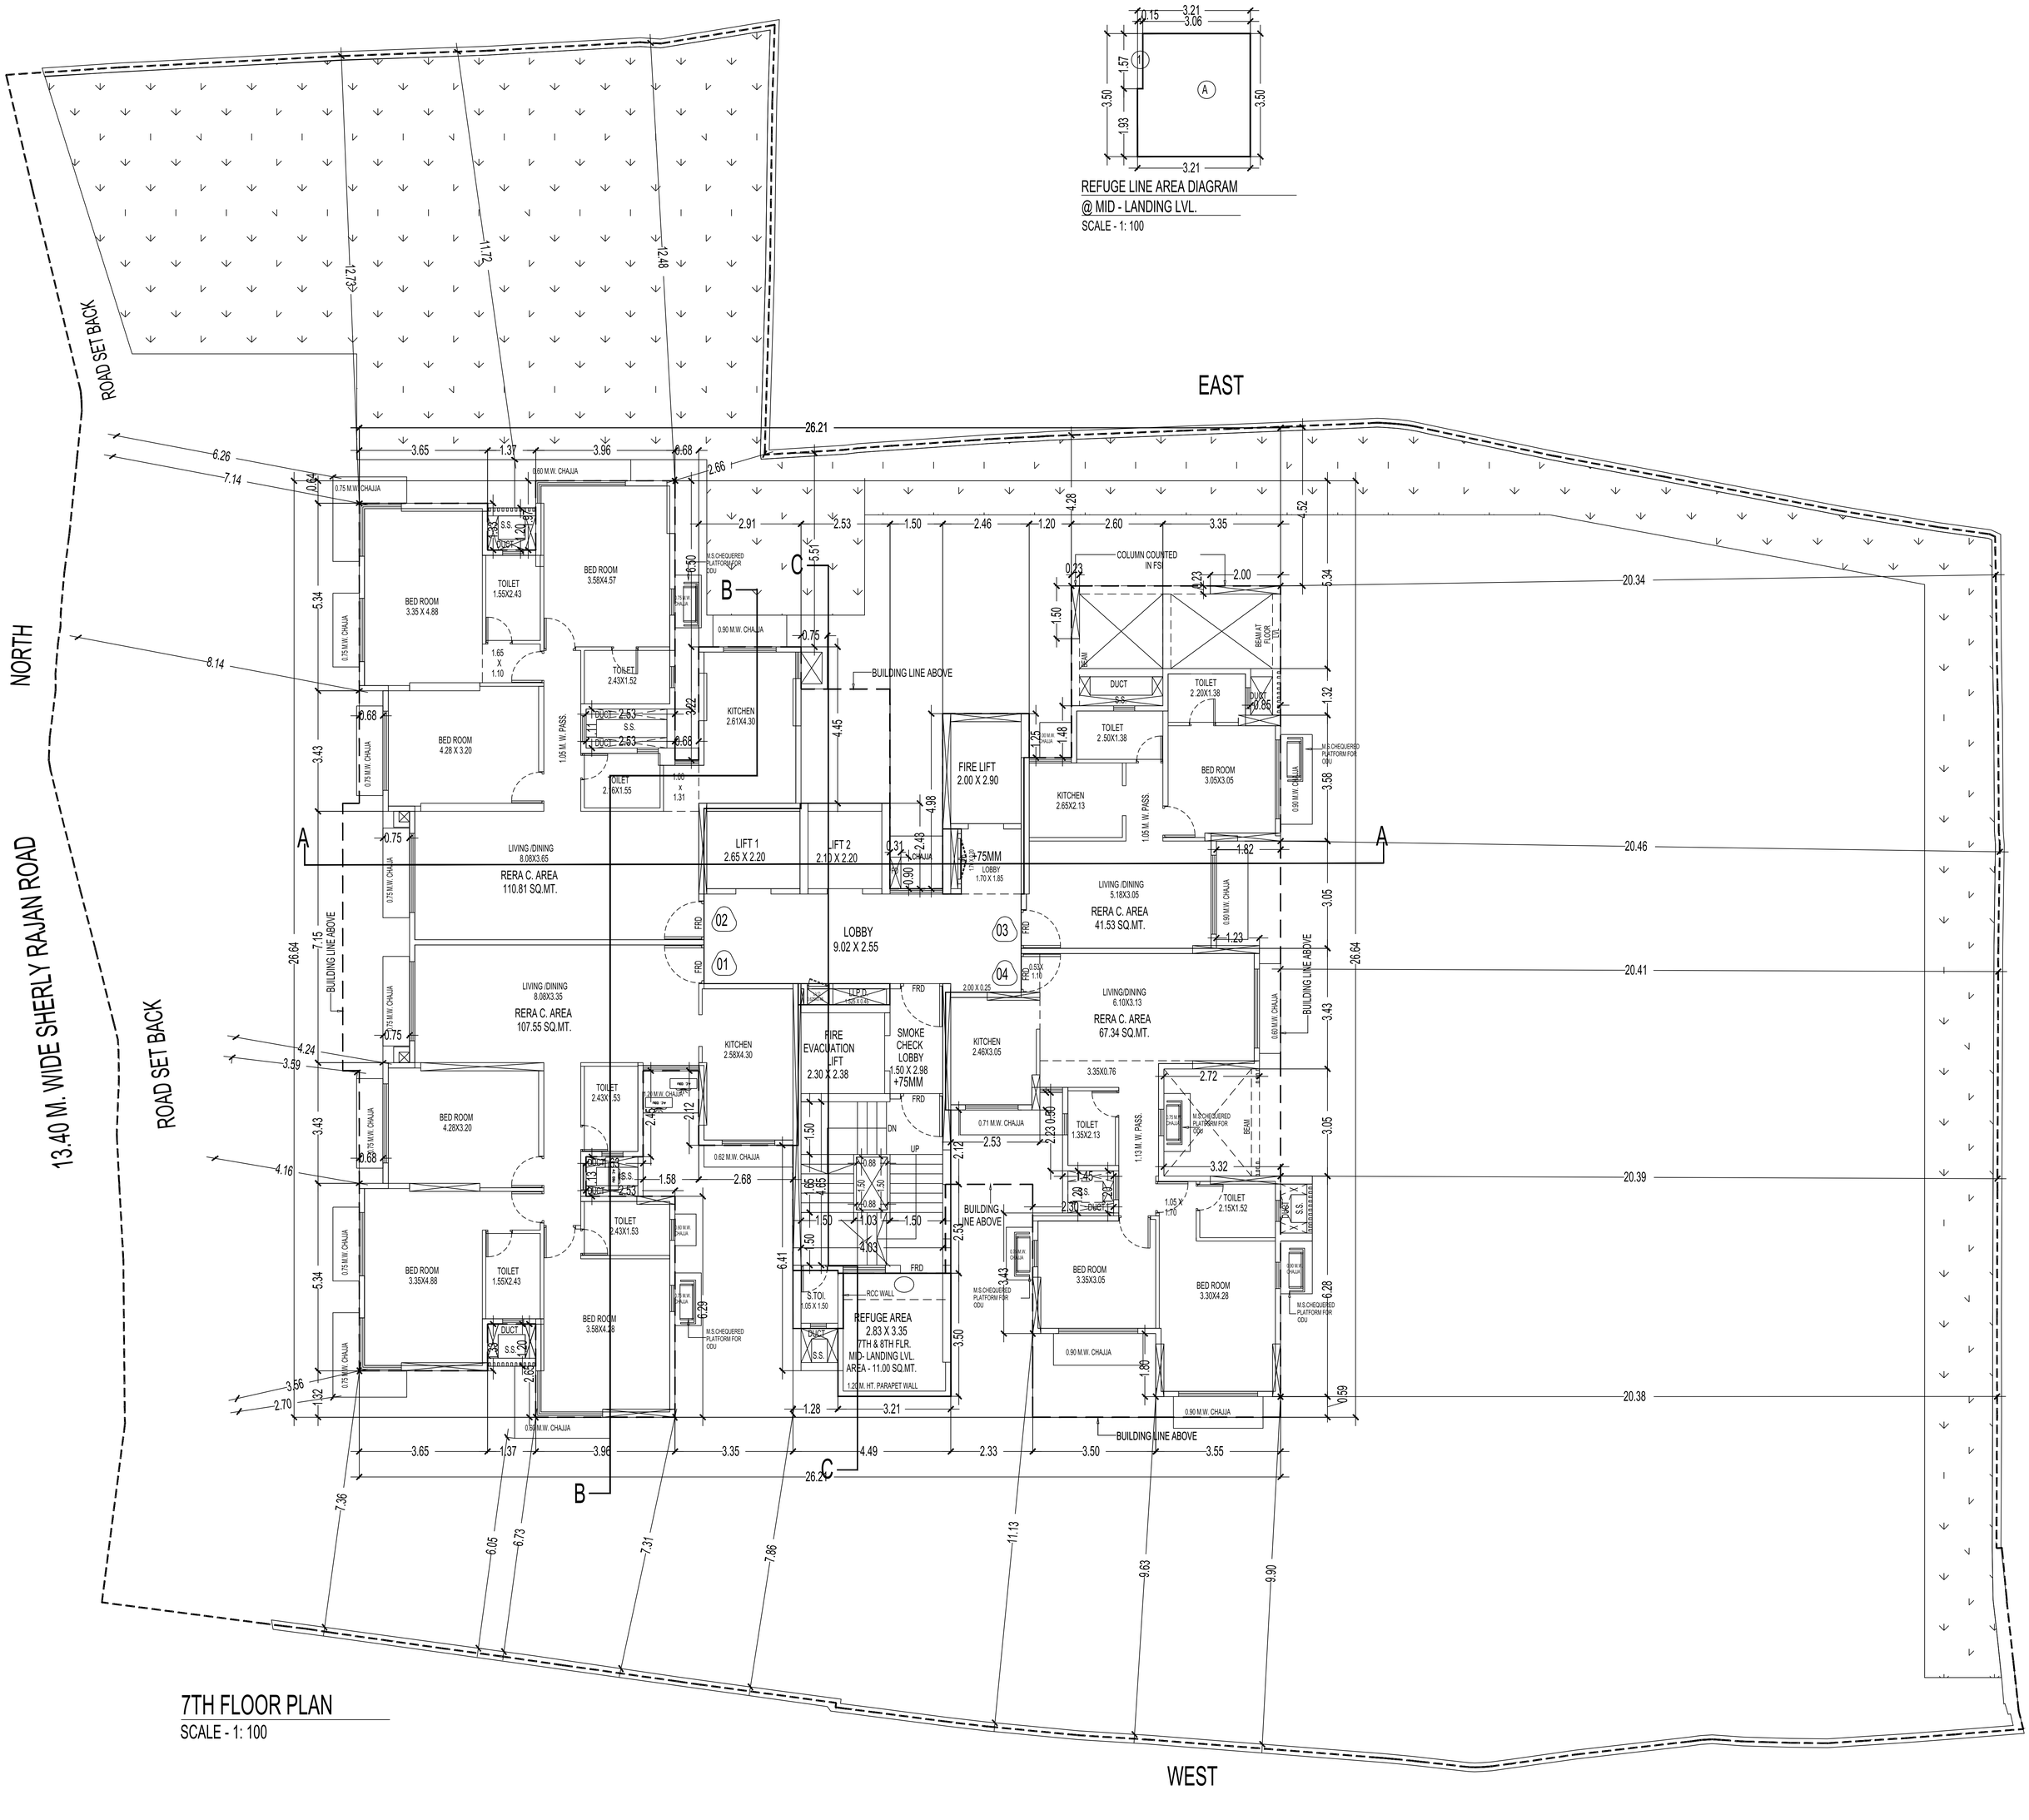
NORTH
EAST
WEST
13.40 M. WIDE SHERLY RAJAN ROAD
ROAD SET BACK
ROAD SET BACK
BUILDING LINE ABOVE
BUILDING LINE ABOVE
BUILDING LINE ABOVE


8TH & 9TH FLOOR LINE AREA DIAGRAM

SCALE - 1: 100

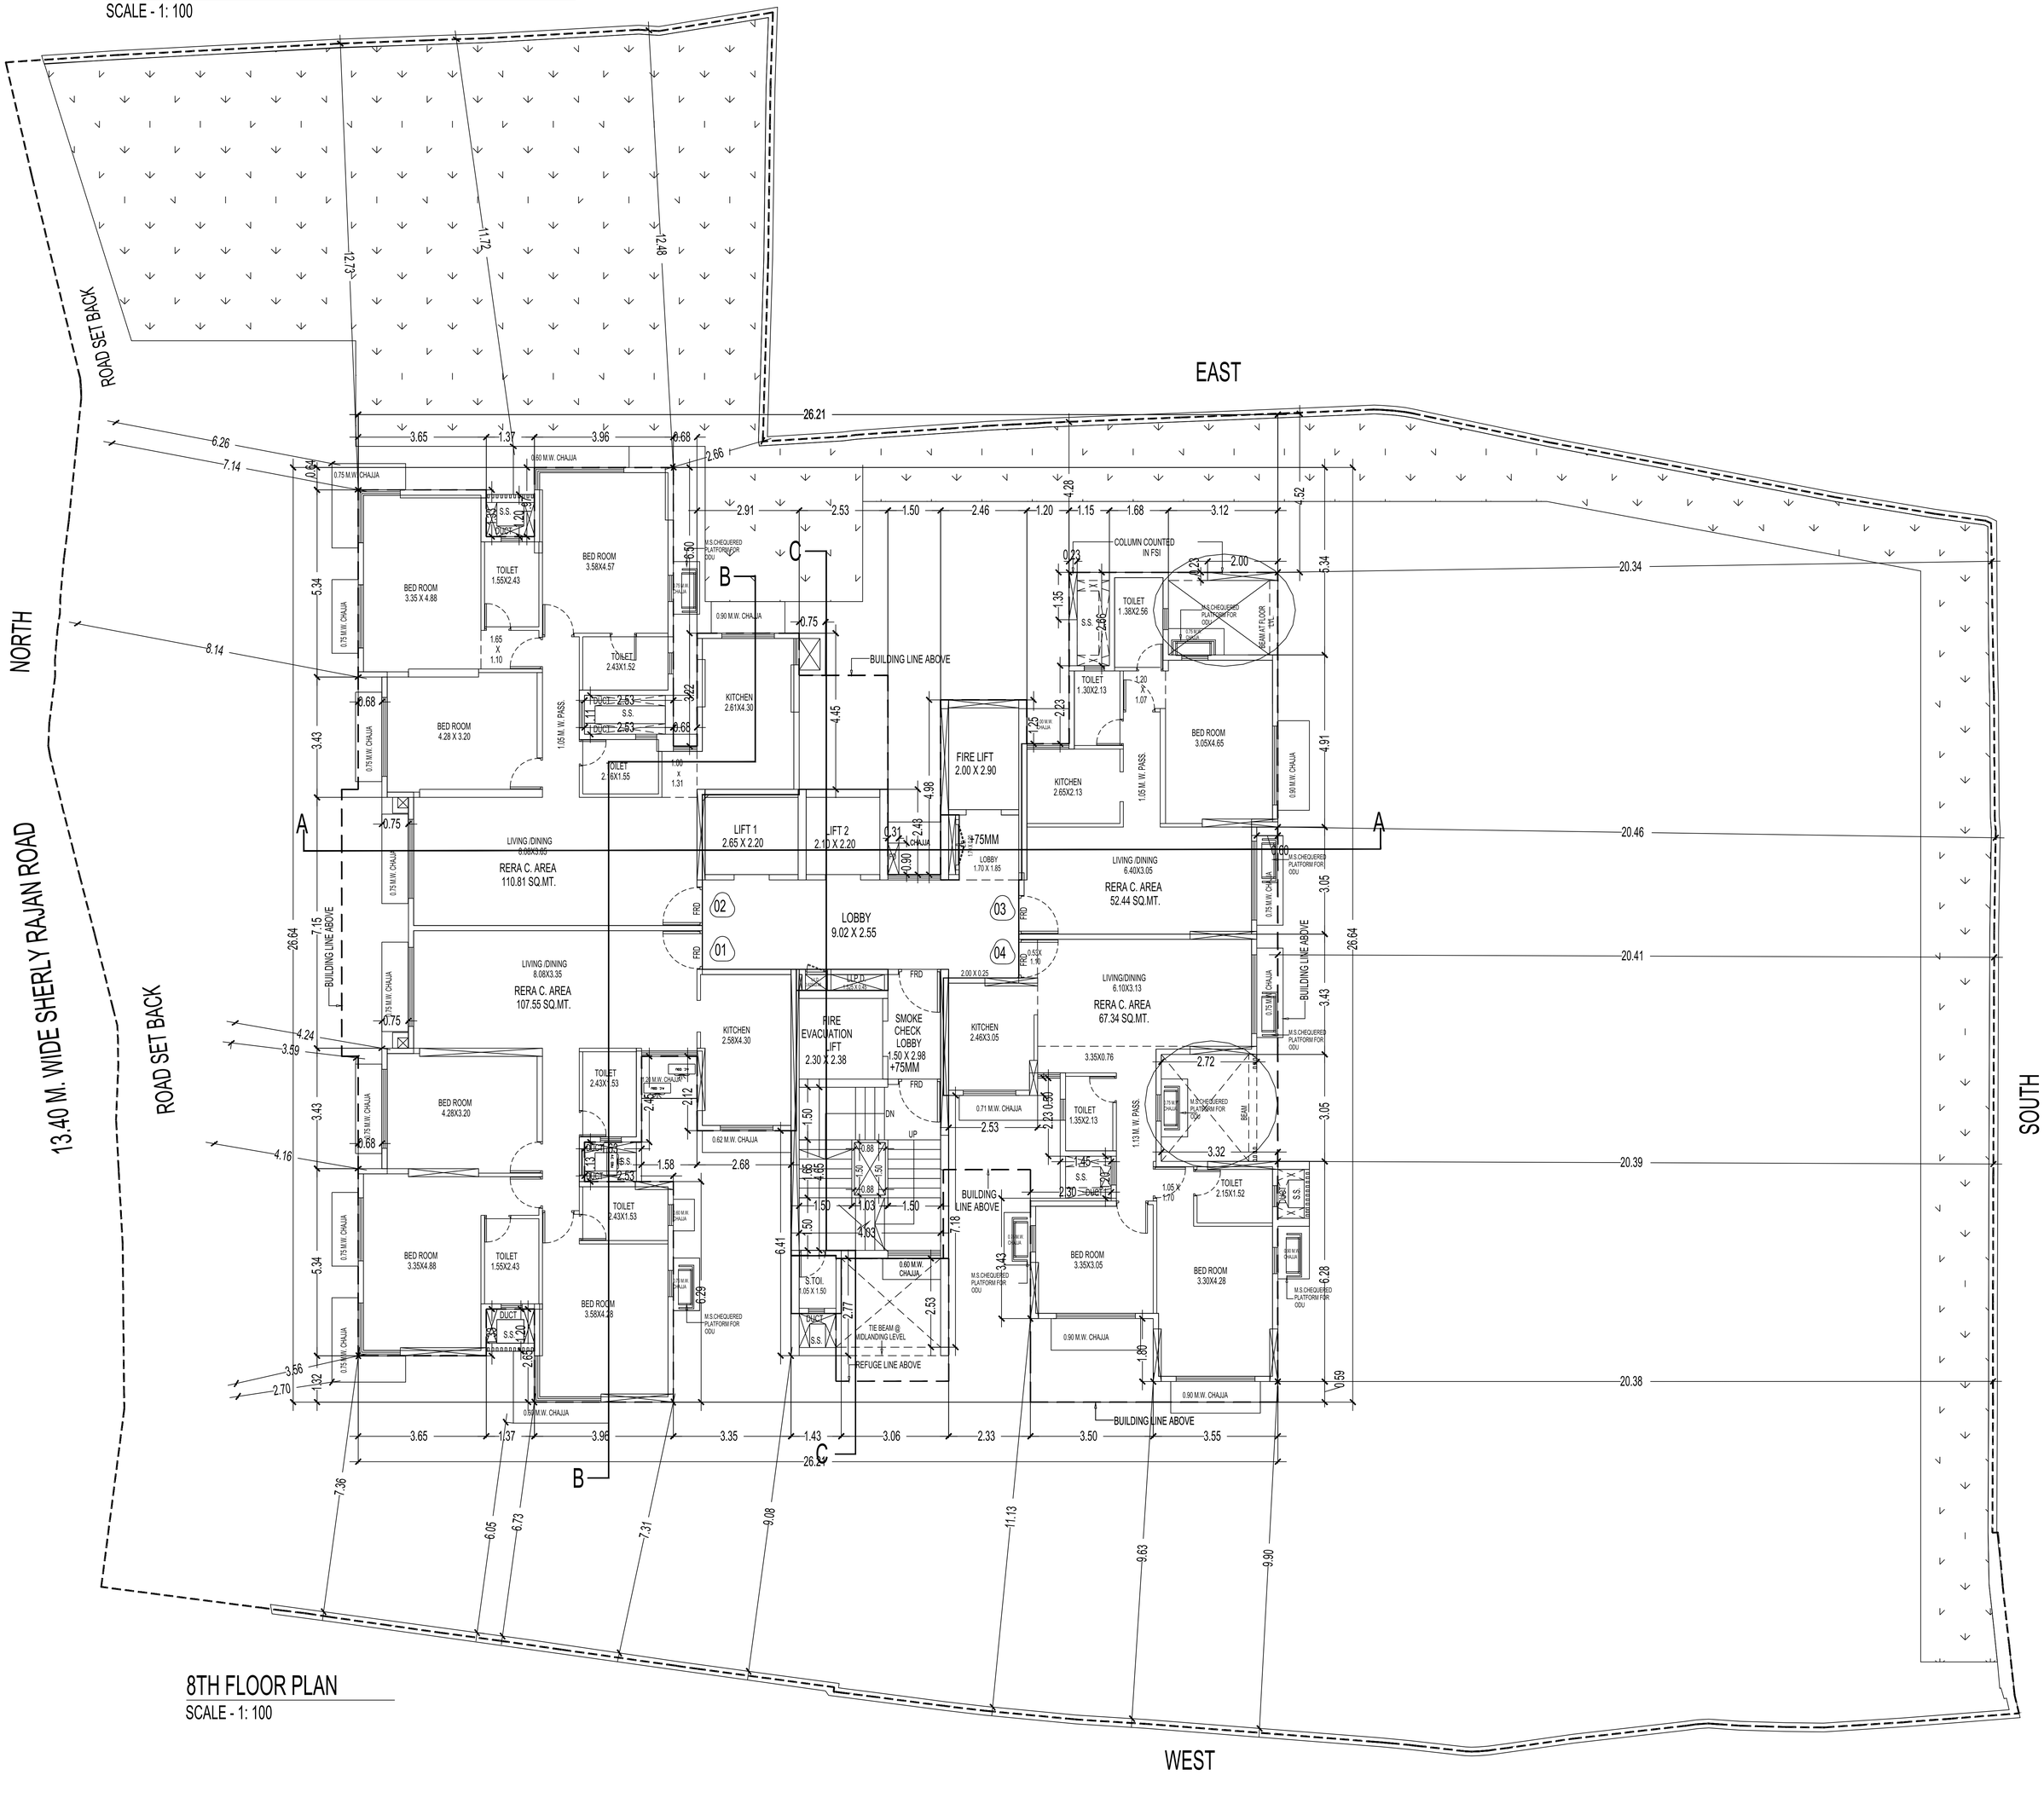

8TH FLOOR PLAN

SCALE - 1: 100

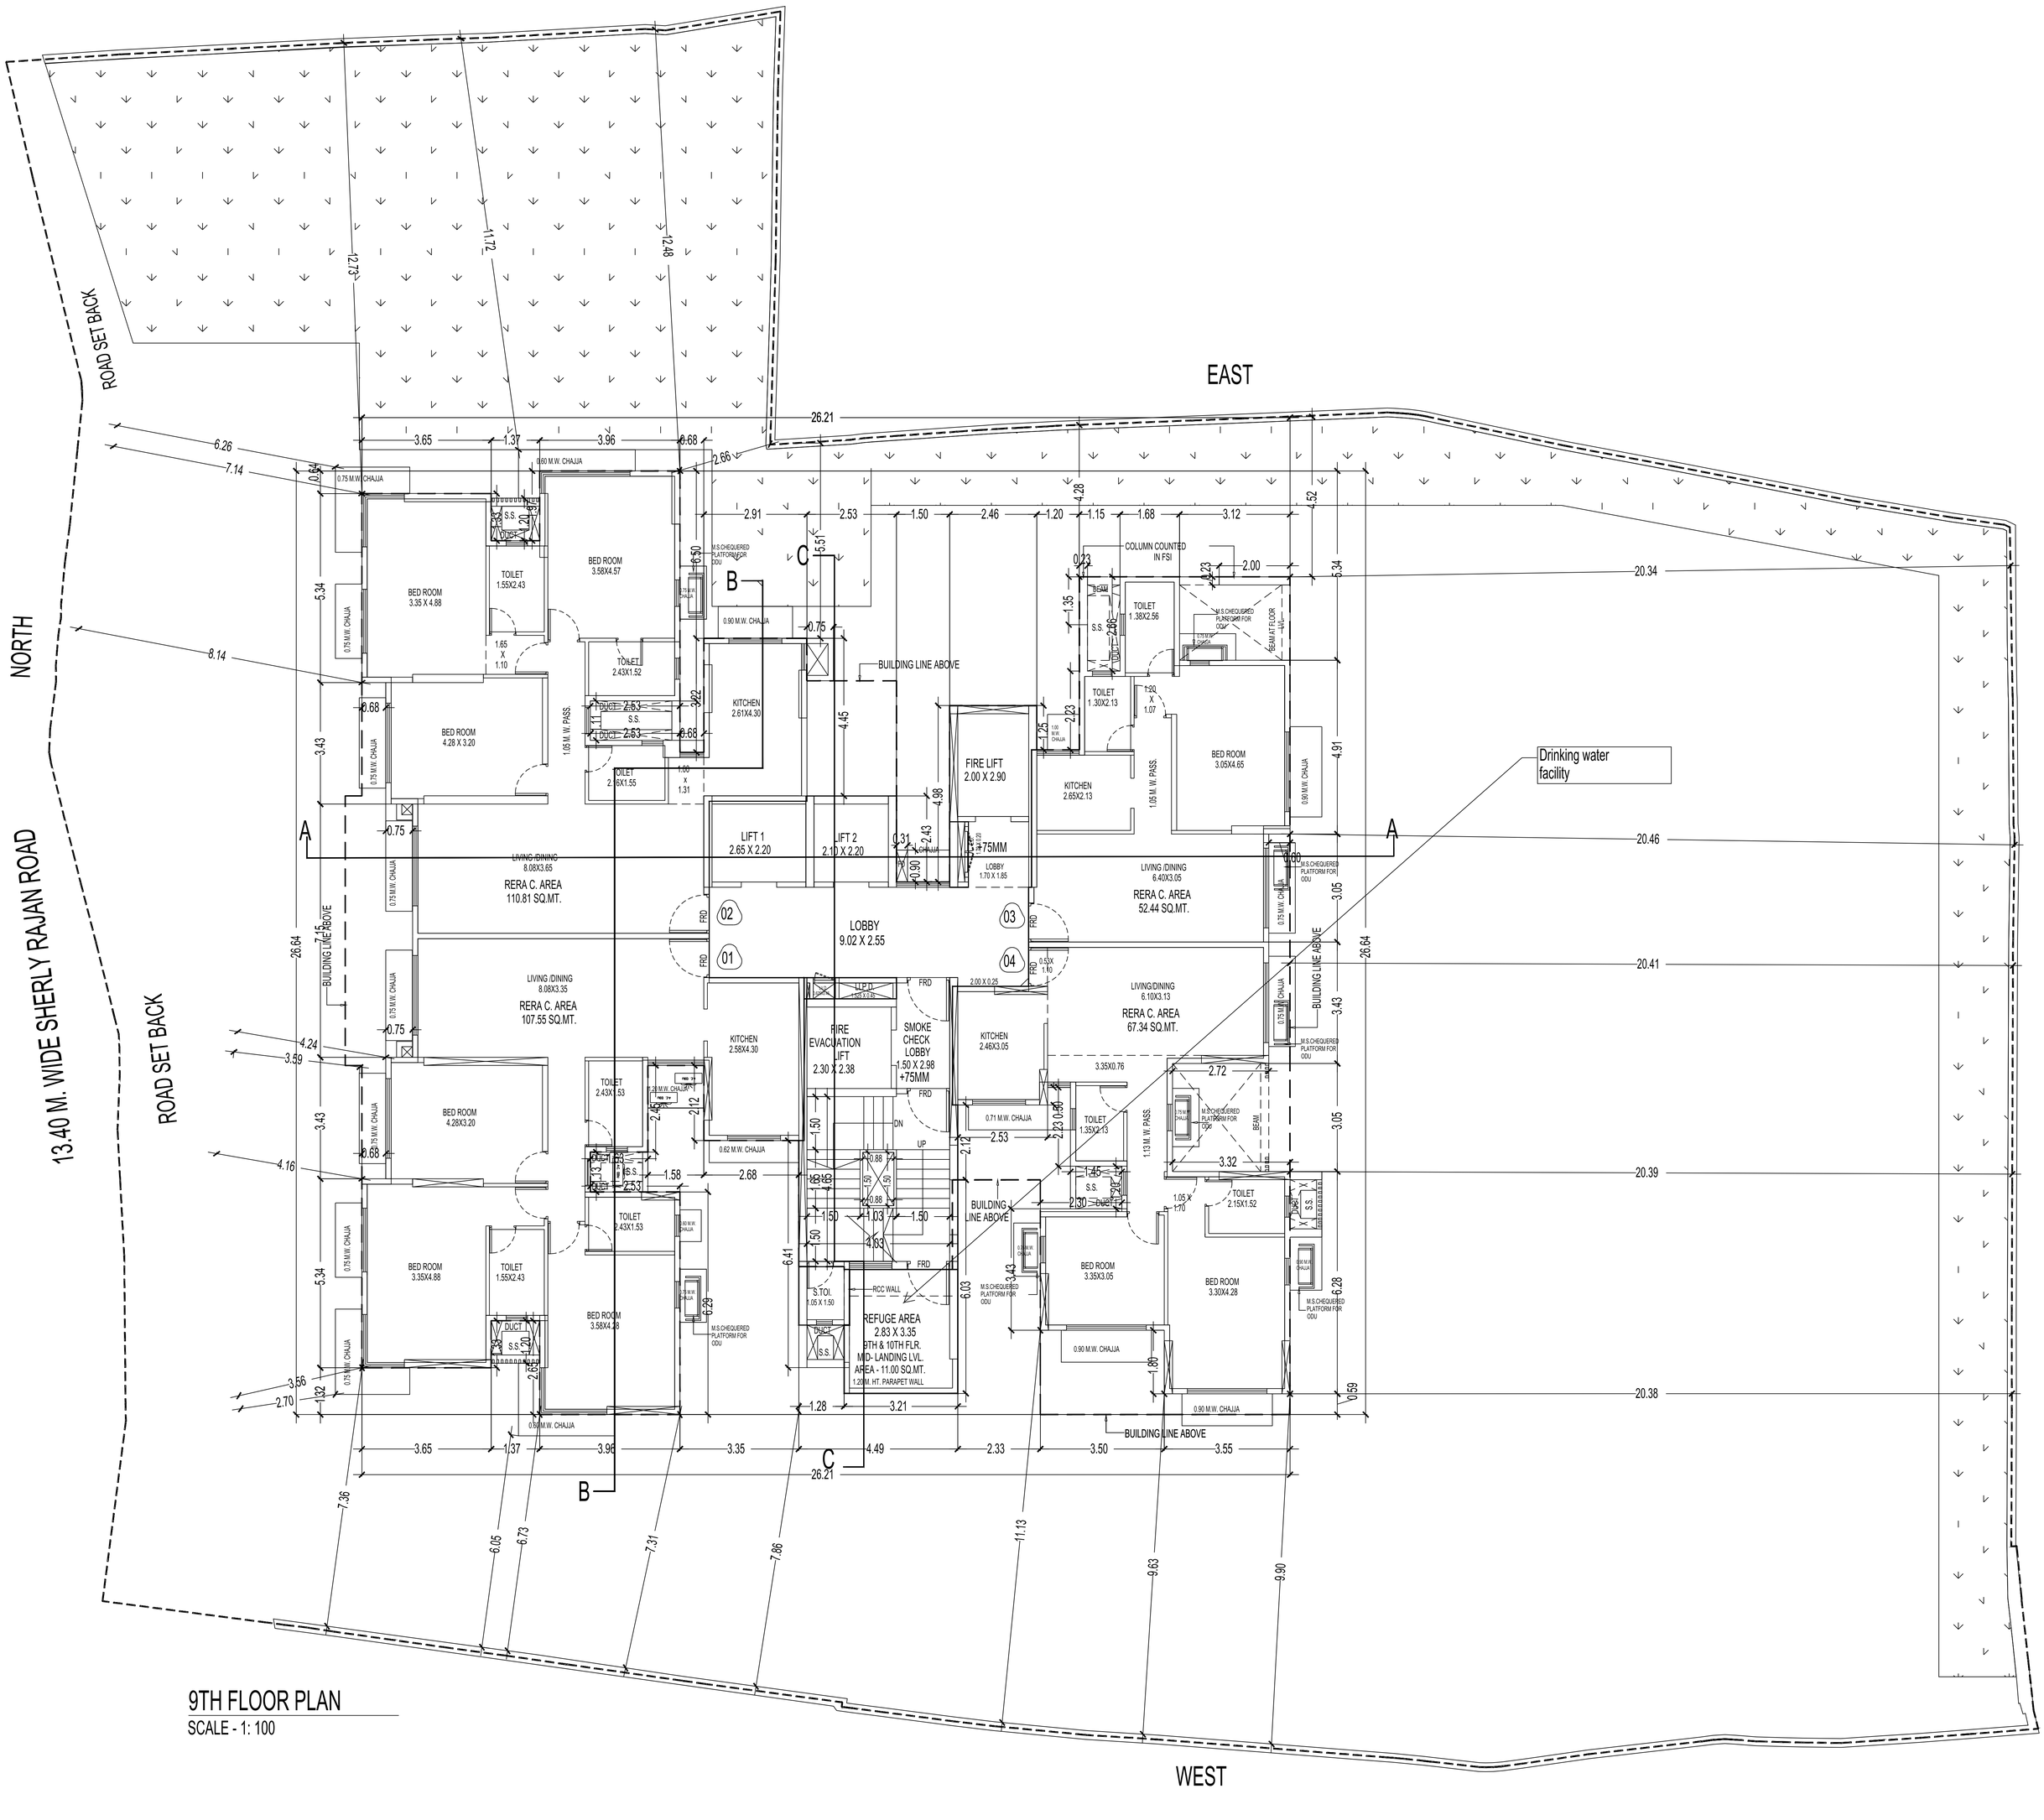

9TH FLOOR PLAN

SCALE - 1: 100

SCALE - 1: 100

NORTH

EAST

SOUTH

WEST

ROAD SET BACK

ROAD SET BACK

13.40 M. WIDE SHERLY RAJAN ROAD

BED ROOM 3.35 X 4.88

BED ROOM 4.95 X 3.20

BED ROOM 3.58X4.57

TOILET 1.55X2.43

TOILET 2.43X1.52

TOILET 2.16X1.55

KITCHEN 2.61X4.30

LIVING /DINING 6.72 X 3.50

RERA C. AREA 117.39 SQ.MT.

LIFT 1 2.65 X 2.20

LIFT 2 2.10 X 2.20

FIRE LIFT 2.00 X 2.90

LOBBY 9.02 X 2.55

LOBBY 1.70 X 1.85

LIVING /DINING 6.72X3.50

RERA C. AREA 116.59 SQ.MT.

BED ROOM 4.95X3.20

BED ROOM 3.35X4.88

BED ROOM 3.58X4.28

TOILET 2.43X1.53

TOILET 1.55X2.43

KITCHEN 2.58X4.30

FIRE EVACUATION LIFT 2.30 X 2.38

SMOKE CHECK LOBBY 1.50 X 2.98 +75MM

KITCHEN 2.44X3.05

LIVING/DINING 6.10X3.05

RERA C. AREA 72.95 SQ.MT.

TOILET 2.12X1.43

TOILET 2.20X1.53

TOILET 2.15X1.52

BED ROOM 3.35X3.15

BED ROOM 3.30X4.28

LIVING /DINING 6.40X3.05

RERA C. AREA 59.79 SQ.MT.

TOILET 2.560X1350

TOILET 1.30X2.13

KITCHEN 2.65X2.13

BED ROOM 3.05x3.65

BED ROOM 3.05X3.05

BUILDING LINE ABOVE

REFUGE LINE ABOVE

COLUMN COUNTED IN FSI

M.S.CHEQUERED PLATFORM FOR ODU

0.90 M.W. CHAJJA

0.75 M.W. CHAJJA

0.60 M.W. CHAJJA

0.50 M.W. CHAJJA

1.65 M.W. DECK

1.05 M. W. PASS.

1210MM. WIDE PASS.

DUCT

S.S.

TIE BEAM @ MDJANDING LEVEL

26.67

20.34

20.46

20.41


20.39

20.38

10TH FLOOR PLAN

SCALE - 1: 100

SCALE - 1: 100

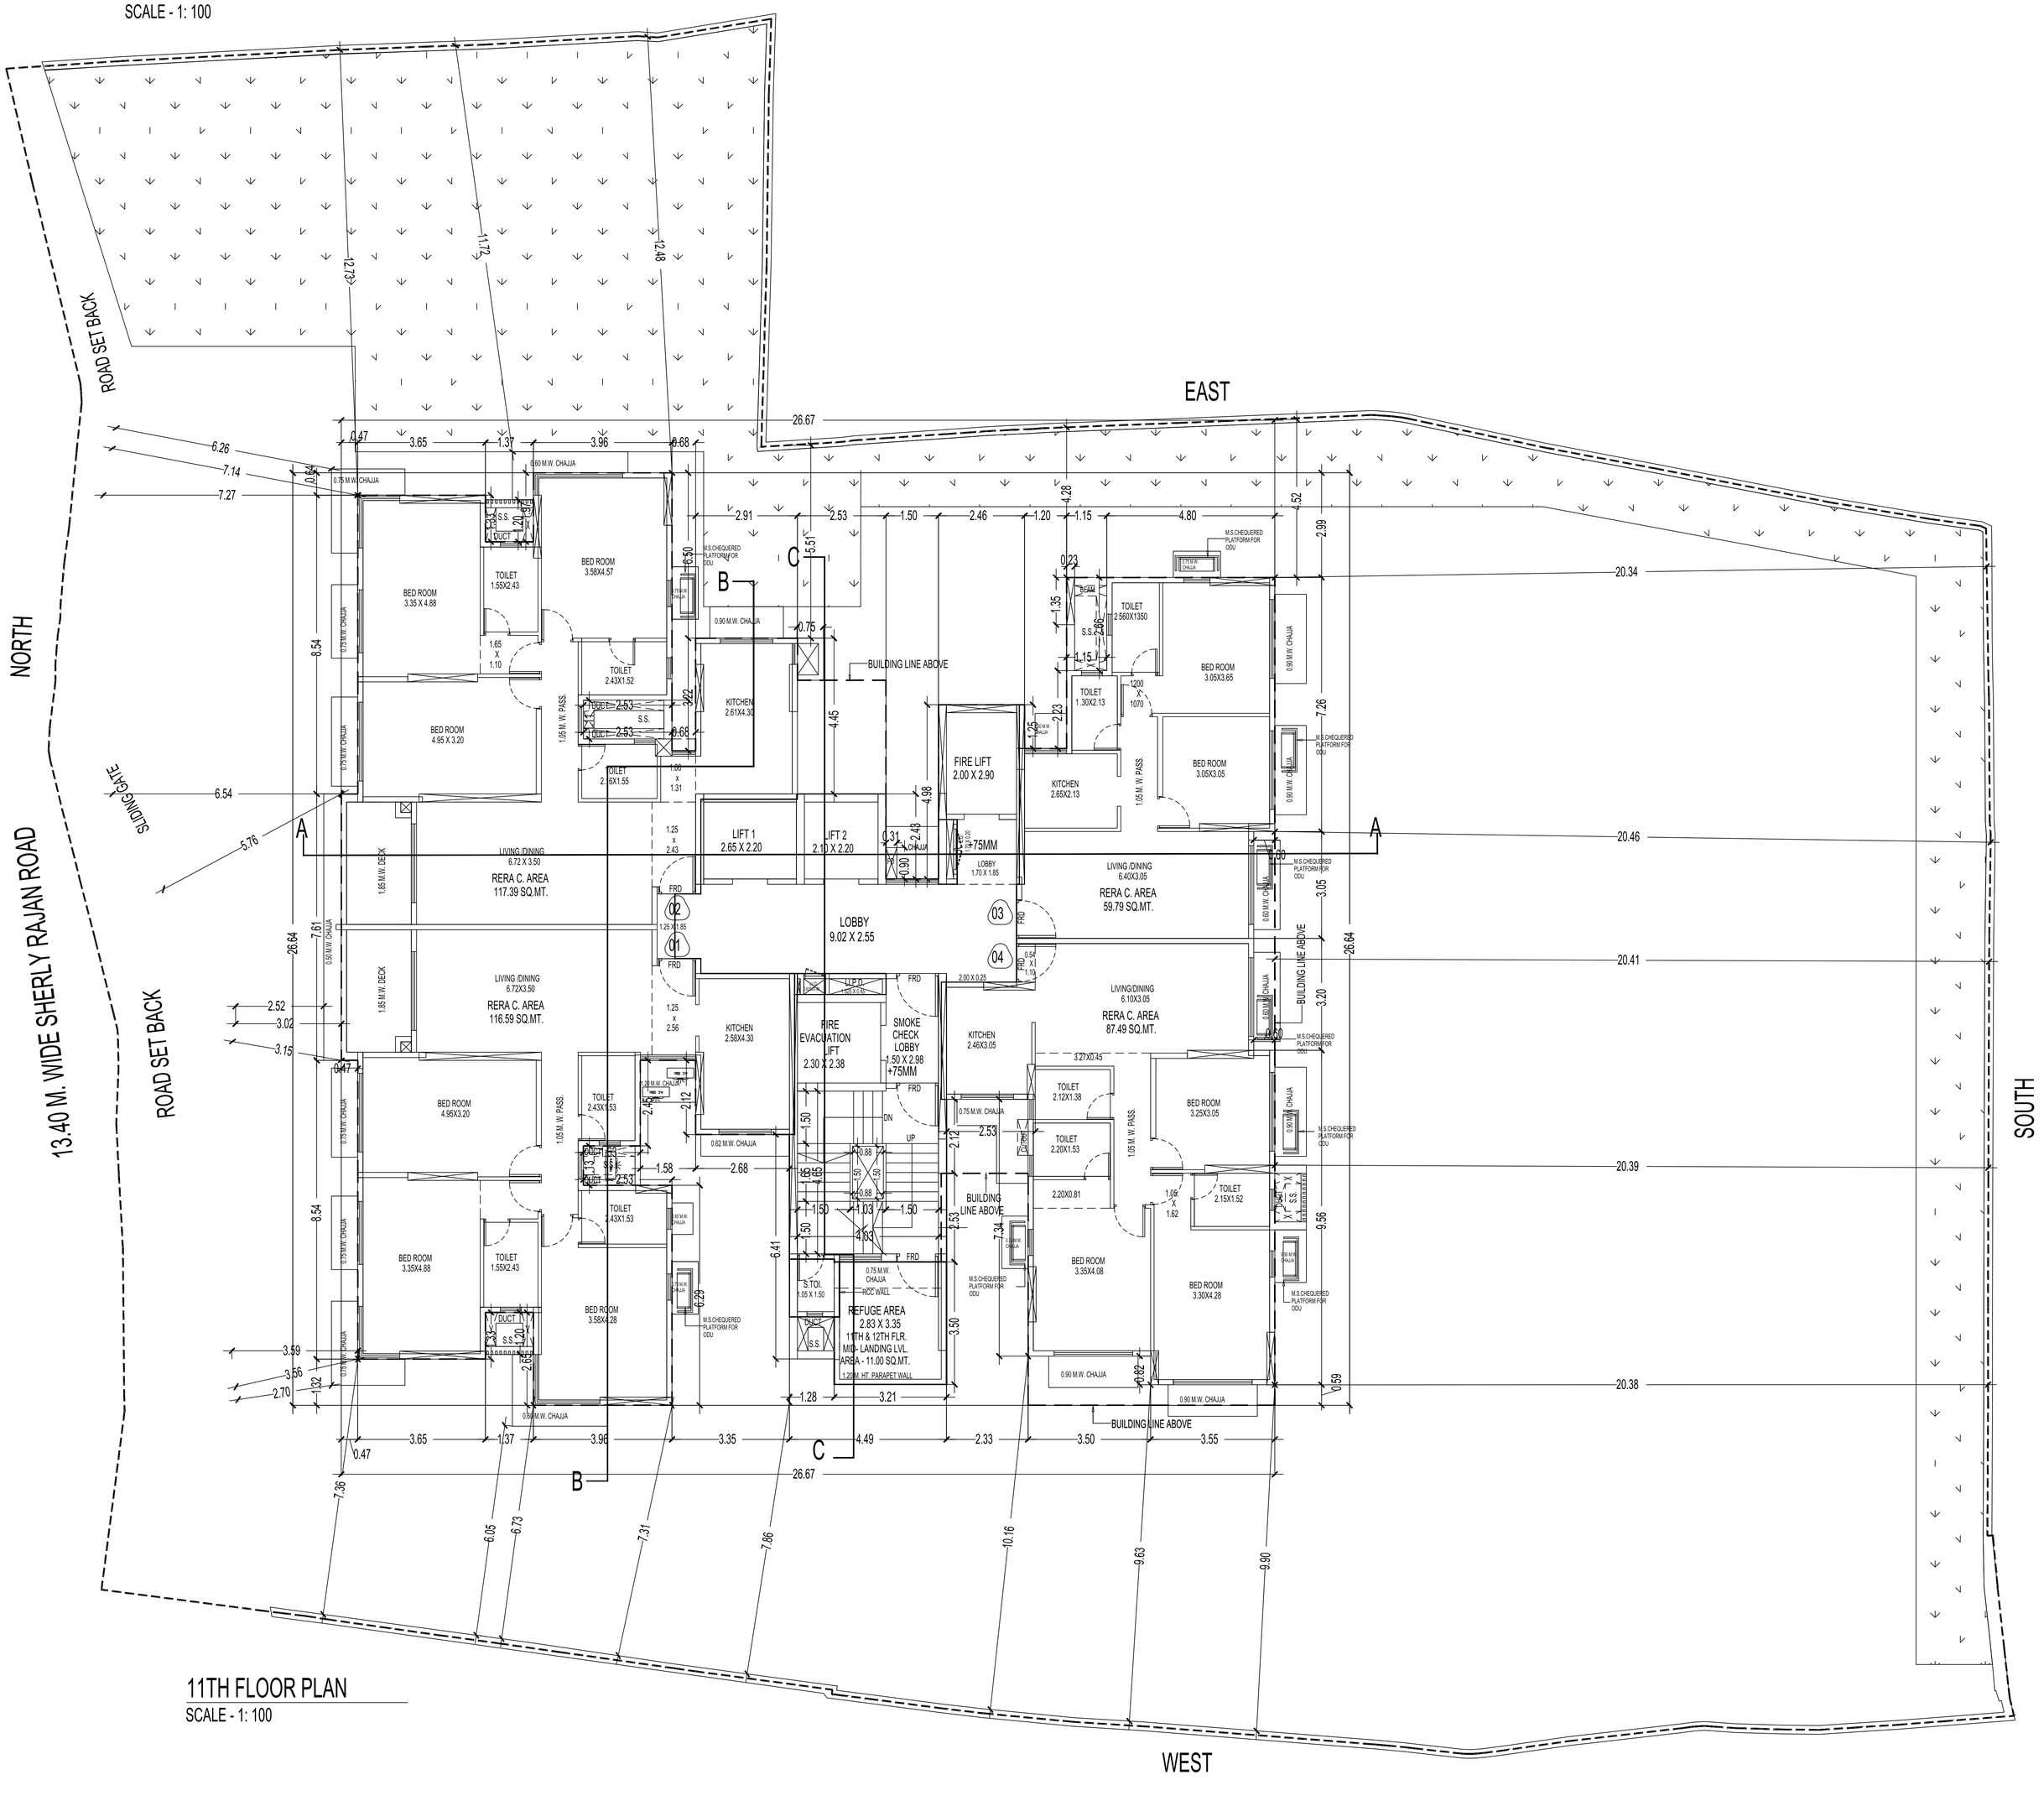


11TH FLOOR PLAN

SCALE - 1: 100

12TH TO 15TH FLOOR LINE AREA DIAGRAM

SCALE - 1: 100

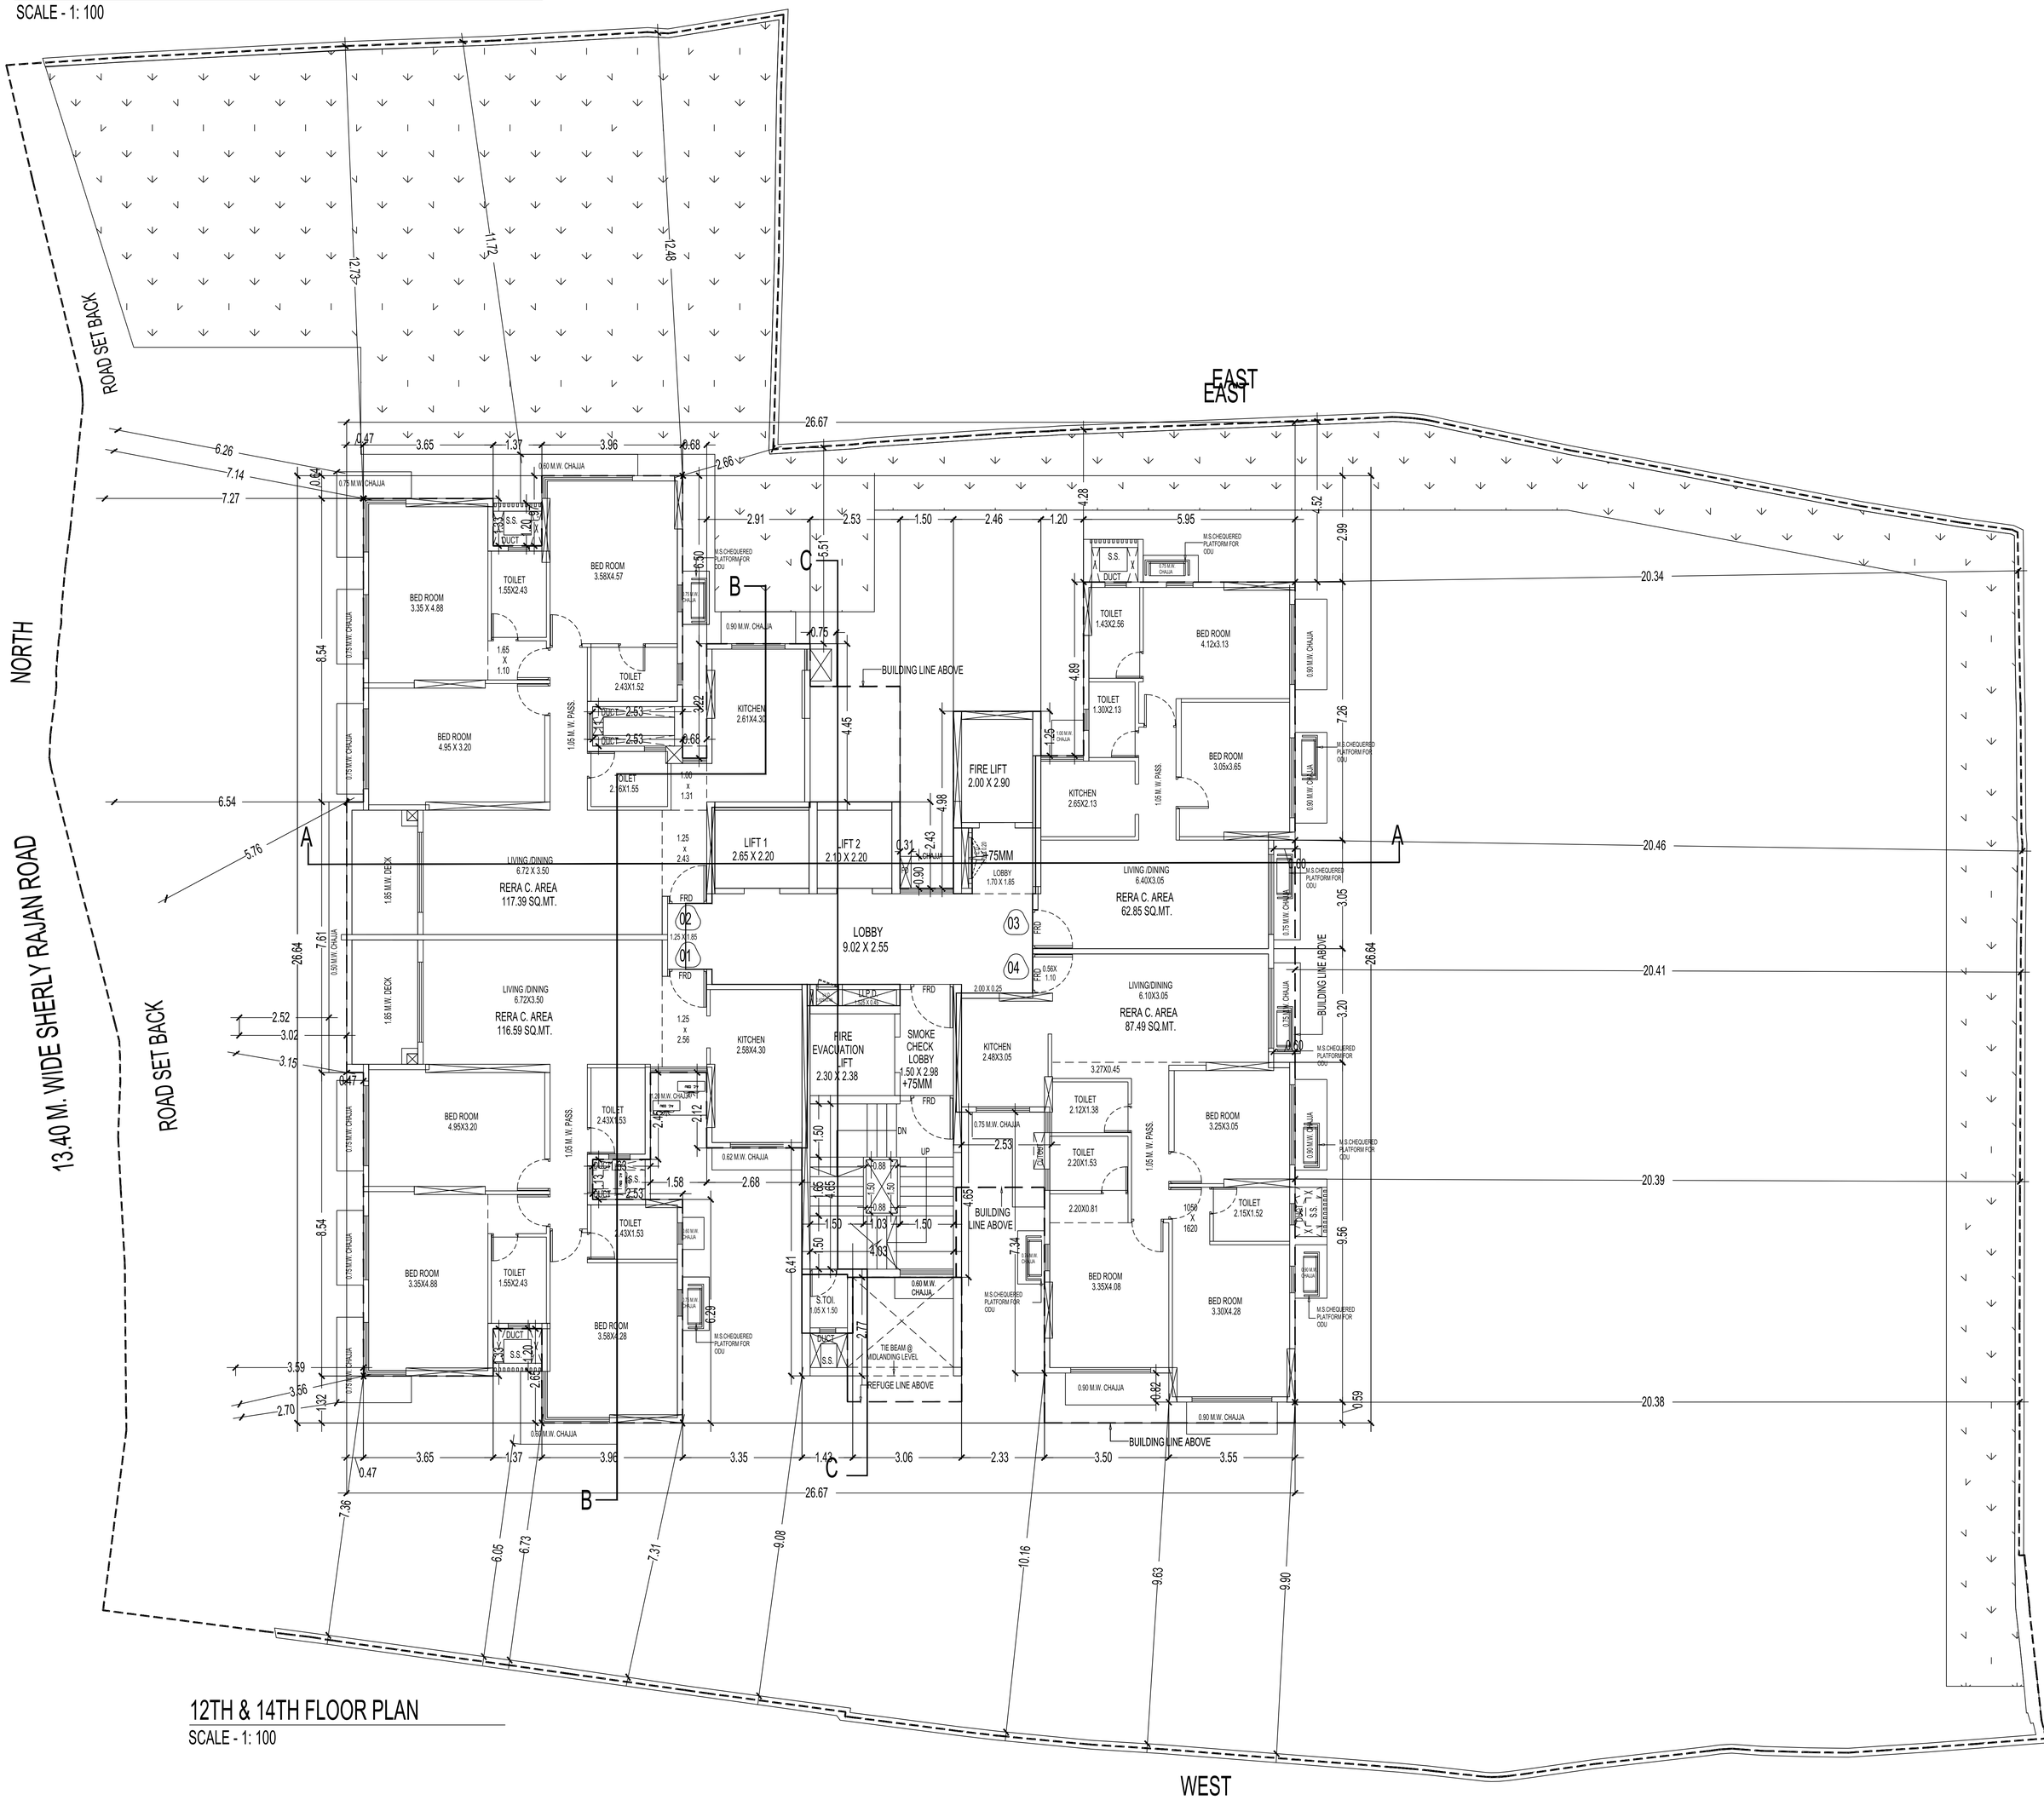

12TH & 14TH FLOOR PLAN

SCALE - 1: 100

NORTH

EAST

SOUTH

WEST

13.40 M. WIDE SHERLY RAJAN ROAD

ROAD SET BACK

ROAD SET BACK

BED ROOM 3.35 X 4.88

TOILET 1.55X2.43

BED ROOM 3.58X4.57

TOILET 2.43X1.52

BED ROOM 4.95 X 3.20

TOILET 2.16X1.55

KITCHEN 2.61X4.30

LIVING /DINING 6.72 X 3.50

RERA C. AREA 117.39 SQ.MT.

LIFT 1 2.65 X 2.20

LIFT 2 2.10 X 2.20

FIRE LIFT 2.00 X 2.90

LOBBY 9.02 X 2.55

LOBBY 1.70 X 1.85

+75MM

BUILDING LINE ABOVE

TOILET 1.43X2.56

BED ROOM 4.12x3.13

TOILET 1.30X2.13

KITCHEN 2.65X2.13

BED ROOM 3.05x3.65

LIVING /DINING 6.40X3.05

RERA C. AREA 62.85 SQ.MT.

LIVING /DINING 6.72X3.50

RERA C. AREA 116.59 SQ.MT.

BED ROOM 4.95X3.20

TOILET 2.43X1.53

KITCHEN 2.58X4.30

FIRE EVACUATION LIFT 2.30 X 2.38

SMOKE CHECK LOBBY 1.50 X 2.98 +75MM

KITCHEN 2.48X3.05

LIVING/DINING 6.10X3.05

RERA C. AREA 87.49 SQ.MT.

BED ROOM 3.35X4.88

TOILET 1.55X2.43

BED ROOM 3.58X4.28

REFUGE AREA 2.83 X 3.35 13TH & 14TH FLR. 15TH & 16TH FLR. MID- LANDING LVL. AREA - 11.00 SQ.MT. 1.20M. HT. PARAPET WALL

TOILET 2.12X1.38

TOILET 2.20X1.53

2.20X0.81

BED ROOM 3.25X3.05

TOILET 2.15X1.52

BED ROOM 3.35X4.08

BED ROOM 3.30X4.28

BUILDING LINE ABOVE

BUILDING LINE ABOVE

BUILDING LINE ABOVE

0.75 M.W. CHAJJA

0.60 M.W. CHAJJA

0.90 M.W. CHAJJA

1.85 M.W. DECK

1.05 M. W. PASS.

M.S.CHEQUERED PLATFORM FOR ODU

S.S. DUCT

FRD

RCC WALL

UP

DN

S.TOI. 1.05 X 1.50

26.67

20.46

20.41

20.39


20.38

13TH & 15TH FLOOR PLAN

SCALE - 1: 100

16TH FLOOR LINE AREA DIAGRAM

SCALE - 1: 100

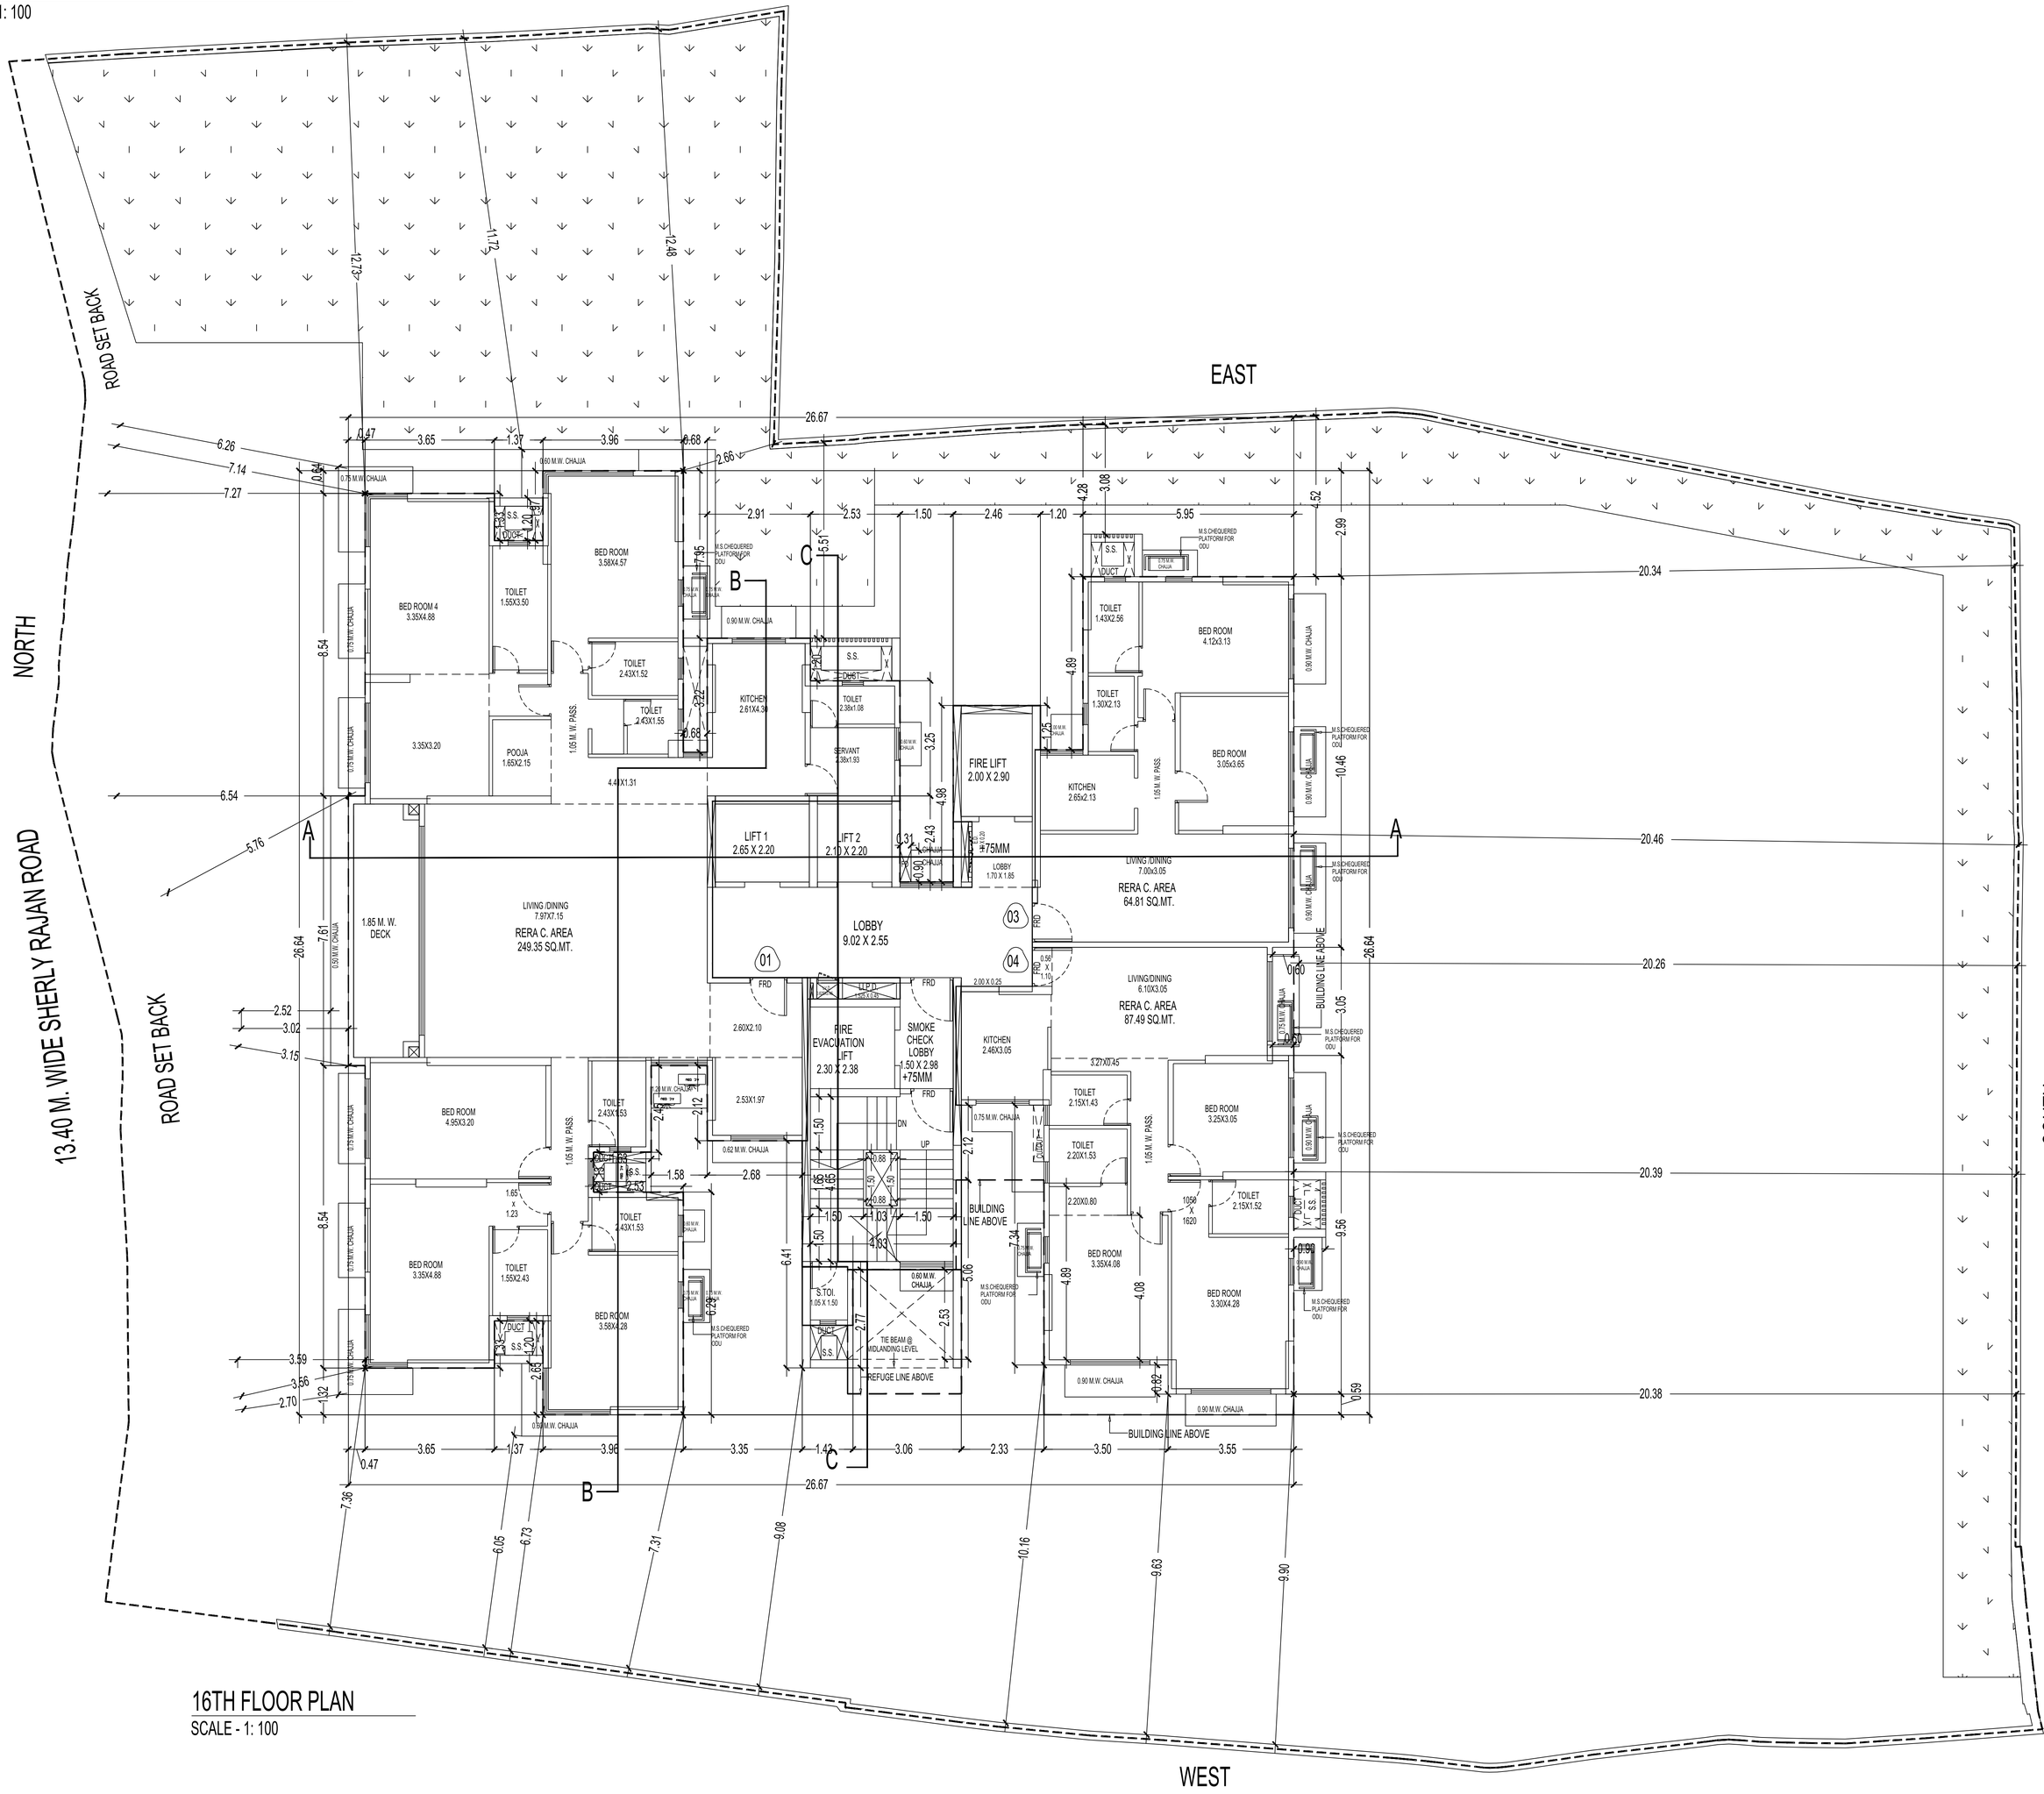

16TH FLOOR PLAN

SCALE - 1: 100

NORTH

EAST

SOUTH

WEST

13.40 M. WIDE SHERLY RAJAN ROAD

ROAD SET BACK

ROAD SET BACK

Door??

BED ROOM 4
3.35X4.88

TOILET
1.55X3.50

BED ROOM
3.58X4.57

TOILET
2.43X1.52

TOILET
1.43
X1.55

POOJA
1.65X2.15

3.35X3.20

KITCHEN
2.61X4.36

TOILET
2.38x1.08

SERVANT
2.38x1.93

LIFT 1
2.65 X 2.20

LIFT 2
2.10 X 2.20

FIRE LIFT
2.00 X 2.90

LOBBY
1.70 X 1.85

LOBBY
9.02 X 2.55

LIVING /DINING
7.97X7.15

RERA C. AREA
249.35 SQ.MT.

1.85 M. W.
DECK

LIVING /DINING
7.00X3.05

RERA C. AREA
64.81 SQ.MT.

KITCHEN
2.65X2.13

TOILET
1.43X2.96

BED ROOM
4.12x3.13

TOILET
1.30X2.13

BED ROOM
3.05x3.65

FIRE
EVACUATION
LIFT
2.30 X 2.38

SMOKE
CHECK
LOBBY
1.50 X 2.98
+75MM

KITCHEN
2.46X3.05

LIVING/DINING
6.69X3.05

RERA C. AREA
100.99 SQ.MT.

BED ROOM
4.95X3.20

TOILET
2.43X1.53

TOILET
2.43X1.53

BED ROOM
3.35X4.88

TOILET
1.55X2.43

BED ROOM
3.58X4.28

REFUGE AREA
2.83 X 3.35
17TH & 18TH FLR.
MID- LANDING LVL.
AREA - 11.00 SQ.MT.
1.20 M. HT. PARAPET WALL

DECK
2.33 X 1.97

TOILET
2145X1425

TOILET
2.20X1.53

2.20X0.80

TOILET
2.15X1.52

BED ROOM
3.25X3.05

BED ROOM
3.35X5.49

BED ROOM
3.30X4.87

17TH FLOOR PLAN

SCALE - 1: 100

17TH & 18TH FLOOR LINE AREA DIAGRAM

SCALE - 1: 100

NORTH

SOUTH

EAST

WEST

13.40 M. WIDE SHERLY RAJAN ROAD

ROAD SET BACK

ROAD SET BACK

MULTI PURPOSE ROOM (with alcove). 3.35 X 5.04 TO BE HANDED OVER TO BMC
RERA C. AREA 38.10 SQ.MT.

MULTI PURPOSE ROOM (with alcove). 5.42 X 3.33 TO BE HANDED OVER TO BMC
RERA C. AREA 38.22 SQ.MT.

MULTI PURPOSE ROOM (with alcove). 5.42 X 3.11 TO BE HANDED OVER TO BMC
RERA C. AREA 39.42 SQ.MT.

MULTI PURPOSE ROOM (with alcove). 3.05 X 5.16 TO BE HANDED OVER TO BMC
RERA C. AREA 38.37 SQ.MT.

LIVING /DINING 2.53 X 4.30
RERA C. AREA 73.97 SQ.MT. SALE

MULTI PURPOSE ROOM (with alcove). 4.12 X 4.54 TO BE HANDED OVER TO BMC
RERA C. AREA 38.69 SQ.MT.

MULTI PURPOSE ROOM (with alcove). 5.25 X 2.90 TO BE HANDED OVER TO BMC
RERA C. AREA 38.87 SQ.MT.

MULTI PURPOSE ROOM (with alcove). 4.65 X 3.04 TO BE HANDED OVER TO BMC
RERA C. AREA 38.05 SQ.MT.

MULTI PURPOSE ROOM (with alcove). 4.43 X 4.86 TO BE HANDED OVER TO BMC
RERA C. AREA 41.71 SQ.MT.

1.20 M. W. PASSAGE

1.20 M. W. PASS.

1.05 M. W. PASS.

LOBBY 9.02 X 2.55

LIFT 1 2.65 X 2.20

LIFT 2 2.10 X 2.20

FIRE LIFT 2.00 X 2.90

FIRE EVACUATION LIFT 2.30 X 2.38

SMOKE CHECK LOBBY 1.50 X 2.98 +75MM

+75MM

LOBBY 1.70 X 1.85

ROOF ABOVE REFUGE AREA TIE BEAM @ MIDLANDING LEVEL

Door?

TOILET 1.45 X 1.10

TOILET 1.10 X 1.95

TOILET 2.38x1.08

TOILET 1.43X2.56

TOILET 1.70 X 1.15

TOILET 1.60 X 1.10

TOILET 1.55X2.43

TOILET 4.43X1.53

TOILET 2.15 X 1.52

BED ROOM 3.35X4.88

KITCHEN 3.58X4.28

BEDROOM 3.25 X 4.25

DECK 2.33 X 1.97

STORE 1.38x1.93

S.TOT 1.05 X 1.50

ALCOVE

DUCT

S.S.

M.S.CHEQUERED PLATFORM FOR ODU

0.90 M.W. CHAJJA

0.75 M.W. CHAJJA

0.60 M.W. CHAJJA

0.63 M.W. CHAJJA

FRD

DN

UP

18TH FLOOR PLAN

SCALE - 1: 100