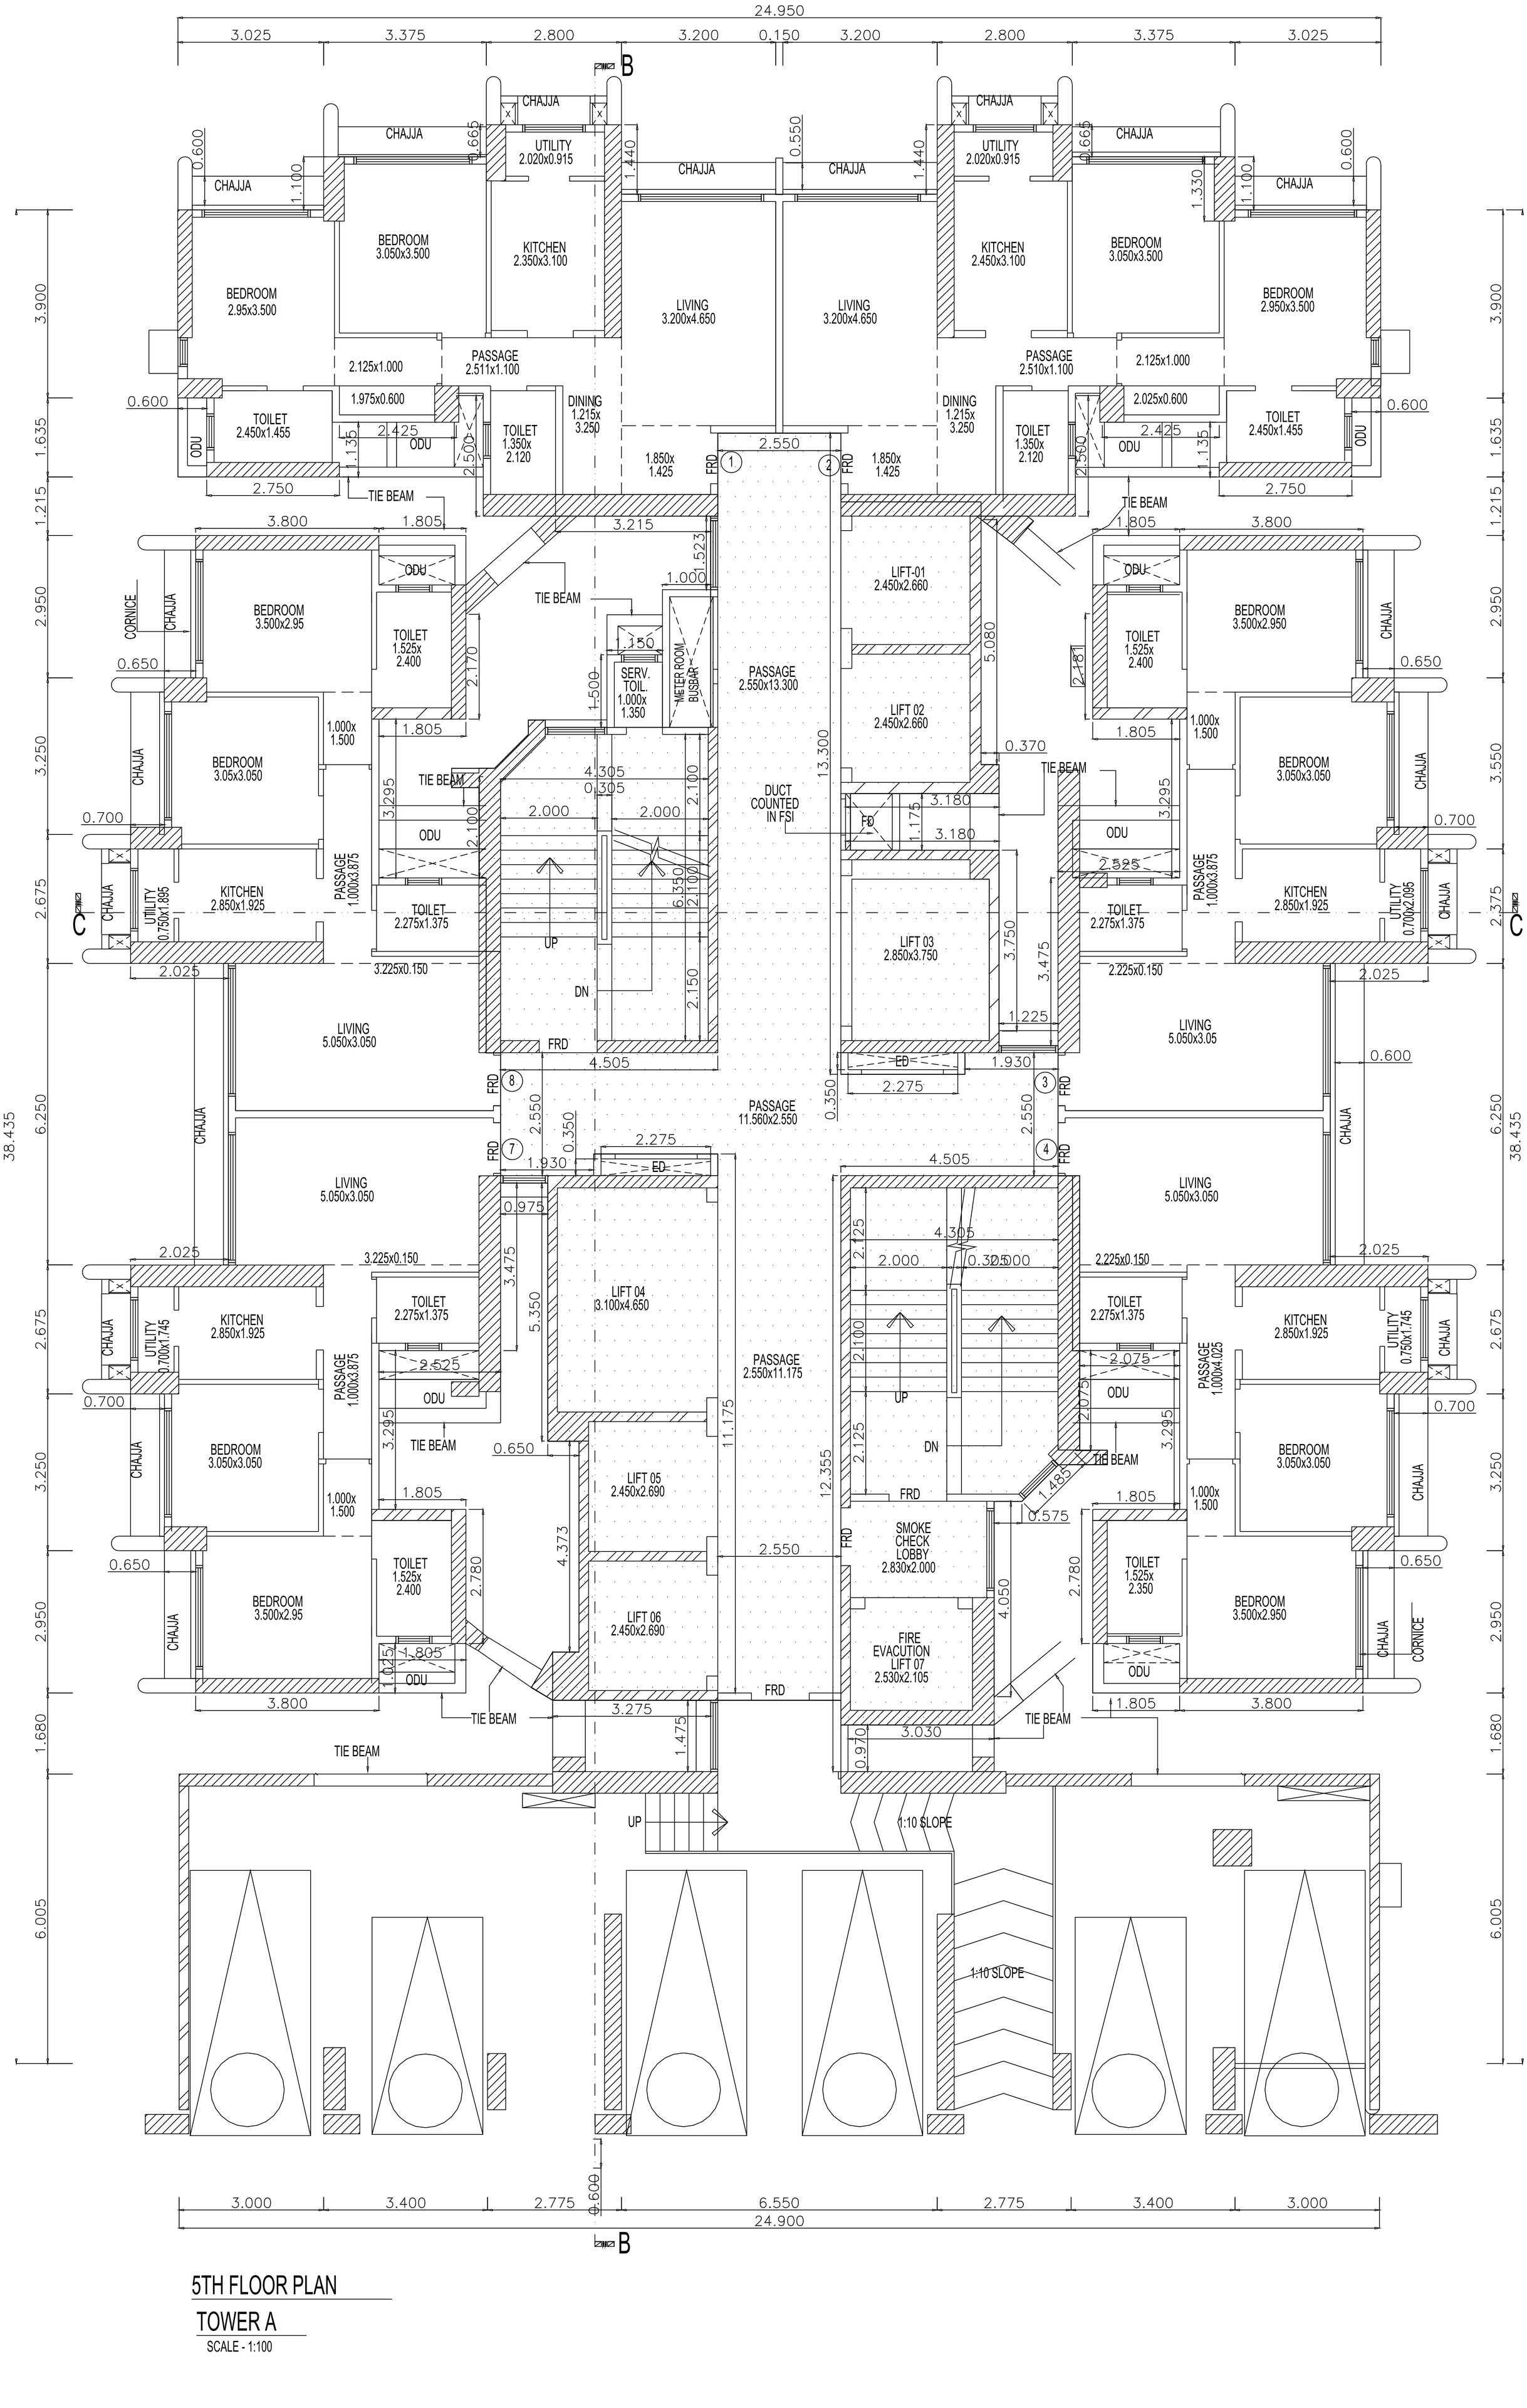


5TH FLOOR PLAN

TOWER A

SCALE - 1:100


REFUGE AREA
FOR 7TH FLOOR
REQUIRED REFUGE AREA = 151.422
PERMISSIBLE REFUGE AREA = 160.886
PROPOSED REFUGE AREA = 153.559

PARAPET WALL 1.20M


7TH FLOOR PLAN (ECO DECK LVL)

TOWER A

SCALE - 1:100

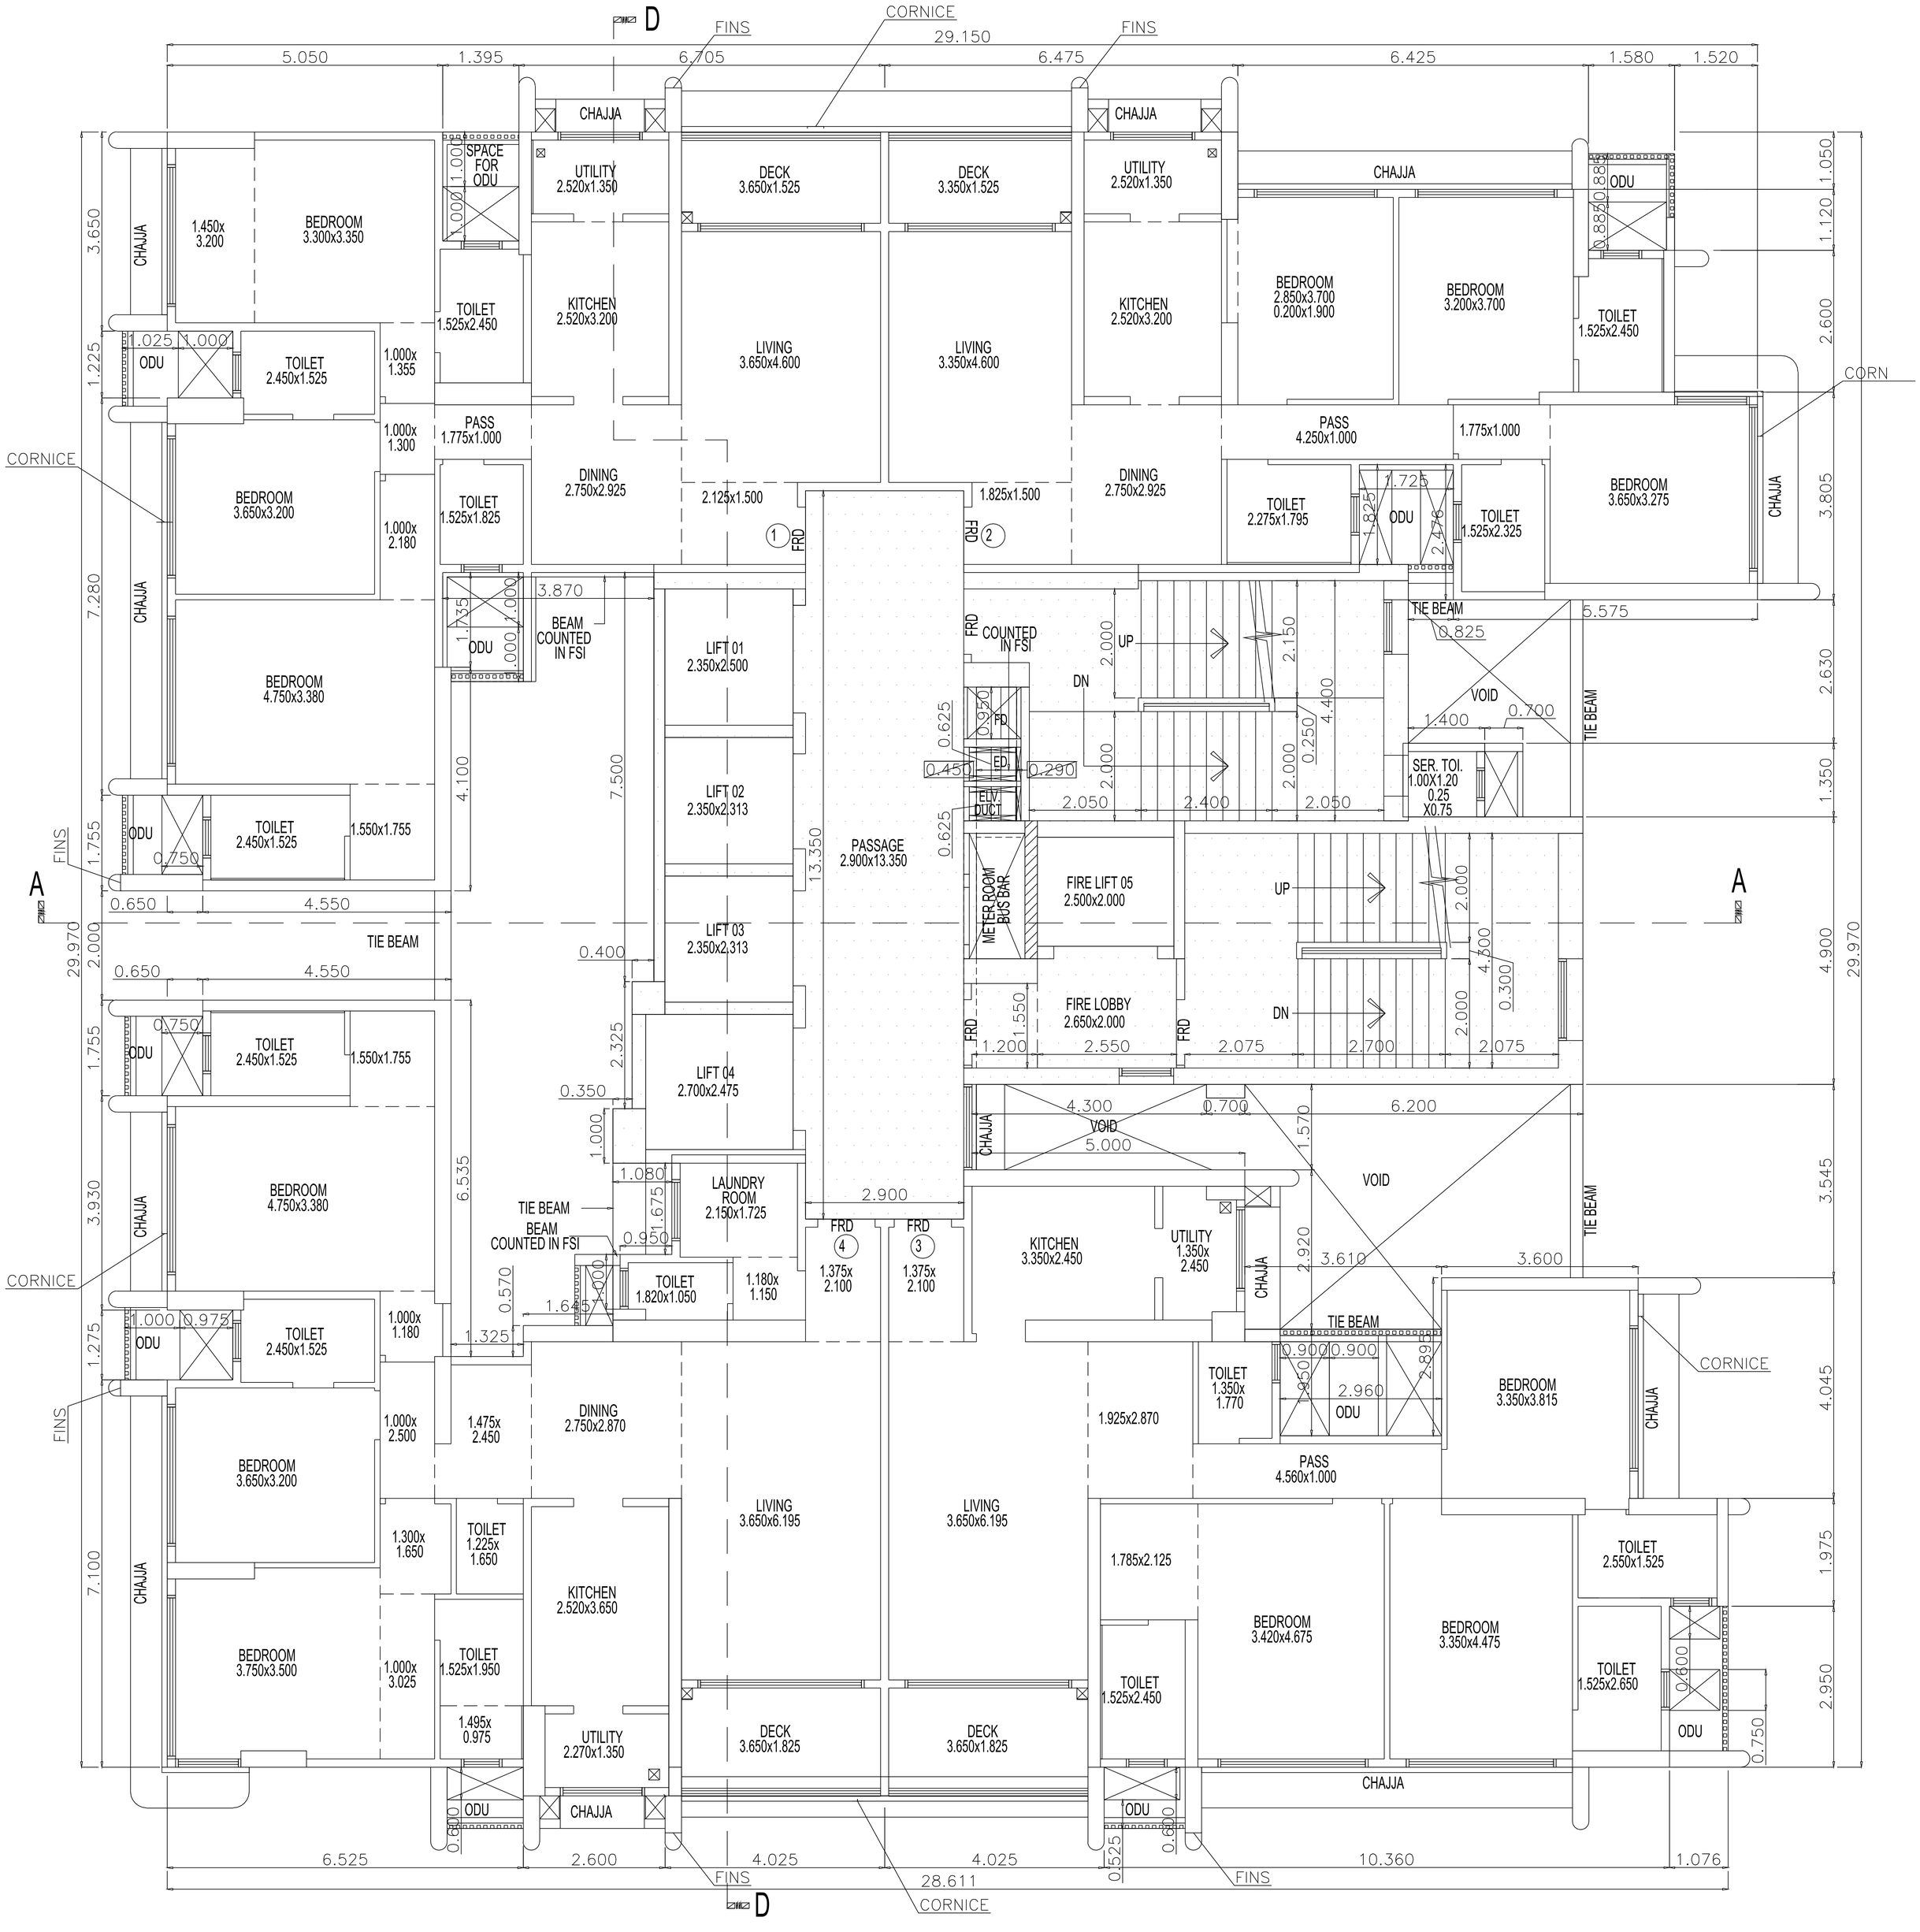


TYPICAL 8TH TO 11TH FLOOR PLAN
(TOWER B)
SCALE - 1:100

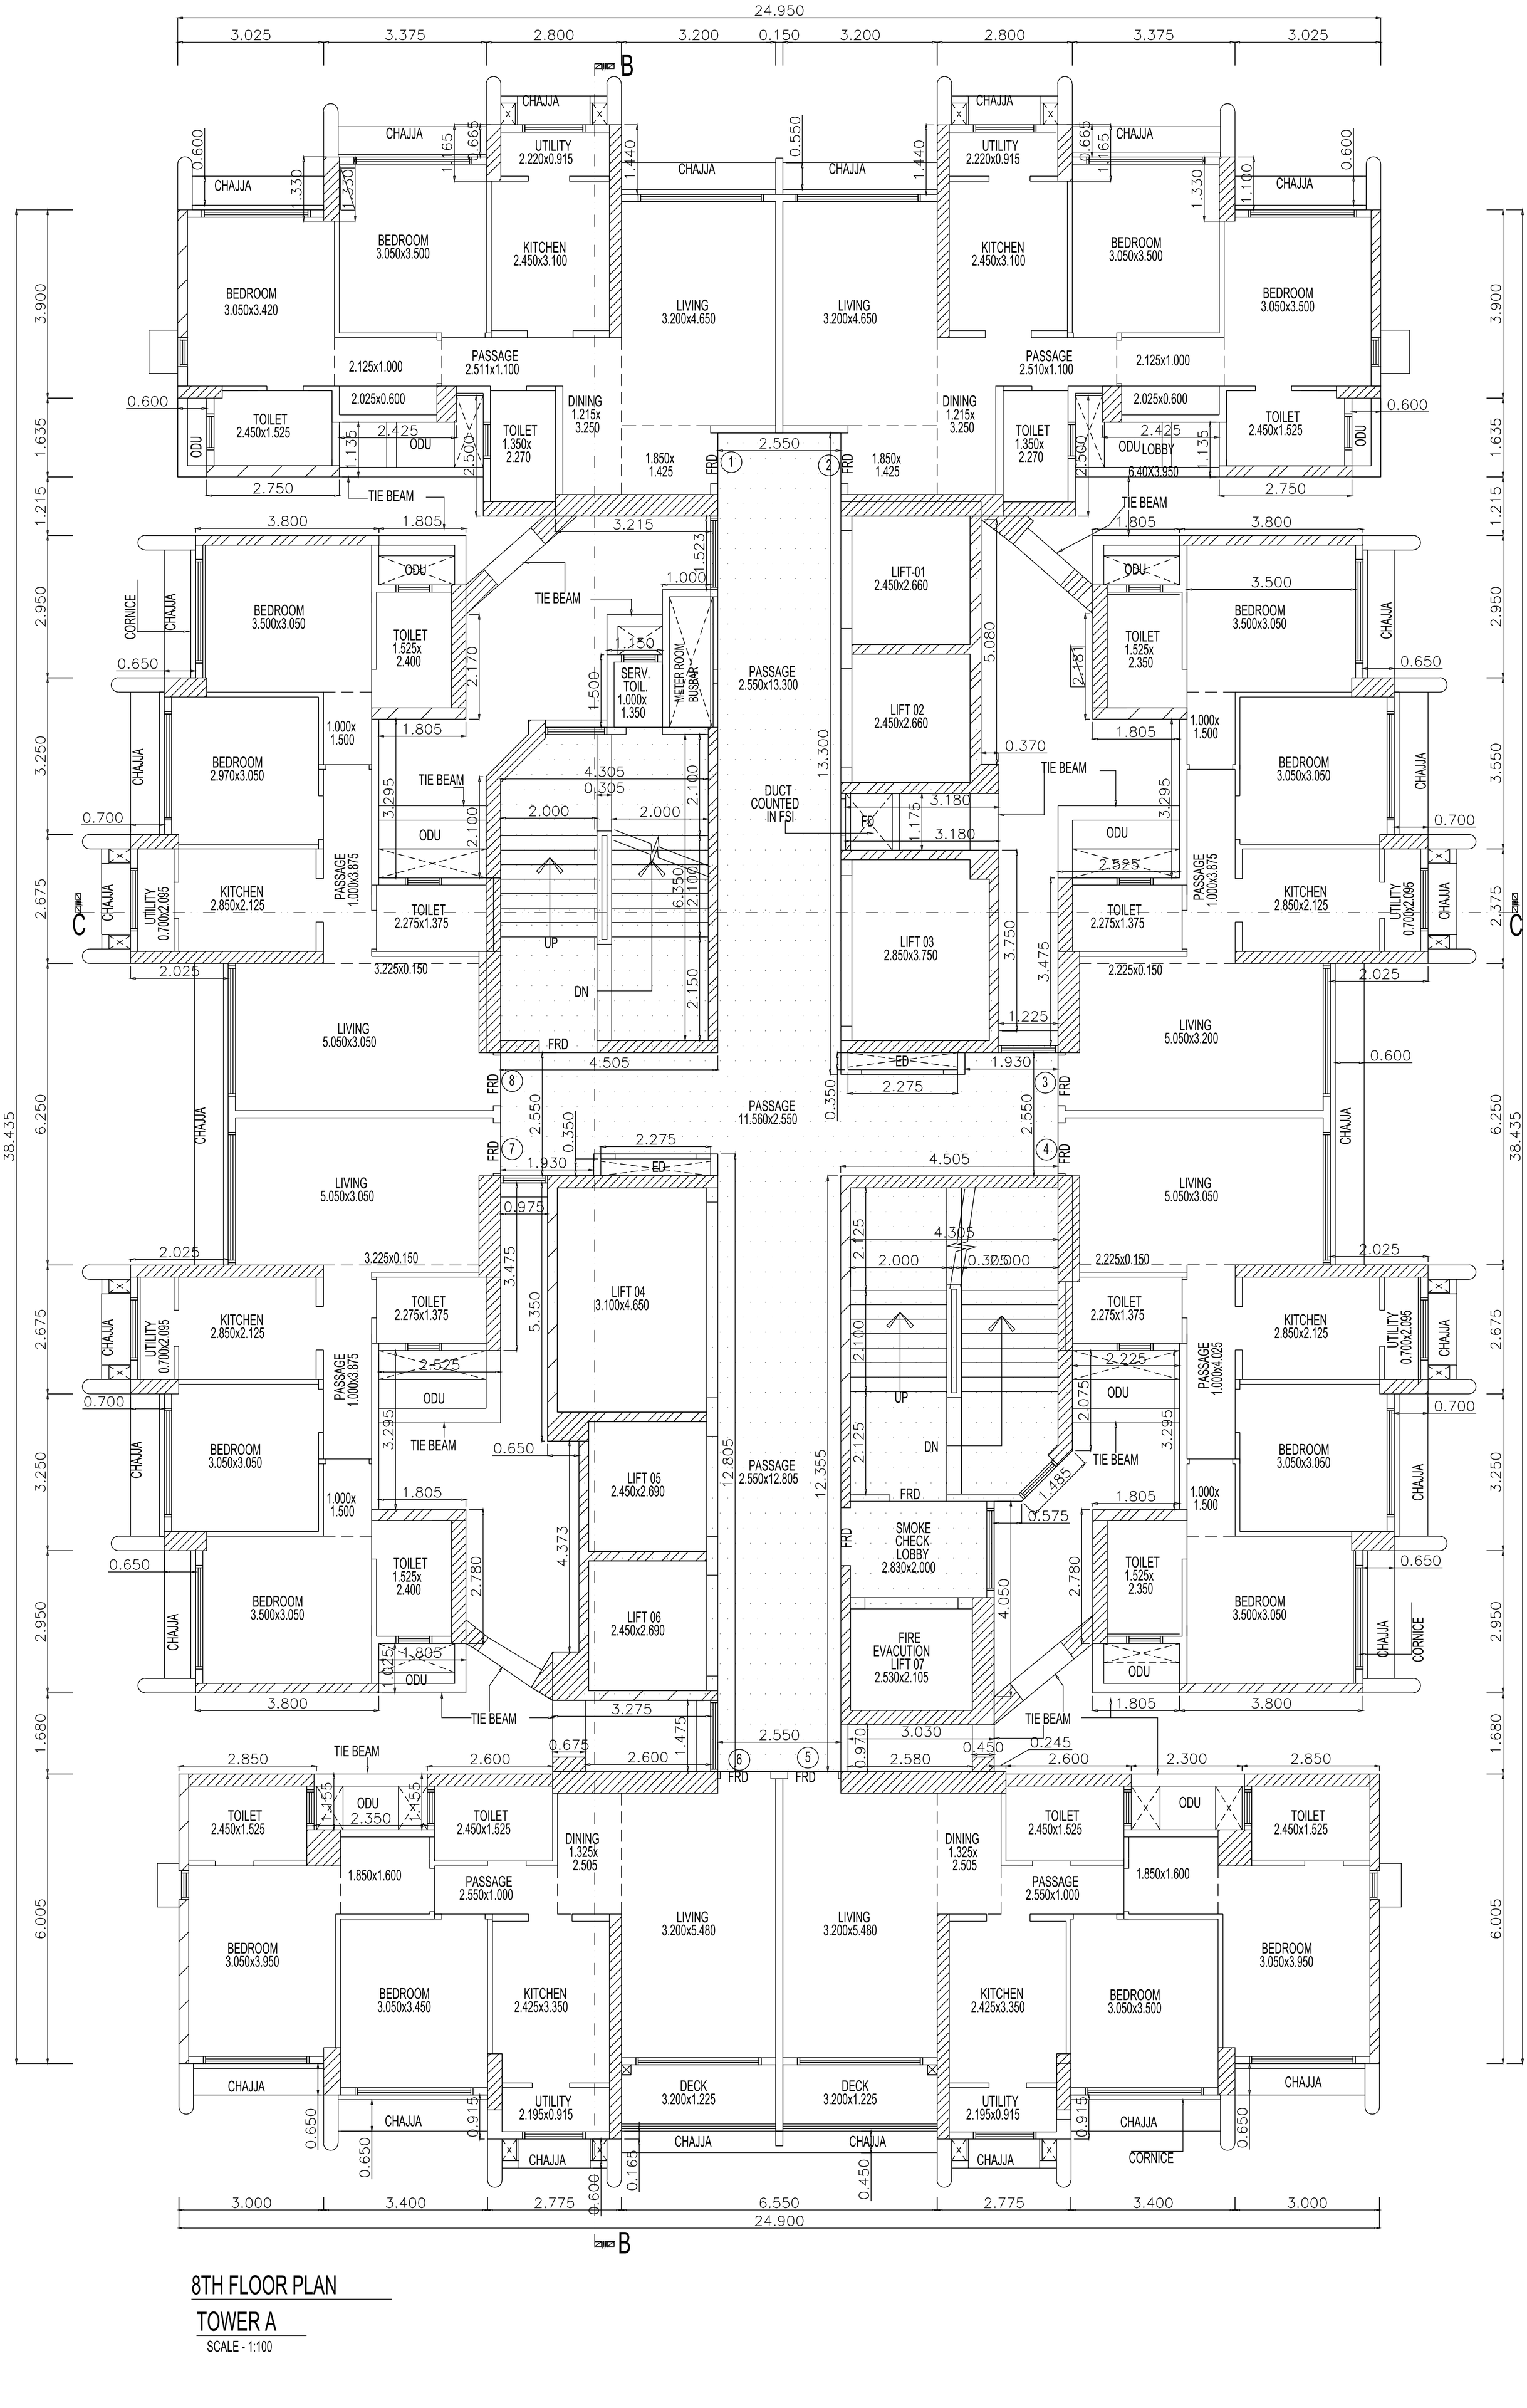

8TH FLOOR PLAN

TOWER A


SCALE - 1:100

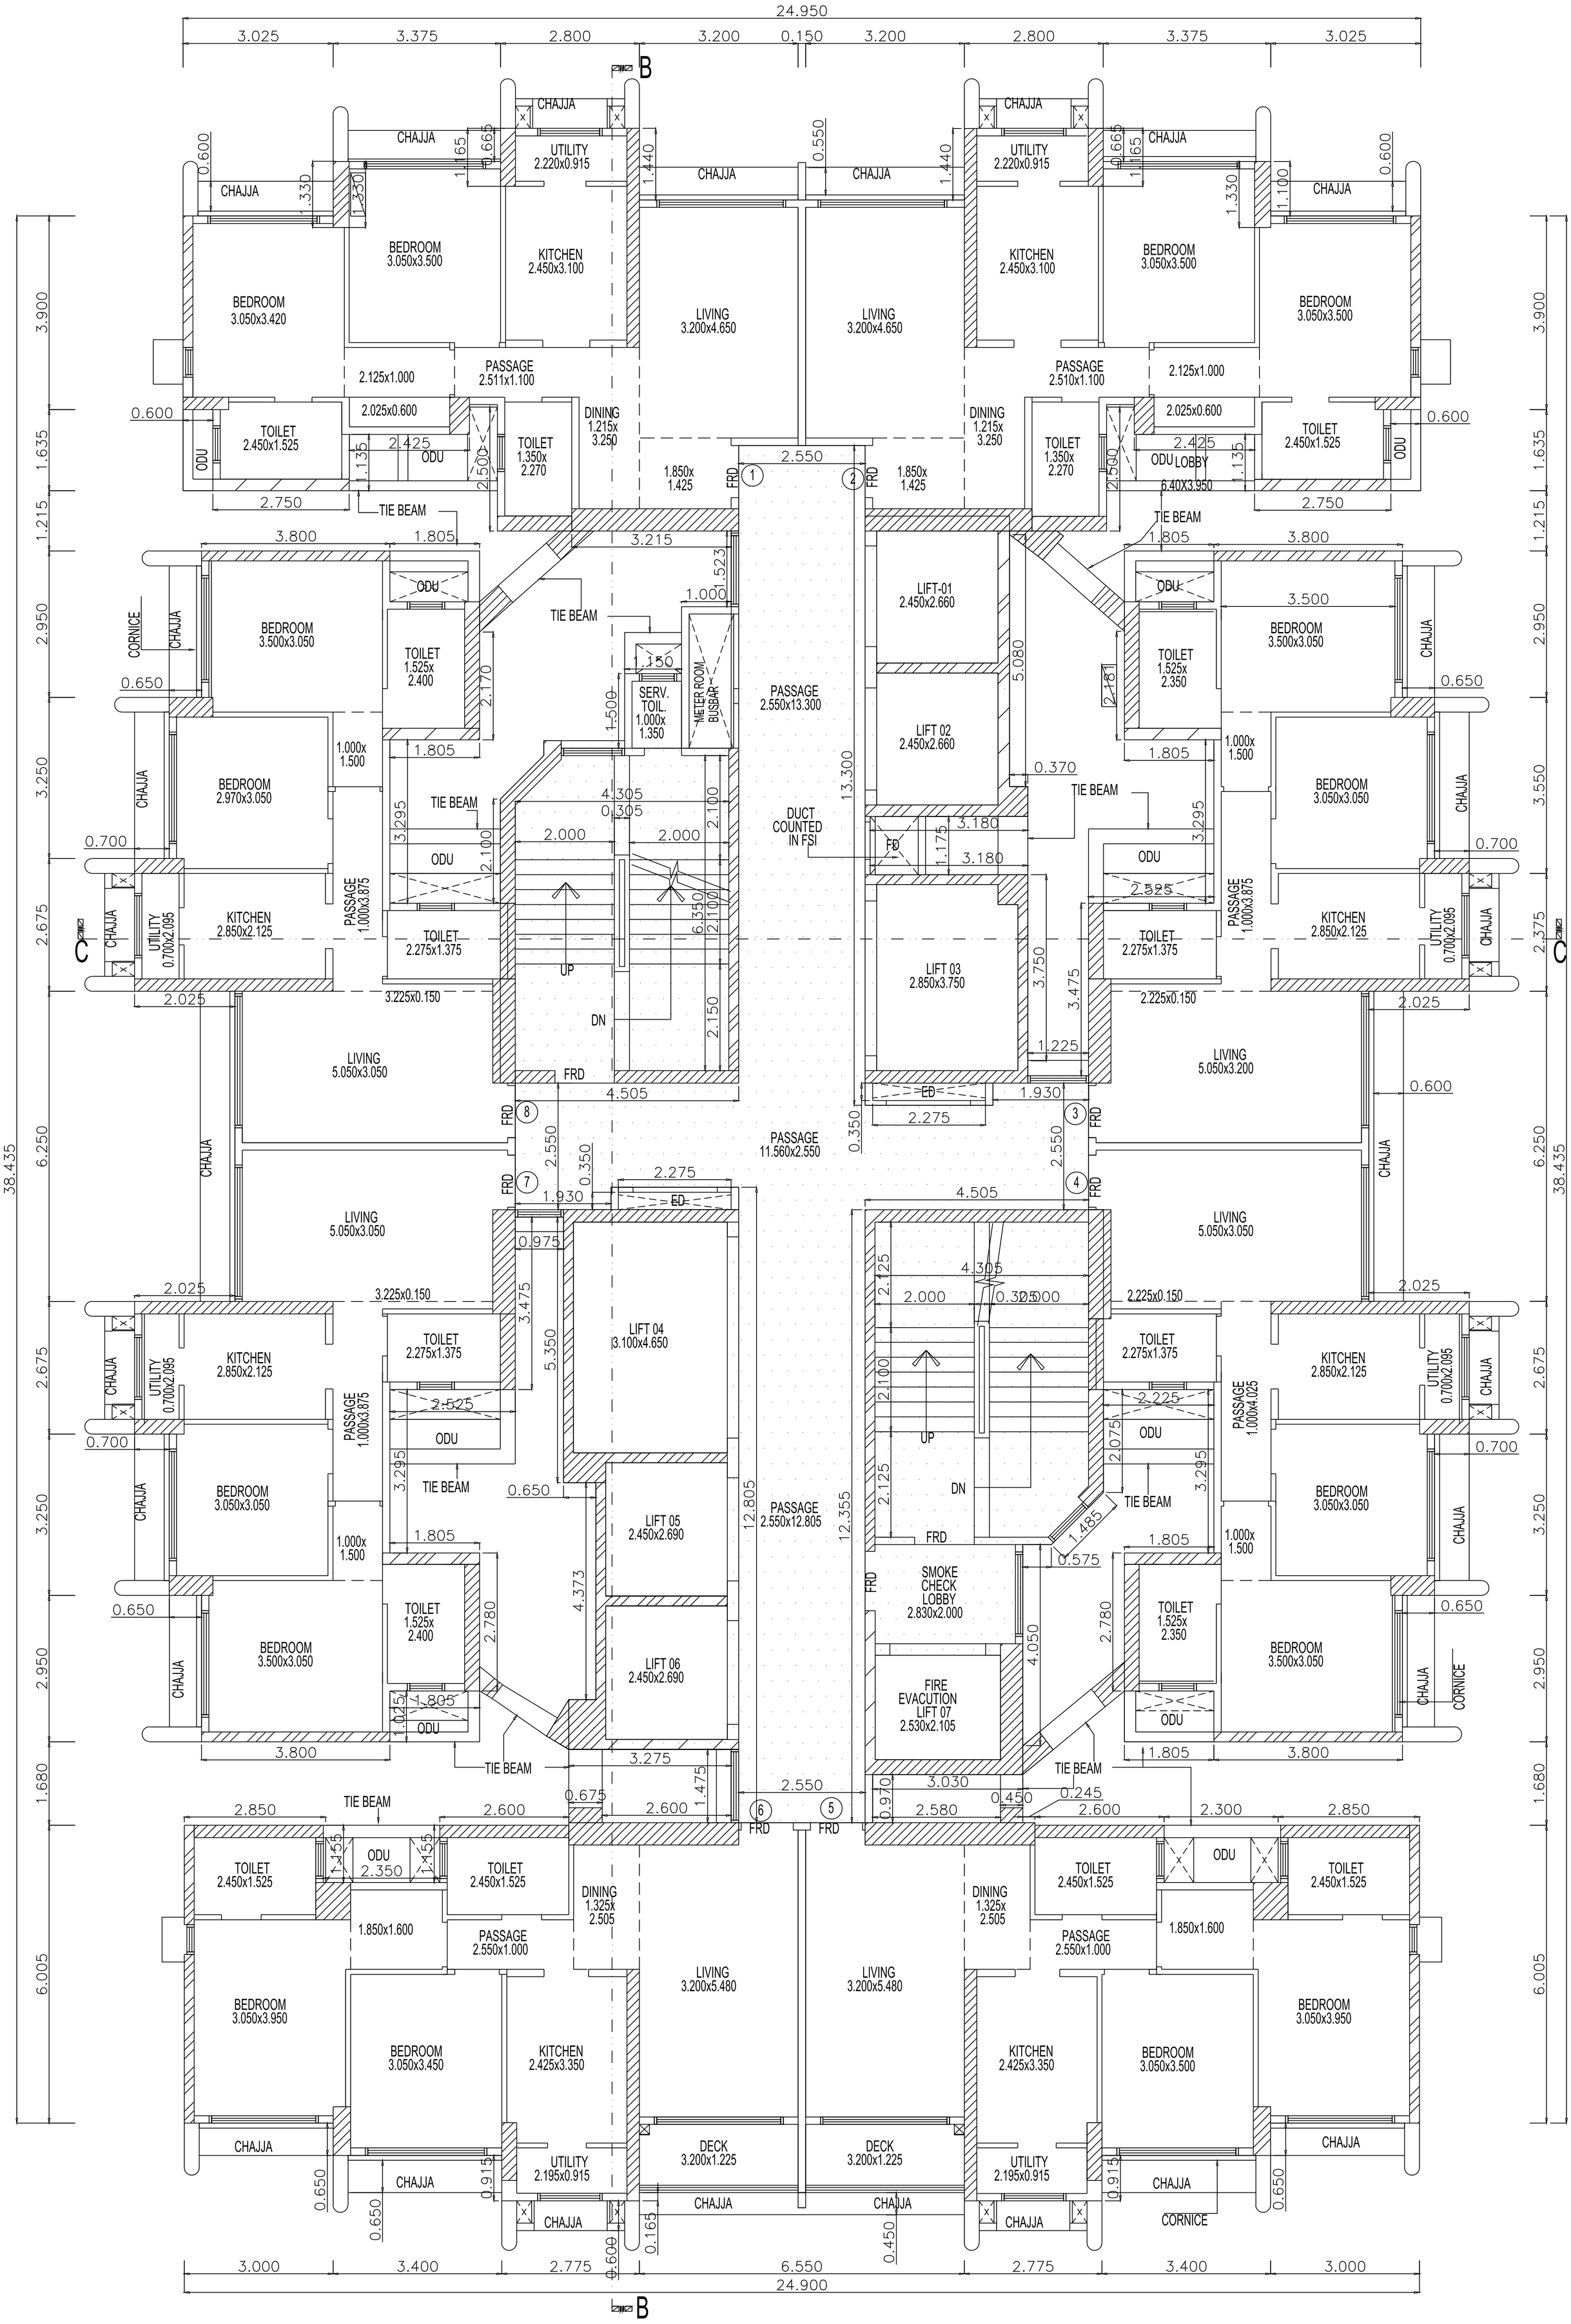

9TH FLOOR PLAN

TOWER A


SCALE - 1:100

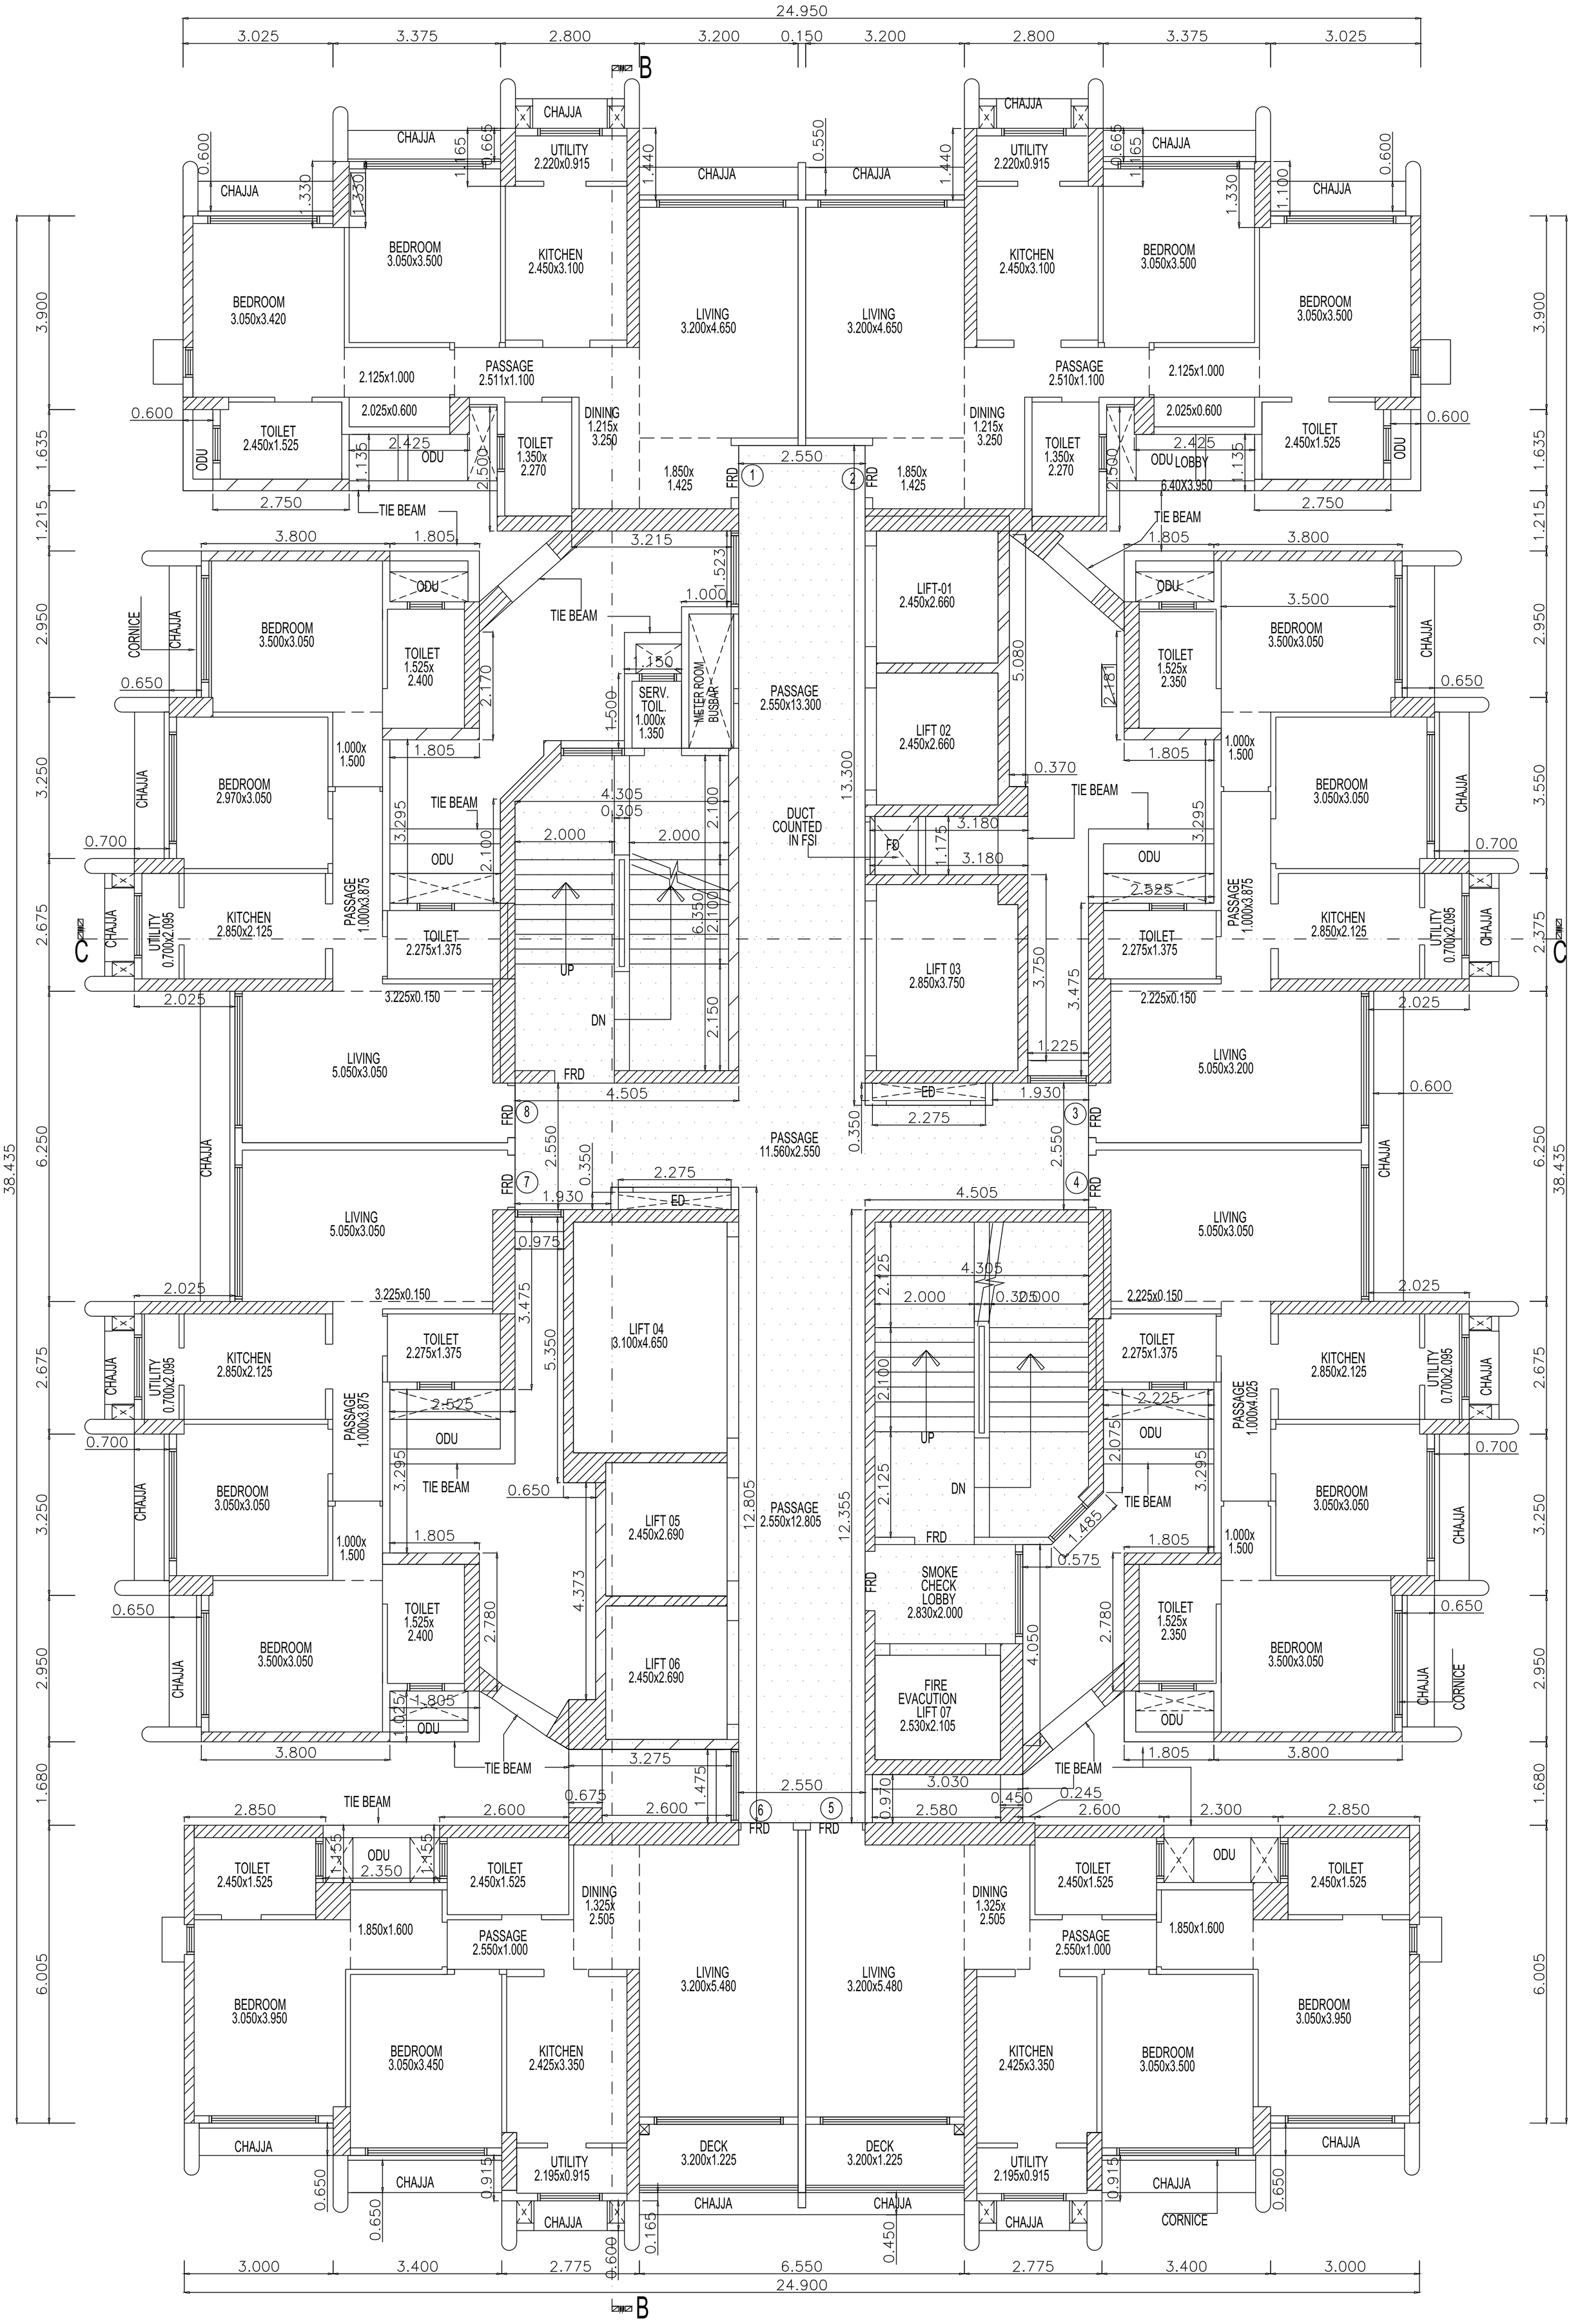


10TH FLOOR PLAN

TOWER A

SCALE - 1:100

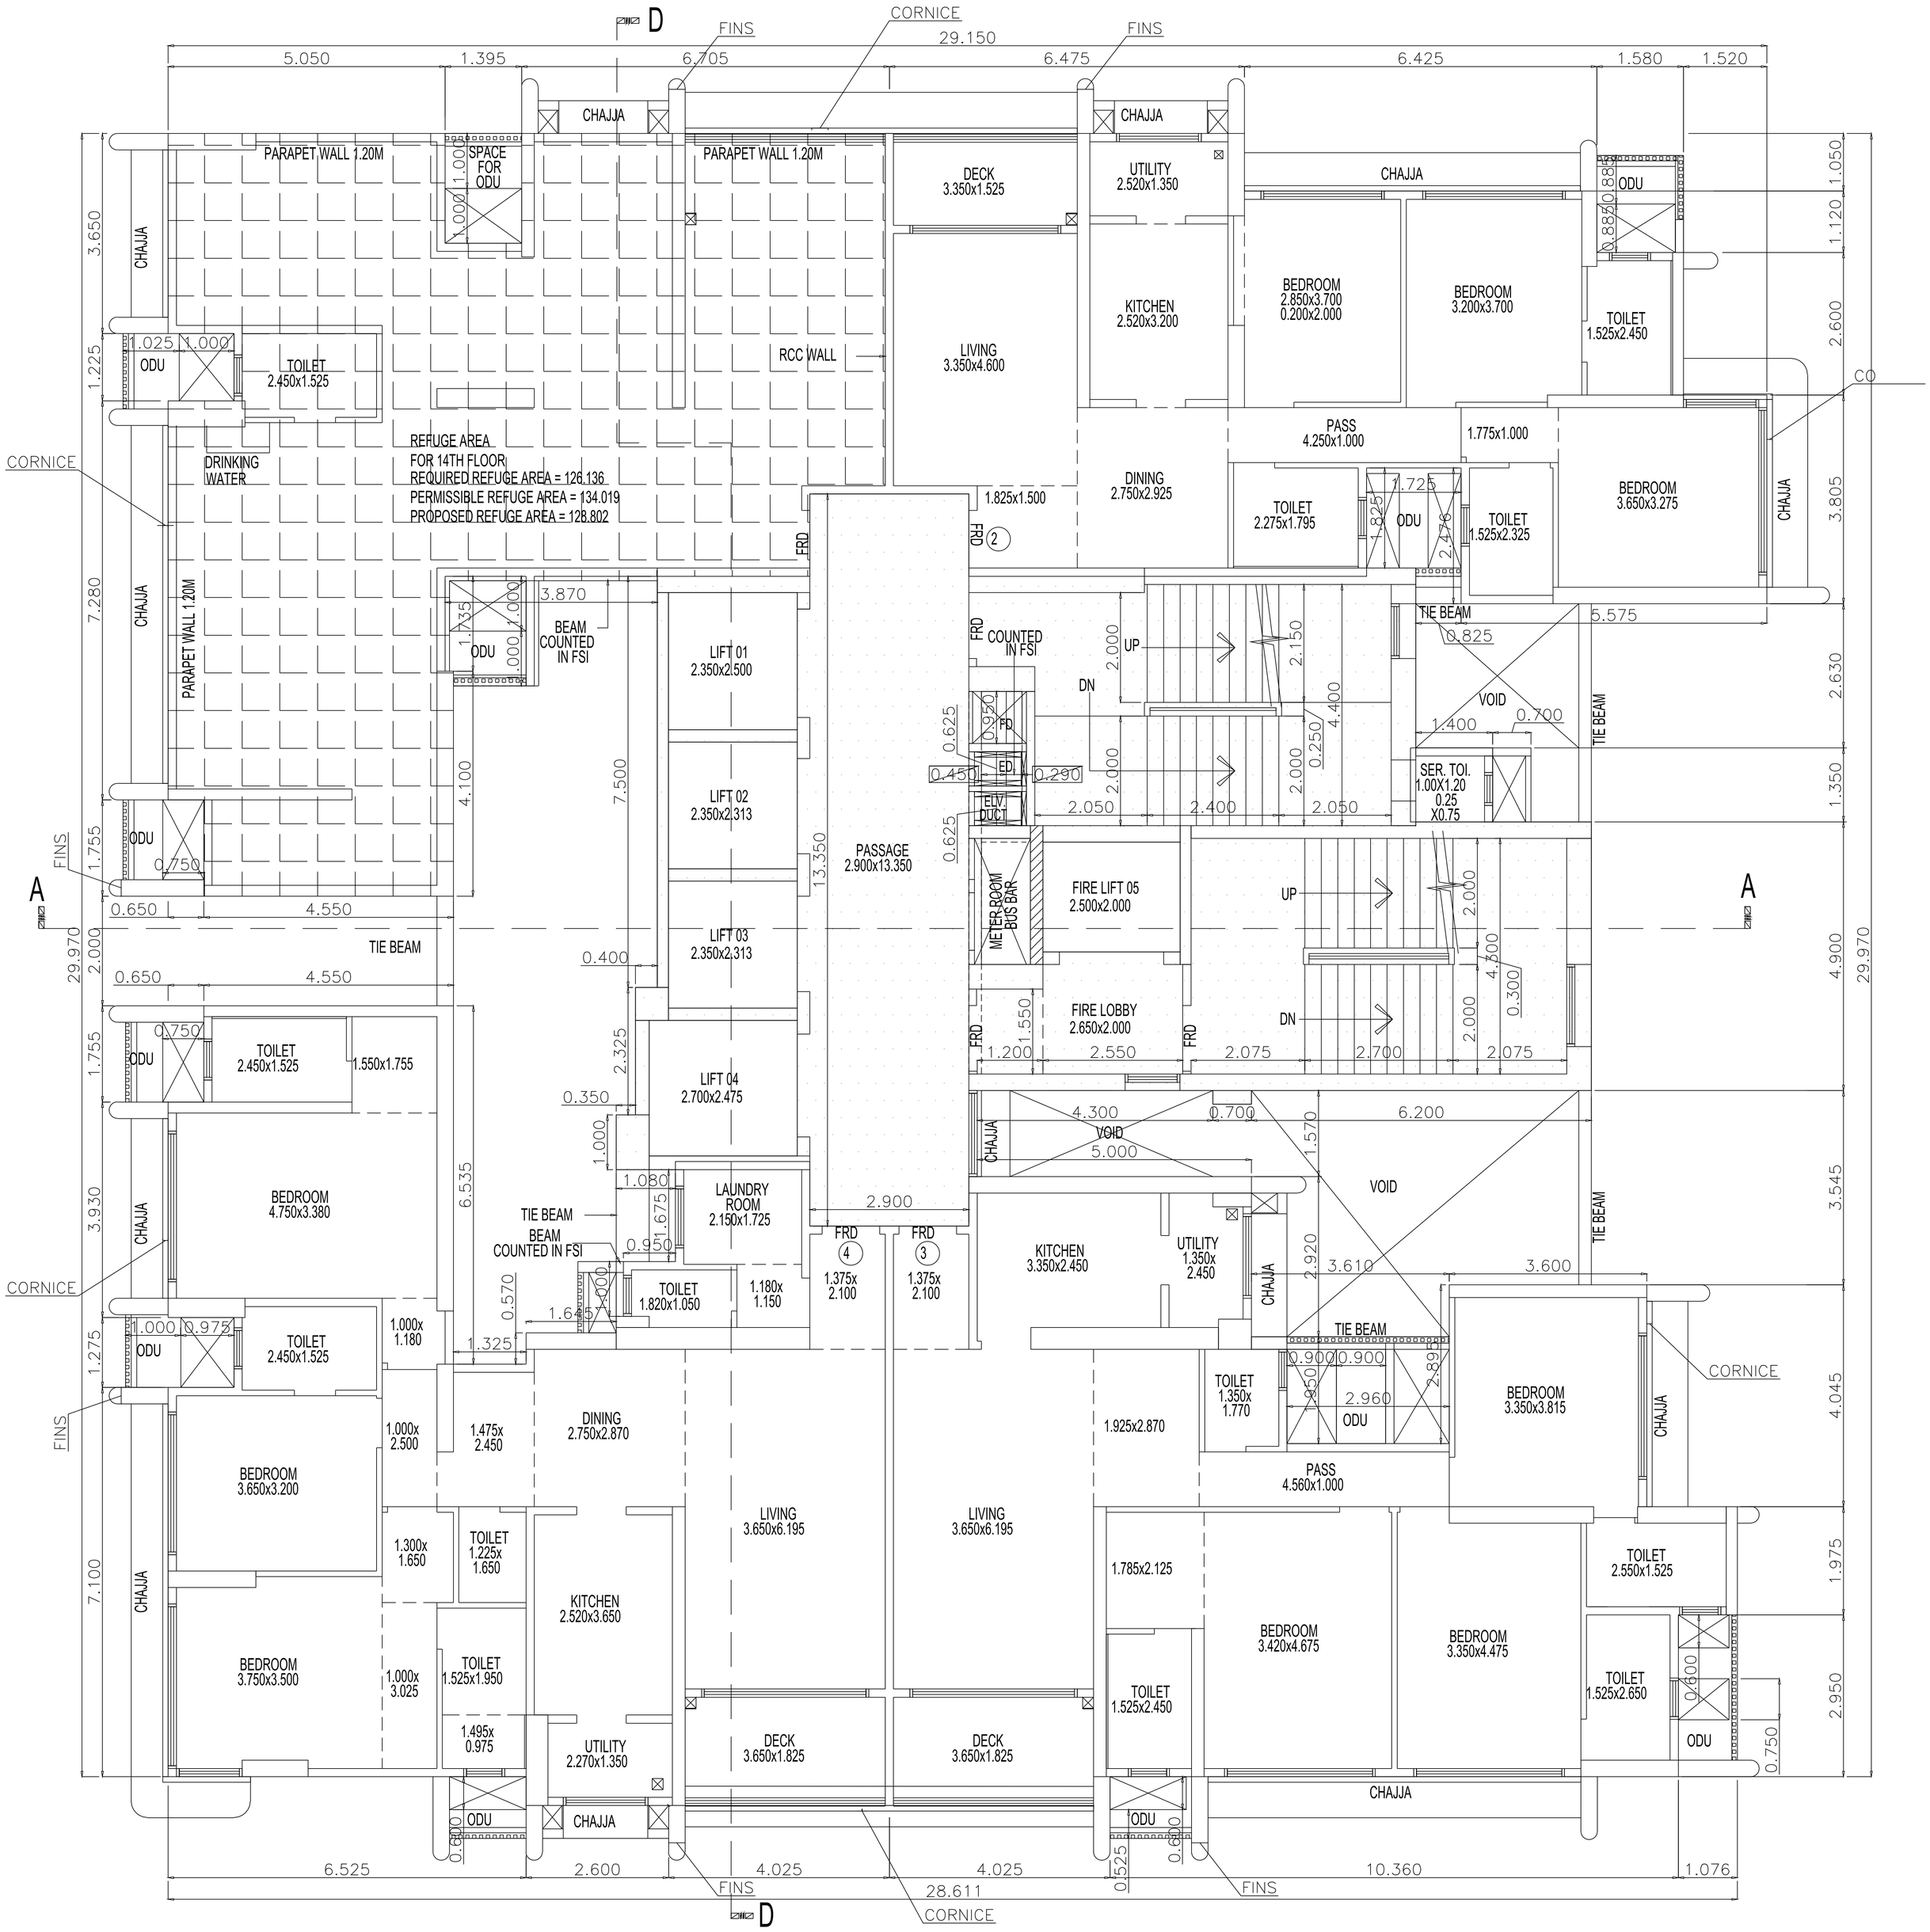


14TH REFUGE FLOOR PLAN
(TOWER B)
SCALE - 1:100

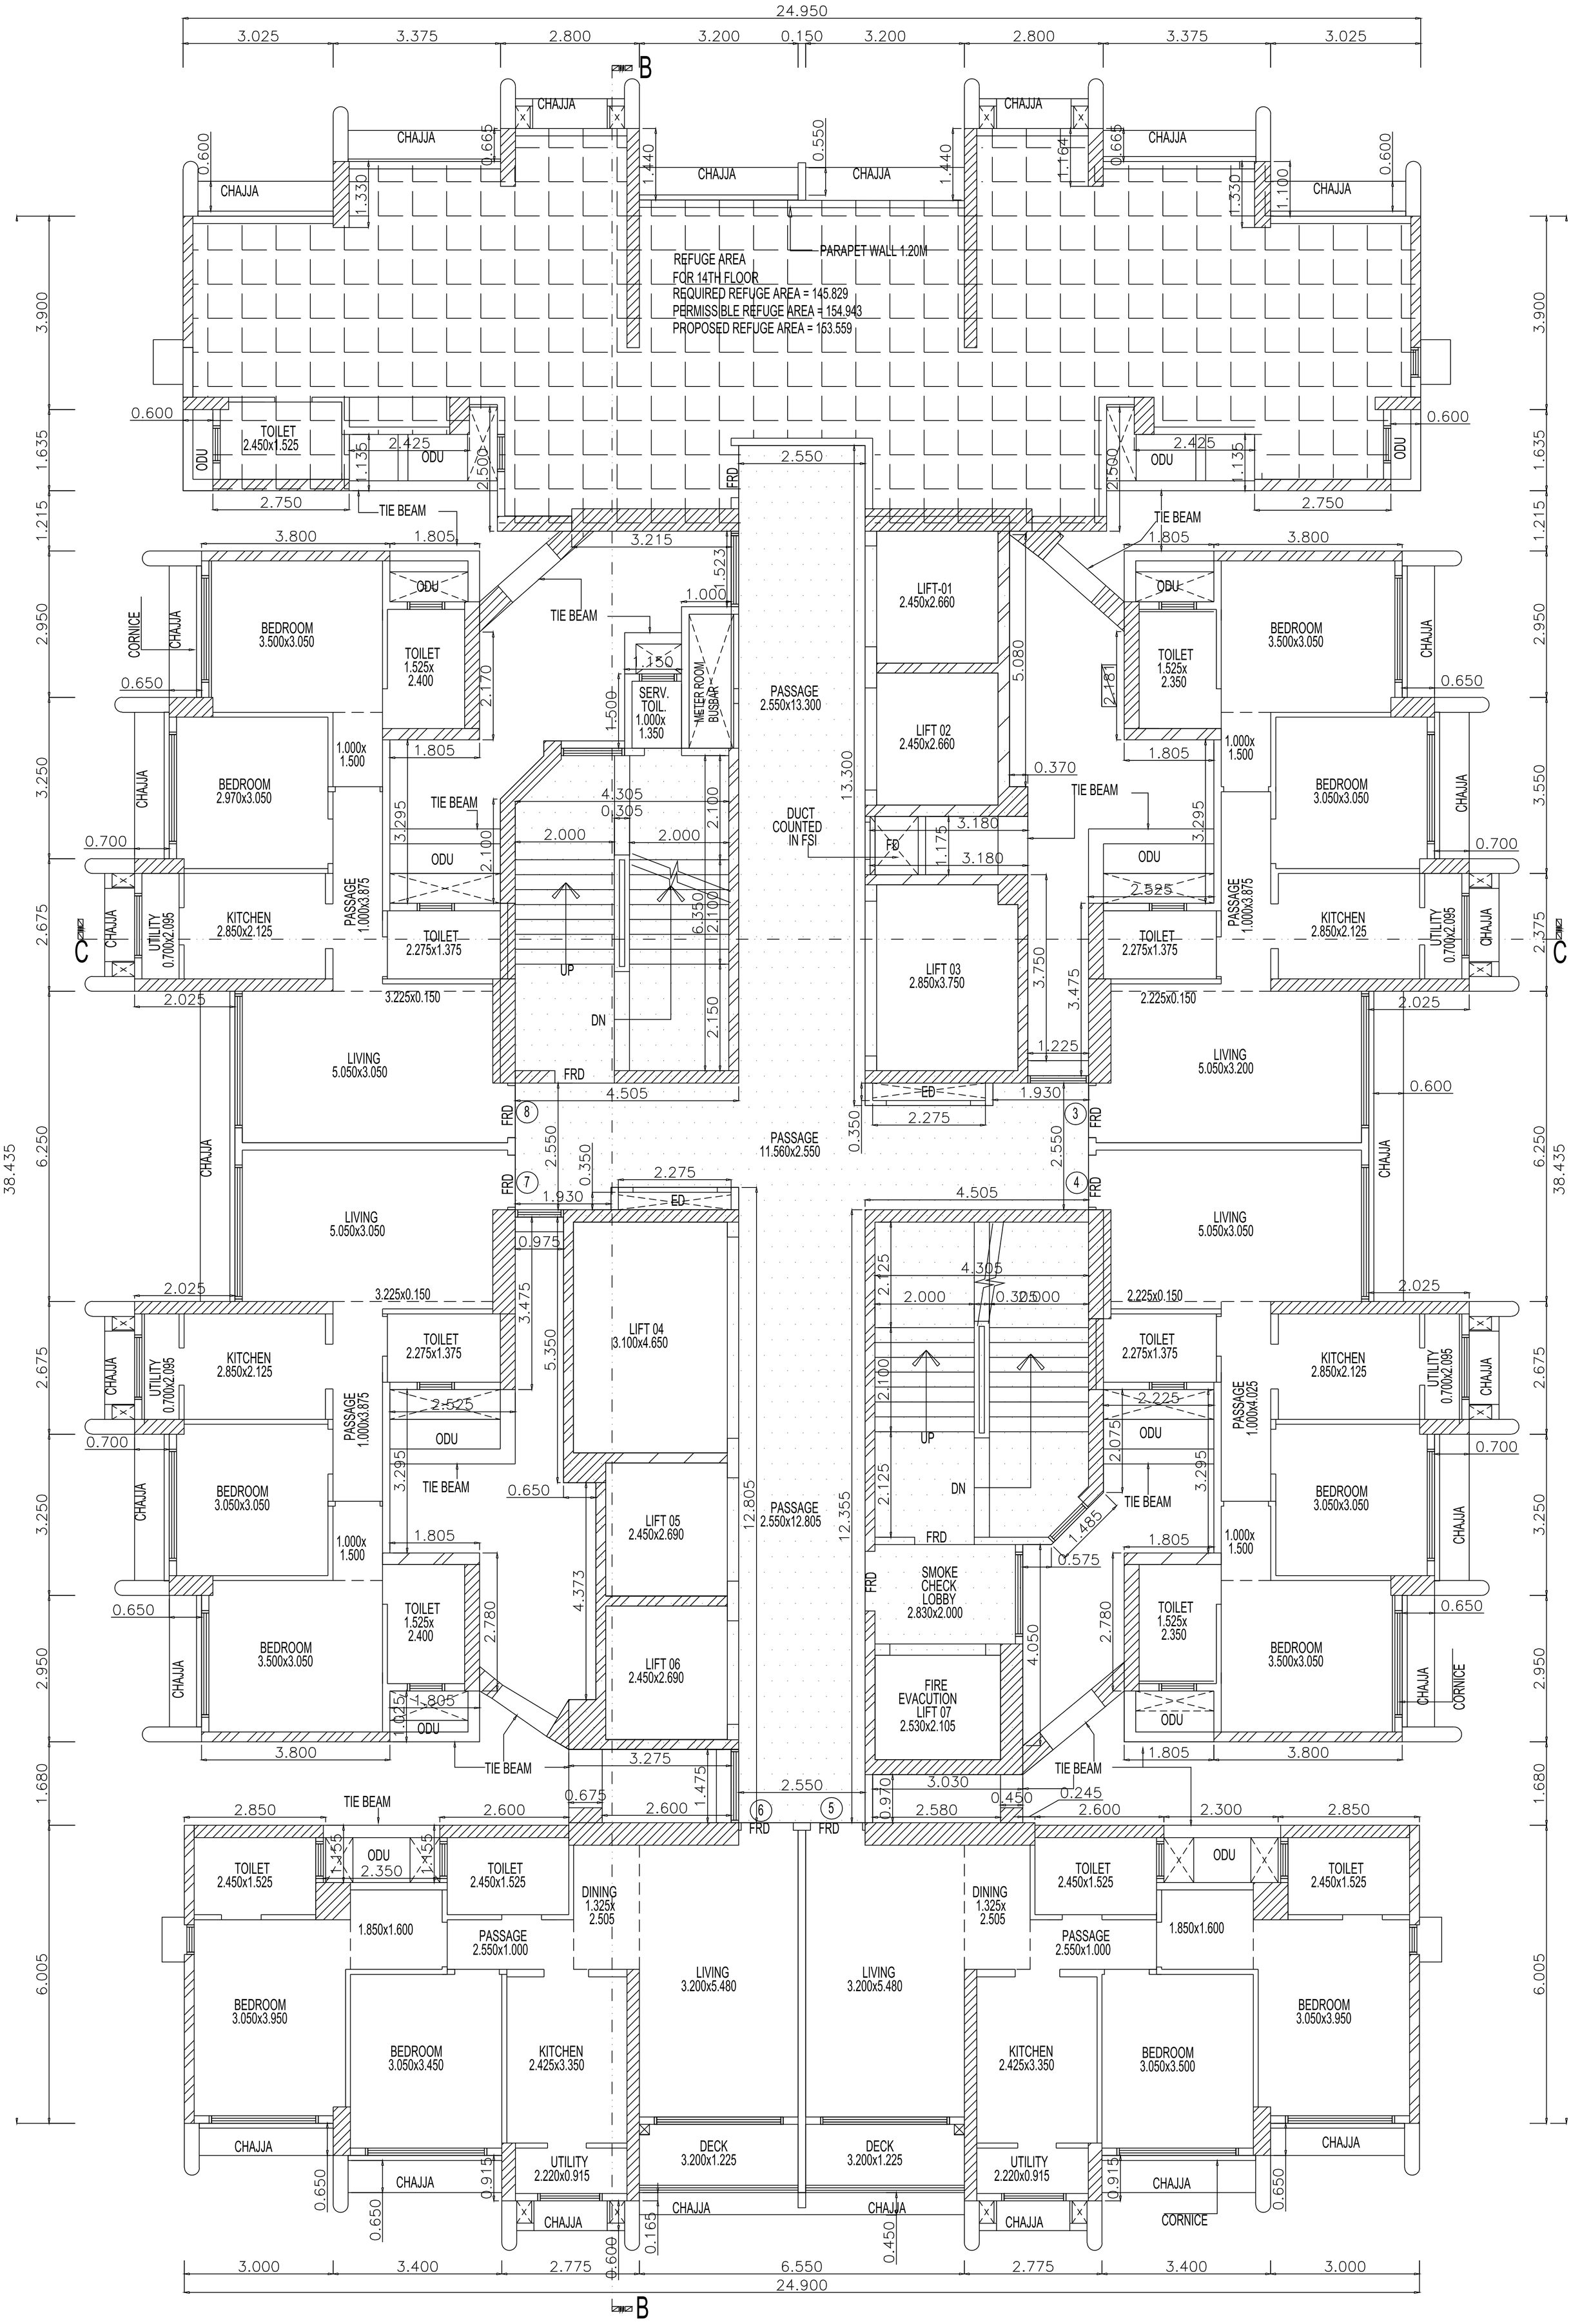

14TH FLOOR PLAN(REFUGE FLOOR PLAN)

TOWER A


SCALE - 1:100

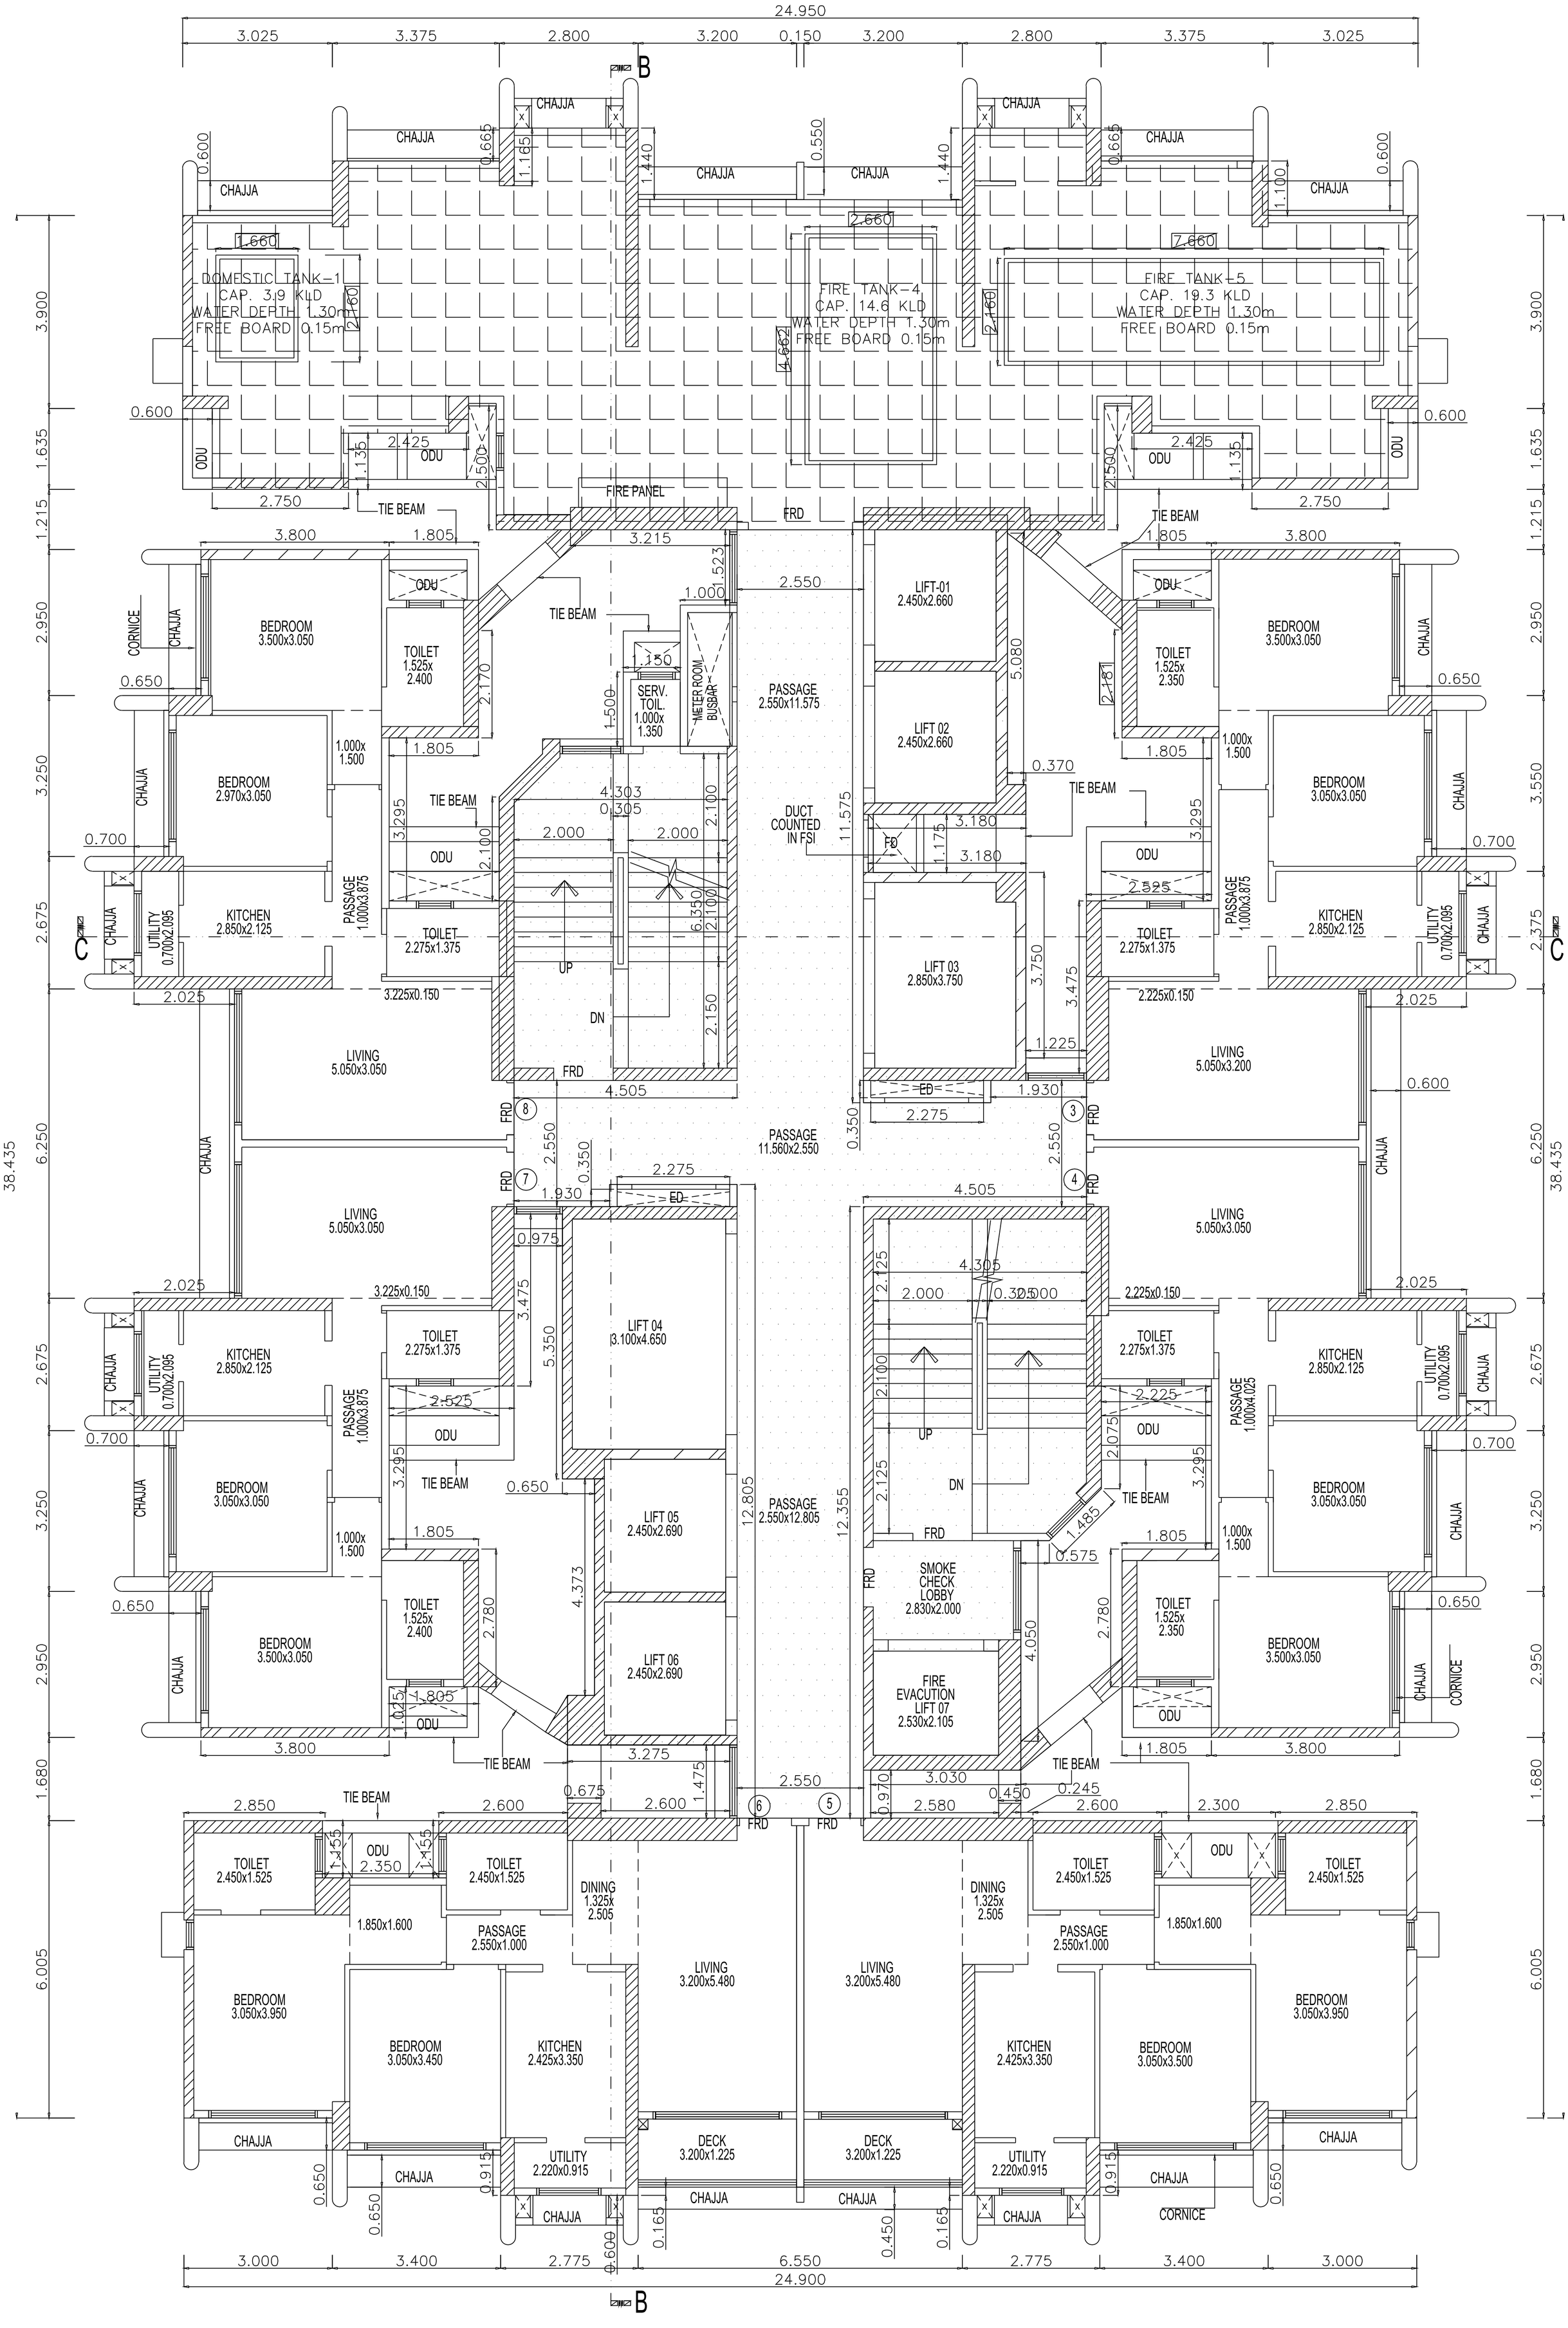


19TH FLOOR PLAN(BREAK PRESSURE TANK)

TOWER A


SCALE - 1:100

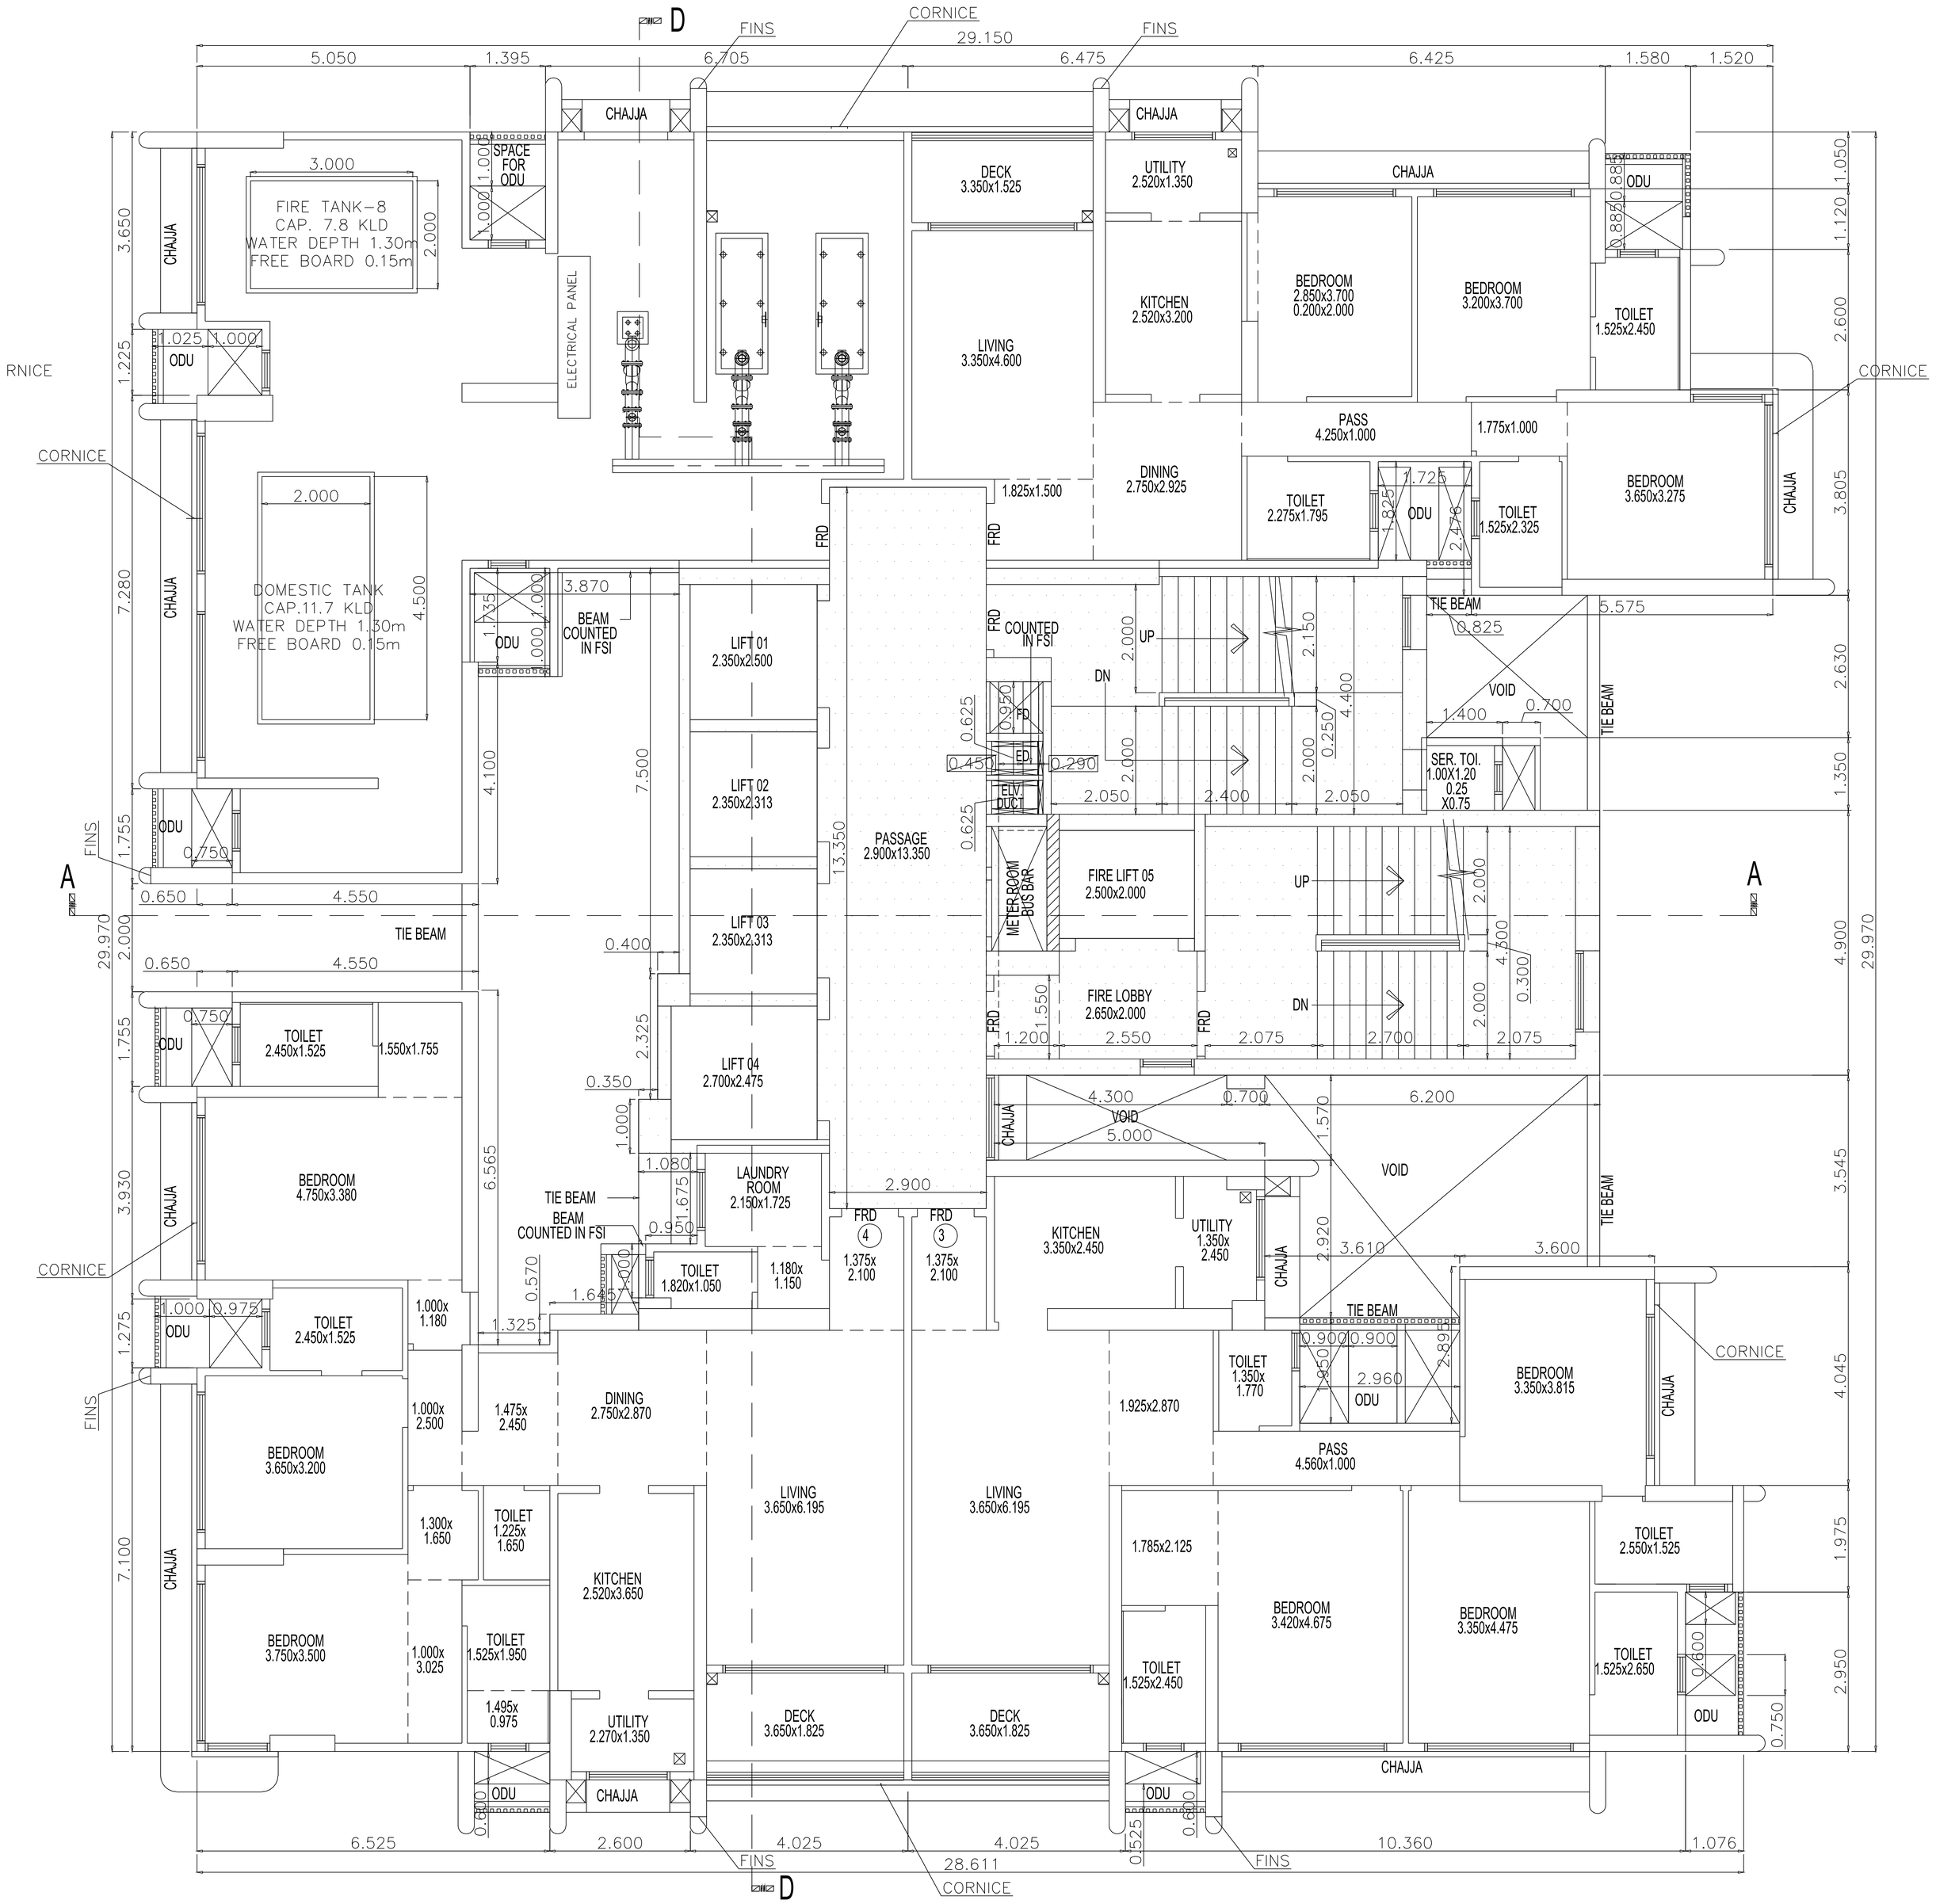

19TH BREAK PRESSURE TANK FLOOR PLAN
(TOWER B)
SCALE - 1:100

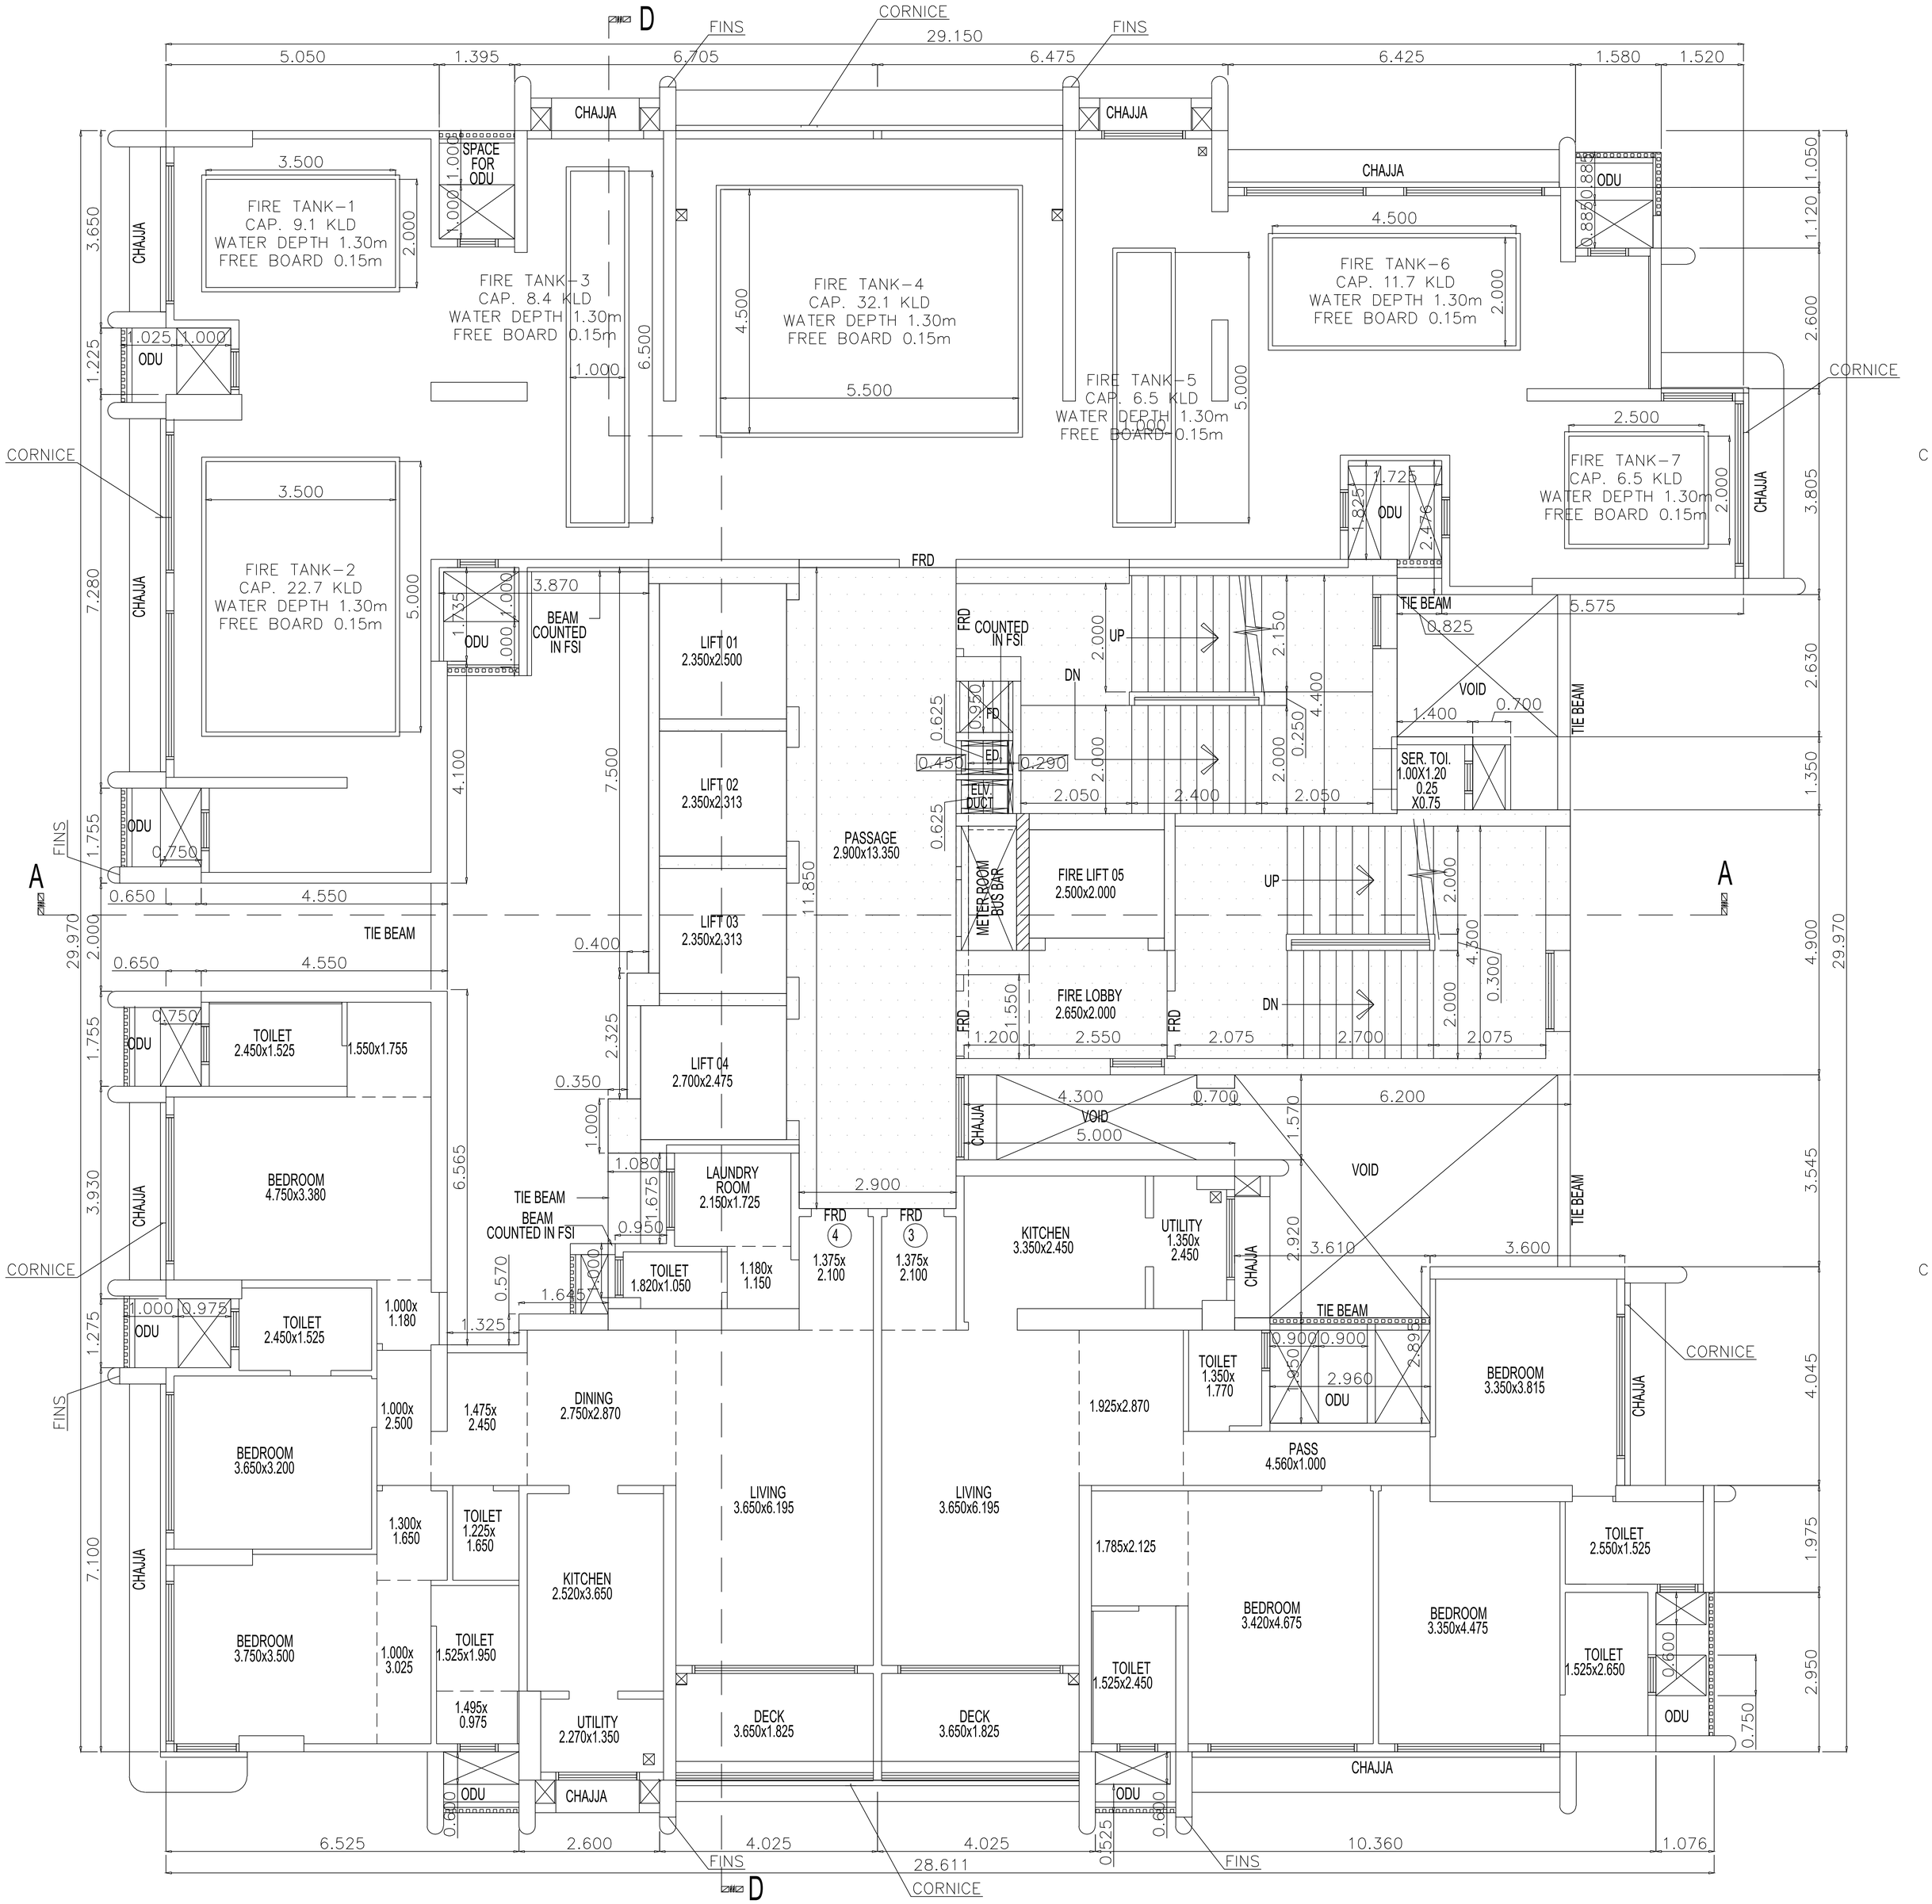


20TH BREAK PRESSURE TANK FLOOR PLAN
(TOWER B)
SCALE - 1:100

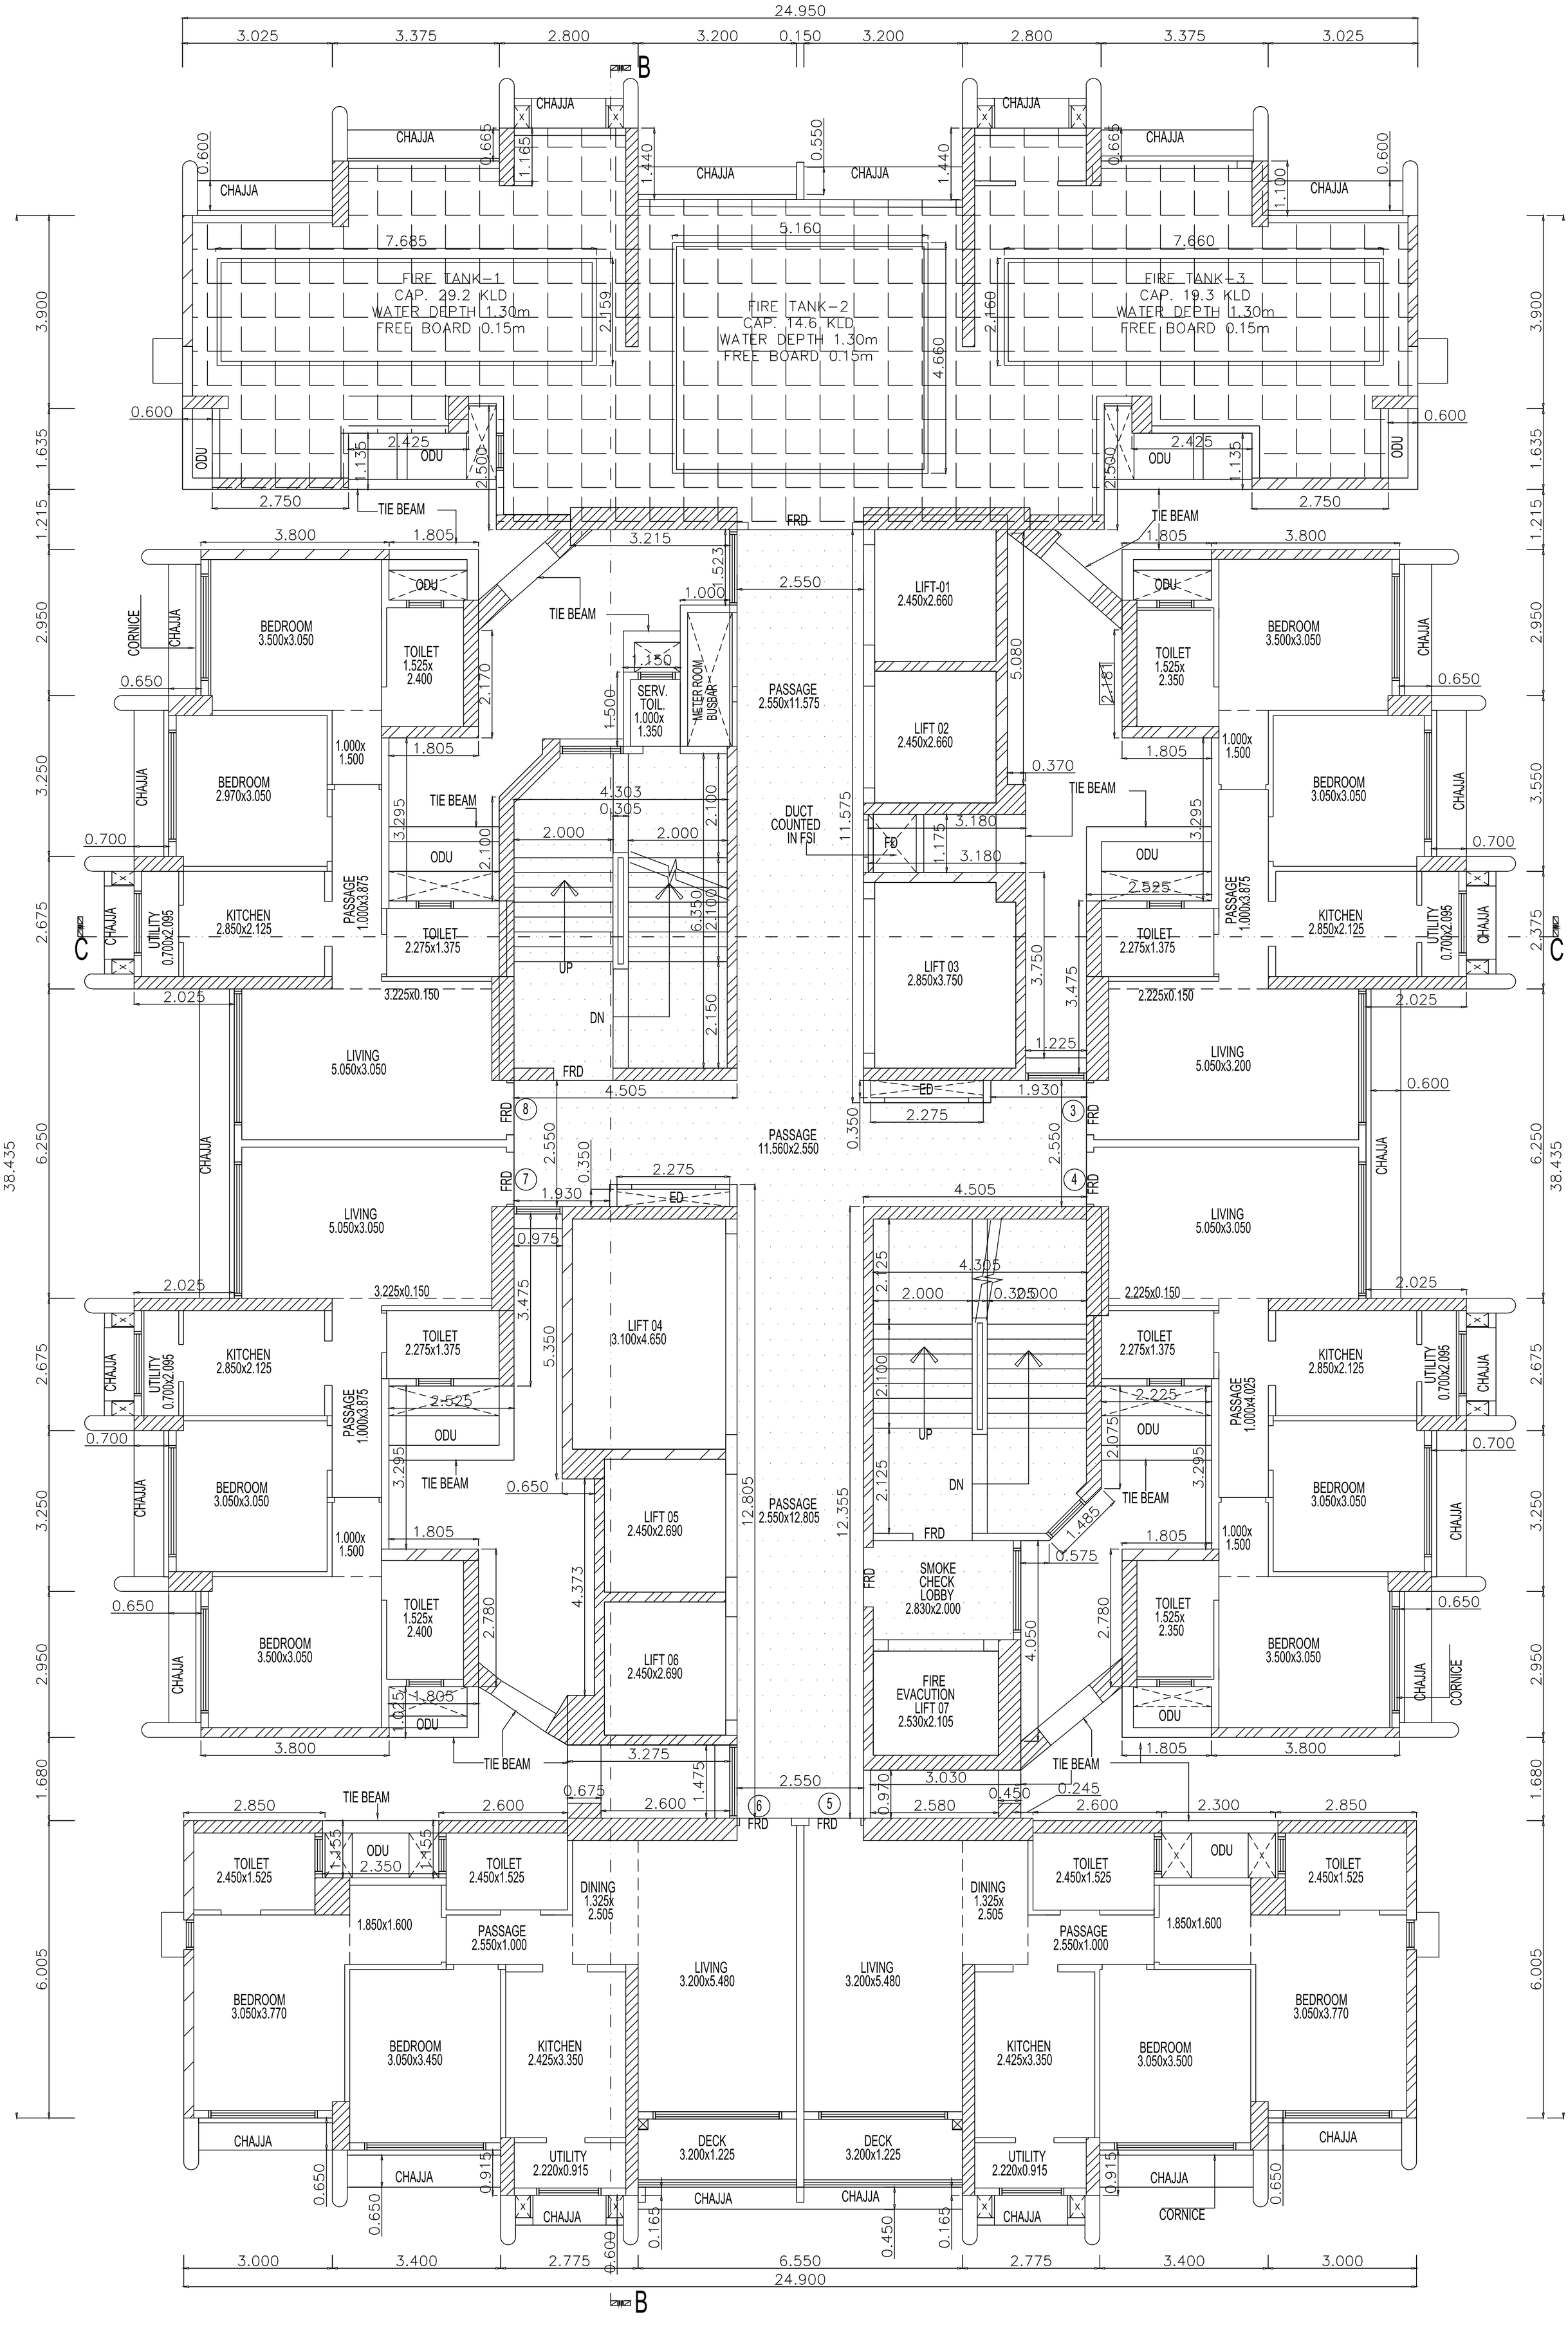


20TH FLOOR PLAN(BREAK PRESSURE TANK)

TOWER A

SCALE - 1:100

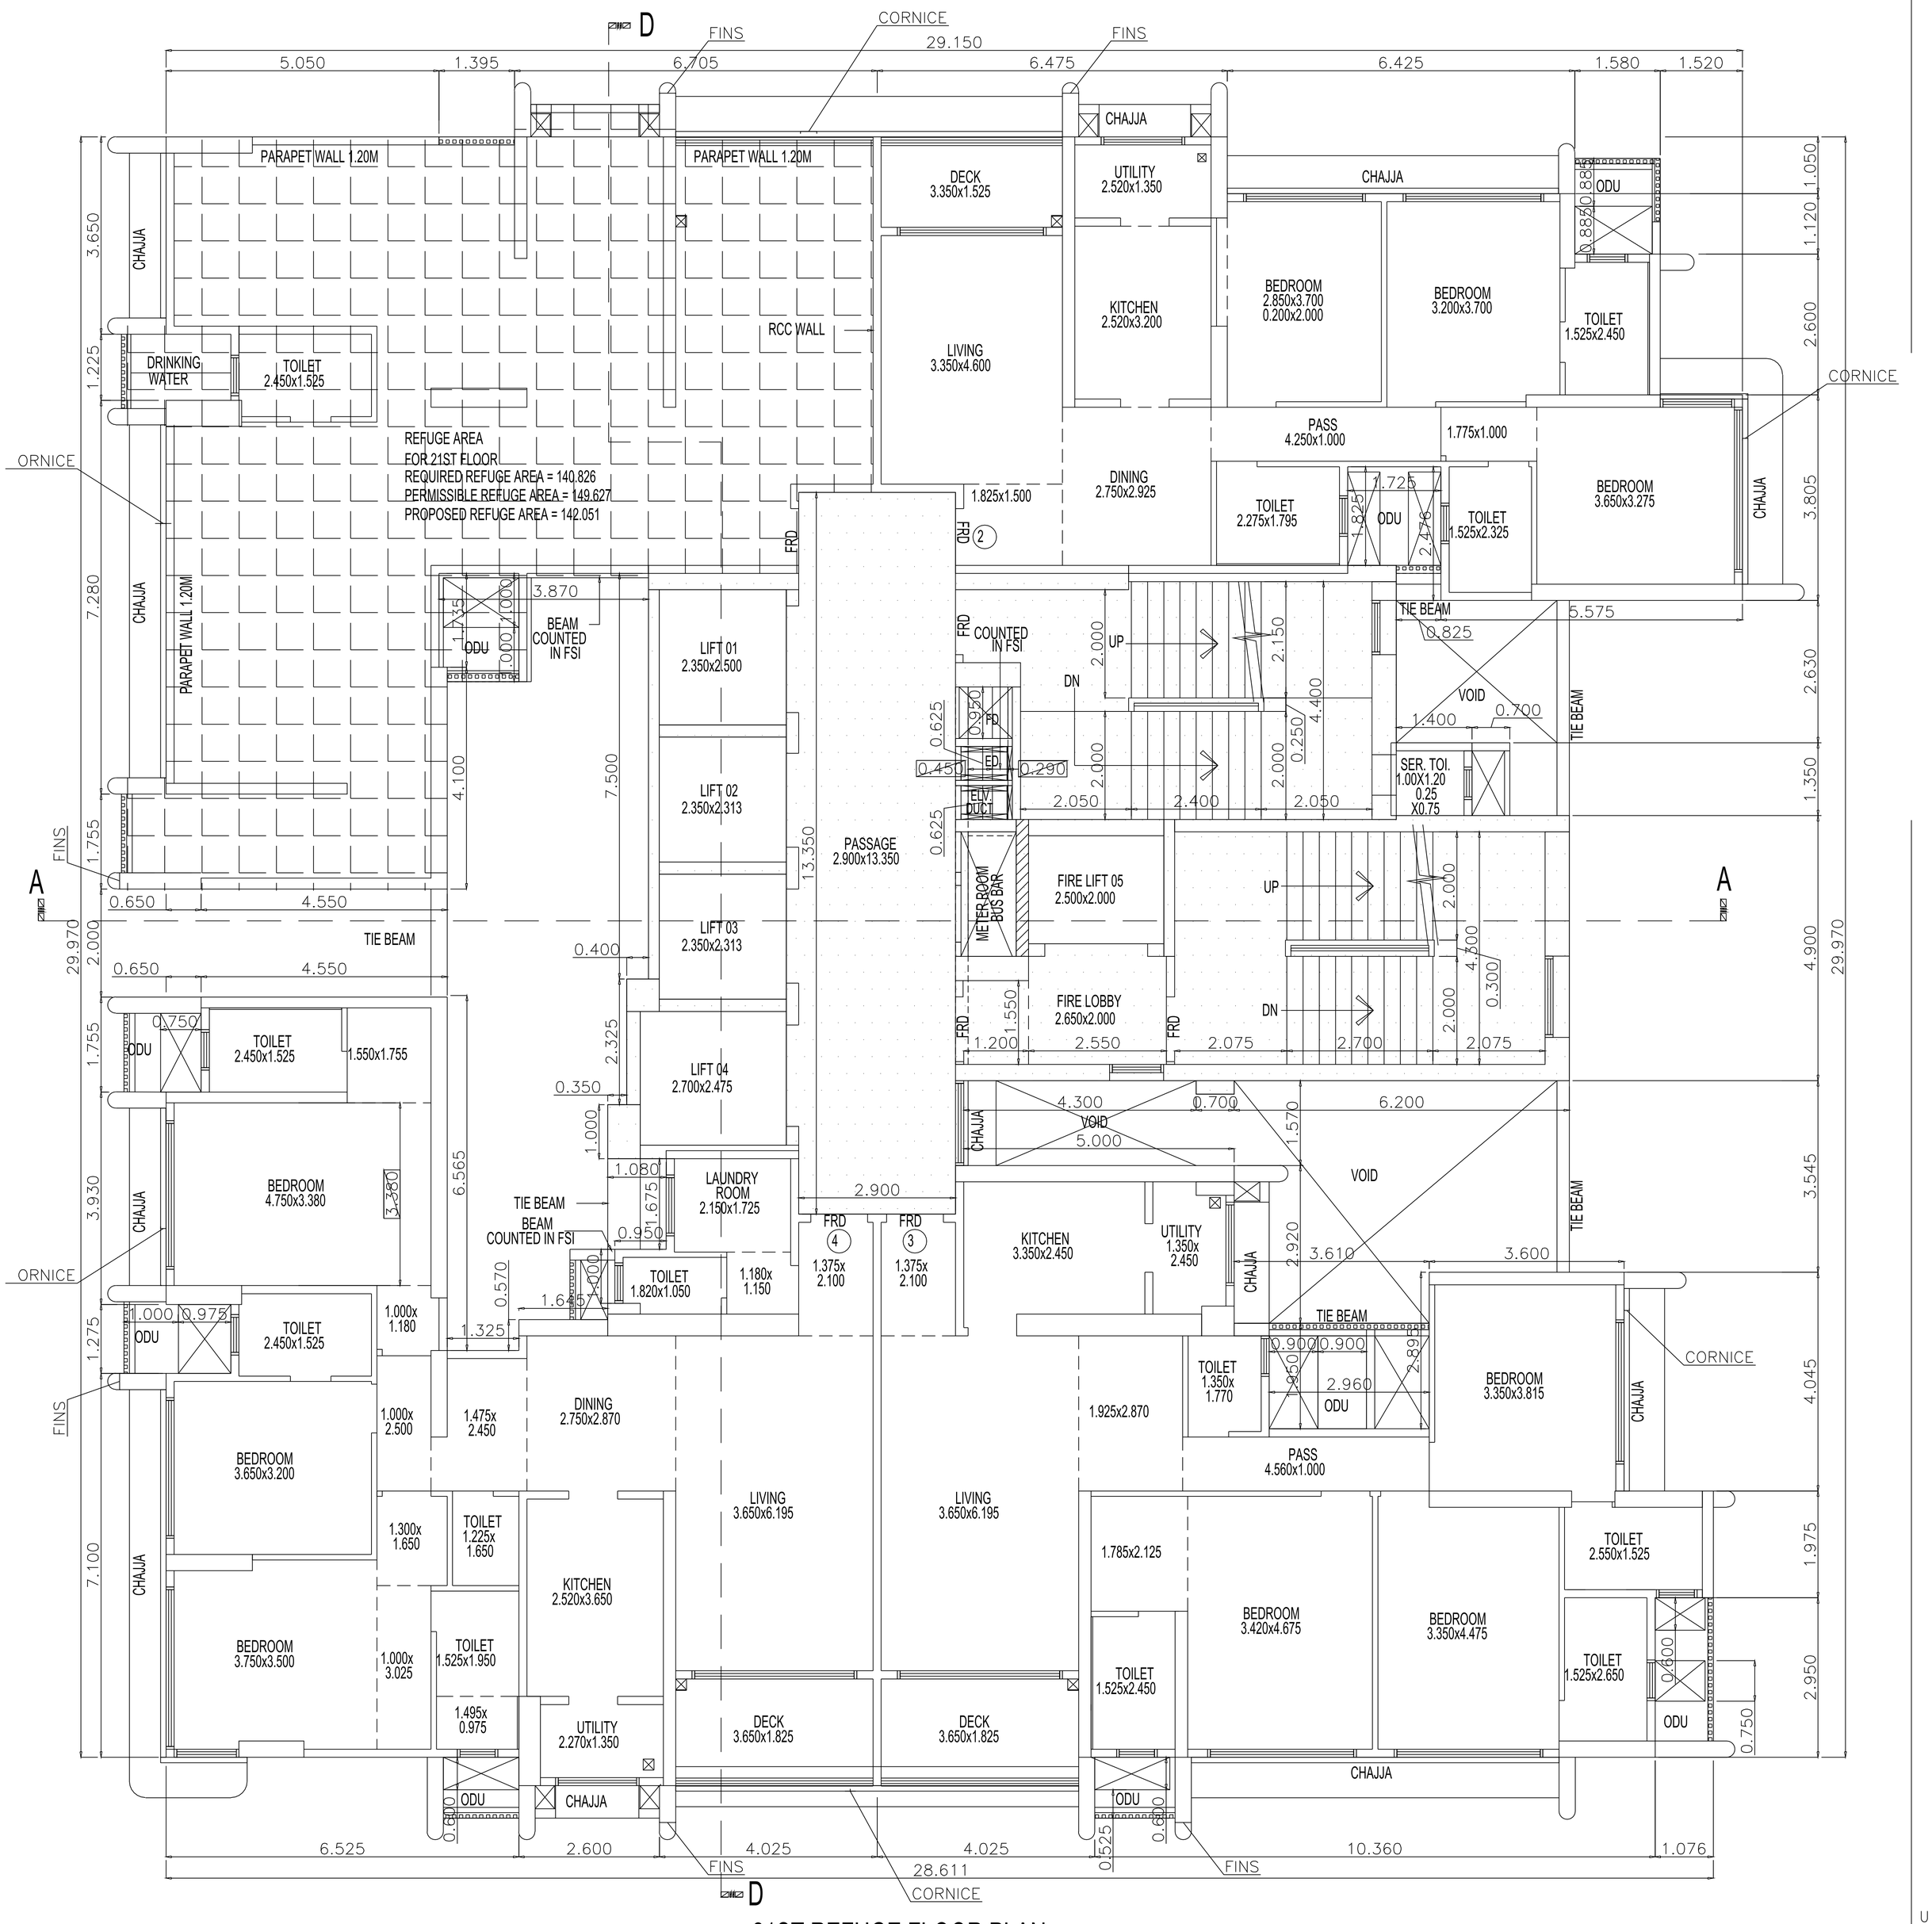

21ST REFUGE FLOOR PLAN
(TOWER B)
SCALE - 1:100

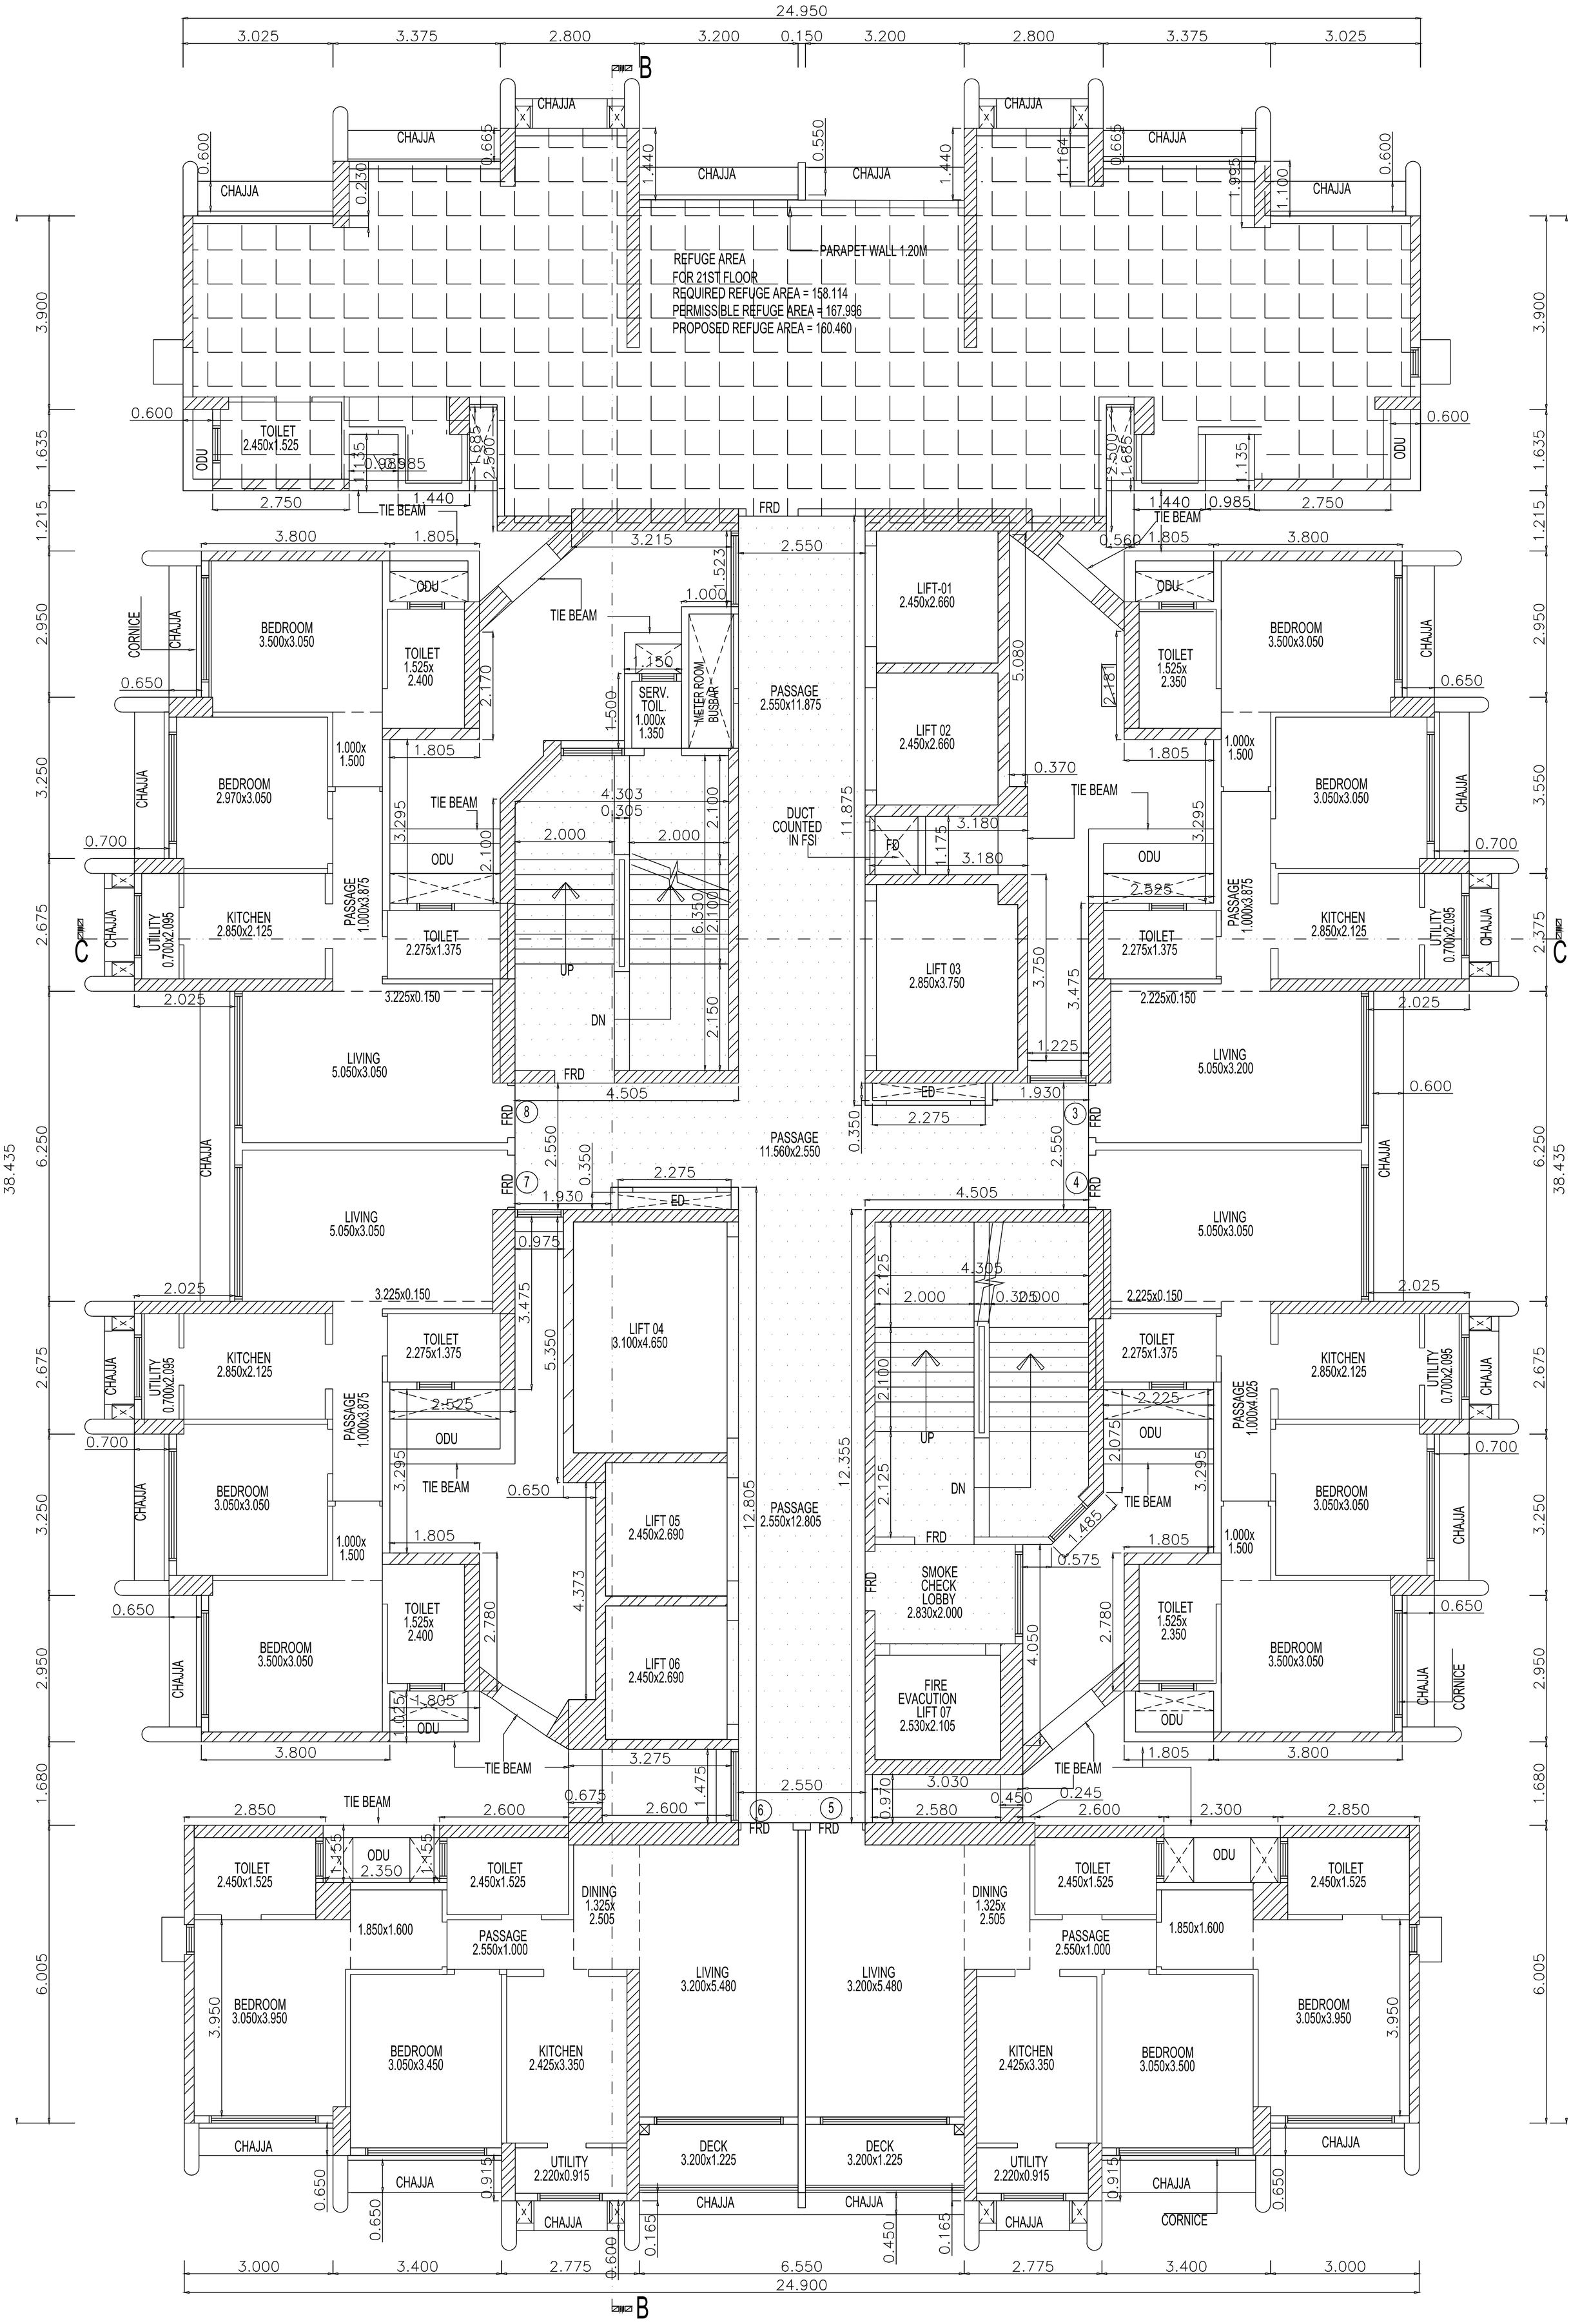

21ST FLOOR PLAN(REFUGE FLOOR PLAN)

TOWER A

SCALE - 1:100