
FOR 3RD & 5TH FLOOR

SCALE - 1:100

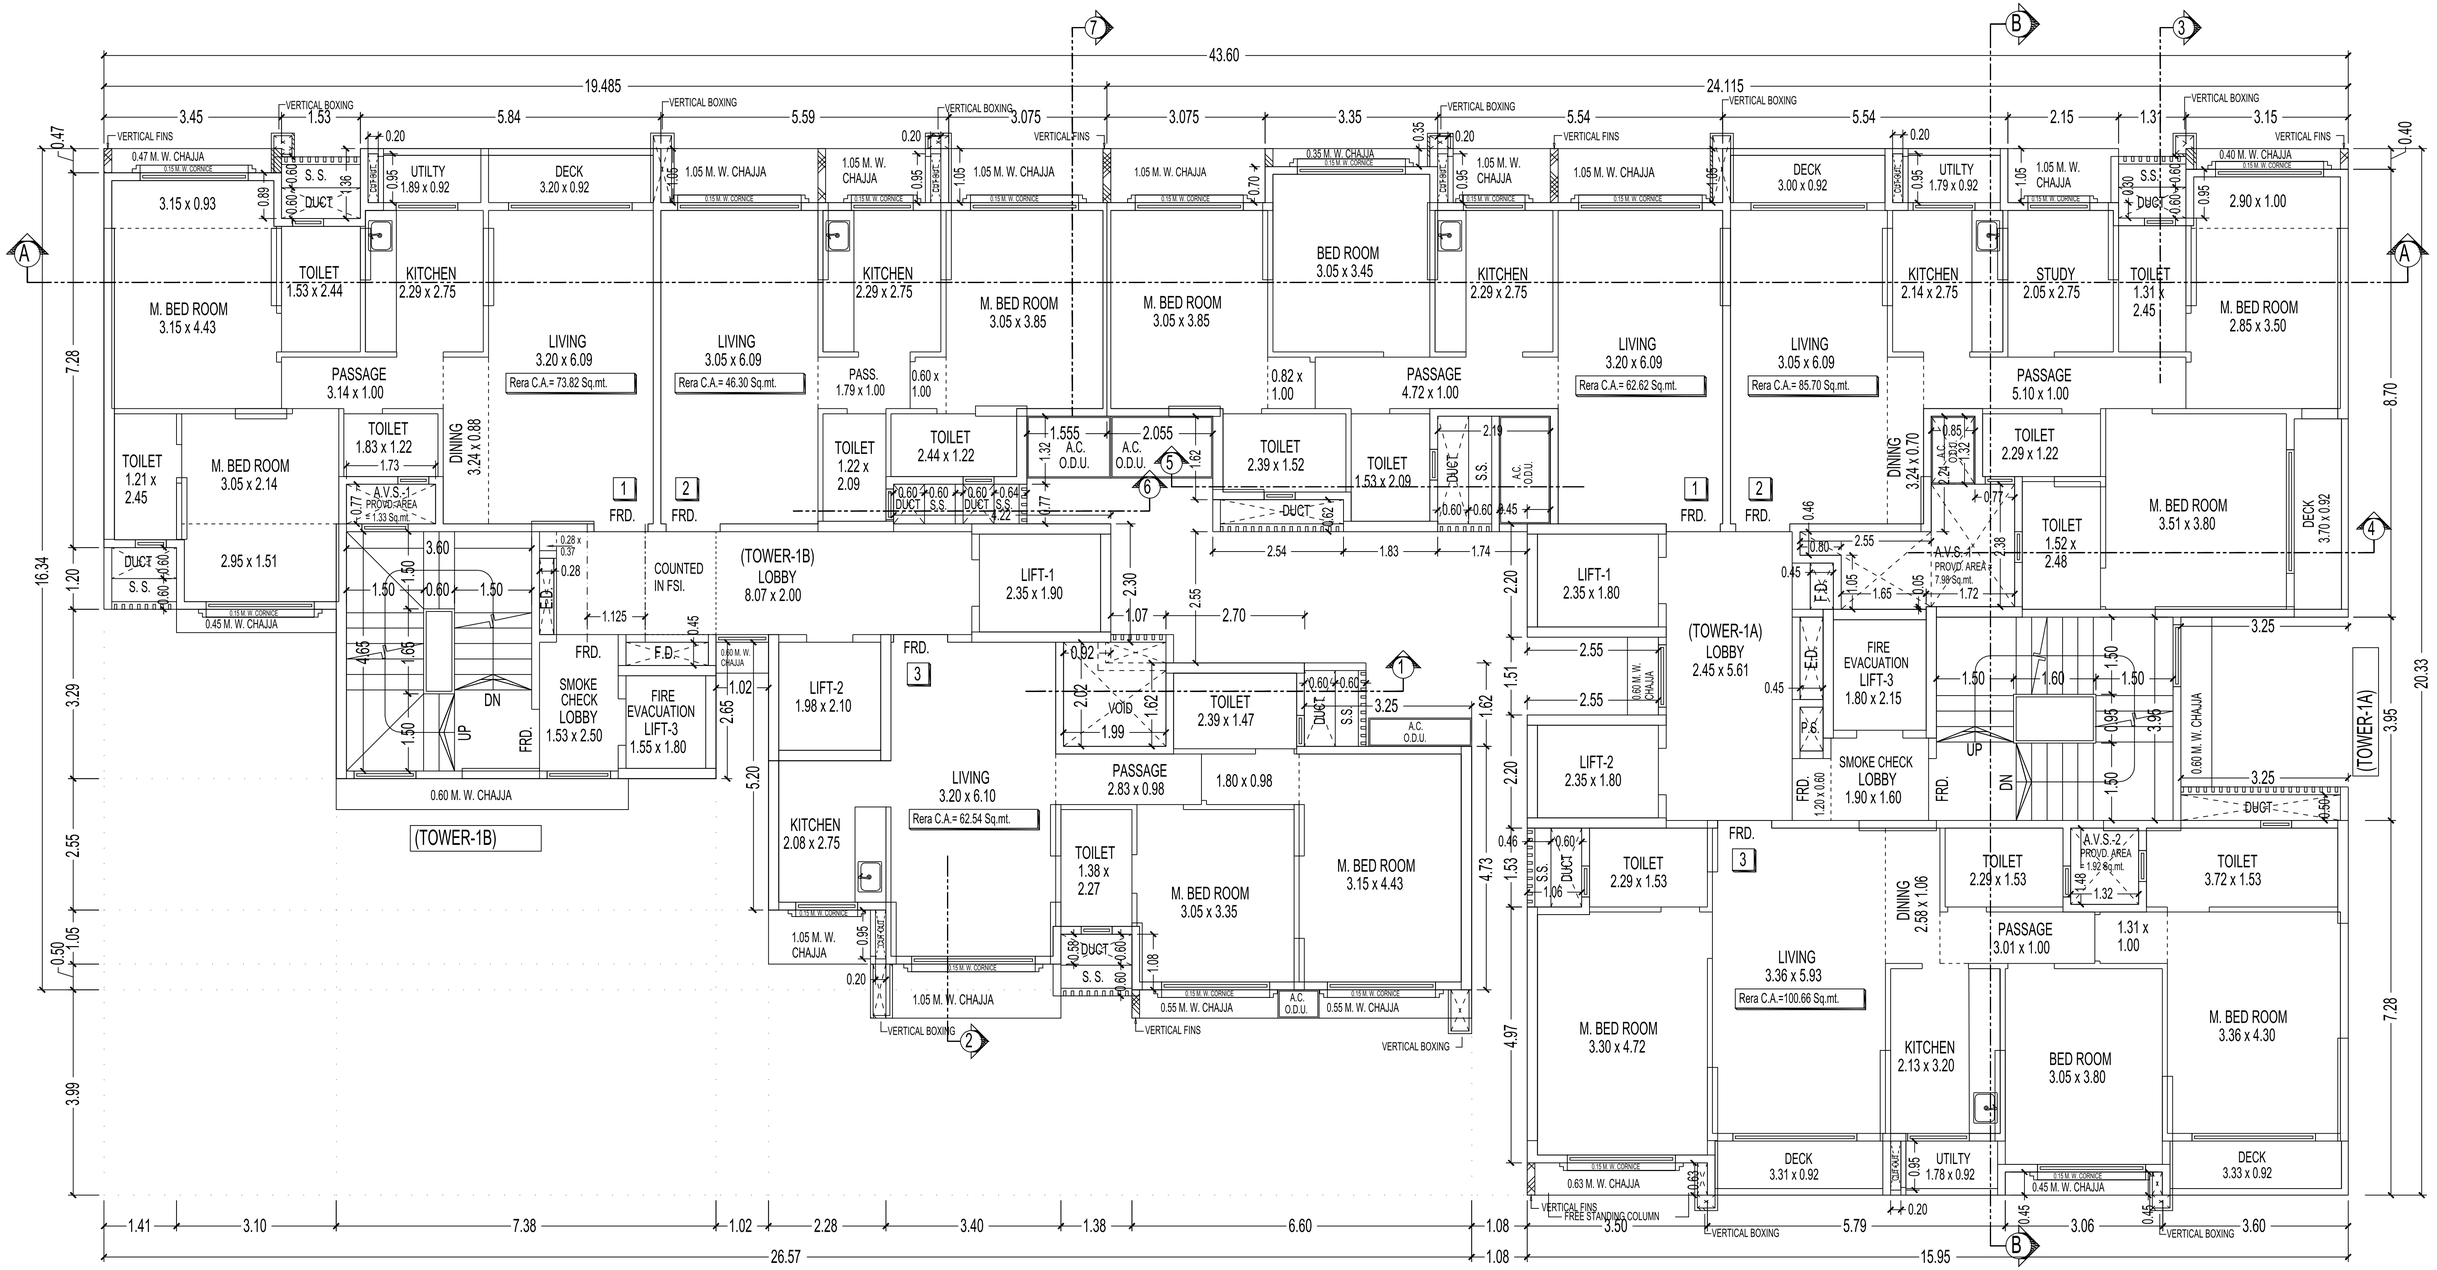


(TOWER-1A & 1B) 3RD FLOOR PLAN


SCALE - 1:100

FOR 4TH FLOOR

SCALE - 1:100

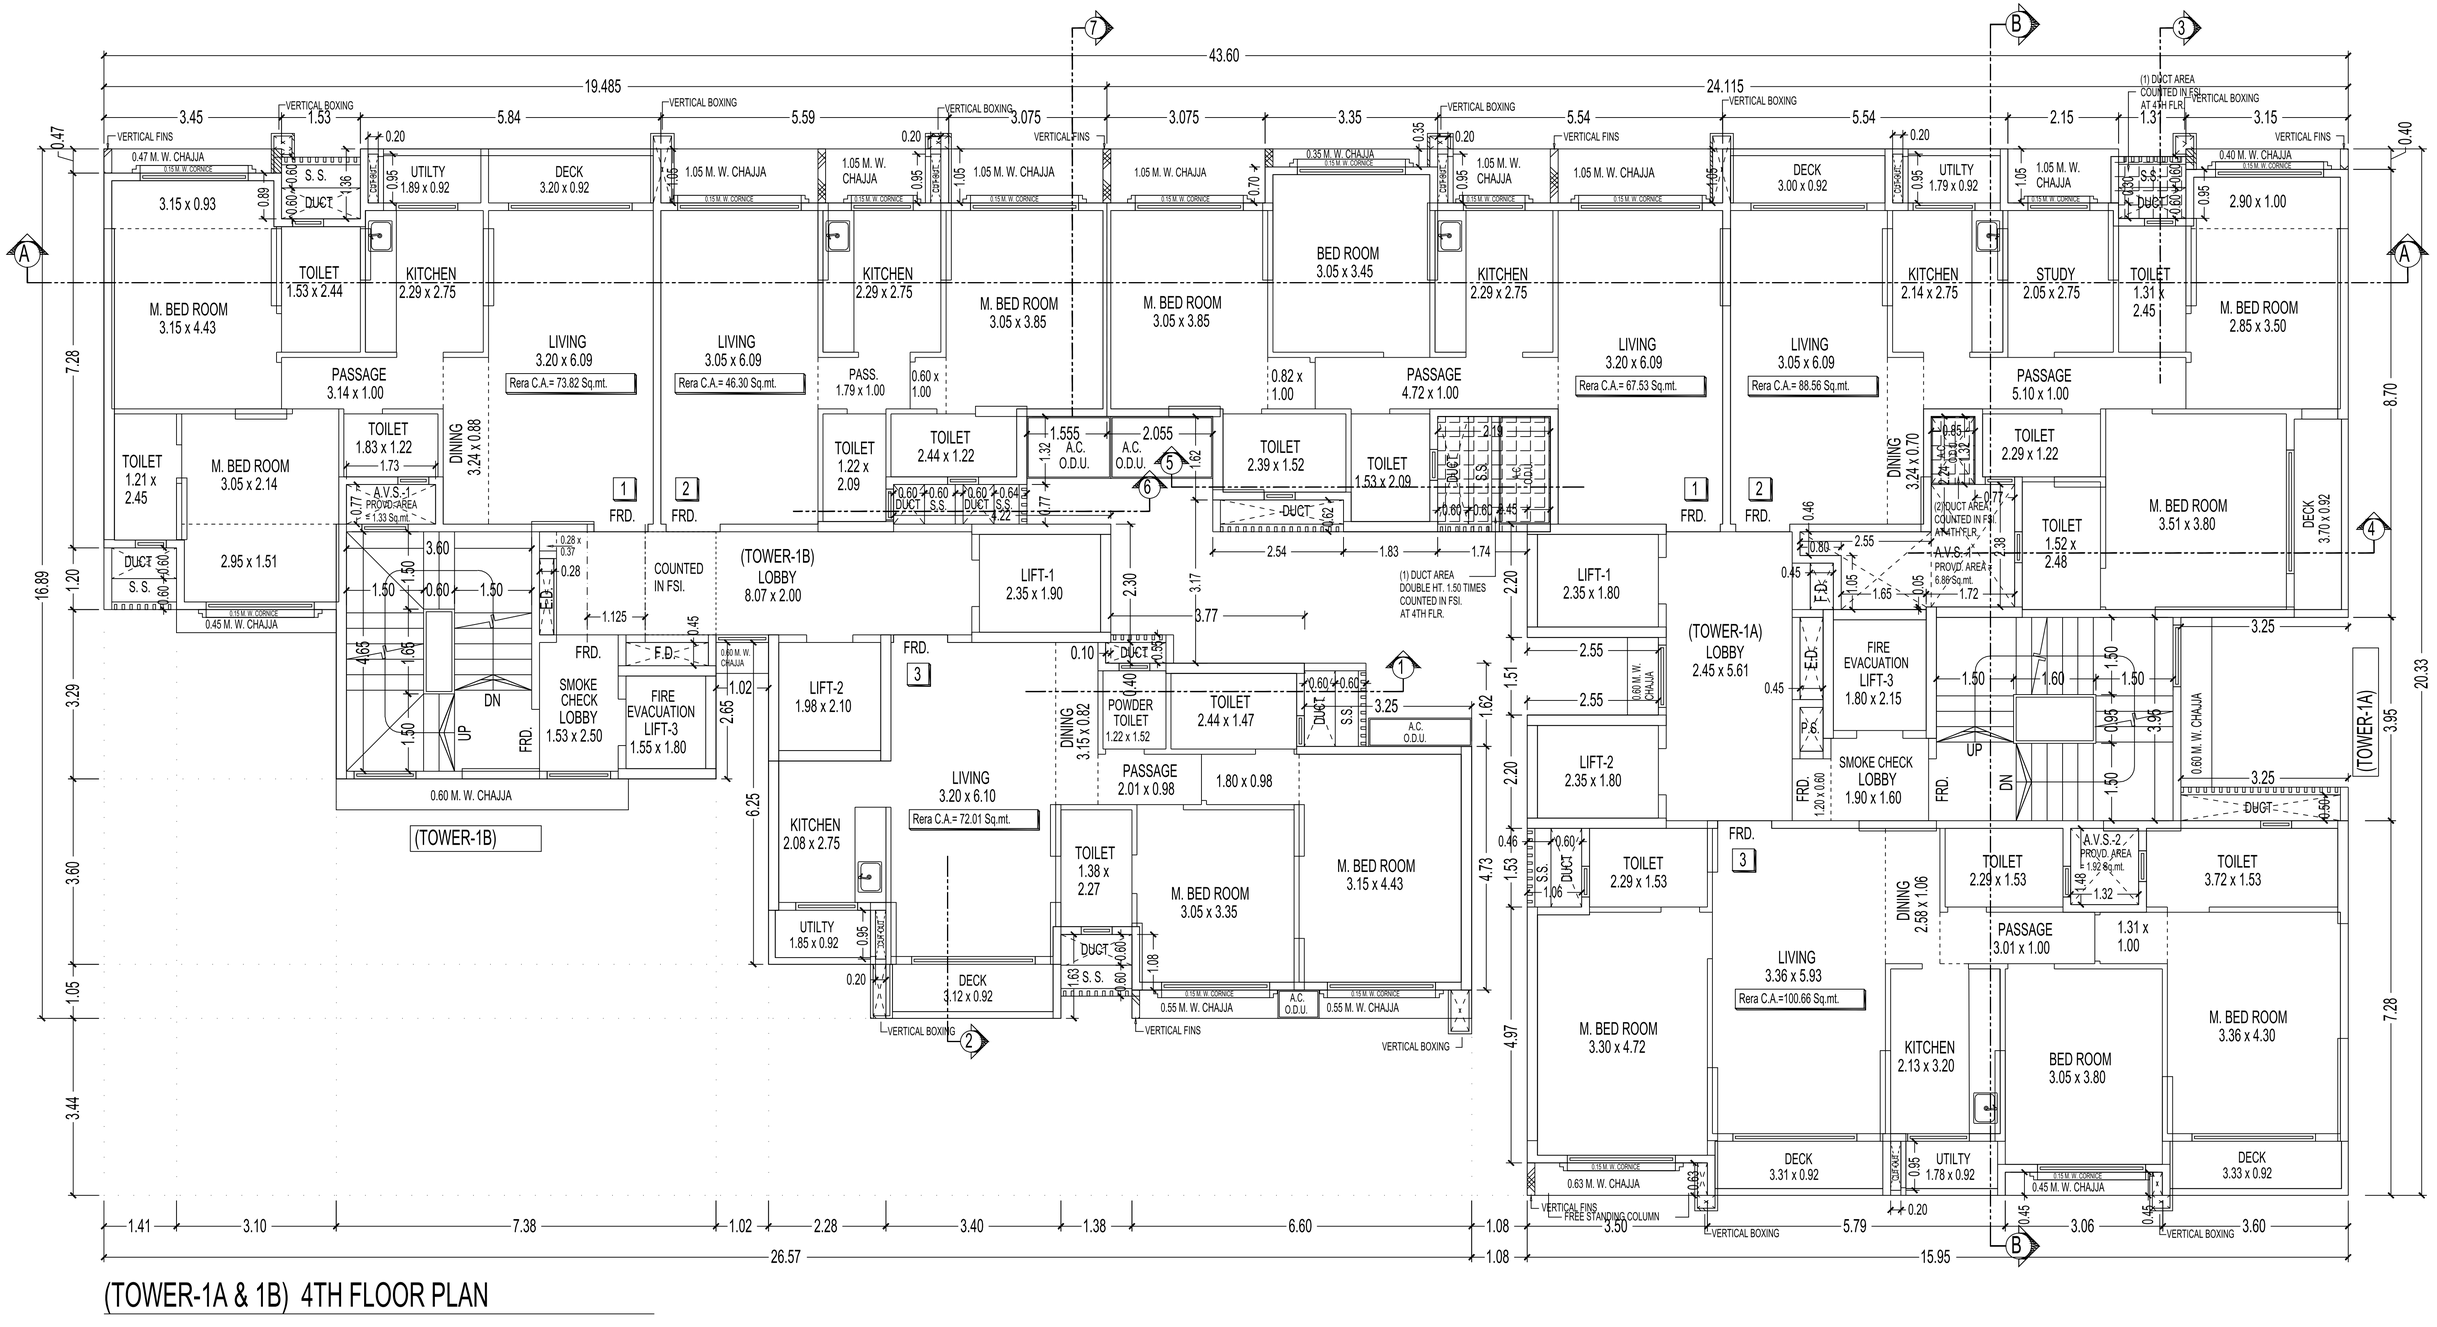

(TOWER-1A & 1B) 4TH FLOOR PLAN

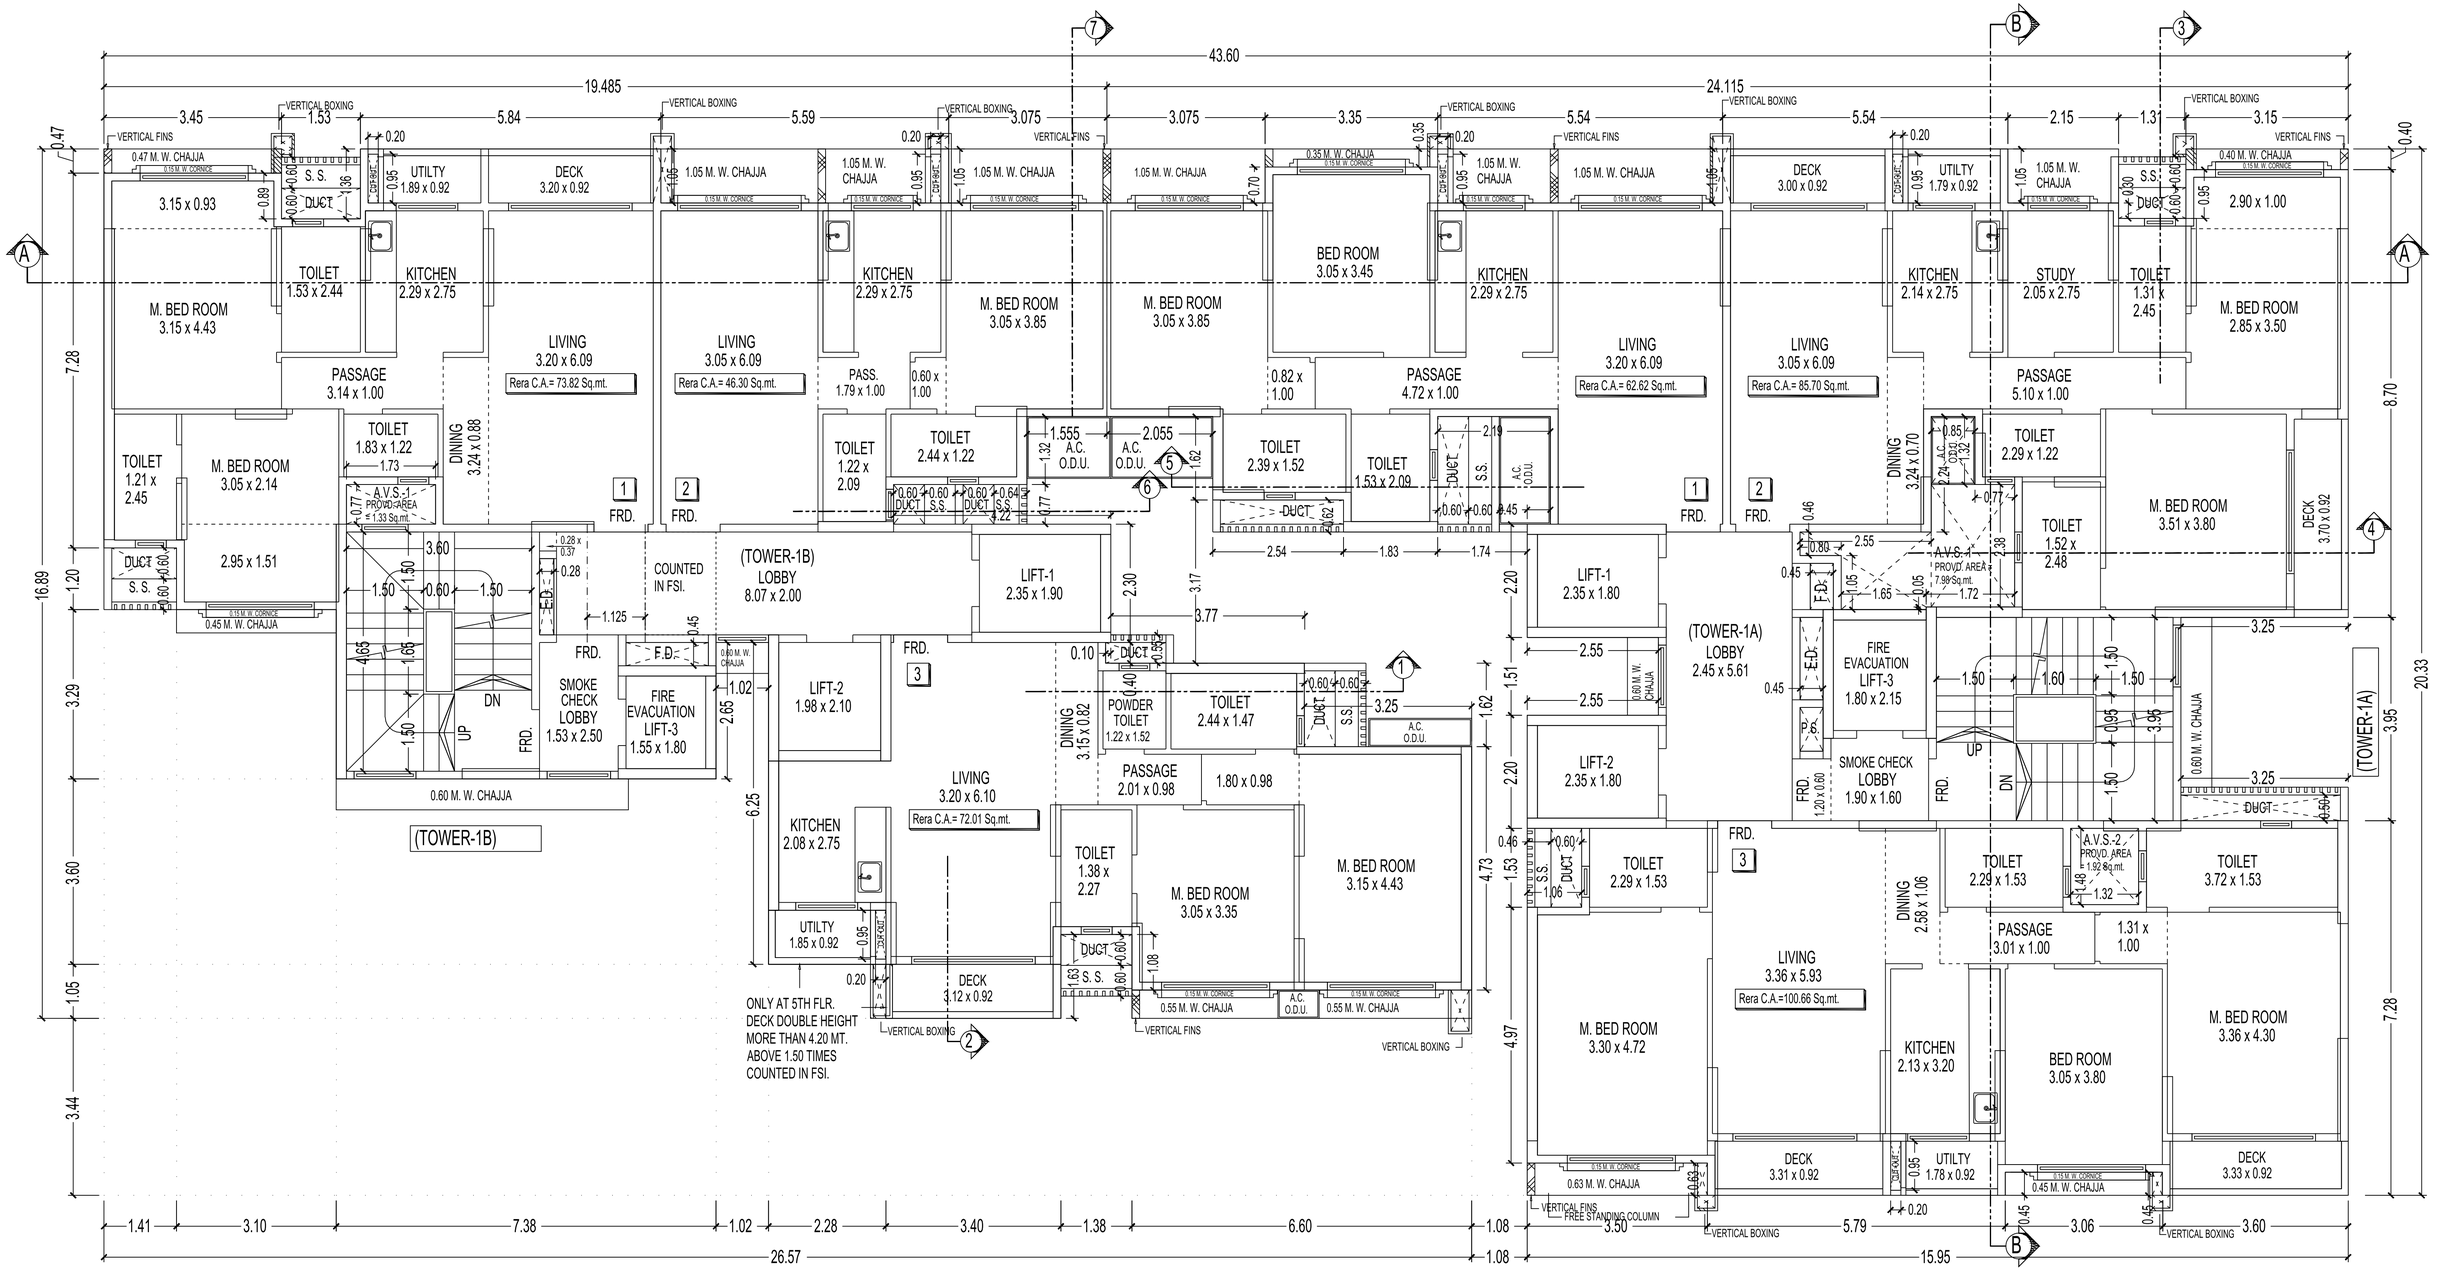


(TOWER-1A & 1B) 5TH FLOOR PLAN

SCALE - 1:100

FOR 6TH FLOOR


SCALE - 1:100

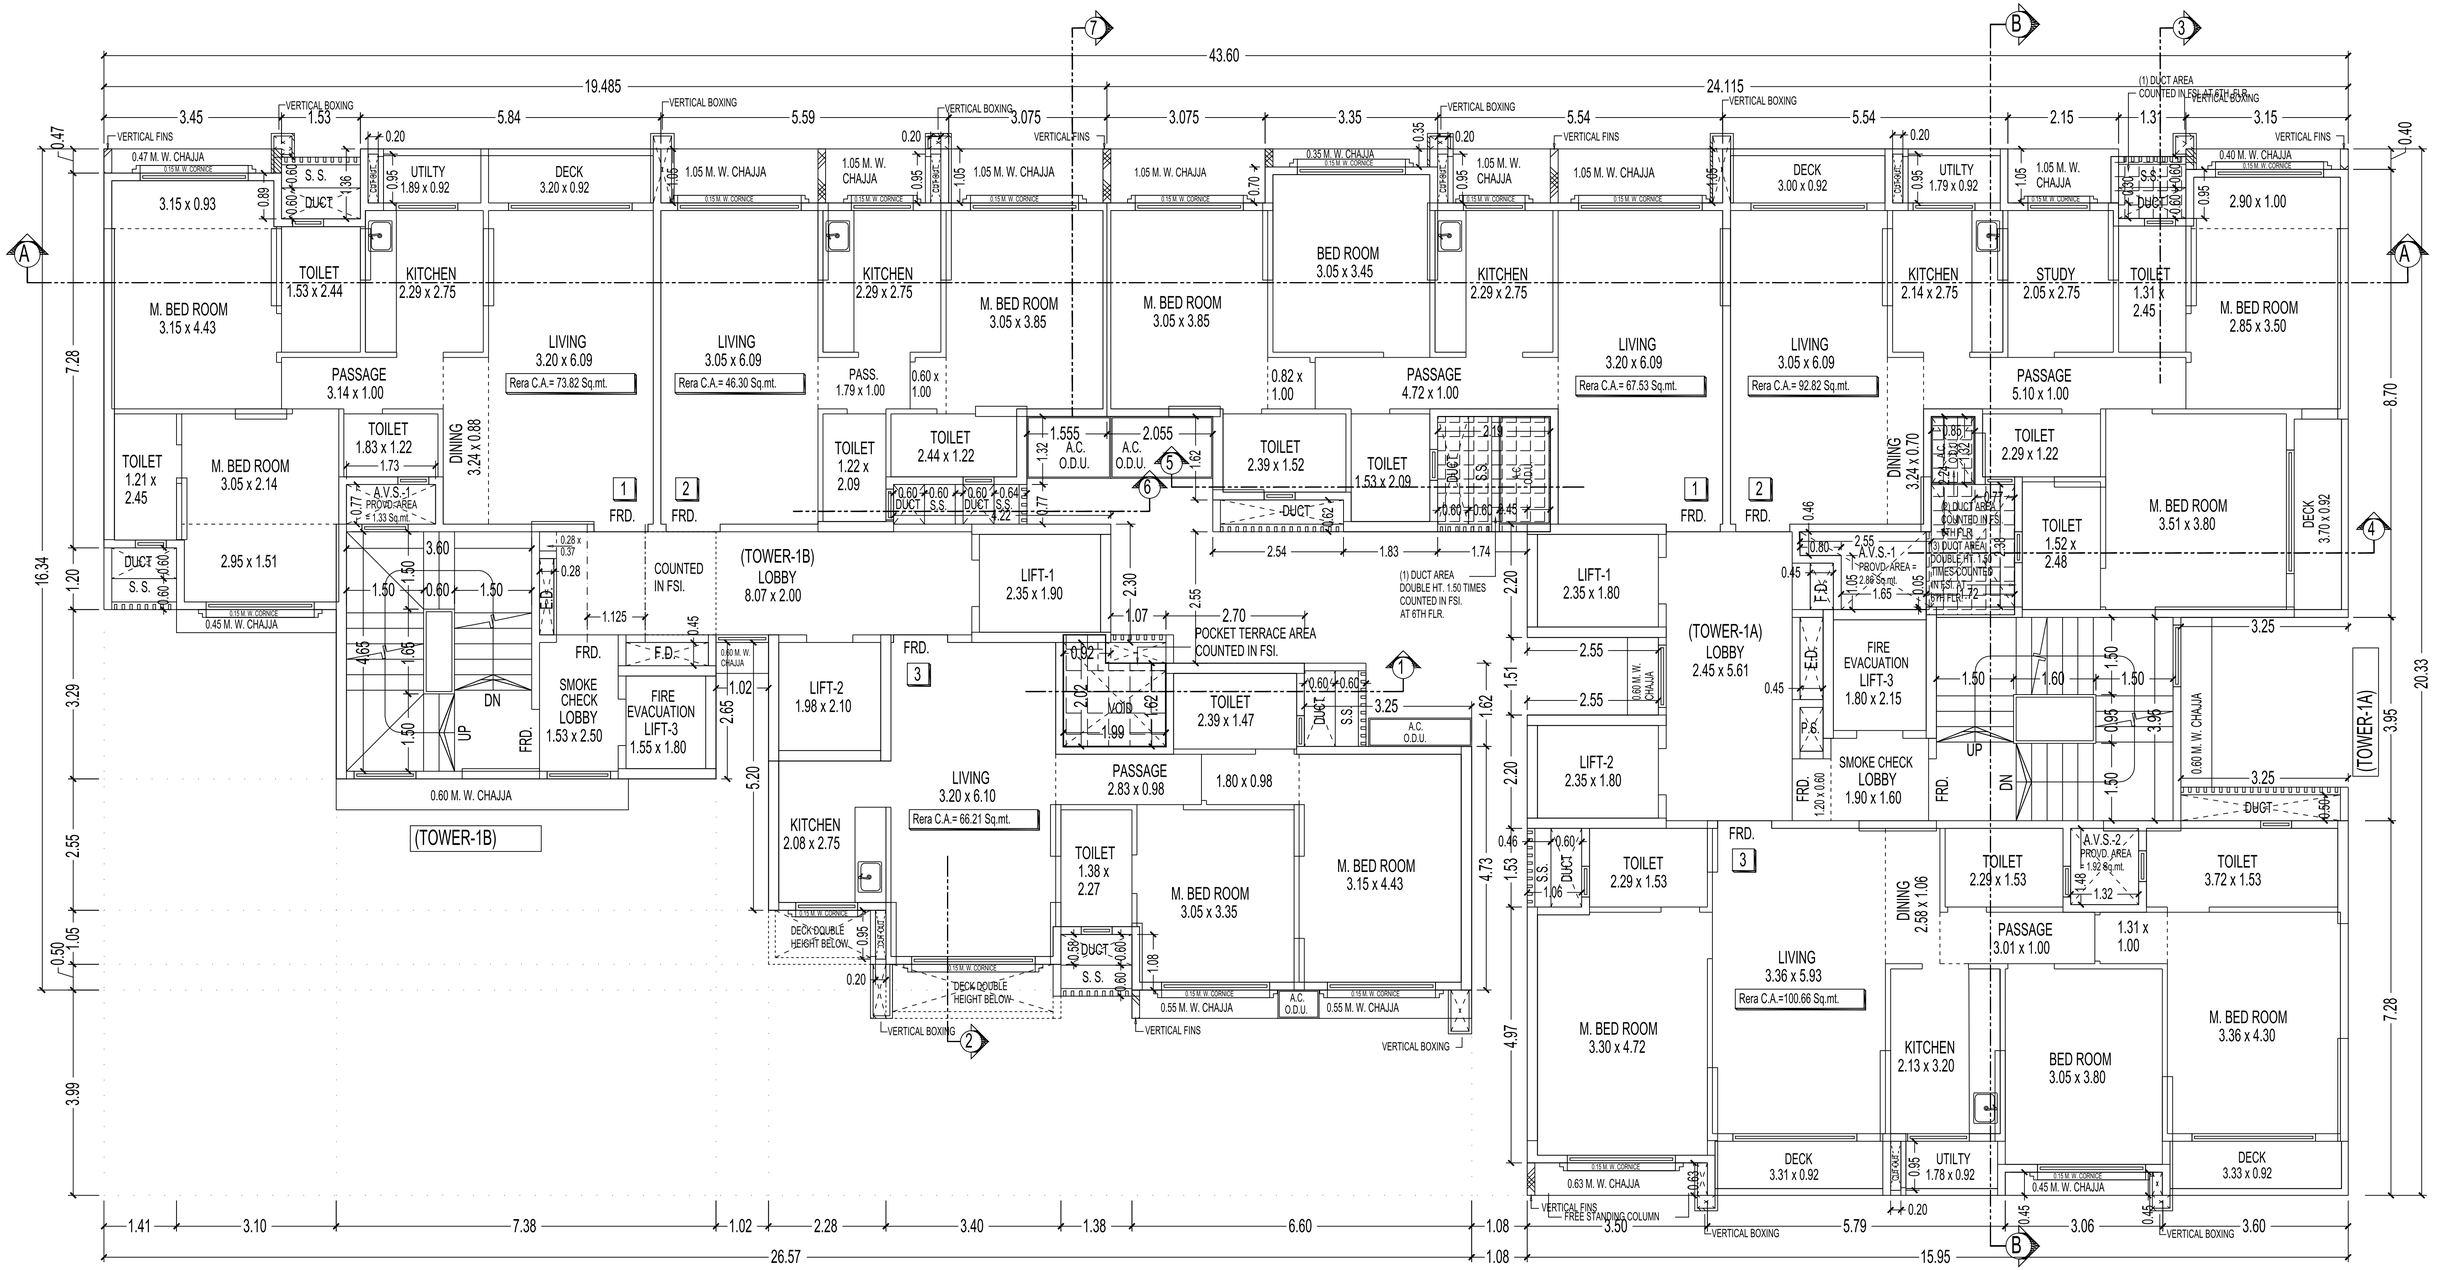

(TOWER-1A & 1B) 6TH FLOOR PLAN

FOR 7TH REFUGE FLOOR

SCALE - 1:100

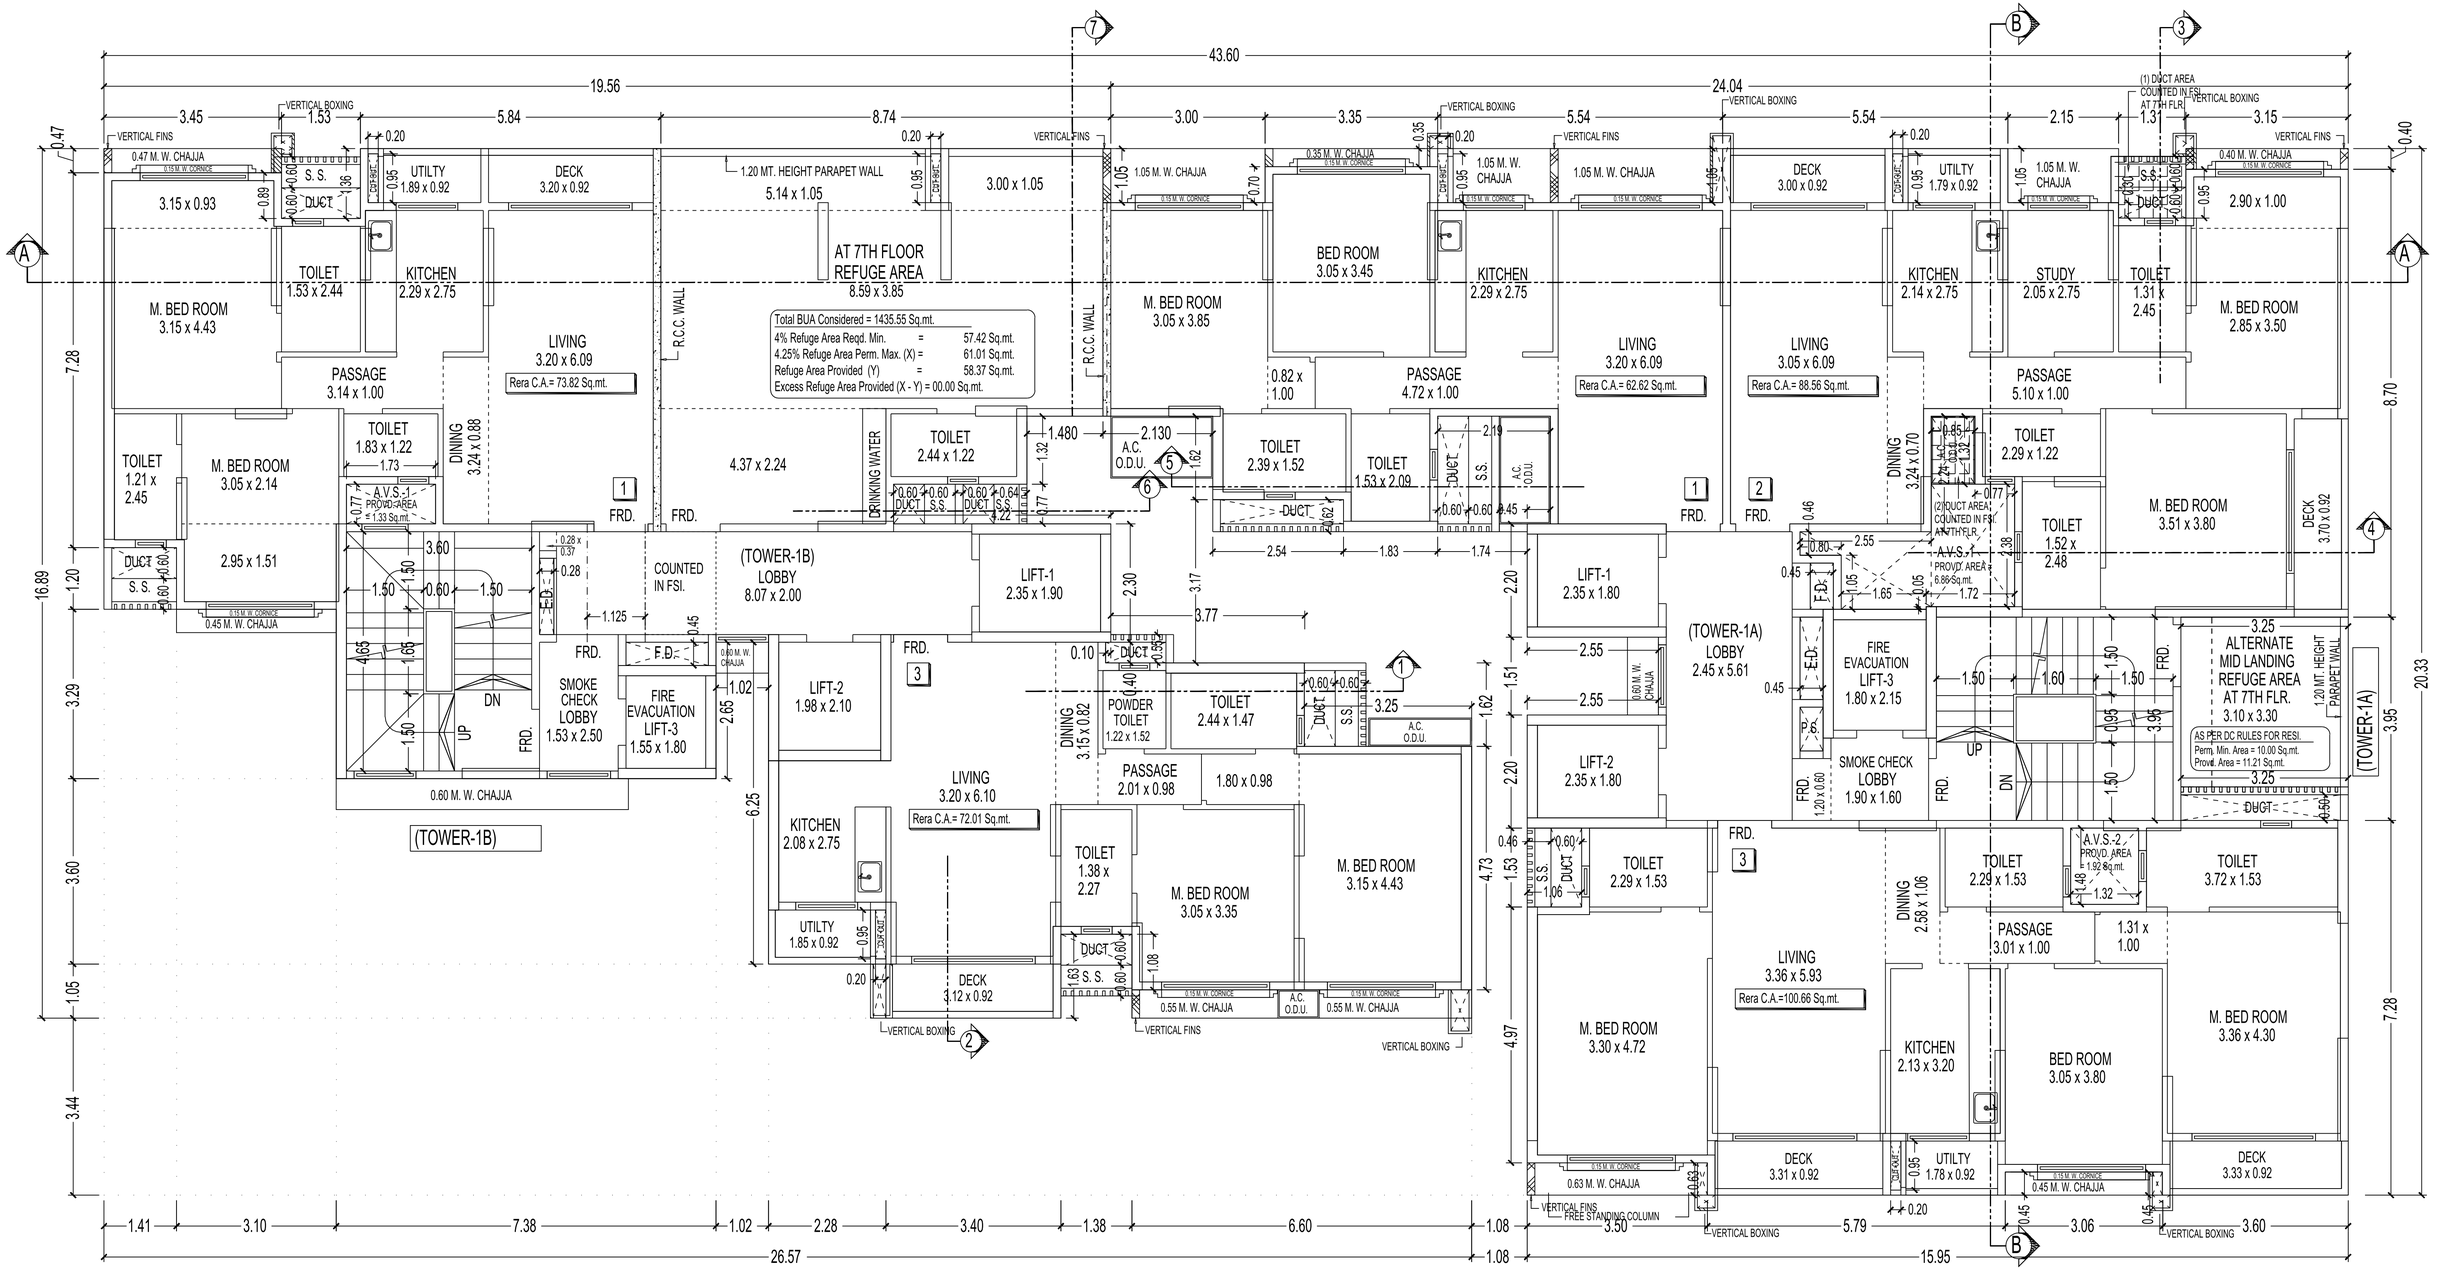


(TOWER-1A & 1B) 7TH REFUGE FLOOR PLAN


SCALE - 1:100

FOR 8TH, 9TH FLOOR

SCALE - 1:100

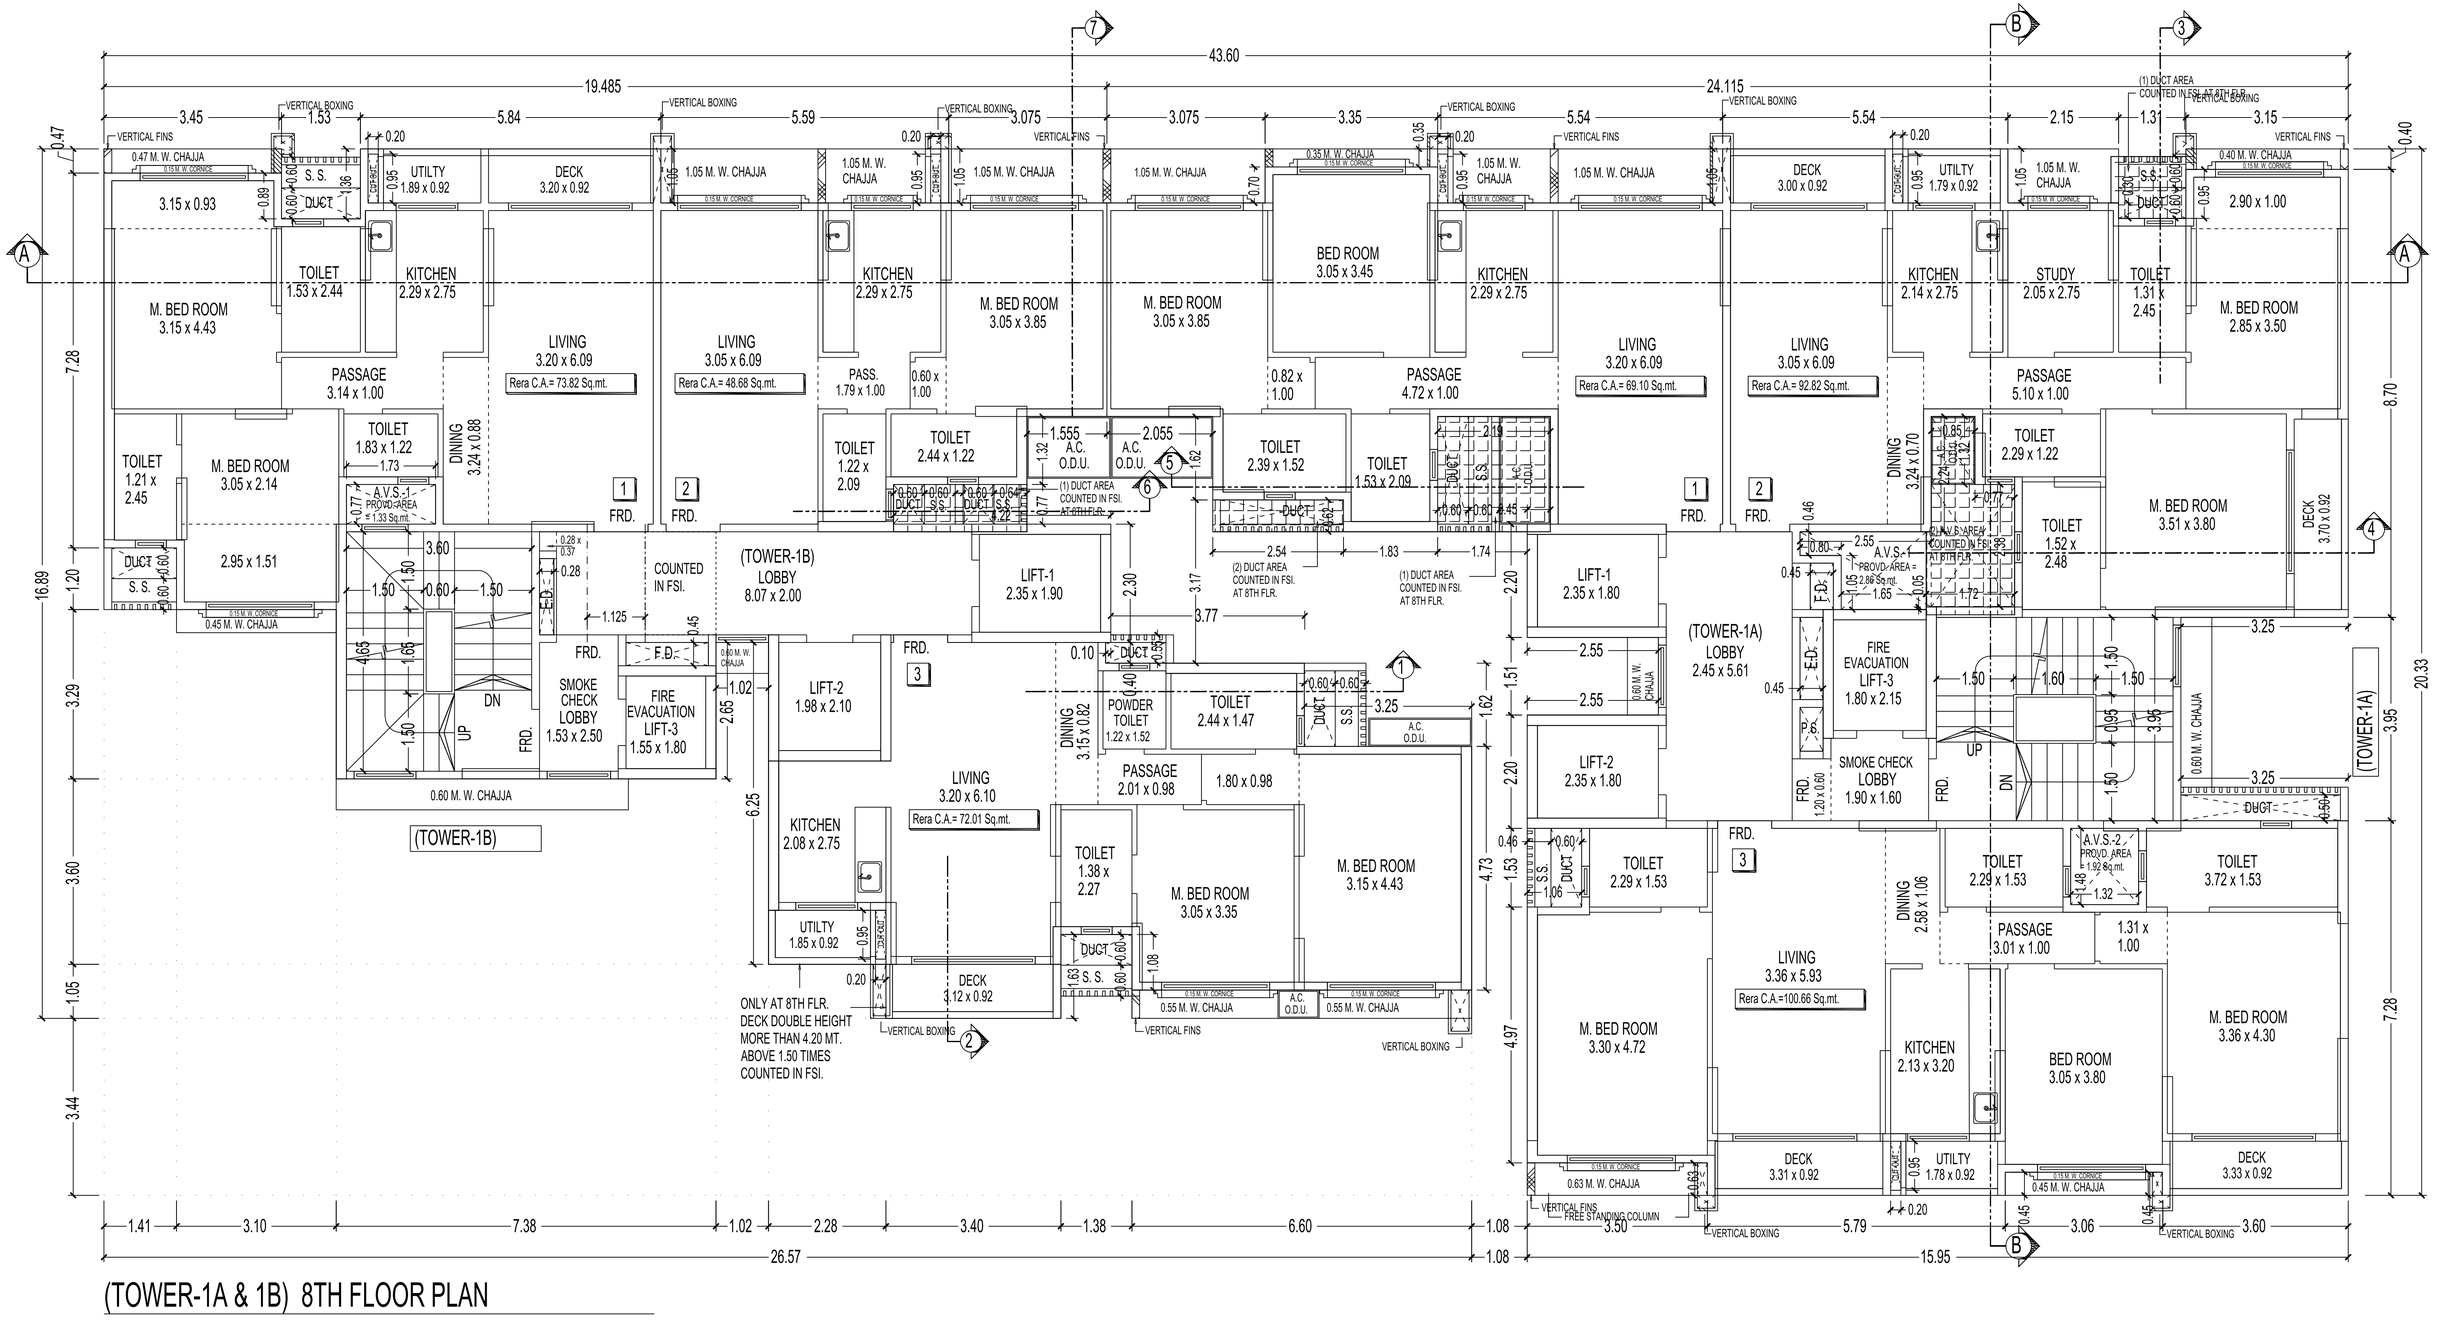

(TOWER-1A & 1B) 8TH FLOOR PLAN

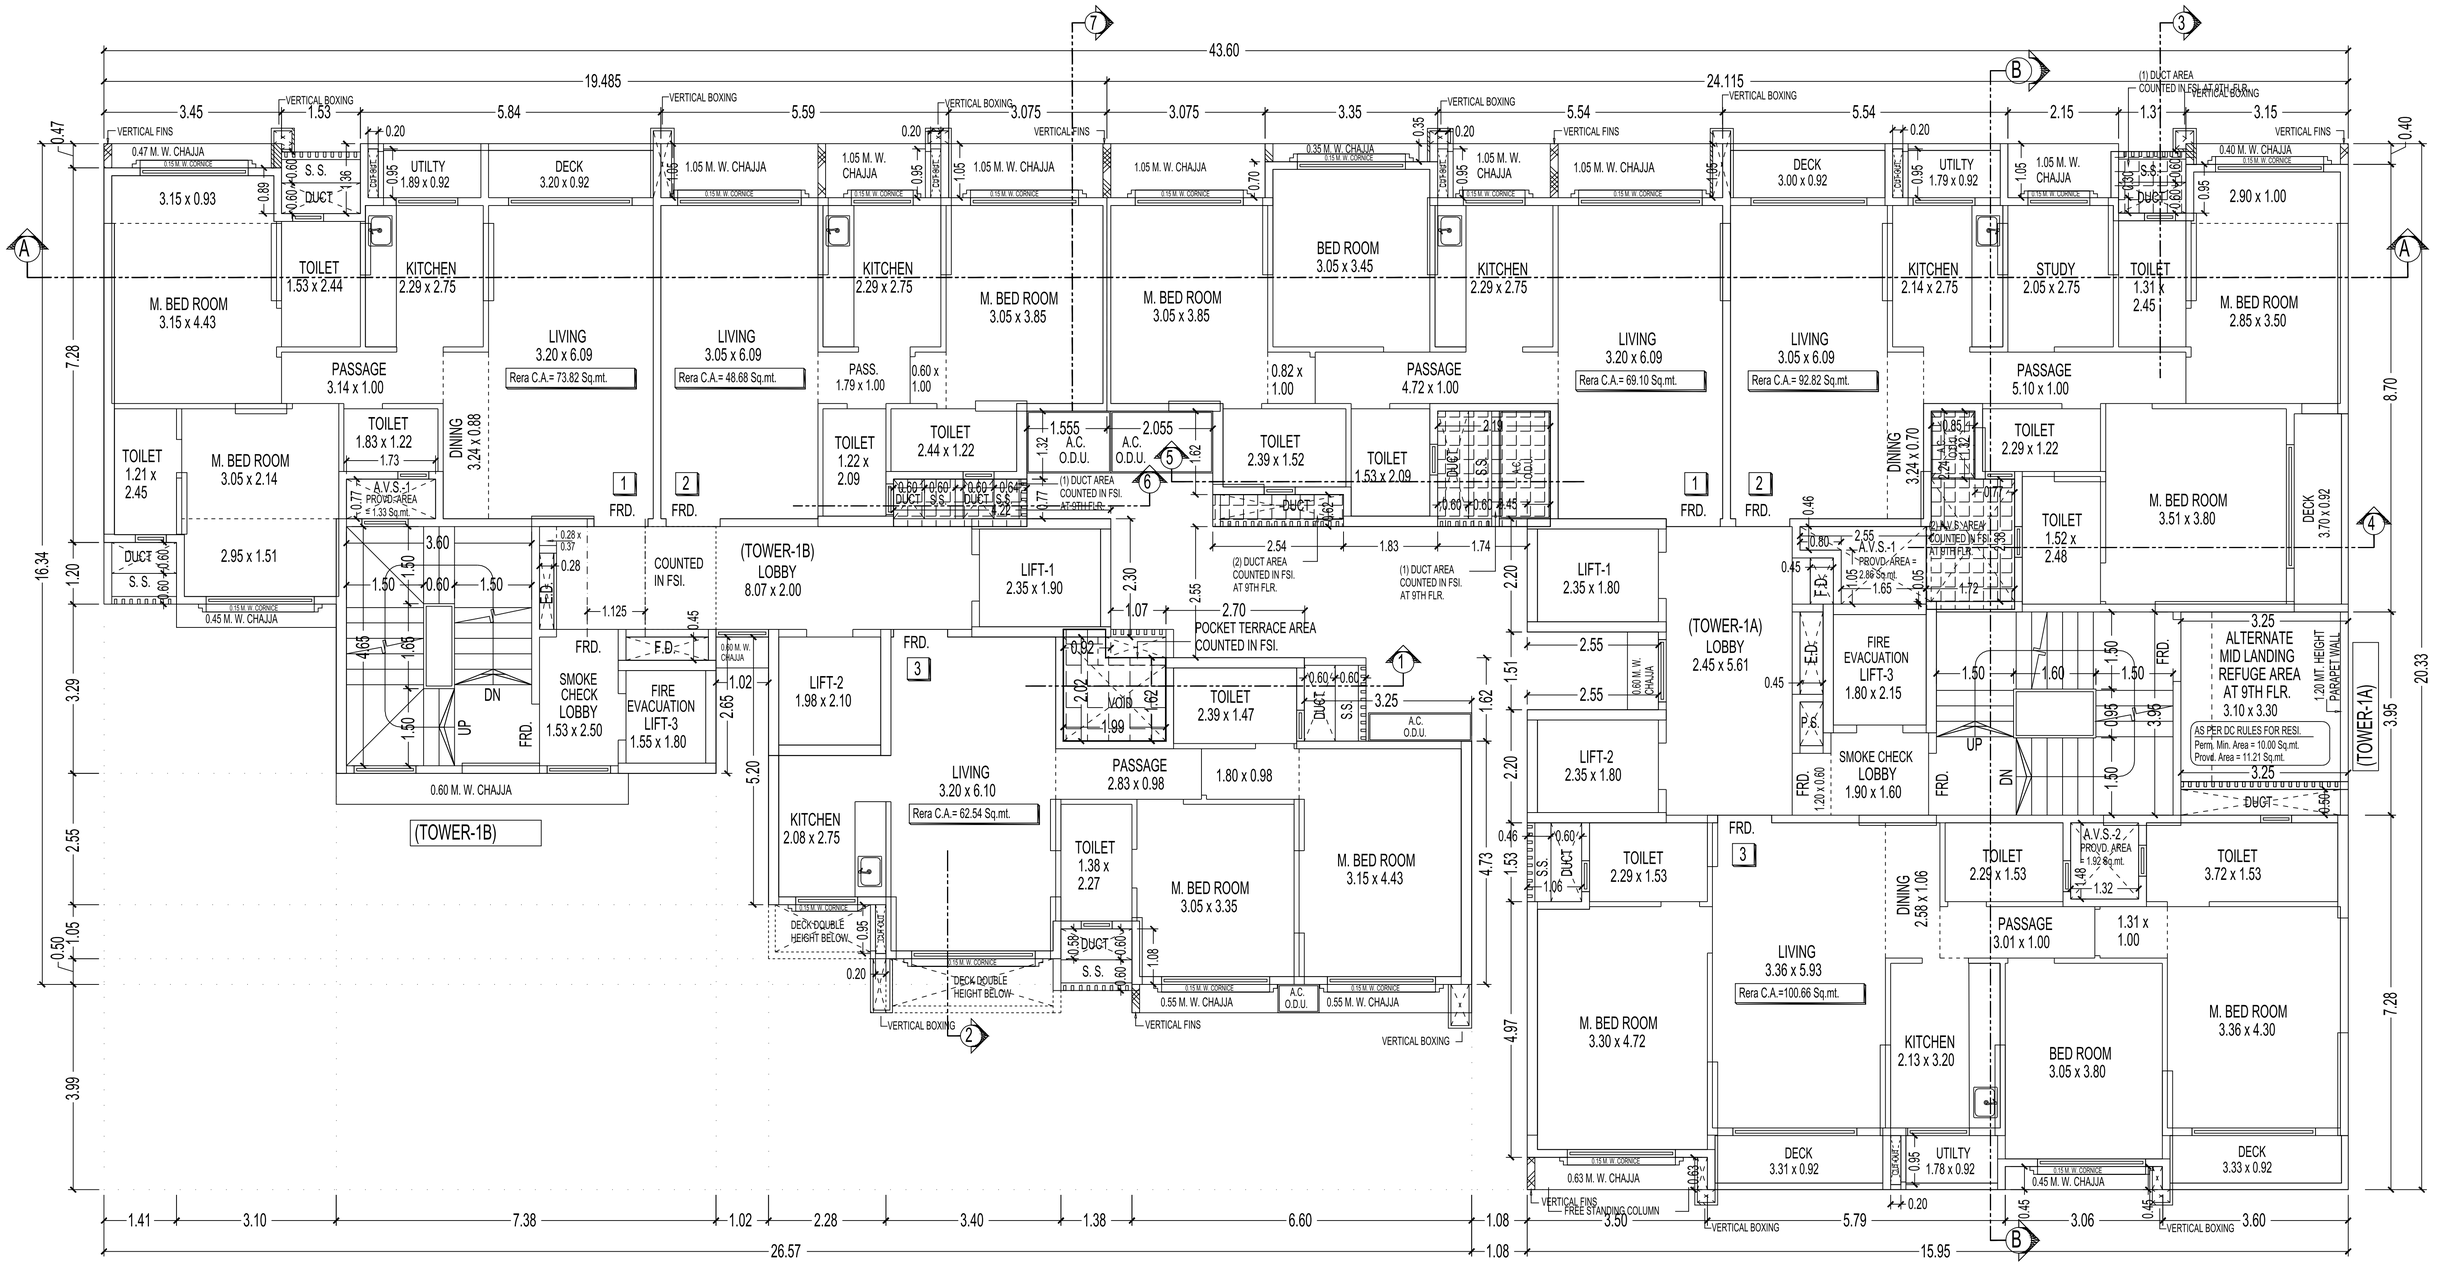


(TOWER-1A & 1B) 9TH FLOOR PLAN

SCALE - 1:100


FOR 10TH FLOOR

SCALE - 1:100

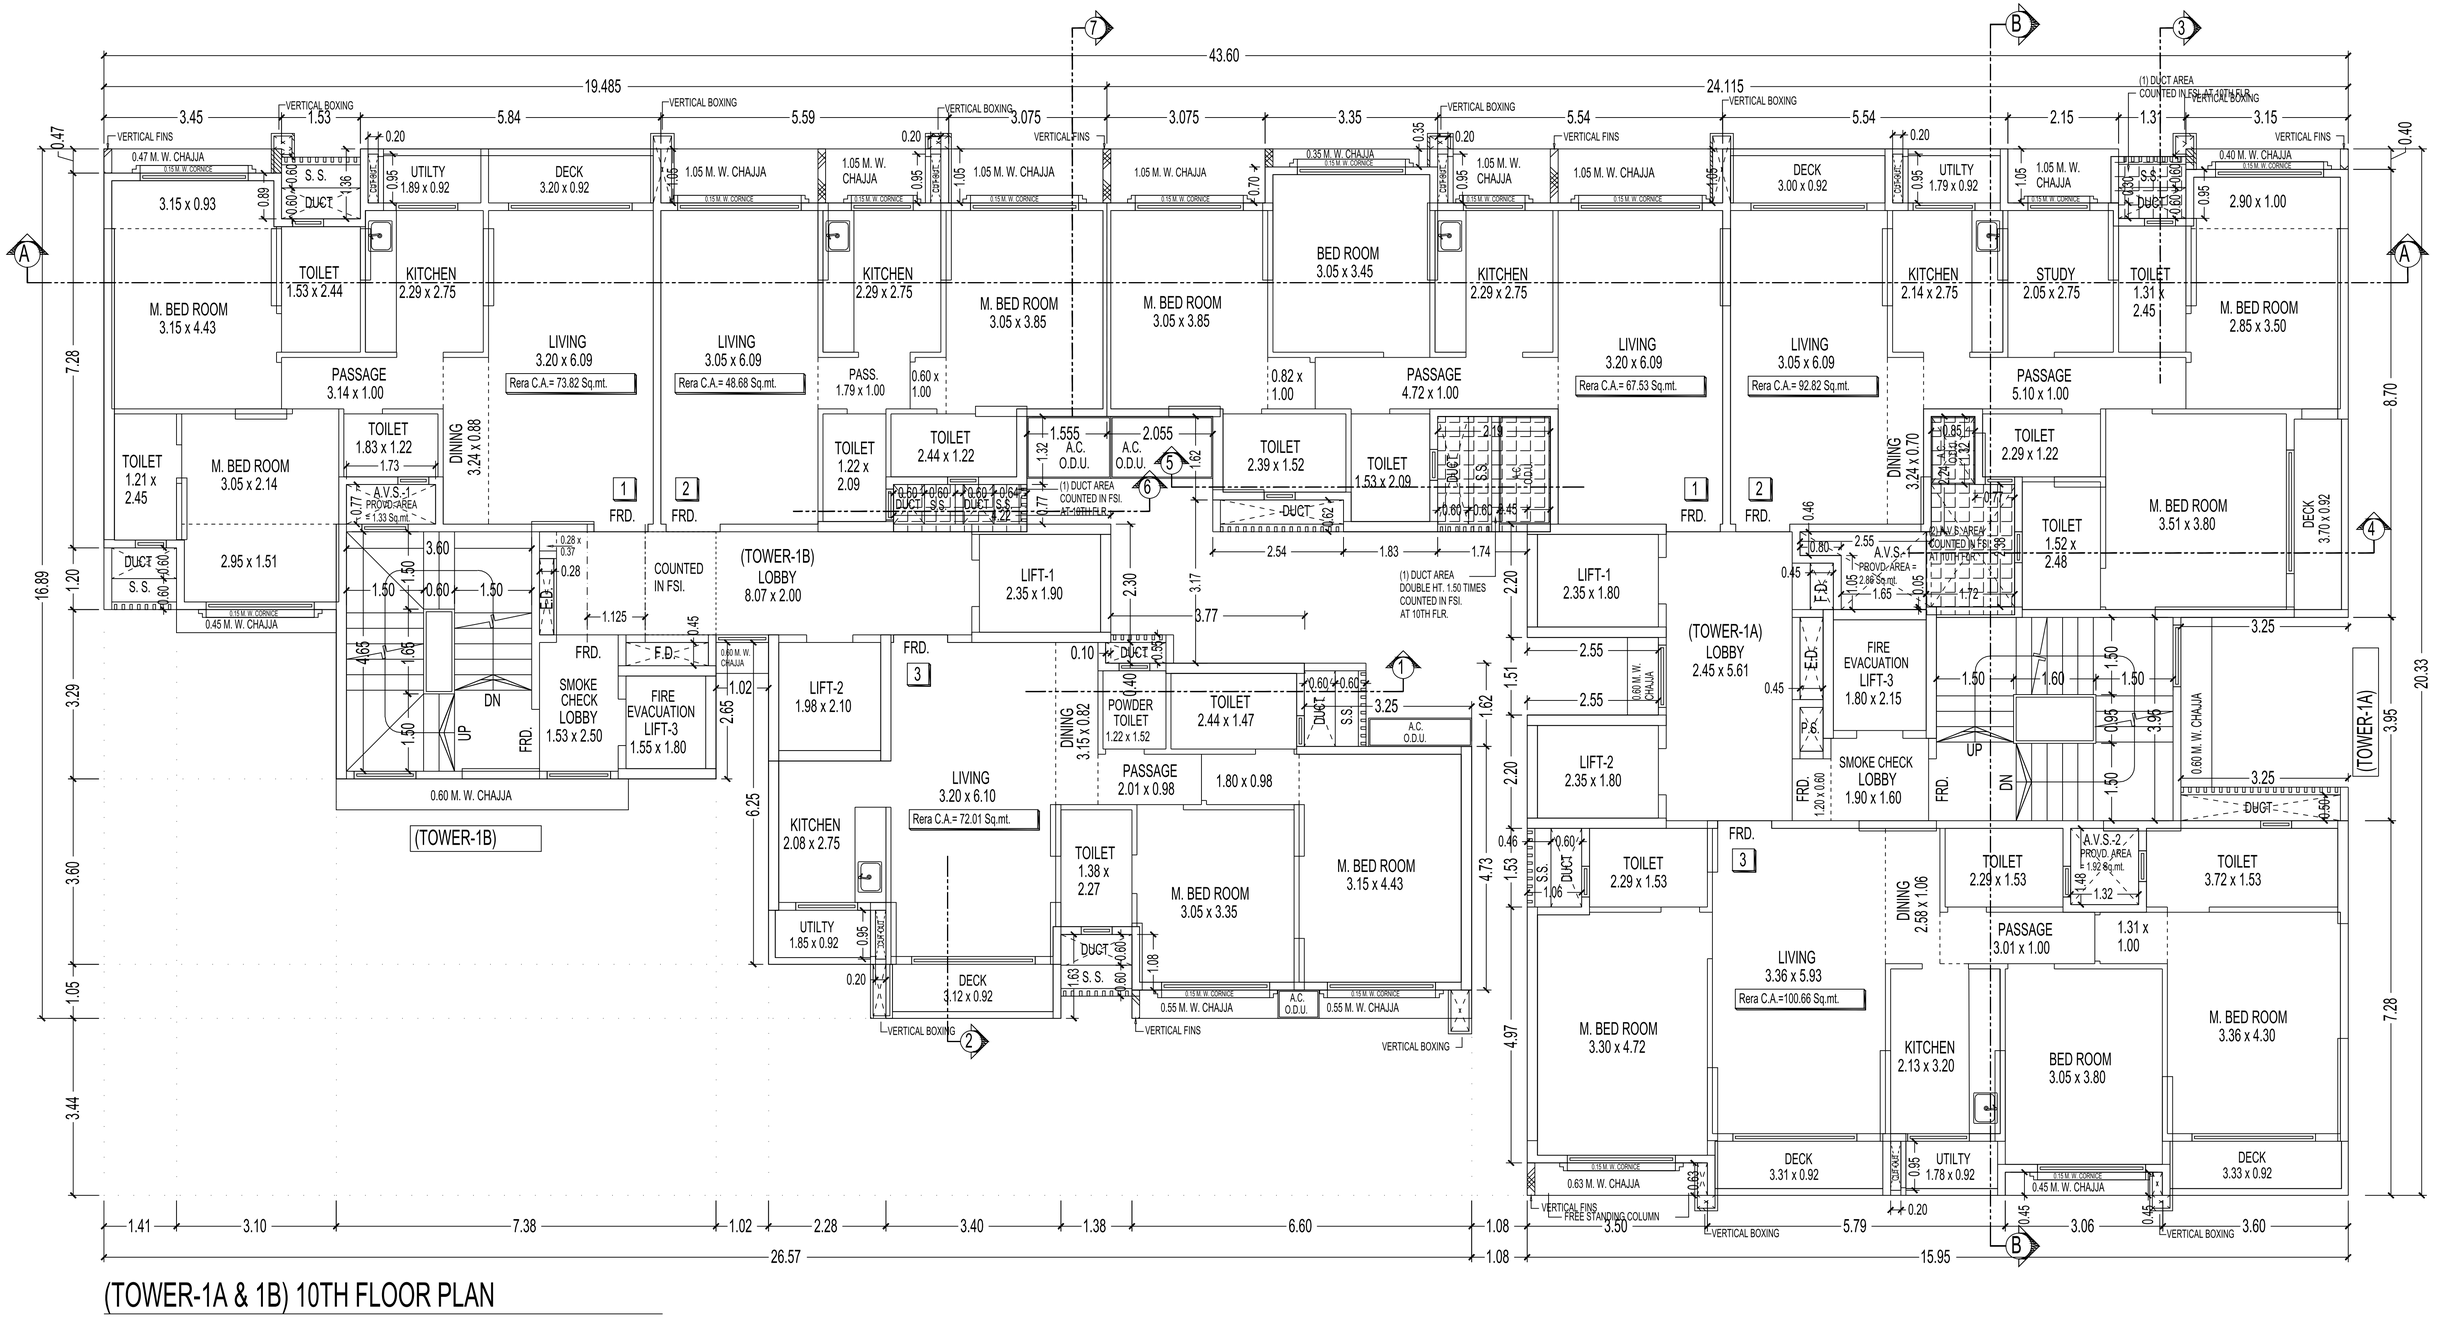

(TOWER-1A & 1B) 10TH FLOOR PLAN


FOR 11TH FLOOR
SCALE - 1:100

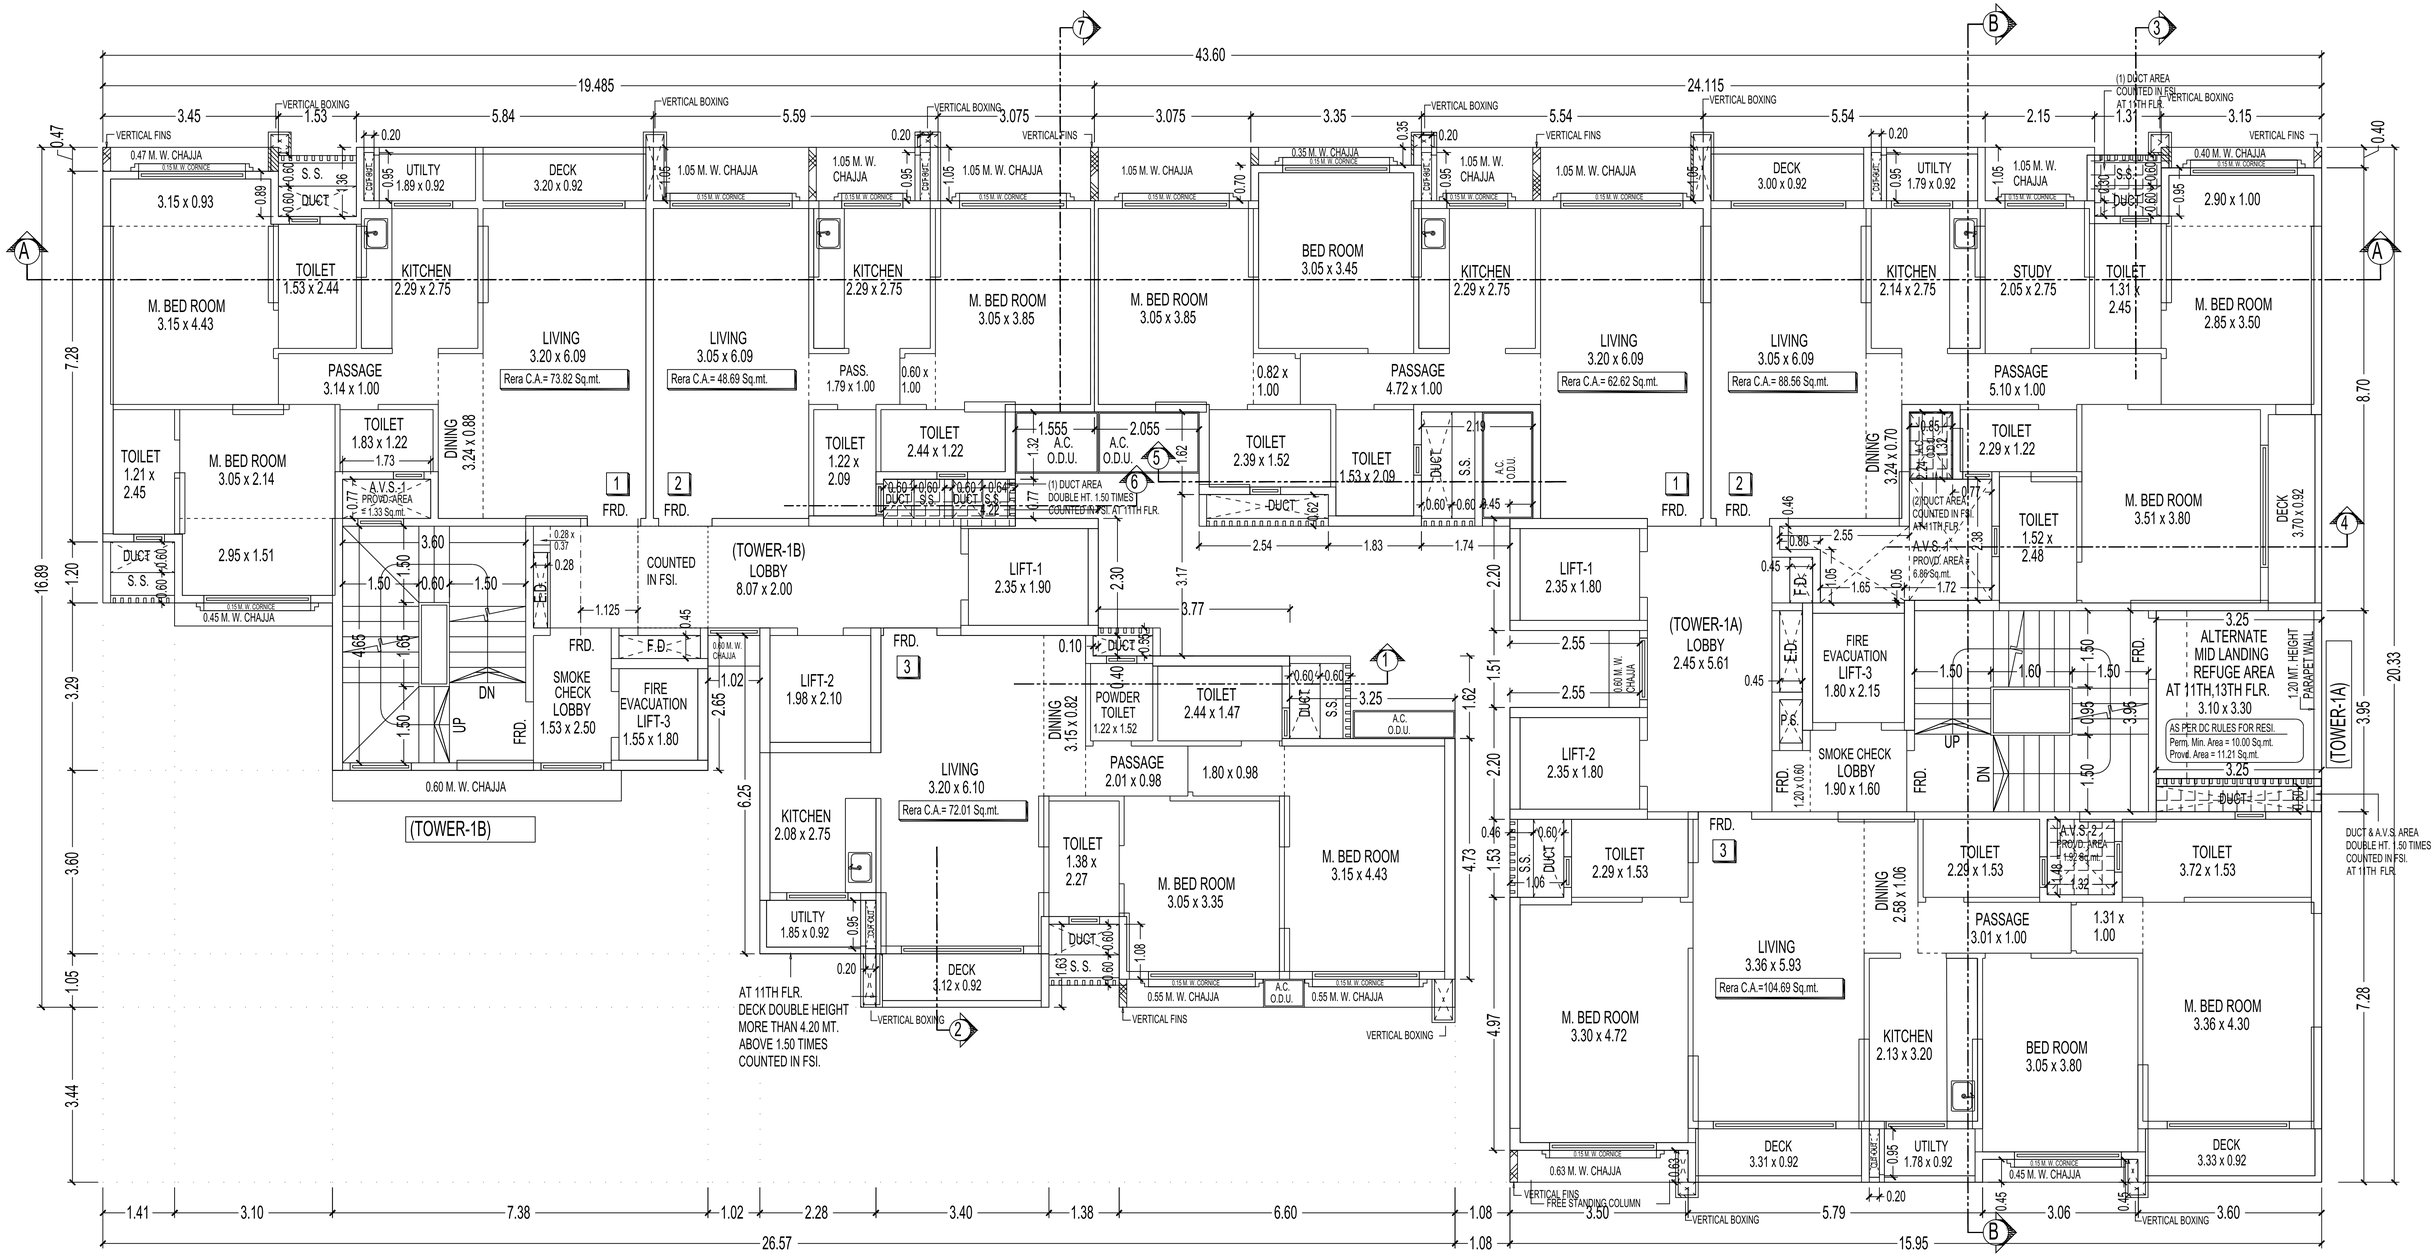

(TOWER-1A & 1B) 11TH FLOOR PLAN
SCALE - 1:100

FOR 12TH FLOOR


SCALE - 1:100

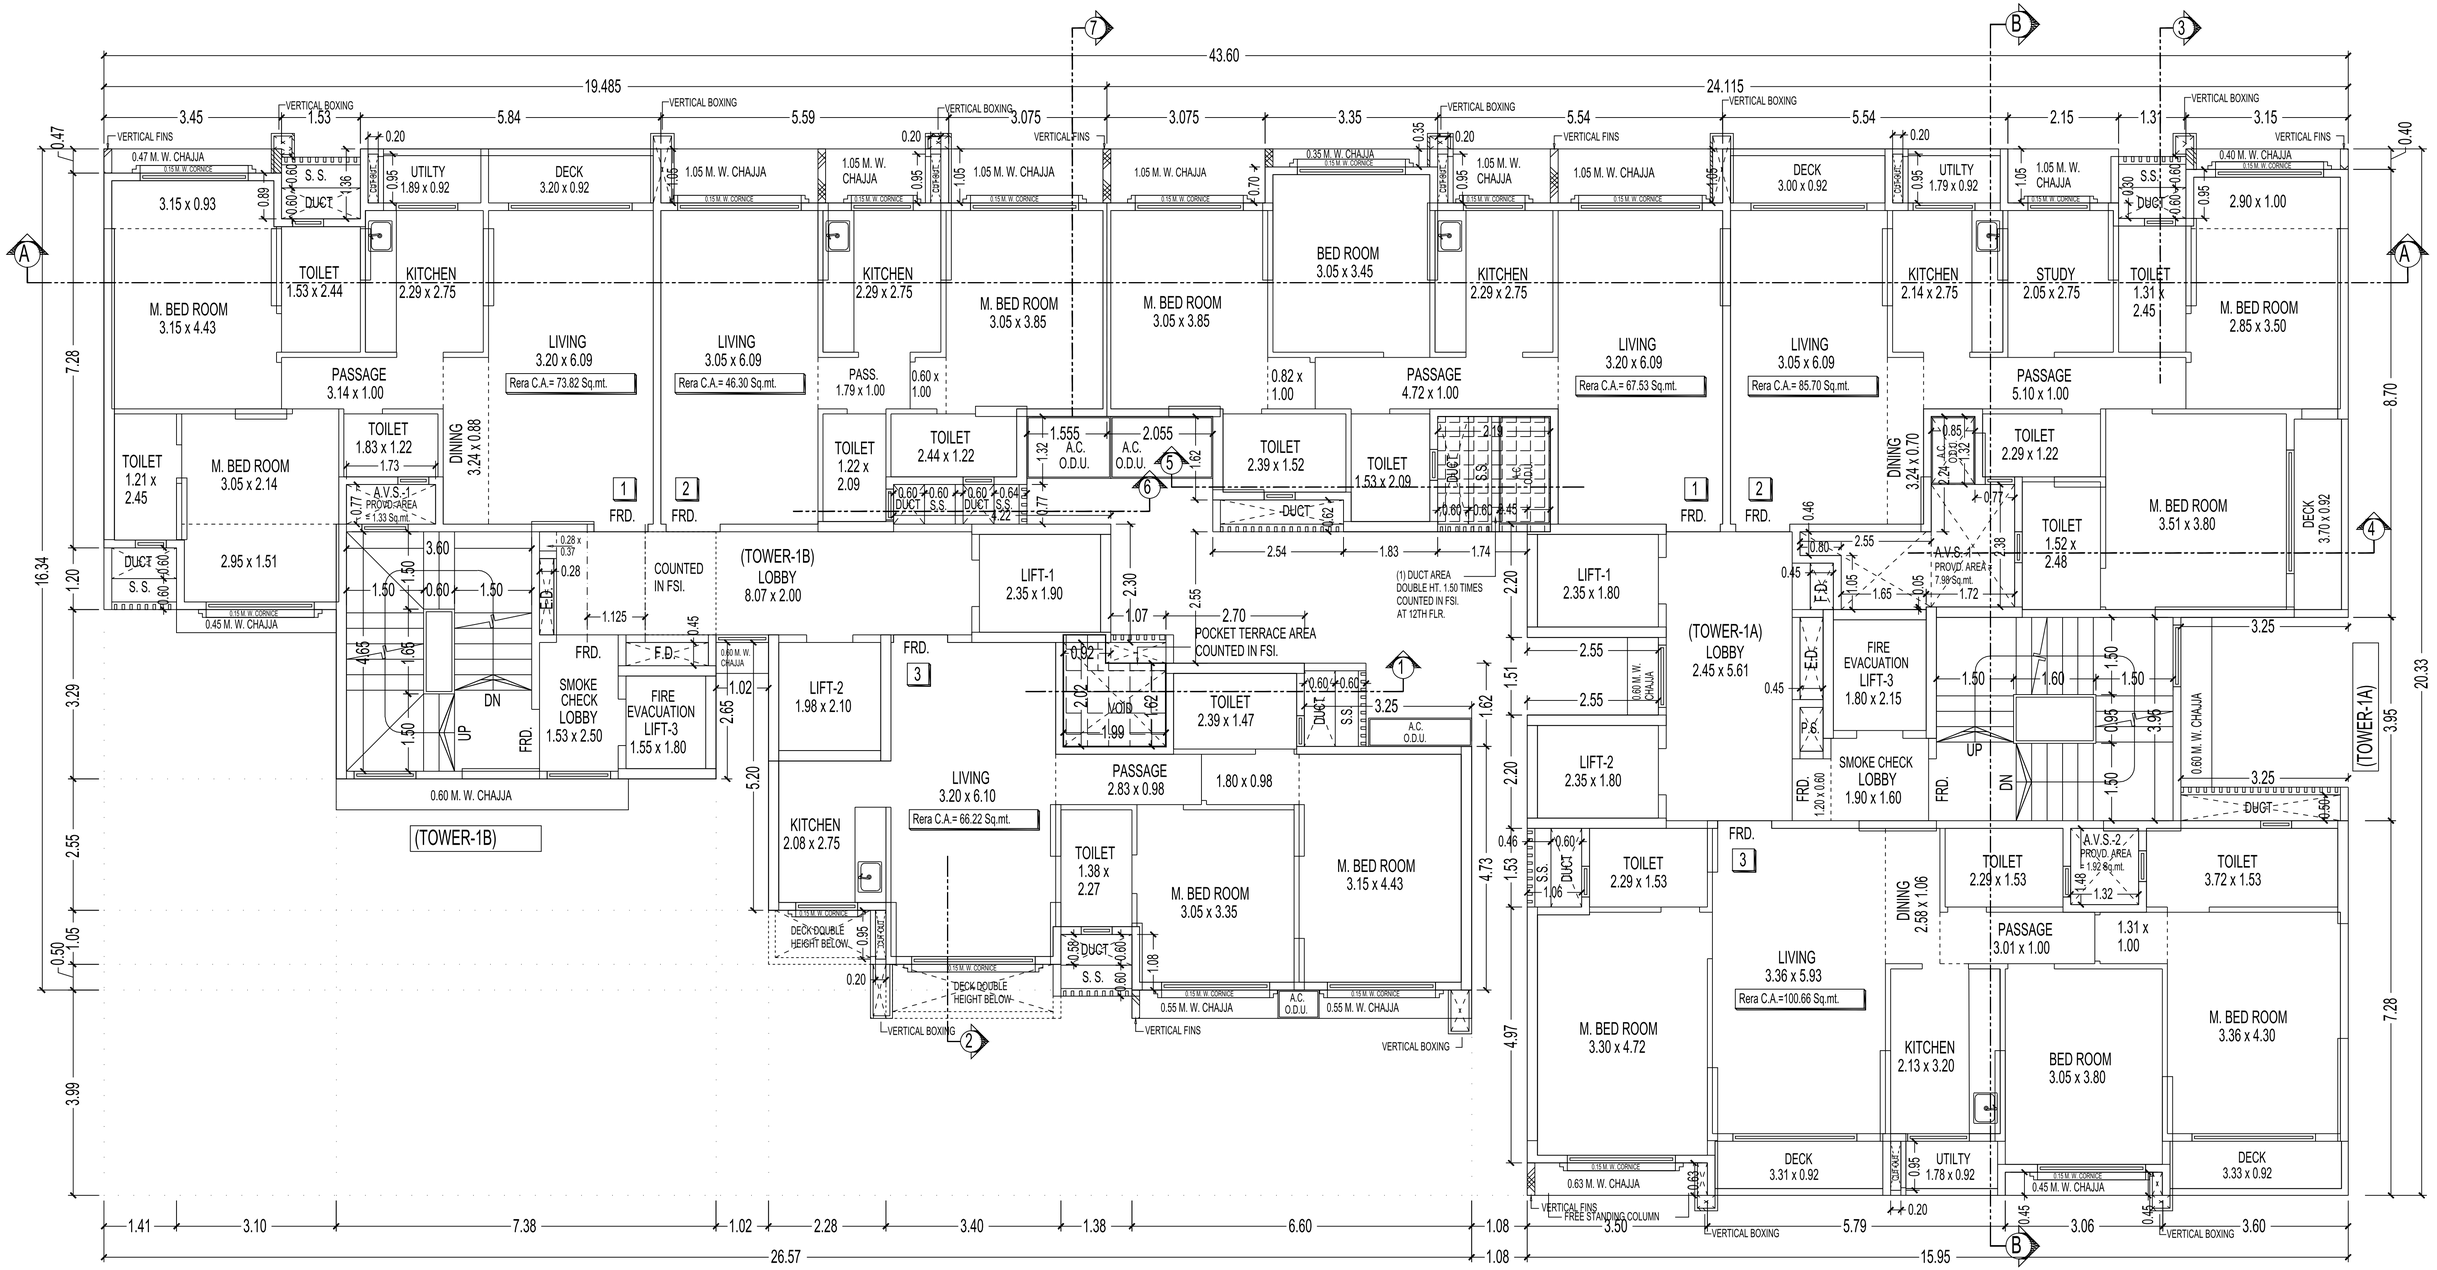

(TOWER-1A & 1B) 12TH FLOOR PLAN

FOR 13TH FLOOR

SCALE - 1:100

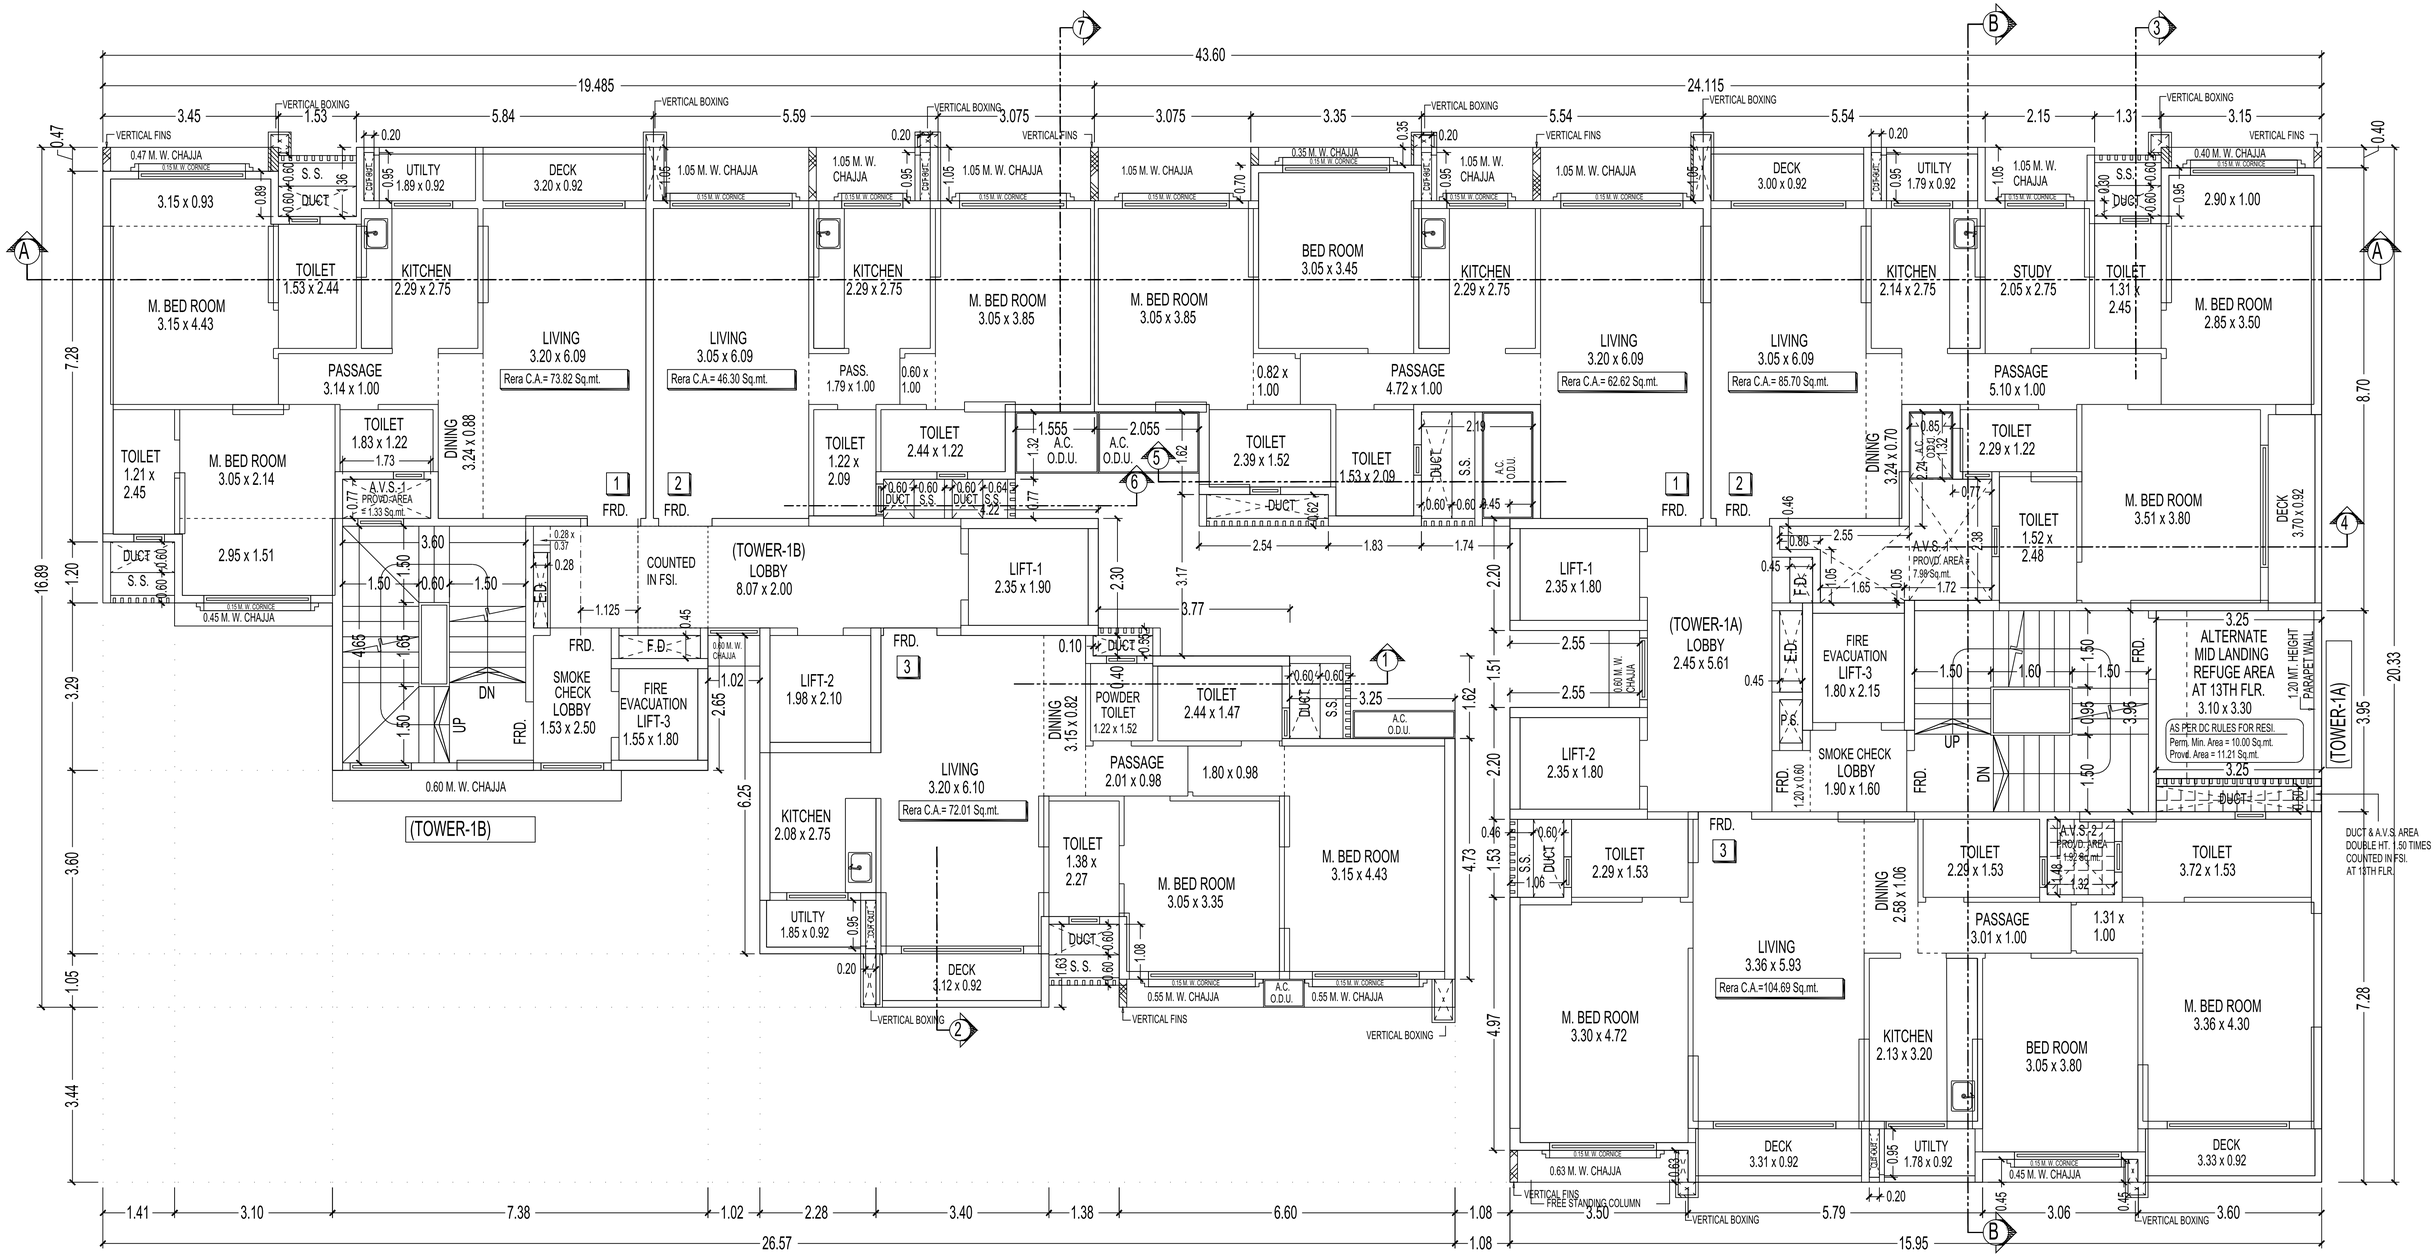


(TOWER-1A & 1B) 13TH FLOOR PLAN

SCALE - 1:100

FOR 14TH REFUGE FLOOR
SCALE - 1:100


FOR 14TH REFUGE FLOOR
SCALE - 1:100

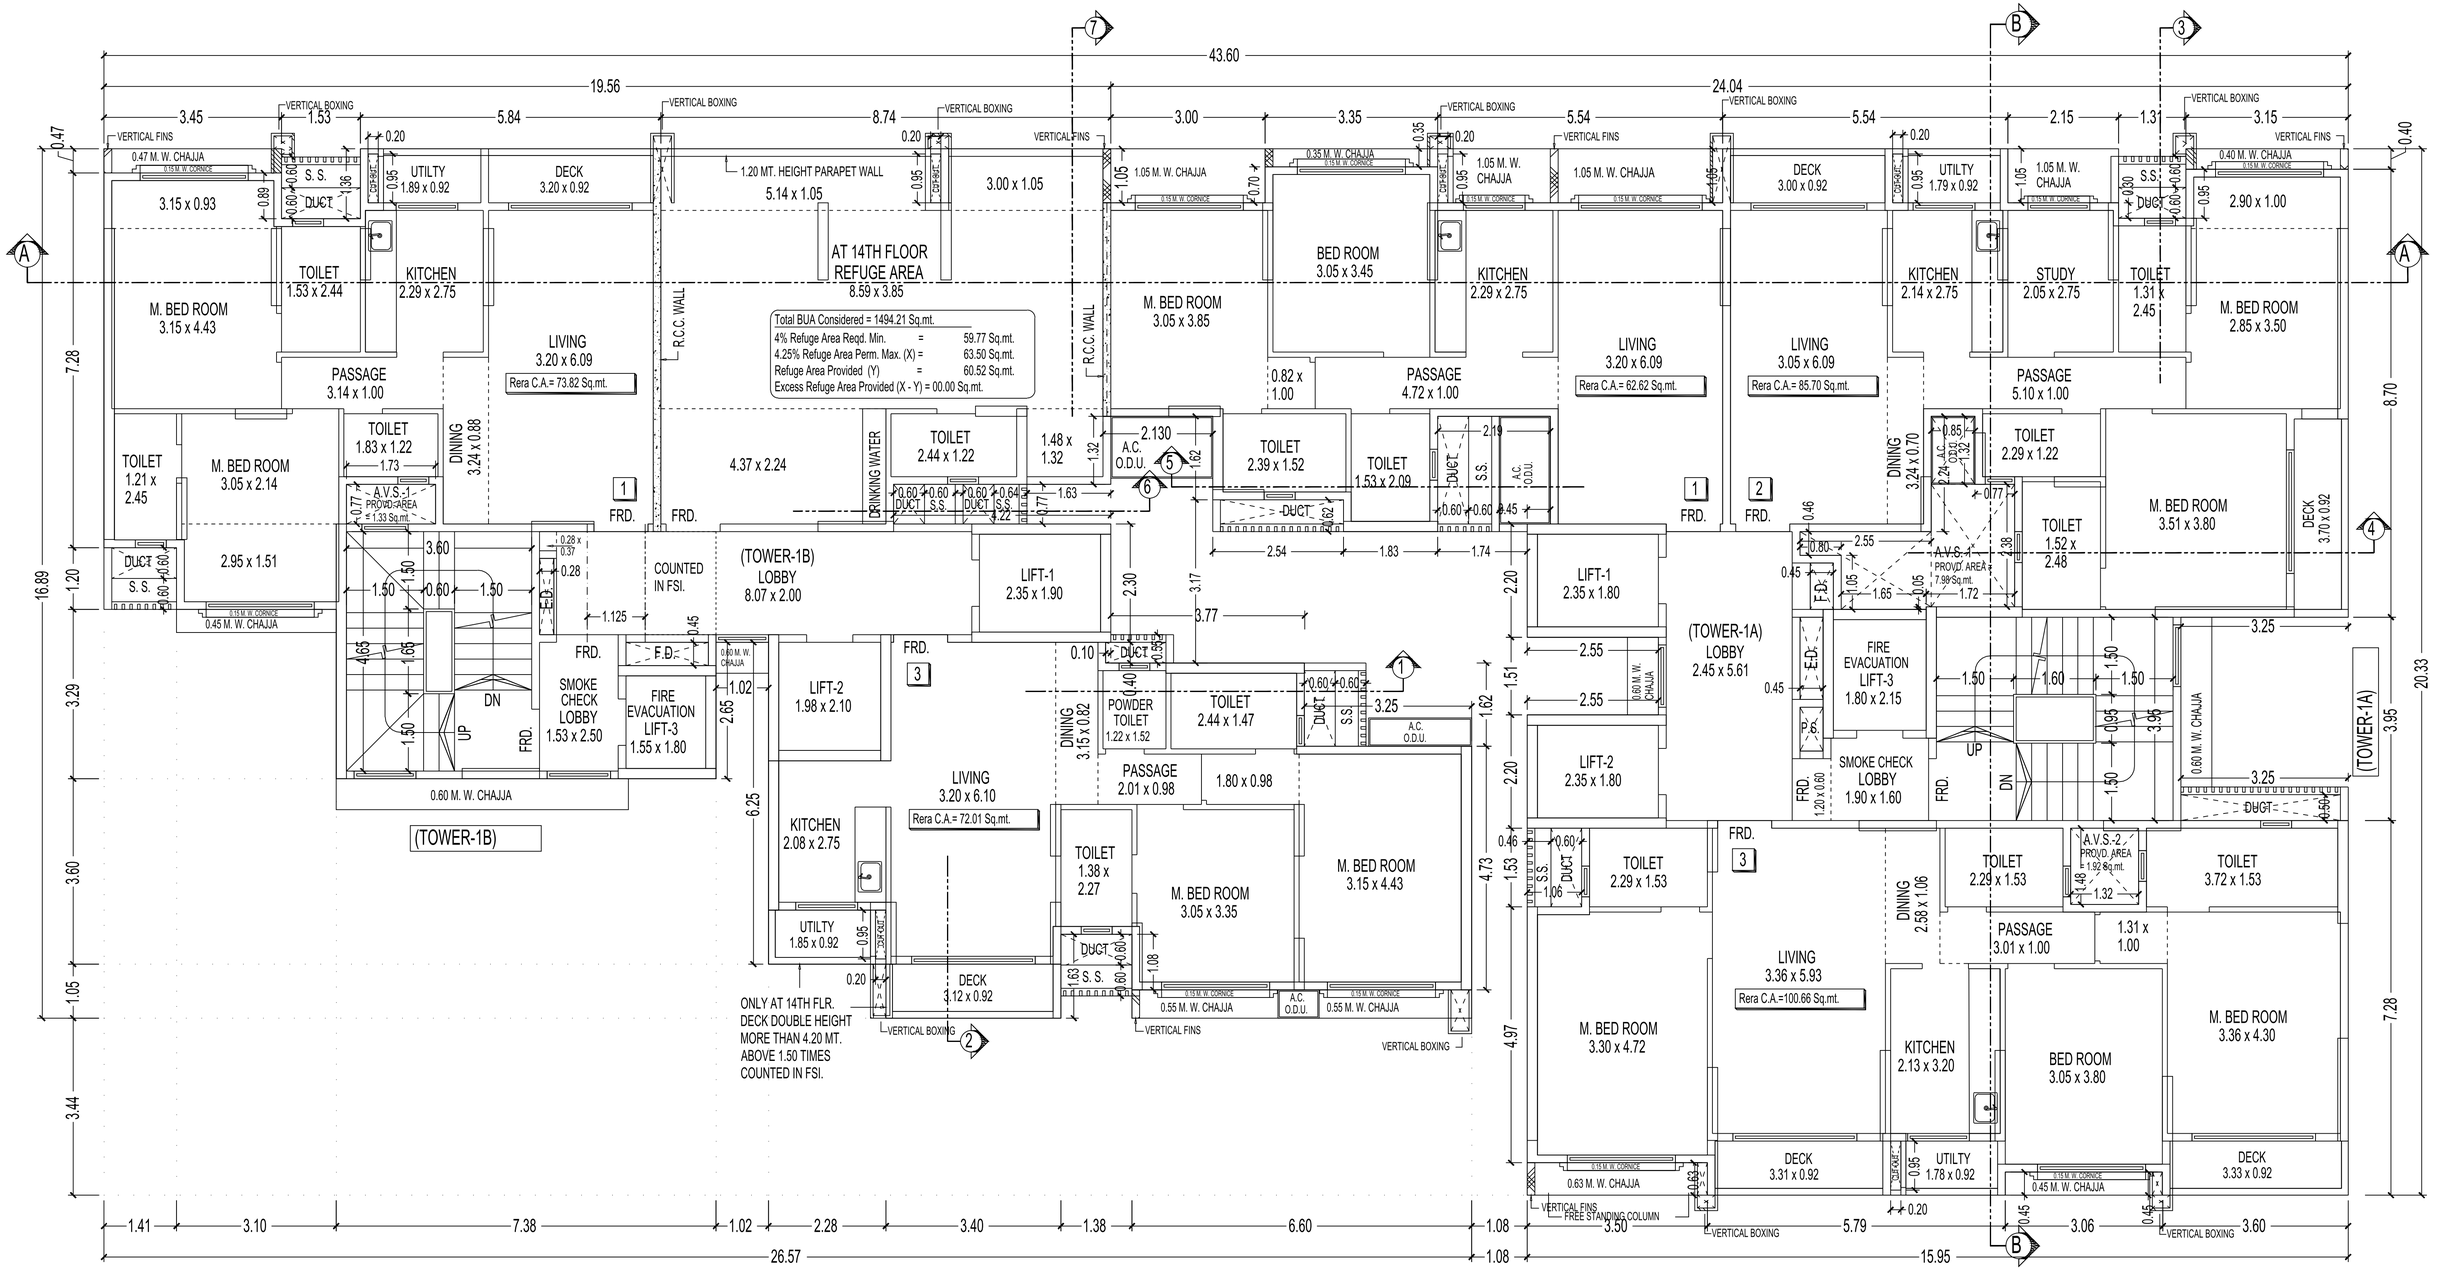

(TOWER-1A & 1B) 14TH REFUGE FLOOR PLAN
SCALE - 1:100


FOR 15TH FLOOR

SCALE - 1:100

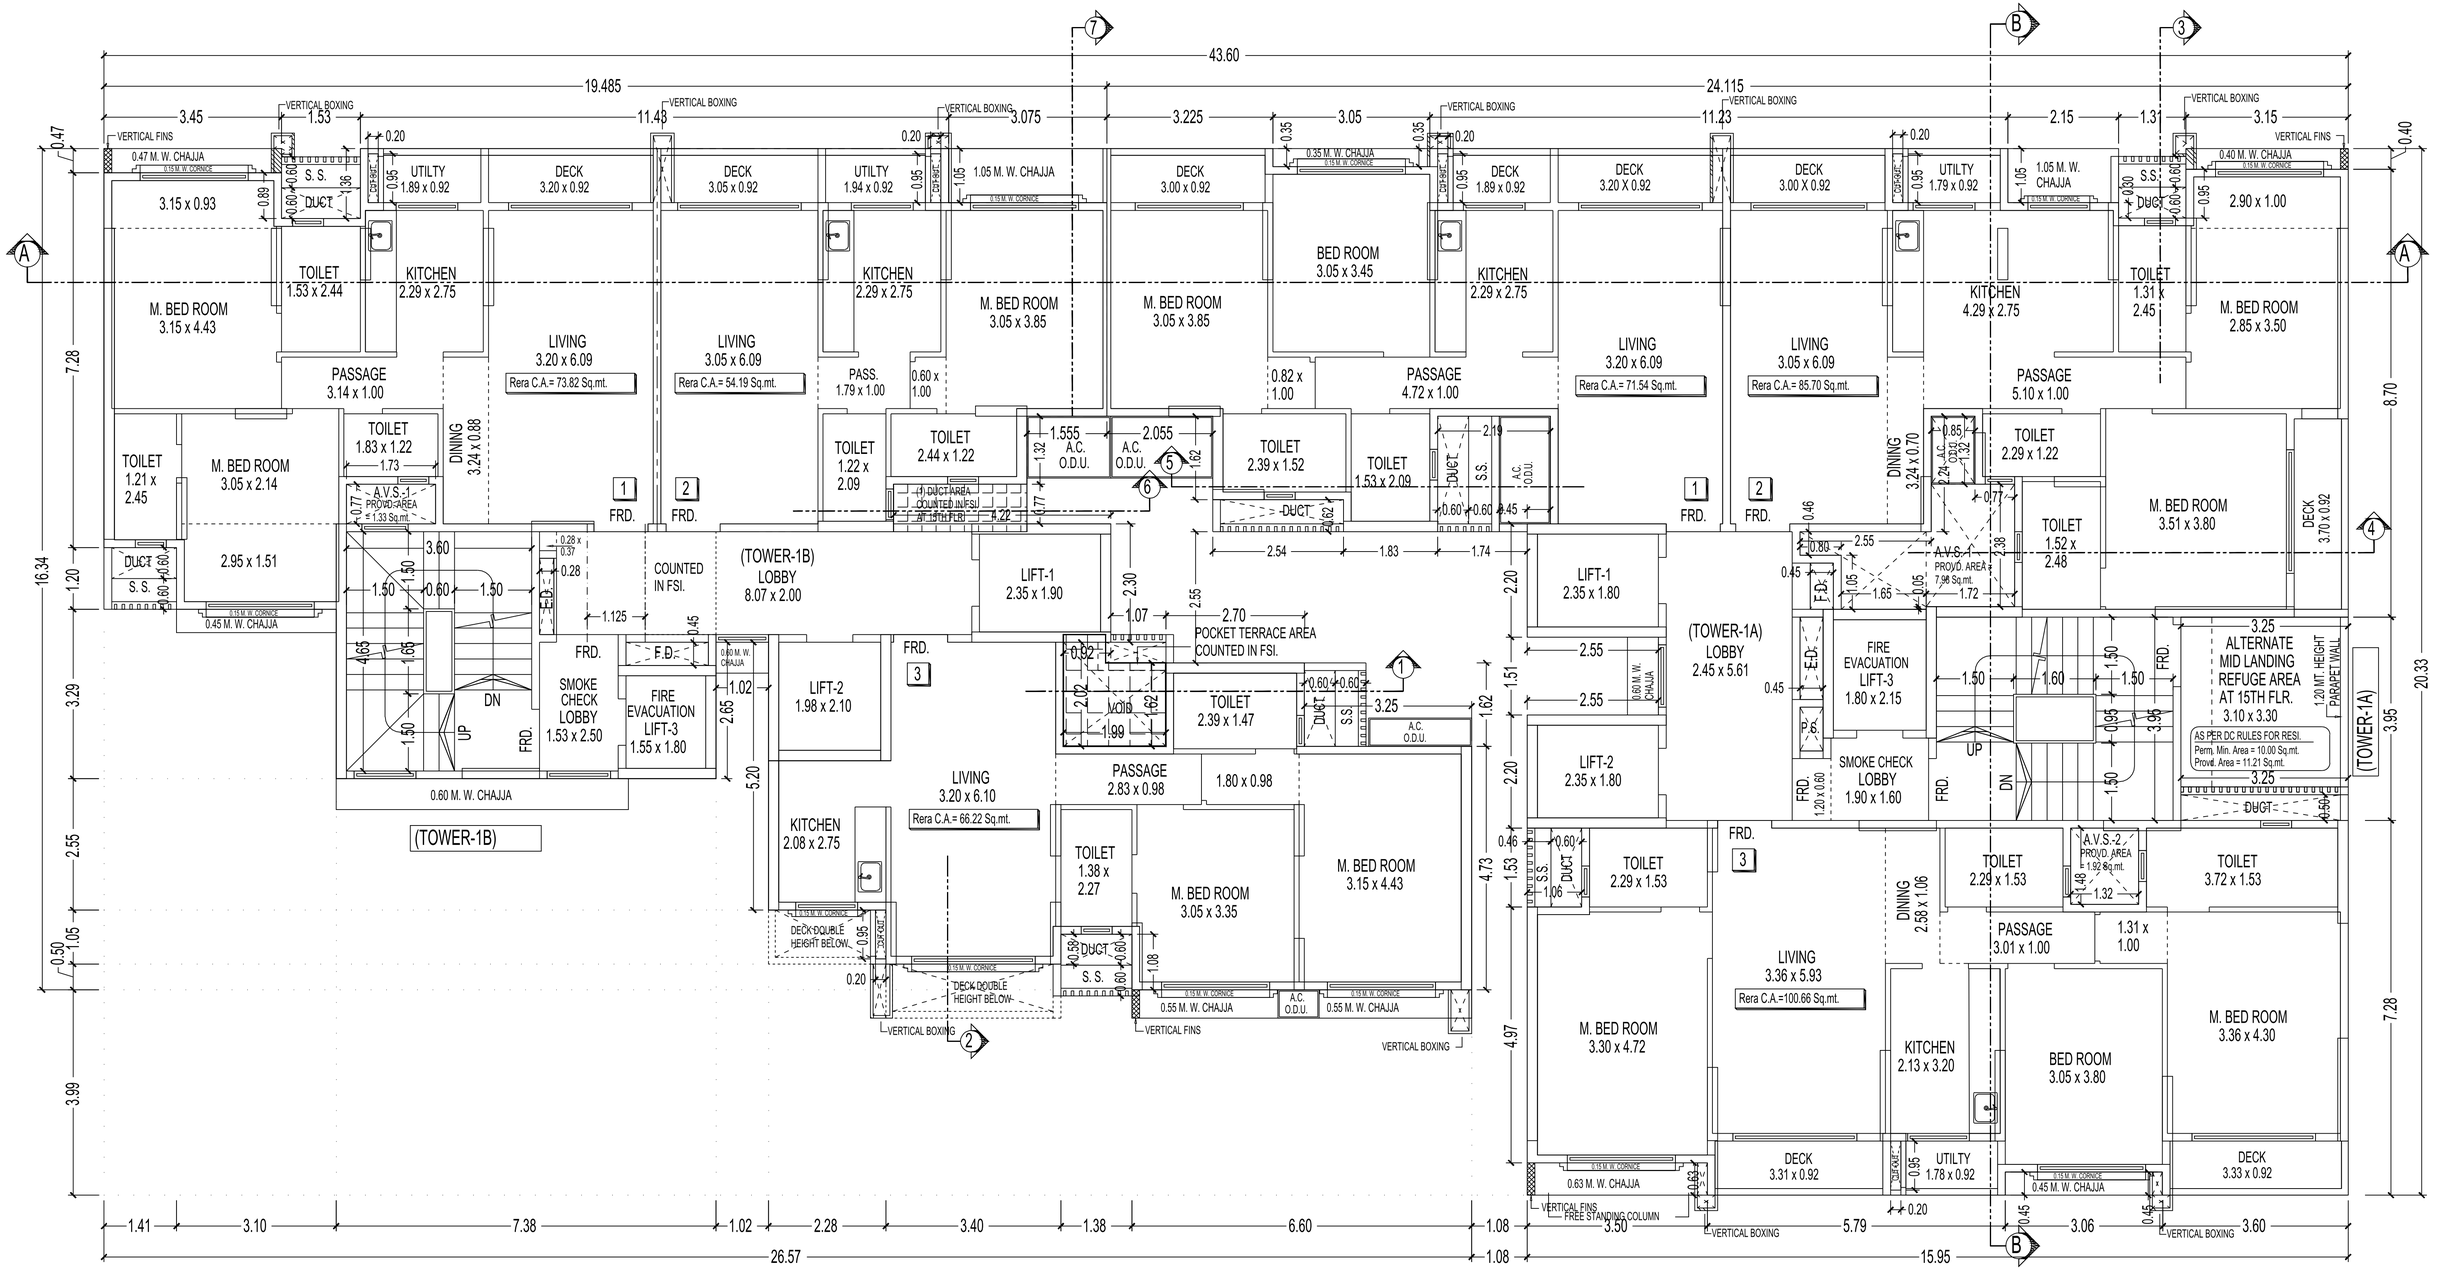

(TOWER-1A & 1B) 15TH FLOOR PLAN

SCALE - 1:100

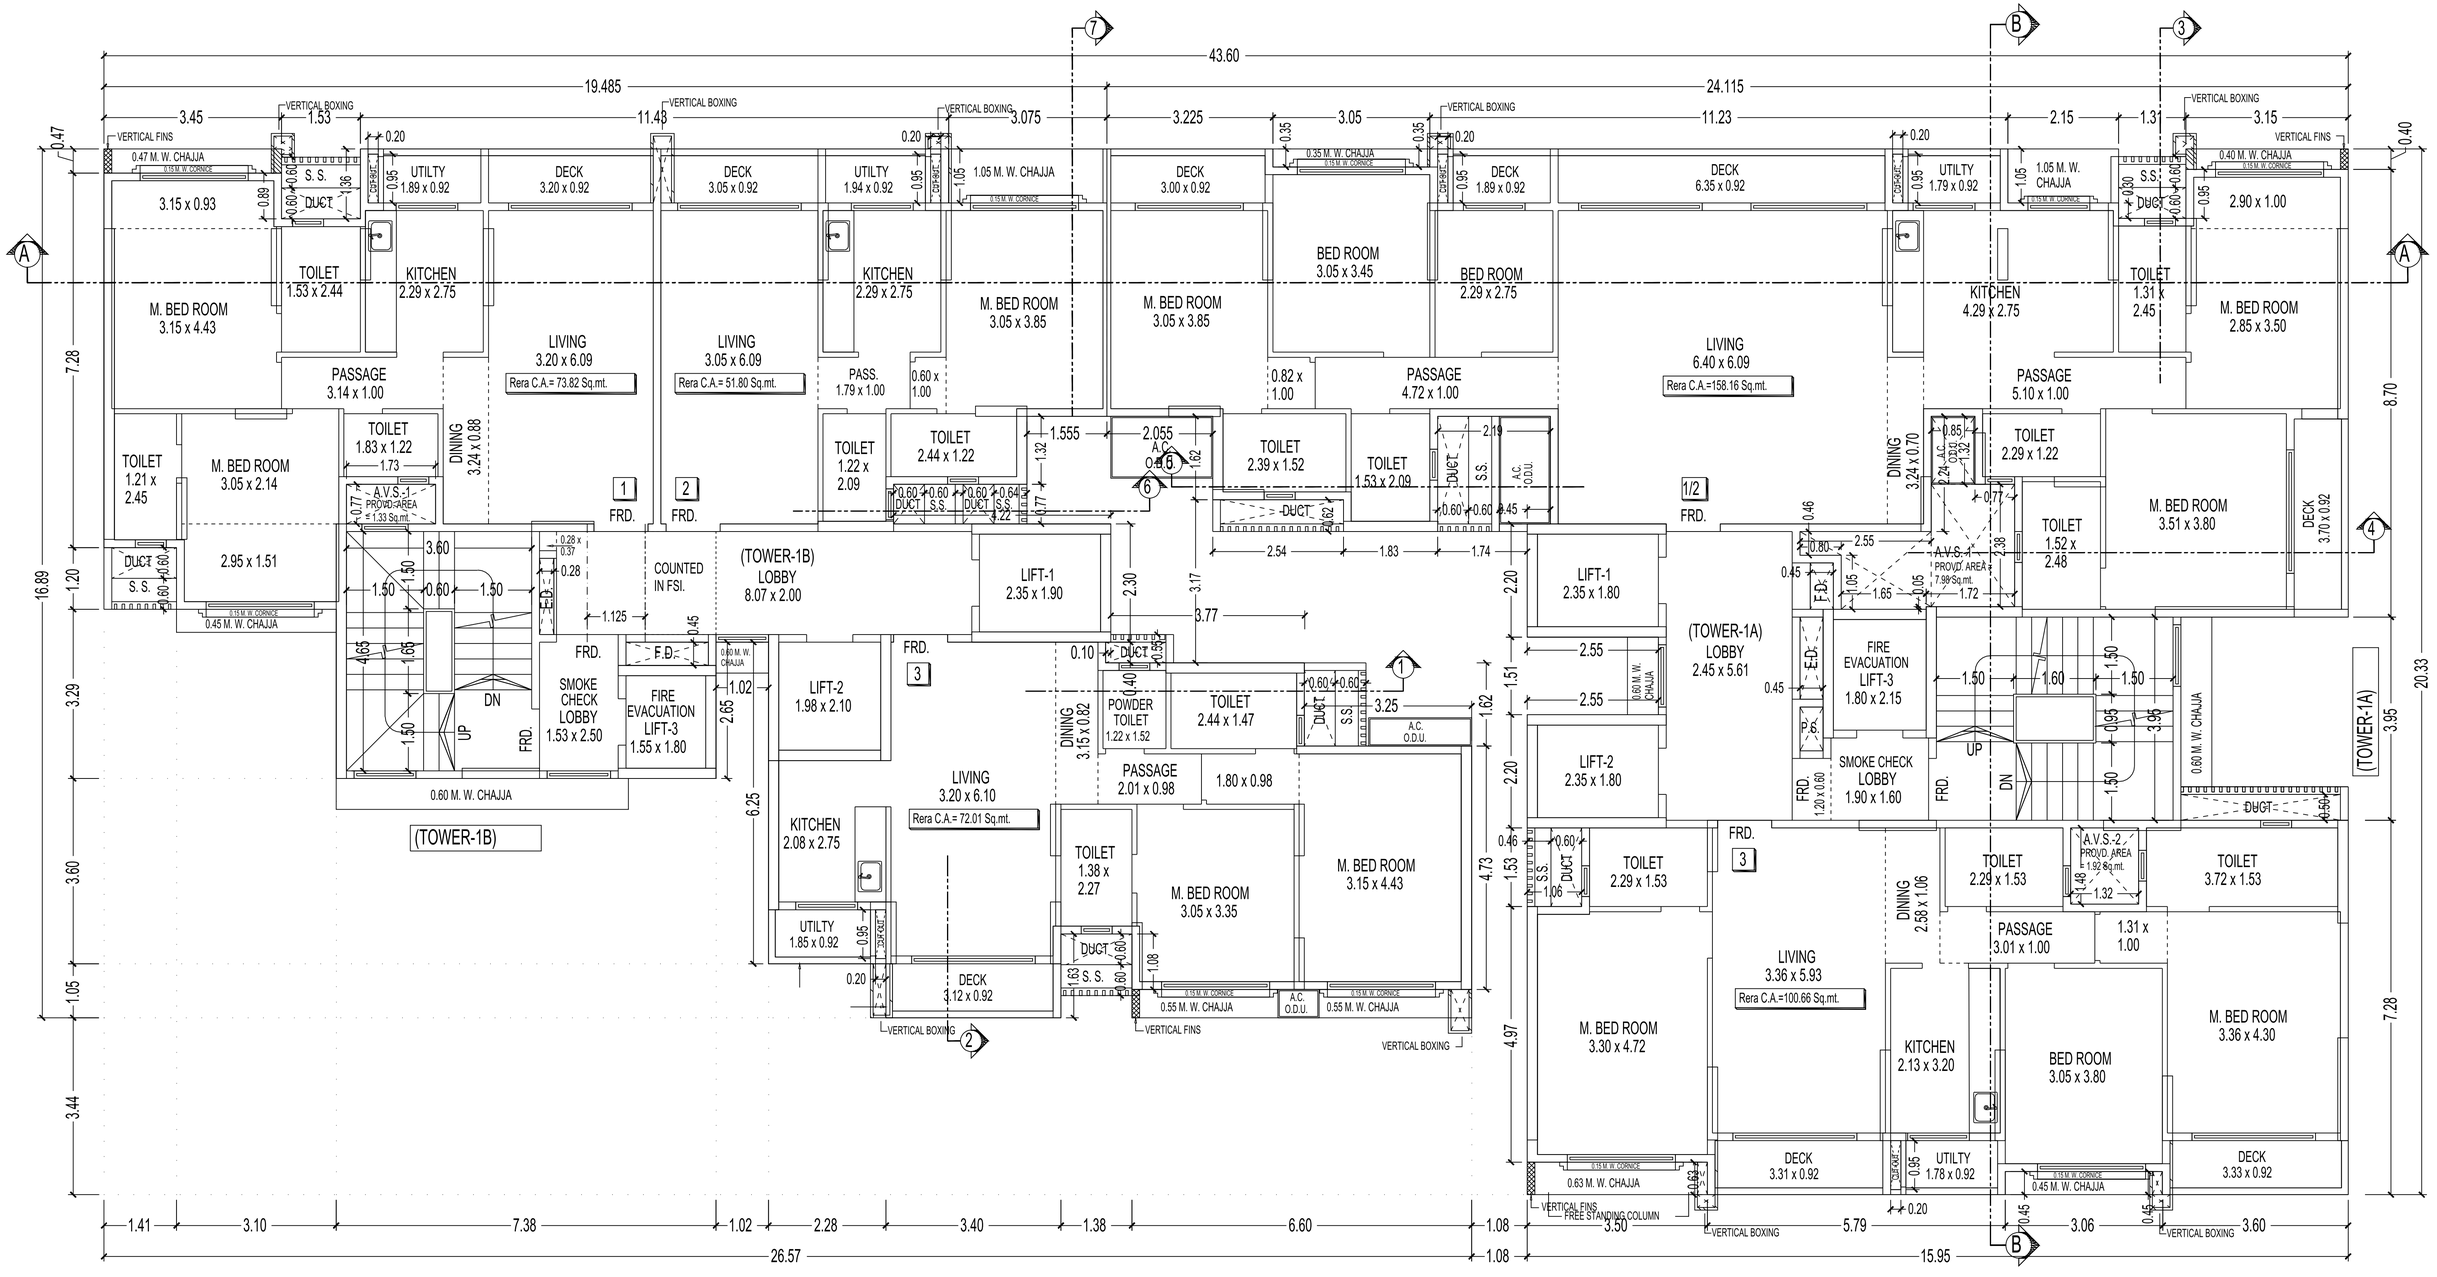

(TOWER-1A & 1B) 16TH FLOOR PLAN