

AREA DIAGRAM

SCALE 1:100

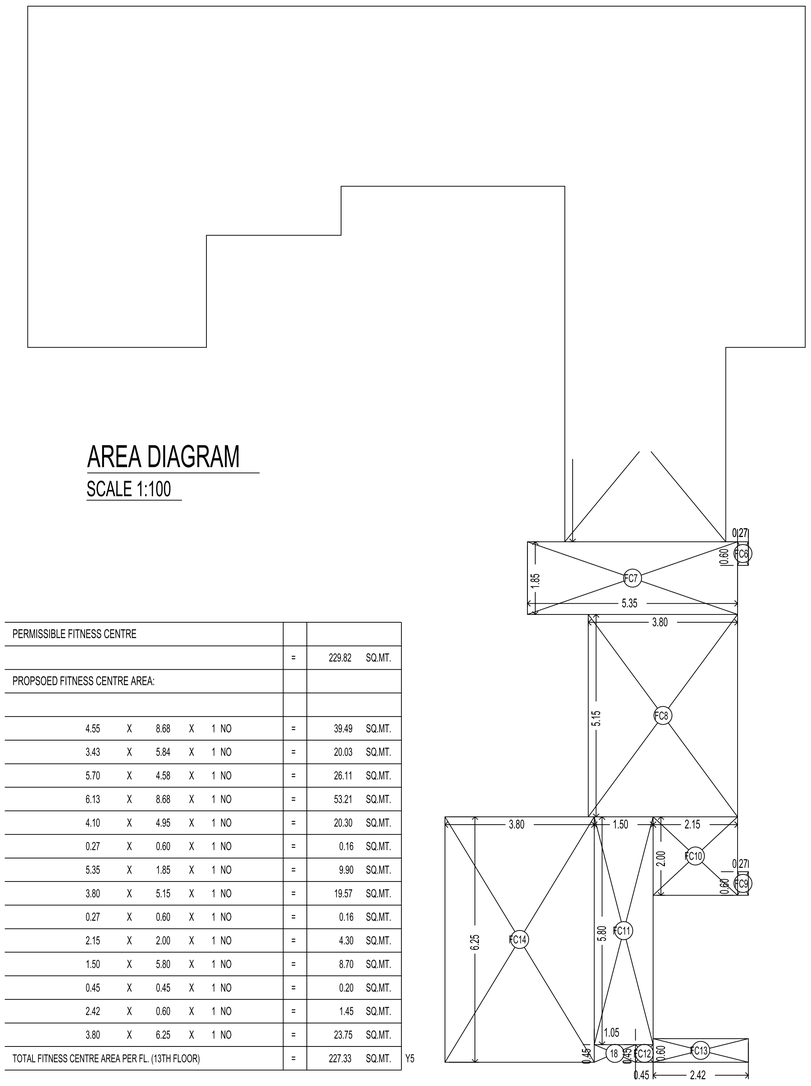

PERMISSIBLE FITNESS CENTRE								
						=	229.82	SQ.MT.
PROPSOED FITNESS CENTRE AREA:								
4.55	X	8.68	X	1	NO	=	39.49	SQ.MT.
3.43	X	5.84	X	1	NO	=	20.03	SQ.MT.
5.70	X	4.58	X	1	NO	=	26.11	SQ.MT.
6.13	X	8.68	X	1	NO	=	53.21	SQ.MT.
4.10	X	4.95	X	1	NO	=	20.30	SQ.MT.
0.27	X	0.60	X	1	NO	=	0.16	SQ.MT.
5.35	X	1.85	X	1	NO	=	9.90	SQ.MT.
3.80	X	5.15	X	1	NO	=	19.57	SQ.MT.
0.27	X	0.60	X	1	NO	=	0.16	SQ.MT.
2.15	X	2.00	X	1	NO	=	4.30	SQ.MT.
1.50	X	5.80	X	1	NO	=	8.70	SQ.MT.
0.45	X	0.45	X	1	NO	=	0.20	SQ.MT.
2.42	X	0.60	X	1	NO	=	1.45	SQ.MT.
3.80	X	6.25	X	1	NO	=	23.75	SQ.MT.
TOTAL FITNESS CENTRE AREA PER FL. (13TH FLOOR)						=	227.33	SQ.MT.

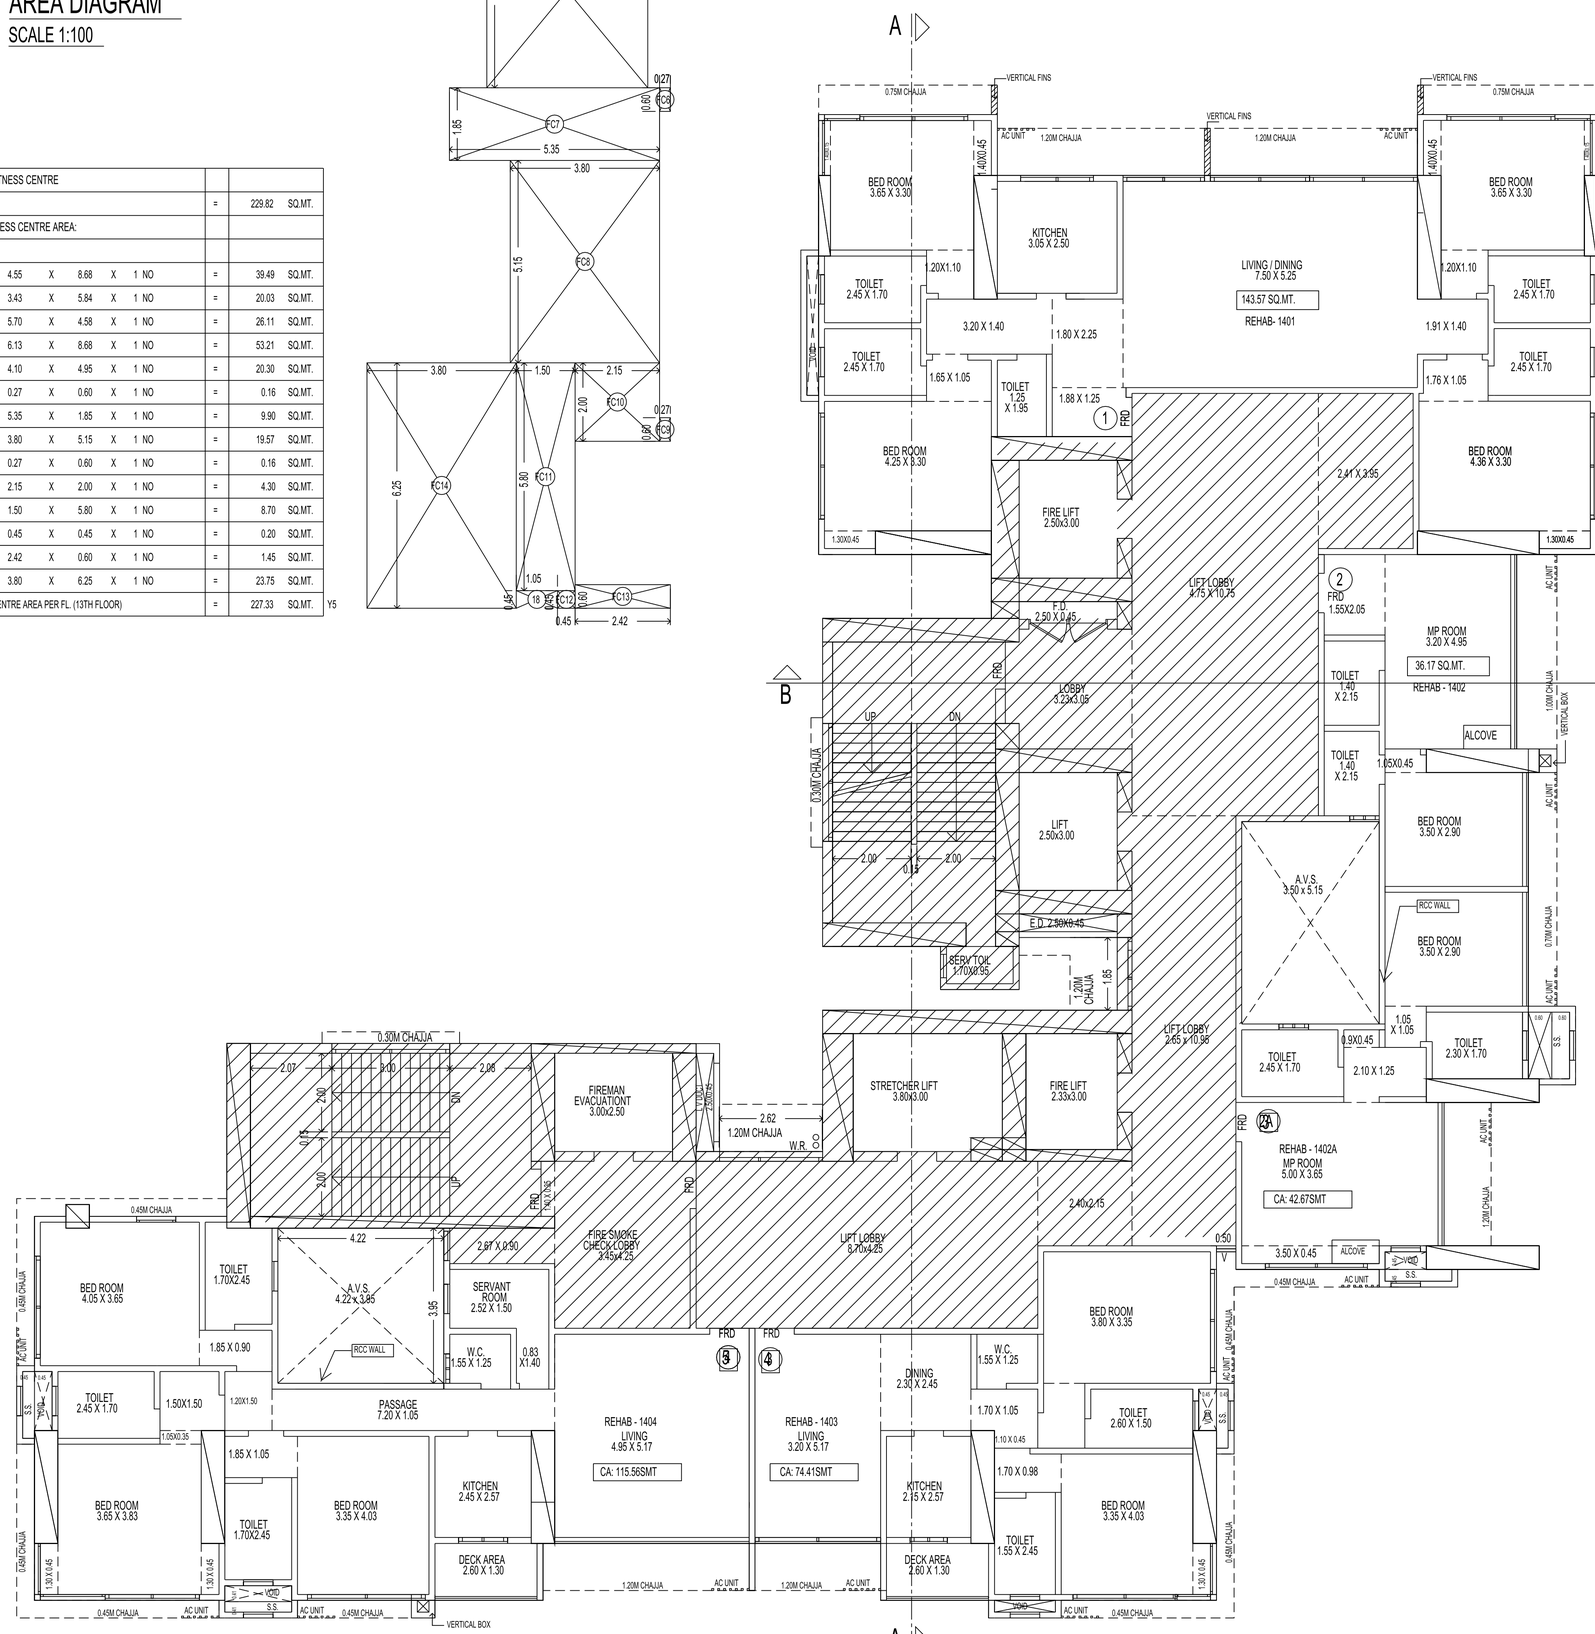

14TH FLOOR PLAN

SCALE 1:100

PROFORMA - B

CONTENTS OF SHEET

13TH SERVICE FLOOR PLAN, 14TH FLOOR PLAN

DESCRIPTION OF PROPOSAL & PROPERTY

PROPOSED REDEVELOPMENT OF PROPERTY BEARING C.S. NO.150A/10,155/10 & 155C/10 OF MATUNGA DIVISION SITUATED AT DR. B.A.ROAD MUMBAI-400019 IN F/N WARD.

PLANS FOR CONCESSIONS

KSHITIJKU MAR RADHESHY AM VARMA

S.E.(BP)-XII

SURAJ PRADEEP P AMBRE

A.E.(BP)-I

NAME OF APPLICANT

POPATLAL DHANRAJ VARDHAN

M/s. PD Lifestyle LLP

NORTH LINE	JOB NO.	DATE	CHECKED	DRAWN BY
	2025	12.08.2025	SSJ	SSC

NAME, ADDRESS & SIGNATURE OF CONSULTING ARCHITECT

NAME, ADDRESS & SIGNATURE OF ARCHITECT

KANHERE ASSOCIATES LLP
UNIT NO.13 & 14, 2ND FLOOR, SHOPPILINK BUILDING,
DOSTI ACRES, WADALA EAST, MUMBAI 400 037.

Aditya Mahendra Mane

LICENSE SURVEYOR
ADITYA MANE
LIC NO. M840001363

SCALE 1:100


A



A

15TH FLOOR PLAN

SCALE 1:100

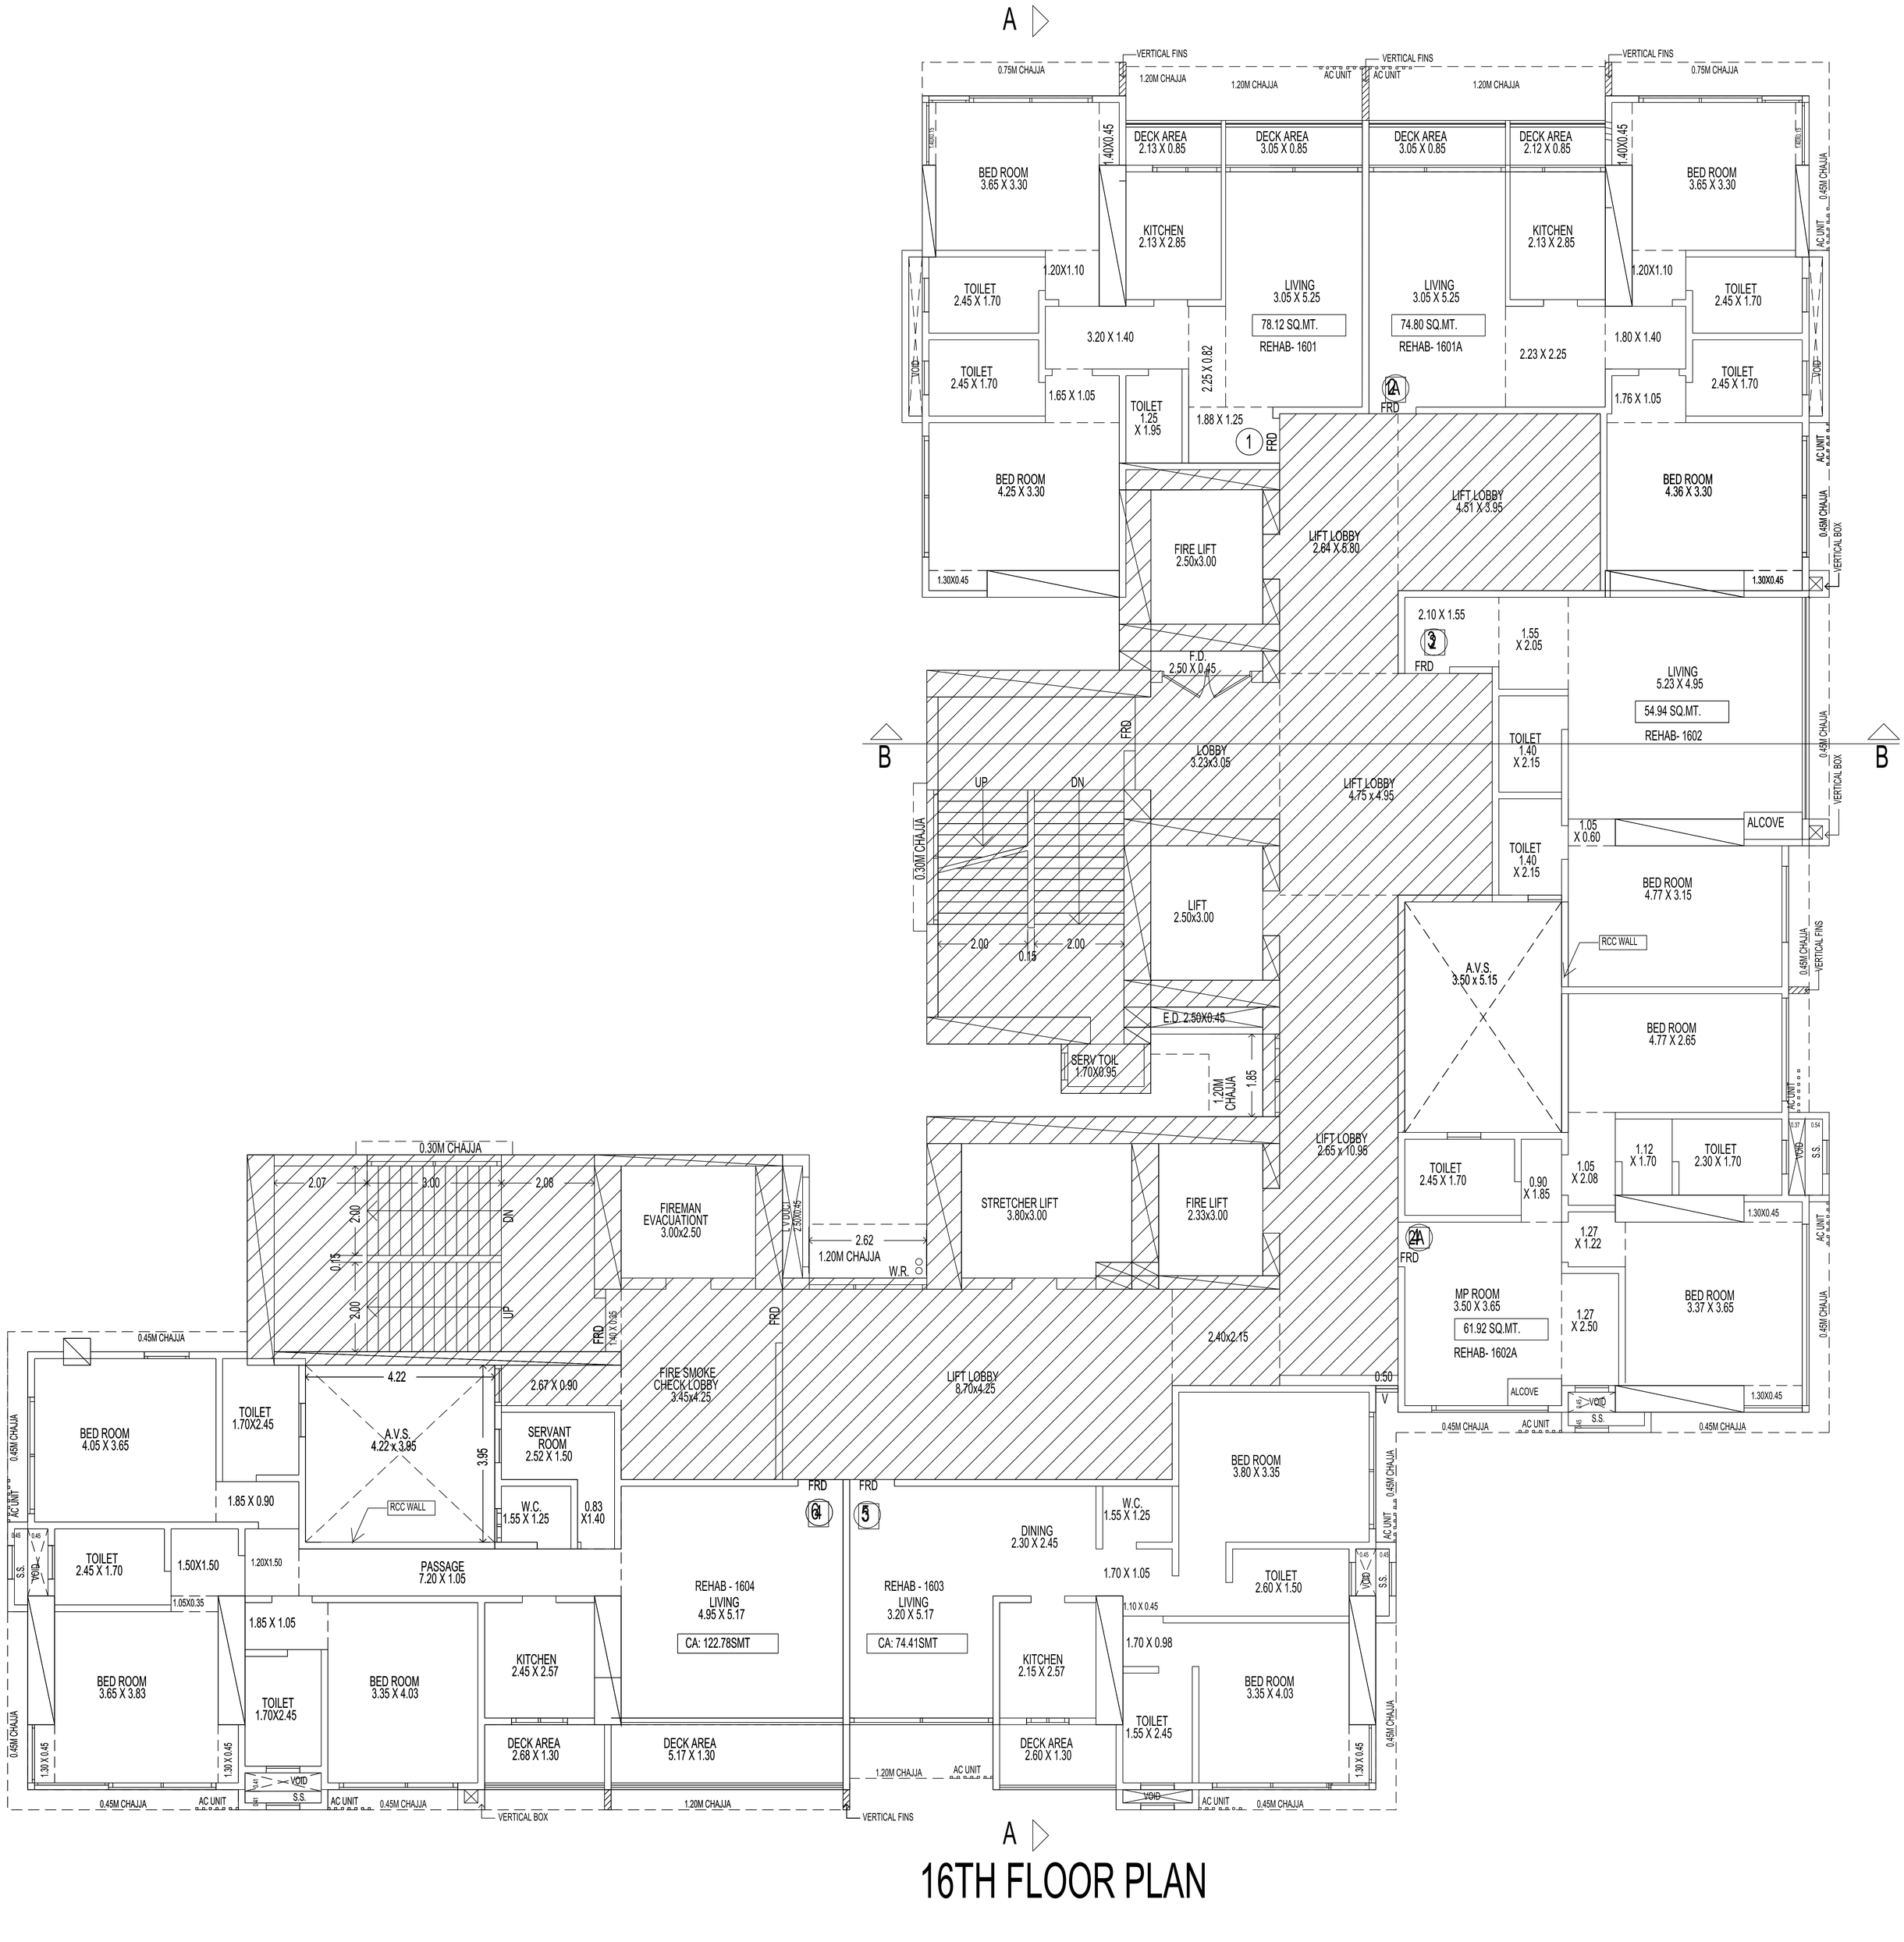

16TH FLOOR PLAN

SCALE 1:100

A

B

B

A


17TH FLOOR PLAN

SCALE 1:100



18TH FLOOR PLAN

SCALE 1:100

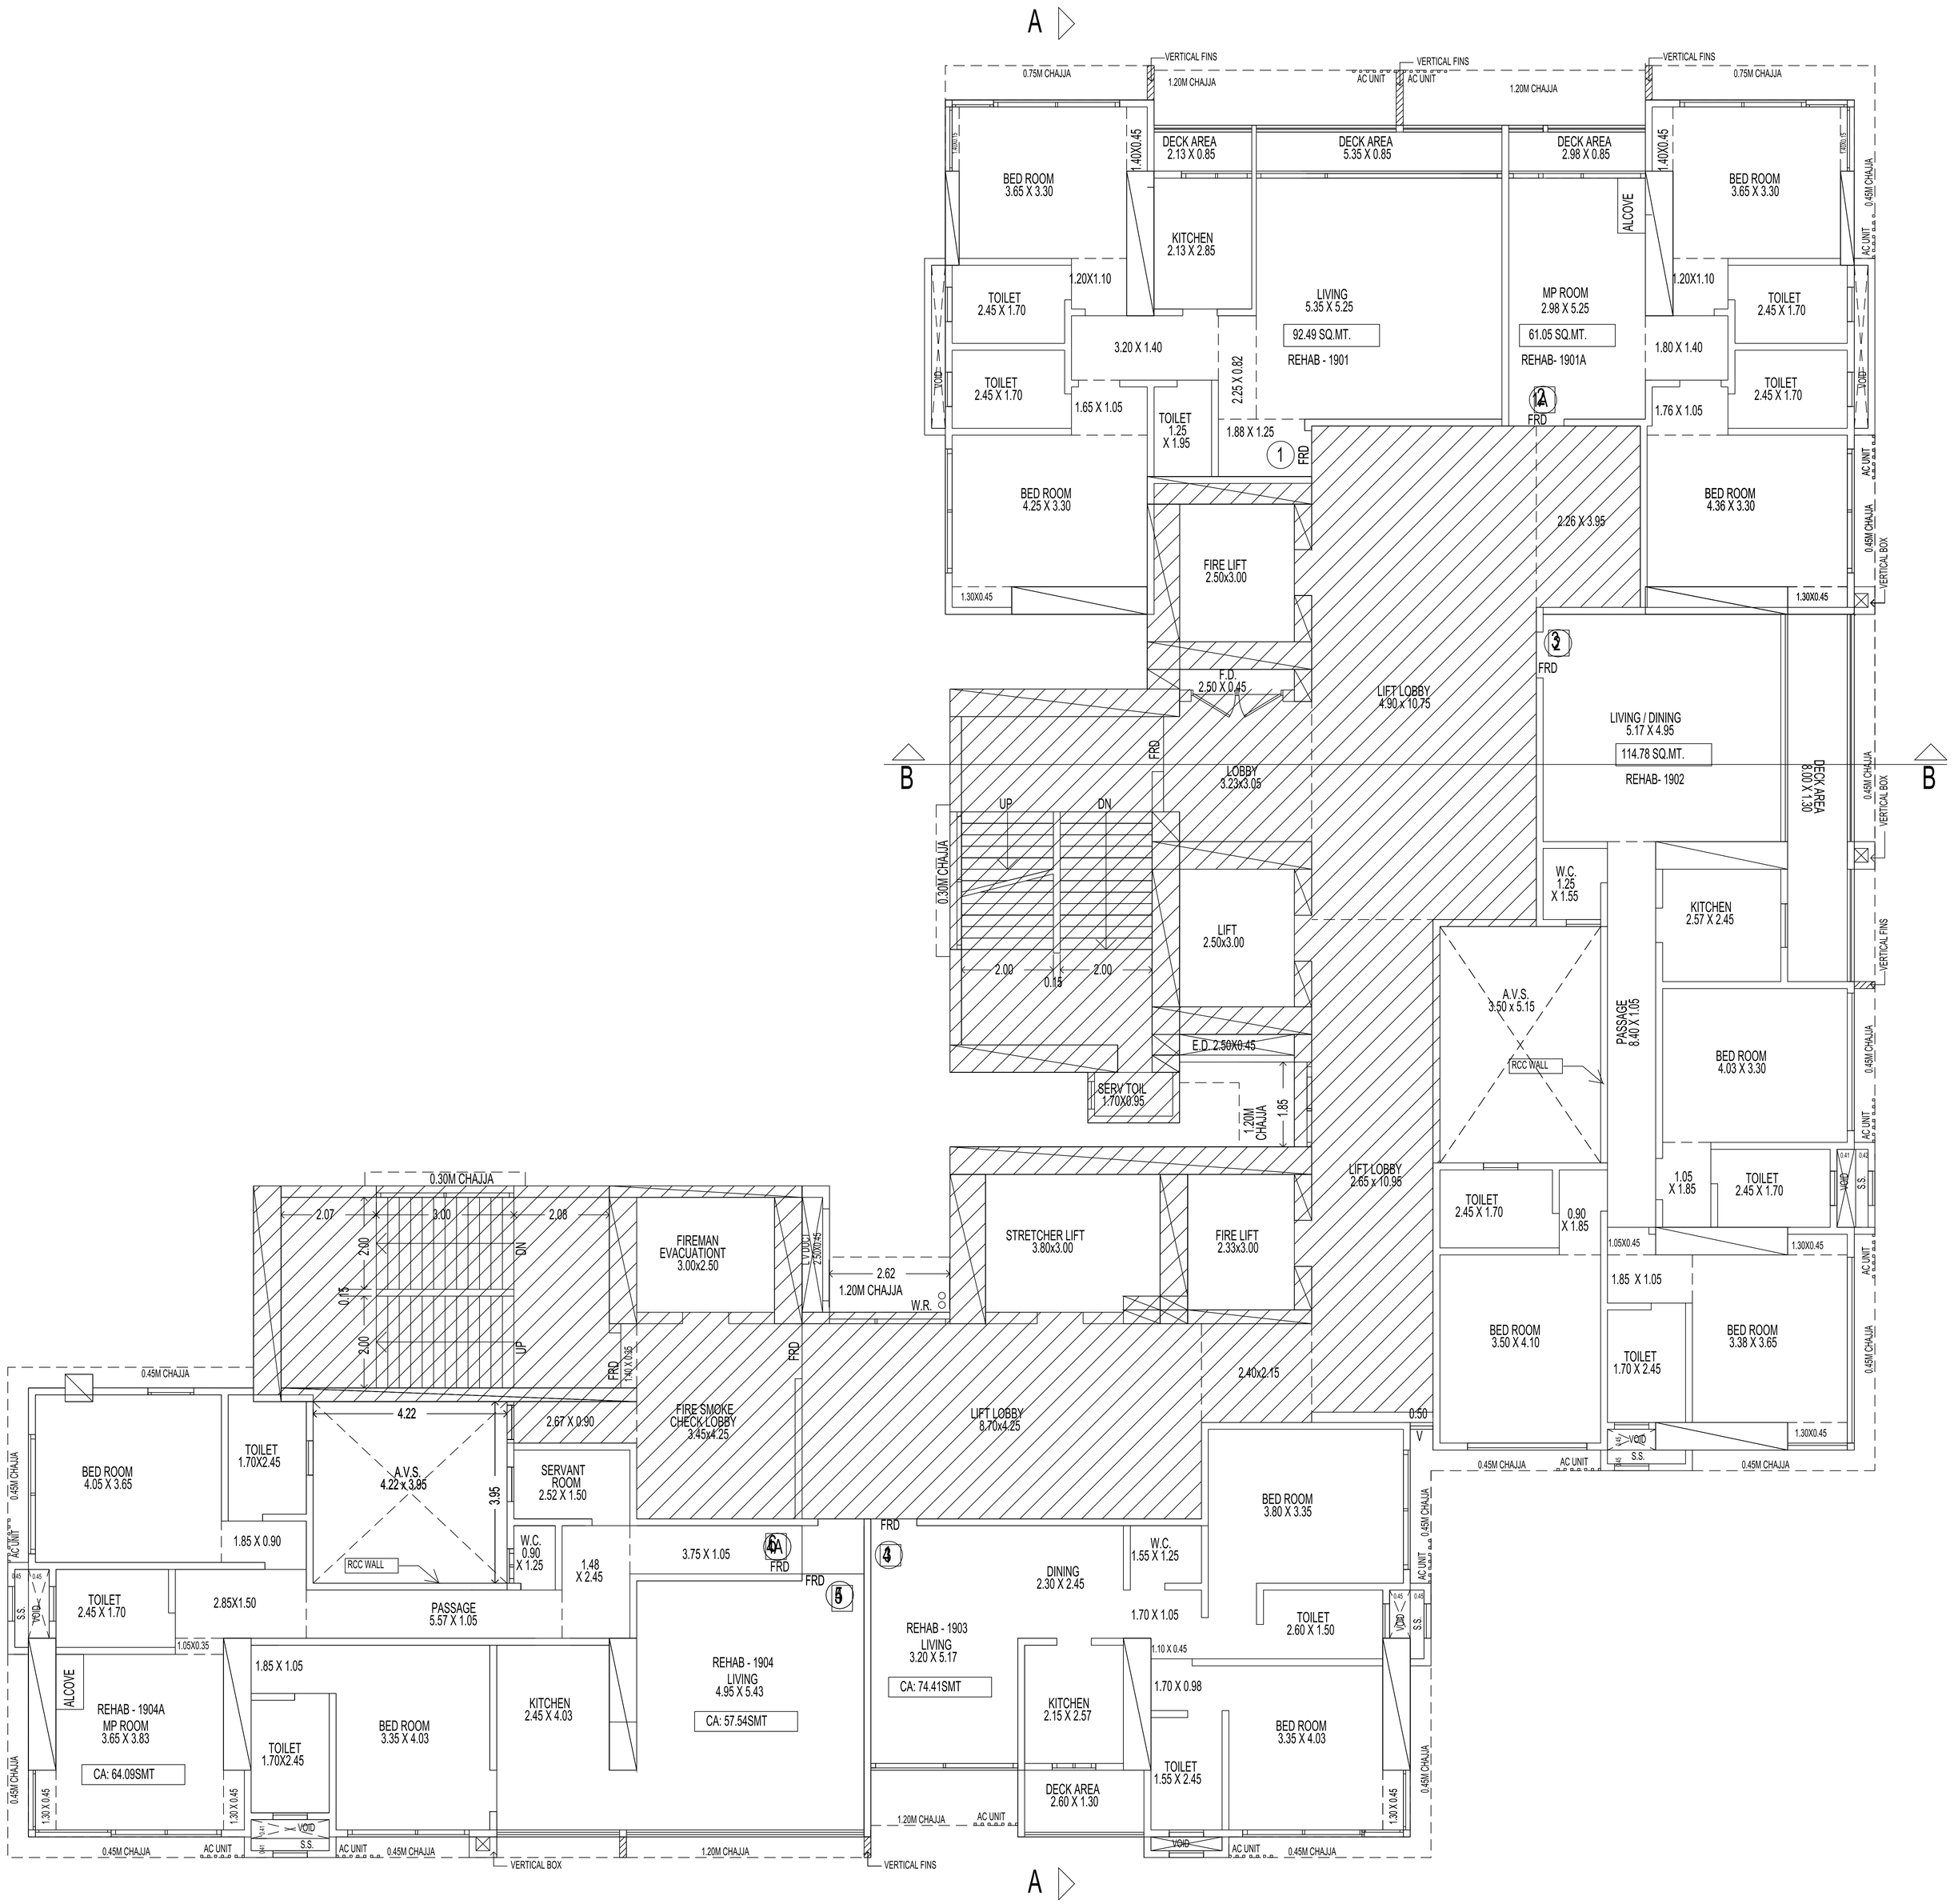

19TH FLOOR PLAN

SCALE 1:100

SCALE 1:100



21ST FLOOR PLAN

SCALE 1:100



22ND TO 26TH, 30TH FLOOR PLAN


SCALE 1:100



A

27TH FLOOR PLAN

SCALE 1:100

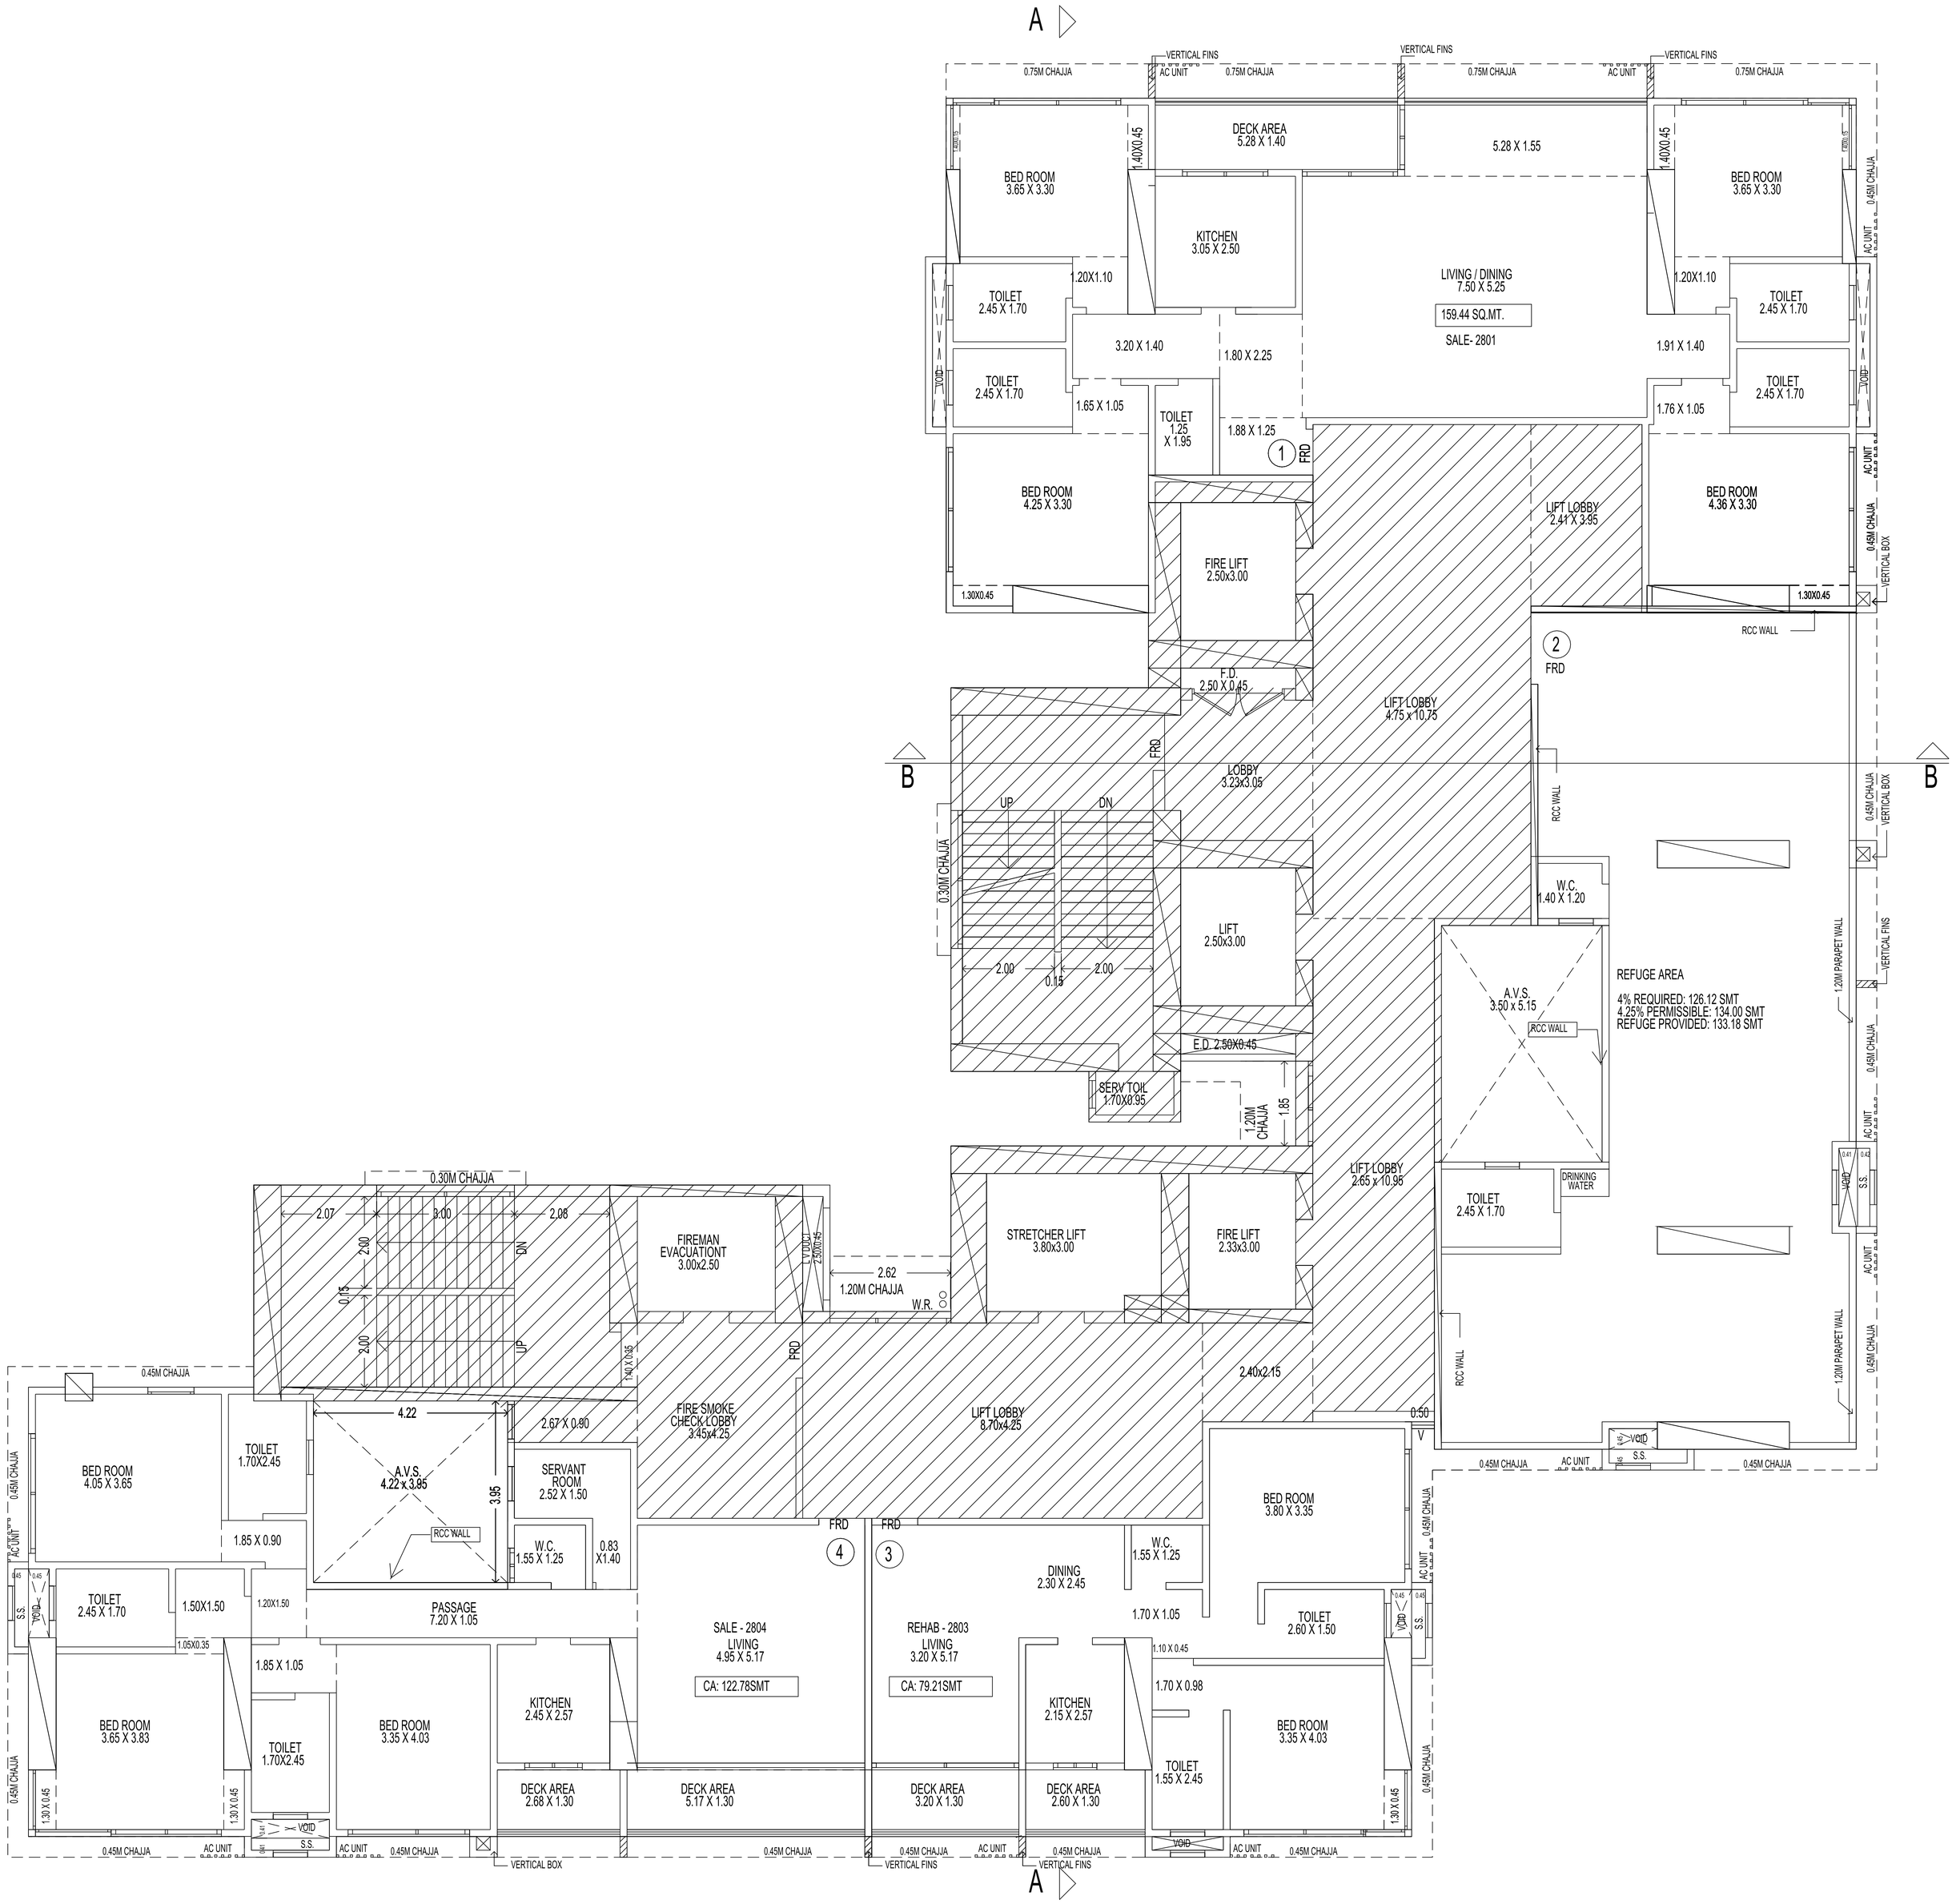

28TH FLOOR PLAN

SCALE 1:100


A



A

29TH FLOOR PLAN

SCALE 1:100

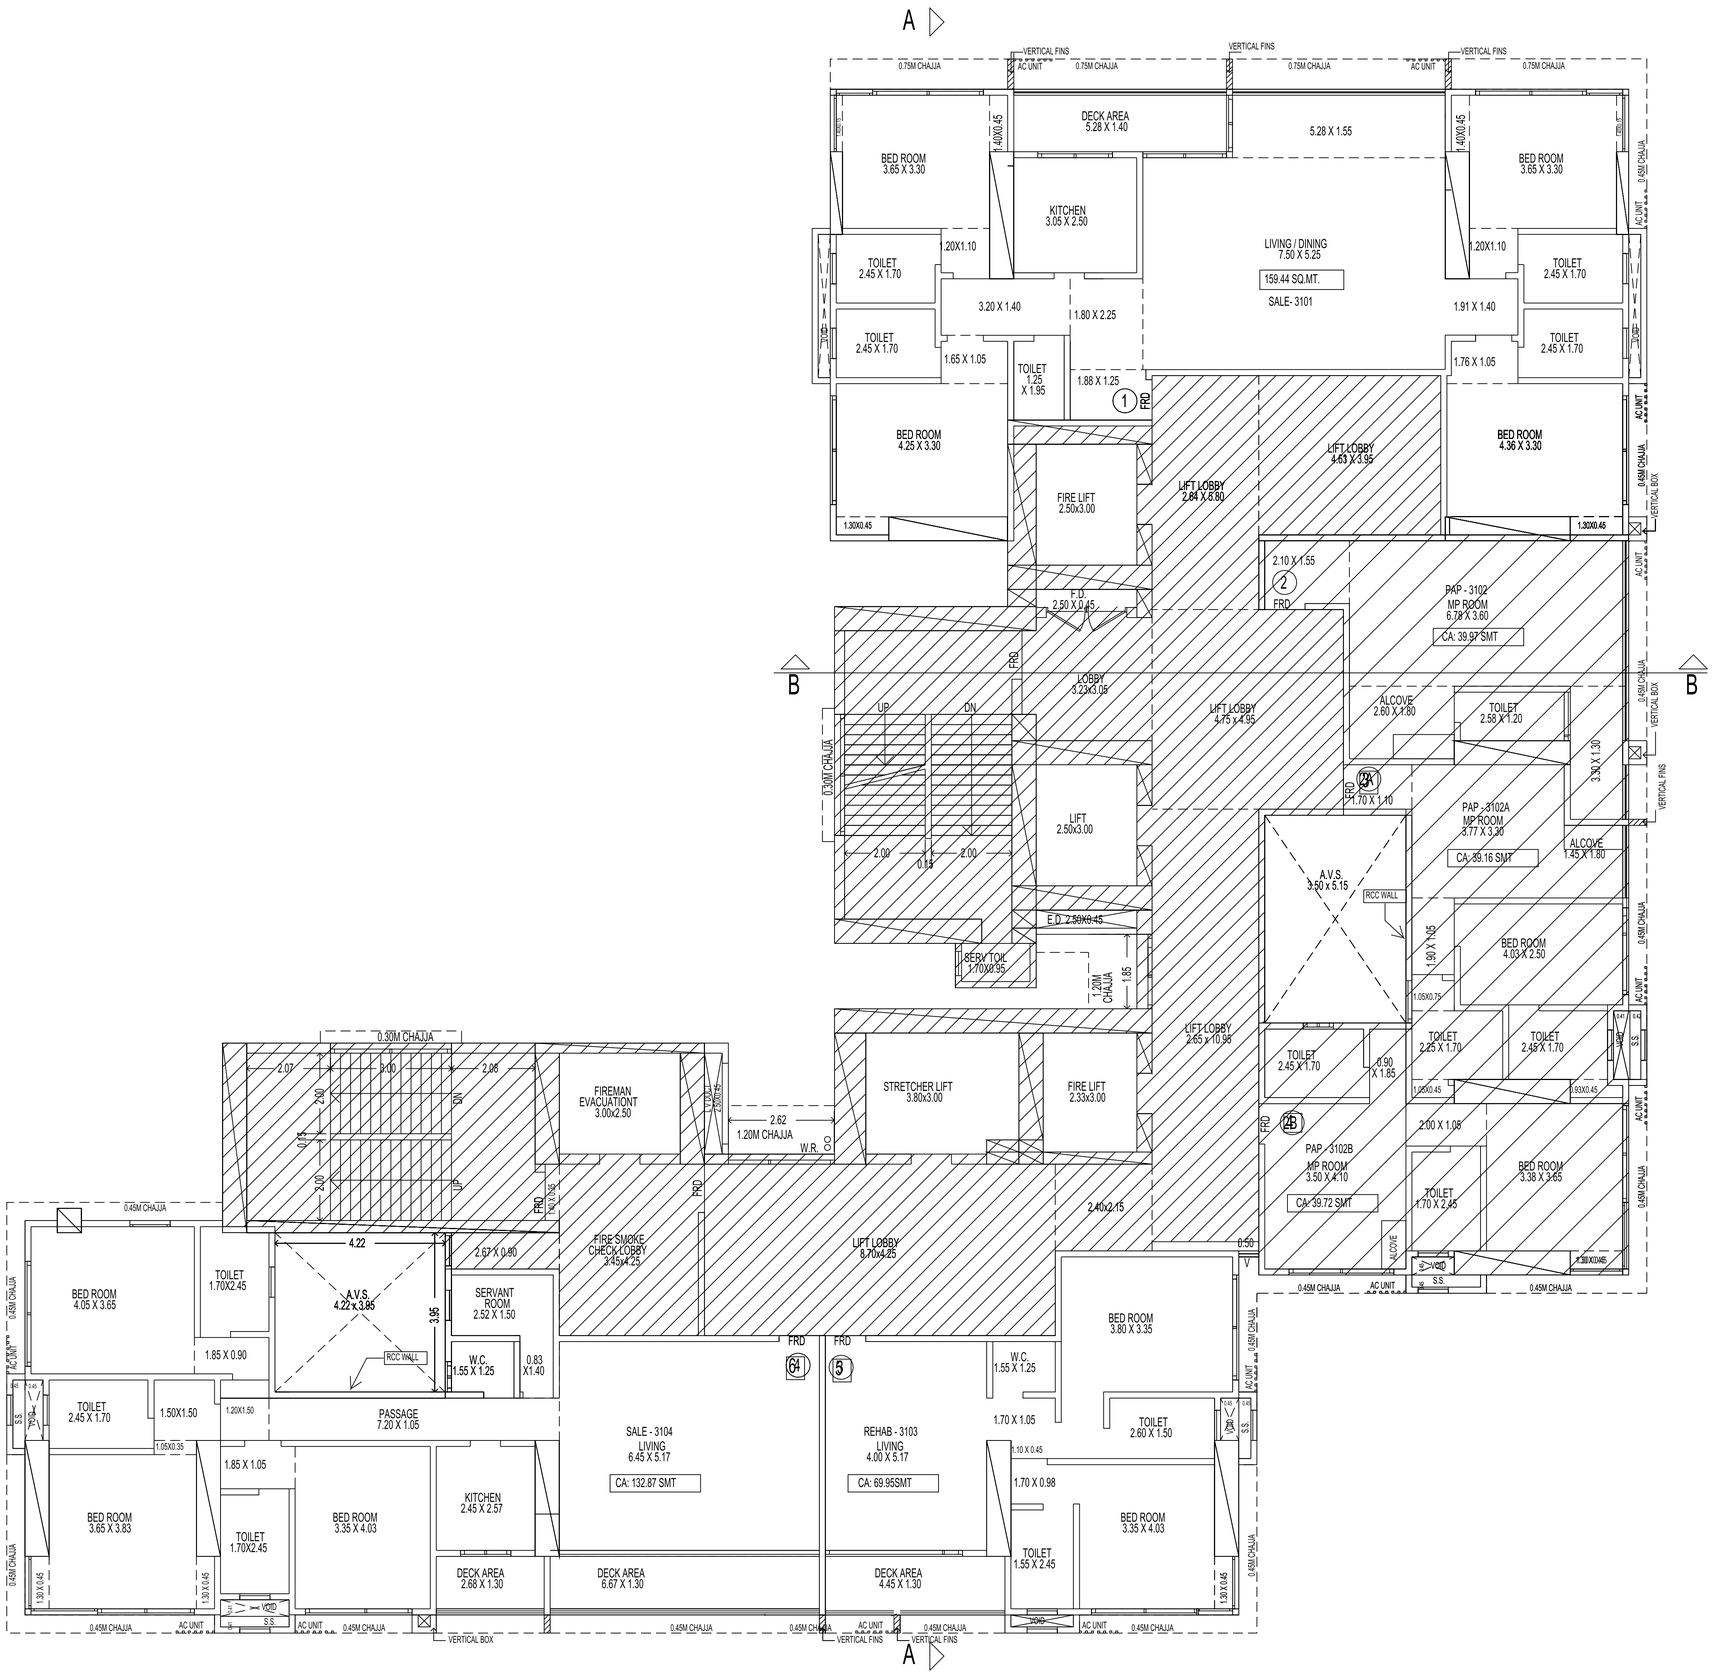

31ST FLOOR PLAN

SCALE 1:100




32ND FLOOR PLAN

SCALE 1:100

WEST

SCALE 1:100

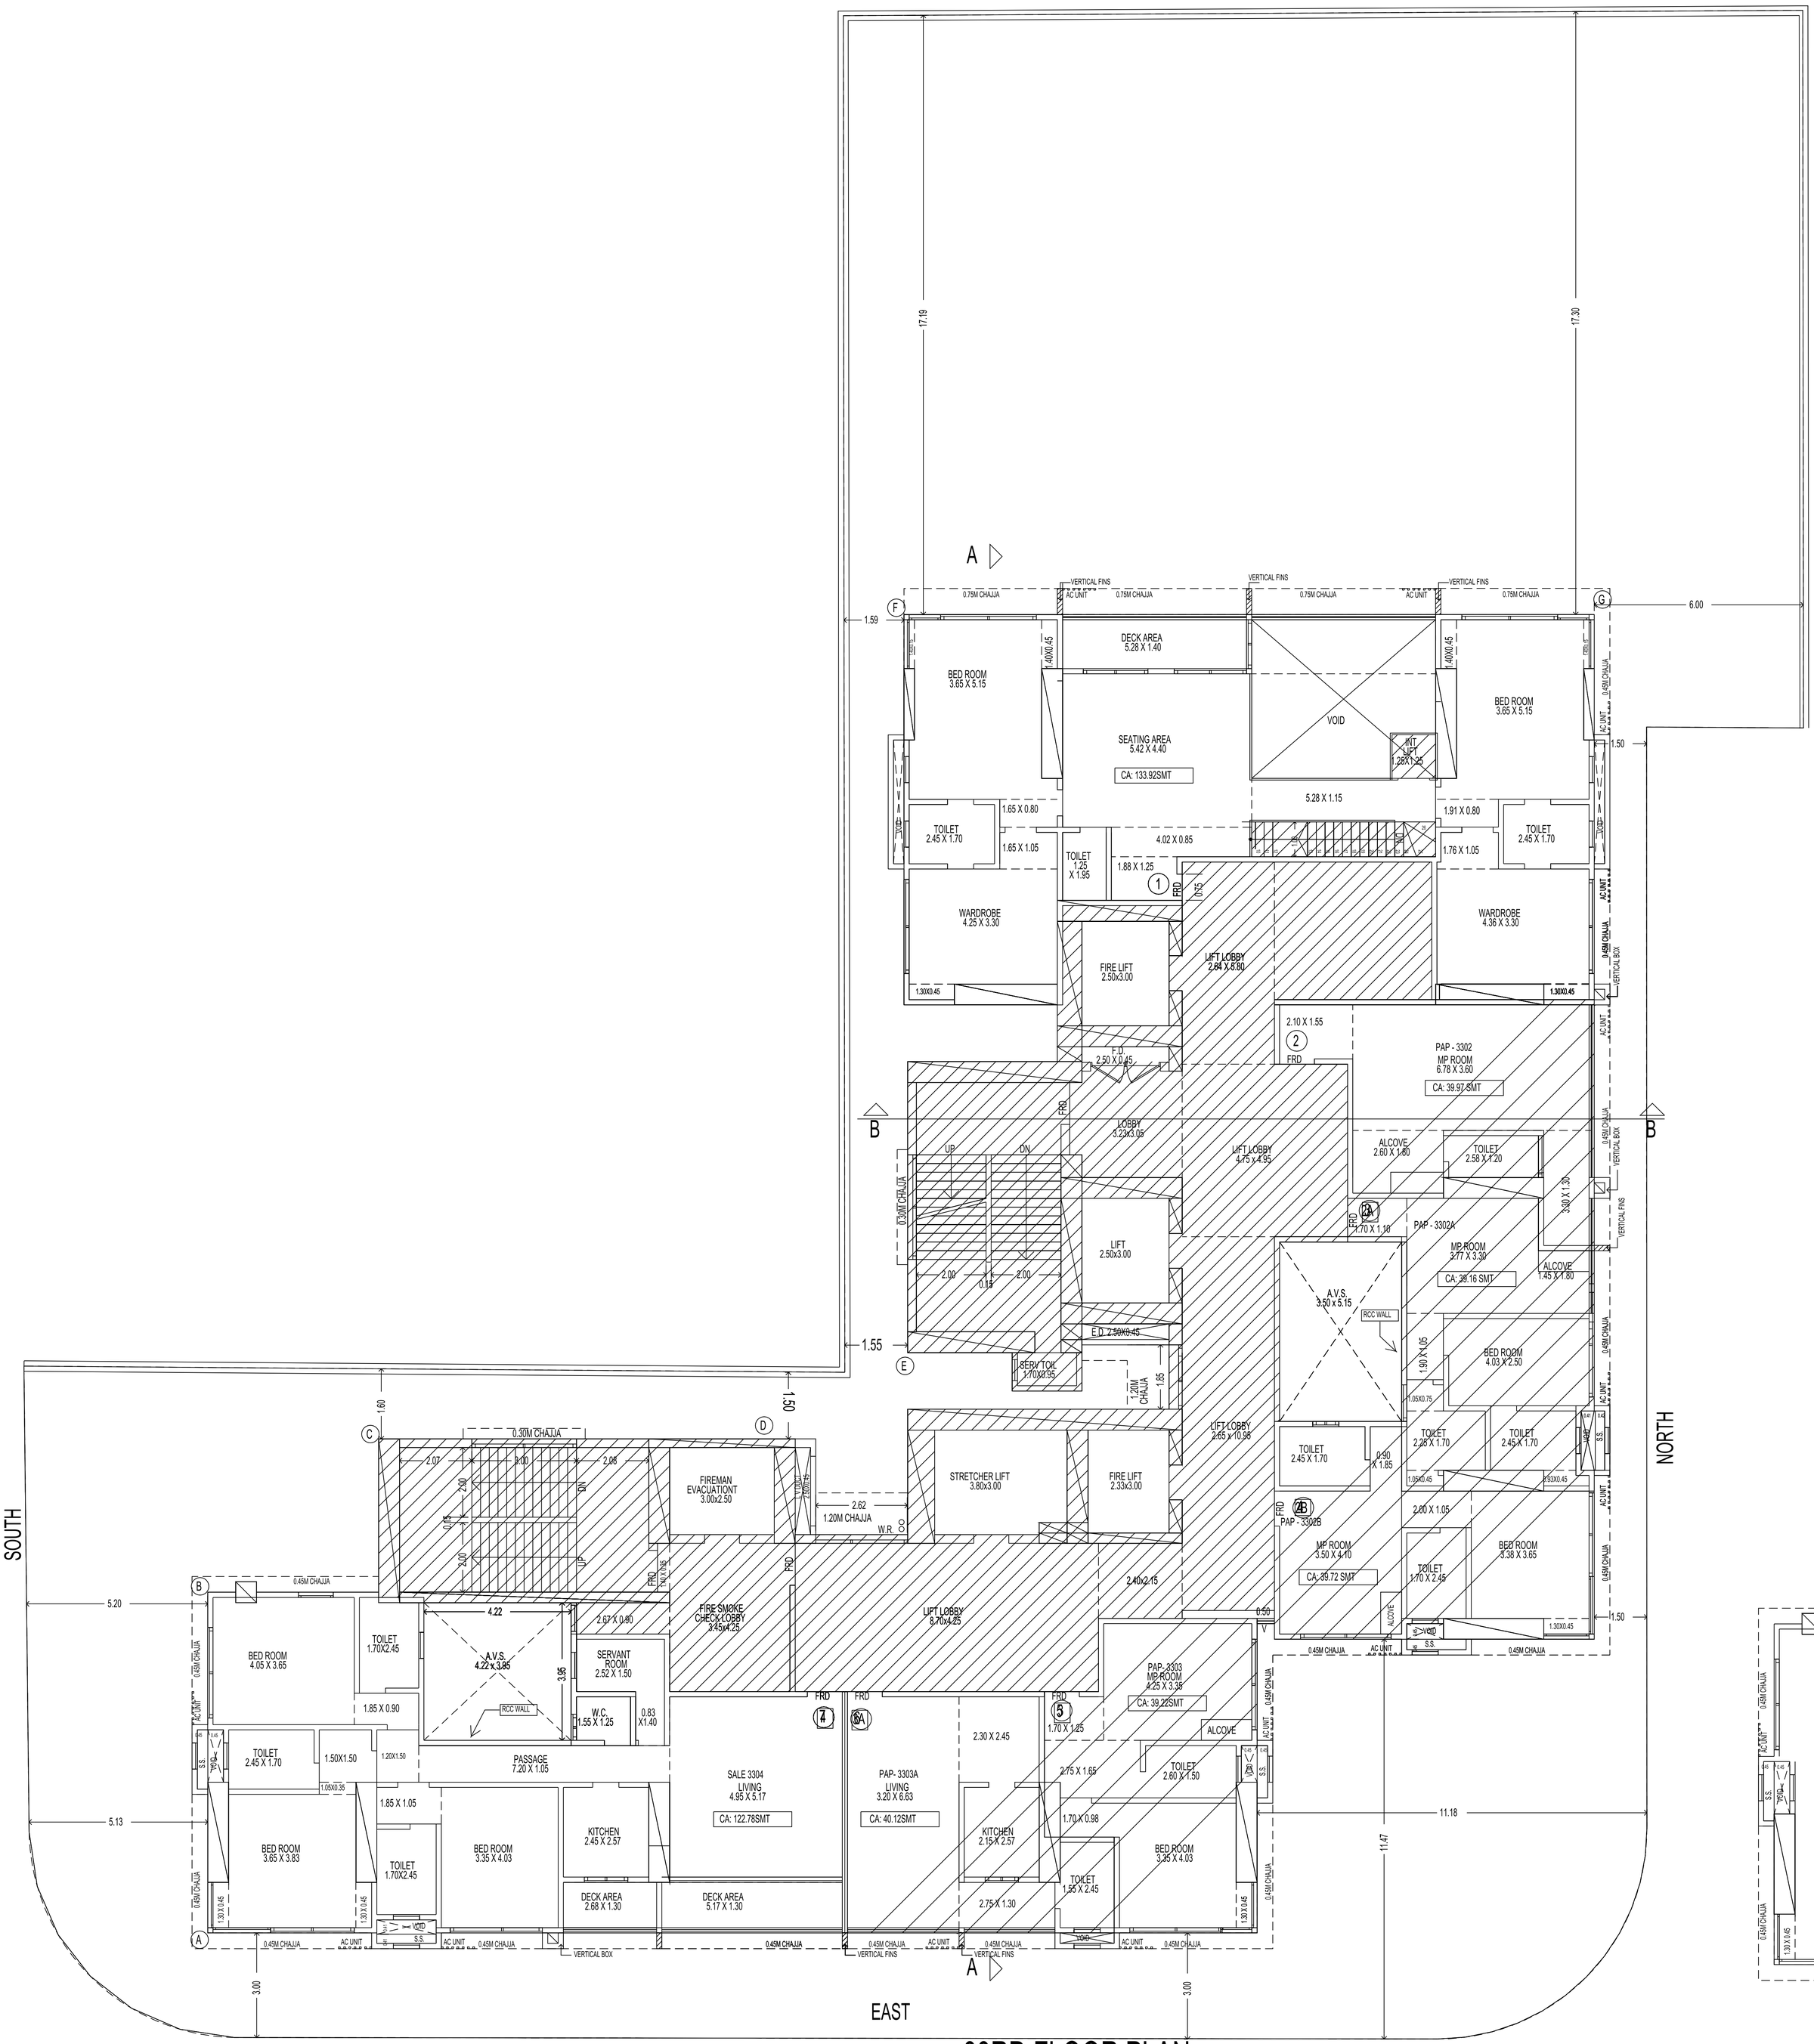

33RD FLOOR PLAN

SCALE 1:100