
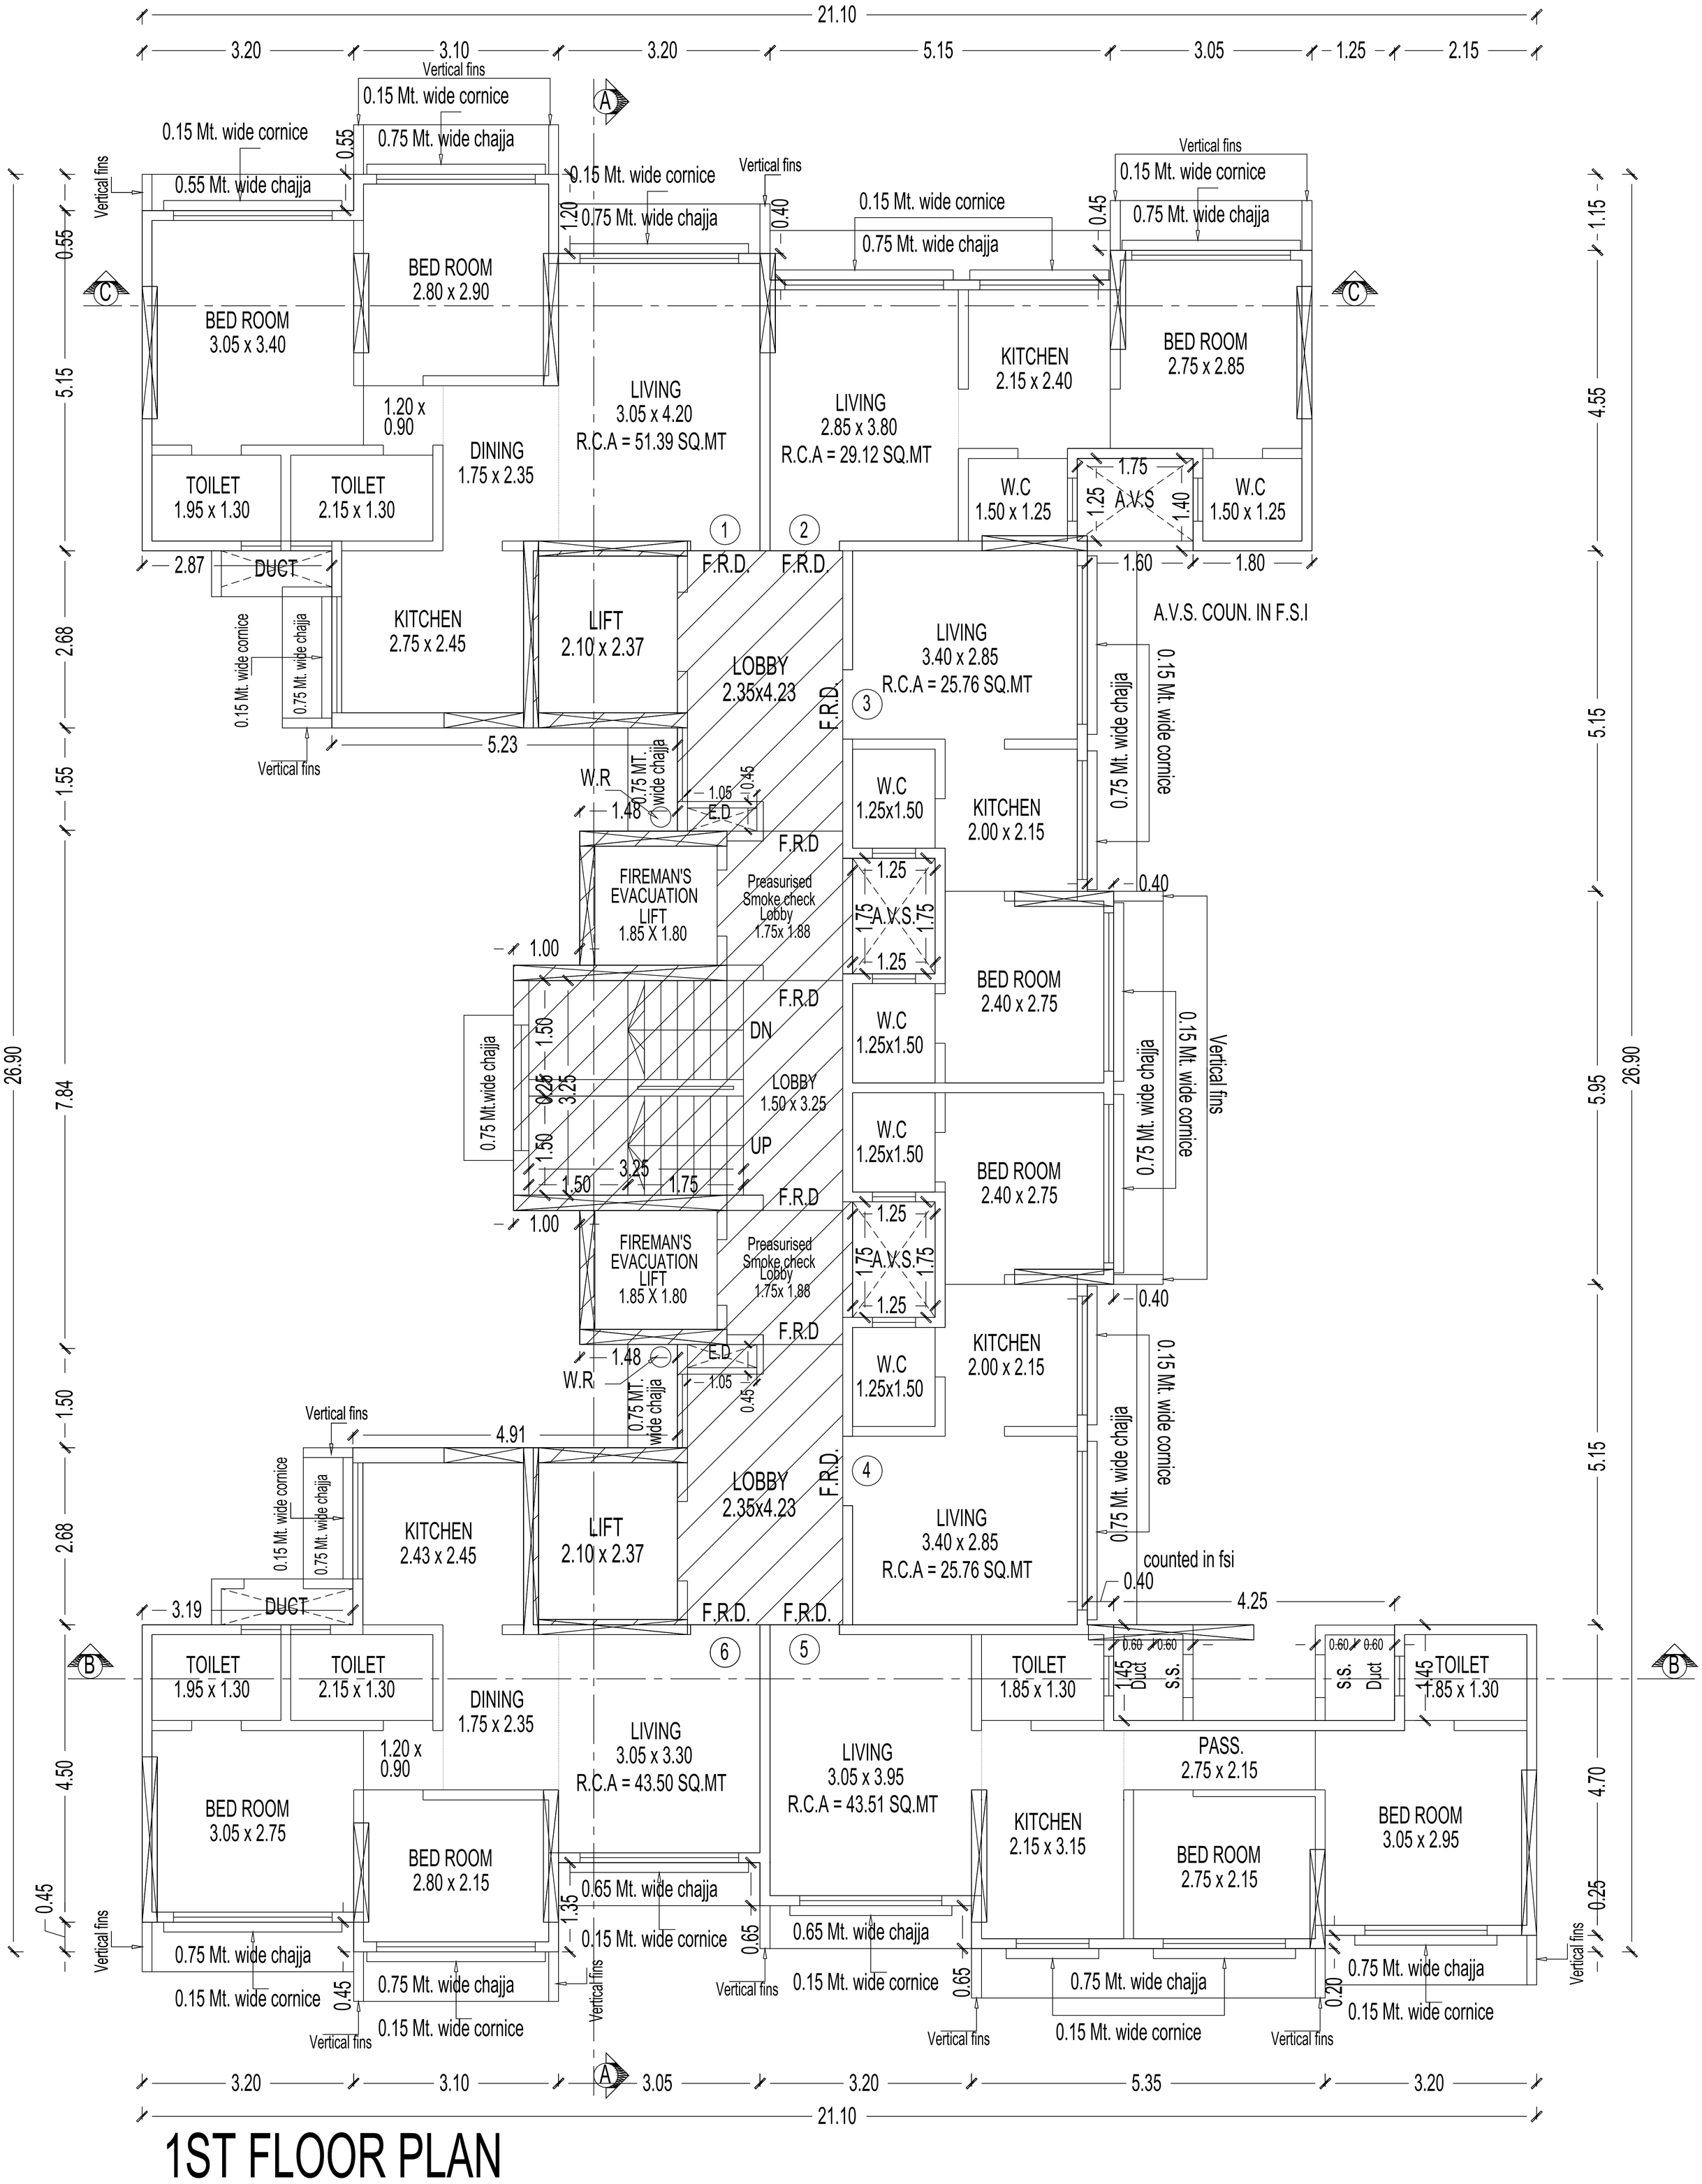


1ST FLOOR PLAN


SCALE :- 1:100

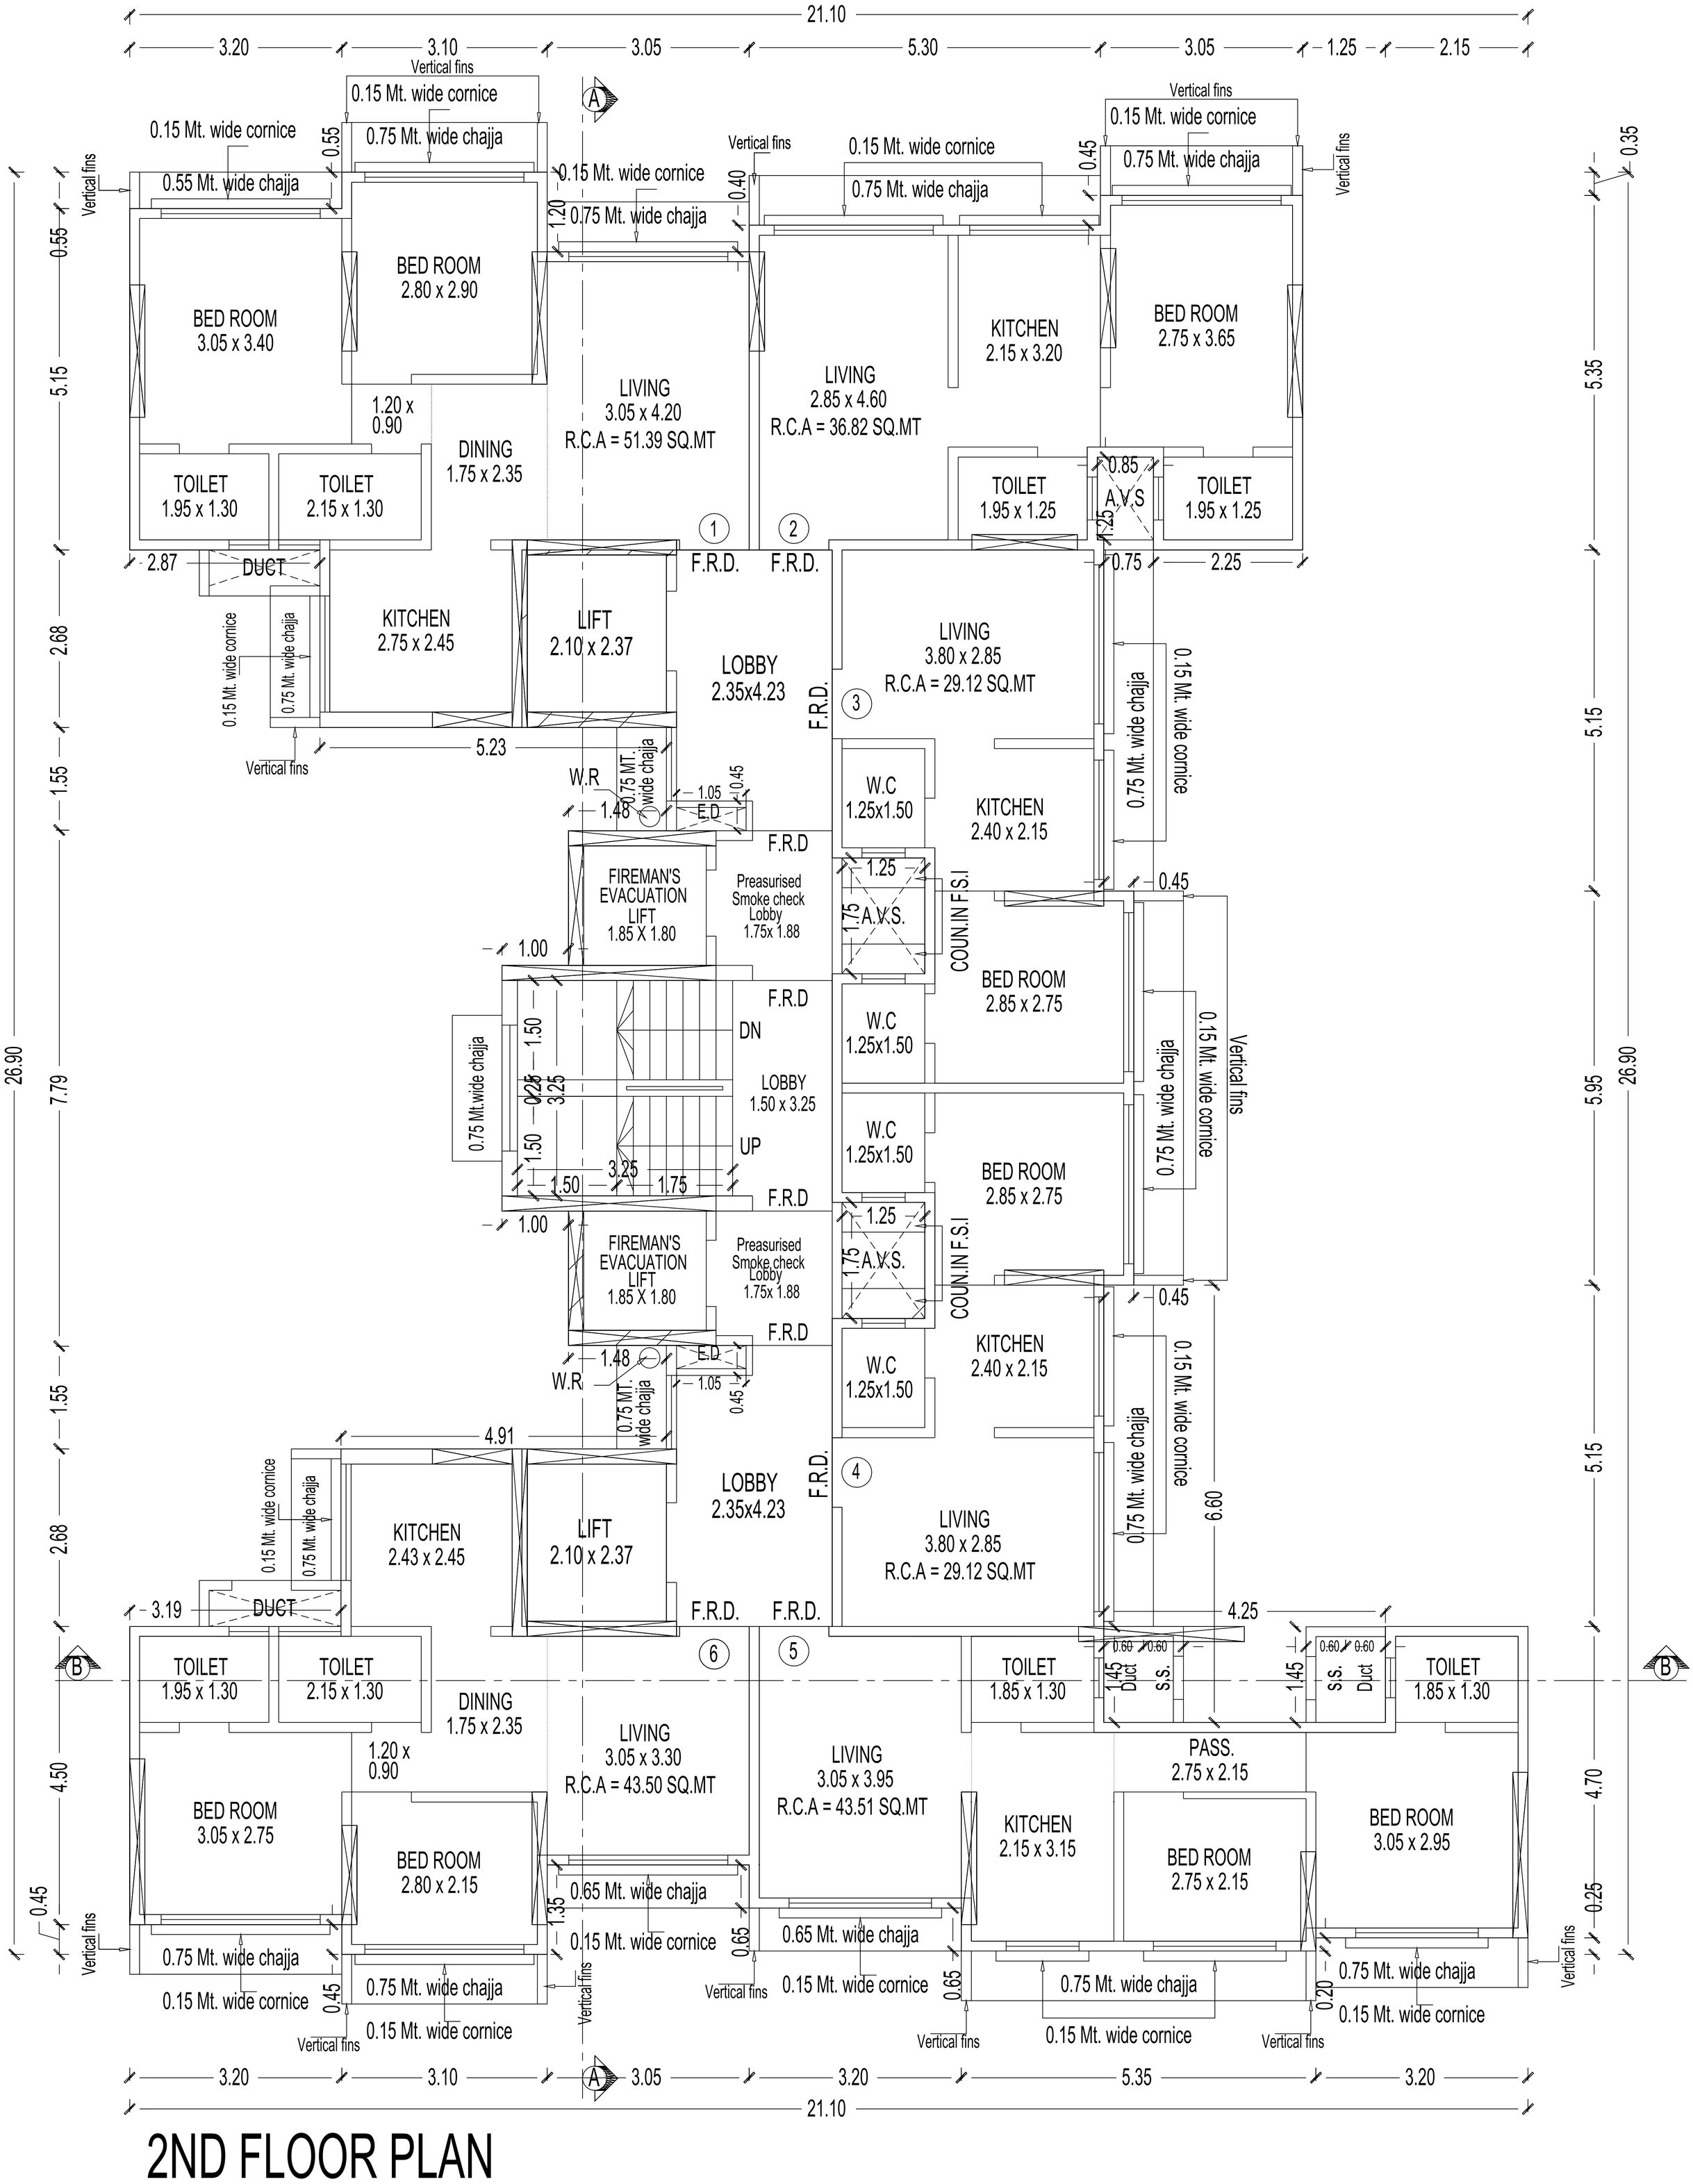

2ND FLOOR PLAN

SCALE :- 1:100


SCALE :- 1:100

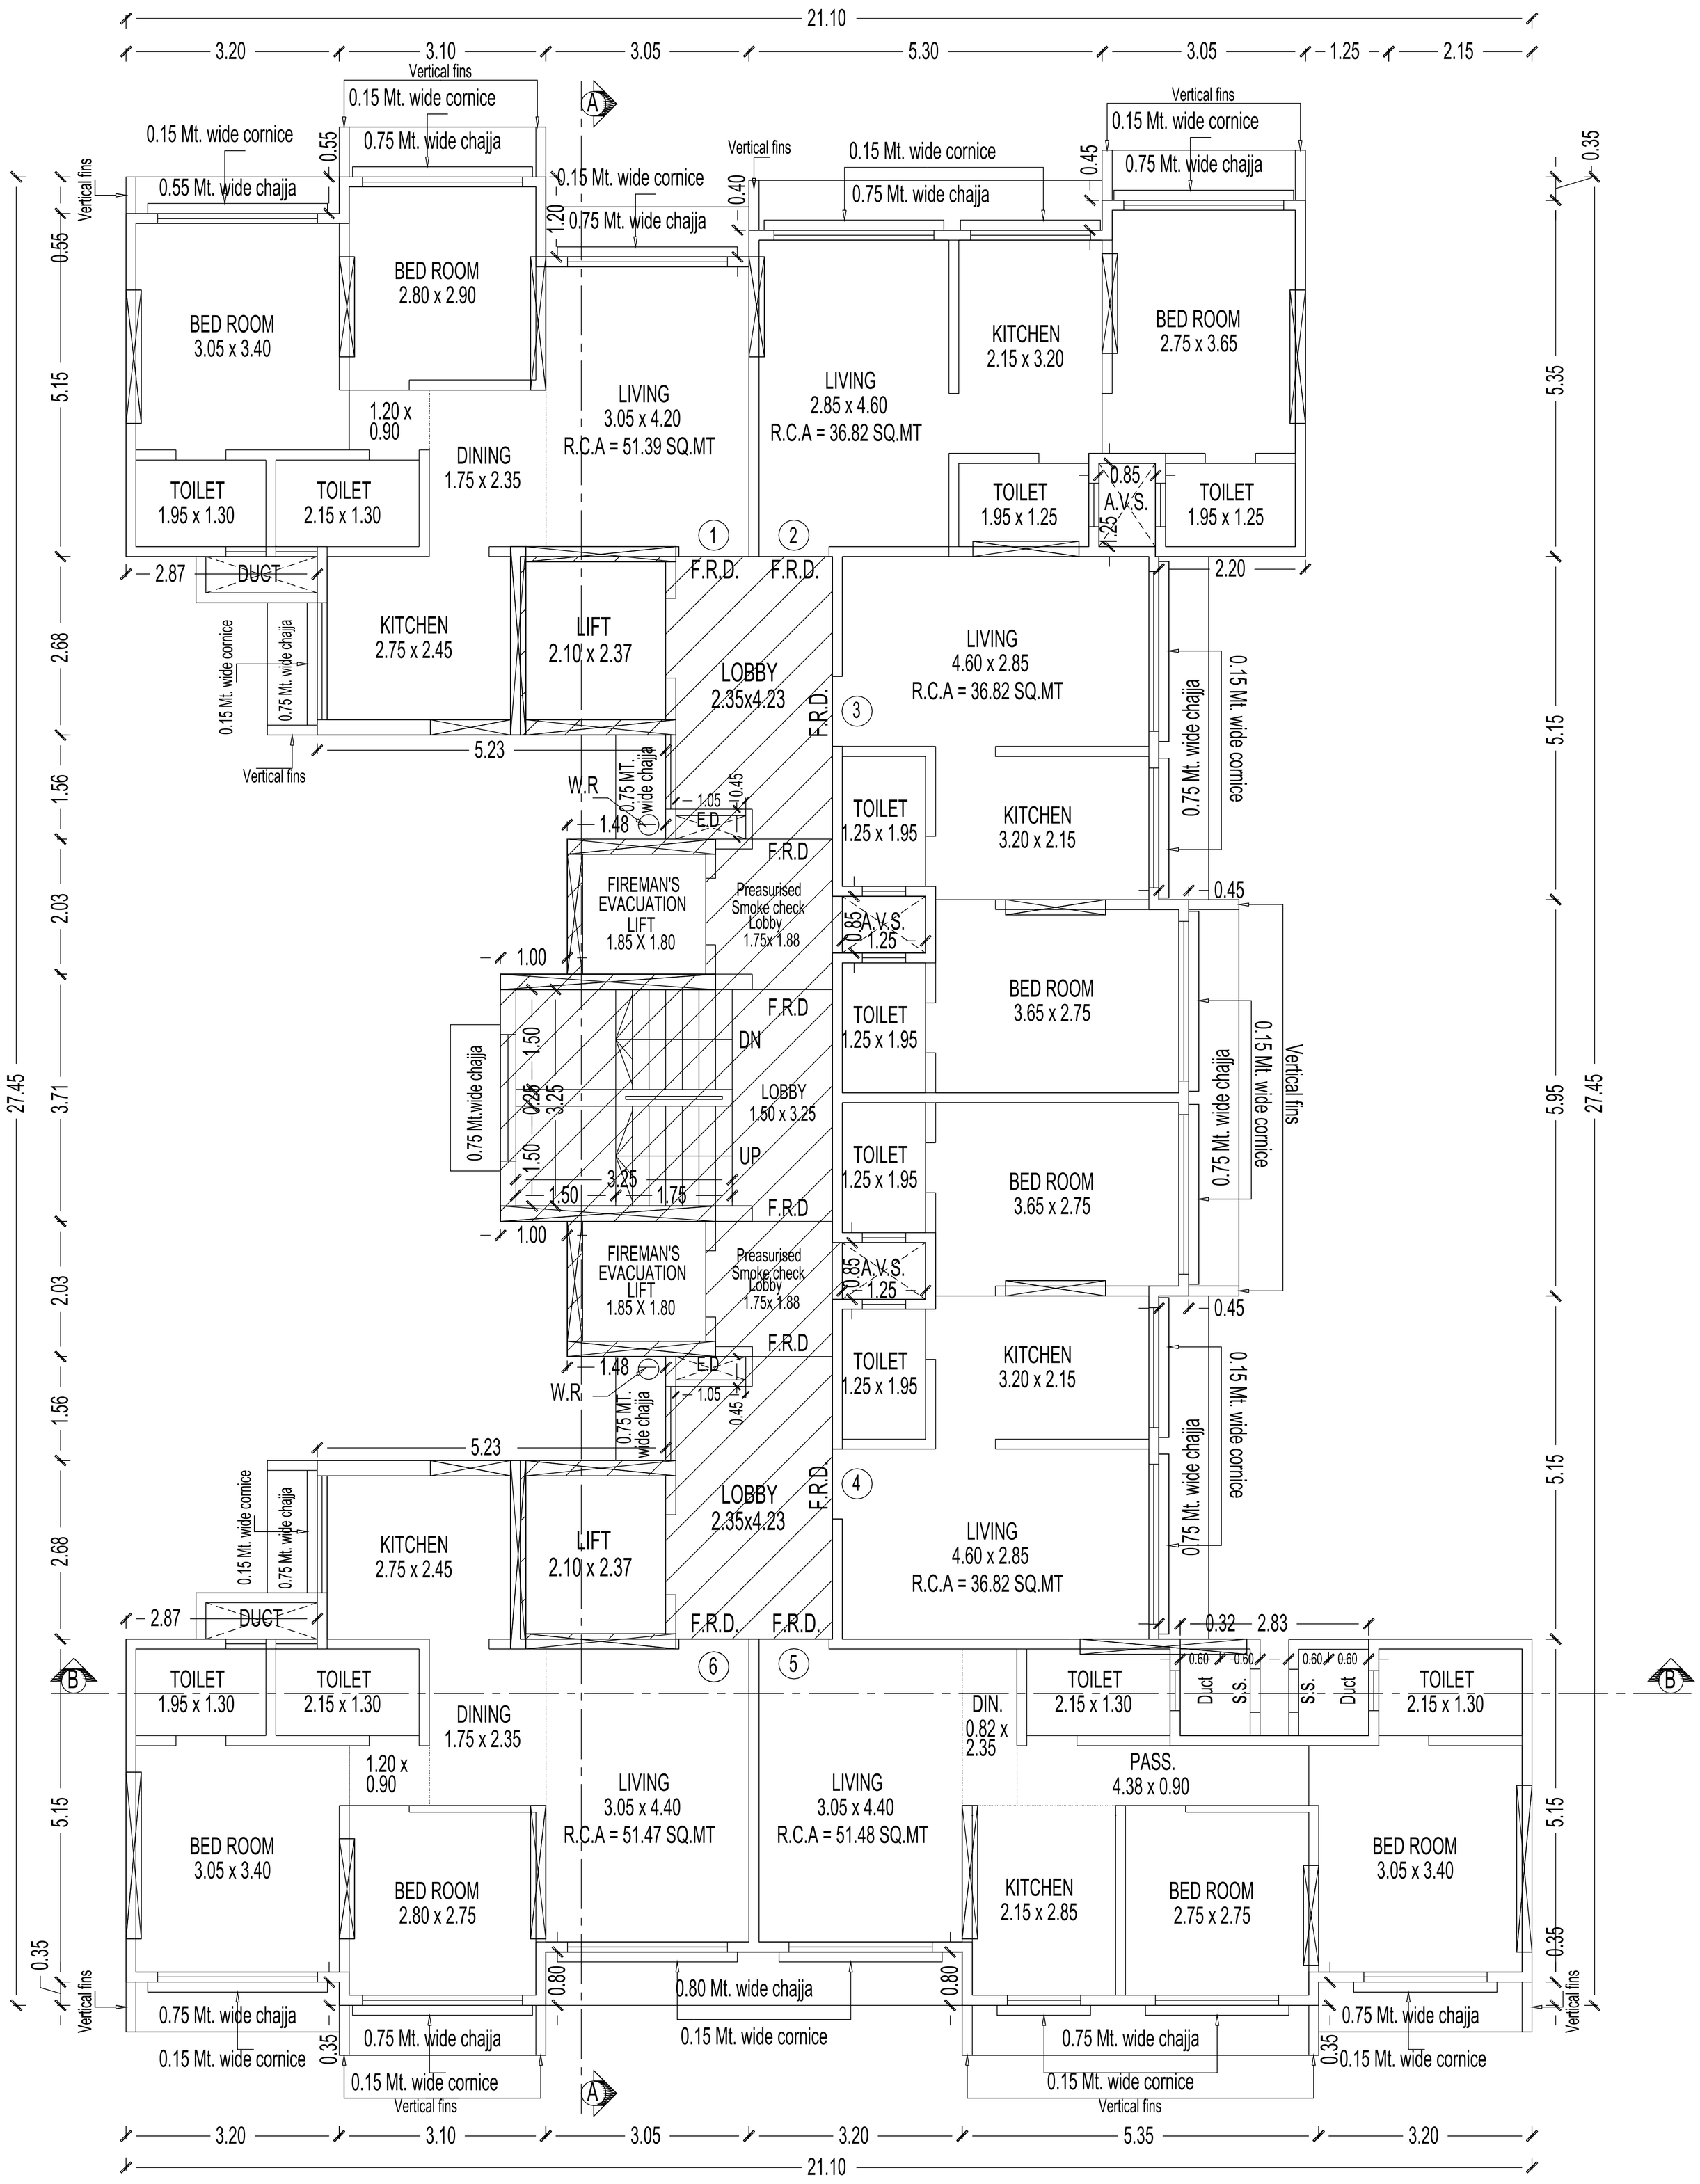

3RD & 4TH FLOOR PLAN

SCALE :- 1:100

SCALE :- 1:100

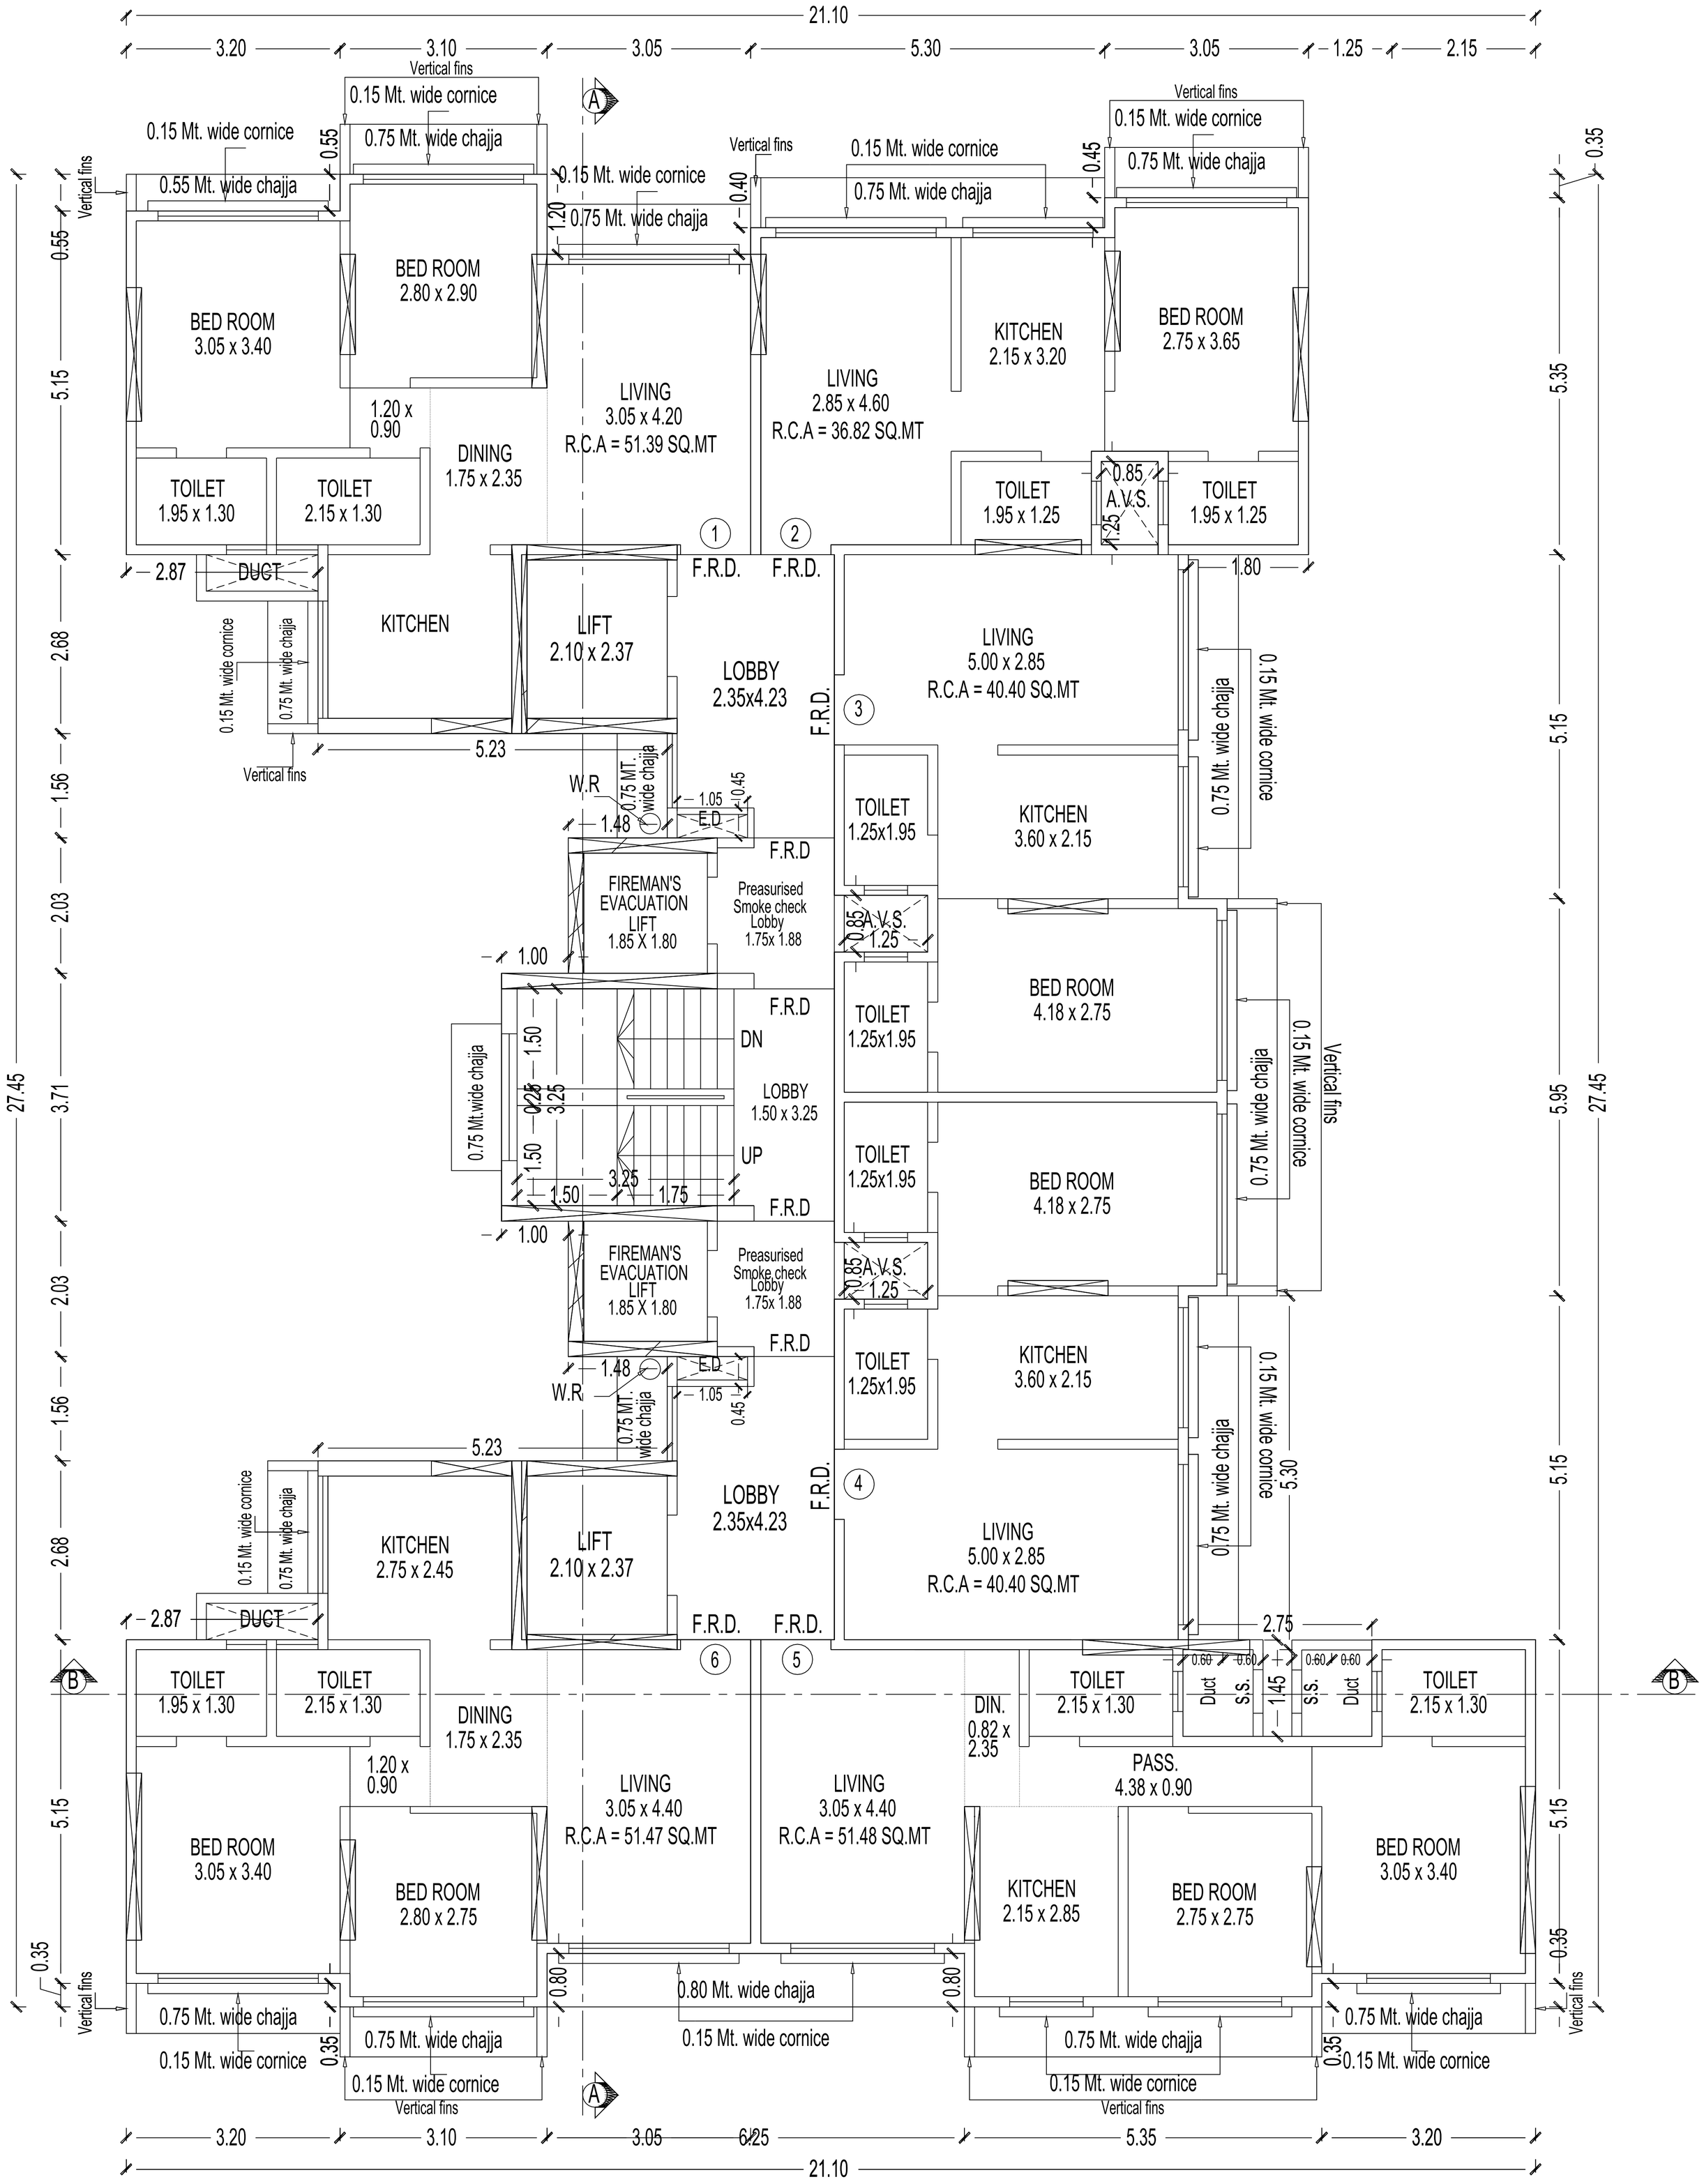


6TH FLOOR PLAN

SCALE :- 1:100

7TH FLOOR PLAN


FILE 1O? P
S +EET 1O. 03 ?09

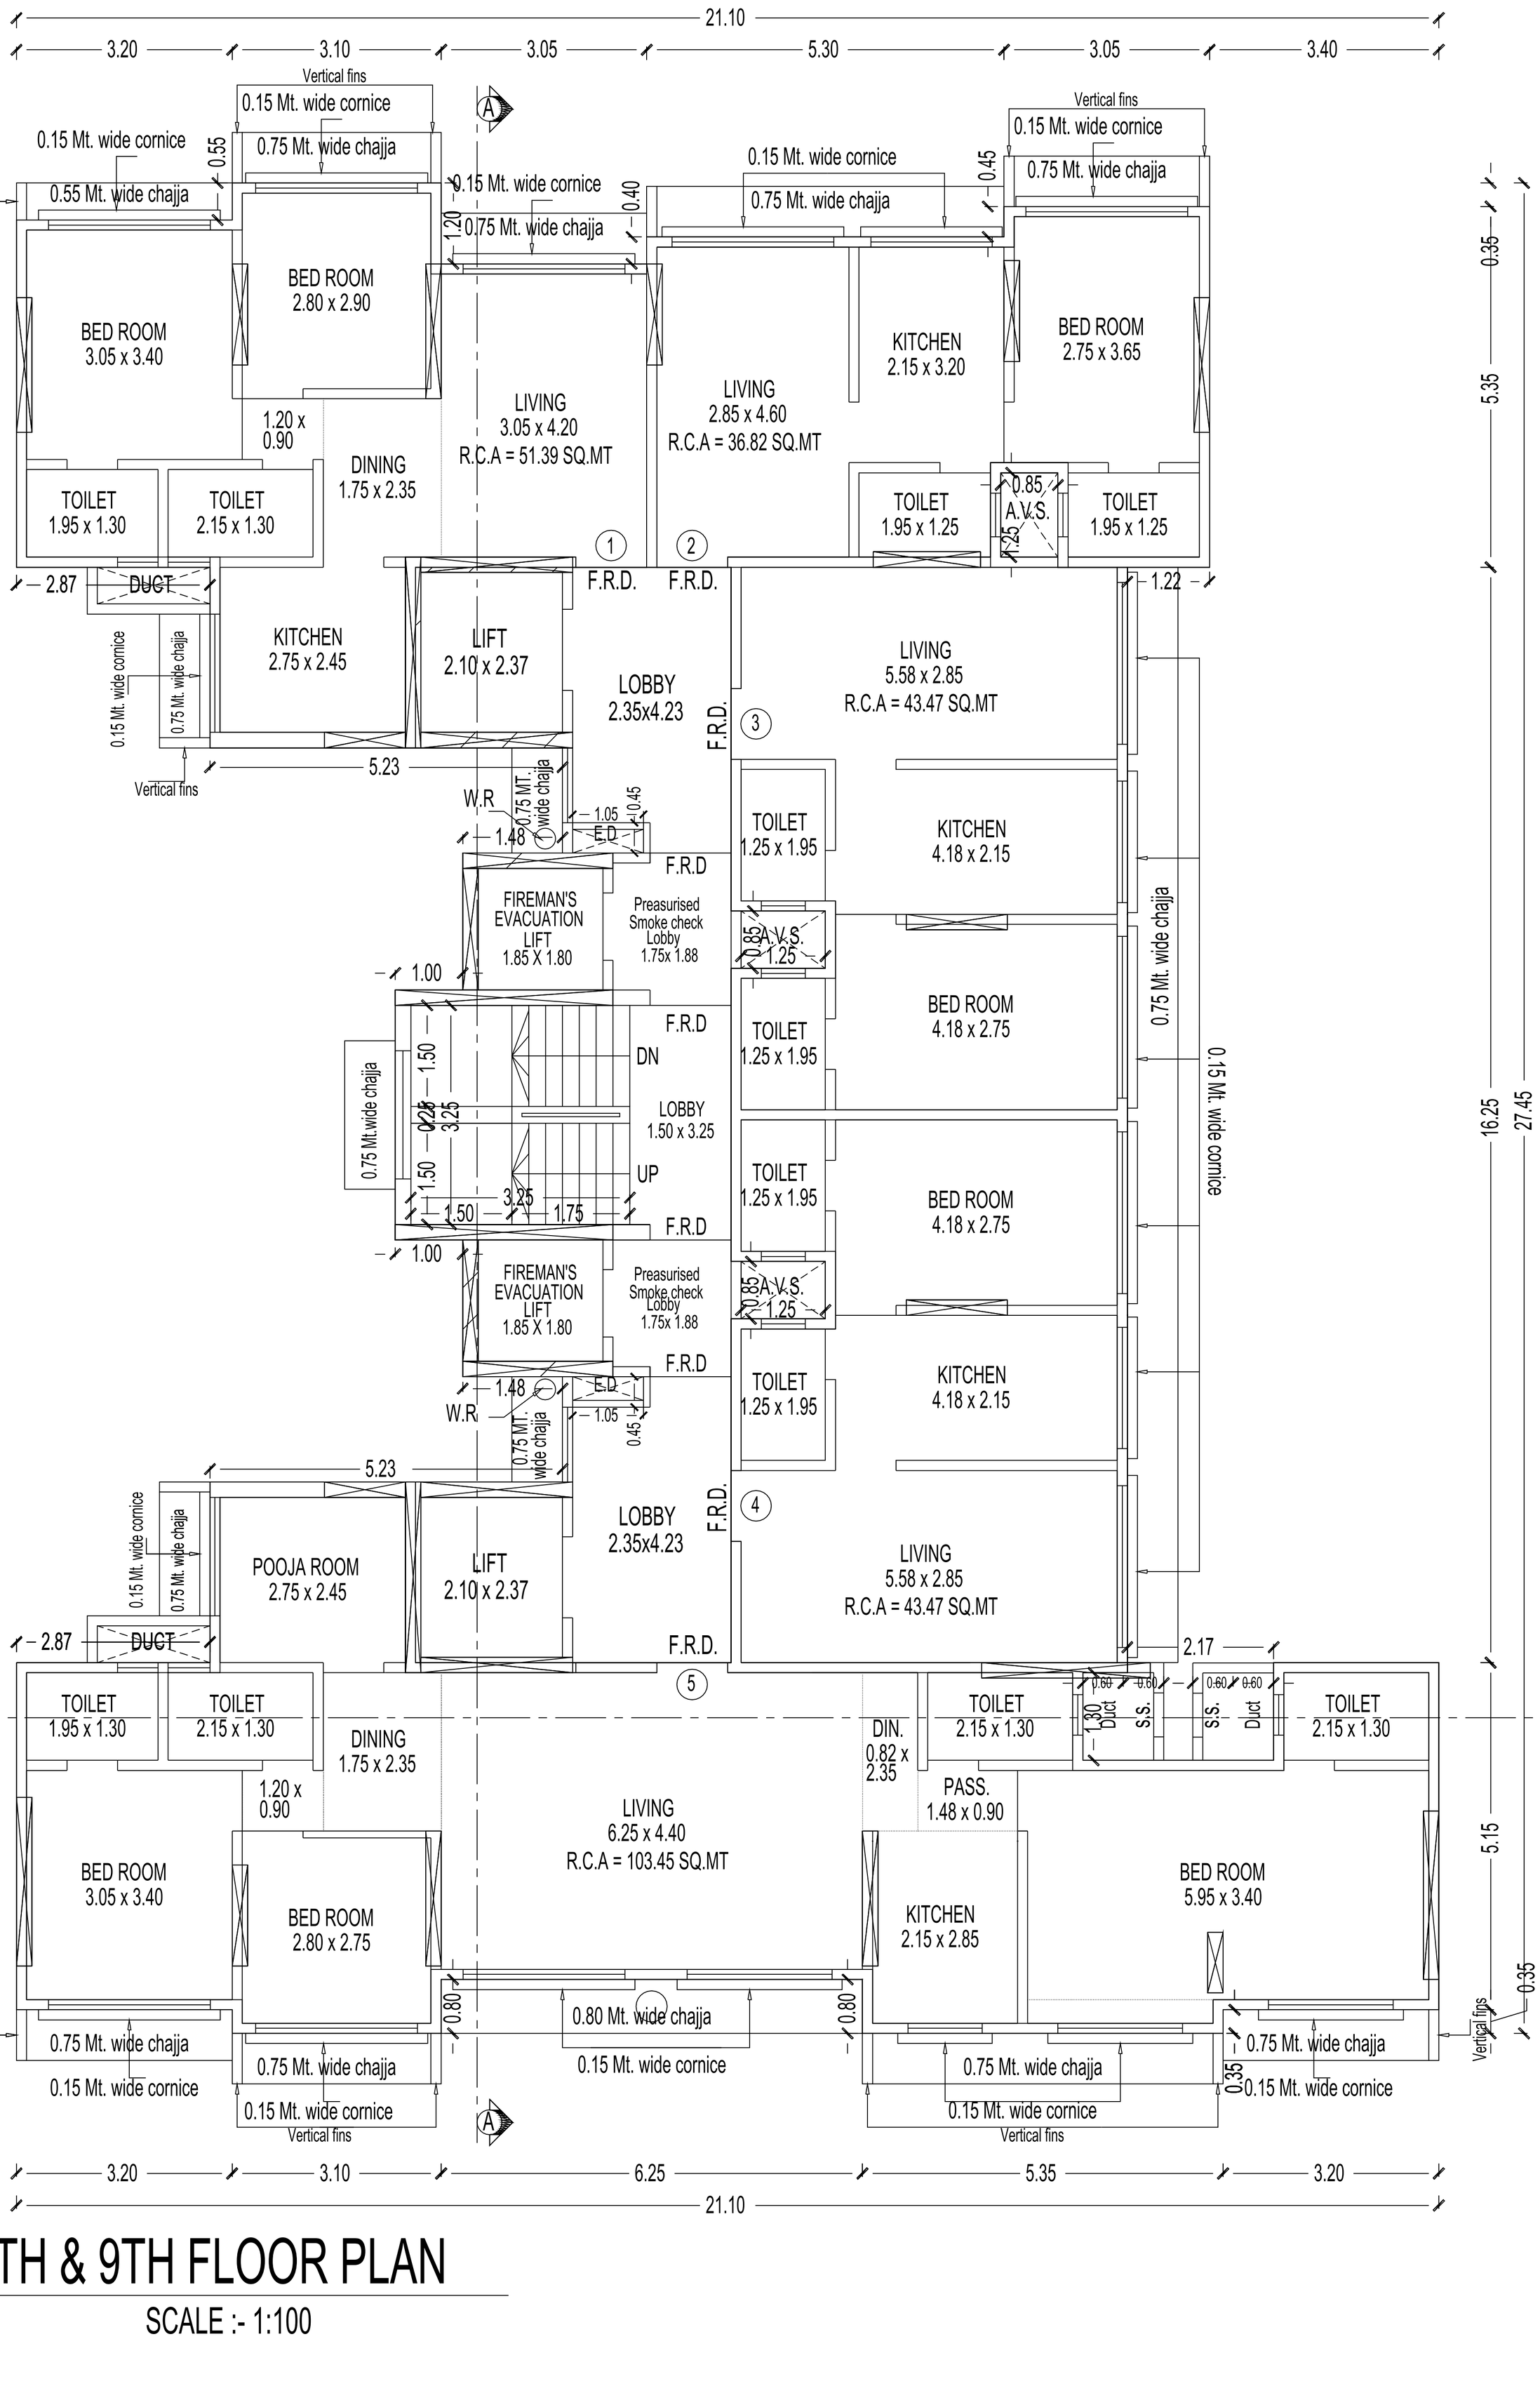

8TH & 9TH FLOOR PLAN

SCALE :- 1:100


SCALE :- 1:100

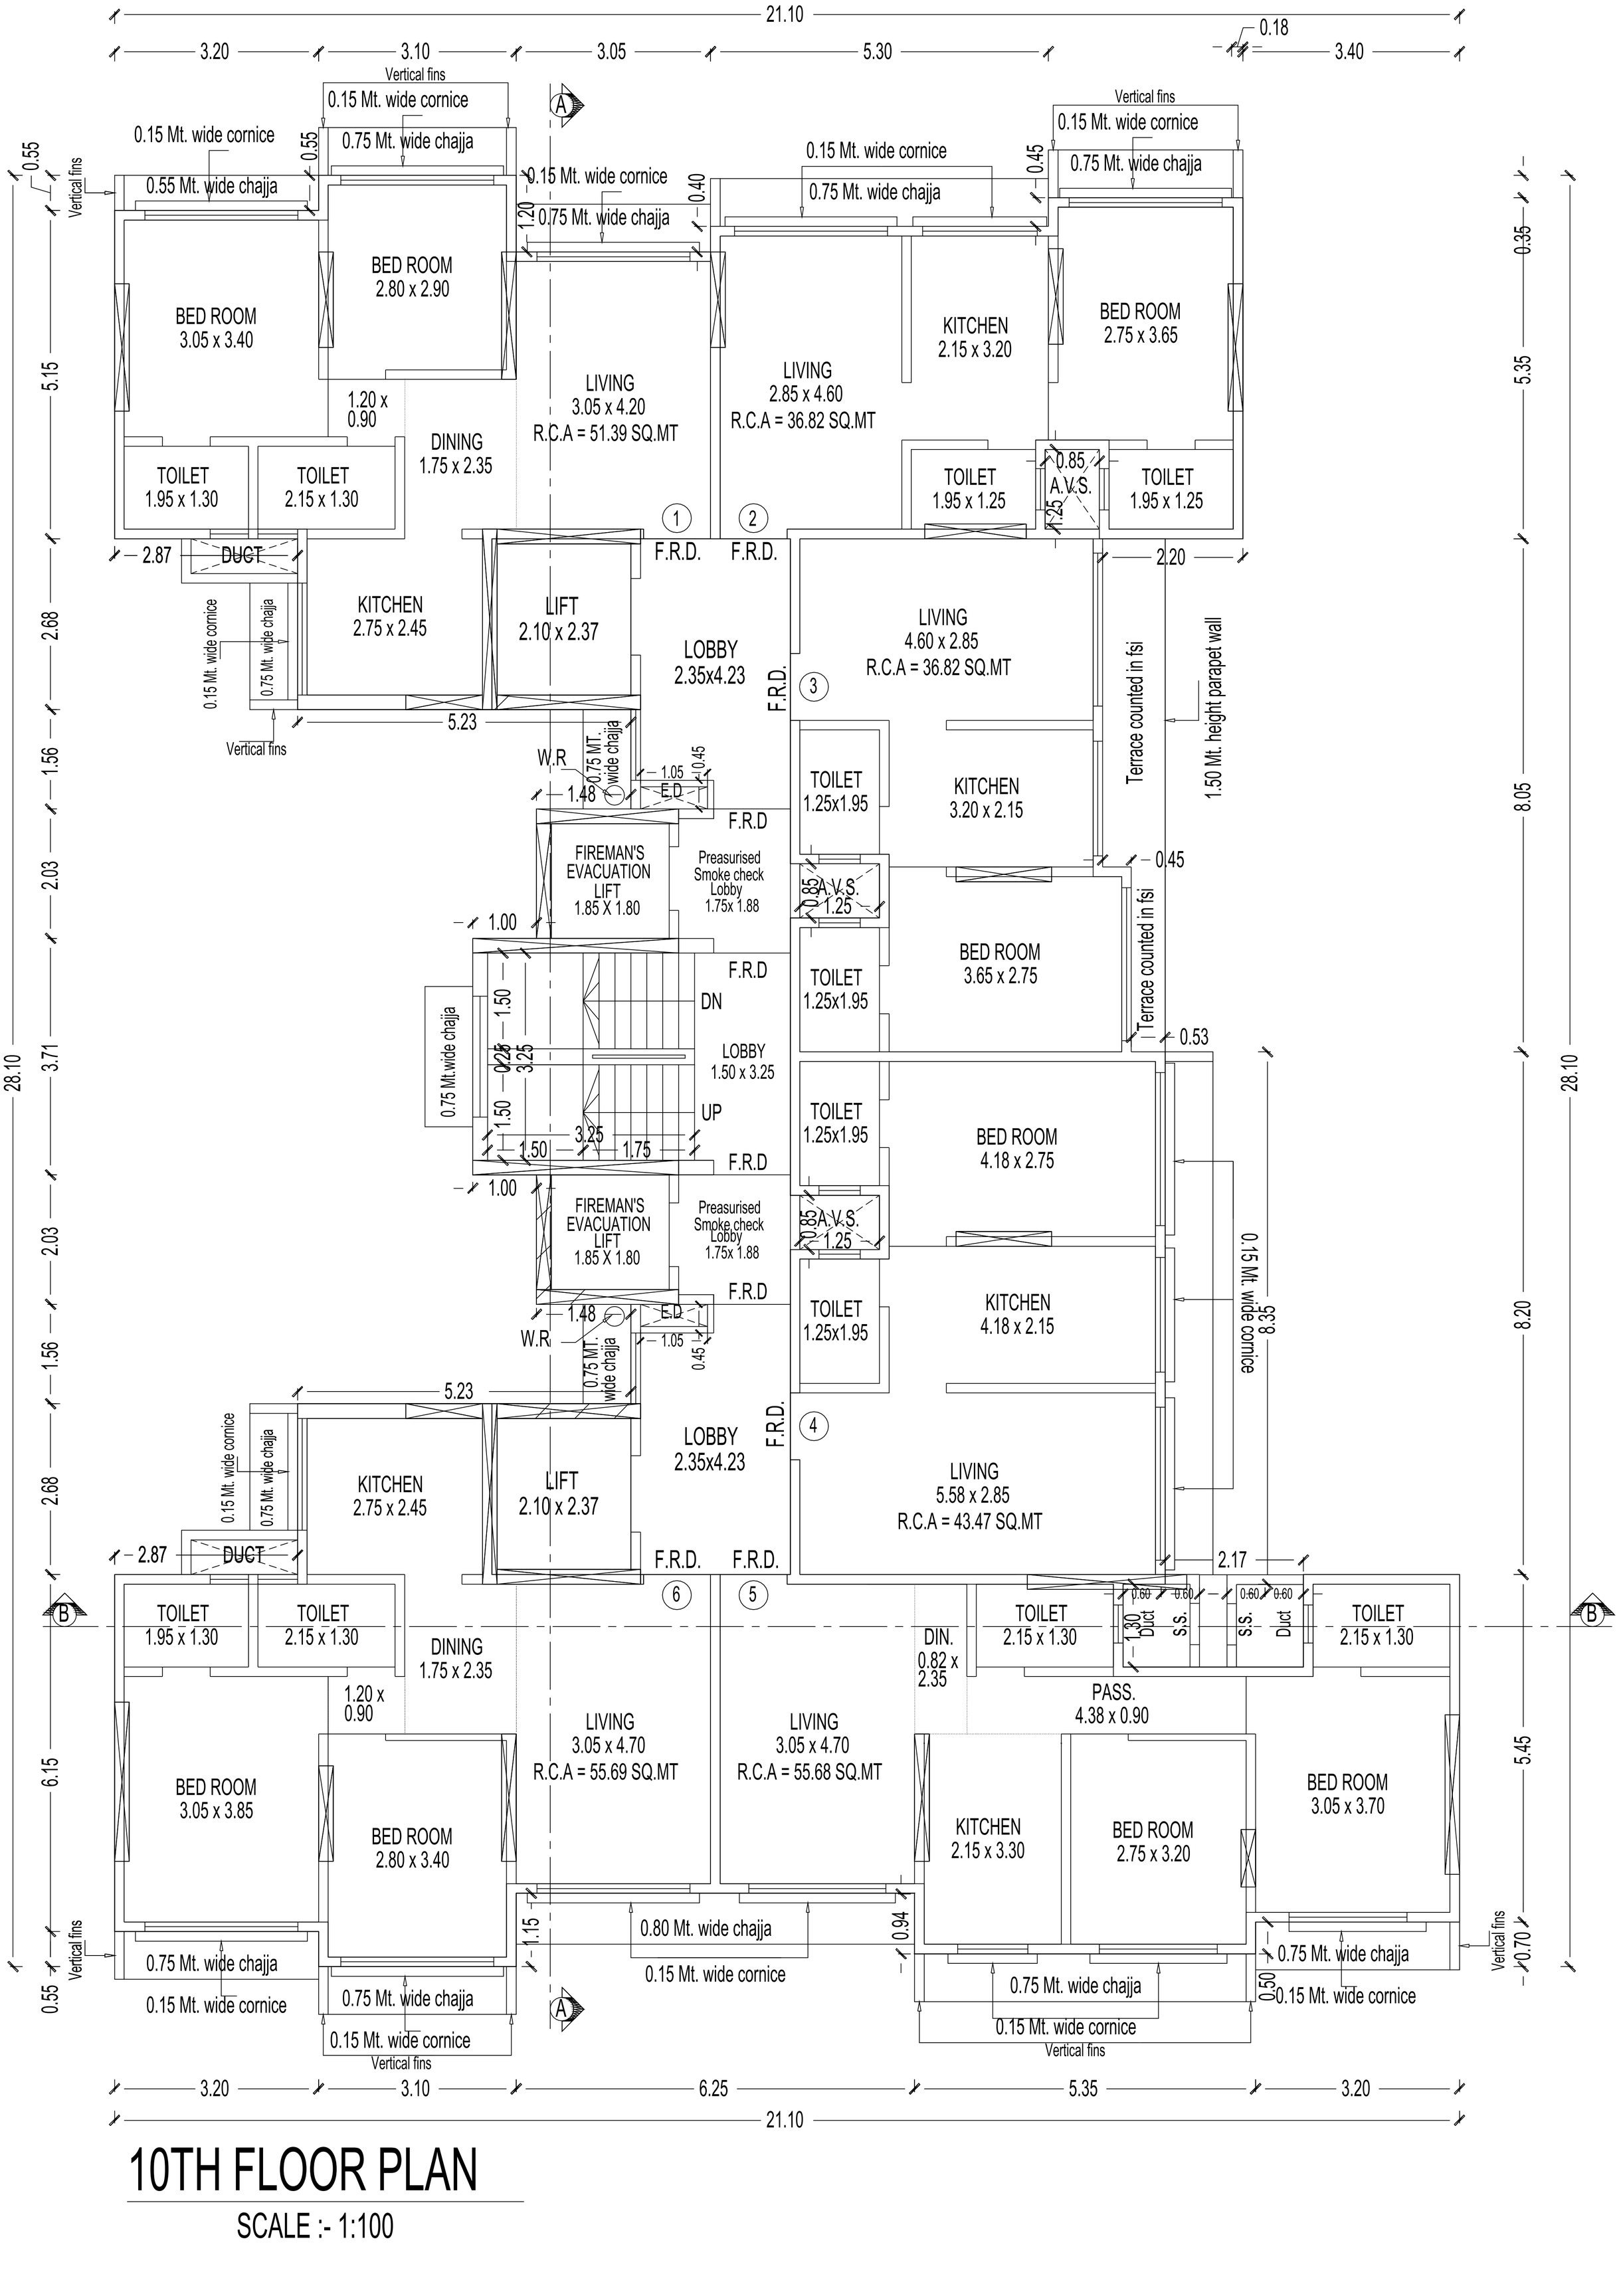

10TH FLOOR PLAN

SCALE :- 1:100

11TH FLOOR PLAN

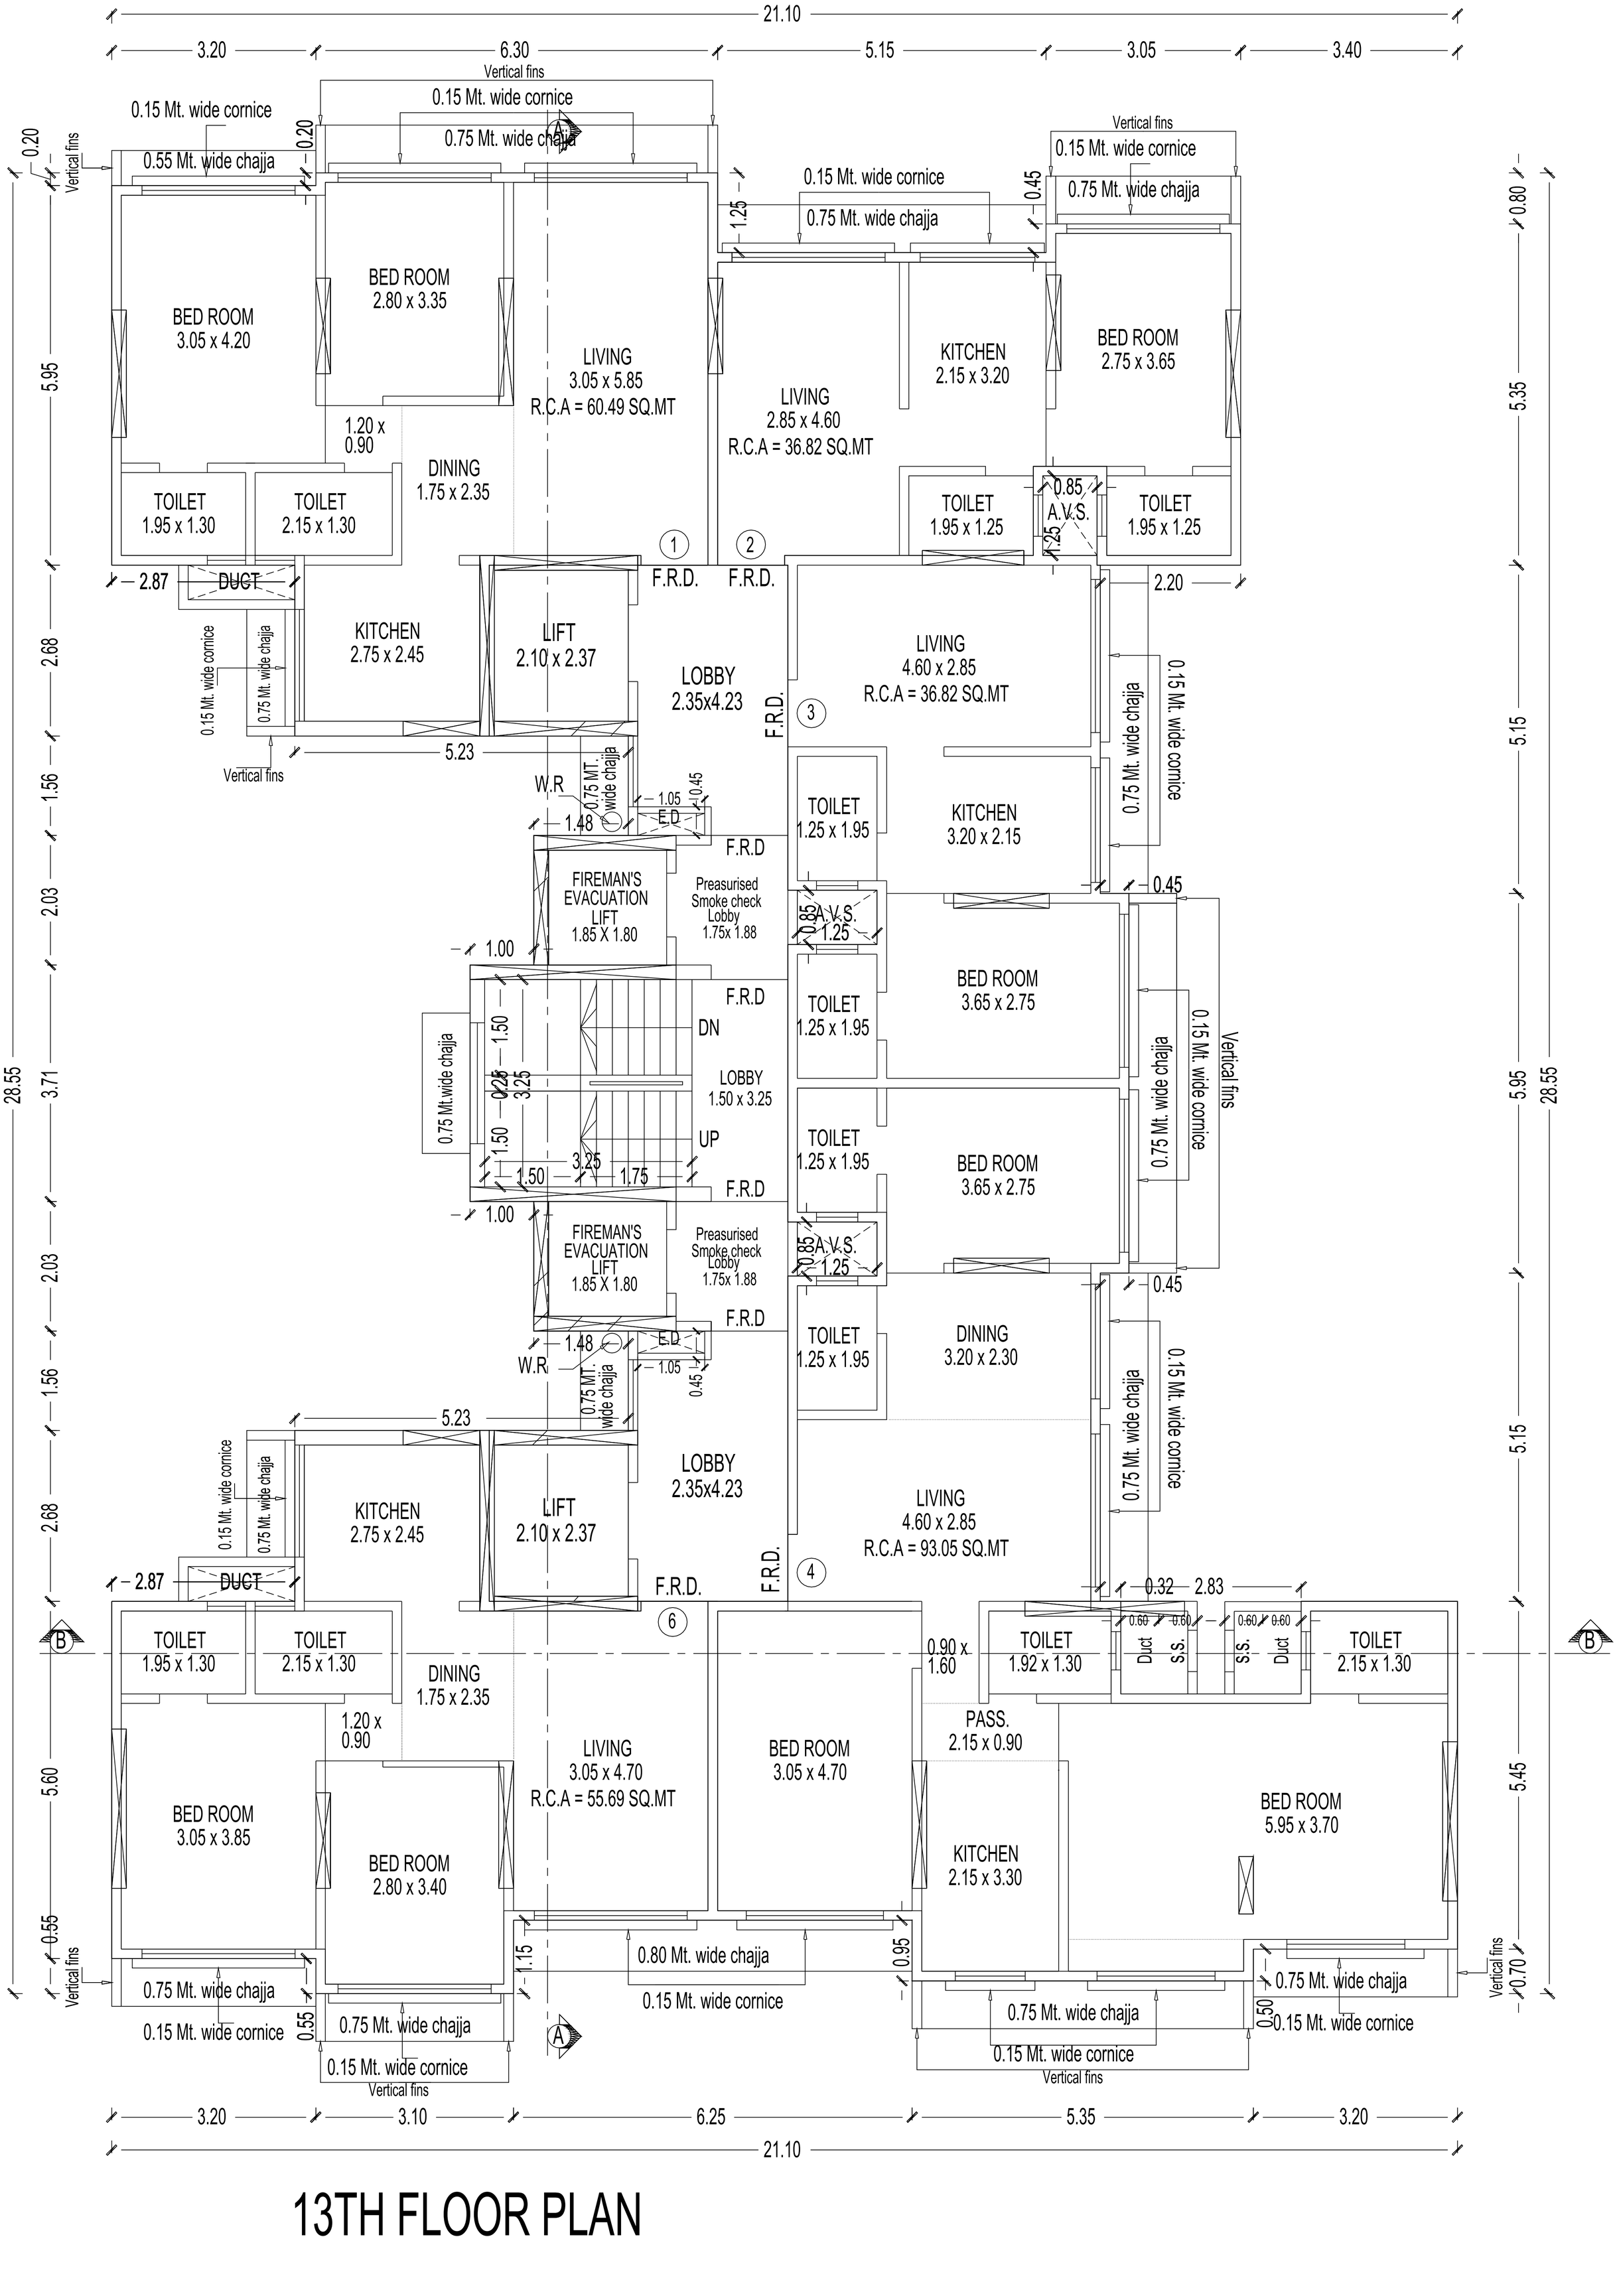

13TH FLOOR PLAN

14TH FLOOR PLAN

SCALE :- 1:100


15TH FLOOR PLAN

FILE NO ? P
S +EET NO. 04 ?09

16TH FLOOR PLAN

SCALE :- 1:100


SCALE- 1:100

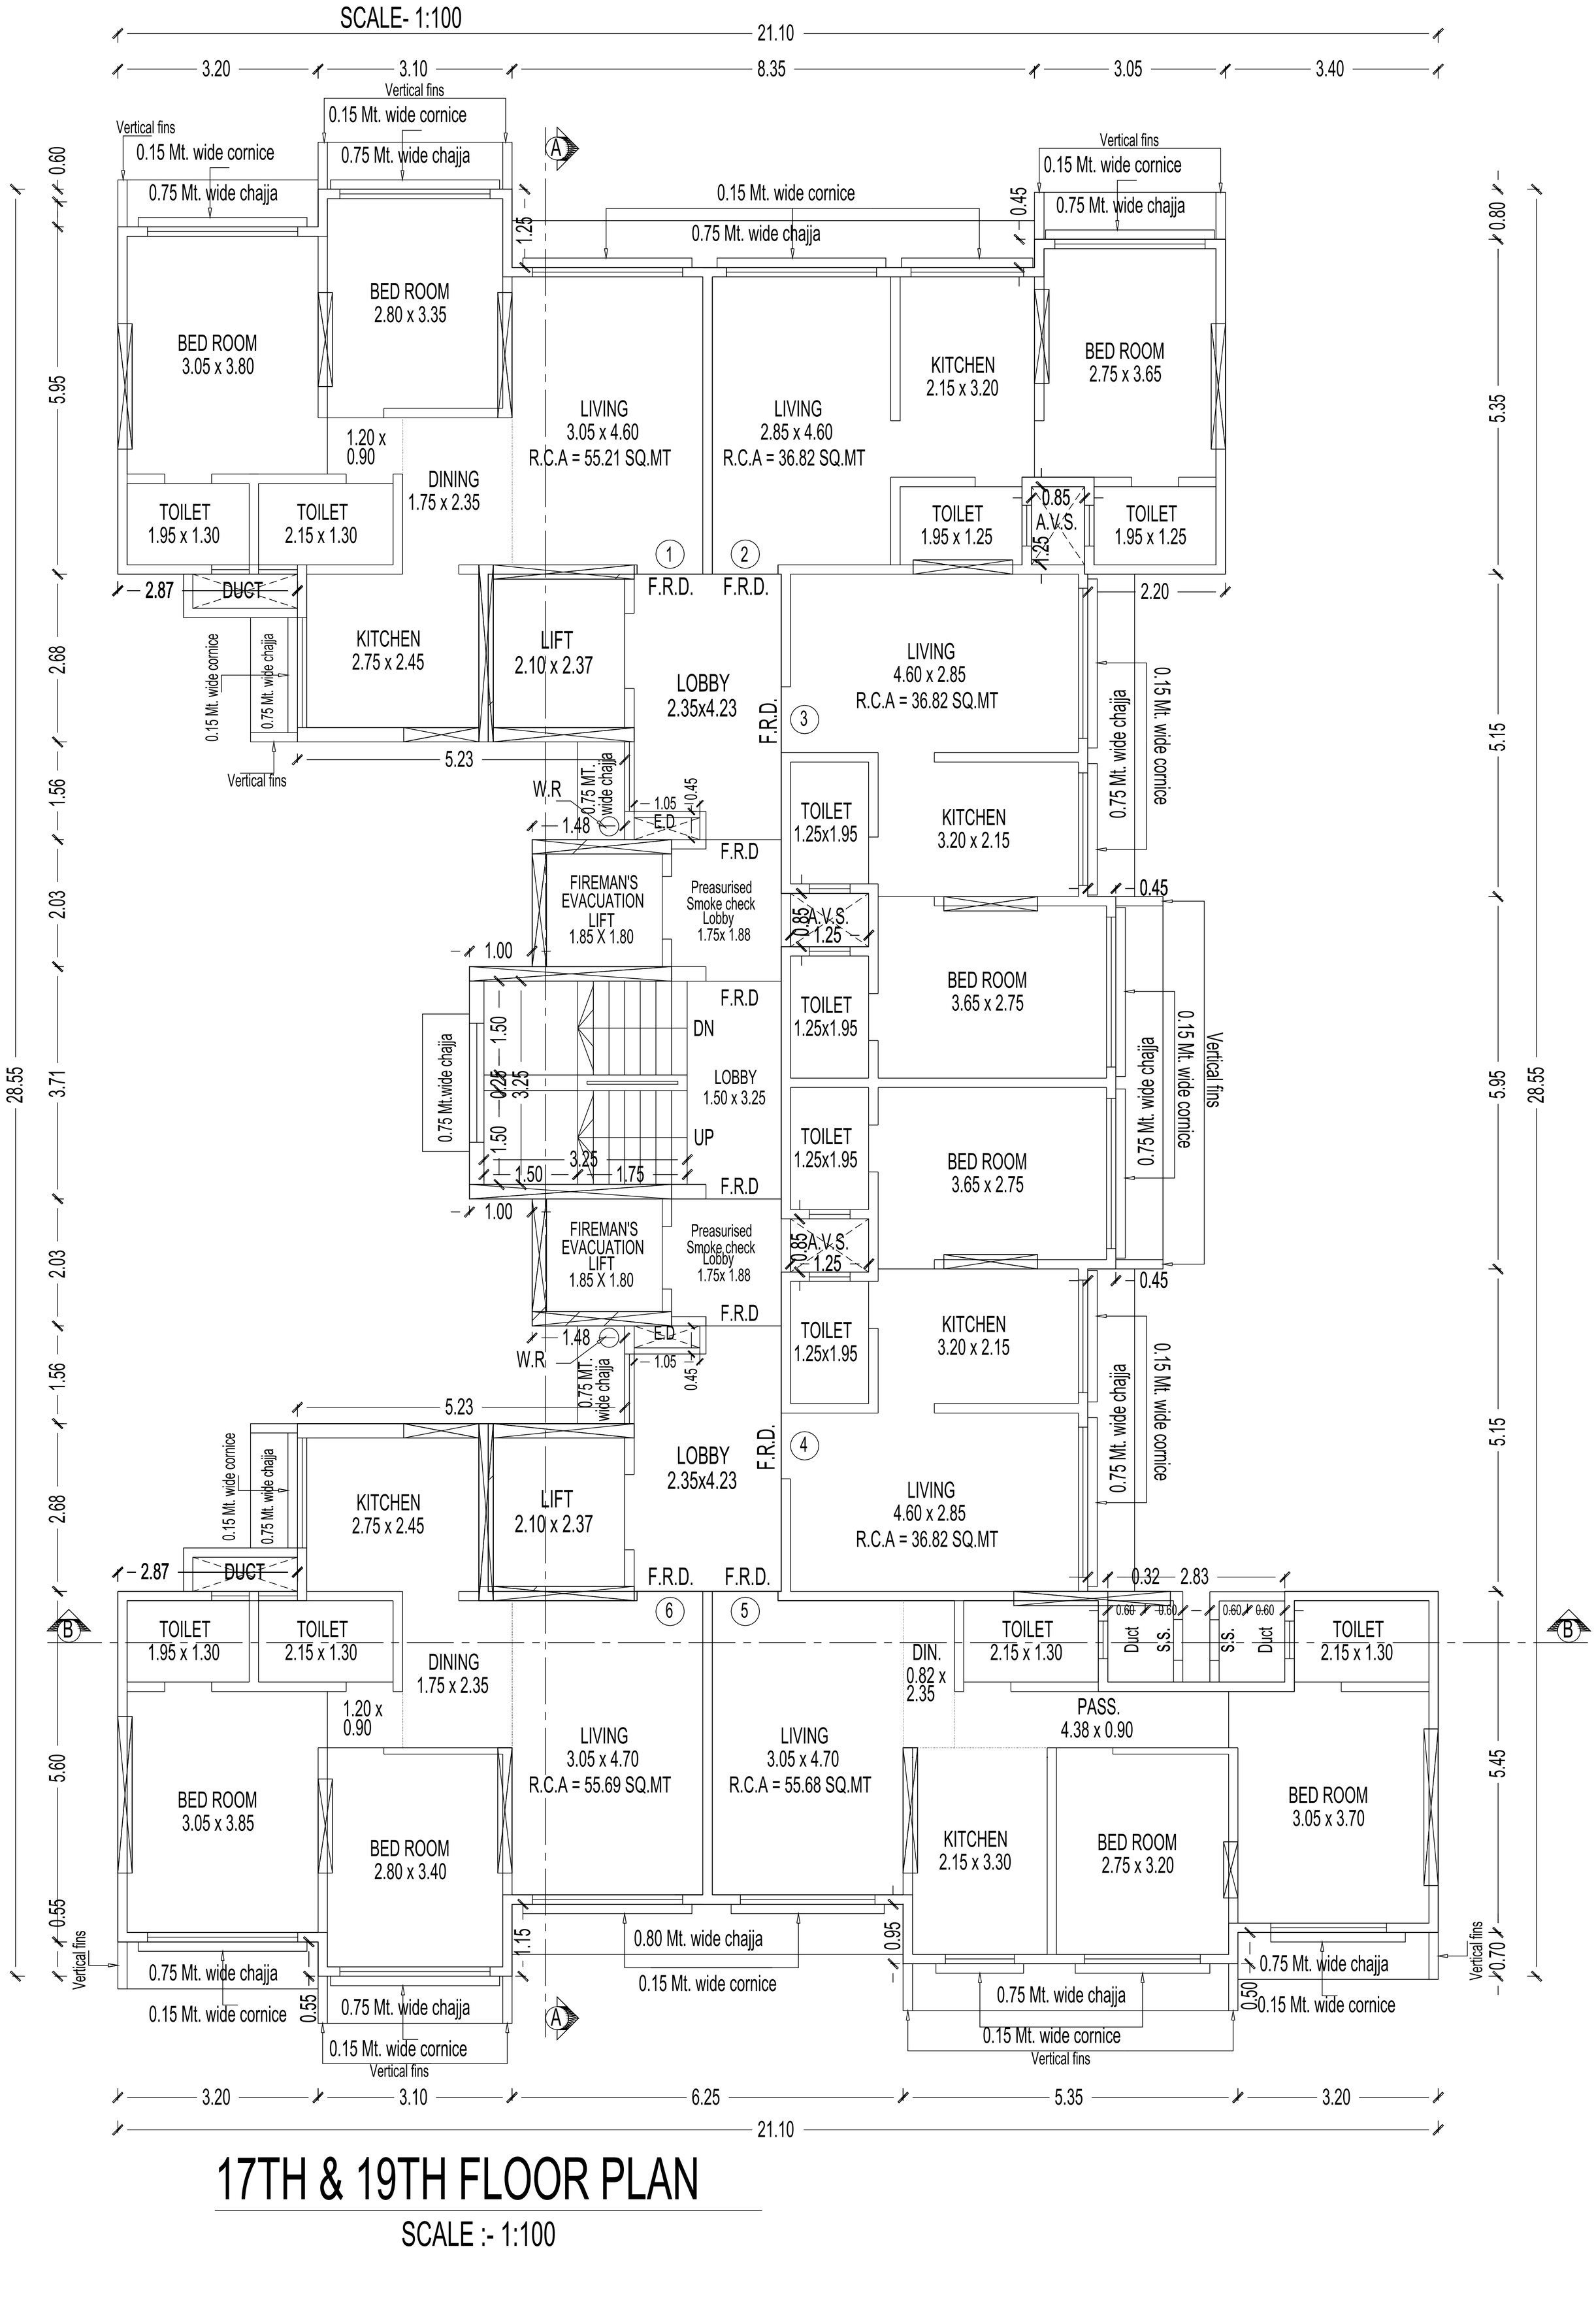

17TH & 19TH FLOOR PLAN

SCALE :- 1:100

SCALE- 1:100

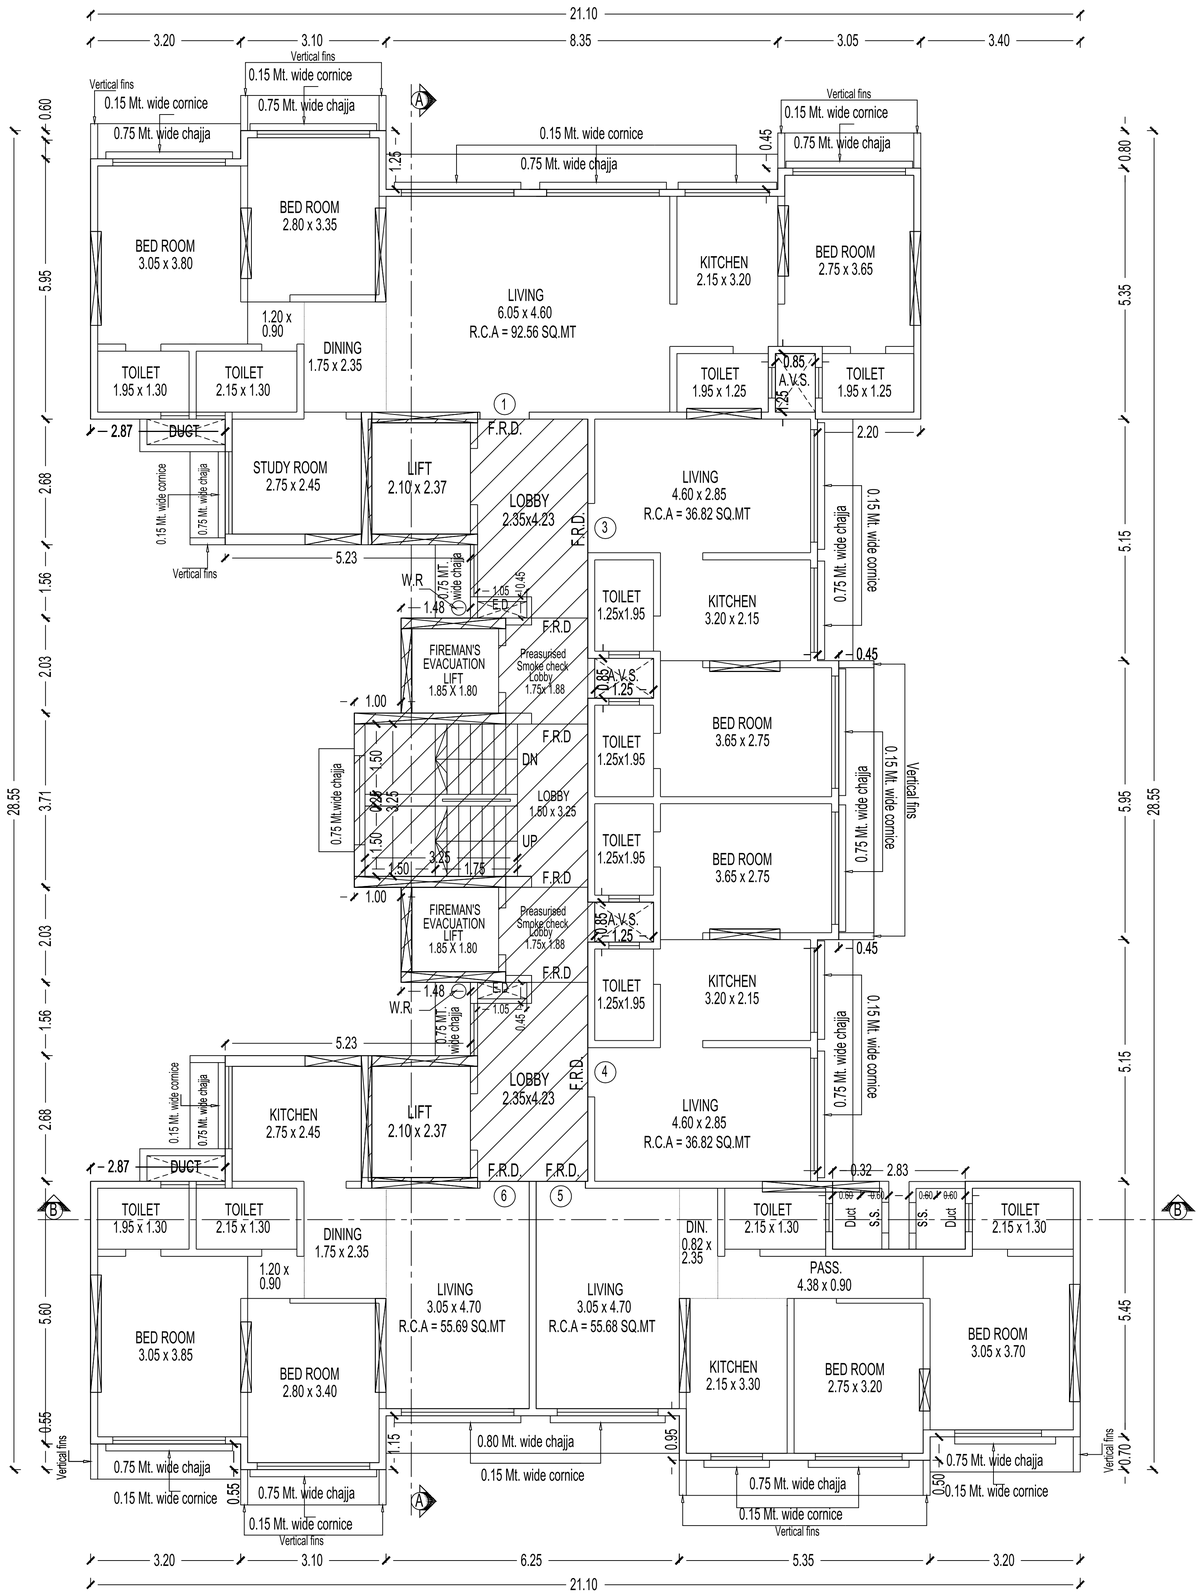

18TH FLOOR PLAN

SCALE :- 1:100

FORM -II

CONTENTS OF SHEET

FLOOR PLANS & REFUGE AREA CALCULATION

DESCRIPTION OF P