45.50 MT. WIDE D.P ROAD
SOUTH

EAST

WEST

NORTH
18.30 MT. WIDE D.P ROAD

SET BACK AREA

CHANGE AS PER FINAL PROFORMA

FITNESS CENTER AREA
25.00 X 18.77

PERMISSIBLE FITNESS CENTER BUILT UP AREA
TOTAL PROPOSED BUA = 2458.55 X 2 / 100 = 489.88 SQ.MT.
FITNESS CENTER AREA PERMISSIBLE = 489.88 SQ.MT.
TOTAL PROPOSED AREA = 489.82 SQ.MT.

MIN.1.50M WIDTH

DECK
28.08 X 13.40
+6.15 MT. LVL

C - WING
2.00 M. W. PASS

B - WING

A - WING
2.00 M. W. PASS

D - WING

SOCIETY OFFICE
2.74 X 3.80
AREA - 19.98 SQ.MT.

LIFT 2.37 X 2.37

LIFT 2.30 X 2.30

LIFT 2.30 X 2.20

FIRE LIFT 2.75 X 2.10

KITCHEN 3.77 X 3.13

KITCHEN 3.77 X 3.18

LOBBY 2.74 X 3.80

LOBBY 2.74 X 3.65

SMOKE CHECK LOBBY 2.30 X 2.20

CHECK LOBBY 2.30 X 2.20

STORE 2.10 X 1.75

LIVING 5.63 X 4.13
RERA CARPET 130.17 SQ.MT.

DINING 3.55 X 3.20

LIVING 5.63 X 3.95
RERA CARPET 129.71 SQ.MT.

DINING 3.55 X 3.20

BED RM 4.72 X 3.77

BED RM 4.72 X 3.65

BED RM 4.58 X 3.78

BED RM 4.58 X 3.65

BED RM 3.32 X 3.65

TOILET 1.53 X 2.55

TOI. 1.53 X 2.45

TOI. 1.53 X 2.55

PASS 1.16 X 3.78

DOUBLE HEIGHT

BLDG LINE ABOVE

CANOPY ABOVE

1.20 M.W. CHAJJA

CHAJJA

ELECT. SHAFT

SPACE FOR LIFT

UP

DN

FRD

AVS

CO1

CO2

CO3

CO4

CO5

CO6

1ST FLOOR PLAN
SCALE:-1:100

1ST FLOOR PLAN
SCALE:-1:100

hatch AH&RR tenaments

45.50 MT. WIDE D.P ROAD

SOUTH

EAST

WEST

TERRACE
OPEN TO SKY

DECK BELOW

C - WING
2.00 M. W. PASS

B - WING
2.00 M. W. PASS

A - WING
2.00 M. W. PASS

D - WING

SET BACK AREA

2ND FLOOR PLAN
SCALE:-1:100

NORTH
18.30 MT. WIDE D.P ROAD

2ND FLOOR PLAN
SCALE:-1:100

45.50 MT. WIDE D.P ROAD
SOUTH

EAST

WEST


NORTH

18.30 MT. WIDE D.P ROAD

3RD TO 6TH & 8TH, 9TH FLOOR PLAN
SCALE:-1:100

3RD TO 5TH FLOOR PLAN
SCALE:-1:100

SET BACK AREA

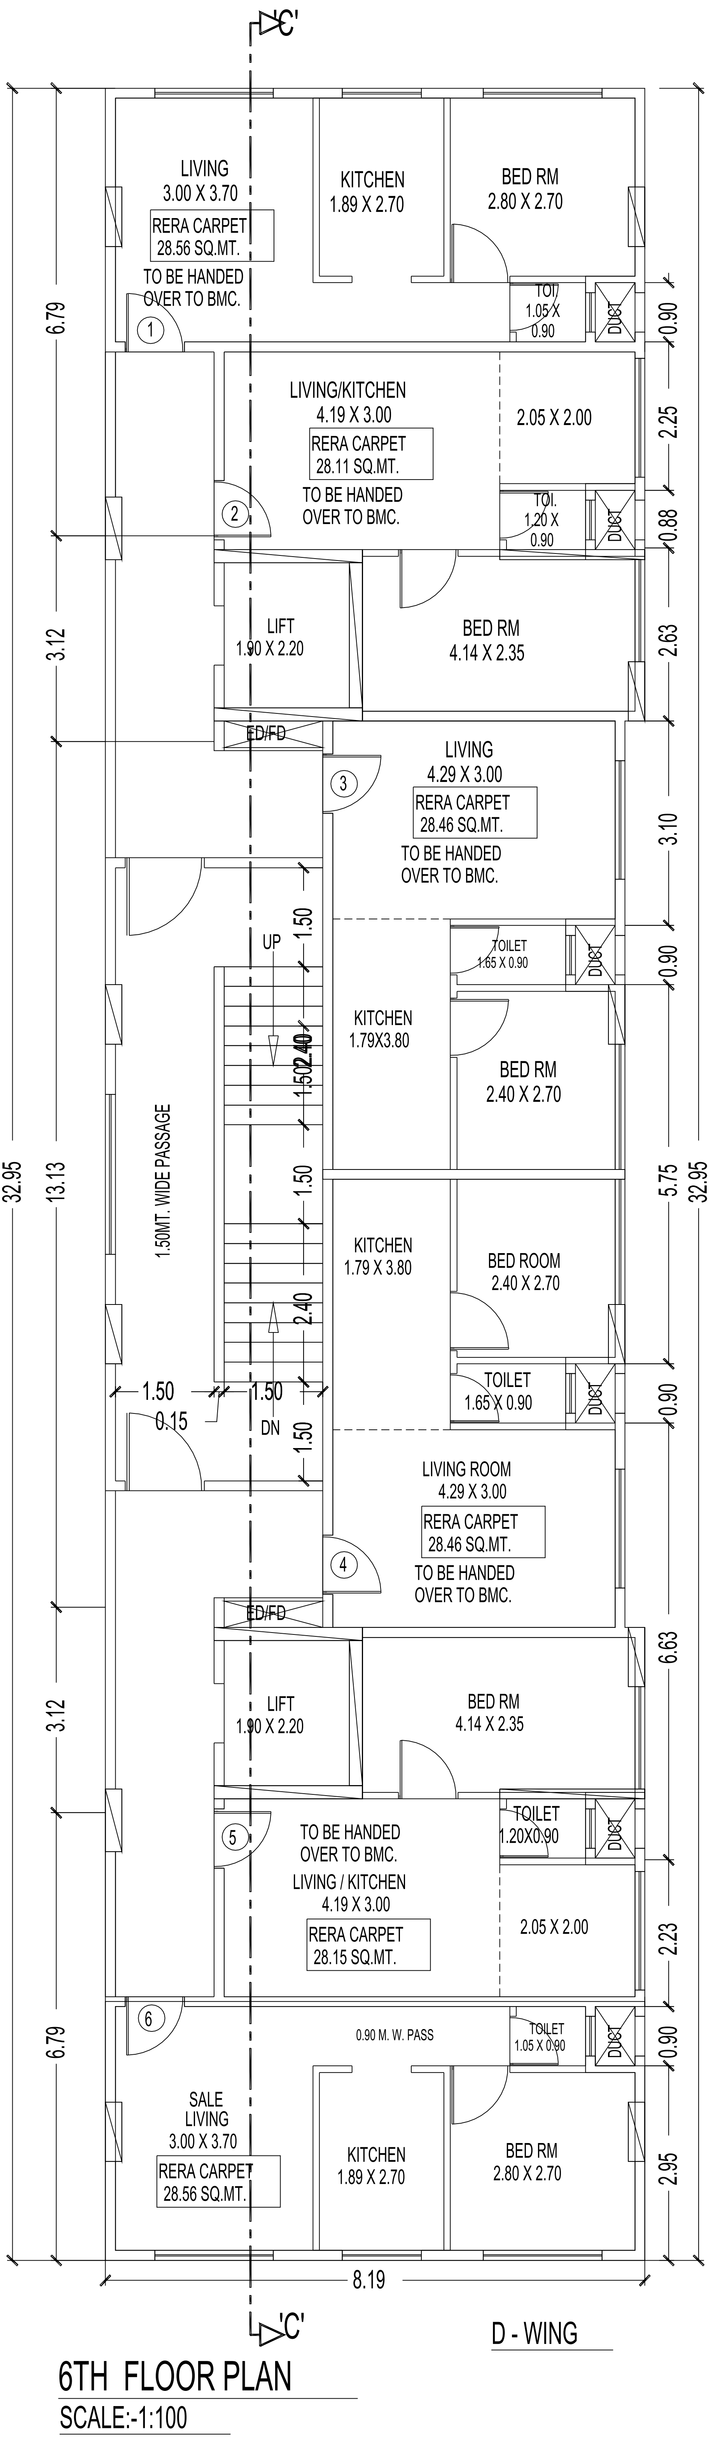

D - WING

6TH FLOOR PLAN

SCALE:-1:100

45.50 MT. WIDE D.P ROAD
SOUTH

EAST

WEST

provide toilet and drinking facility

SET BACK AREA

NORTH
18.30 MT. WIDE D.P ROAD

7TH REFUGE FLOOR PLAN
SCALE:-1:100

7TH FLOOR PLAN
SCALE:-1:100

45.50 MT. WIDE D.P ROAD

SOUTH

EAST

WEST

NORTH

18.30 MT. WIDE D.P ROAD

SET BACK AREA

25TH FLOOR PLAN

SCALE:-1:100

BMC FILE NO. P-22854/2024/(629/1258)/H/E Ward/BANDRA-EAST (6/19)

PROFORMA - B

PLANS FOR CONSIDERATION

DNYANESHWAR BHIMRAO BANDGAR

S.E.(BP)H/W-NE

SHAIKH ASIF MUSA

A.E.(BP)H

Digitally signed by SHAIKH ASIF MUSA
DN: cn=IN, o=BRIHANMUMBAI MUNICIPAL CORPORATION, ou=BUILDING PROPOSAL, 2.5.4.20=5539de2bd5ae44a2b2f25b61dca5e5897707eb4aee82267fbd971e6f0b8e8955, serialNumber=e8f37744f30a3981b8970193b05e28024d497bf41b397a79d5bf1e6f0b8e8955, cn=SHAIKH ASIF MUSA
Date: 2024.12.17 20:53:42 +05'30'

NAME AND ADD. OF L. S.

NAVIN VATNANI
LICENSED SURVEYOR

51, SWASTIK PLAZA, SECOND FLOOR,
V. L. MEHTA ROAD, J.V.P.D. SCHEME,
VILE PARLE (WEST), MUMBAI- 400049

SIGNATURE OF L. S.

NAVIN JAIKRISHA N VATNANI
Digitally signed by NAVIN JAIKRISHNA VATNANI
Date: 2024.12.13 17:48:26 +05'30'

CONTENTS OF SHEET

25TH FLOOR PLAN.
DIAGRAM & CALCULATION.

DESCRIPTION OF PROPOSAL AND PROPERTY

PROPOSED REDEVELOPMENT ON PLOT BEARING CTS NO. 629/1258 OF VILLAGE BANDRA (EAST) AT M KELKAR MARG, BANDRA (E). MUMBAI

NAME AND ADD. OF APPLICANT

M/s. ARHAN HOMES LLP, CA to Owner.

SIGN. OF APPLICANT

ABHAY SHYAMSUNDER CHANDAK
Digitally signed by ABHAY SHYAMSUNDER CHANDAK
Date: 2024.12.13 17:32:58 +05'30'

DRG.NO.	SCALE	DATE	DRN.BY.	CHKD.BY.
	AS SHOWN			