



A
A'
B
B'
D
D'
19.35
1.15
2.95
2.45
6.25
2.45
2.95
1.15
S.S.
TOILET
2.35 x 1.35
CHAJJA
STANDING COLUMN
BED ROOM
3.65 x 3.05
KITCHEN
2.15 x 3.45
KITCHEN
2.15 x 3.25
CORNICE
F.R.D.
TOILET
2.15 x 1.20
PASSAGE
1.20 x 0.90
BED ROOM
3.35 x 2.90
LIVING/DINING
5.50 x 3.95
R.C.A. = 61.40 SQ.MT.
LIVING/DINING
5.50 x 4.10
R.C.A. = 61.45 SQ.MT.
01
02
FINS
LIFT
2.95 x 2.10
LIFT
2.95 x 2.15
M.S. A.C. PLATFORM
TIE BEAM AT
1.00 M. BELOW
FLOOR LEVEL
TIE BEAM
COUNTED IN FSI
COLUMN
COUNTED IN FSI
R.C.C. WALL
BED ROOM
3.05 x 3.70
TOILET
2.15 x 1.20
AVS
KITCHEN
2.05 x 3.05
PASSAGE
3.35 x 0.90
TOILET
2.00 x 1.20
VERTICAL BOXING
UP
FIREMEN
EVACUATION
LIFT
2.60 x 2.05
SMOKE
CHECK
LOBBY
3.80 x 2.05
LIVING
3.65 x 2.90
R.C.A. = 38.06 SQ.MT.
03
STRETCHER
LIFT
2.75 x 2.00
LOBBY
2.25 x 26.29
04
LIVING
3.80 x 2.90
R.C.A. = 38.06 SQ.MT.
BED ROOM
3.05 x 3.60
45.39
7.25
4.55
3.05
1.98
4.90
7.51
5.45
7.80
2.87
3.07
3.20
1.65
1.50
06
05
5th FLOOR PLAN
SCALE 1:100

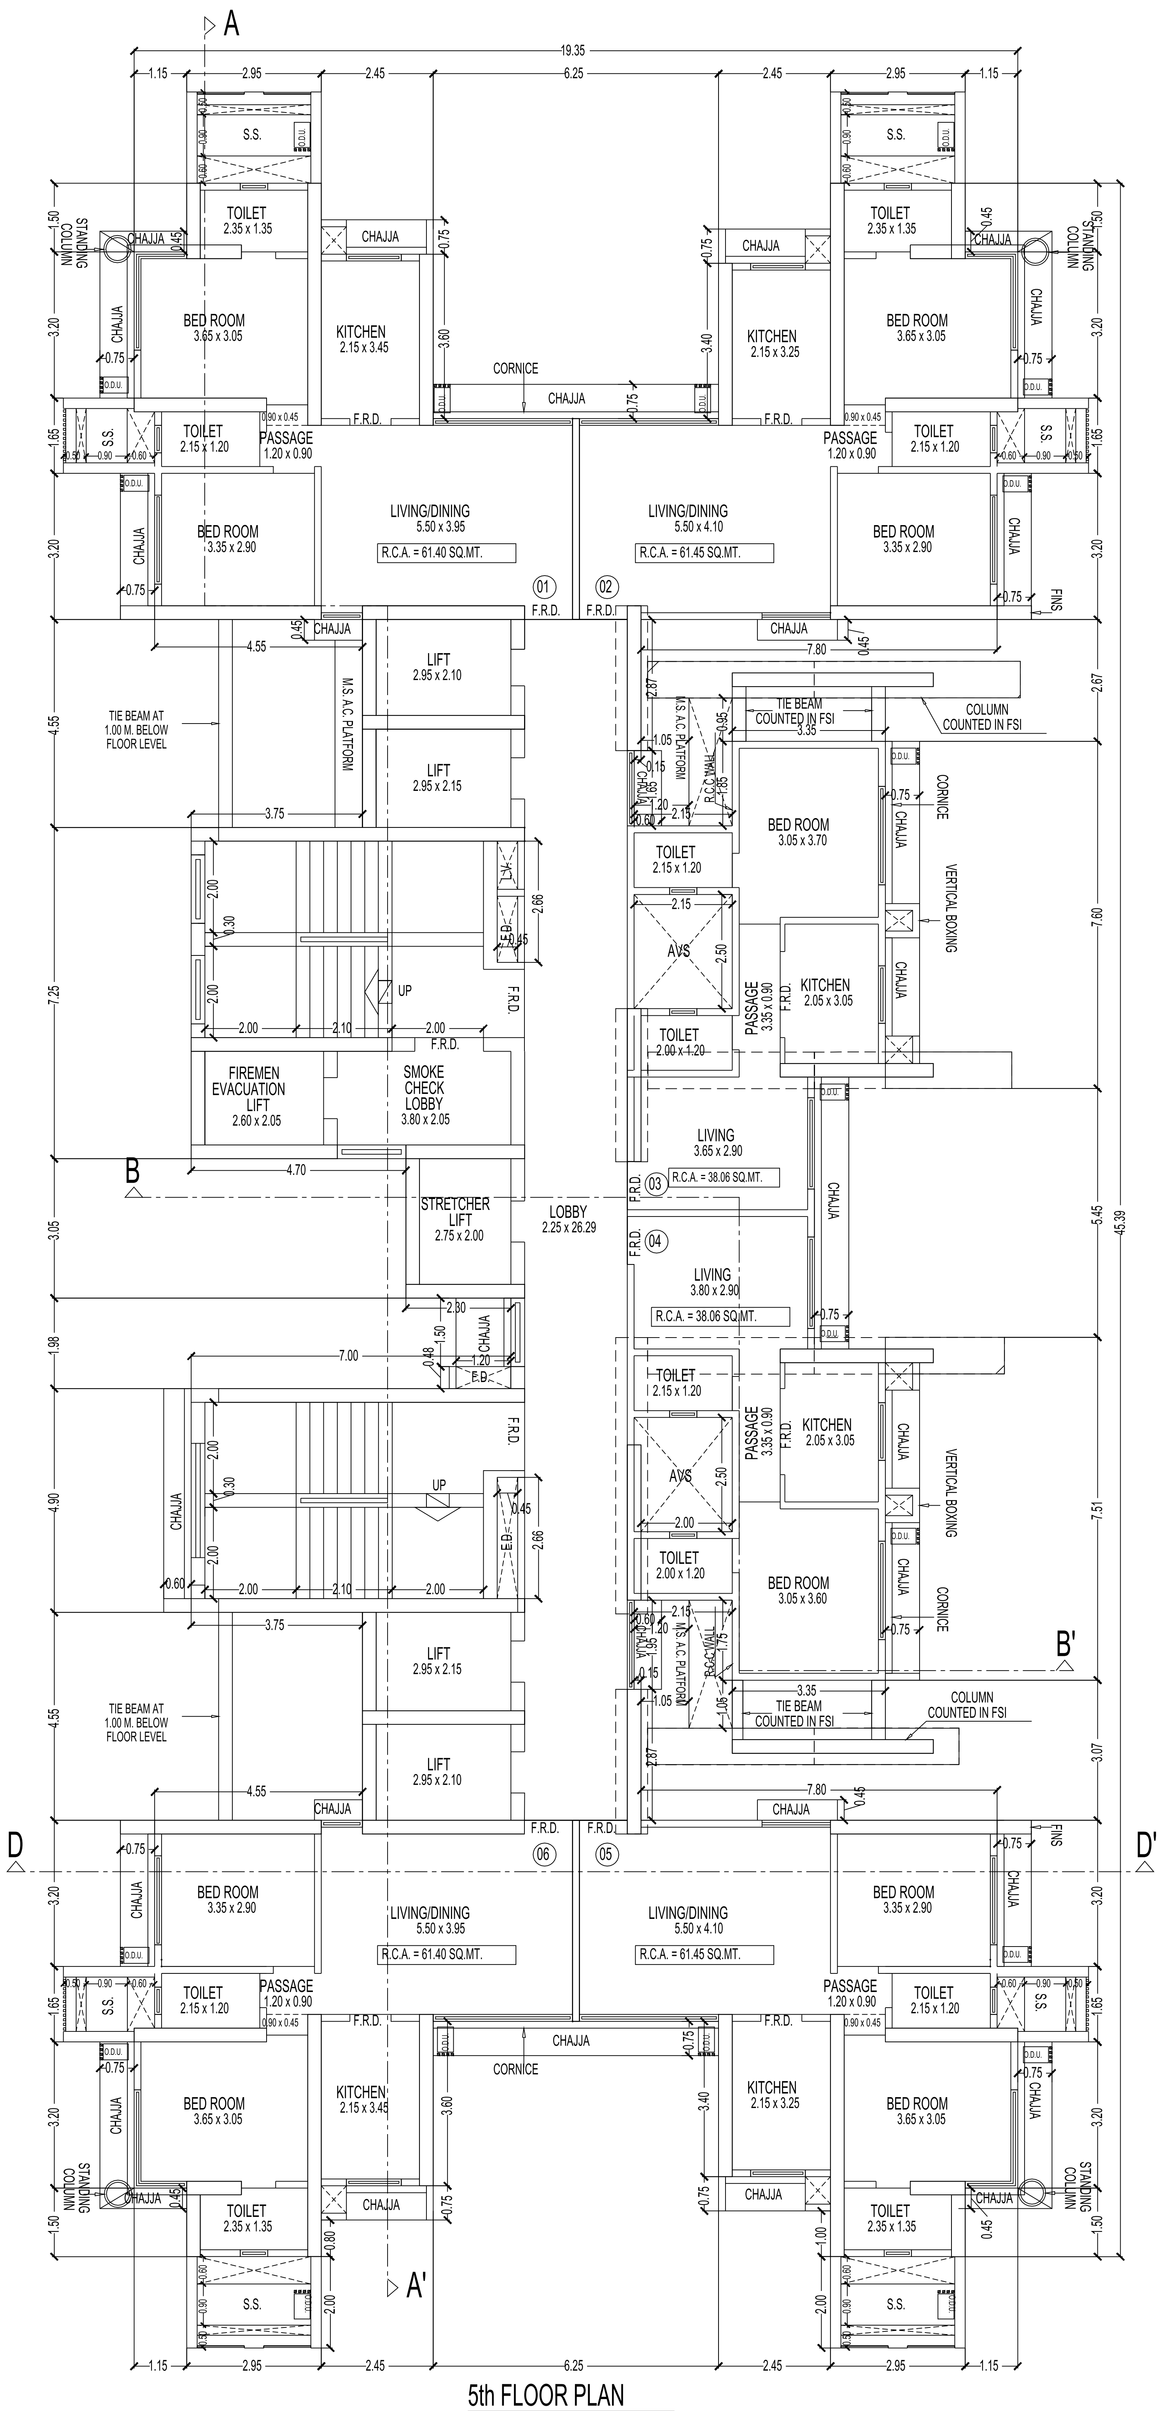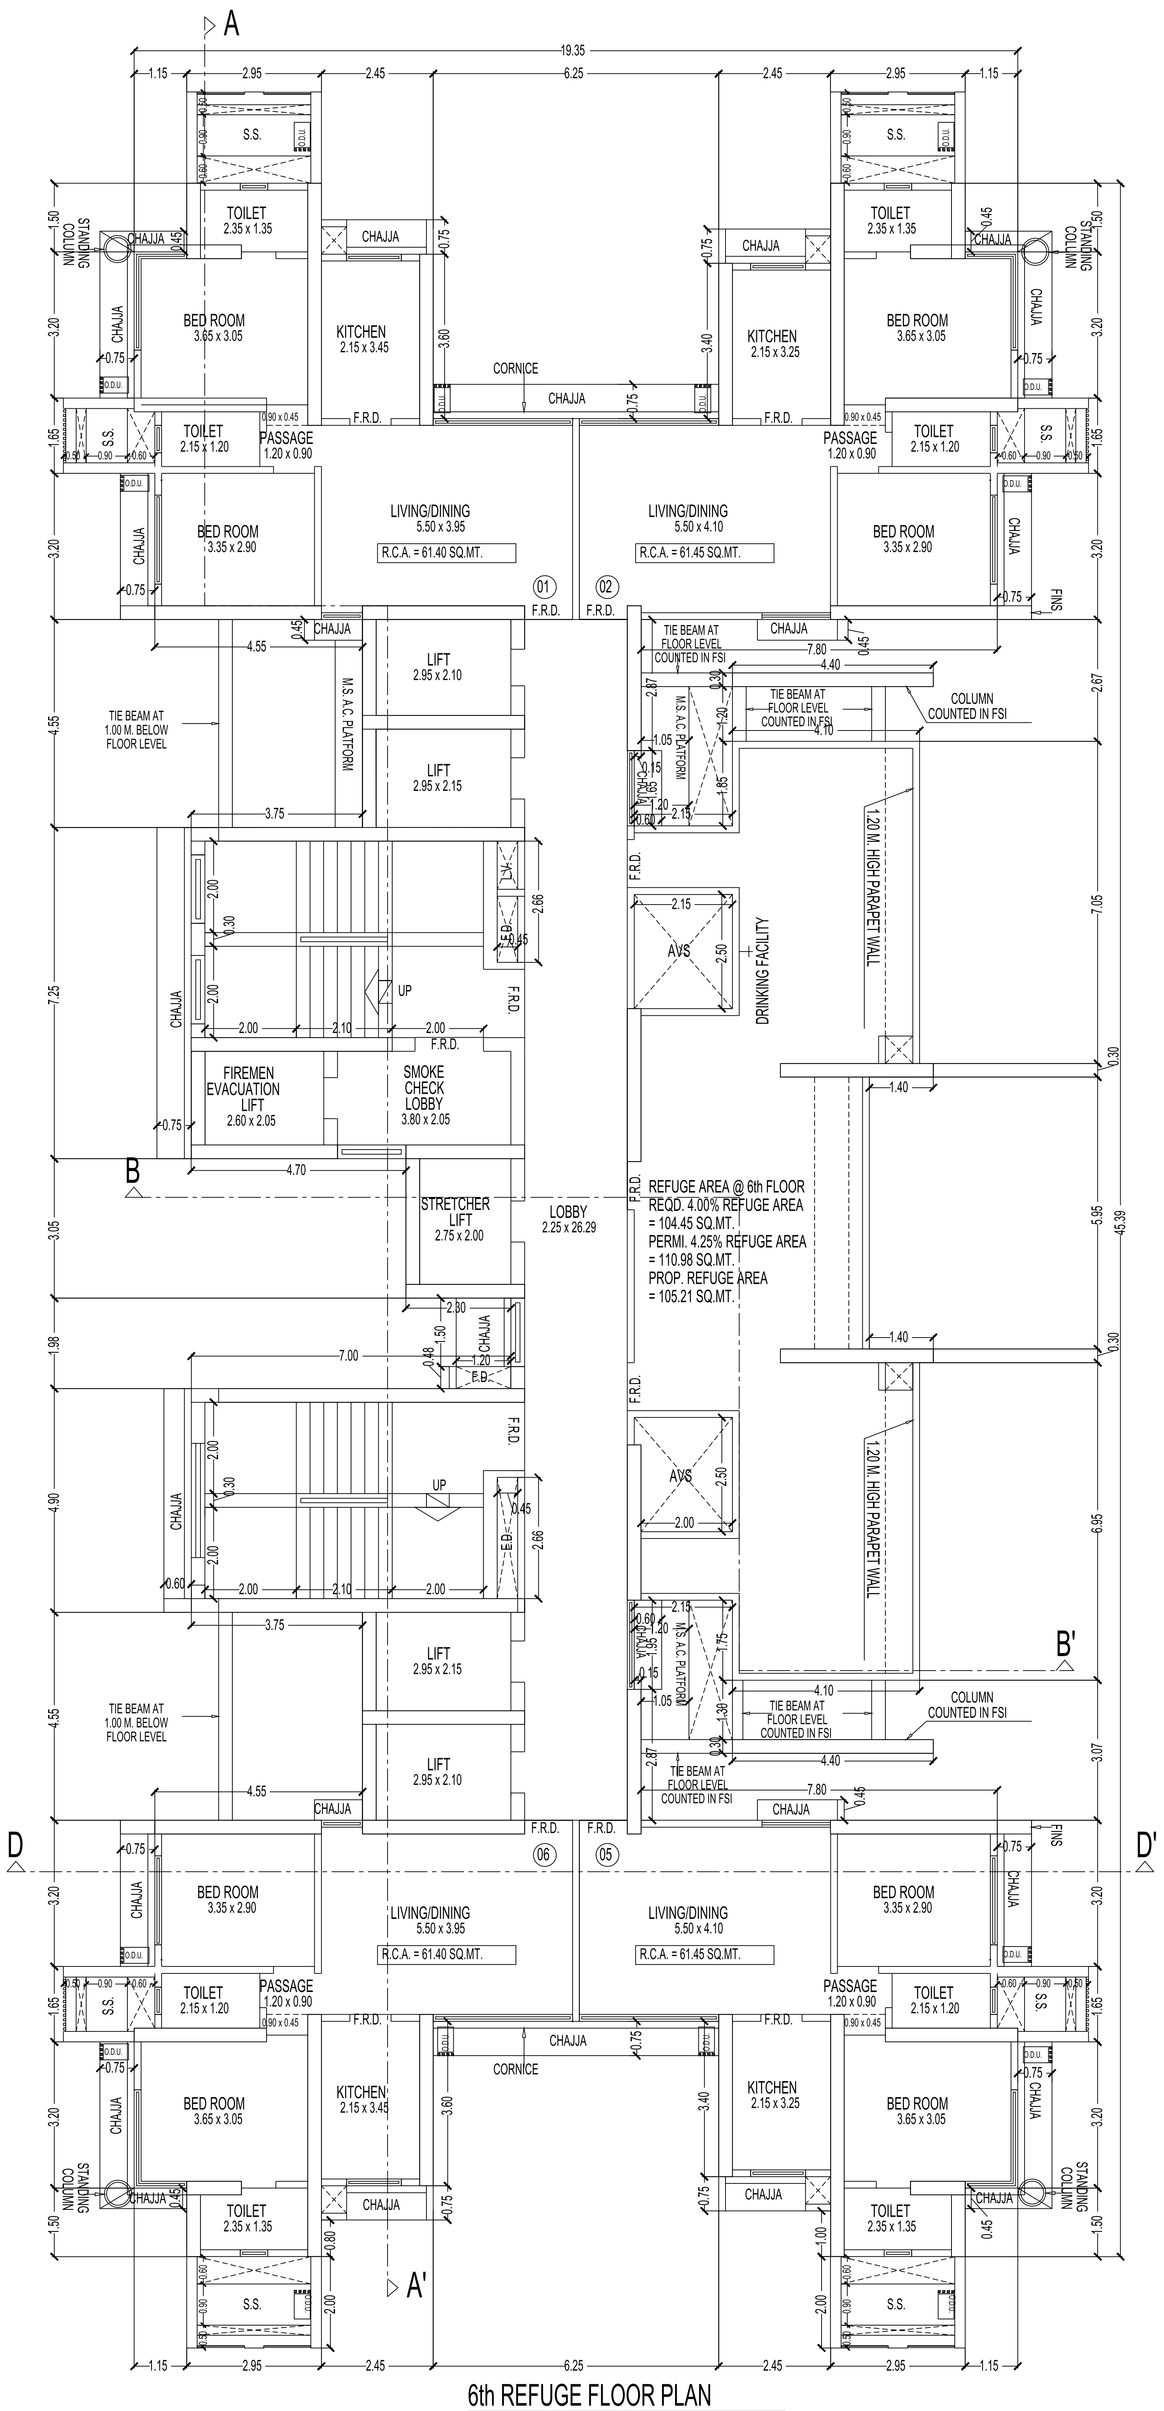

6th REFUGE FLOOR PLAN


SCALE 1:100


FILE No. :- P-24911/2025/(395A And Other)/R/N Ward/BORIVALI-R/N

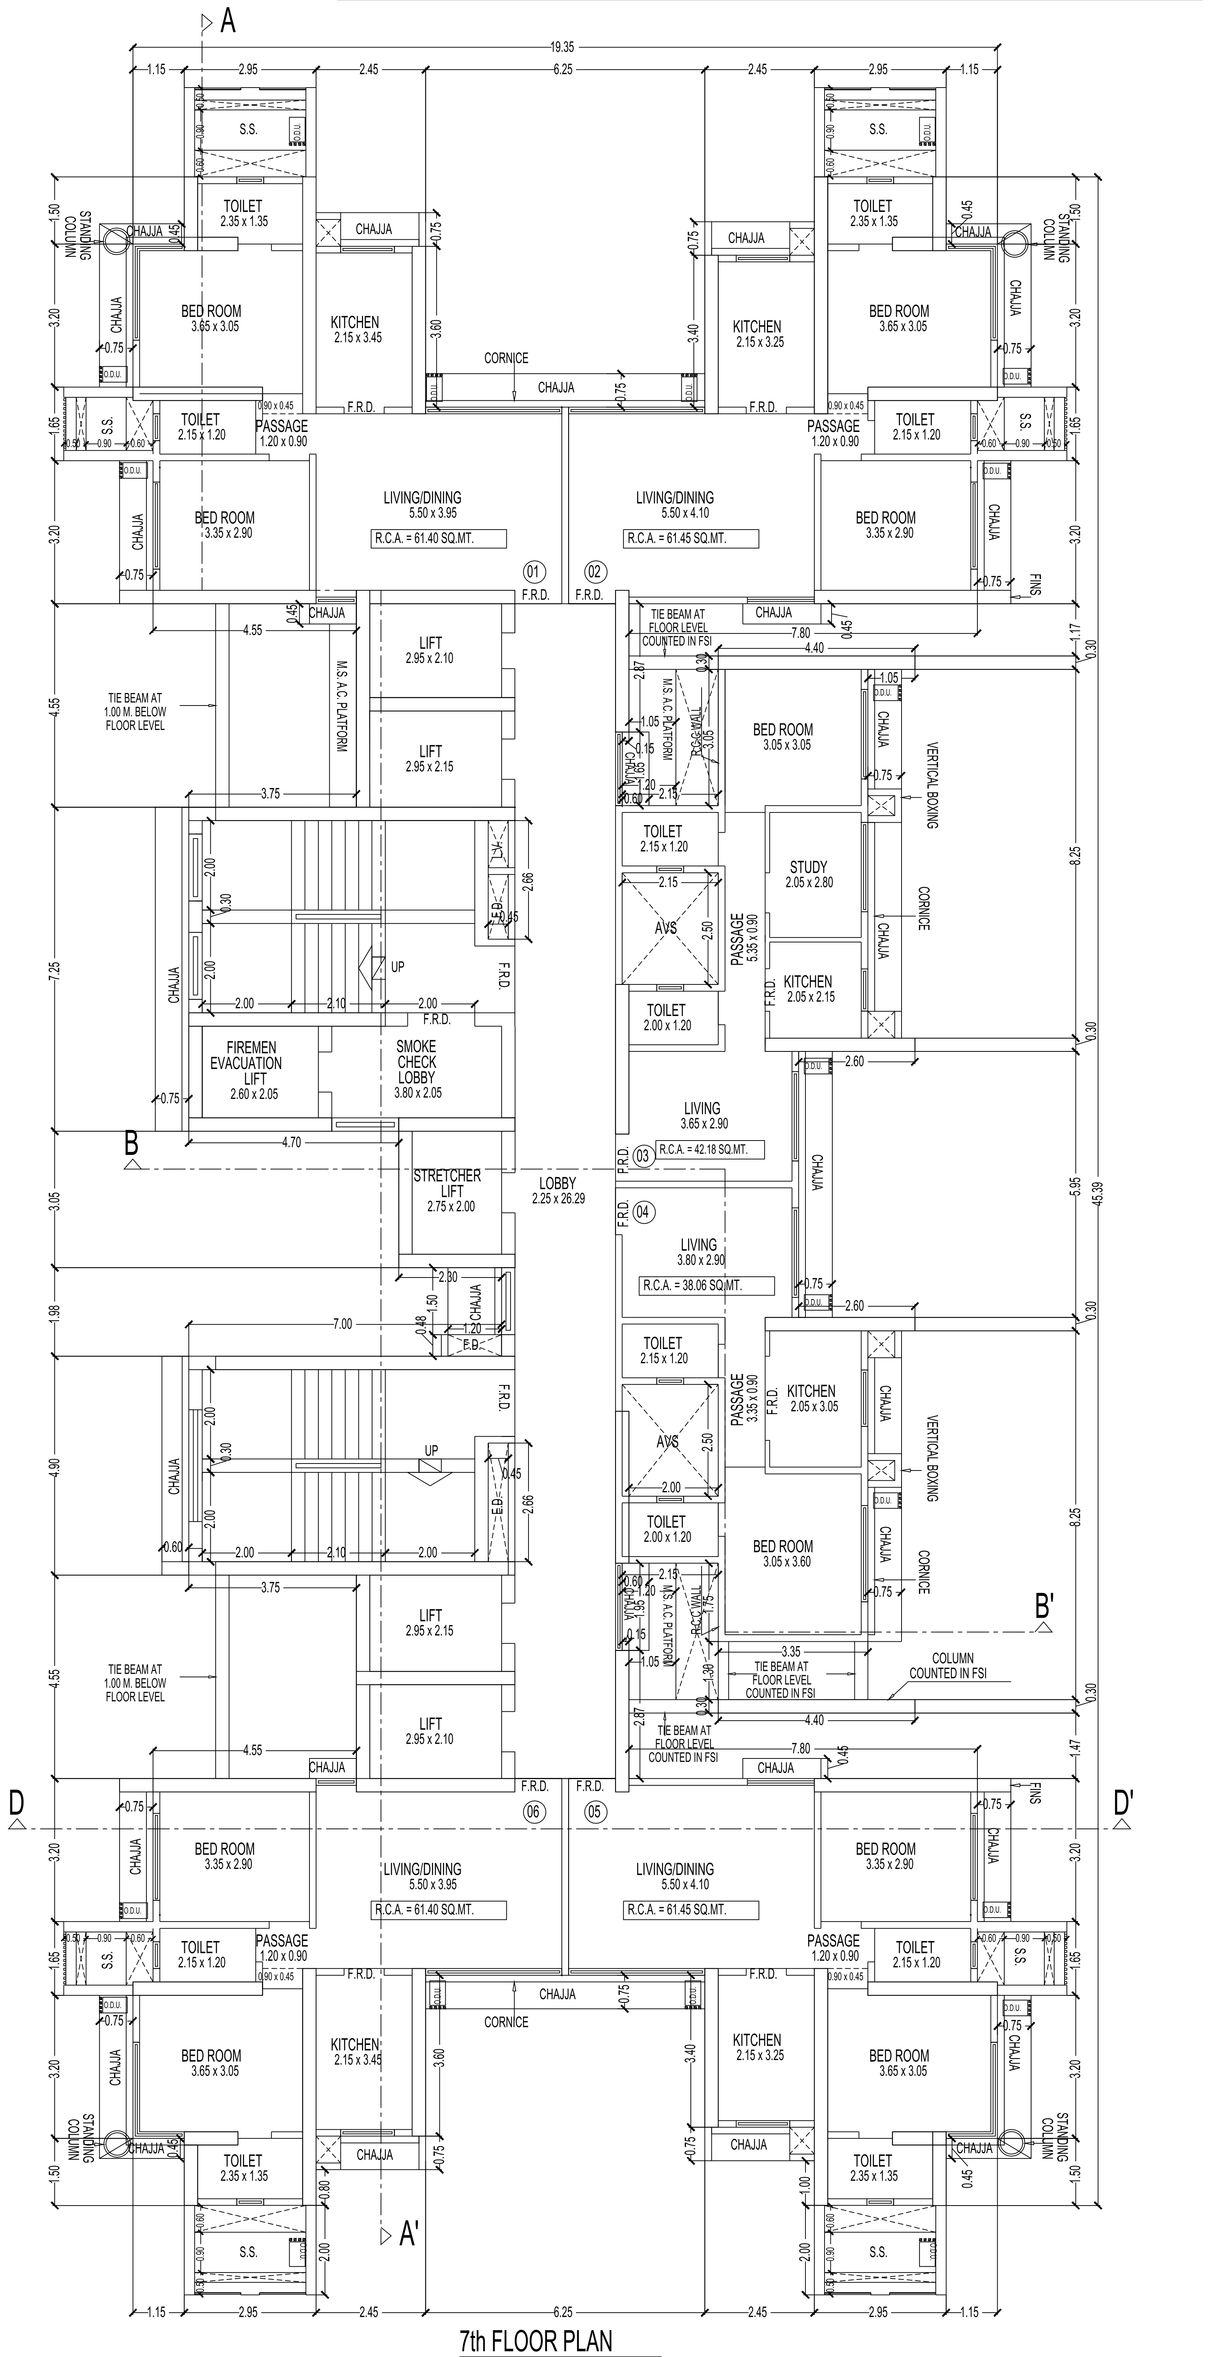

7th FLOOR PLAN


SCALE 1:100

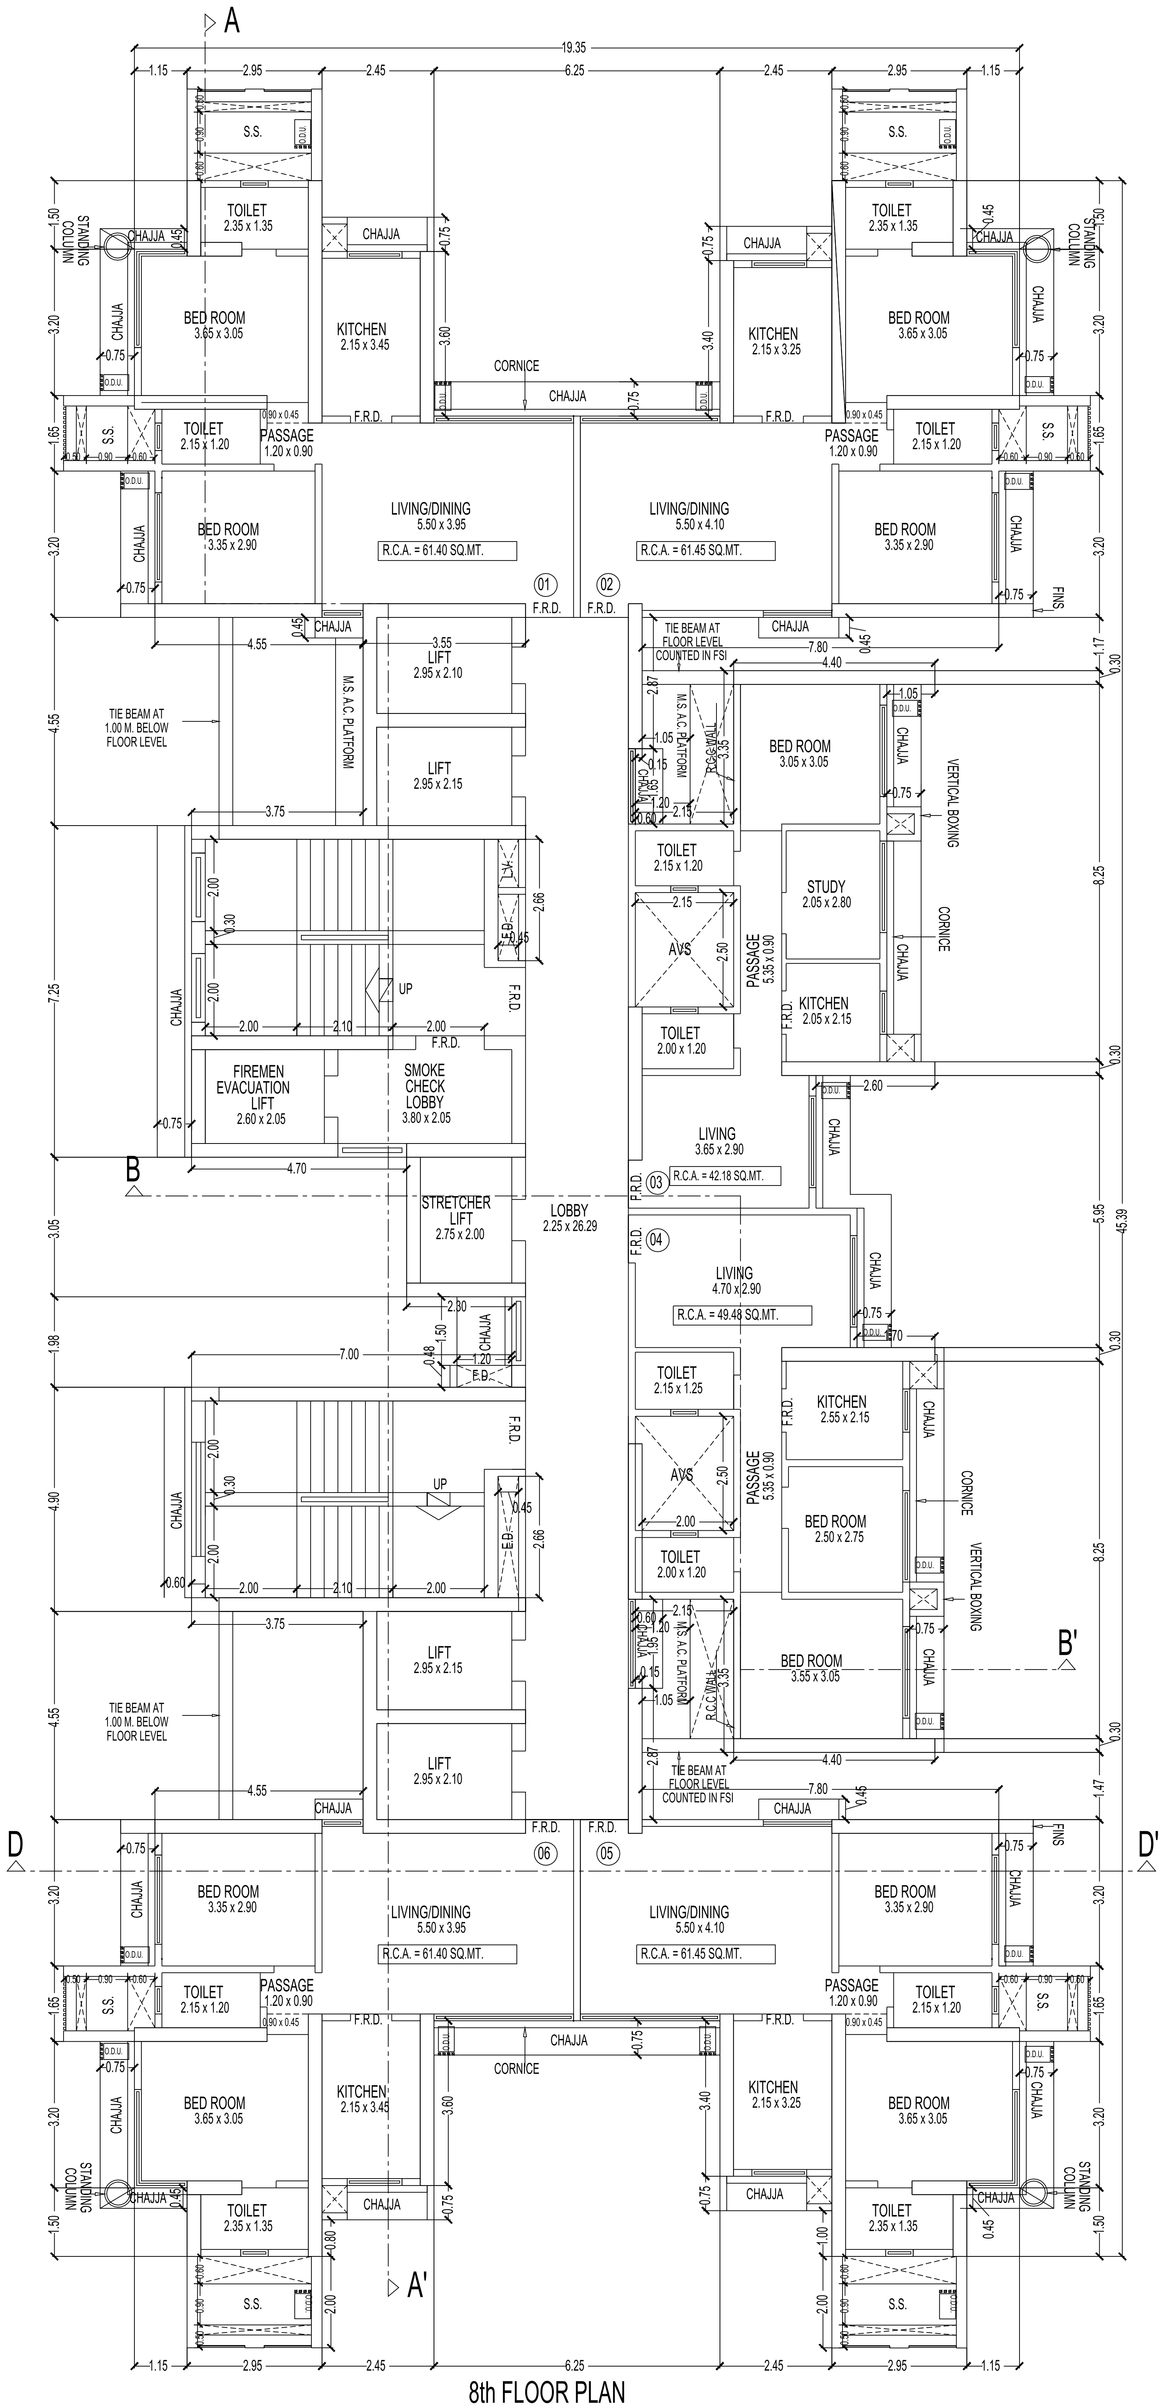
A
A'
B
B'
D
D'
19.35
1.15
2.95
2.45
6.25
2.45
2.95
1.15
S.S.
TOILET
2.35 x 1.35
CHAJJA
BED ROOM
3.65 x 3.05
KITCHEN
2.15 x 3.45
KITCHEN
2.15 x 3.25
CORNICE
STANDING COLUMN
TOILET
2.15 x 1.20
PASSAGE
1.20 x 0.90
F.R.D.
LIVING/DINING
5.50 x 3.95
R.C.A. = 61.40 SQ.MT.
LIVING/DINING
5.50 x 4.10
R.C.A. = 61.45 SQ.MT.
BED ROOM
3.35 x 2.90
FINS
01
02
TIE BEAM AT
1.00 M. BELOW
FLOOR LEVEL
M.S. A.C. PLATFORM
LIFT
2.95 x 2.10
LIFT
2.95 x 2.15
TIE BEAM AT
FLOOR LEVEL
COUNTED IN FSI
R.C.C. WALL
BED ROOM
3.05 x 3.05
VERTICAL BOXING
STUDY
2.05 x 2.80
AVS
PASSAGE
5.35 x 0.90
KITCHEN
2.05 x 2.15
TOILET
2.00 x 1.20
UP
FIREMEN
EVACUATION
LIFT
2.60 x 2.05
SMOKE
CHECK
LOBBY
3.80 x 2.05
LIVING
3.65 x 2.90
R.C.A. = 42.18 SQ.MT.
03
STRETCHER
LIFT
2.75 x 2.00
LOBBY
2.25 x 26.29
04
LIVING
4.70 x 2.90
R.C.A. = 49.48 SQ.MT.
E.P.
TOILET
2.15 x 1.25
KITCHEN
2.55 x 2.15
BED ROOM
2.50 x 2.75
BED ROOM
3.55 x 3.05
06
05
45.39
8th FLOOR PLAN
SCALE 1:100

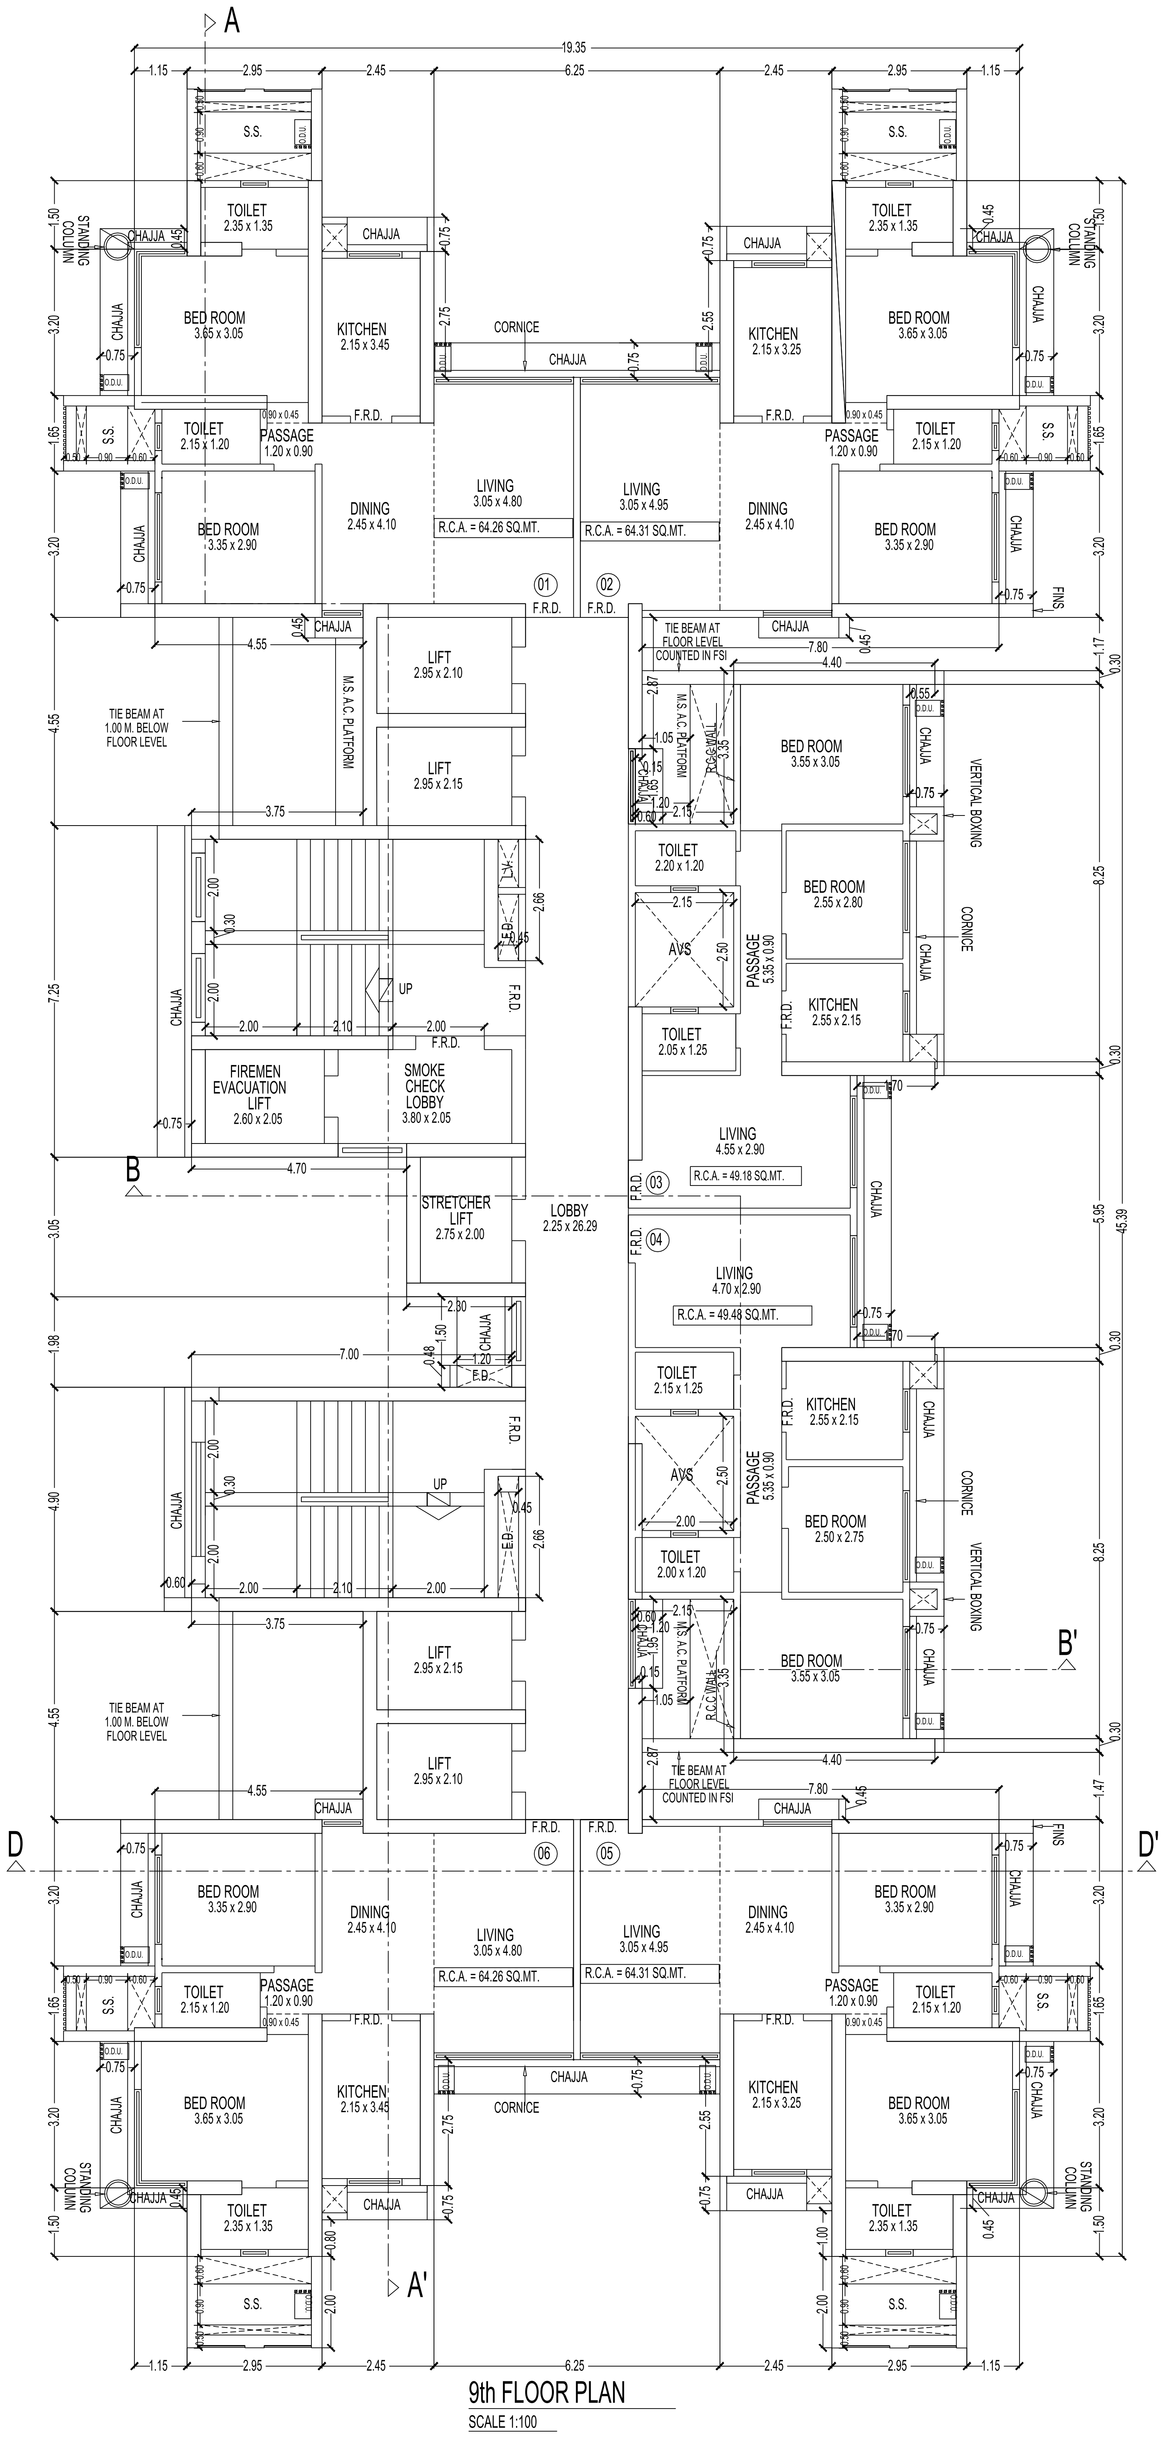


9th FLOOR PLAN

SCALE 1:100

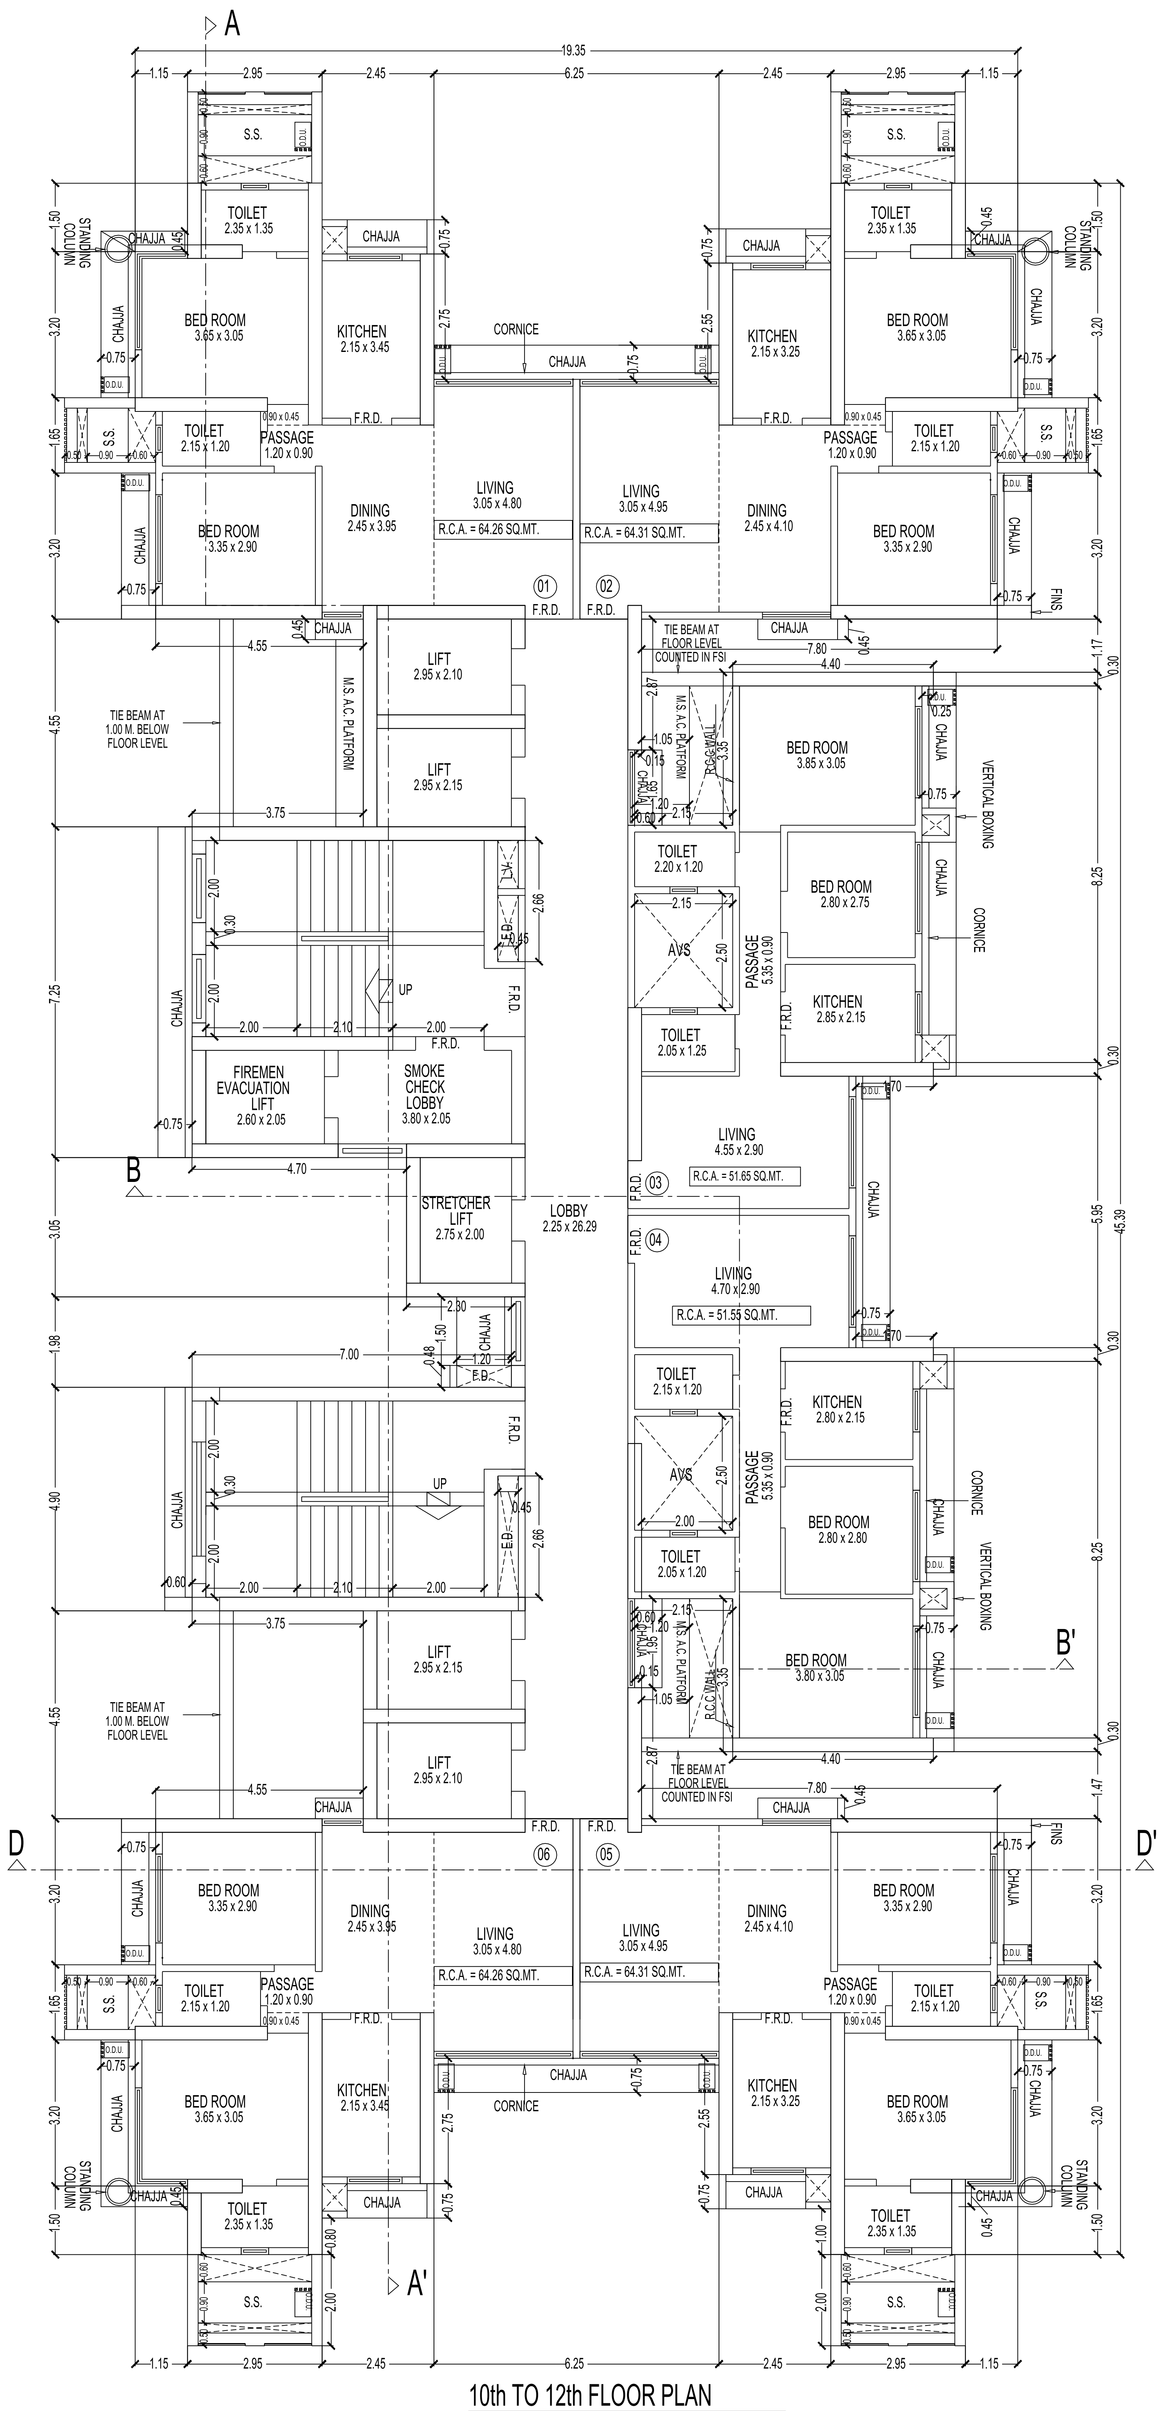

A
A'
B
B'
D
D'
19.35
1.15
2.95
2.45
6.25
2.45
2.95
1.15
S.S.
TOILET
2.35 x 1.35
CHAJJA
STANDING COLUMN
BED ROOM
3.65 x 3.05
KITCHEN
2.15 x 3.45
KITCHEN
2.15 x 3.25
CORNICE
F.R.D.
TOILET
2.15 x 1.20
PASSAGE
1.20 x 0.90
S.S.
BED ROOM
3.35 x 2.90
DINING
2.45 x 3.95
LIVING
3.05 x 4.80
R.C.A. = 64.26 SQ.MT.
LIVING
3.05 x 4.95
R.C.A. = 64.31 SQ.MT.
DINING
2.45 x 4.10
FINS
01
02
TIE BEAM AT
1.00 M. BELOW
FLOOR LEVEL
M.S. A.C. PLATFORM
LIFT
2.95 x 2.10
LIFT
2.95 x 2.15
TIE BEAM AT
FLOOR LEVEL
COUNTED IN FSI
7.80
4.40
R.C.C. WALL
BED ROOM
3.85 x 3.05
VERTICAL BOXING
TOILET
2.20 x 1.20
AVS
PASSAGE
5.35 x 0.90
BED ROOM
2.80 x 2.75
KITCHEN
2.85 x 2.15
TOILET
2.05 x 1.25
UP
F.E.
FIREMEN
EVACUATION
LIFT
2.60 x 2.05
SMOKE
CHECK
LOBBY
3.80 x 2.05
LIVING
4.55 x 2.90
R.C.A. = 51.65 SQ.MT.
STRETCHER
LIFT
2.75 x 2.00
LOBBY
2.25 x 26.29
03
04
LIVING
4.70 x 2.90
R.C.A. = 51.55 SQ.MT.
KITCHEN
2.80 x 2.15
BED ROOM
2.80 x 2.80
BED ROOM
3.80 x 3.05
45.39
05
06
10th TO 12th FLOOR PLAN
SCALE 1:100


FILE No. :- P-24911/2025/(395A And Other)/R/N Ward/BORIVALI-R/N

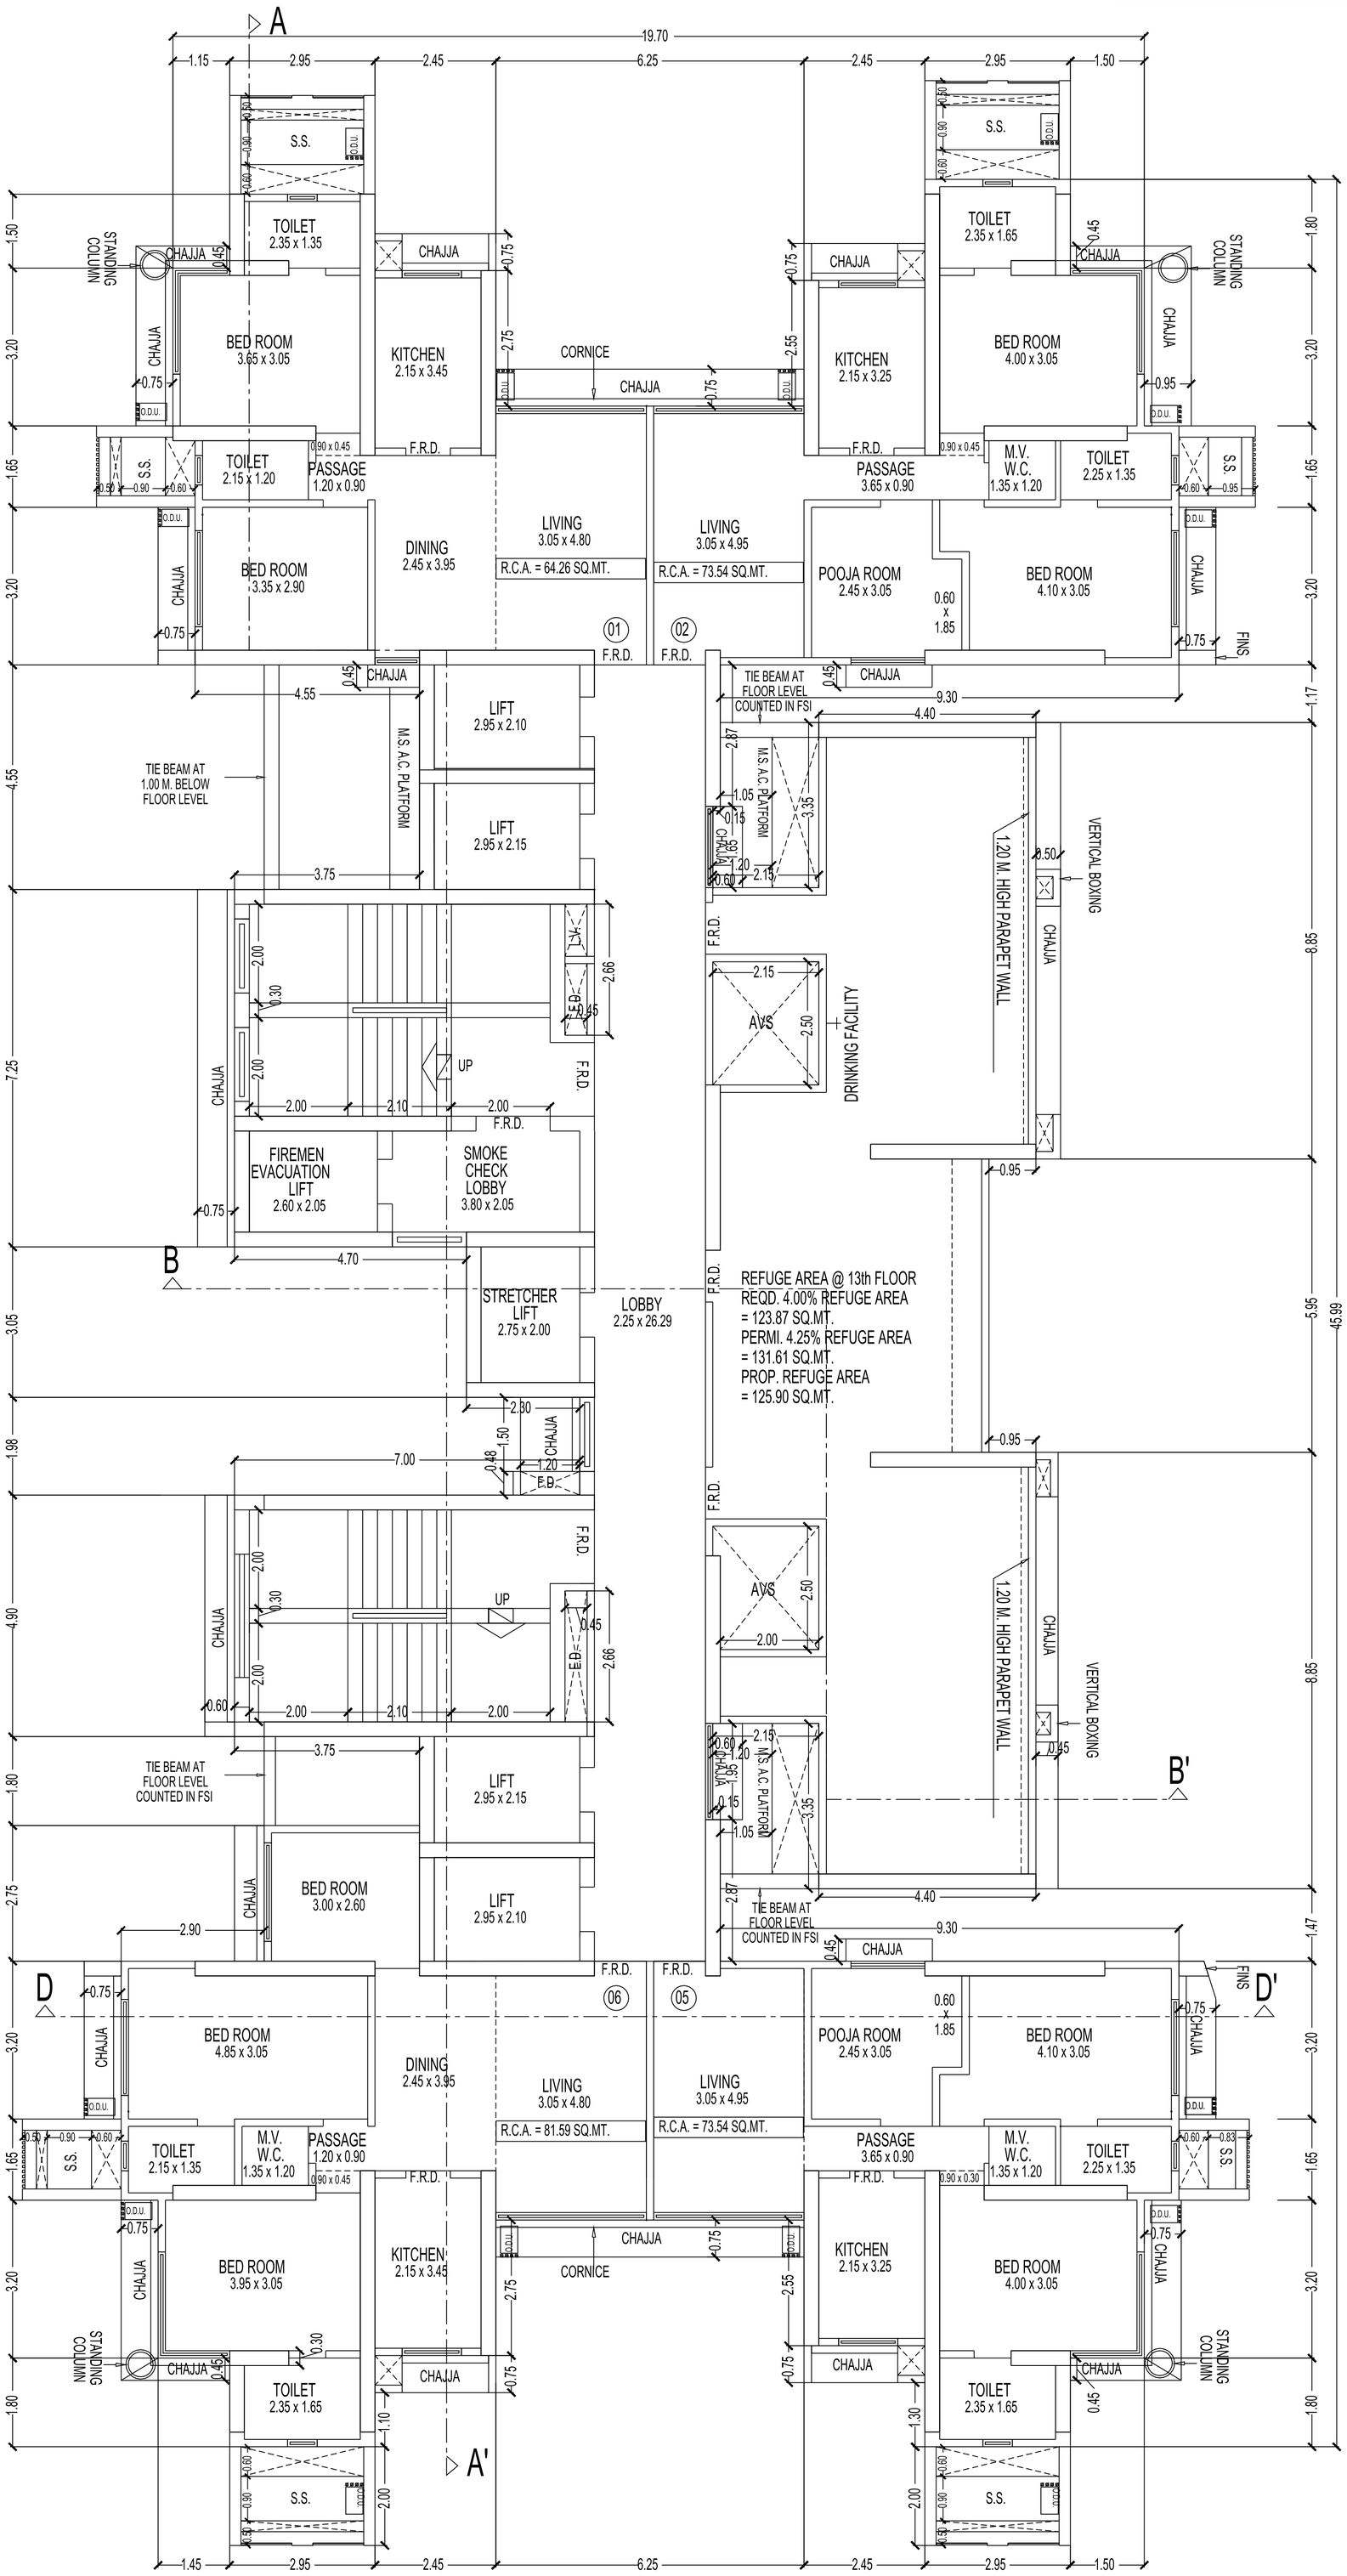

13th REFUGE FLOOR PLAN


SCALE 1:100

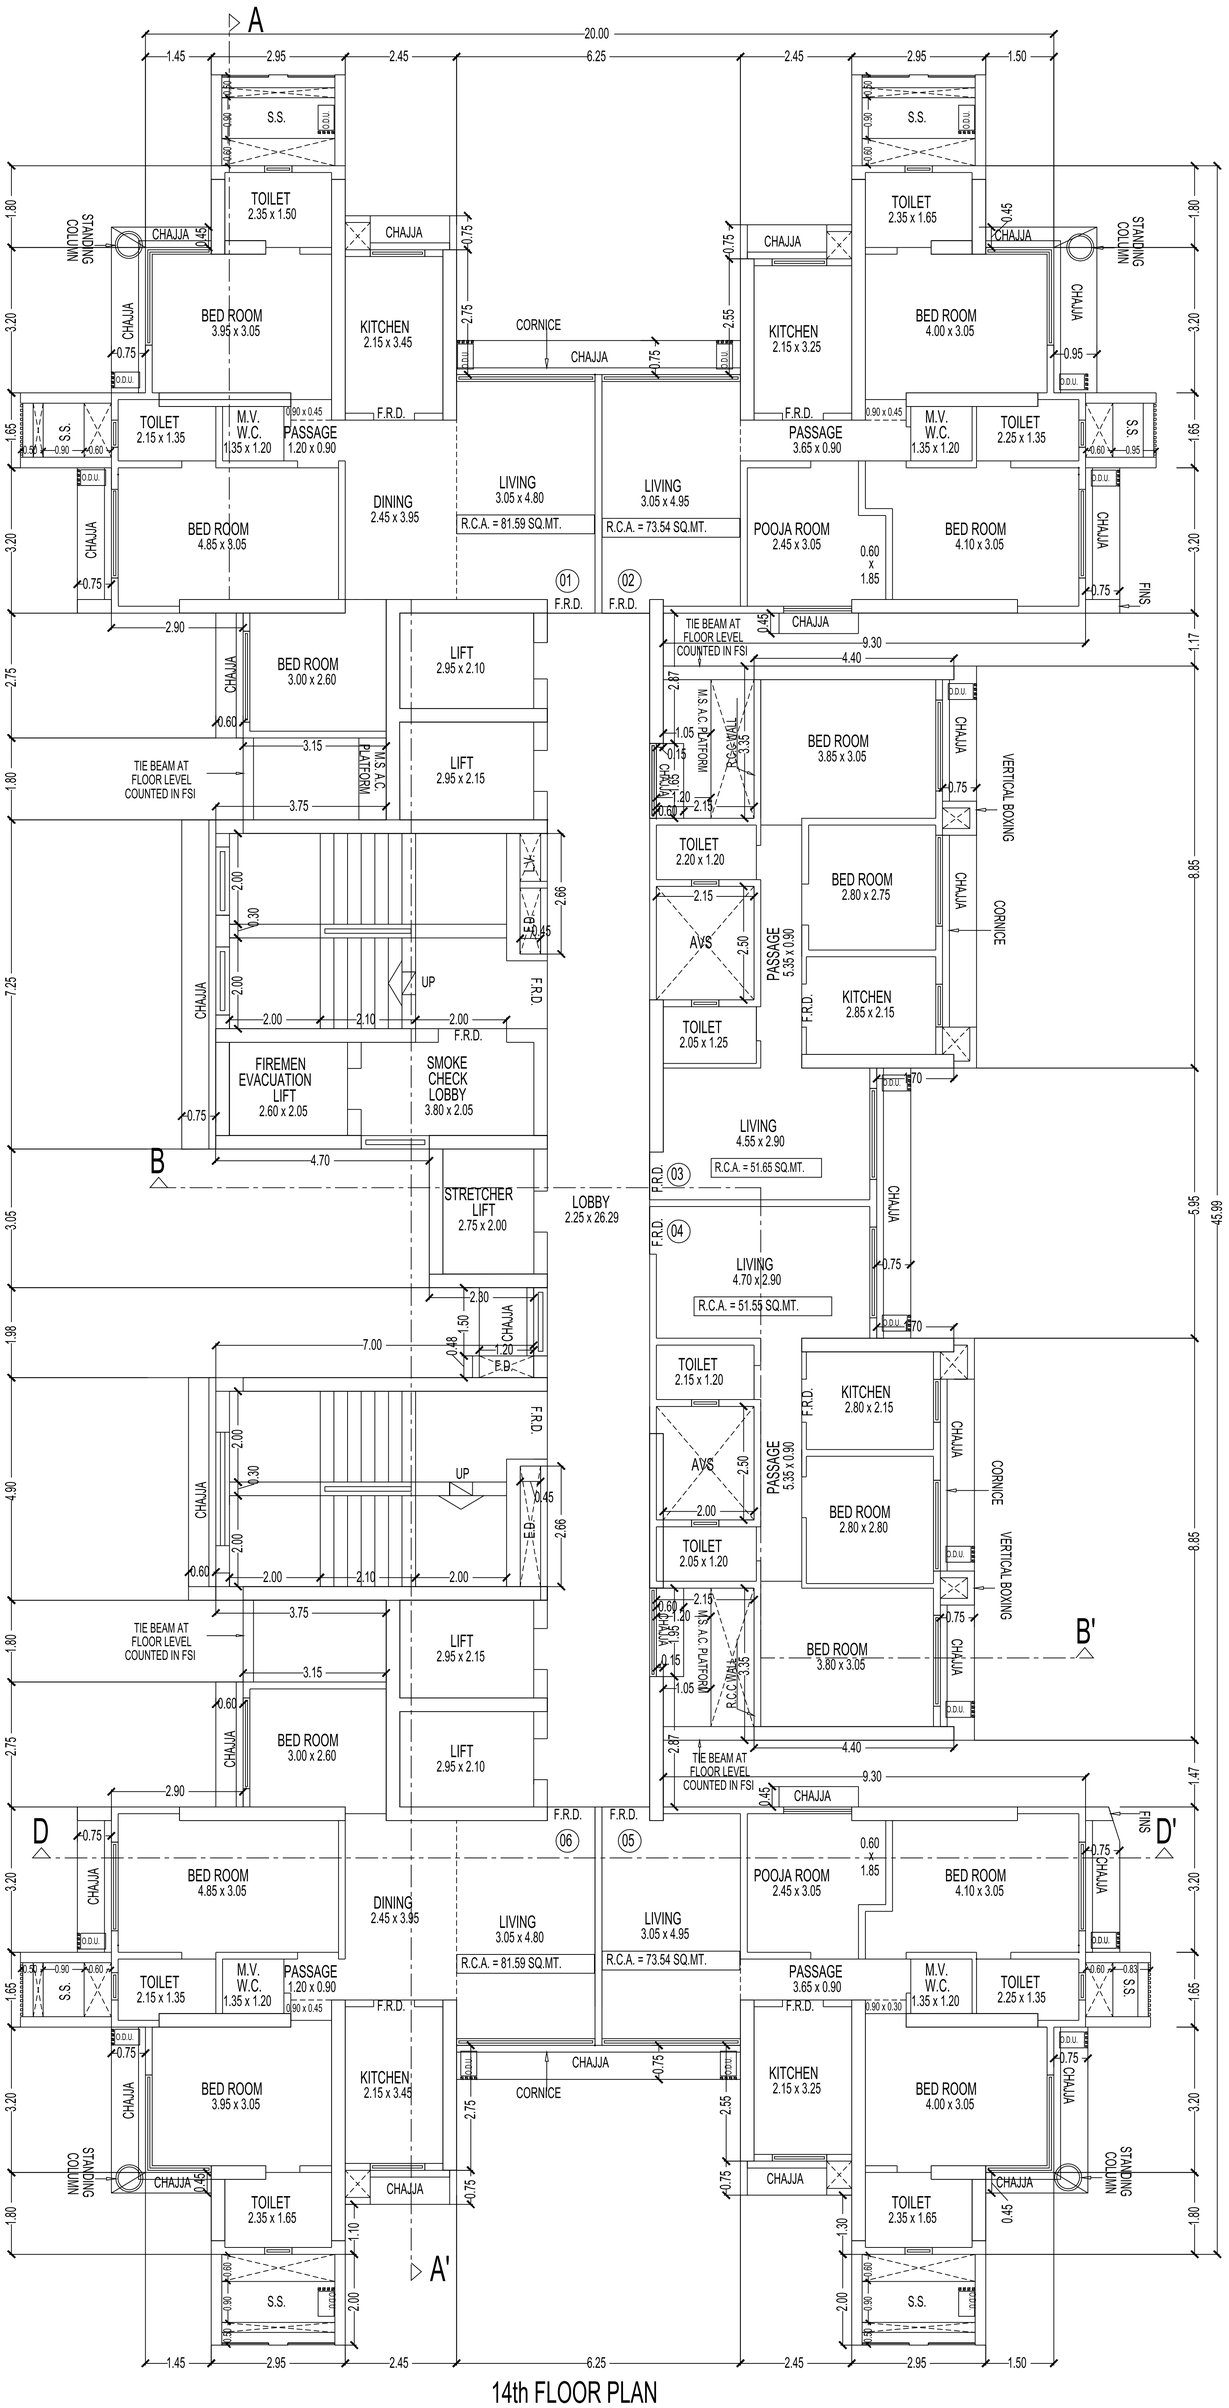
A
A'
B
B'
D
D'
20.00
45.99
TOILET 2.35 x 1.50
BED ROOM 3.95 x 3.05
KITCHEN 2.15 x 3.45
TOILET 2.15 x 1.35
M.V. W.C. 1.35 x 1.20
PASSAGE 1.20 x 0.90
BED ROOM 4.85 x 3.05
DINING 2.45 x 3.95
LIVING 3.05 x 4.80
R.C.A. = 81.59 SQ.MT.
LIVING 3.05 x 4.95
R.C.A. = 73.54 SQ.MT.
TOILET 2.35 x 1.65
KITCHEN 2.15 x 3.25
BED ROOM 4.00 x 3.05
PASSAGE 3.65 x 0.90
M.V. W.C. 1.35 x 1.20
TOILET 2.25 x 1.35
POOJA ROOM 2.45 x 3.05
BED ROOM 4.10 x 3.05
BED ROOM 3.00 x 2.60
LIFT 2.95 x 2.10
LIFT 2.95 x 2.15
TIE BEAM AT FLOOR LEVEL COUNTED IN FSI
M.S.A.C. PLATFORM
BED ROOM 3.85 x 3.05
TOILET 2.20 x 1.20
AVS
PASSAGE 5.35 x 0.90
BED ROOM 2.80 x 2.75
KITCHEN 2.85 x 2.15
TOILET 2.05 x 1.25
FIREMEN EVACUATION LIFT 2.60 x 2.05
SMOKE CHECK LOBBY 3.80 x 2.05
LIVING 4.55 x 2.90
R.C.A. = 51.65 SQ.MT.
STRETCHER LIFT 2.75 x 2.00
LOBBY 2.25 x 26.29
LIVING 4.70 x 2.90
R.C.A. = 51.55 SQ.MT.
KITCHEN 2.80 x 2.15
BED ROOM 2.80 x 2.80
BED ROOM 3.80 x 3.05
UP
F.R.D.
CHAJJA
CORNICE
VERTICAL BOXING
STANDING COLUMN
FINS
S.S.
O.D.U.
R.C.C. WALL
14th FLOOR PLAN
SCALE 1:100

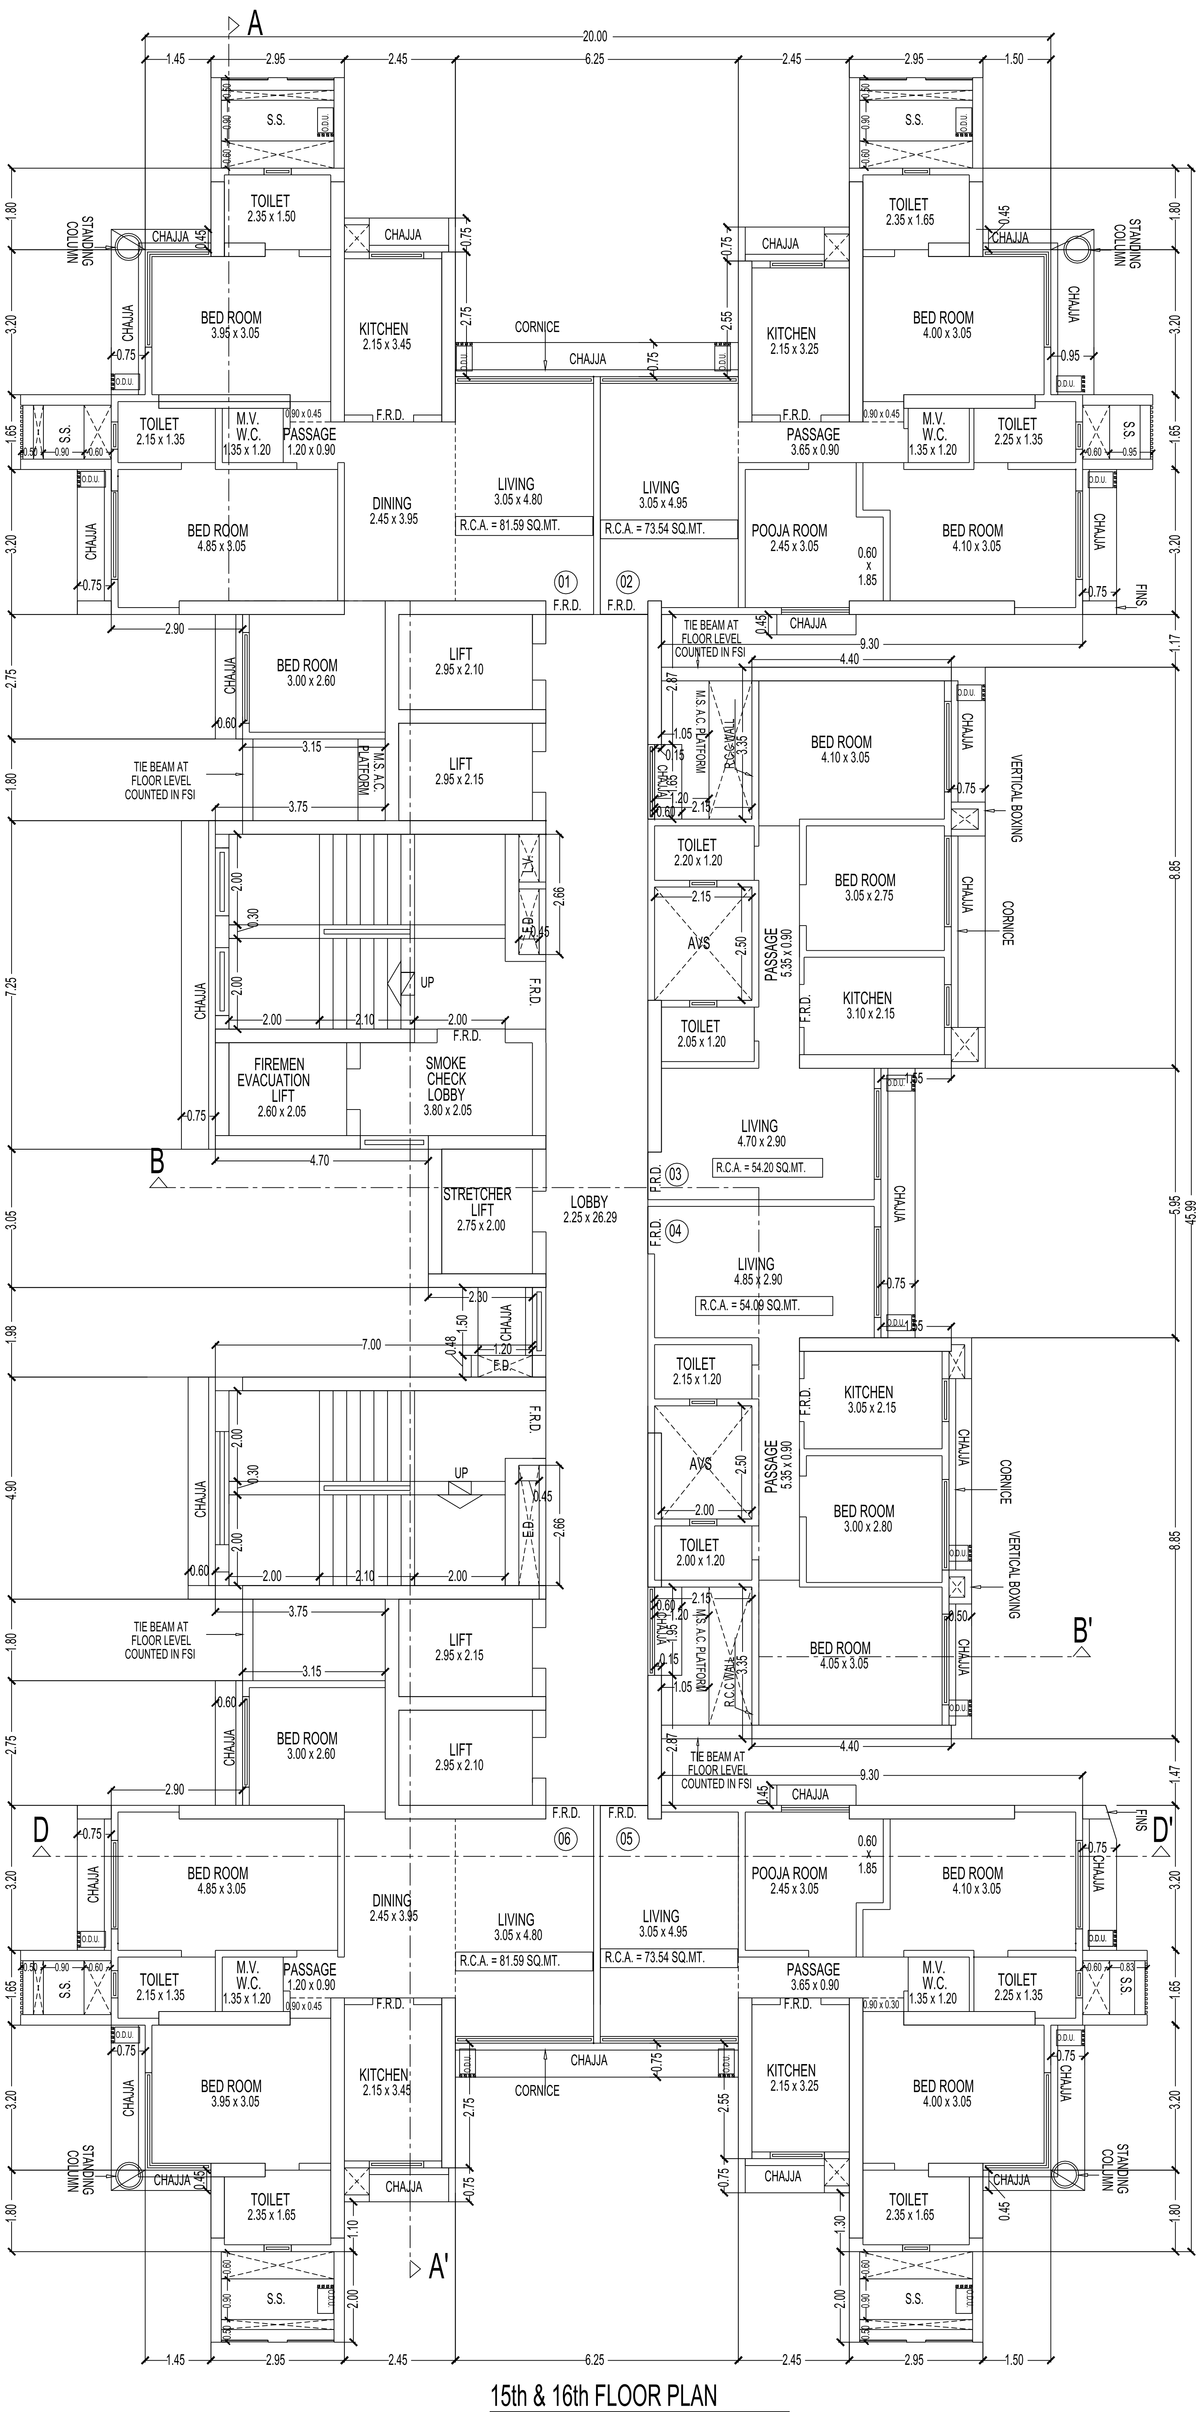

15th & 16th FLOOR PLAN


SCALE 1:100

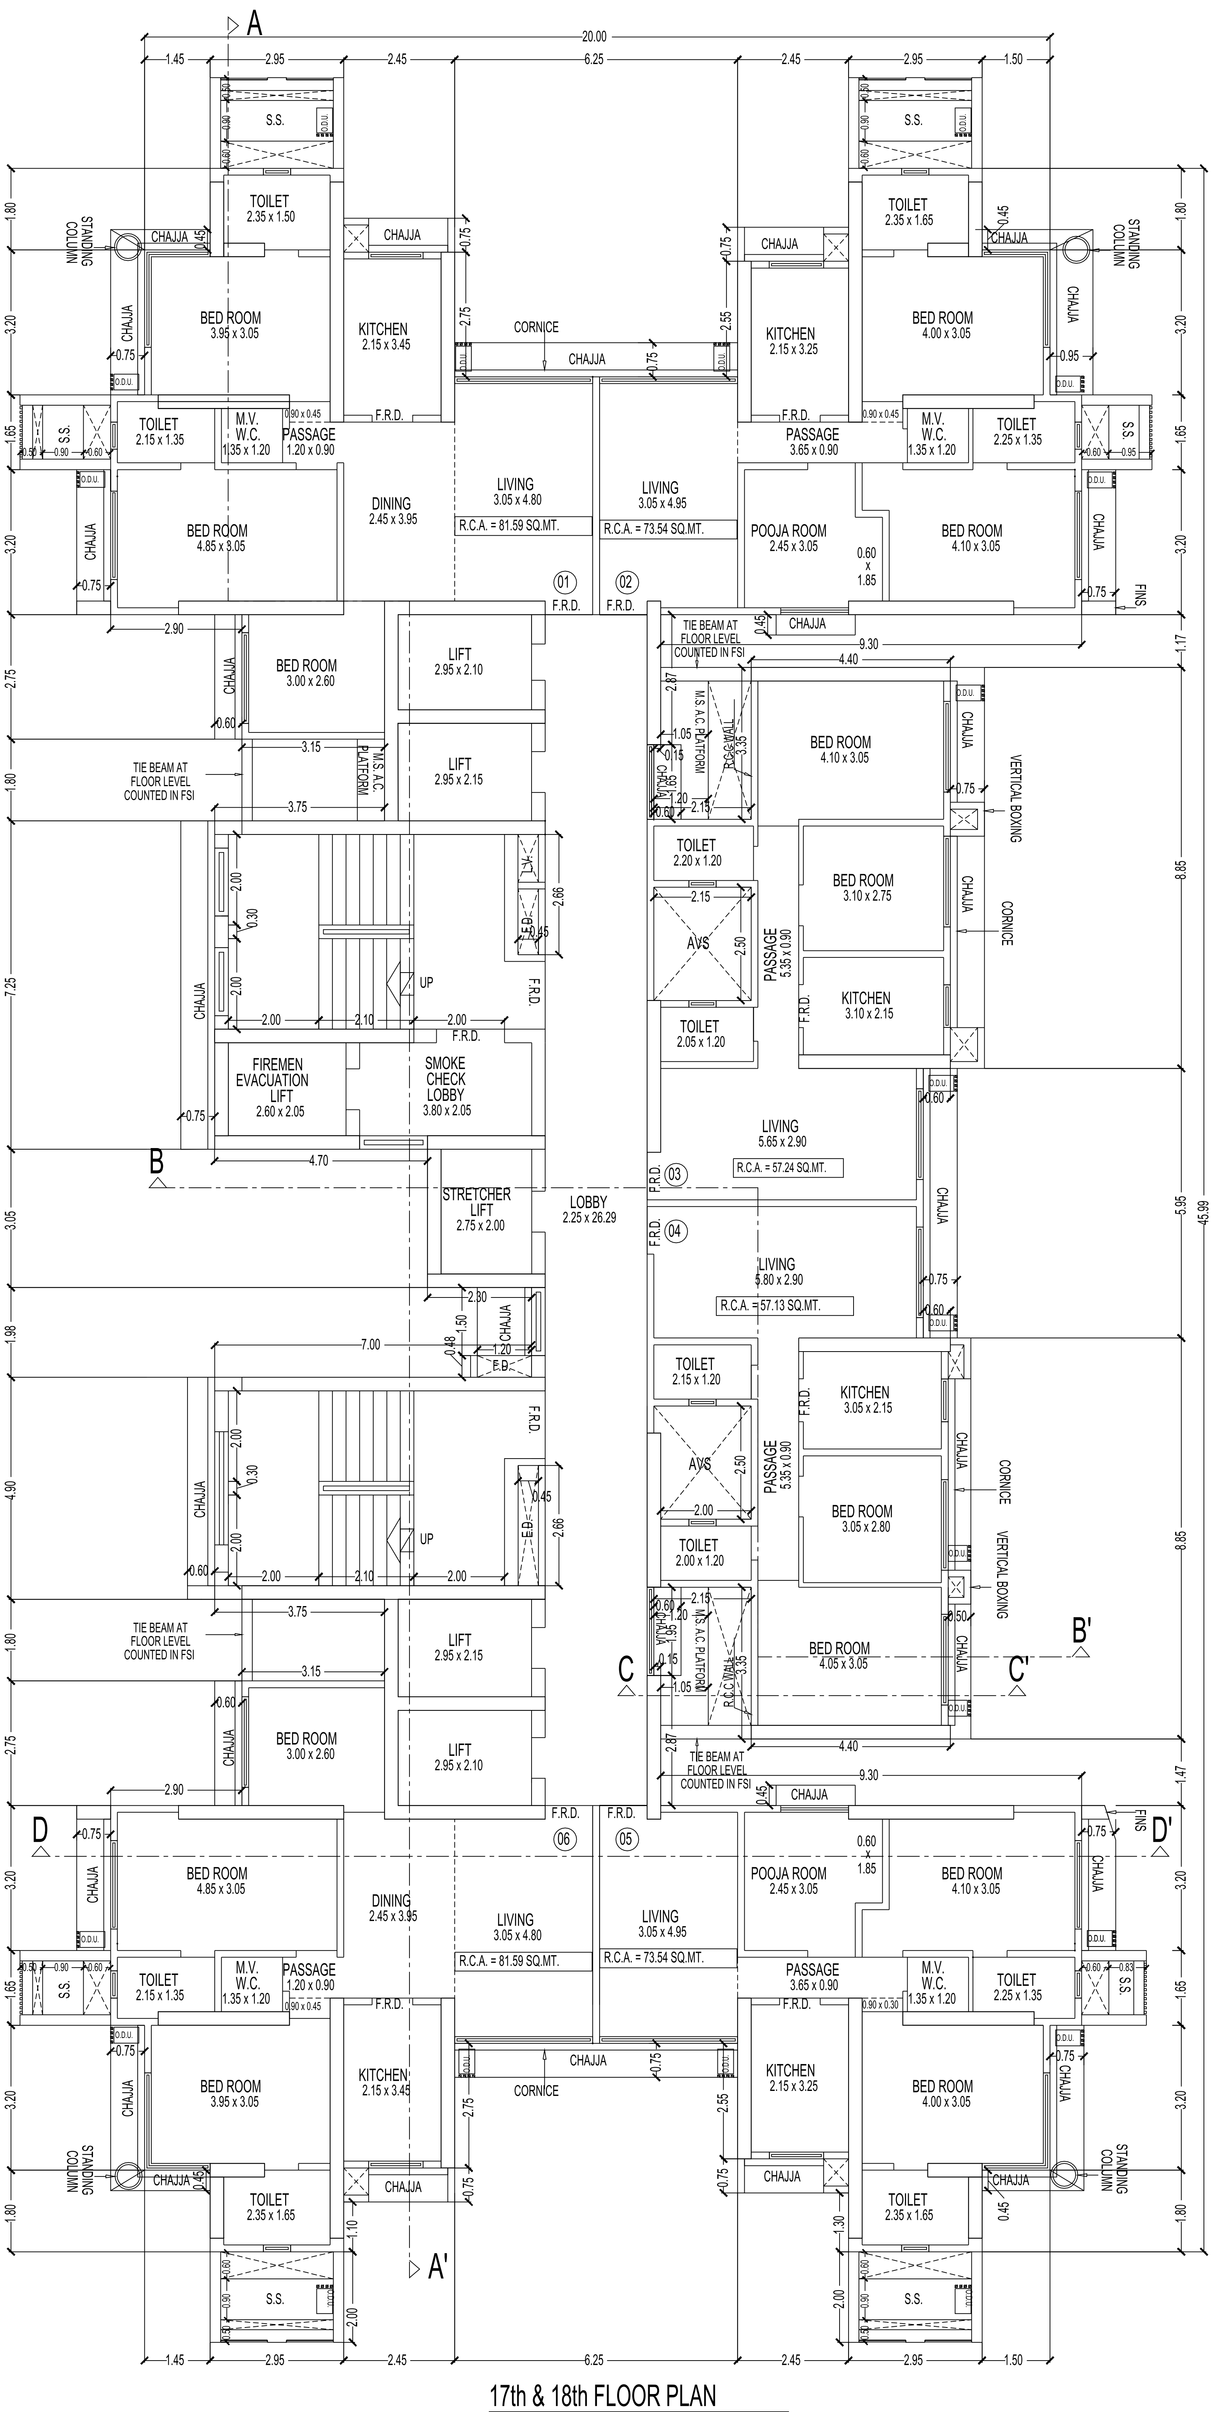

17th & 18th FLOOR PLAN


SCALE 1:100

FILE No. :- P-24911/2025/(395A And Other)/R/N Ward/BORIVALI-R/N

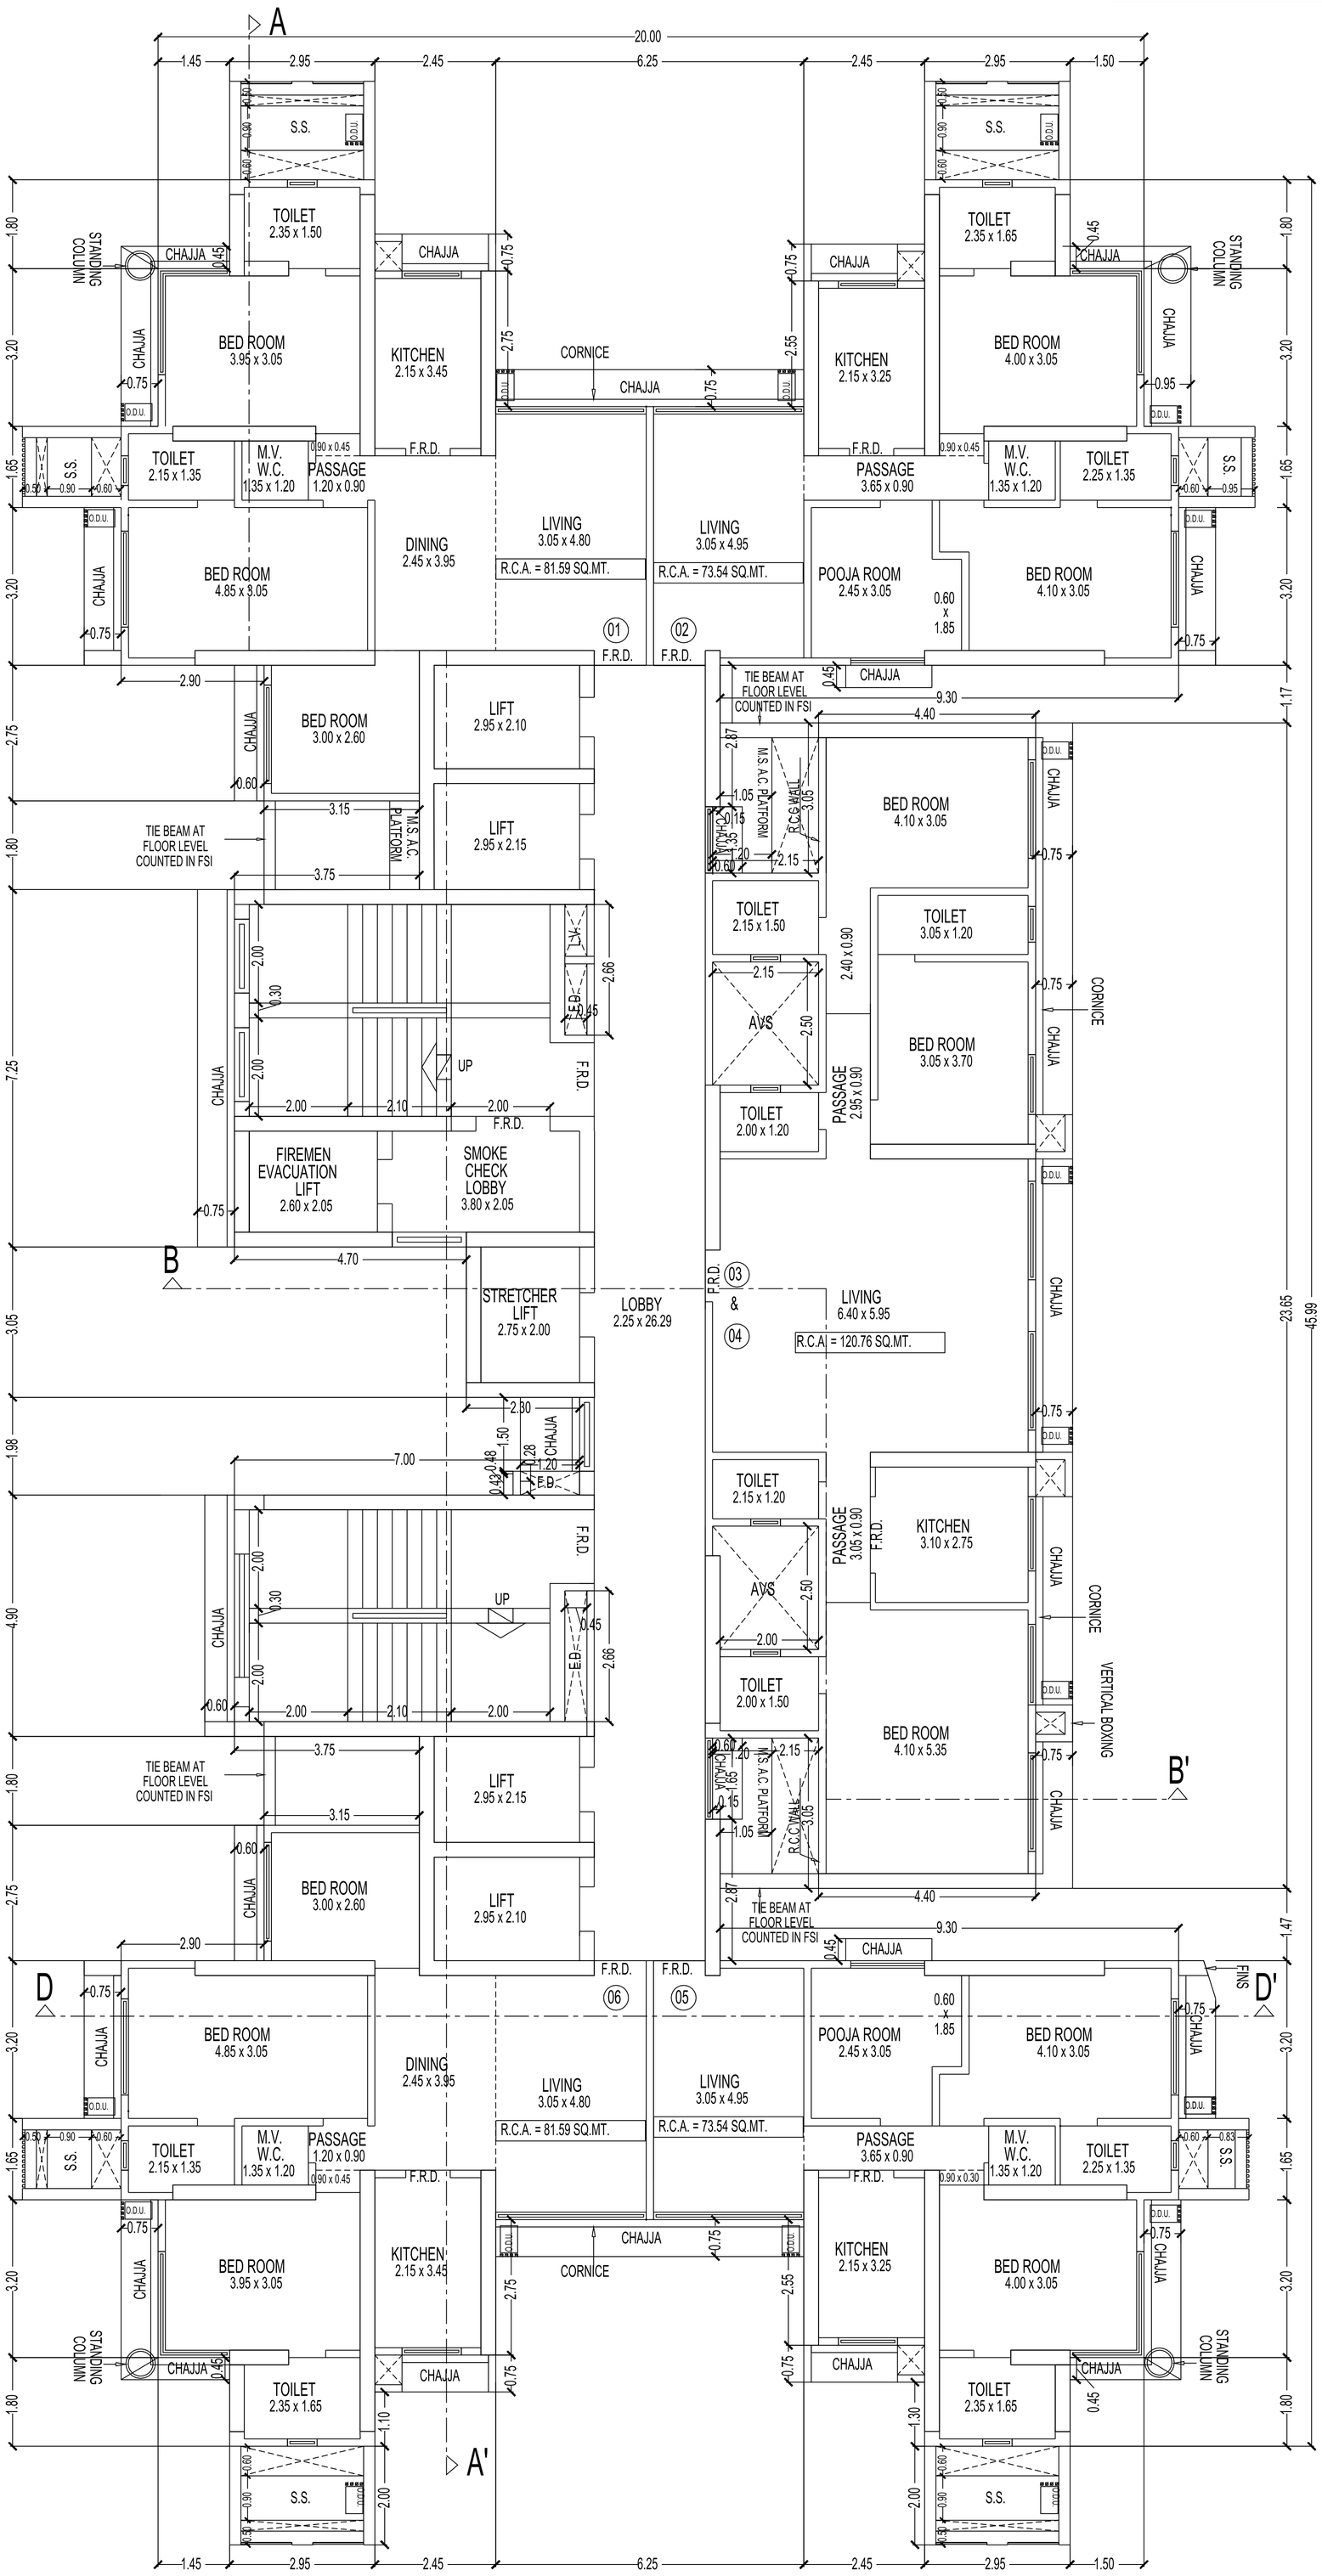

19th, 21st & 22nd FLOOR PLAN


SCALE 1:100

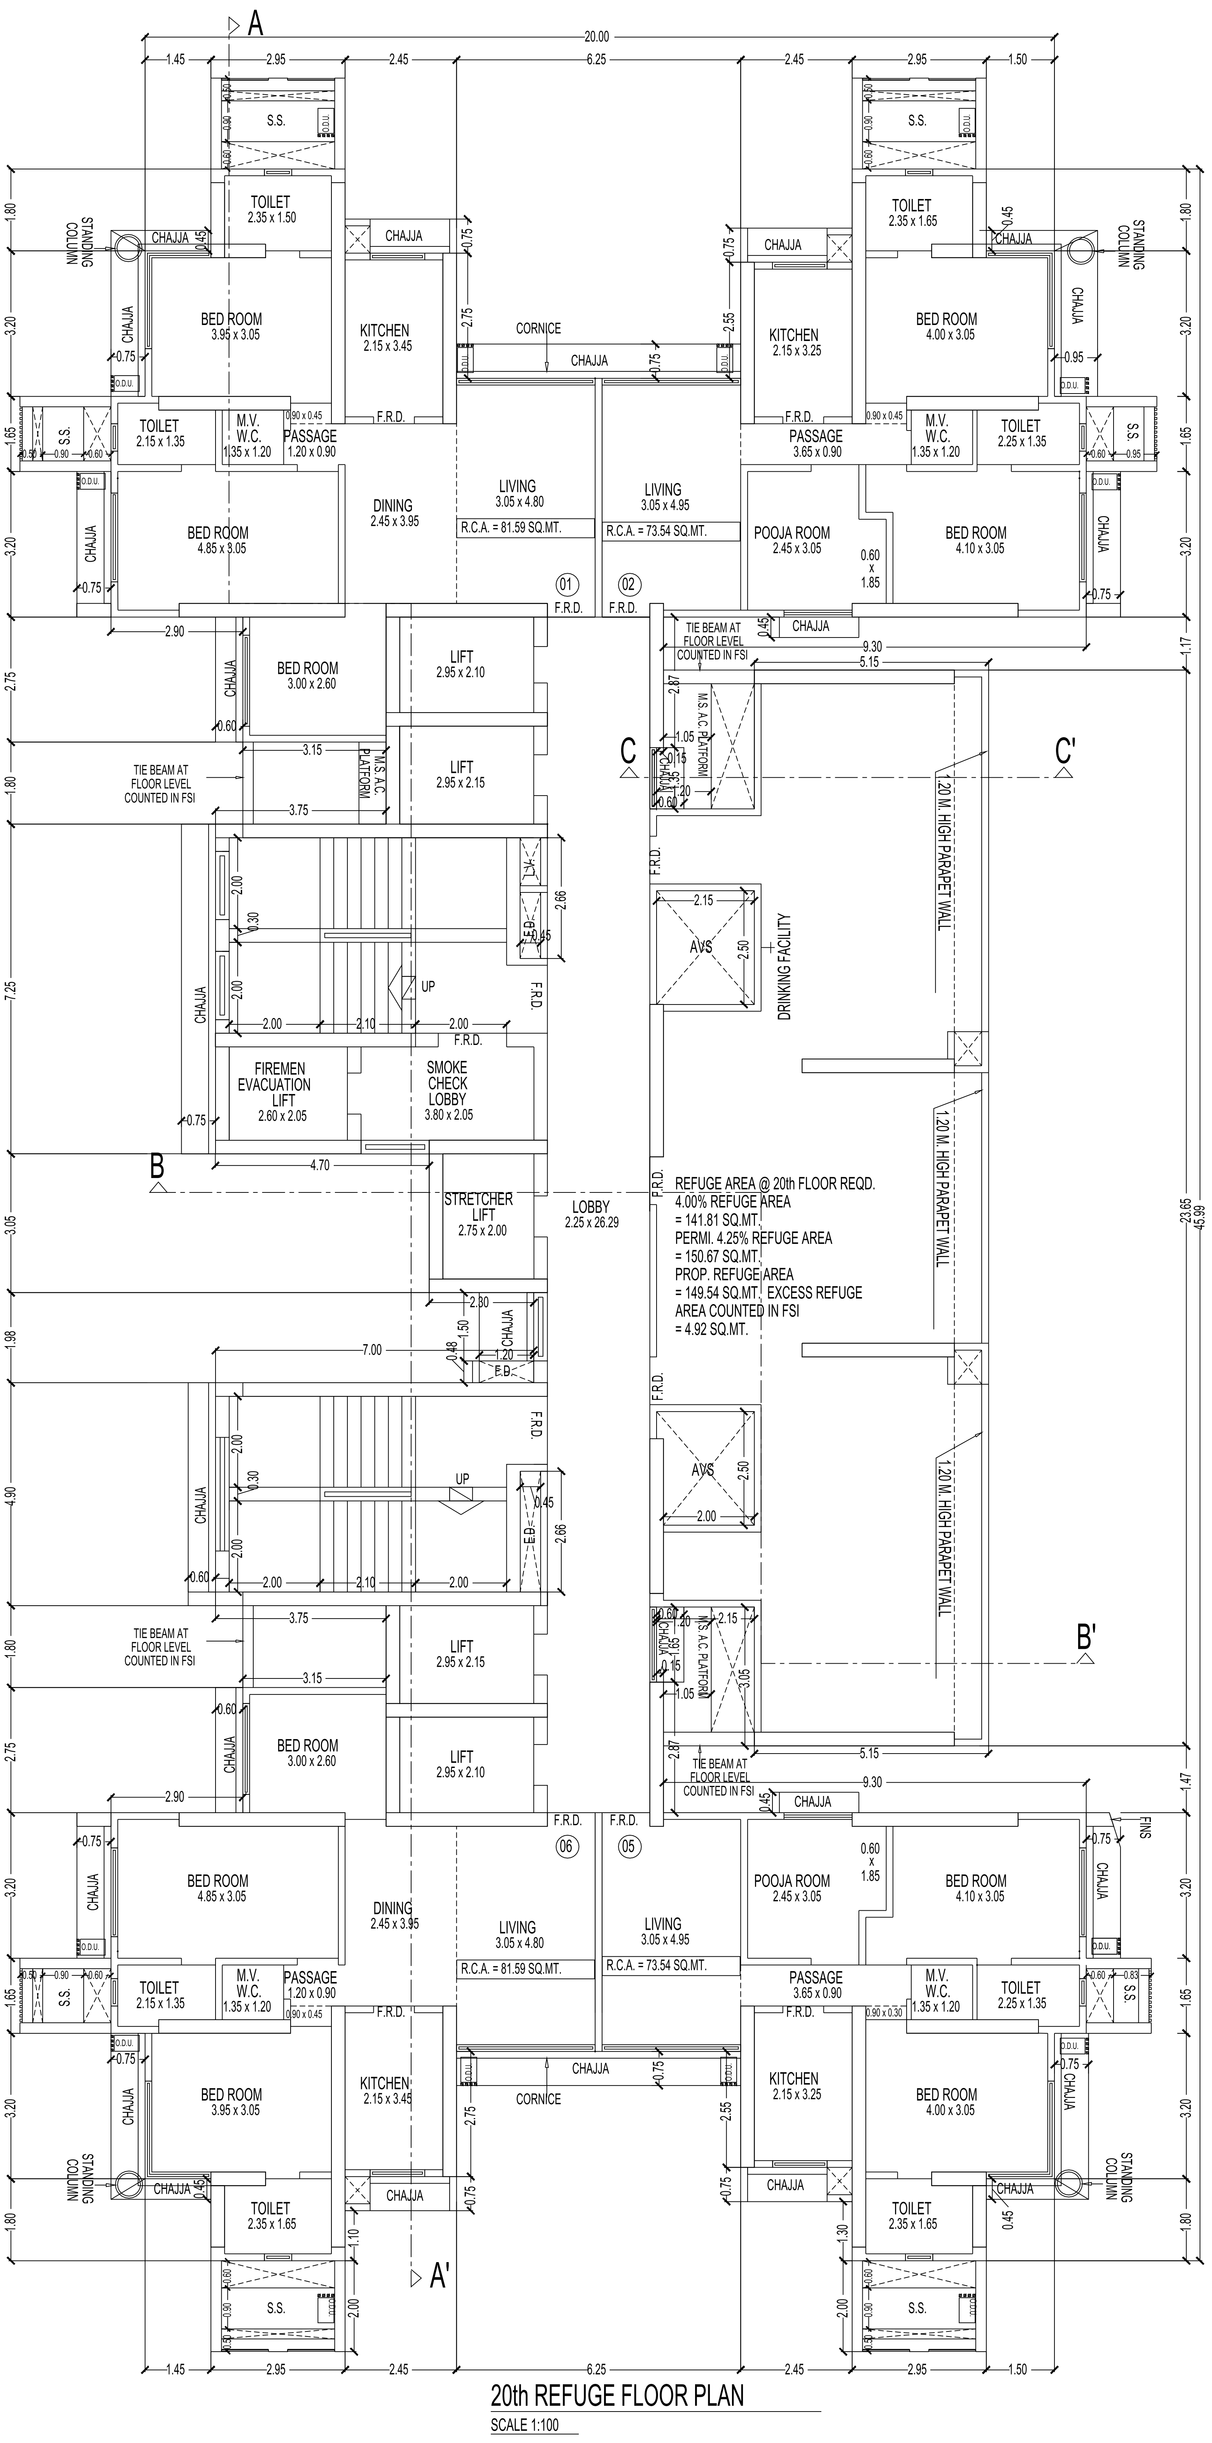


20th REFUGE FLOOR PLAN

SCALE 1:100

FILE No. :- P-24911/2025/(395A And Other)/R/N Ward/BORIVALI-R/N

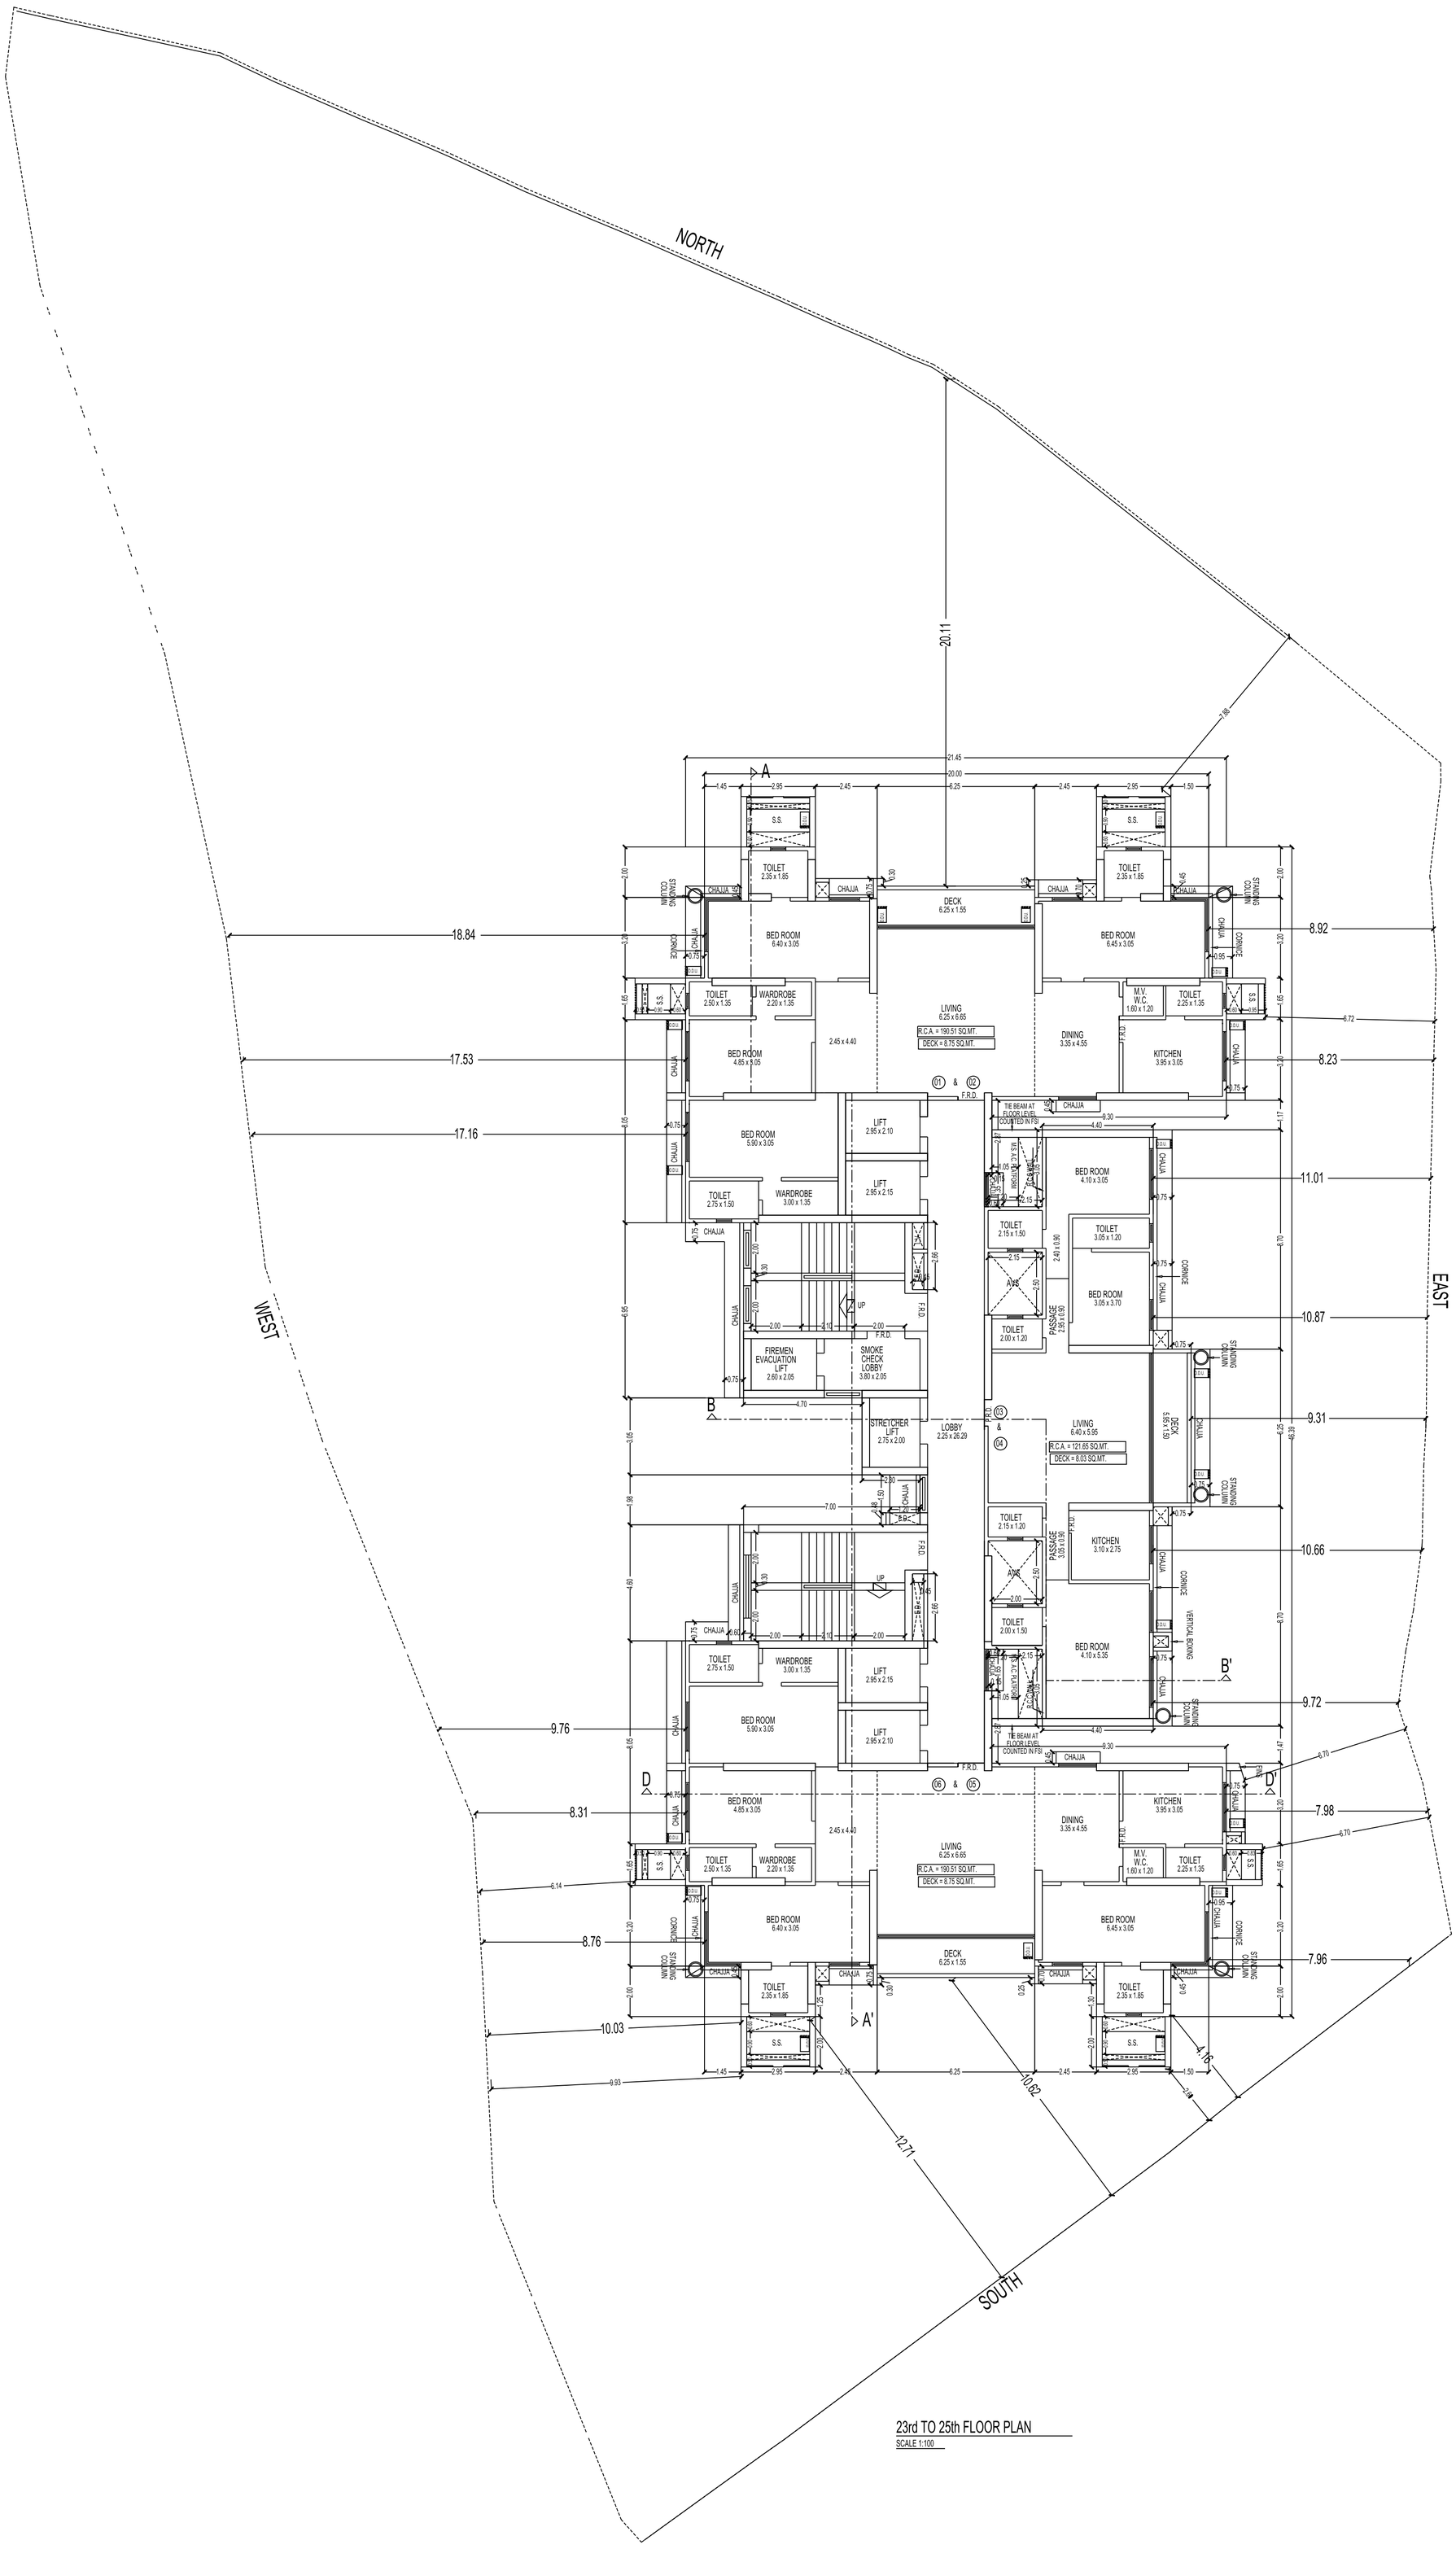

FILE No. :- P-24911/2025/(395A And Other)/R/N Ward/BORIVALI-R/N

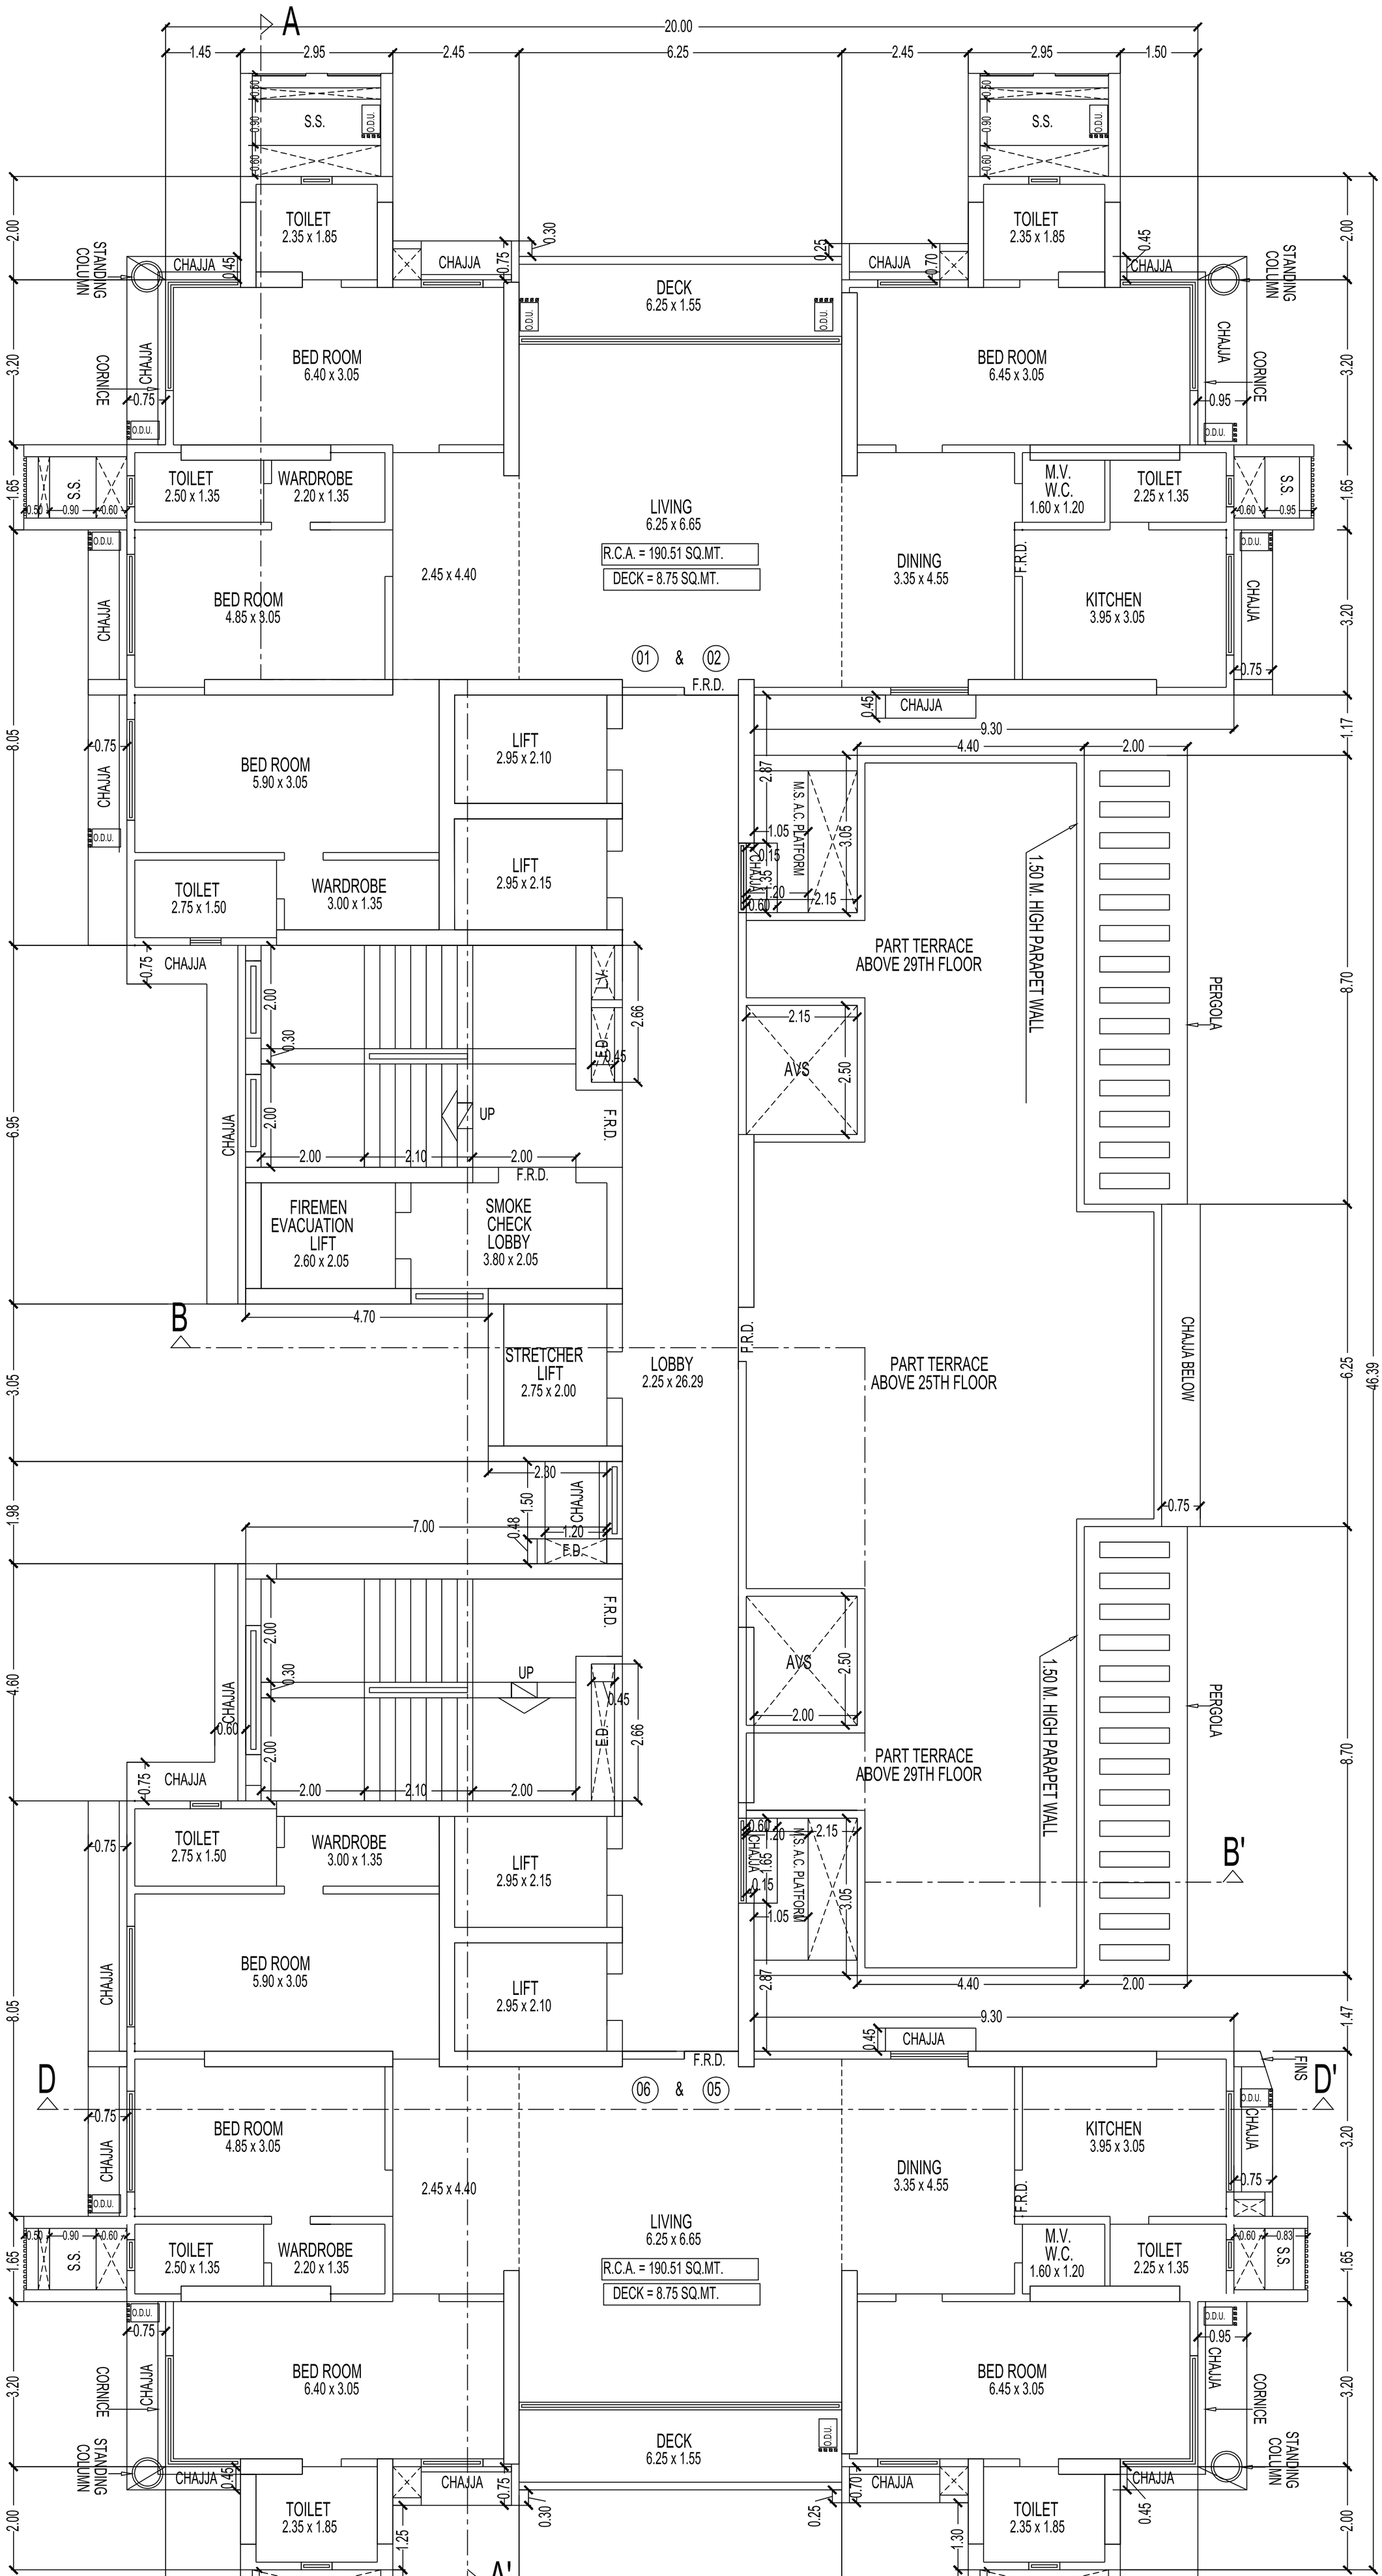

26th FLOOR PLAN

SCALE 1:100