
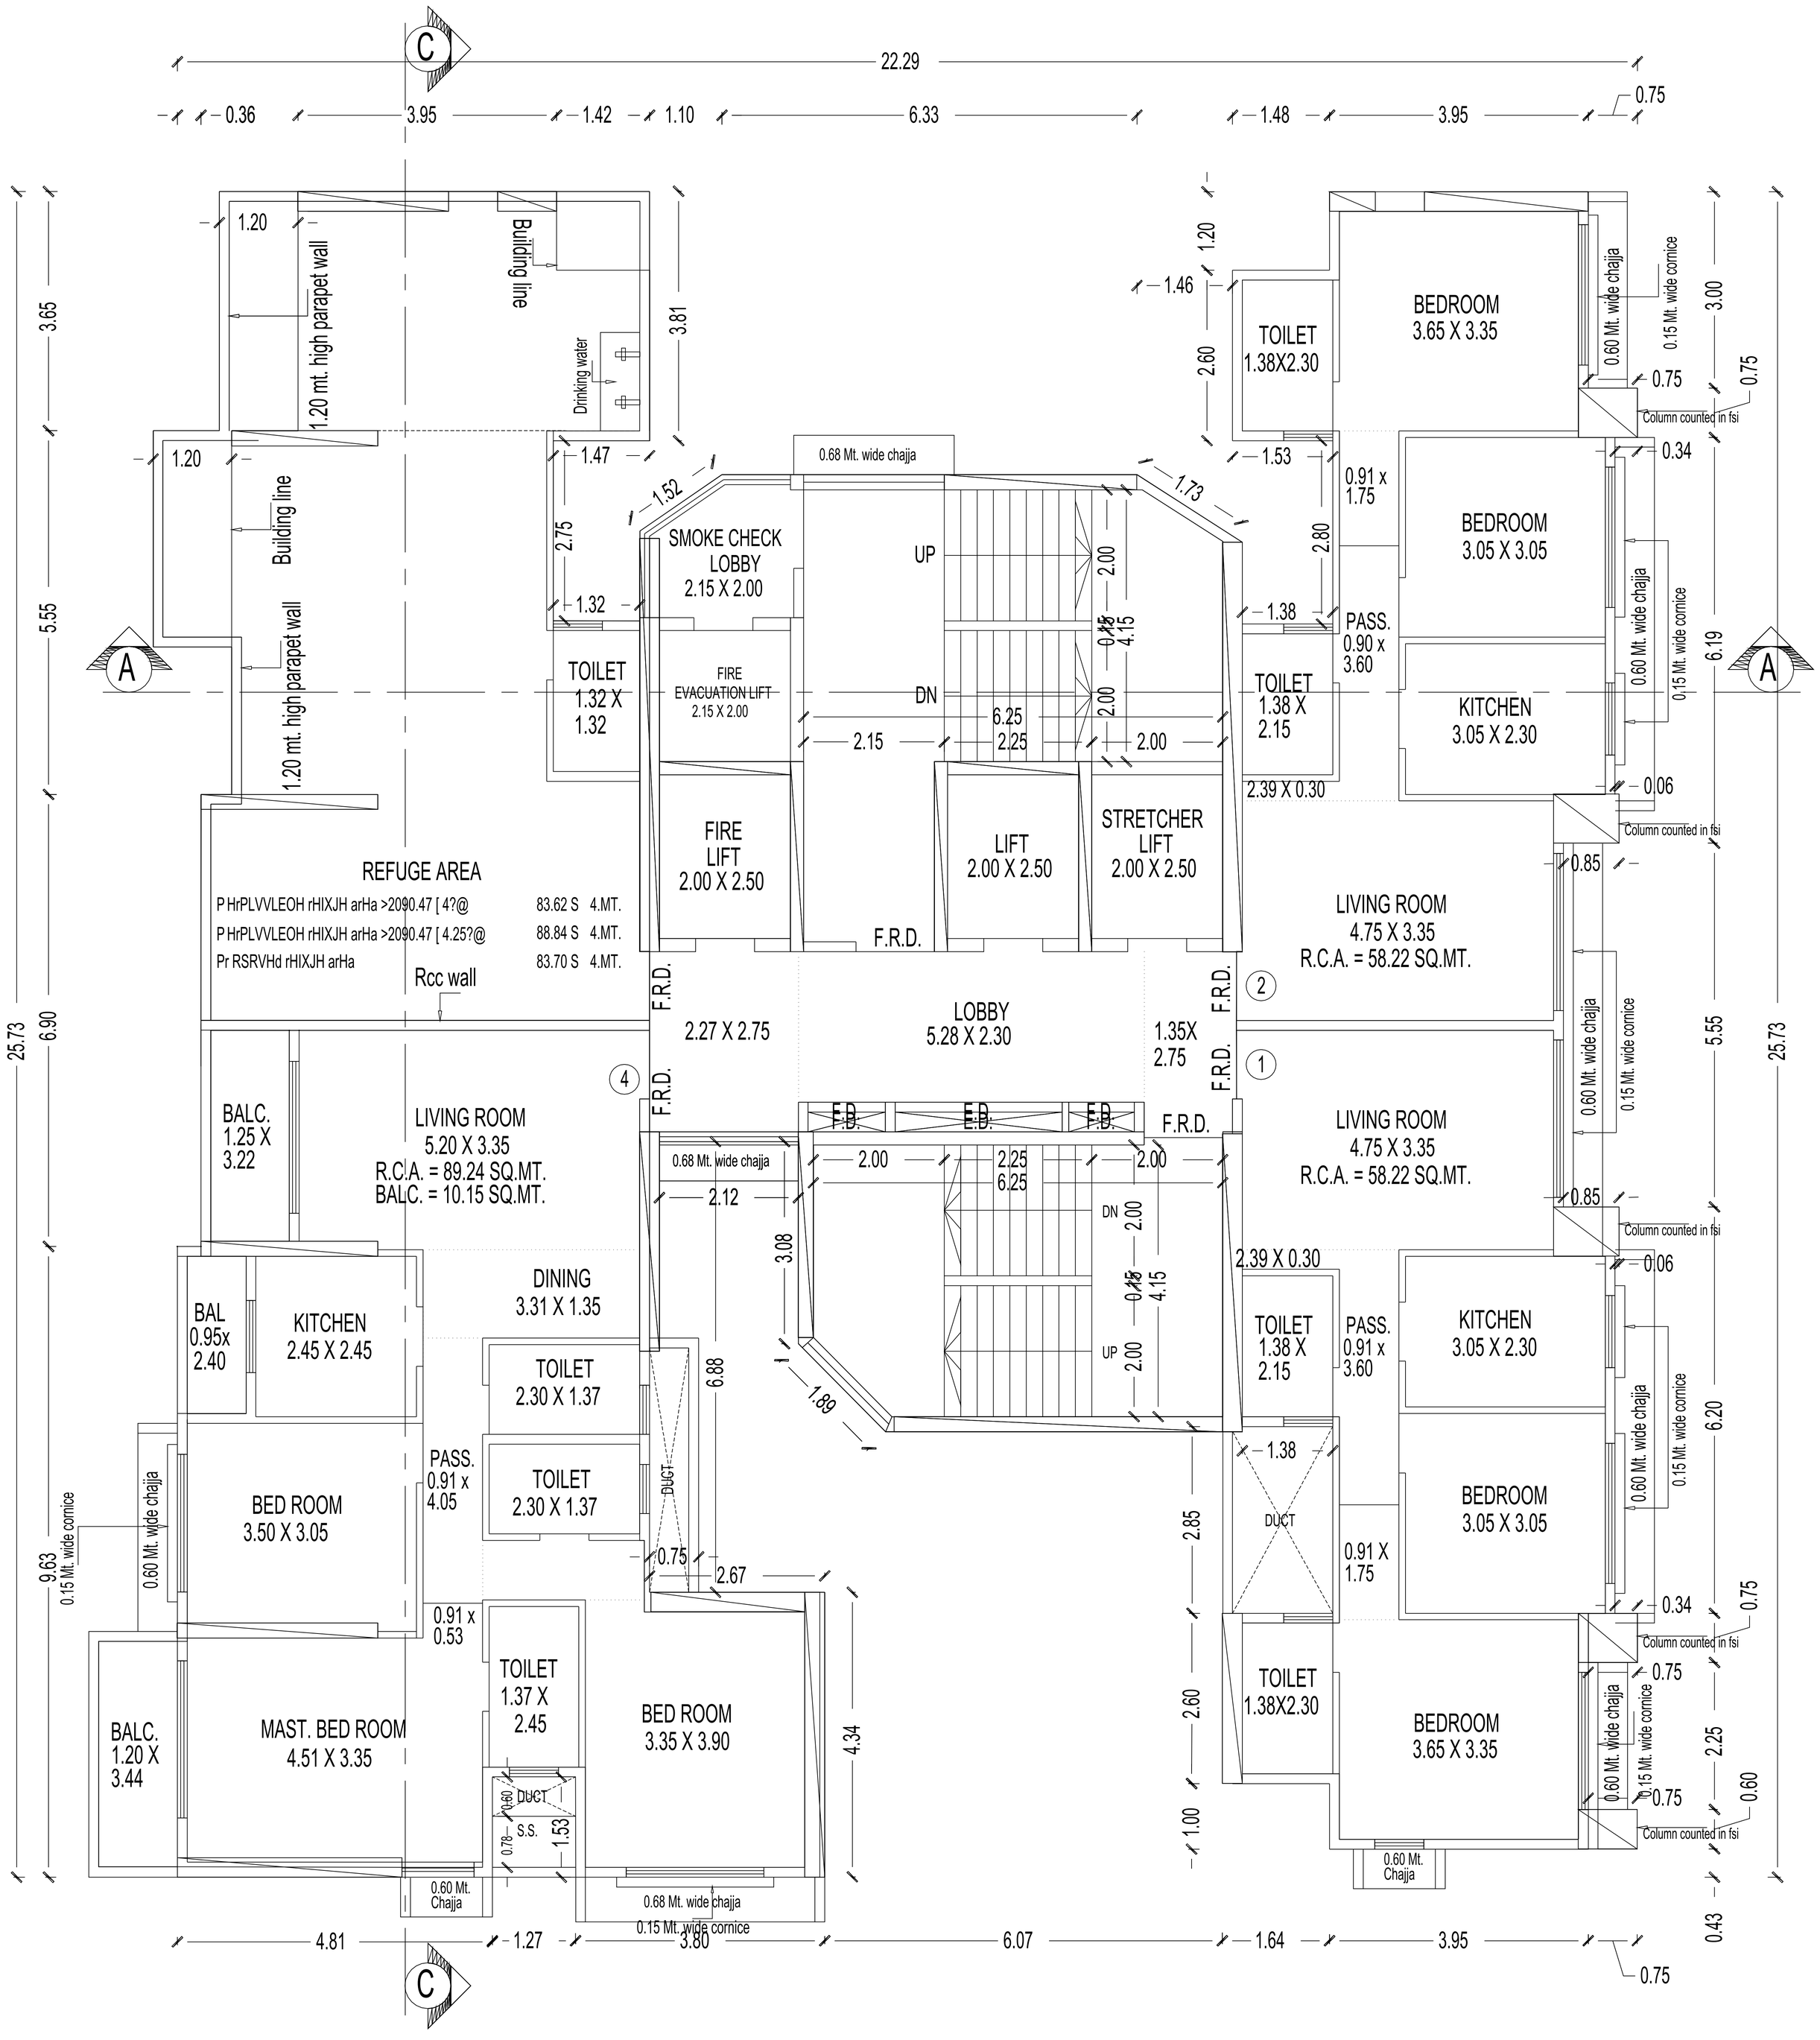


3RD & 10TH (REFUGE) FLOOR PLAN

SCALE :- 1:100


WING - A

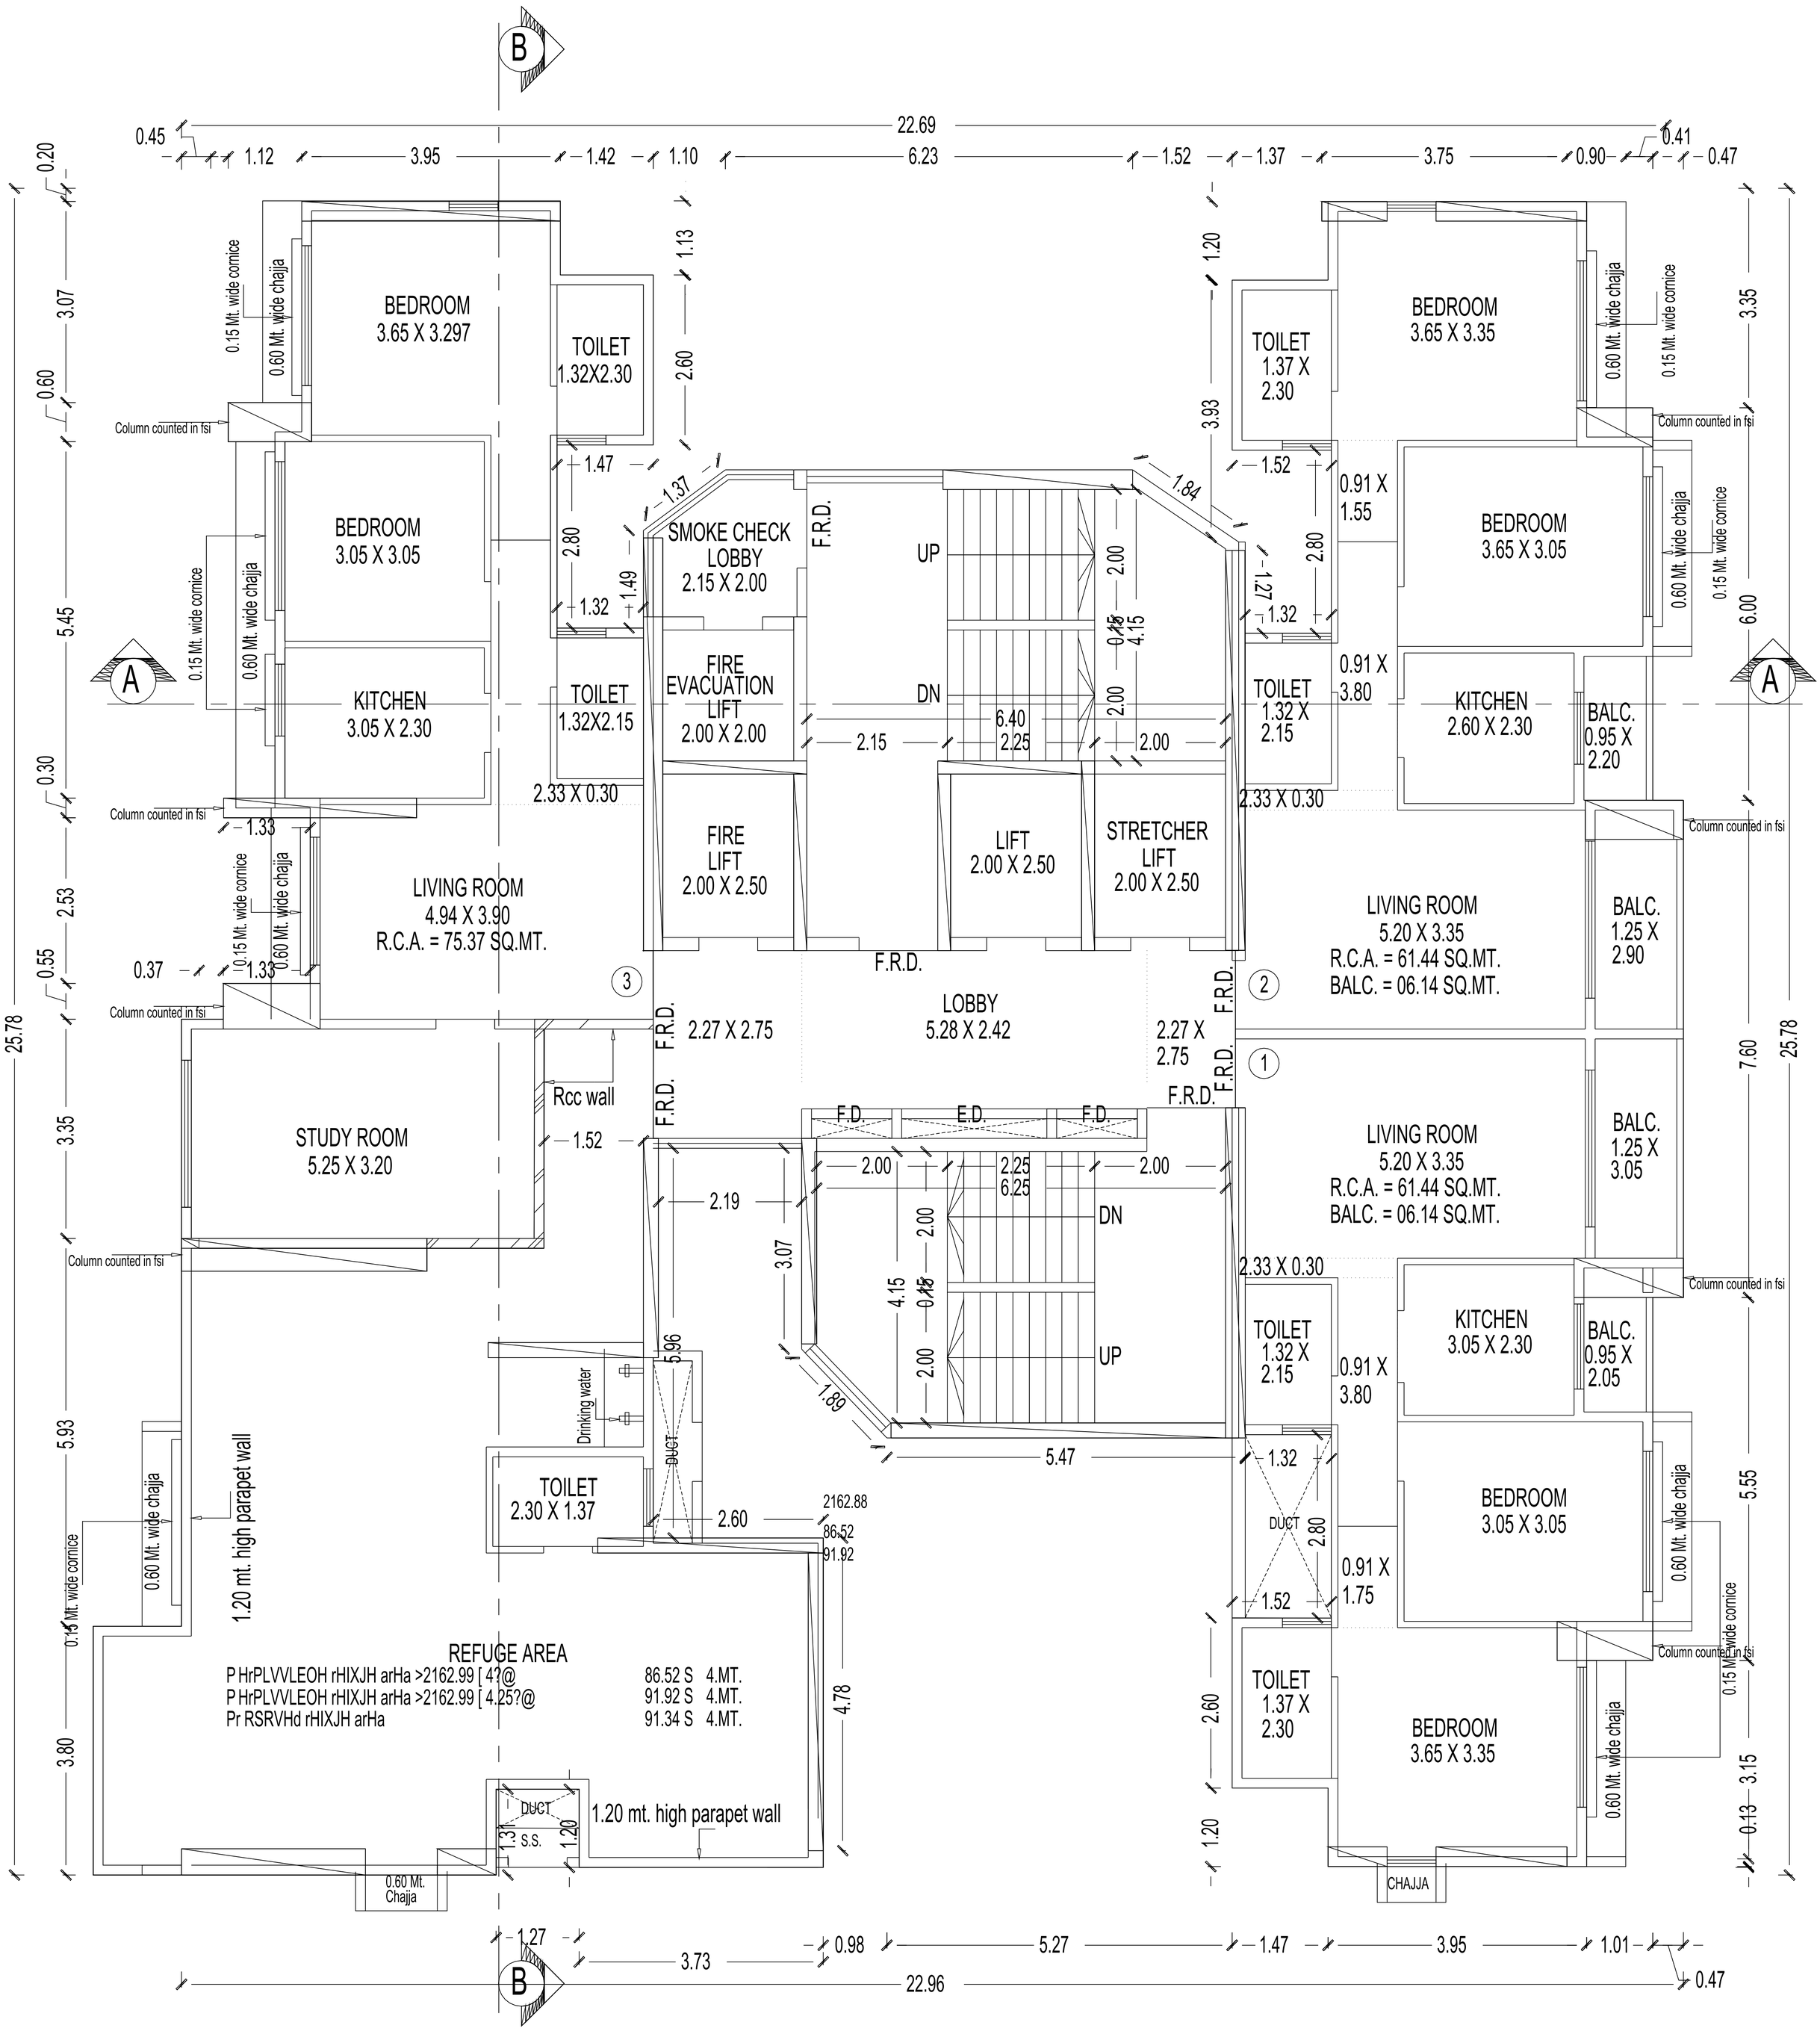

3RD & 10TH (REFUGE) FLOOR PLAN

SCALE :- 1:100

WING - B

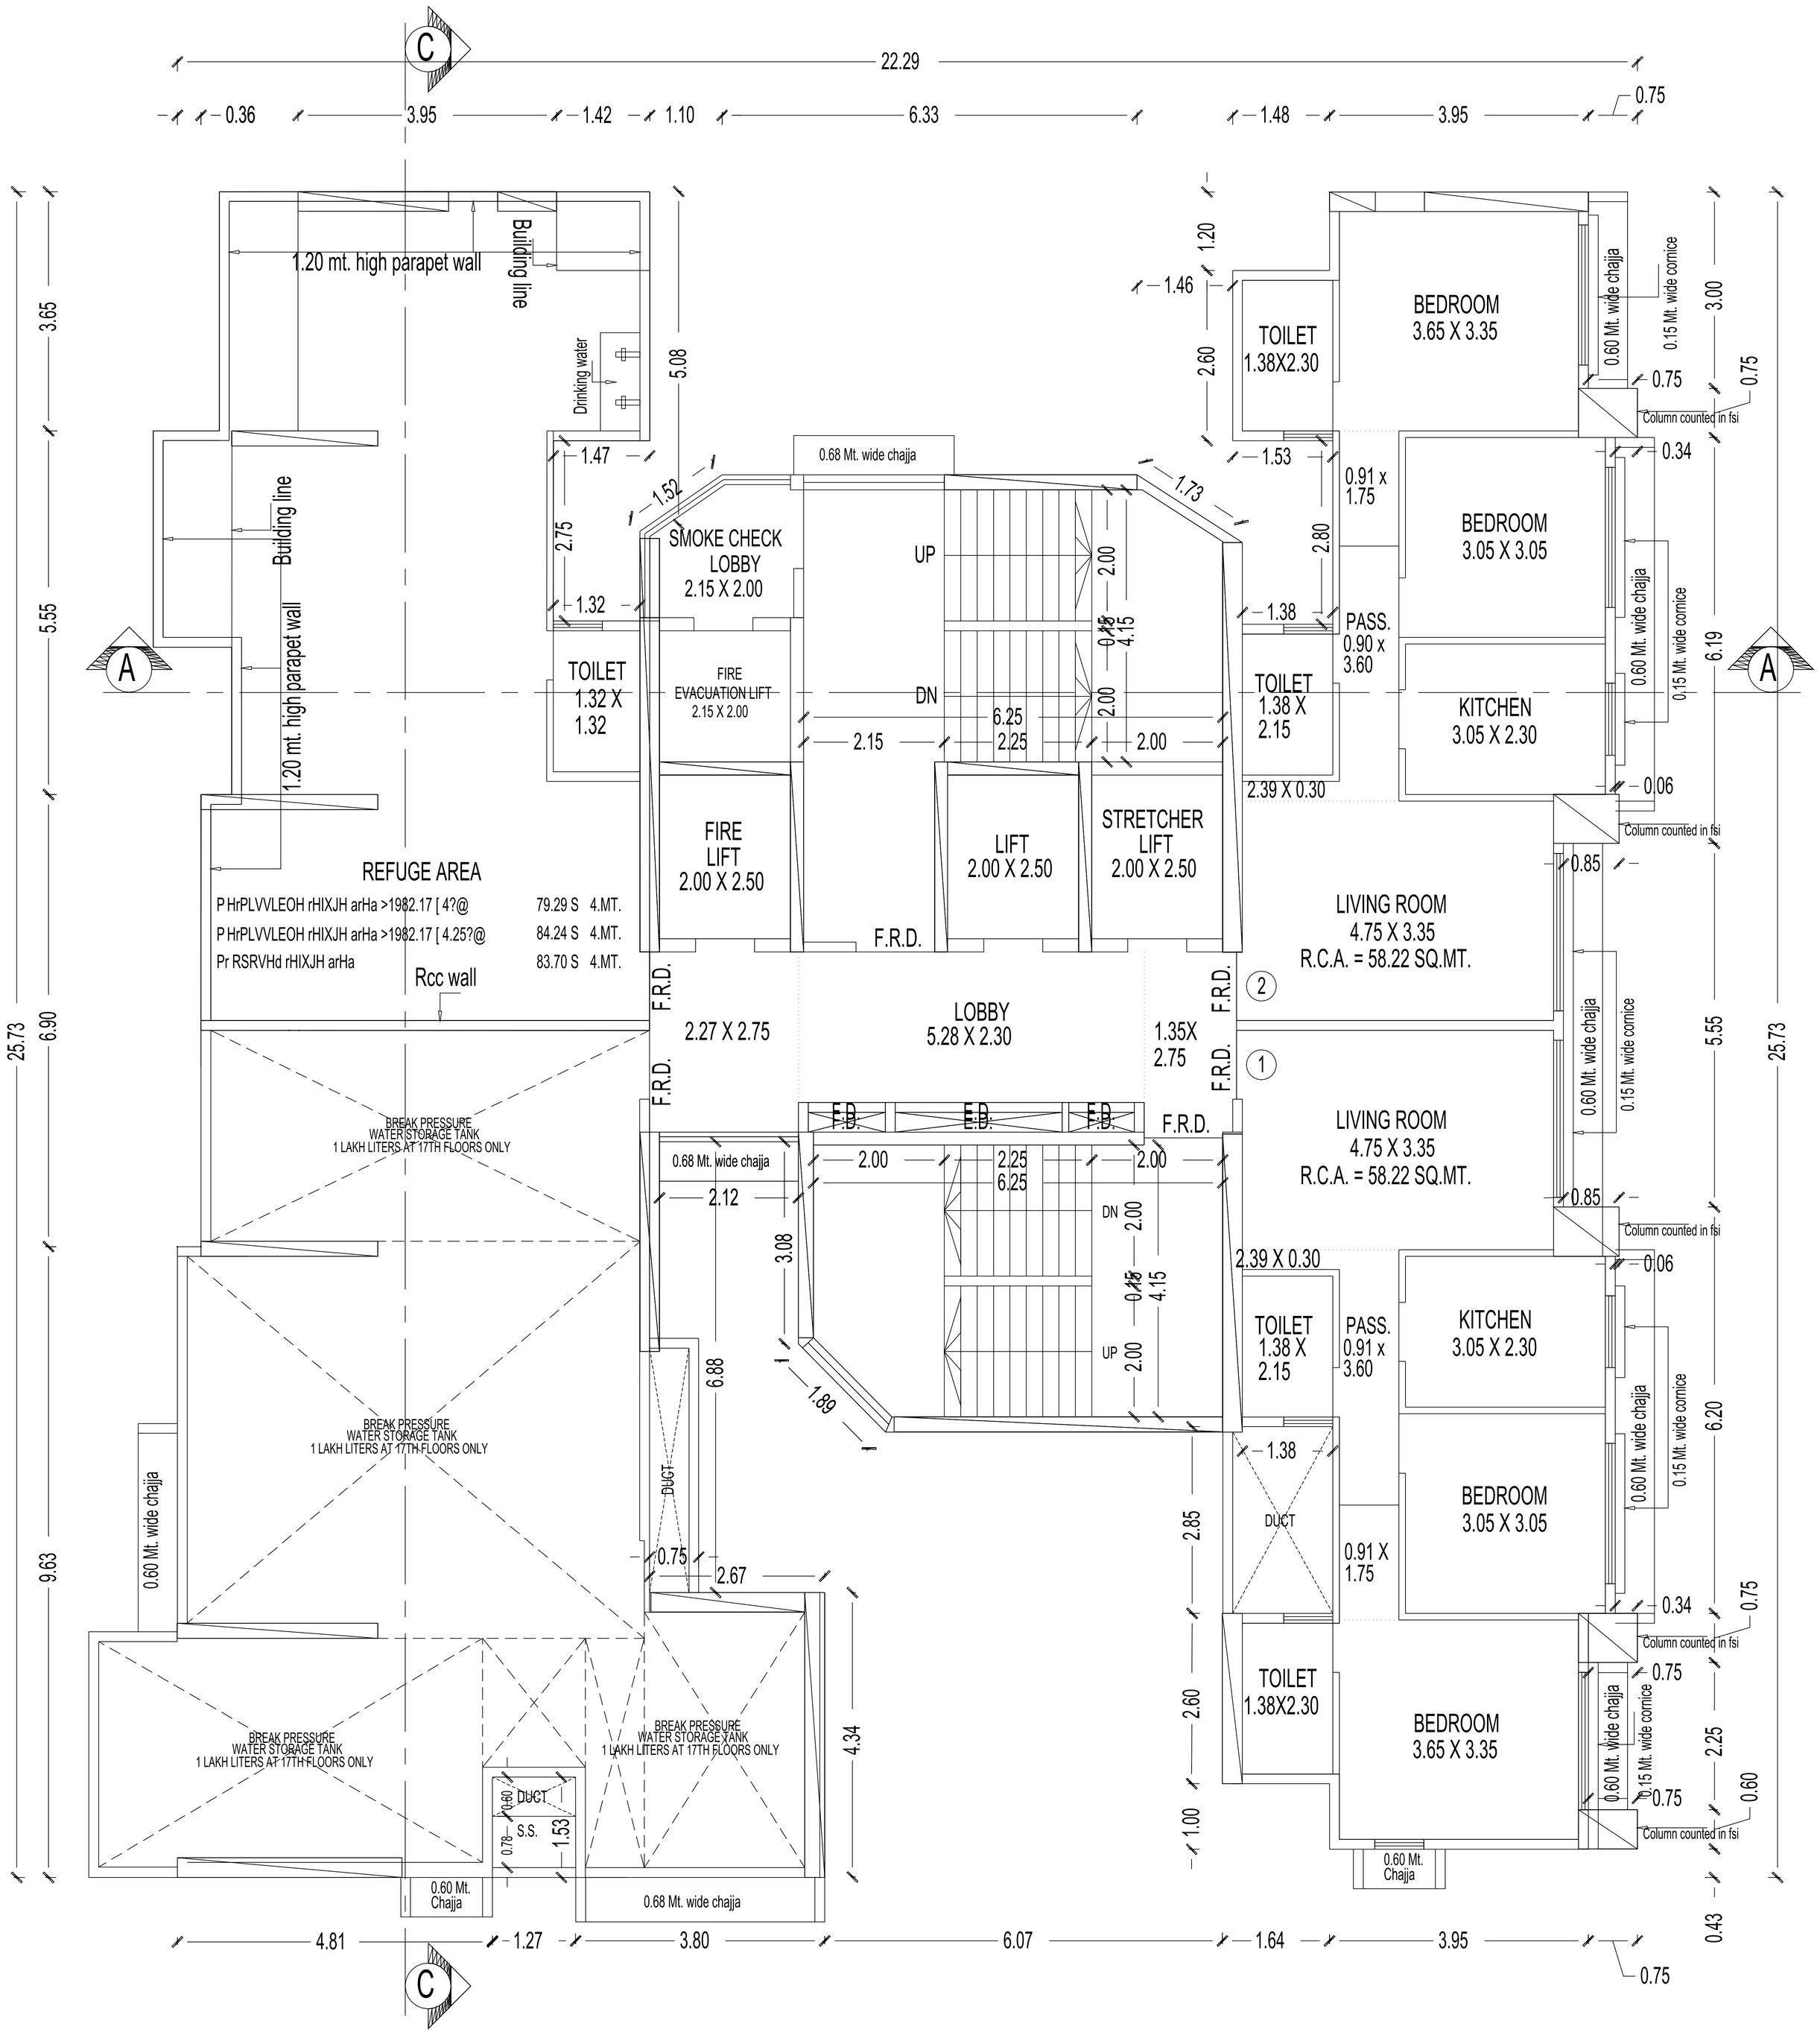

17TH (REFUGE) FLOOR PLAN

SCALE :- 1:100

WING - A

B

22.69

0.45 | 1.12 | 3.95 | 1.42 | 1.10 | 6.23 | 1.52 | 1.37 | 3.75 | 0.90 | 0.41 | 0.47

0.20 | 3.07 | 0.60 | 5.45 | 0.30 | 2.53 | 0.55 | 3.35 | 5.93 | 3.80 | 0.15 Mt. wide cornice | 0.60 Mt. wide chajja

25.78

BREAK PRESSURE
WATER STORAGE TANK
1 LAKH LITERS AT 17TH FLOORS ONLY

Column counted in fsi

0.60 Mt. wide chajja

1.13 | 2.60 | 2.80 | 1.48 | 1.49 | 1.32 | 1.37

SMOKE CHECK
LOBBY
2.15 X 2.00

F.R.D.

FIRE
EVACUATION
LIFT
2.00 X 2.00

UP | DN

2.00 | 0.15 | 4.15 | 2.00 | 6.40 | 2.15 | 2.25 | 2.00

FIRE
LIFT
2.00 X 2.50

LIFT
2.00 X 2.50

STRETCHER
LIFT
2.00 X 2.50

F.R.D.

LOBBY
5.28 X 2.42

2.27 X 2.75

2.27 X
2.75

F.R.D.

F.D. | E.D. | F.D.

Rcc wall

2.00 | 2.25 | 6.25 | 2.00 | 2.19 | 3.07 | 4.15 | 1.89 | 5.47

DN | UP

Drinking water

DUCT

5.96

TOILET
2.30 X 1.37

2.60 | 2162.88 | 86.52 | 91.92

1.20 mt. high parapet wall

REFUGE AREA

P HrPLVVLEOH rHIXJH arHa >2078.98 [4?@	83.16 S	4.MT.
P HrPLVVLEOH rHIXJH arHa >2078.98 [4.25?@	88.36 S	4.MT.
Pr RSRVHd rHIXJH arHa	88.37 S	4.MT.

4.78

DUCT | 1.30 | S.S. | 1.20 | 1.20 mt. high parapet wall

1.84 | 1.52 | 3.93 | 1.20 | 1.27 | 1.32 | 2.80

TOILET
1.37 X
2.30

BEDROOM
3.65 X 3.35

0.91 X
1.55

BEDROOM
3.65 X 3.05

TOILET
1.32 X
2.15

0.91 X
3.80

KITCHEN
2.60 X 2.30

BALC.
0.95 X
2.20

2.33 X 0.30

Column counted in fsi

2

LIVING ROOM
5.20 X 3.35
R.C.A. = 61.44 SQ.MT.
BALC. = 06.14 SQ.MT.

BALC.
1.25 X
2.90

1

LIVING ROOM
5.20 X 3.35
R.C.A. = 61.44 SQ.MT.
BALC. = 06.14 SQ.MT.

BALC.
1.25 X
3.05

TOILET
1.32 X
2.15

0.91 X
3.80

KITCHEN
3.05 X 2.30

BALC.
0.95 X
2.05

DUCT | 2.80 | 1.32

BEDROOM
3.05 X 3.05

0.91 X
1.75

1.52

TOILET
1.37 X
2.30

BEDROOM
3.65 X 3.35

CHAJJA

7.60 | 5.55 | 3.15 | 0.13 | 1.20 | 2.60


1.27 | 3.73 | 0.98 | 5.27 | 1.47 | 3.95 | 1.01 | 0.47

B

17TH (REFUGE) FLOOR PLAN


SCALE :- 1:100

WING - B

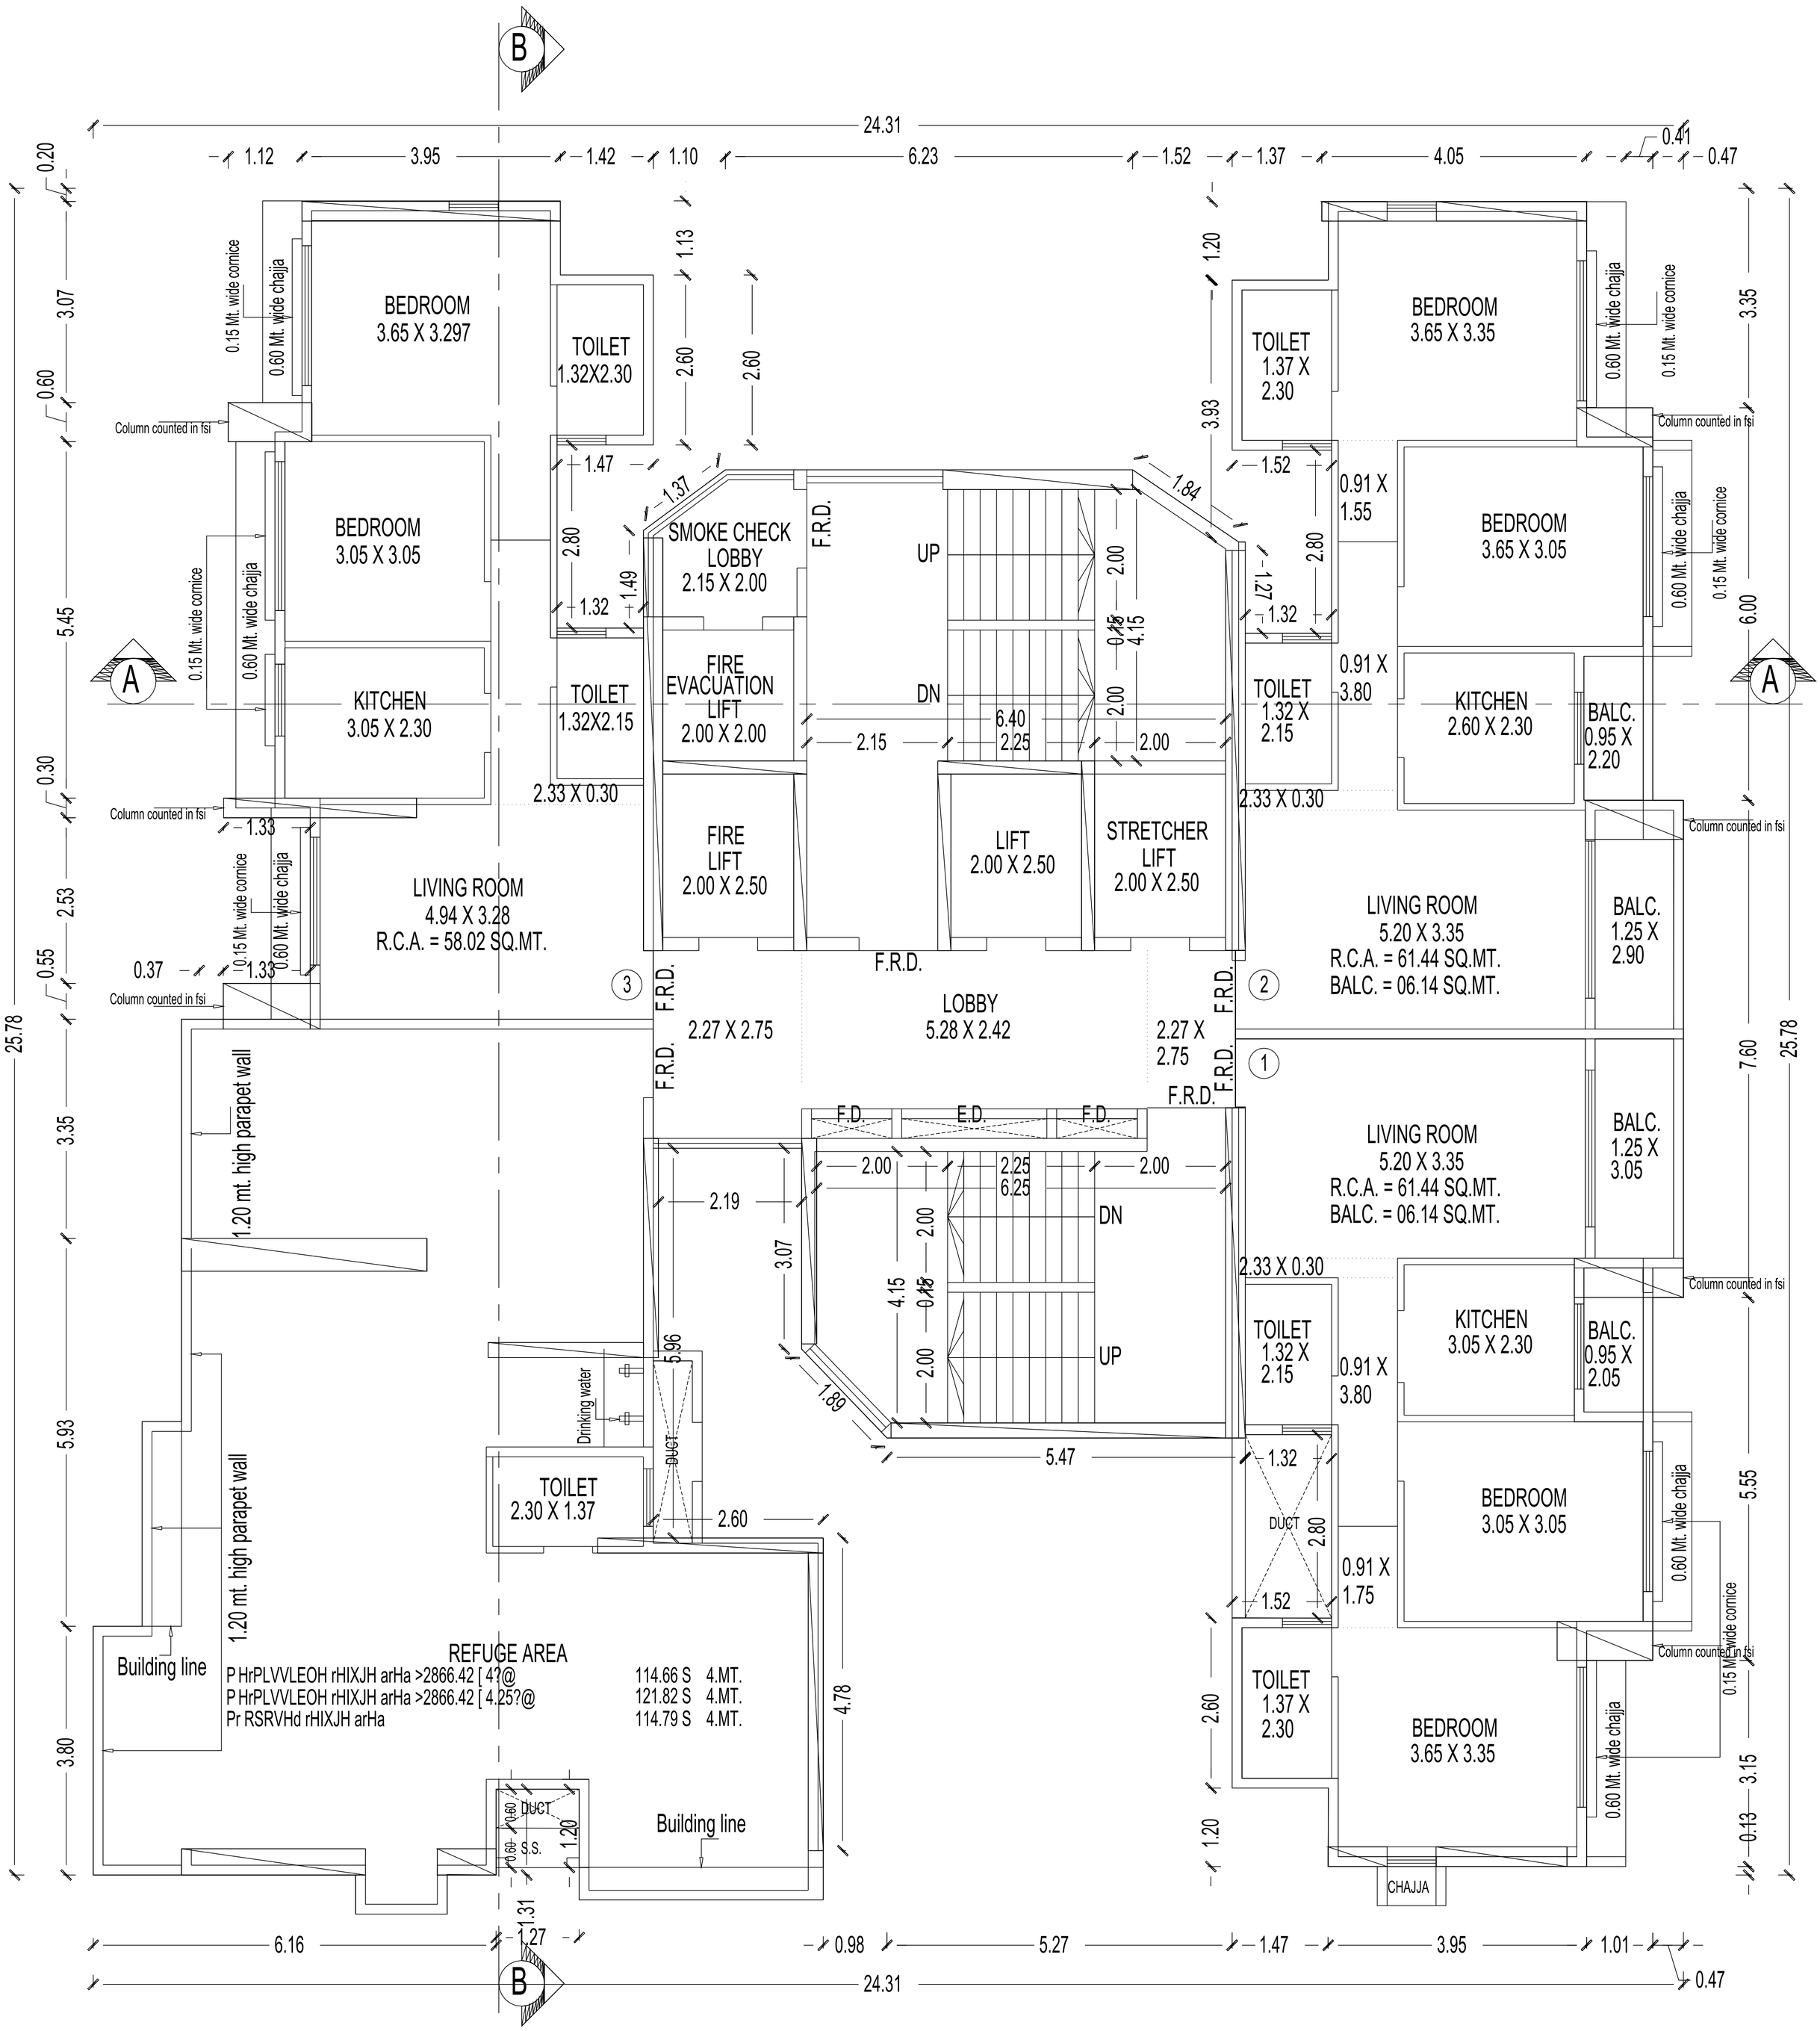

24TH (REFUGE) FLOOR PLAN


SCALE :- 1:100 WING - B

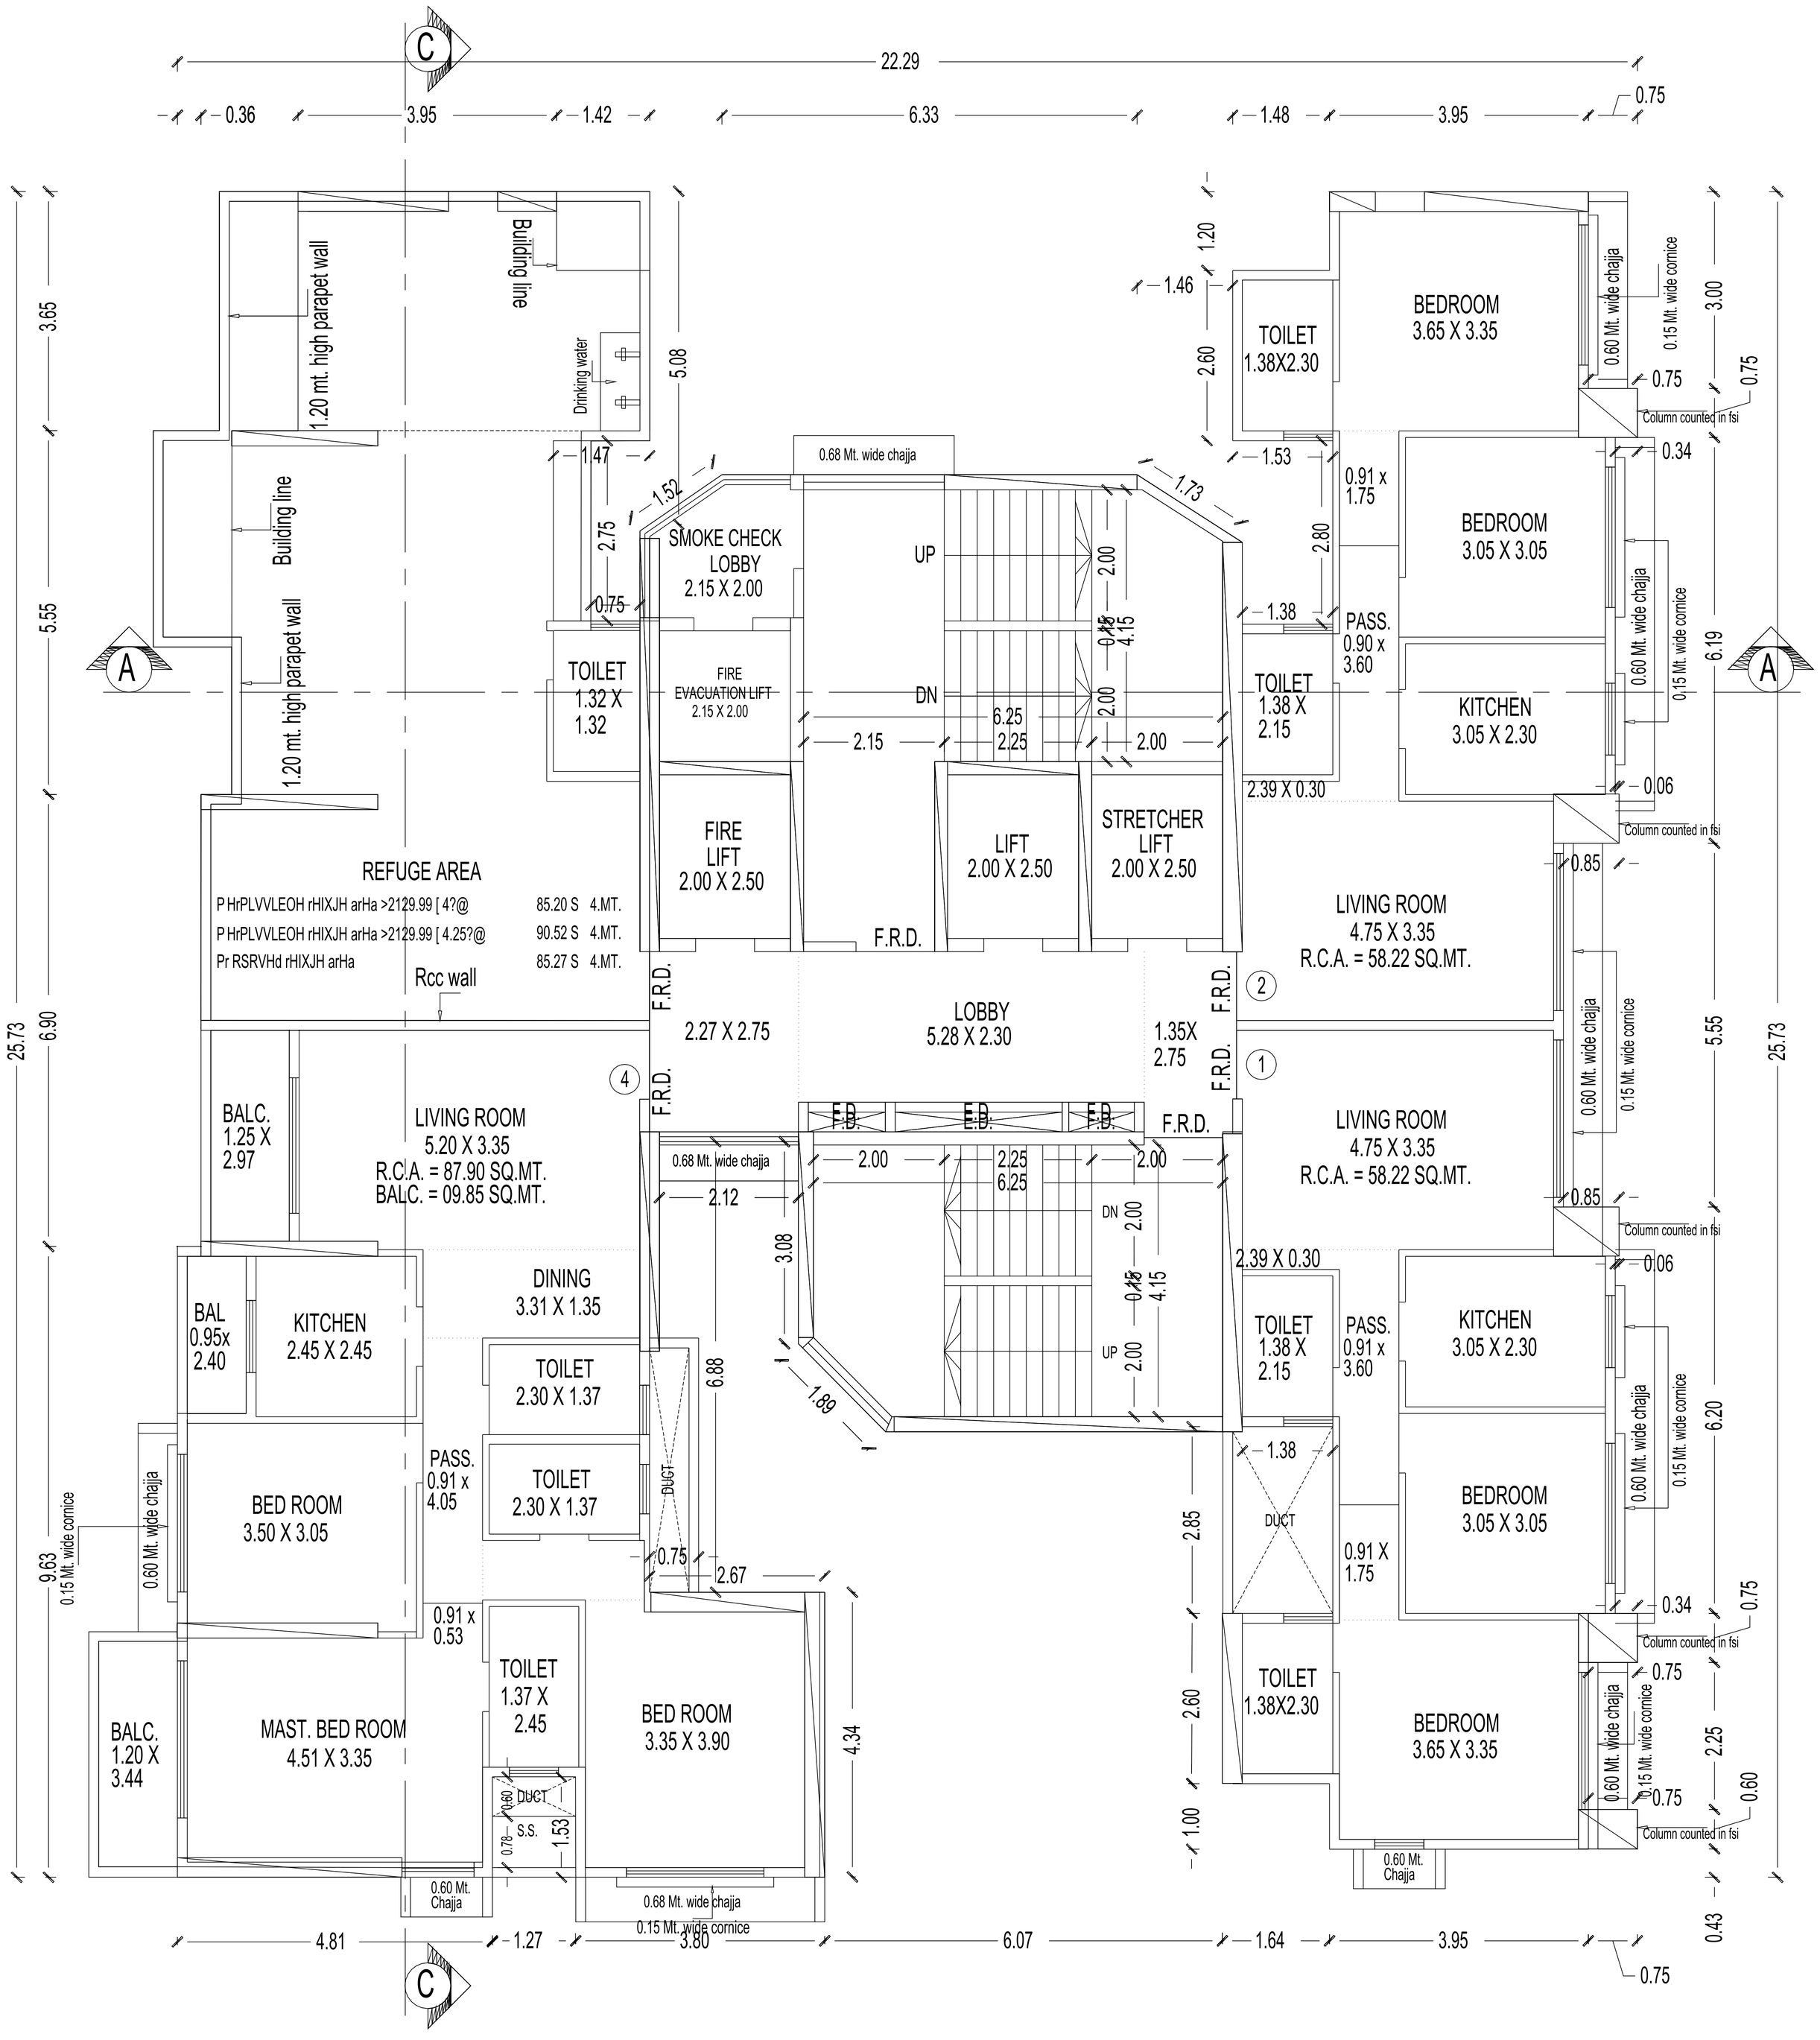

24TH (REFUGE) FLOOR PLAN

SCALE :- 1:100

WING - A

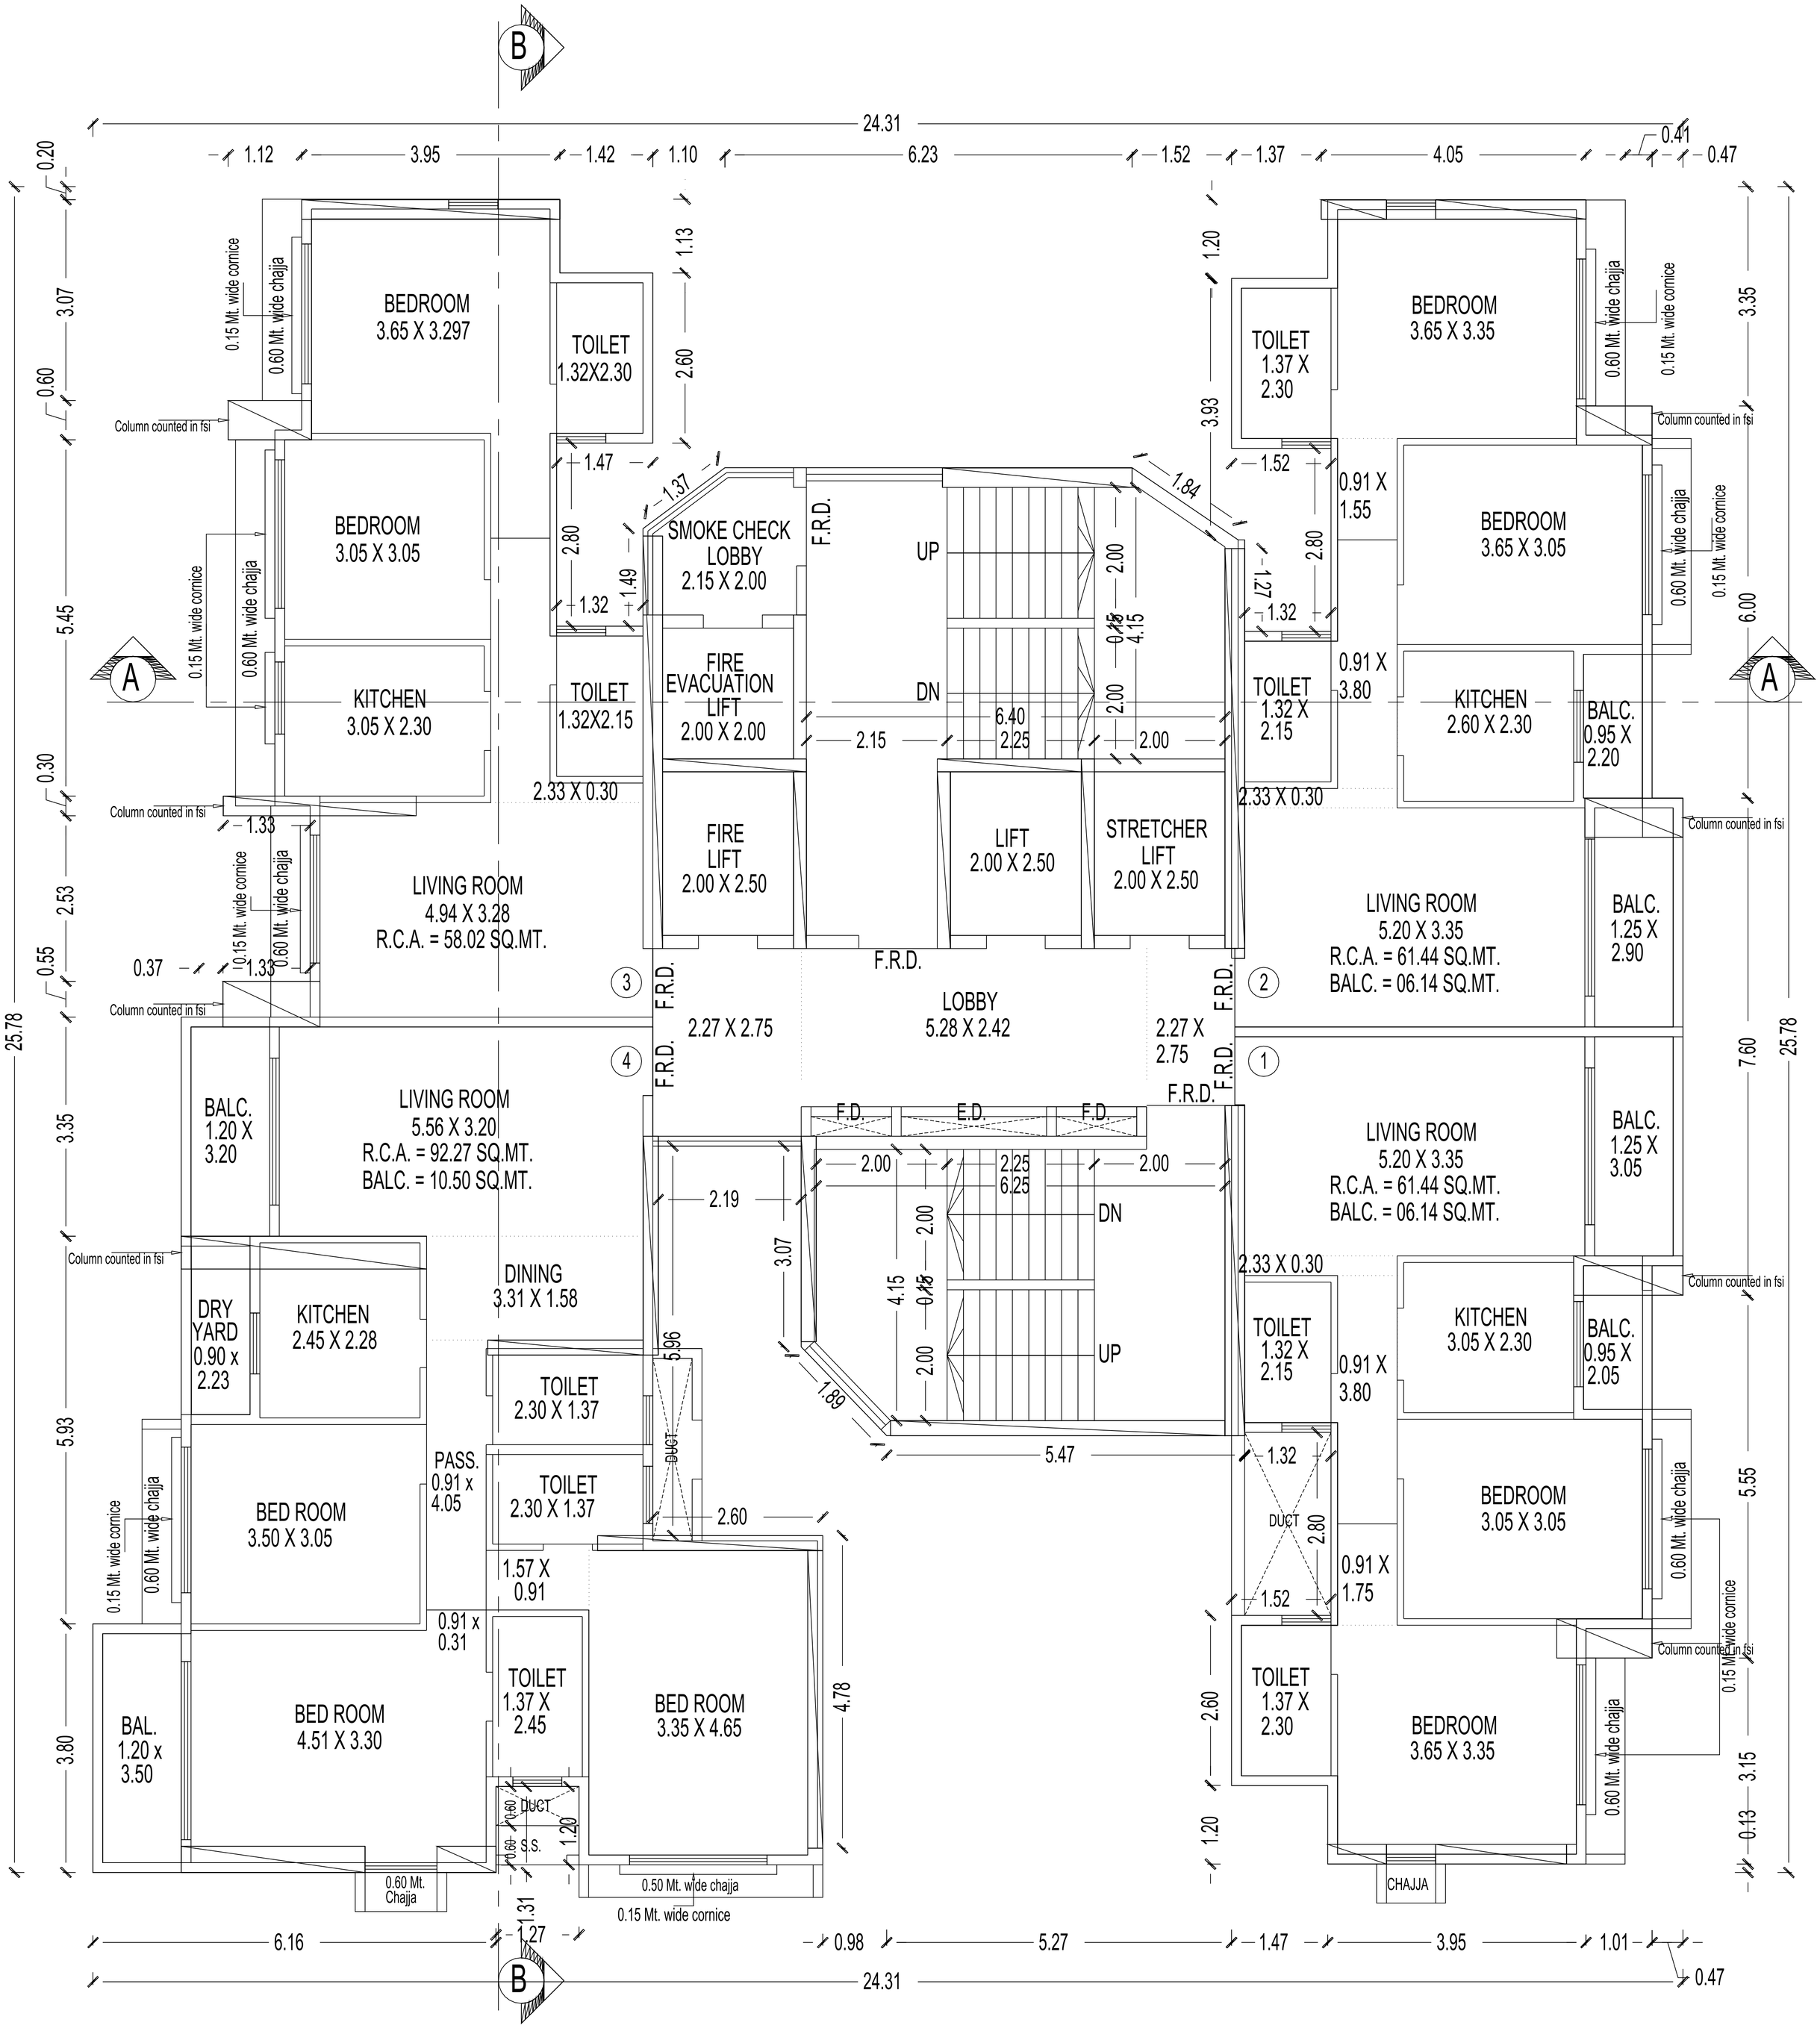


1ST, 2ND, 4TH TO 9TH, 11TH TO 16TH, 18TH TO 23RD,

25TH TO 27TH FLOOR PLAN

SCALE :- 1:100

WING - B

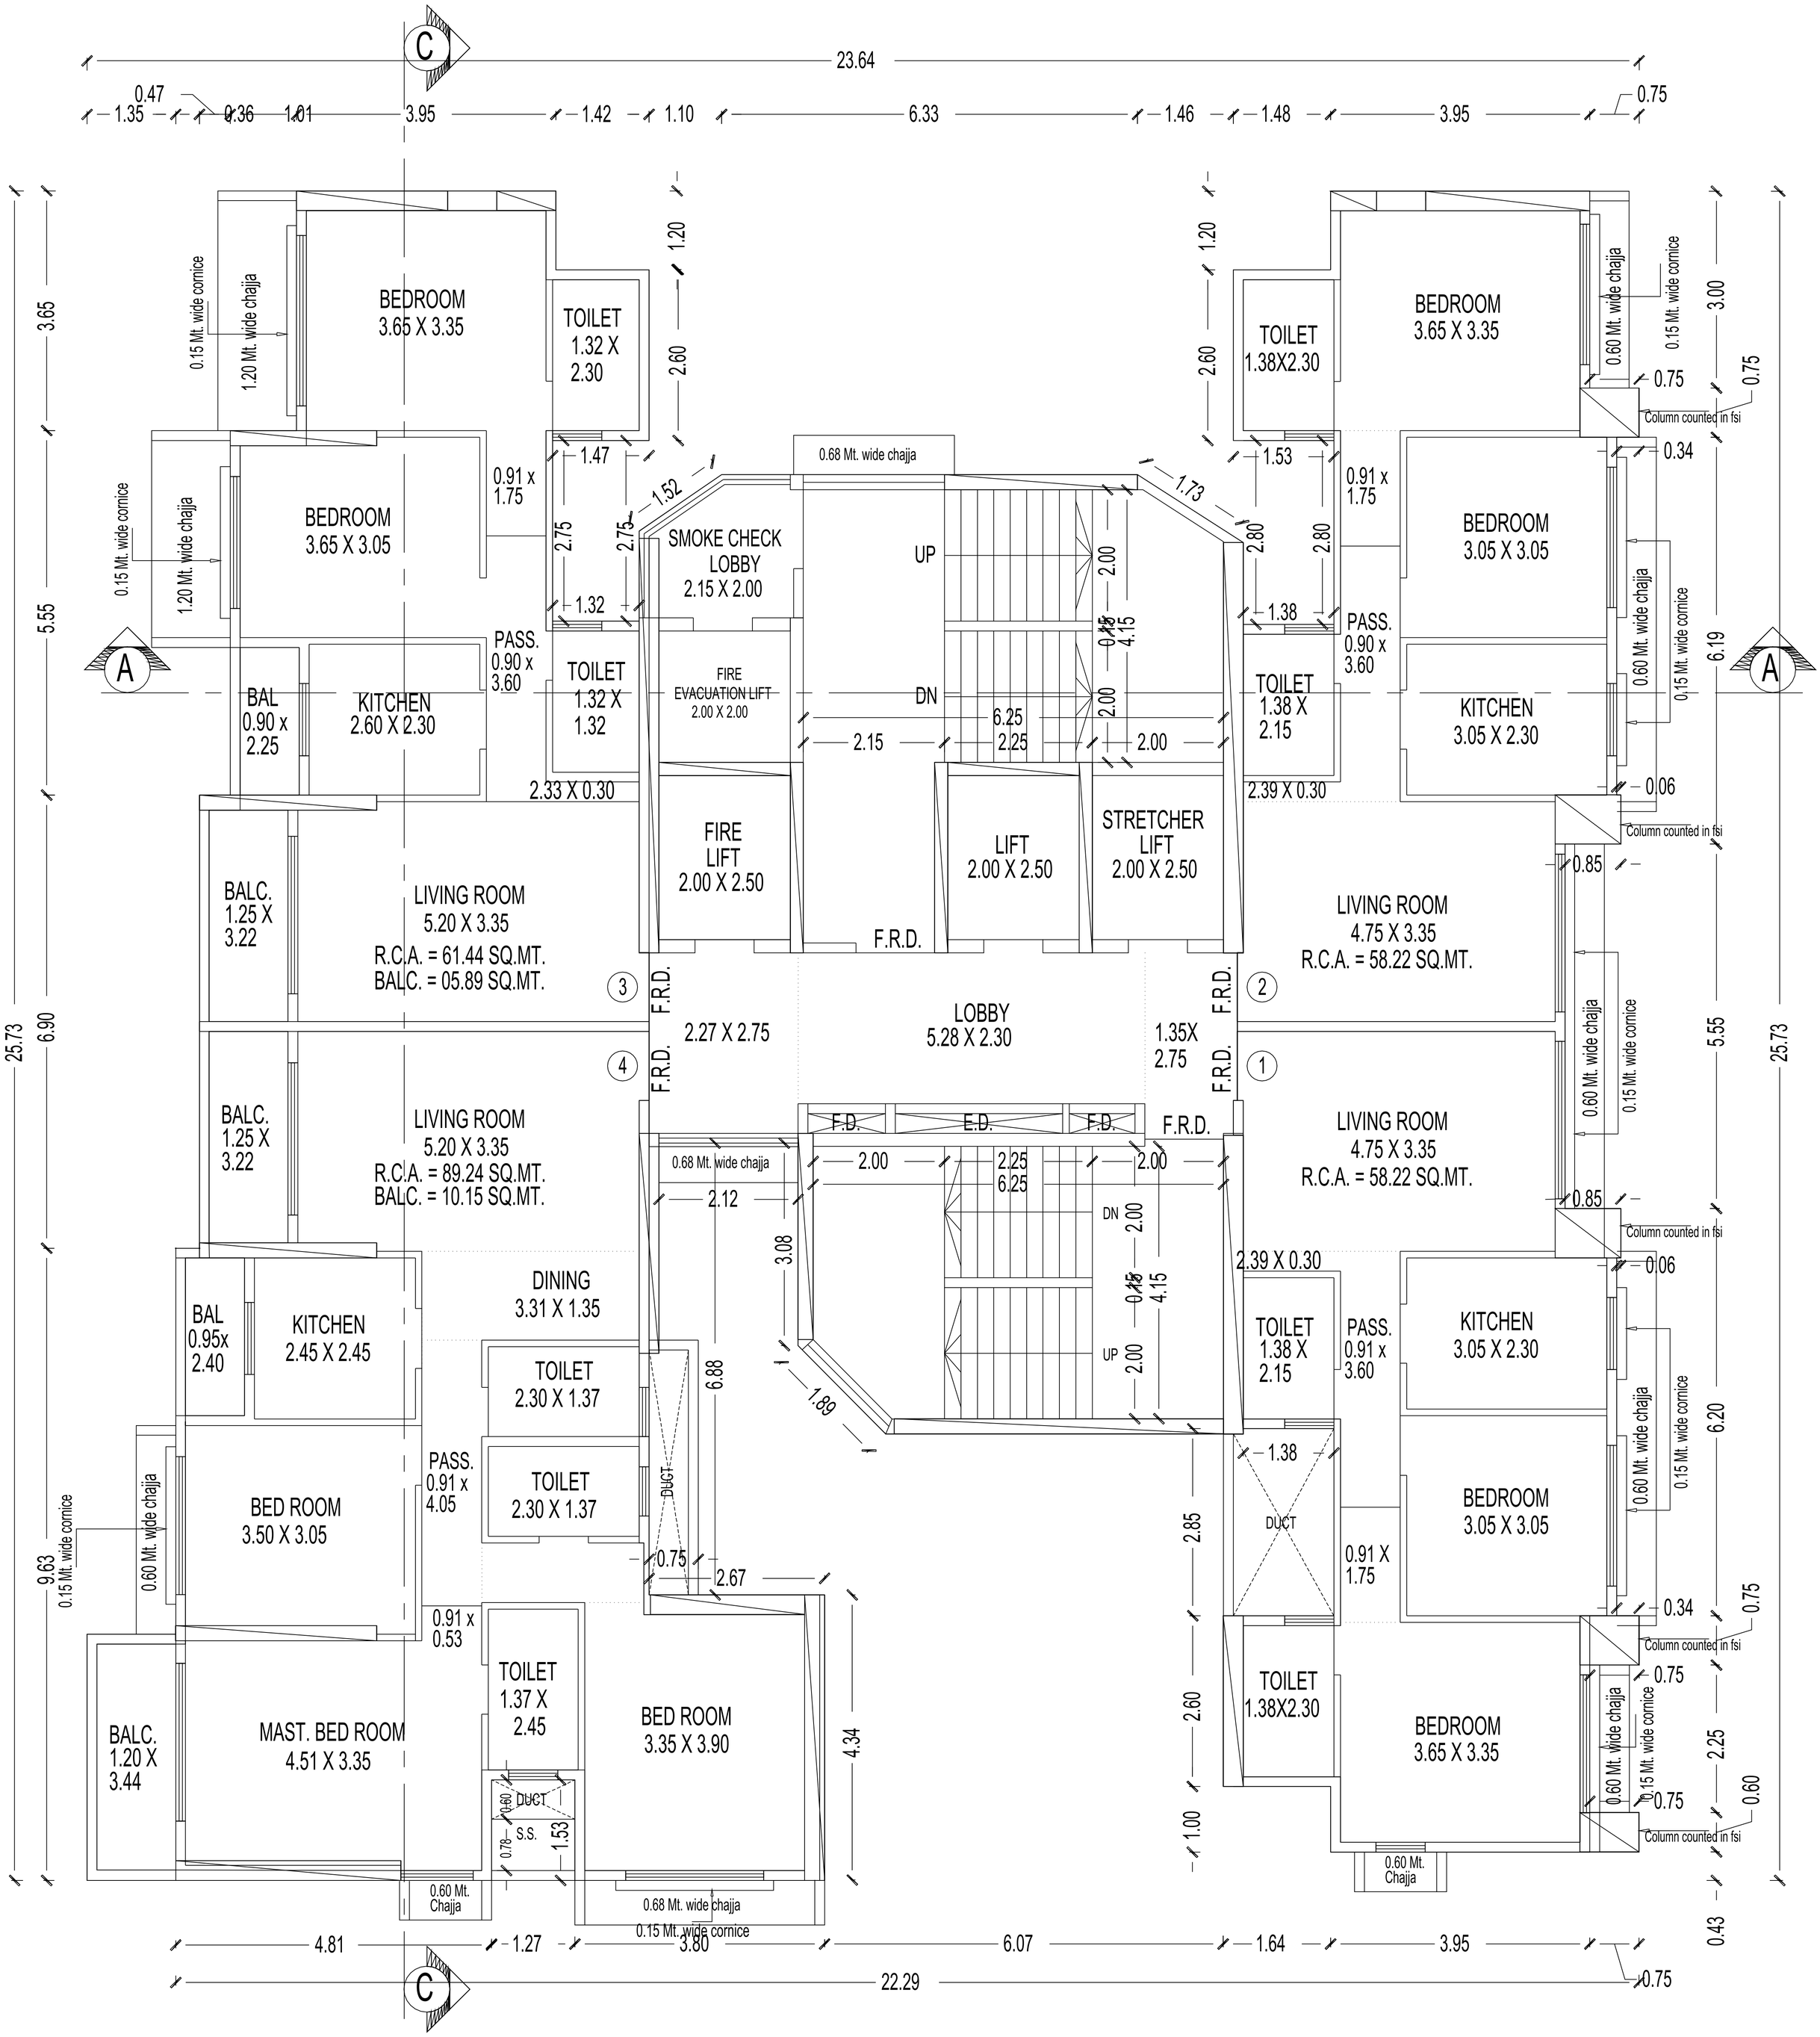


1ST, 2ND, 4TH TO 9TH, 11TH TO 16TH, 18TH TO 23RD,

25TH TO 28TH FLOOR PLAN

SCALE :- 1:100

WING - A

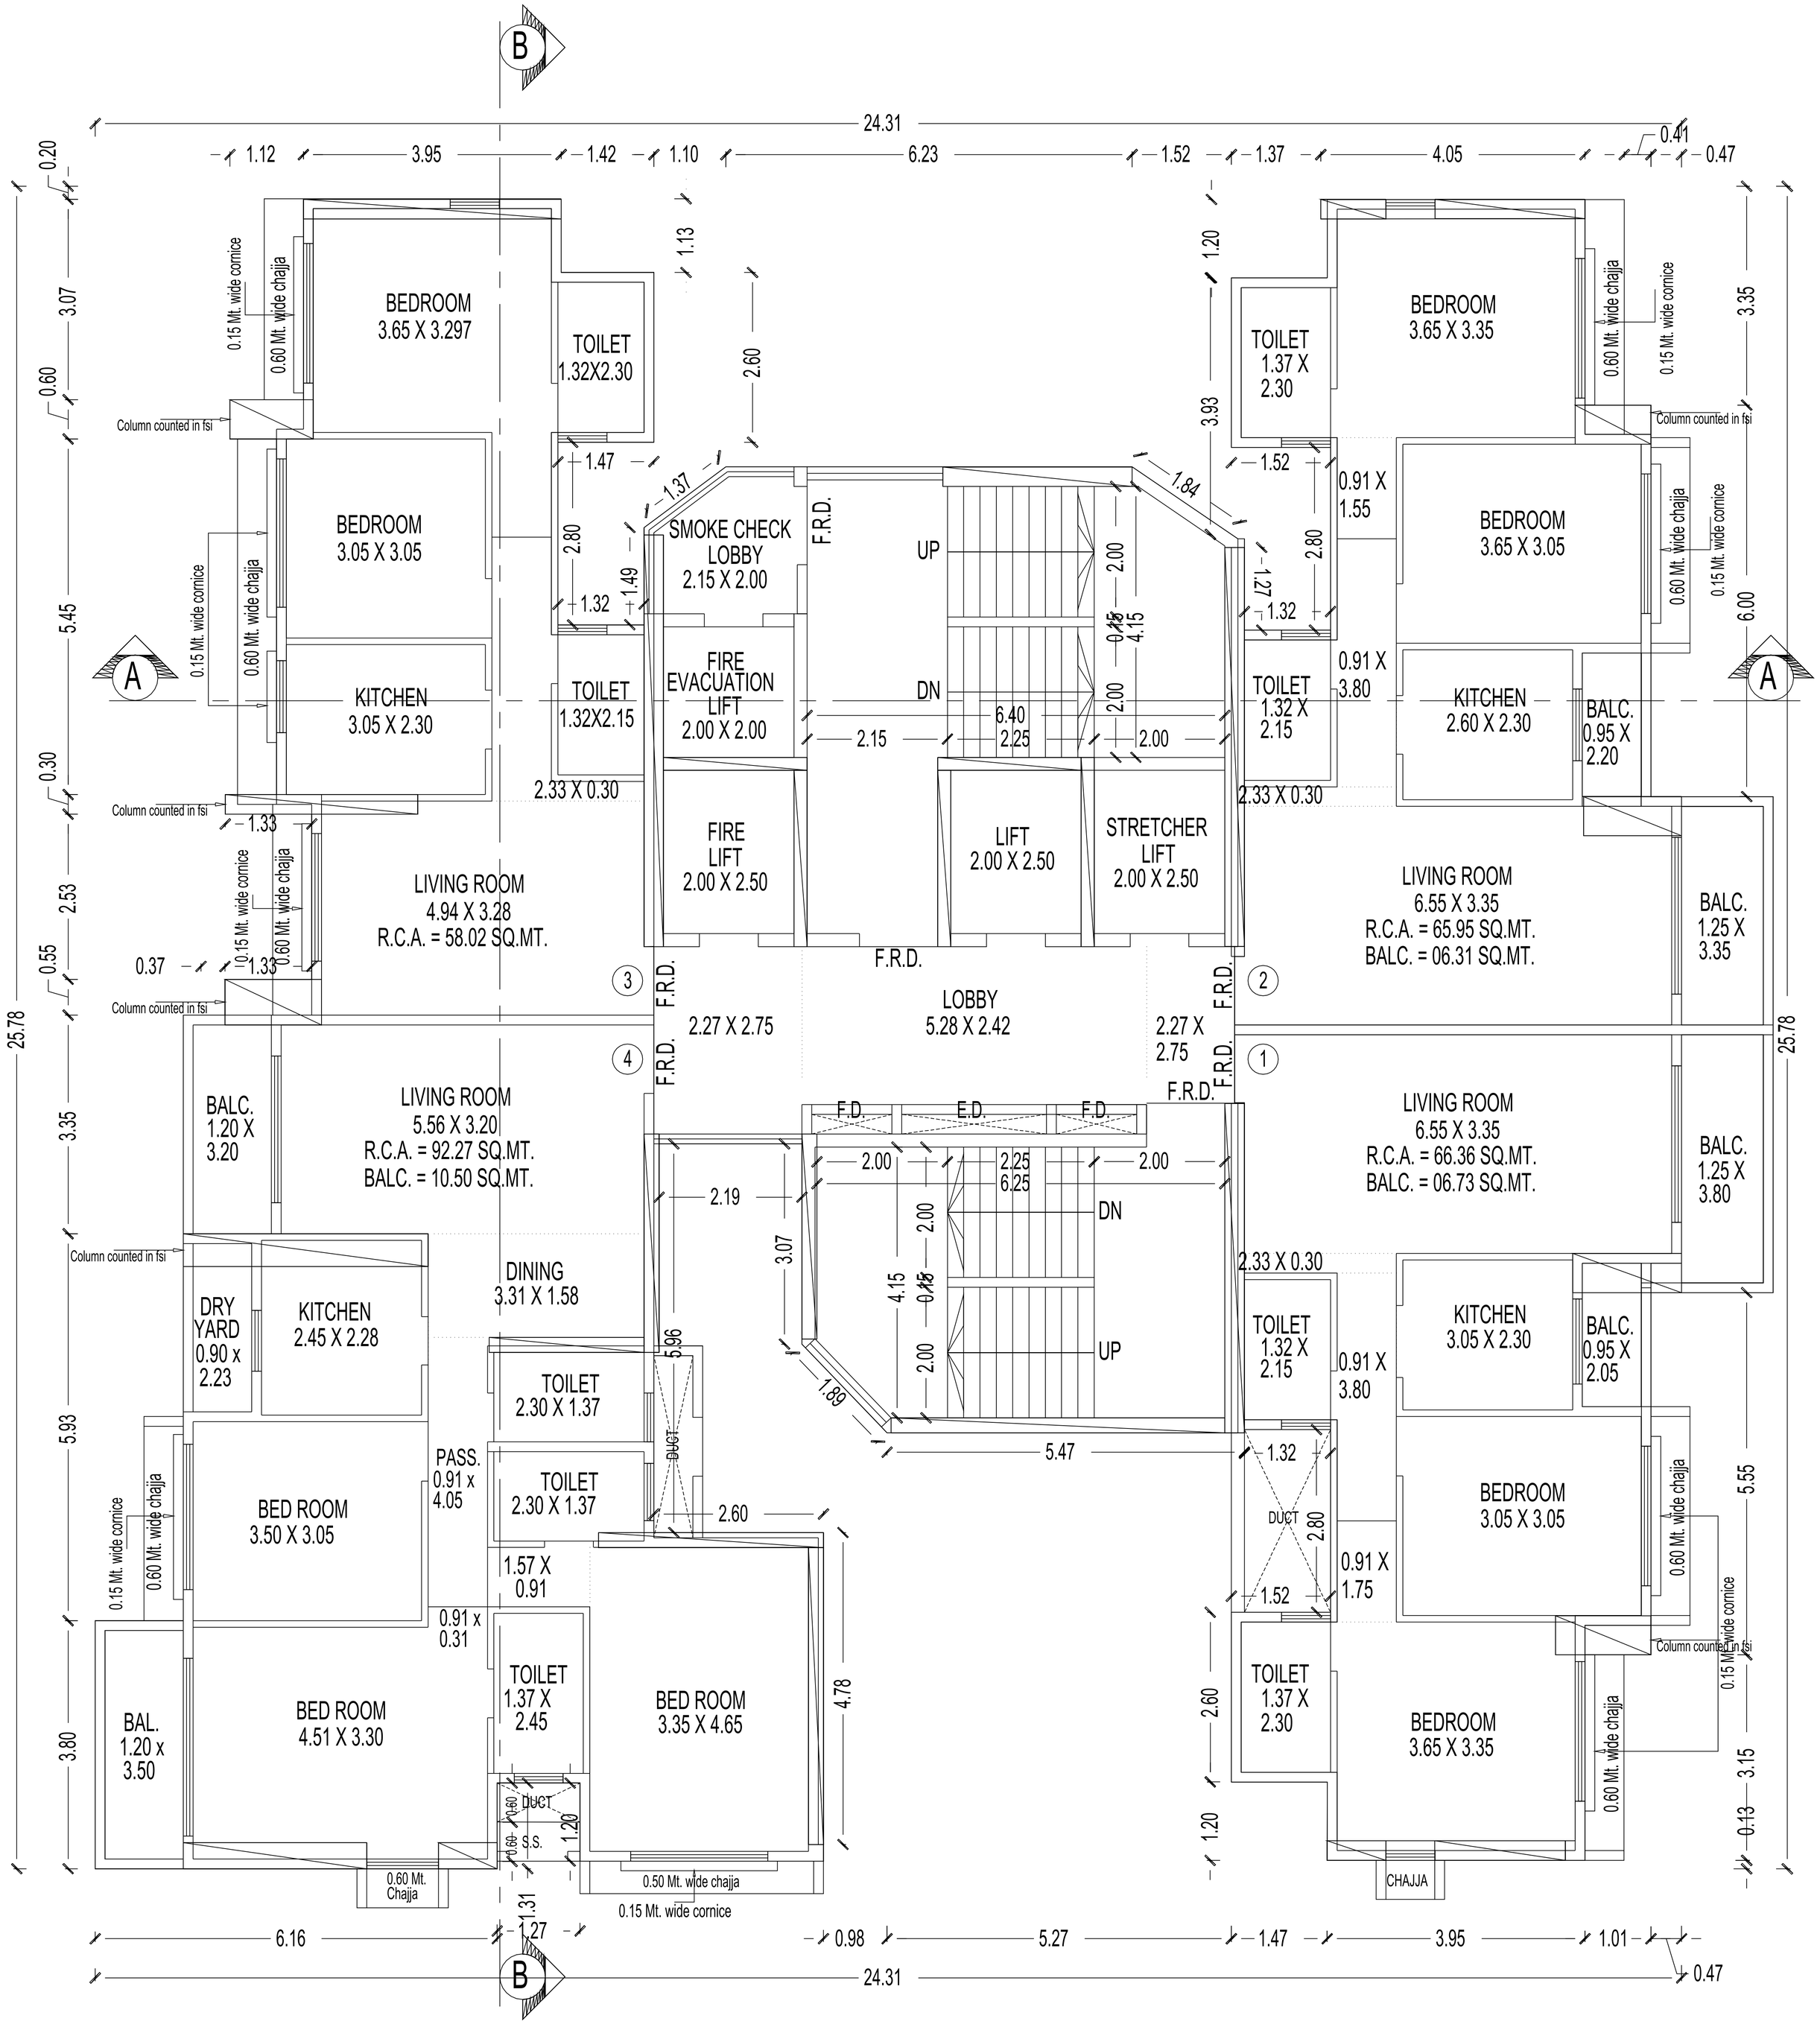

28TH TO 30TH FLOOR PLAN


SCALE :- 1:100

WING - B

SHEET NO. 08 /17

FILE NO- P-20375/2024/(1007)/P/S Ward/PAHADI GOREGAON-W

NORTH

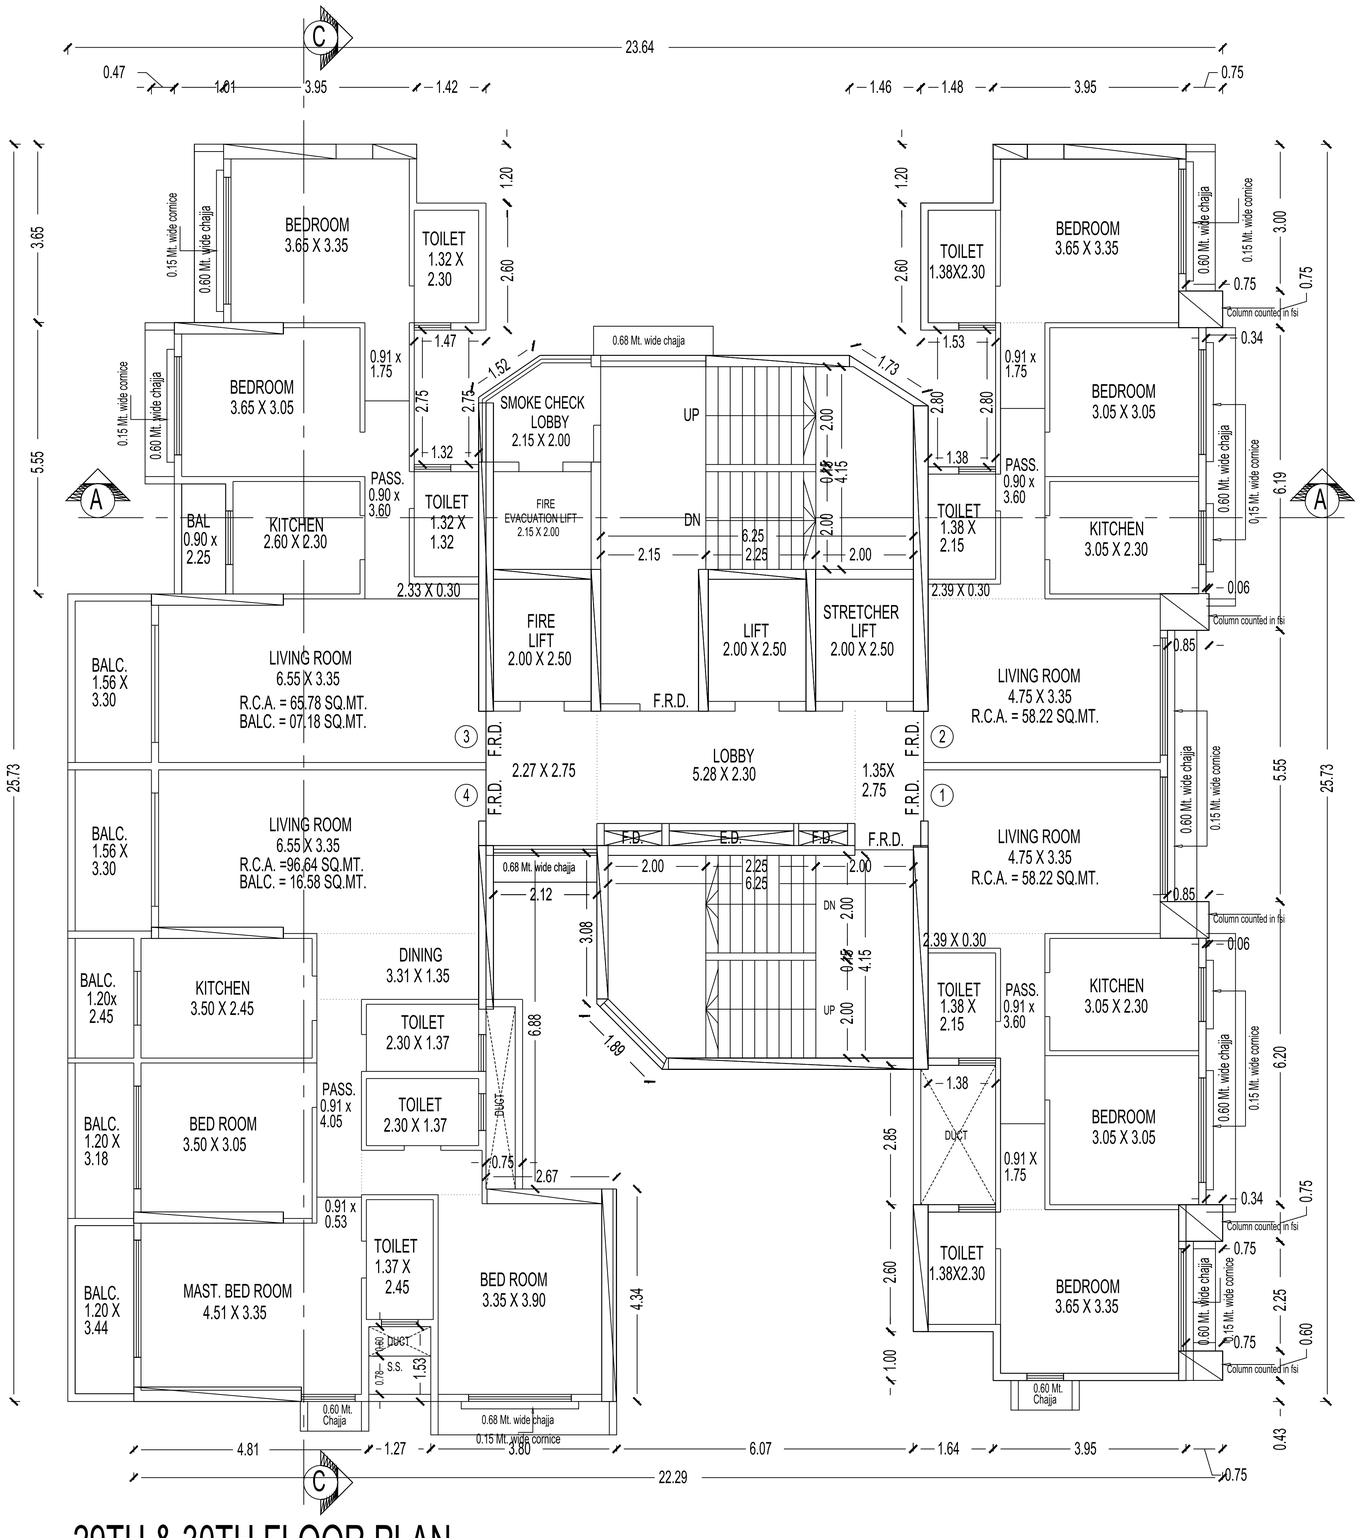


29TH & 30TH FLOOR PLAN

SCALE :- 1:100 WING - A

SHEET NO. 09 /17


FILE NO- P-20375/2024/(1007)/P/S Ward/PAHADI GOREGAON-W

NORTH

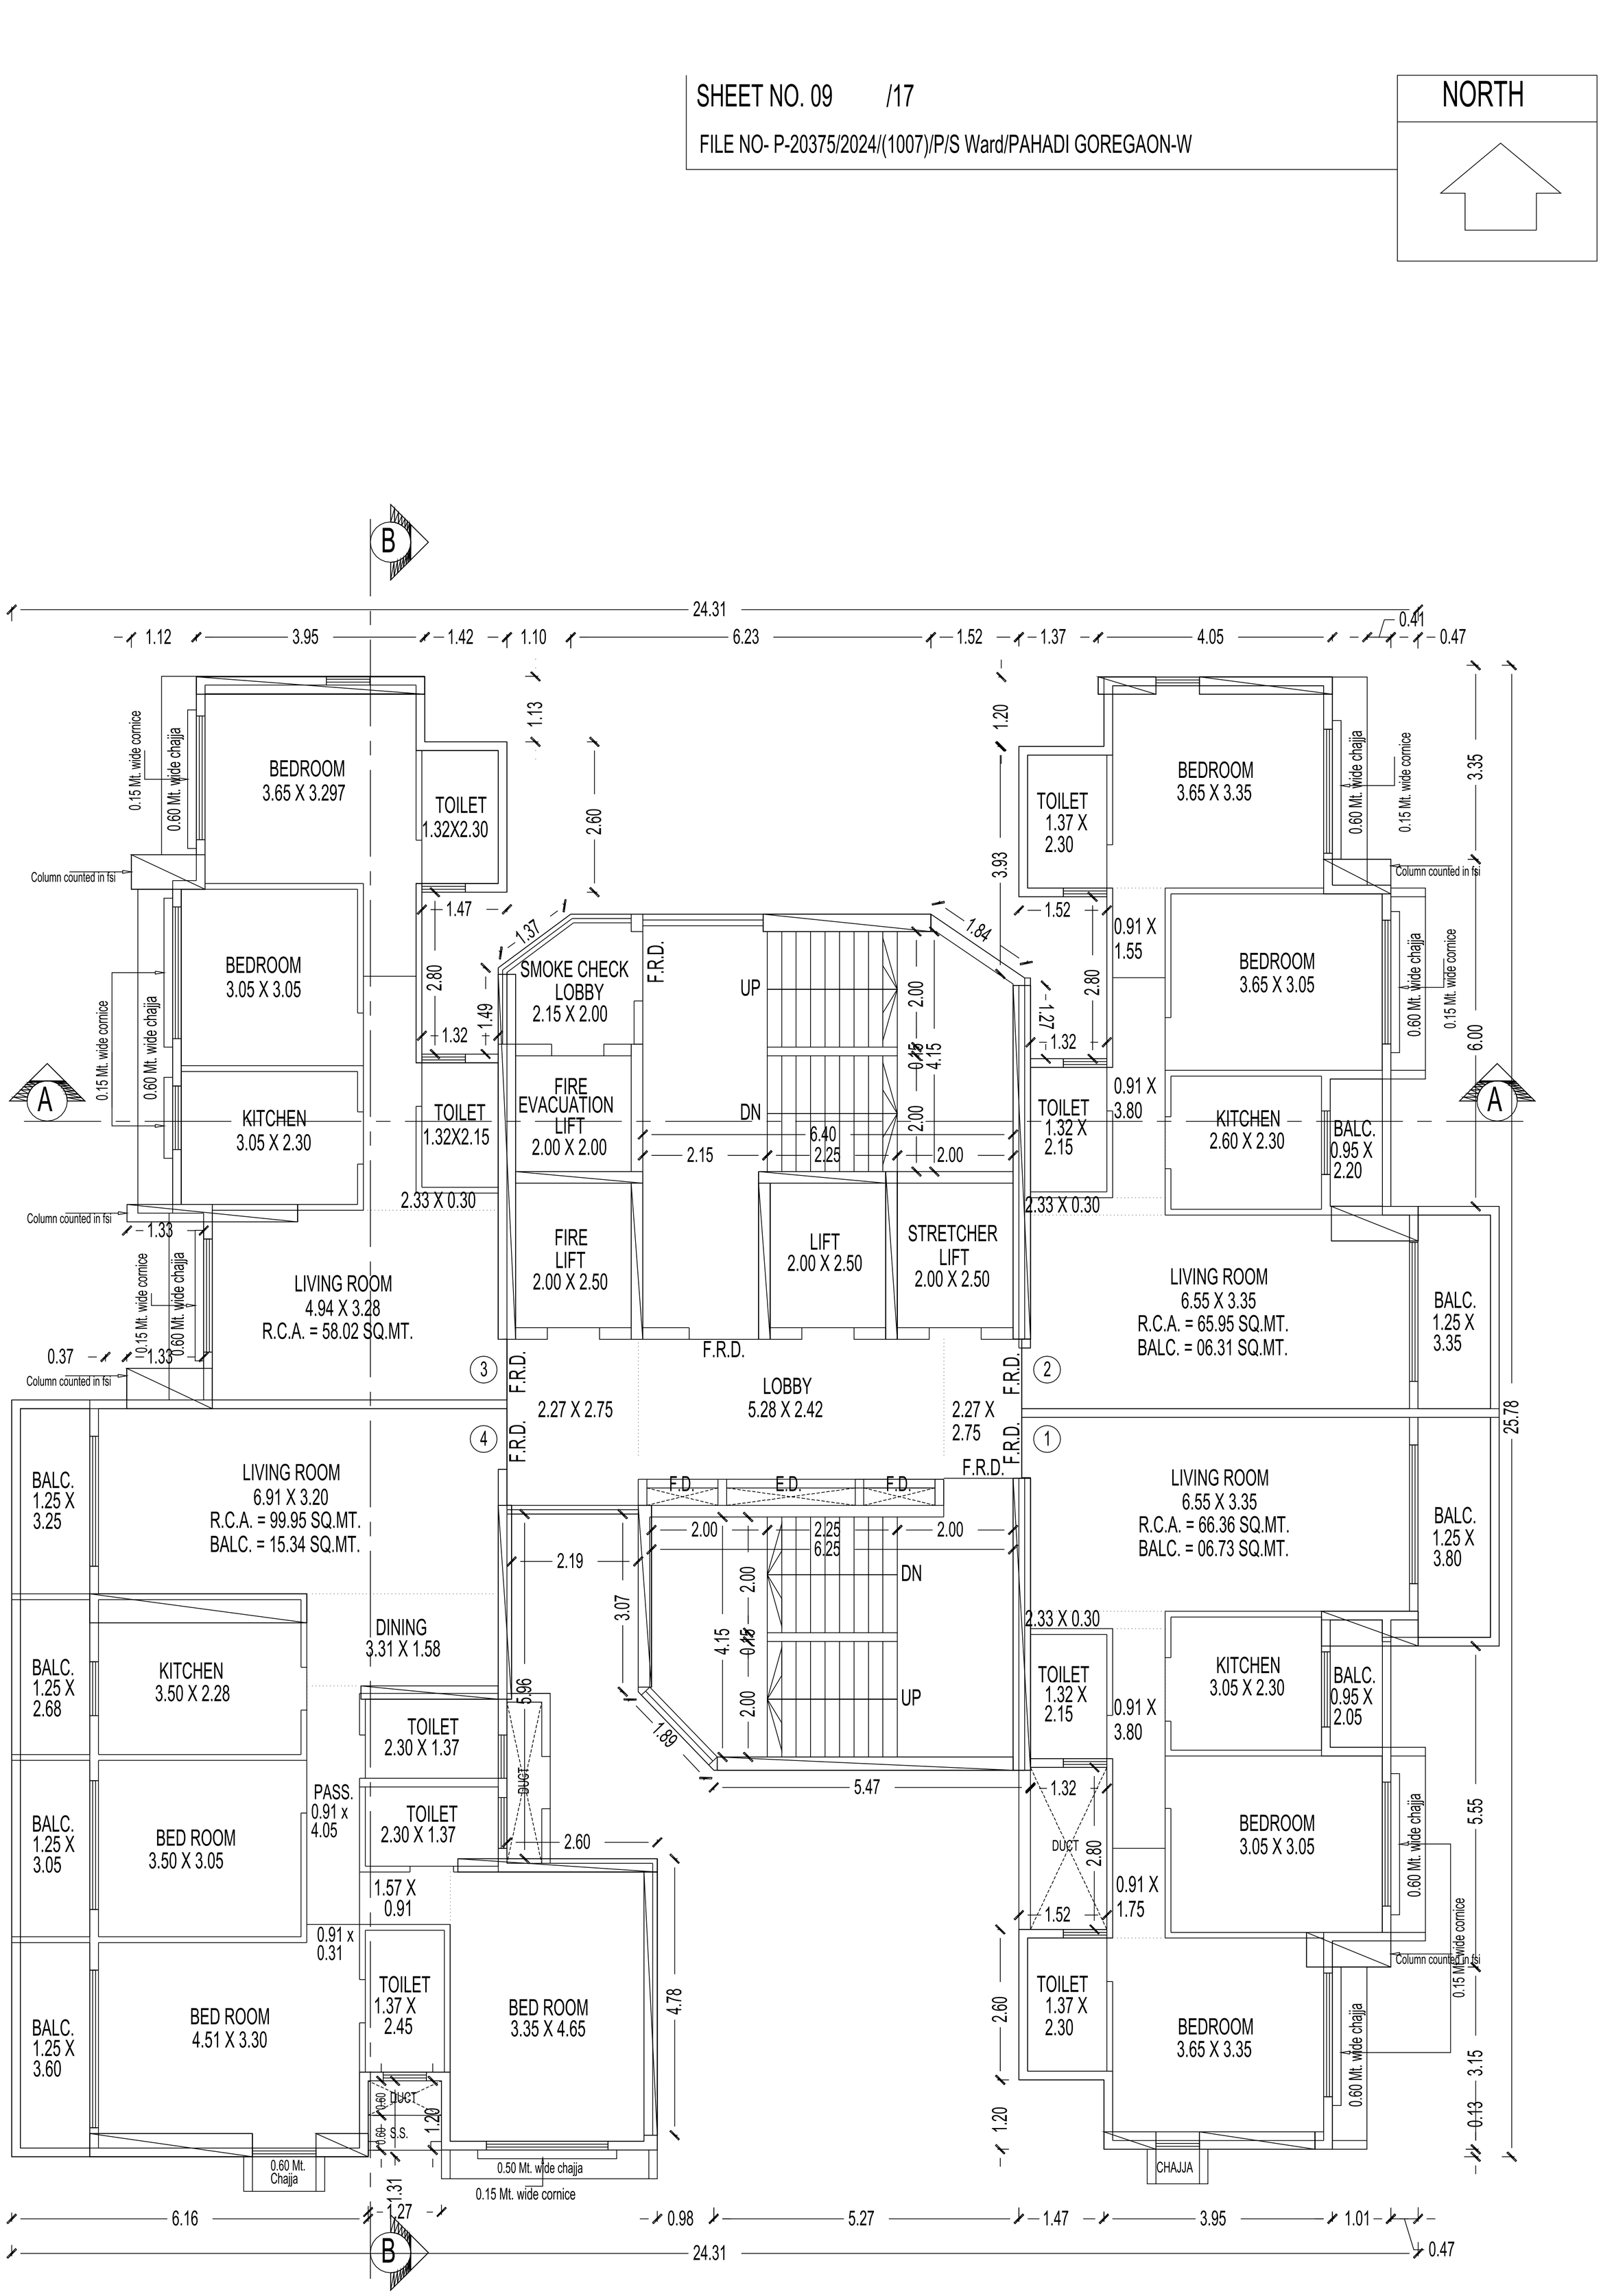

31ST & 32ND FLOOR PLAN


SCALE :- 1:100 WING - B

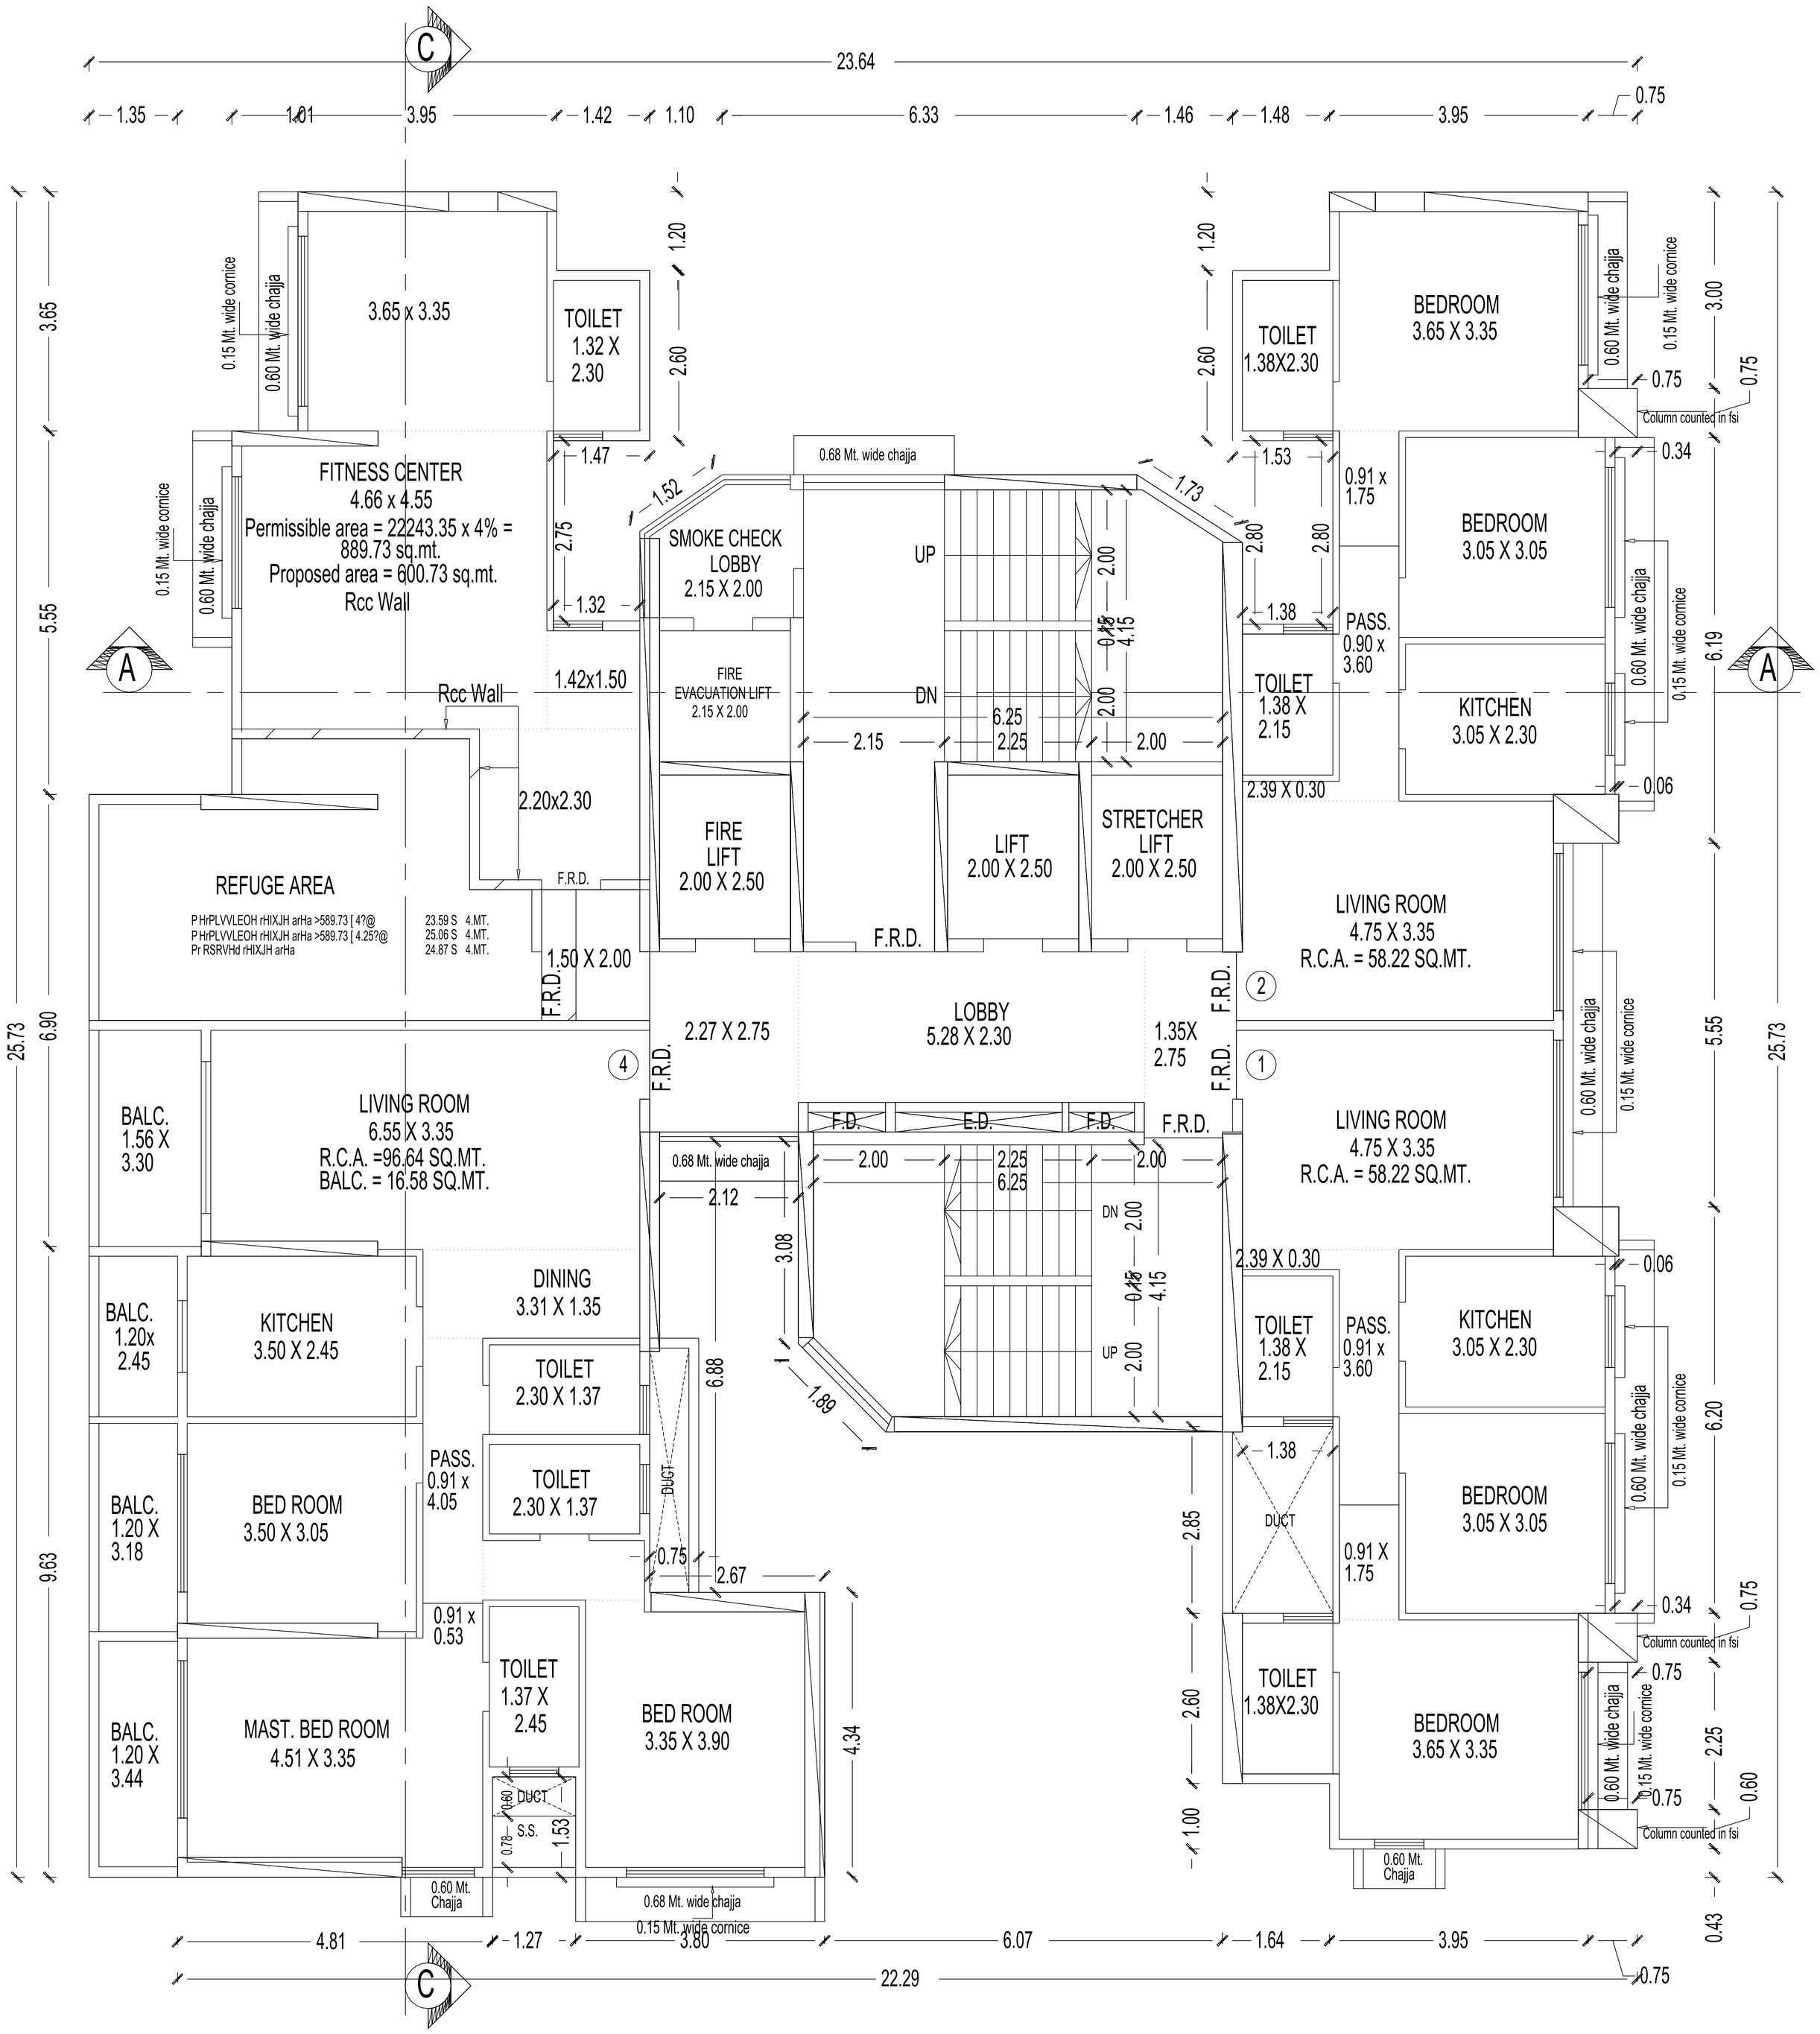

31ST (REFUGE) FLOOR PLAN

SCALE :- 1:100

WING - A

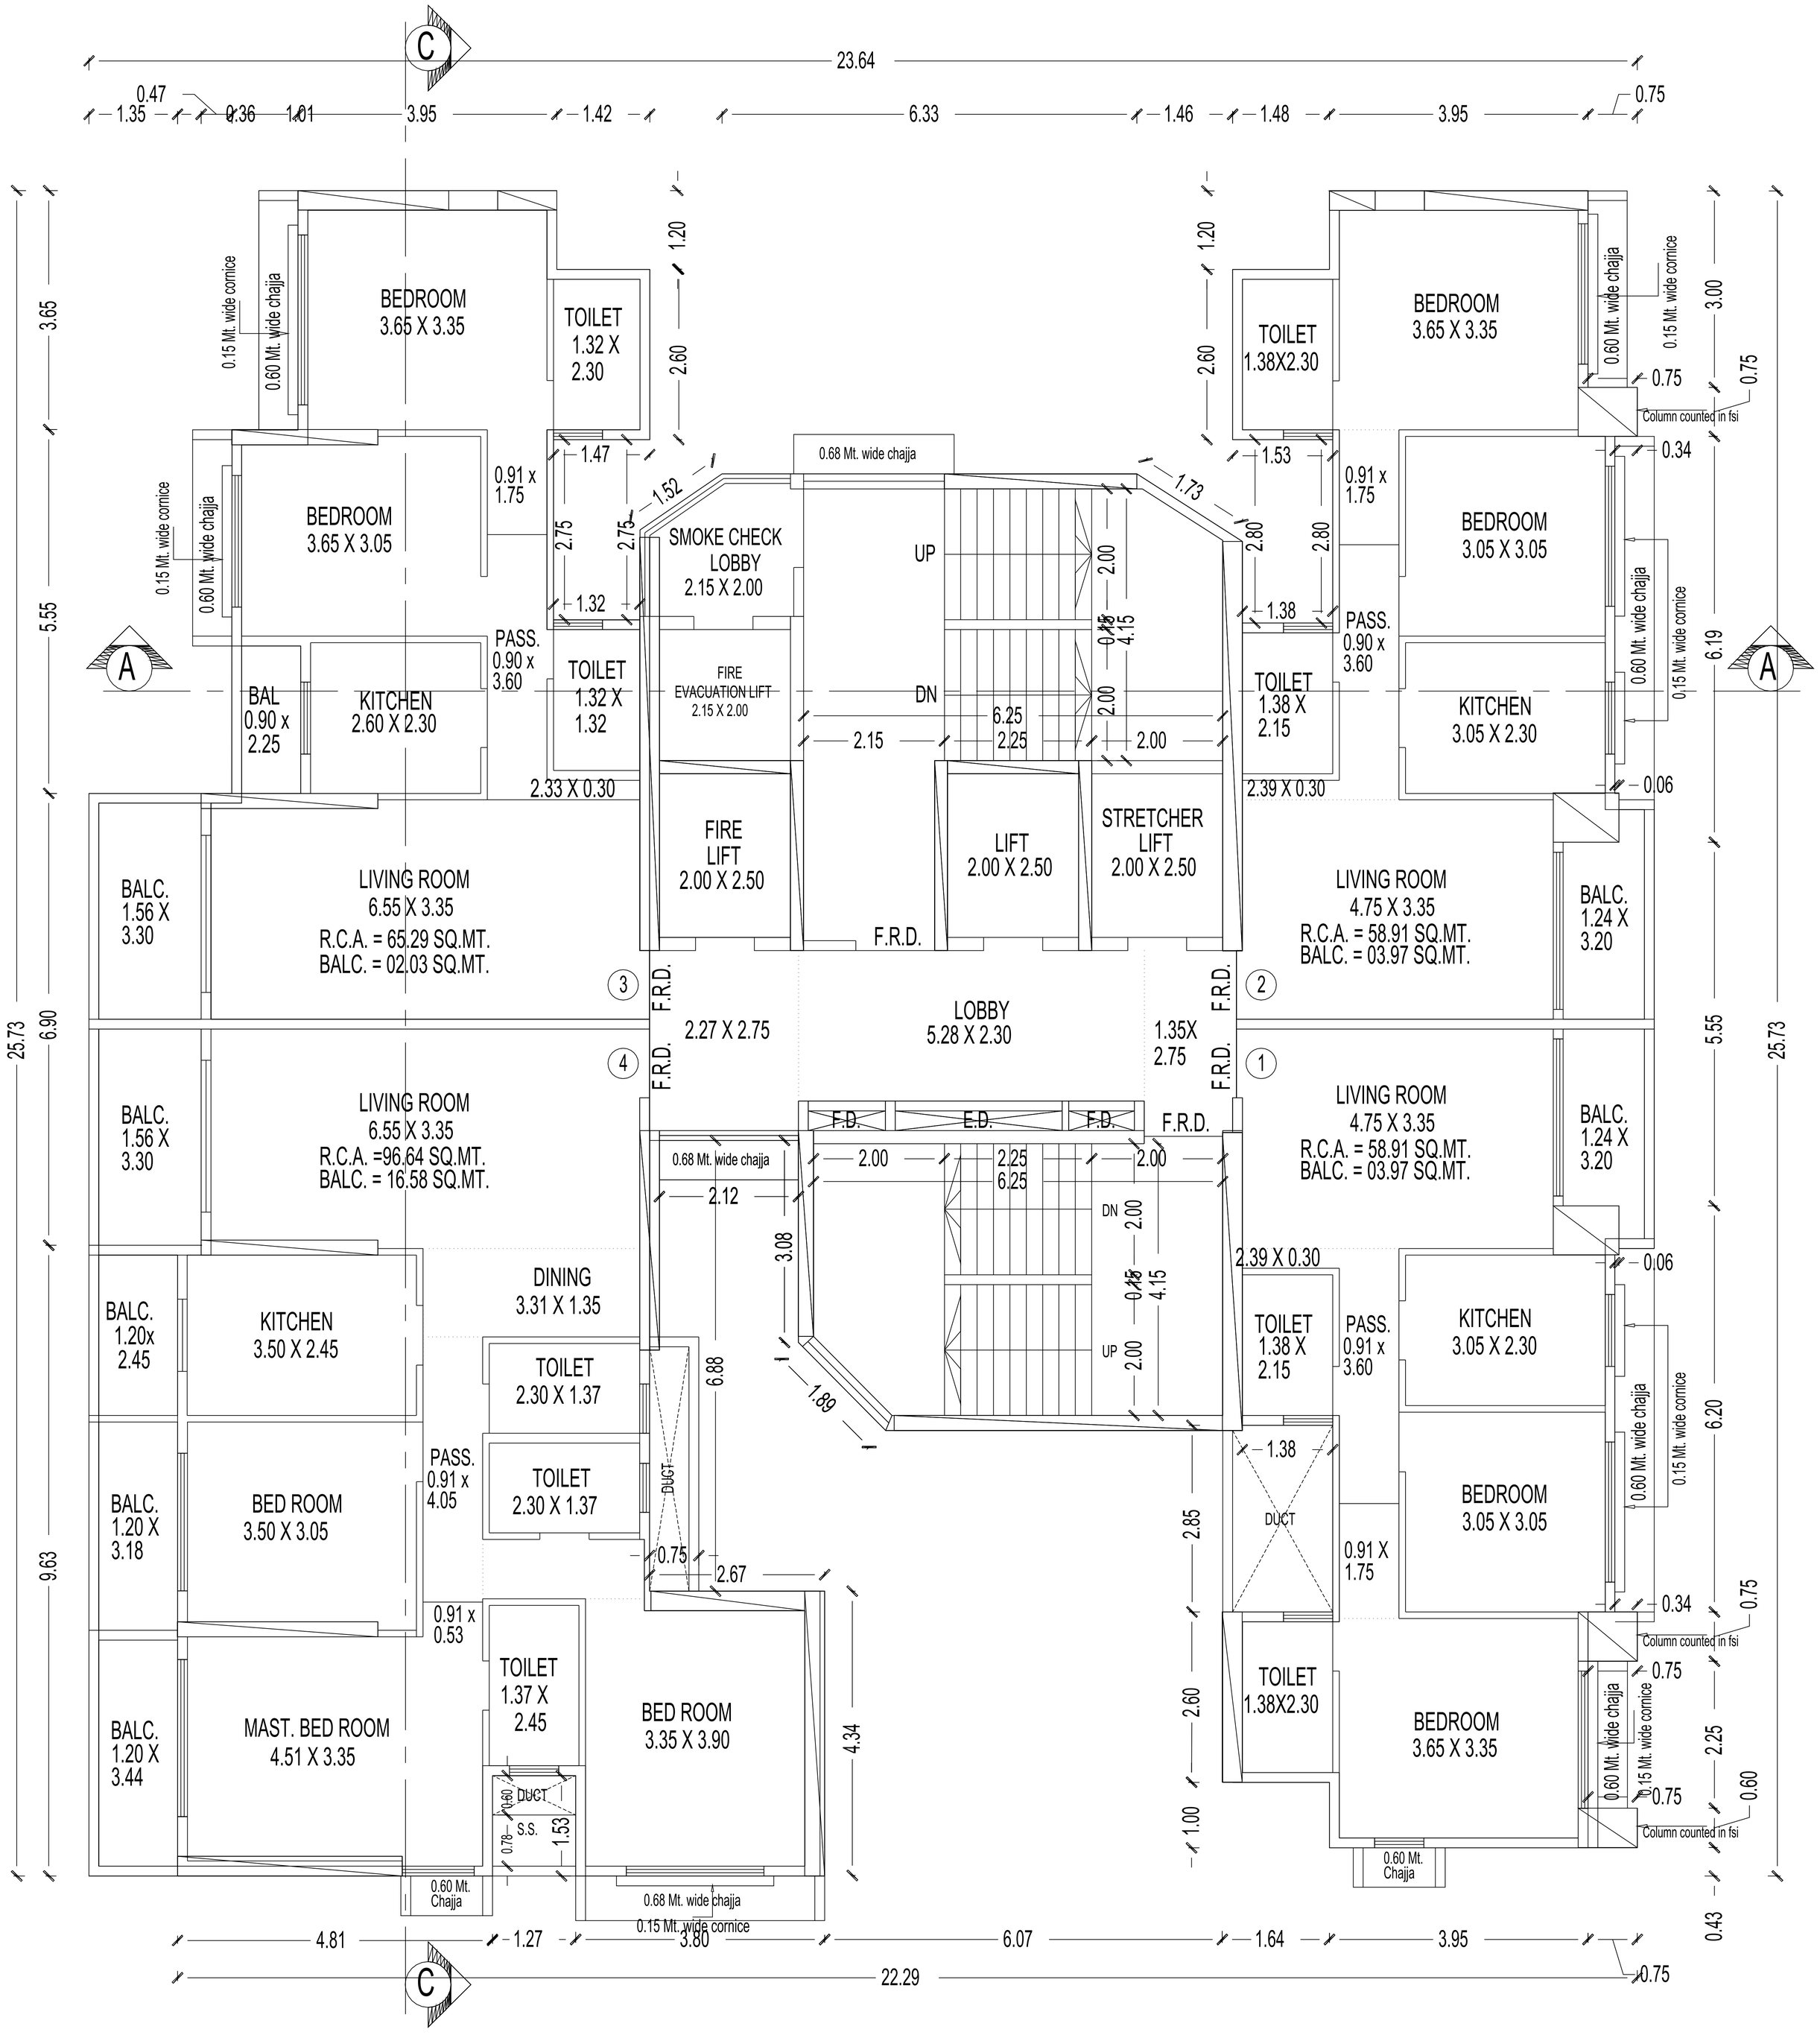

32ND FLOOR PLAN

SCALE :- 1:100 WING - A