STAIRCASE AREA
LIFT WELL AREA
TOTAL STAIRCASE AREA

NET BUILT UP AREA
[X1 - (Y2+Y3)]

Built Up Area Diagram For 13TH Floor

Scale: 1:100 (Wing - 'C' & Wing- 'D')

Required Area (4%) : 158.27 SQ. MT.
Required Area (4.25%) : 168.17 SQ. MT
Proposed Area : 160.21 SQ. MT.
Excess Area Counted in FSI : NIL

14th Floor Plan (Refuge)

Scale: 1:100 (Wing - 'C' & Wing- 'D')

File No. :-

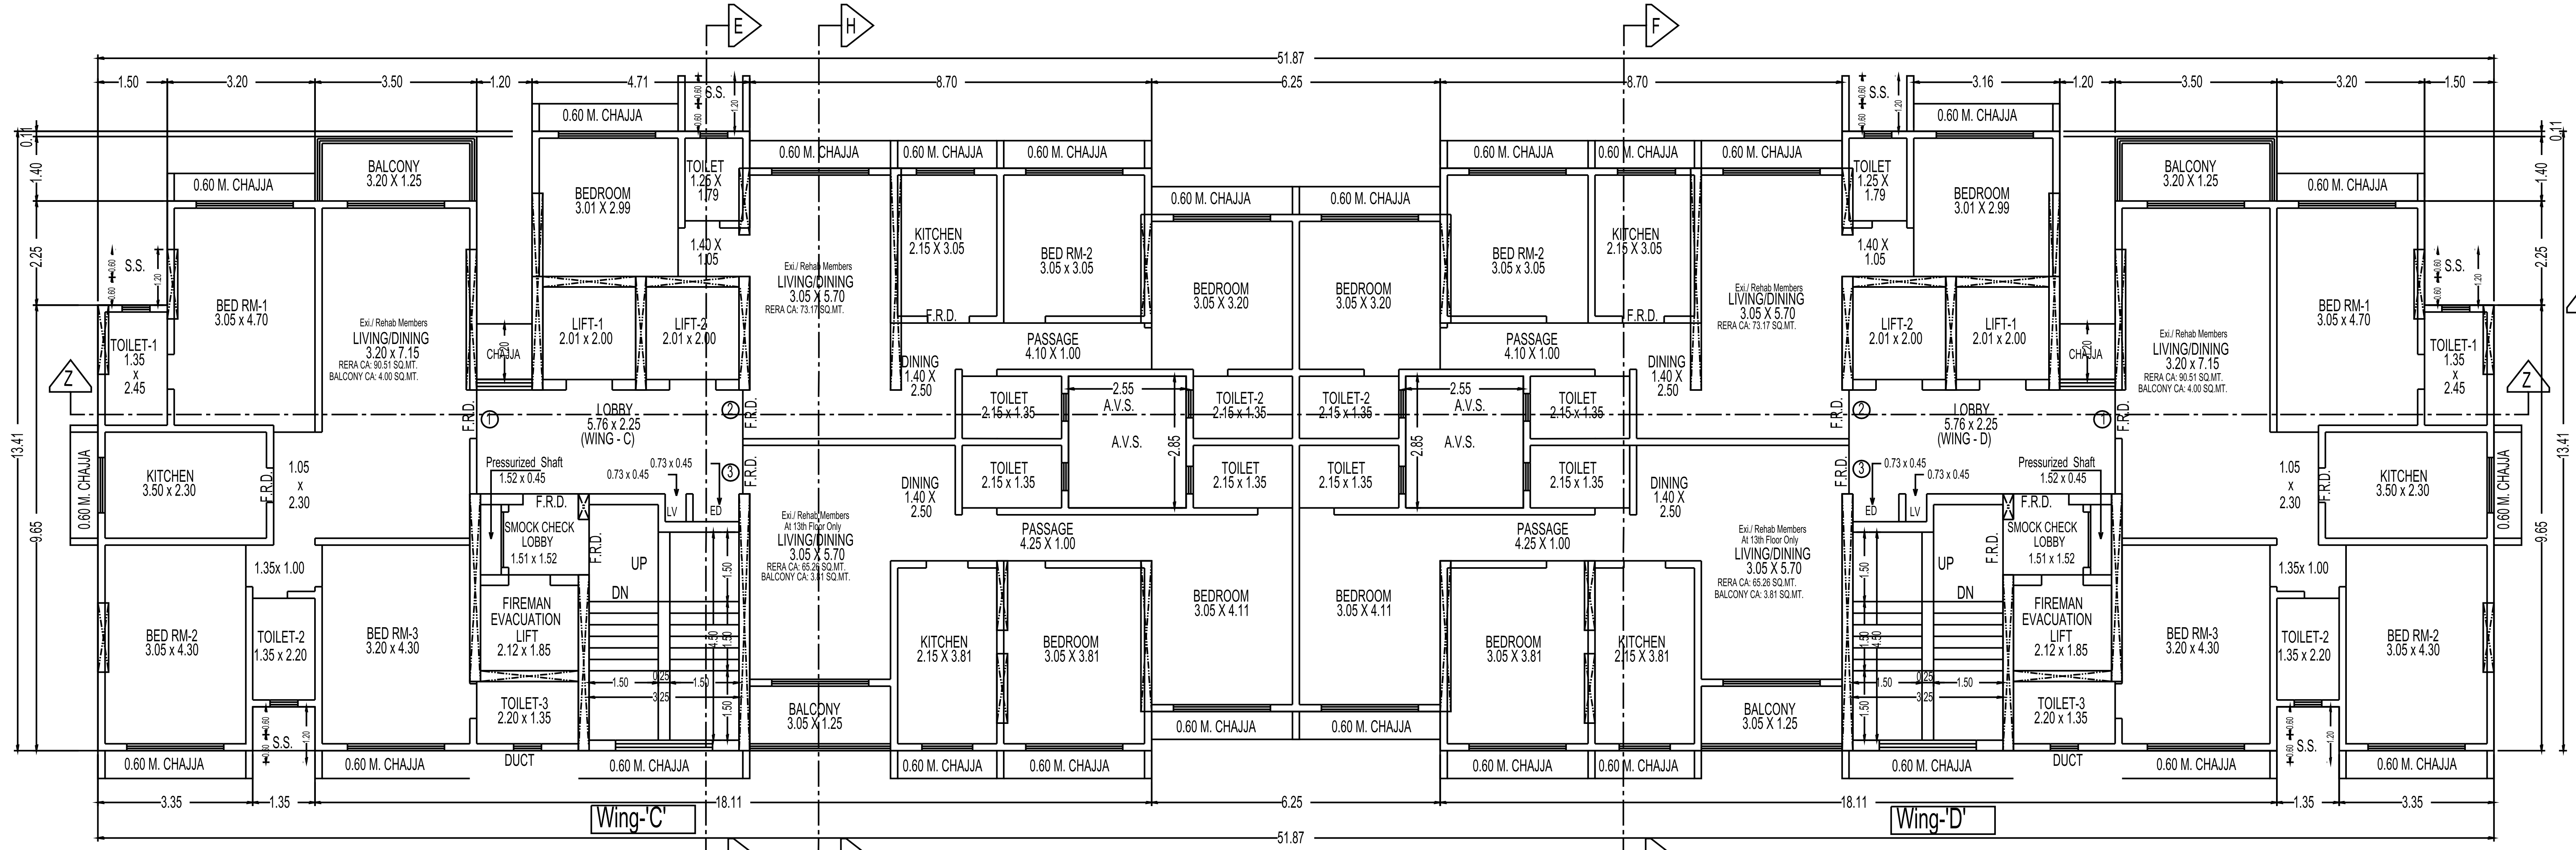

15th to 20th Floor Plan

Scale: 1:100   (Wing - 'C' & Wing- 'D')

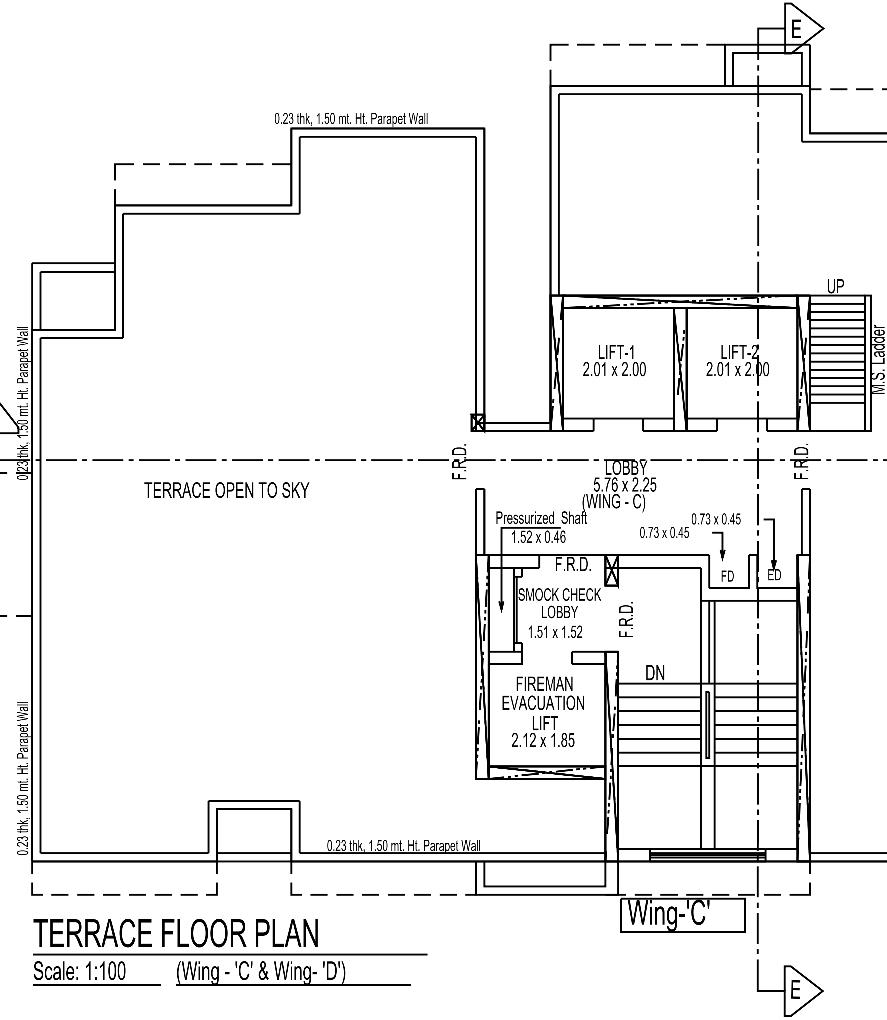

CHAJJA BELOW
0.23 thk. 1.50 mt. Ht. Parapet Wall
TERRACE OPEN TO SKY
LIFT-1 2.01 X 2.00
LIFT-2 2.01 X 2.00
LOBBY 5.76 X 2.25 (WING - C)
LOBBY 5.76 X 2.25 (WING - D)
AVS
UP
M.S. Ladder
Pressurized Shaft 1.52 X 0.45
SMOCK CHECK LOBBY 1.51 X 1.52
FIREMAN EVACUATION LIFT 2.12 X 1.85
F.R.D.
DN
Wing-'C'
Wing-'D'

TERRACE FLOOR PLAN

Scale: 1:100   (Wing - 'C' & Wing- 'D')

FLAT NO. - 01	(4th & 5th Floor)		(WING - C & WING - D)			4 NOS.	
1	0.15	X	1.05	X	1 NO	=	0.16 SQ.MT.

FLAT NO. - 01 (7th to 10th Floor)						(WING - C & WING - D)
1	0.15	X	1.05	X	1	NO
2	3.20	X	0.15	X	1	NO
3	6.40	X	1.50	X	1	NO
4	7.90	X	8.35	X	1	NO

Scale: 1:100 (Wing - 'C' & Wing- 'D')

21st Floor Plan

Scale: 1:100 (Wing - 'C' & Wing- 'D')