
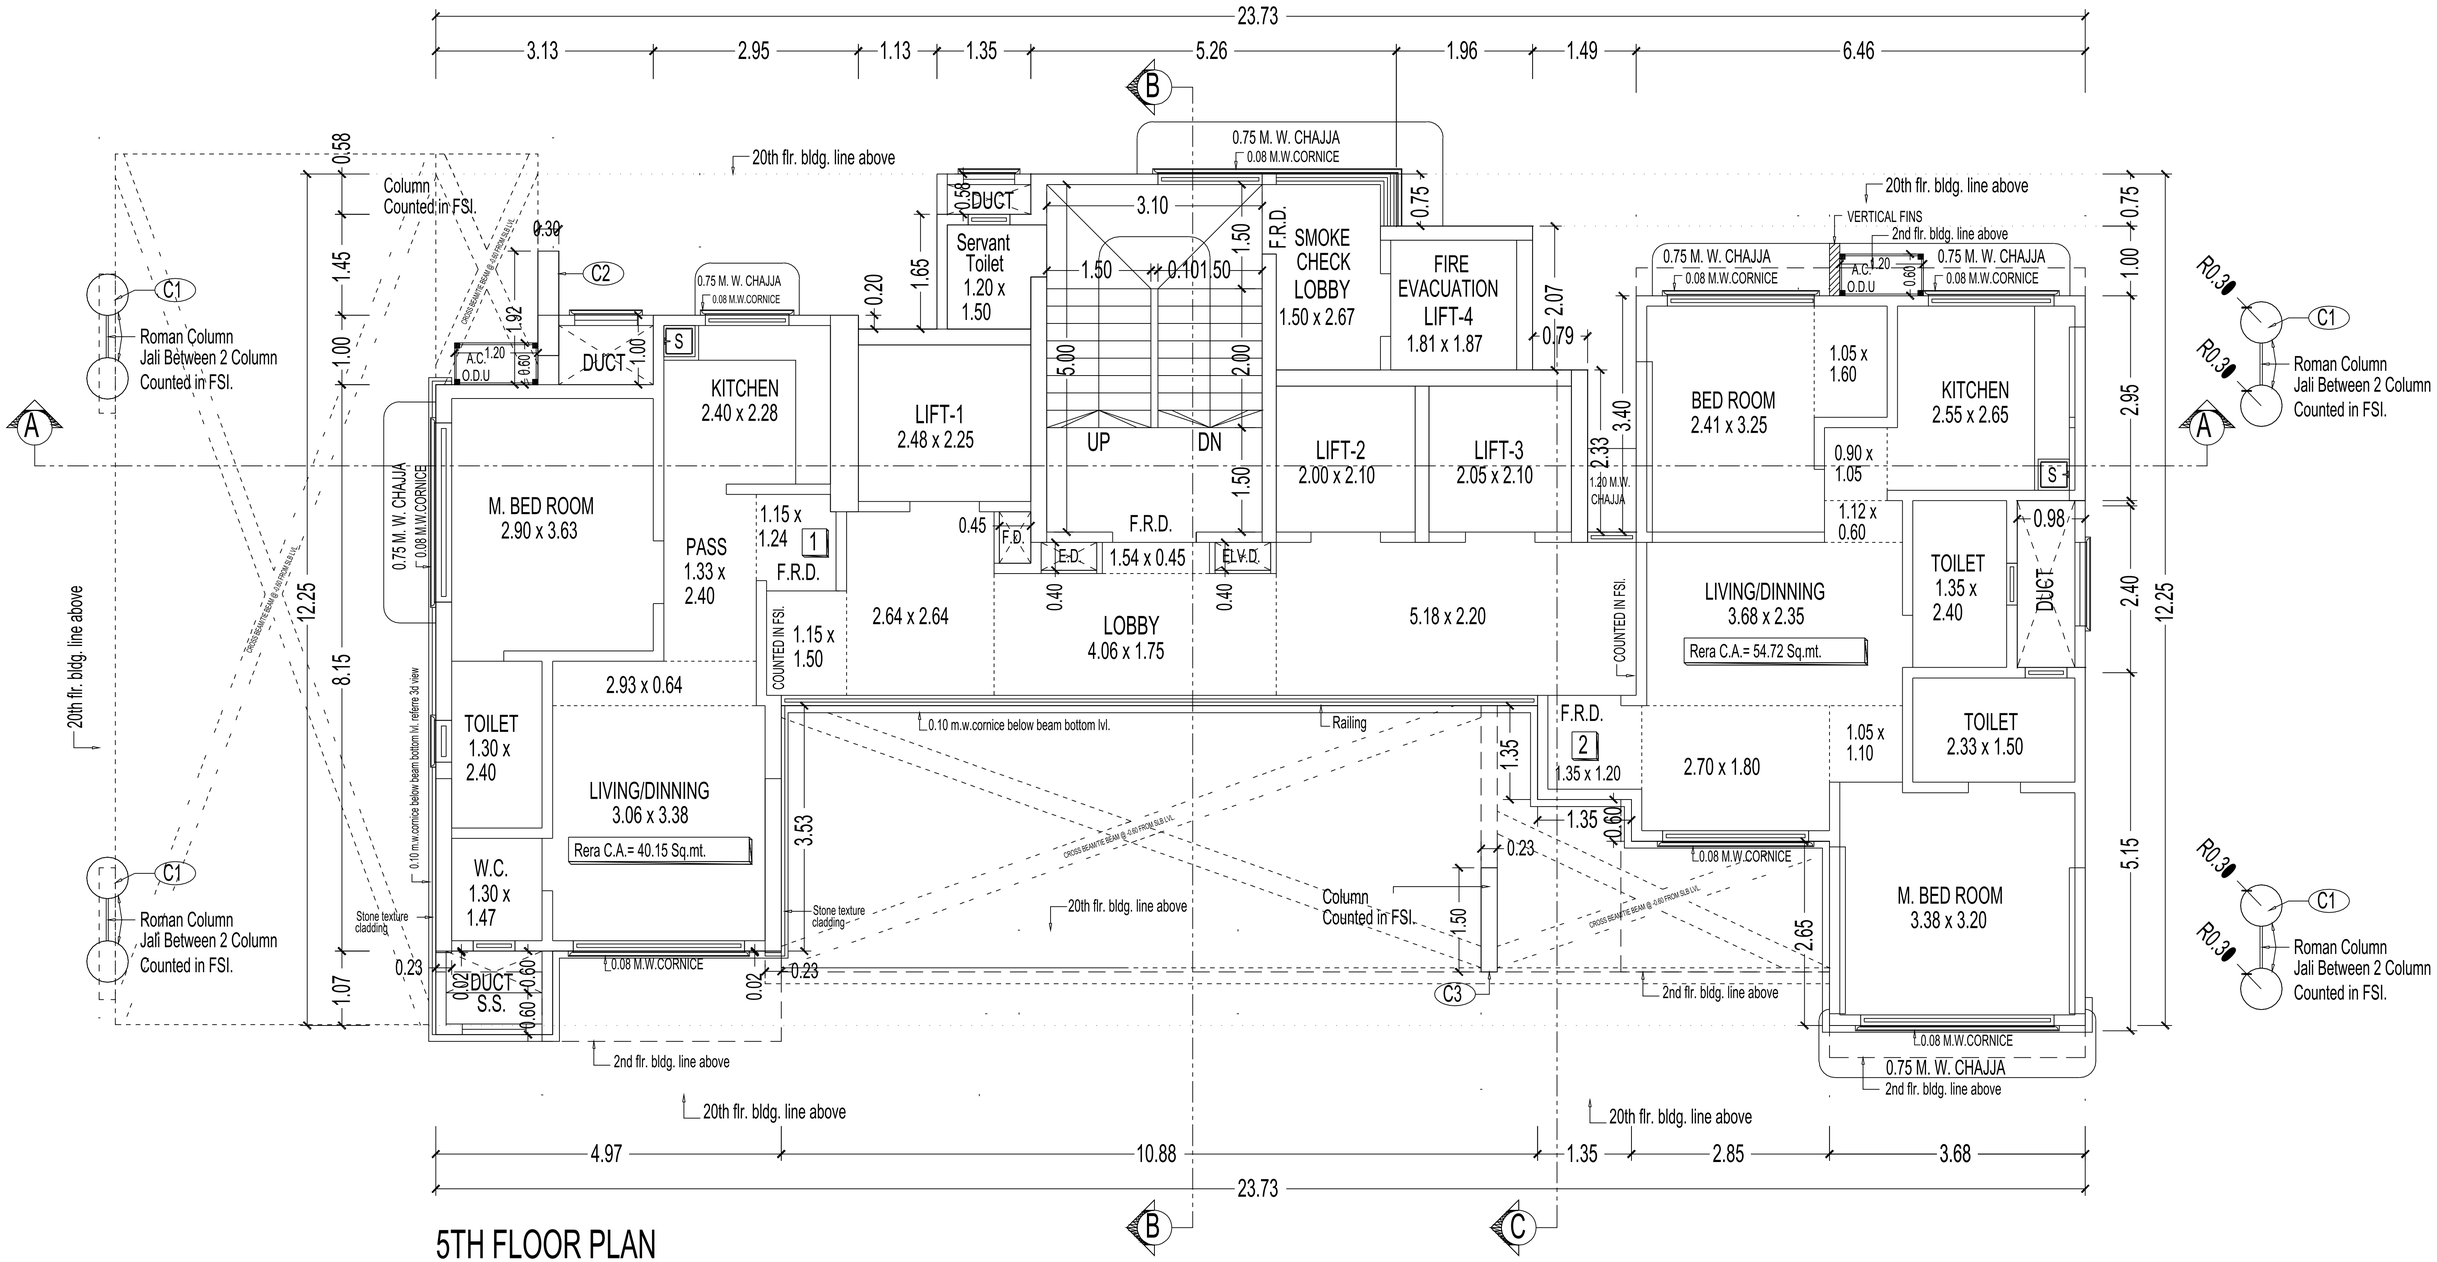


5TH FLOOR PLAN

SCALE - 1:100


6TH FLOOR PLAN

SCALE - 1:100

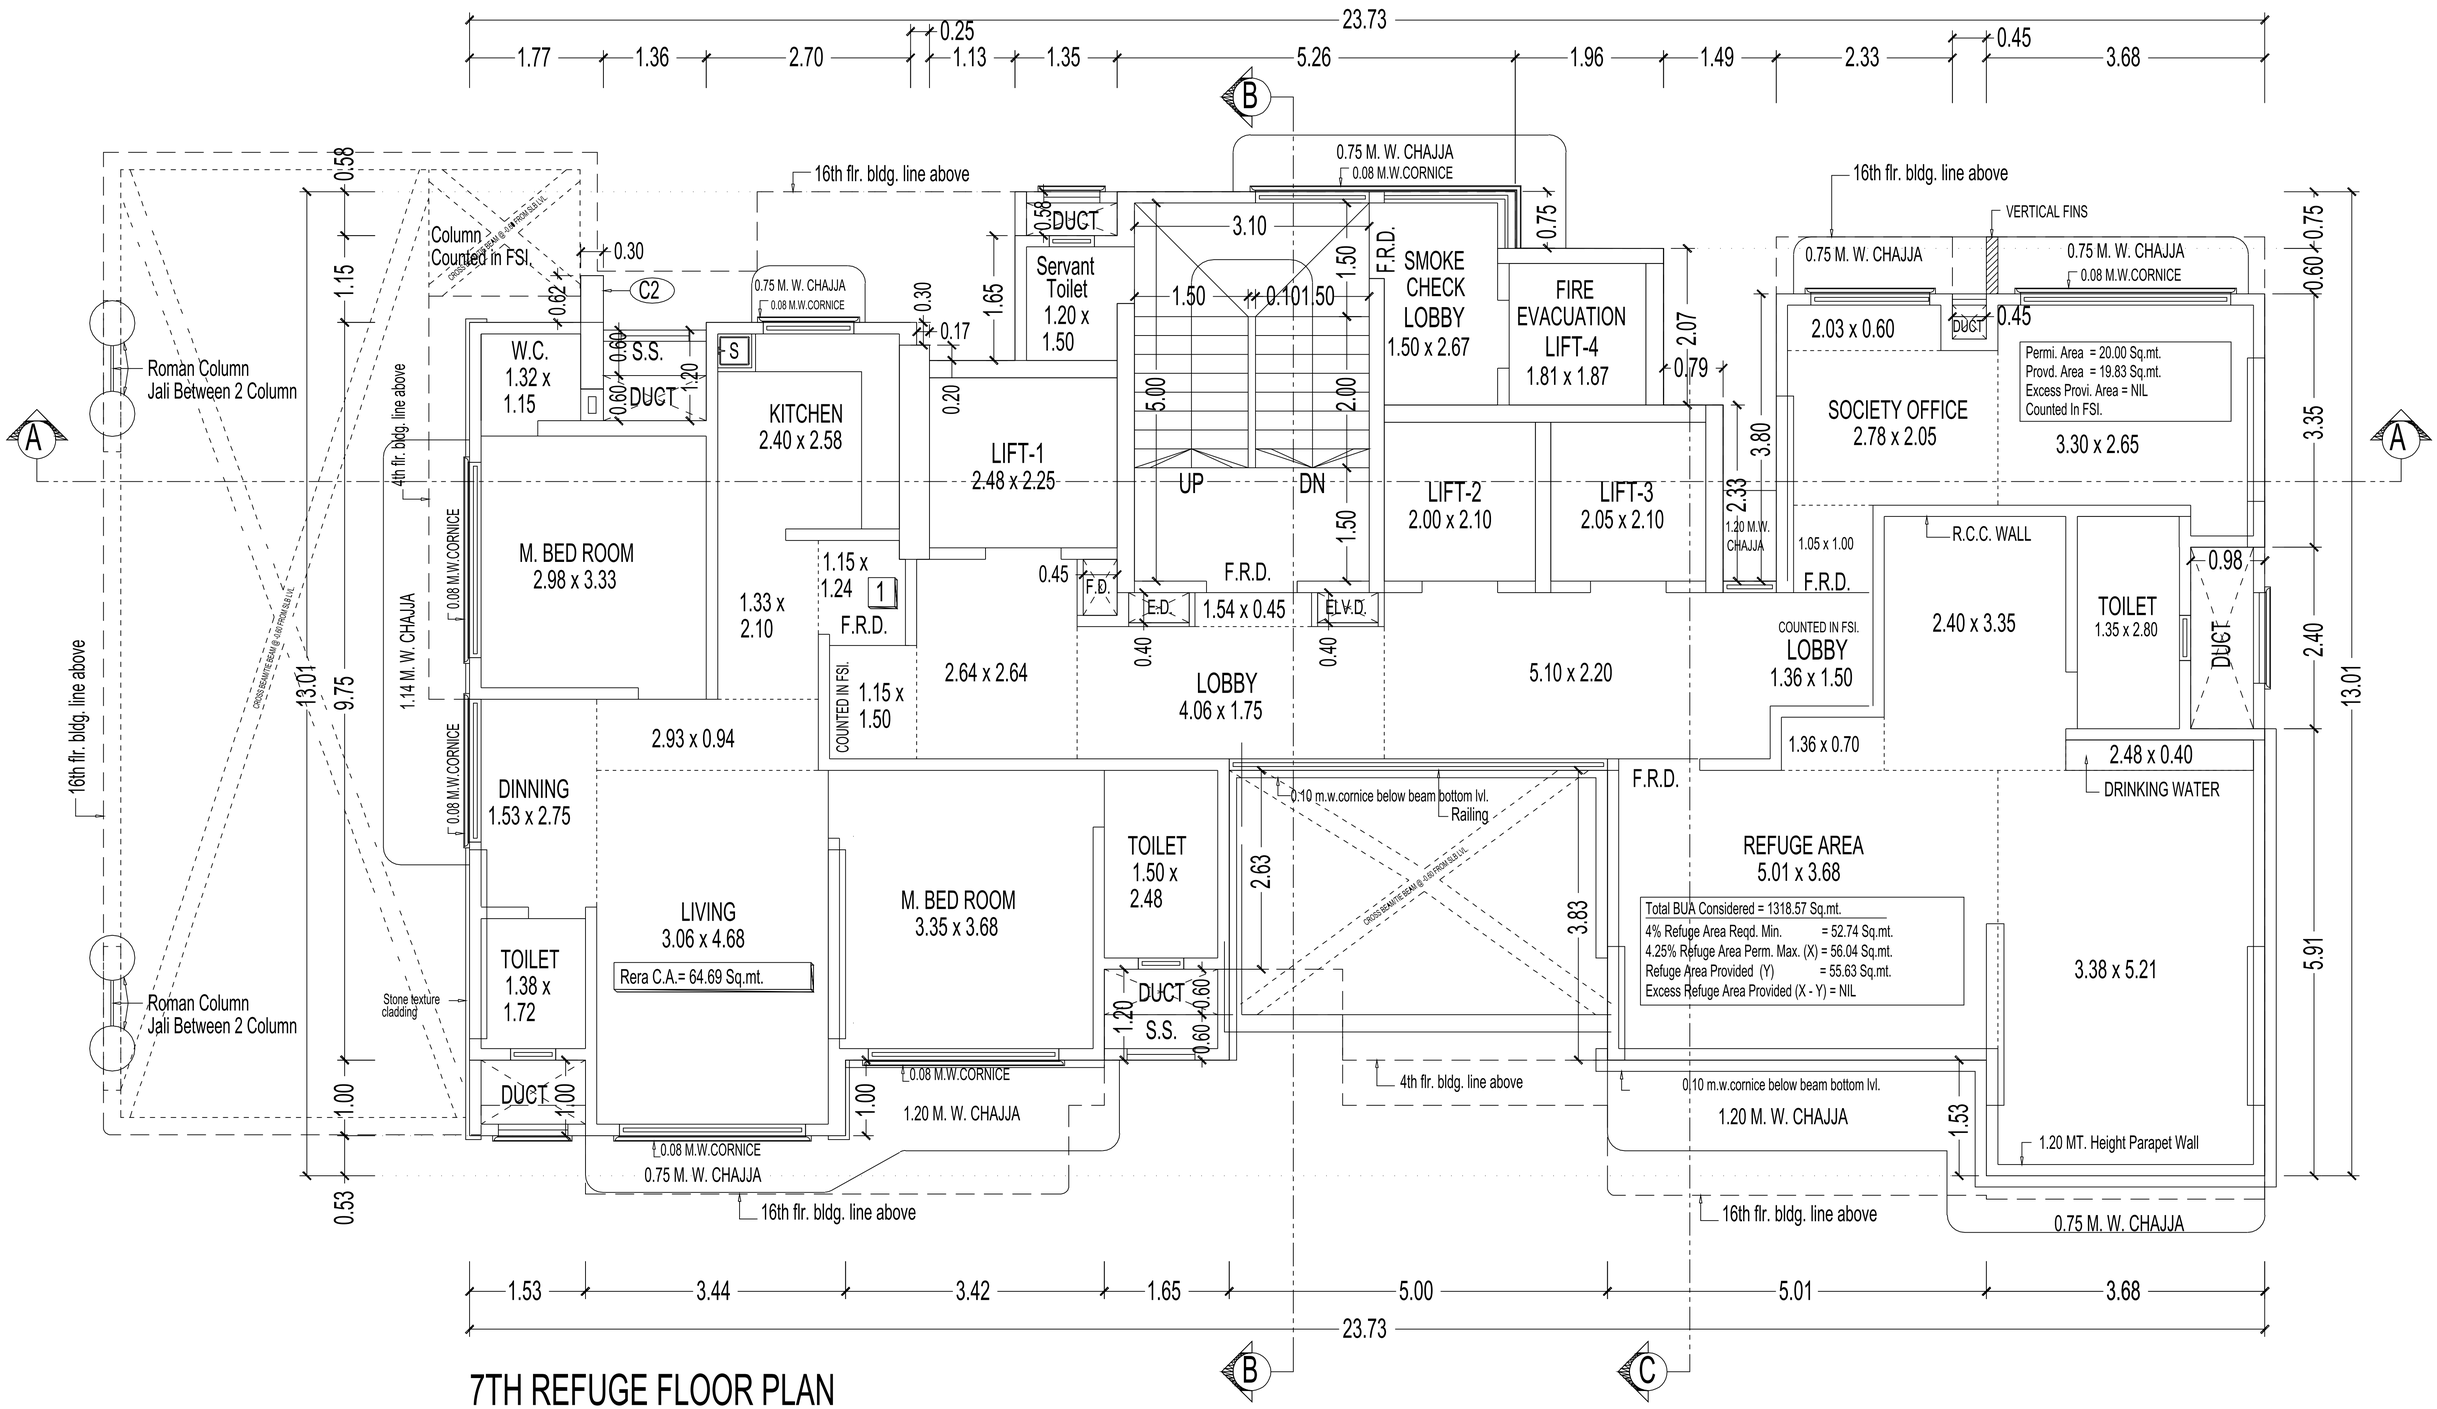


7TH REFUGE FLOOR PLAN

SCALE - 1:100

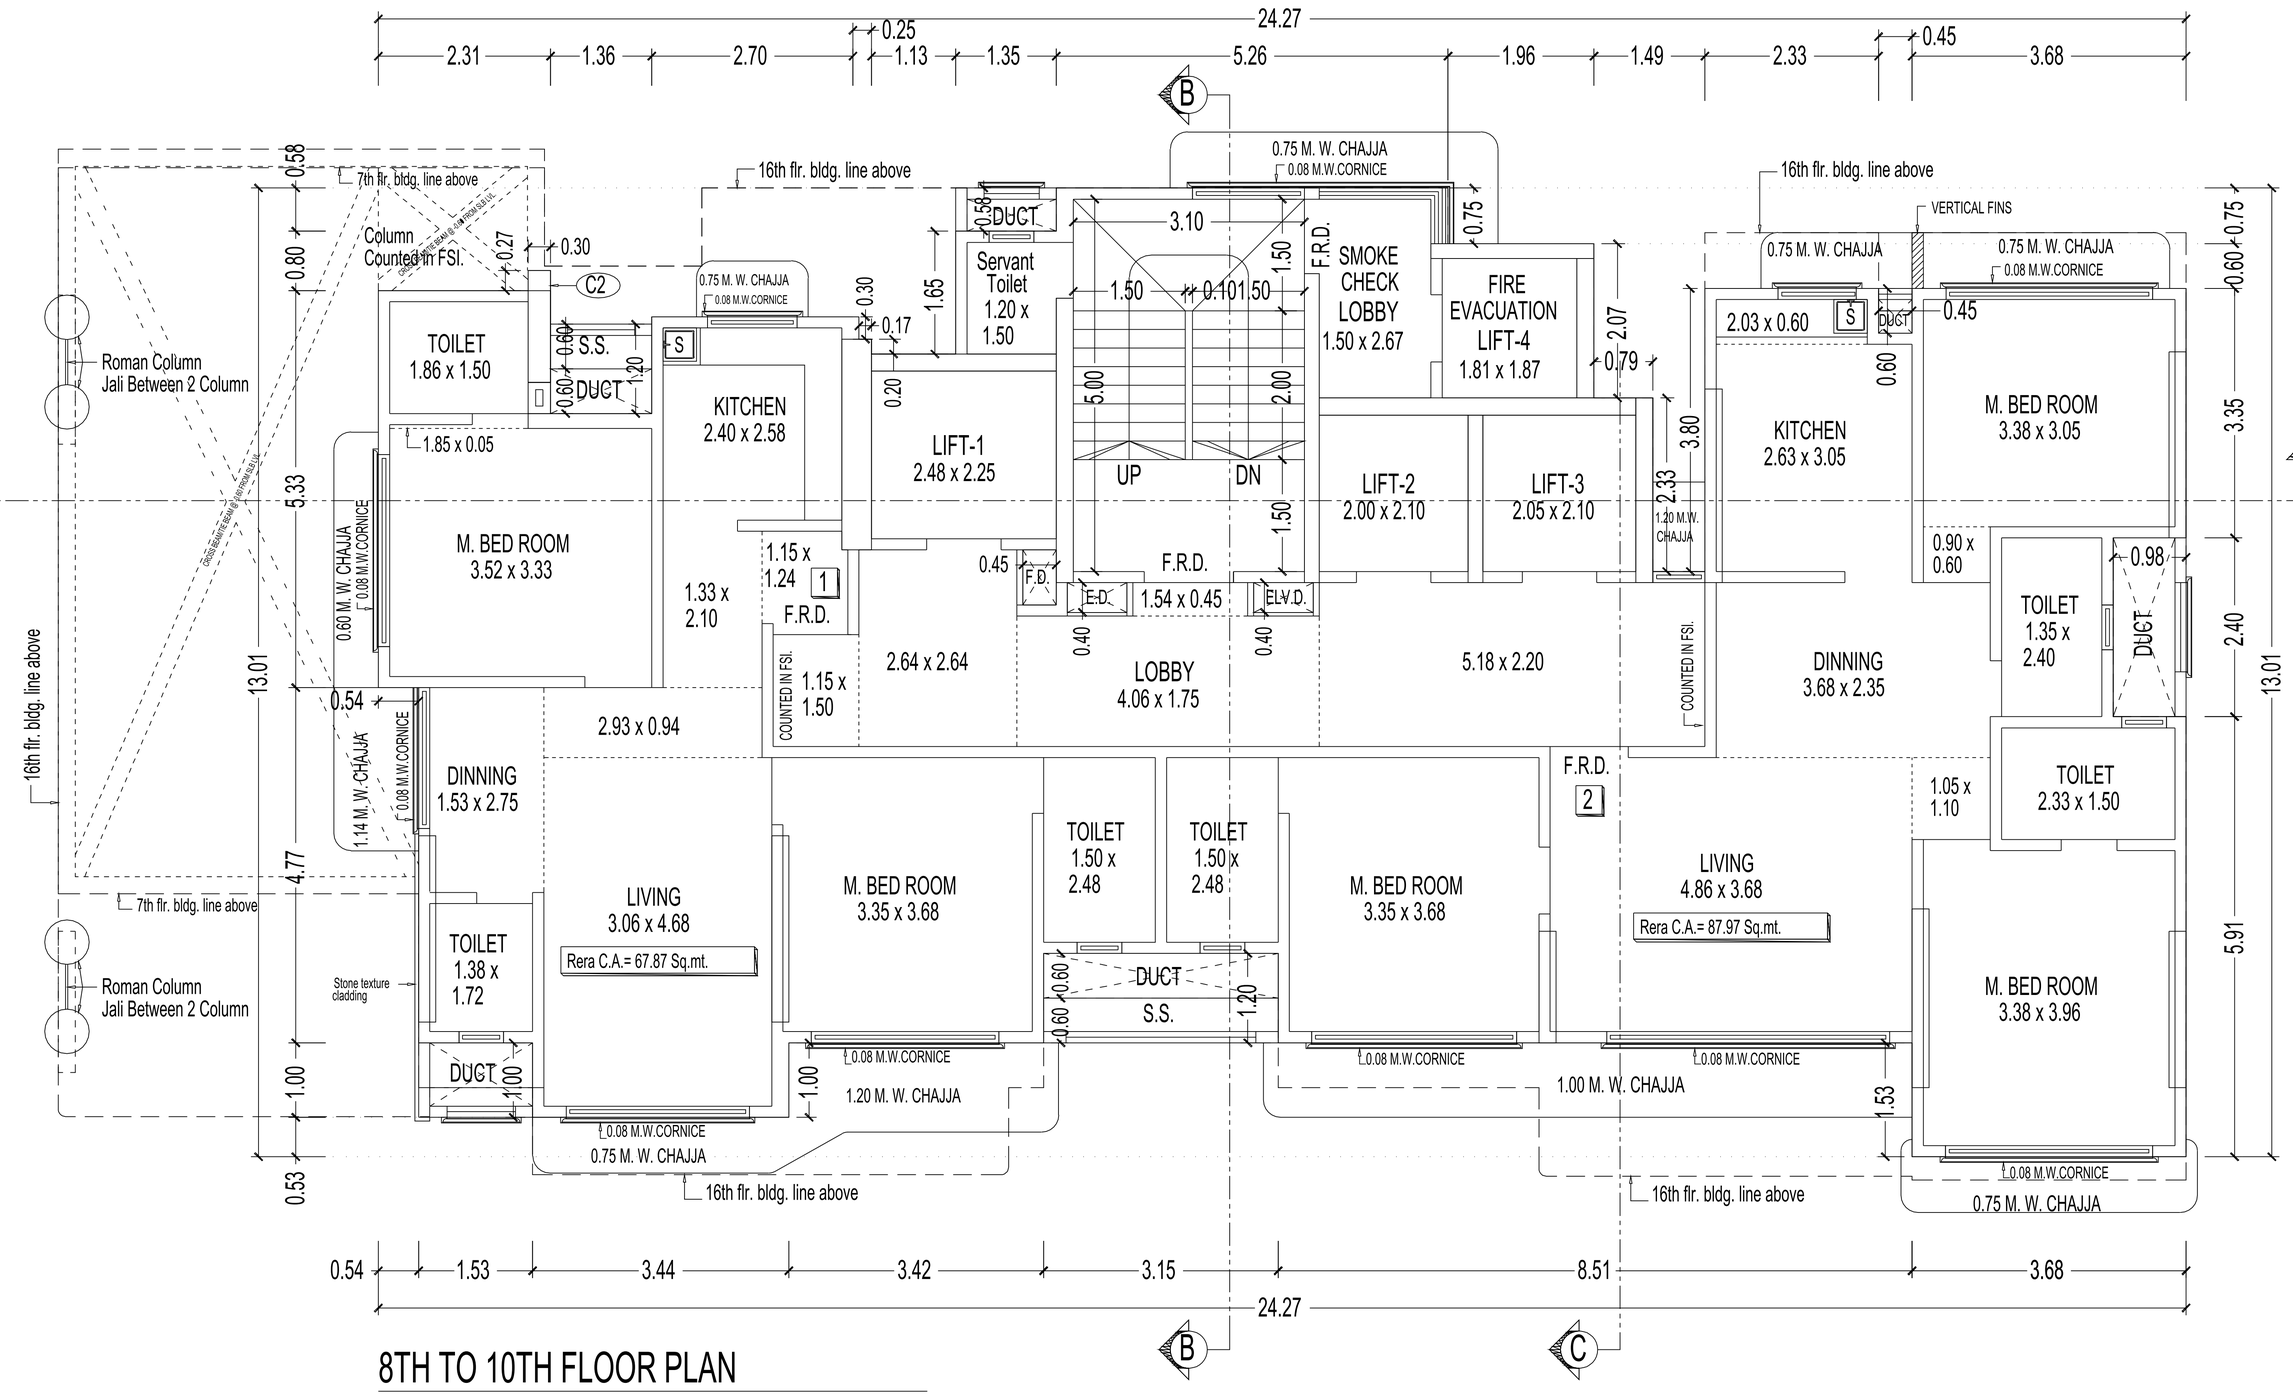

8TH TO 10TH FLOOR PLAN

SCALE - 1:100

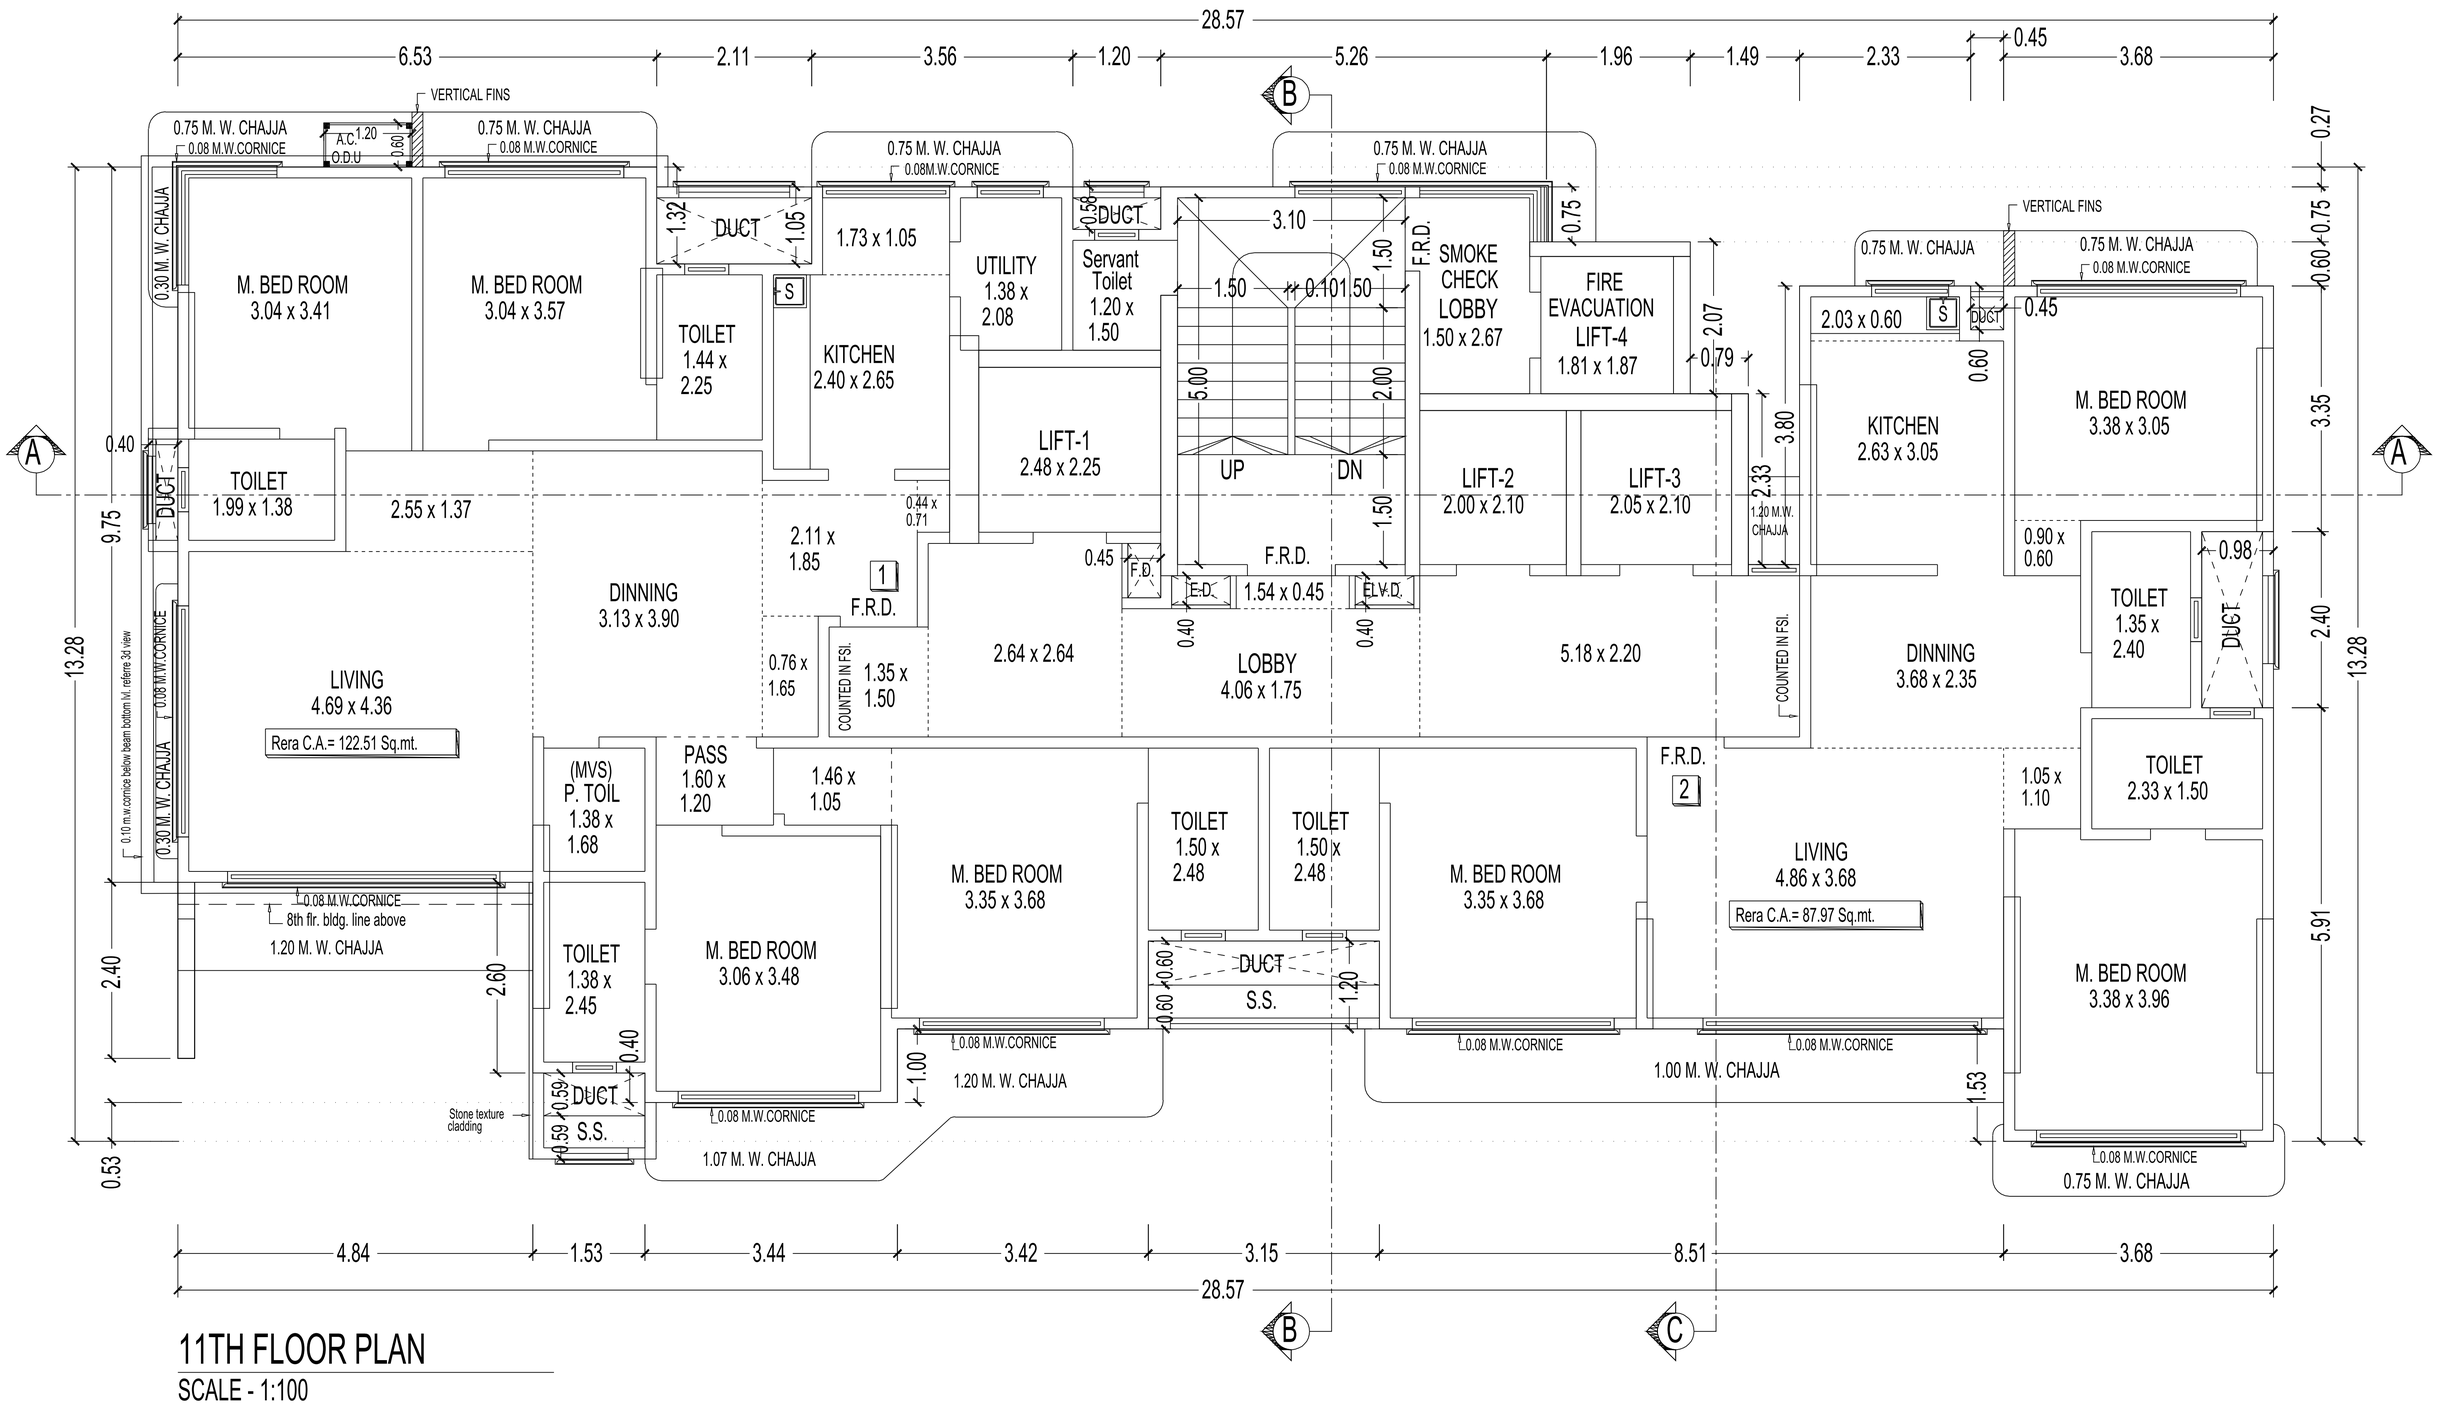

11TH FLOOR PLAN


SCALE - 1:100

12TH FLOOR PLAN

SCALE - 1:100


13TH FLOOR PLAN

SCALE - 1:100

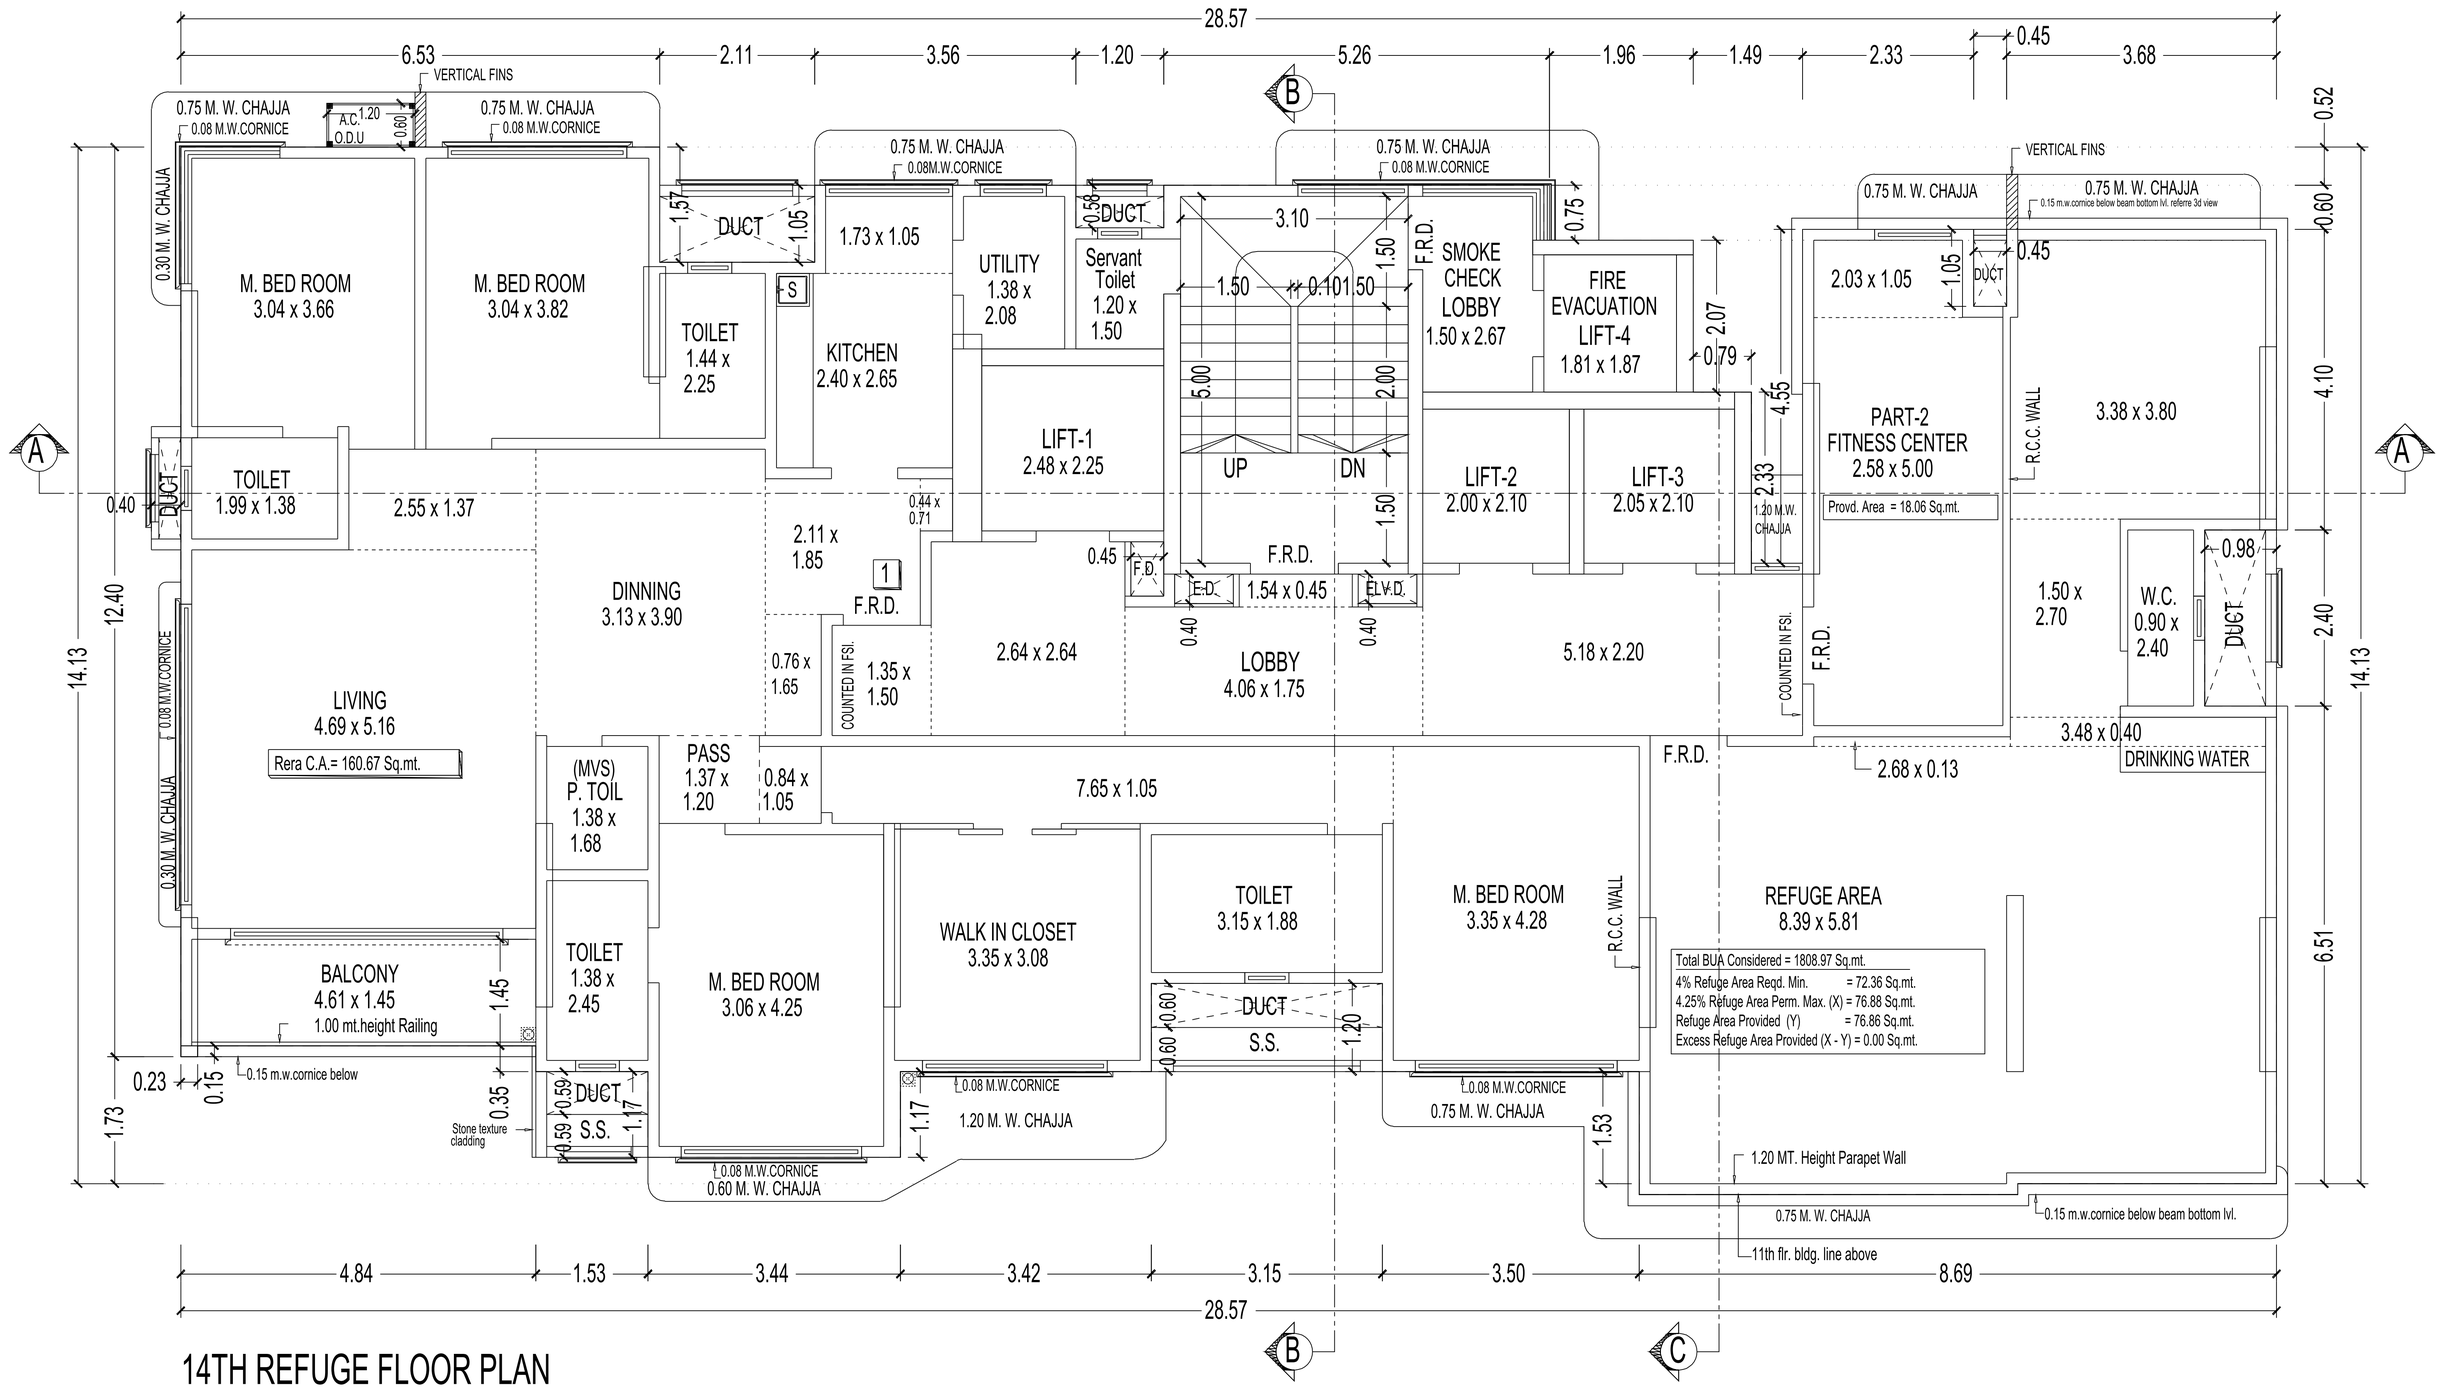


14TH REFUGE FLOOR PLAN

SCALE - 1:100

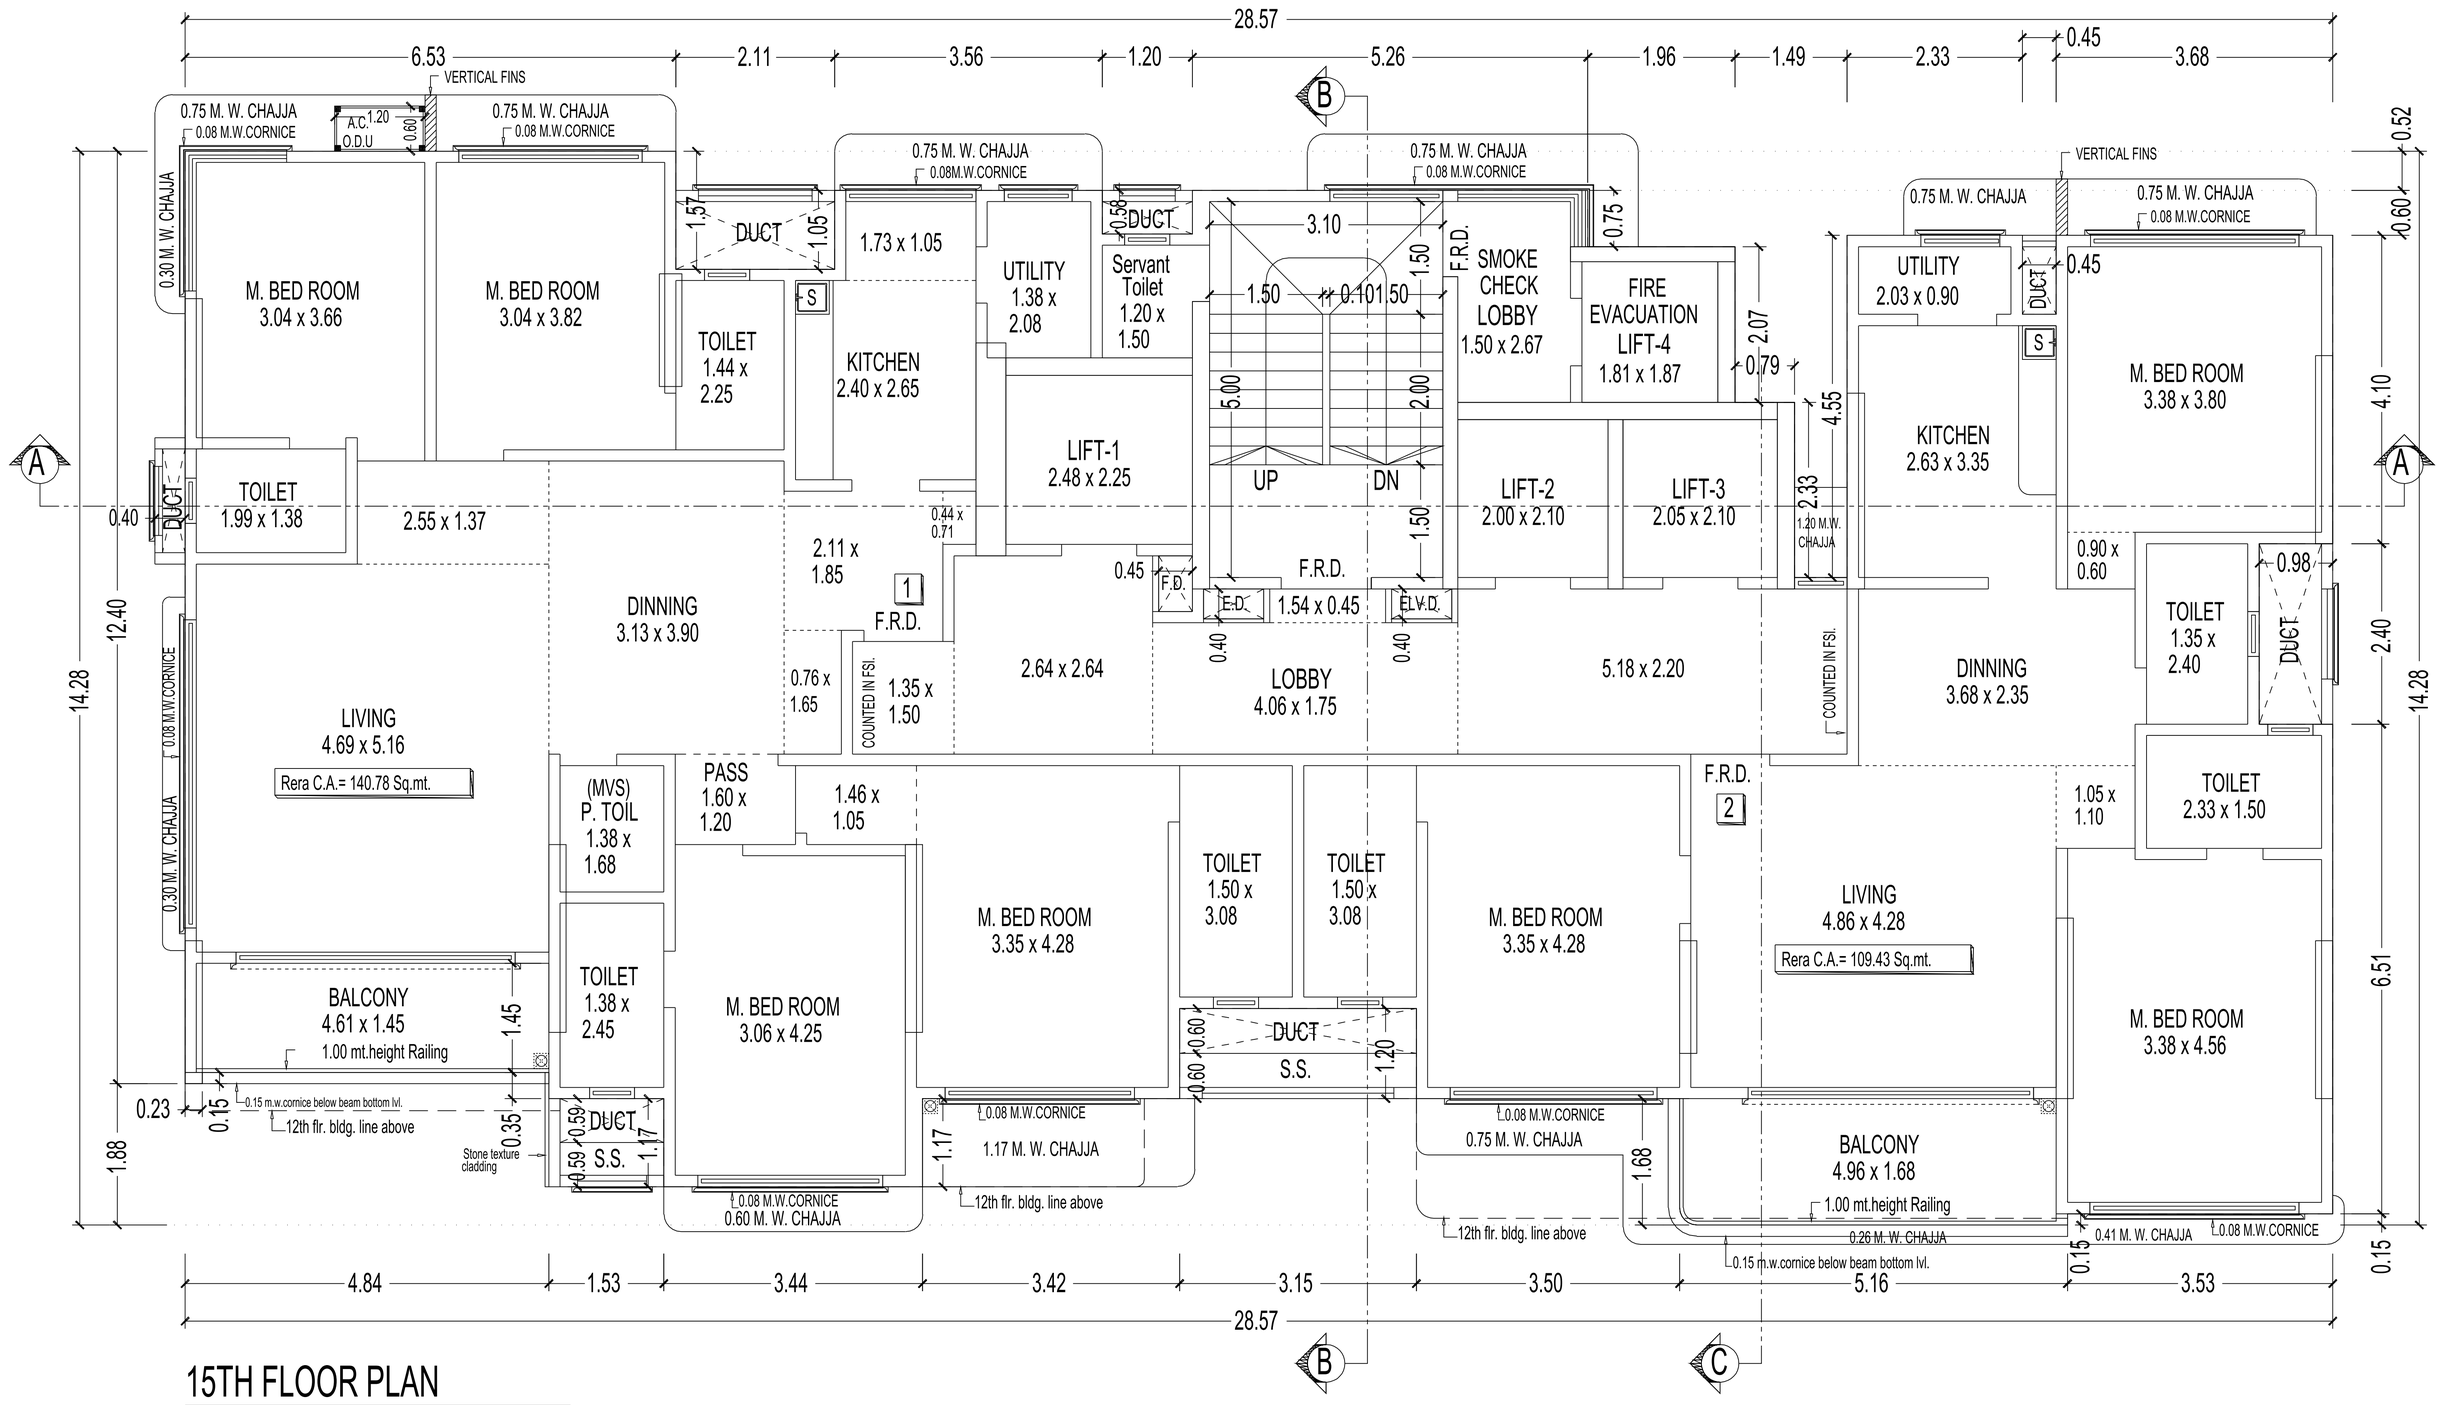

15TH FLOOR PLAN

SCALE - 1:100

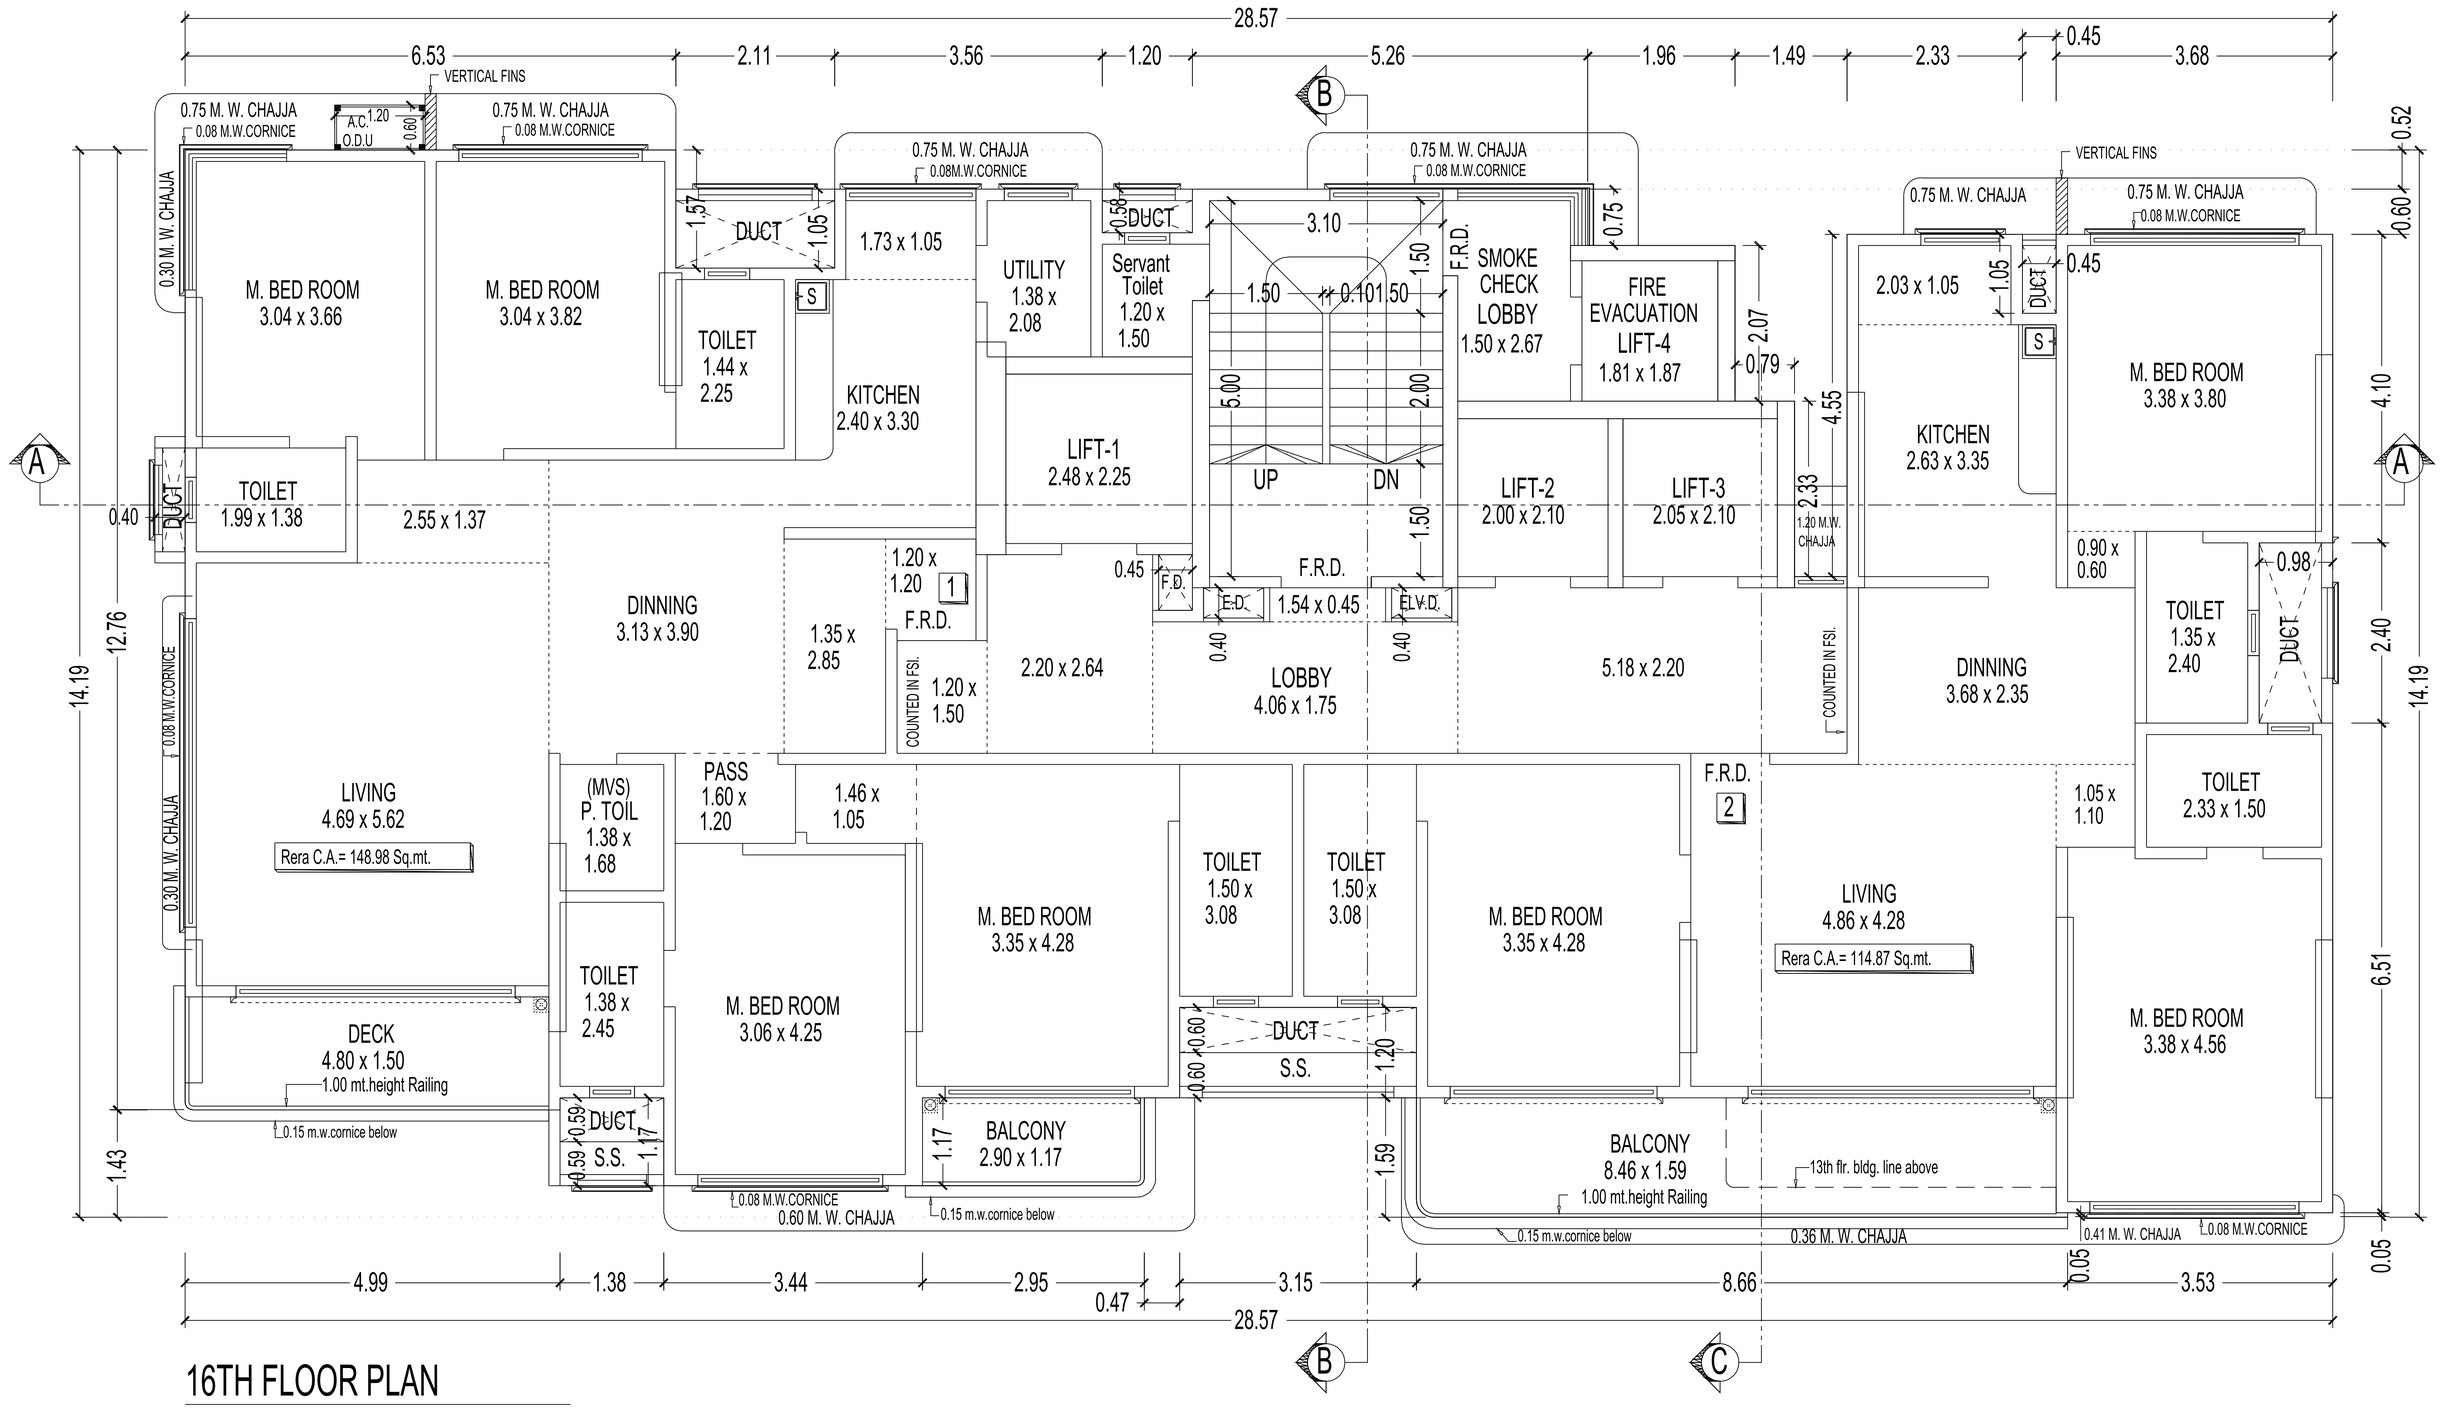


16TH FLOOR PLAN

SCALE - 1:100

17TH FLOOR PLAN

SCALE - 1:100

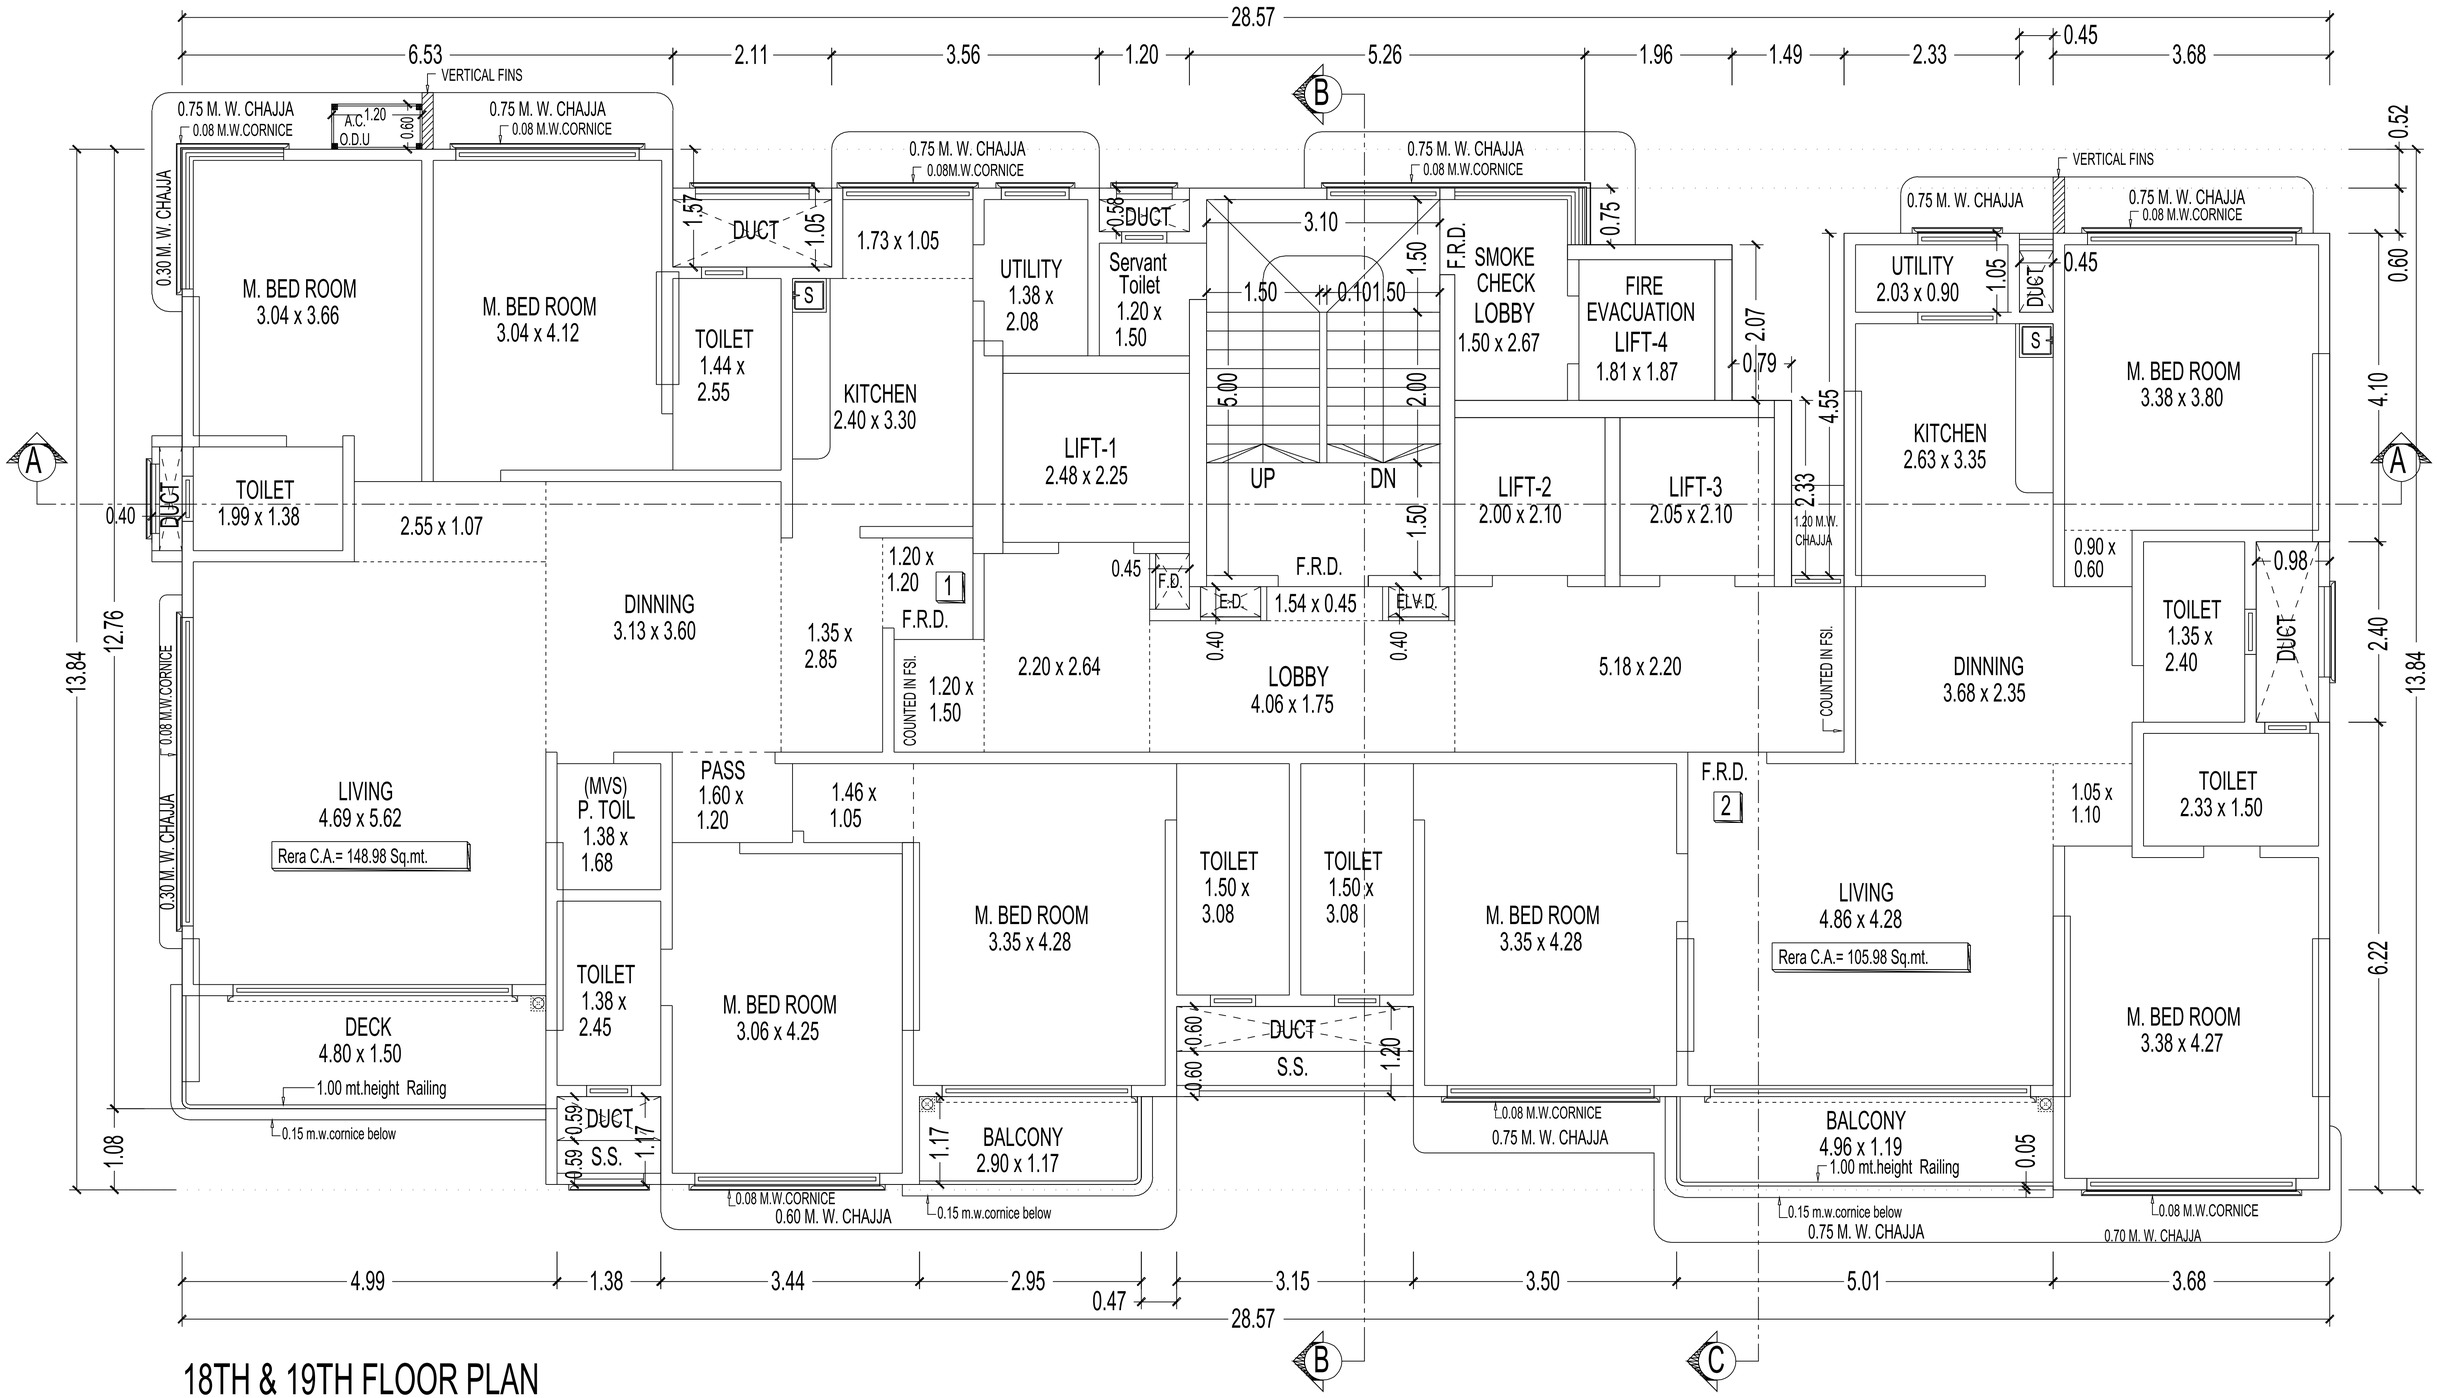

18TH & 19TH FLOOR PLAN

SCALE - 1:100

28.57
6.53
2.11
3.56
1.20
5.26
1.96
1.49
2.33
0.45
3.68
VERTICAL FINS
0.75 M. W. CHAJJA
0.08 M.W.CORNICE
A.C O.D.U 1.20 0.60
Terrace line above
0.30 M. W. CHAJJA
M. BED ROOM 3.04 x 3.66
M. BED ROOM 3.04 x 4.12
TOILET 1.44 x 2.55
DUCT 1.57 1.05
1.73 x 1.05
KITCHEN 2.40 x 3.30
UTILITY 1.38 x 2.08
DUCT 0.58
Servant Toilet 1.20 x 1.50
S
3.10
1.50
0.10
1.50
F.R.D.
SMOKE CHECK LOBBY 1.50 x 2.67
0.75
FIRE EVACUATION LIFT-4 1.81 x 1.87
2.07
0.79
4.55
UTILITY 2.03 x 0.90
1.05
DUCT
0.45
KITCHEN 2.63 x 3.35
M. BED ROOM 3.38 x 3.80
0.52
0.60
4.10
2.40
13.84
12.76
1.08
A
B
C
TOILET 1.99 x 1.38
DUCT 0.40
2.55 x 1.07
DINNING 3.13 x 3.60
1.35 x 2.85
1.20 x 1.20
1
F.R.D.
COUNTED IN FSI.
1.20 x 1.50
2.20 x 2.64
LIFT-1 2.48 x 2.25
5.00
UP
DN
2.00
1.50
0.45
F.D.
E.D.
1.54 x 0.45
ELV.D.
0.40
0.40
LOBBY 4.06 x 1.75
LIFT-2 2.00 x 2.10
LIFT-3 2.05 x 2.10
5.18 x 2.20
2.33
1.20 M.W. CHAJJA
COUNTED IN FSI.
0.90 x 0.60
0.98
TOILET 1.35 x 2.40
DUCT
DINNING 3.68 x 2.35
LIVING 4.69 x 5.62
Rera C.A.= 148.98 Sq.mt.
PASS 1.60 x 1.20
1.46 x 1.05
(MVS) P. TOIL 1.38 x 1.68
TOILET 1.38 x 2.45
M. BED ROOM 3.06 x 4.25
M. BED ROOM 3.35 x 4.28
TOILET 1.50 x 3.08
TOILET 1.50 x 3.08
M. BED ROOM 3.35 x 4.28
F.R.D.
2
1.05 x 1.10
TOILET 2.33 x 1.50
LIVING 4.86 x 4.28
Rera C.A.= 105.98 Sq.mt.
M. BED ROOM 3.38 x 4.27
DECK 4.80 x 1.50
1.00 mt.height Railing
0.15 m.w.cornice below
DUCT 0.59 0.59 1.17
S.S.
BALCONY 2.90 x 1.17
1.17
0.08 M.W.CORNICE
0.60 M. W. CHAJJA
0.15 m.w.cornice below
DUCT 0.60 0.60 1.20
S.S.
0.08 M.W.CORNICE
0.75 M. W. CHAJJA
BALCONY 4.96 x 1.19
1.00 mt.height Railing
0.05
0.15 m.w.cornice below
0.75 M. W. CHAJJA
0.70 M. W. CHAJJA
0.08 M.W.CORNICE
6.22
Terrace line above
4.99
1.38
3.44
2.95
0.27
3.35
3.50
5.01
3.68
28.57

20TH FLOOR PLAN

SCALE - 1:100