

SCALE - 1:100

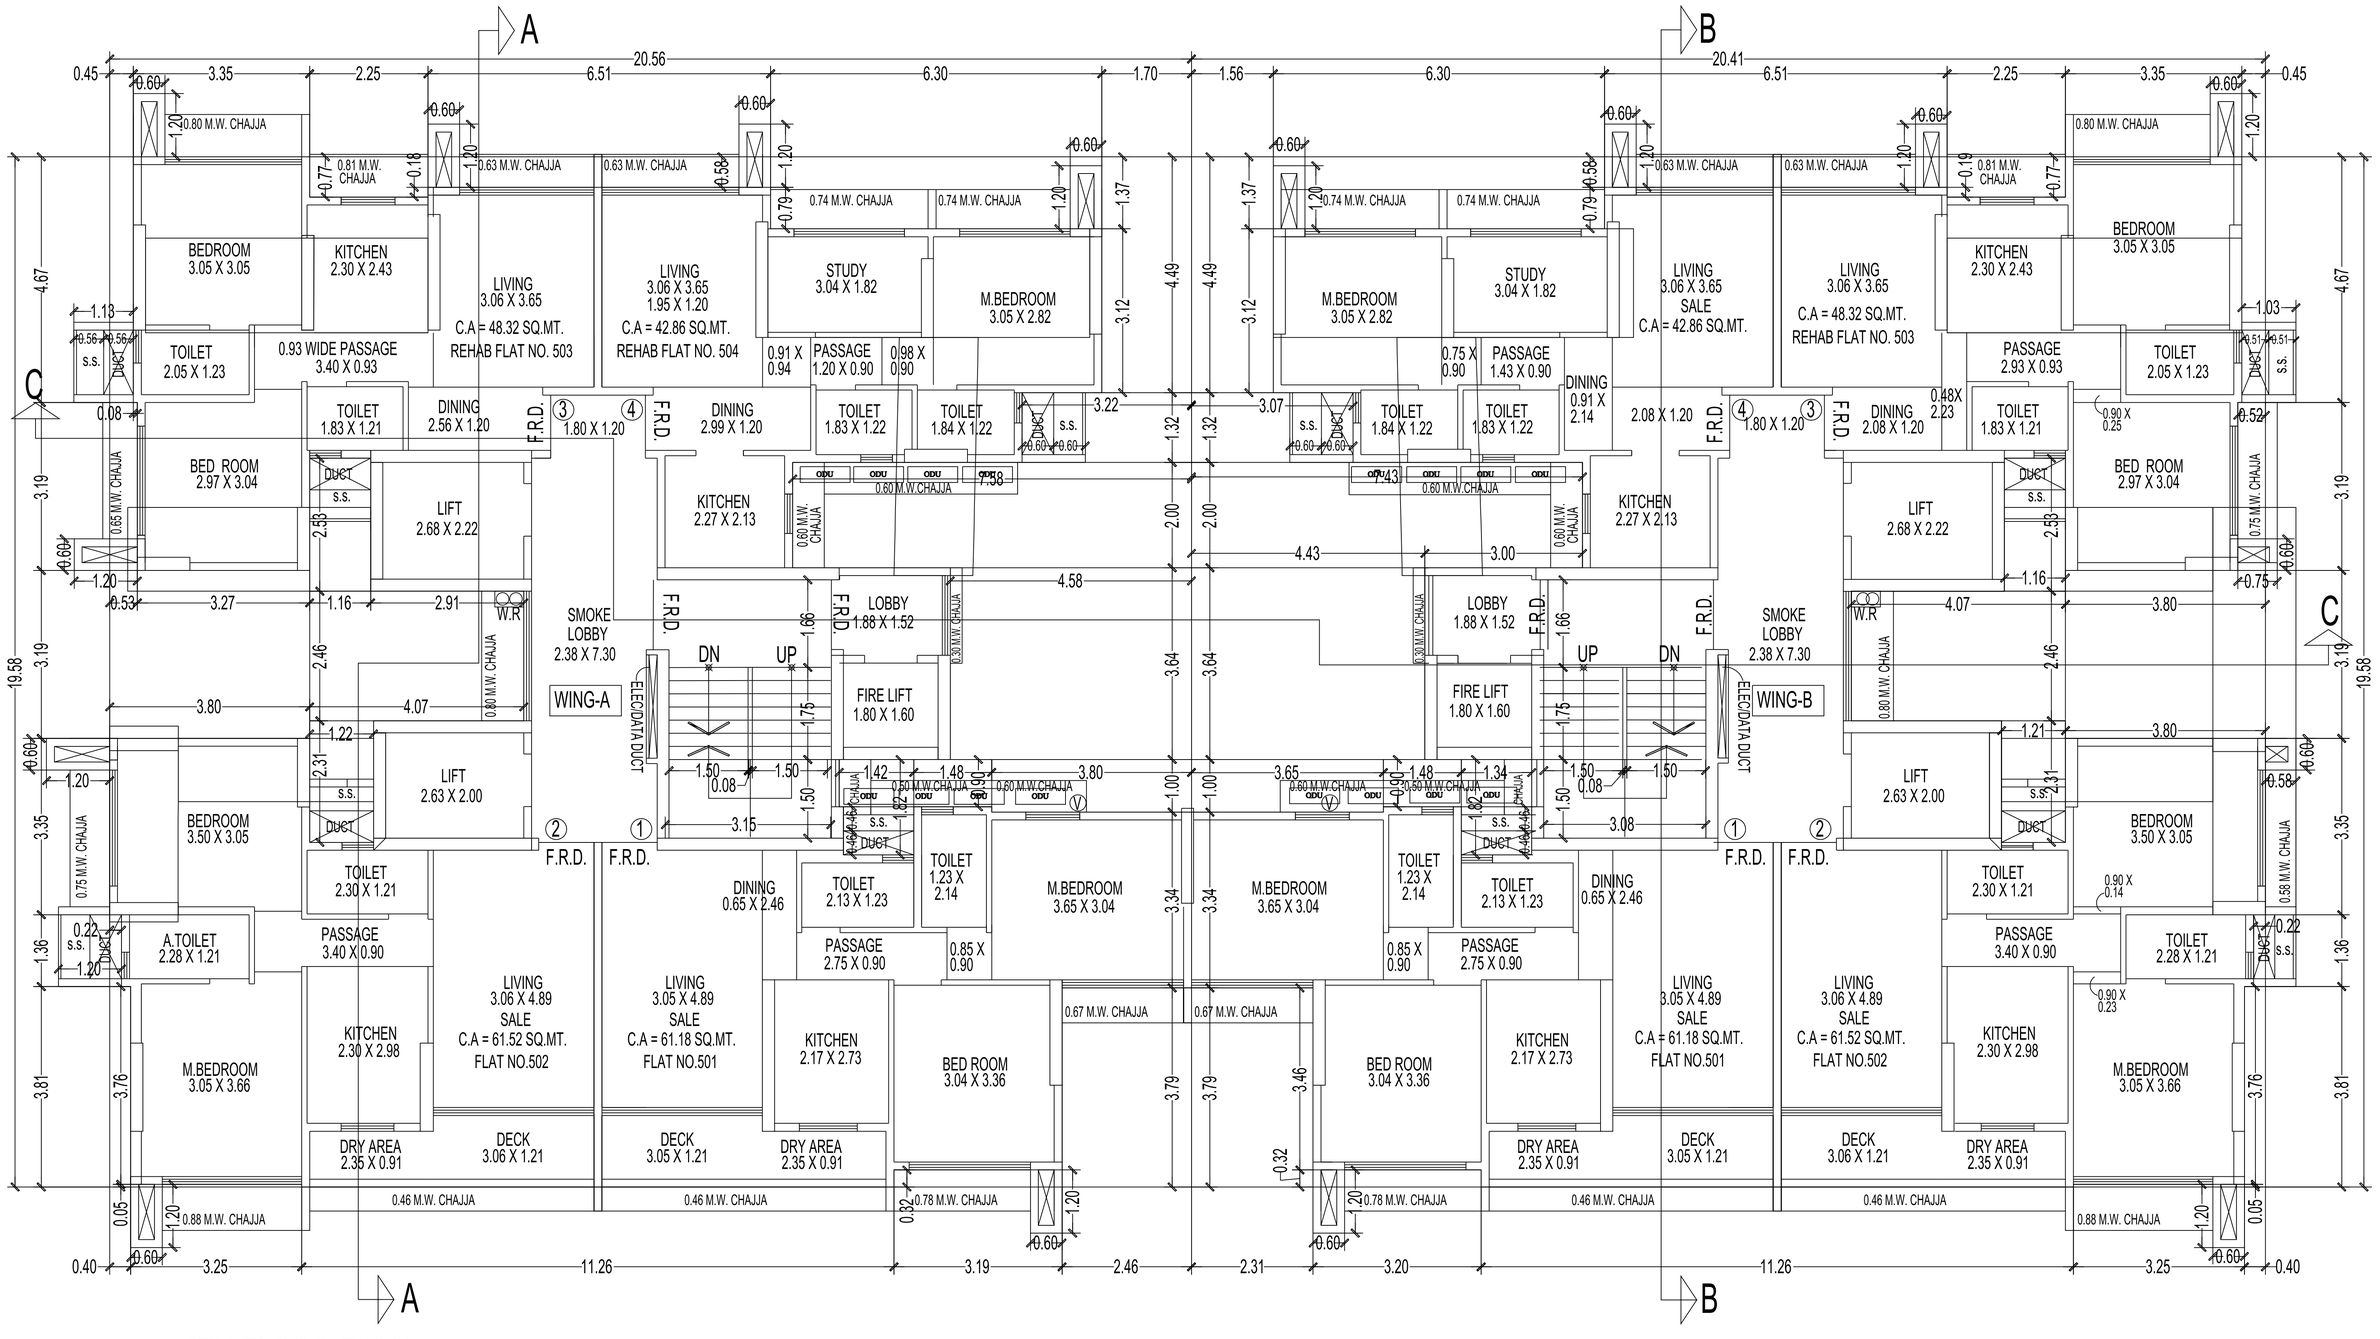


5TH FLOOR PLAN


SCALE - 1:100

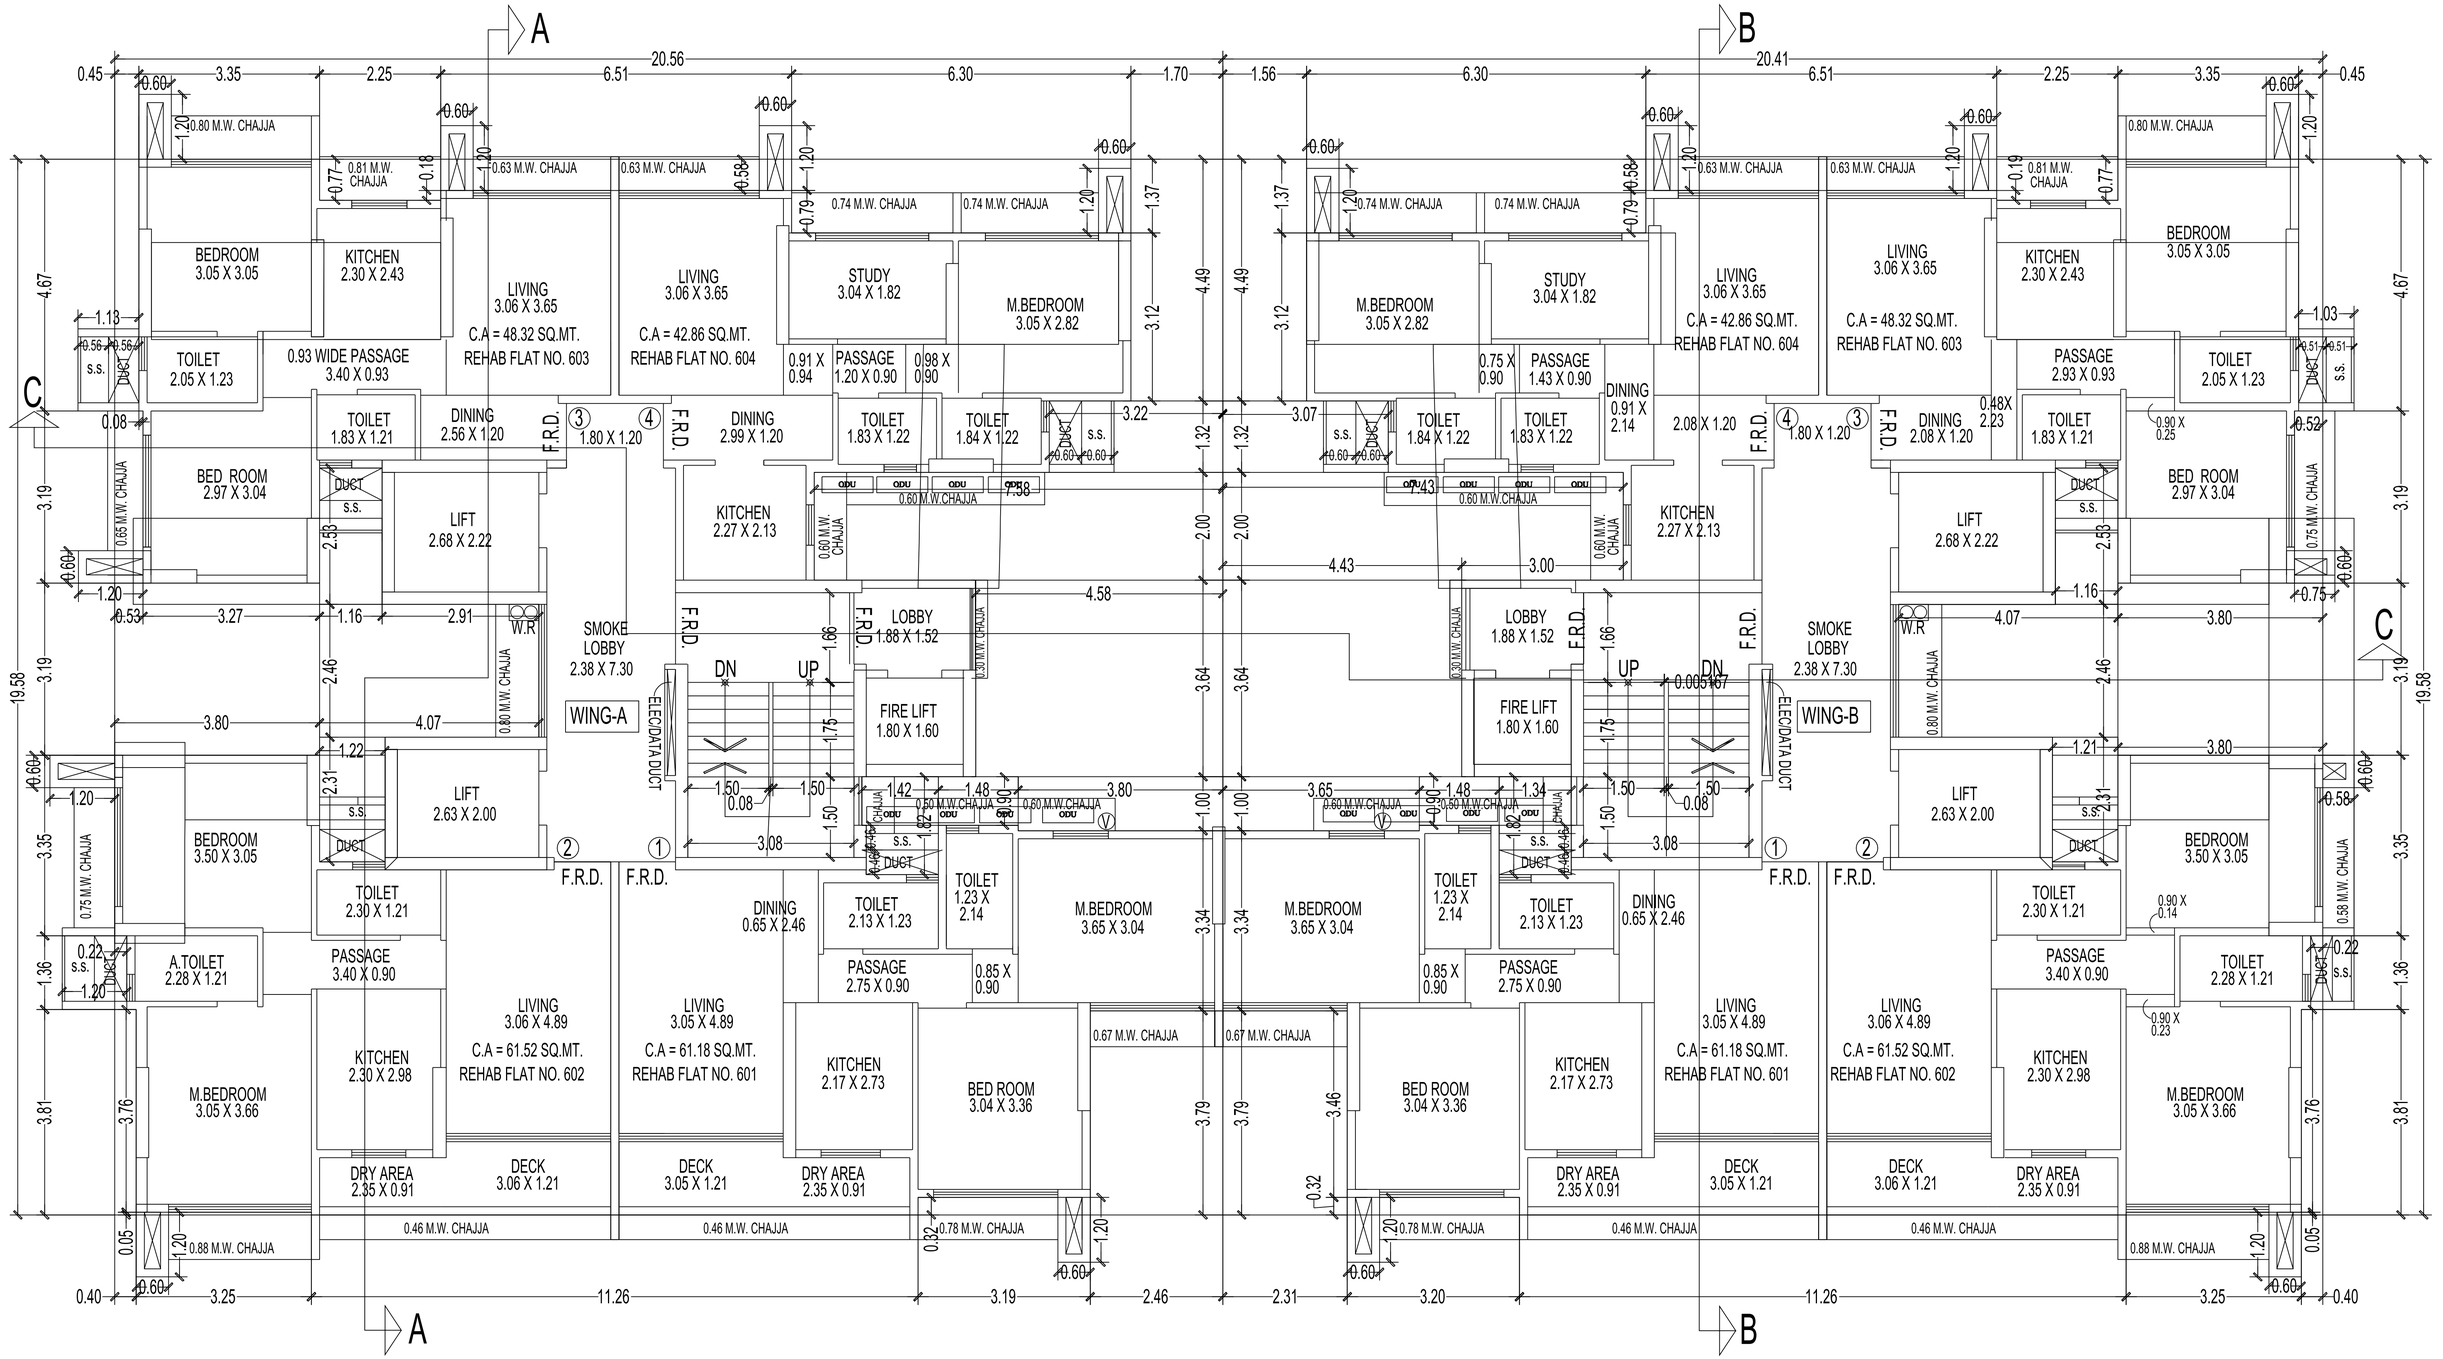


6TH FLOOR PLAN

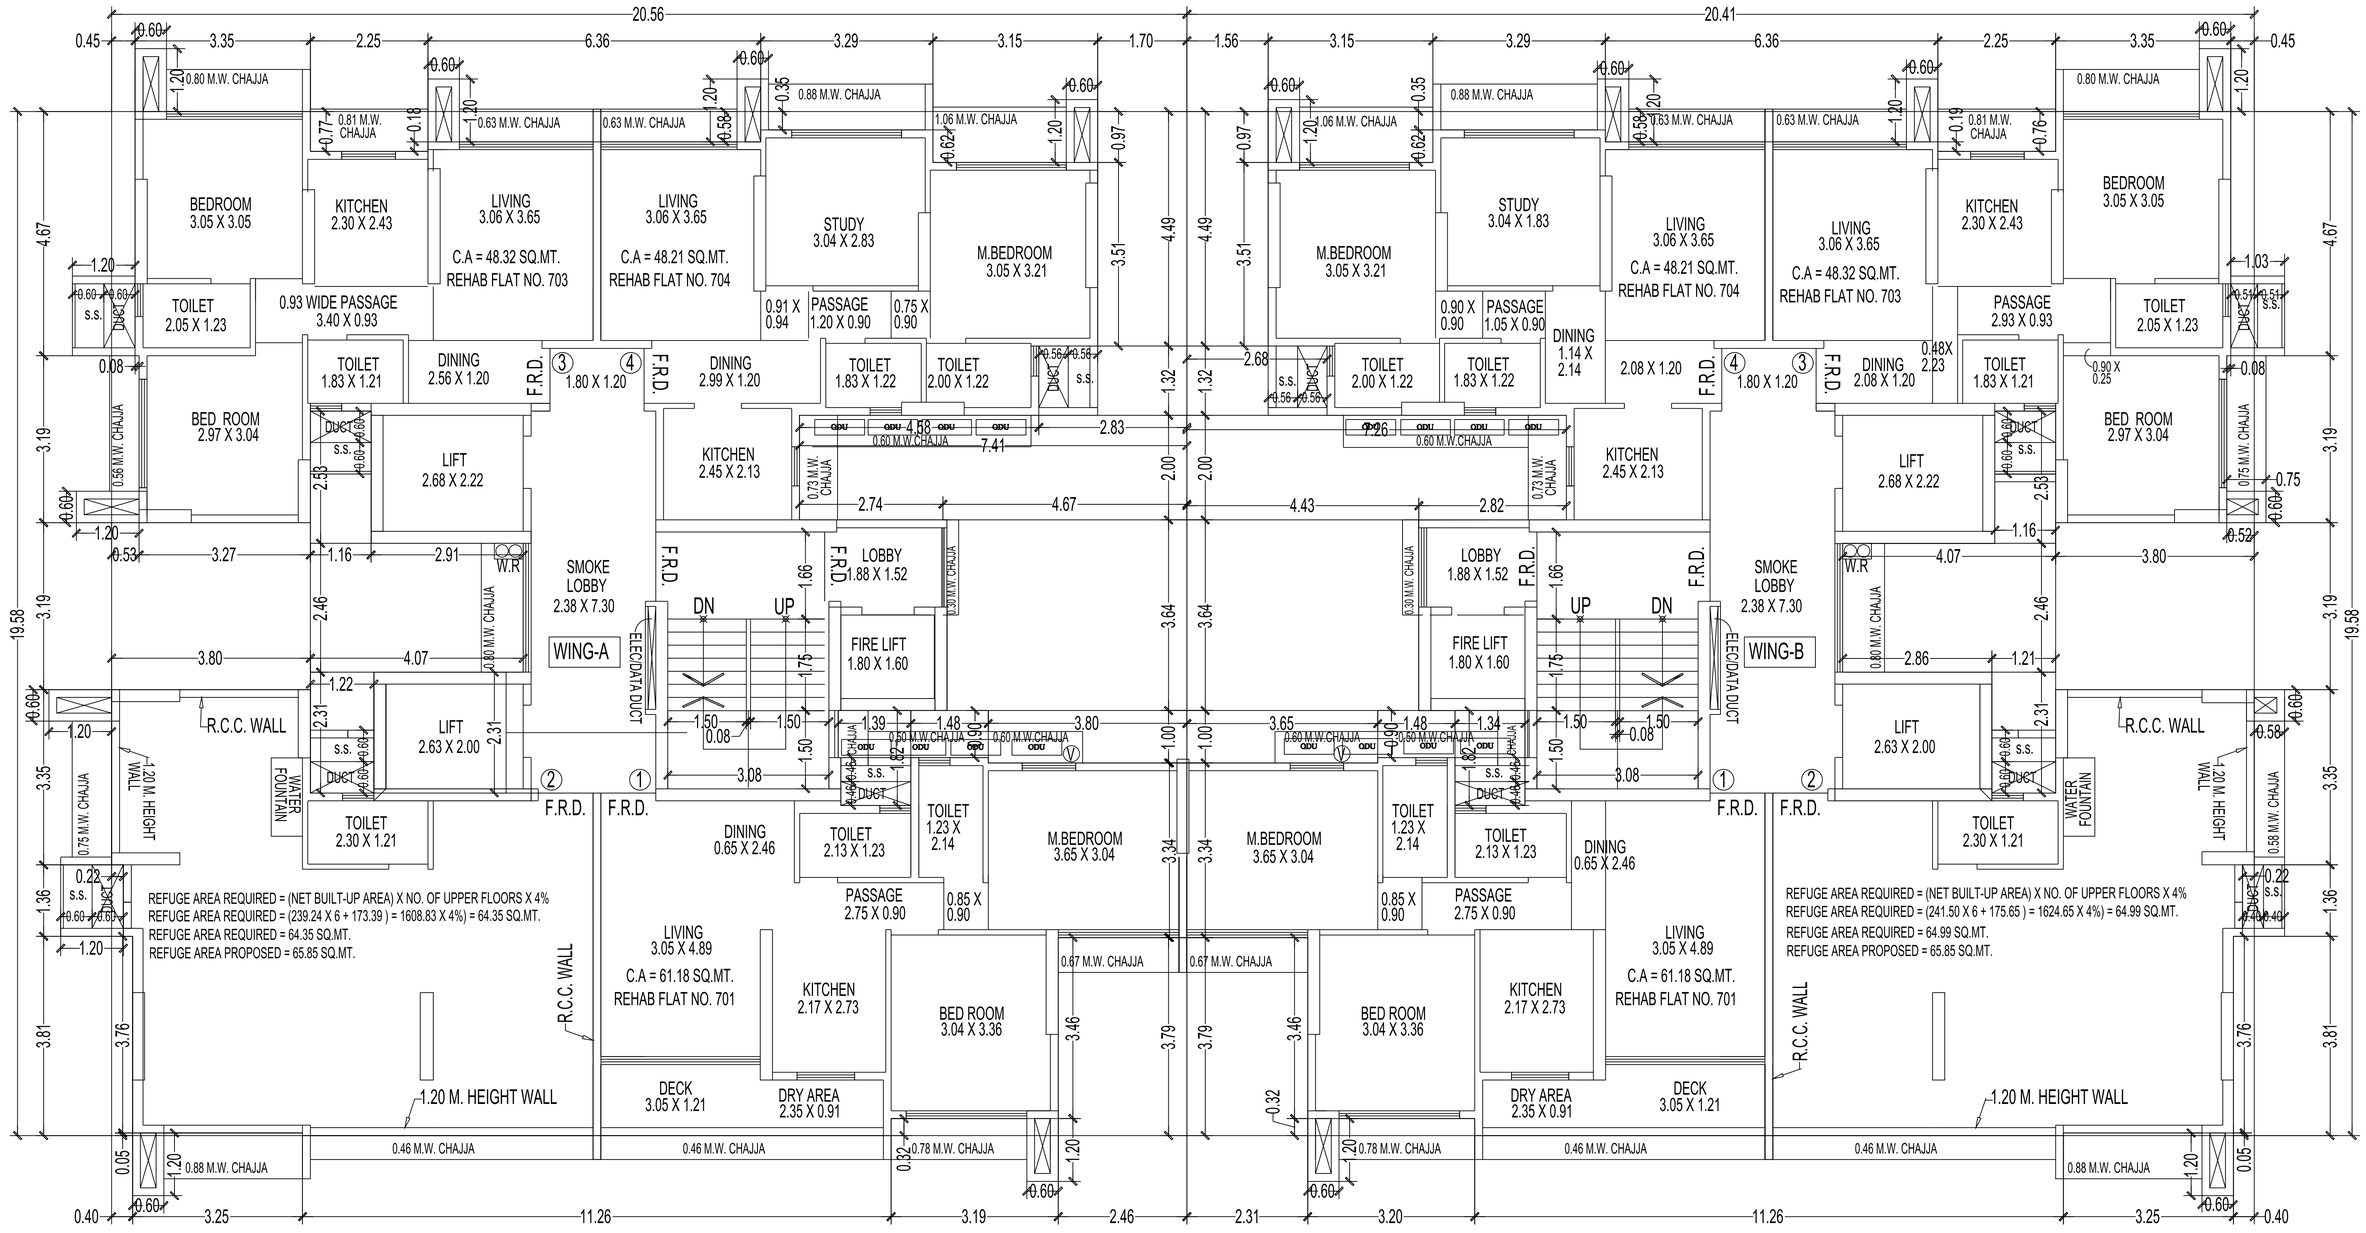


7TH FLOOR PLAN
SCALE - 1:100

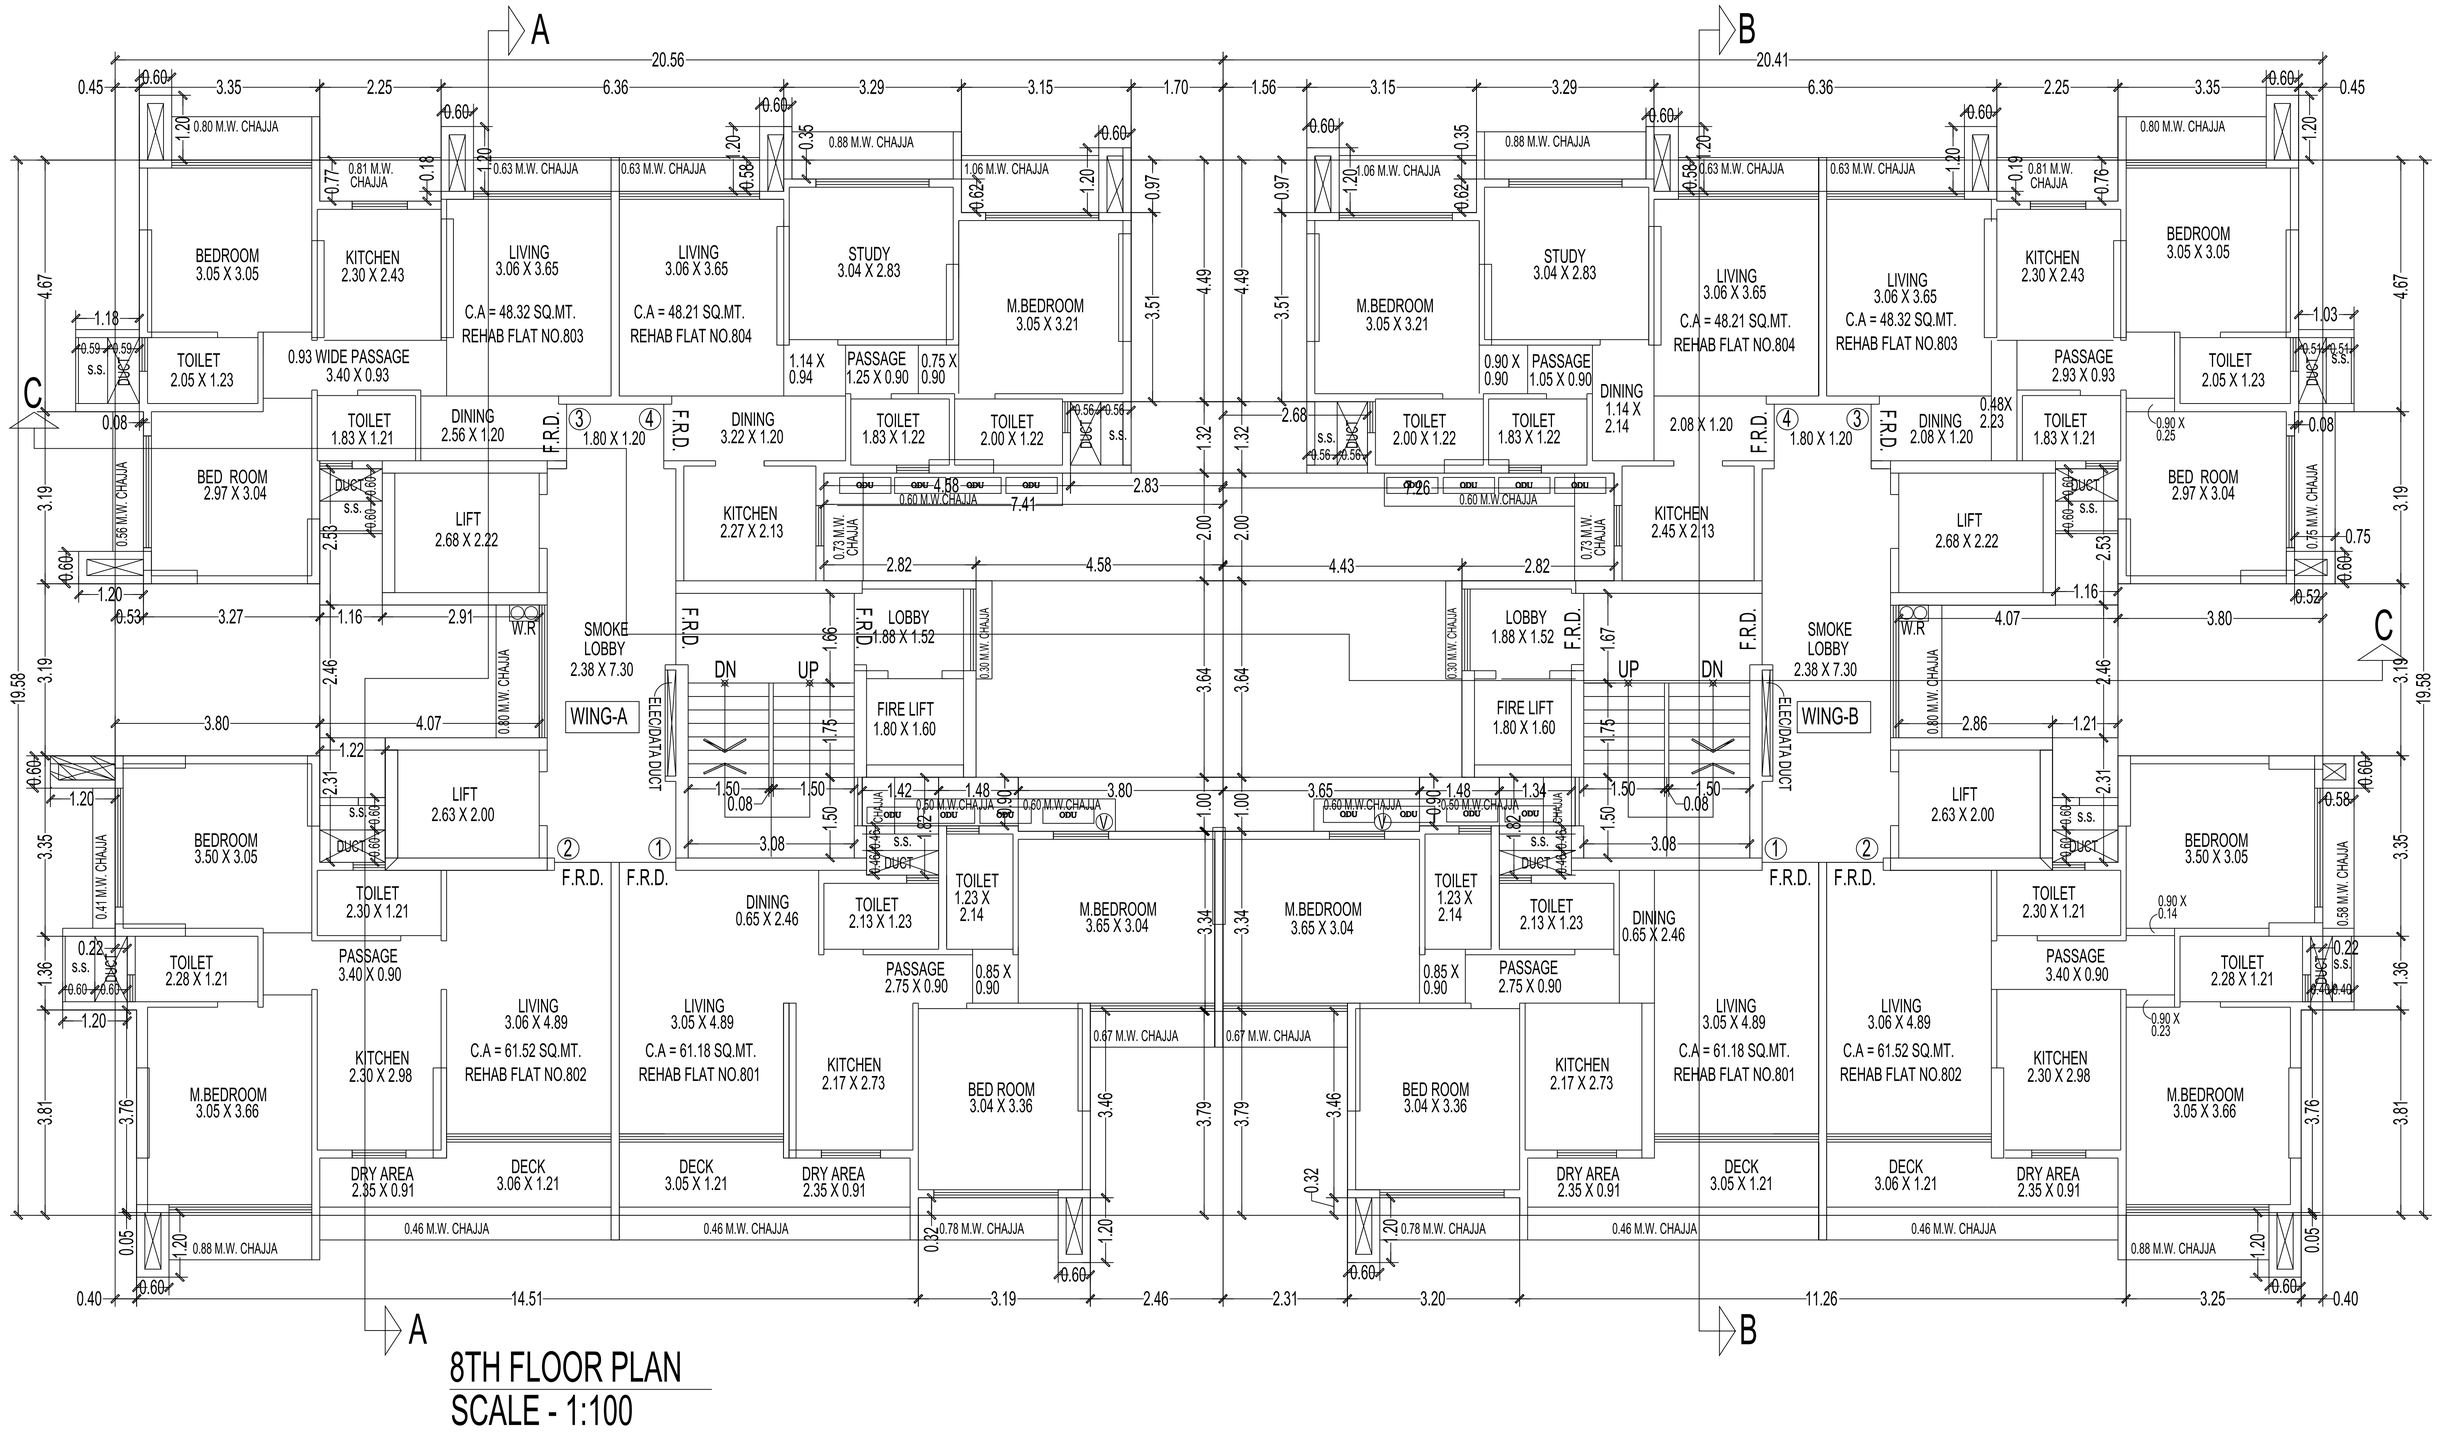


8TH FLOOR PLAN
SCALE - 1:100

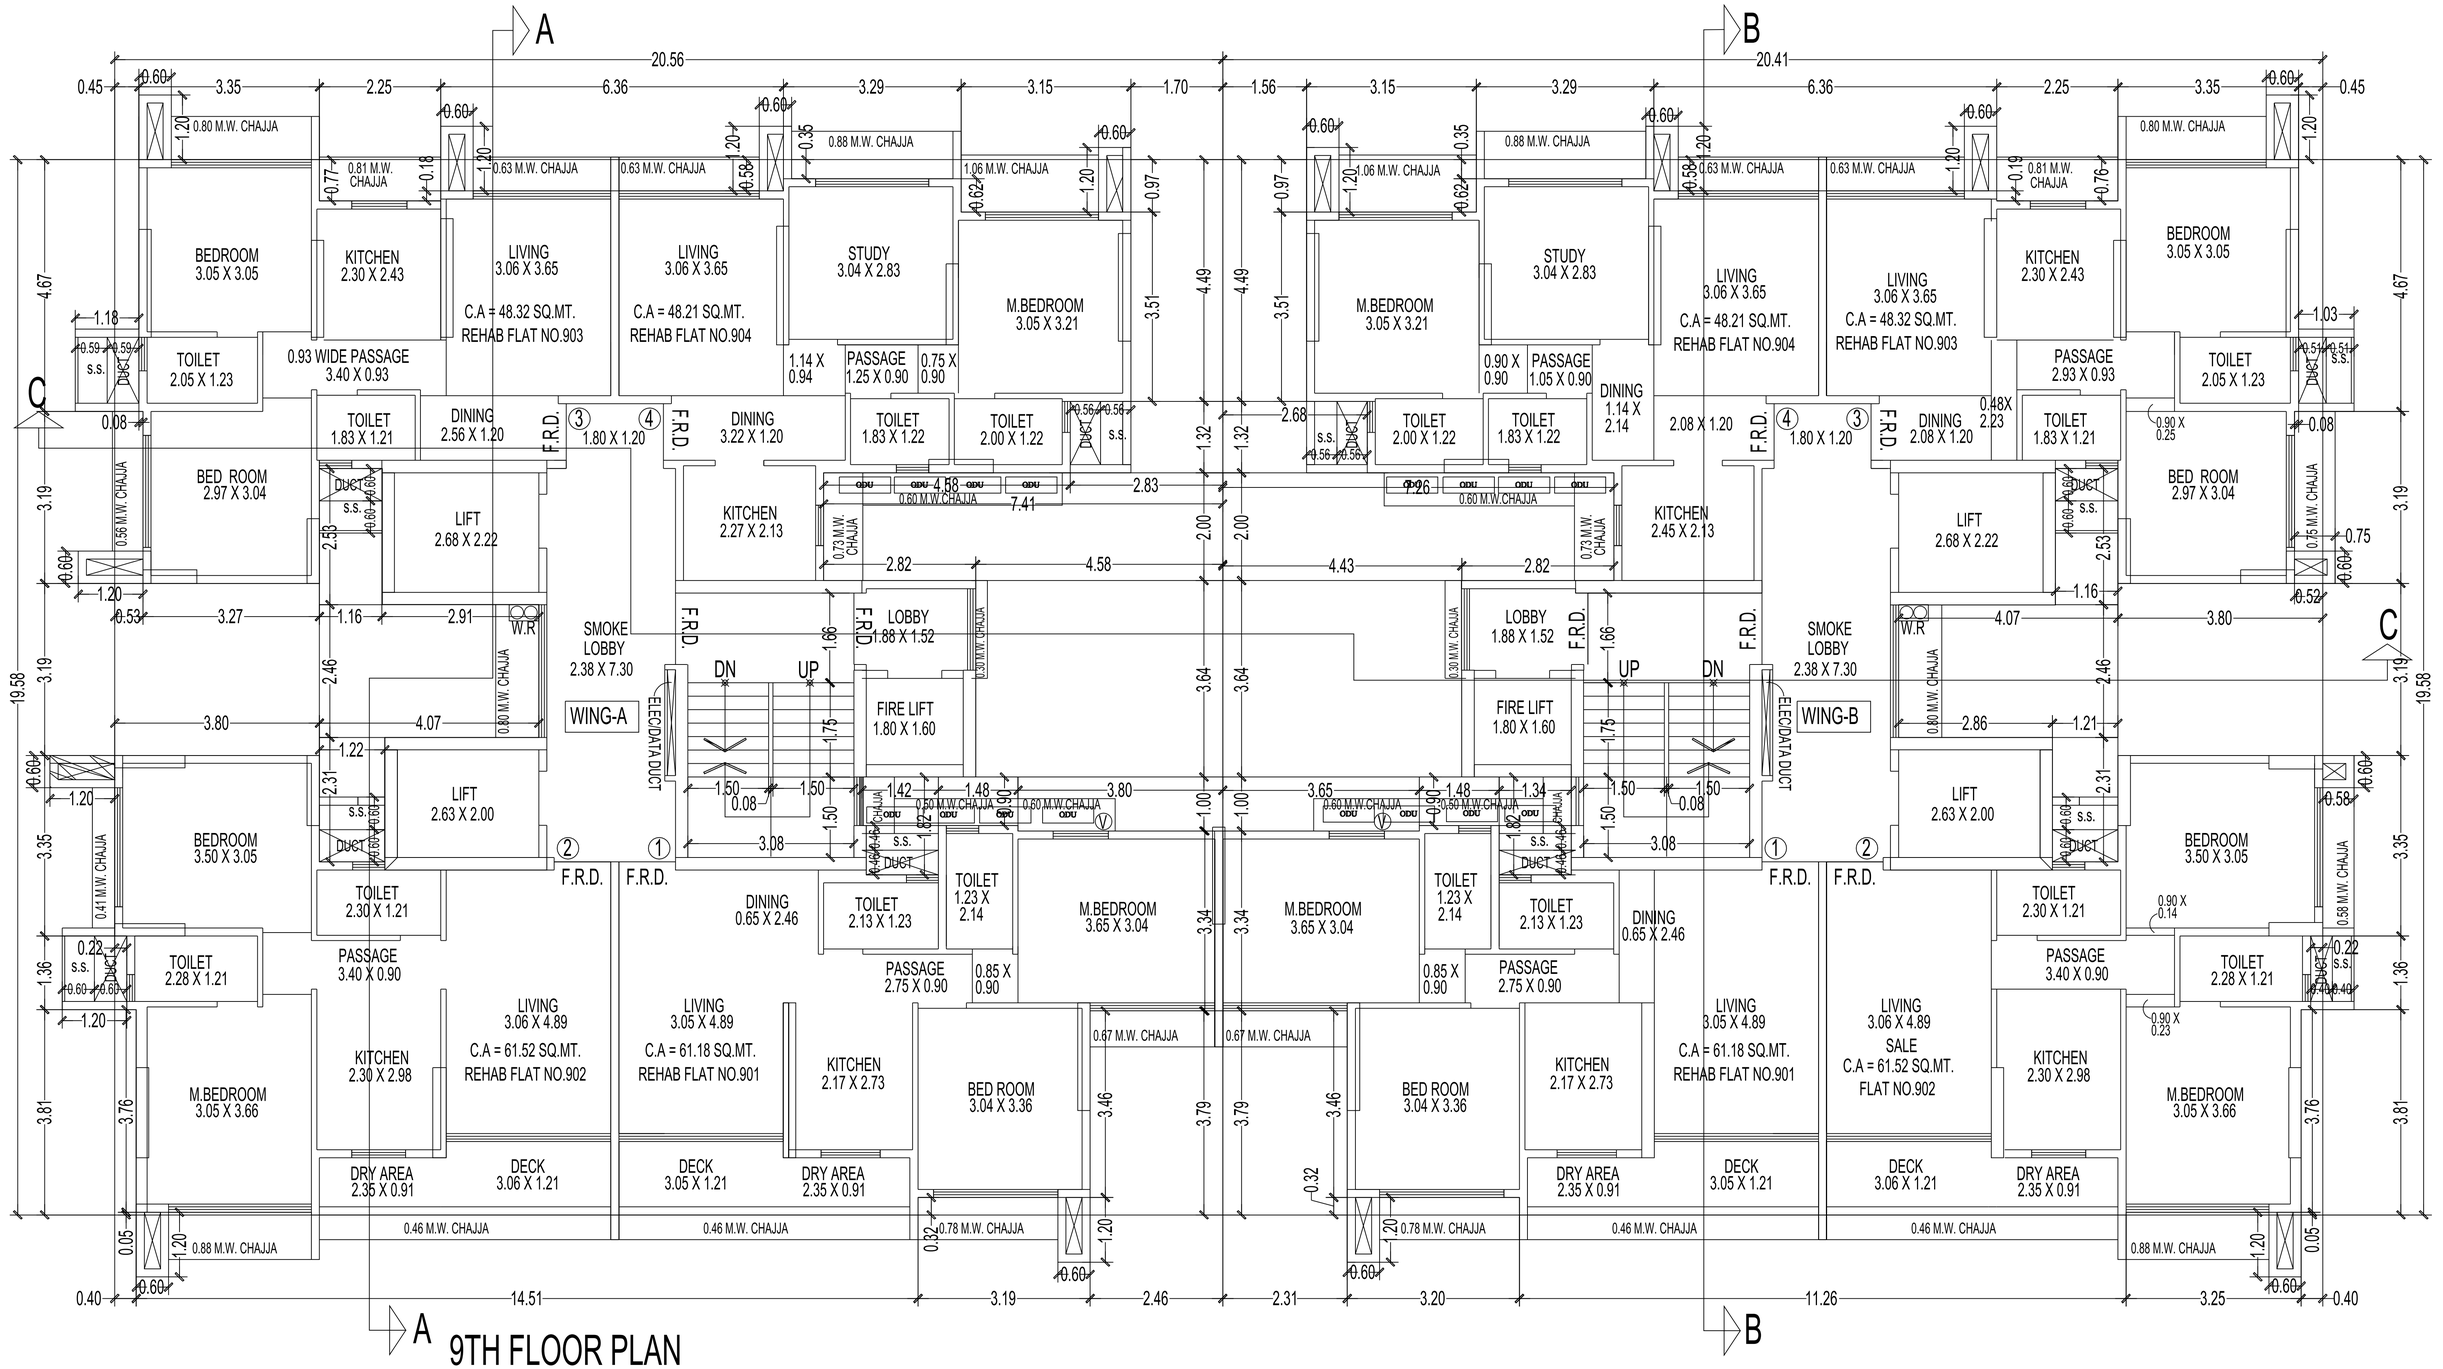

A
B
C
20.56
20.41
BEDROOM 3.05 X 3.05
KITCHEN 2.30 X 2.43
LIVING 3.06 X 3.65
C.A = 48.32 SQ.MT.
REHAB FLAT NO.903
LIVING 3.06 X 3.65
C.A = 48.21 SQ.MT.
REHAB FLAT NO.904
STUDY 3.04 X 2.83
M.BEDROOM 3.05 X 3.21
TOILET 2.05 X 1.23
0.93 WIDE PASSAGE 3.40 X 0.93
TOILET 1.83 X 1.21
DINING 2.56 X 1.20
TOILET 1.83 X 1.22
TOILET 2.00 X 1.22
DINING 3.22 X 1.20
BED ROOM 2.97 X 3.04
LIFT 2.68 X 2.22
KITCHEN 2.27 X 2.13
LOBBY 1.88 X 1.52
SMOKE LOBBY 2.38 X 7.30
FIRE LIFT 1.80 X 1.60
WING-A
WING-B
LIFT 2.63 X 2.00
BEDROOM 3.50 X 3.05
TOILET 2.30 X 1.21
TOILET 2.28 X 1.21
PASSAGE 3.40 X 0.90
LIVING 3.06 X 4.89
C.A = 61.52 SQ.MT.
REHAB FLAT NO.902
LIVING 3.05 X 4.89
C.A = 61.18 SQ.MT.
REHAB FLAT NO.901
KITCHEN 2.30 X 2.98
KITCHEN 2.17 X 2.73
BED ROOM 3.04 X 3.36
M.BEDROOM 3.65 X 3.04
M.BEDROOM 3.05 X 3.66
DRY AREA 2.35 X 0.91
DECK 3.06 X 1.21
DECK 3.05 X 1.21
DRY AREA 2.35 X 0.91
TOILET 2.13 X 1.23
TOILET 1.23 X 2.14
PASSAGE 2.75 X 0.90
0.85 X 0.90
DINING 0.65 X 2.46
KITCHEN 2.45 X 2.13
LIVING 3.06 X 4.89
SALE
C.A = 61.52 SQ.MT.
FLAT NO.902
PASSAGE 2.93 X 0.93
DINING 2.08 X 1.20
DINING 1.14 X 2.14
PASSAGE 1.25 X 0.90
PASSAGE 1.05 X 0.90
0.75 X 0.90
1.14 X 0.94
0.90 X 0.90
0.48X 2.23
0.90 X 0.25
0.90 X 0.14
0.90 X 0.23
F.R.D.
DUCT
s.s.
ODU
0.80 M.W. CHAJJA
0.81 M.W. CHAJJA
0.63 M.W. CHAJJA
0.88 M.W. CHAJJA
1.06 M.W. CHAJJA
0.60 M.W.CHAJJA
0.73 M.W. CHAJJA
0.56 M.W. CHAJJA
0.30 M.W. CHAJJA
0.41 M.W. CHAJJA
0.58 M.W. CHAJJA
0.75 M.W. CHAJJA
0.67 M.W. CHAJJA
0.46 M.W. CHAJJA
0.78 M.W. CHAJJA
W.R
UP
DN
ELEC/DATA DUCT
14.51
3.19
2.46
2.31
3.20
11.26
3.25
0.40
9TH FLOOR PLAN
SCALE - 1:100

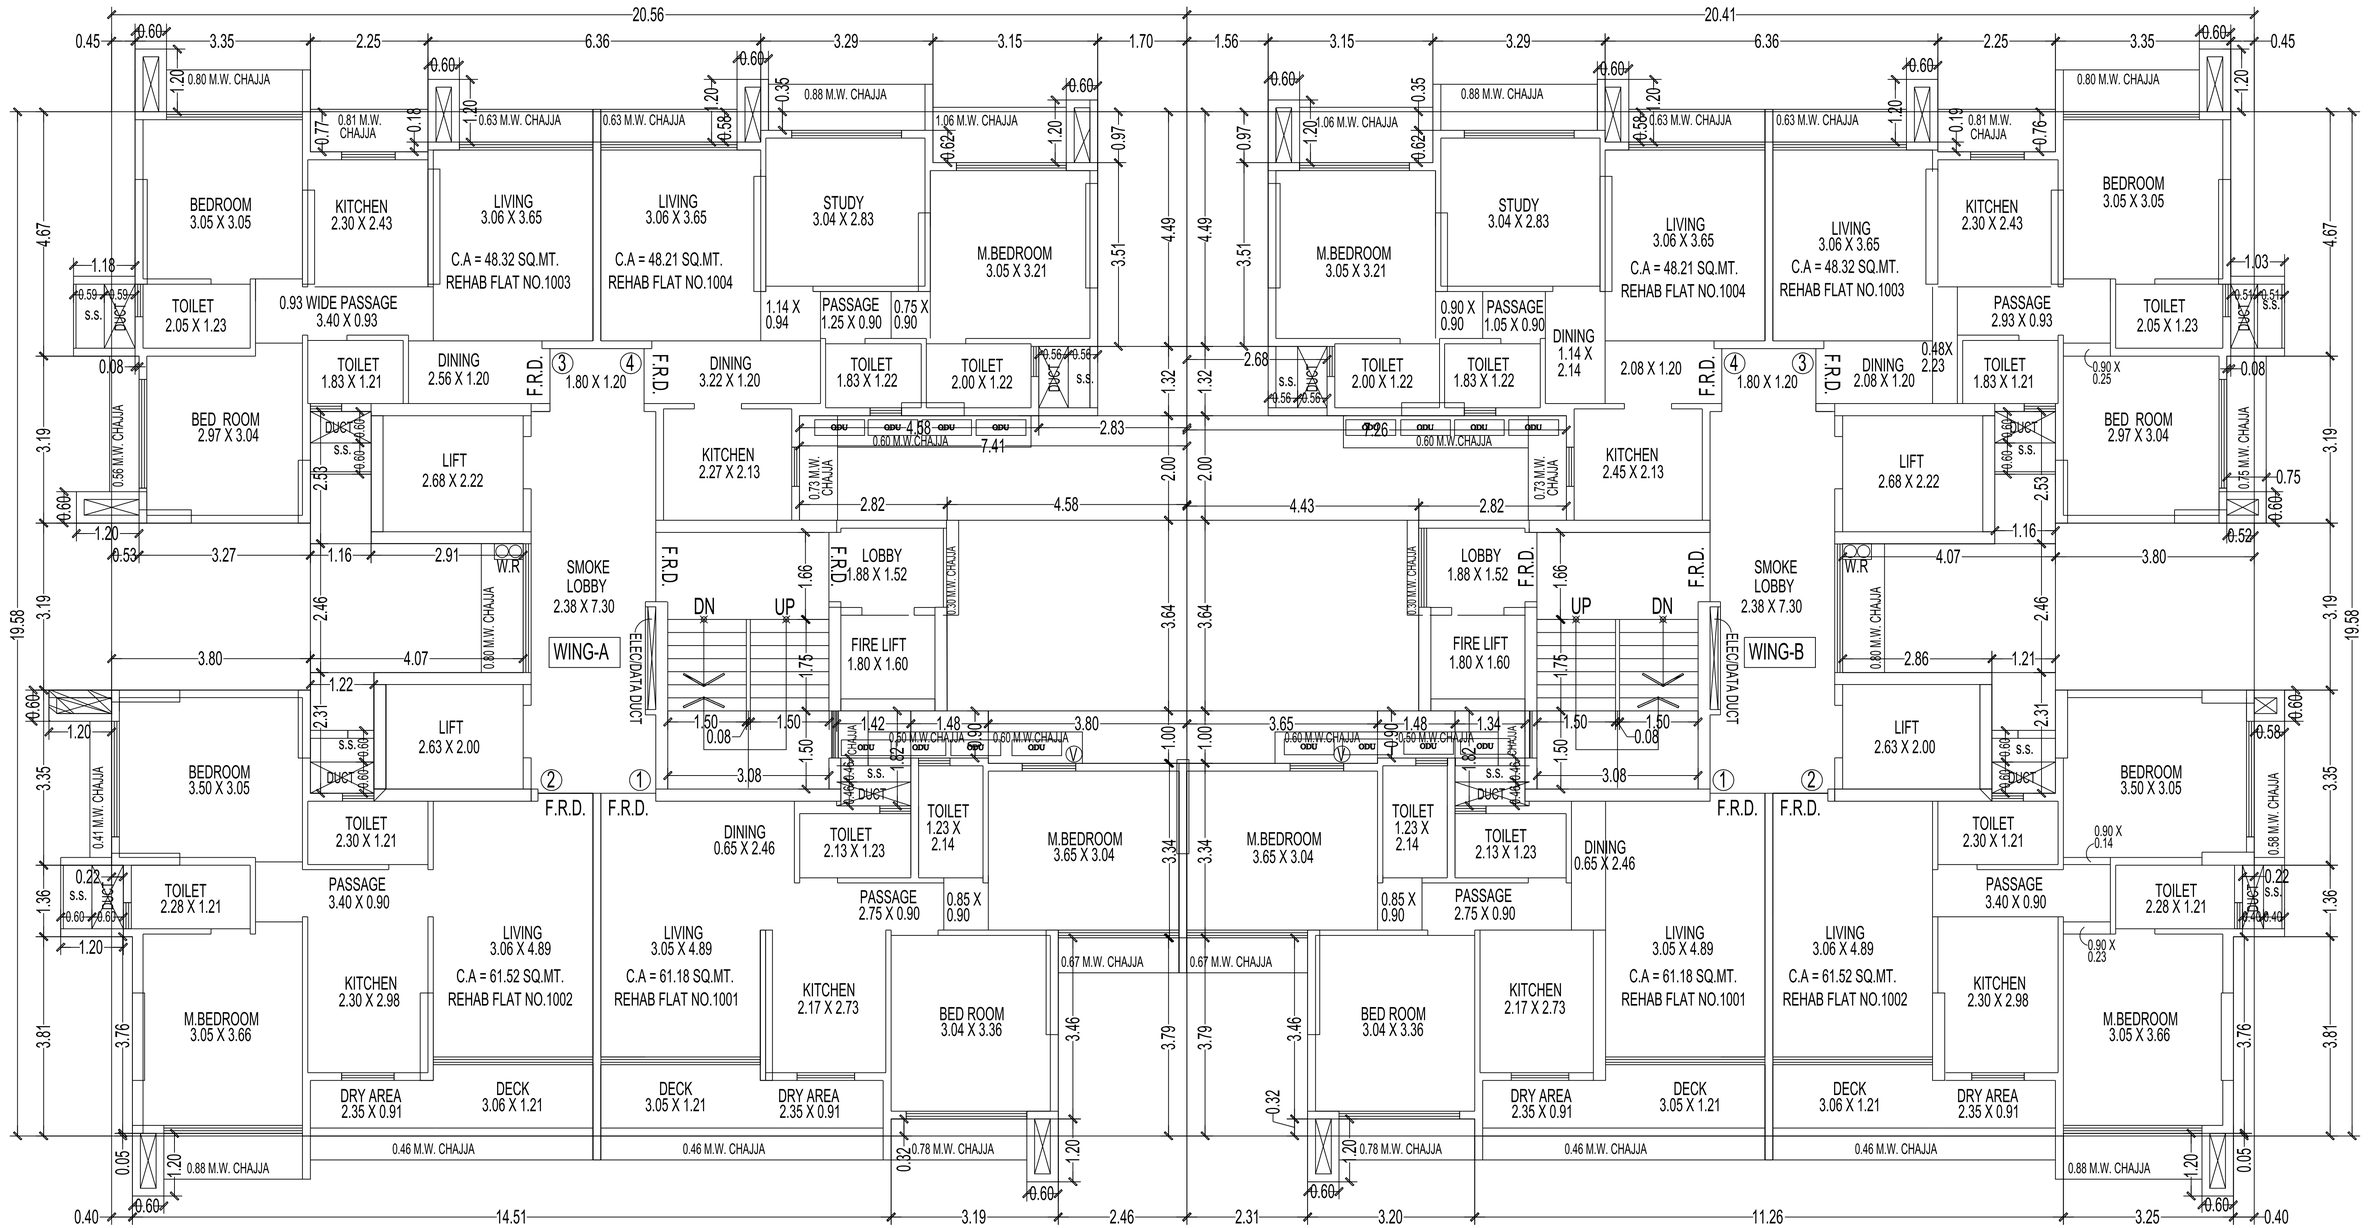


10TH FLOOR PLAN
SCALE - 1:100

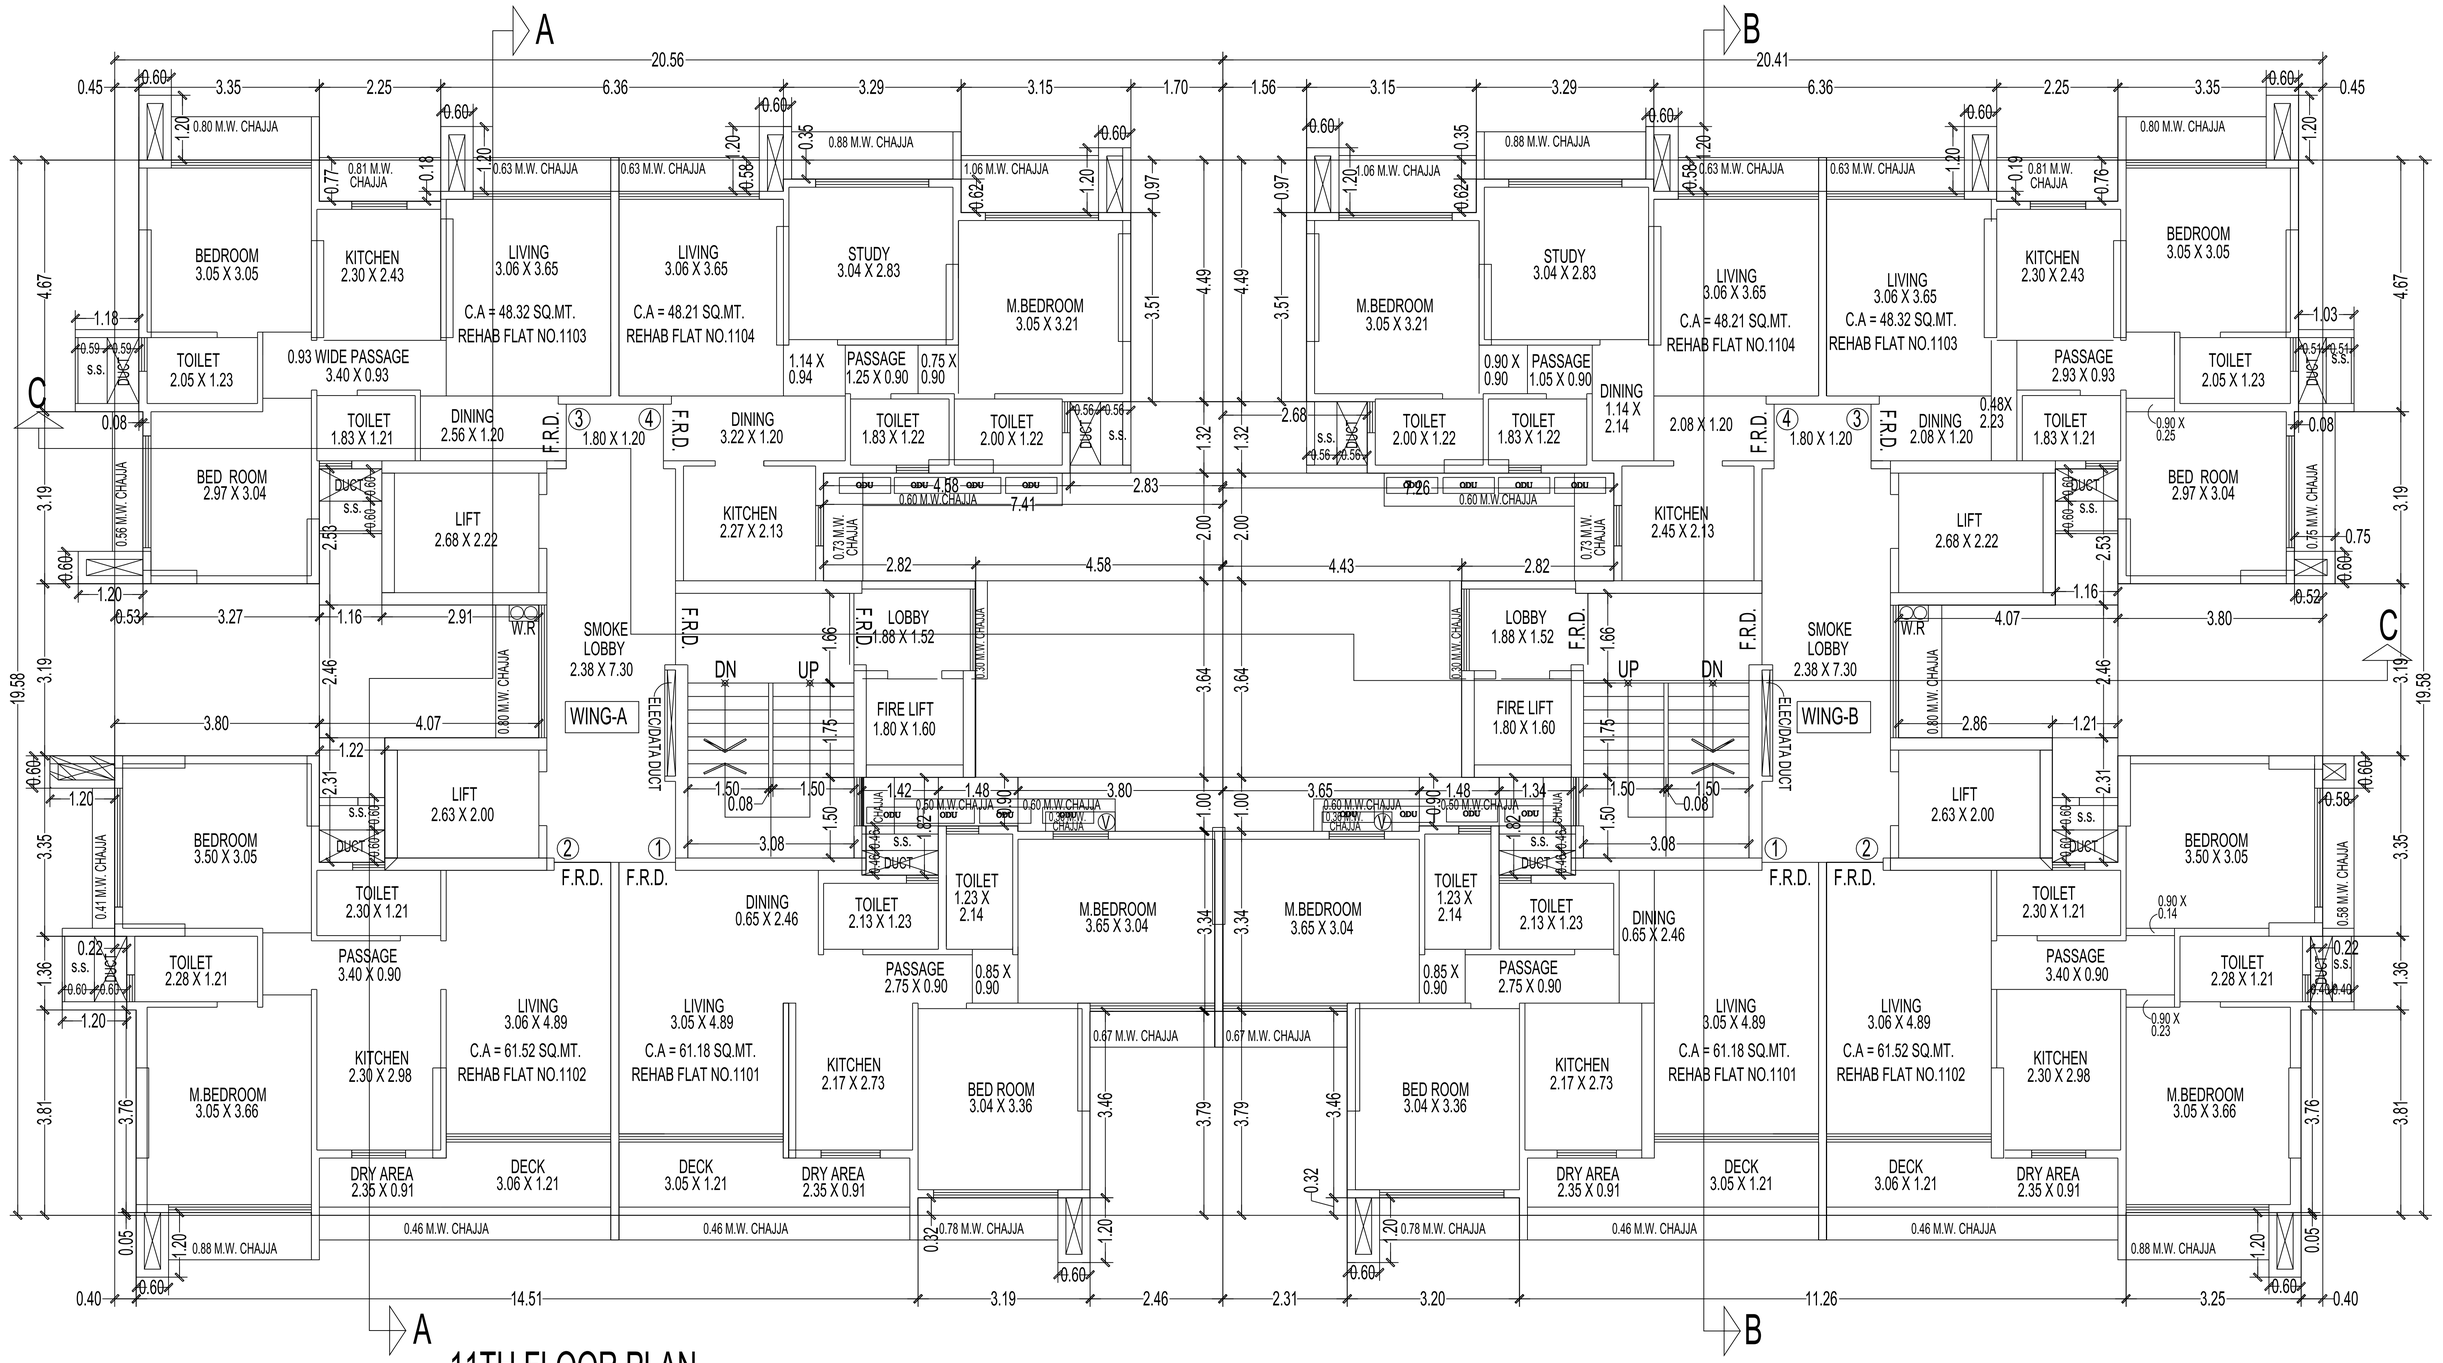


11TH FLOOR PLAN
SCALE - 1:100

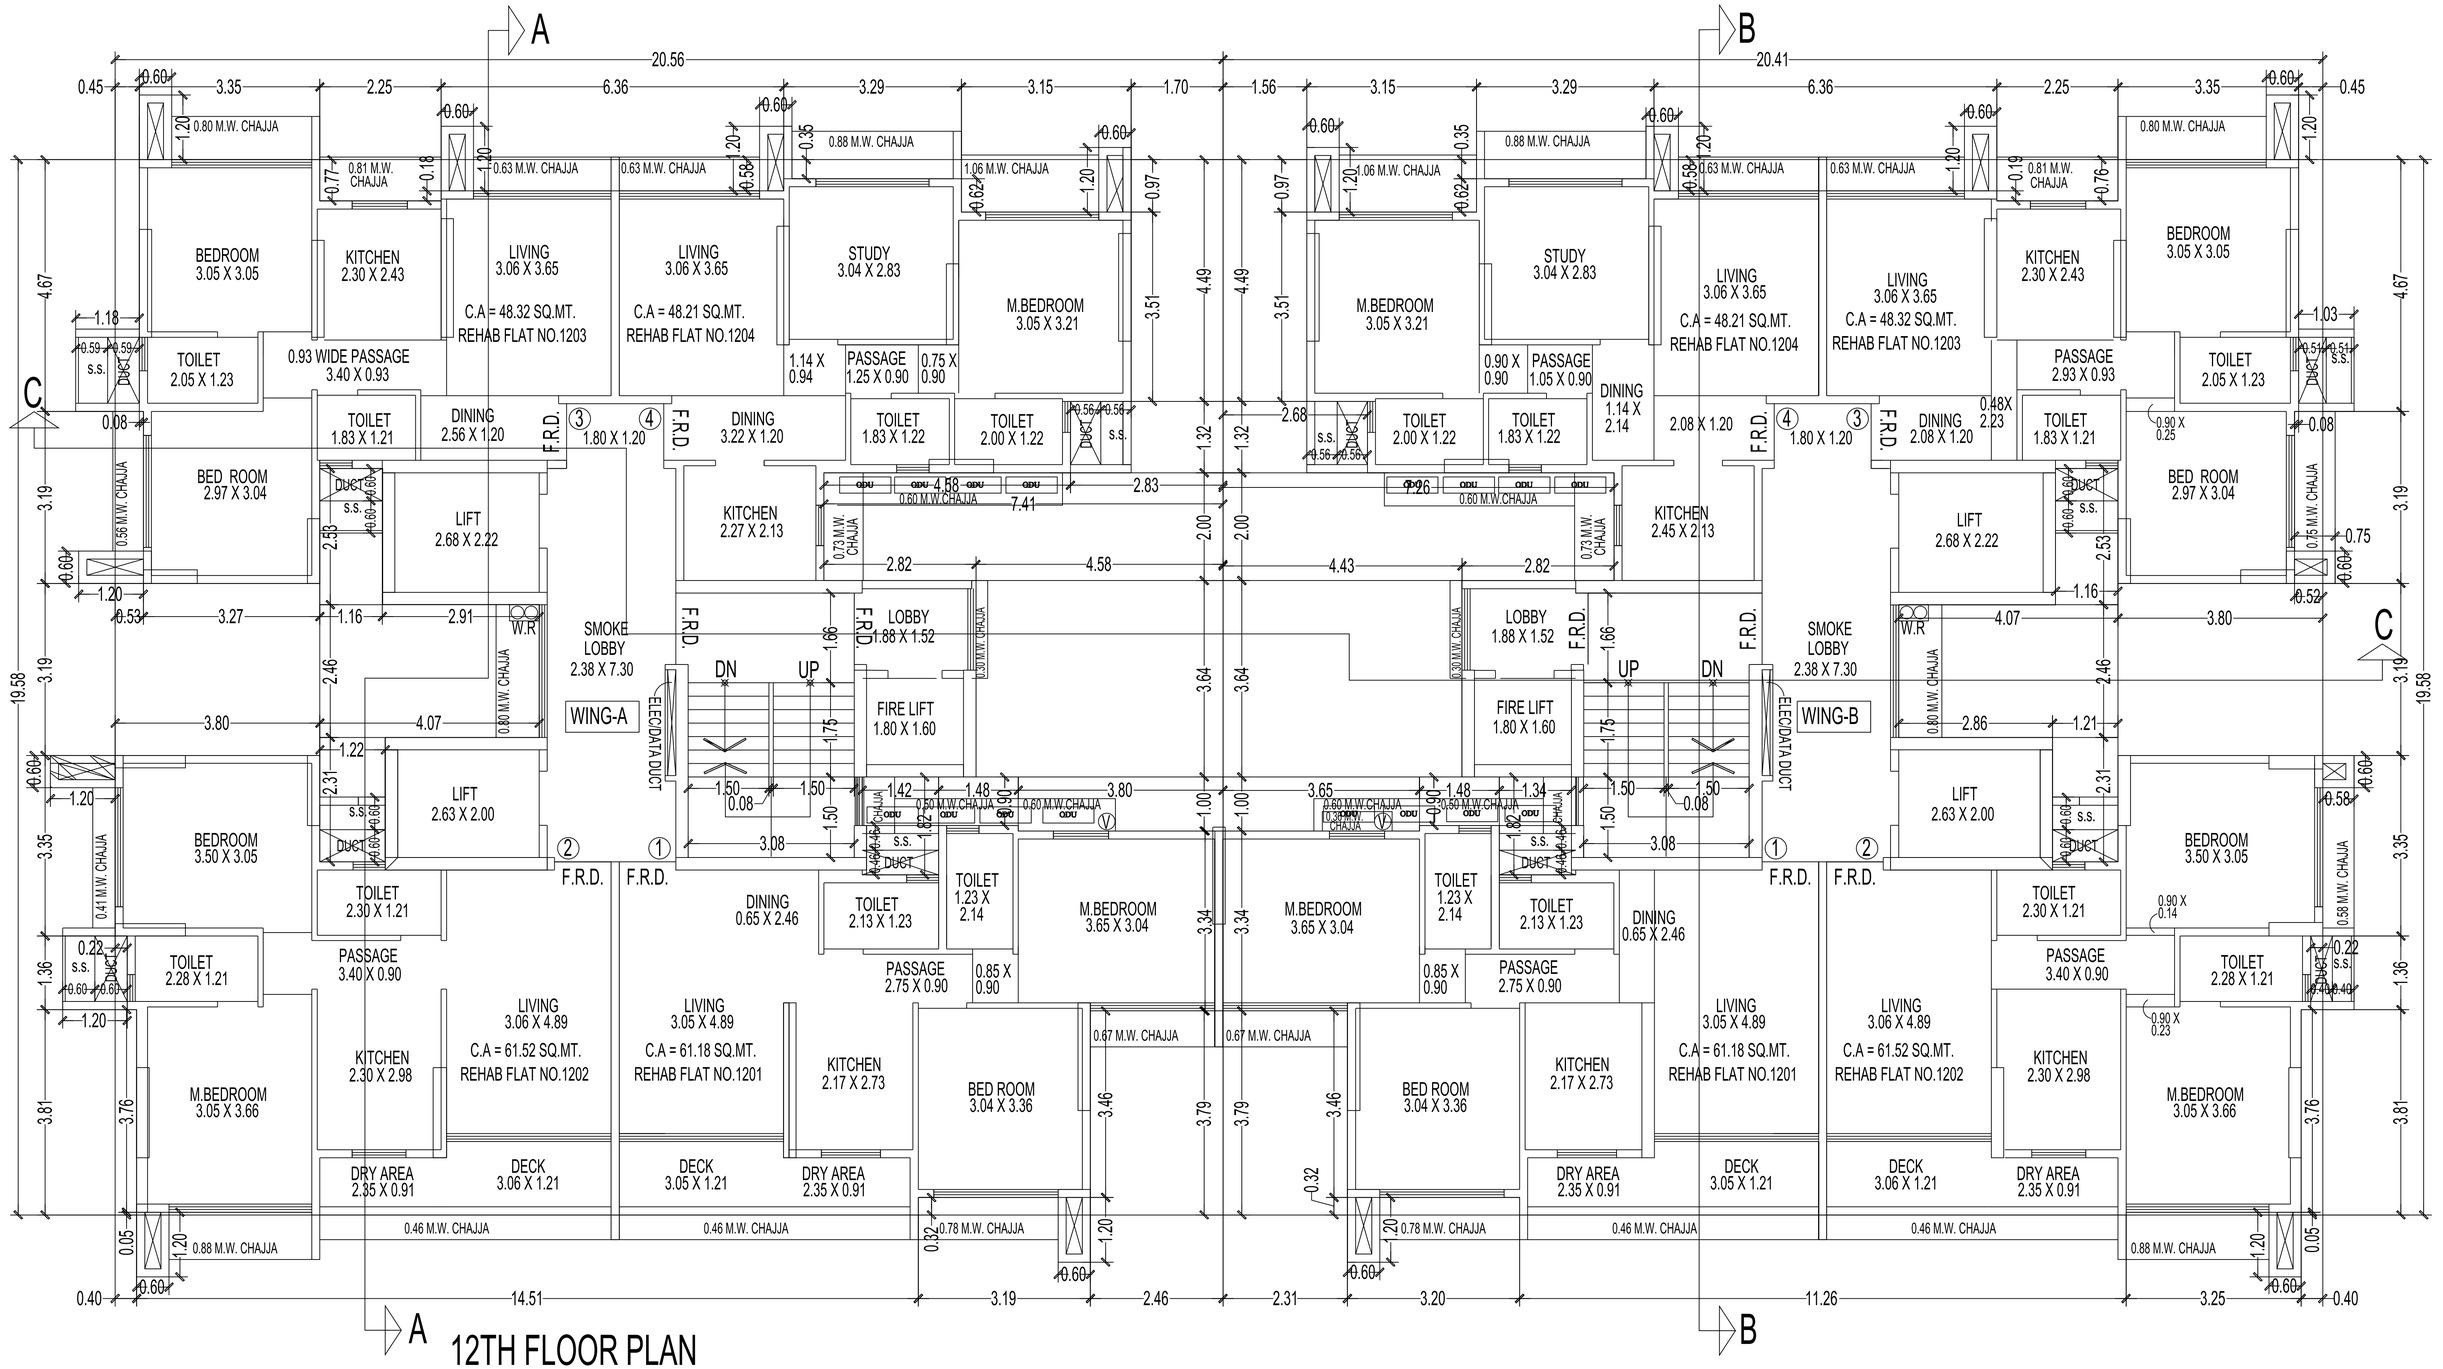

12TH FLOOR PLAN
SCALE - 1:100

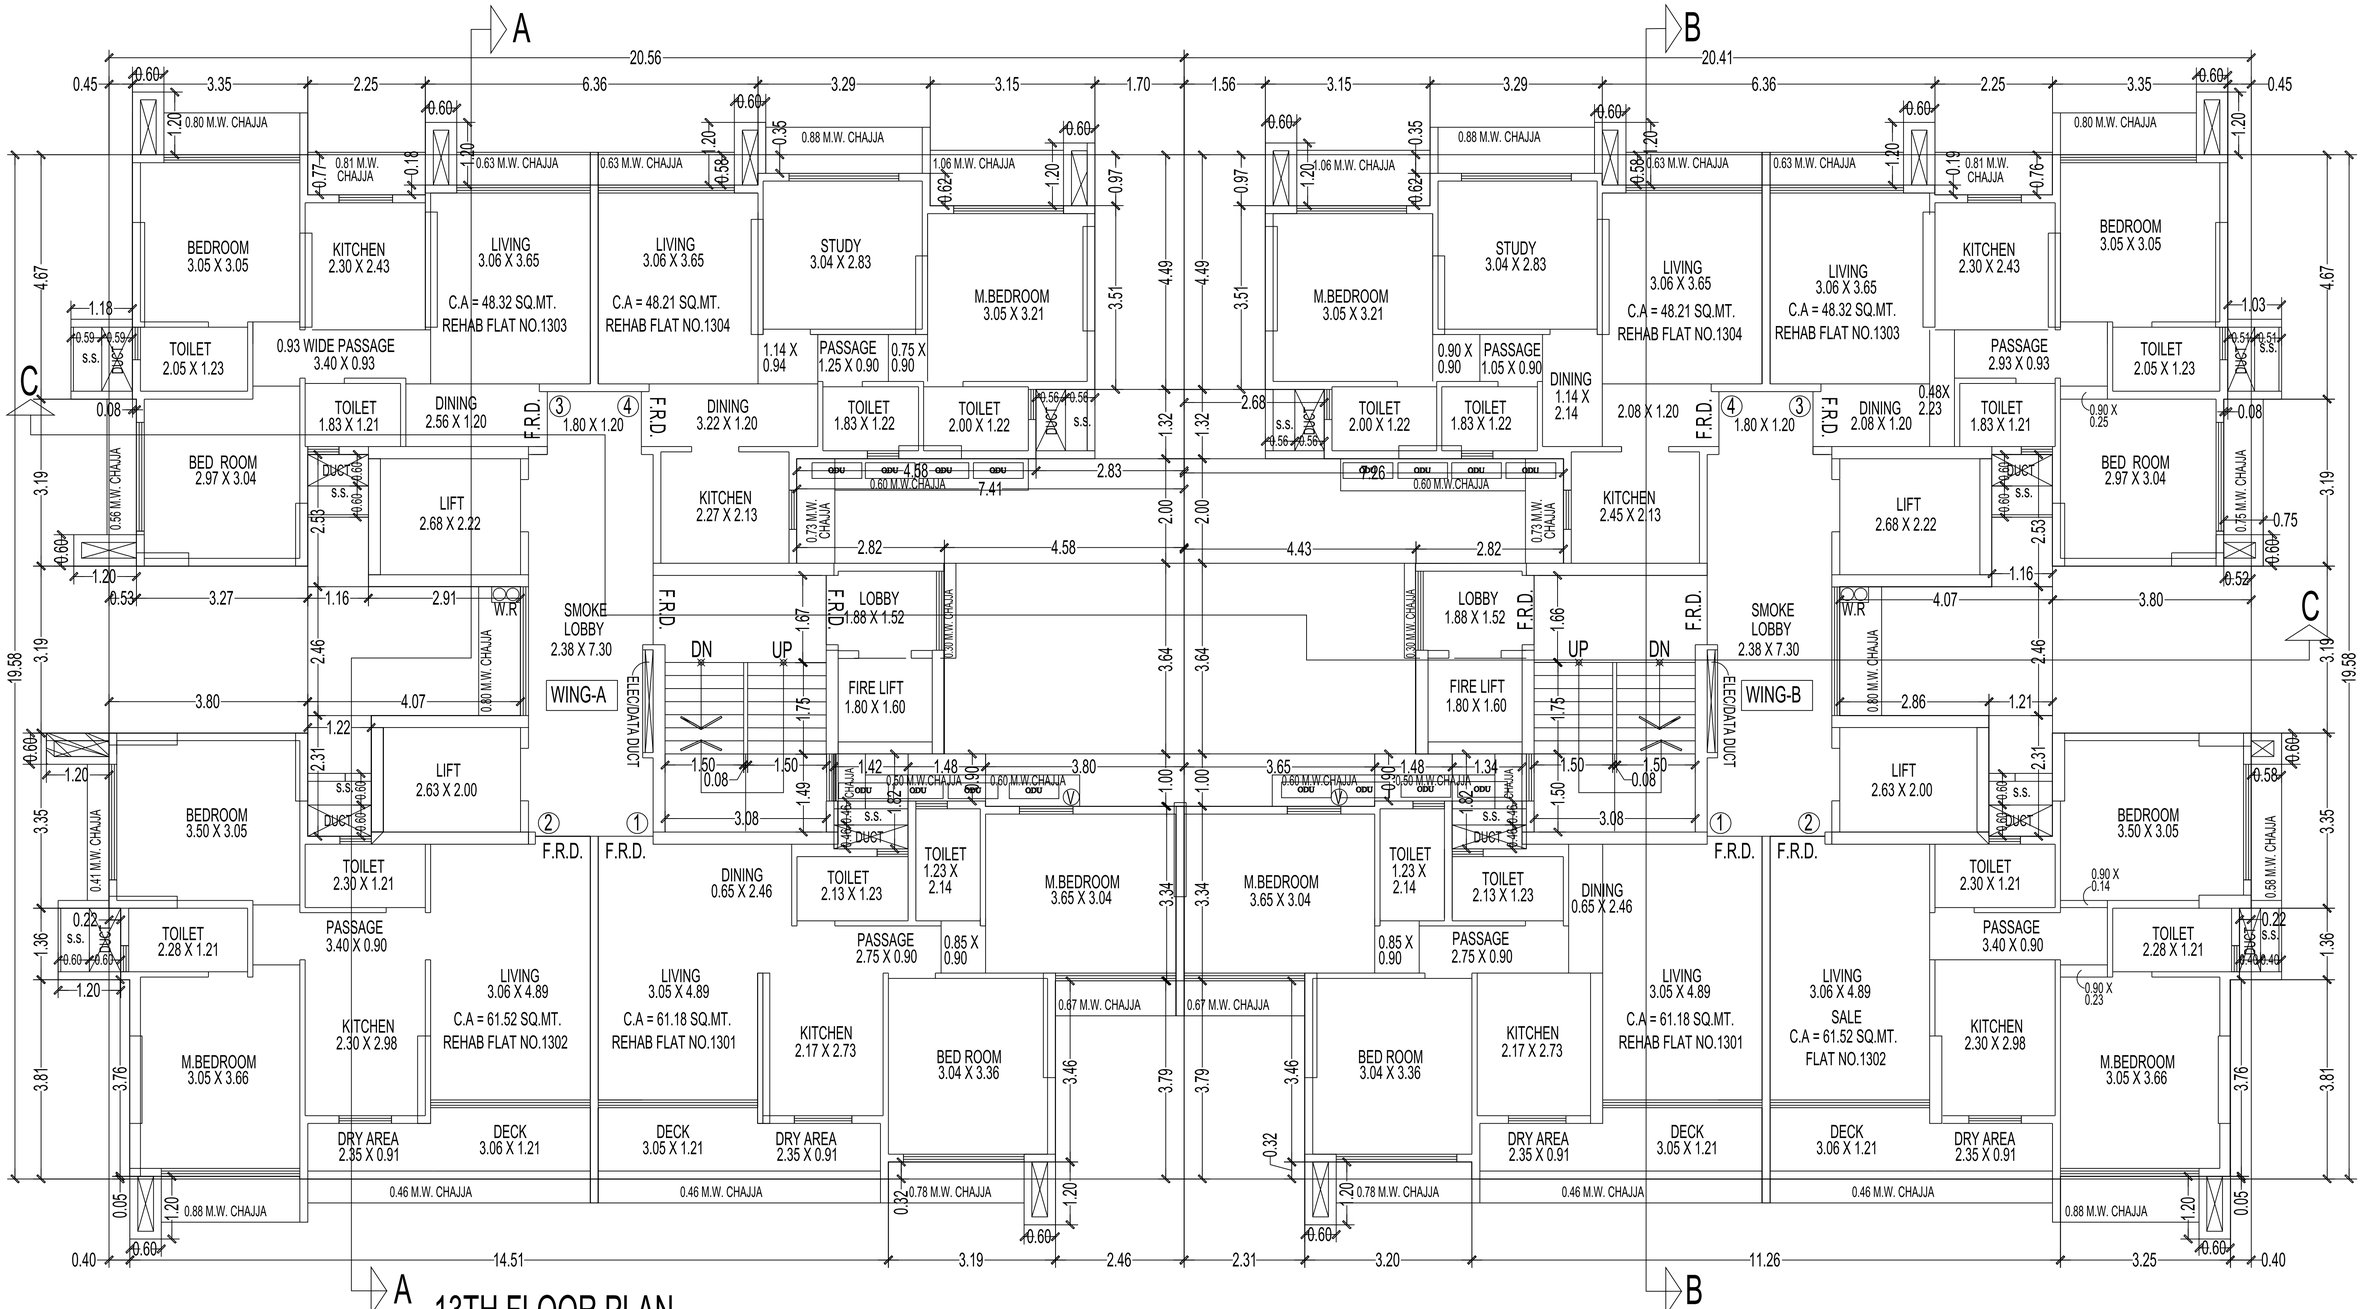

A
B
C
C
20.56
20.41
WING-A
WING-B
ELEC/DATA DUCT
SMOKE LOBBY 2.38 X 7.30
FIRE LIFT 1.80 X 1.60
LOBBY 1.88 X 1.52
UP
DN
F.R.D.
W.R
BEDROOM 3.05 X 3.05
KITCHEN 2.30 X 2.43
LIVING 3.06 X 3.65
C.A = 48.32 SQ.MT. REHAB FLAT NO.1303
LIVING 3.06 X 3.65
C.A = 48.21 SQ.MT. REHAB FLAT NO.1304
STUDY 3.04 X 2.83
M.BEDROOM 3.05 X 3.21
TOILET 2.05 X 1.23
0.93 WIDE PASSAGE 3.40 X 0.93
TOILET 1.83 X 1.21
DINING 2.56 X 1.20
DINING 3.22 X 1.20
TOILET 1.83 X 1.22
TOILET 2.00 X 1.22
1.14 X 0.94
PASSAGE 1.25 X 0.90
0.75 X 0.90
BED ROOM 2.97 X 3.04
LIFT 2.68 X 2.22
KITCHEN 2.27 X 2.13
BEDROOM 3.50 X 3.05
TOILET 2.30 X 1.21
TOILET 2.28 X 1.21
PASSAGE 3.40 X 0.90
M.BEDROOM 3.05 X 3.66
KITCHEN 2.30 X 2.98
LIVING 3.06 X 4.89
C.A = 61.52 SQ.MT. REHAB FLAT NO.1302
LIVING 3.05 X 4.89
C.A = 61.18 SQ.MT. REHAB FLAT NO.1301
KITCHEN 2.17 X 2.73
BED ROOM 3.04 X 3.36
DRY AREA 2.35 X 0.91
DECK 3.06 X 1.21
DECK 3.05 X 1.21
DRY AREA 2.35 X 0.91
FIRE LIFT 1.80 X 1.60
LOBBY 1.88 X 1.52
M.BEDROOM 3.65 X 3.04
TOILET 1.23 X 2.14
TOILET 2.13 X 1.23
PASSAGE 2.75 X 0.90
0.85 X 0.90
DINING 0.65 X 2.46
LIVING 3.06 X 3.65
C.A = 48.21 SQ.MT. REHAB FLAT NO.1304
LIVING 3.06 X 3.65
C.A = 48.32 SQ.MT. REHAB FLAT NO.1303
STUDY 3.04 X 2.83
M.BEDROOM 3.05 X 3.21
TOILET 2.00 X 1.22
TOILET 1.83 X 1.22
DINING 1.14 X 2.14
0.90 X 0.90
PASSAGE 1.05 X 0.90
KITCHEN 2.45 X 2.13
LIFT 2.68 X 2.22
DINING 2.08 X 1.20
TOILET 1.83 X 1.21
BEDROOM 3.05 X 3.05
KITCHEN 2.30 X 2.43
PASSAGE 2.93 X 0.93
TOILET 2.05 X 1.23
BED ROOM 2.97 X 3.04
LIFT 2.63 X 2.00
BEDROOM 3.50 X 3.05
TOILET 2.30 X 1.21
PASSAGE 3.40 X 0.90
TOILET 2.28 X 1.21
KITCHEN 2.30 X 2.98
LIVING 3.06 X 4.89
SALE
C.A = 61.52 SQ.MT.
FLAT NO.1302
M.BEDROOM 3.05 X 3.66
DRY AREA 2.35 X 0.91
DECK 3.06 X 1.21
0.80 M.W. CHAJJA
0.63 M.W. CHAJJA
0.88 M.W. CHAJJA
1.06 M.W. CHAJJA
0.81 M.W. CHAJJA
0.60 M.W.CHAJJA
0.73 M.W. CHAJJA
0.56 M.W. CHAJJA
0.75 M.W. CHAJJA
0.41 M.W. CHAJJA
0.58 M.W. CHAJJA
0.46 M.W. CHAJJA
0.78 M.W. CHAJJA
0.67 M.W. CHAJJA
0.50 M.W.CHAJJA
F.R.D.
DUCT
S.S.
ODU
13TH FLOOR PLAN
SCALE - 1:100

SCALE - 1:100

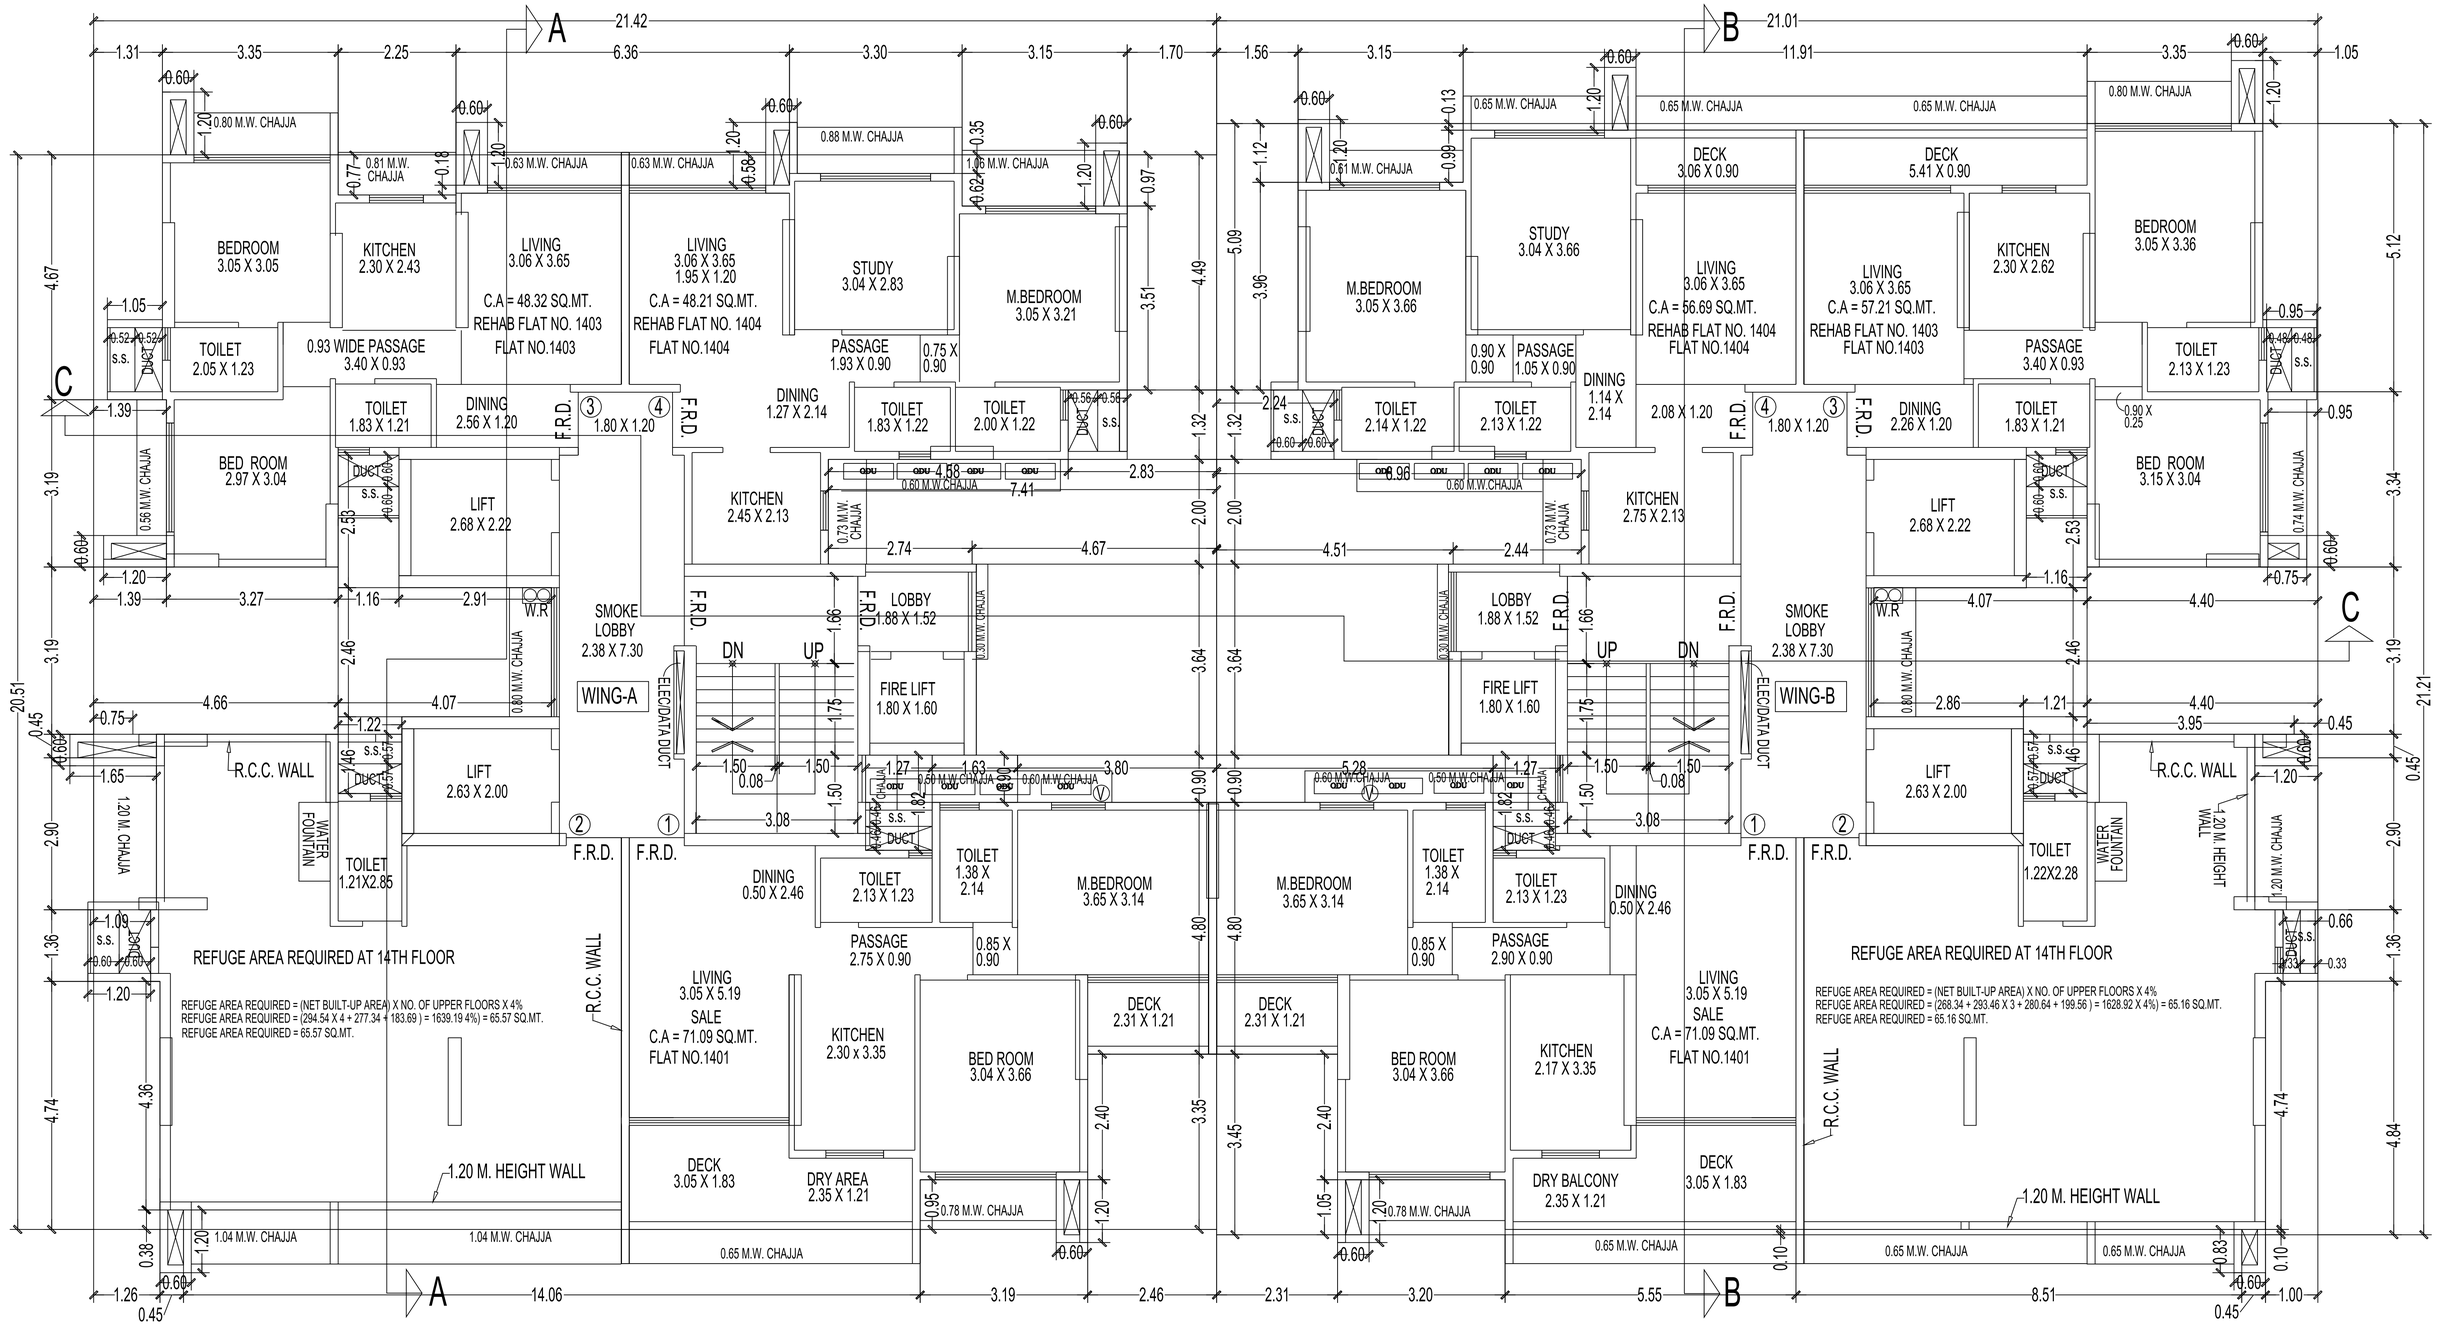


14TH FLOOR PLAN

SCALE - 1:100

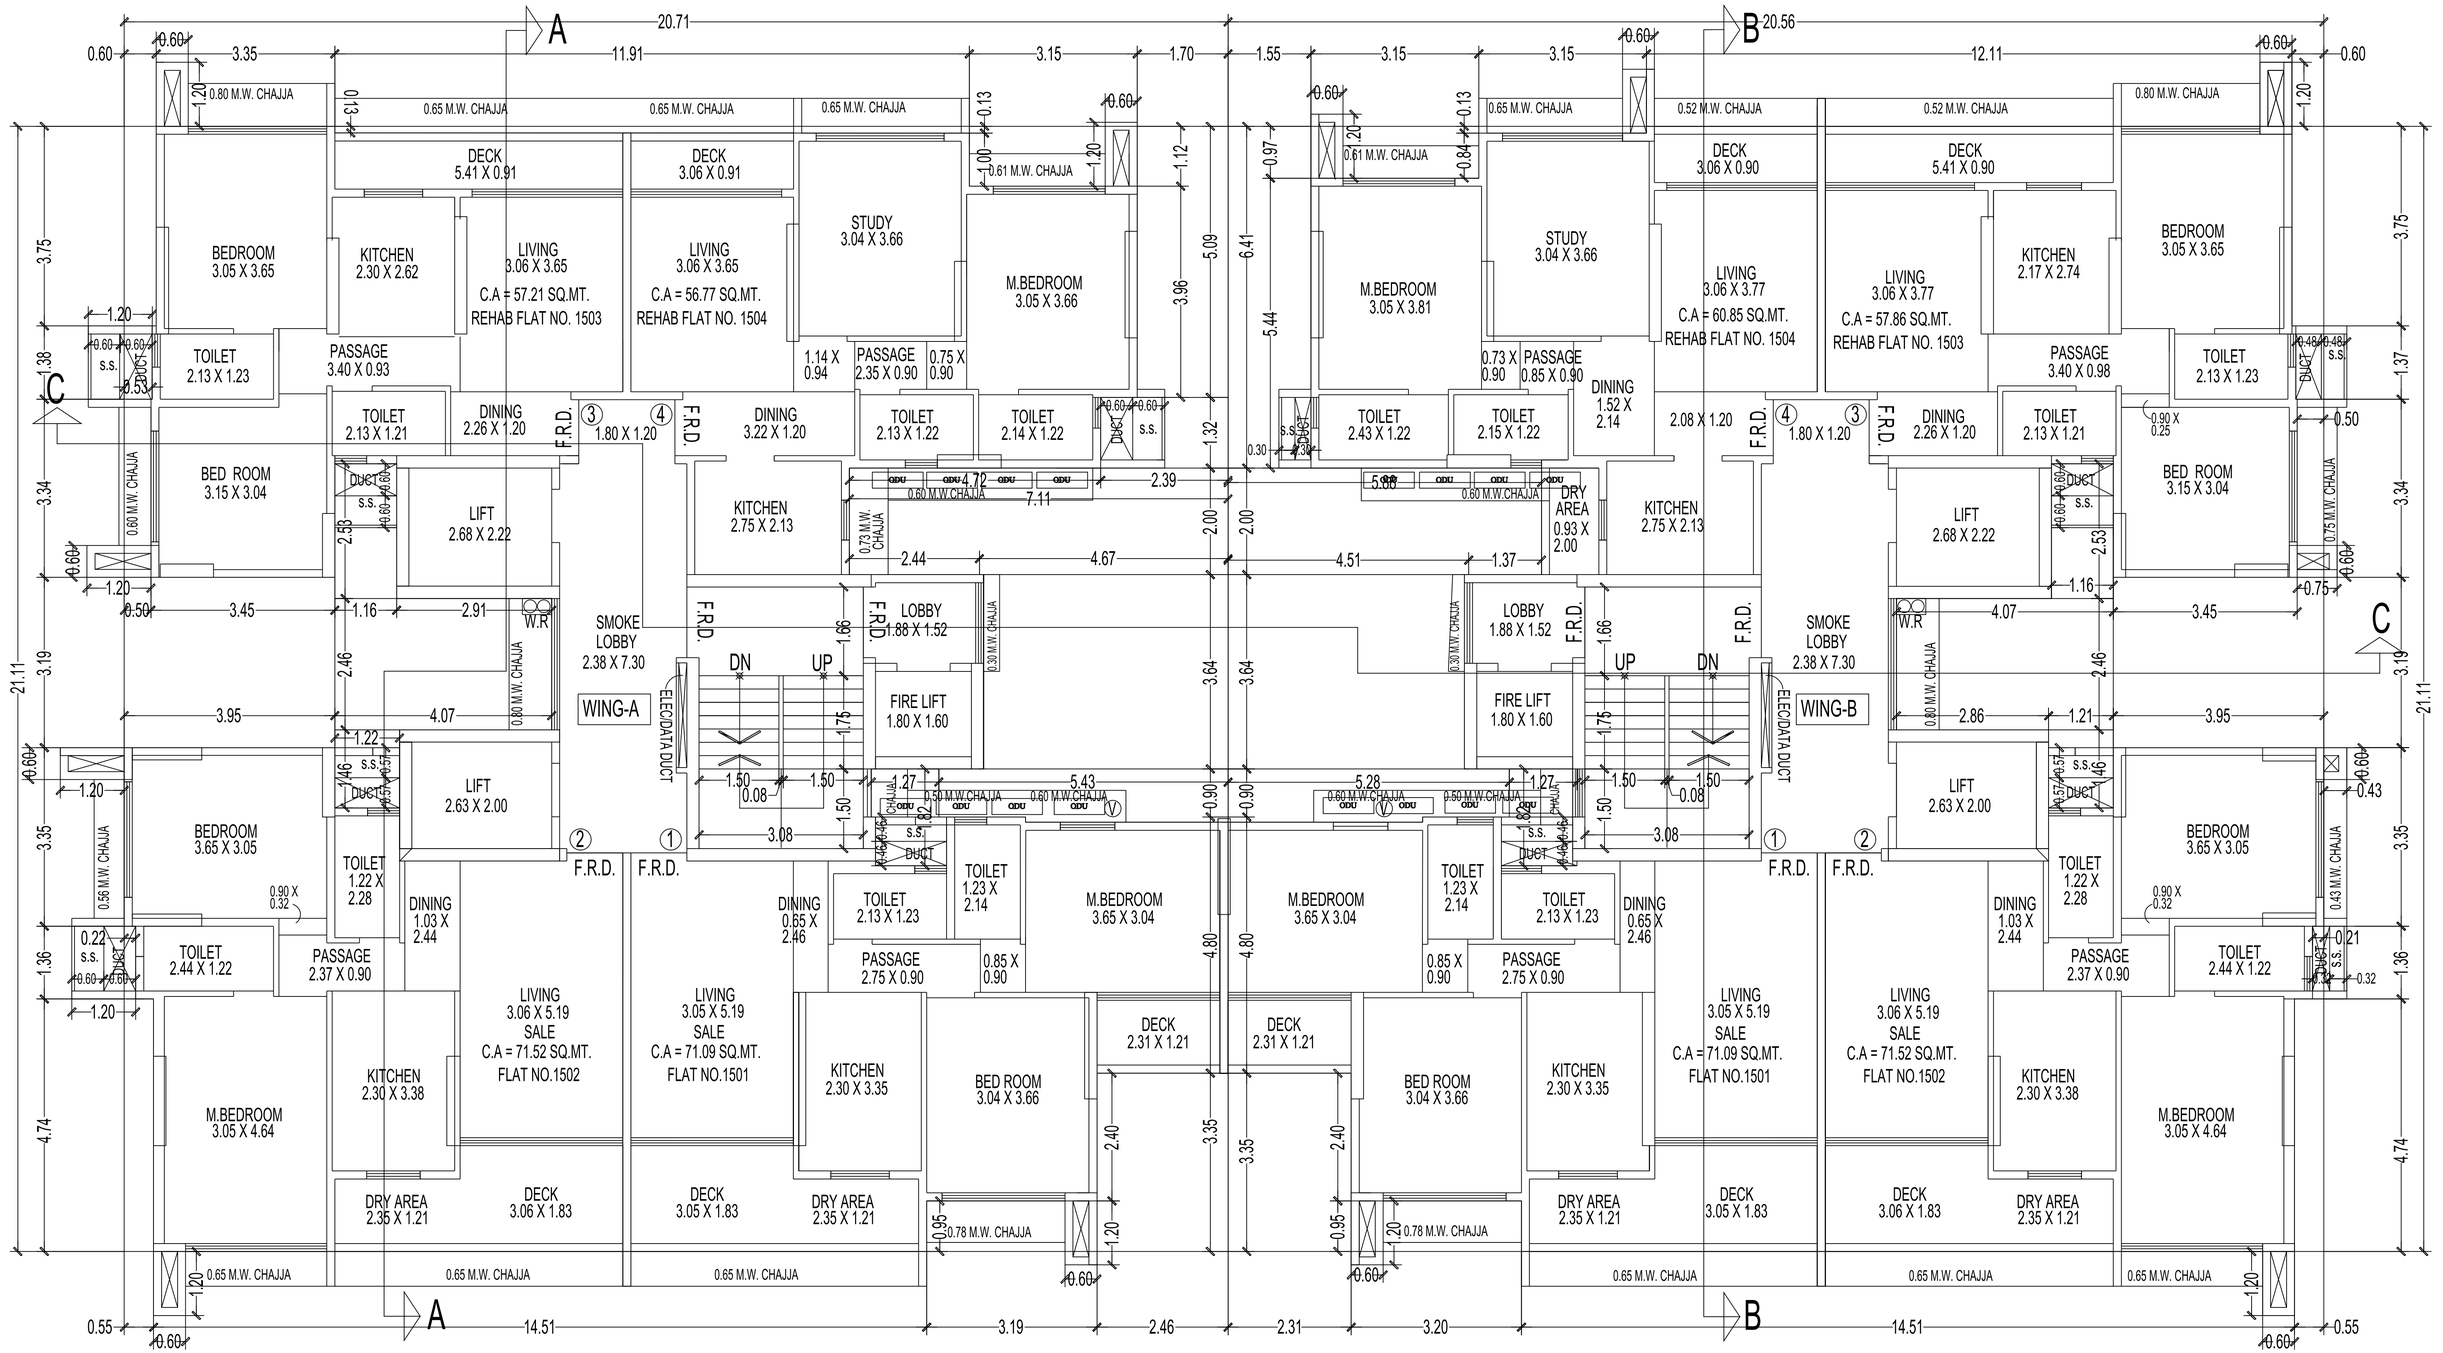


15TH FLOOR PLAN

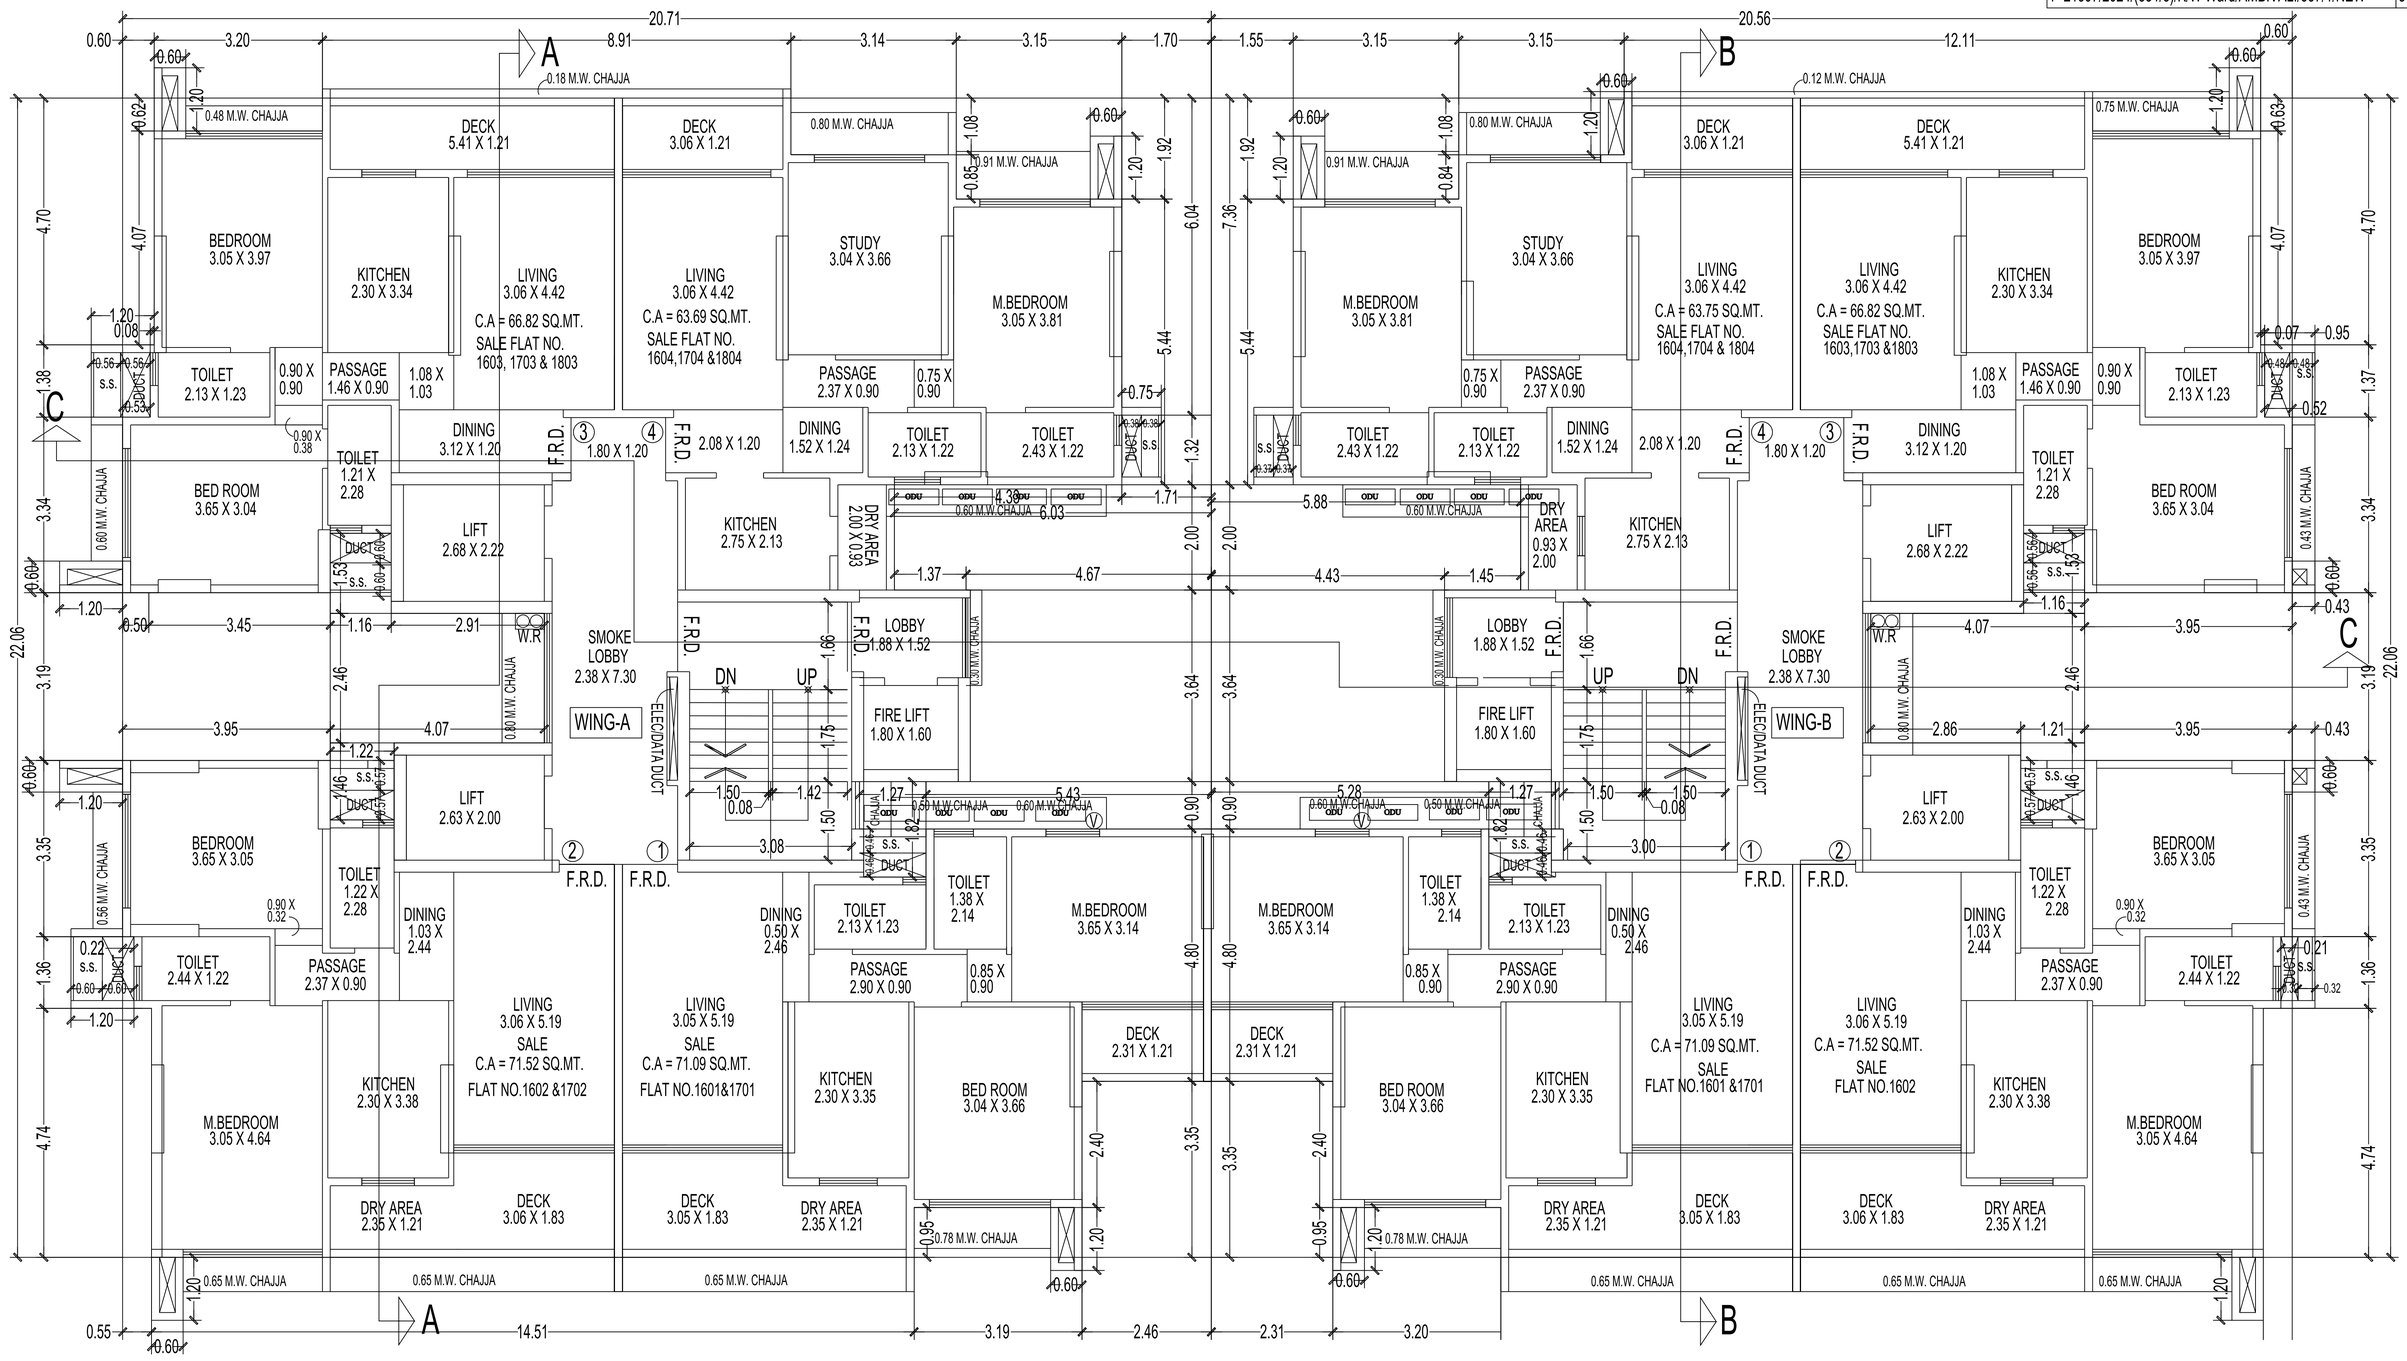

16TH TO 18TH FLOOR PLAN

SCALE - 1:100

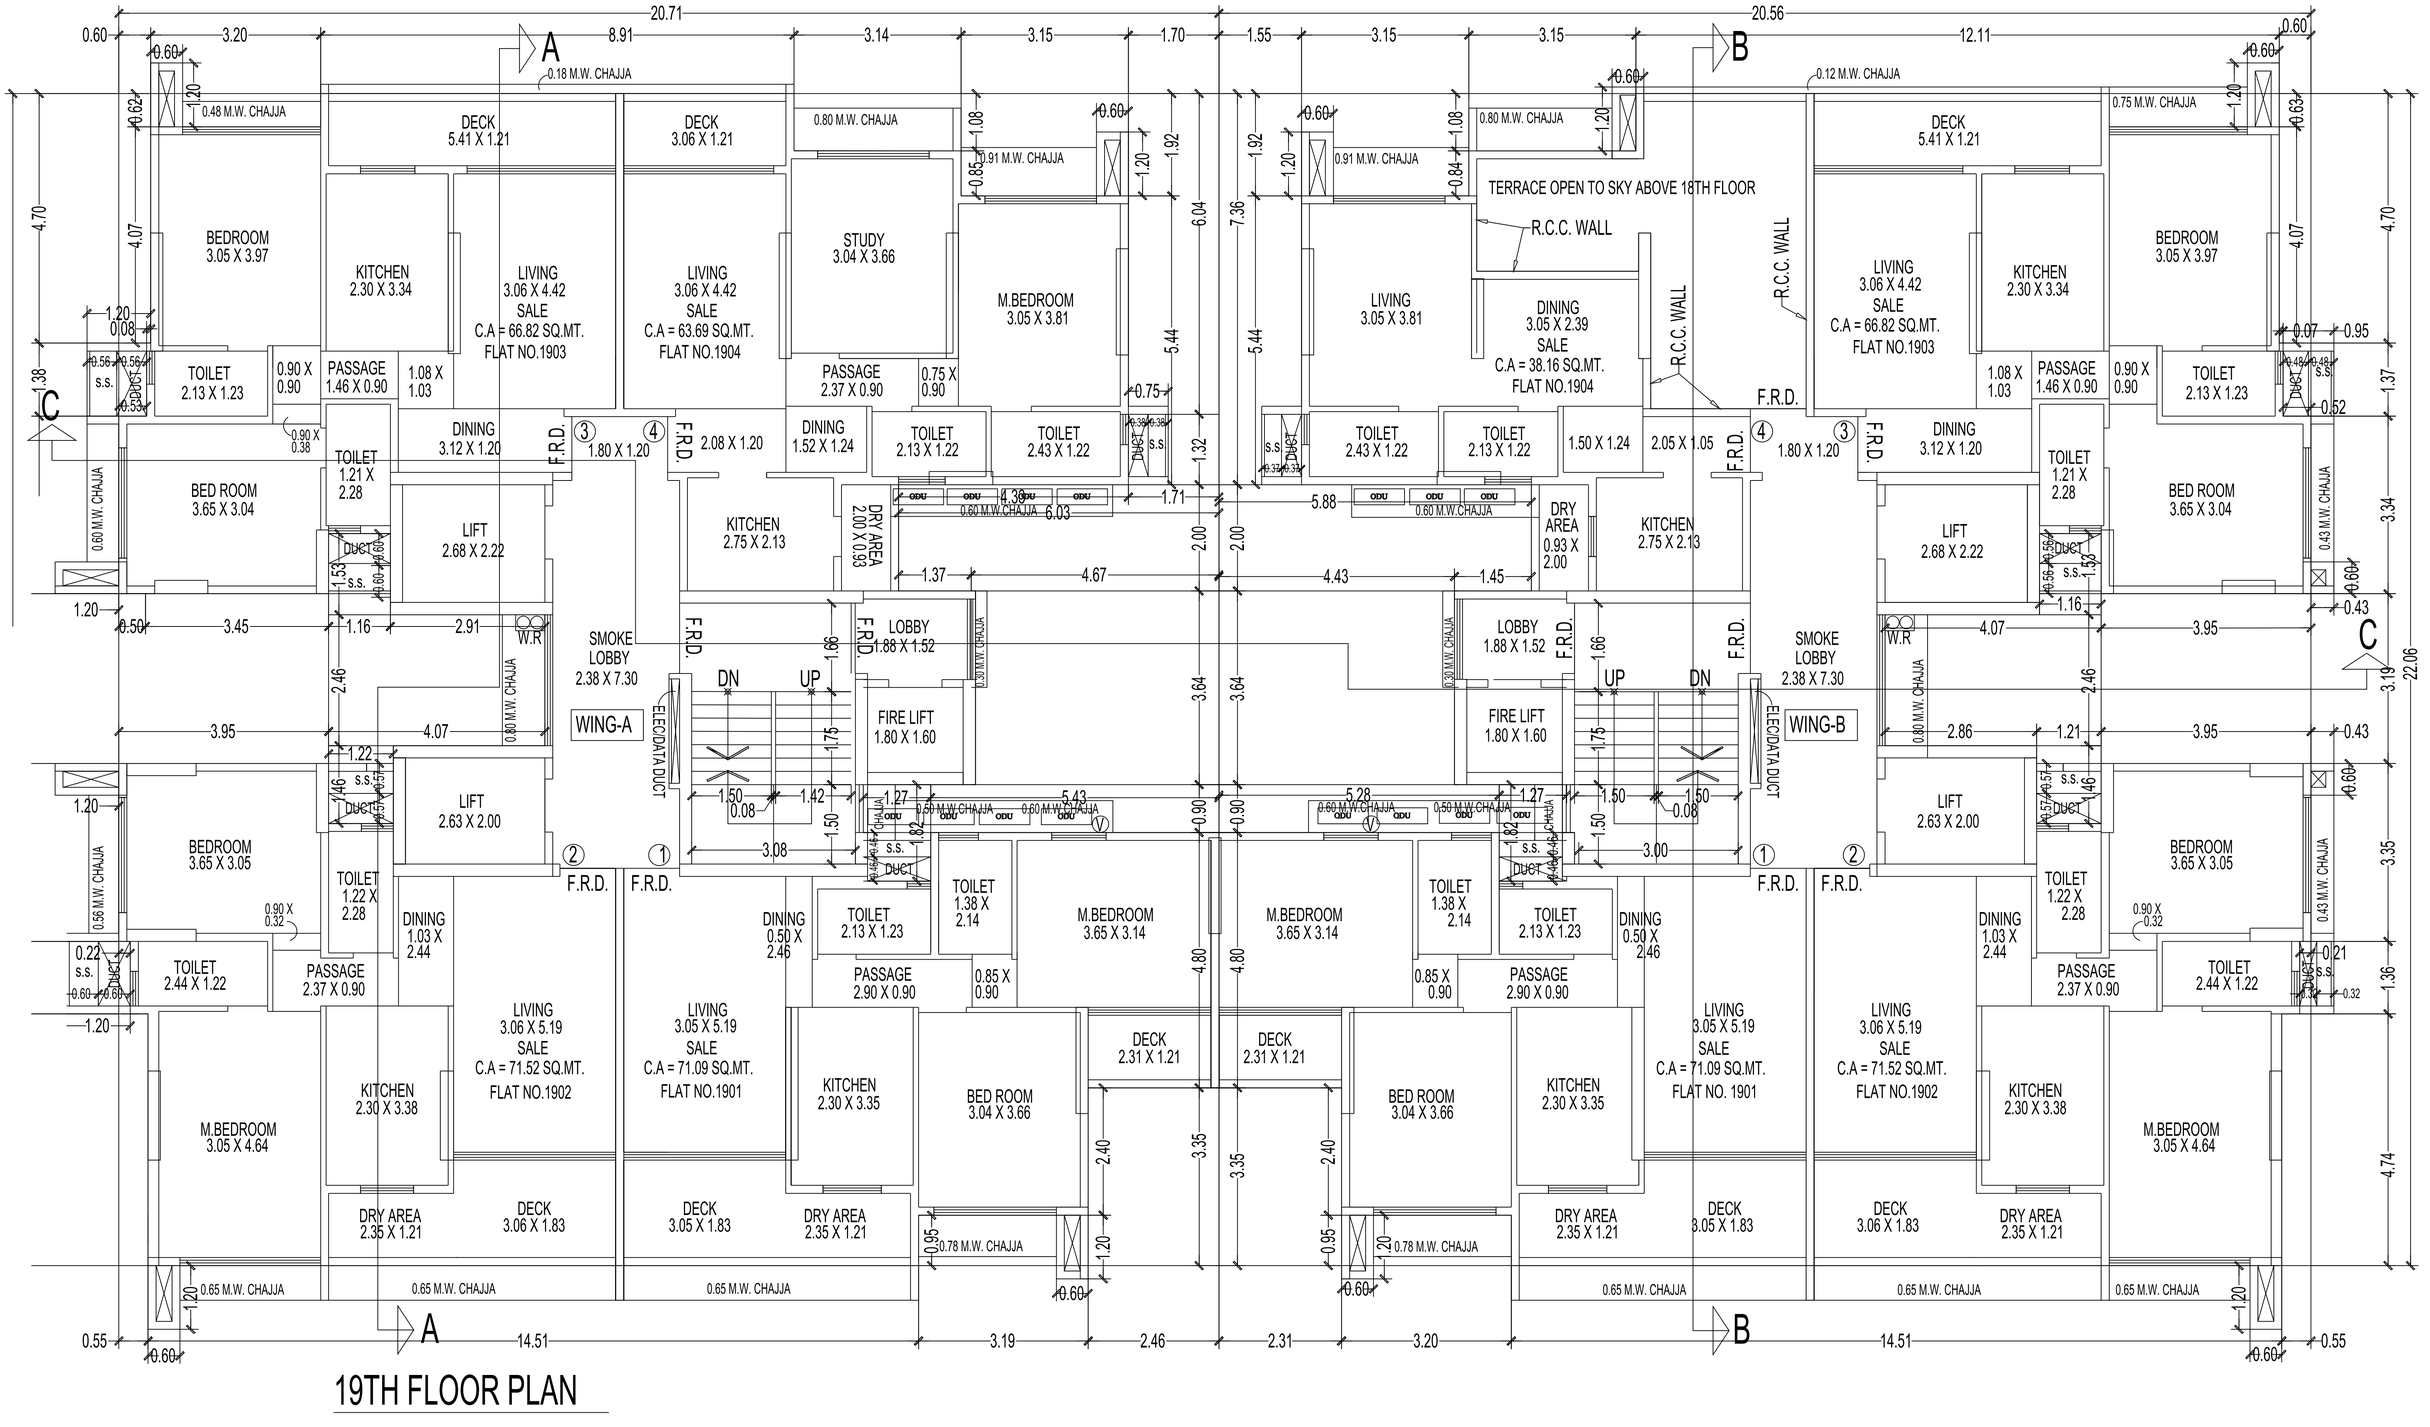

19TH FLOOR PLAN