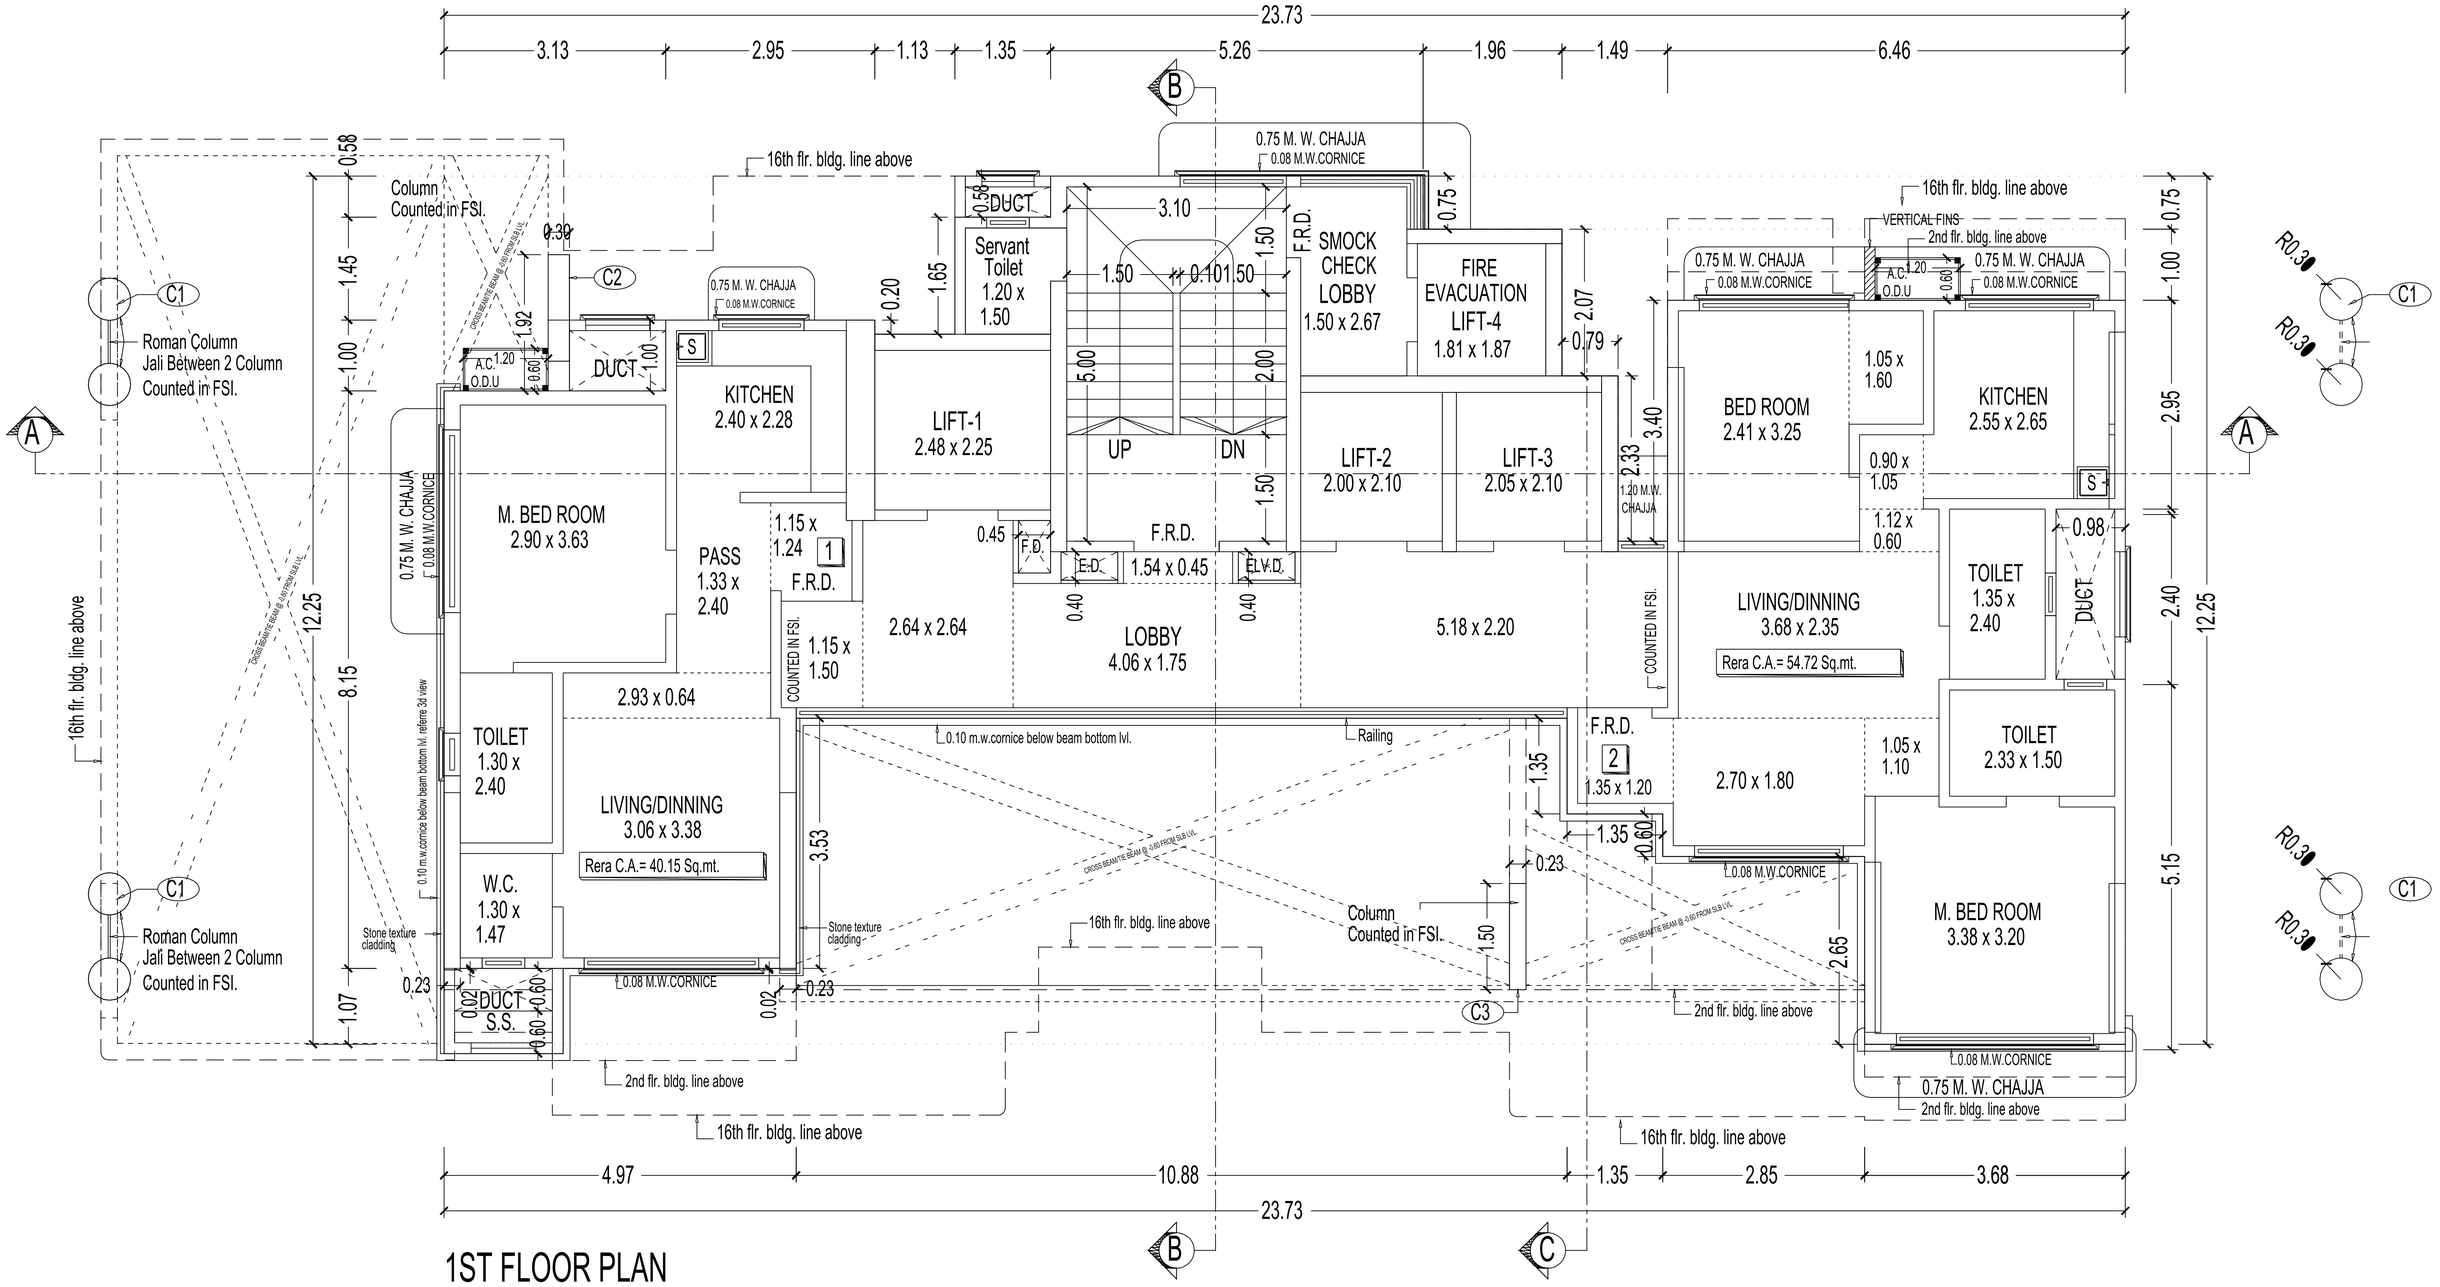



1ST FLOOR PLAN

SCALE - 1:100

23.73
3.13 2.95 1.13 1.35 5.26 1.96 1.49 6.46
A B C
16th flr. bldg. line above
3rd flr. bldg. line above
Column Counted in FSI.
Roman Column Jali Between 2 Column
CROSS BEAM/TIE BEAM @ 0.60 FROM SLB.T/L
0.75 M. W. CHAJJA
0.08 M.W.CORNICE
0.10 m.w.cornice below beam bottom lvl.
Railing
Stone texture cladding
VERTICAL FINS
C2
C3
S
DUCT
KITCHEN 2.40 x 2.28
M. BED ROOM 2.98 x 3.63
PASS 1.33 x 2.40
TOILET 1.38 x 2.40
TOILET 1.30 x 1.77
LIVING/DINNING 3.06 x 4.68
Rera C.A.= 45.06 Sq.mt.
Servant Toilet 1.20 x 1.50
LIFT-1 2.48 x 2.25
LIFT-2 2.00 x 2.10
LIFT-3 2.05 x 2.10
SMOCK CHECK LOBBY 1.50 x 2.67
FIRE EVACUATION LIFT-4 1.81 x 1.87
LOBBY 4.06 x 1.75
2.64 x 2.64
5.18 x 2.20
F.R.D.
UP
DN
ELV.D.
COUNTED IN FSI.
BED ROOM 2.41 x 3.65
KITCHEN 2.55 x 3.05
LIVING/DINNING 3.68 x 2.35
Rera C.A.= 64.48 Sq.mt.
TOILET 1.35 x 2.40
TOILET 2.33 x 1.50
M. BED ROOM 3.38 x 3.66
2.85 x 3.68
1.05 x 2.00
0.90 x 1.05
1.12 x 0.60
1.05 x 1.10
1.20 x 1.20
1.15 x 1.24
1.15 x 1.50
2.93 x 0.64
1.54 x 0.45
1.20 M.W. CHAJJA
A.C. O.D.U 1.20 x 0.60
0.58 1.45 1.00 8.45 0.23
12.71
0.75 1.65 0.20 1.92 1.00 1.50 5.00 2.00 1.50 2.07 0.79 3.80 2.33 1.35 0.23 1.50 2.48 1.23
0.60 3.35 2.40 5.61
4.83
4.97 10.88 1.35 2.85 3.68
23.73

2ND FLOOR PLAN

SCALE - 1:100

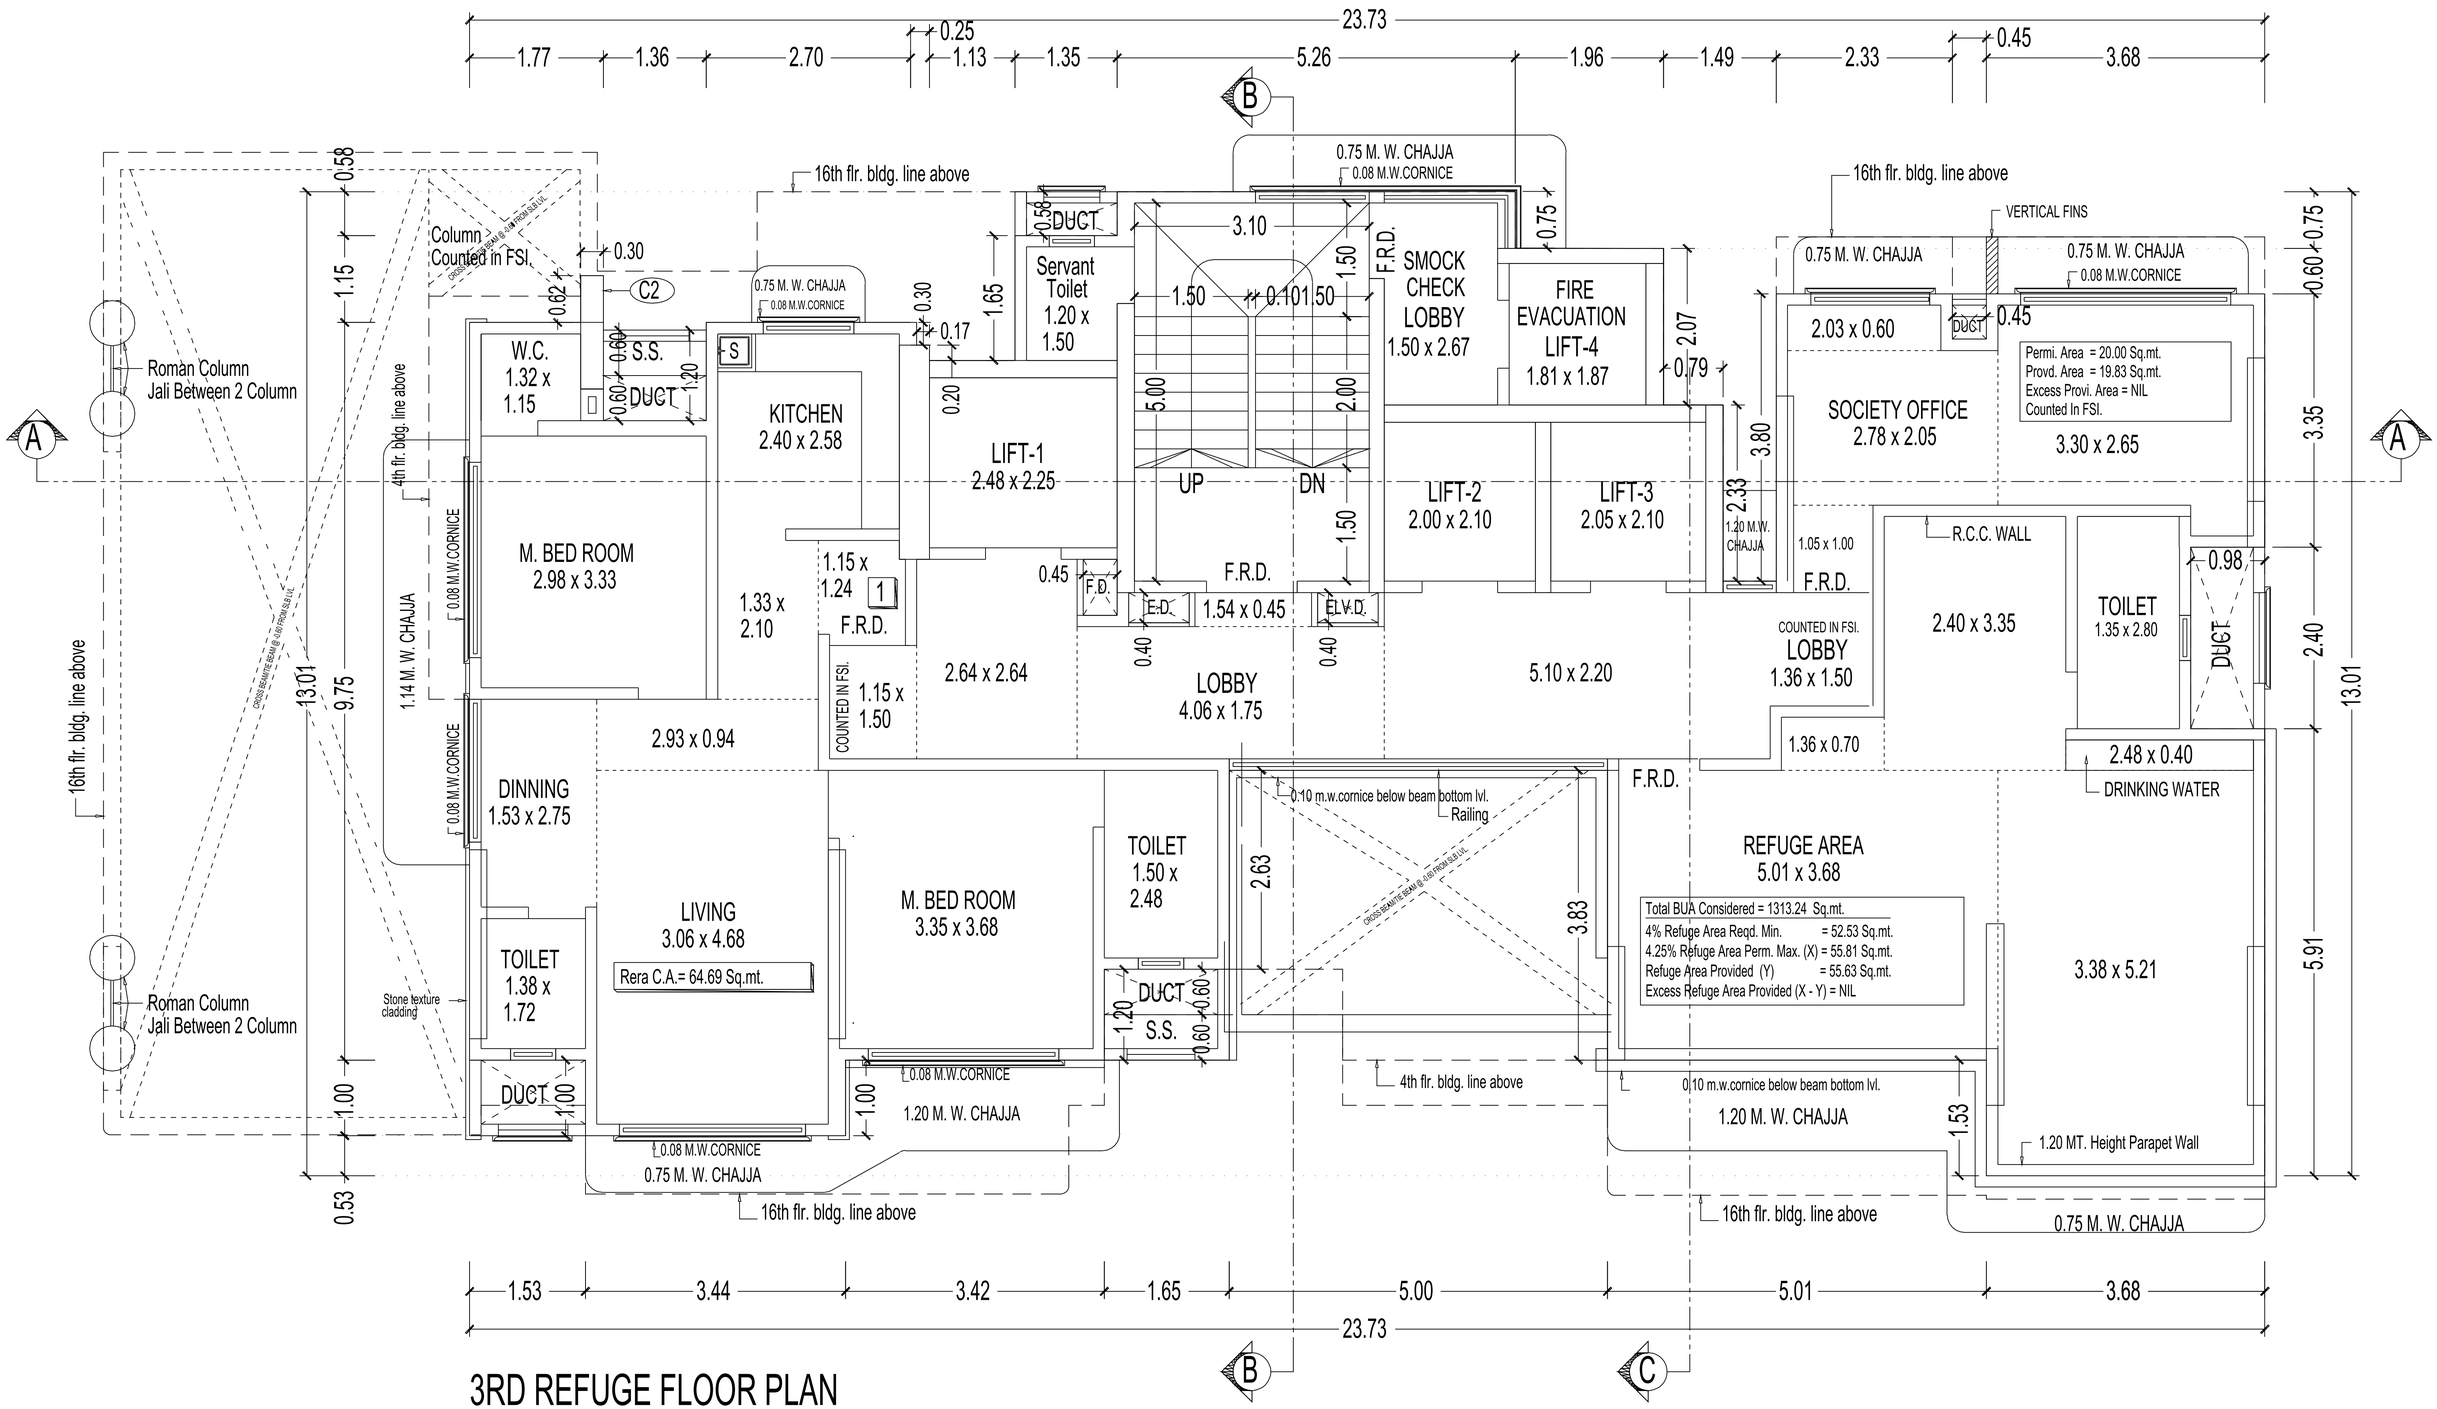


3RD REFUGE FLOOR PLAN

SCALE - 1:100


4TH TO 6TH FLOOR PLAN

SCALE - 1:100

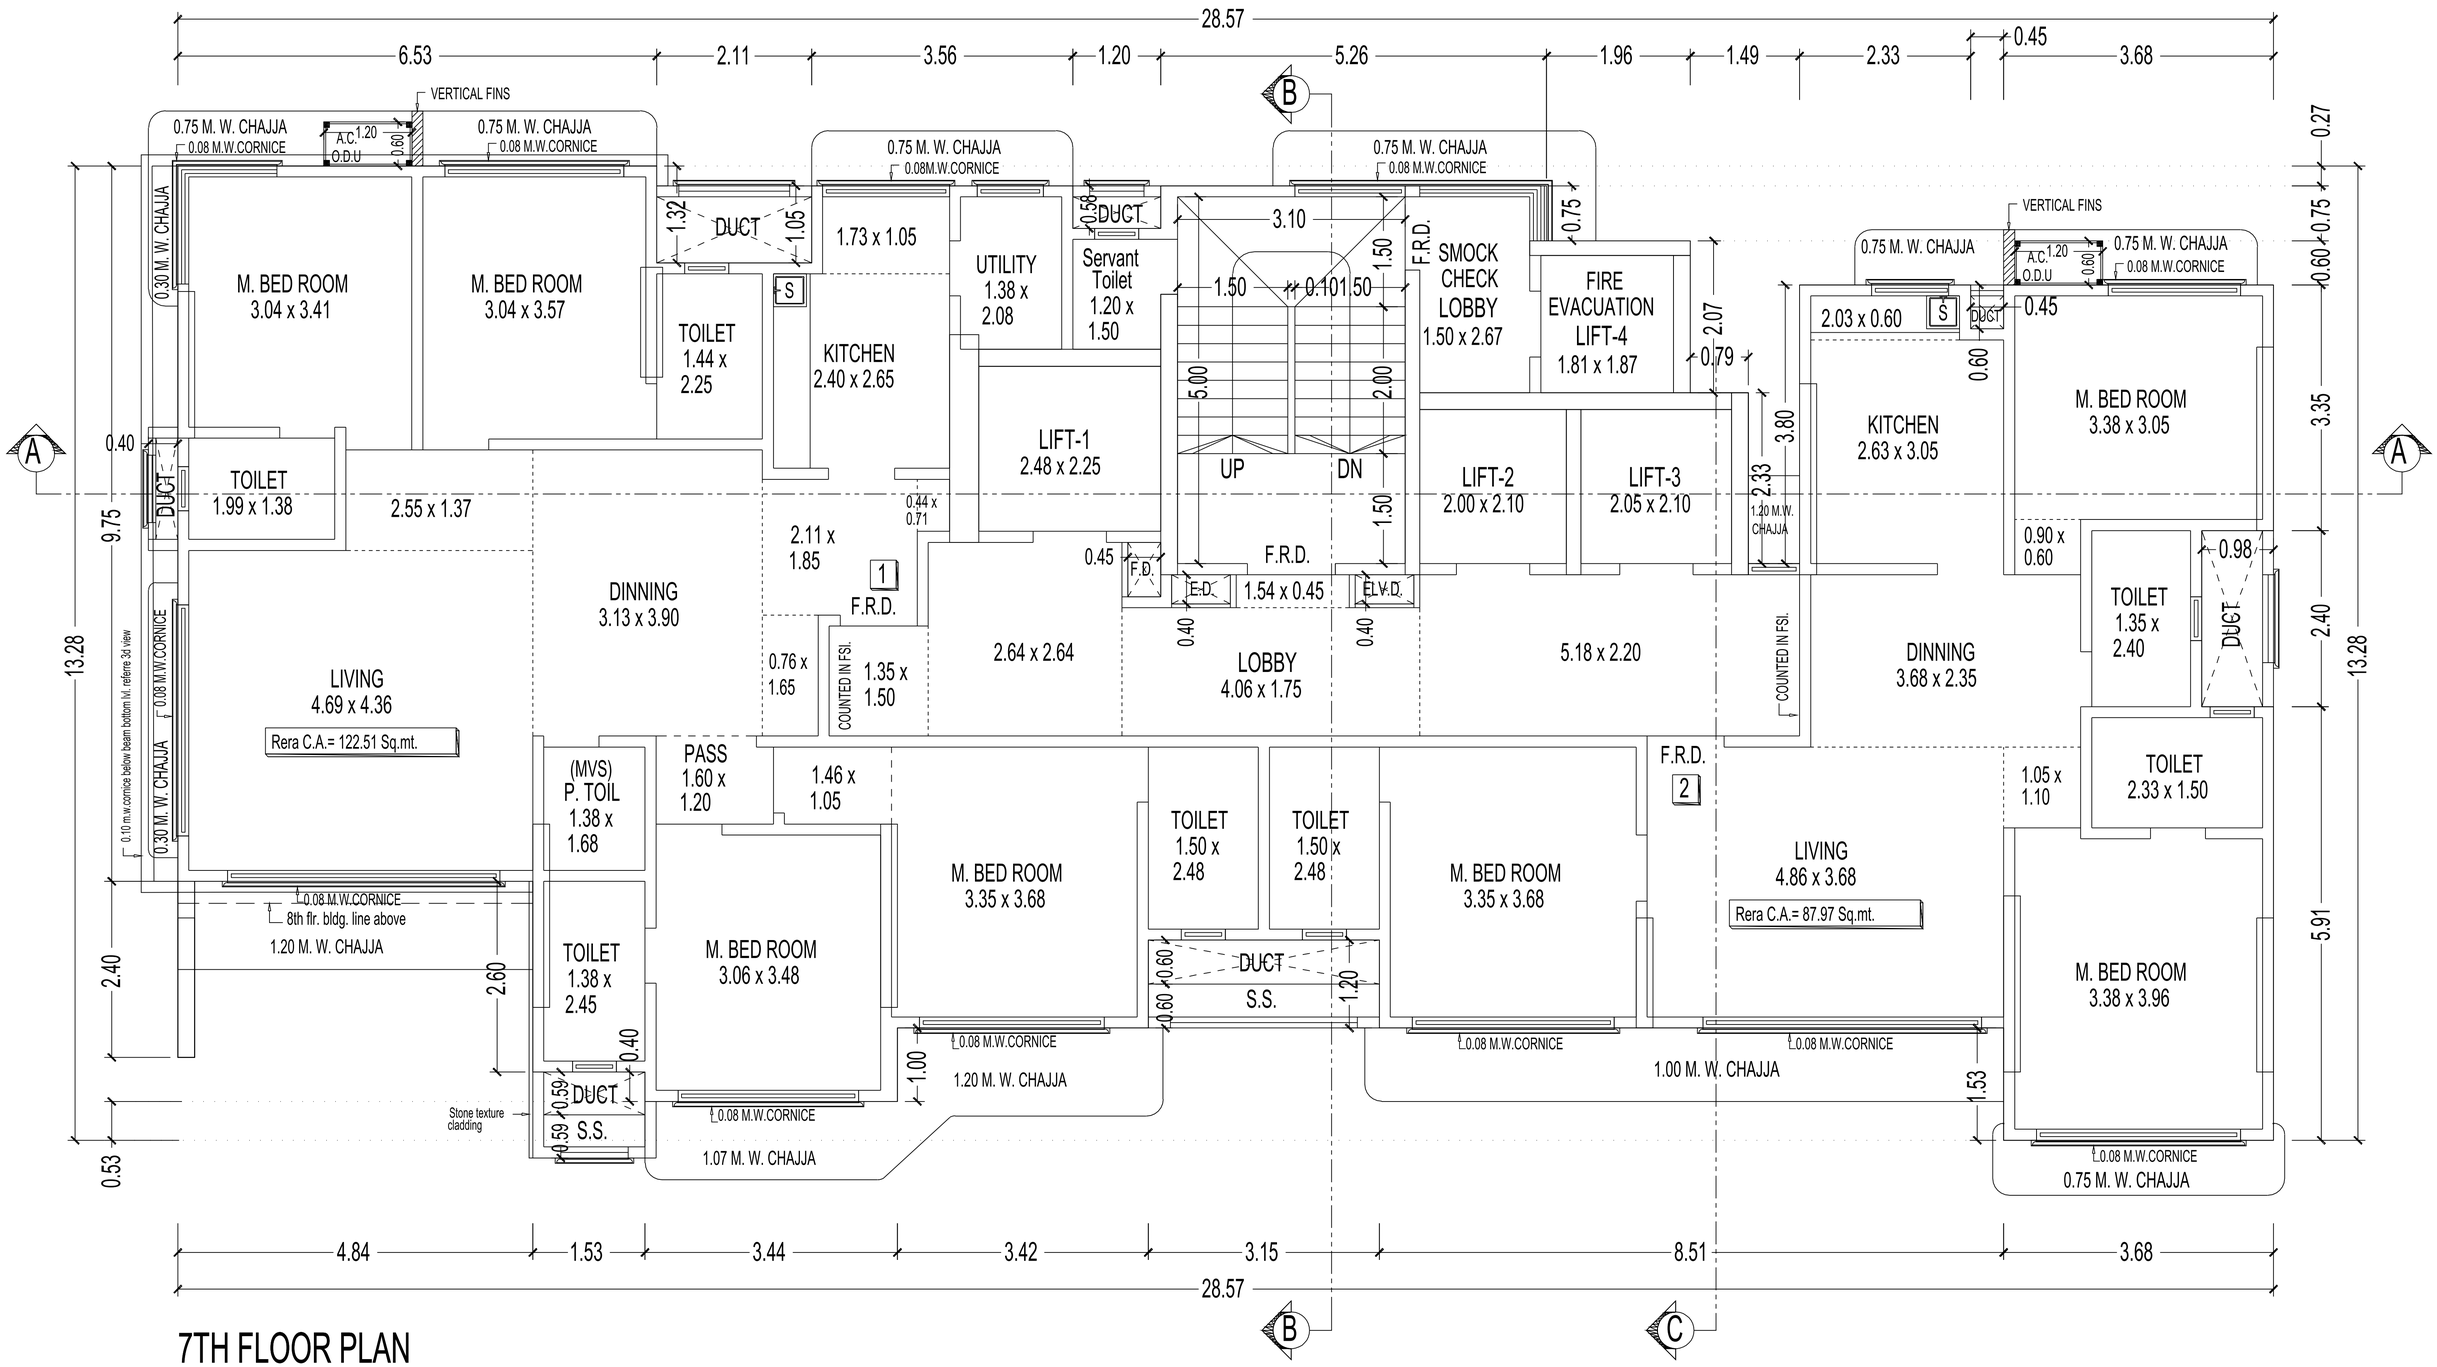

7TH FLOOR PLAN

SCALE - 1:100

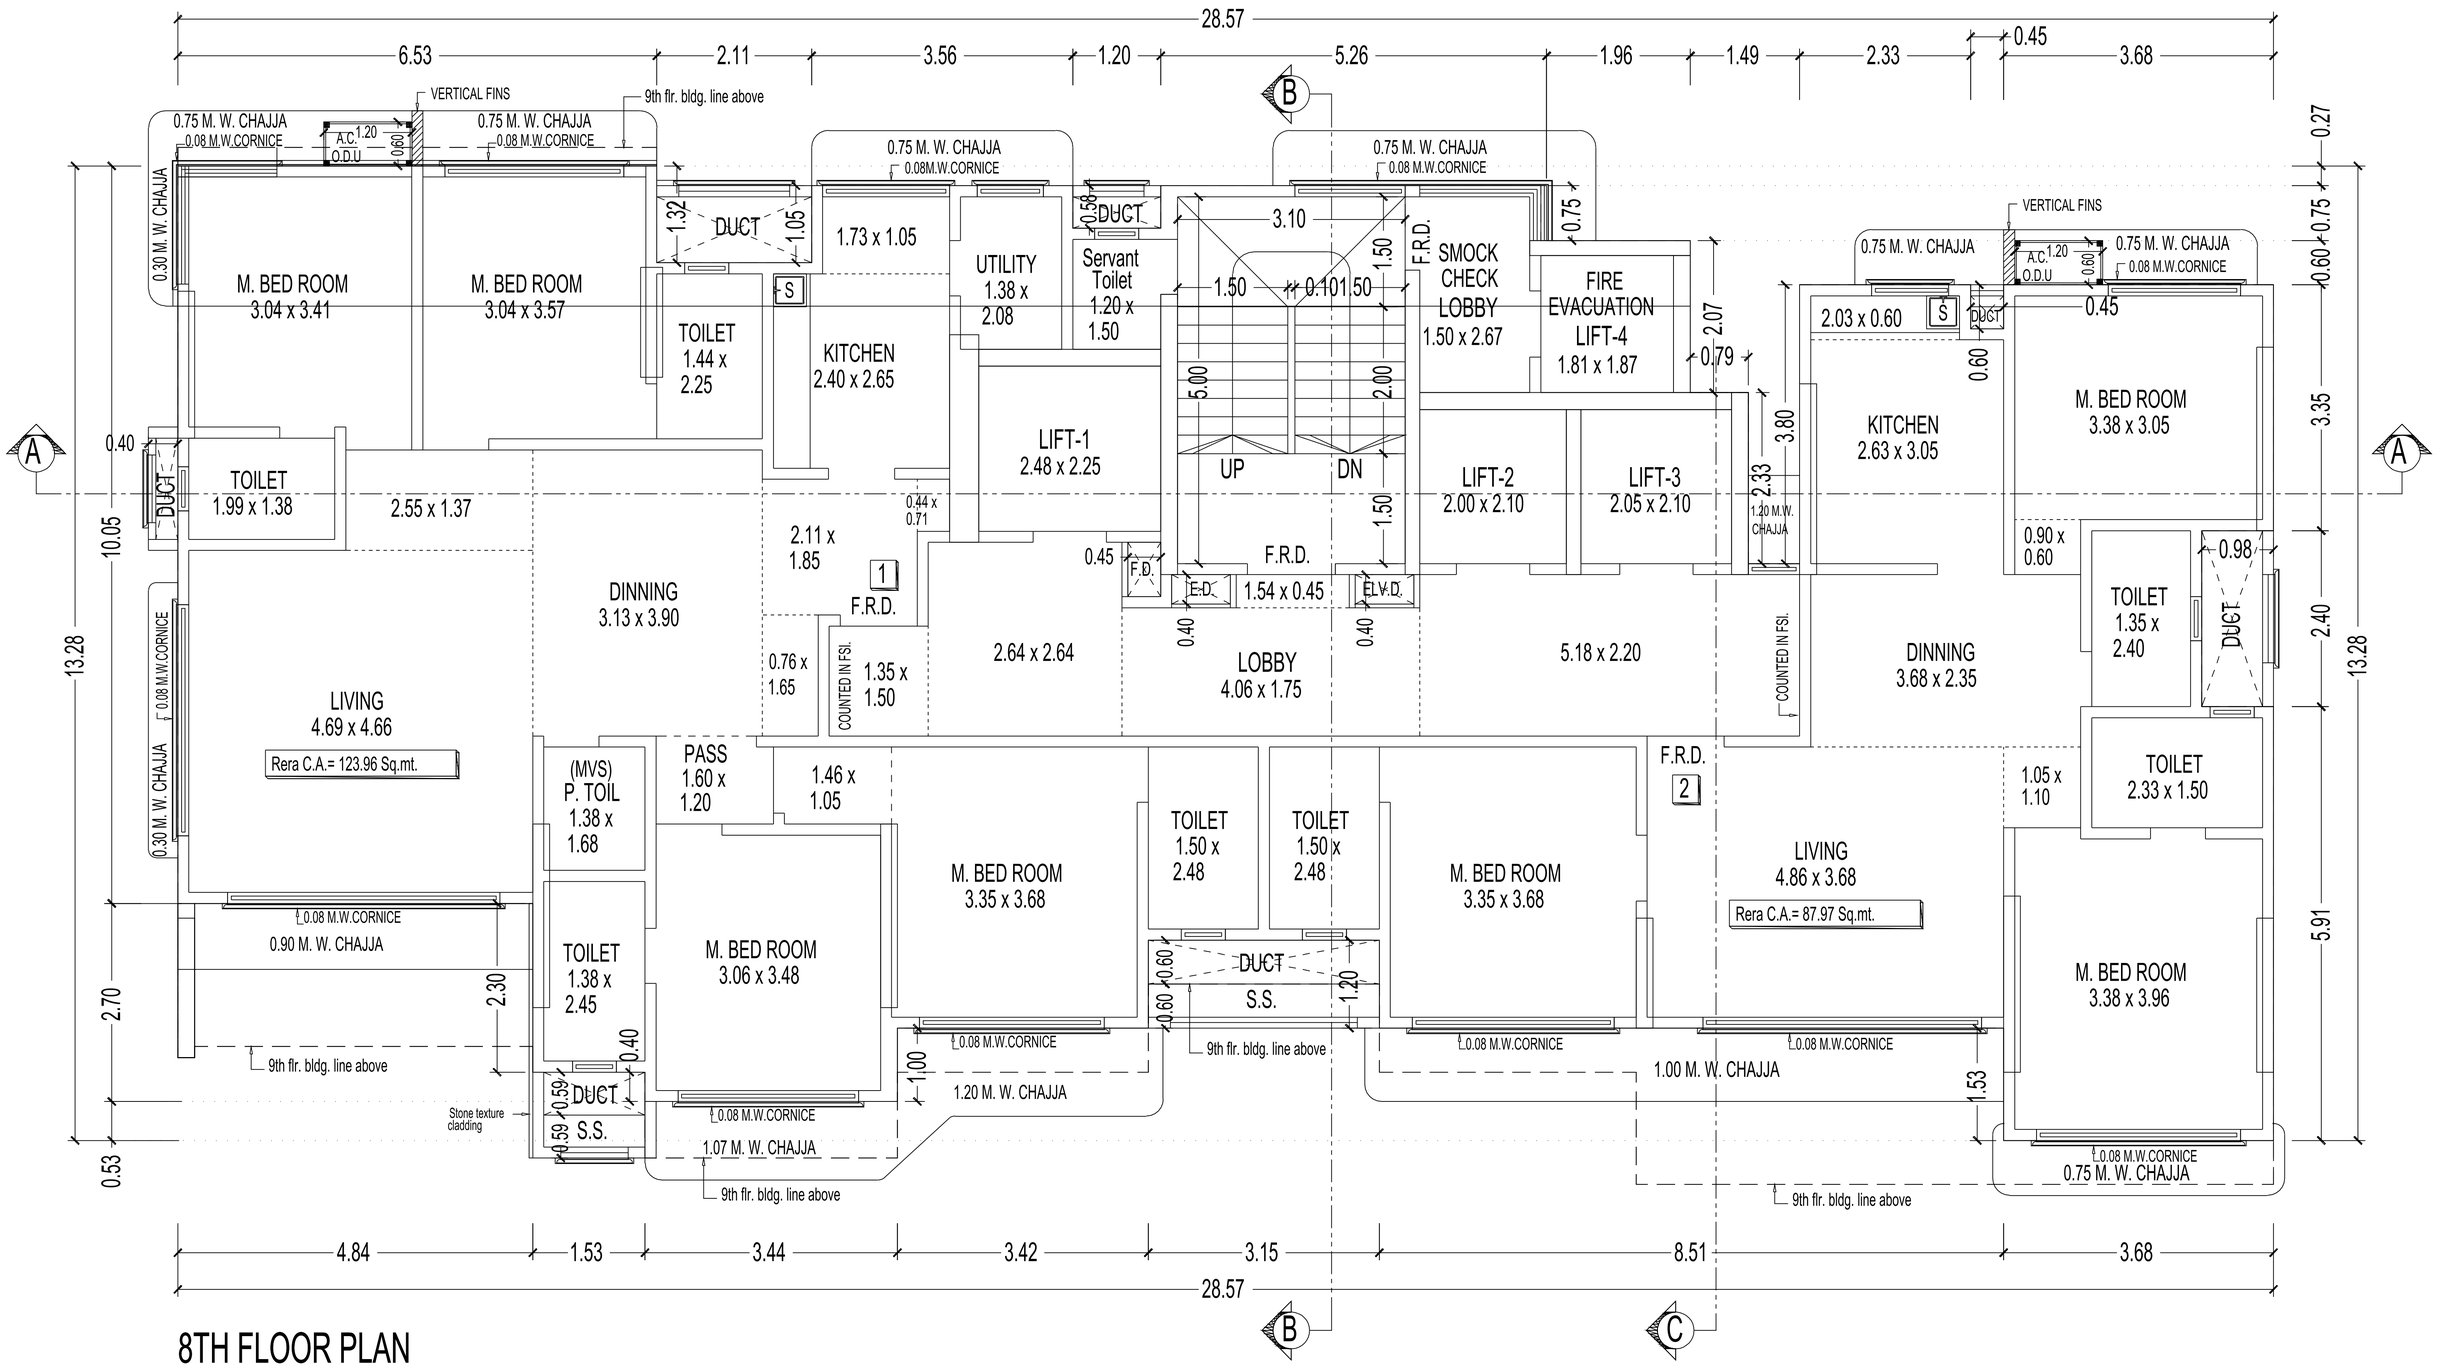


8TH FLOOR PLAN

SCALE - 1:100

9TH FLOOR PLAN

SCALE - 1:100

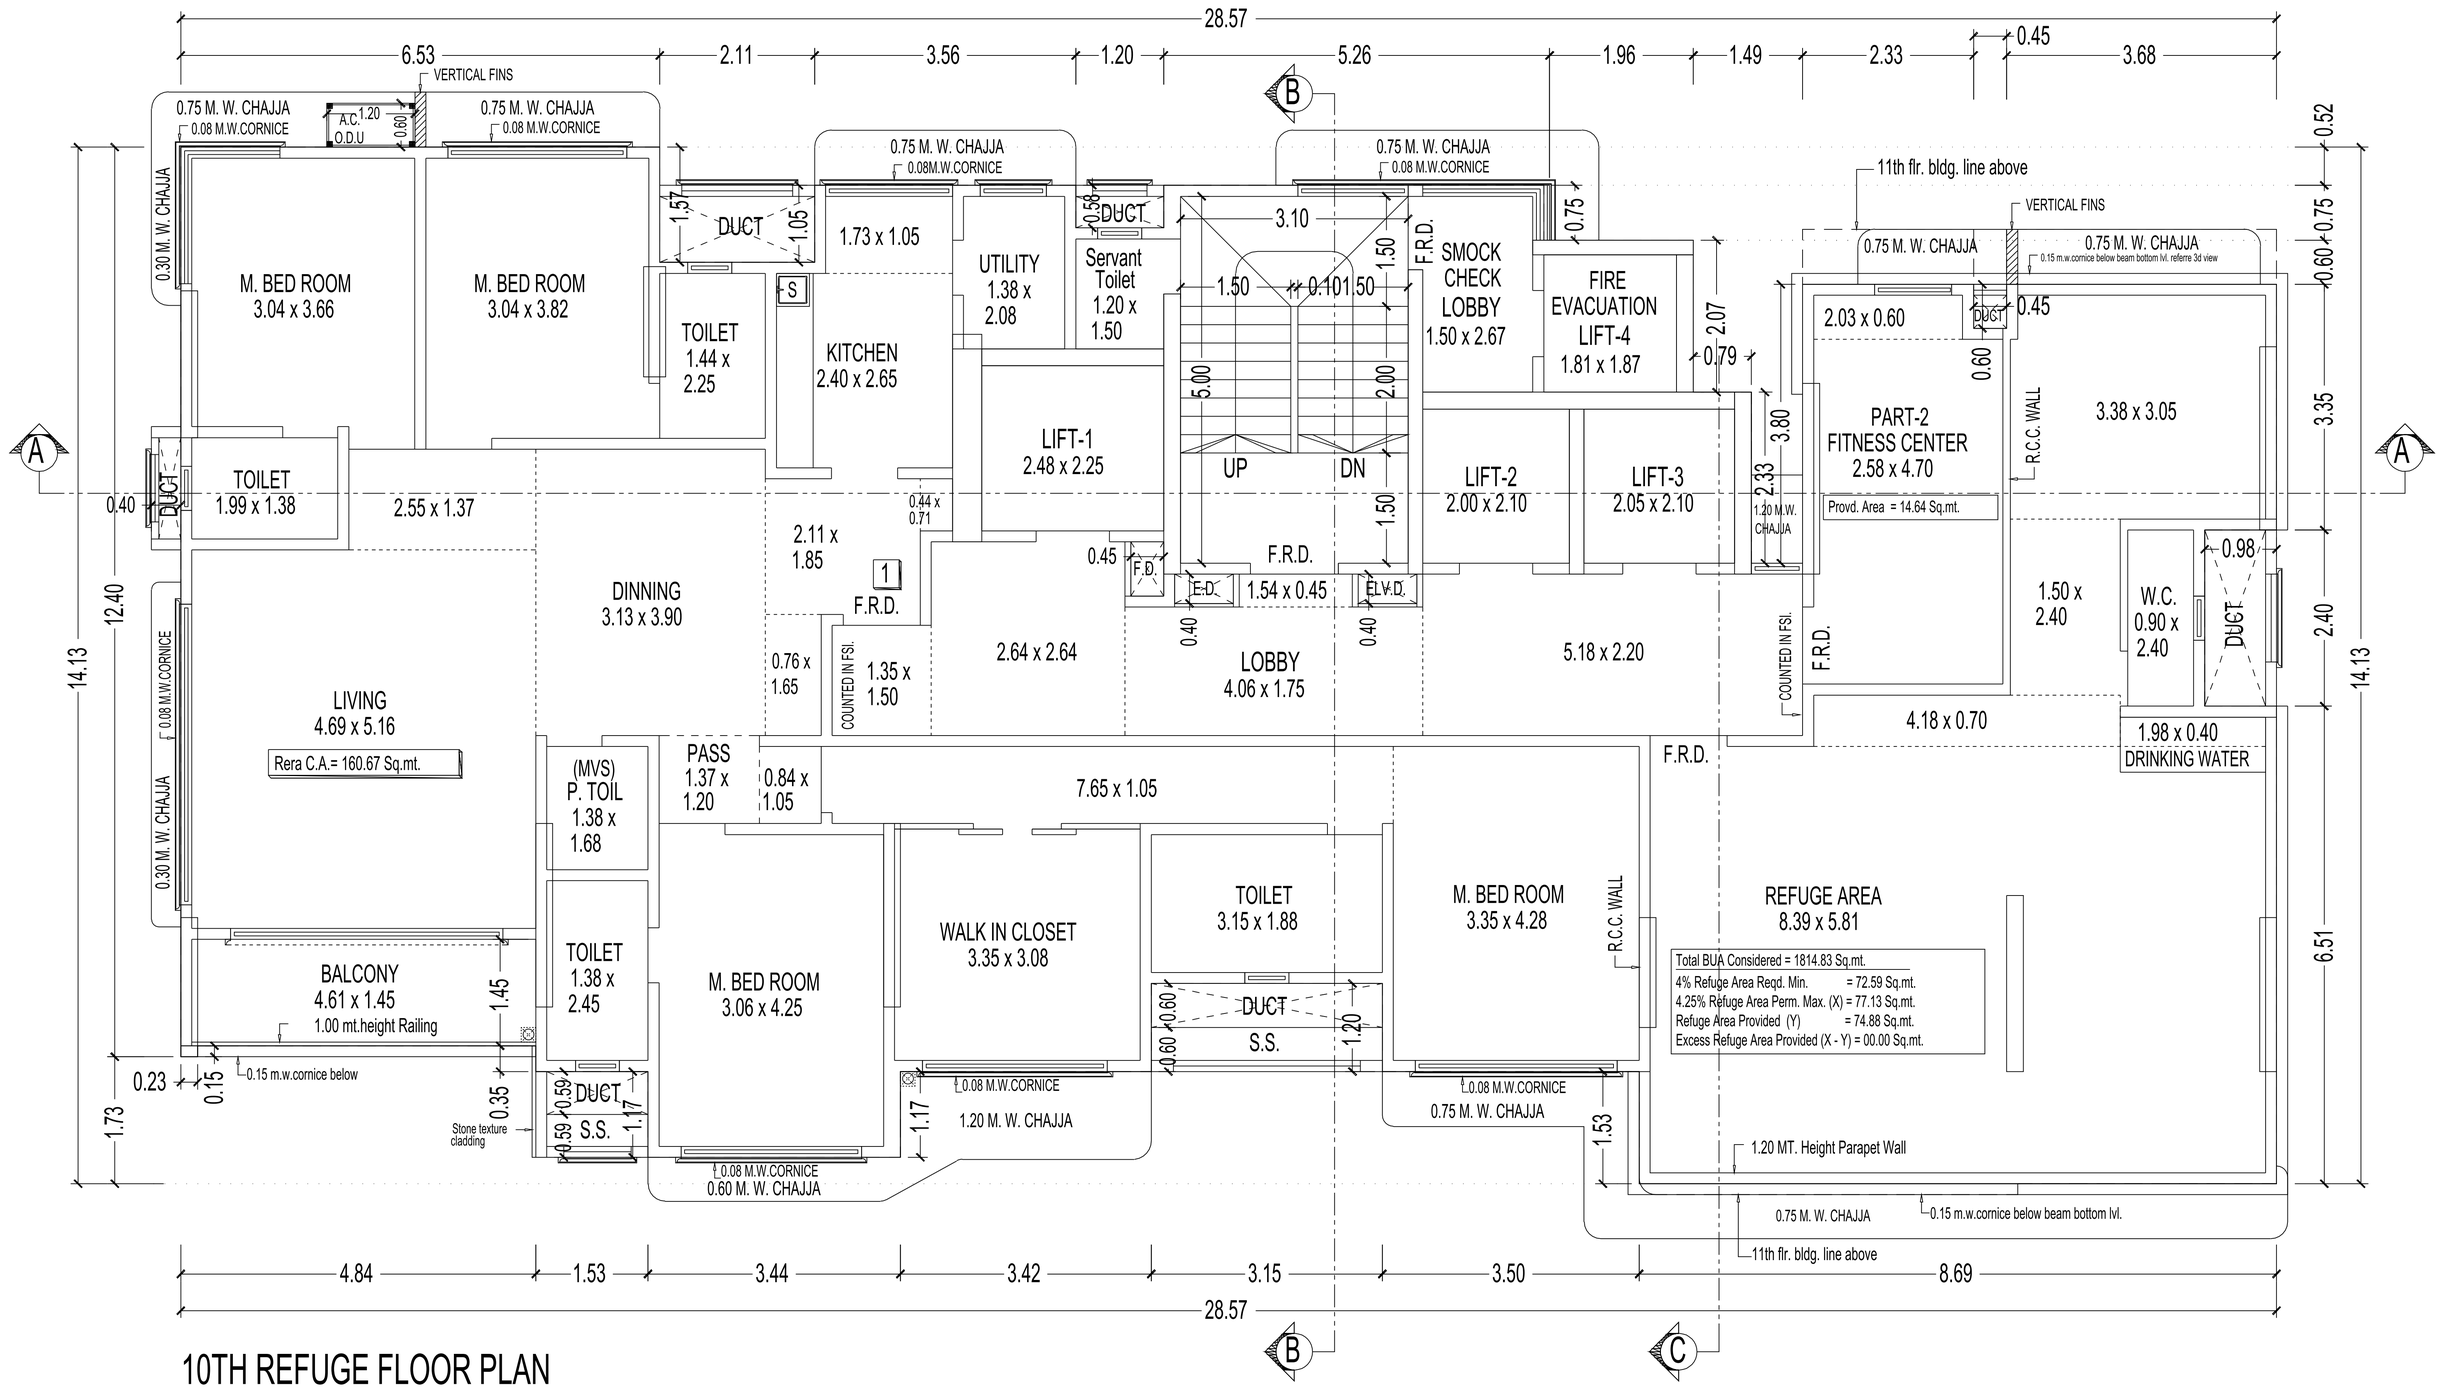


10TH REFUGE FLOOR PLAN

SCALE - 1:100

11TH FLOOR PLAN

SCALE - 1:100

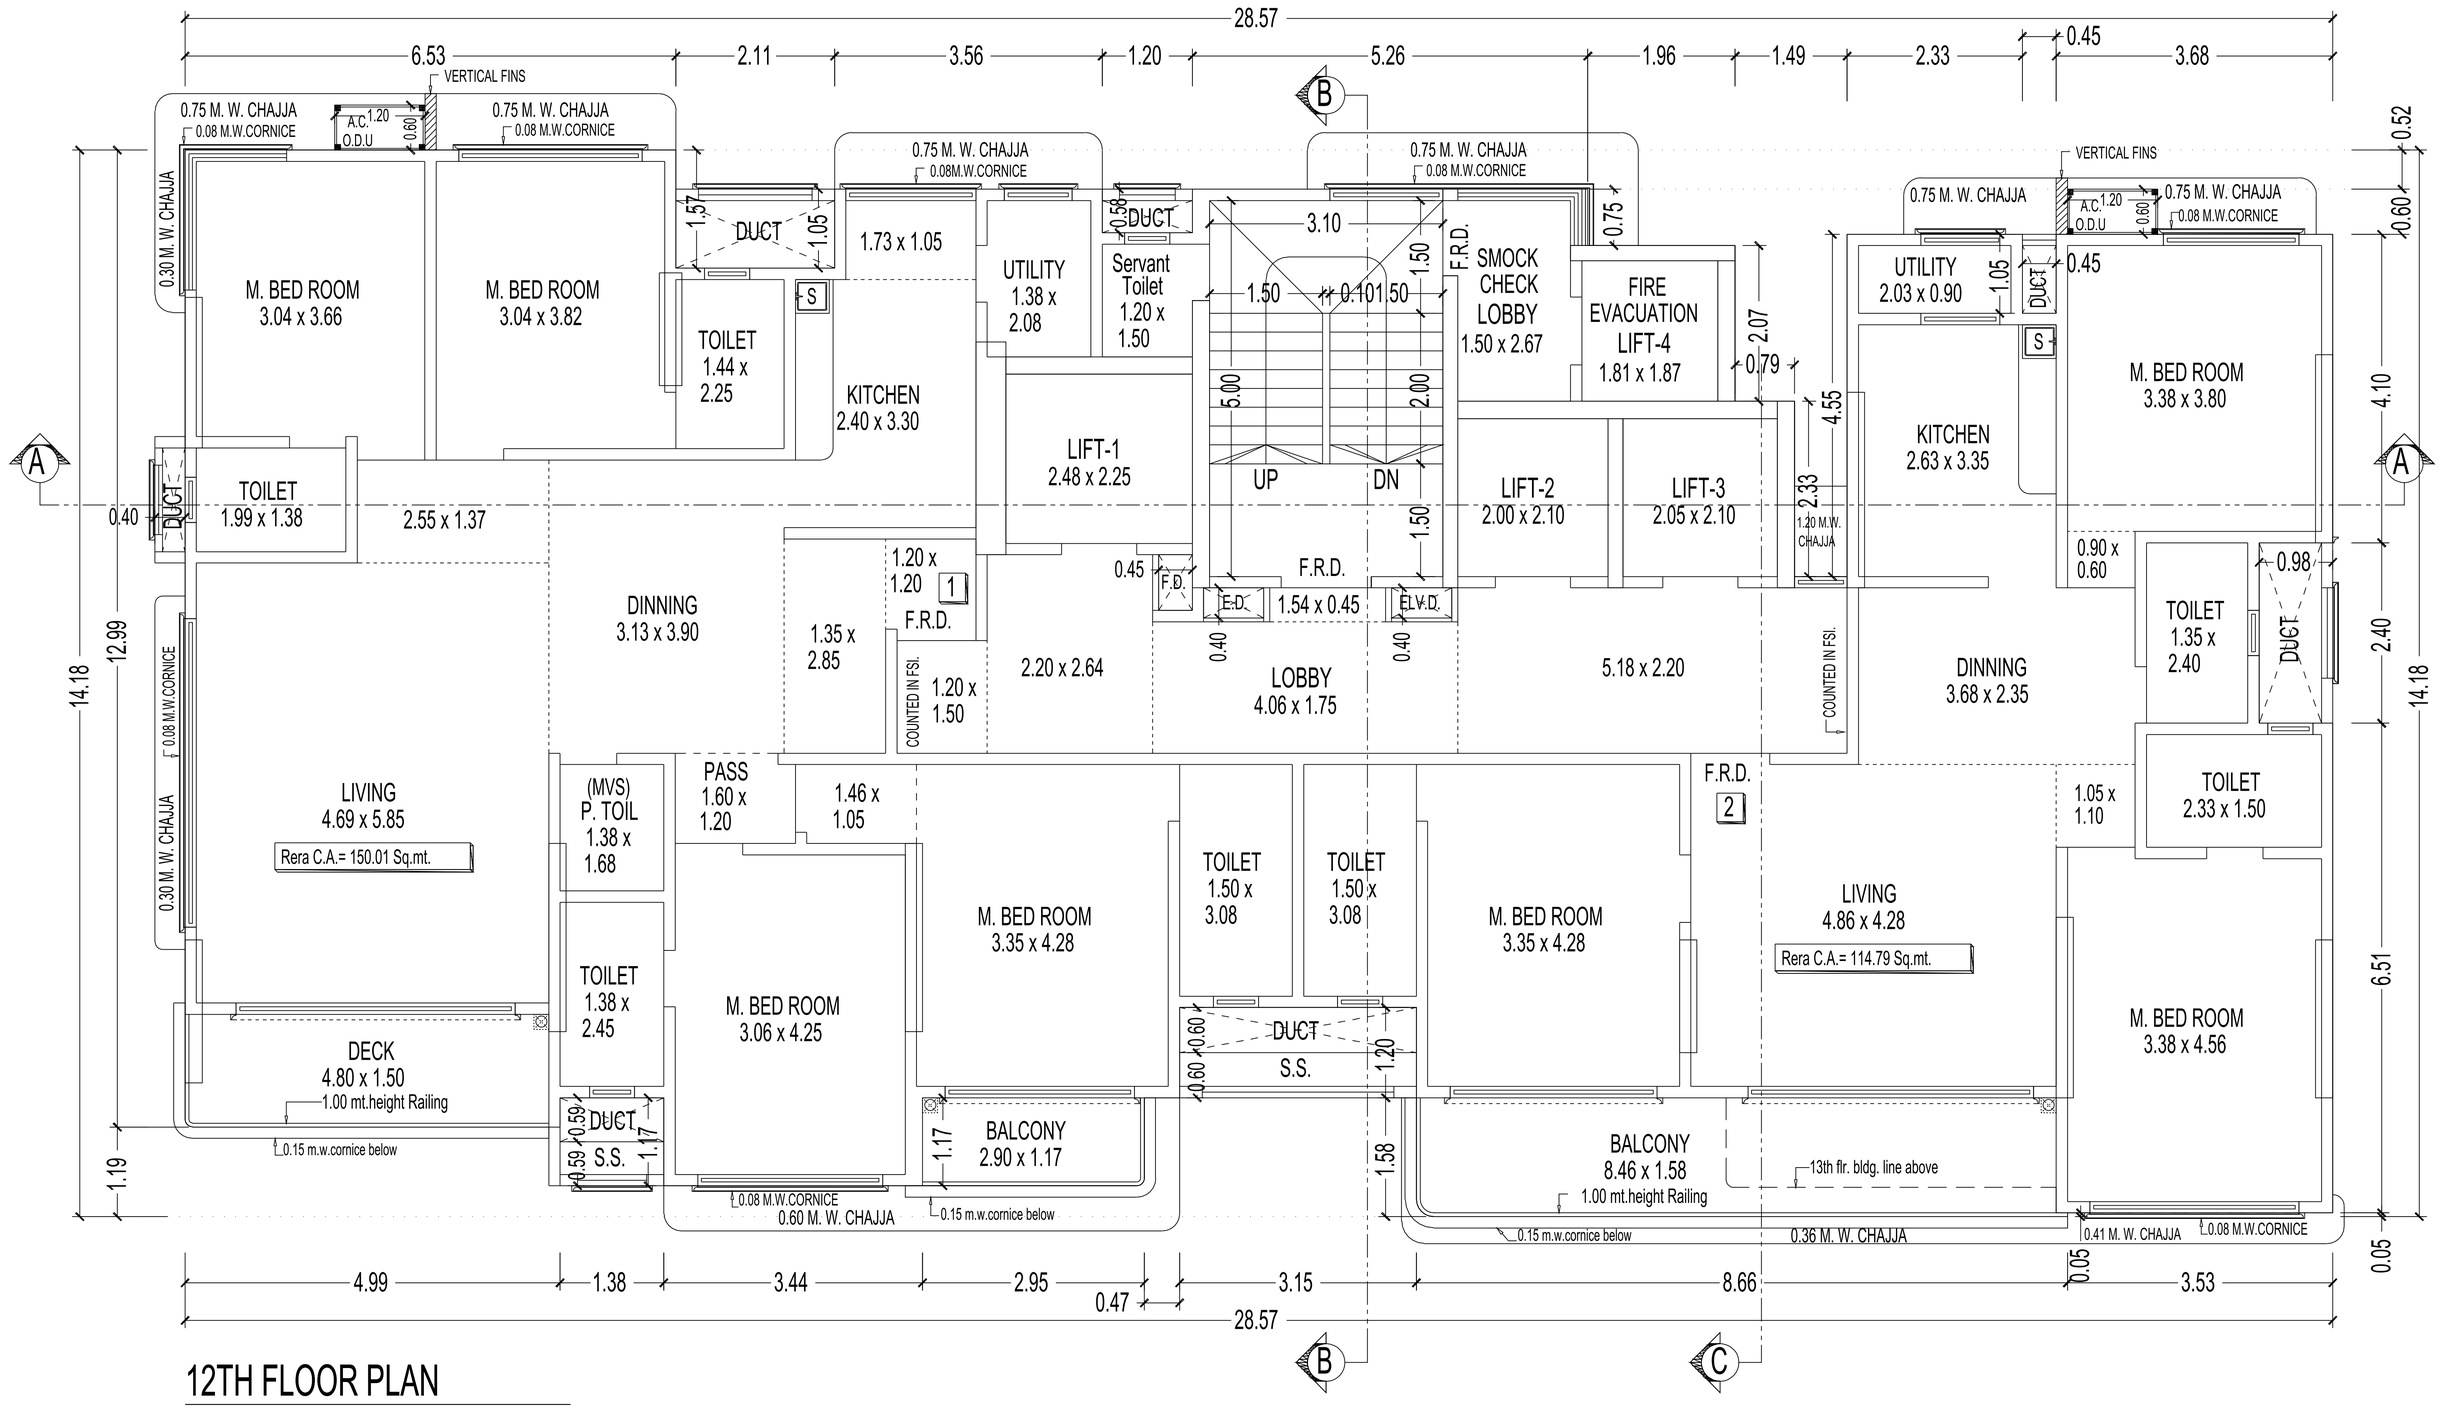


12TH FLOOR PLAN

SCALE - 1:100

13TH FLOOR PLAN

SCALE - 1:100

28.57
6.53
2.11
3.56
1.20
5.26
1.96
1.49
2.33
0.45
3.68
VERTICAL FINS
0.75 M. W. CHAJJA
0.08 M.W.CORNICE
A.C.1.20 O.D.U
0.60
0.30 M. W. CHAJJA
M. BED ROOM 3.04 x 3.66
M. BED ROOM 3.04 x 4.12
TOILET 1.44 x 2.55
DUCT
1.57
1.05
S
1.73 x 1.05
KITCHEN 2.40 x 3.30
UTILITY 1.38 x 2.08
0.58
Servant Toilet 1.20 x 1.50
LIFT-1 2.48 x 2.25
3.10
1.50
0.10
5.00
2.00
UP
DN
F.R.D.
SMOCK CHECK LOBBY 1.50 x 2.67
0.75
FIRE EVACUATION LIFT-4 1.81 x 1.87
2.07
0.79
LIFT-2 2.00 x 2.10
LIFT-3 2.05 x 2.10
4.55
2.33
1.20 M.W. CHAJJA
UTILITY 2.03 x 0.90
KITCHEN 2.63 x 3.35
M. BED ROOM 3.38 x 3.80
0.52
0.60
4.10
14.13
12.99
A
B
C
TOILET 1.99 x 1.38
DUCT
0.40
2.55 x 1.07
DINNING 3.13 x 3.60
1.35 x 2.85
1.20 x 1.20
1
F.R.D.
COUNTED IN FSI.
1.20 x 1.50
2.20 x 2.64
0.45
F.D.
E.D.
1.54 x 0.45
EL.V.D.
0.40
LOBBY 4.06 x 1.75
5.18 x 2.20
0.90 x 0.60
0.98
TOILET 1.35 x 2.40
DINNING 3.68 x 2.35
2.40
LIVING 4.69 x 5.85
Rera C.A.= 153.03 Sq.mt.
(MVS) P. TOIL 1.38 x 1.68
PASS 1.60 x 1.20
1.46 x 1.05
TOILET 1.38 x 2.45
M. BED ROOM 3.06 x 4.25
M. BED ROOM 3.35 x 4.28
TOILET 1.50 x 3.08
TOILET 1.50 x 3.08
M. BED ROOM 3.35 x 4.28
F.R.D.
2
1.05 x 1.10
TOILET 2.33 x 1.50
LIVING 4.86 x 4.28
Rera C.A.= 106.61 Sq.mt.
M. BED ROOM 3.38 x 3.56
6.51
DECK 4.80 x 1.50
1.00 mt.height Railing
0.15 m.w.cornice below
1.14
0.59
1.17
S.S.
0.60
1.20
BALCONY 2.90 x 1.17
0.08 M.W.CORNICE
0.60 M. W. CHAJJA
0.15 m.w.cornice below
0.08 M.W.CORNICE
0.75 M. W. CHAJJA
14th flr. bldg. line above
BALCONY 4.34 x 1.19
1.00 mt.height Railing
0.34
0.15 m.w.cornice below
0.75 M. W. CHAJJA
BALCONY 3.48 x 1.00
1.00 mt.height Railing
0.70 M. W. CHAJJA
4.99
1.38
3.44
2.95
0.47
3.15
4.12
4.39
3.68
28.57

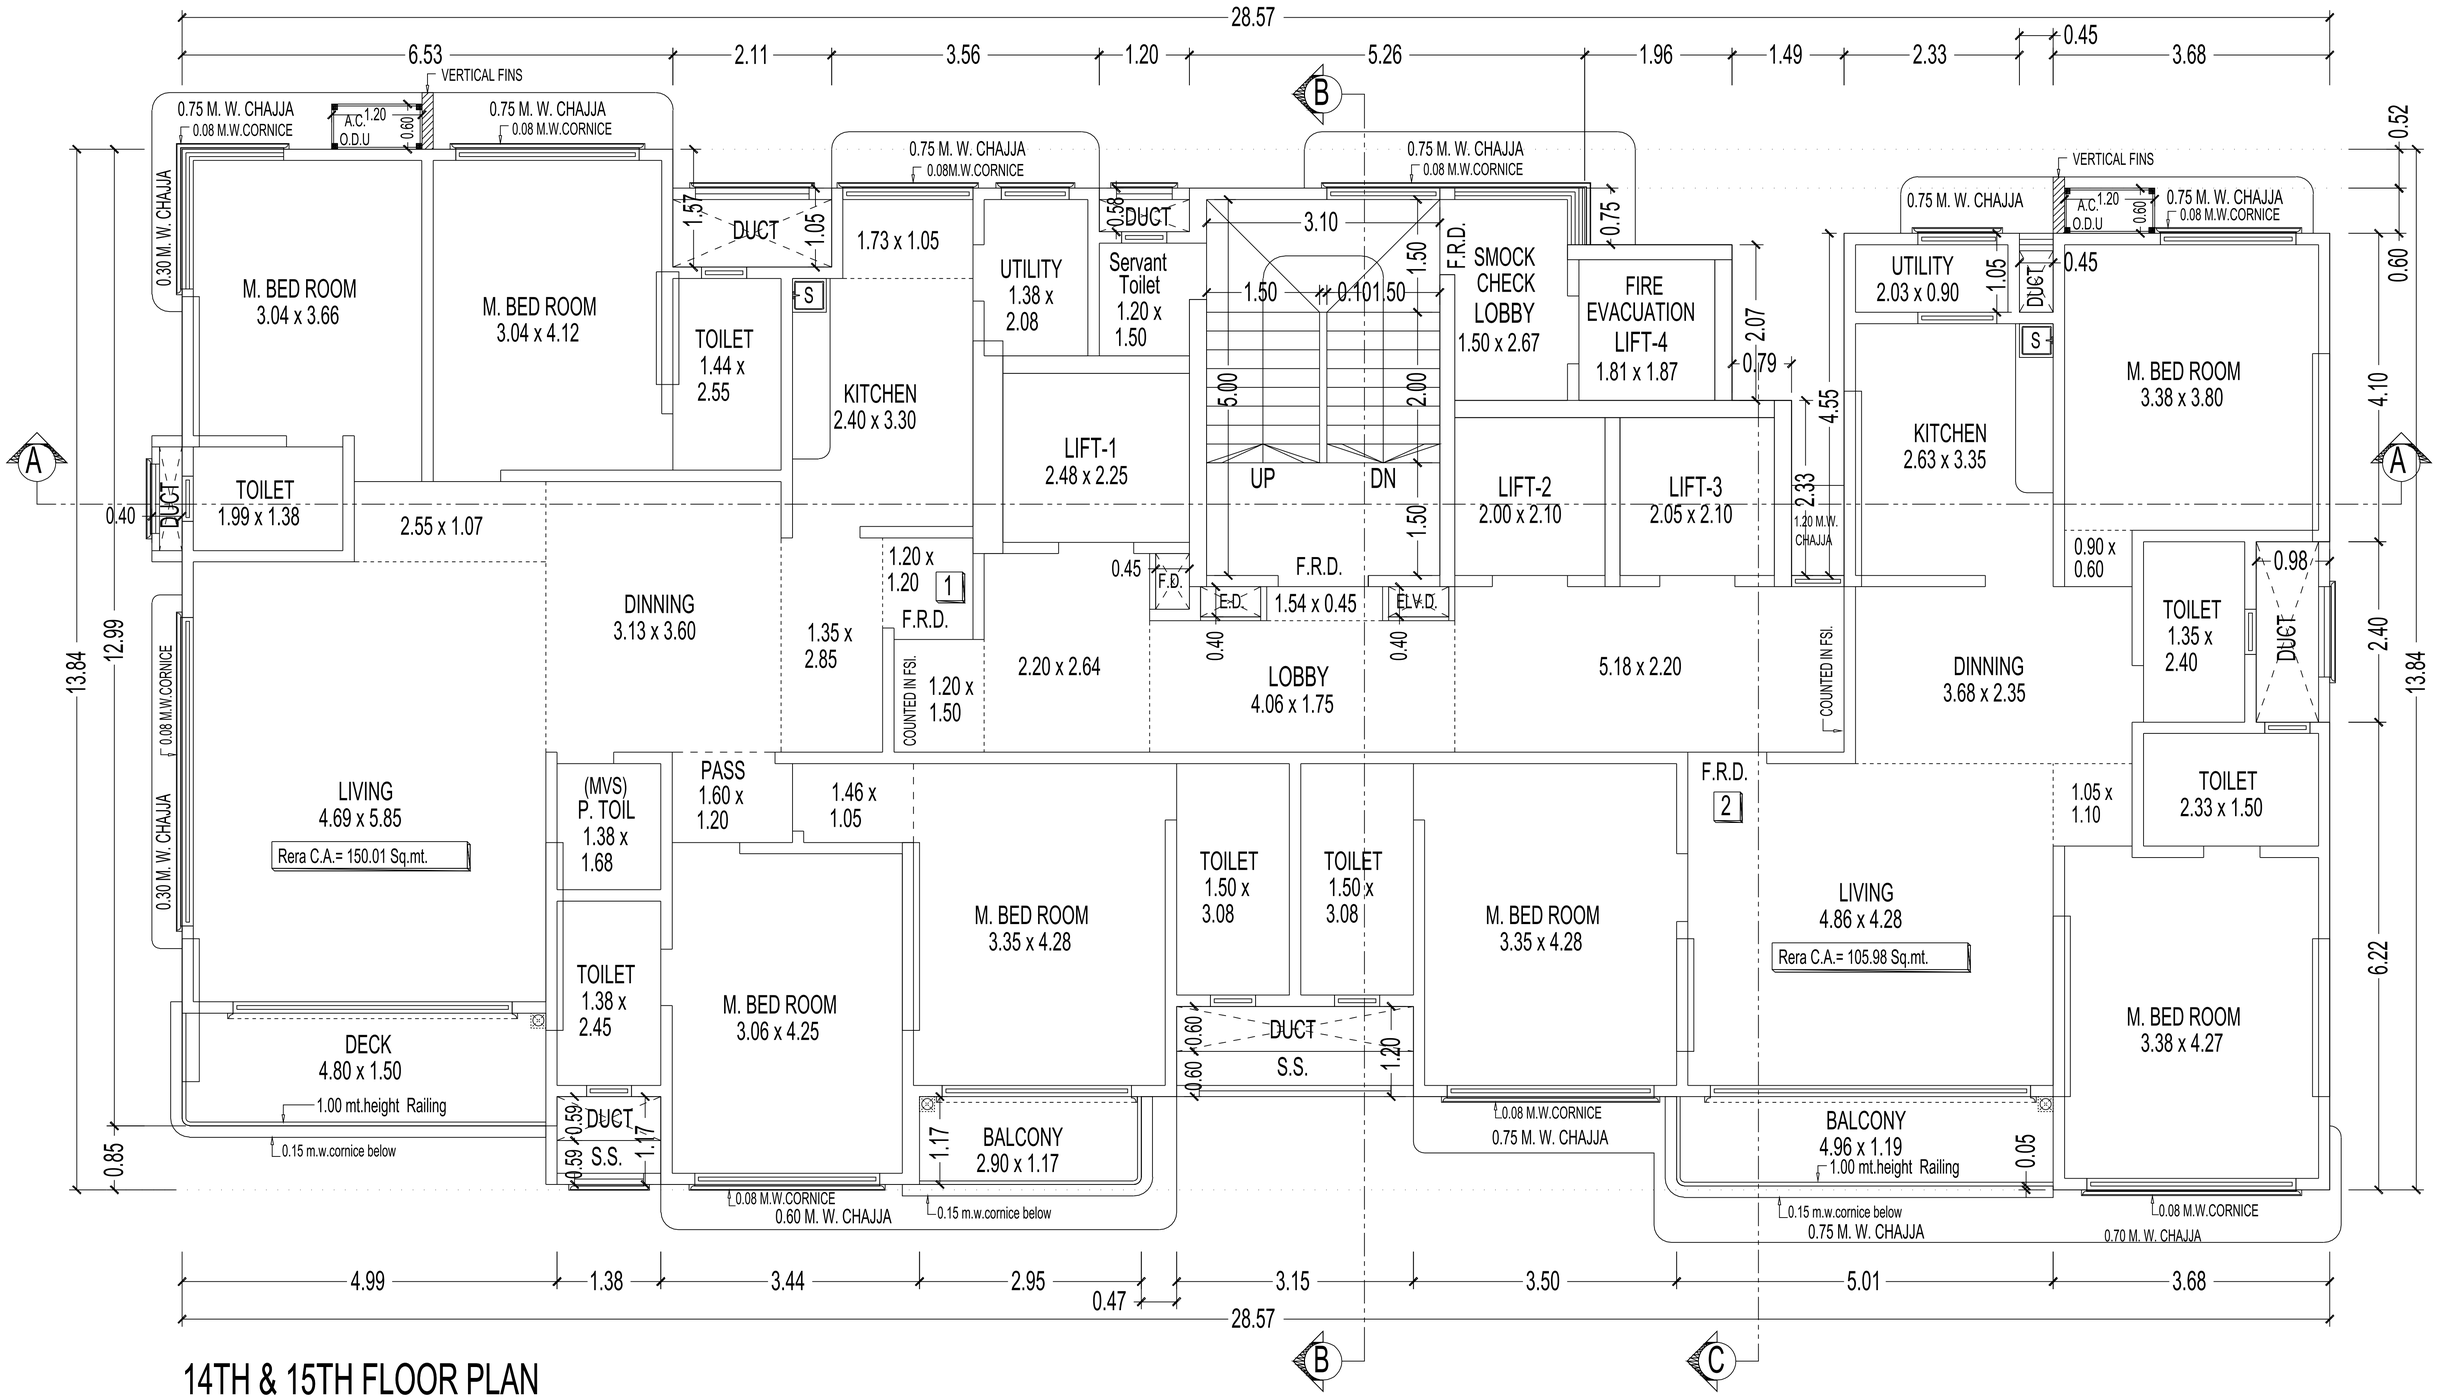

14TH & 15TH FLOOR PLAN

SCALE - 1:100

28.57

6.53 | 2.11 | 3.56 | 1.20 | 5.26 | 1.96 | 1.49 | 2.33 | 0.45 | 3.68

VERTICAL FINS

0.75 M. W. CHAJJA
0.08 M.W.CORNICE
A.C. O.D.U 1.20 x 0.60

Terrace line above

0.30 M. W. CHAJJA

M. BED ROOM 3.04 x 3.66

M. BED ROOM 3.04 x 4.12

TOILET 1.44 x 2.55

DUCT 1.57 x 1.05

1.73 x 1.05

KITCHEN 2.40 x 3.30

UTILITY 1.38 x 2.08

DUCT 0.58

Servant Toilet 1.20 x 1.50

3.10

1.50 | 0.10 | 1.50

5.00 | 2.00

UP | DN

LIFT-1 2.48 x 2.25

F.R.D.

SMOCK CHECK LOBBY 1.50 x 2.67

FIRE EVACUATION LIFT-4 1.81 x 1.87

0.75 | 2.07 | 0.79

LIFT-2 2.00 x 2.10

LIFT-3 2.05 x 2.10

4.55 | 2.33

1.20 M.W. CHAJJA

TOILET 1.99 x 1.38

DUCT 0.40

2.55 x 1.07

DINNING 3.13 x 3.60

1.35 x 2.85

1.20 x 1.20 (1) F.R.D.

COUNTED IN FSI.

1.20 x 1.50

2.20 x 2.64

0.45 F.D. E.D. 1.54 x 0.45 ELV.D.

0.40 | 0.40

LOBBY 4.06 x 1.75

1.50

5.18 x 2.20

COUNTED IN FSI.

0.75 M. W. CHAJJA
VERTICAL FINS
A.C. O.D.U 1.20 x 0.60
0.75 M. W. CHAJJA
0.08 M.W.CORNICE

UTILITY 2.03 x 0.90

1.05 | DUCT | S

0.45

M. BED ROOM 3.38 x 3.80

KITCHEN 2.63 x 3.35

0.90 x 0.60

TOILET 1.35 x 2.40

0.98 | DUCT

DINNING 3.68 x 2.35

0.52 | 0.60 | 4.10 | 2.40 | 13.84

0.08 M.W.CORNICE

LIVING 4.69 x 5.85

Rera C.A.= 150.01 Sq.mt.

(MVS) P. TOIL 1.38 x 1.68

PASS 1.60 x 1.20

1.46 x 1.05

TOILET 1.38 x 2.45

M. BED ROOM 3.06 x 4.25

M. BED ROOM 3.35 x 4.28

TOILET 1.50 x 3.08

TOILET 1.50 x 3.08

M. BED ROOM 3.35 x 4.28

F.R.D. 2

LIVING 4.86 x 4.28

Rera C.A.= 106.61 Sq.mt.

1.05 x 1.10

TOILET 2.33 x 1.50

M. BED ROOM 3.38 x 4.27

Terrace line above

DECK 4.80 x 1.50

1.00 mt.height Railing

0.15 m.w.cornice below

0.85

DUCT 0.59 x 1.17

S.S. 0.59 x 1.17

0.08 M.W.CORNICE
0.60 M. W. CHAJJA

BALCONY 2.90 x 1.17

0.15 m.w.cornice below

DUCT 0.60 x 1.20

S.S. 0.60

0.08 M.W.CORNICE
0.75 M. W. CHAJJA

BALCONY 4.96 x 1.19

1.00 mt.height Railing

0.05

0.15 m.w.cornice below
0.75 M. W. CHAJJA

0.70 M. W. CHAJJA
0.08 M.W.CORNICE

6.22

Terrace line above

4.99 | 1.38 | 3.44 | 2.95 | 0.27 | 3.35 | 3.50 | 5.01 | 3.68

28.57

16TH FLOOR PLAN

SCALE - 1:100