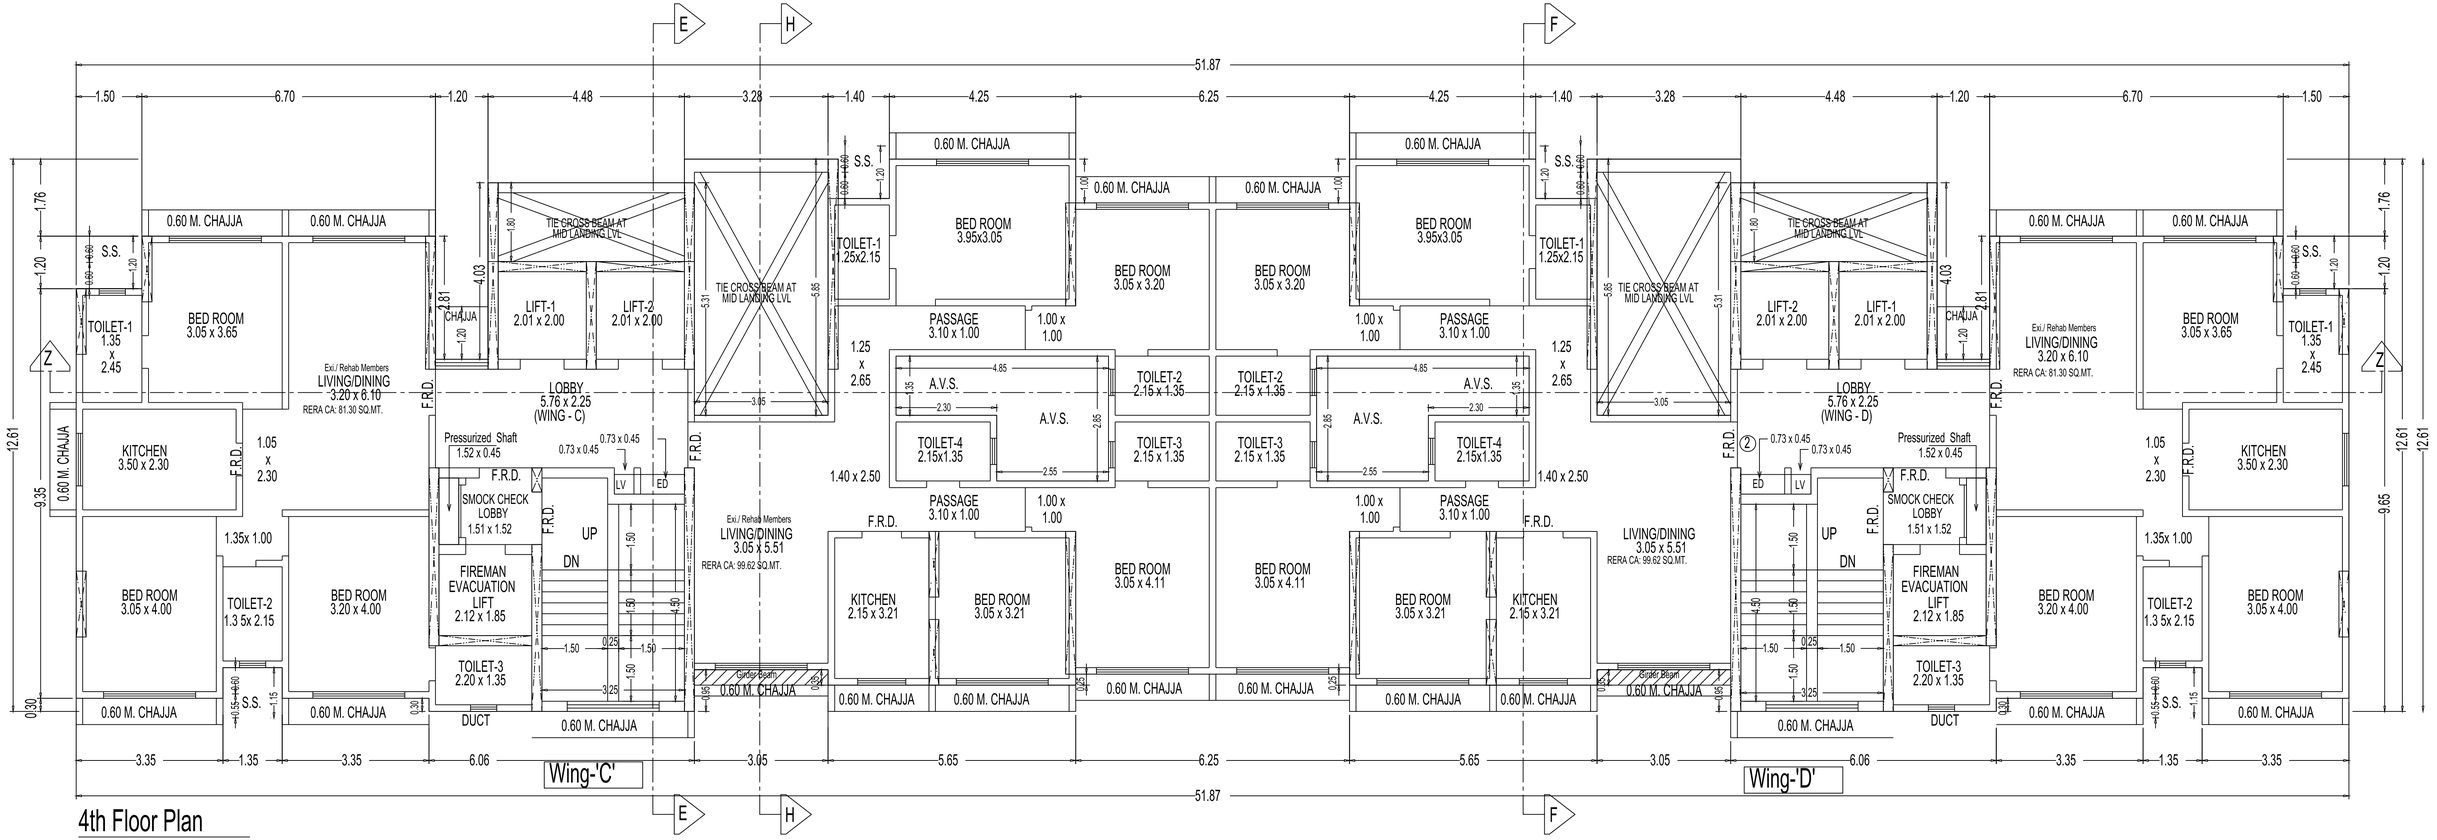
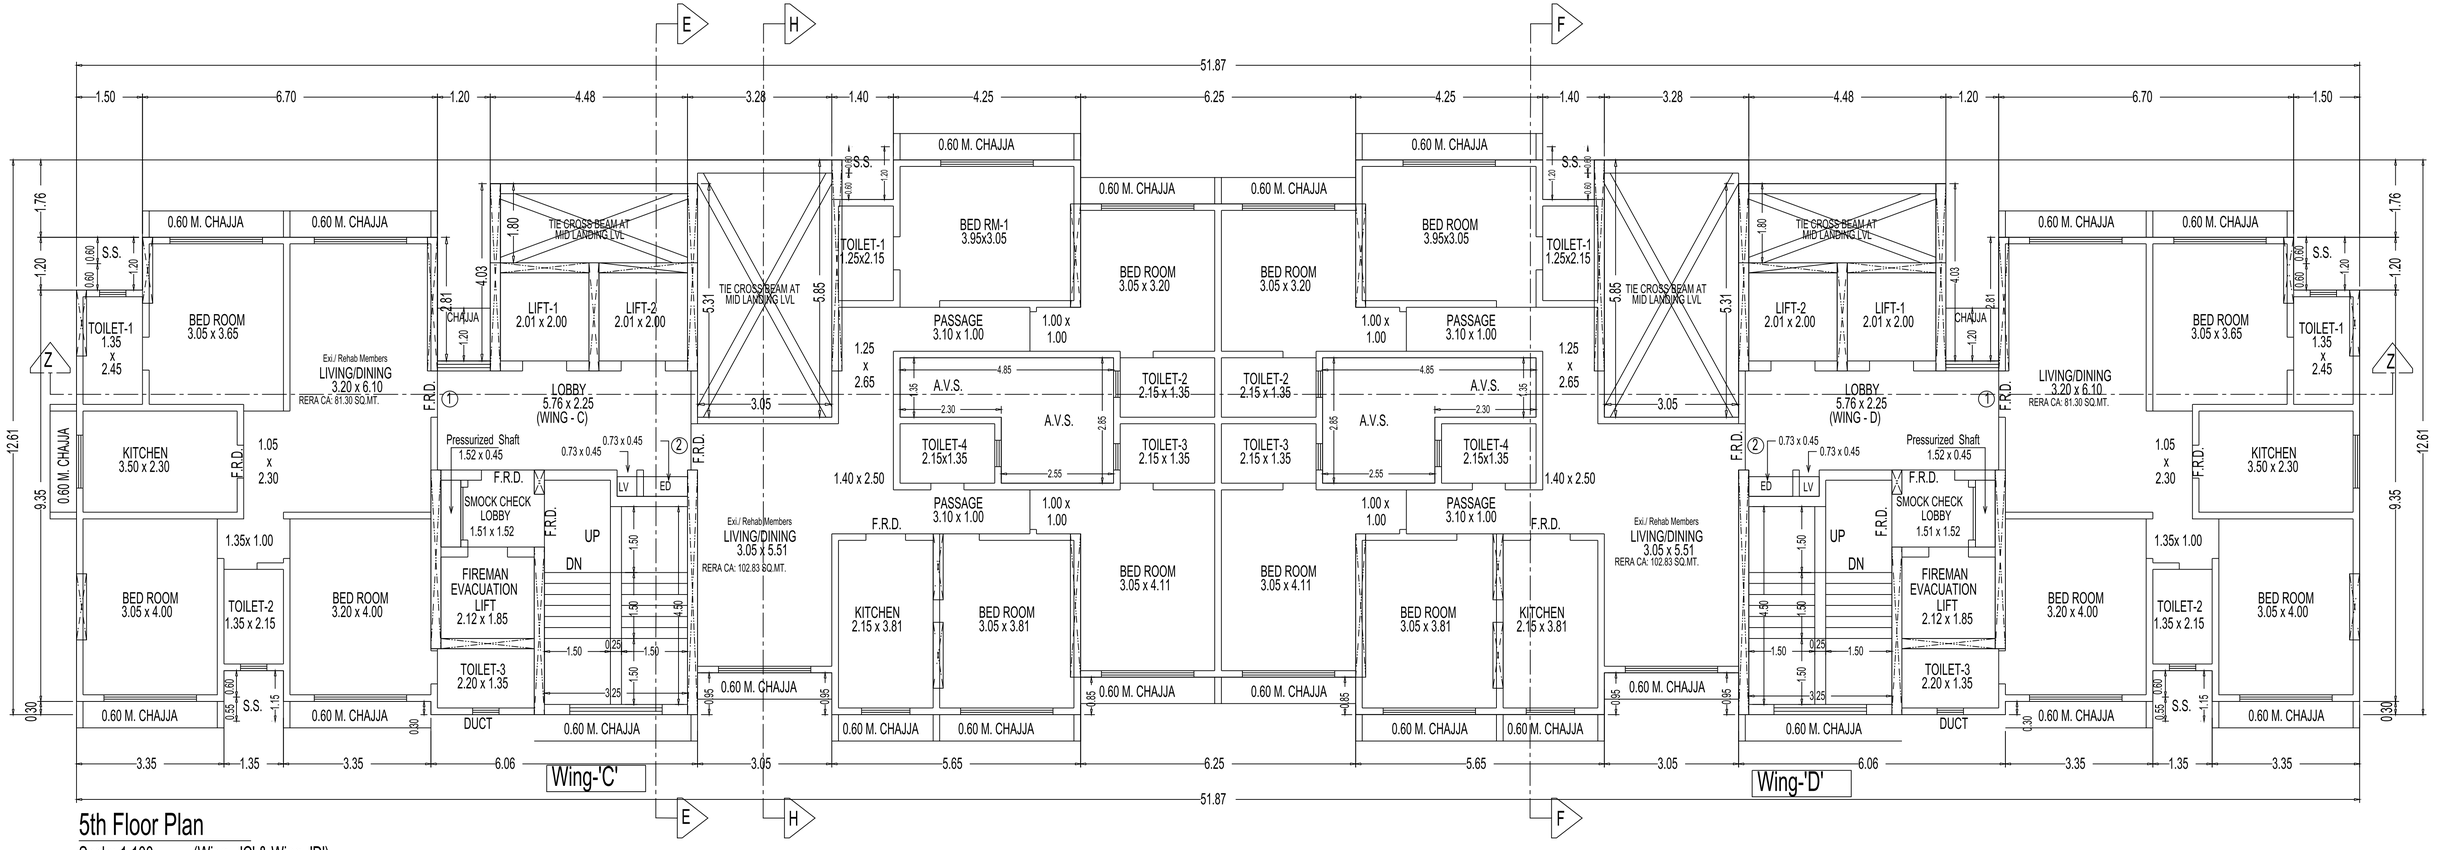



# 4th Floor Plan

Scale: 1:100 (Wing - 'C' & Wing- 'D')



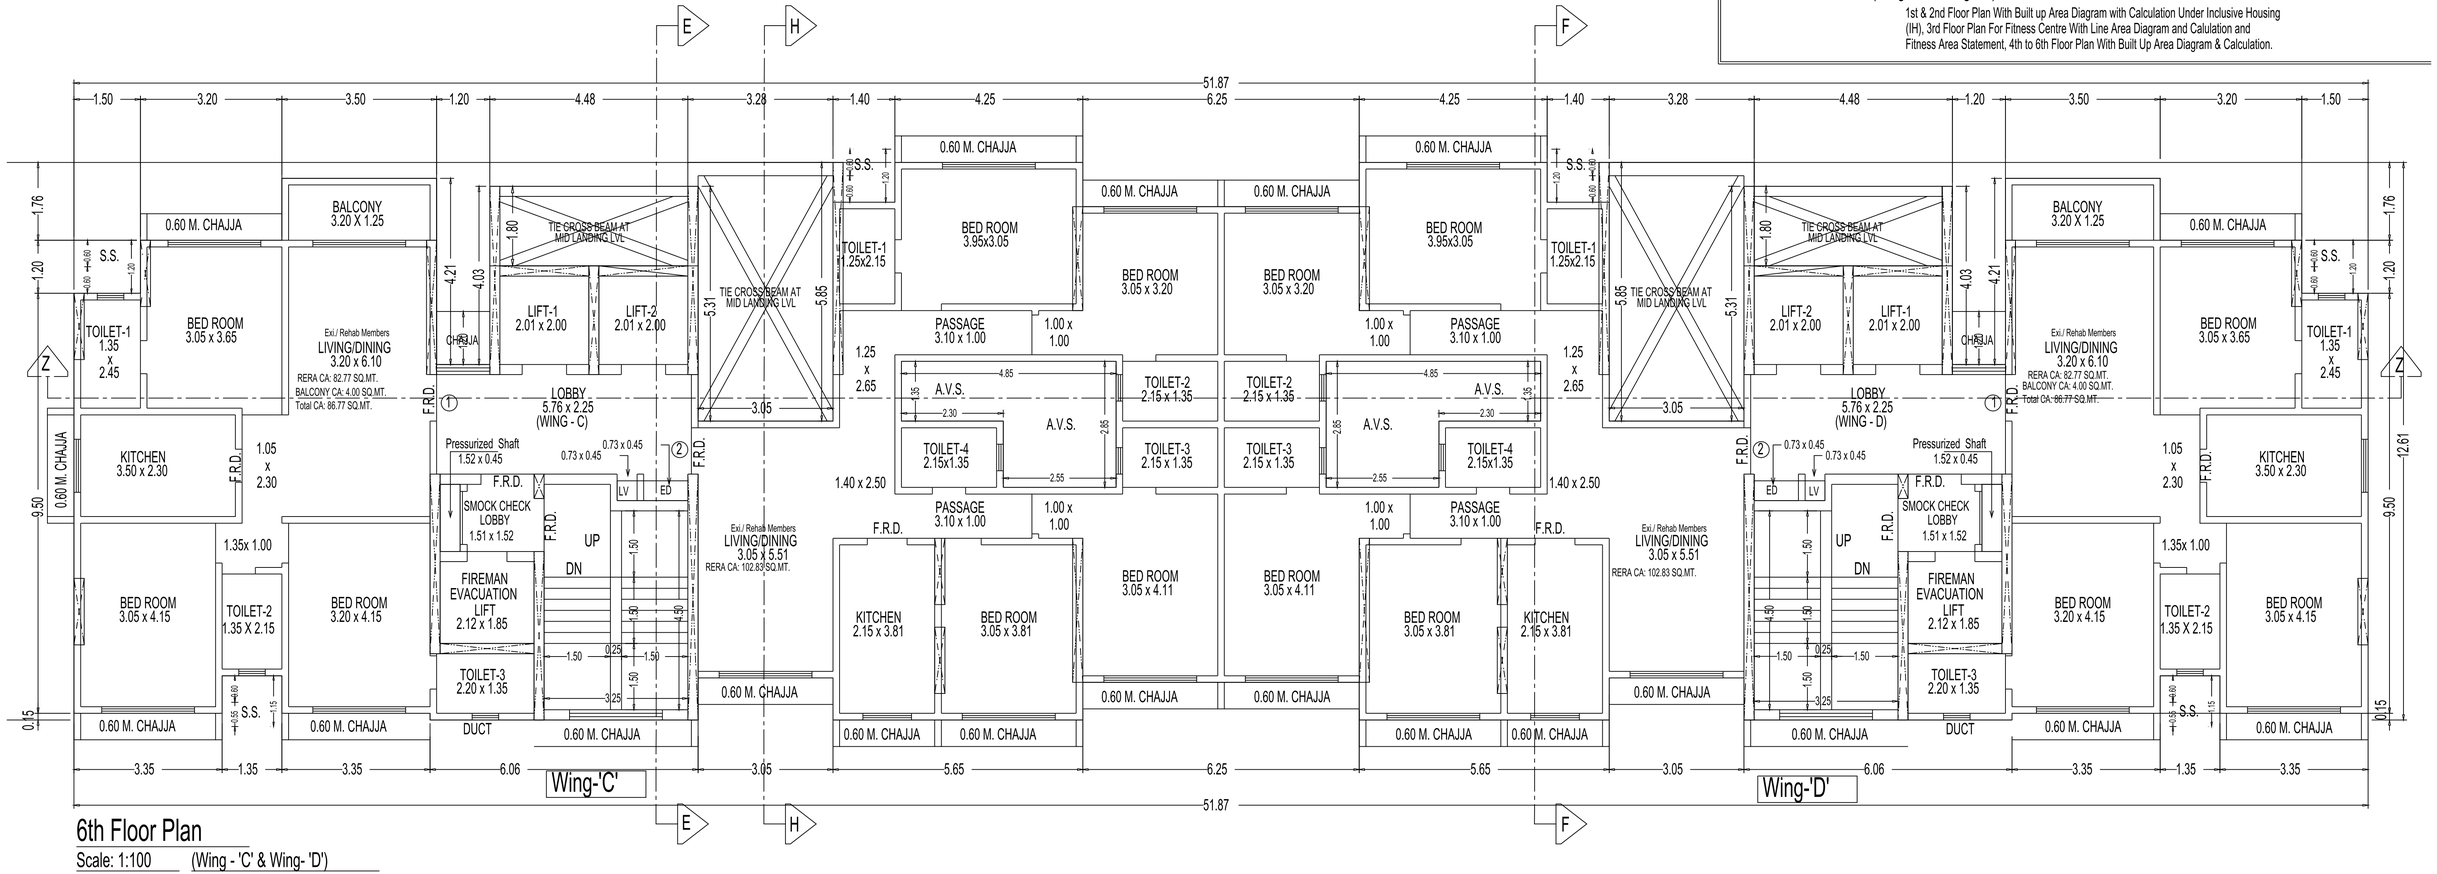

## 5th Floor Plan

Scale: 1:100 (Wing - 'C' & Wing- 'D')

File No. :- P-25364/2025/(325/A/2 AND Other) / P/N Ward / VALNAI | SHEET NO. :- 5/8


CONTENTS OF SHEET : (Wing- 'C' & Wing- 'D')

1st & 2nd Floor Plan With Built up Area Diagram with Calculation Under Inclusive Housing (IH), 3rd Floor Plan For Fitness Centre With Line Area Diagram and Calulation and Fitness Area Statement, 4th to 6th Floor Plan With Built Up Area Diagram & Calculation.





## 6th Floor Plan

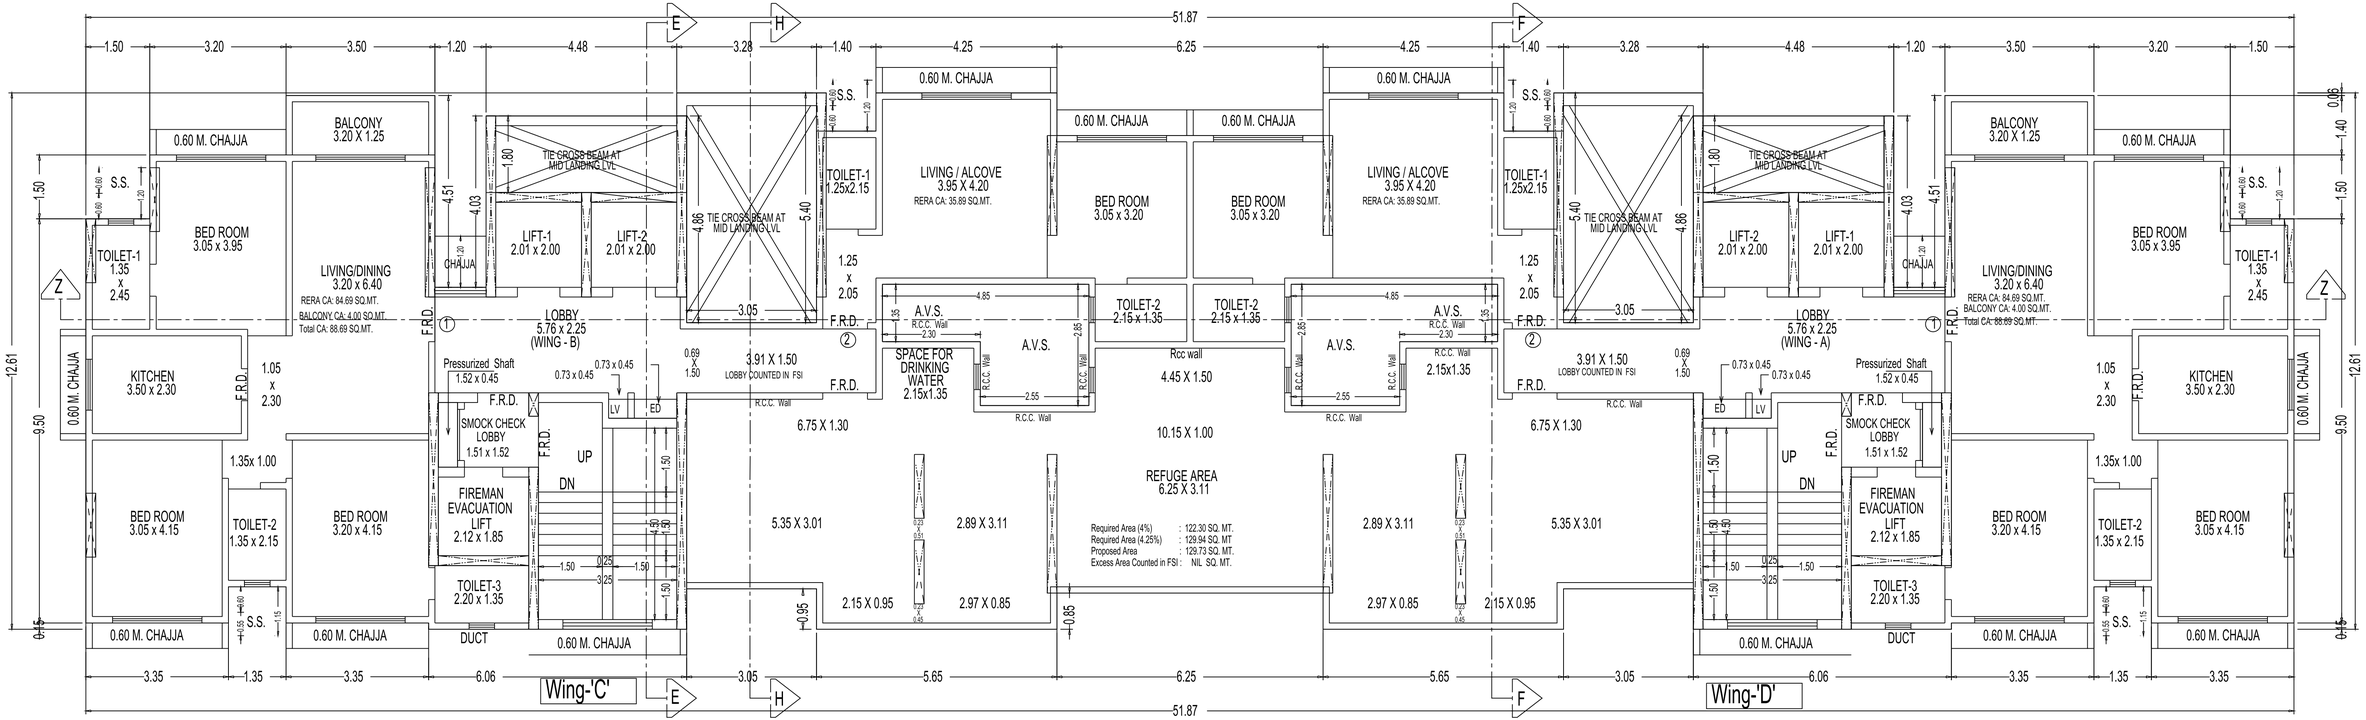
Scale: 1:100 (Wing - 'C' & Wing- 'D')




7th (Refuge) Floor Plan

| | | | | | | | | |
|---|---|---|---|---|---|---|---|---|
| R5 | 5.65 | X | 0.85 | X | 2 NOS | = | 9.61 | SQ.MT. |
| R6 | 1.40 | X | 4.71 | X | 2 NOS | = | 13.19 | SQ.MT. |
| TOTAL REFUGE AREA | | | | | | = | 129.73 | SQ.MT. |

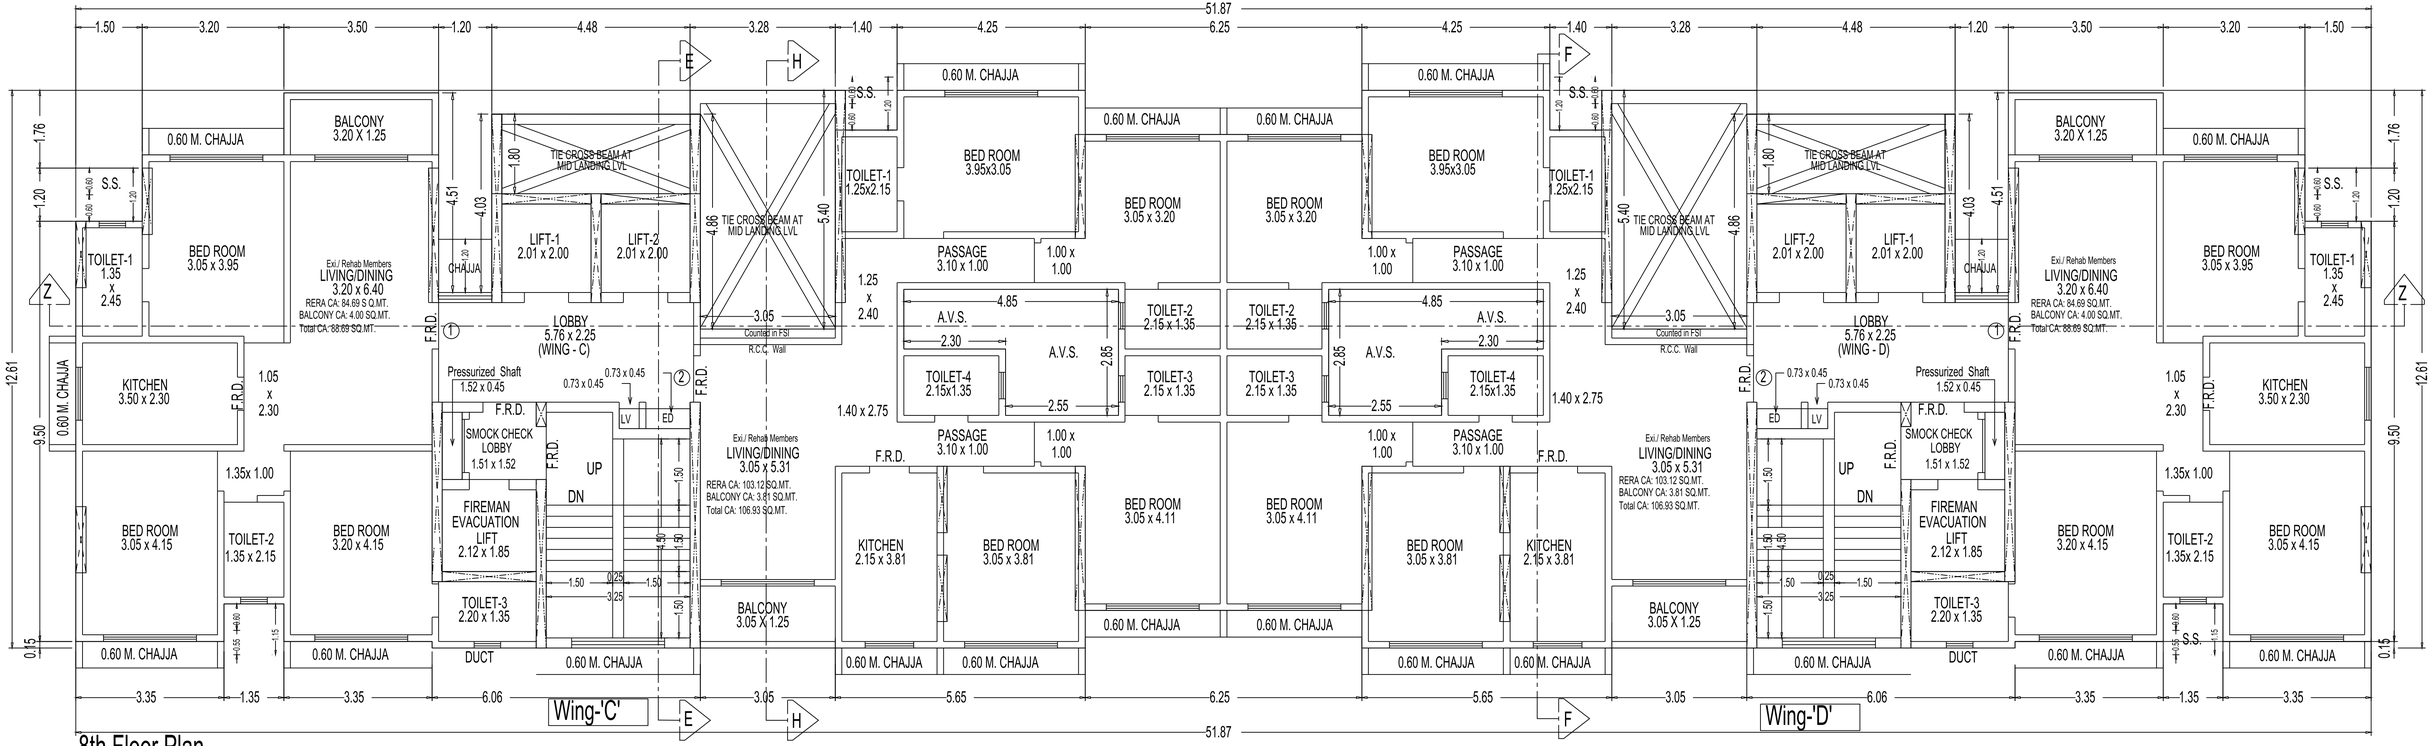


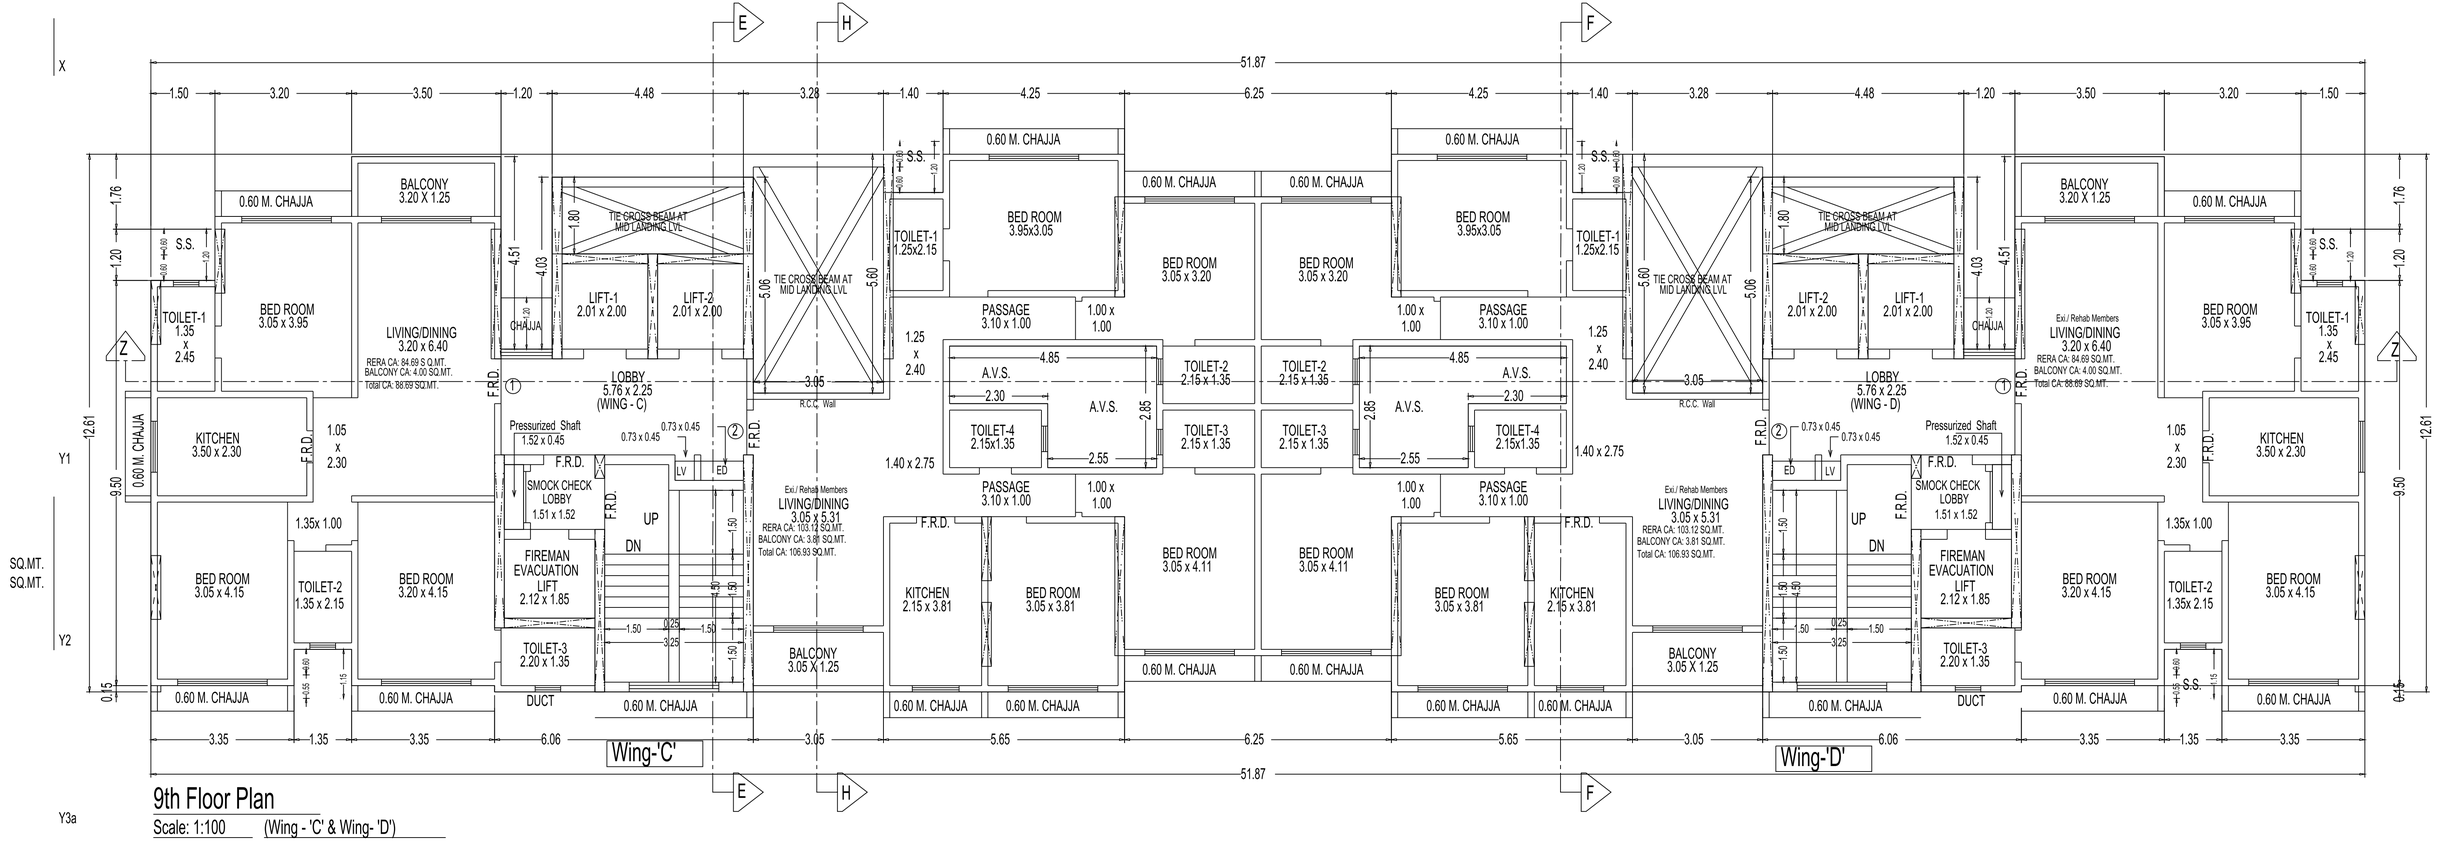


# 9th Floor Plan


Scale: 1:100 (Wing - 'C' & Wing- 'D')

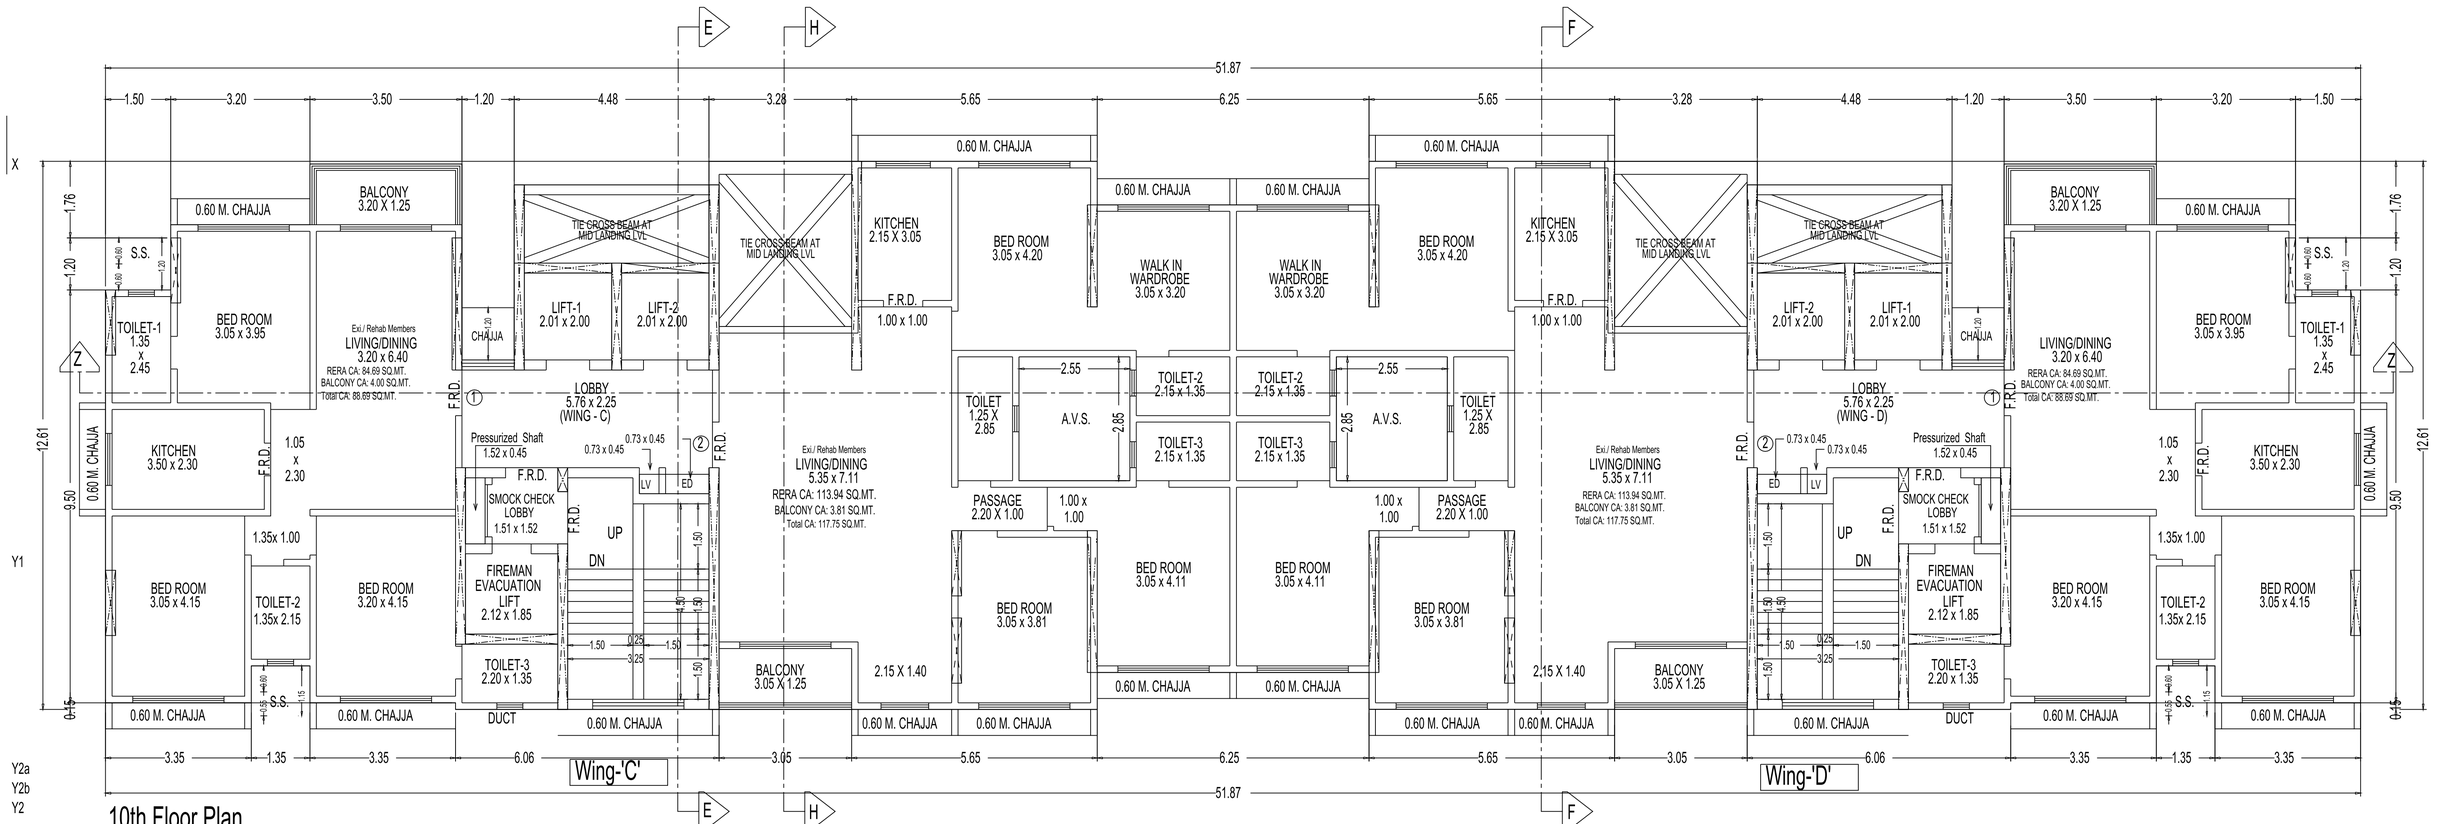Scale: 1:100 (Wing - 'C' & Wing- 'D')




File No. :-

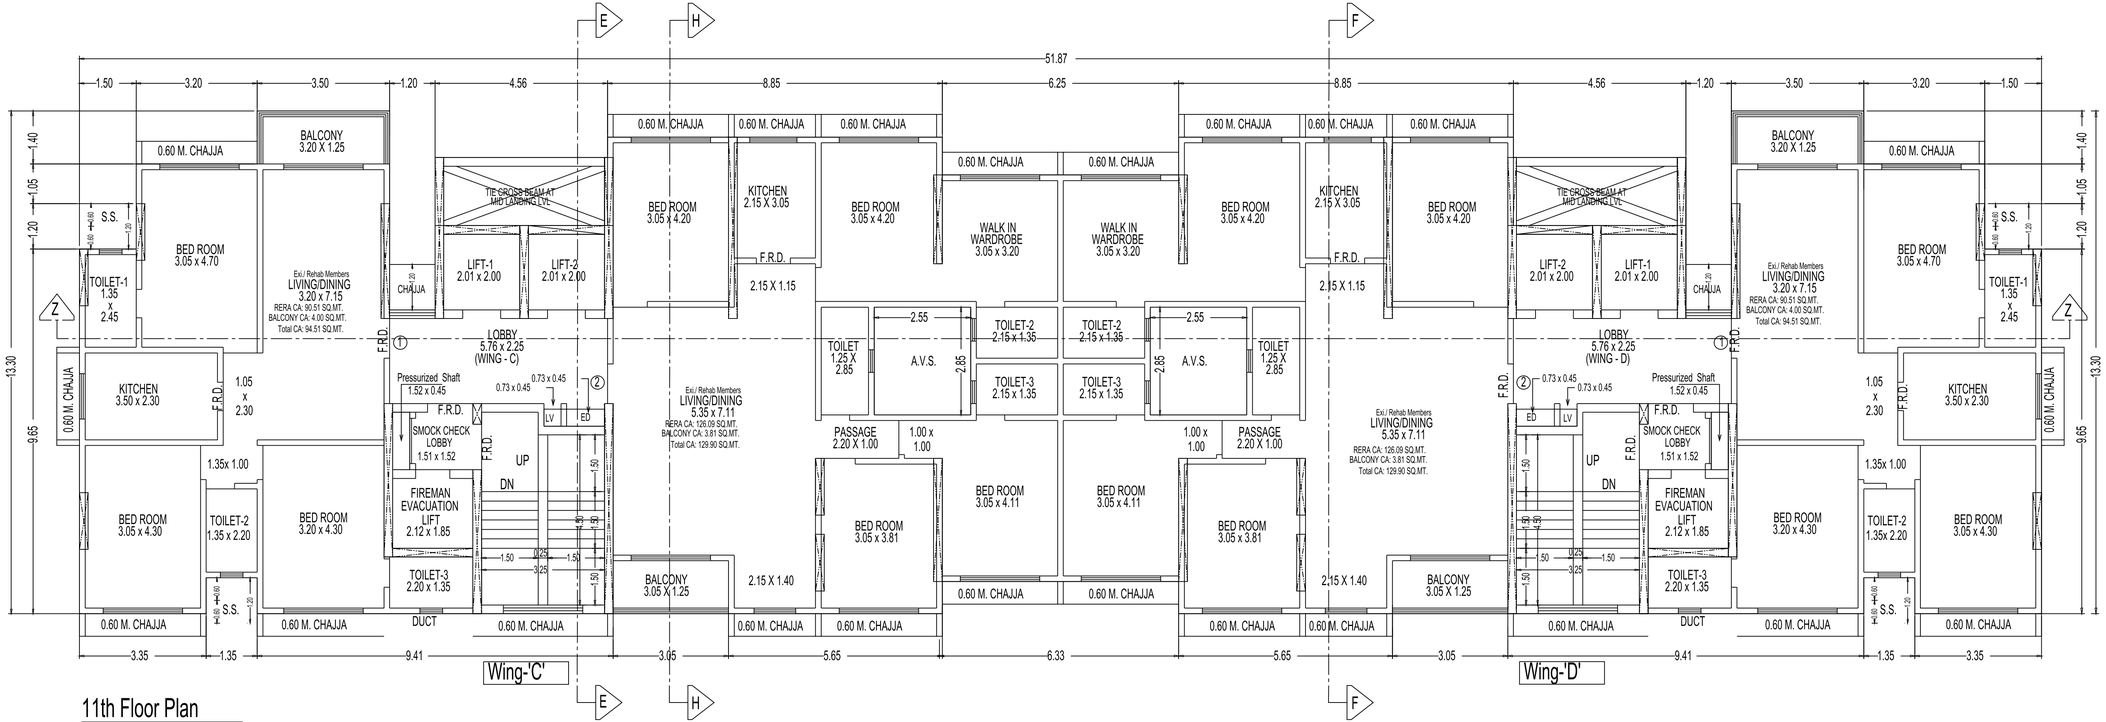CONTENTS OF SHEET : (Wing- 'C' & Wing- 'D')





## 11th Floor Plan

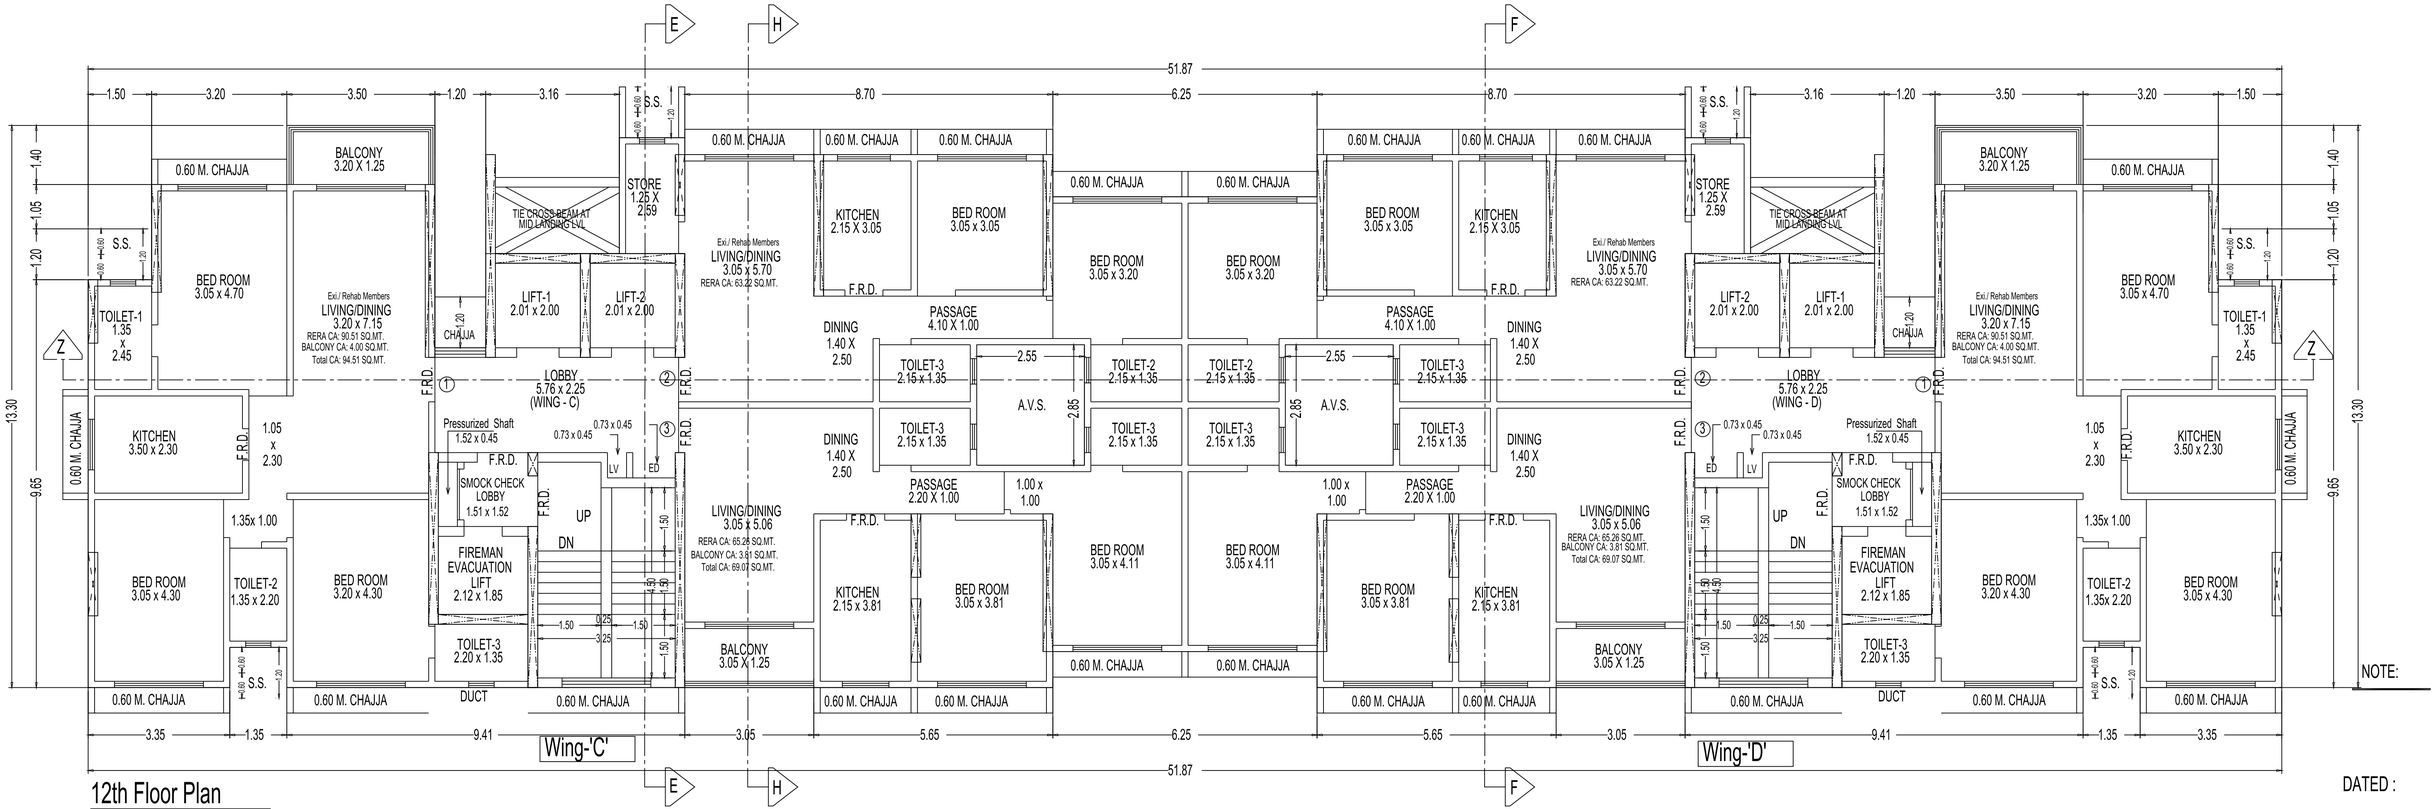Scale: 1:100 (Wing - 'C' & Wing- 'D')





## 12th Floor Plan

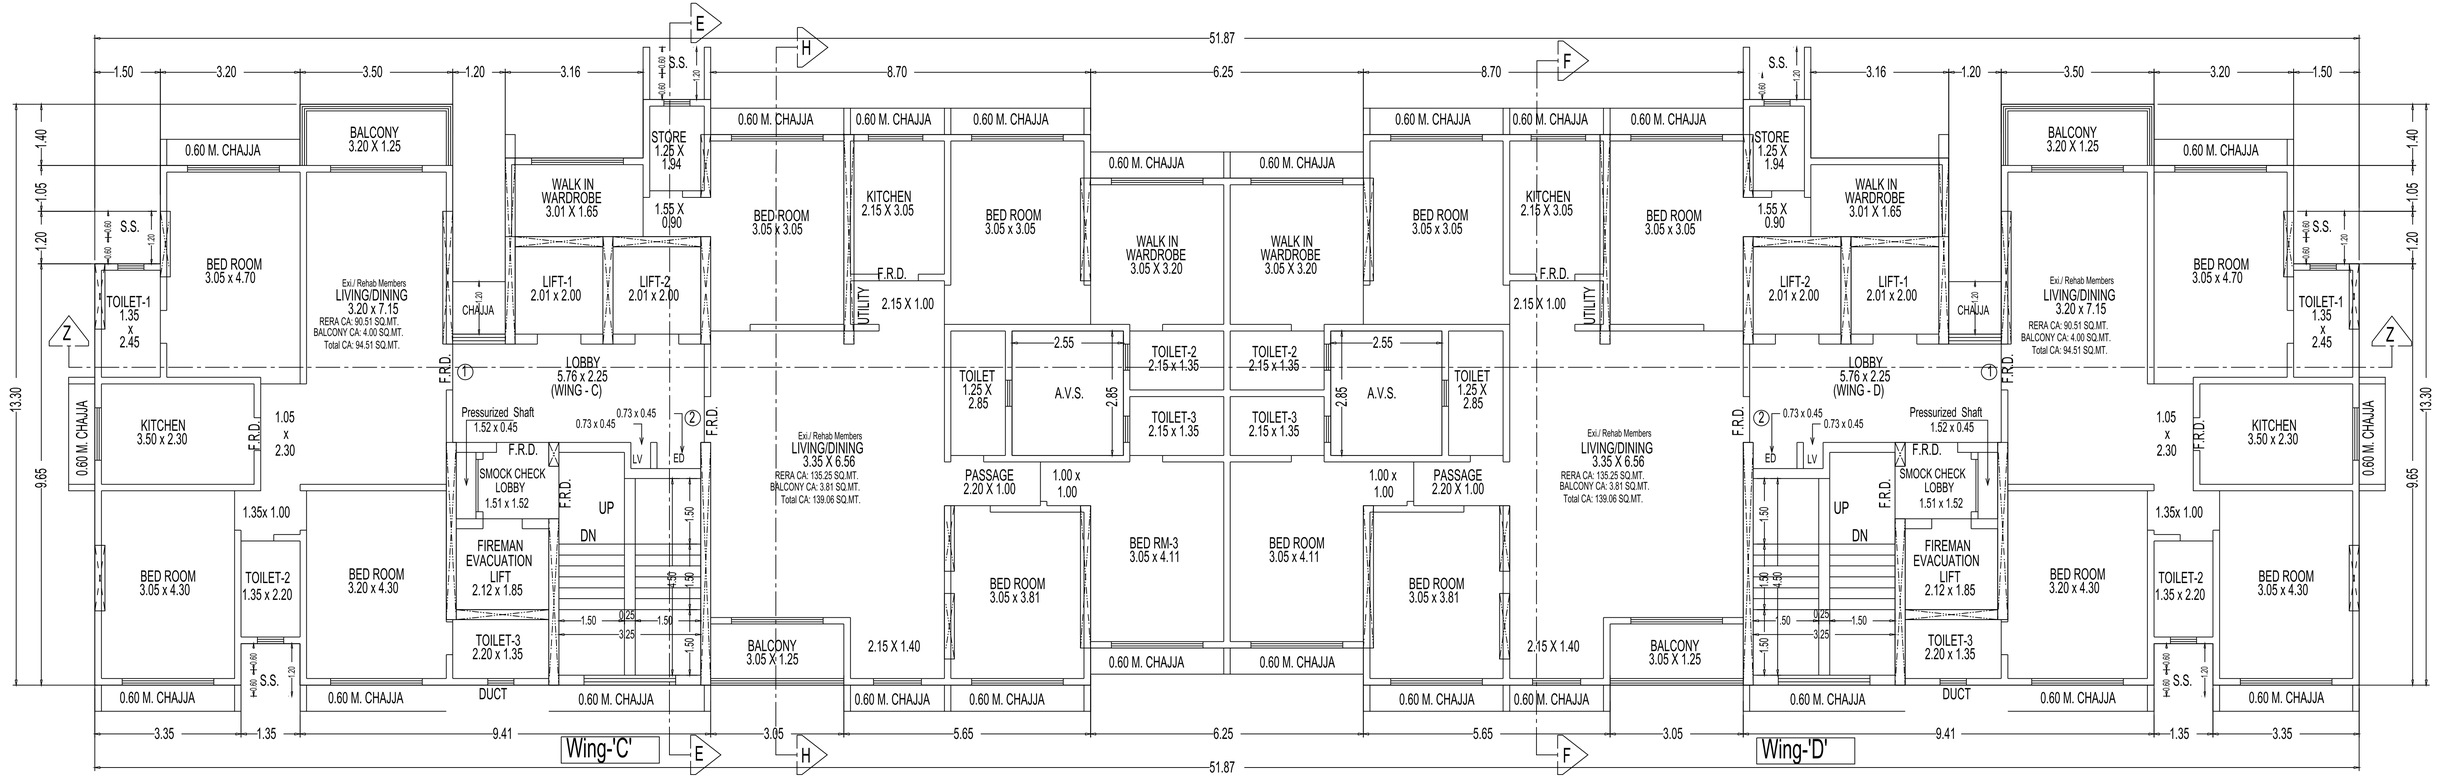Scale: 1:100 (Wing - 'C' & Wing- 'D')





13th Floor Plan

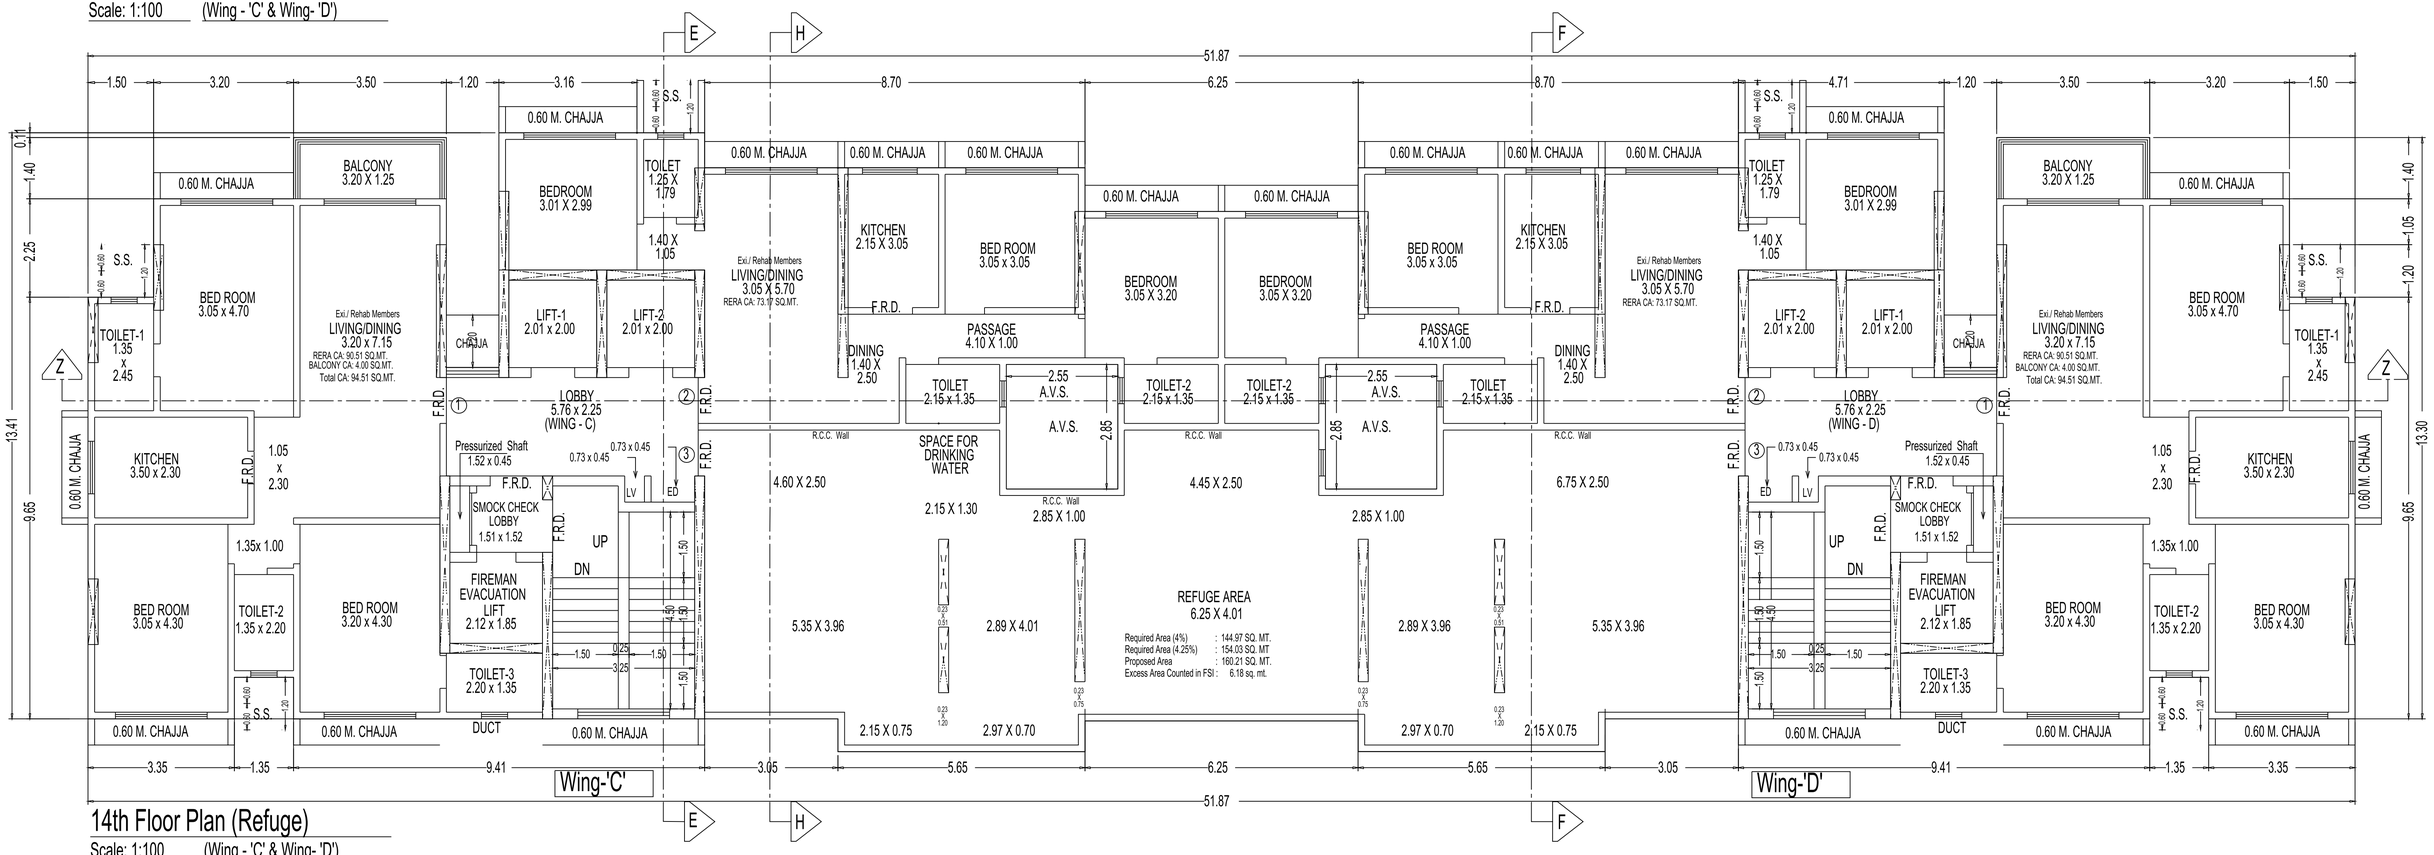Scale: 1:100 (Wing - 'C' & Wing- 'D')





14th Floor Plan (Refuge)

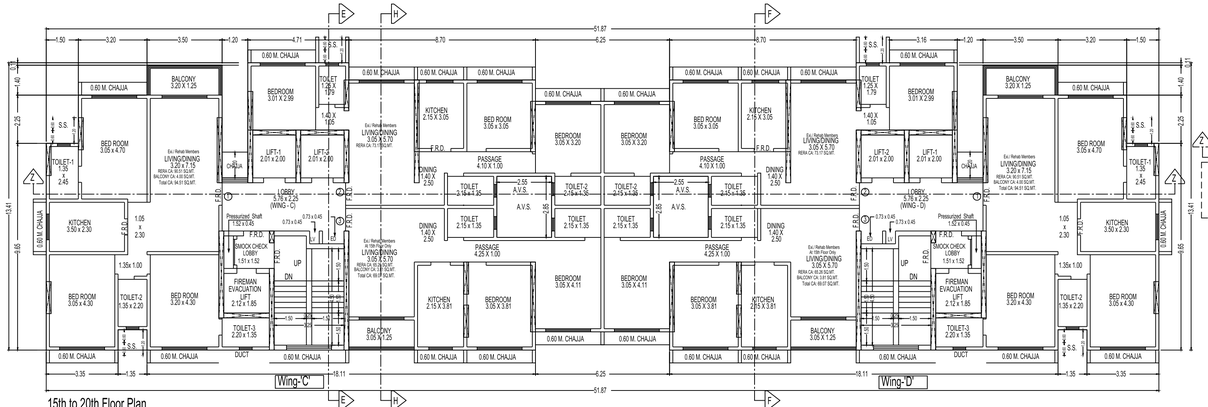Scale: 1:100 (Wing - 'C' & Wing- 'D')





15th to 20th Floor Plan

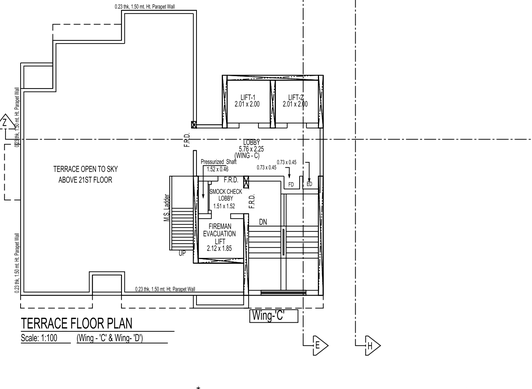Scale: 1:100 (Wing - 'C' & Wing- 'D')




TERRACE FLOOR PLAN

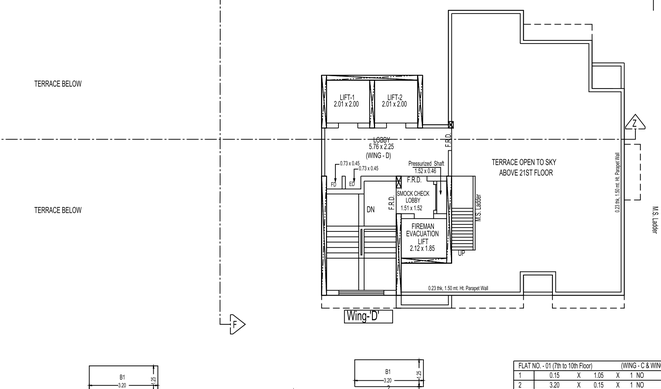Scale: 1:100 (Wing - 'C' & Wing- 'D')





File No. :-

| FLAT NO. - 01 | (4th & 5th Floor) | (WING - C & WING - D) | 4 NOS. |
|---|---|---|---|
| 1 | 0.15 X 1.05 X 1 NO | + | 0.16 = 992 MT. |

| FLAT NO. - 01 (7th to 10th Floor) | | | | (WING - C & WING - D) |
|---|---|---|---|---|
| 1 | 0.15 | X | 1.05 | X 1 NO |
| 2 | 3.20 | X | 0.15 | X 1 NO |
| 3 | 6.40 | X | 1.50 | X 1 NO |

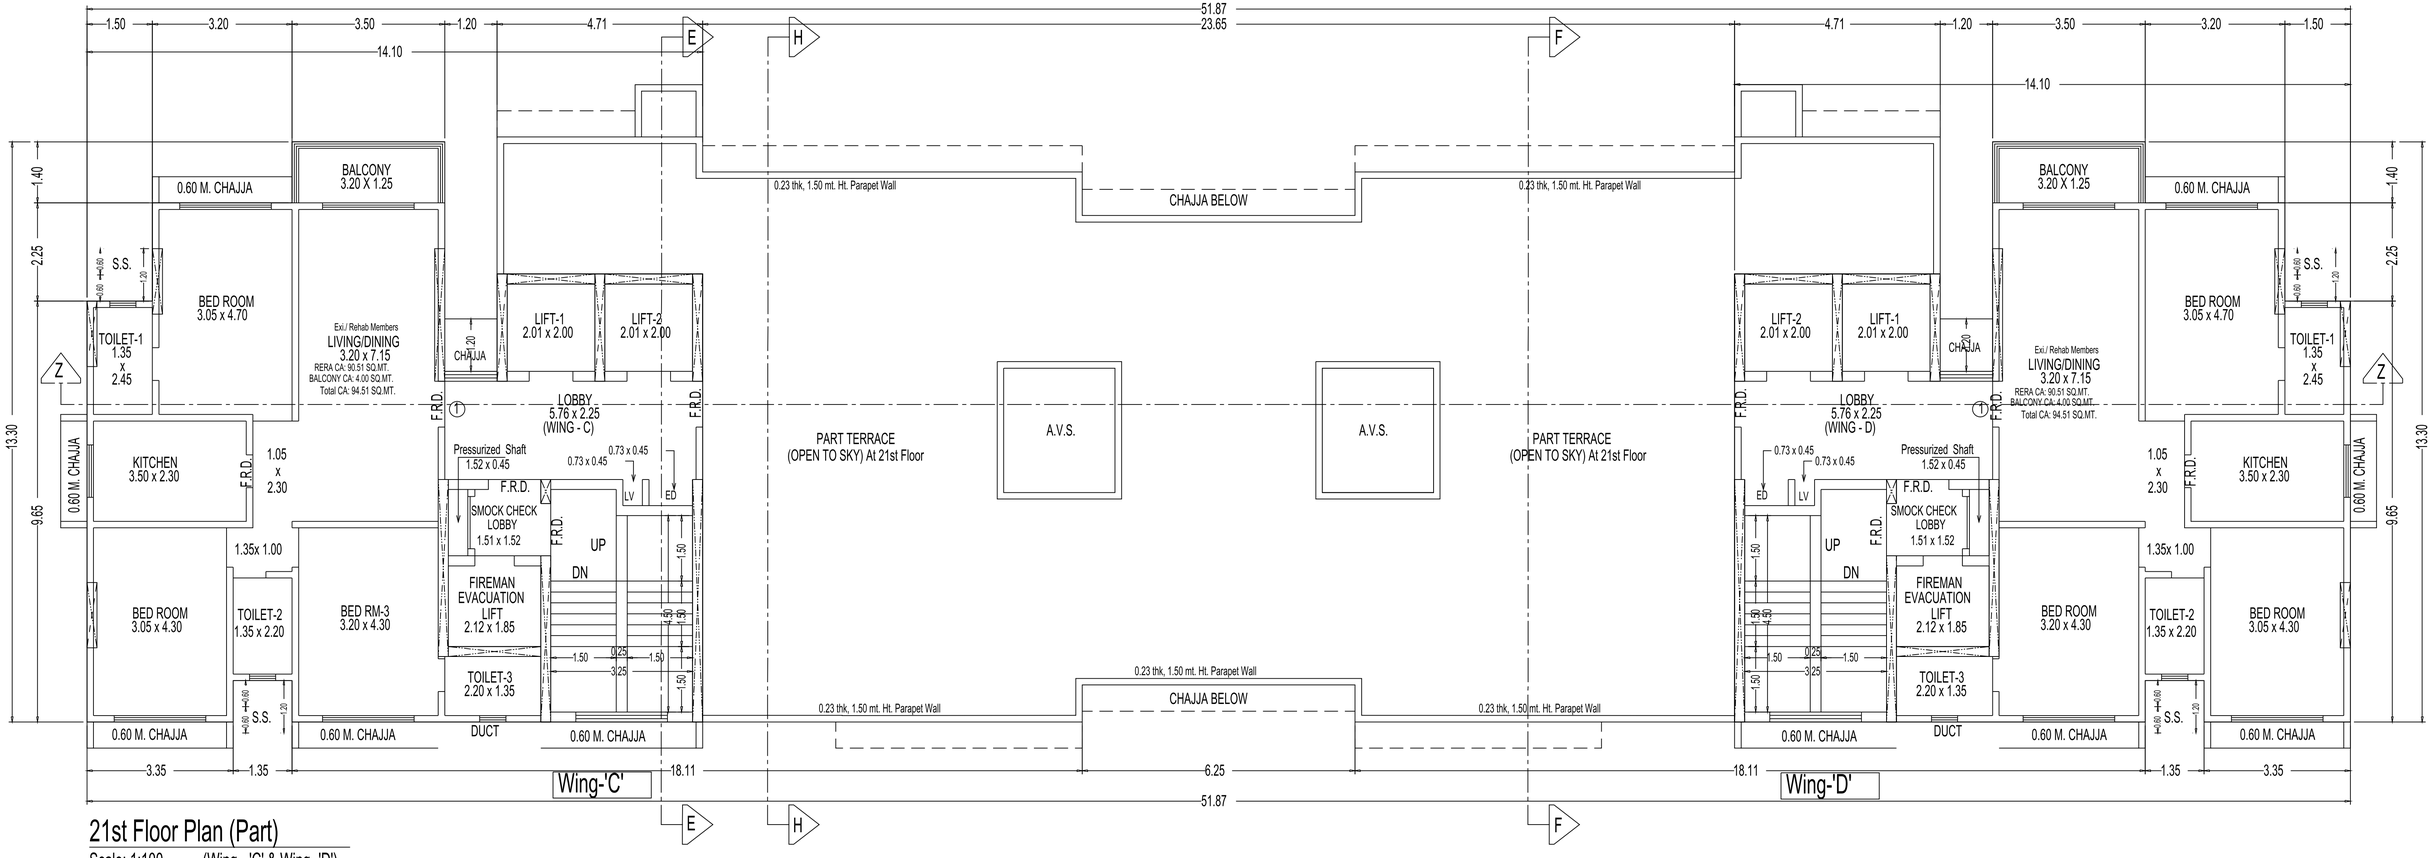Scale: 1:100 (Wing - 'C' & Wing- 'D')




## 21st Floor Plan (Part)

Scale: 1:100 (Wing - 'C' & Wing- 'D')