
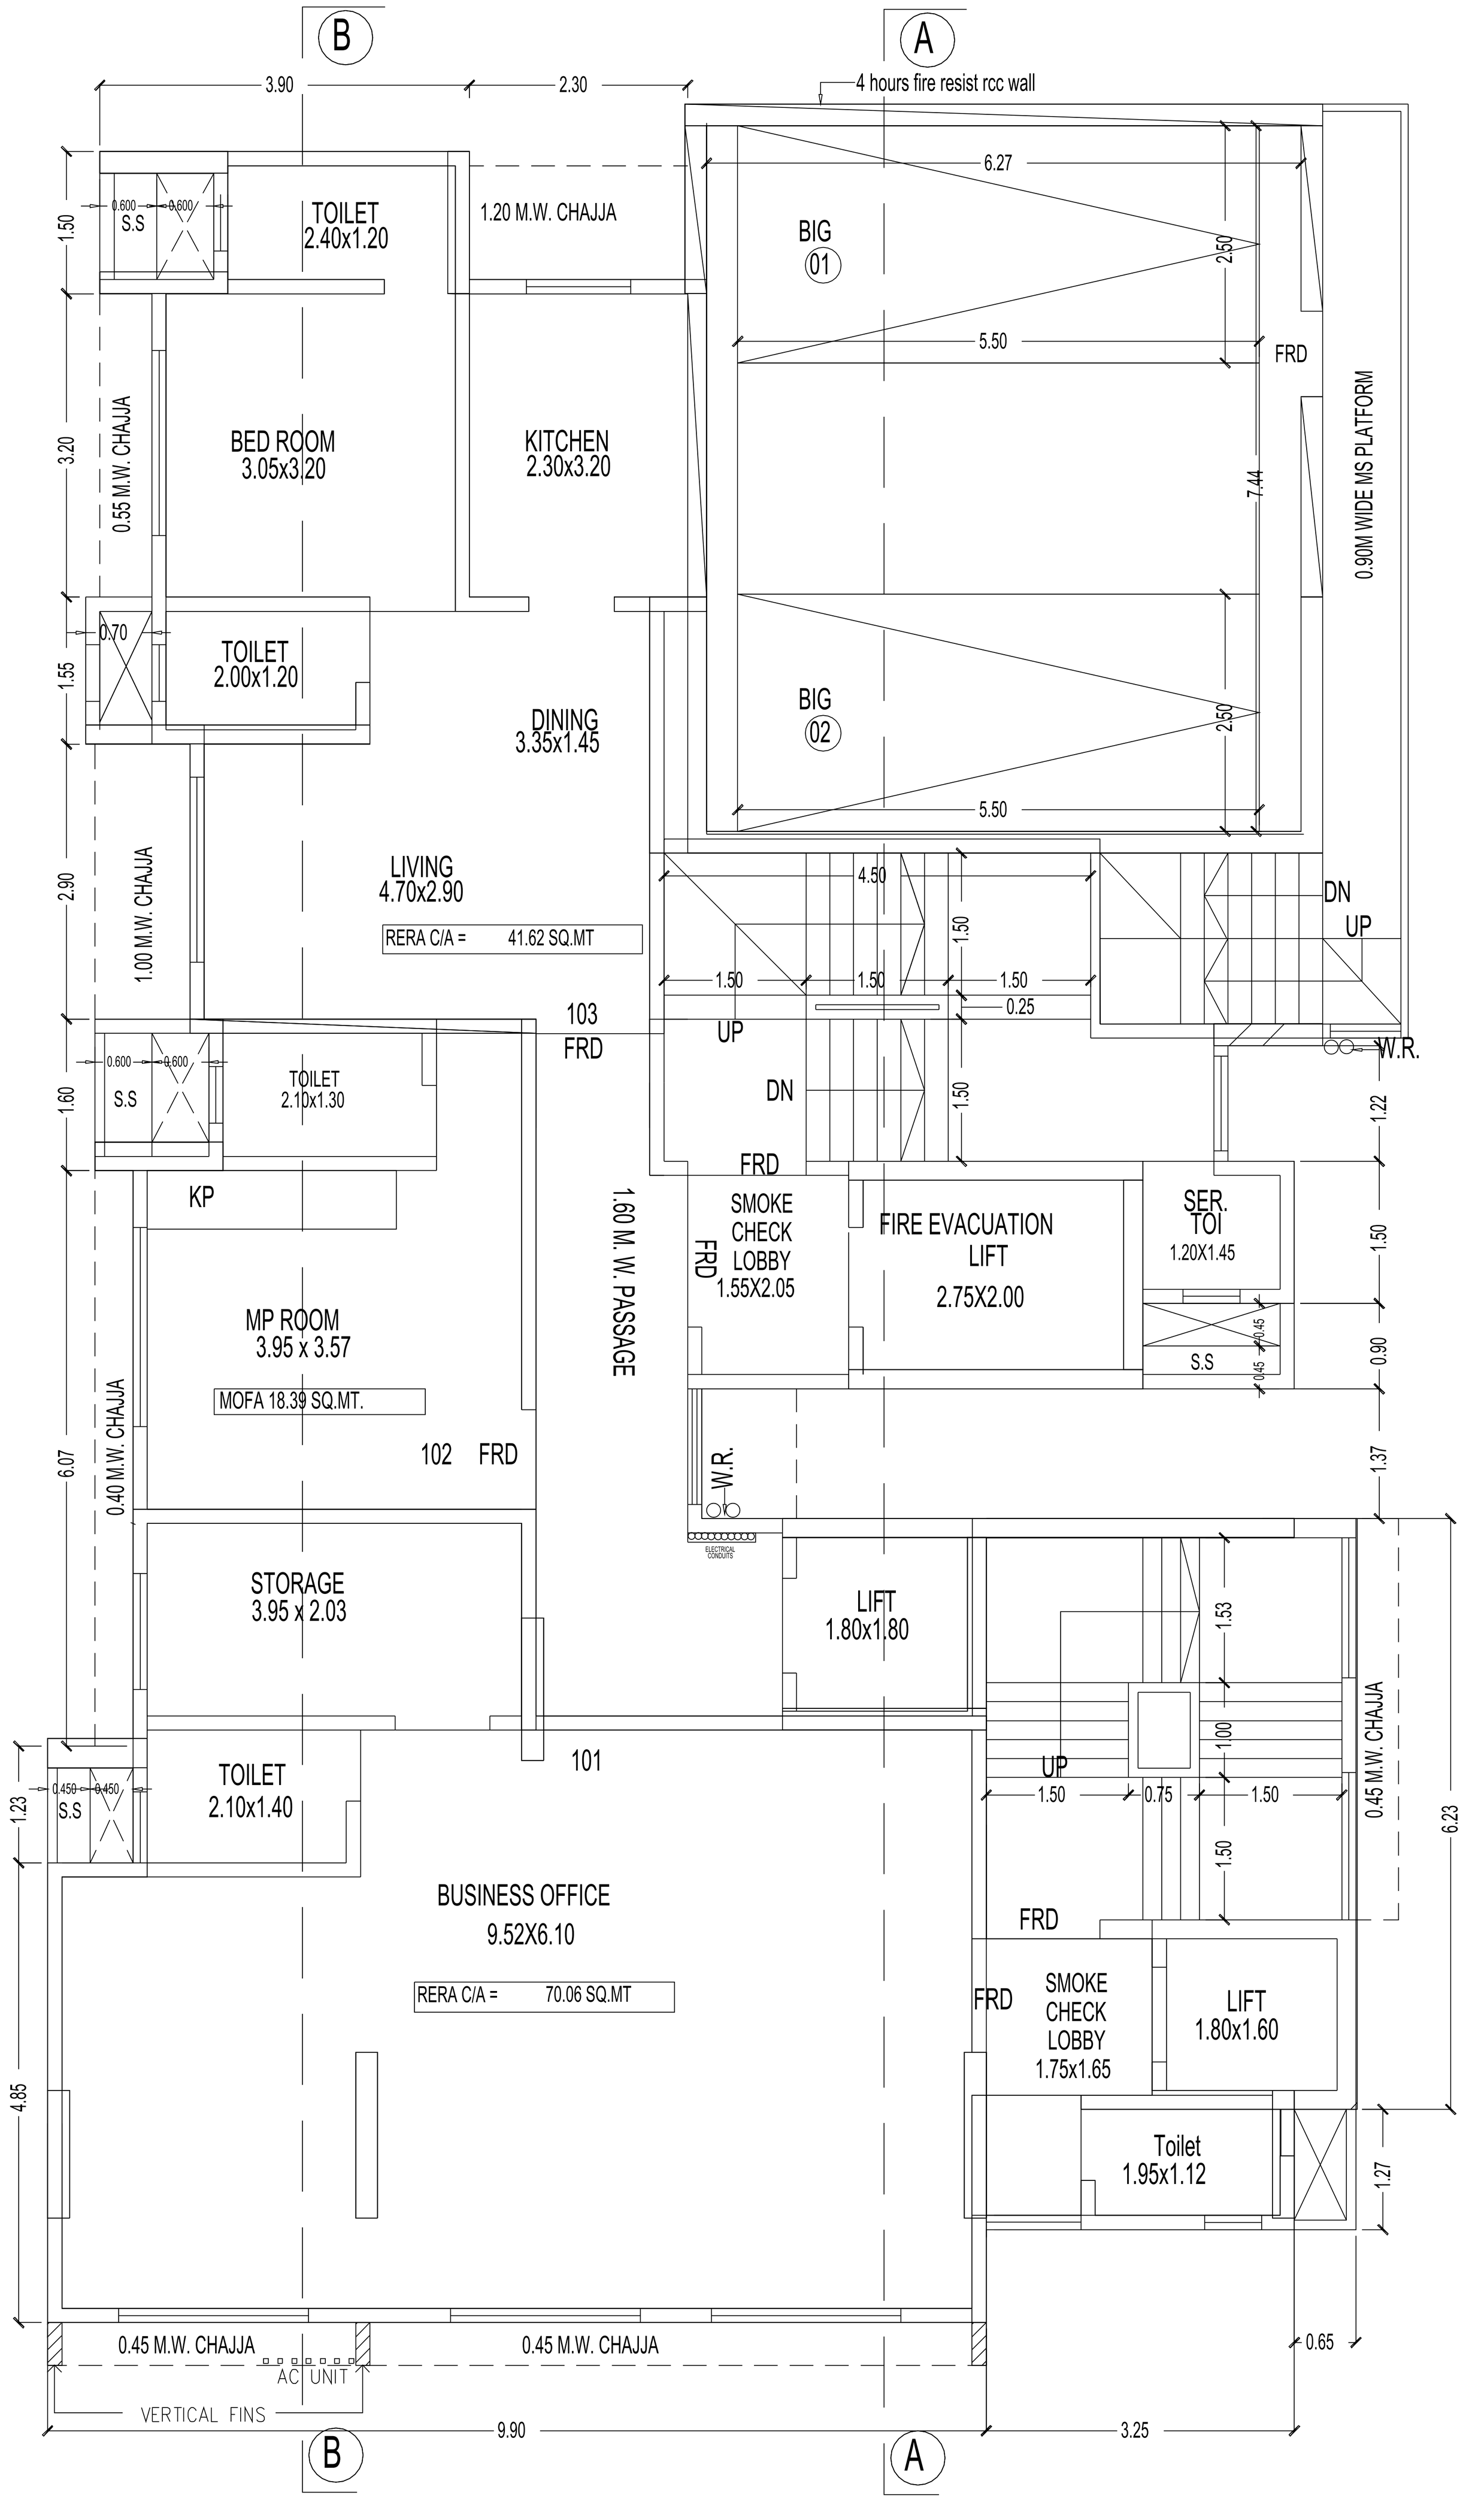



1ST FLOOR PLAN

SCALE - 1:100

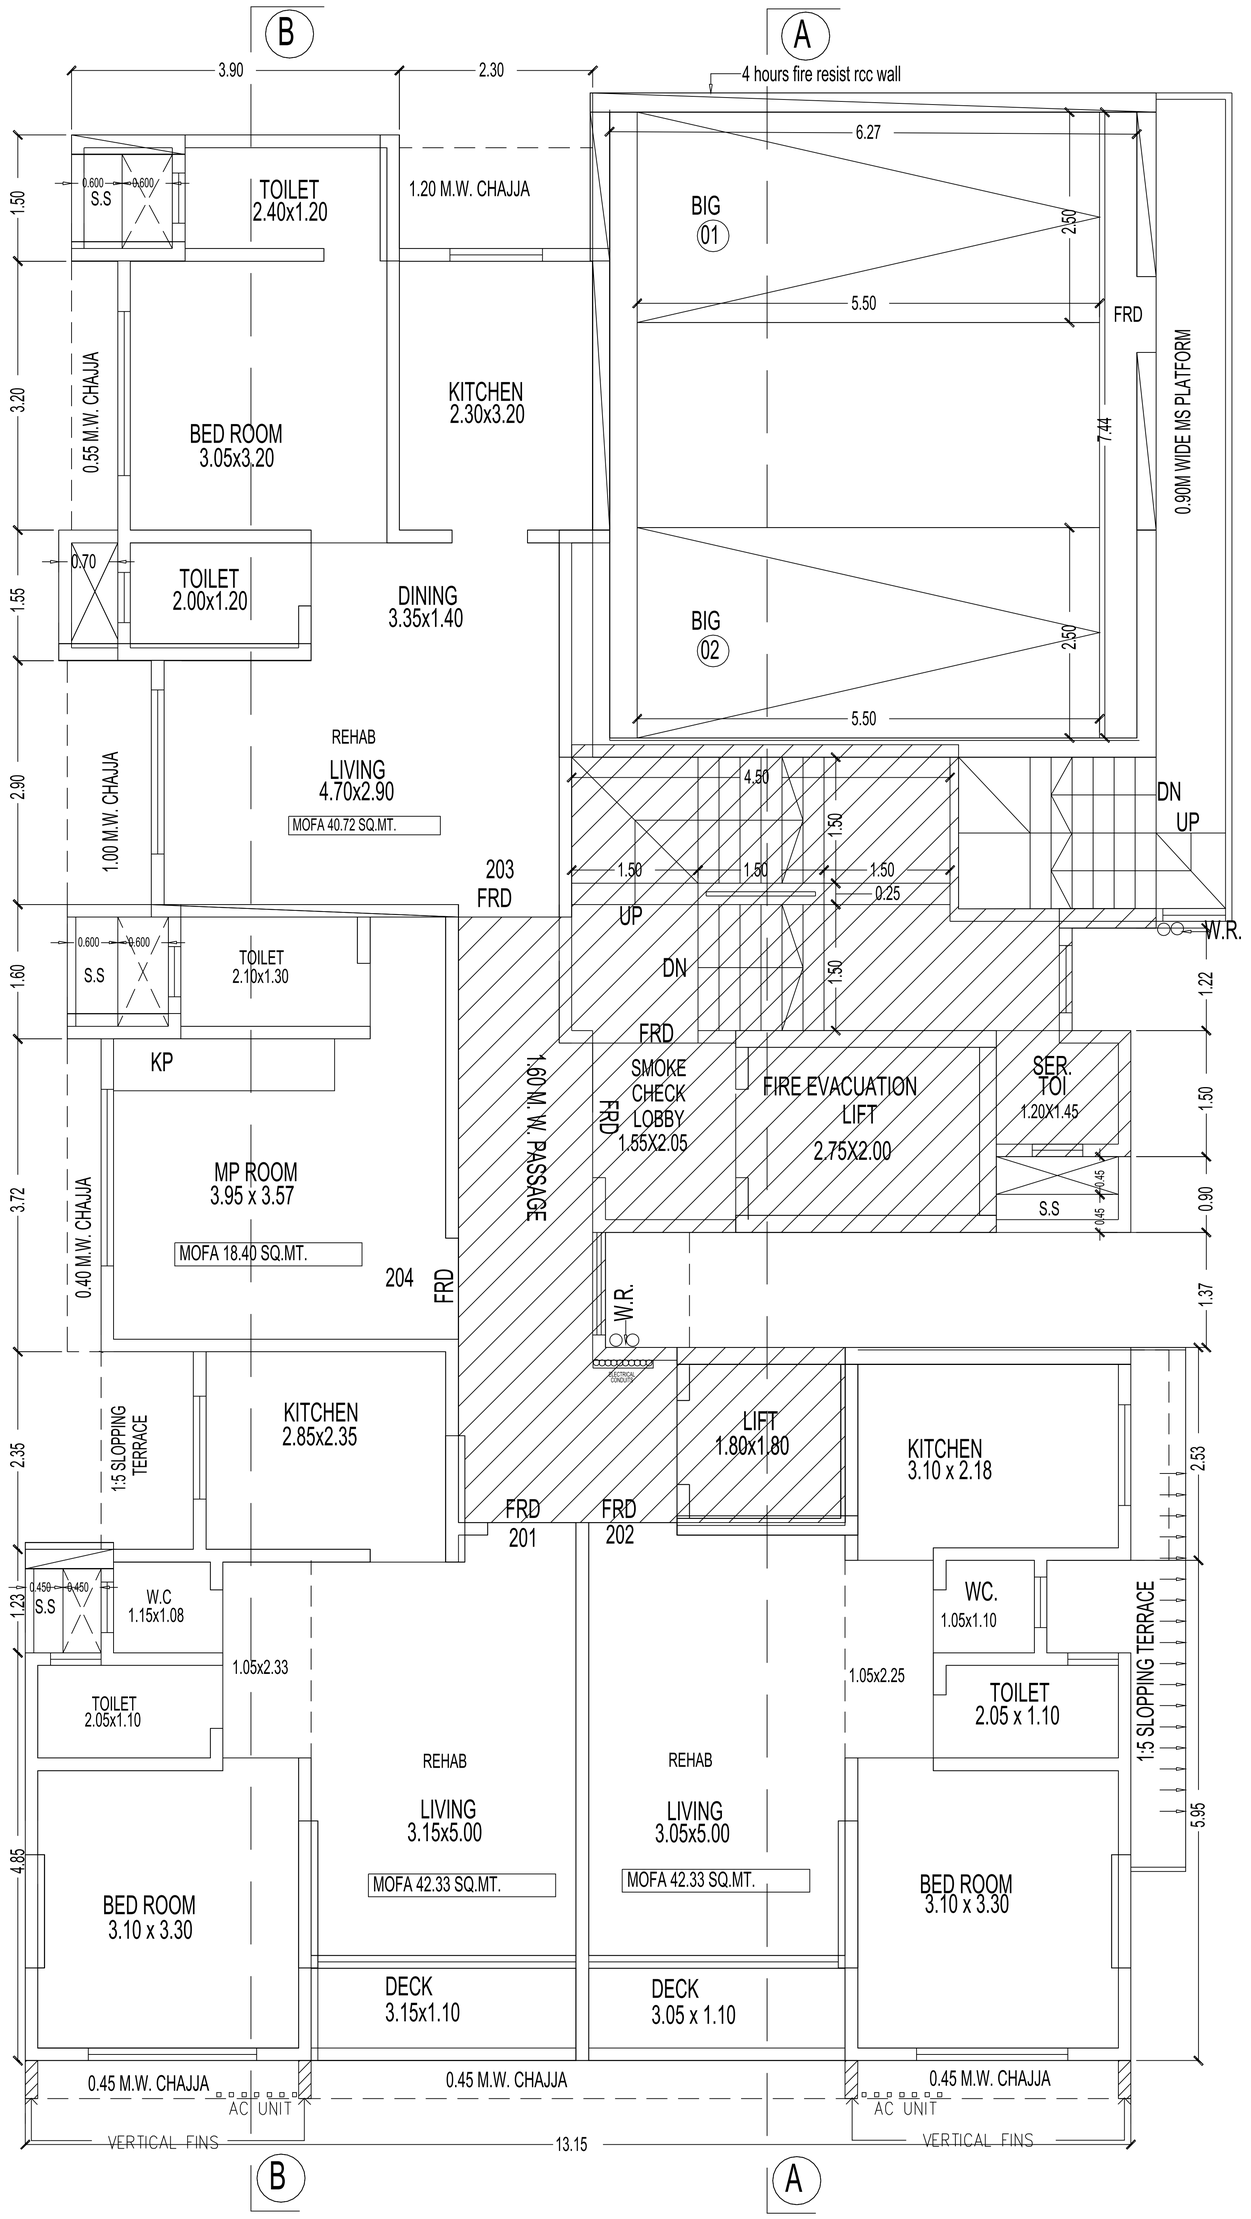


2ND FLOOR PLAN

SCALE - 1:100

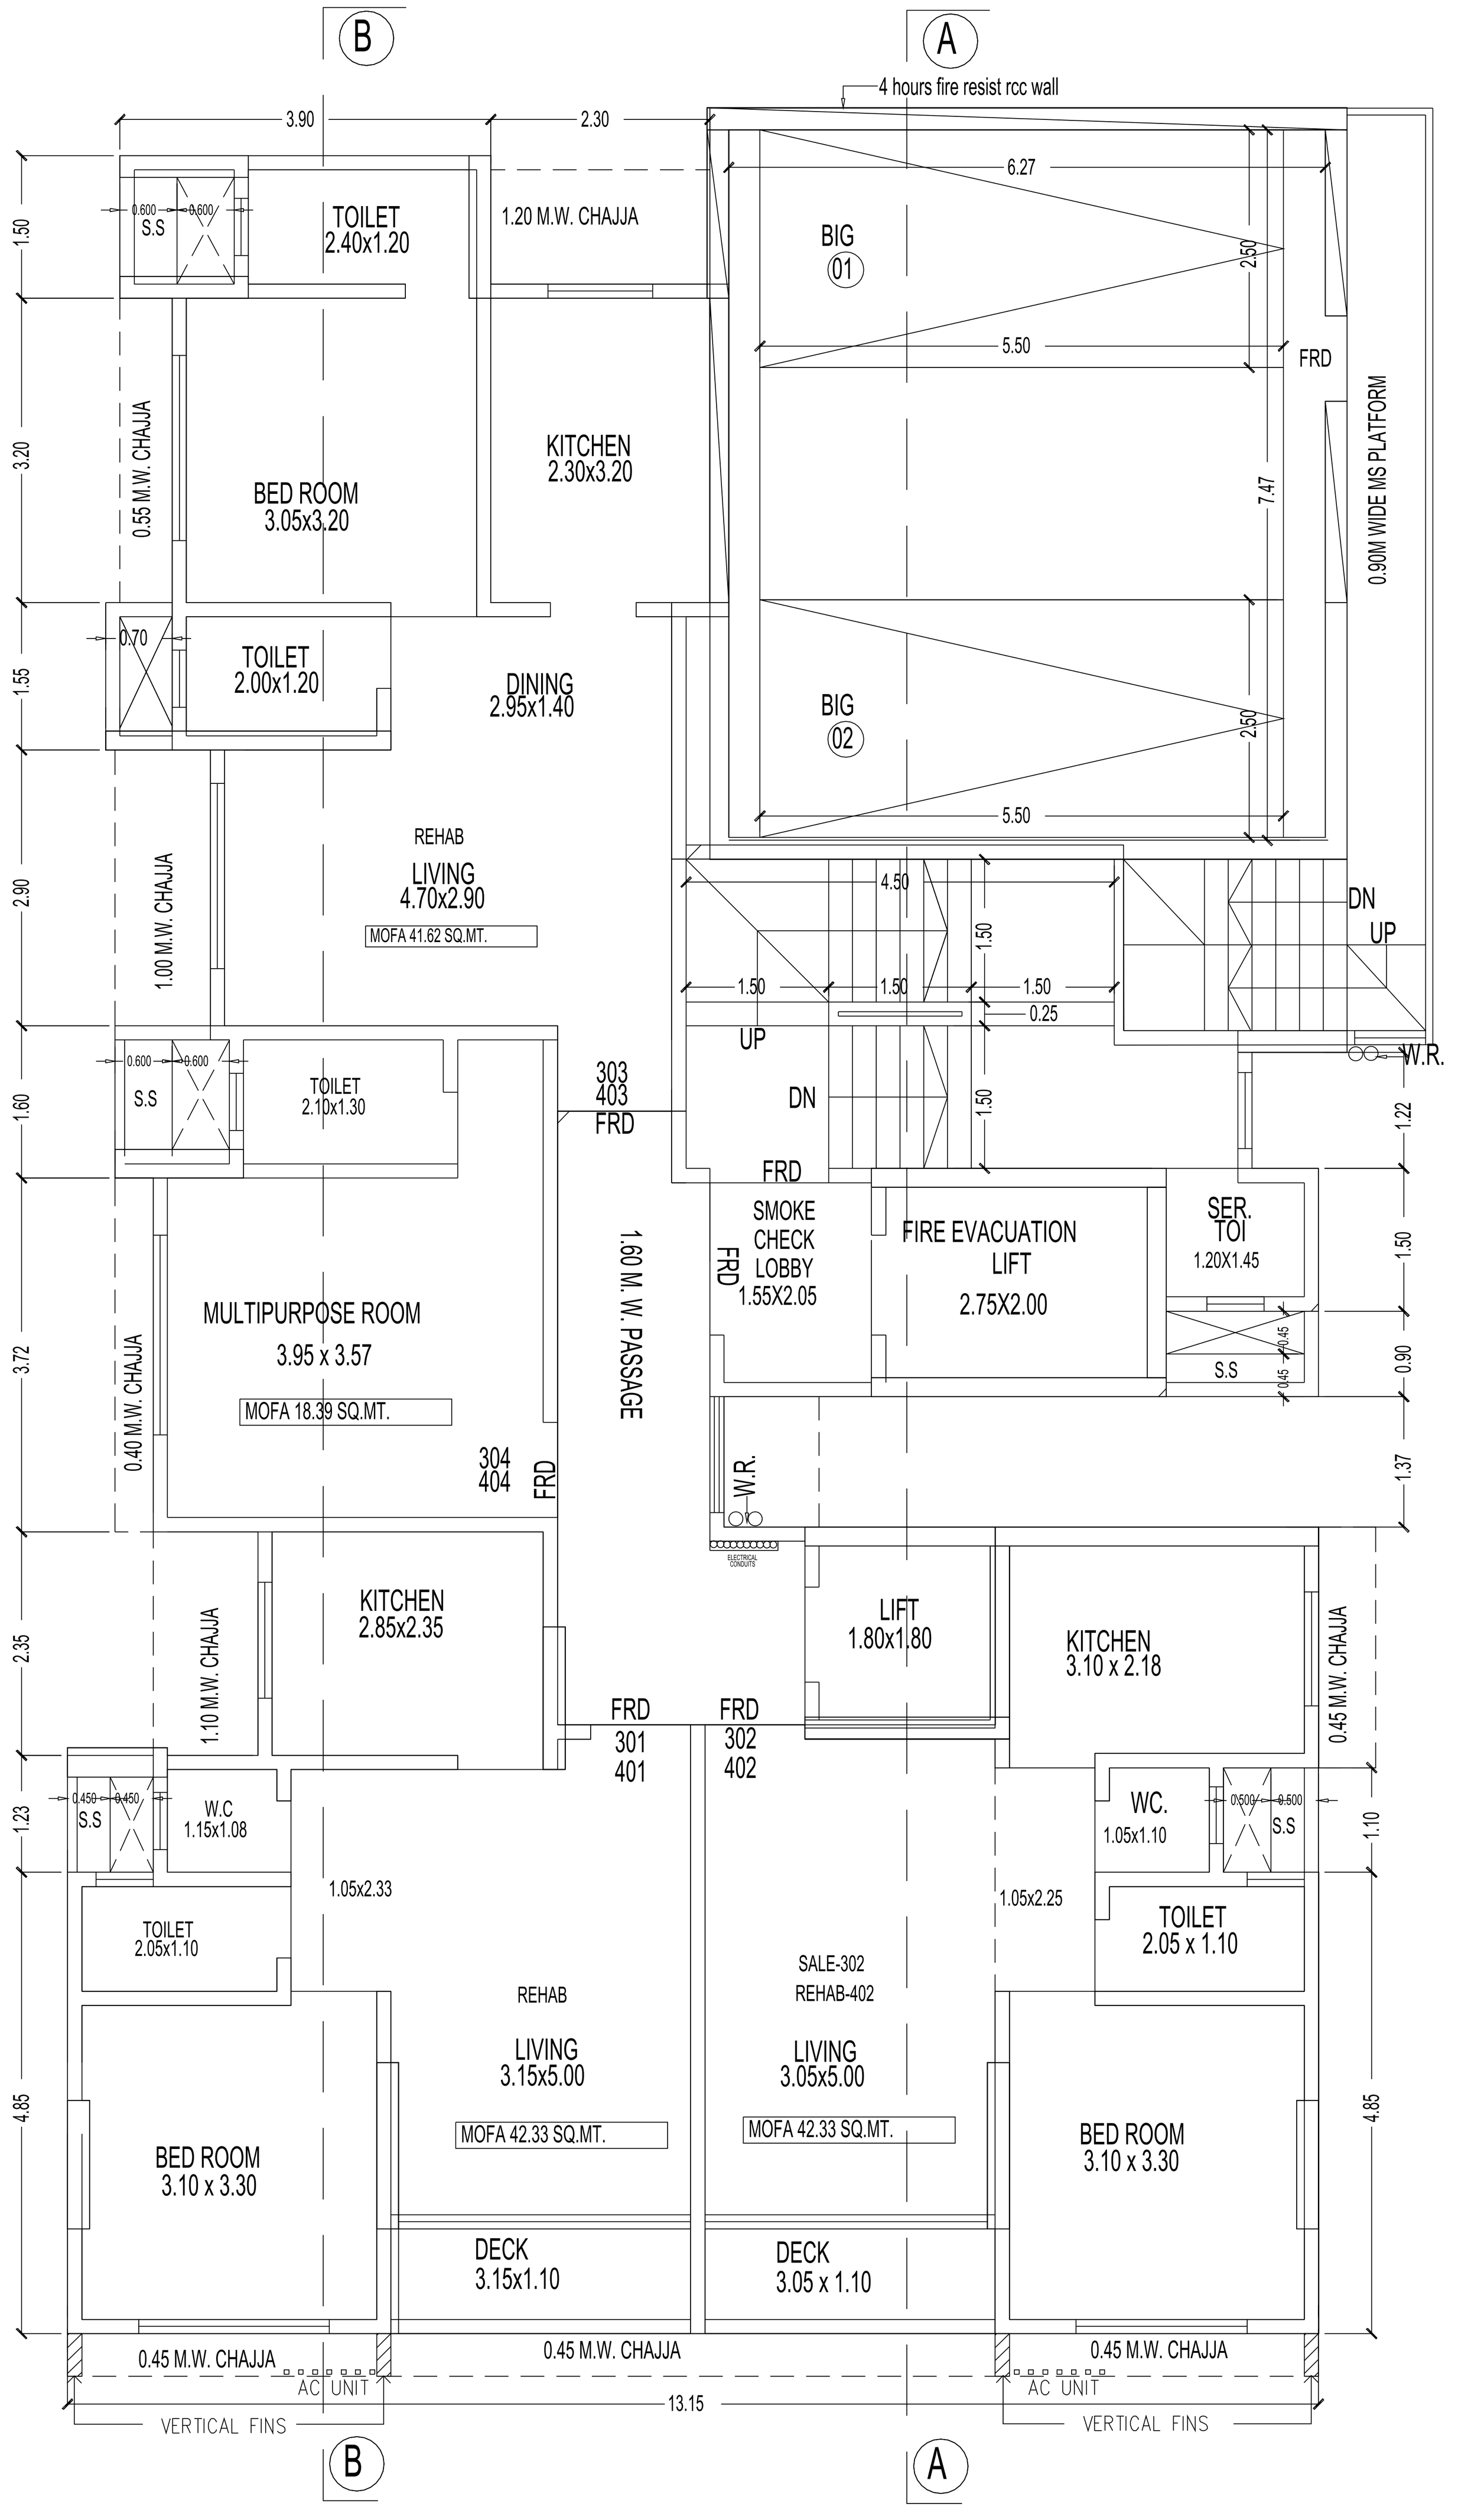


3RD & 4TH FLOOR PLAN

SCALE - 1:100

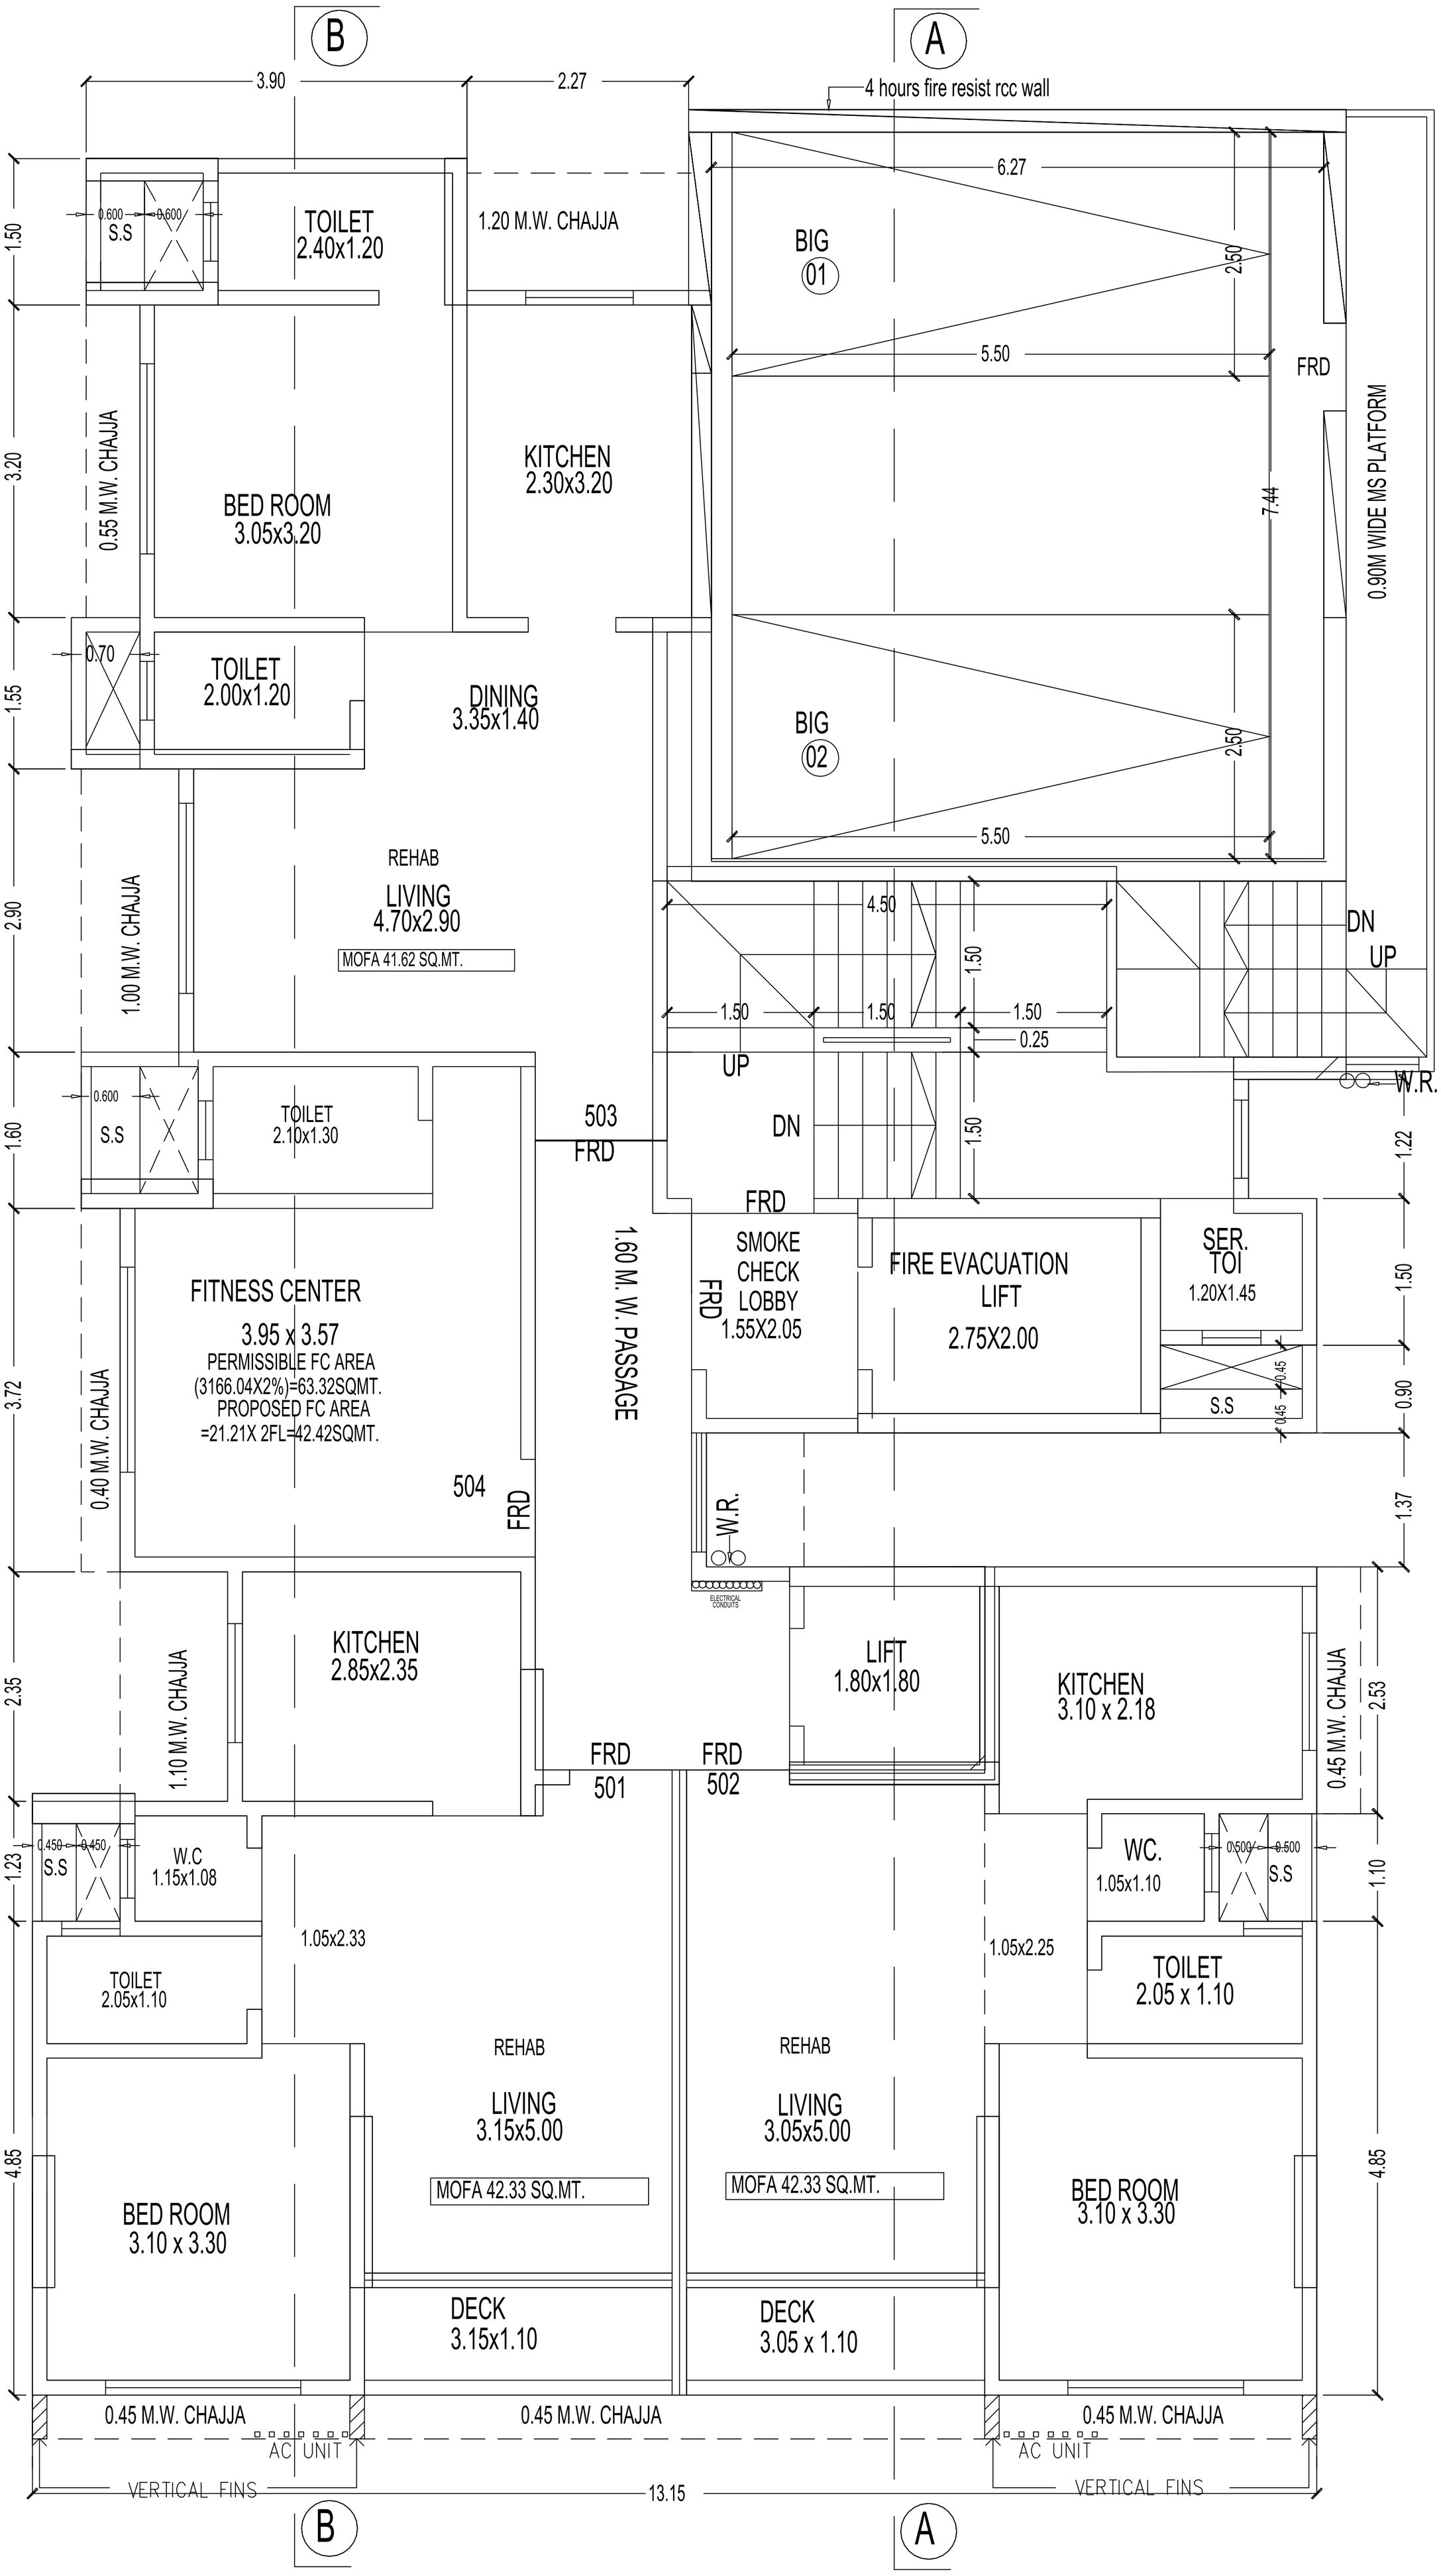


5TH FLOOR PLAN

SCALE - 1:100

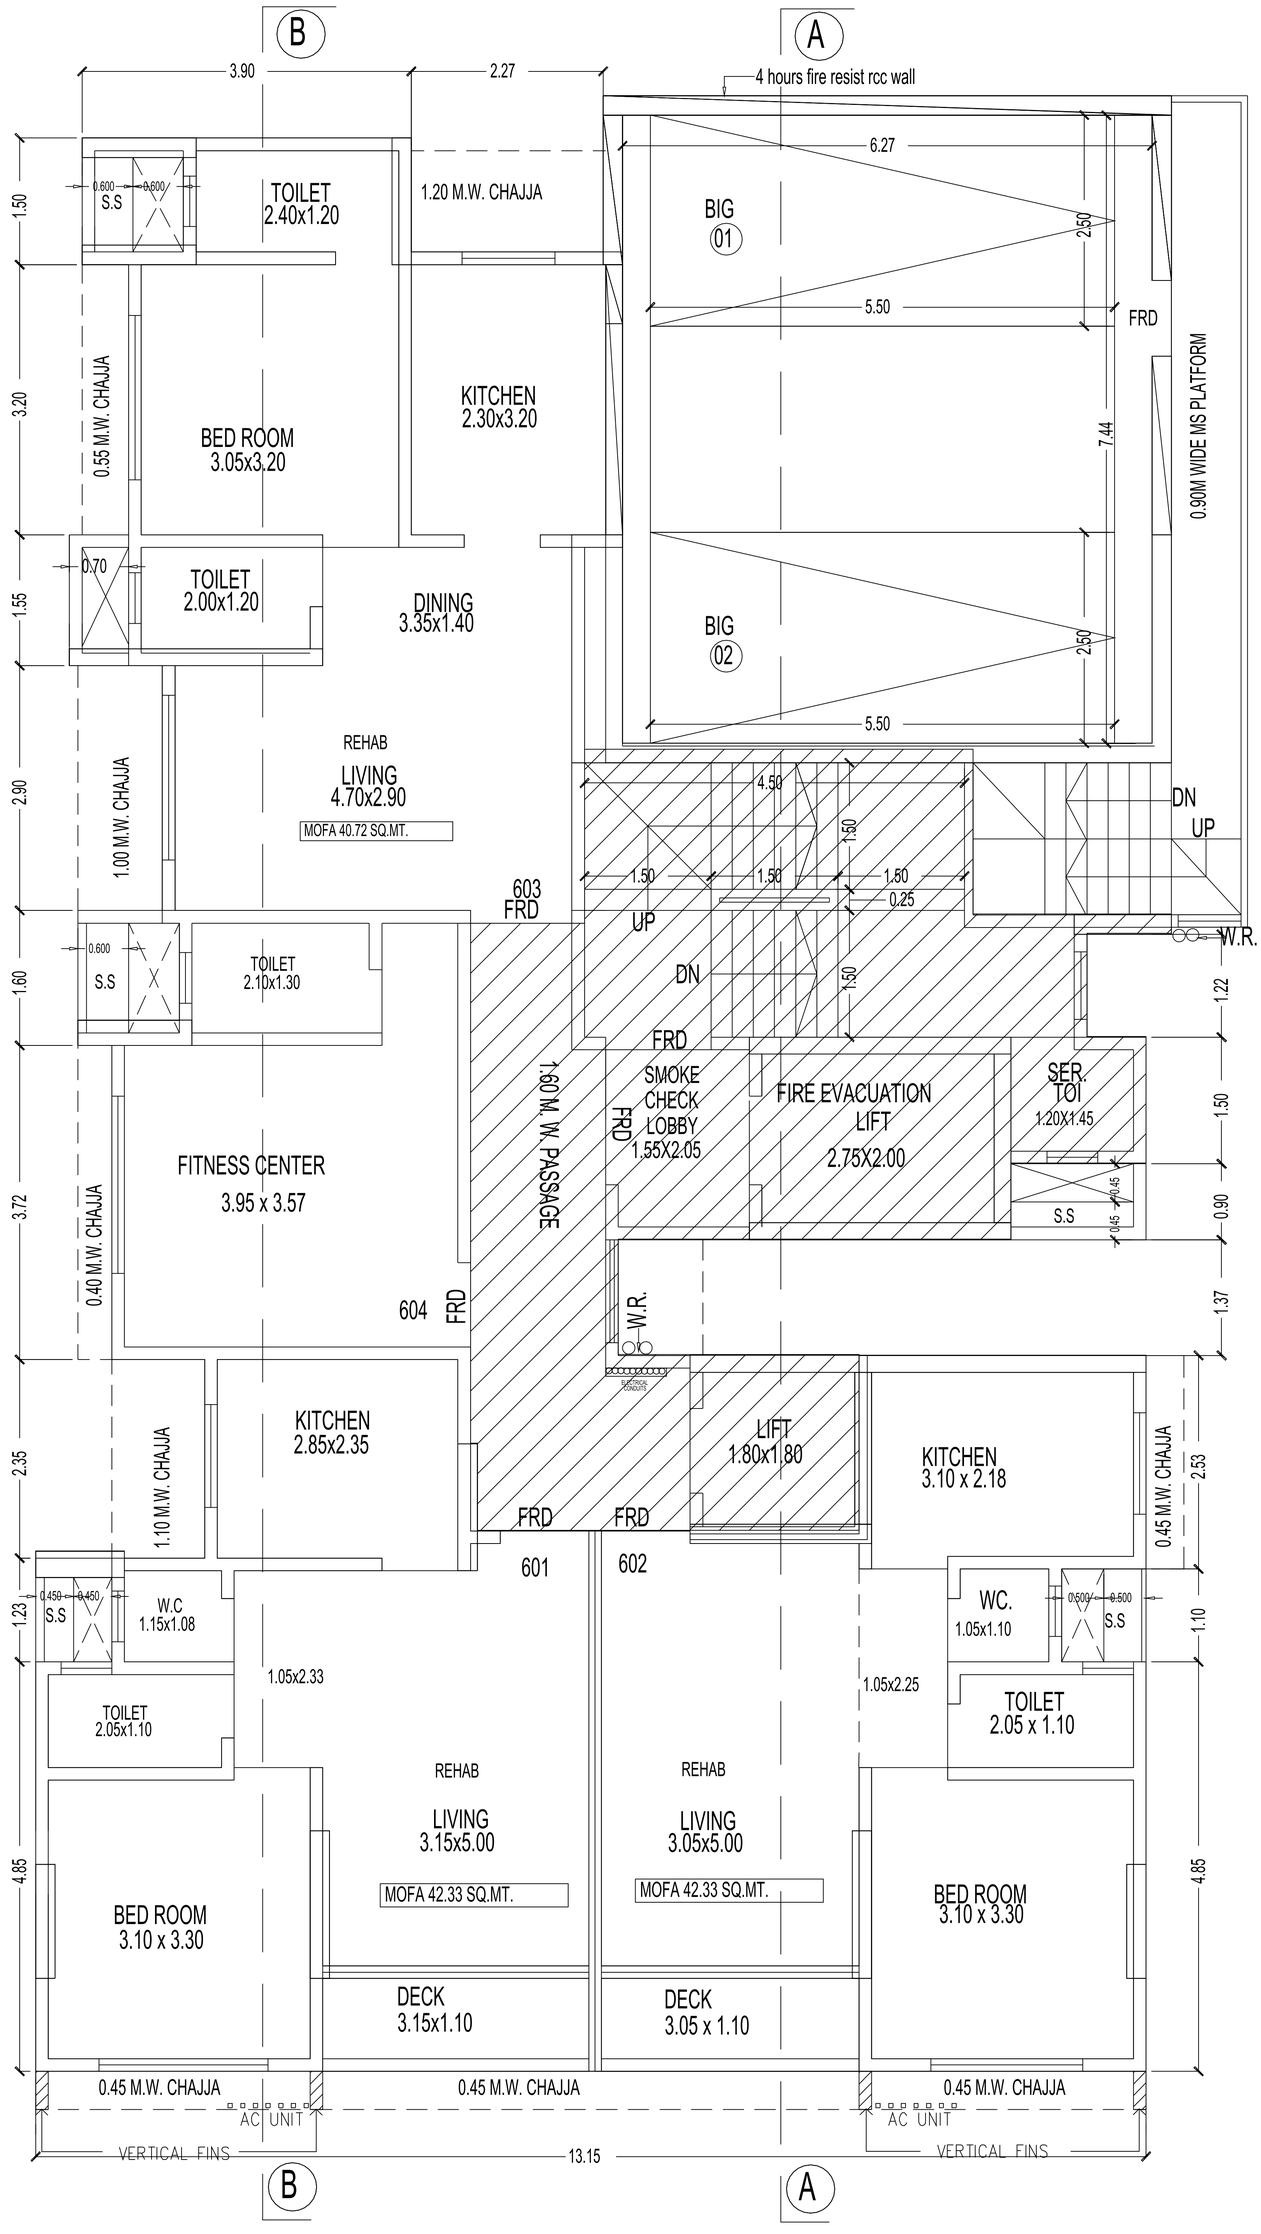


6TH FLOOR PLAN

SCALE - 1:100

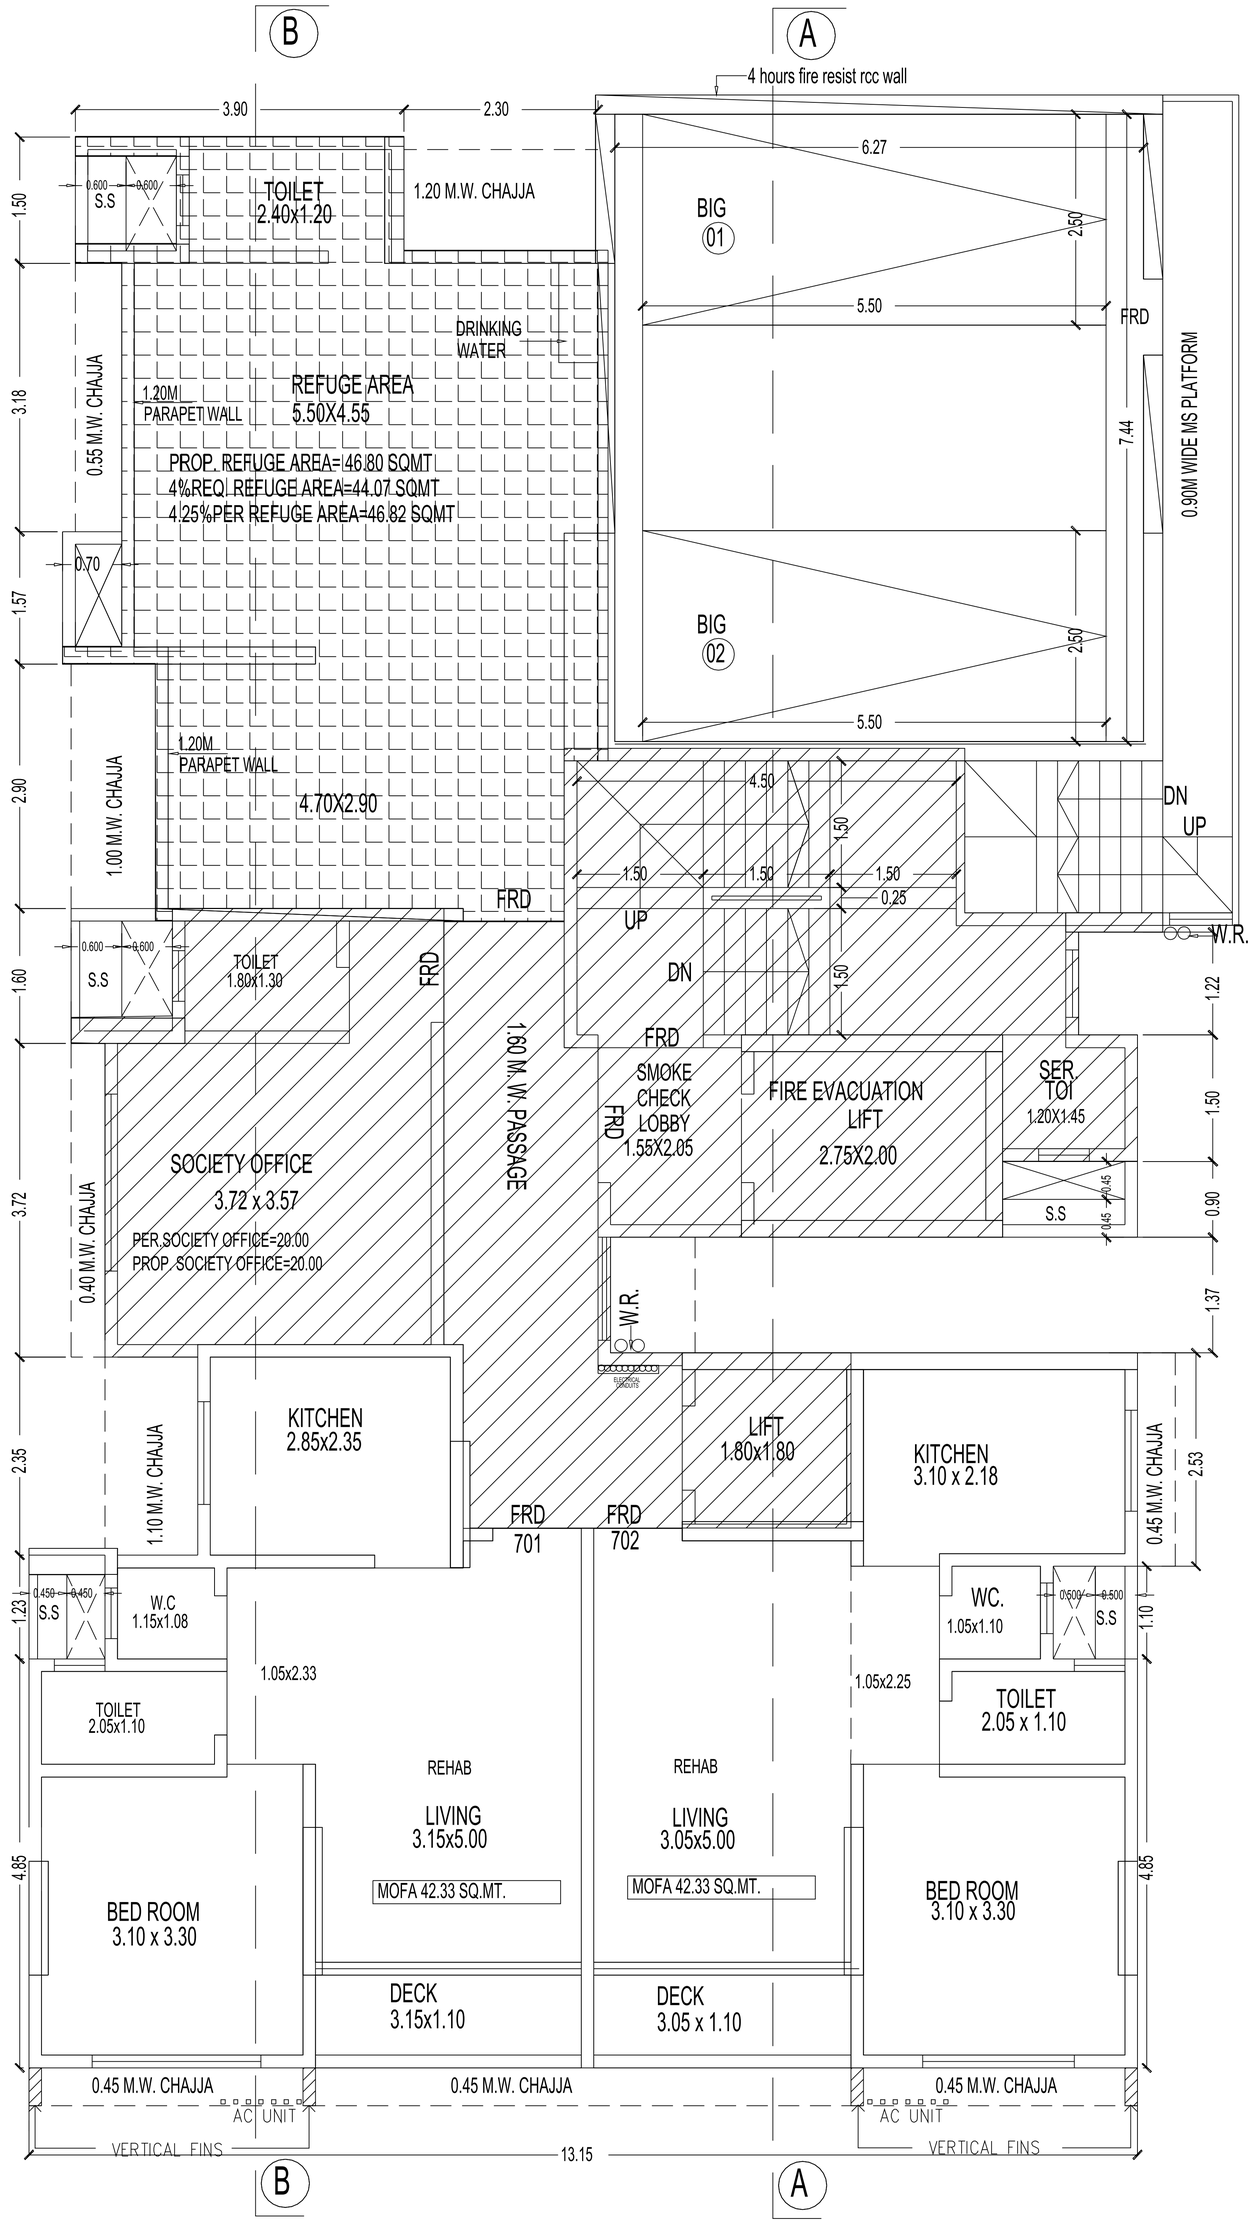


7TH FLOOR PLAN

SCALE - 1:100

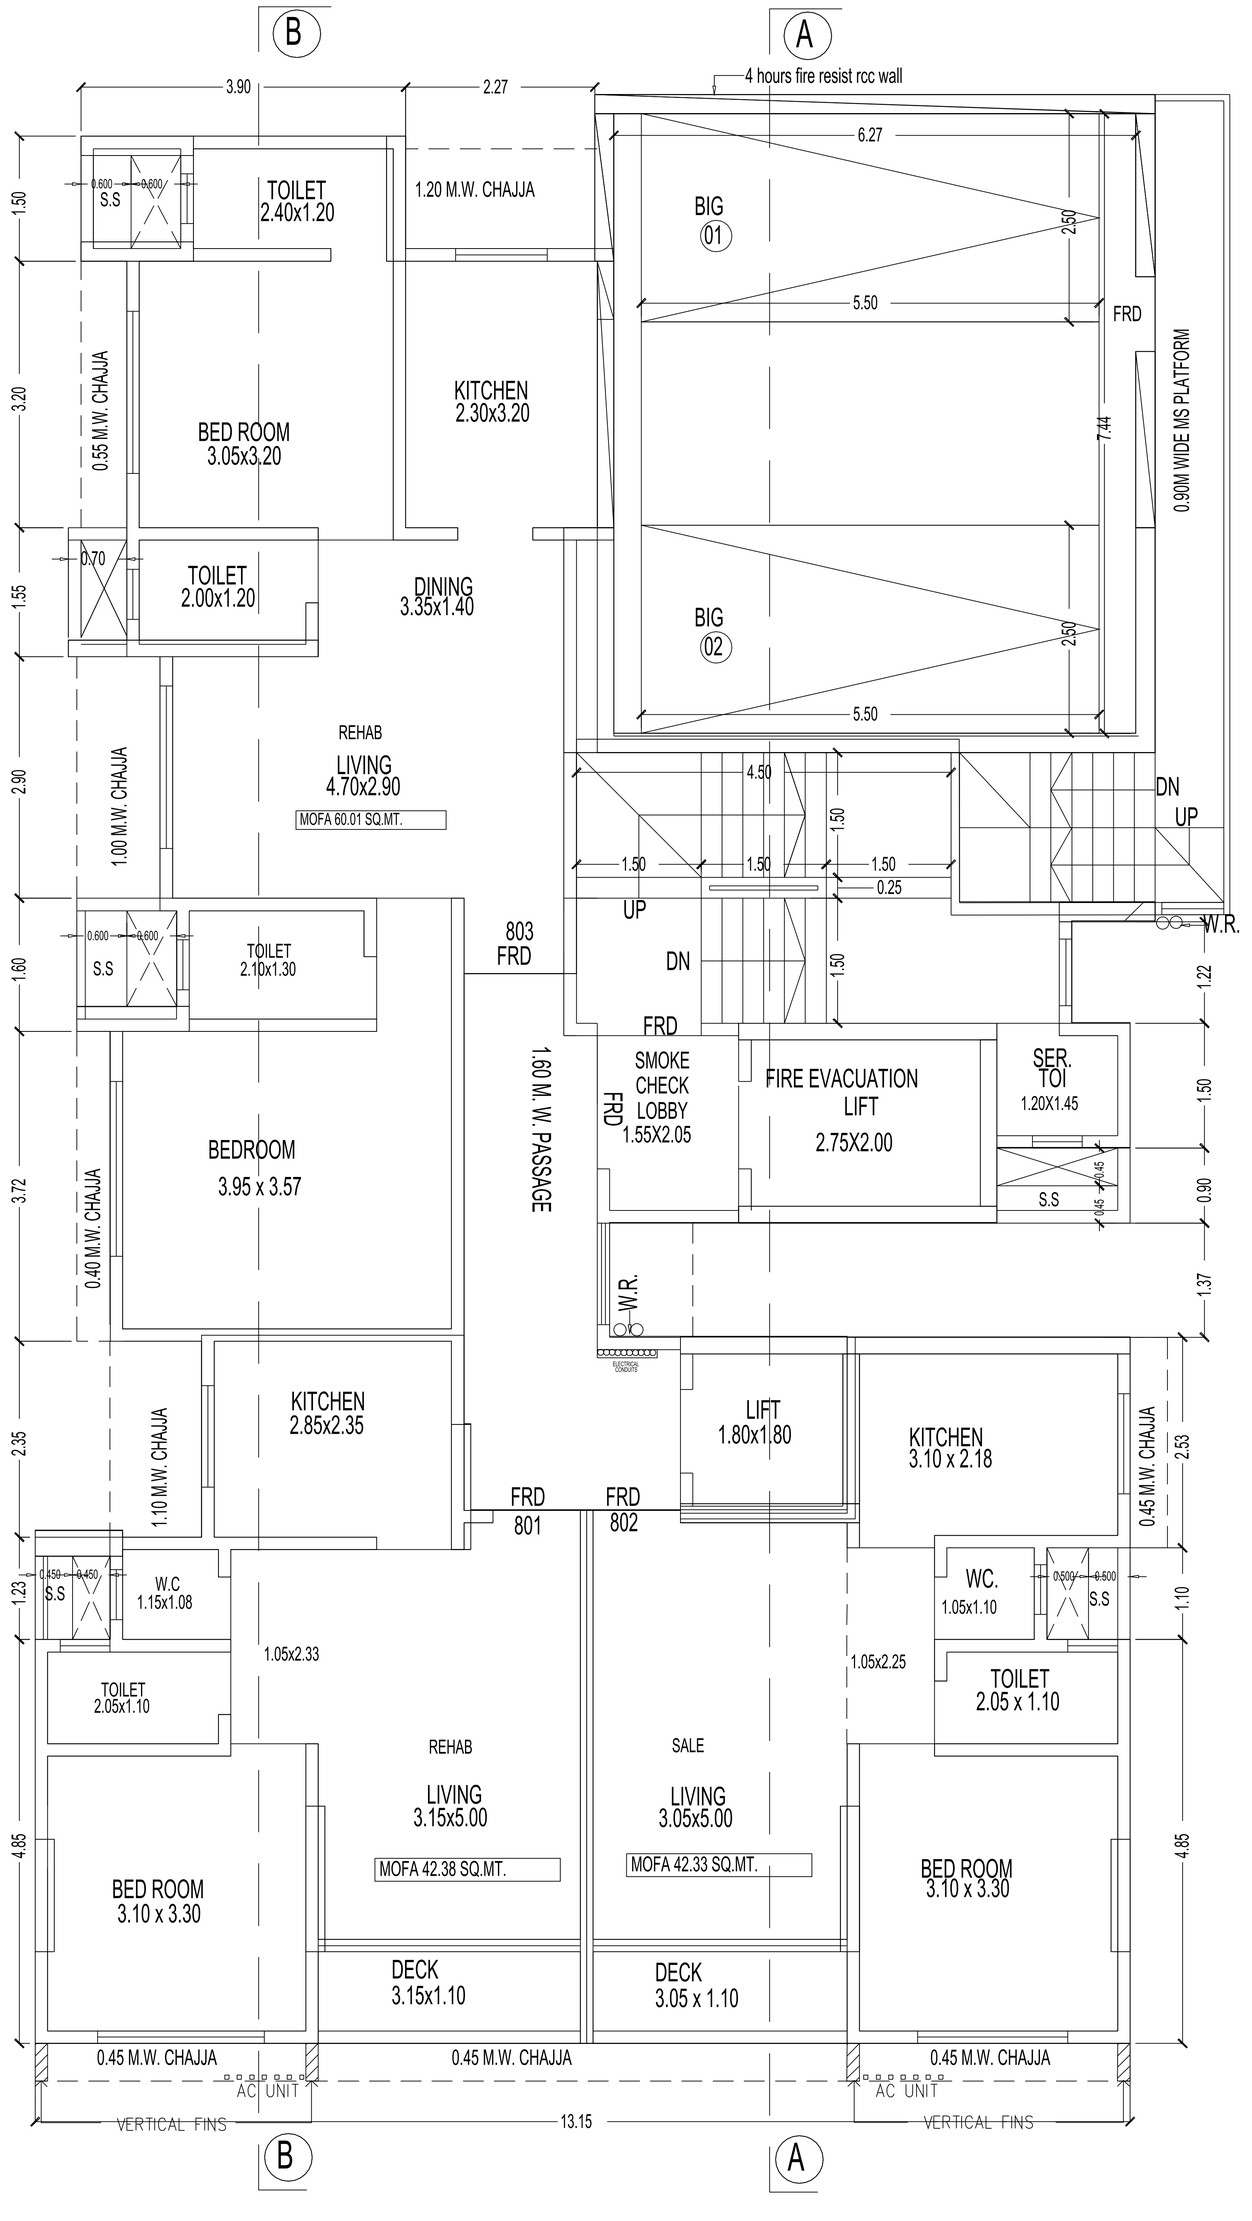


8TH FLOOR PLAN

SCALE - 1:100

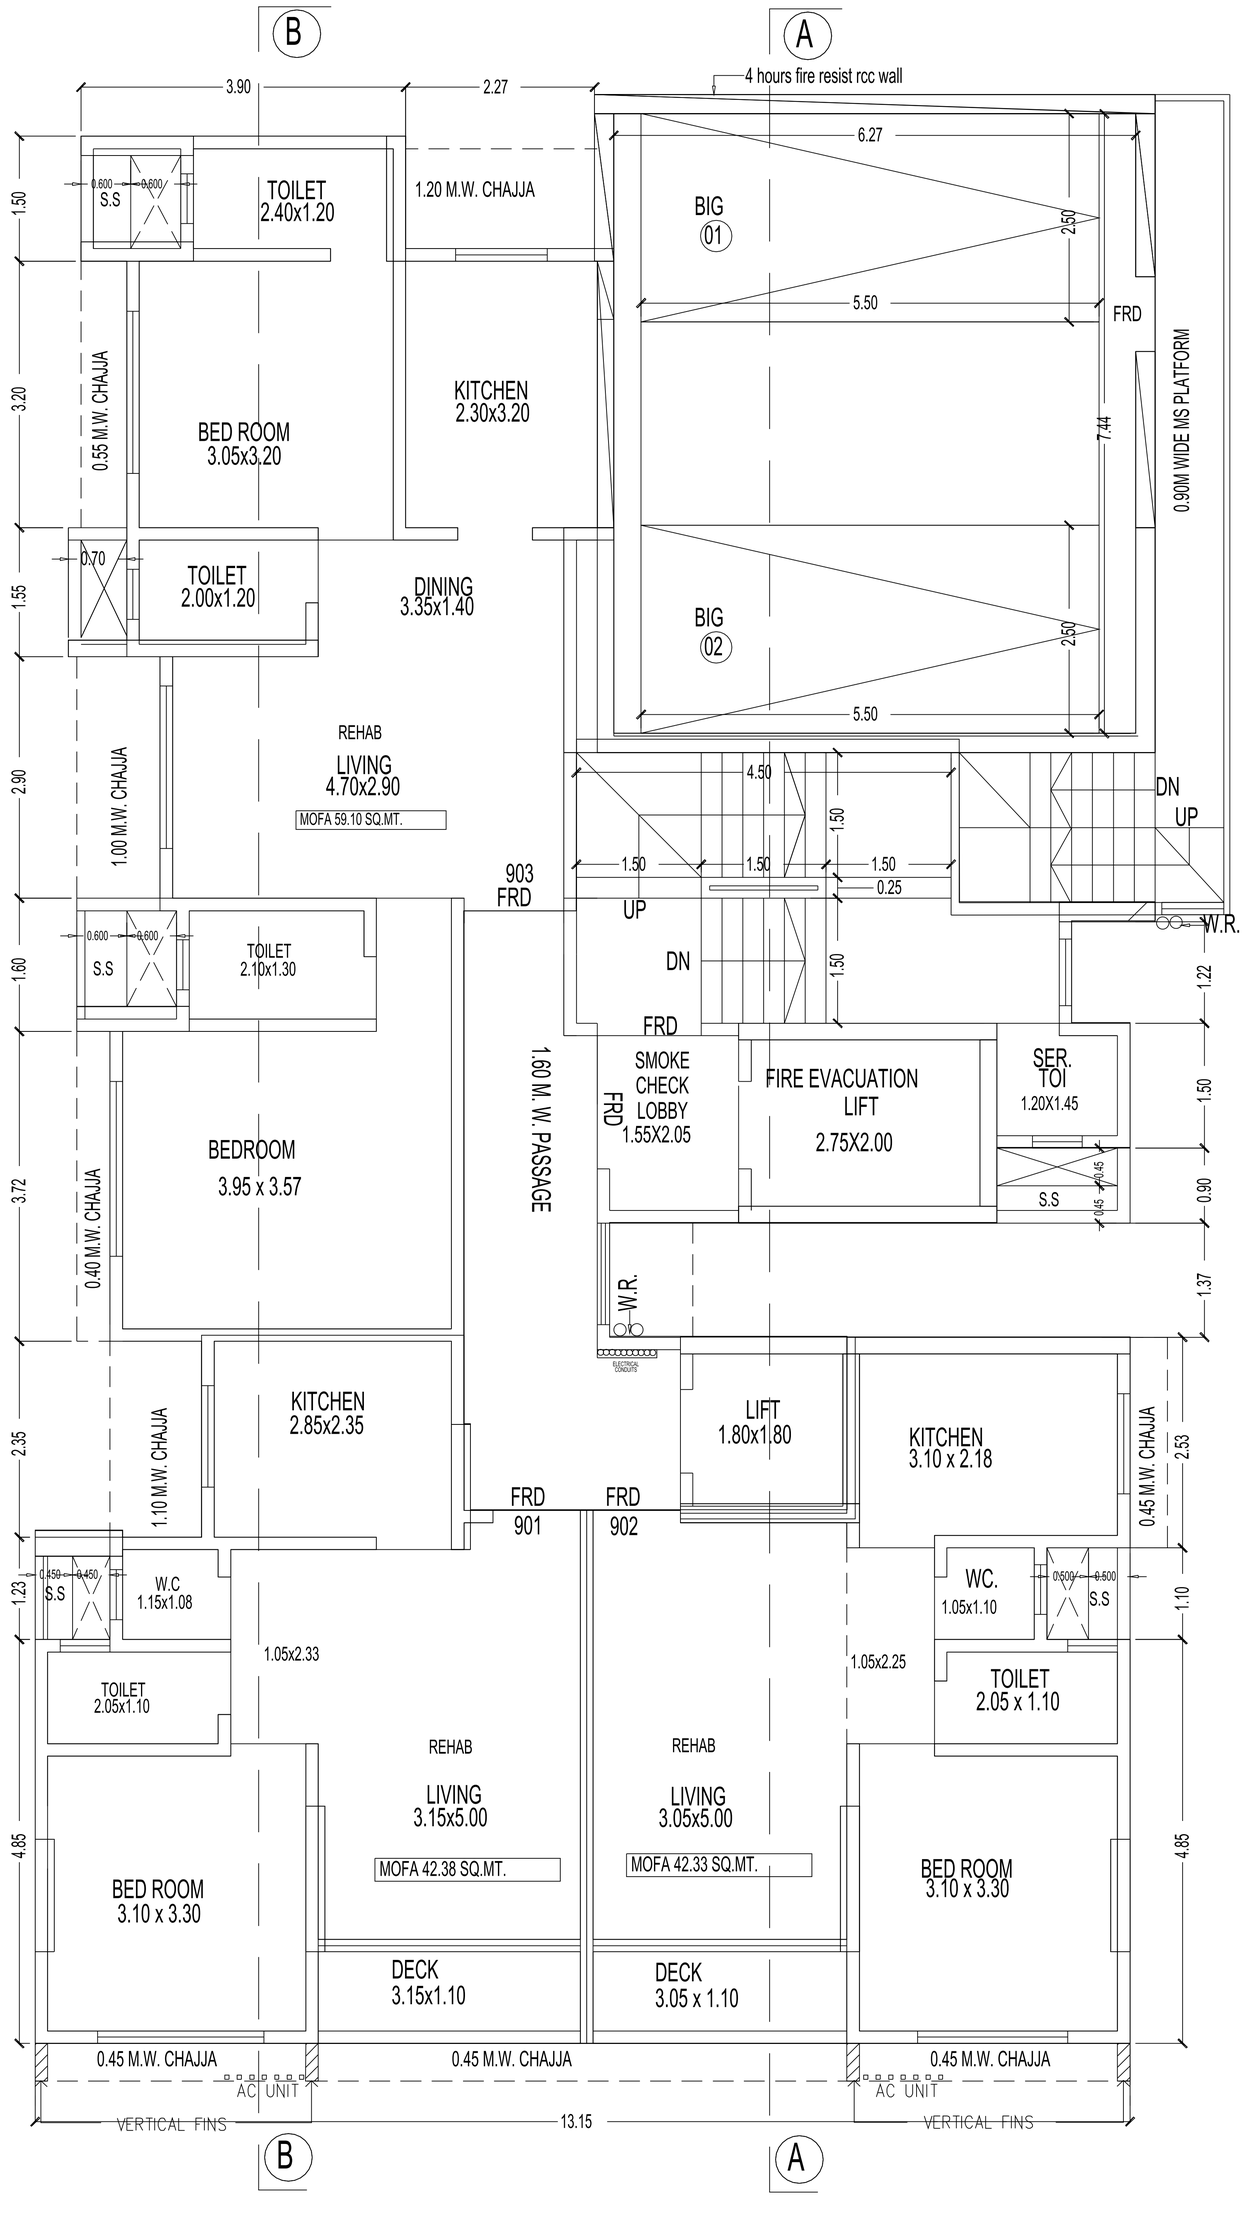


9TH FLOOR PLAN

SCALE - 1:100

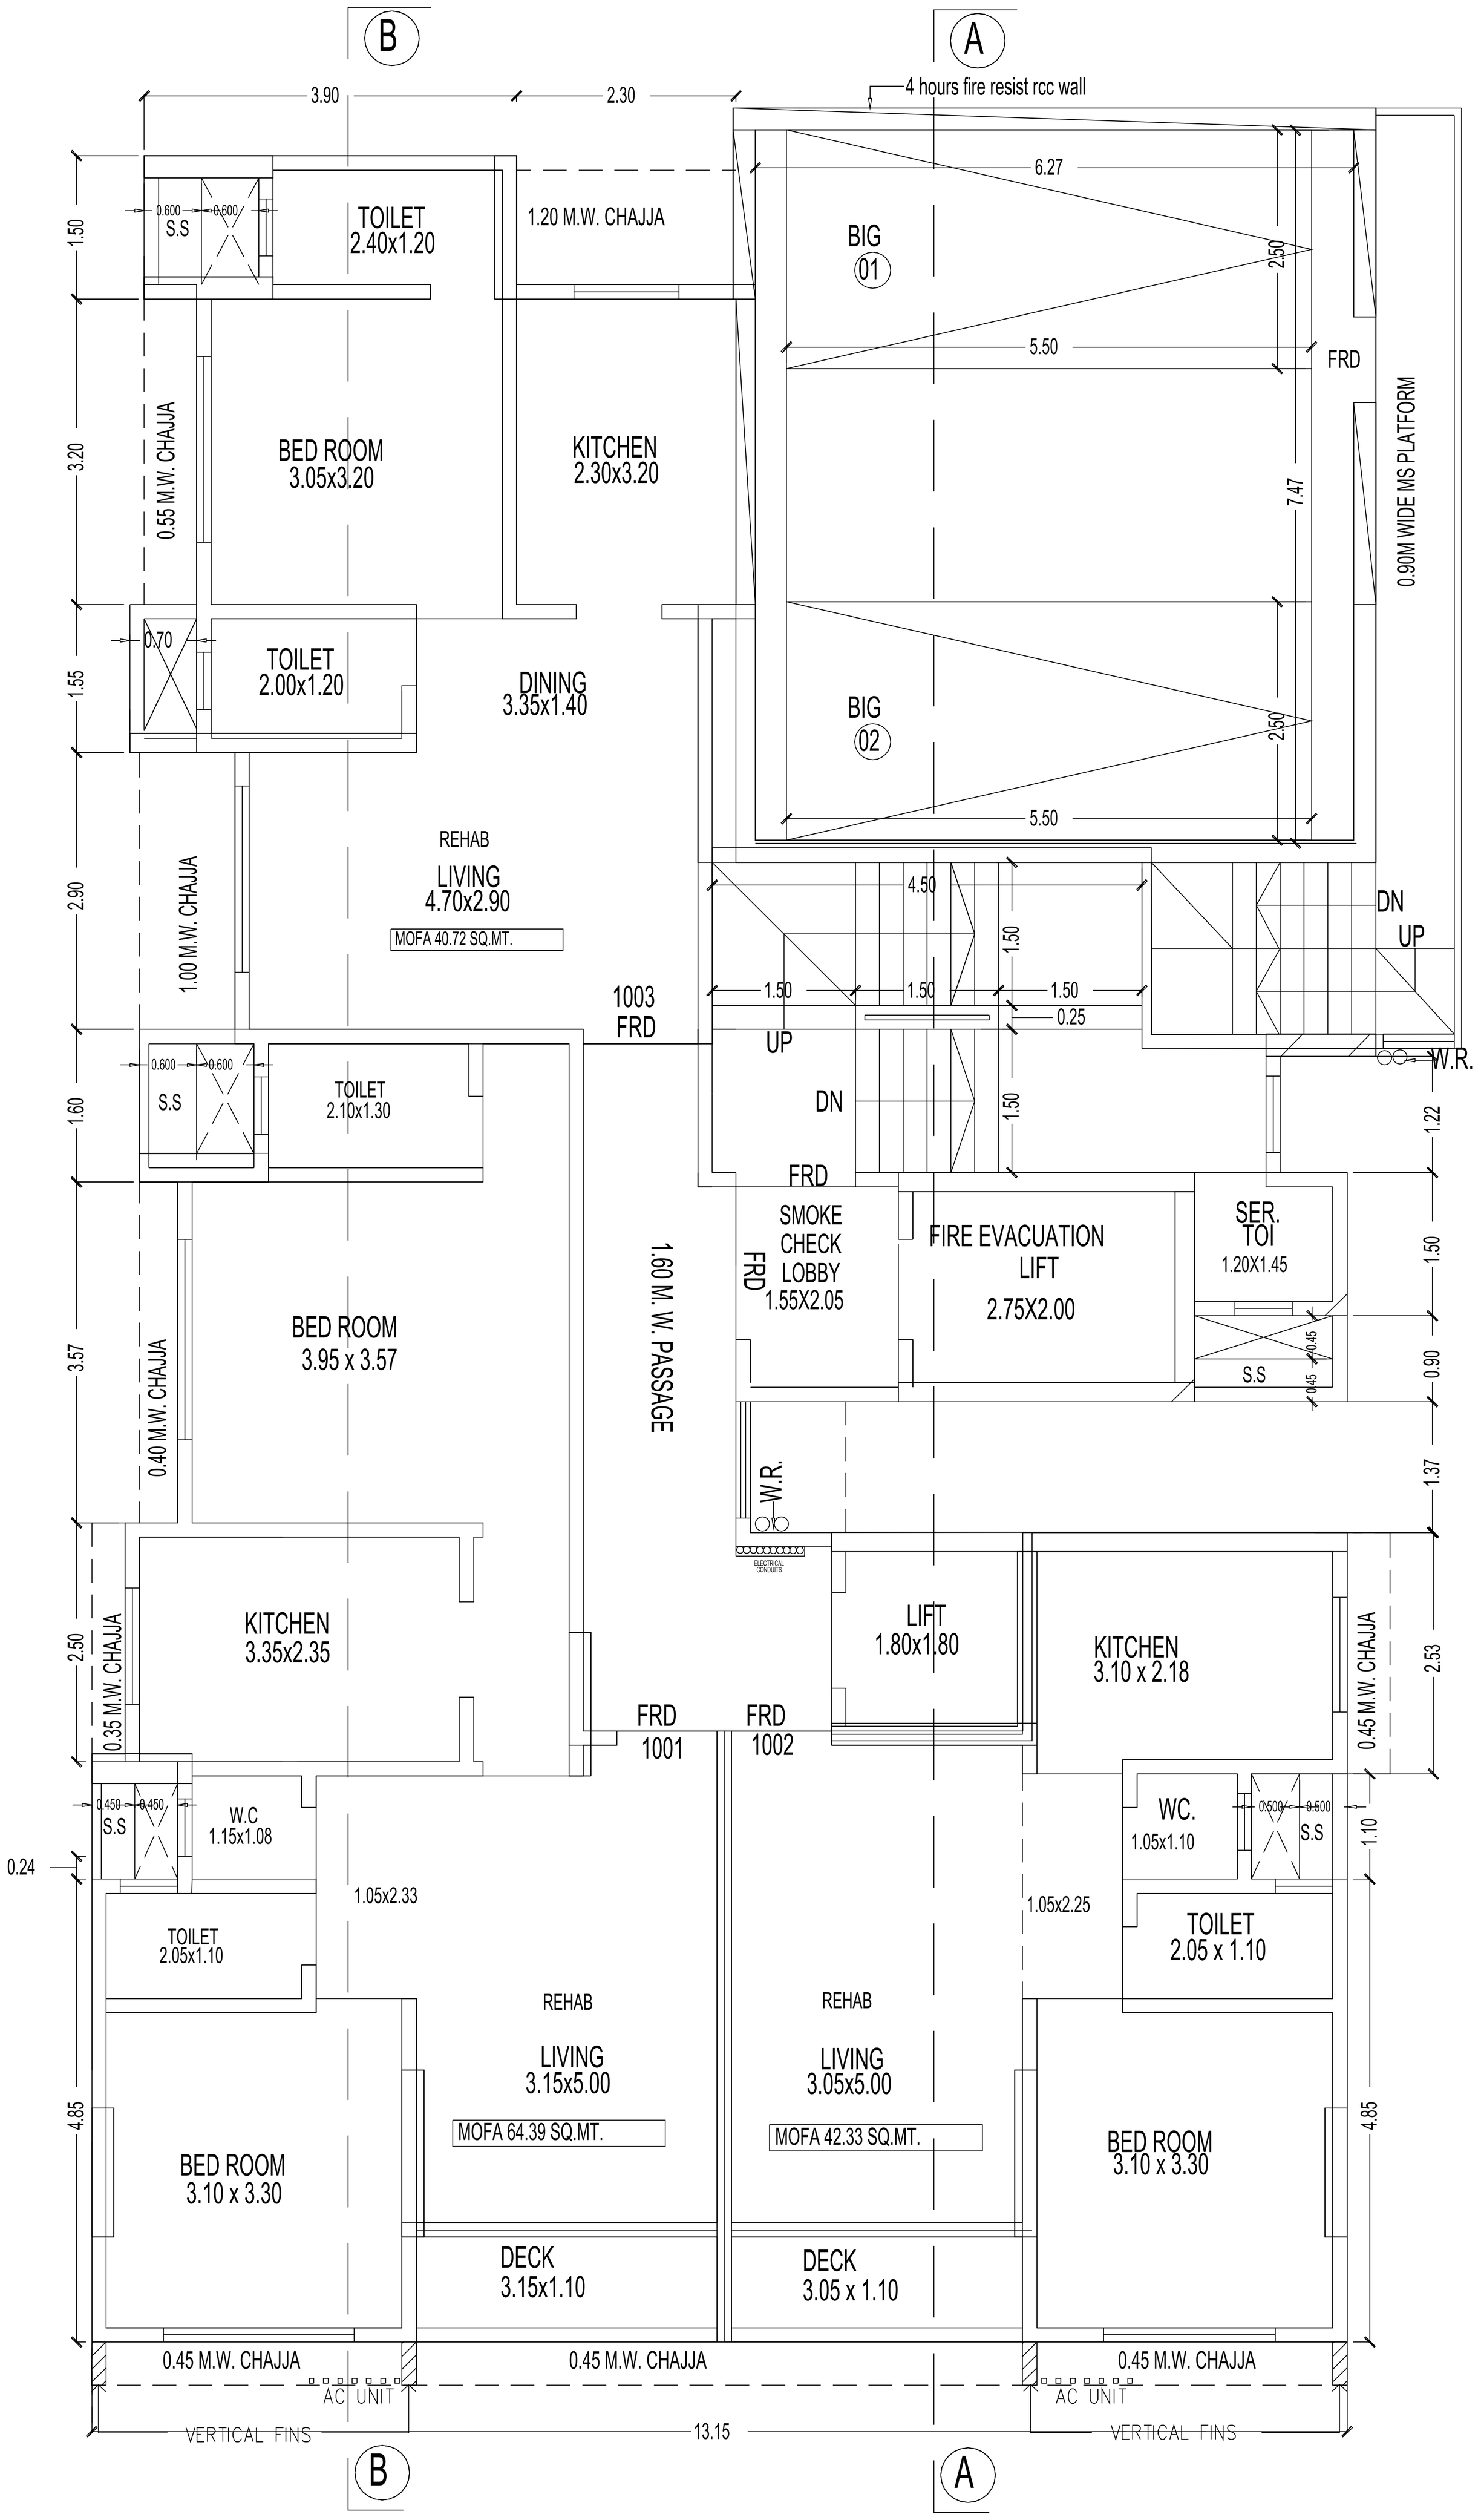


10TH FLOOR PLAN

SCALE - 1:100

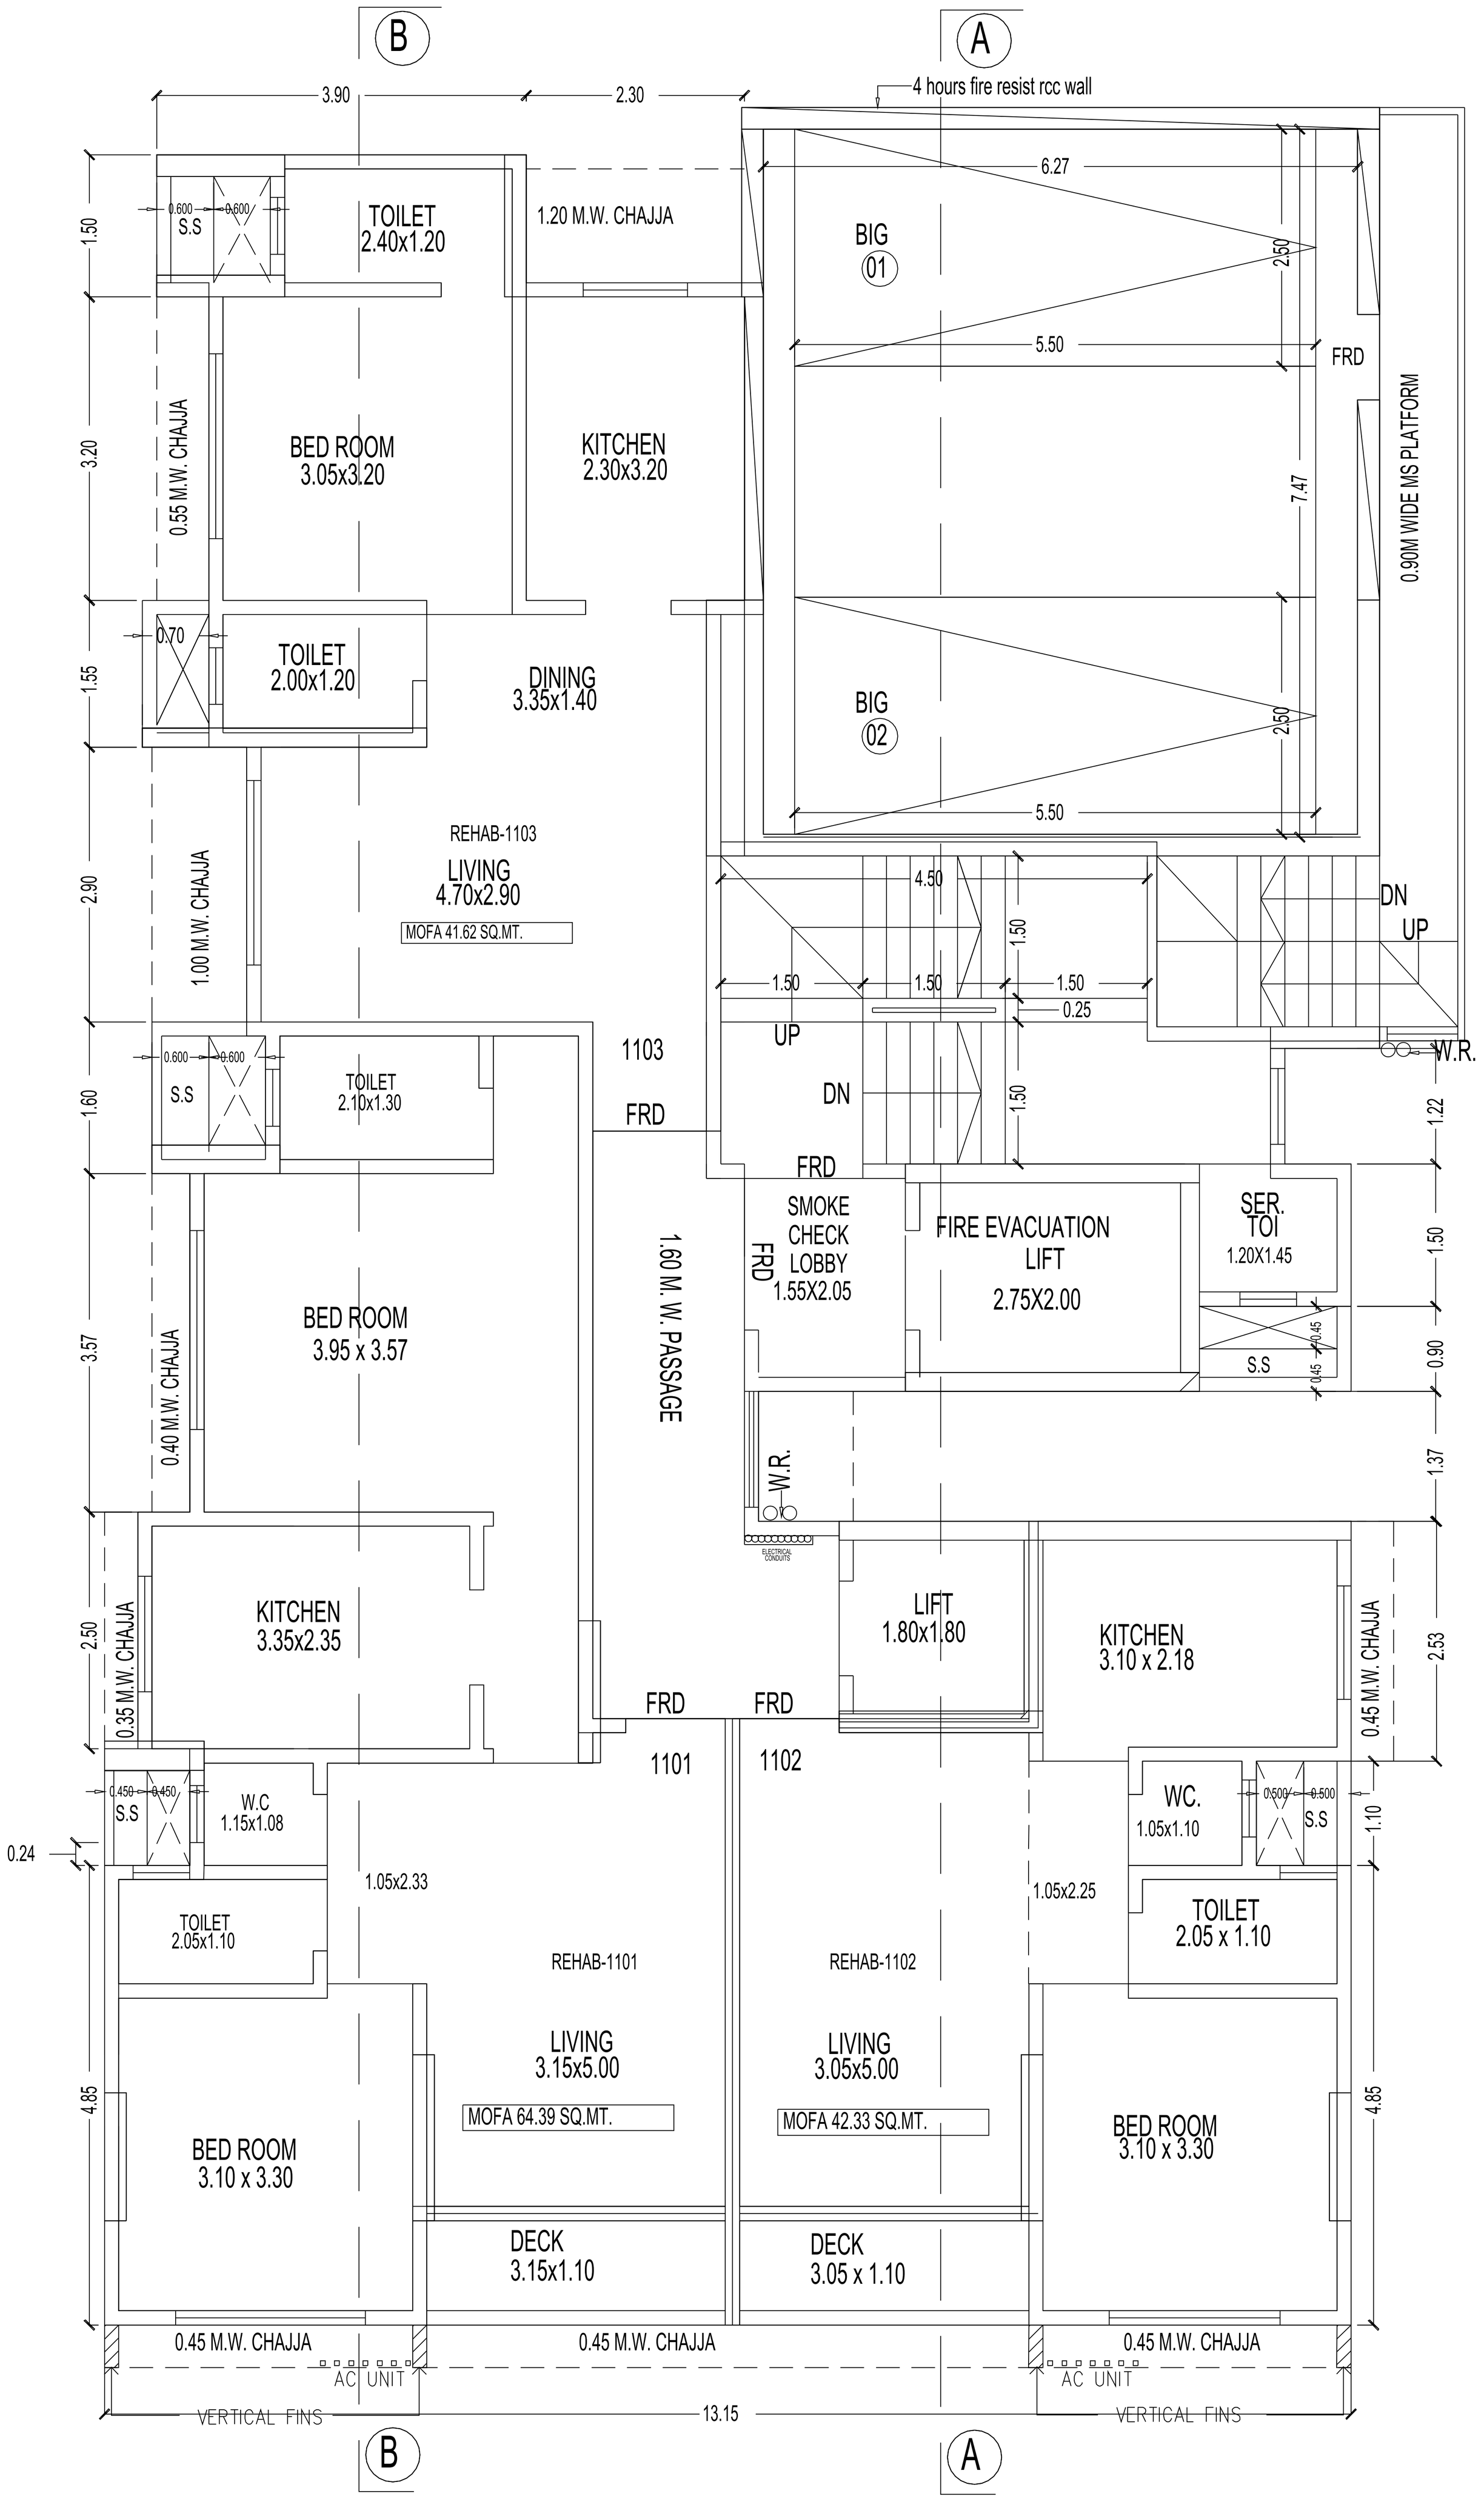


11TH FLOOR PLAN

SCALE - 1:100

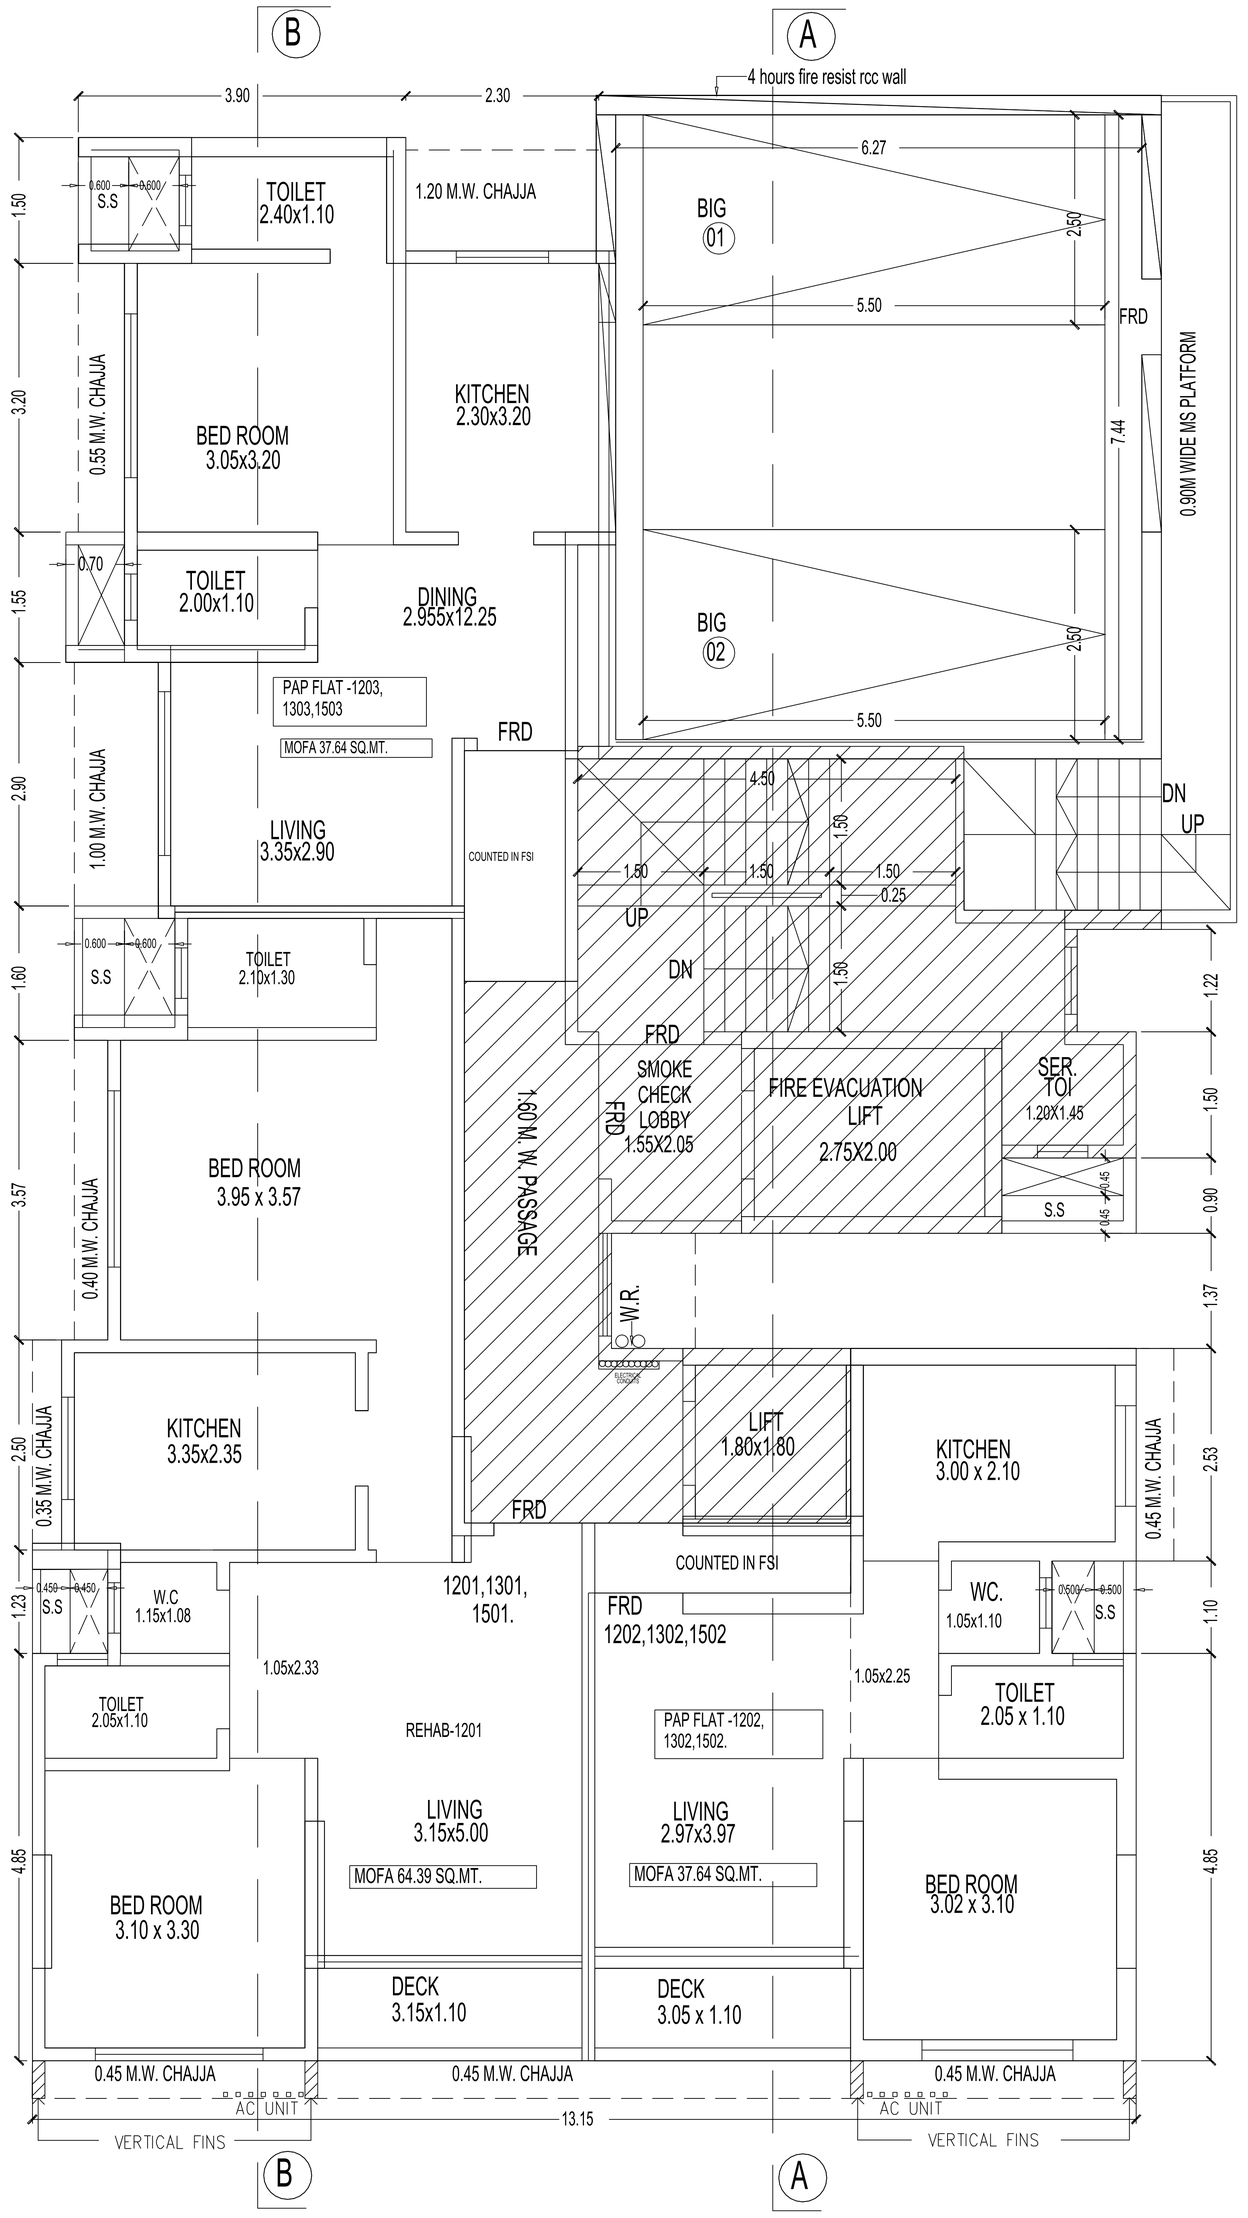


12TH,13TH,15TH FLOOR PLAN

SCALE - 1:100

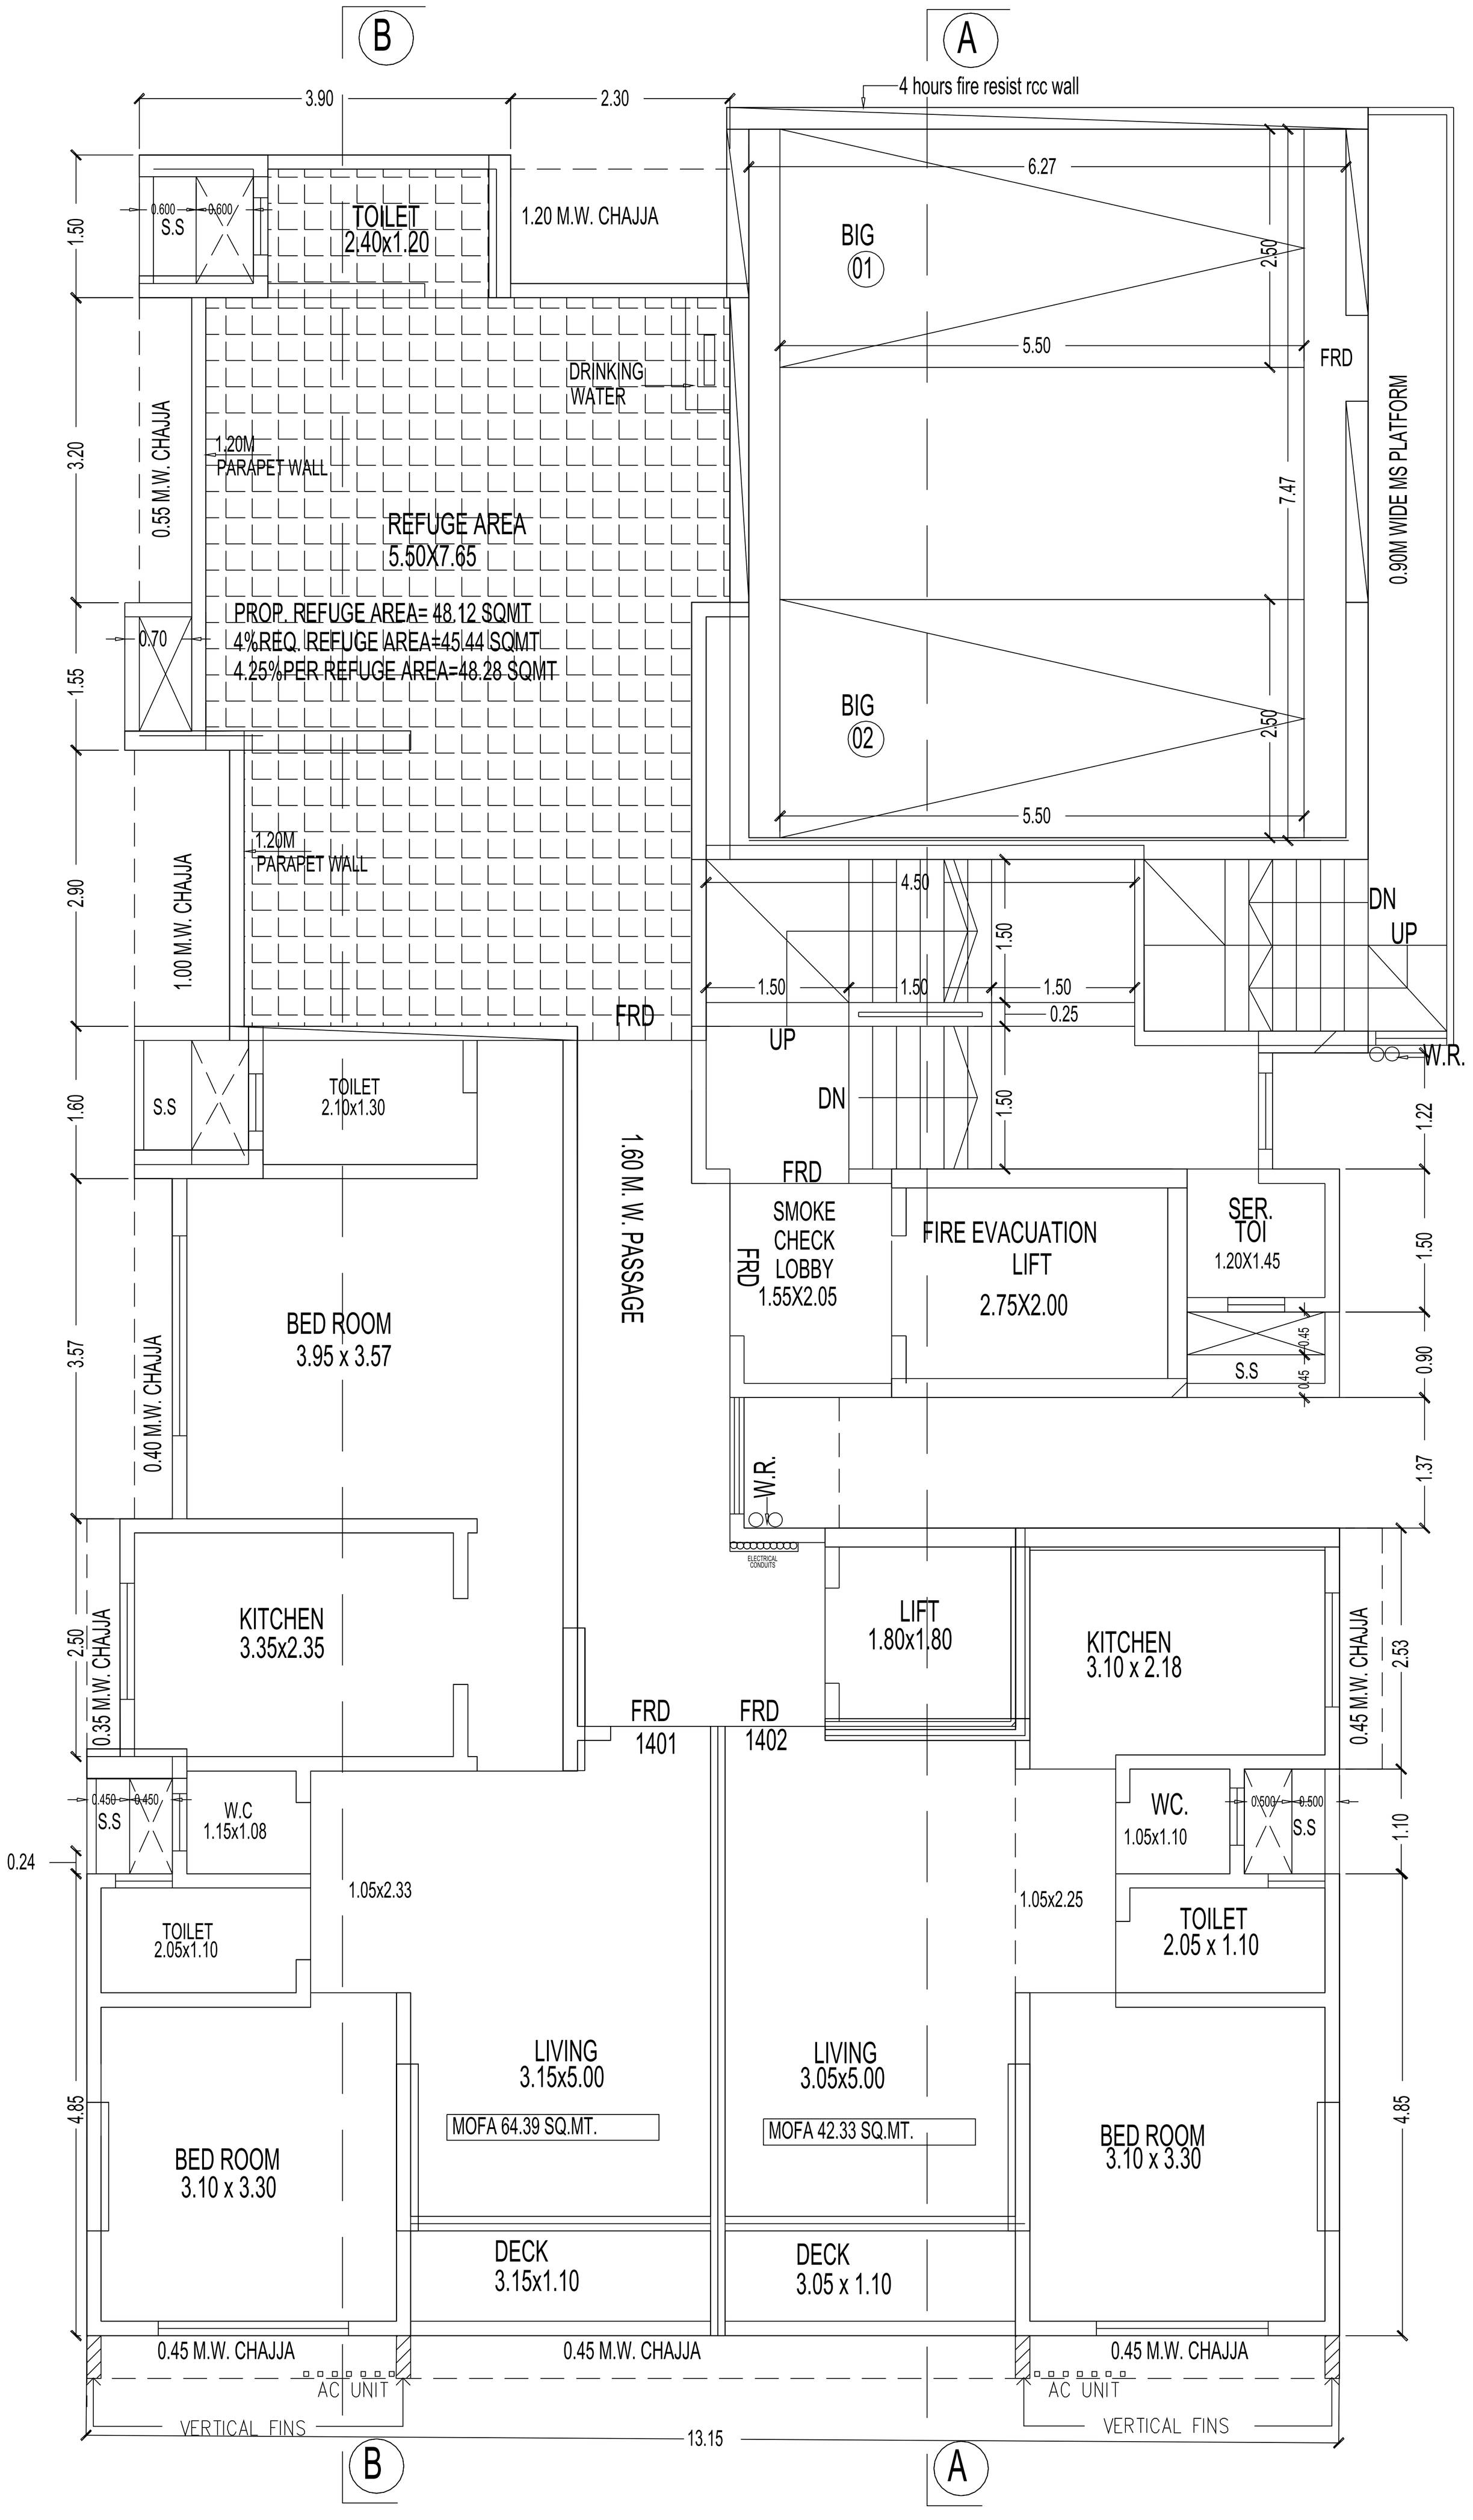

14TH REFUGE FLOOR PLAN

SCALE - 1:100

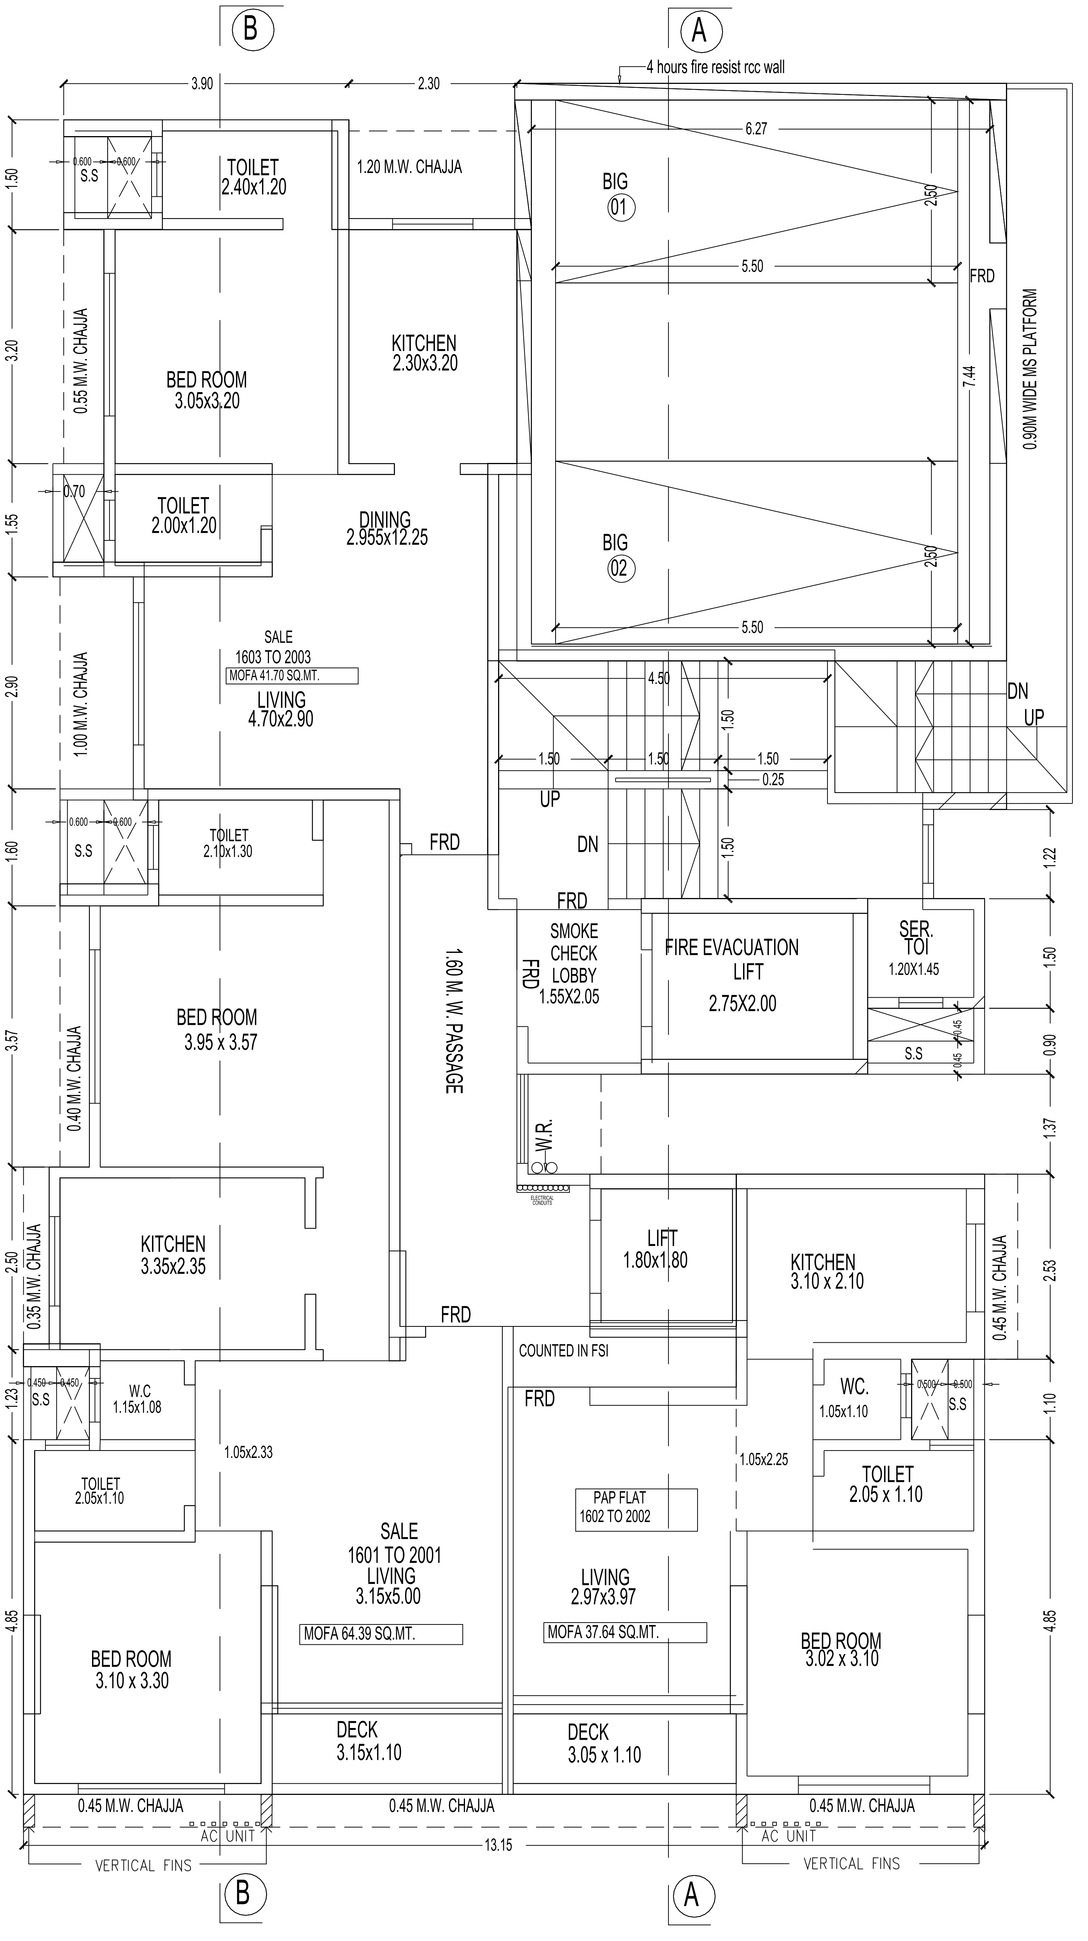

16TH TO 20TH FLOOR PLAN

SCALE - 1:100