

2ND FLOOR LINE AREA DIAGRAM

SCALE - 1: 100

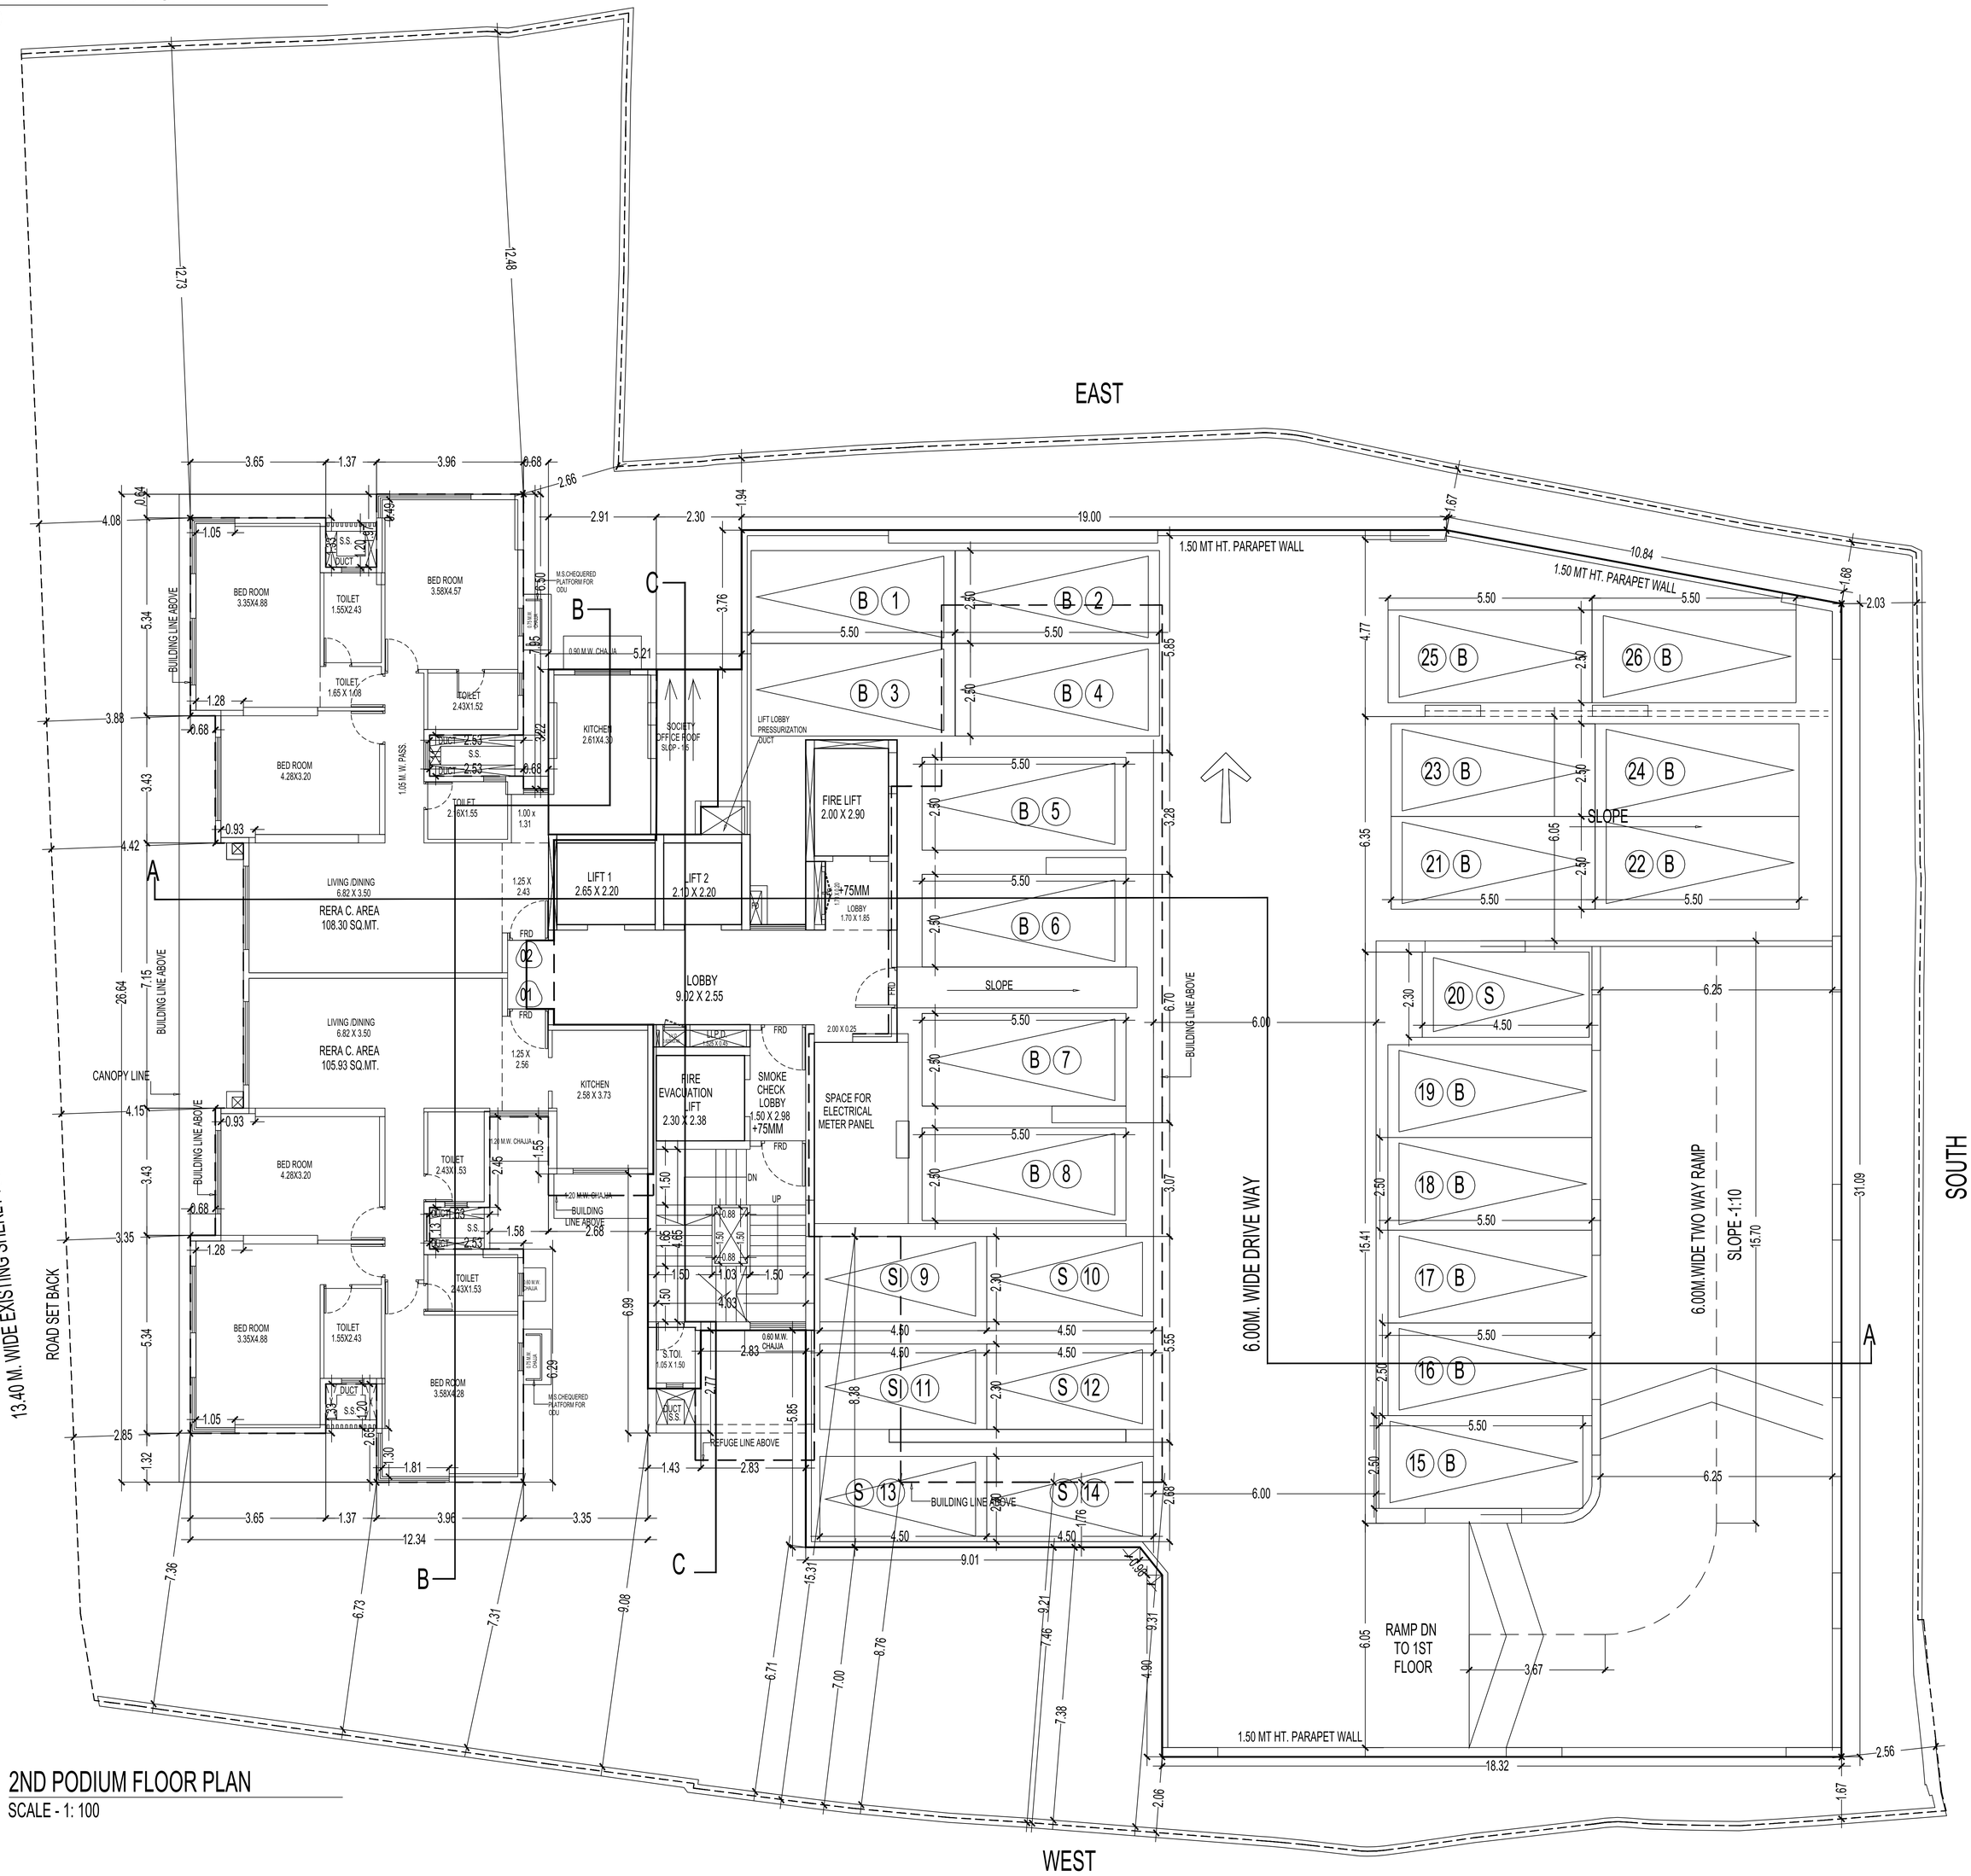


2ND PODIUM FLOOR PLAN

SCALE - 1: 100

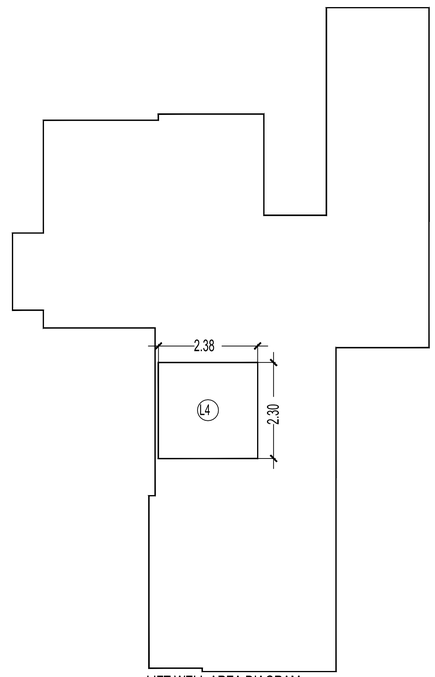

LIFT WELL AREA DIAGRAM
@ 4TH & 5TH FLOOR
SCALE - 1: 100

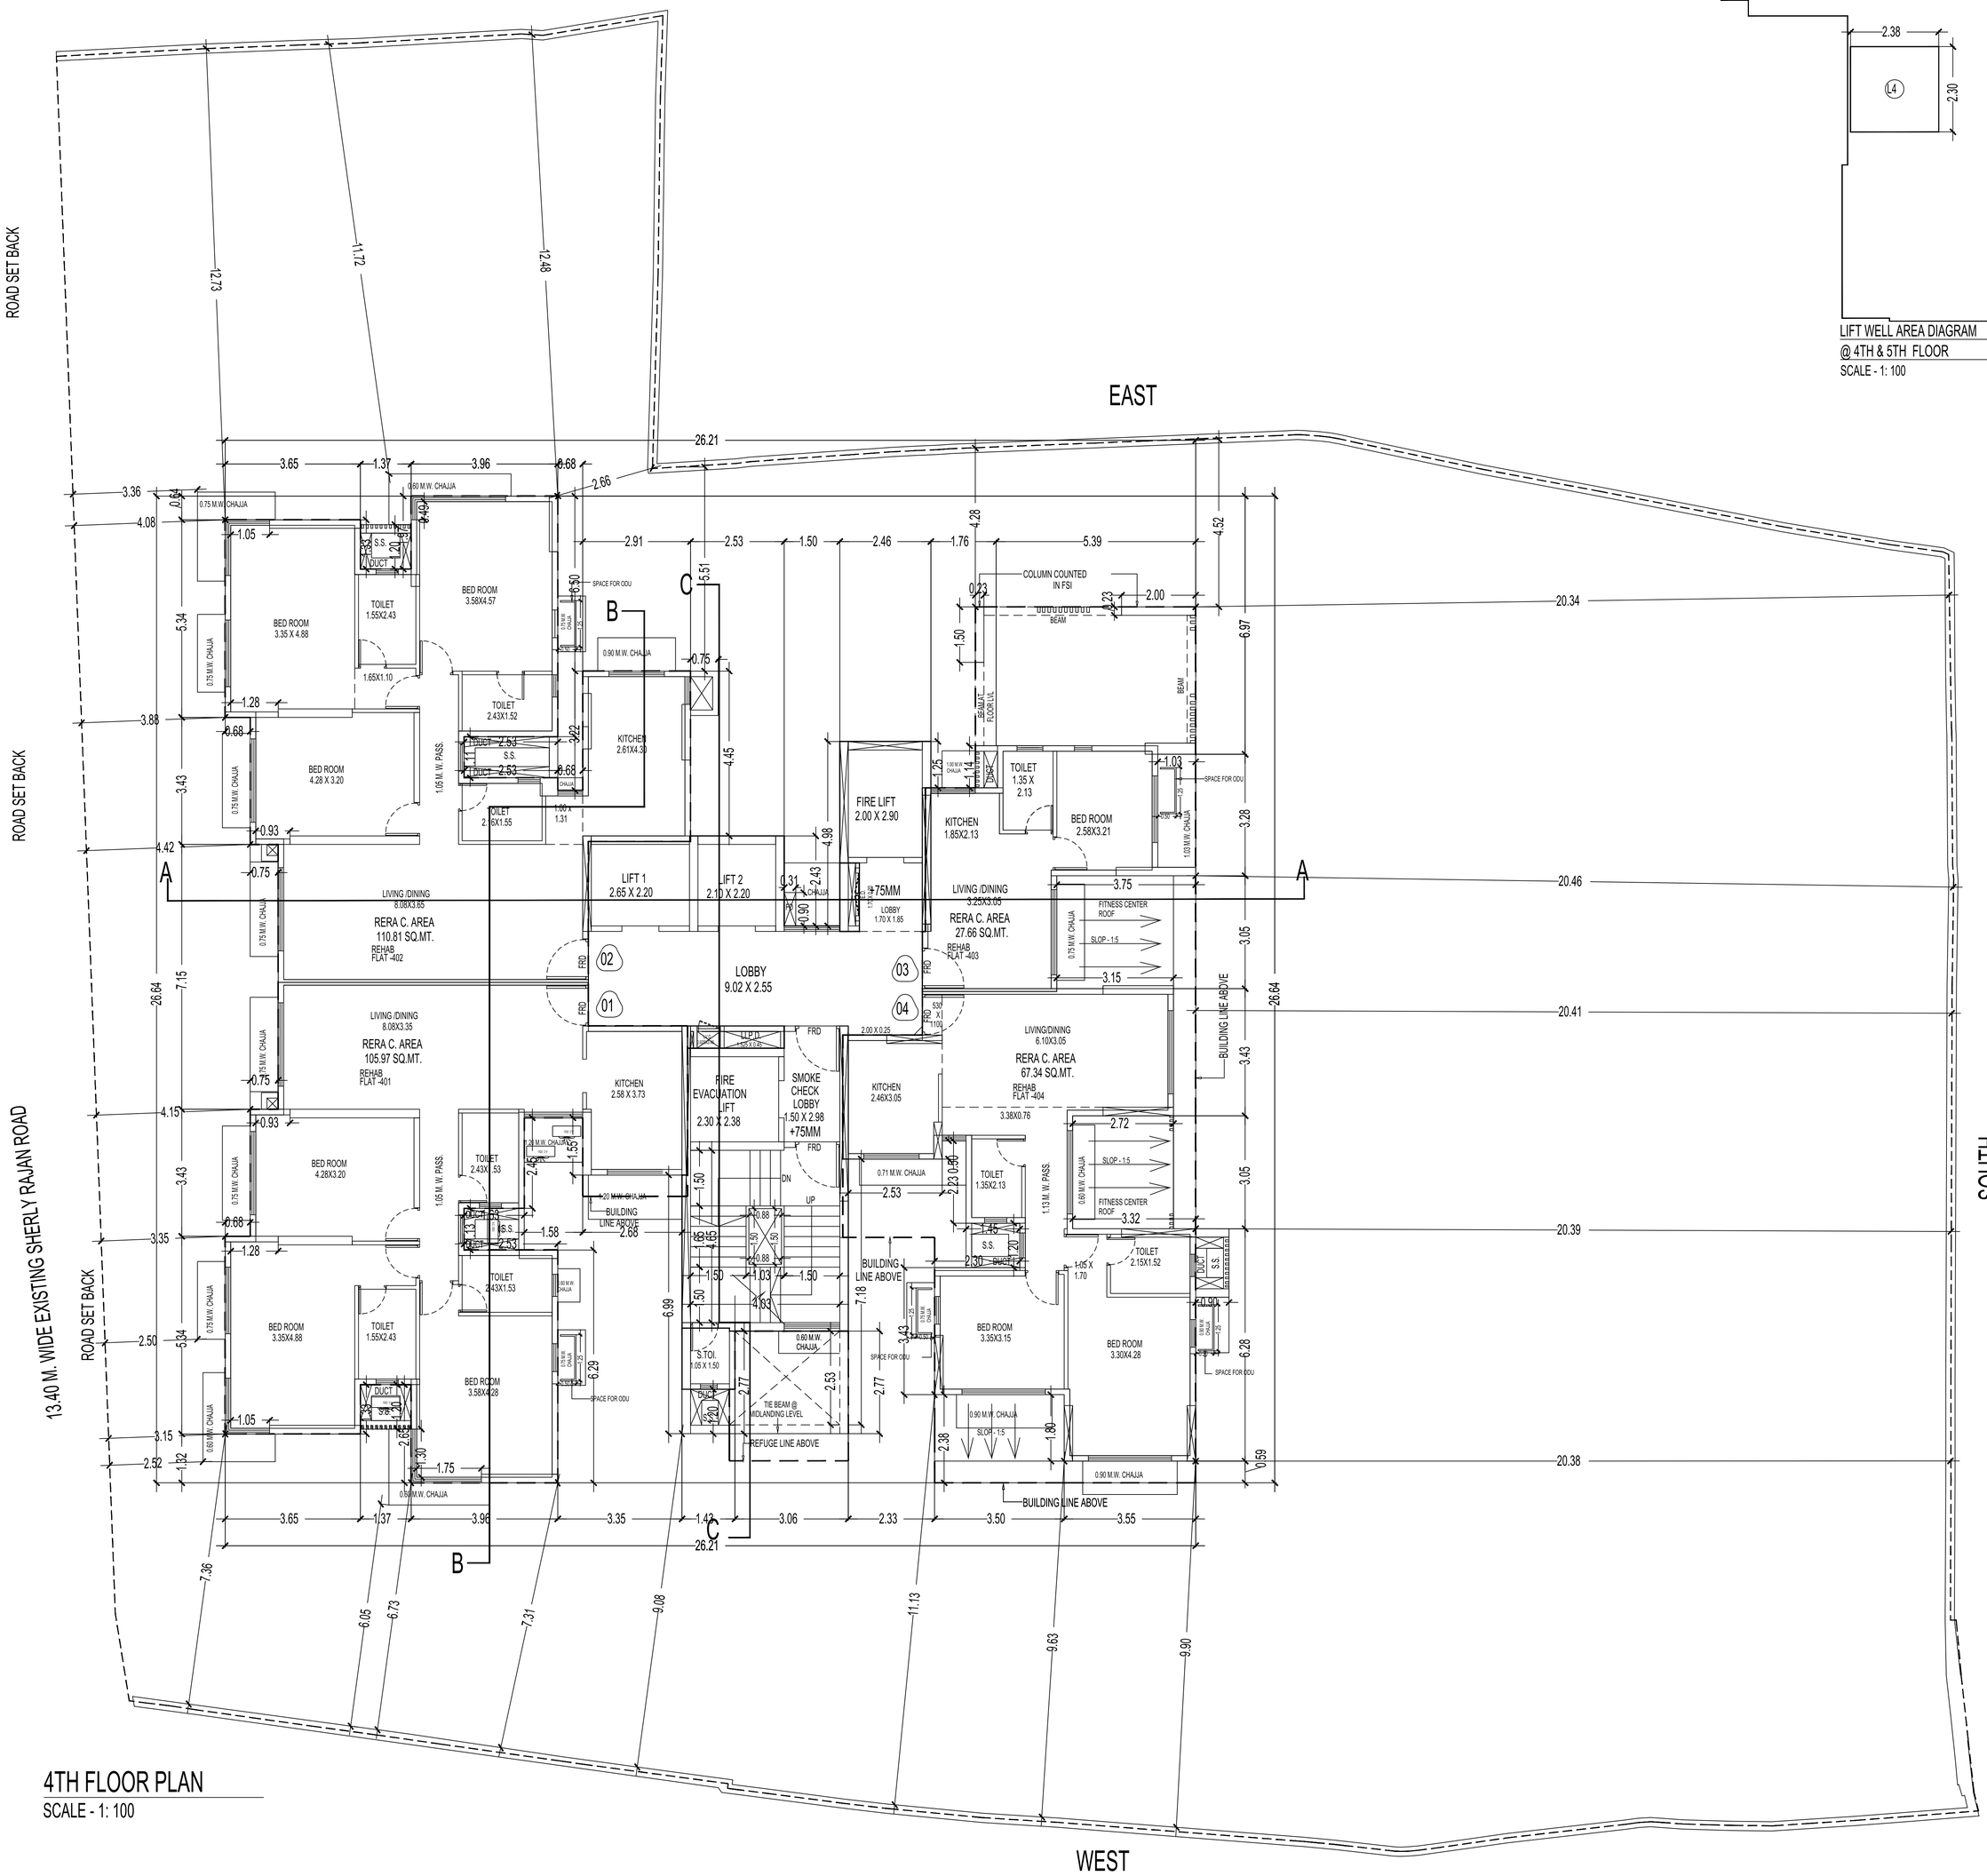



4TH FLOOR PLAN
SCALE - 1: 100

5TH FLOOR LINE AREA DIAGRAM

SCALE - 1: 100

SCALE - 1: 100

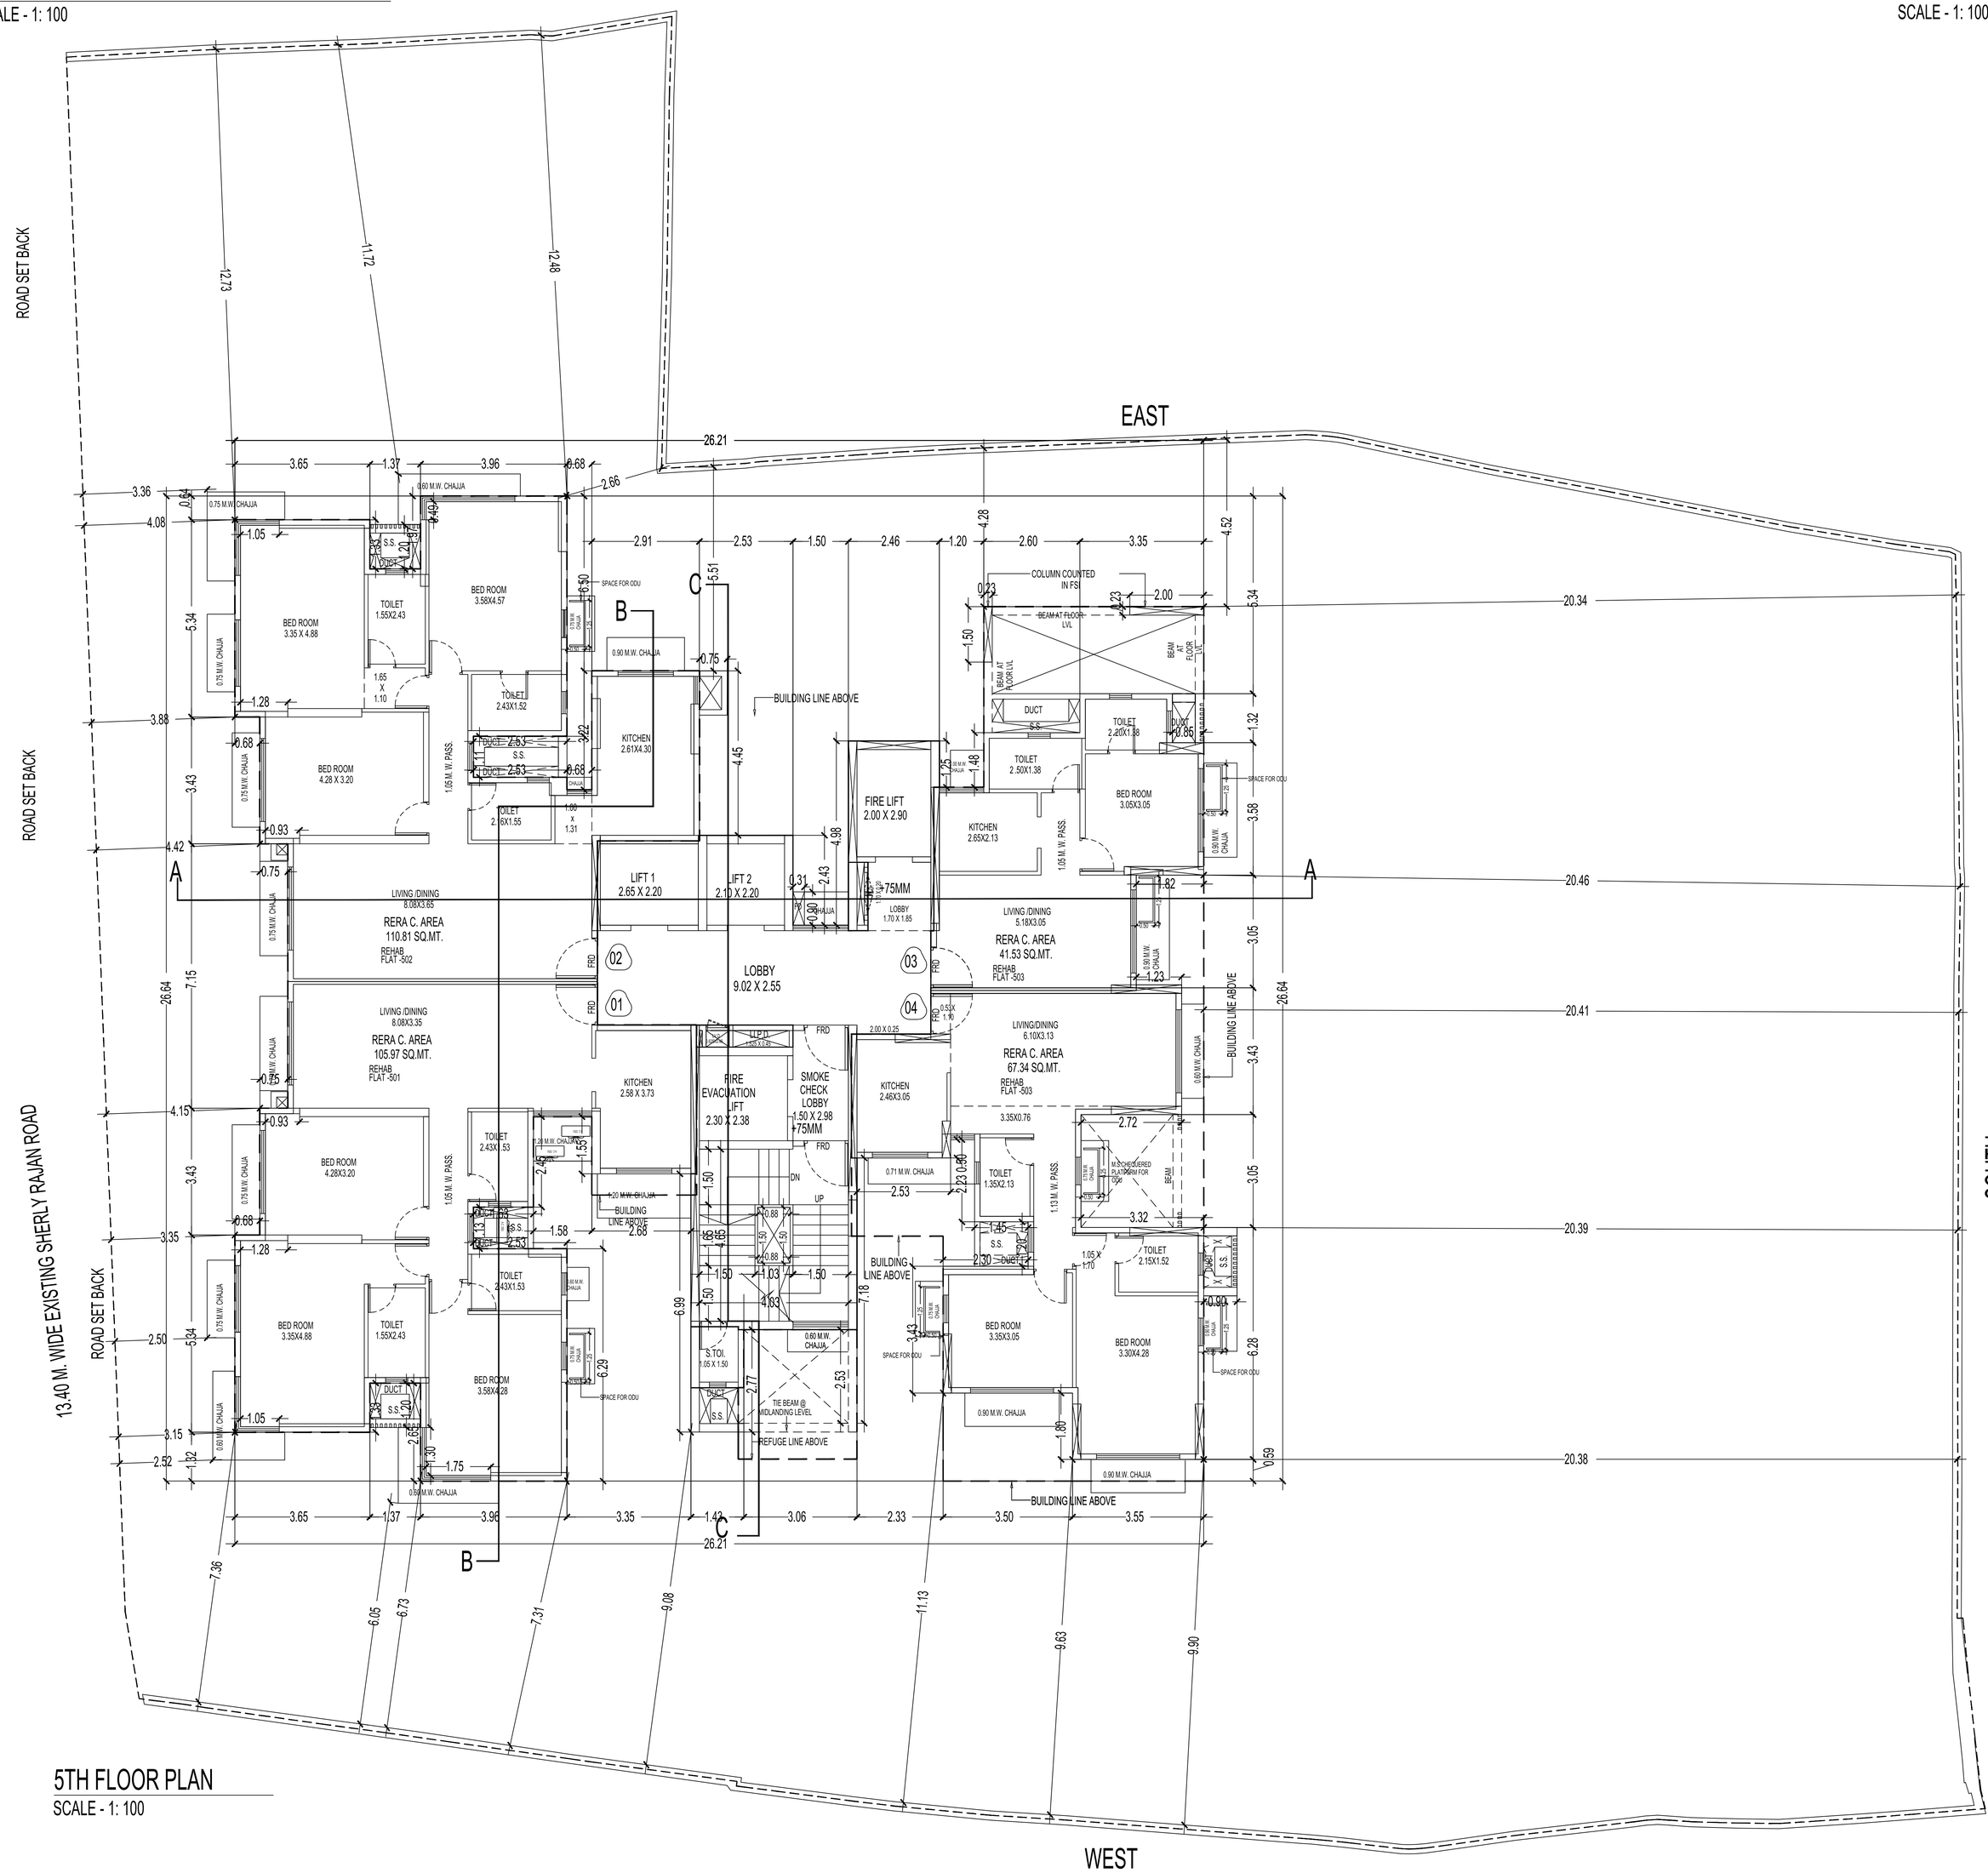

NORTH
SOUTH
EAST
WEST
ROAD SET BACK
ROAD SET BACK
ROAD SET BACK
13.40 M. WIDE EXISTING SHERLY RAJAN ROAD
BUILDING LINE ABOVE
REFUGE LINE ABOVE
BUILDING LINE ABOVE
BUILDING LINE ABOVE
BUILDING

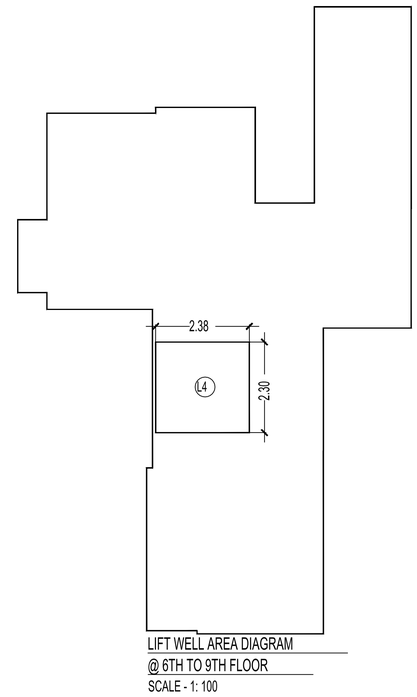

LIFT WELL AREA DIAGRAM
@ 6TH TO 9TH FLOOR
SCALE - 1: 100




6TH FLOOR PLAN
SCALE - 1: 100

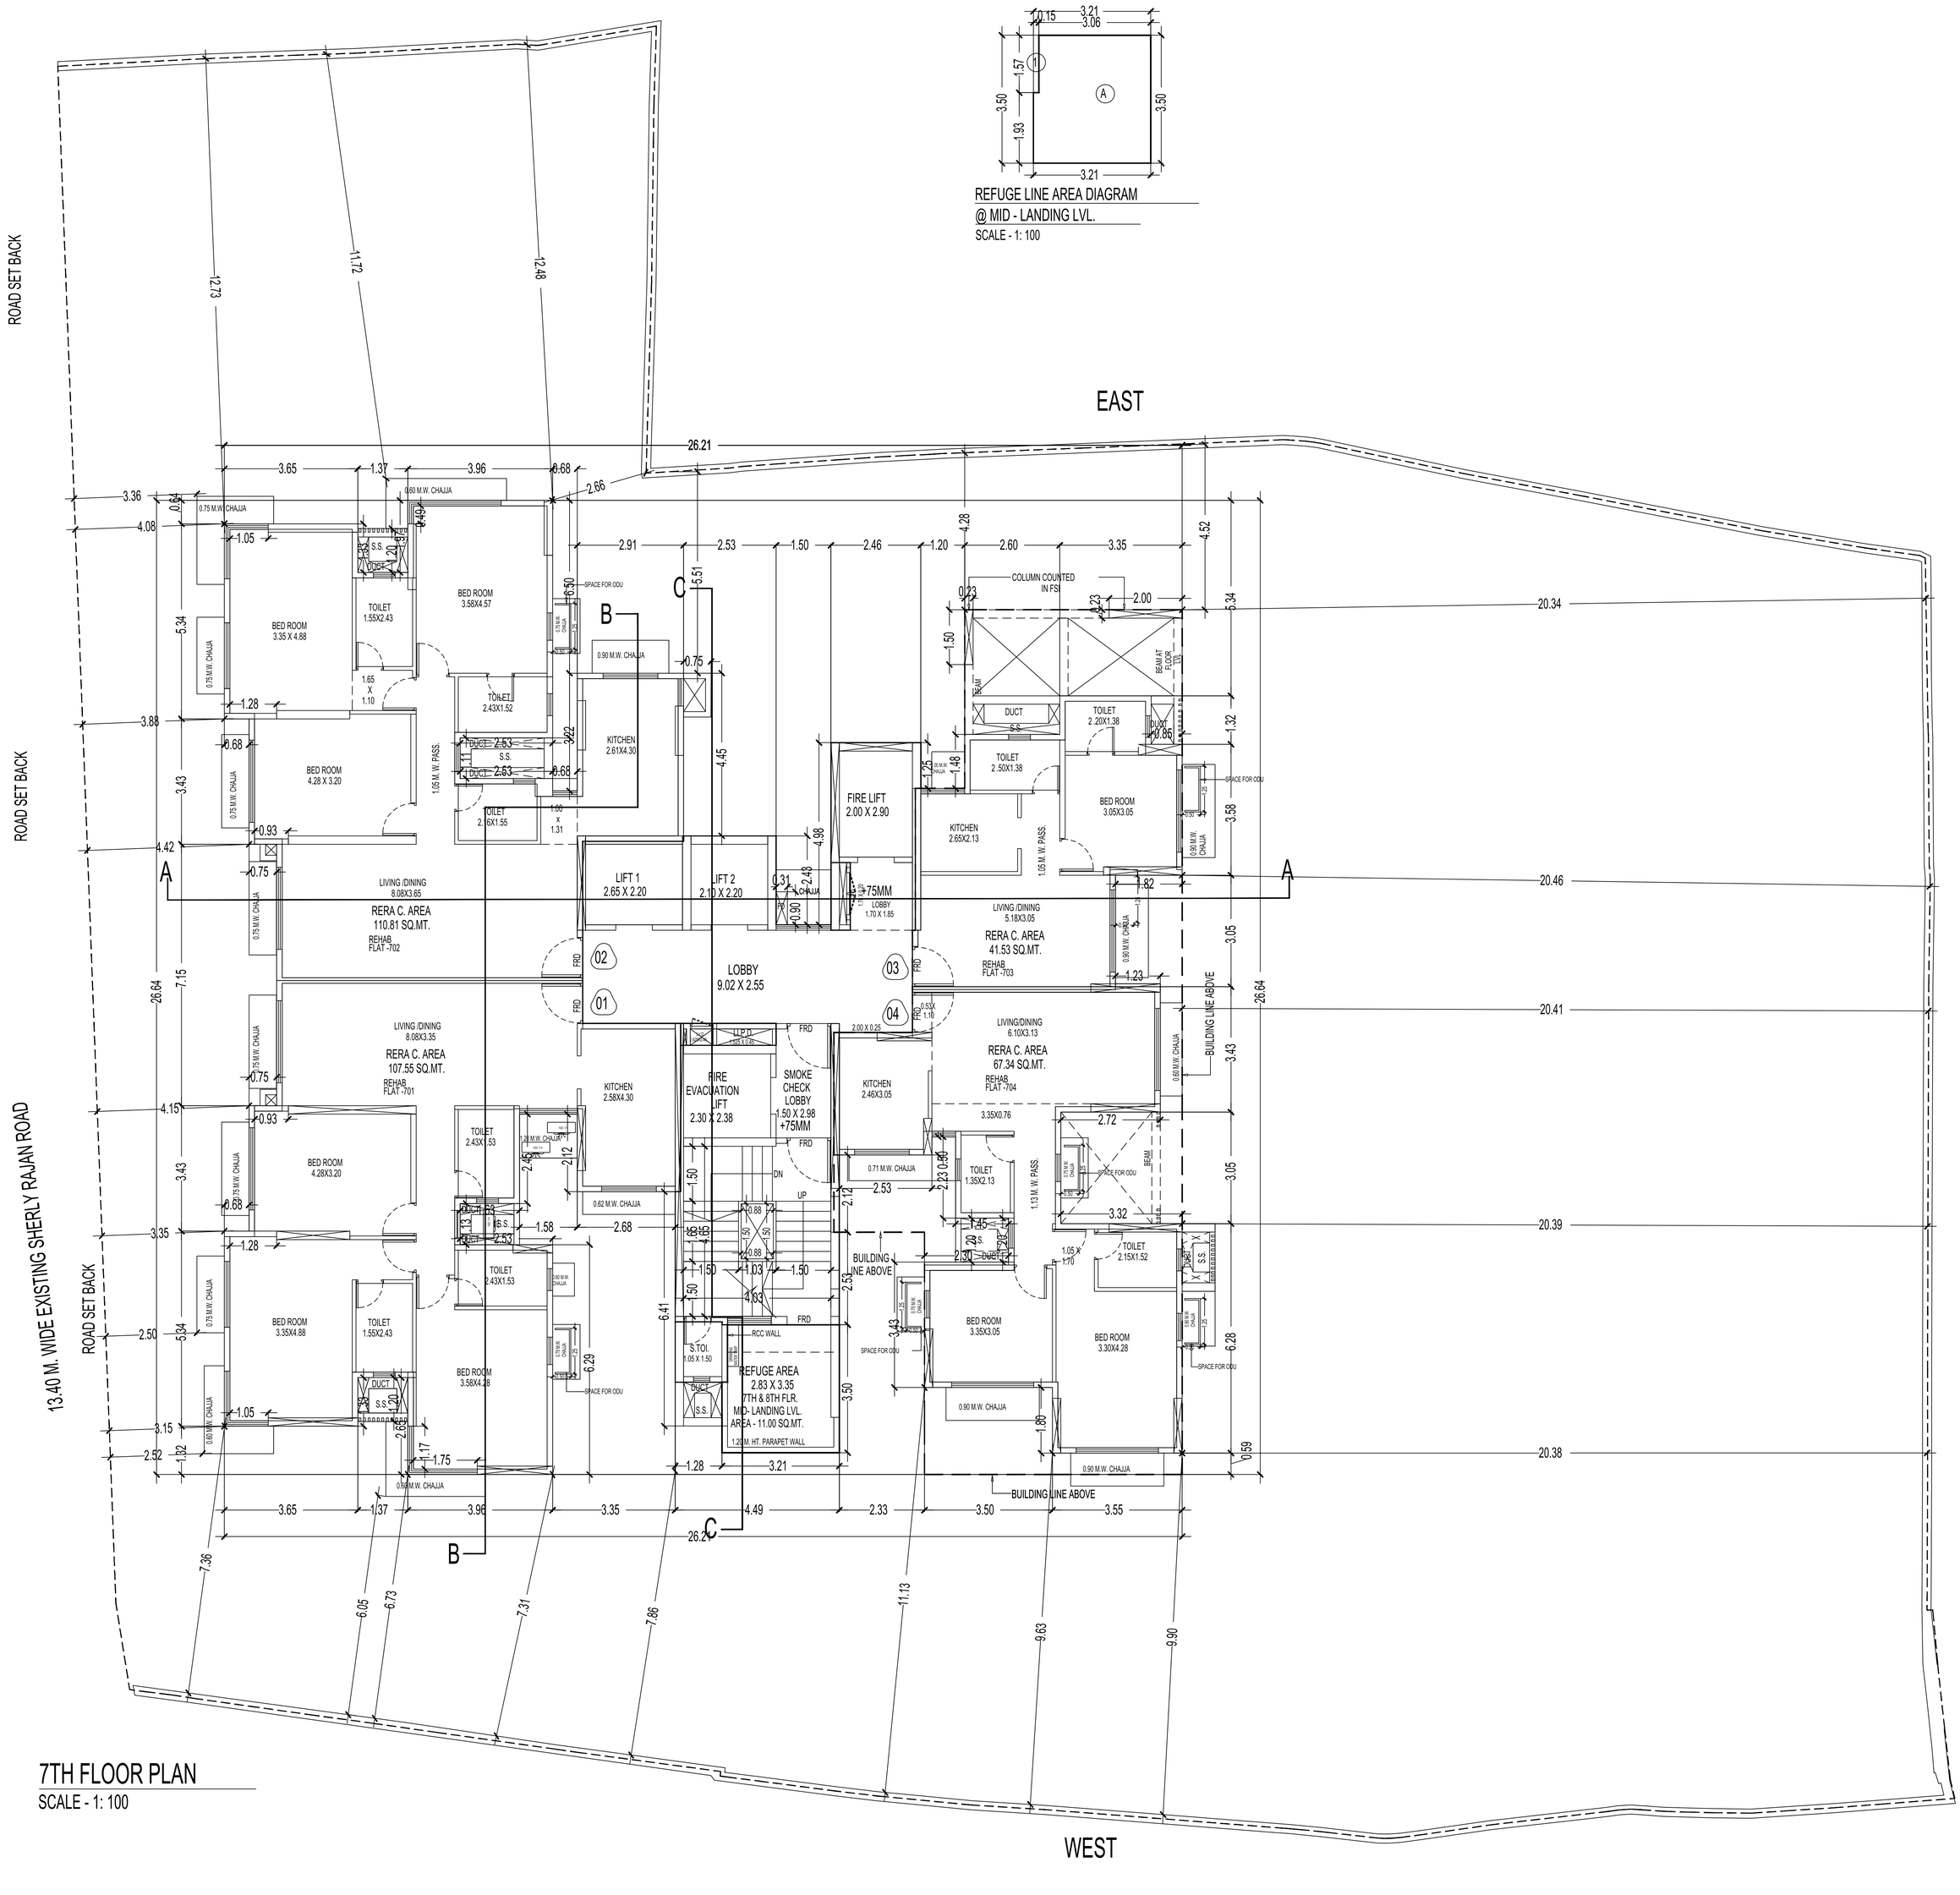
REFUGE LINE AREA DIAGRAM
@ MID - LANDING LVL.
SCALE - 1: 100
7TH FLOOR PLAN
SCALE - 1: 100
NORTH
SOUTH
EAST
WEST
ROAD SET BACK
13.40 M. WIDE EXISTING SHERLY RAJAN ROAD
LIFT 1
2.65 X 2.20
LIFT 2
2.10 X 2.20
FIRE LIFT
2.00 X 2.90
LOBBY
9.02 X 2.55
LOBBY
1.70 X 1.85
FIRE
EVACUATION
LIFT
2.30 X 2.38
SMOKE
CHECK
LOBBY
1.50 X 2.98
+75MM
REFUGE AREA
2.83 X 3.35
7TH & 8TH FLR.
MID- LANDING LVL.
AREA - 11.00 SQ.MT.
1.20 M. HT. PARAPET WALL
RERA C. AREA
110.81 SQ.MT.
REHAB
FLAT -702
RERA C. AREA
107.55 SQ.MT.
REHAB
FLAT -701
RERA C. AREA
41.53 SQ.MT.
REHAB
FLAT -703
RERA C. AREA
67.34 SQ.MT.
REHAB
FLAT -704
BUILDING
LINE ABOVE
COLUMN COUNTED
IN FSI
SPACE FOR ODU
BED ROOM
3.35 X 4.88
BED ROOM
4.28 X 3.20
BED ROOM
3.58X4.57
BED ROOM
4.28X3.20
BED ROOM
3.35X4.88
BED ROOM
3.58X4.28
BED ROOM
3.05X3.05
BED ROOM
3.35X3.05
BED ROOM
3.30X4.28
TOILET
1.55X2.43
TOILET
2.43X1.52
TOILET
2.6X1.55
TOILET
2.43X1.53
TOILET
1.55X2.43
TOILET
2.50X1.38
TOILET
2.20X1.38
TOILET
1.35X2.13
TOILET
2.15X1.52
KITCHEN
2.61X4.30
KITCHEN
2.58X4.30
KITCHEN
2.65X2.13
KITCHEN
2.46X3.05
LIVING /DINING
8.08X3.65
LIVING /DINING
8.08X3.35
LIVING /DINING
5.18X3.05
LIVING/DINING
6.10X3.13
DUCT
S.S.
S TOI.
1.05 X 1.50
RCC WALL
0.75 M.W. CHAJJA
0.60 M.W. CHAJJA
0.90 M.W. CHAJJA
0.71 M.W. CHAJJA
0.62 M.W. CHAJJA
1.05 M. W. PASS.
1.13 M. W. PASS.
BEAM
BEAM AT
FLOOR
LVL.
DN
UP
FRD
LIFT
26.21
20.34
20.46
20.41
20.39
20.38
26.64
6.34
4.52
3.58
3.05
3.43
6.28
6.29
6.41
3.50
7.36
6.05
6.73
7.31
7.86
11.13
9.63
9.90


8TH & 9TH FLOOR LINE AREA DIAGRAM

SCALE - 1: 100

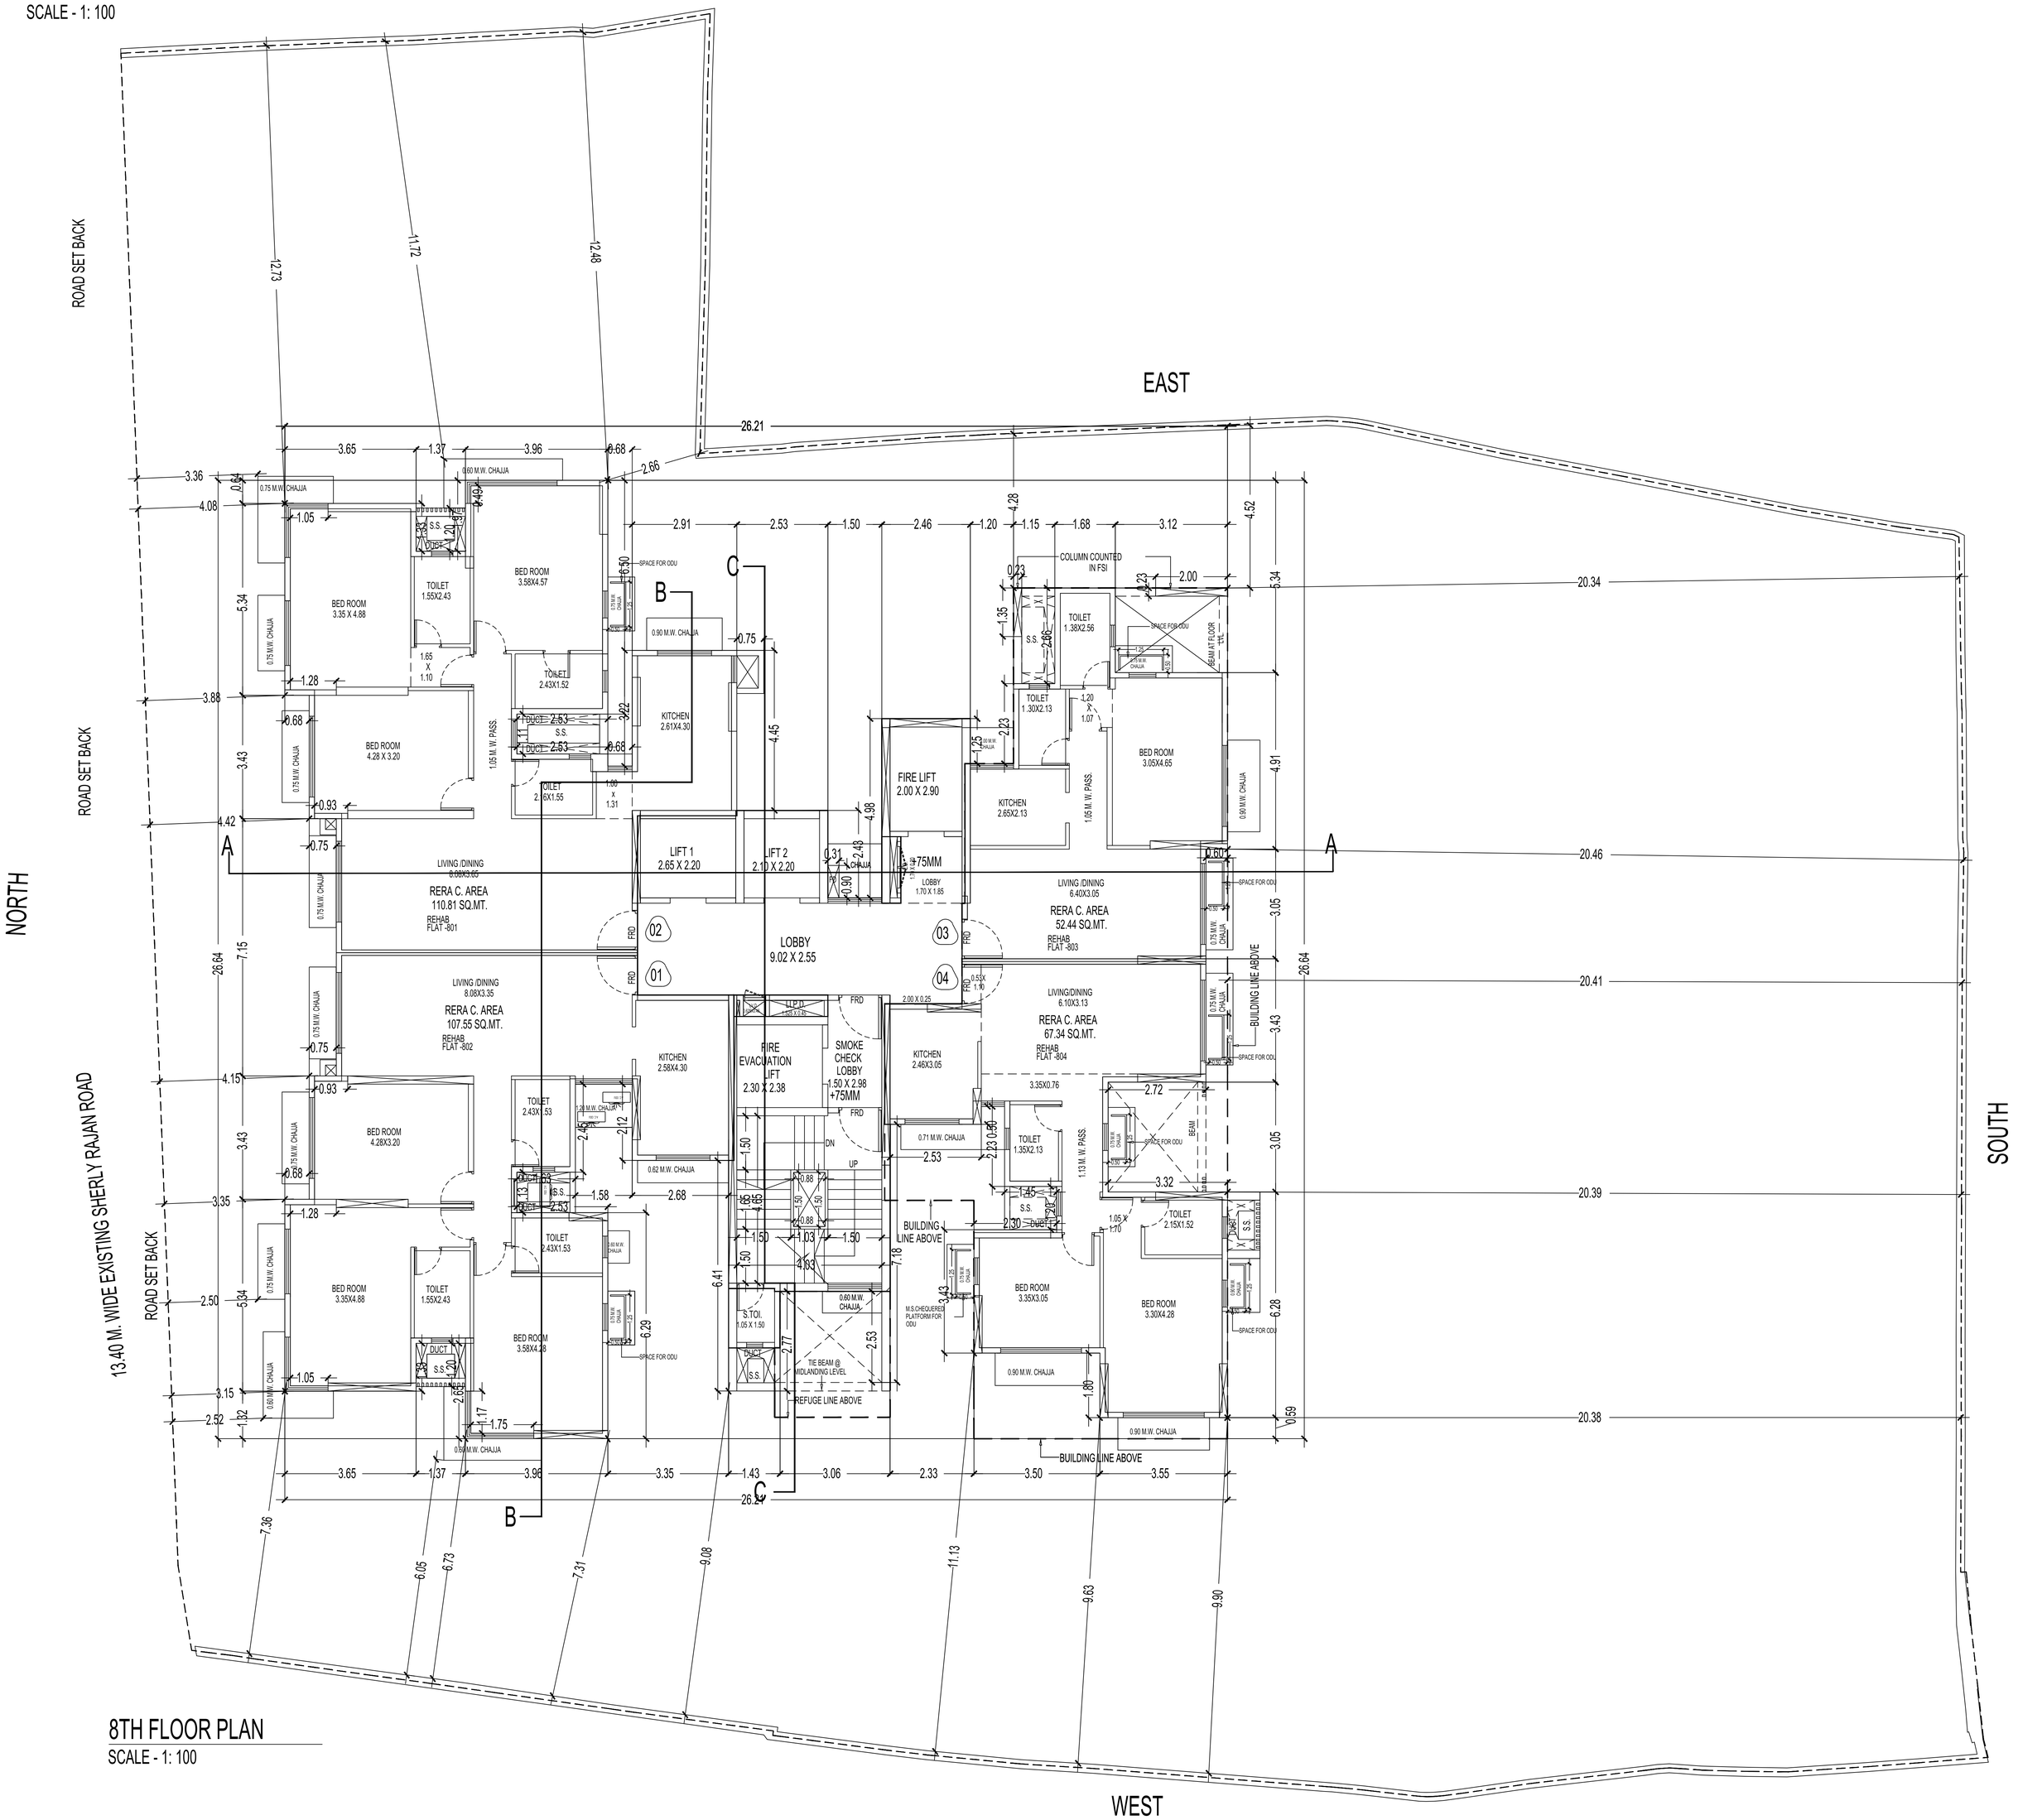

8TH FLOOR PLAN


SCALE - 1: 100

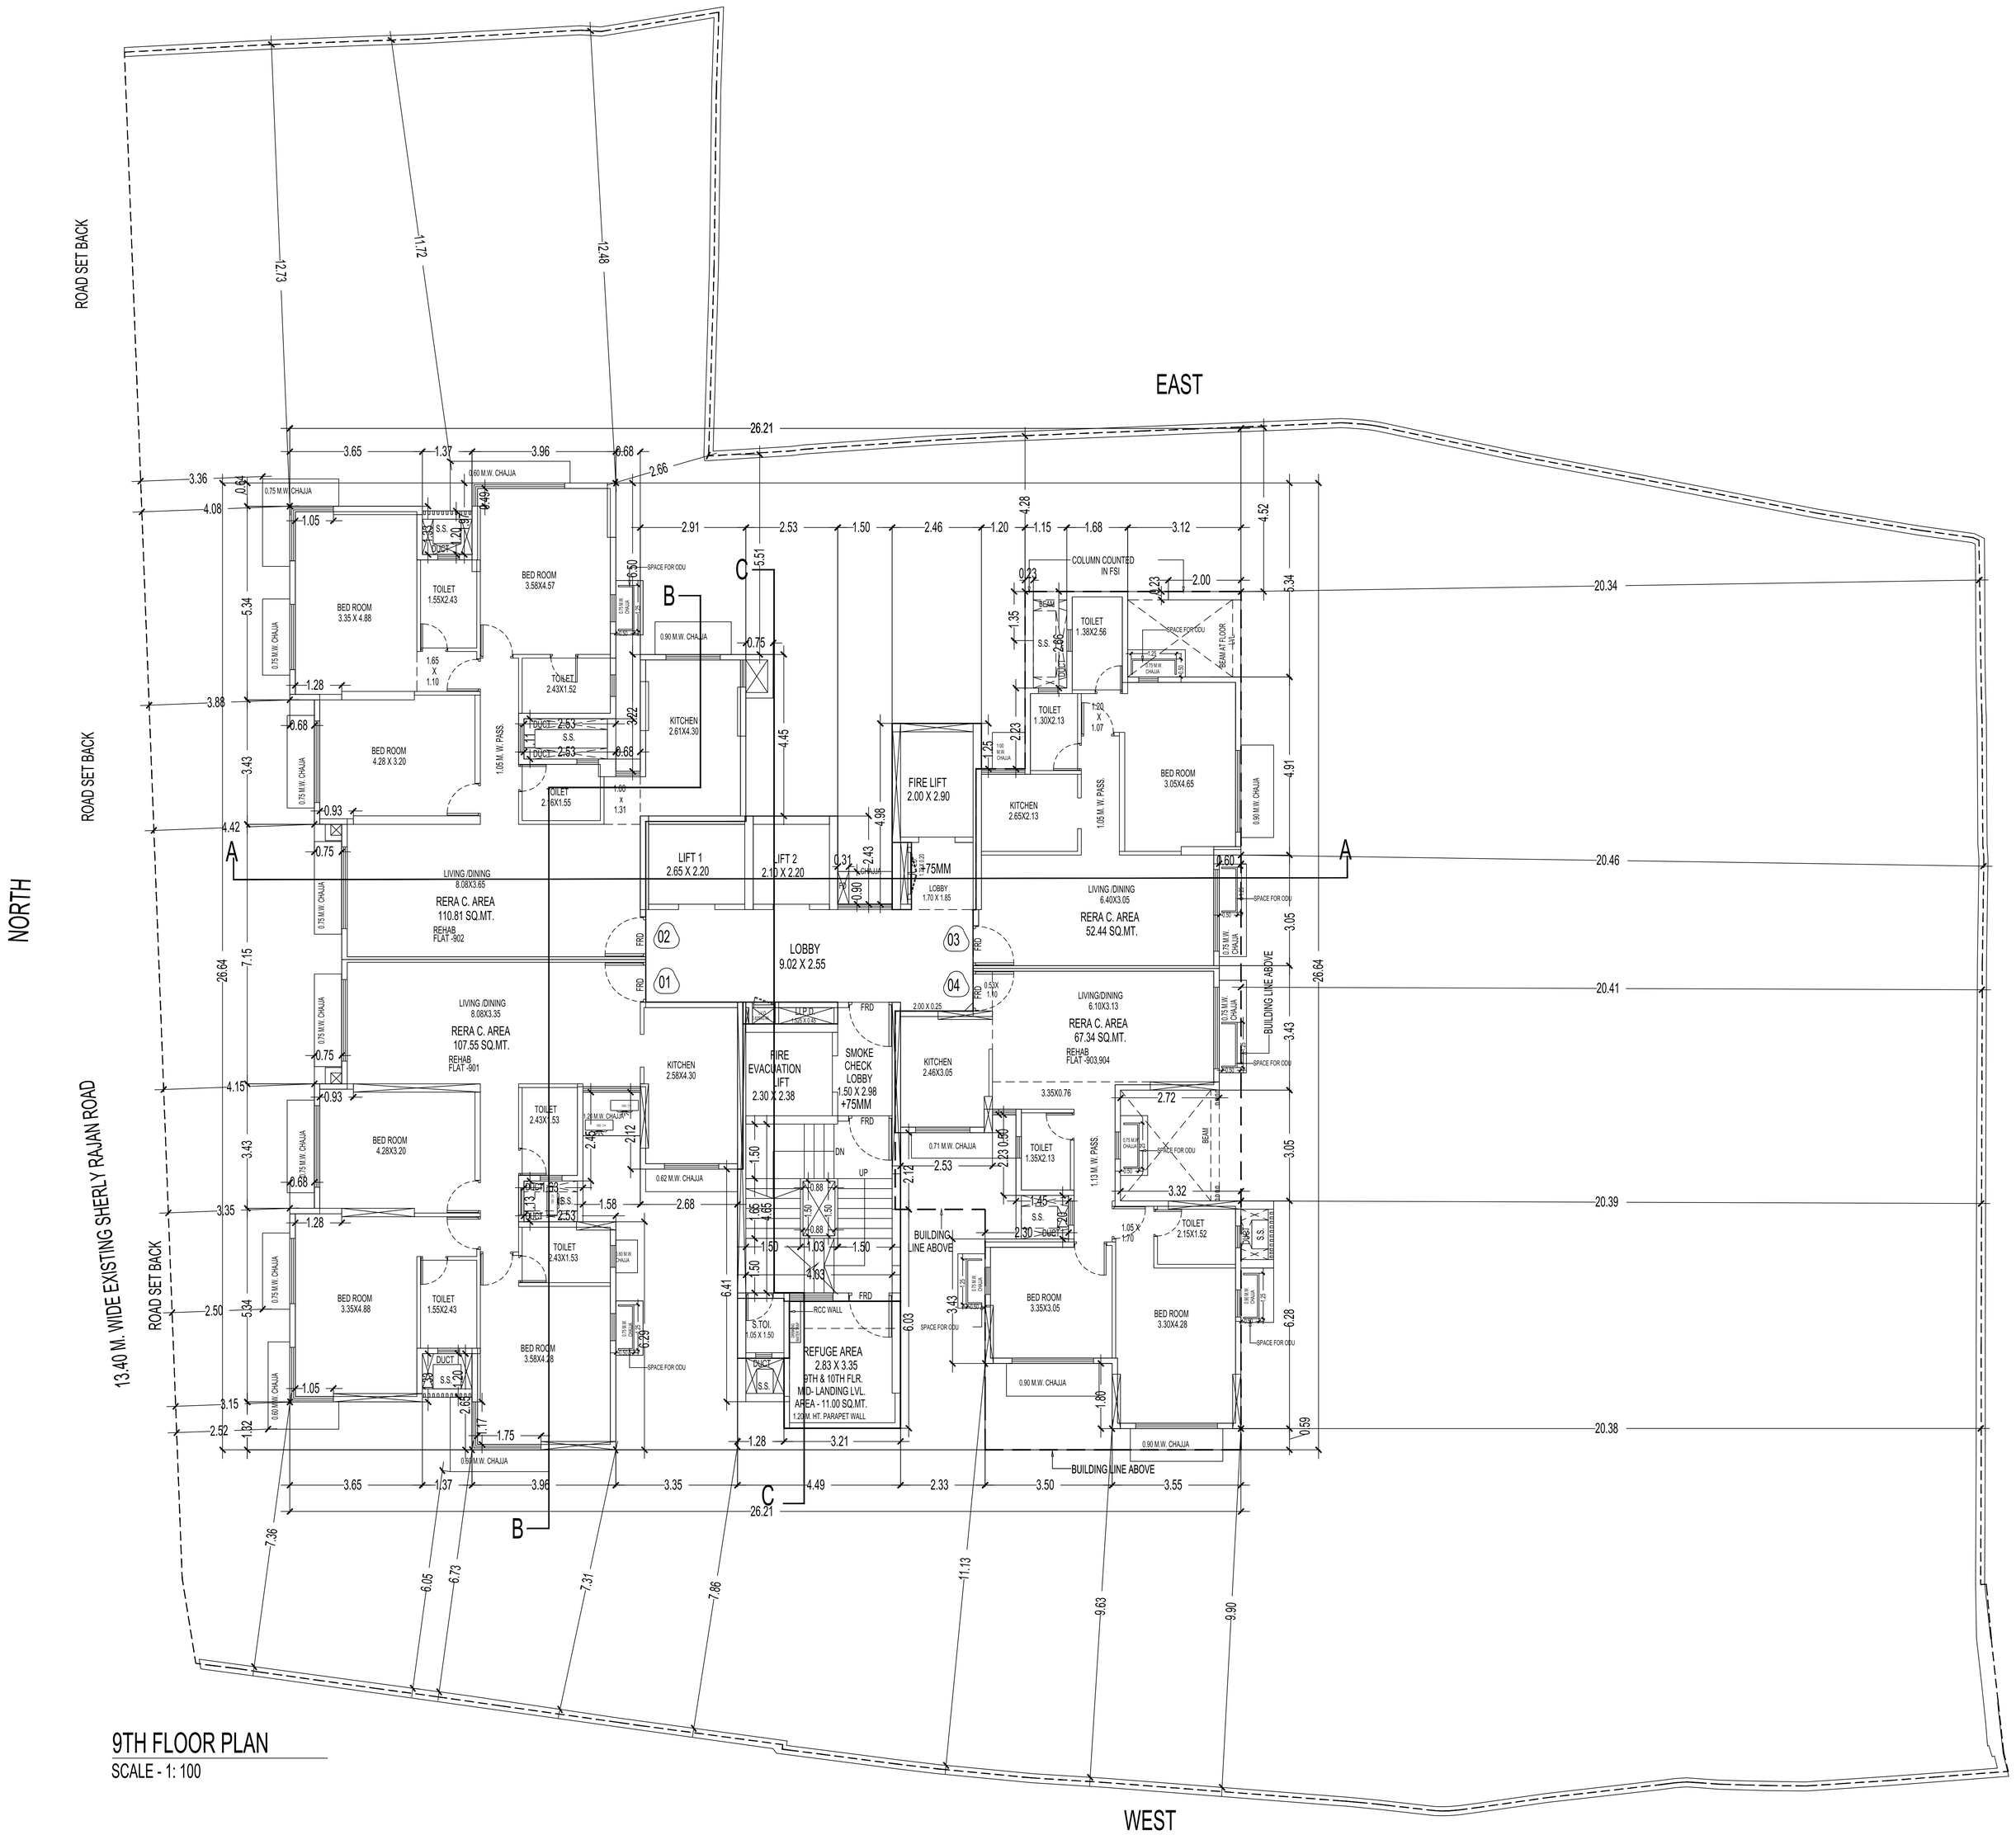

9TH FLOOR PLAN

SCALE - 1: 100

SCALE - 1: 100

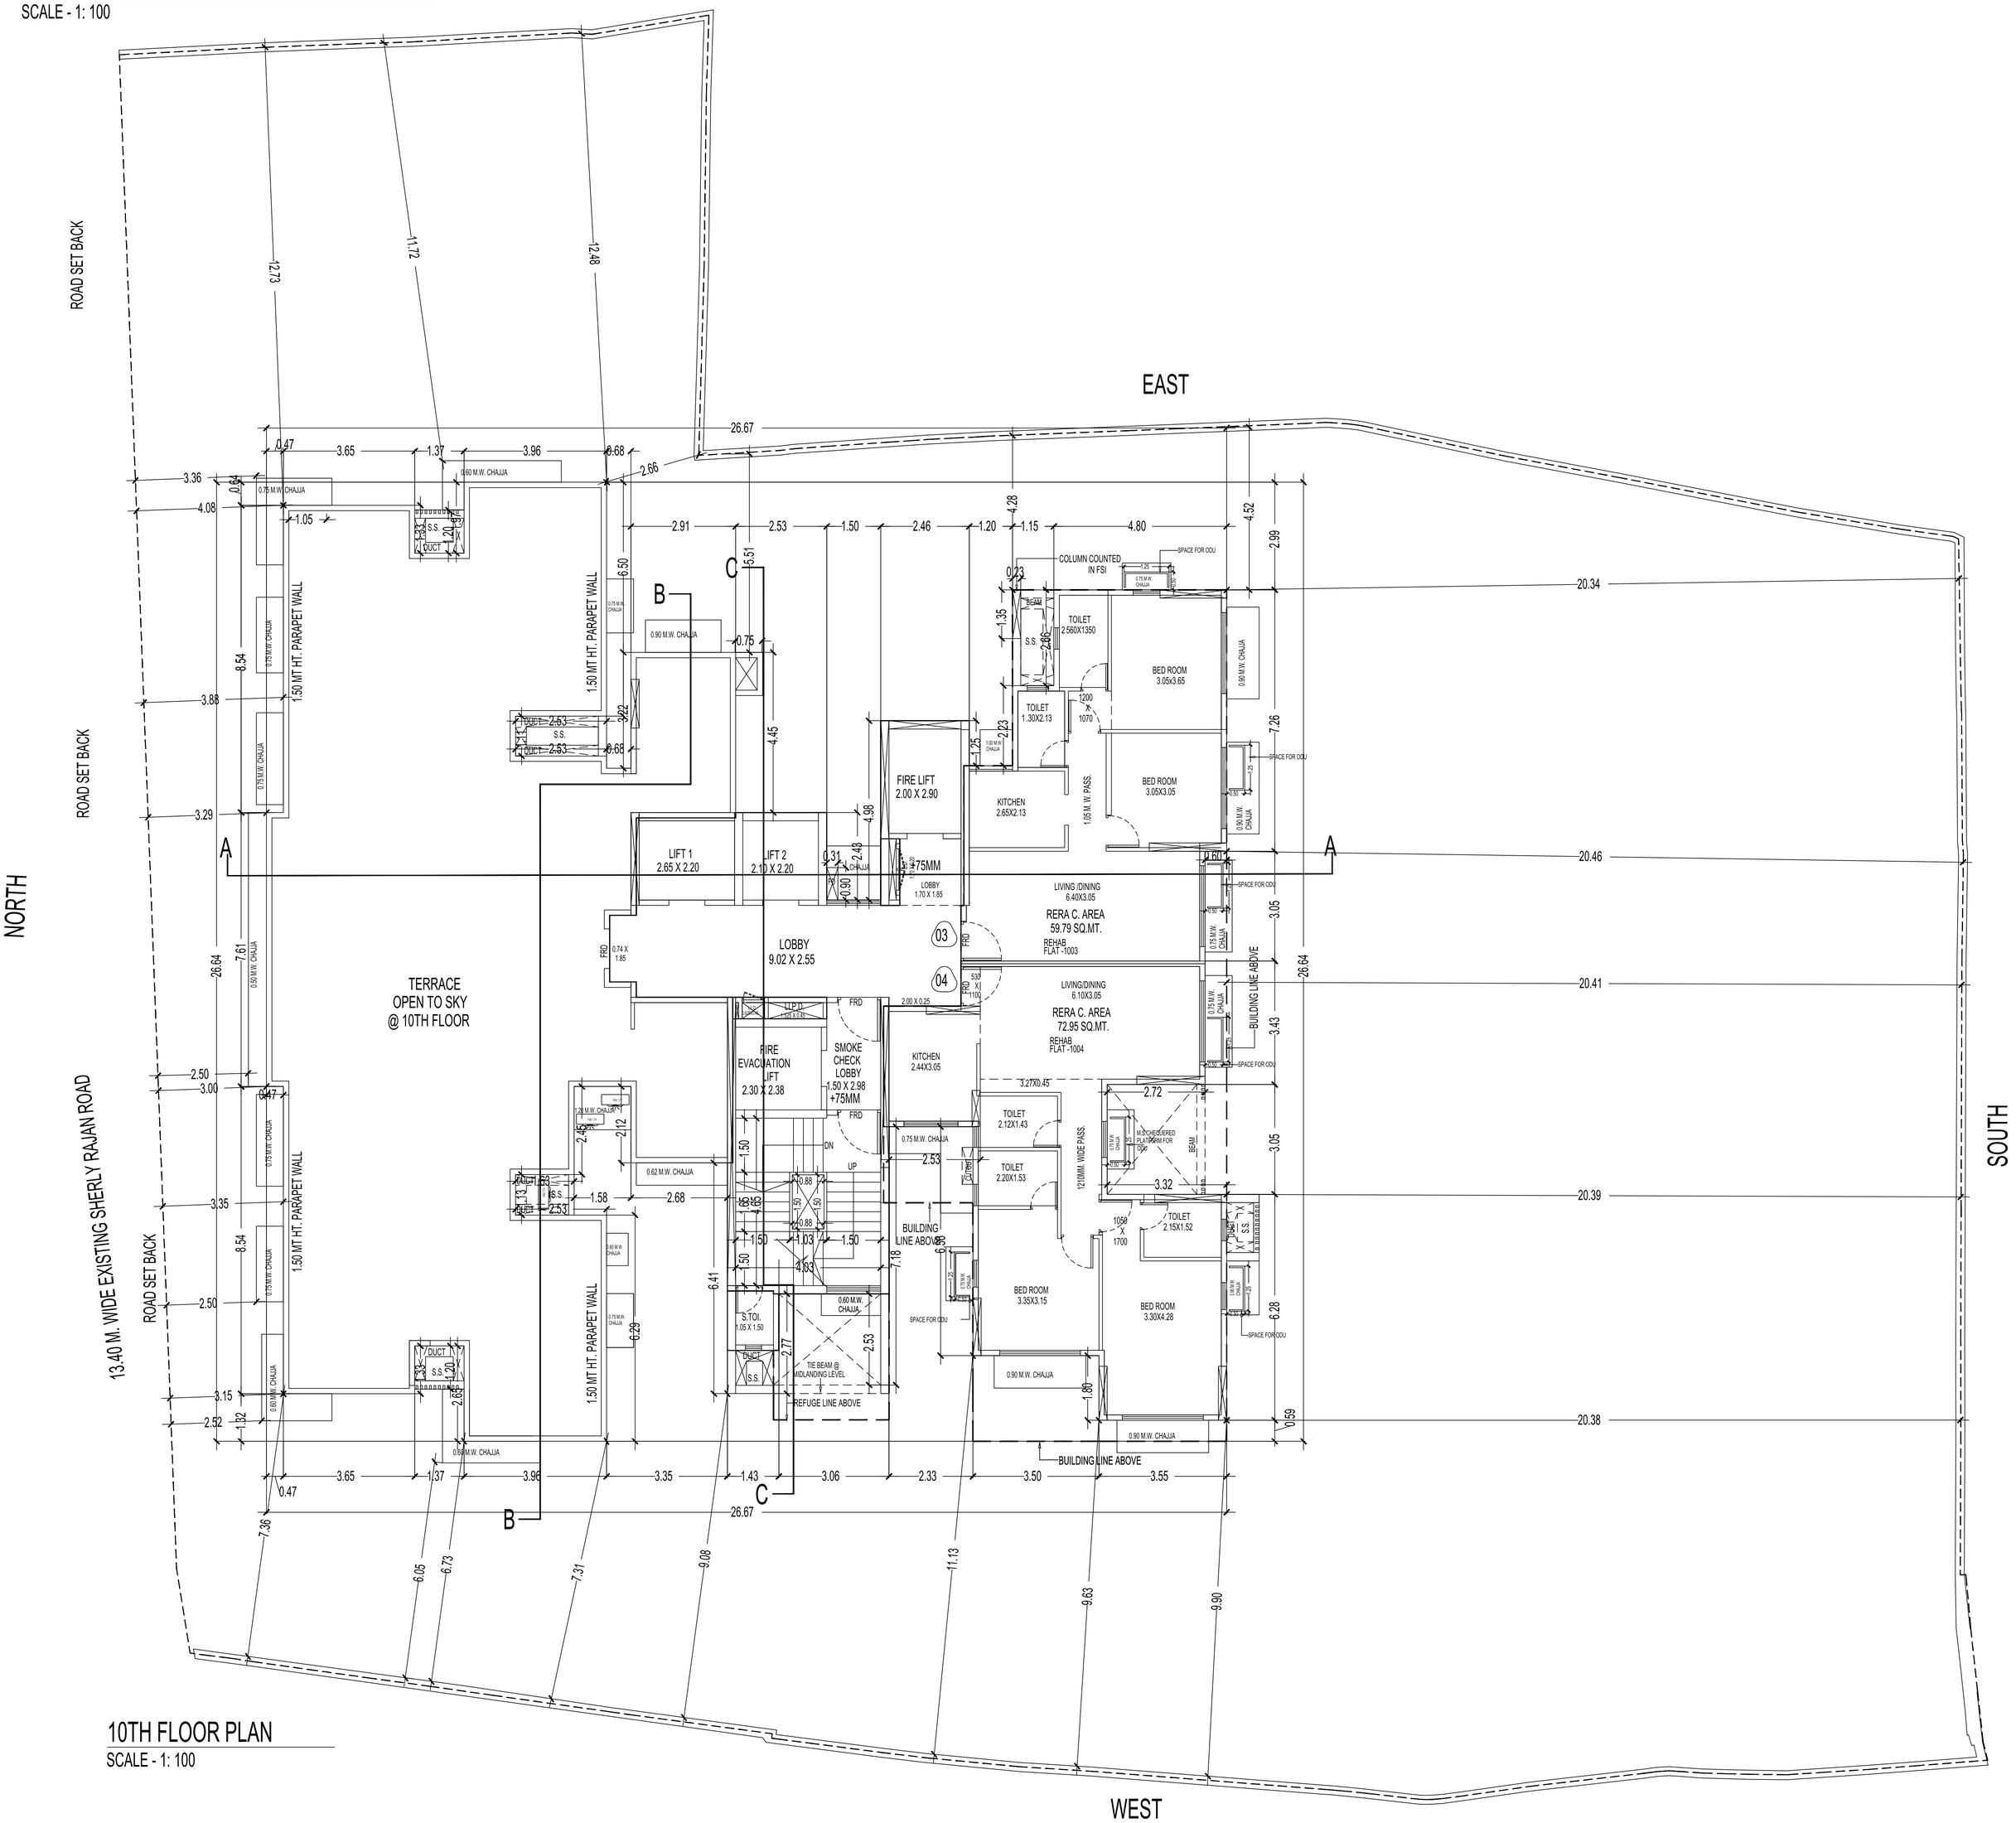
EAST
WEST
NORTH
SOUTH
ROAD SET BACK
ROAD SET BACK
ROAD SET BACK
13.40 M. WIDE EXISTING SHERLY RAJAN ROAD
TERRACE OPEN TO SKY @ 10TH FLOOR
1.50 MT HT. PARAPET WALL
1.50 MT HT. PARAPET WALL
1.50 MT HT. PARAPET WALL
0.75 M.W. CHAJJA
0.60 M.W. CHAJJA
0.90 M.W. CHAJJA
0.50 M.W. CHAJJA
FIRE LIFT 2.00 X 2.90
LIFT 1 2.65 X 2.20
LIFT 2 2.10 X 2.20
LOBBY 1.70 X 1.85
LOBBY 9.02 X 2.55
FIRE EVACUATION LIFT 2.30 X 2.38
SMOKE CHECK LOBBY 1.50 X 2.98 +75MM
LIVING /DINING 6.40X3.05
RERA C. AREA 59.79 SQ.MT.
REHAB FLAT -1003
LIVING/DINING 6.10X3.05
RERA C. AREA 72.95 SQ.MT.
REHAB FLAT -1004
KITCHEN 2.65X2.13
KITCHEN 2.44X3.05
TOILET 2.560X1350
TOILET 1.30X2.13
TOILET 2.12X1.43
TOILET 2.20X1.53
TOILET 2.15X1.52
BED ROOM 3.05x3.65
BED ROOM 3.05X3.05
BED ROOM 3.35X3.15
BED ROOM 3.30X4.28
COLUMN COUNTED IN FSI
SPACE FOR ODU
BEAM
S.S.
DUCT
S.TOI. 1.05 X 1.50
TIE BEAM @ MIDLANDING LEVEL
REFUGE LINE ABOVE
BUILDING LINE ABOVE
1.05 M. W. PASS.
1210MM. WIDE PASS.
M.S.CHEQUERED PLATE/GRM FOR ODU
26.67
20.34
20.46
20.41
20.39
20.38
26.64
10TH FLOOR PLAN
SCALE - 1: 100

11TH FLOOR PLAN

SCALE - 1: 100

SCALE - 1: 100

NORTH

NORTH

13.40 M. WIDE EXISTING SHERLY RAJAN ROAD

ROAD SET BACK

ROAD SET BACK

ROAD SET BACK

TERRACE BELOW

REFUGE AREA 2.83 X 3.35 11TH & 12TH FLR. MIN. LANDING LVL AREA - 11.00 SQ.MT. 1.20M HT. PARAPET WALL

FIRE EVACUATION LIFT 2.30 X 2.38

LIFT 1 2.65 X 2.20

LIFT 2 2.10 X 2.20

LOBBY 9.02 X 2.55

SMOKE CHECK LOBBY 1.50 X 2.38 +150MM

FIRE LIFT 2.00 X 2.90

LOBBY 1.70 X 1.65

KITCHEN 2.40X3.05

KITCHEN 2.65X2.13

BED ROOM 3.50X4.08

BED ROOM 3.30X4.28

BED ROOM 3.25X3.05

BED ROOM 3.65X3.05

BED ROOM 3.05X0.65

TOILET 2.20X1.53

TOILET 2.12X1.38

TOILET 2.18X1.52

TOILET 1.30X2.13

TOILET 2.66X1.35Ø

LIVING/DINING 6.10X3.05

LIVING DINING 6.40X3.05

RERA C. AREA 87.49 SQ.MT.

RERA C. AREA 59.79 SQ.MT.

1.05 M. W. PASS.

1.05 M. W. PASS.

BUILDING LINE ABOVE

BUILDING LINE ABOVE

0.90 M.W. CHAJJA

0.75 M.W. CHAJJA

0.60 M.W. CHAJJA

SPACE FOR ODU

WEST

EAST

SOUTH

A

B

C

20.38

20.39

20.41


20.46

20.34

26.64


12TH TO 15TH FLOOR LINE AREA DIAGRAM

SCALE - 1: 100

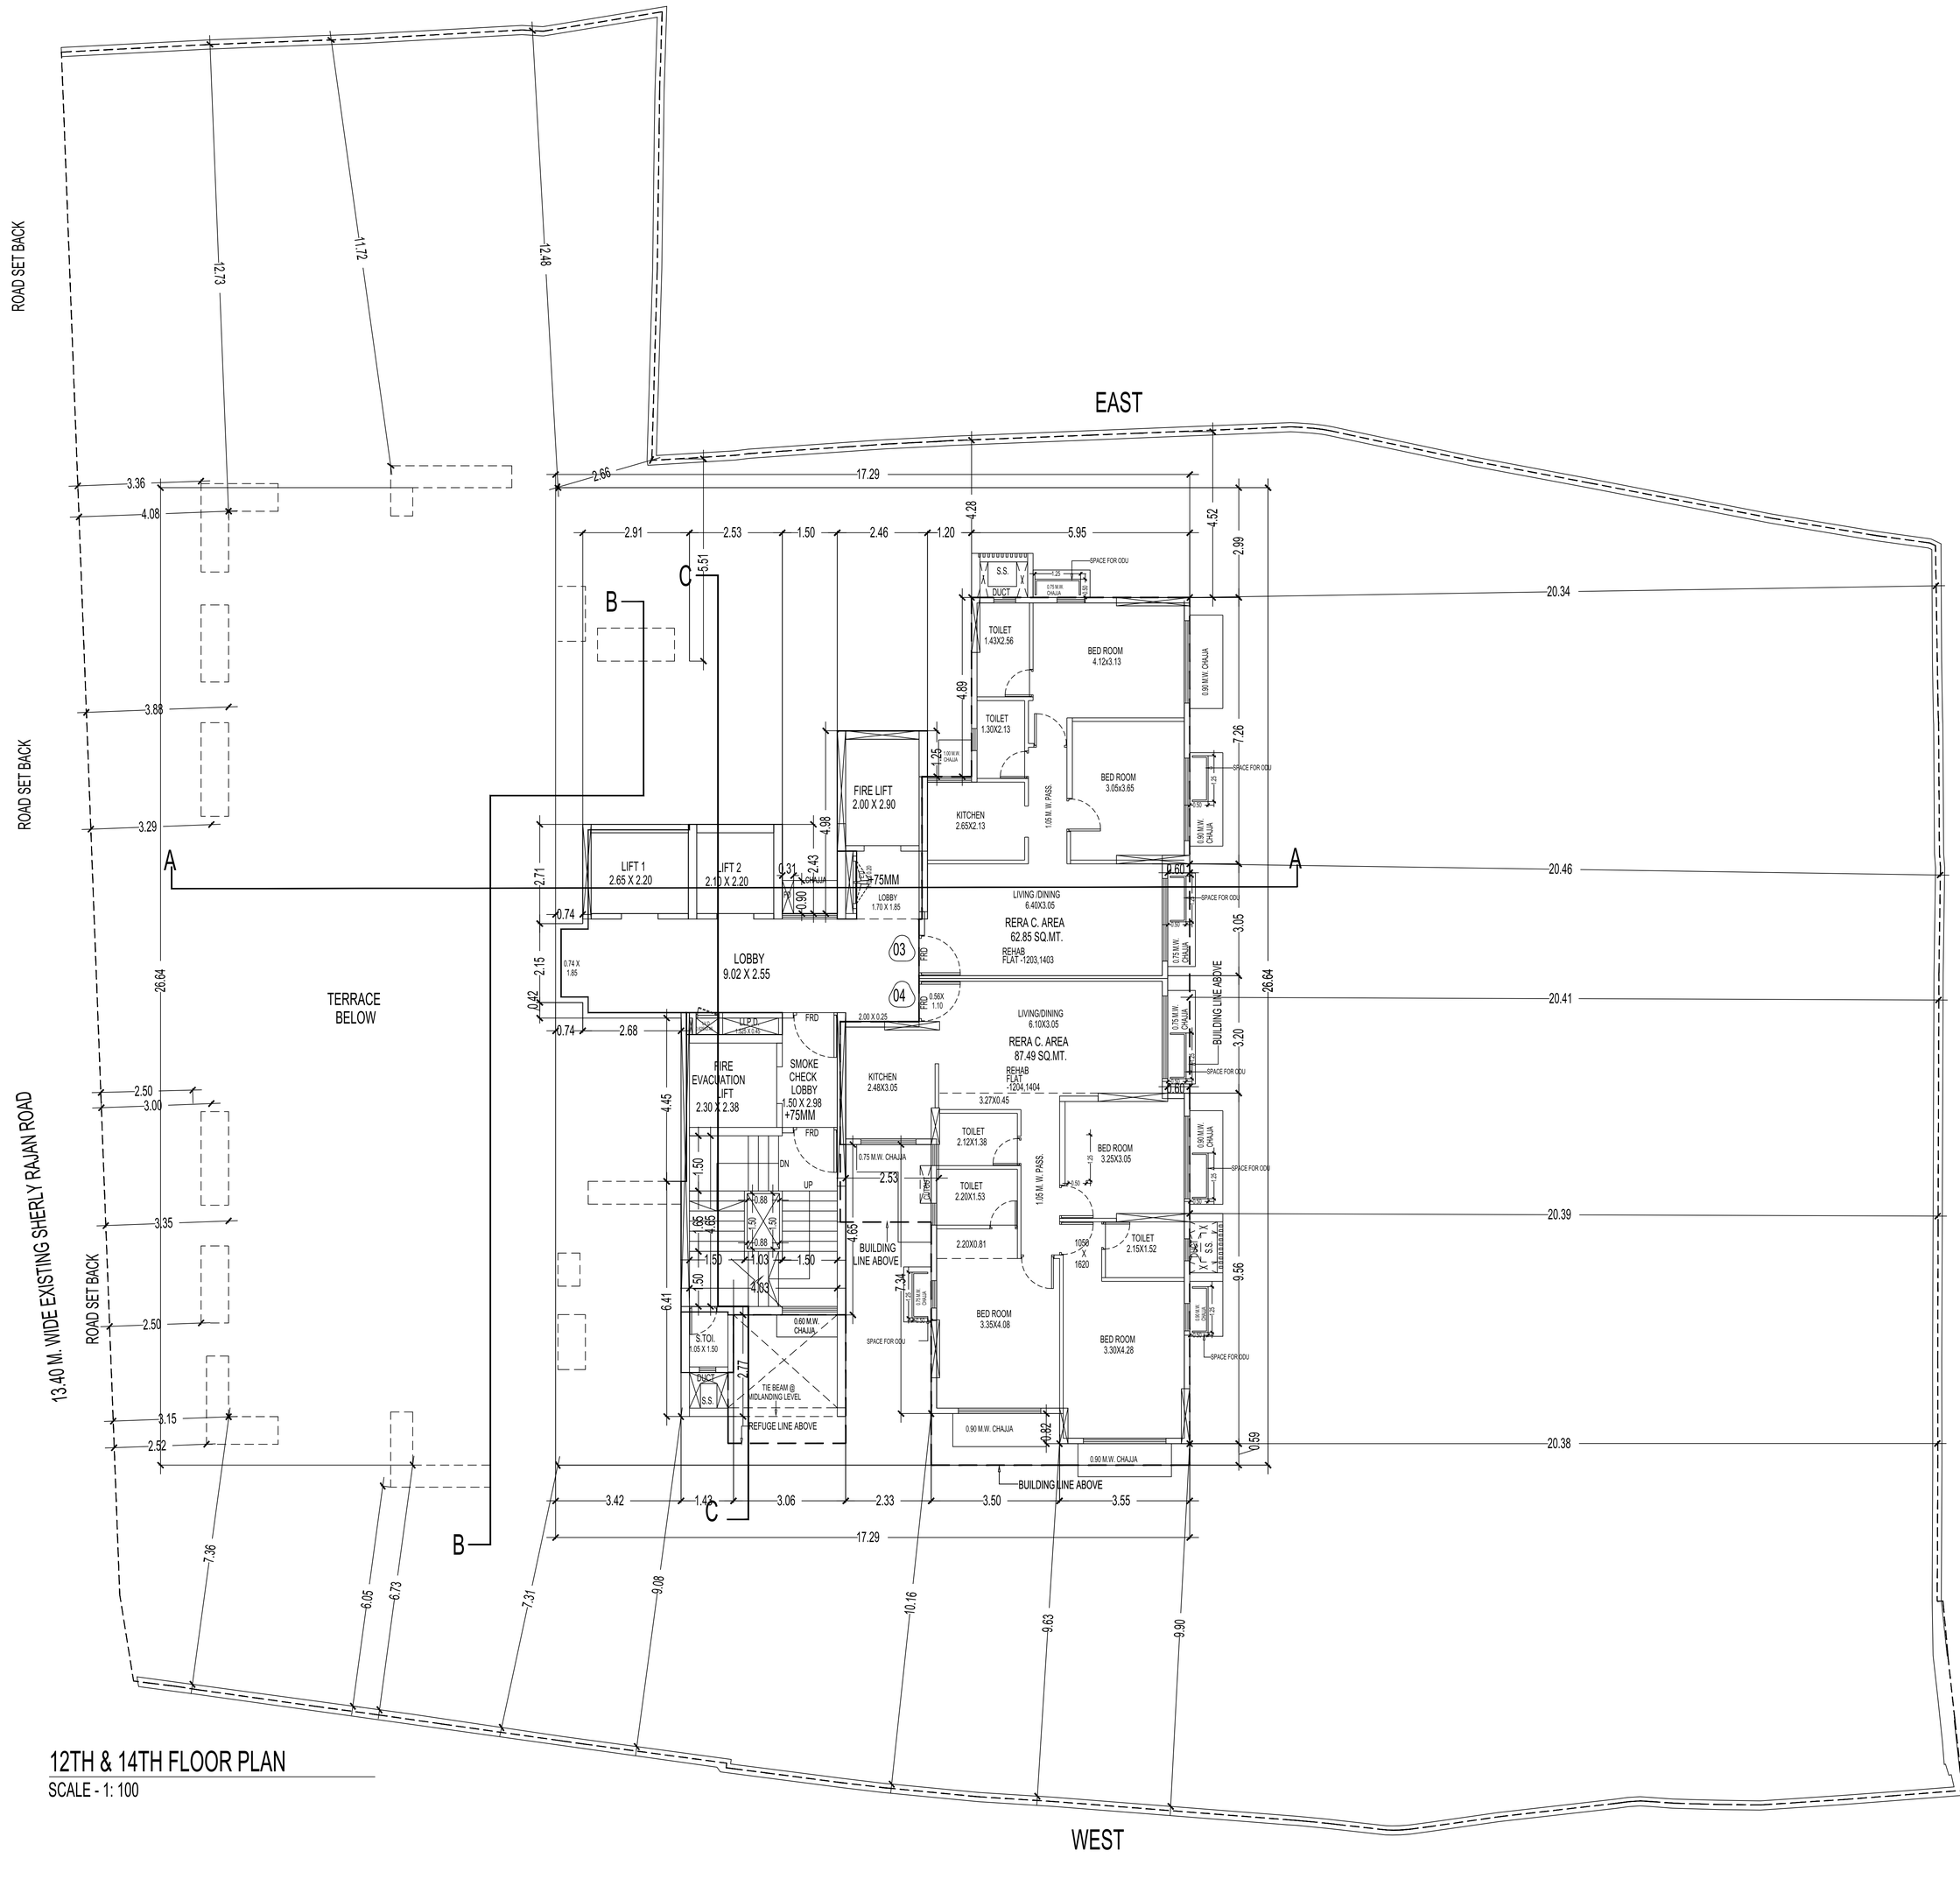

12TH & 14TH FLOOR PLAN

SCALE - 1: 100

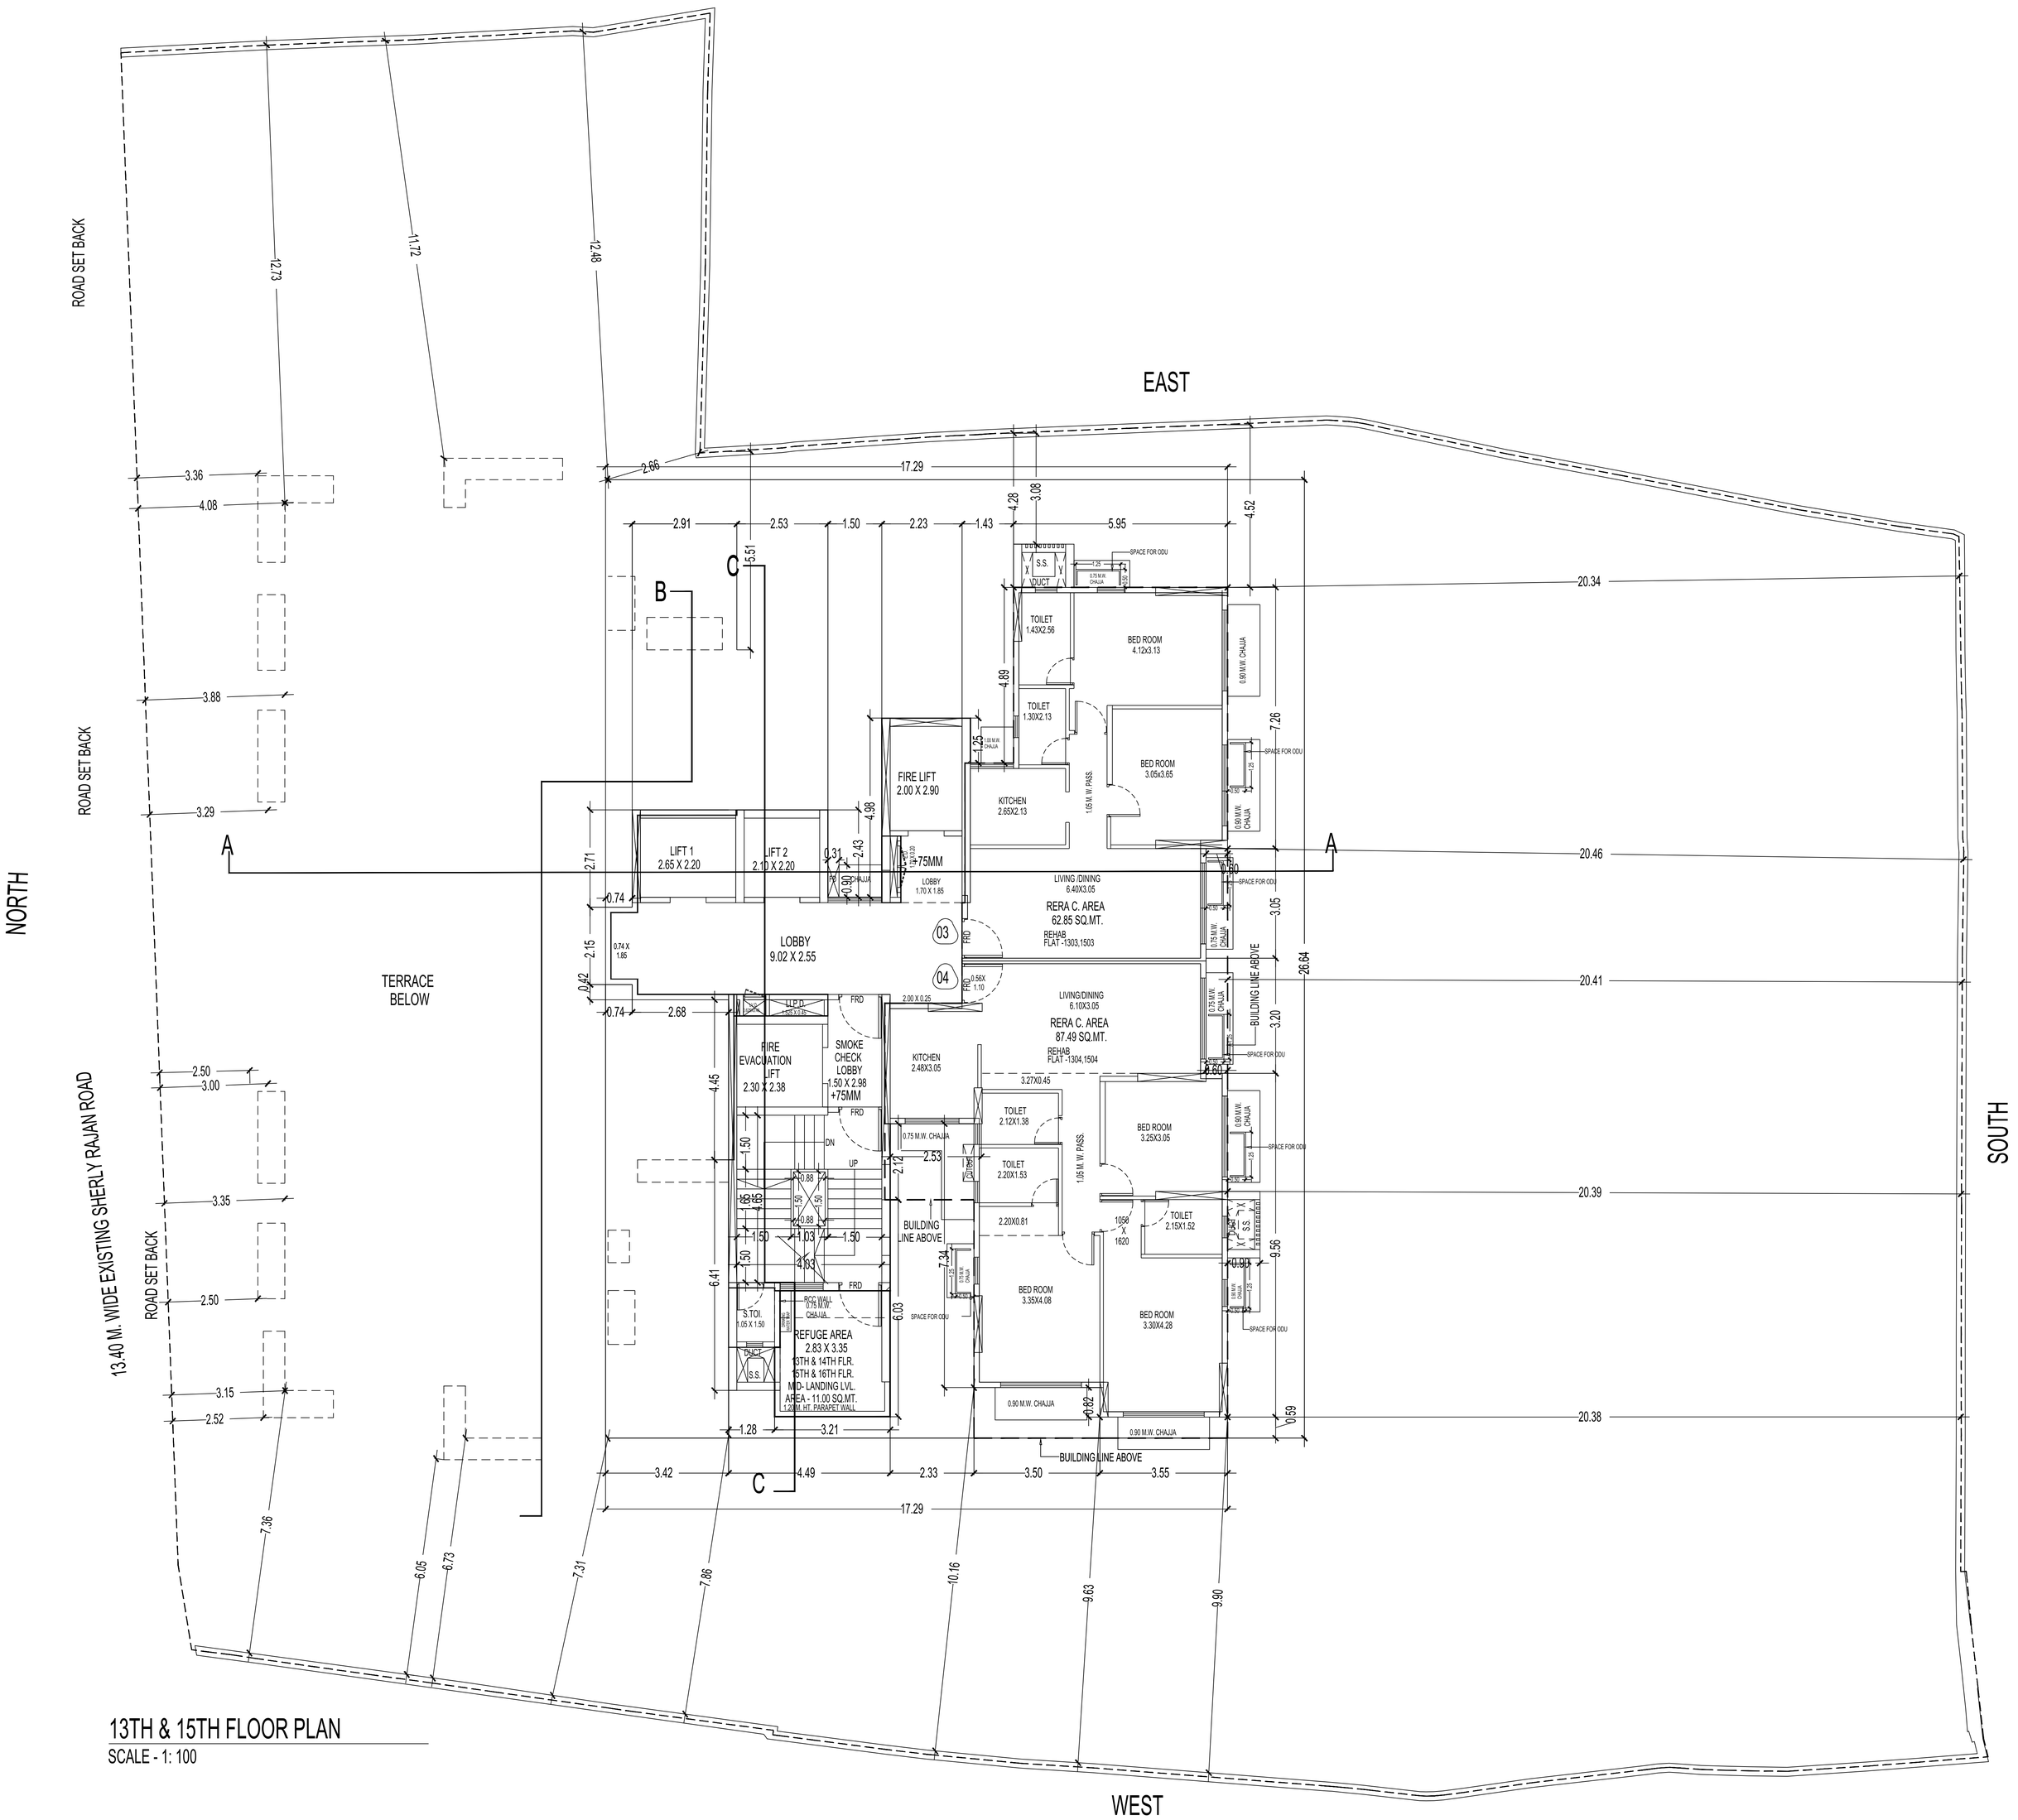


13TH & 15TH FLOOR PLAN

SCALE - 1: 100


16TH FLOOR LINE AREA DIAGRAM

SCALE - 1: 100

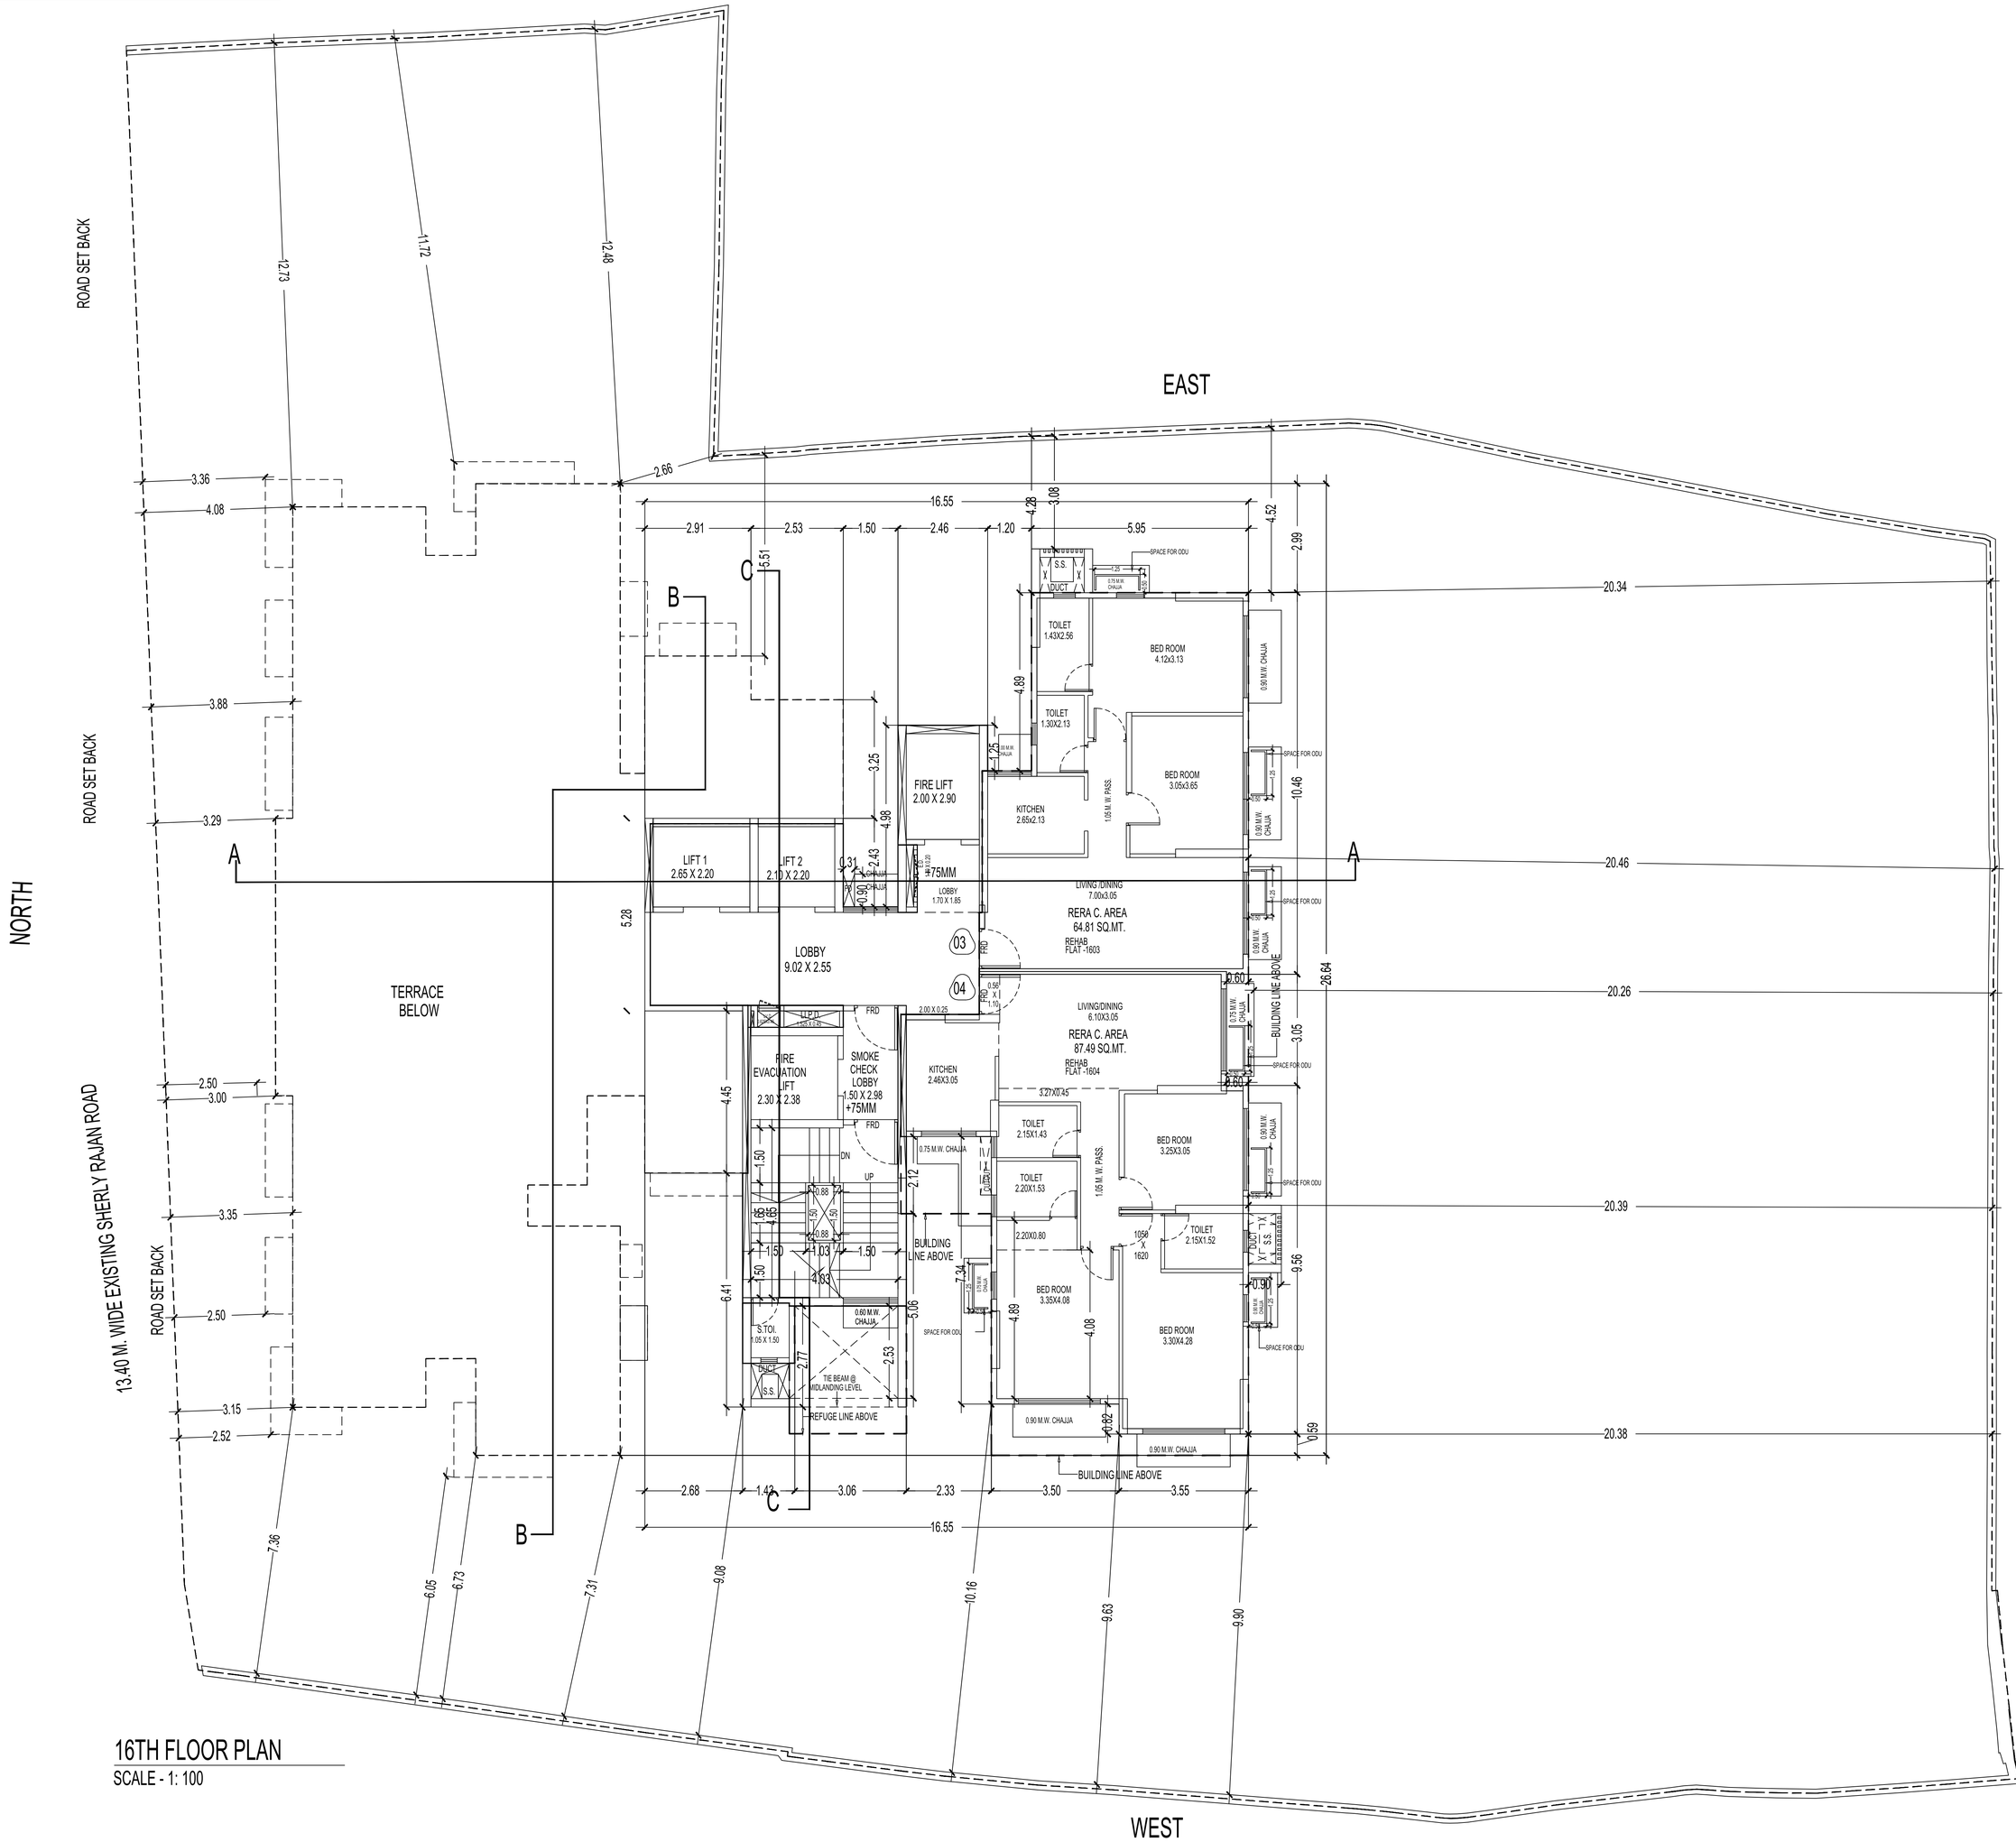

16TH FLOOR PLAN

SCALE - 1: 100

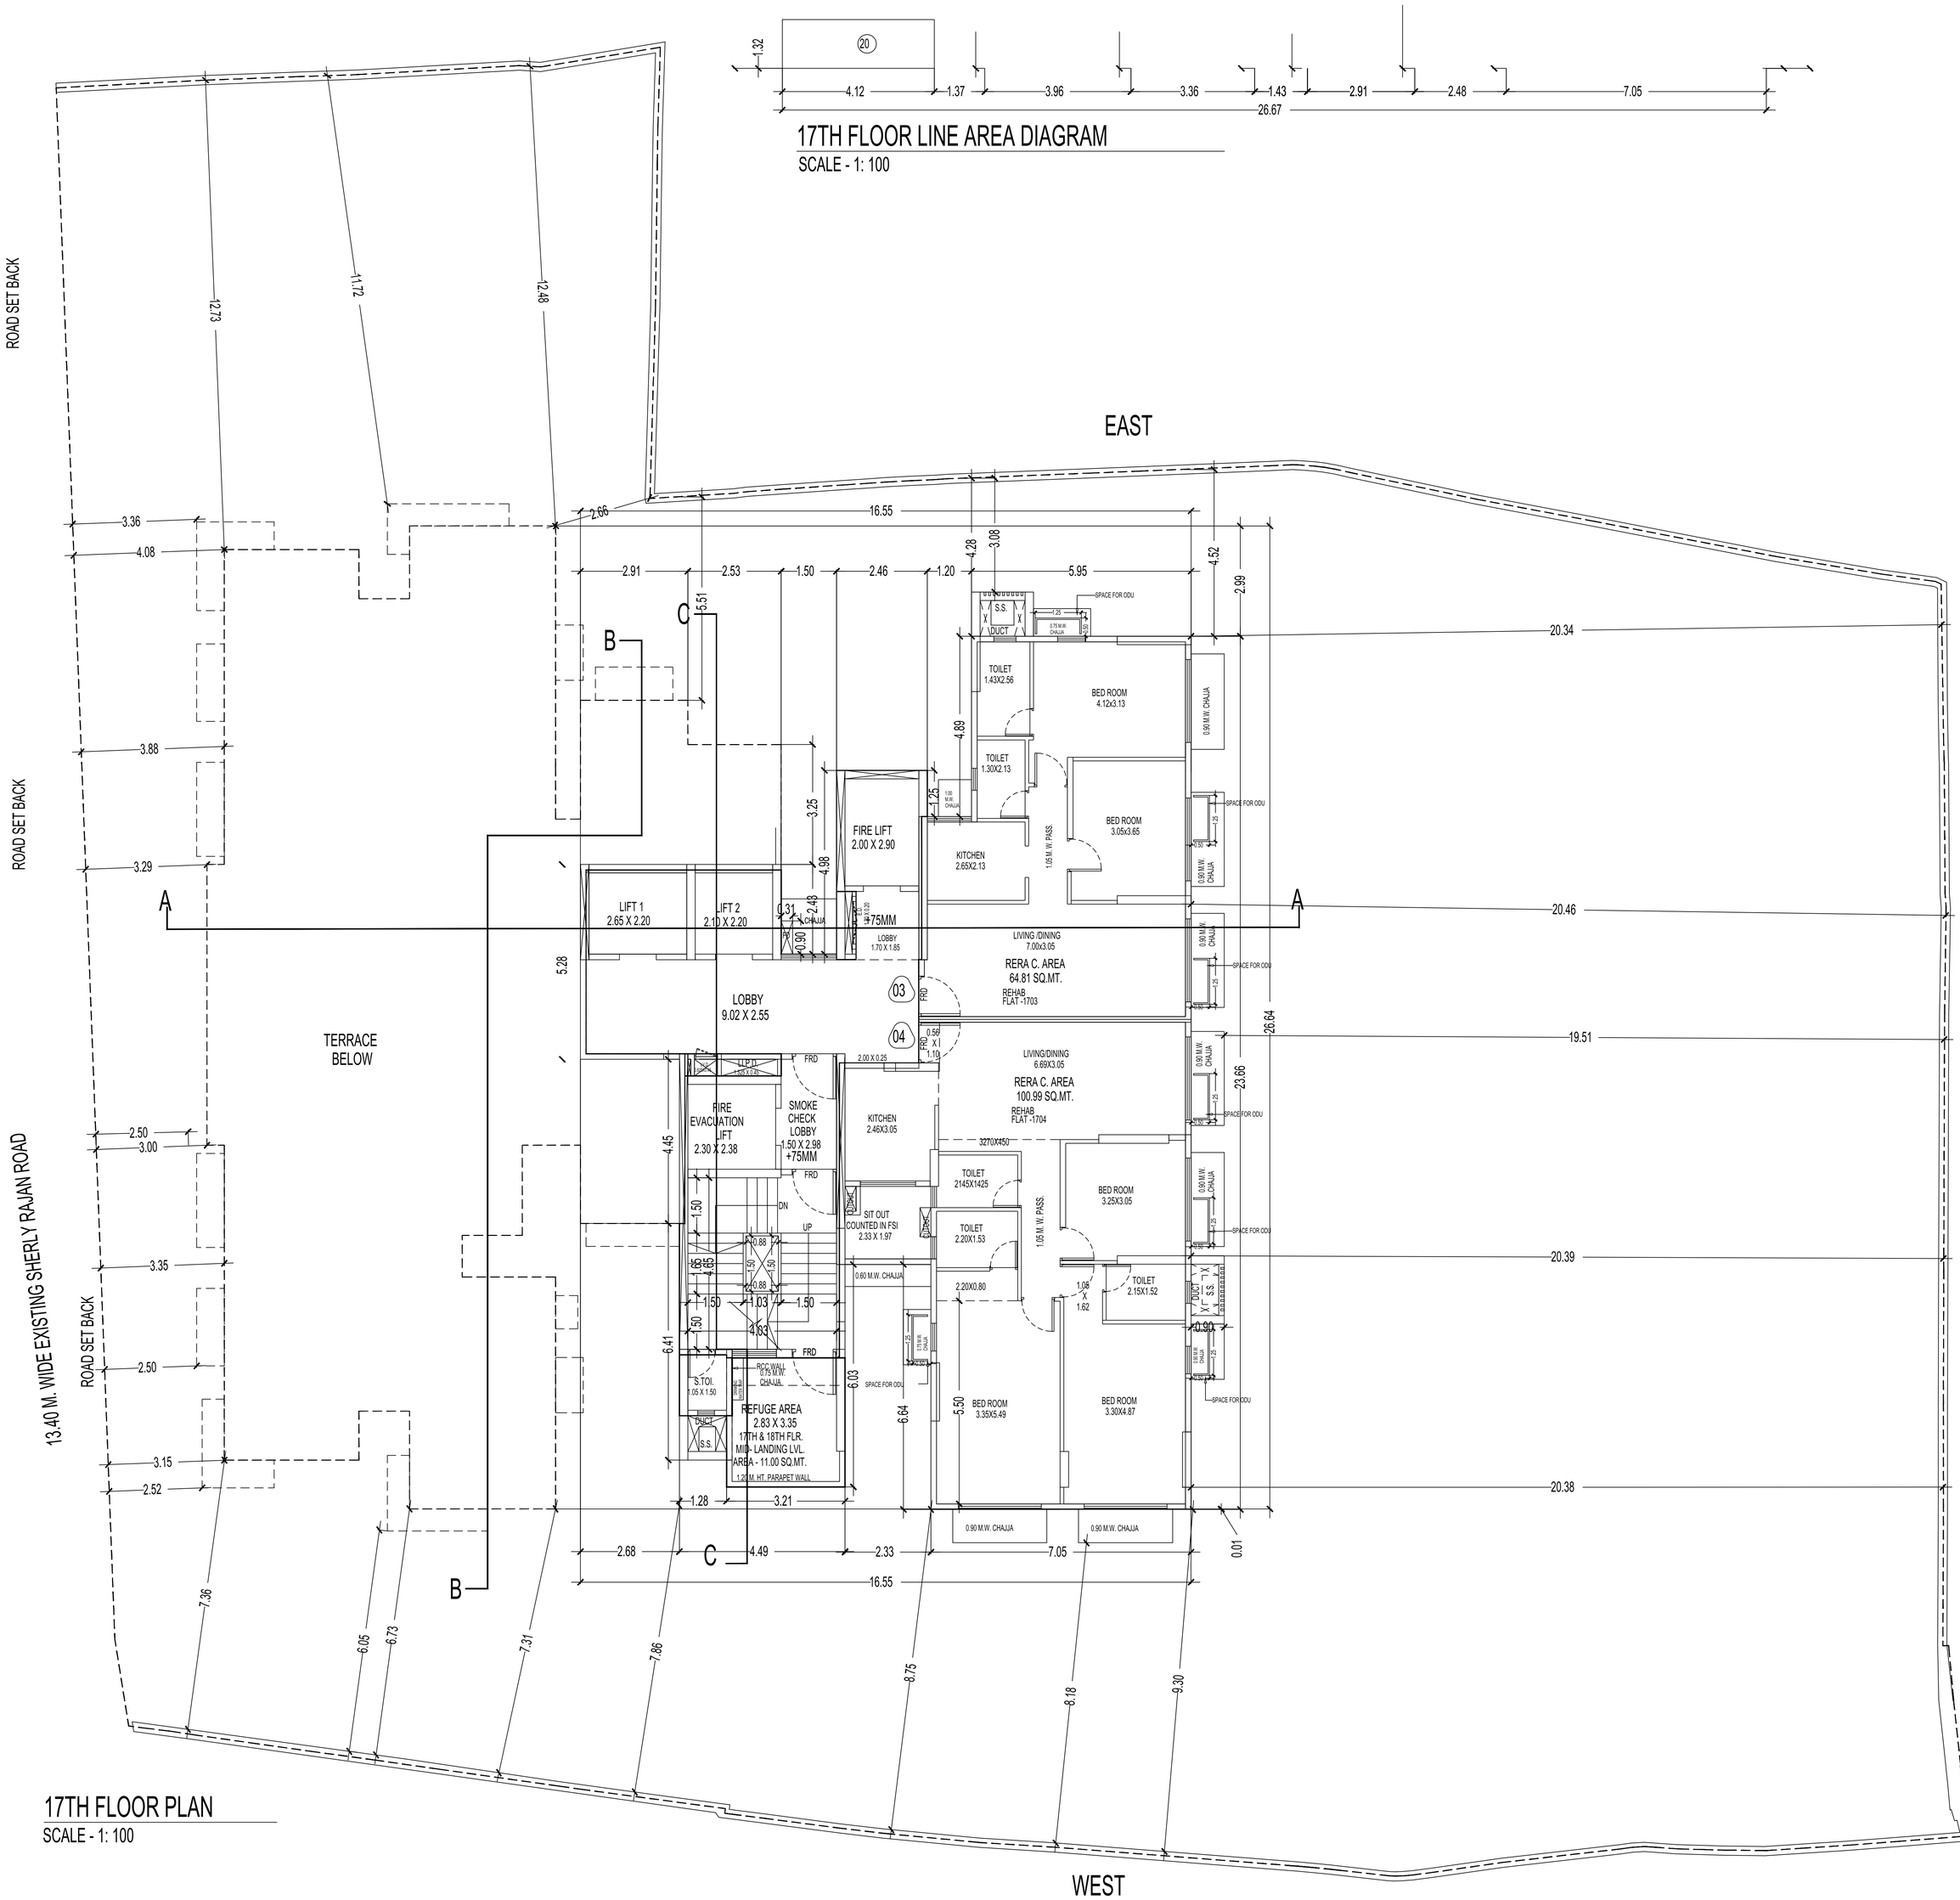
EAST
WEST
NORTH
SOUTH
ROAD SET BACK
ROAD SET BACK
ROAD SET BACK
13.40 M. WIDE EXISTING SHERLY RAJAN ROAD
TERRACE BELOW
LIFT 1 2.65 X 2.20
LIFT 2 2.10 X 2.20
FIRE LIFT 2.00 X 2.90
LOBBY 1.70 X 1.85
LOBBY 9.02 X 2.55
FIRE EVACUATION LIFT 2.30 X 2.38
SMOKE CHECK LOBBY 1.50 X 2.98 +75MM
REFUGE AREA 2.83 X 3.35 17TH & 18TH FLR. MID- LANDING LVL. AREA - 11.00 SQ.MT.
1.20 M. HT. PARAPET WALL
S.S. DUCT
TOILET 1.43X2.56
BED ROOM 4.12x3.13
TOILET 1.30X2.13
KITCHEN 2.65X2.13
BED ROOM 3.05x3.65
LIVING /DINING 7.00x3.05
RERA C. AREA 64.81 SQ.MT.
REHAB FLAT -1703
LIVING/DINING 6.69X3.05
RERA C. AREA 100.99 SQ.MT.
REHAB FLAT -1704
KITCHEN 2.46X3.05
SIT OUT COUNTED IN FSI 2.33 X 1.97
TOILET 2145X1425
TOILET 2.20X1.53
2.20X0.80
BED ROOM 3.25X3.05
TOILET 2.15X1.52
BED ROOM 3.35X5.49
BED ROOM 3.30X4.87
S.TOI. 1.05 X 1.50
SPACE FOR ODU
0.90 M.W. CHAJJA
0.60 M.W. CHAJJA
1.05 M. W. PASS.
3270X450
3270X450
FRD
UP
DN
S.S. DUCT
RCC WALL 0.75 M.W. CHAJJA
20
1.32
4.12
1.37
3.96
3.36
1.43
2.91
2.48
7.05
26.67
17TH FLOOR LINE AREA DIAGRAM
SCALE - 1: 100
16.55
20.34
20.46
19.51
20.39
20.38
26.64
23.66
6.64
6.03
6.41
4.45
5.28
5.51
4.89
4.98
3.25
2.43
4.52
2.99
4.28
3.08
2.66
3.36
4.08
3.88
3.29
2.50
3.00
3.35
2.50
3.15
2.52
7.36
6.05
6.73
7.31
7.86
8.75
8.18
9.30
17TH FLOOR PLAN
SCALE - 1: 100