
P AREA [X1 - (Y2+Y3)]	=	163.01 SQ.

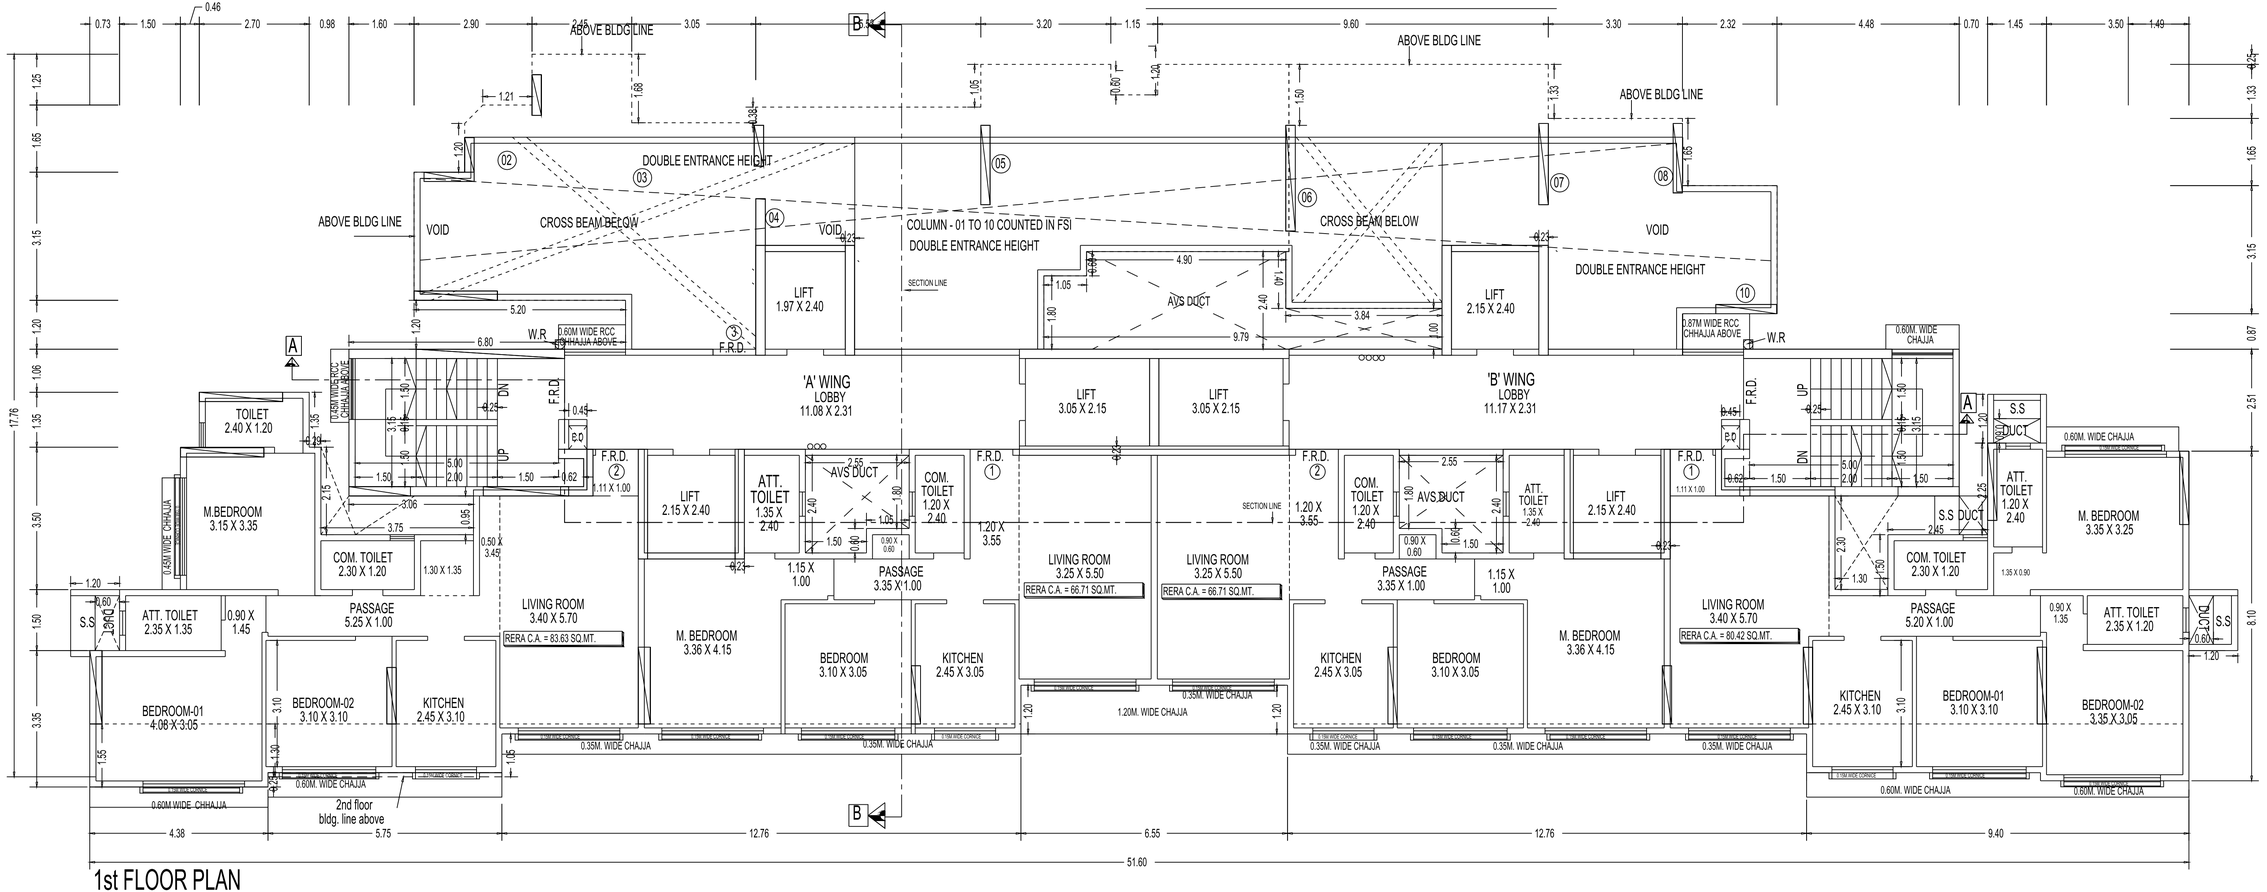


1st FLOOR PLAN

SCALE 1:100

D2


TOTAL DU

NET BUILT UP AREA
[X1 - (Y2+Y3)]

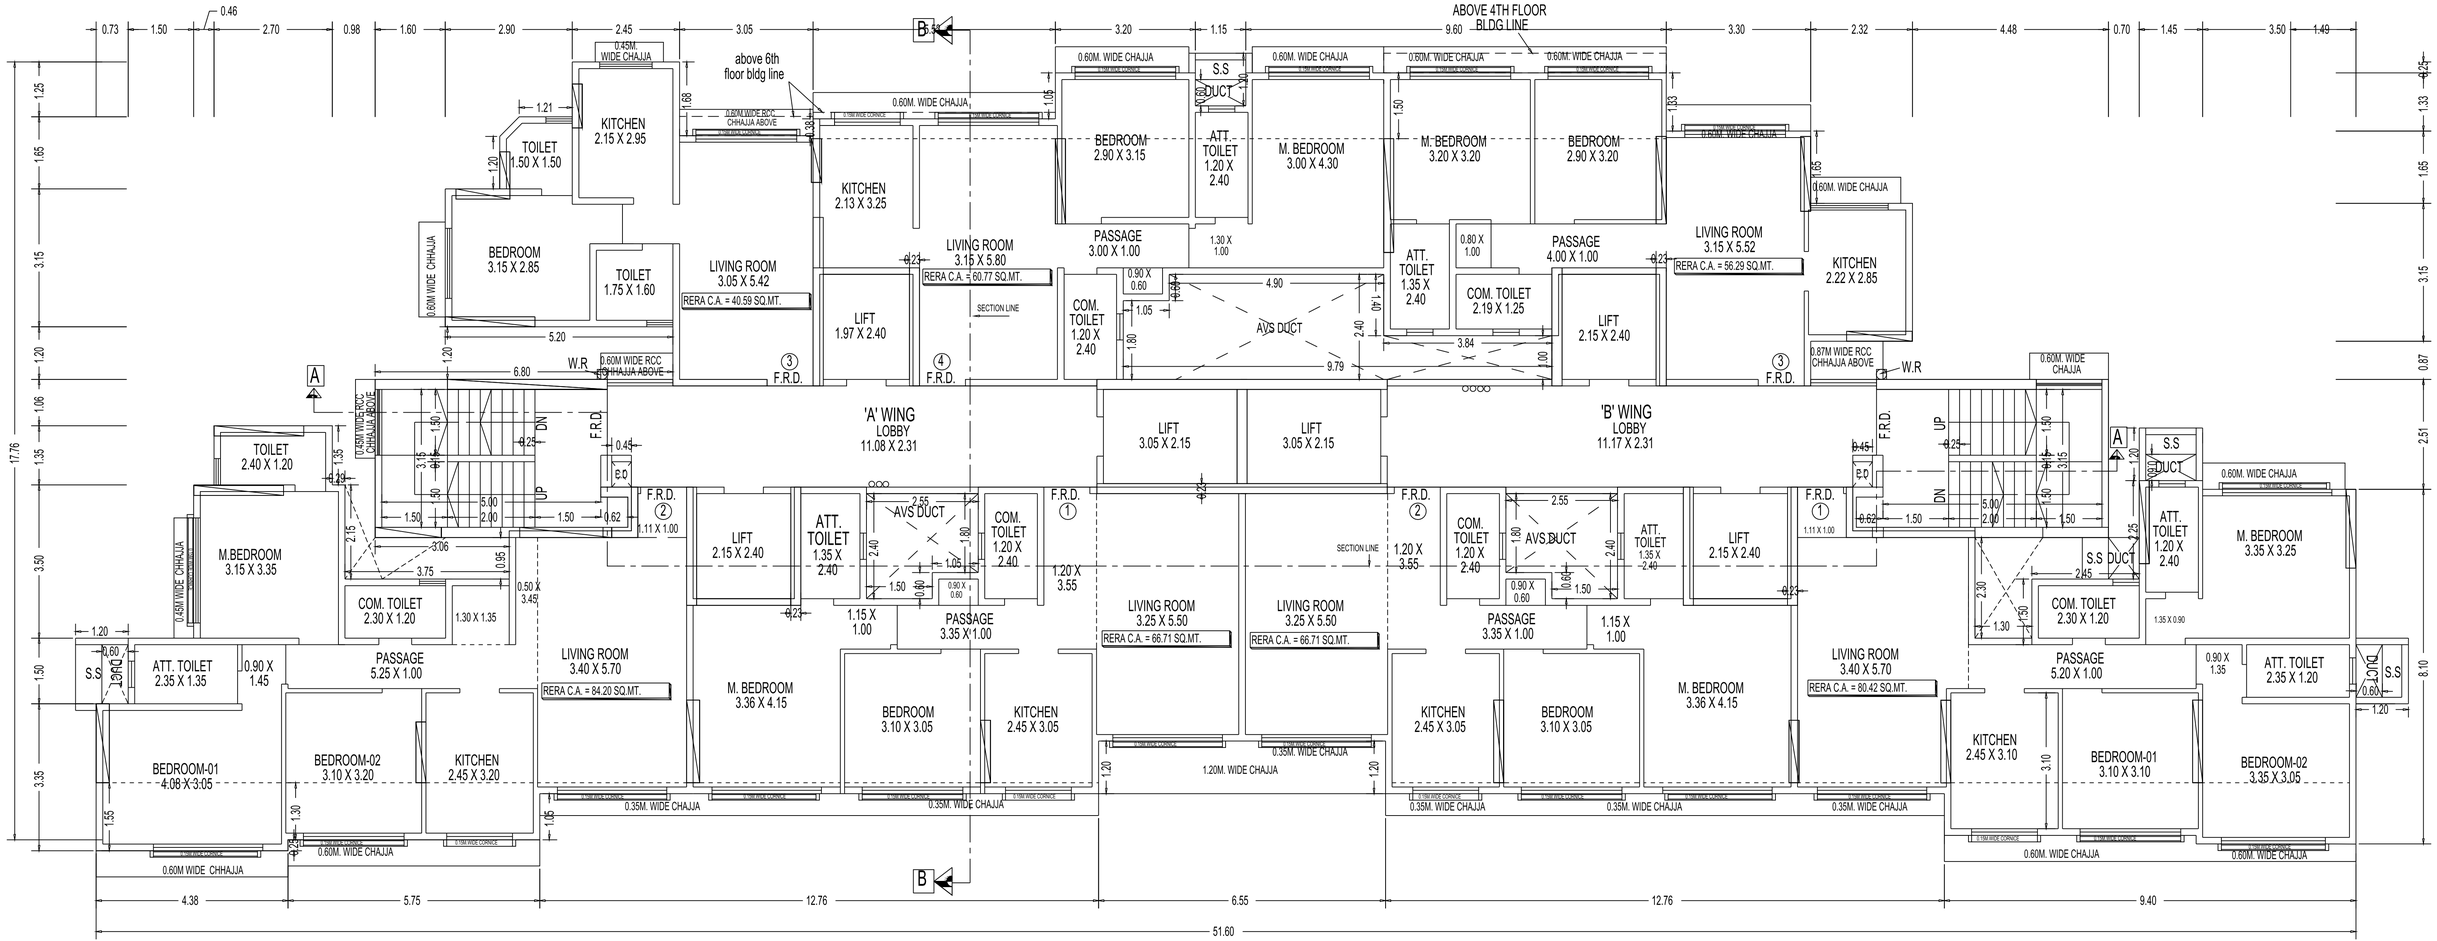


2nd & 3RD FLOOR PLAN

SCALE 1:100

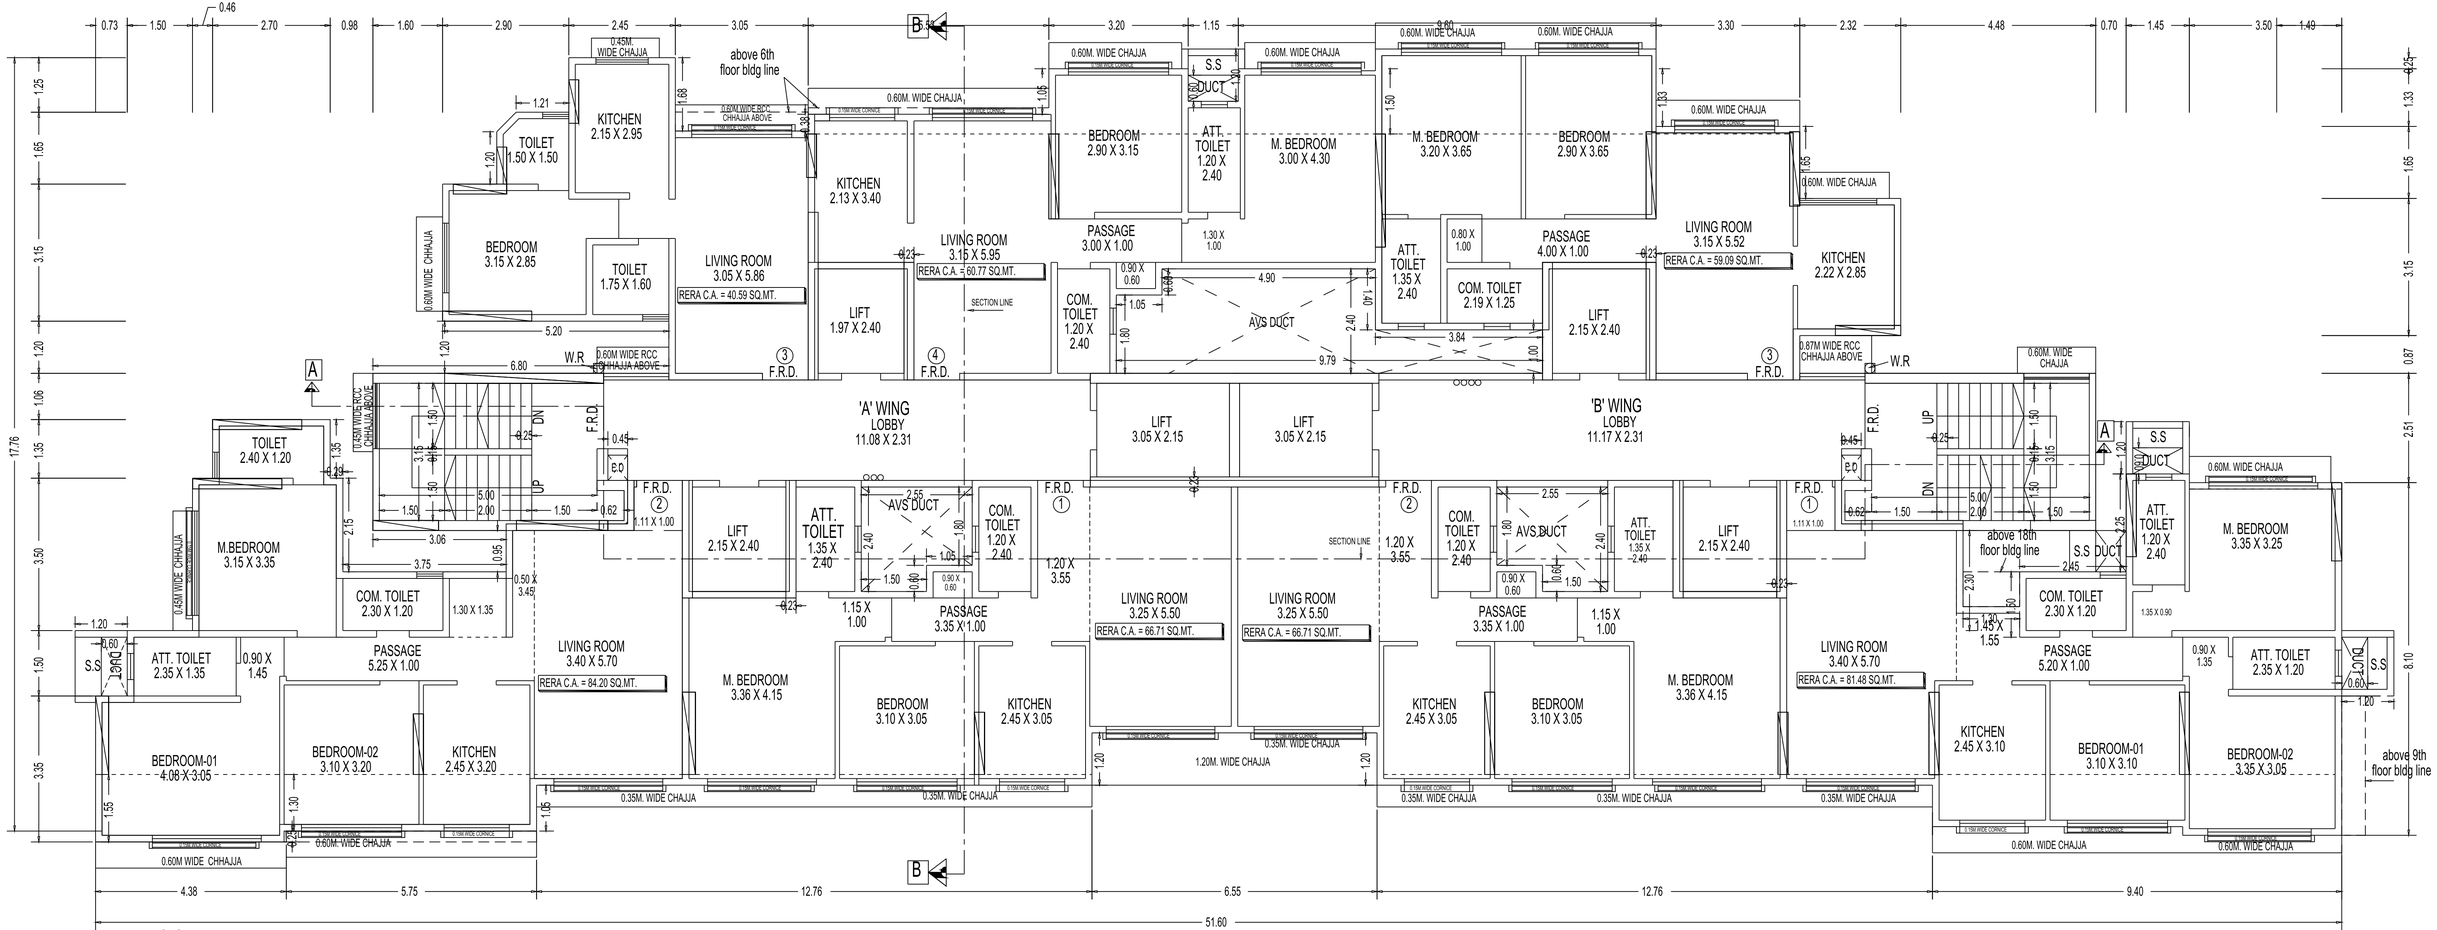

4th FLOOR PLAN


SCALE 1:100

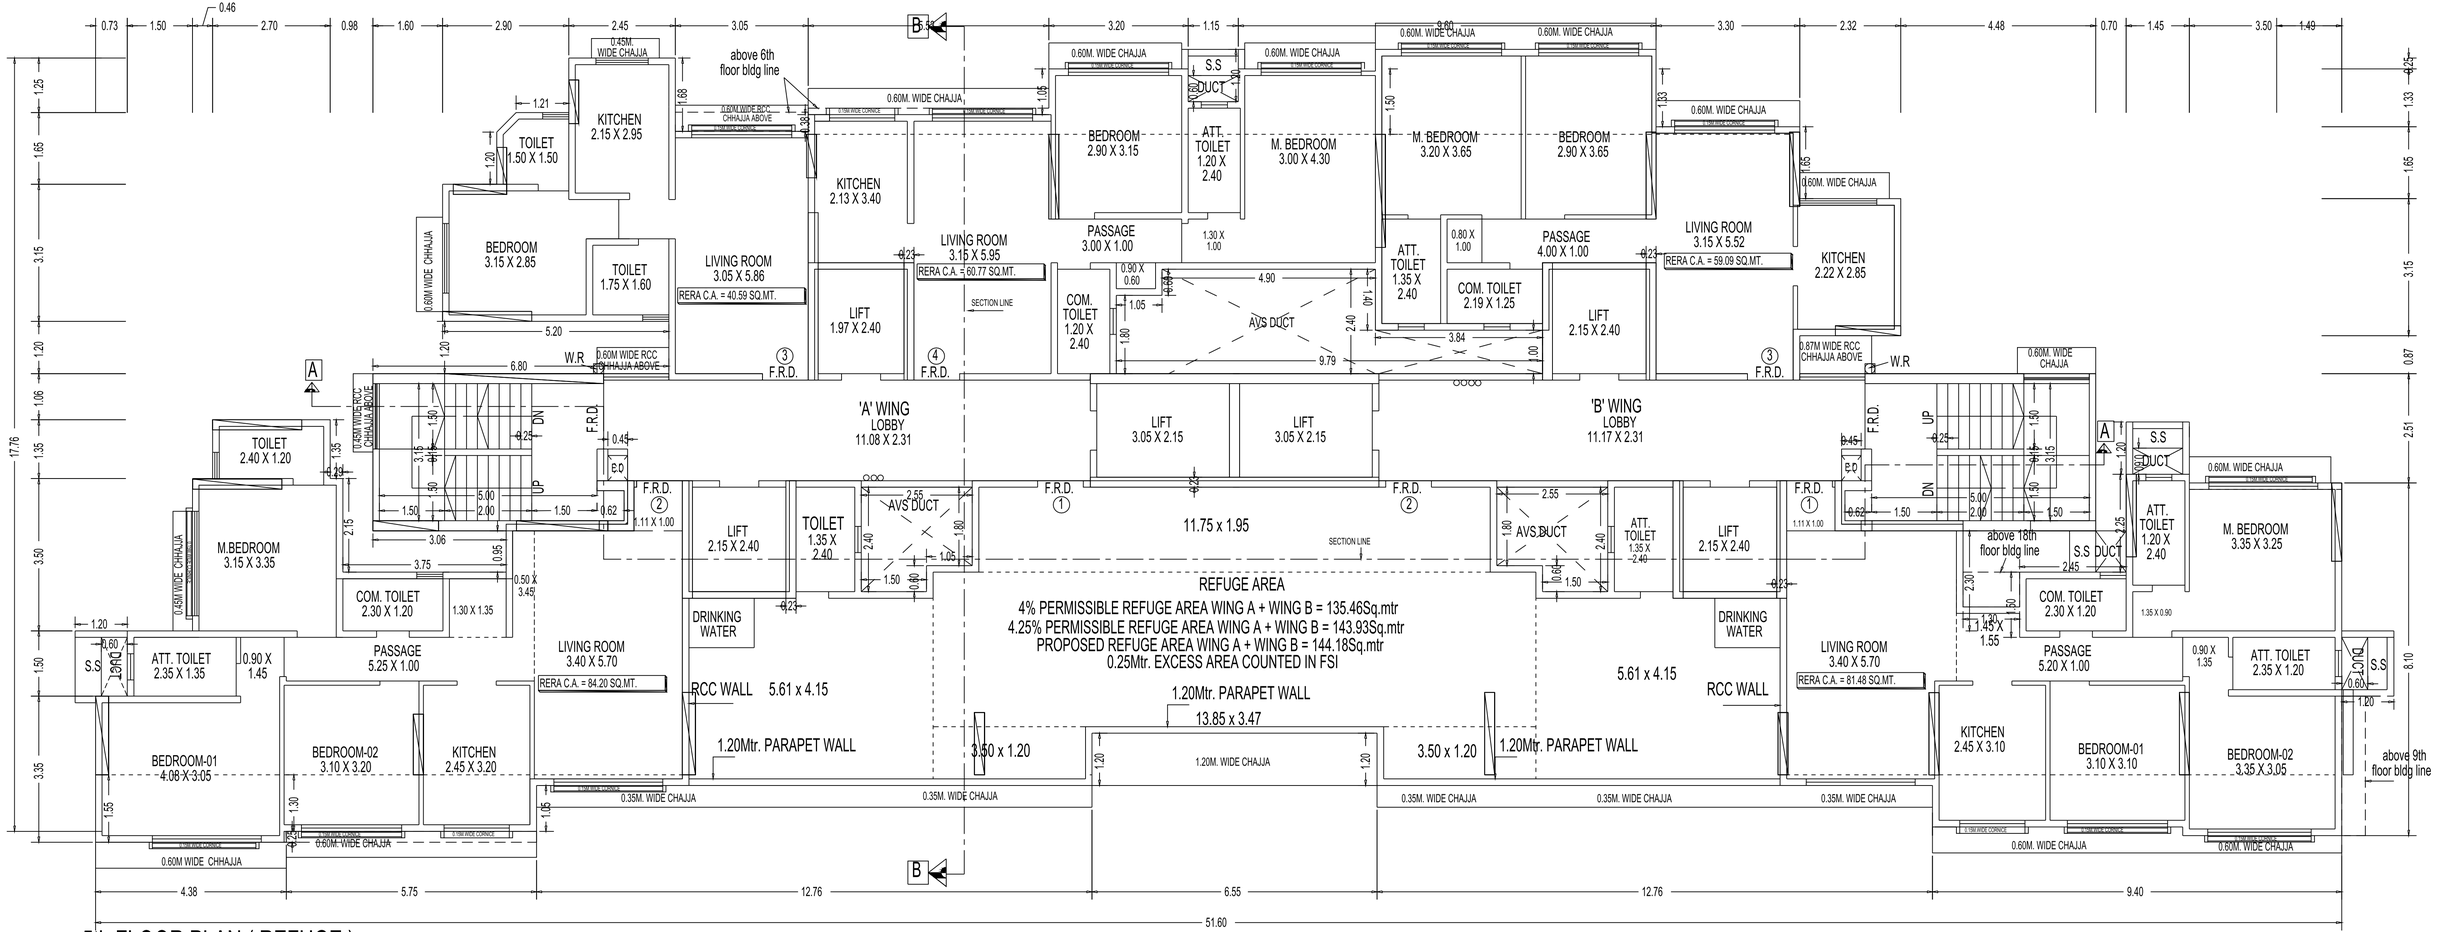

5th FLOOR PLAN (REFUGE)


SCALE 1:100

UP AREA 1 - (Y2+Y3)]	=	225.35 SQ.MT.

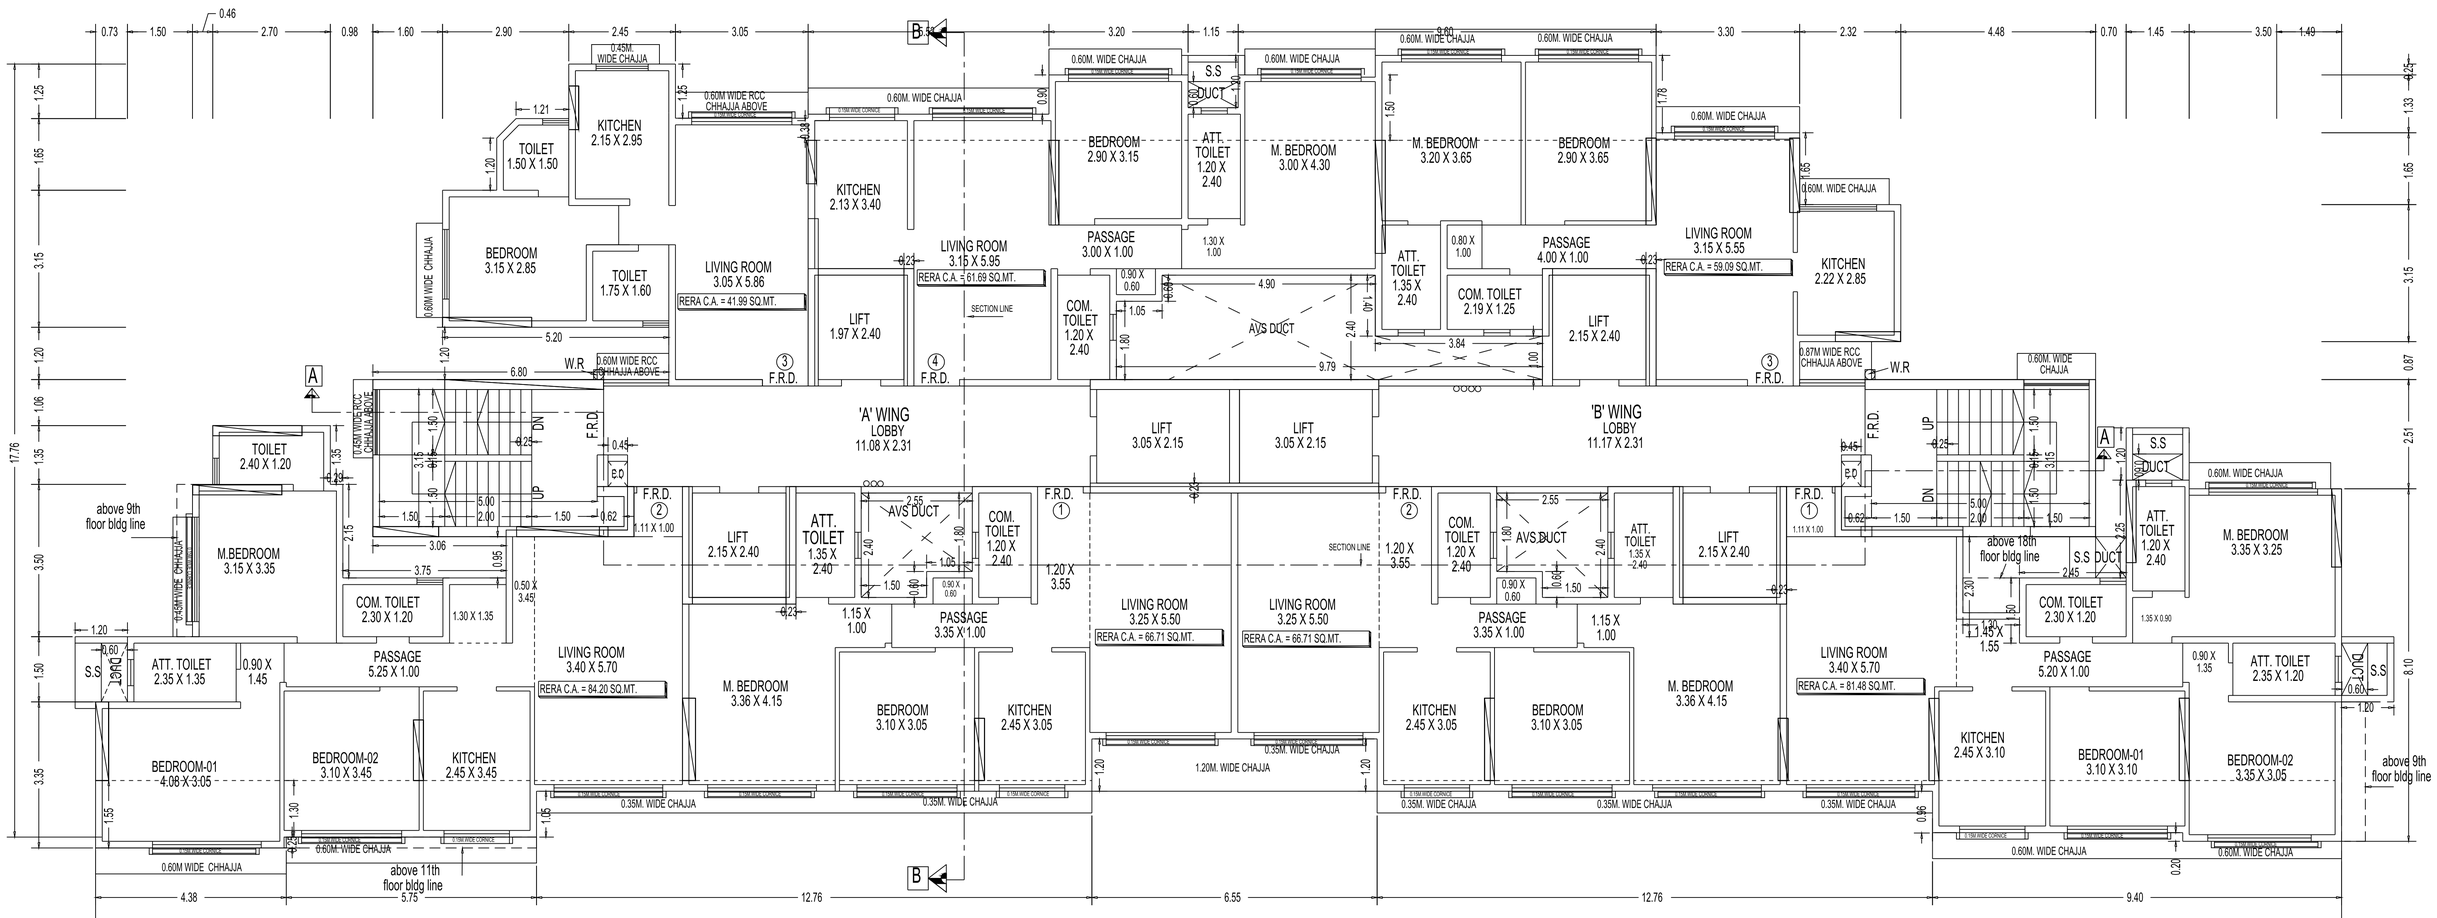


6th,7th & 8th FLOOR PLAN


SCALE 1:100

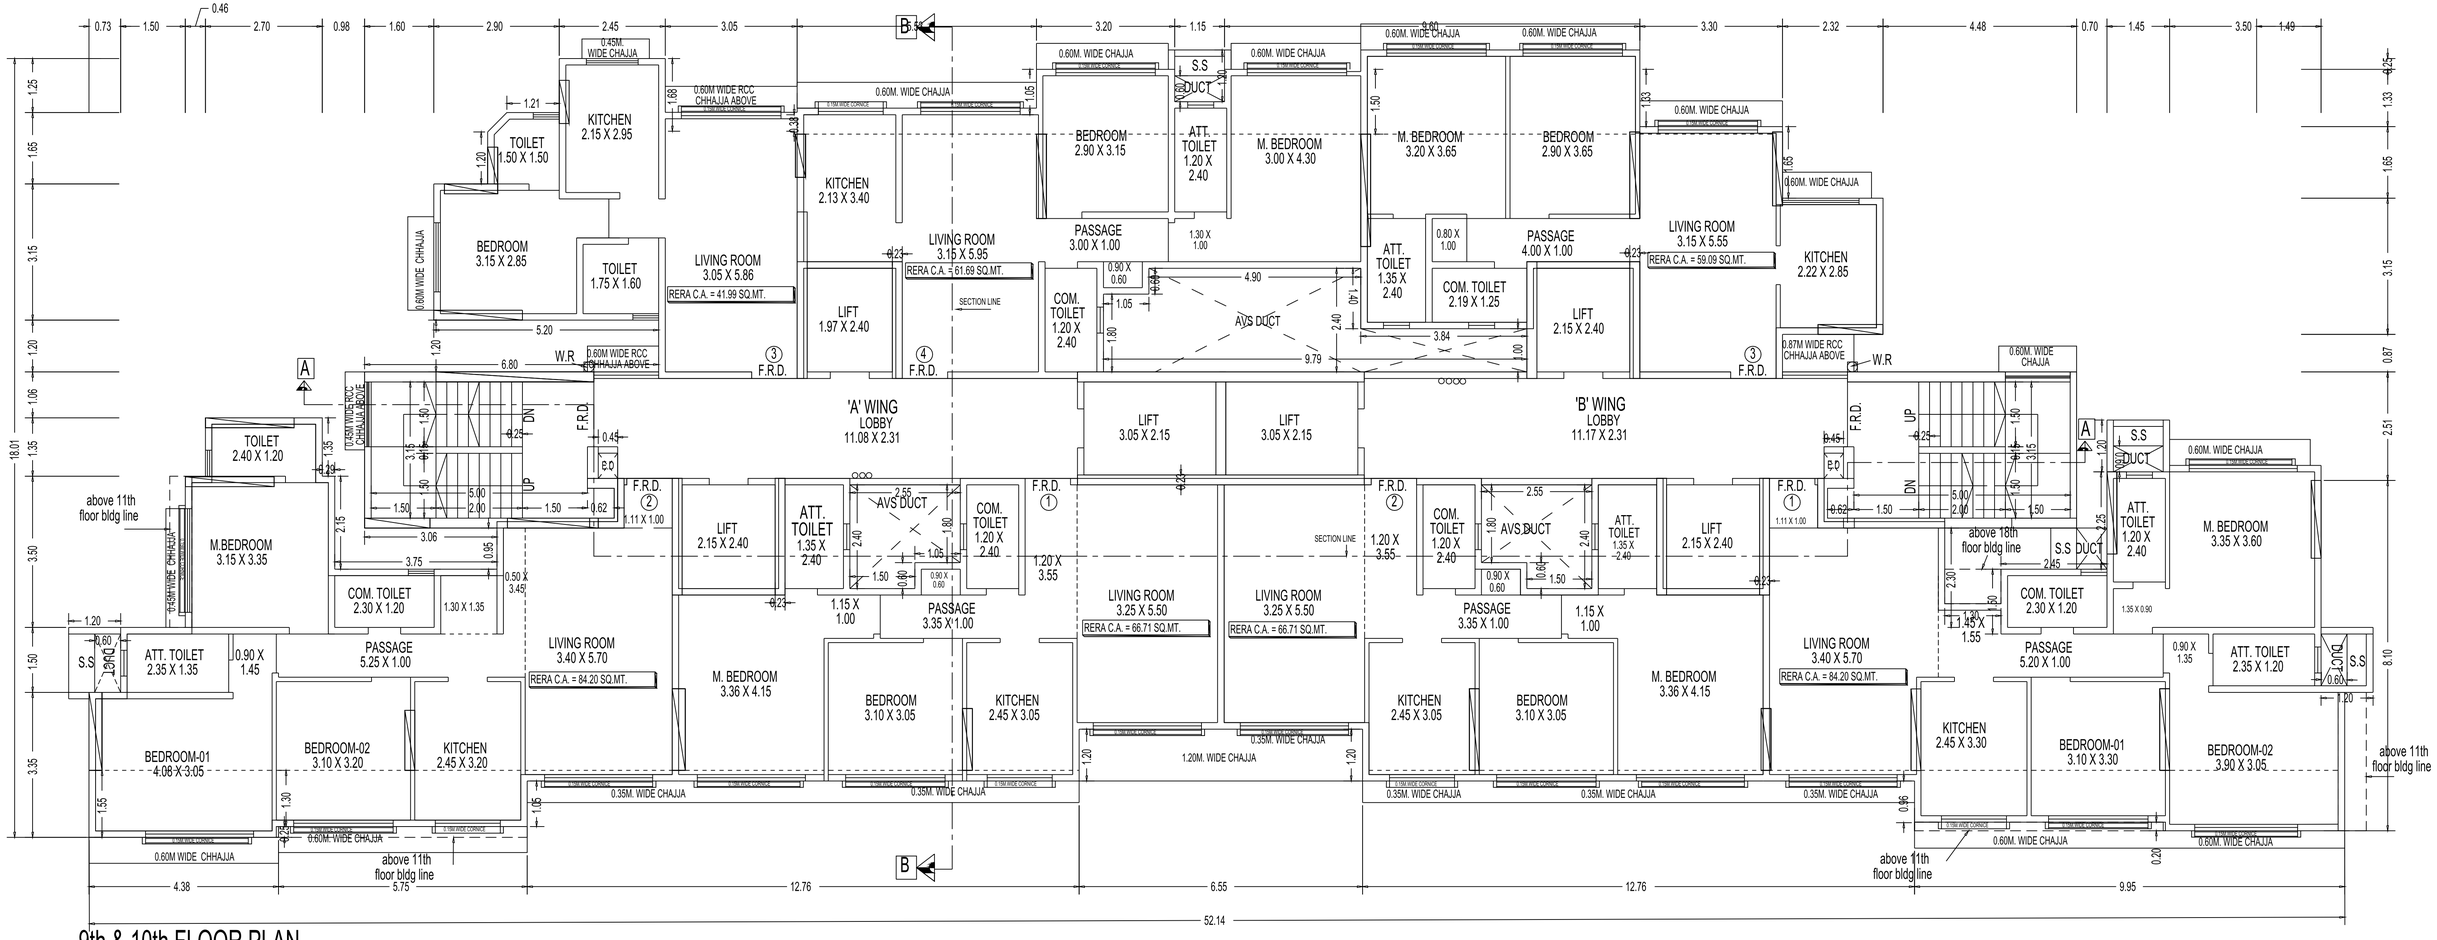

9th & 10th FLOOR PLAN


SCALE 1:100

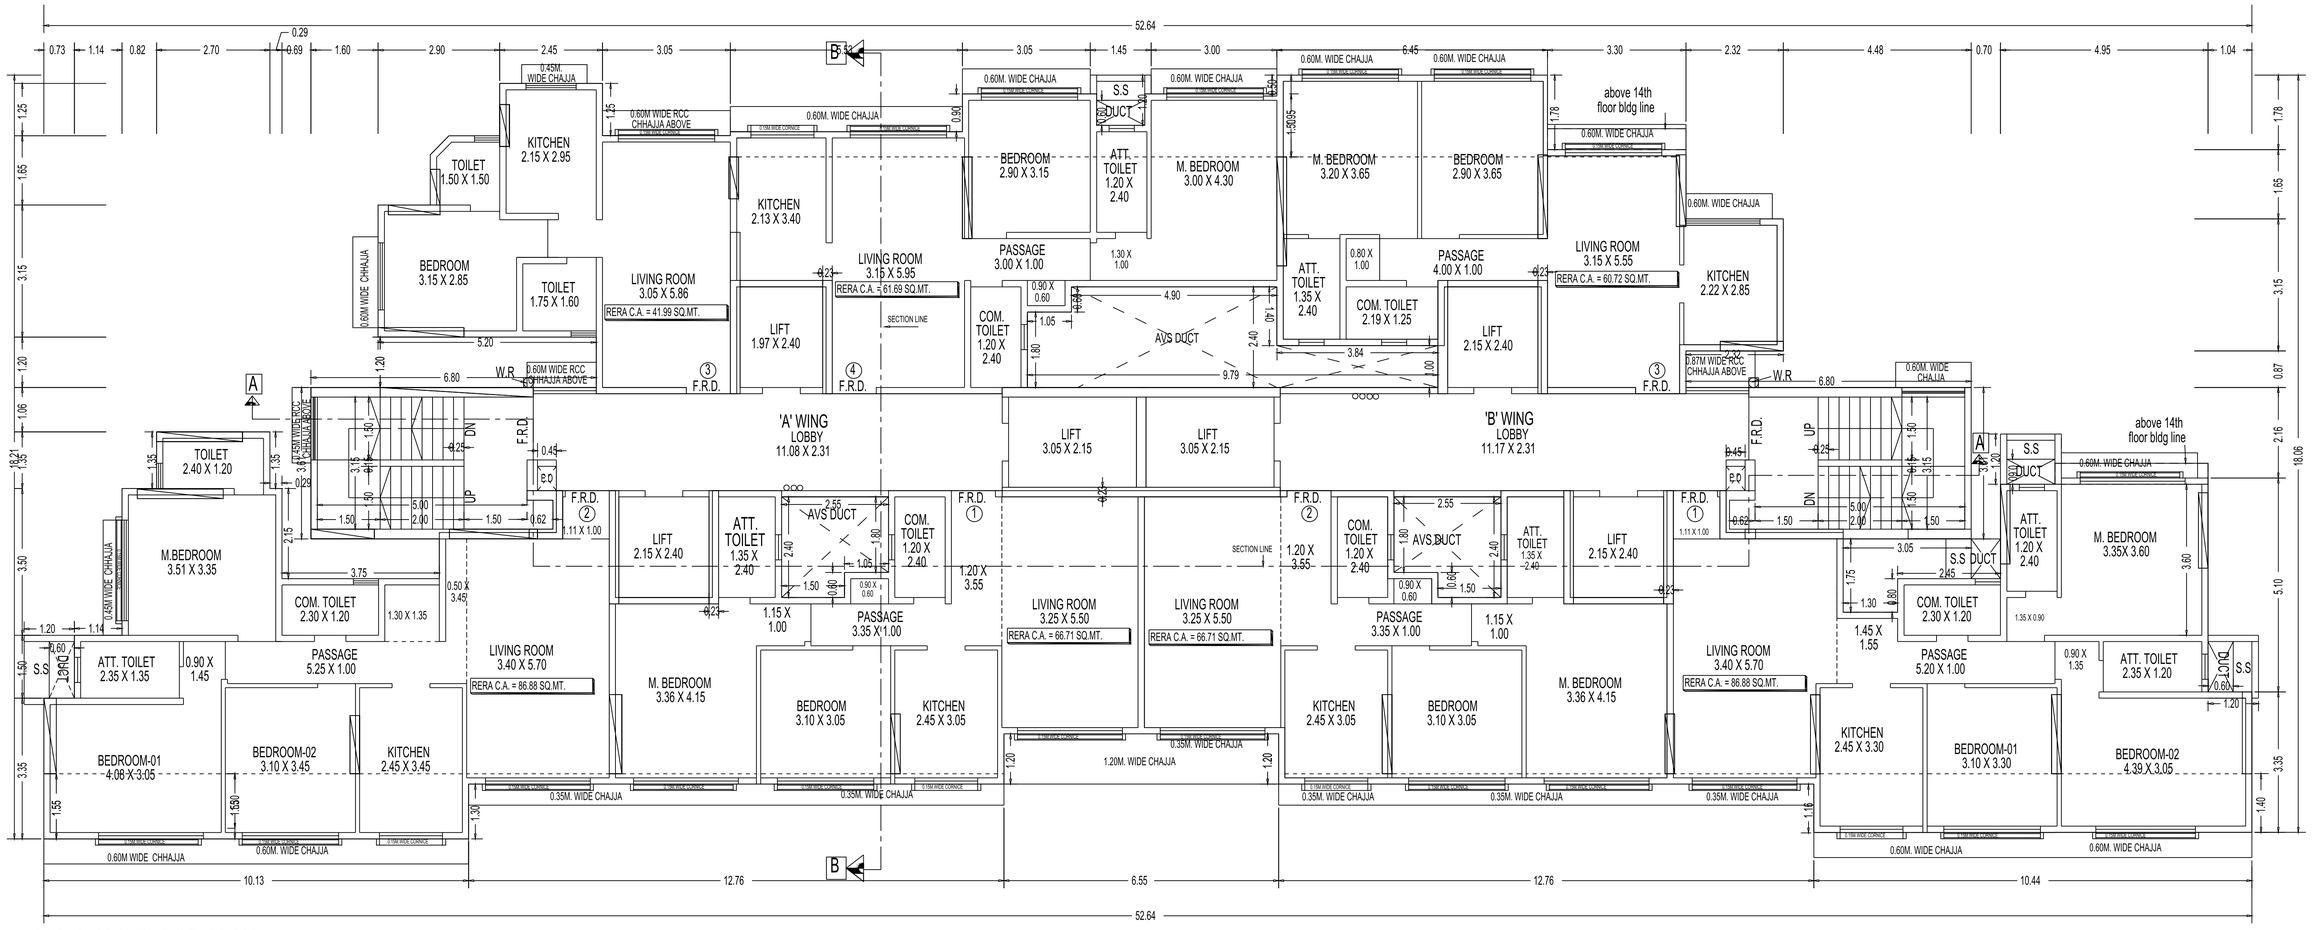
52.64
0.73
1.14
0.82
2.70
0.29
0.69
1.60
2.90
2.45
3.05
3.05
1.45
3.00
6.45
3.30
2.32
4.48
0.70
4.95
1.04
0.45M WIDE CHAJJA
0.60M WIDE RCC CHHAJJA ABOVE
0.60M WIDE CHAJJA
0.15M WIDE CORNICE
KITCHEN 2.15 X 2.95
TOILET 1.50 X 1.50
BEDROOM 3.15 X 2.85
TOILET 1.75 X 1.60
LIVING ROOM 3.05 X 5.86
RERA C.A. = 41.99 SQ.MT.
KITCHEN 2.13 X 3.40
LIVING ROOM 3.15 X 5.95
RERA C.A. = 61.69 SQ.MT.
BEDROOM 2.90 X 3.15
S.S DUCT
ATT. TOILET 1.20 X 2.40
M. BEDROOM 3.00 X 4.30
PASSAGE 3.00 X 1.00
1.30 X 1.00
above 14th floor bldg line
M. BEDROOM 3.20 X 3.65
BEDROOM 2.90 X 3.65
ATT. TOILET 1.35 X 2.40
0.80 X 1.00
PASSAGE 4.00 X 1.00
COM. TOILET 2.19 X 1.25
LIVING ROOM 3.15 X 5.55
RERA C.A. = 60.72 SQ.MT.
KITCHEN 2.22 X 2.85
0.67M WIDE RCC CHHAJJA ABOVE
SECTION LINE
LIFT 1.97 X 2.40
COM. TOILET 1.20 X 2.40
AVS DUCT
LIFT 2.15 X 2.40
F.R.D.
W.R
6.80
5.20
3.84
9.79
4.90
'A' WING LOBBY 11.08 X 2.31
'B' WING LOBBY 11.17 X 2.31
LIFT 3.05 X 2.15
LIFT 3.05 X 2.15
UP
DN
TOILET 2.40 X 1.20
M.BEDROOM 3.51 X 3.35
COM. TOILET 2.30 X 1.20
ATT. TOILET 2.35 X 1.35
PASSAGE 5.25 X 1.00
BEDROOM-01 4.08 X 3.05
BEDROOM-02 3.10 X 3.45
KITCHEN 2.45 X 3.45
LIVING ROOM 3.40 X 5.70
RERA C.A. = 86.88 SQ.MT.
M. BEDROOM 3.36 X 4.15
BEDROOM 3.10 X 3.05
KITCHEN 2.45 X 3.05
LIVING ROOM 3.25 X 5.50
RERA C.A. = 66.71 SQ.MT.
PASSAGE 3.35 X 1.00
1.20M WIDE CHAJJA
0.35M. WIDE CHAJJA
0.60M WIDE CHHAJJA
10.13
12.76
6.55
12.76
10.44
52.64
18.21
18.06
11th & 13th FLOOR PLAN
SCALE 1:100

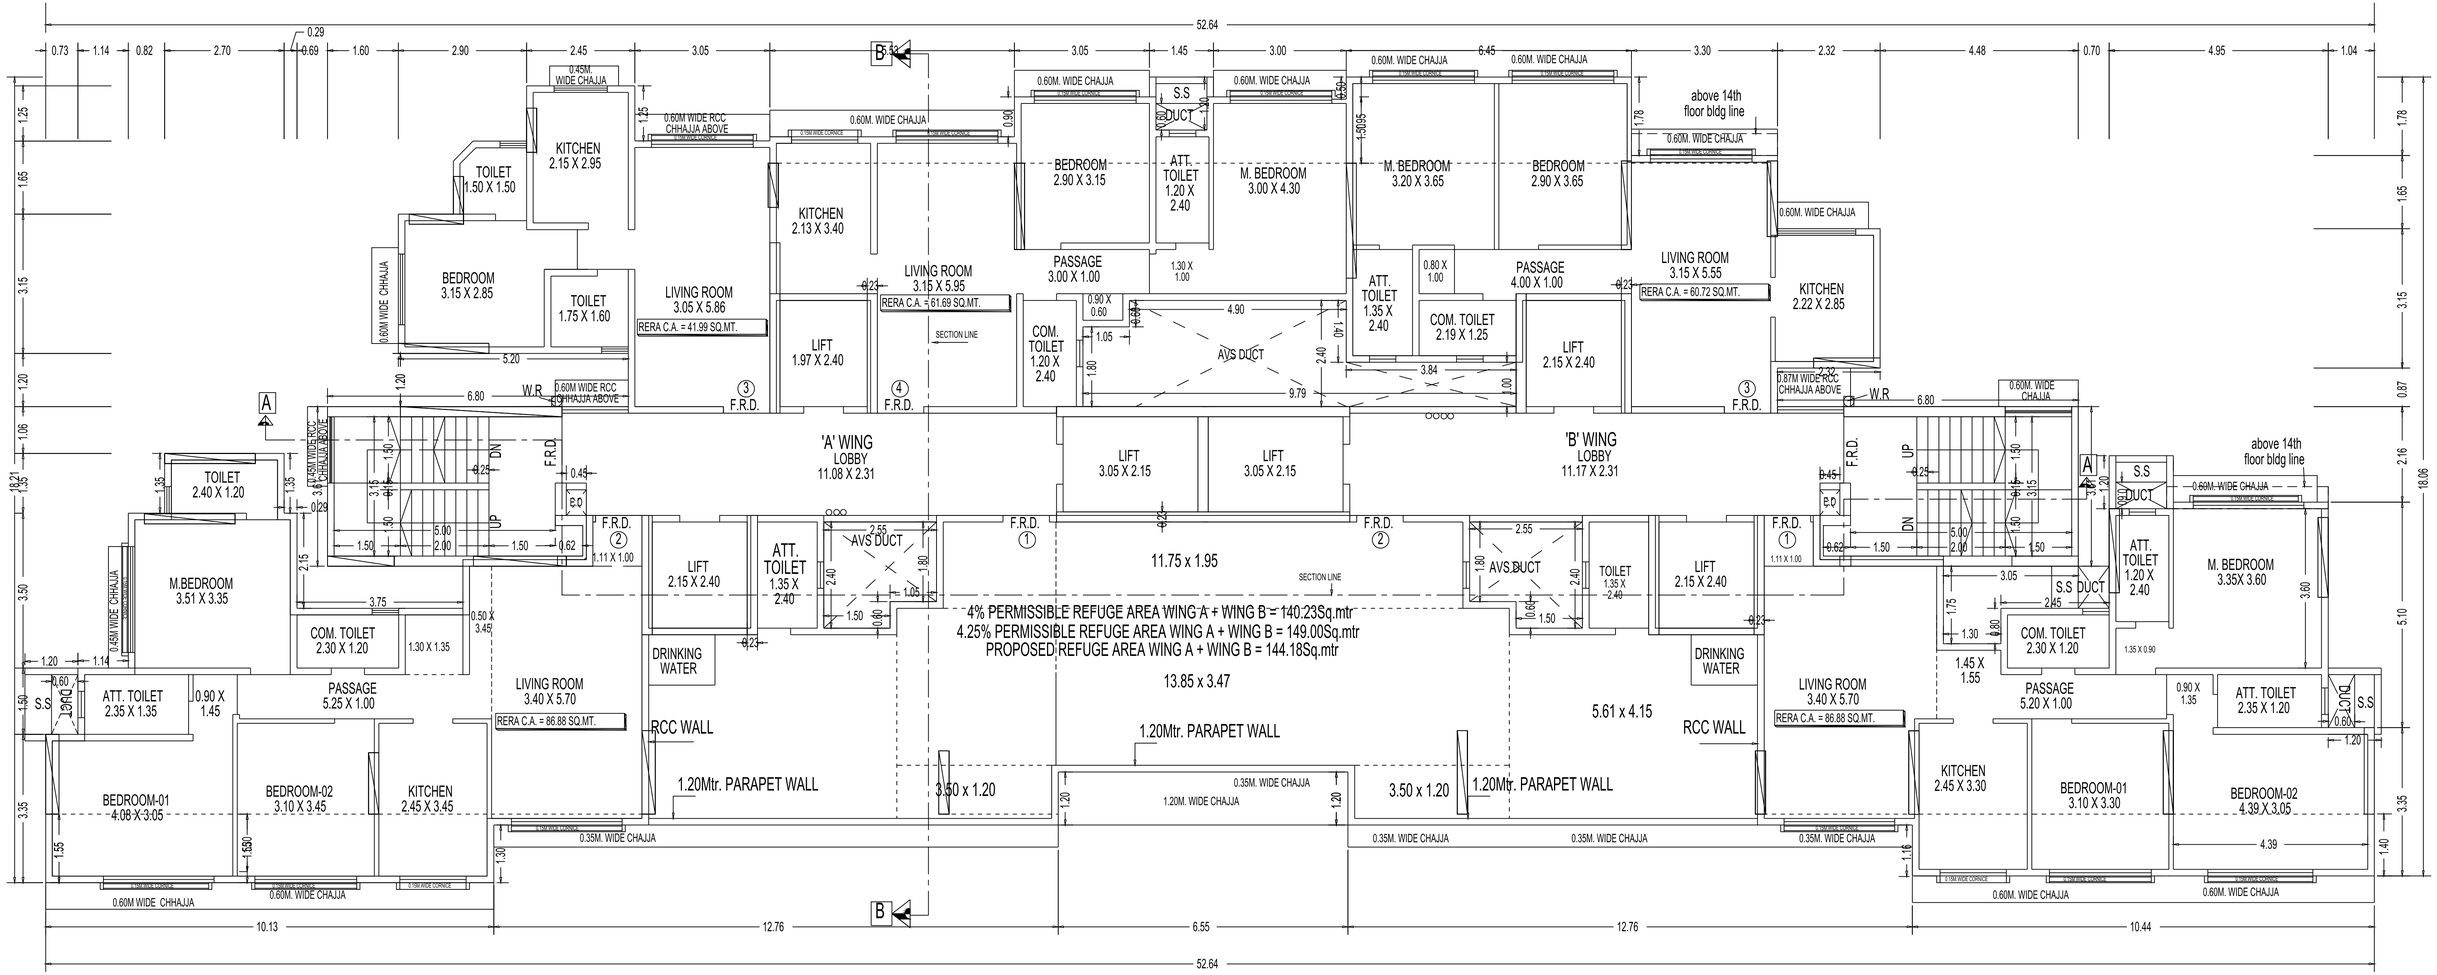

12th FLOOR PLAN (REFUGE)

SCALE 1:100

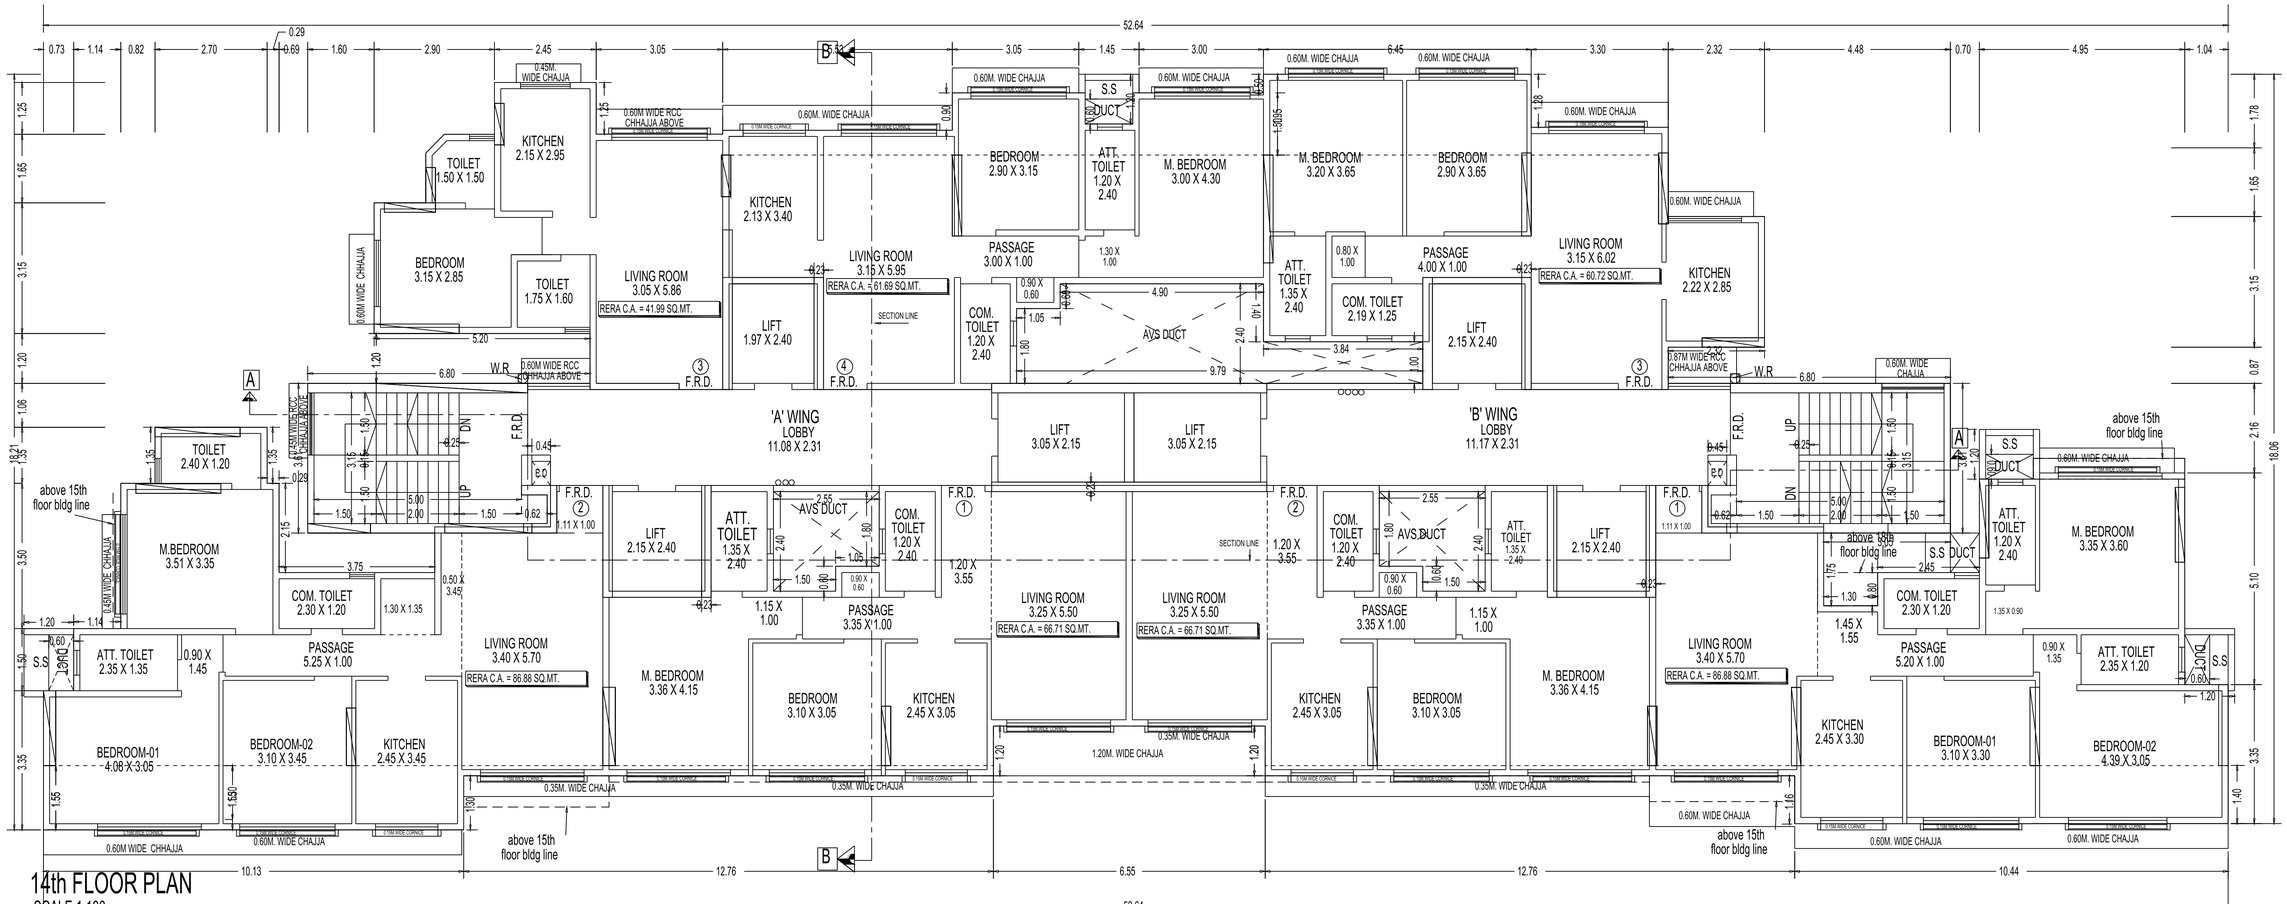


14th FLOOR PLAN

SCALE 1:100


D3


TOTAL DU

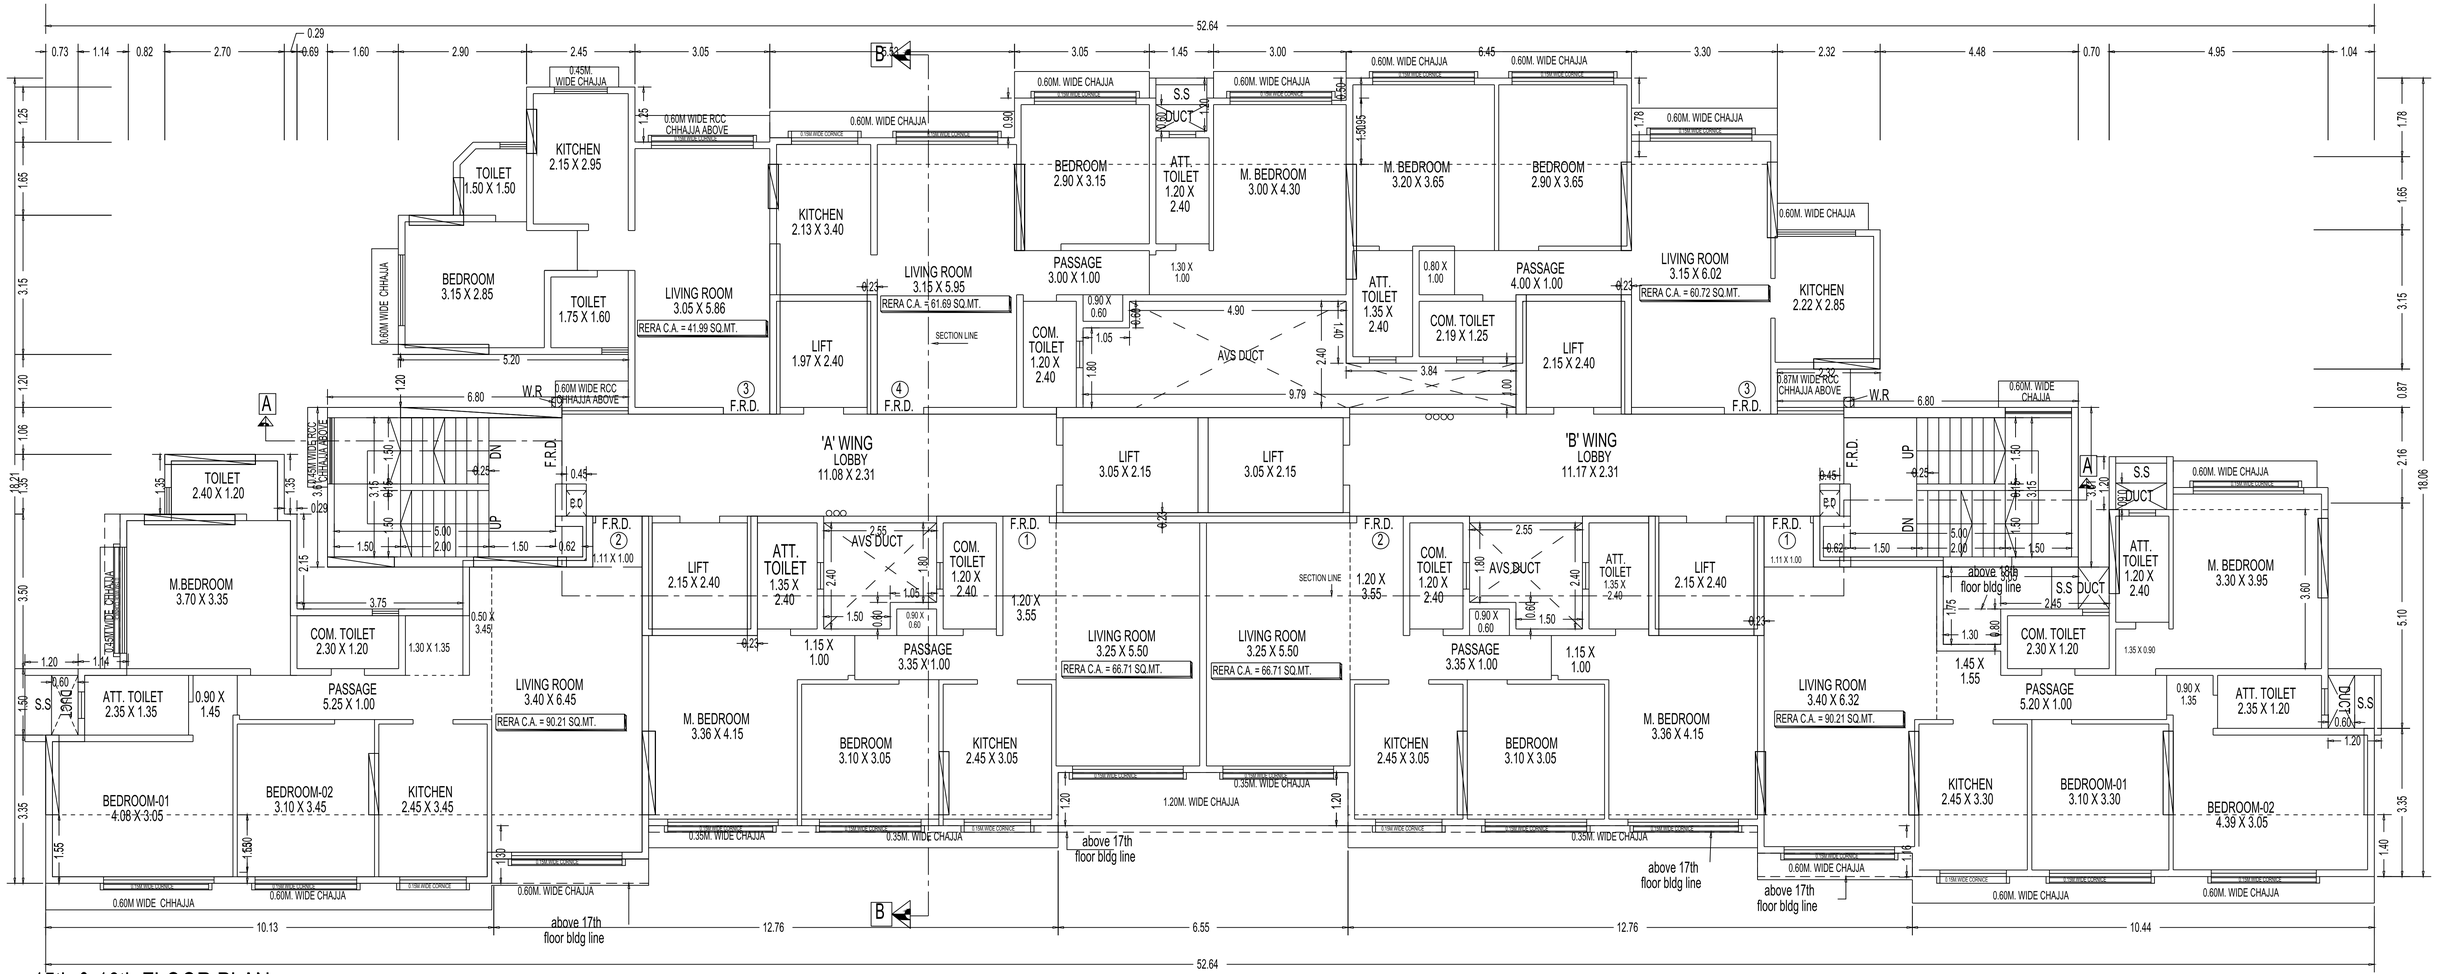

15th & 16th FLOOR PLAN


SCALE 1:100

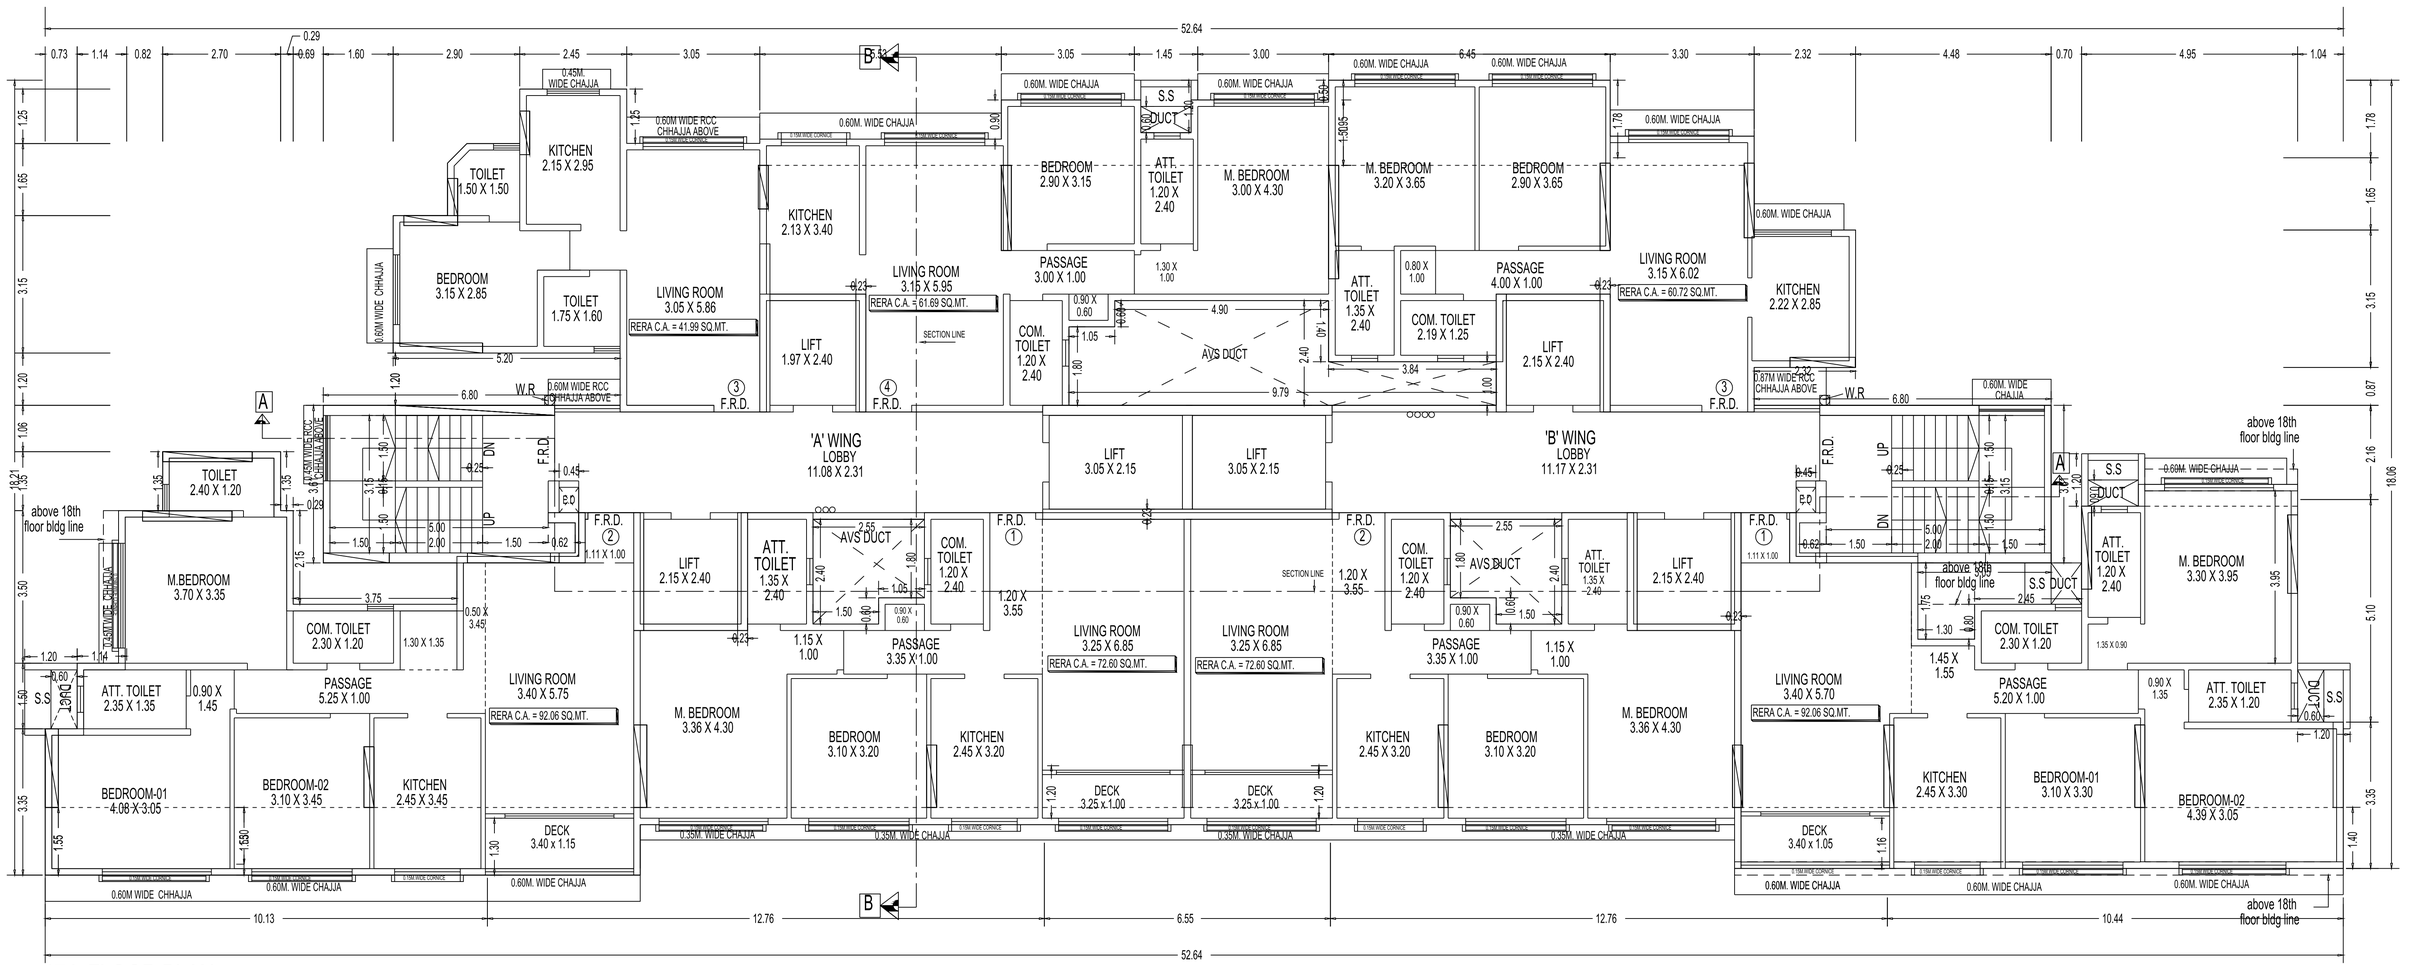
52.64
'A' WING
LOBBY
11.08 X 2.31
'B' WING
LOBBY
11.17 X 2.31
LIFT
3.05 X 2.15
LIFT
3.05 X 2.15
KITCHEN
2.15 X 2.95
TOILET
1.50 X 1.50
BEDROOM
3.15 X 2.85
TOILET
1.75 X 1.60
LIVING ROOM
3.05 X 5.86
RERA C.A. = 41.99 SQ.MT.
KITCHEN
2.13 X 3.40
LIFT
1.97 X 2.40
LIVING ROOM
3.15 X 5.95
RERA C.A. = 61.69 SQ.MT.
BEDROOM
2.90 X 3.15
PASSAGE
3.00 X 1.00
ATT. TOILET
1.20 X 2.40
M. BEDROOM
3.00 X 4.30
M. BEDROOM
3.20 X 3.65
BEDROOM
2.90 X 3.65
ATT. TOILET
1.35 X 2.40
COM. TOILET
2.19 X 1.25
PASSAGE
4.00 X 1.00
LIFT
2.15 X 2.40
LIVING ROOM
3.15 X 6.02
RERA C.A. = 60.72 SQ.MT.
KITCHEN
2.22 X 2.85
COM. TOILET
1.20 X 2.40
AVS DUCT
SECTION LINE
S.S DUCT
0.45M. WIDE CHAJJA
0.60M WIDE RCC CHHAJJA ABOVE
0.60M. WIDE CHAJJA
0.87M WIDE RCC CHHAJJA ABOVE
above 18th floor bldg line
TOILET
2.40 X 1.20
M.BEDROOM
3.70 X 3.35
COM. TOILET
2.30 X 1.20
PASSAGE
5.25 X 1.00
ATT. TOILET
2.35 X 1.35
LIVING ROOM
3.40 X 5.75
RERA C.A. = 92.06 SQ.MT.
BEDROOM-01
4.08 X 3.05
BEDROOM-02
3.10 X 3.45
KITCHEN
2.45 X 3.45
DECK
3.40 x 1.15
M. BEDROOM
3.36 X 4.30
BEDROOM
3.10 X 3.20
KITCHEN
2.45 X 3.20
PASSAGE
3.35 X 1.00
LIVING ROOM
3.25 X 6.85
RERA C.A. = 72.60 SQ.MT.
DECK
3.25 x 1.00
LIVING ROOM
3.40 X 5.70
RERA C.A. = 92.06 SQ.MT.
DECK
3.40 x 1.05
KITCHEN
2.45 X 3.30
BEDROOM-01
3.10 X 3.30
BEDROOM-02
4.39 X 3.05
ATT. TOILET
2.35 X 1.20
M. BEDROOM
3.30 X 3.95
0.35M. WIDE CHAJJA
0.60M. WIDE CHAJJA
0.60M WIDE CHHAJJA
10.13
12.76
6.55
12.76
10.44
18.06
17th FLOOR PLAN
SCALE 1:100

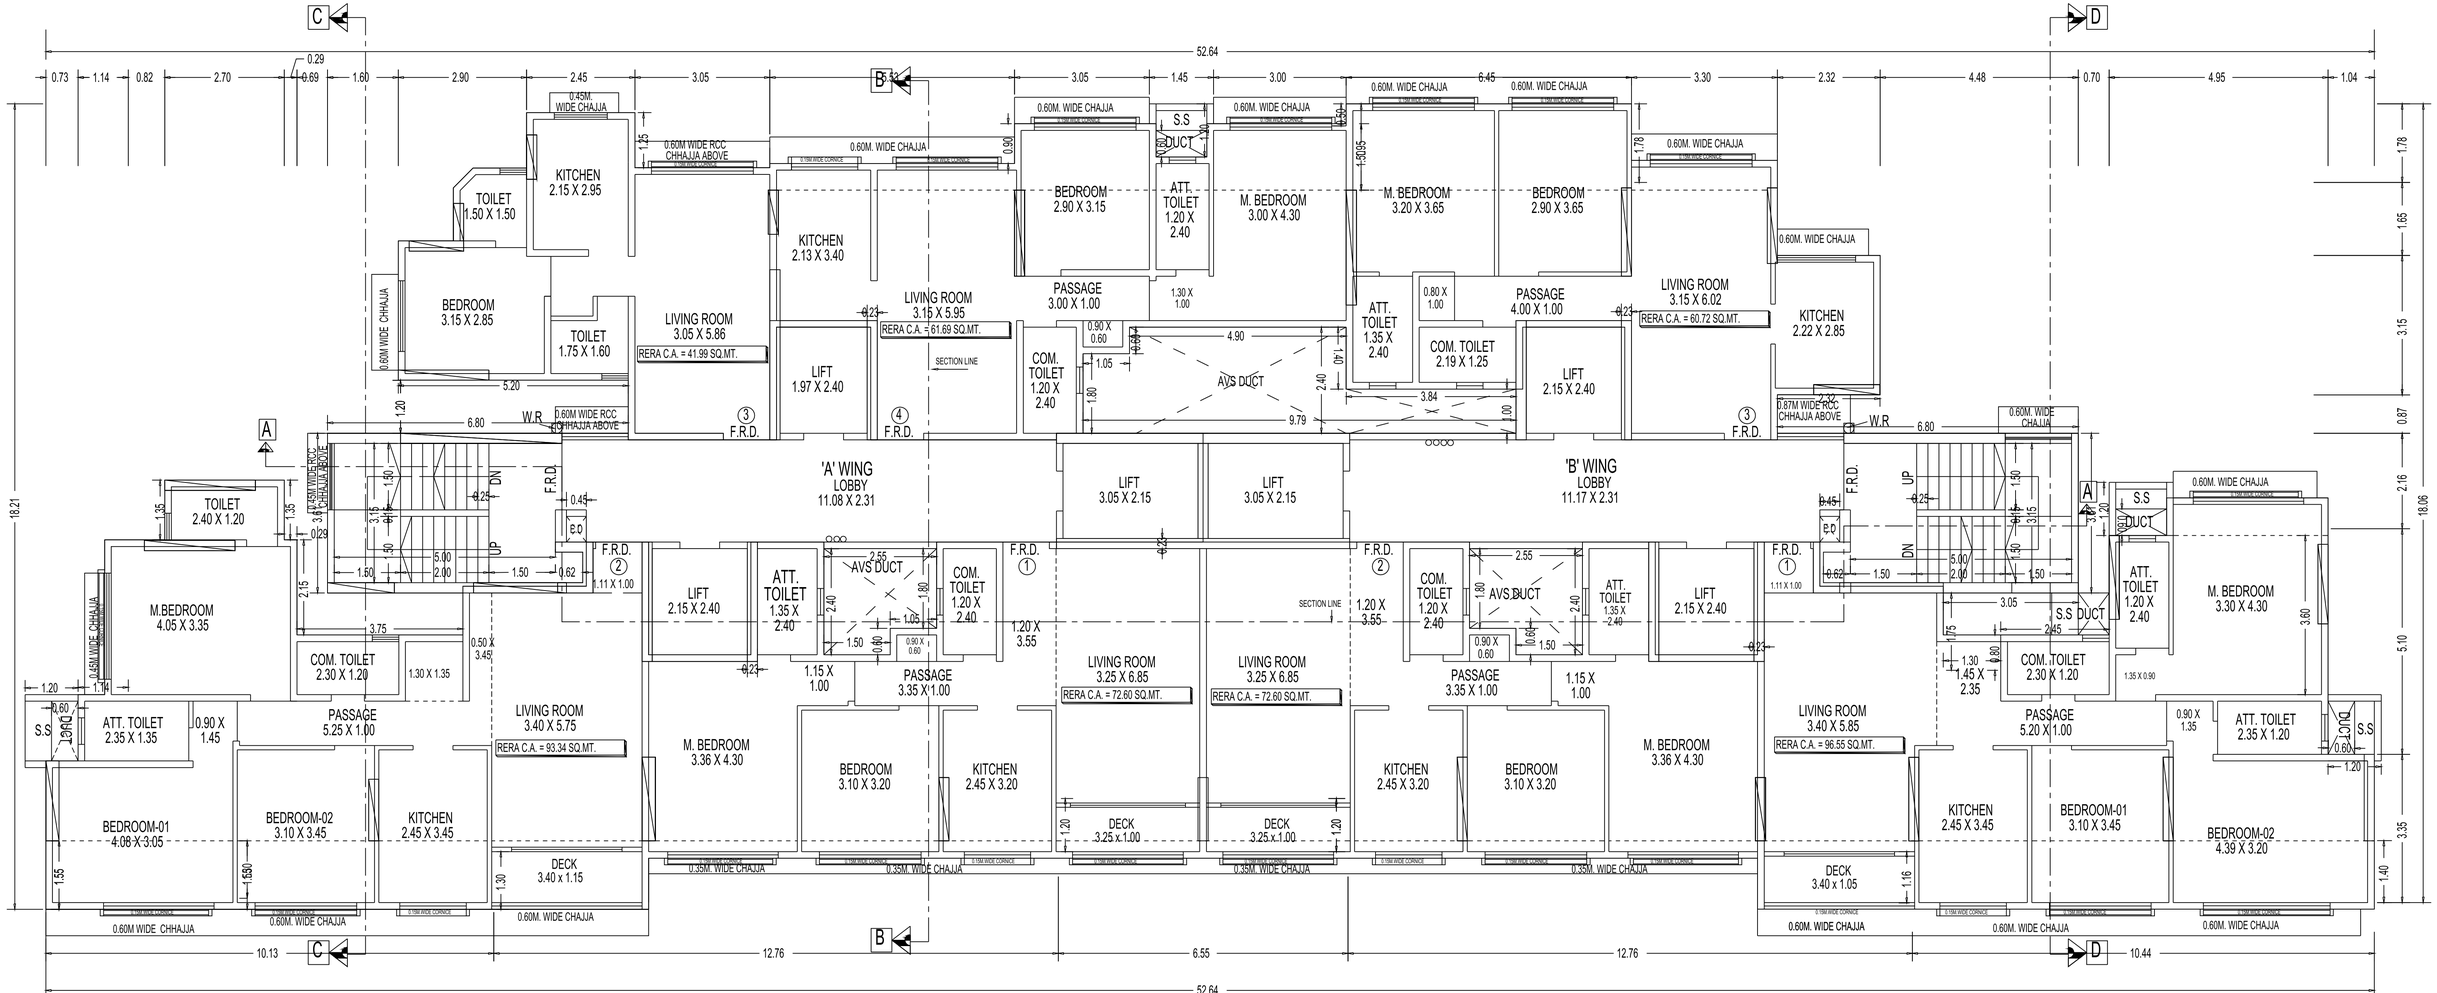

18th FLOOR PLAN

SCALE 1:100

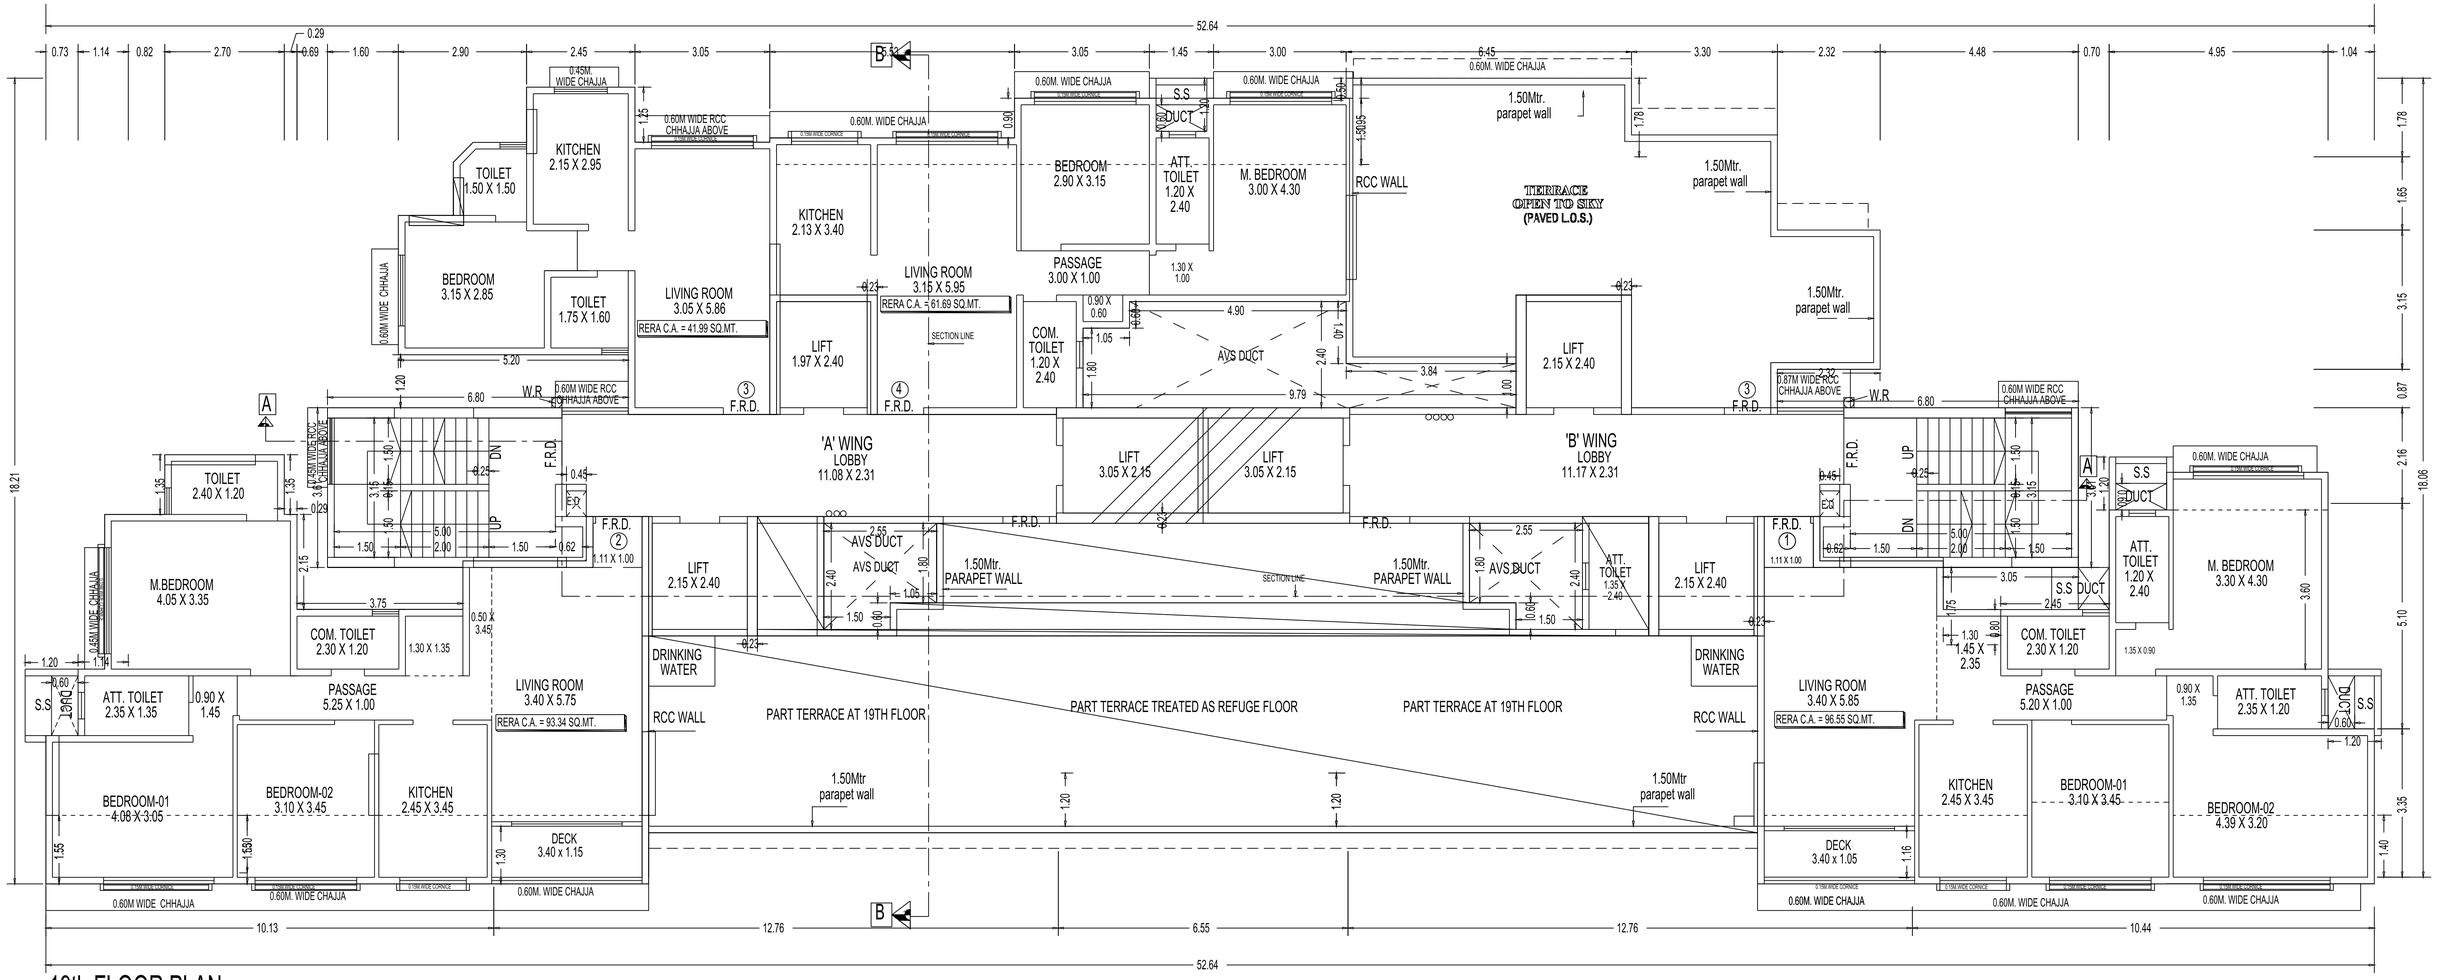

19th FLOOR PLAN

SCALE 1:100