

"E"
"D"
"C"
"B"
"A"
"F"
EAST
WEST
NORTH
SOUTH
C.T.S.NO.832/2
C.T.S.NO.832
C.T.S.NO.1012
( WING - A )
( WING - B )
MASTER BED 5.02X3.95
BED ROOM 5.10X3.50
BED ROOM 4.12X3.50
BED ROOM 4.25X3.50
BED ROOM 5.02X3.95
BED ROOM 4.12X3.50
BED ROOM 5.10X3.50
BED ROOM 4.25X3.50
BED ROOM 5.02X3.95
LIVING 8.64X4.10
LIVING 8.64X4.10
KITCHEN 3.00X4.28
KITCHEN 3.00X4.28
FOYER 3.15X1.60
FOYER 3.15X1.60
LOBBY 6.85X2.61
LOBBY 3.00X7.50
LOBBY 2.00X1.95
LOBBY 2.70X2.20
FIRE LIFT 2.85X2.20
LIFT 2.50X2.20
LIFT 2.50X2.20
LIFT 2.50X2.20
DECK 2.40X2.41
DECK 2.40X2.41
SERVANT 1.95X2.05
SERVANT 1.95X2.05
DINING 2.45X1.90
DINING 2.45X1.90
TOILET 2.45X1.85 M.V.
TOILET 2.45X1.85 M.V.
TOILET 2.45X1.80 M.V.
TOILET 2.45X1.80 M.V.
TOILET 2.75X1.68
TOILET 2.75X1.68
TOILET 2.28X2.03
TOILET 2.28X2.03
TOILET 2.28X2.03
TOILET 2.28X2.03
M1 1.95X2.13
M1 1.95X2.13
B1 1.95X0.80
B1 1.95X0.80
B1 1.95X2.13
B1 1.95X2.13
W.I.W. 2.20X1.73
W.I.W. 2.20X1.73
W.I.W. 2.20X1.53
W.I.W. 2.20X1.53
BALCONY 4.20X1.63
BALCONY 4.20X1.63
BALCONY 4.20X1.63
BALCONY 4.20X1.63
BALCONY 4.20X1.63
BALCONY 4.20X1.63
STEP/RAISING
STEP/RAISING
PASS. 4.03X1.05
PASS. 4.03X1.05
PASS. 4.45X1.00
PASS. 2.95X1.20
PASS. 2.95X1.20
PASS. 4.45X1.00
PASS. 2.60X1.05
PASS. 3.50X1.05
PASS. 3.50X1.05
PASS. 3.50X1.05
PASS. 3.50X1.05
MASTER BED 3.95X3.20
MASTER BED 3.95X3.20
MASTER BED 3.95X3.35
MASTER BED 3.95X3.35
MASTER BED 3.95X3.35
MASTER BED 3.95X3.35
BED ROOM 3.95X3.35
BED ROOM 3.95X3.35
BED ROOM 3.95X3.35
BED ROOM 3.95X3.35
BED ROOM 3.95X3.05
BED ROOM 3.95X3.05
BED ROOM 3.95X3.05
BED ROOM 3.95X3.05
BED ROOM 4.13X3.20
BED ROOM 4.13X3.20
BED ROOM 3.20X3.05
BED ROOM 3.20X3.05
BED ROOM 4.13X3.20
BED ROOM 4.13X3.20
BED ROOM 3.95X3.80
BED ROOM 3.95X3.80
BED ROOM 3.95X4.20
BED ROOM 3.95X4.20
LIVING/DINING 3.95X5.62
LIVING/DINING 3.95X5.62
LIVING/DINING 3.95X5.62
LIVING/DINING 3.95X5.62
LIVING/DINING 3.95X5.65
LIVING/DINING 3.95X5.65
LIVING 3.95X3.95
LIVING 3.95X3.95
KITCHEN 2.45X3.05
KITCHEN 2.45X3.05
KITCHEN 2.45X3.05
KITCHEN 2.45X3.05
KITCHEN 2.45X3.63
KITCHEN 2.45X3.63
KITCHEN 3.20X2.45
KITCHEN 3.20X2.45
KITCHEN 2.45X3.63
KITCHEN 2.45X3.63
LOBBY 2.60X1.45
LOBBY 2.60X1.45
LOBBY 2.60X1.50
LOBBY 2.60X1.50
LOBBY 2.60X1.45
LOBBY 2.60X1.45
LOBBY 2.60X1.50
LOBBY 2.60X1.50
LOBBY 2.60X1.45
LOBBY 2.60X1.45
LOBBY 2.60X1.50
LOBBY 2.60X1.50
LOBBY 2.60X2.15
LOBBY 3.15X13.38
LOBBY 5.00X2.43
LOBBY 1.63X1.55
FIRE LIFT 2.45X2.45
FIRE LIFT 2.45X2.45
TOILET 1.53X2.45
TOILET 1.53X2.45
TOILET 1.53X2.45
TOILET 1.53X2.45
TOILET 1.49X2.45
TOILET 1.49X2.45
TOILET 1.53X1.75
TOILET 1.53X1.50
TOILET 1.53X2.45
TOILET 1.53X2.45
TOILET 2.45X1.38
TOILET 2.45X1.38
TOILET 2.45X1.38
TOILET 2.45X1.38
TOILET 2.45X1.38
TOILET 2.45X1.38
TOILET 2.45X1.38
TOILET 2.45X1.38
B1 2.17X1.00
B1 2.17X1.00
B1 2.17X1.00
B1 2.17X1.00
B1 1.72X1.40
B1 1.72X1.40
D1 2.60X1.75
D1 2.60X1.75
1.20 M.W.CHAJJA
1.00 M.W.CHAJJA
0.90 M.W.CHAJJA
0.60 M.W.CHAJJA
RCC SLAB 150 THK
RCC SLAB 100 THK
RCC SLAB 125 THK

FILE NO. - P-24461/2024/(832/1)/KW WARD/AMBIVALI | 6/16

7TH FLOOR PLAN

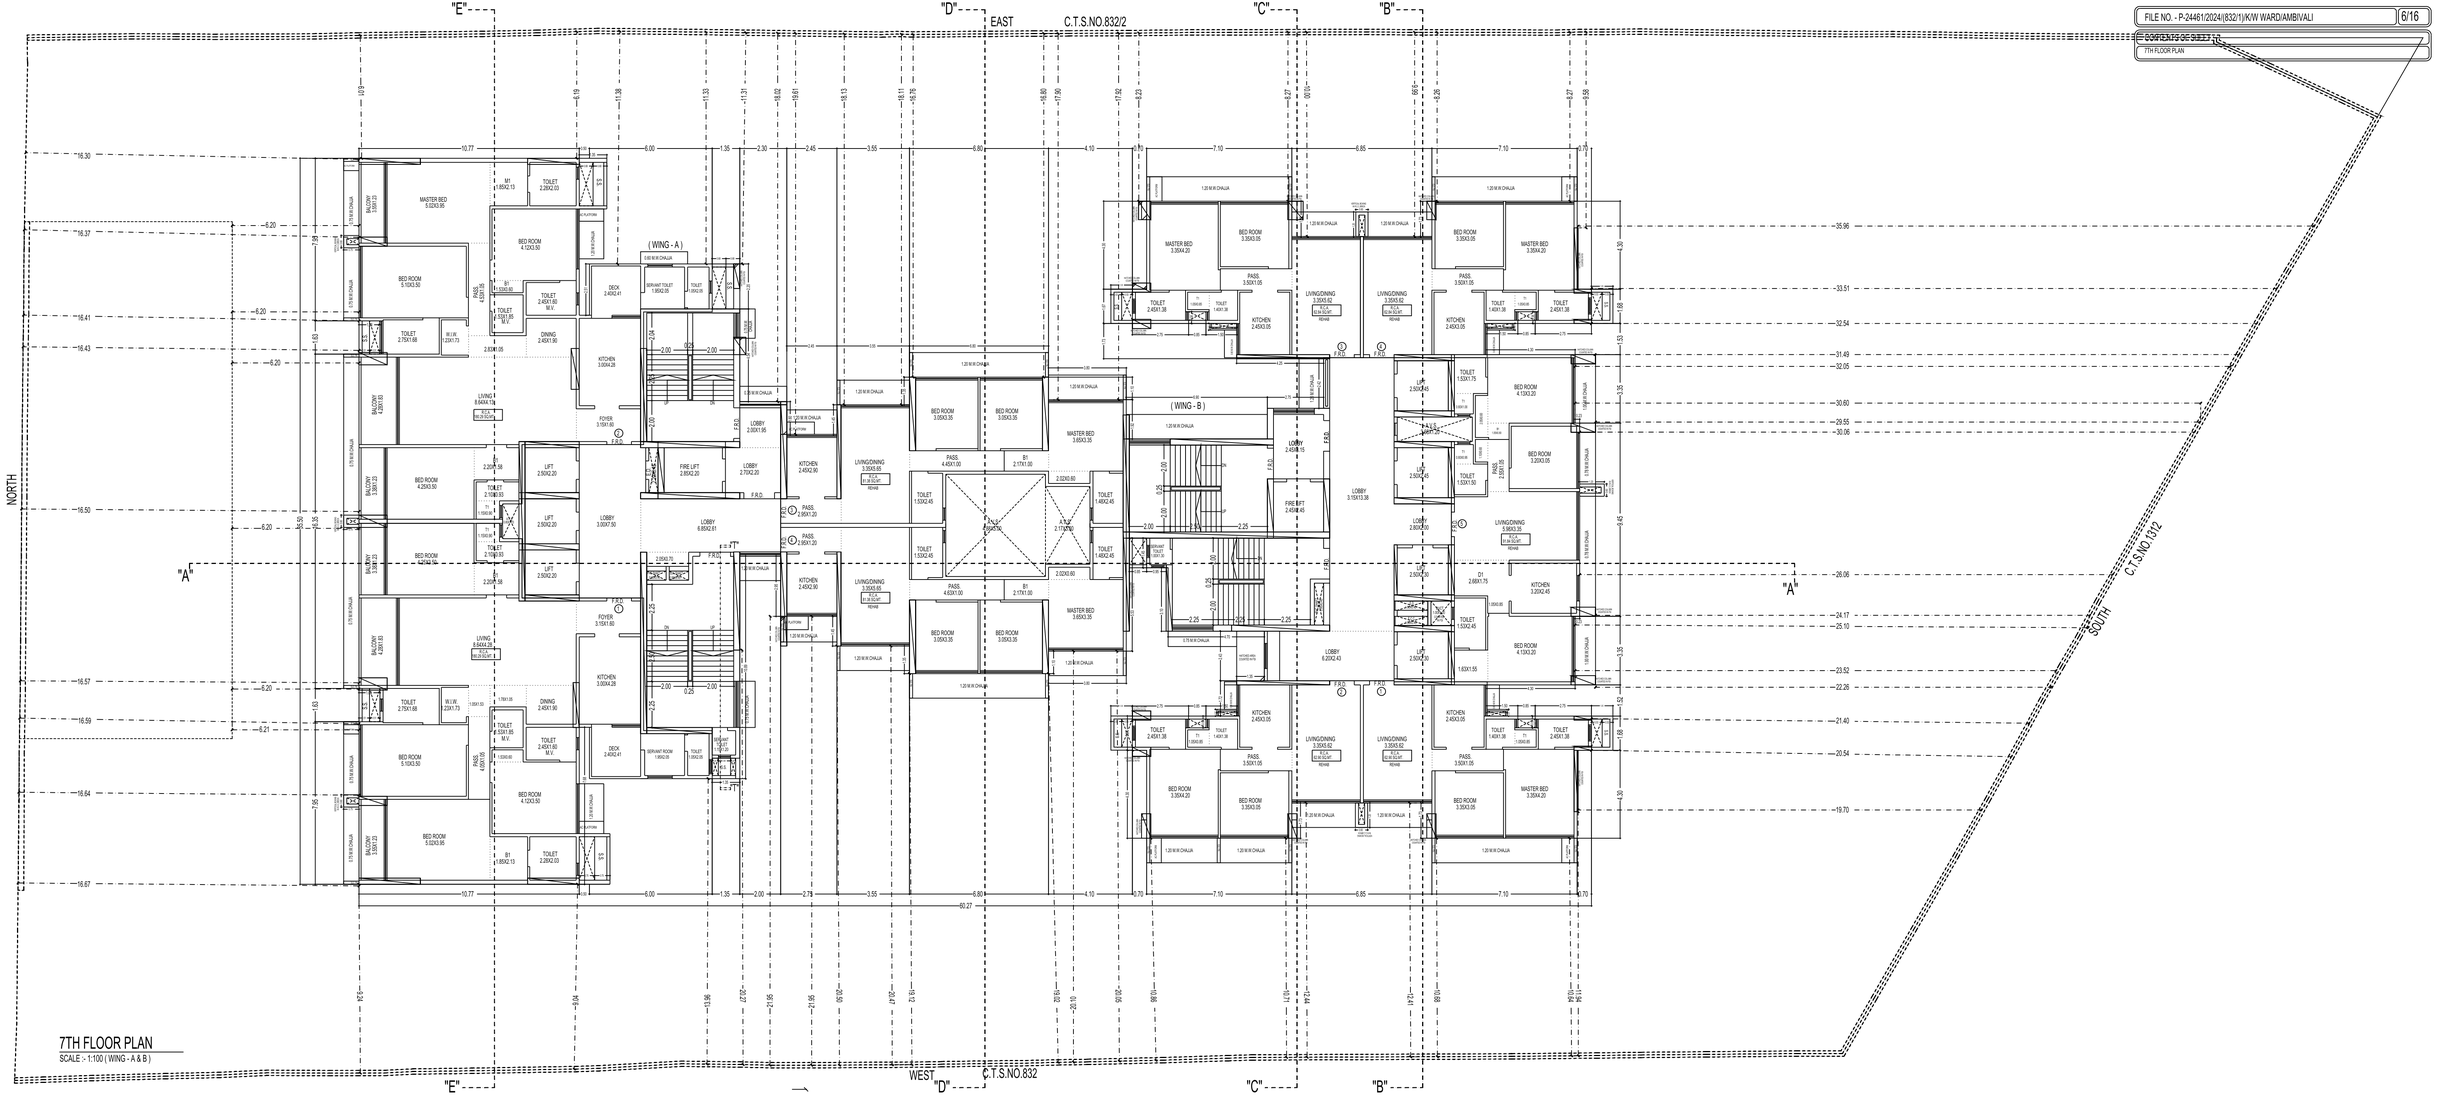


## 7TH FLOOR PLAN

SCALE :- 1:100 ( WING - A & B )

FILE NO. - P-24461/2024/(832/1)/K/W WARd/AMBIVALI 7/16

8TH FLOOR PLAN




8TH FLOOR PLAN
SCALE :- 1:100 ( WING - A & B )

| 8TH FLOOR COLUMN AREA CALCULATION ( WING - B ) | | | | | | | | |
|---|---|---|---|---|---|---|---|---|
| 1 | 0.40 | X | 0.90 | X | 2NOS | = | 0.72 | SQ.MT. |
| 2 | 0.25 | X | 0.90 | X | 1NO | = | 0.23 | SQ.MT. |
| 3 | 0.05 | X | 3.00 | X | 2NOS | = | 0.30 | SQ.MT. |
| 4 | 0.70 | X | 0.30 | X | 2NOS | = | 0.42 | SQ.MT. |
| 5 | 0.90 | X | 0.25 | X | 2NOS | = | 0.45 | SQ.MT. |
| 6 | 1.00 | X | 0.40 | X | 2NOS | = | 0.80 | SQ.MT. |
| 7 | 0.78 | X | 0.45 | X | 2NOS | = | 0.70 | SQ.MT. |
| 8 | 0.25 | X | 1.20 | X | 1NO | = | 0.30 | SQ.MT. |
| 9 | 0.25 | X | 0.53 | X | 2NOS | = | 0.27 | SQ.MT. |
| | | | TOTAL ADDITION | | | = | 4.29 | SQ.MT. |


BUILT UP AREA CALCULATION


| BUILT UP AREA CALCULATION | | | | | | | |
|---|---|---|---|---|---|---|---|
| 8TH FLOOR ( WING - B ) | | | | | | | |
| | 22.75 | X | 32.35 | X | 1NO | = | 735.96 SQ.MT. |

BUILT UP AREA CALCULATION

FILE NO. - P-24461/2024/(832/1)/K/W WARd/AMBIVALI 8/16


9TH TO 11TH FLOOR PLAN

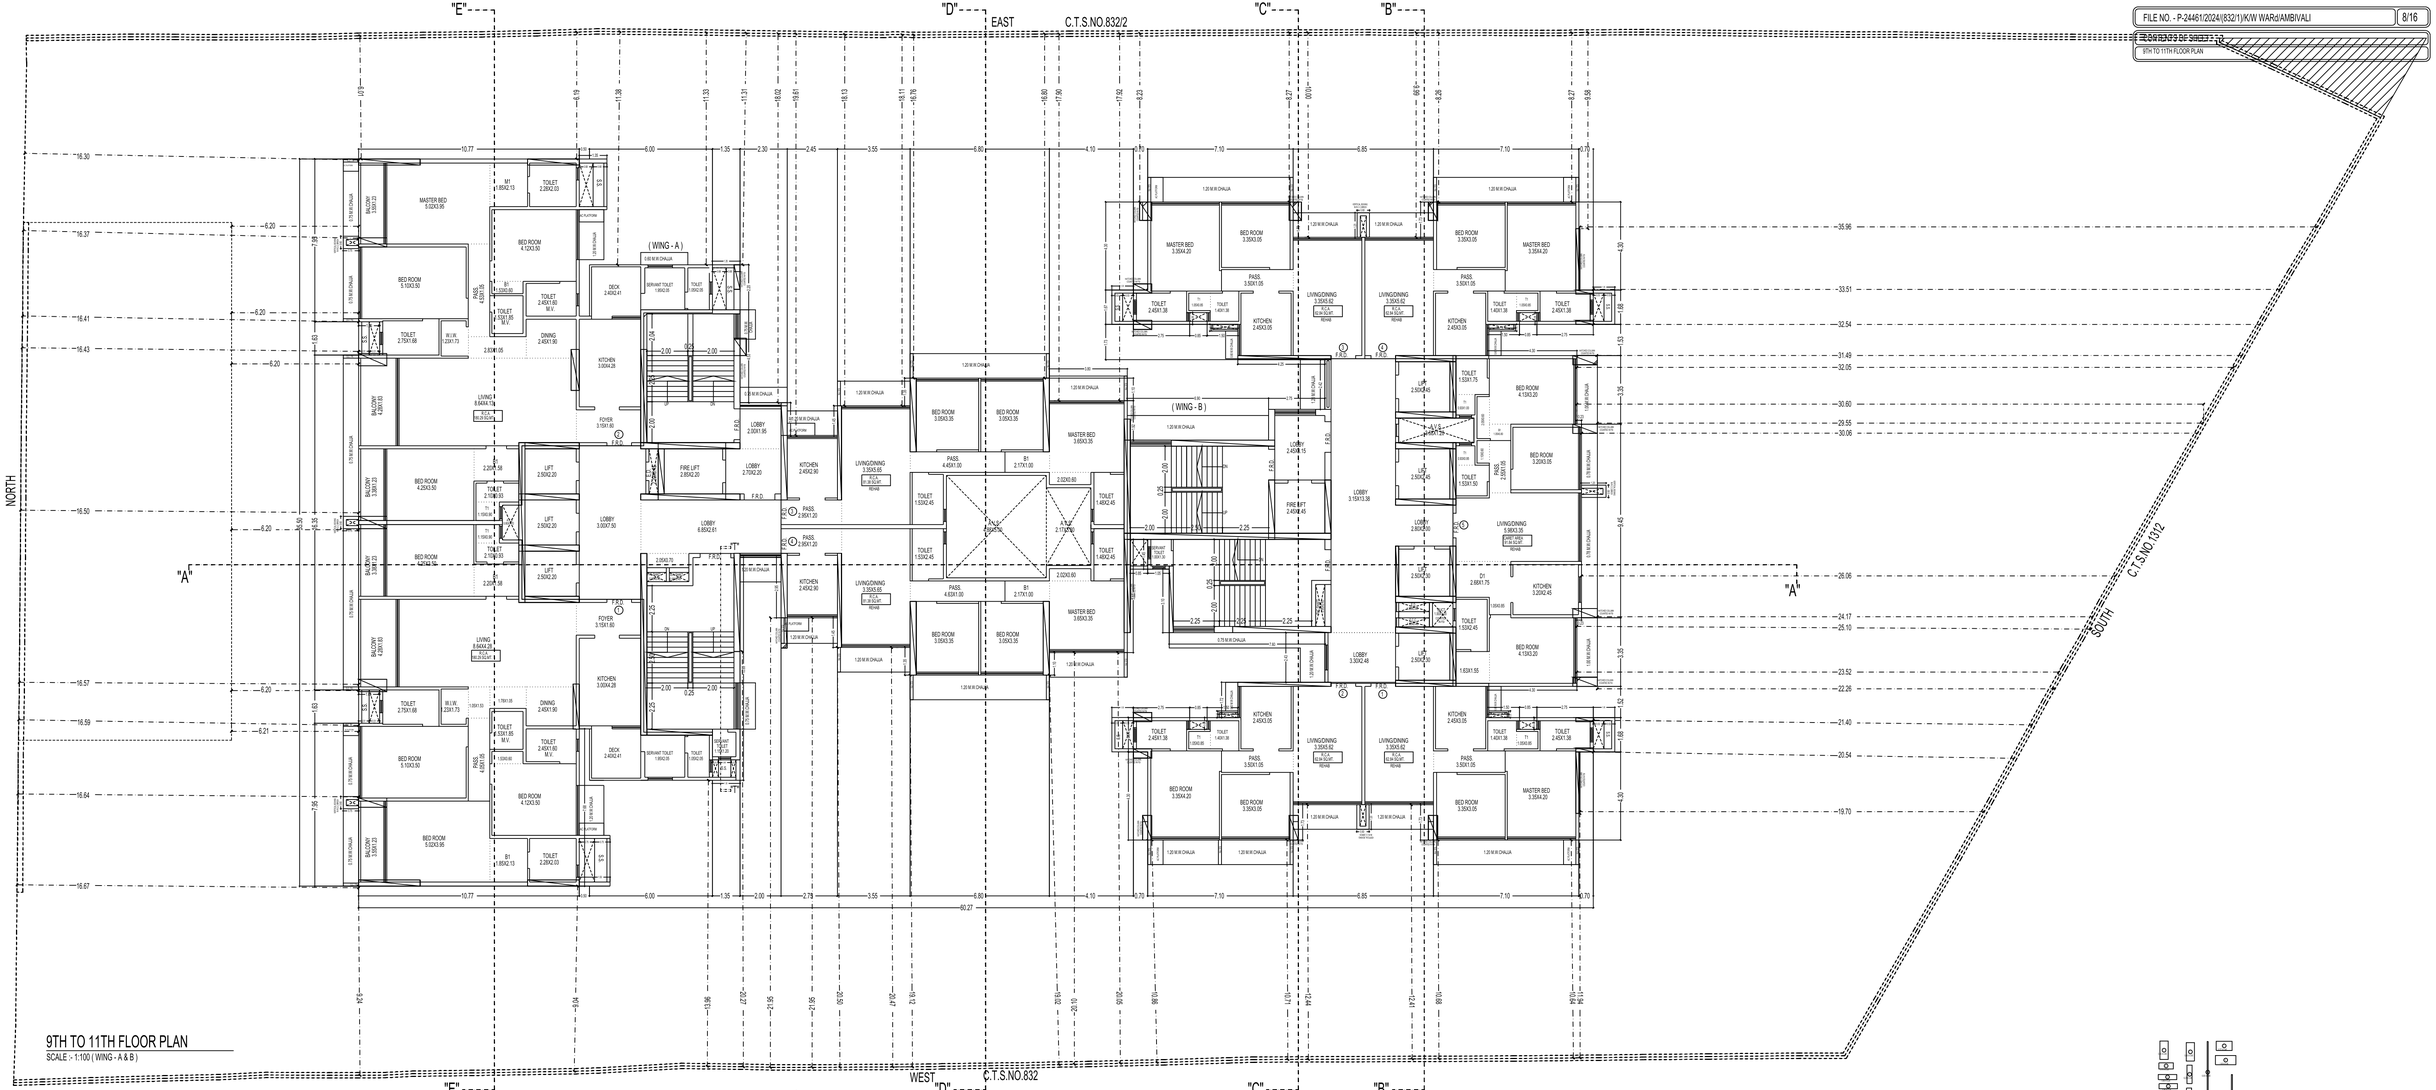


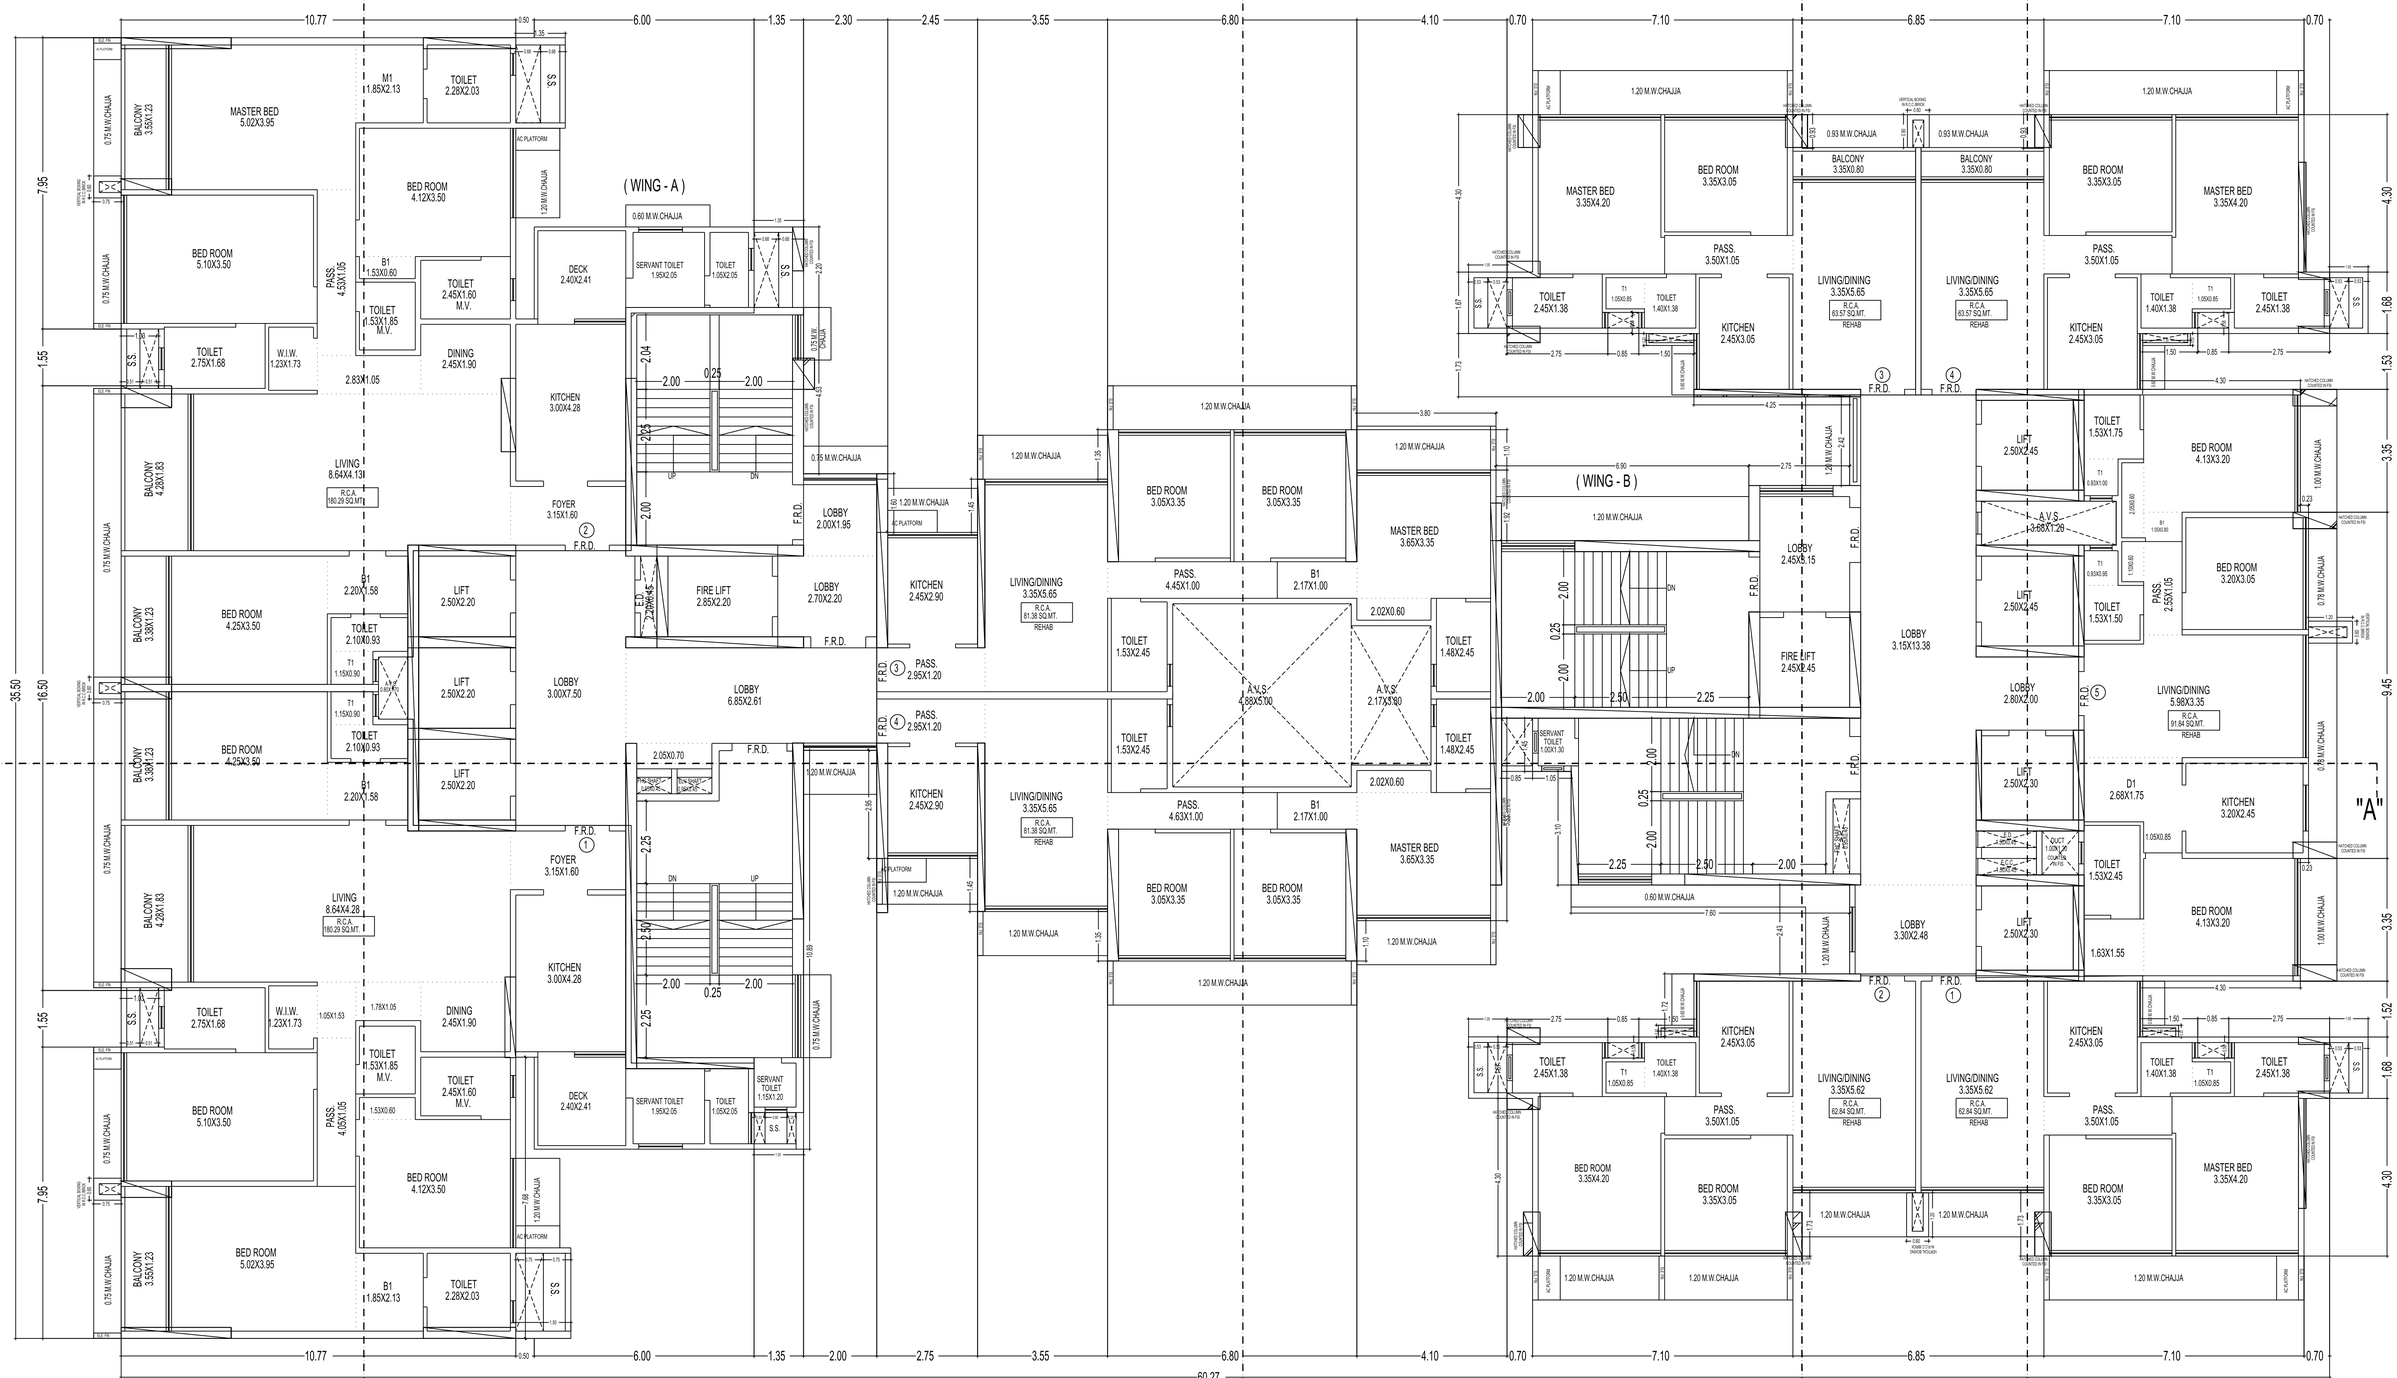


# 12TH FLOOR PLAN

SCALE :- 1:100 ( WING - A & B )

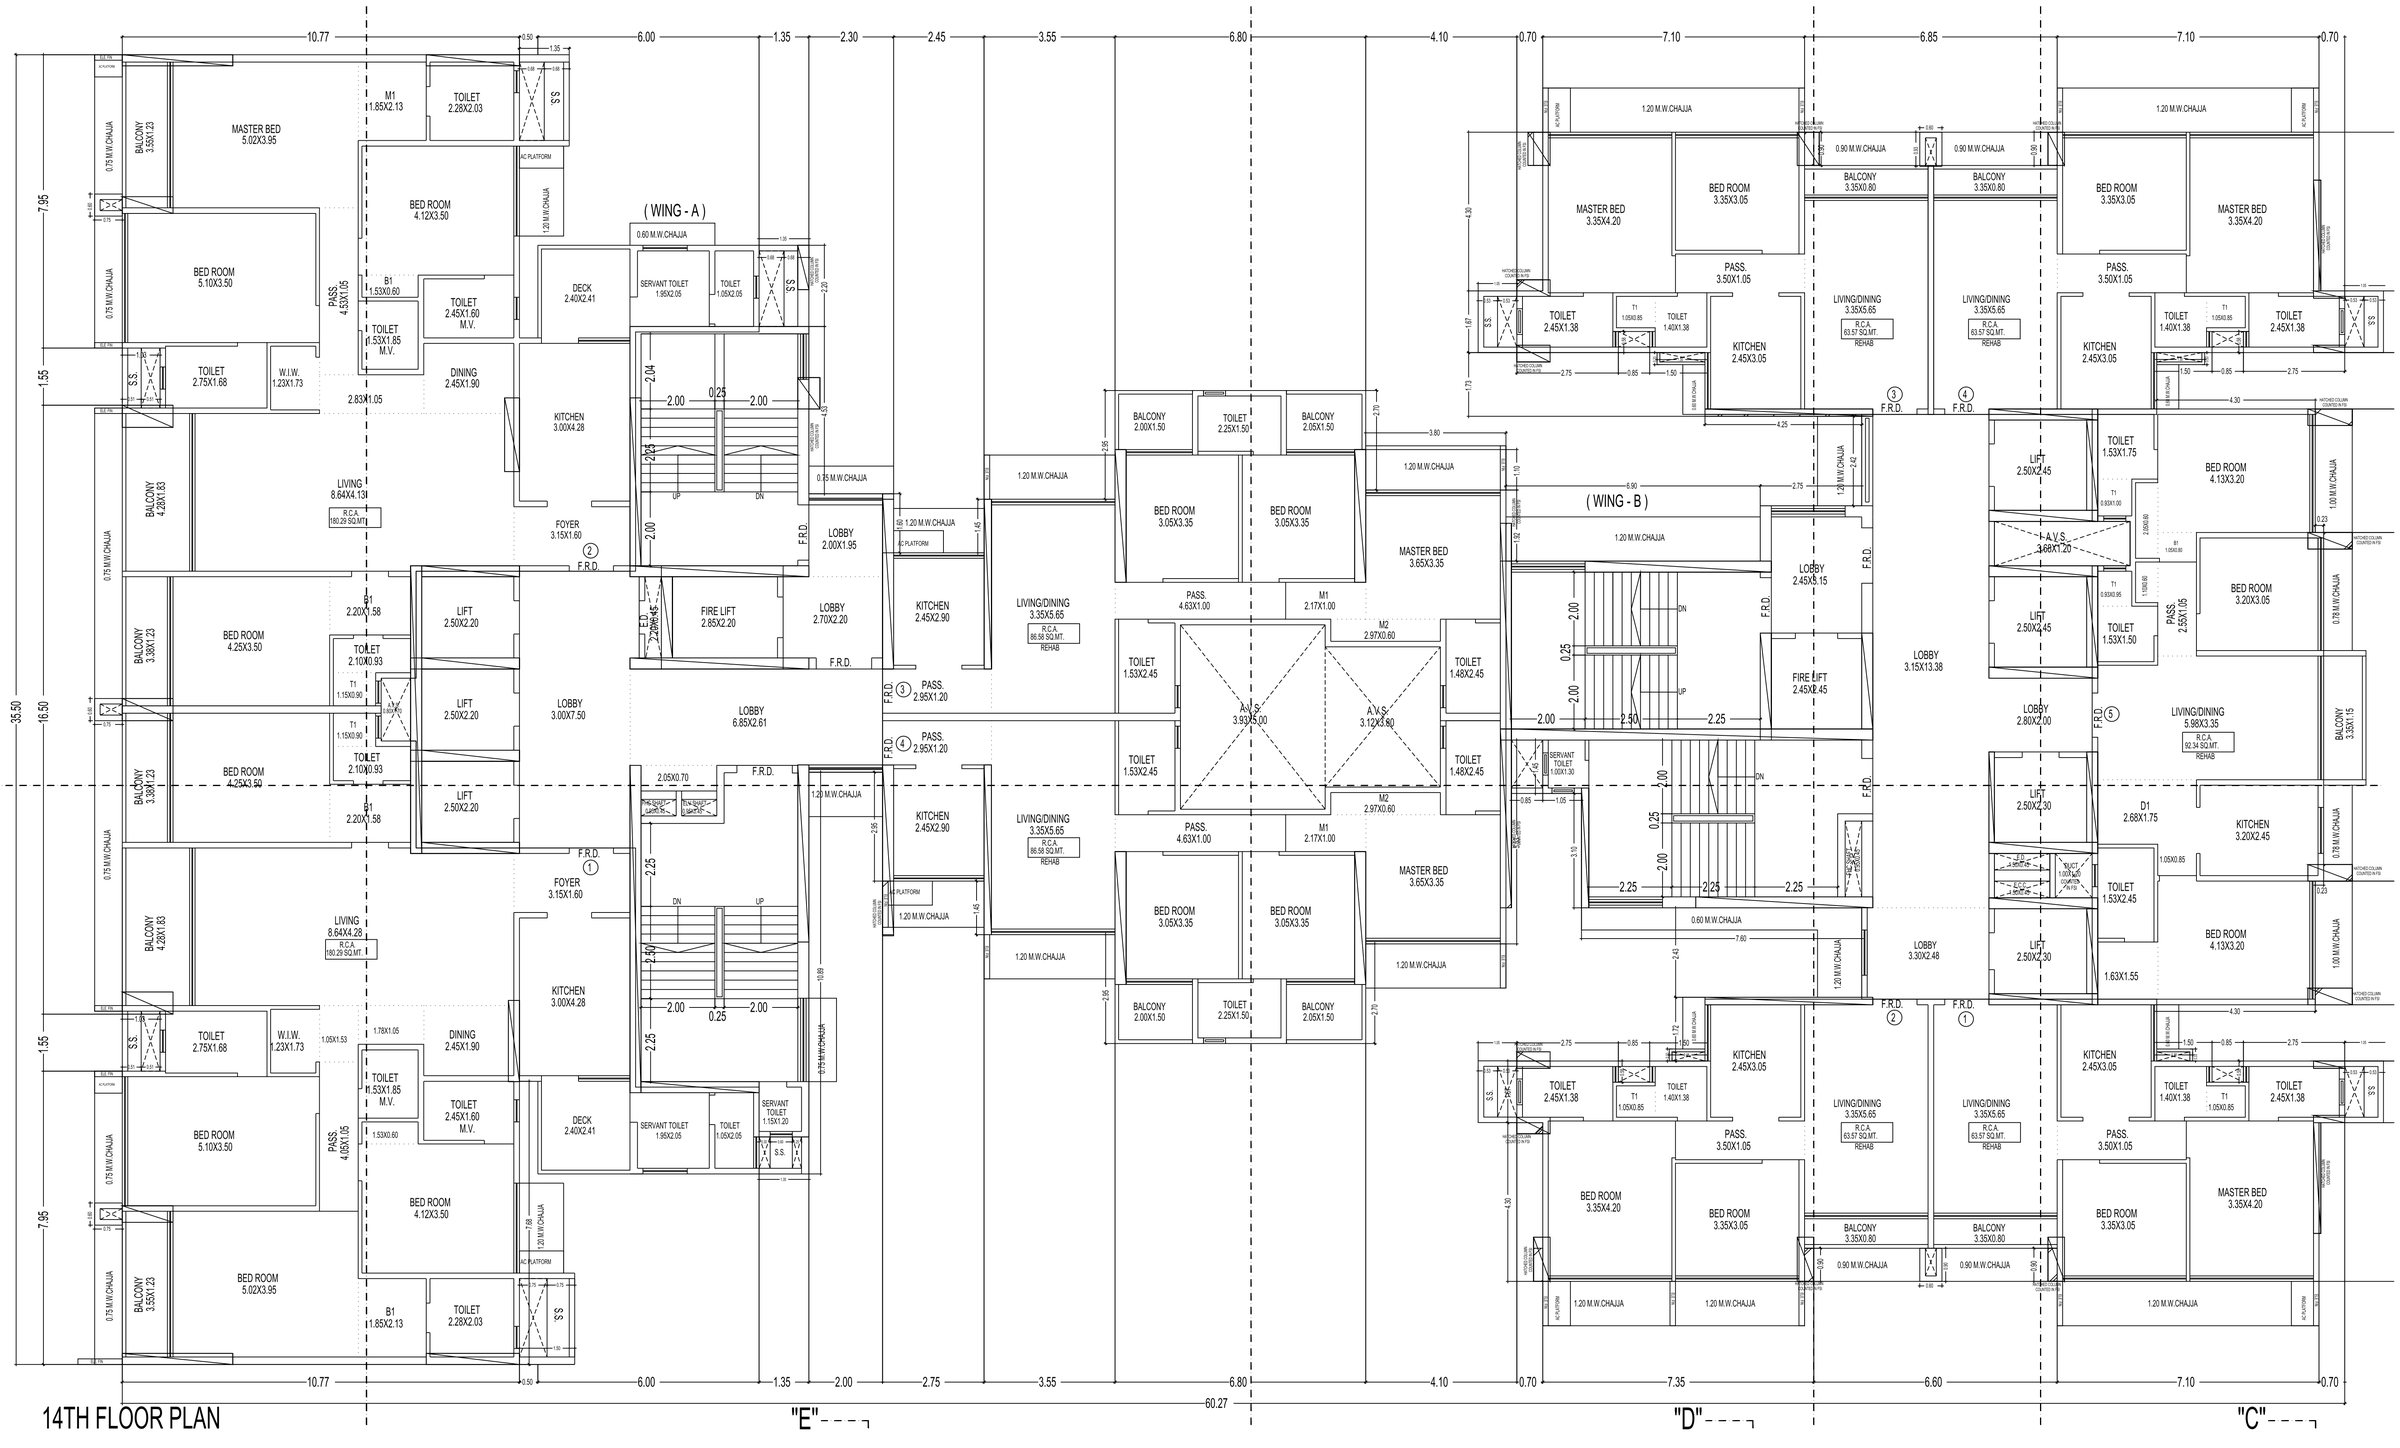
10.77
6.00
1.35
2.30
2.45
3.55
6.80
4.10
0.70
7.10
6.85
7.10
0.70
35.50
16.50
7.95
1.55
1.55
7.95
"A"
( WING - A )
( WING - B )
MASTER BED 5.02X3.95
BED ROOM 5.10X3.50
BED ROOM 4.25X3.50
BED ROOM 4.12X3.50
BED ROOM 5.02X3.95
BALCONY 3.35X1.23
BALCONY 4.28X1.83
BALCONY 3.38X1.23
BALCONY 3.35X1.23
BALCONY 4.28X1.83
BALCONY 3.38X1.23
BALCONY 3.35X1.23
M1 1.85X2.13
B1 1.53X0.60
B1 2.20X1.58
B1 1.85X2.13
TOILET 2.28X2.03
TOILET 1.53X1.85 M.V.
TOILET 2.45X1.60 M.V.
TOILET 2.10X0.93
TOILET 2.10X0.93
TOILET 2.75X1.68
TOILET 2.28X2.03
W.I.W. 1.23X1.73
PASS. 4.53X1.05
PASS. 4.05X1.05
2.83X1.05
1.78X1.05
1.05X1.53
DINING 2.45X1.90
KITCHEN 3.00X4.28
FOYER 3.15X1.60
LIVING 8.64X4.13
R.C.A. 180.29 SQ.MT.
DECK 2.40X2.41
SERVANT TOILET 1.95X2.05
TOILET 1.05X2.05
SERVANT TOILET 1.15X1.20
LOBBY 2.00X1.95
LOBBY 2.70X2.20
LOBBY 3.00X7.50
LOBBY 6.85X2.61
FIRE LIFT 2.85X2.20
LIFT 2.50X2.20
LIFT 2.50X2.20
KITCHEN 2.45X2.90
LIVING/DINING 3.35X5.65
R.C.A. 86.56 SQ.MT. REHAB
PASS. 2.95X1.20
PASS. 2.95X1.20
E.D. 2.20X6.45
2.05X0.70
0.60 M.W.CHAJJA
0.75 M.W.CHAJJA
1.20 M.W.CHAJJA
0.18 M.W.CHAJJA
AC PLATFORM
F.R.D.
UP
DN
2.00
0.25
2.25
2.65
BALCONY 2.00X1.50
BALCONY 2.05X1.50
TOILET 2.25X1.50
BED ROOM 3.05X3.35
BED ROOM 3.05X3.35
MASTER BED 3.65X3.35
PASS. 4.63X1.00
M1 2.17X1.00
M2 2.97X0.60
TOILET 1.53X2.45
TOILET 1.48X2.45
A.V.S. 3.93X5.00
A.V.S. 3.12X3.80
BALCONY 3.35X0.80
0.90 M.W.CHAJJA
BED ROOM 3.35X3.05
MASTER BED 3.35X4.20
PASS. 3.50X1.05
TOILET 2.45X1.38
TOILET 1.40X1.38
T1 1.05X0.85
KITCHEN 2.45X3.05
LIVING/DINING 3.35X5.65
R.C.A. 63.57 SQ.MT. REHAB
LOBBY 2.45X3.15
LOBBY 3.15X13.38
FIRE LIFT 2.45X2.45
SERVANT TOILET 1.00X1.30
LOBBY 2.80X2.00
LOBBY 3.30X2.48
LIFT 2.50X2.45
LIFT 2.50X2.30
TOILET 1.53X1.75
TOILET 1.53X1.50
BED ROOM 4.13X3.20
BED ROOM 3.20X3.05
A.V.S. 3.60X1.20
PASS. 2.55X1.05
LIVING/DINING 5.98X3.35
R.C.A. 92.34 SQ.MT. REHAB
BALCONY 3.35X1.15
D1 2.68X1.75
KITCHEN 3.20X2.45
1.63X1.55
1.00 M.W.CHAJJA
0.78 M.W.CHAJJA
1.05X0.85
2.80X0.80
1.50
0.85
2.75
4.30
0.23
1.15
1.72
1.87
1.73
1.30
1.10
1.45
2.43
2.71
2.70
3.80
4.25
6.90
7.60
10.77
6.00
1.35
2.00
2.75
3.55
6.80
4.10
0.70
7.35
6.60
7.10
0.70
60.27
14TH FLOOR PLAN
"E"
"D"
"C"

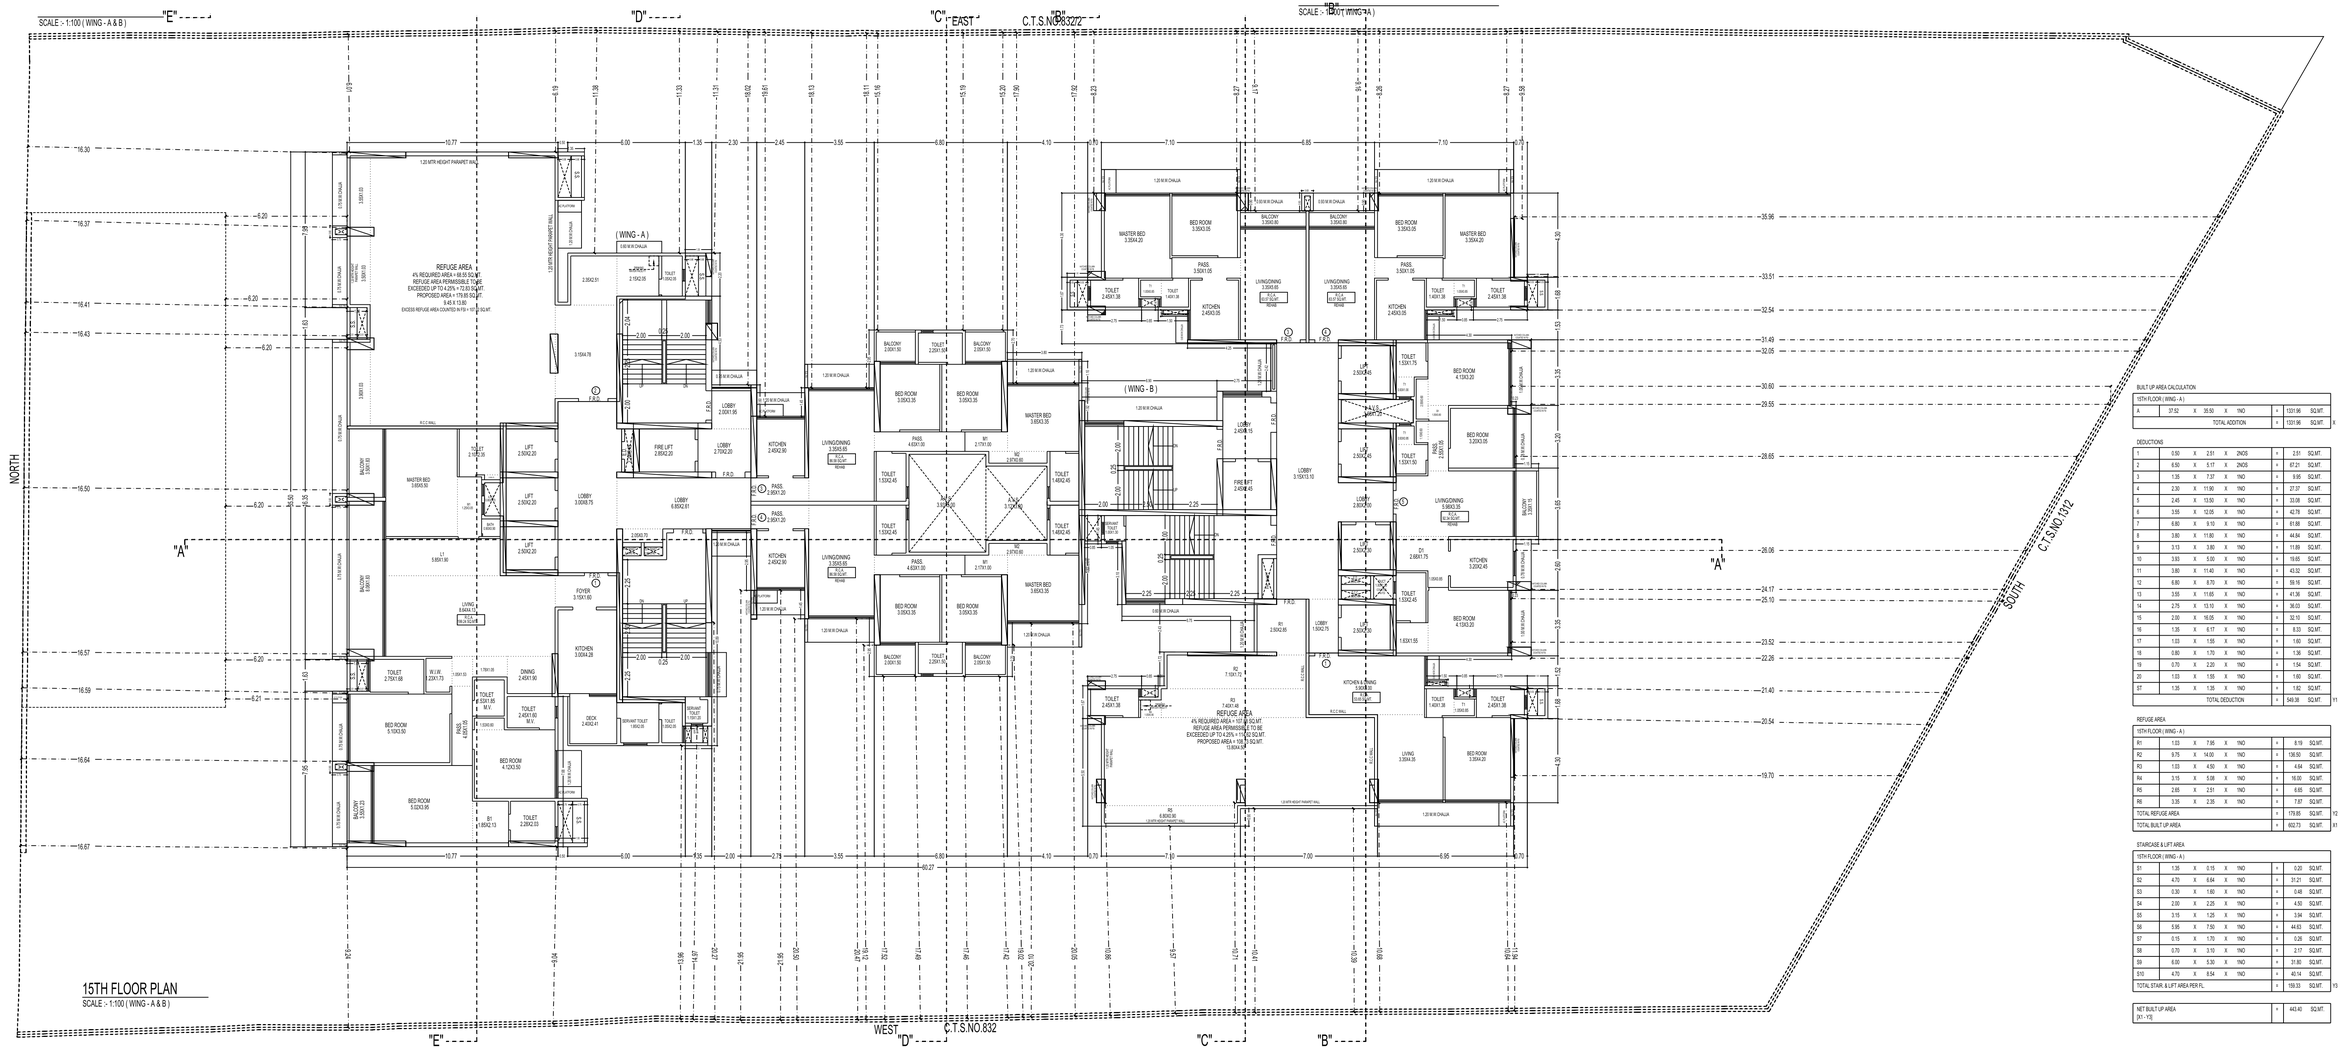


## 15TH FLOOR PLAN

SCALE - 1:100 ( WING - A & B )

BUILT UP AREA CALCULATION

15TH FLOOR ( WING - A )

| | | | | | | | |
|---|---|---|---|---|---|---|---|
| A | 37.62 | X | 26.50 | X | 1NO | = | 1331.96 SQ.MT. |
| | | | | | TOTAL ADDITION | = | 1331.96 SQ.MT. X |

DEDUCTIONS

| | | | | | | | |
|---|---|---|---|---|---|---|---|
| 1 | 0.50 | X | 2.01 | X | 2NOS | = | 2.01 SQ.MT. |
| 2 | 6.50 | X | 5.17 | X | 2NOS | = | 67.21 SQ.MT. |
| 3 | 1.35 | X | 7.37 | X | 1NO | = | 9.95 SQ.MT. |
| 4 | 2.30 | X | 11.90 | X | 1NO | = | 27.37 SQ.MT. |
| 5 | 2.45 | X | 13.50 | X | 1NO | = | 33.08 SQ.MT. |
| 6 | 3.55 | X | 12.05 | X | 1NO | = | 42.78 SQ.MT. |
| 7 | 6.80 | X | 9.10 | X | 1NO | = | 61.88 SQ.MT. |
| 8 | 3.80 | X | 11.80 | X | 1NO | = | 44.84 SQ.MT. |
| 9 | 3.13 | X | 3.80 | X | 1NO | = | 11.89 SQ.MT. |
| 10 | 3.63 | X | 5.20 | X | 1NO | = | 18.65 SQ.MT. |
| 11 | 3.80 | X | 11.40 | X | 1NO | = | 43.32 SQ.MT. |
| 12 | 6.80 | X | 8.70 | X | 1NO | = | 59.16 SQ.MT. |
| 13 | 3.55 | X | 11.65 | X | 1NO | = | 41.36 SQ.MT. |
| 14 | 2.75 | X | 13.10 | X | 1NO | = | 36.03 SQ.MT. |
| 15 | 2.00 | X | 16.05 | X | 1NO | = | 32.10 SQ.MT. |
| 16 | 1.35 | X | 6.17 | X | 1NO | = | 8.33 SQ.MT. |
| 17 | 1.03 | X | 1.55 | X | 1NO | = | 1.60 SQ.MT. |
| 18 | 0.80 | X | 1.70 | X | 1NO | = | 1.36 SQ.MT. |
| 19 | 0.70 | X | 2.20 | X | 1NO | = | 1.54 SQ.MT. |
| 20 | 1.03 | X | 1.55 | X | 1NO | = | 1.60 SQ.MT. |
| ST | 1.35 | X | 1.35 | X | 1NO | = | 1.82 SQ.MT. |
| | | | | | TOTAL DEDUCTION | = | 549.38 SQ.MT. 11 |

REFUGE AREA

15TH FLOOR ( WING - A )

| | | | | | | | |
|---|---|---|---|---|---|---|---|
| R1 | 1.03 | X | 7.95 | X | 1NO | = | 8.19 SQ.MT. |
| R2 | 9.75 | X | 14.00 | X | 1NO | = | 136.50 SQ.MT. |
| R3 | 1.03 | X | 4.50 | X | 1NO | = | 4.64 SQ.MT. |
| R4 | 3.15 | X | 5.08 | X | 1NO | = | 16.00 SQ.MT. |
| R5 | 2.85 | X | 2.51 | X | 1NO | = | 6.65 SQ.MT. |
| R6 | 3.35 | X | 2.35 | X | 1NO | = | 7.87 SQ.MT. |
| TOTAL REFUGE AREA | | | | | | = | 179.85 SQ.MT. Y2 |
| TOTAL BUILT UP AREA | | | | | | = | 602.73 SQ.MT. X1 |

STAIRCASE & LIFT AREA

15TH FLOOR ( WING - A )


| | | | | | | | |
|---|---|---|---|---|---|---|---|
| S1 | 1.35 | X | 0.15 | X | 1NO | = | 0.20 SQ.MT. |
| S2 | 4.70 | X | 6.64 | X | 1NO | = | 31.21 SQ.MT. |
| S3 | 0.30 | X | 1.60 | X | 1NO | = | 0.48 SQ.MT. |
| S4 | 2.00 | X | 2.25 | X | 1NO | = | 4.50 SQ.MT. |
| S5 | 3.15 | X | 1.25 | X | 1NO | = | 3.94 SQ.MT. |
| S6 | 5.95 | X | 7.50 | X | 1NO | = | 44.63 SQ.MT. |
| S7 | 0.15 | X | 1.70 | X | 1NO | = | 0.26 SQ.MT. |
| S8 | 0.70 | X | 3.10 | X | 1NO | = | 2.17 SQ.MT. |
| S9 | 6.00 | X | 5.30 | X | 1NO | = | 31.80 SQ.MT. |
| S10 | 4.70 | X | 8.54 | X | 1NO | = | 40.14 SQ.MT. |
| TOTAL STAIR. & LIFT AREA PER FL. | | | | | | = | 159.33 S3 |

| | | |
|---|---|---|
| NET BUILT UP AREA (X1 - Y2) | = | 443.40 SQ.MT. |

FILE NO. - P-24461/2024/(832/1)/K/W WARd/AMBIVALI | 11/16

CONTENTS OF SHEET :-


16TH FLOOR PLAN & AREA DIAGRAMS

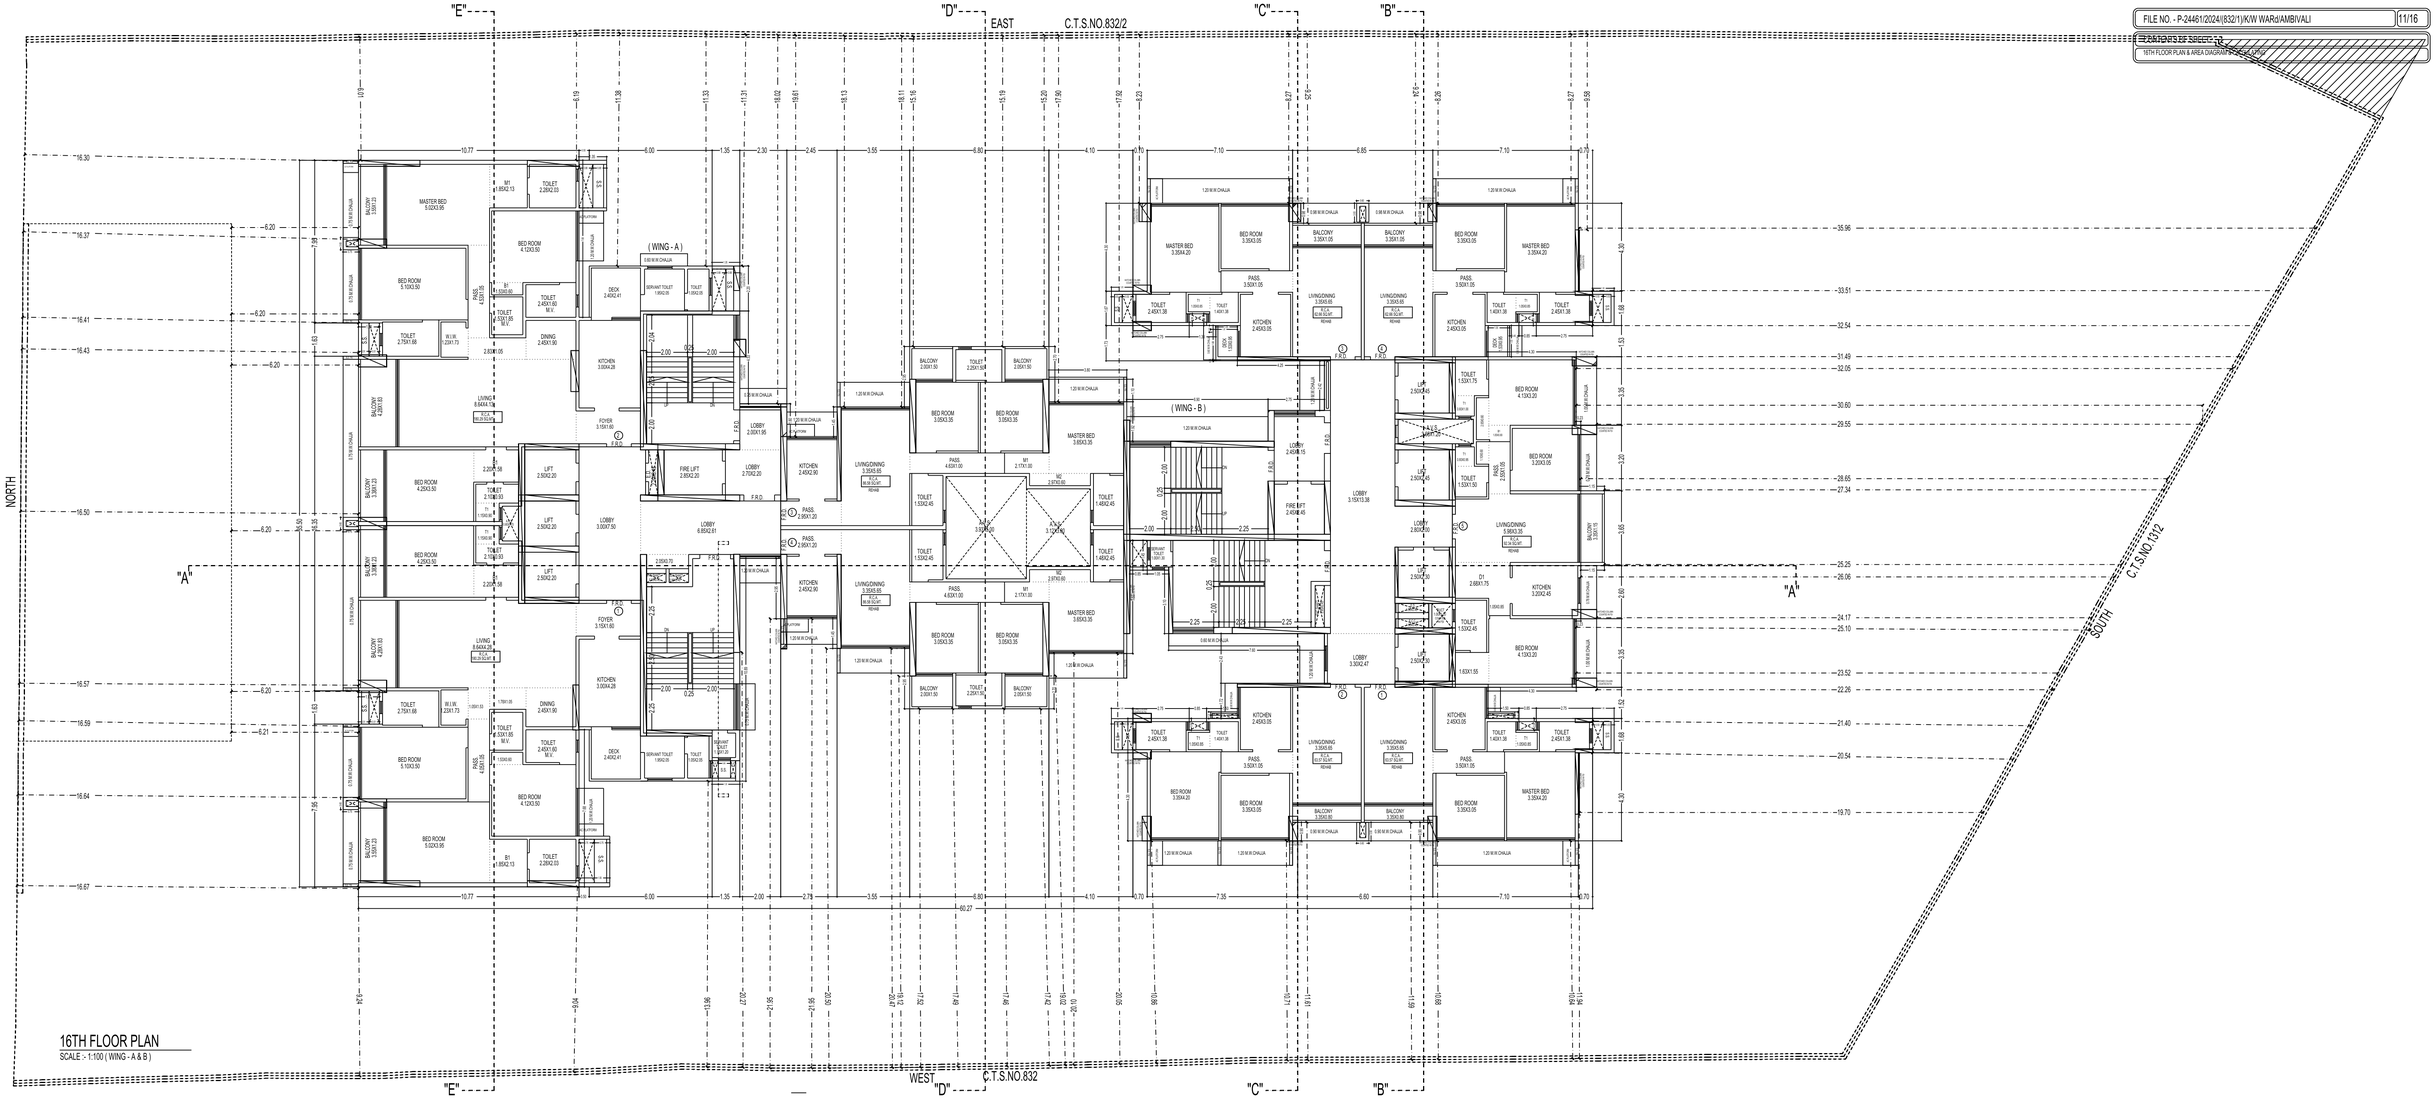


FILE NO. - P-24461/2024/(832/1)/KW WARD/AMBIVALI | 12/16

SHEET NO. OF SHEETS

17TH FLOOR PLAN & AREA DIAGRAM

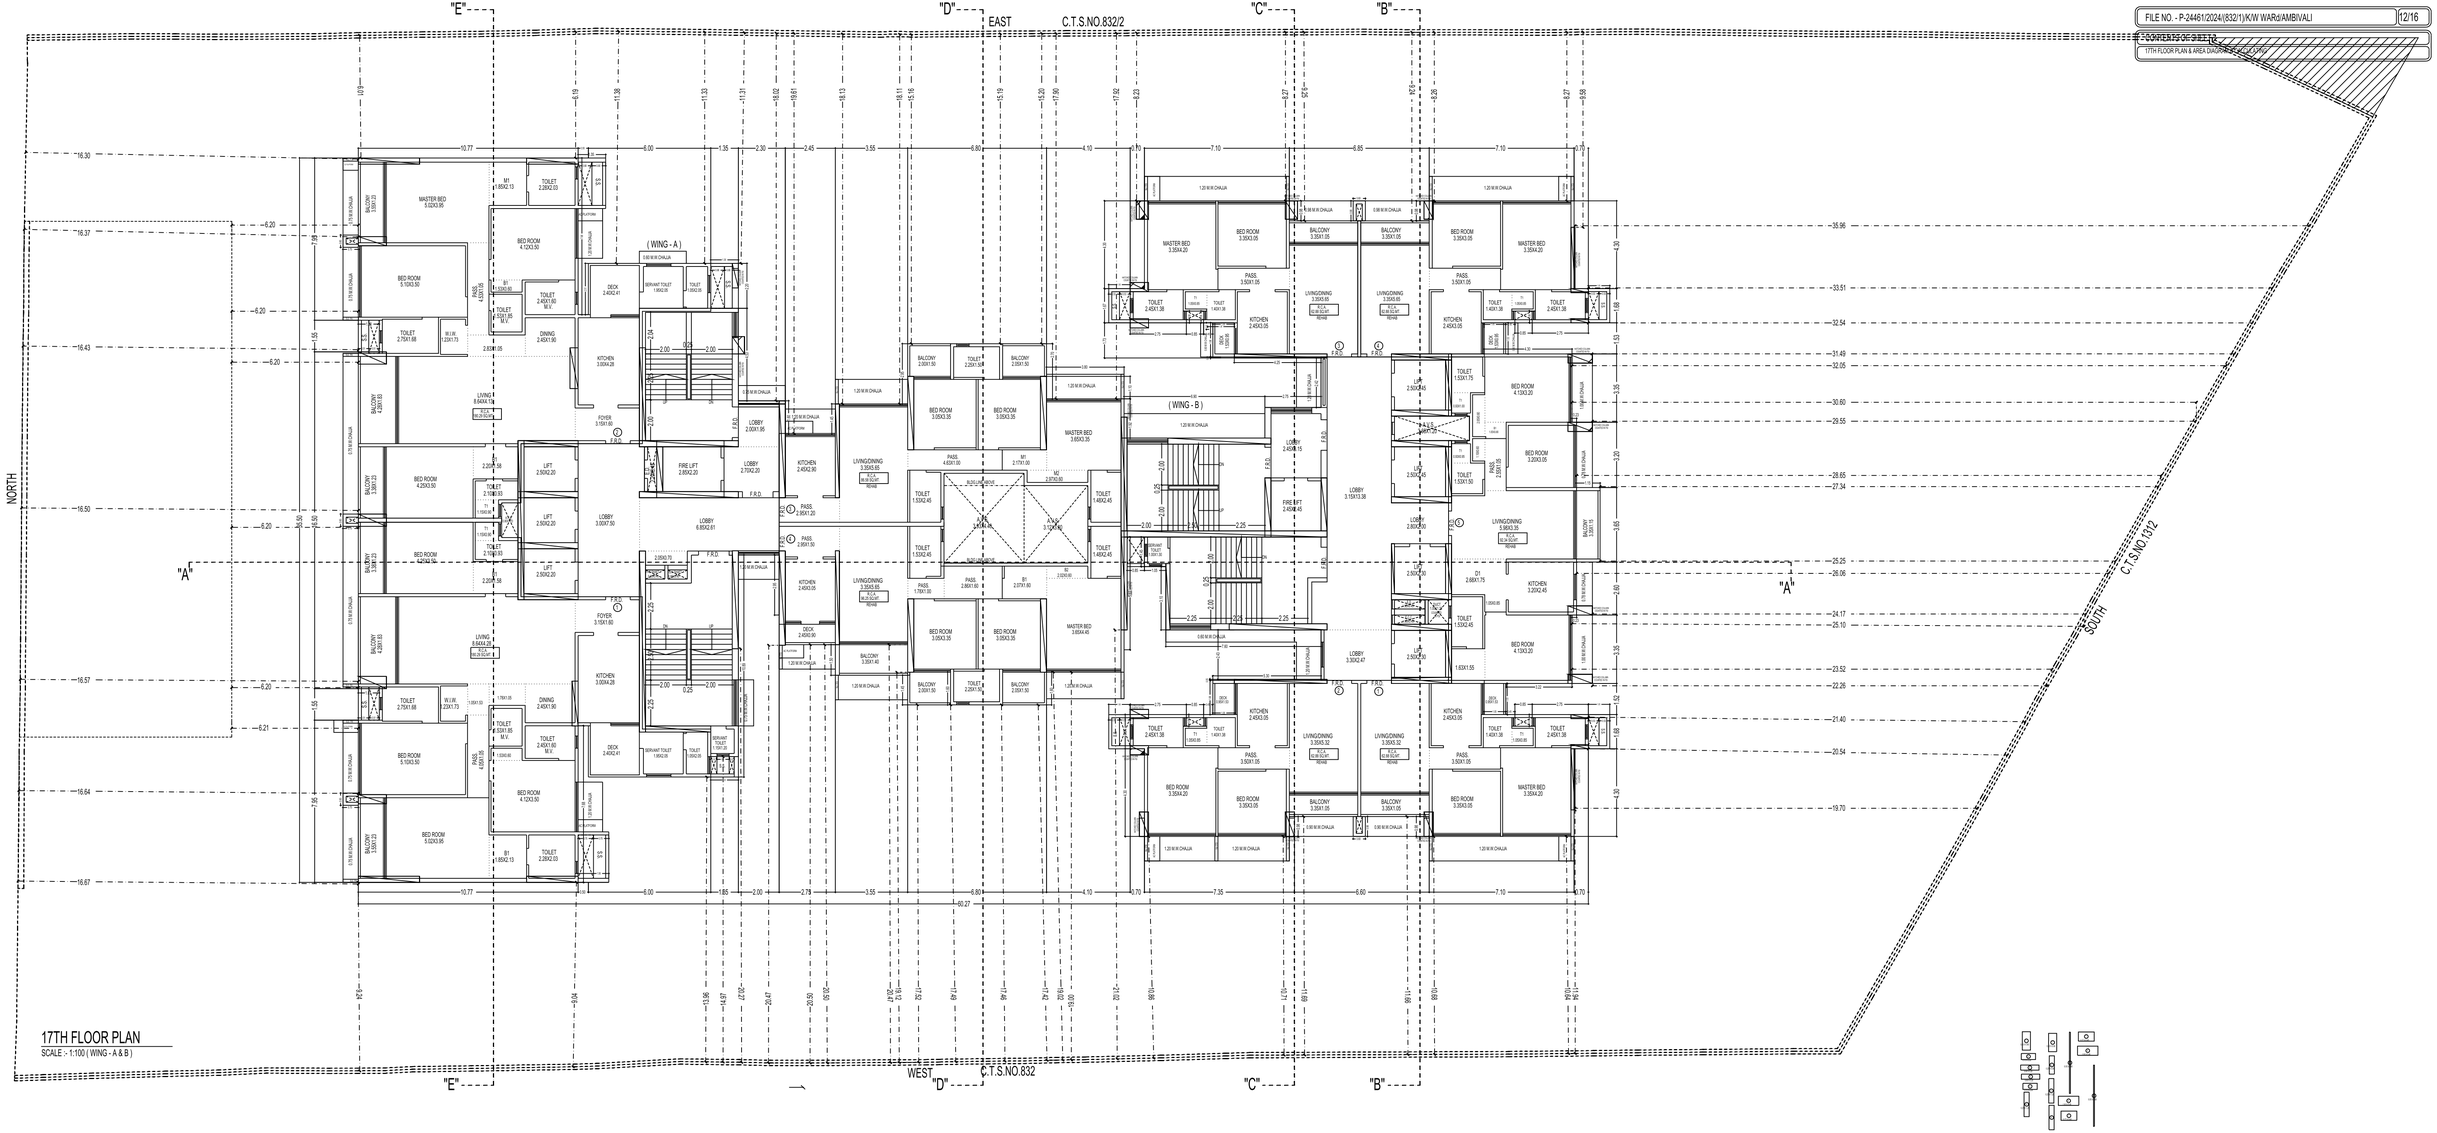

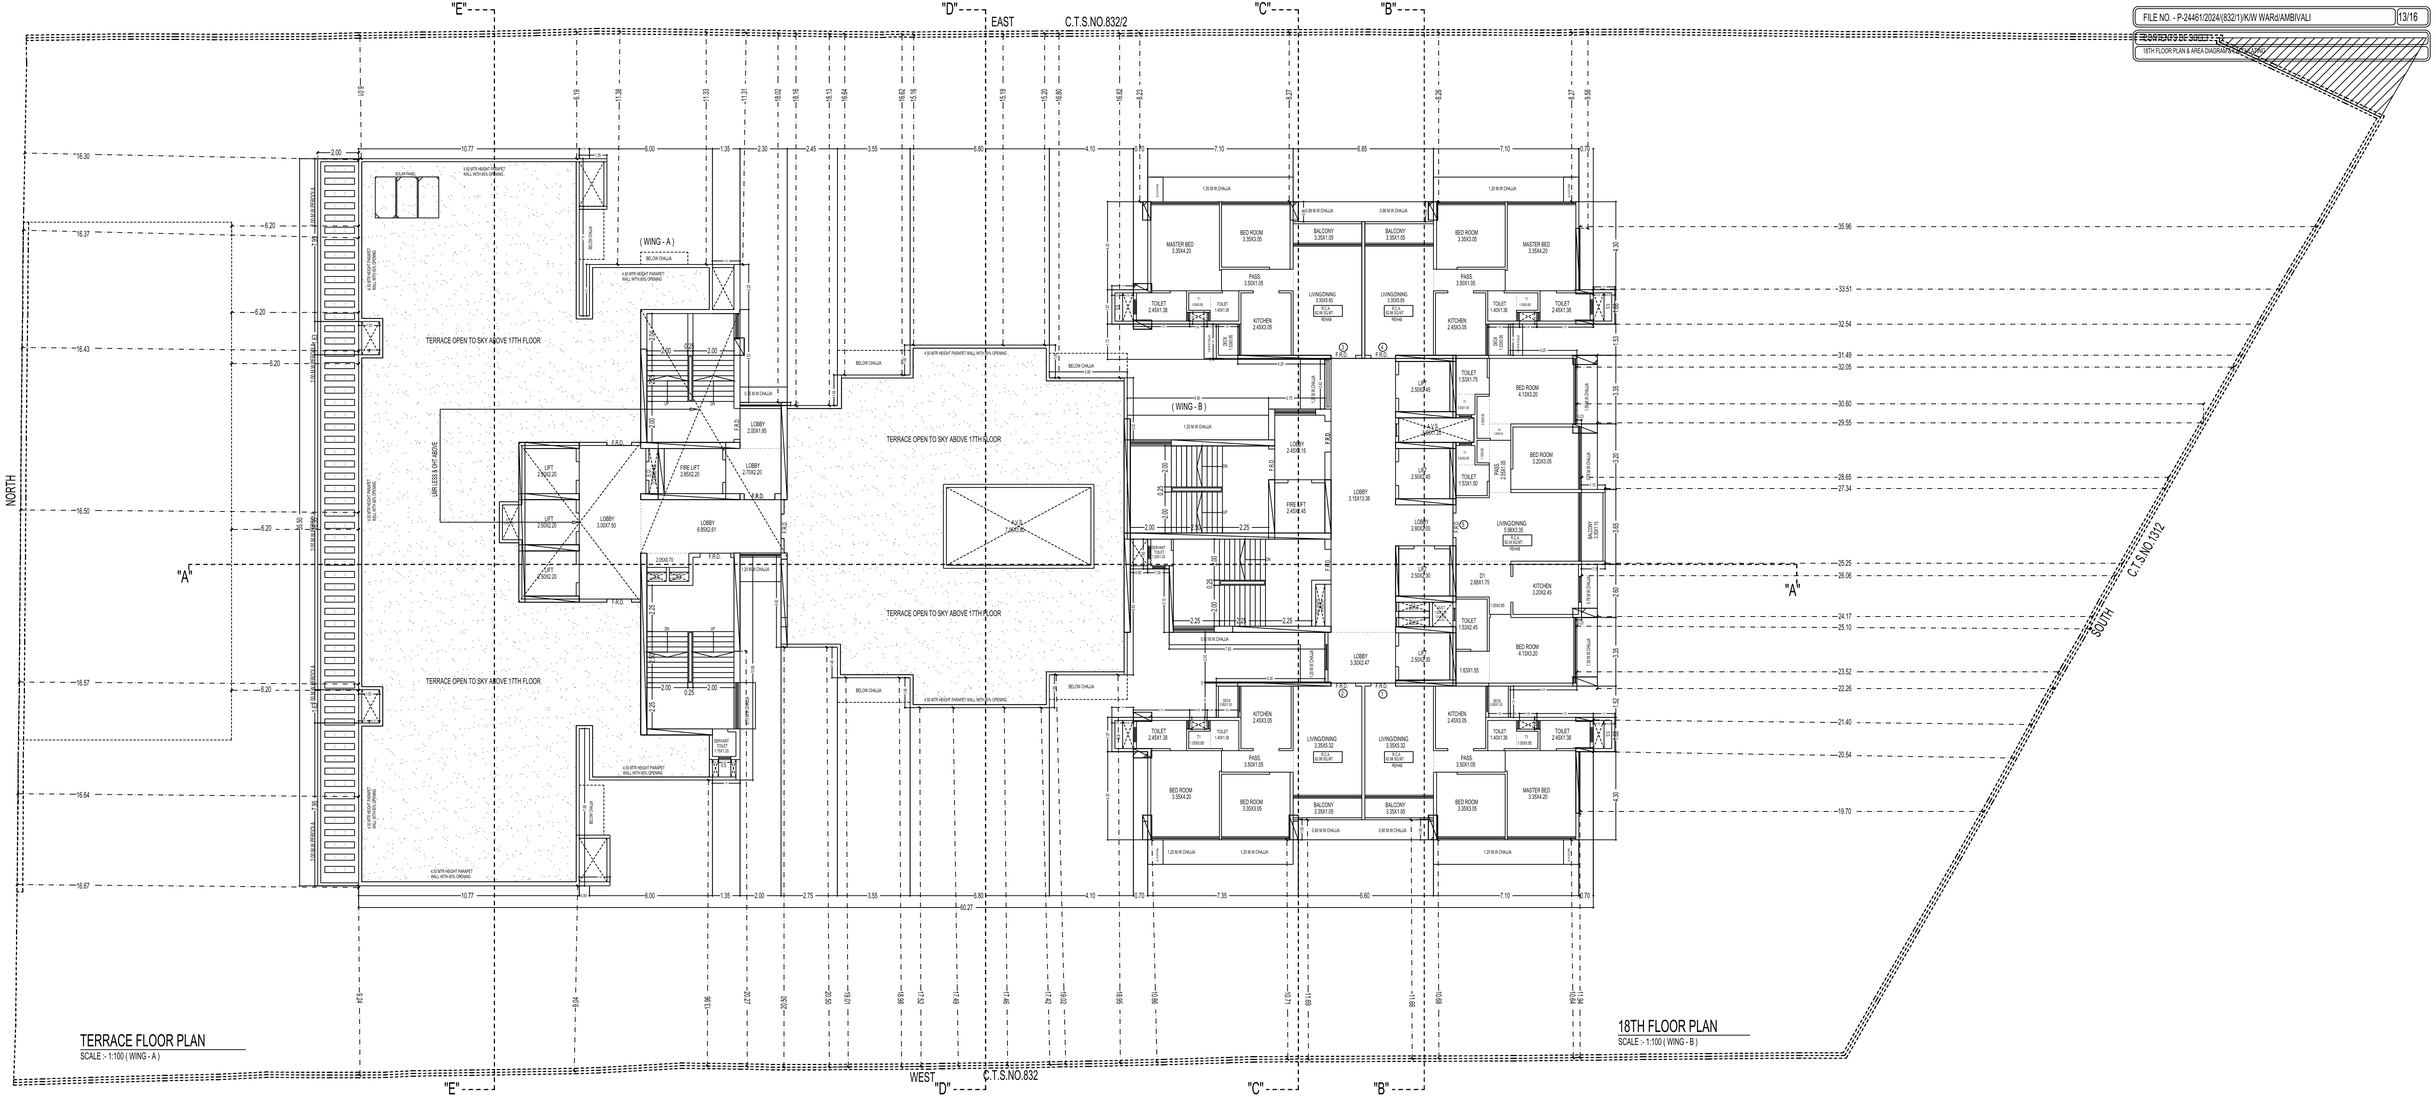



## TERRACE FLOOR PLAN

SCALE :- 1:100 ( WING - A )

## 18TH FLOOR PLAN

SCALE :- 1:100 ( WING - B )

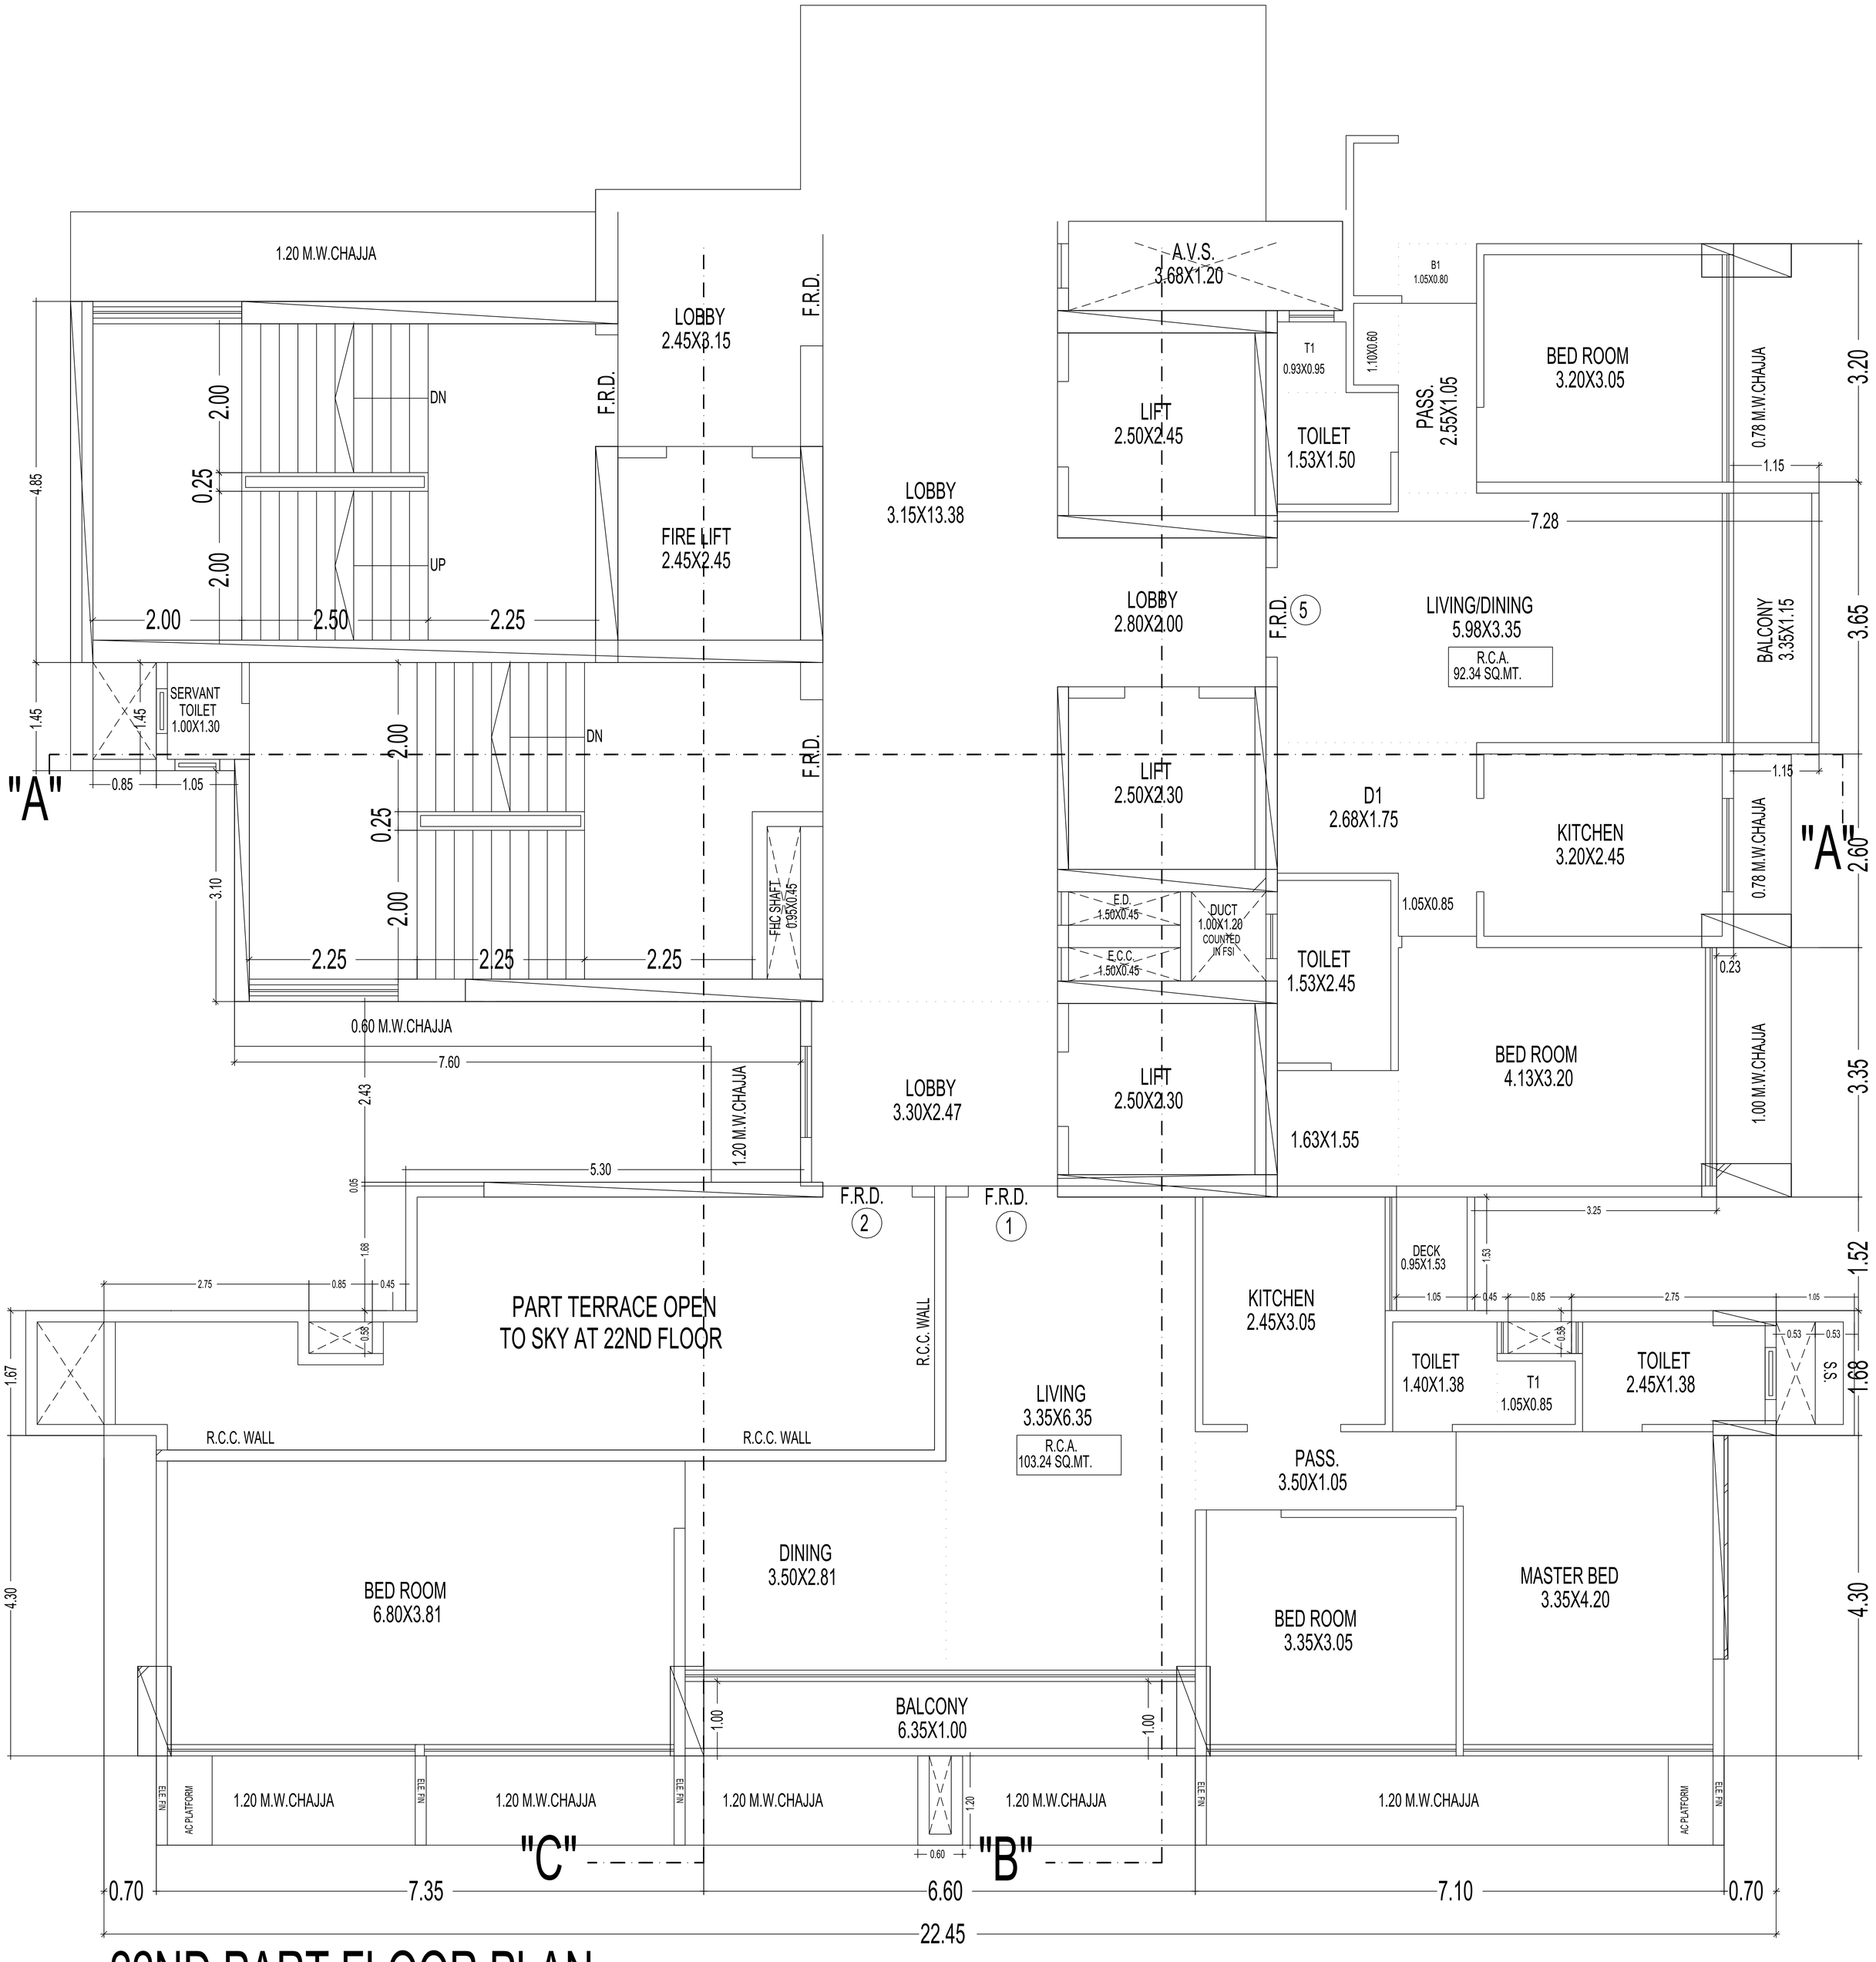


# 22ND PART FLOOR PLAN

SCALE :- 1:100 ( WING - B )

FILE NO. - P-24461/2024/(832/1)/K/W WARSI/AMBIVALI | 14/16

CONTENTS OF SHEET :-
19TH TO 21ST FLOOR & TERRACE FLOOR PLAN WITH CALCULATION

NORTH | SOUTH | EAST | WEST

C.T.S.NO.832/2 | C.T.S.NO.1312 | C.T.S.NO.832

"A" "B" "C" "D" "E"

( WING - B )

TERRACE BELOW

PART TERRACE BELOW

PART TERRACE OPEN TO SKY AT 22ND FLOOR

RCC Wall

TERRACE OPEN TO SKY ABOVE 22ND FLOOR

LWR LESS & CHT ABOVE

BELOW CHAJJA

## 19TH TO 21ST FLOOR PLAN
SCALE :- 1:100 ( WING - B )

## TERRACE FLOOR PLAN
SCALE :- 1:100 ( WING - B )

### COLUMN AREA DIAGRAM
SCALE :- 1:100 ( 19TH TO 22ND FLOOR WING - B )

19TH TO 22ND FLOOR COLUMN AREA CALCULATION ( WING – B )

| | | | | | | | |
|---|---|---|---|---|---|---|---|
| 1 | 0.40 | X | 0.90 | X | 1NO | = | 0.36 SQ.MT. |
| 2 | 0.70 | X | 0.30 | X | 2NOS | = | 0.42 SQ.MT. |
| 3 | 0.90 | X | 0.25 | X | 2NOS | = | 0.45 SQ.MT. |
| 4 | 0.25 | X | 1.20 | X | 1NO | = | 0.30 SQ.MT. |
| 5 | 0.05 | X | 3.00 | X | 2NOS | = | 0.30 SQ.MT. |
| 6 | 1.00 | X | 0.45 | X | 2NOS | = | 0.90 SQ.MT. |
| 7 | 0.78 | X | 0.45 | X | 2NOS | = | 0.70 SQ.MT. |
| | | | TOTAL ADDITION | | | = | 3.43 SQ.MT. X |

BUILT UP AREA CALCULATION

19TH TO 21ST FLOOR ( WING - B )

| | | | | | | | |
|---|---|---|---|---|---|---|---|
| A | 23.33 | X | 31.15 | X | 1NO | = | 726.73 SQ.MT. |
| | | | TOTAL ADDITION | | | = | 726.73 SQ.MT. X |

DEDUCTIONS

| | | | | | | | |
|---|---|---|---|---|---|---|---|
| 1 | 1.00 | X | 4.30 | X | 2NOS | = | 8.60 SQ.MT. |
| 2 | 1.28 | X | 4.30 | X | 2NOS | = | 11.01 SQ.MT. |
| 3 | 0.58 | X | 1.68 | X | 2NOS | = | 1.95 SQ.MT. |
| 4 | 0.85 | X | 0.58 | X | 4NOS | = | 1.97 SQ.MT. |
| 5 | 4.63 | X | 1.53 | X | 1NO | = | 7.08 SQ.MT. |
| 6 | 1.38 | X | 3.35 | X | 2NOS | = | 9.25 SQ.MT. |
| 7 | 1.15 | X | 2.60 | X | 1NO | = | 3.68 SQ.MT. |
| 8 | 1.15 | X | 2.60 | X | 1NO | = | 2.99 SQ.MT. |
| 9 | 4.63 | X | 1.53 | X | 1NO | = | 7.08 SQ.MT. |
| 10 | 0.30 | X | 1.68 | X | 2NOS | = | 1.01 SQ.MT. |

BUILT UP AREA CALCULATION

22ND FLOOR ( WING - B )

| | | | | | | | |
|---|---|---|---|---|---|---|---|
| A | 23.33 | X | 31.15 | X | 1NO | = | 726.73 SQ.MT. |
| | | | TOTAL ADDITION | | | = | 726.73 SQ.MT. X |

DEDUCTIONS

| | | | | | | | |
|---|---|---|---|---|---|---|---|
| 1 | 1.00 | X | 4.30 | X | 2NOS | = | 8.60 SQ.MT. |
| 2 | 1.28 | X | 4.30 | X | 2NOS | = | 11.01 SQ.MT. |
| 3 | 0.58 | X | 1.68 | X | 2NOS | = | 1.95 SQ.MT. |
| 4 | 0.85 | X | 0.58 | X | 4NOS | = | 1.97 SQ.MT. |
| 5 | 4.63 | X | 1.53 | X | 1NO | = | 7.08 SQ.MT. |
| 6 | 1.38 | X | 3.35 | X | 2NOS | = | 9.25 SQ.MT. |
| 7 | 1.15 | X | 3.20 | X | 1NO | = | 3.68 SQ.MT. |
| 8 | 1.15 | X | 2.60 | X | 1NO | = | 2.99 SQ.MT. |
| 9 | 4.63 | X | 1.53 | X | 1NO | = | 7.08 SQ.MT. |
| 10 | 0.30 | X | 1.68 | X | 2NOS | = | 1.01 SQ.MT. |
| 11 | 4.35 | X | 1.68 | X | 2NOS | = | 14.62 SQ.MT. |
| 12 | 0.40 | X | 2.47 | X | 1NO | = | 13.34 SQ.MT. |
| 13 | 4.25 | X | 2.42 | X | 1NO | = | 10.29 SQ.MT. |
| 14 | 2.05 | X | 3.10 | X | 1NO | = | 6.36 SQ.MT. |
| 15 | 1.00 | X | 1.45 | X | 1NO | = | 1.45 SQ.MT. |
| 16 | 1.50 | X | 1.20 | X | 1NO | = | 1.80 SQ.MT. |
| 17 | 3.68 | X | 1.20 | X | 1NO | = | 4.42 SQ.MT. |
| 18 | 6.90 | X | 1.50 | X | 1NO | = | 10.35 SQ.MT. |
| 19 | 4.25 | X | 2.42 | X | 1NO | = | 10.33 SQ.MT. |
| 20 | 5.40 | X | 2.48 | X | 1NO | = | 13.39 SQ.MT. |
| 21 | 1.25 | X | 1.45 | X | 1NO | = | 1.81 SQ.MT. |