
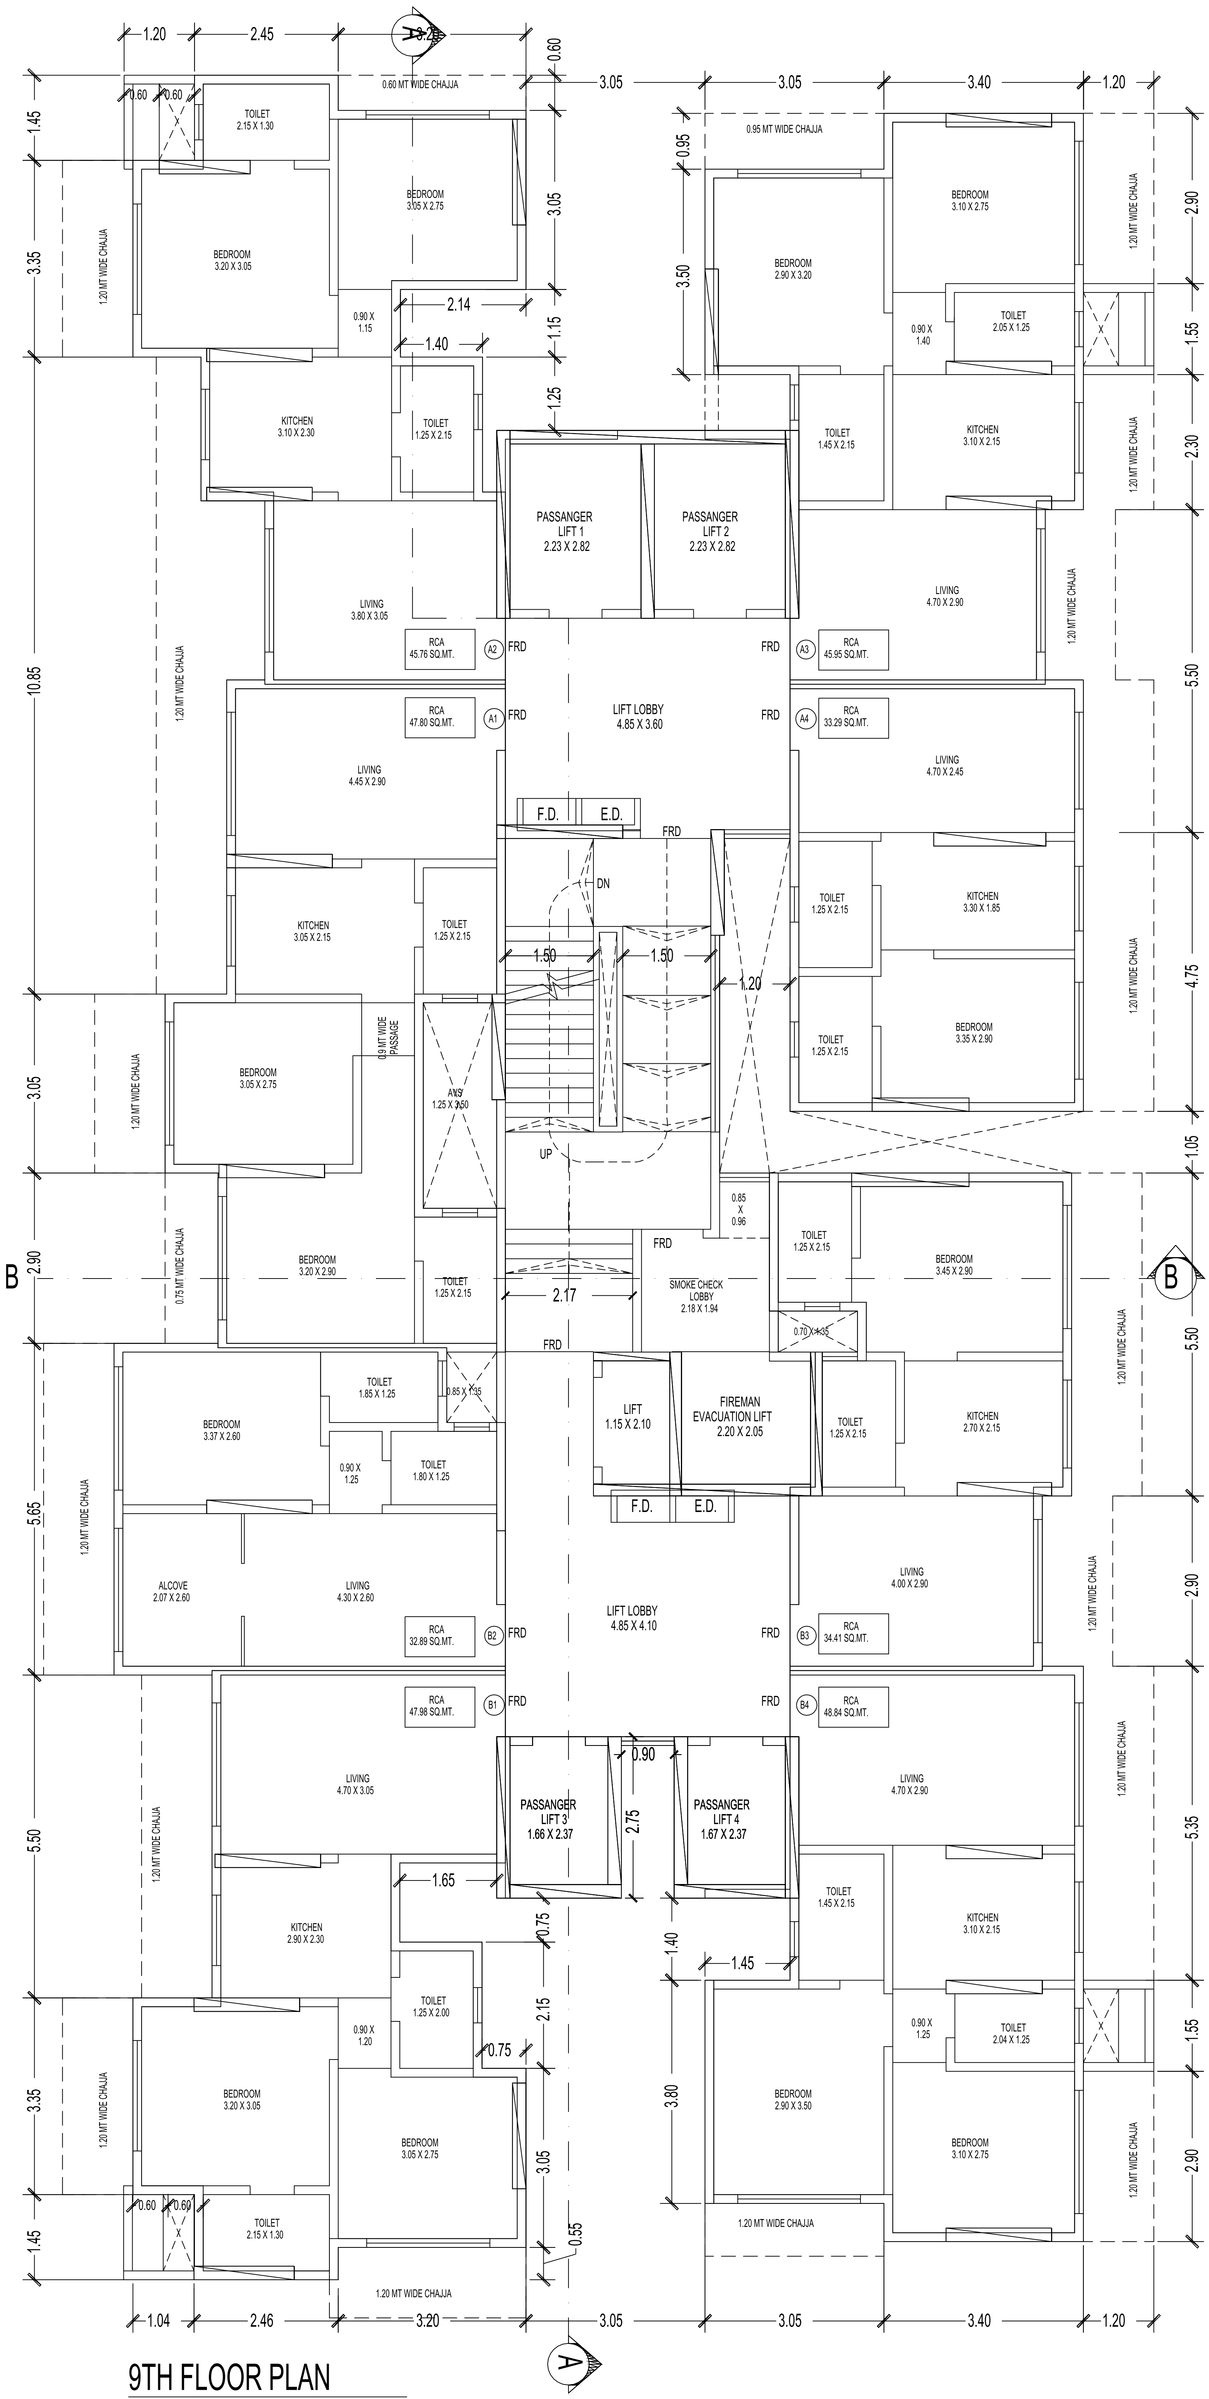



9TH FLOOR PLAN

SCALE 1:100

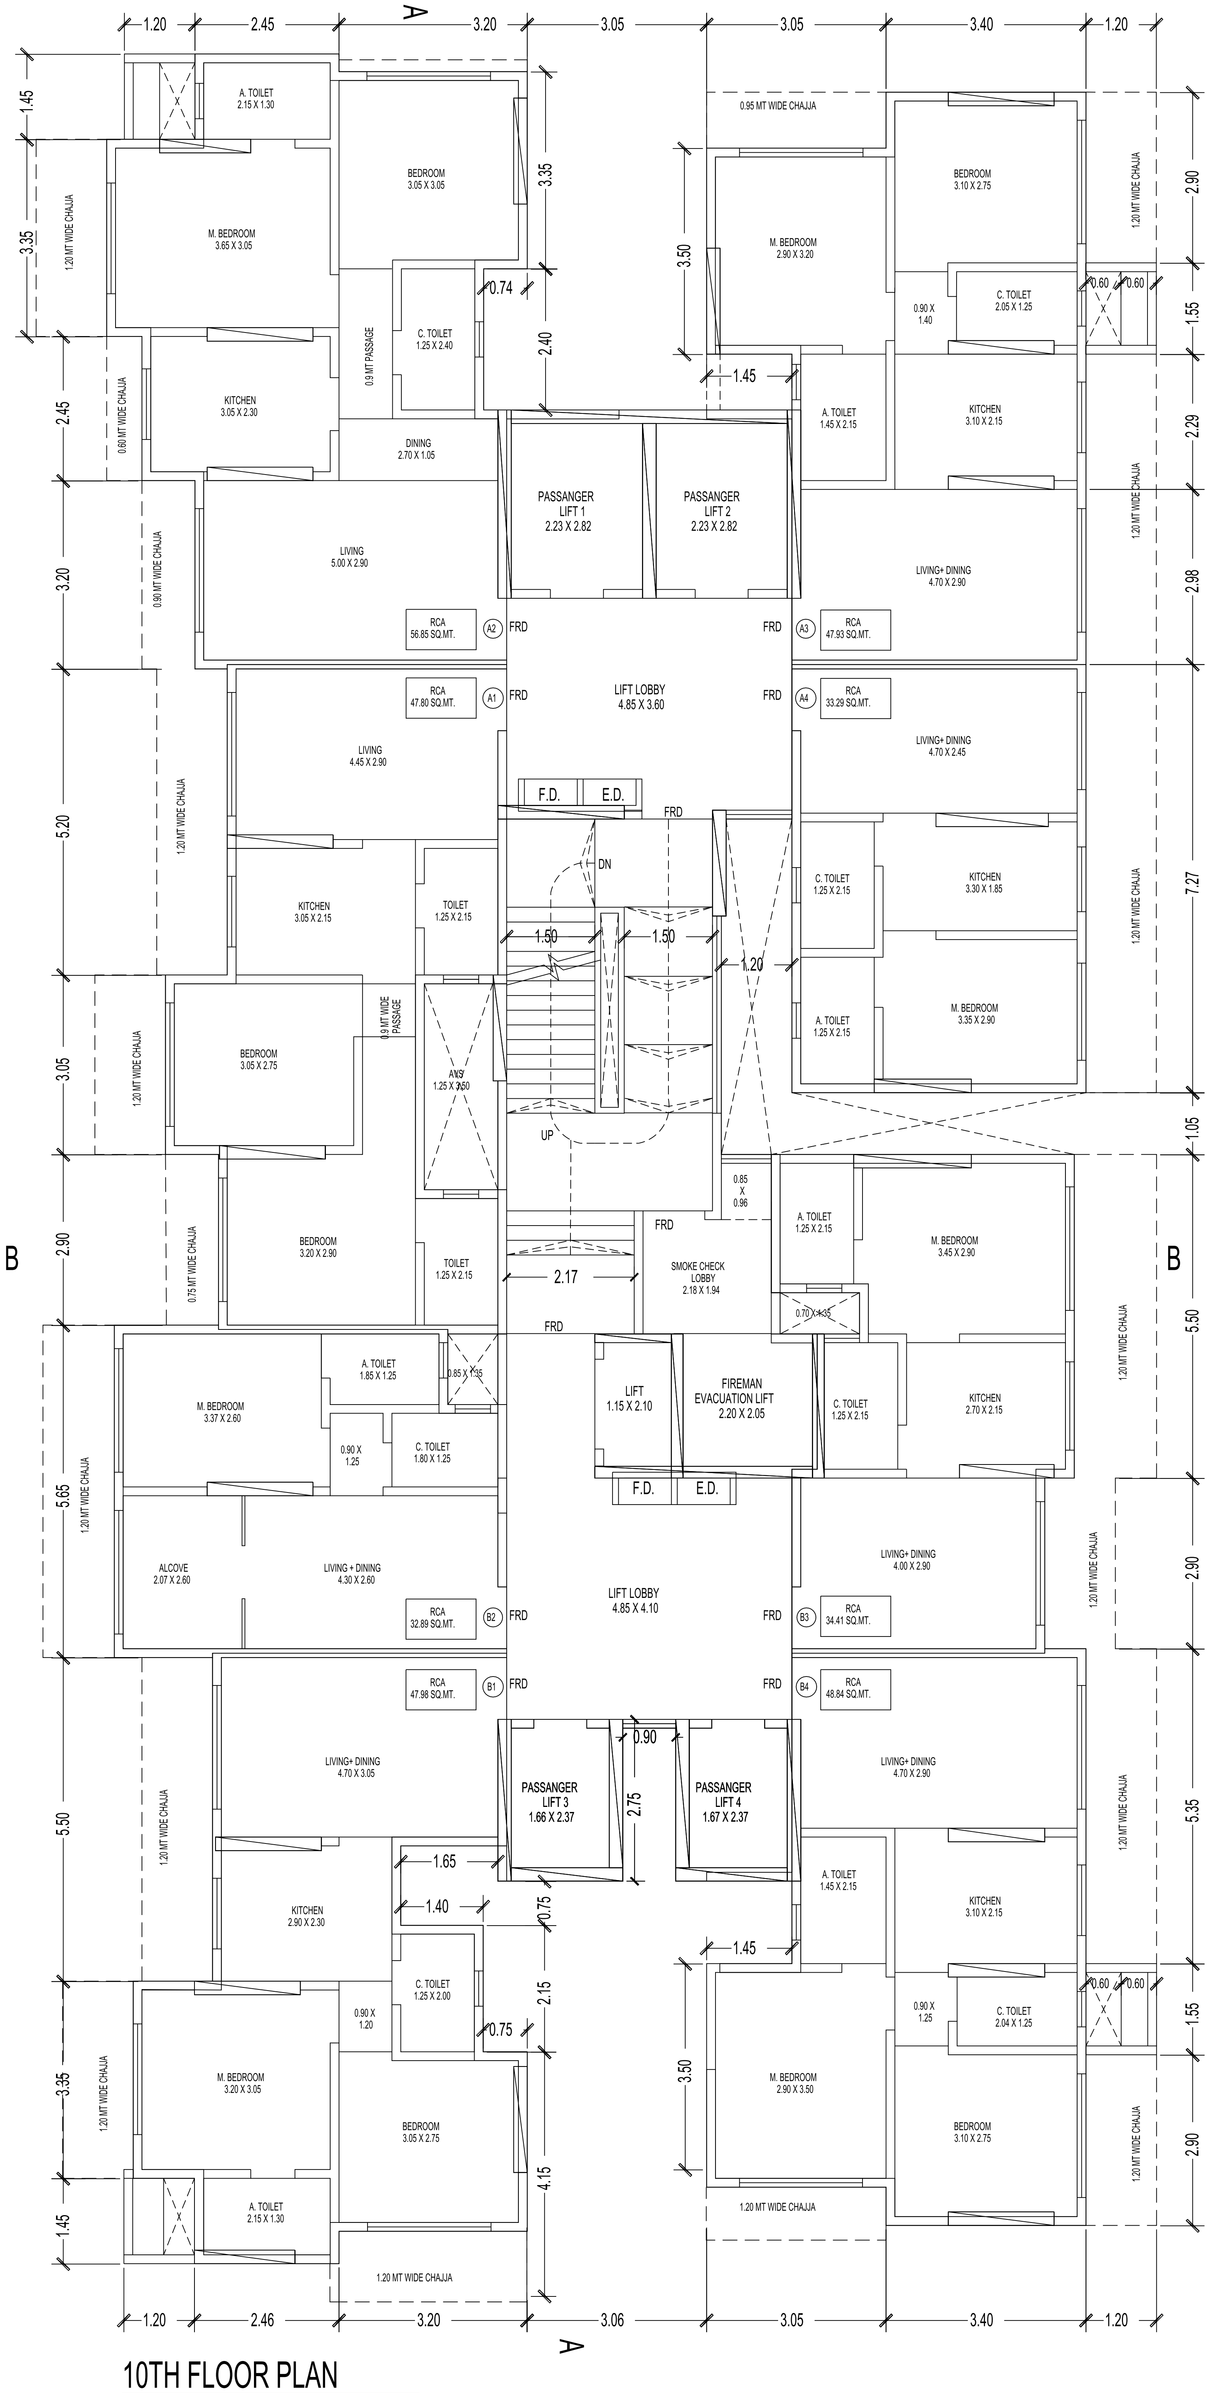


10TH FLOOR PLAN

SCALE 1:100

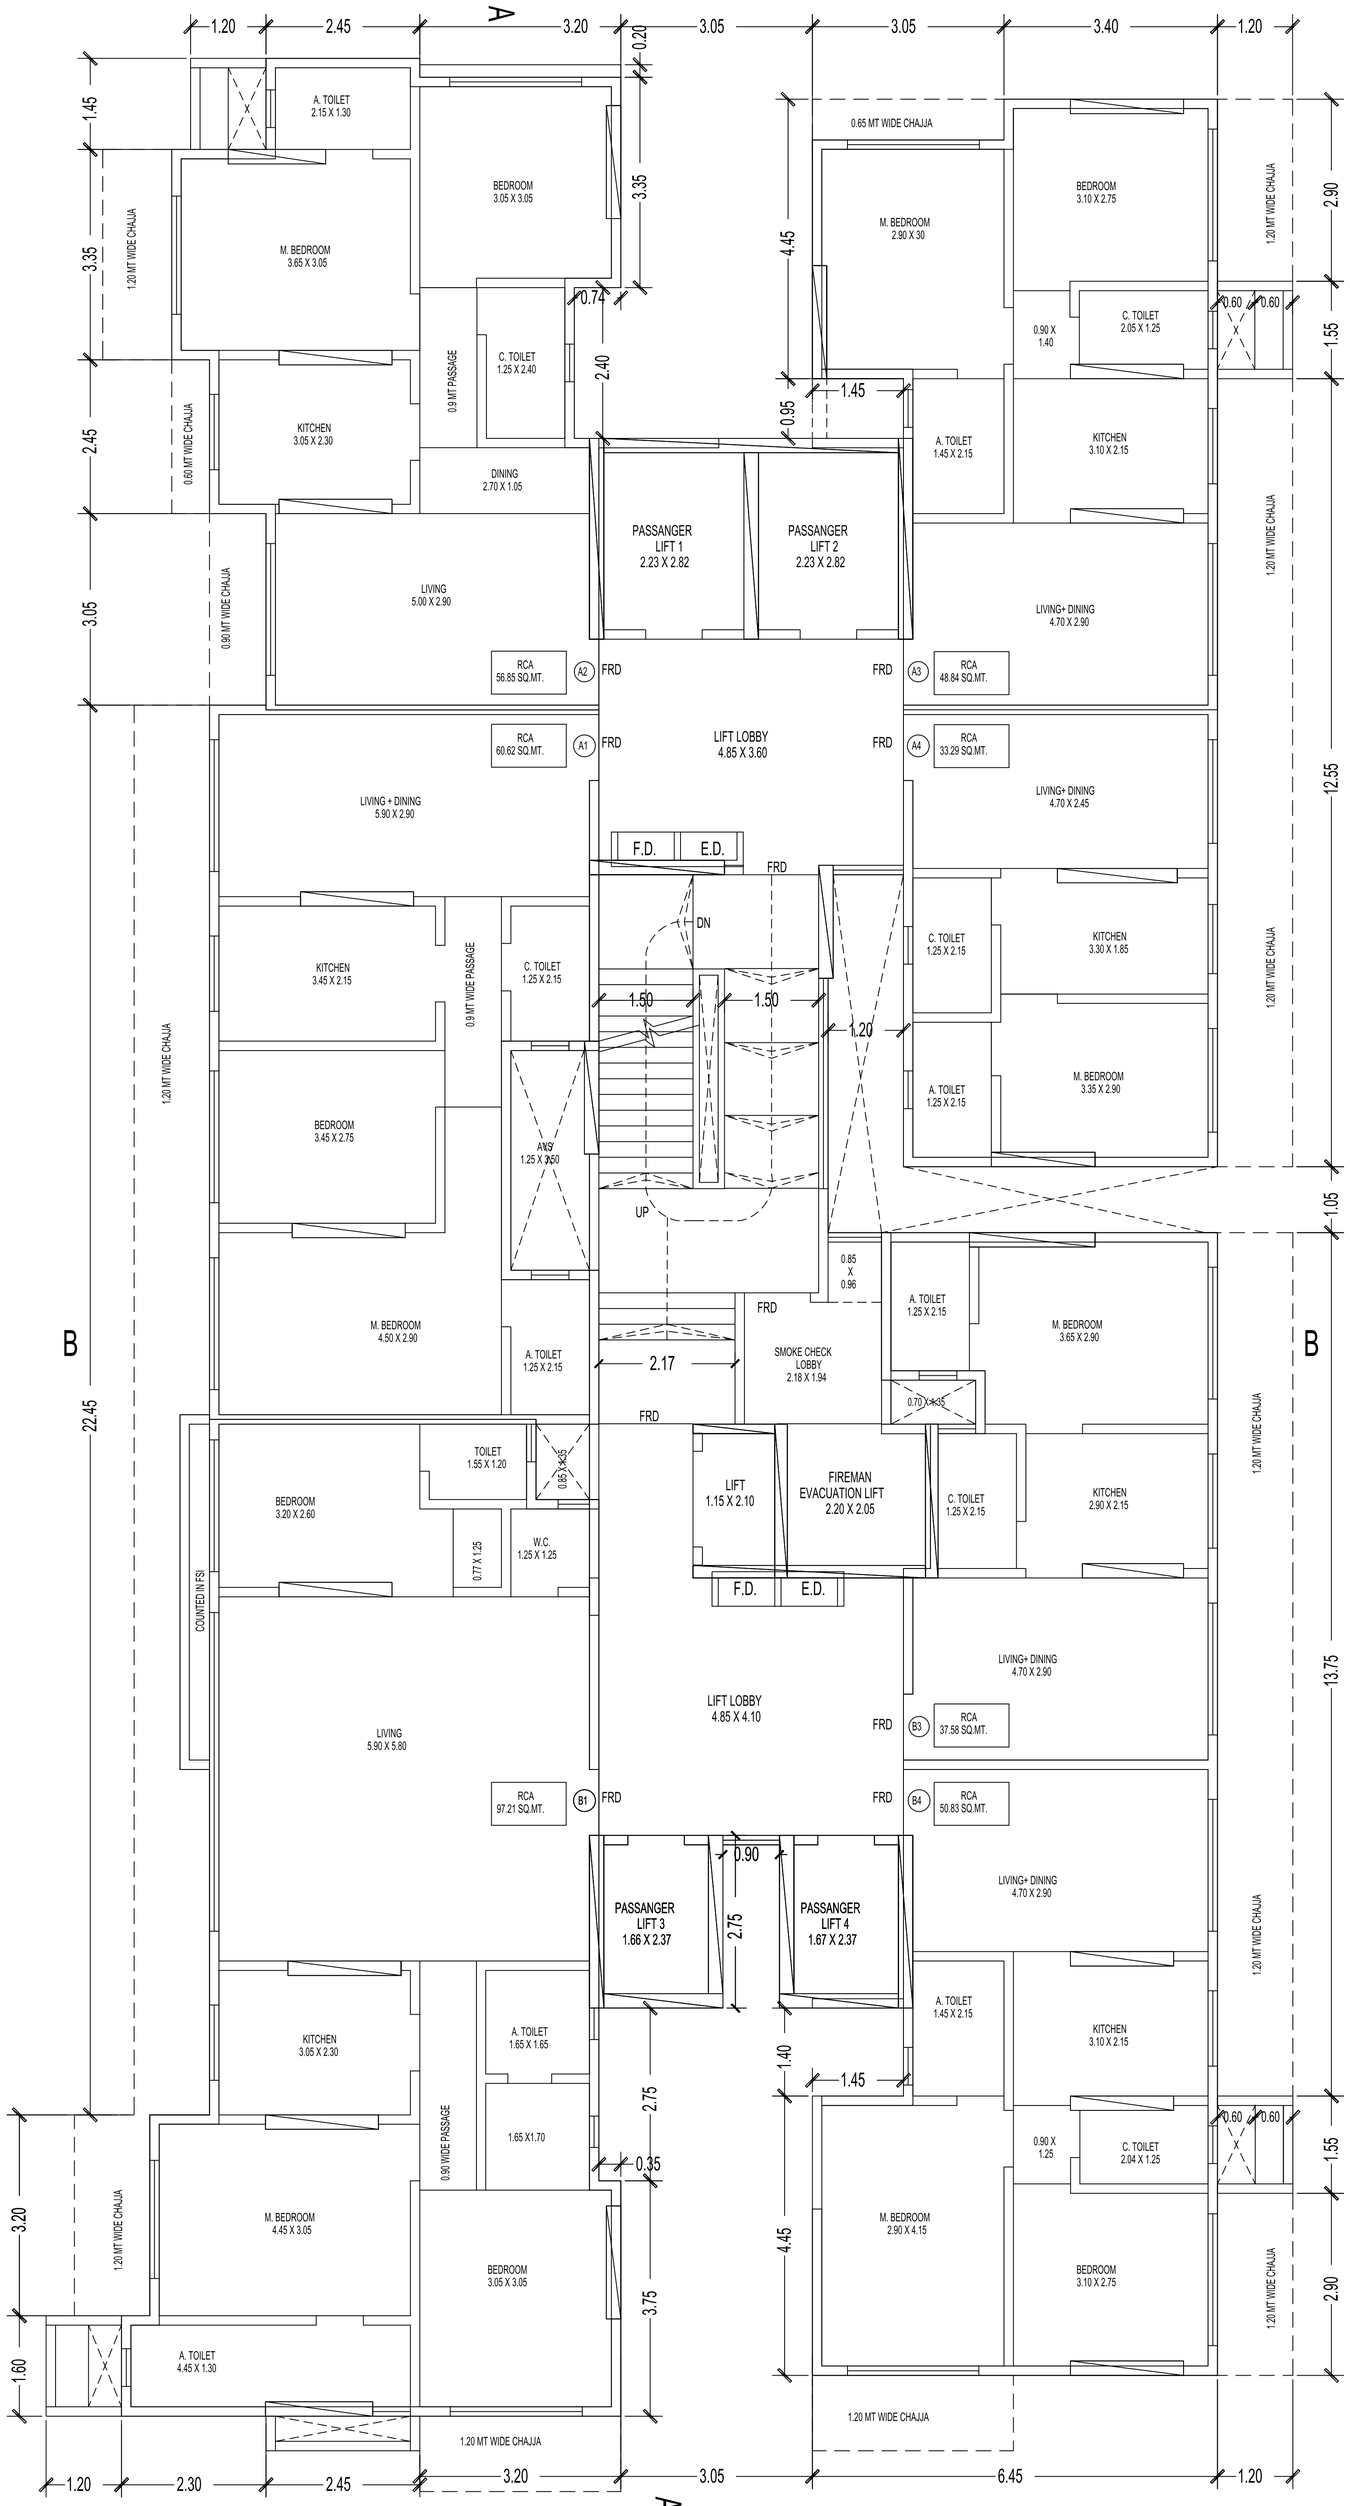


12TH FLOOR PLAN

SCALE 1:100

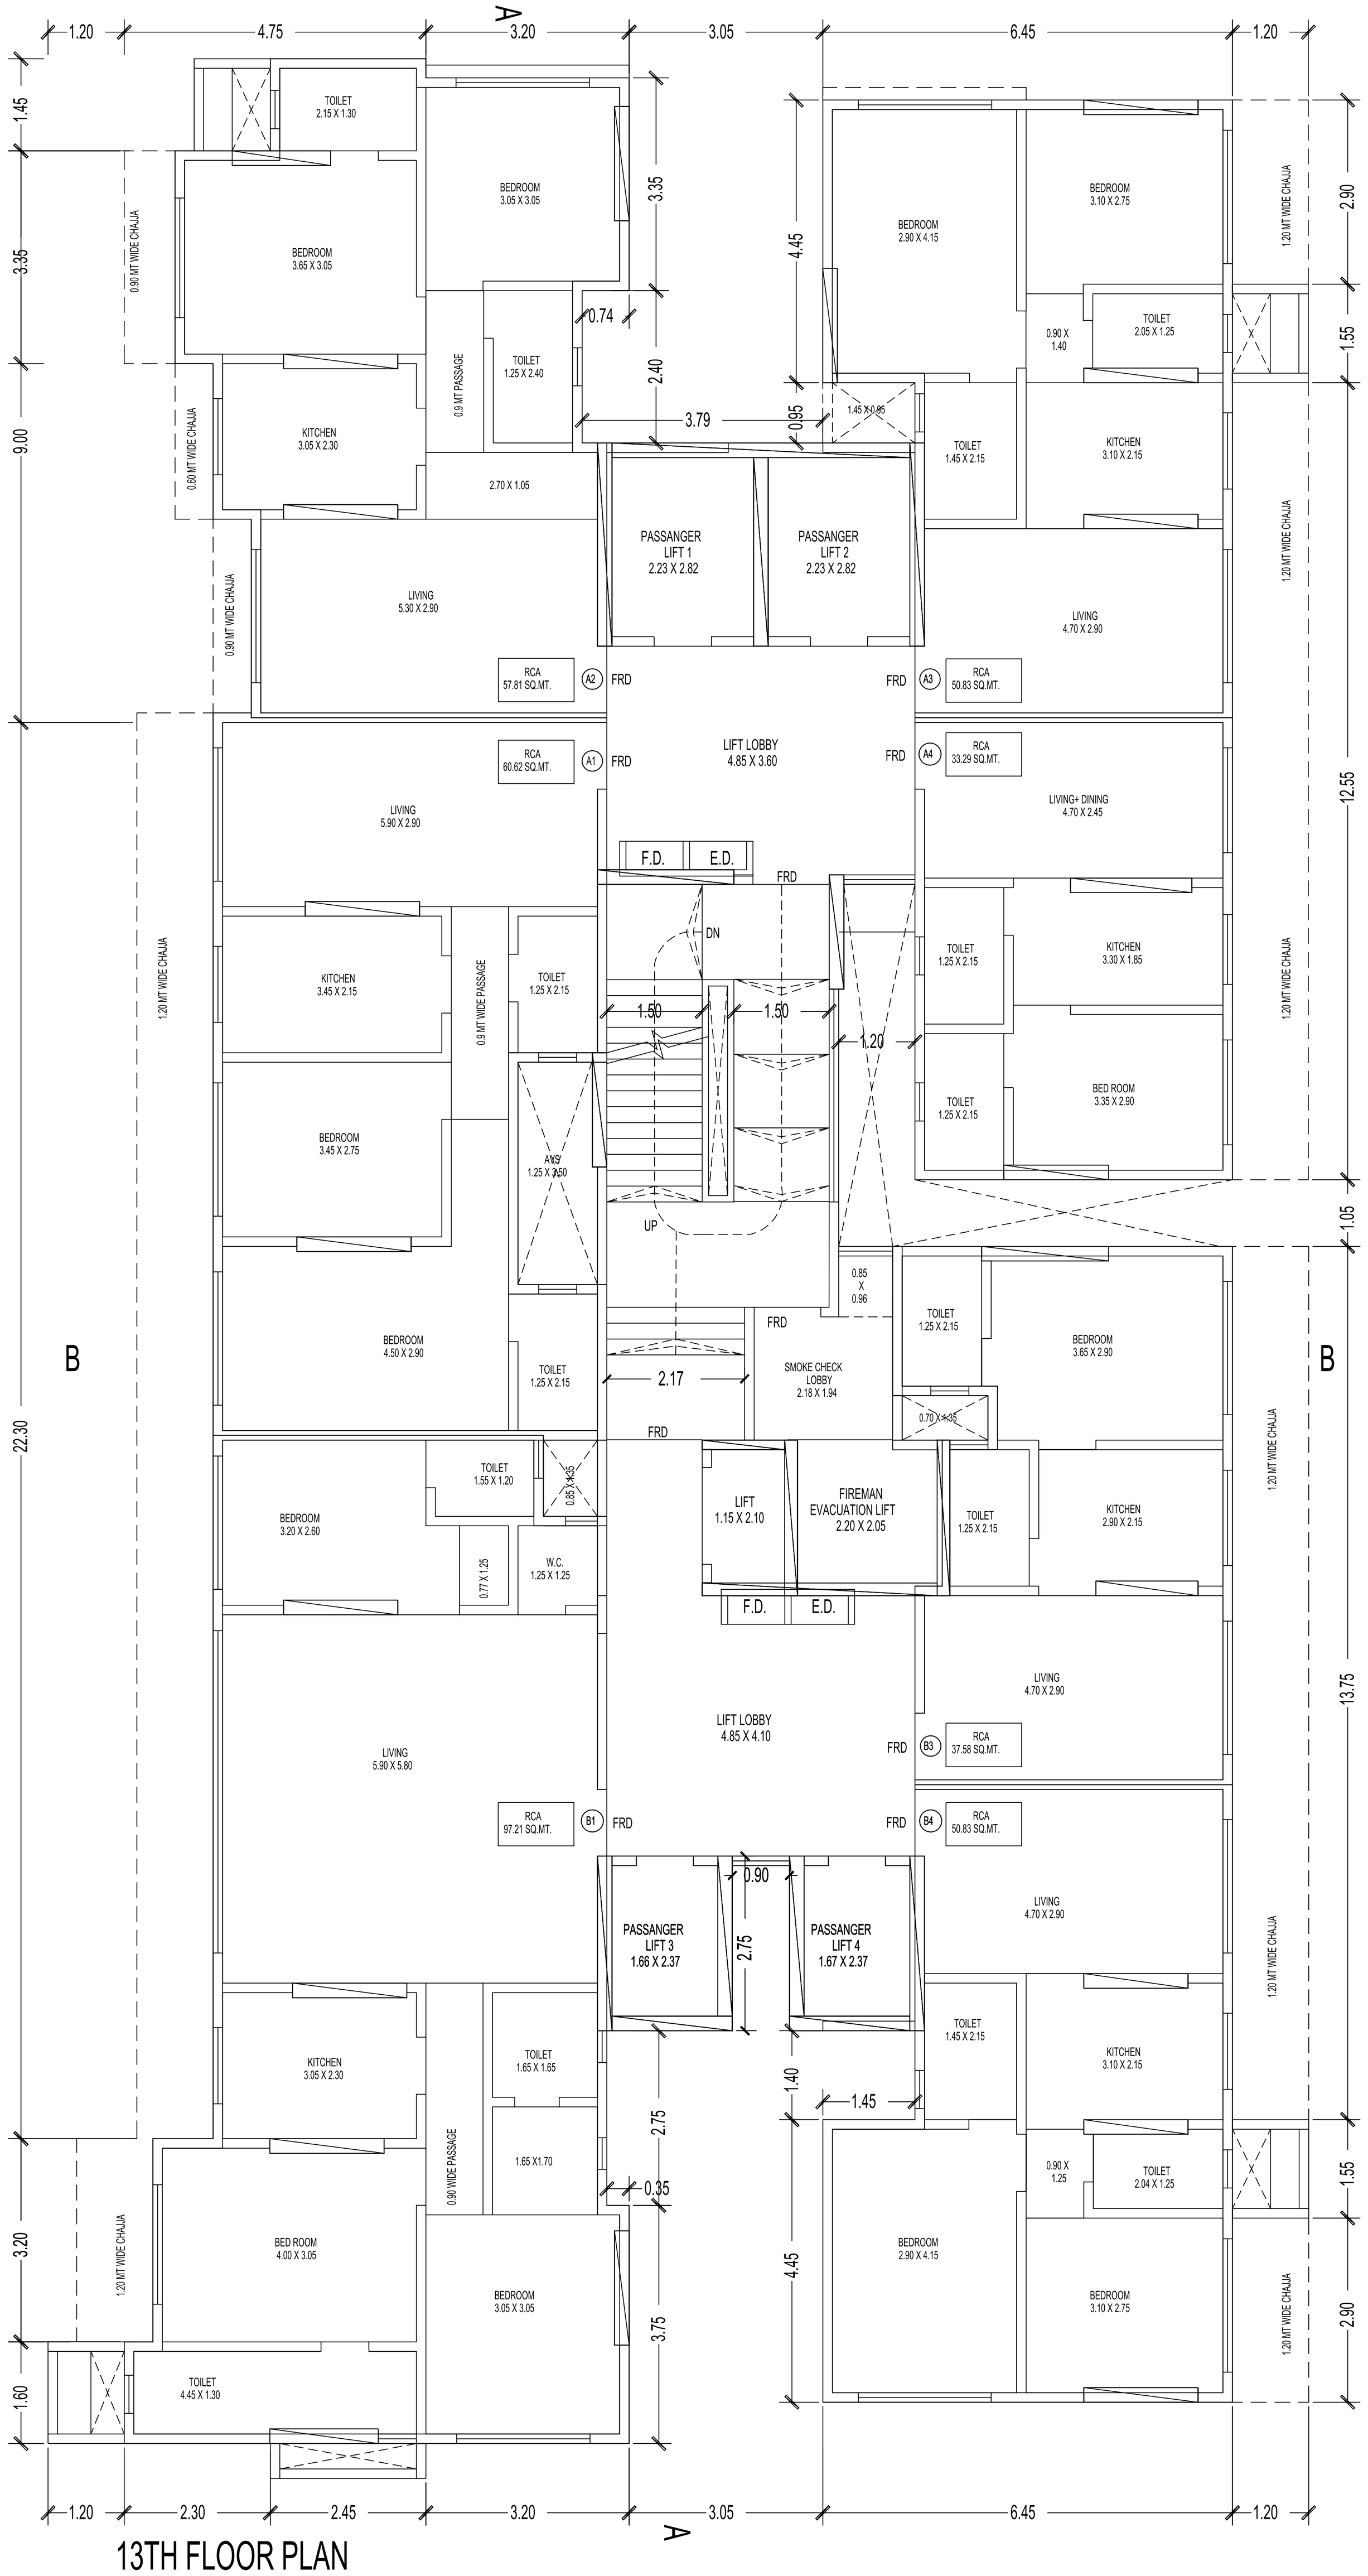


13TH FLOOR PLAN

SCALE 1:100

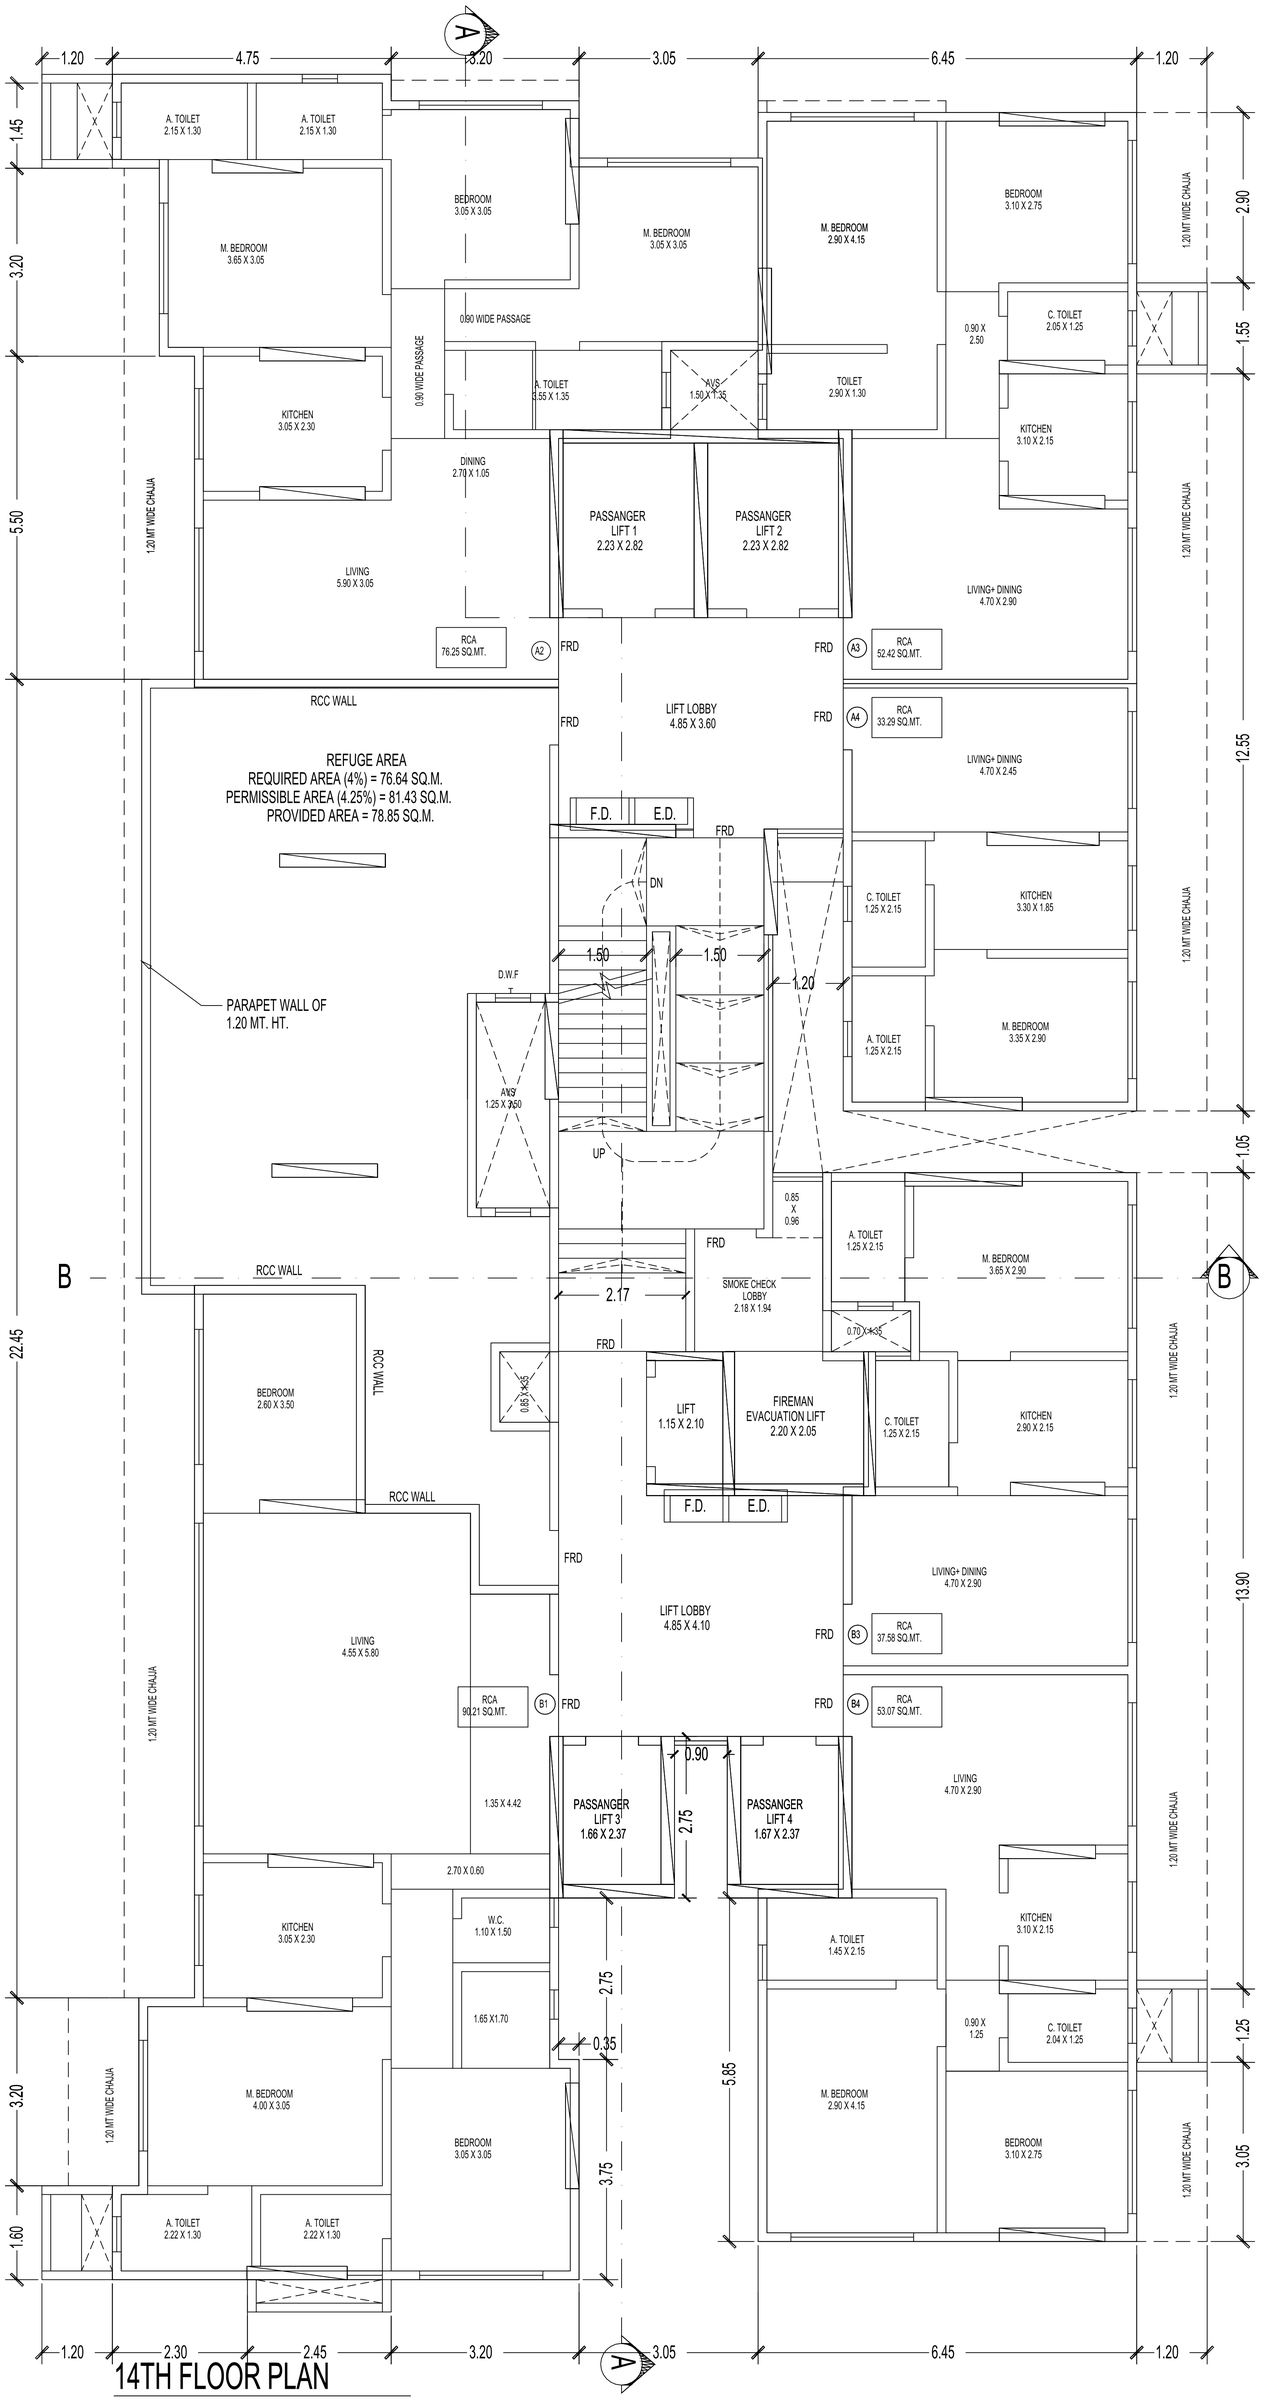


14TH FLOOR PLAN

SCALE 1:100

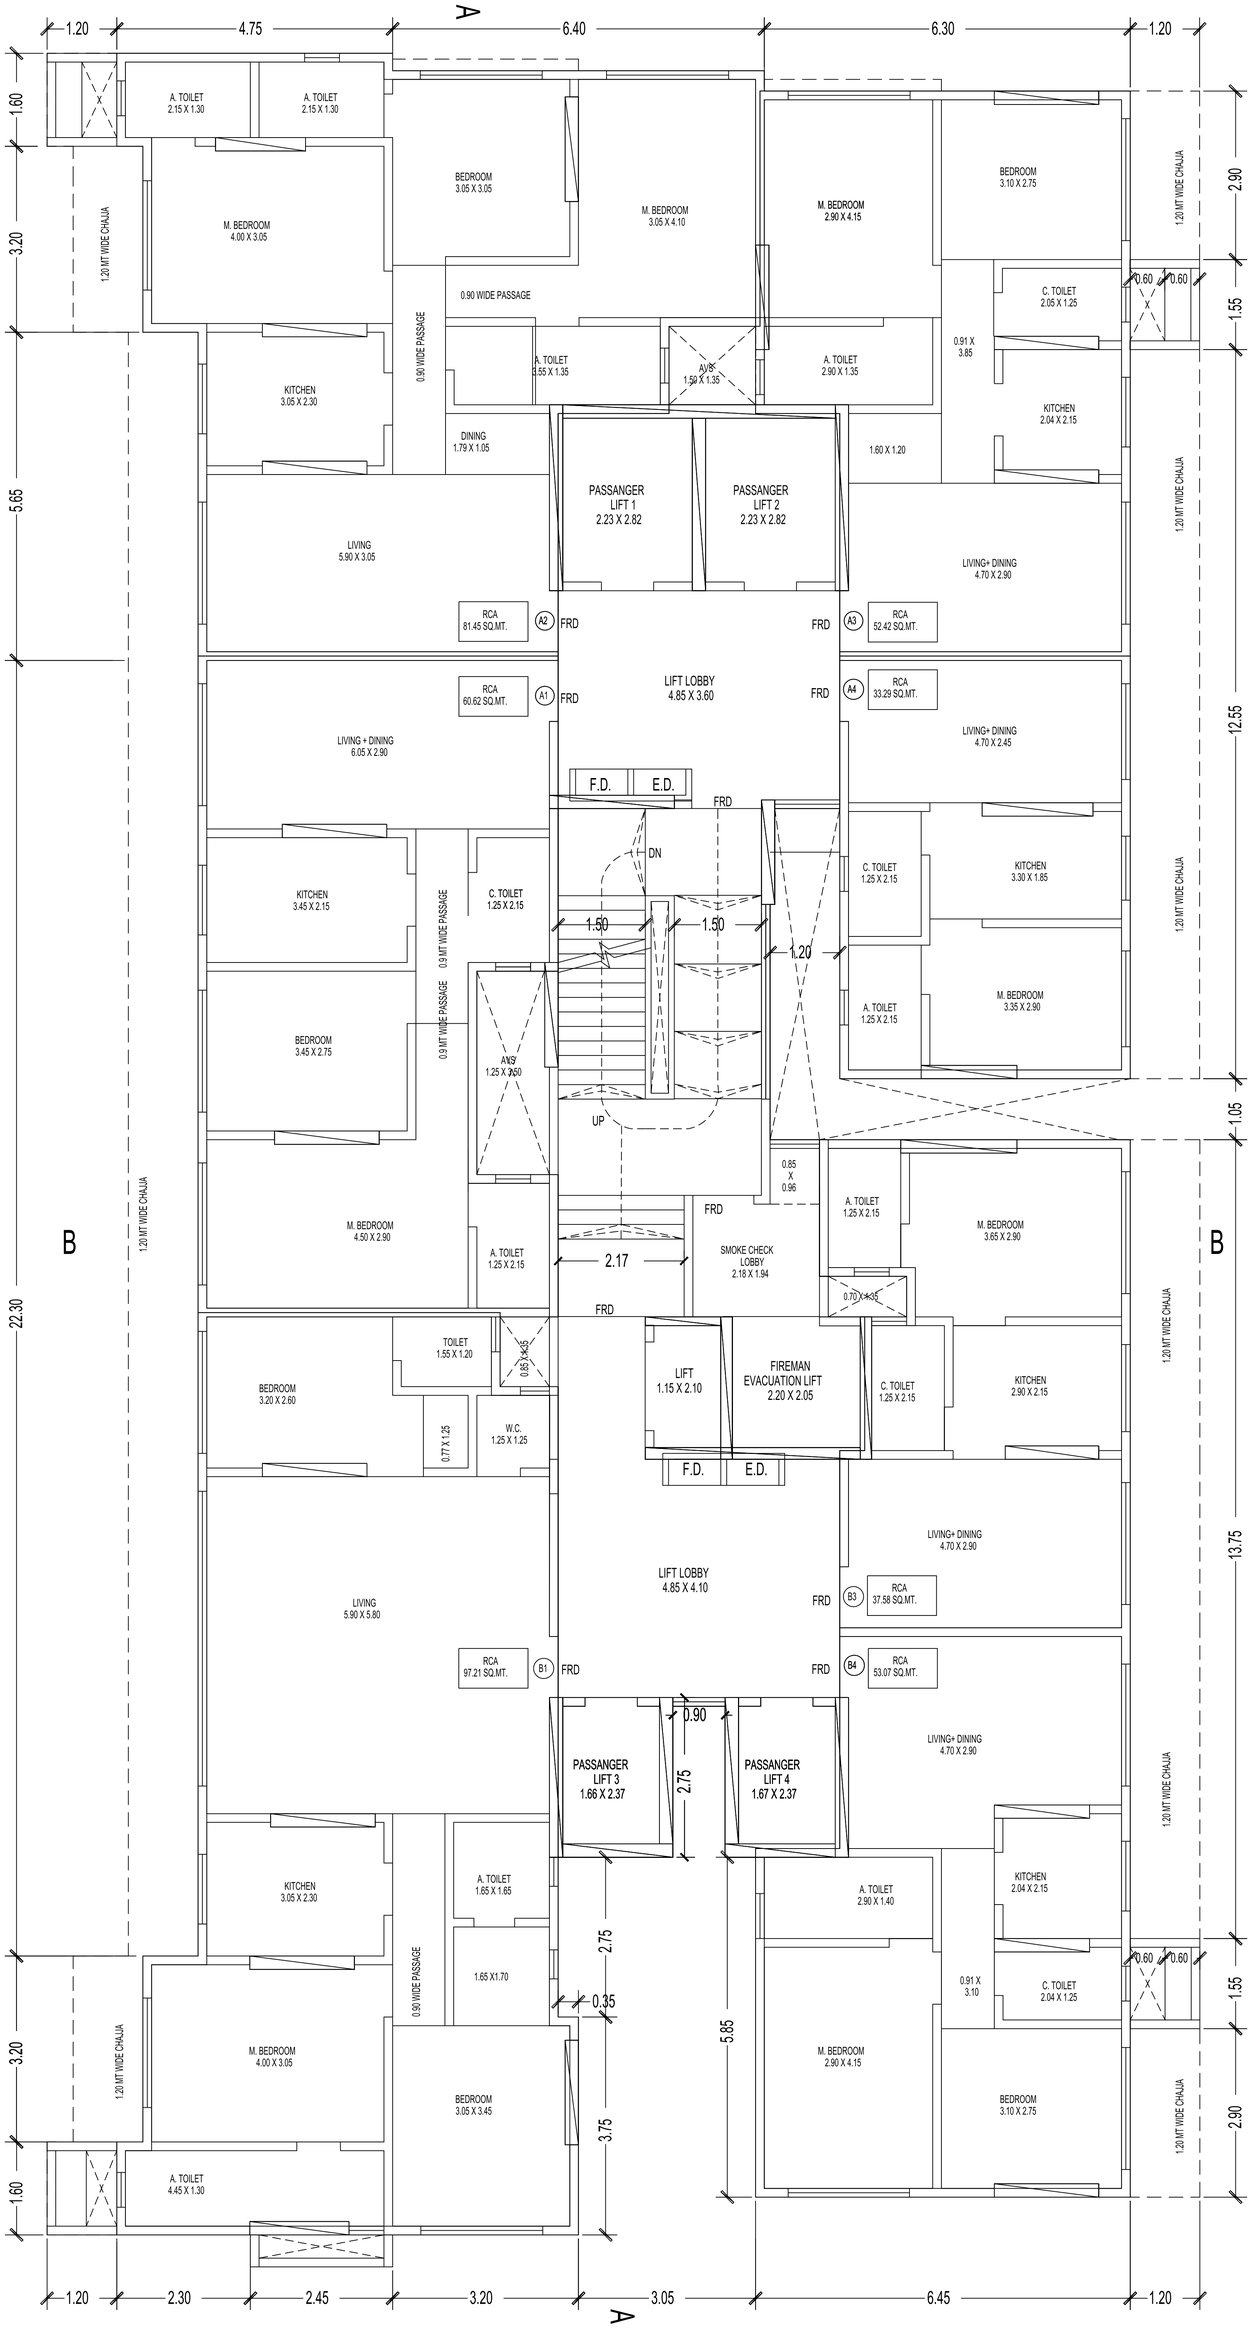


15TH & 16TH FLOOR PLAN

SCALE 1:100

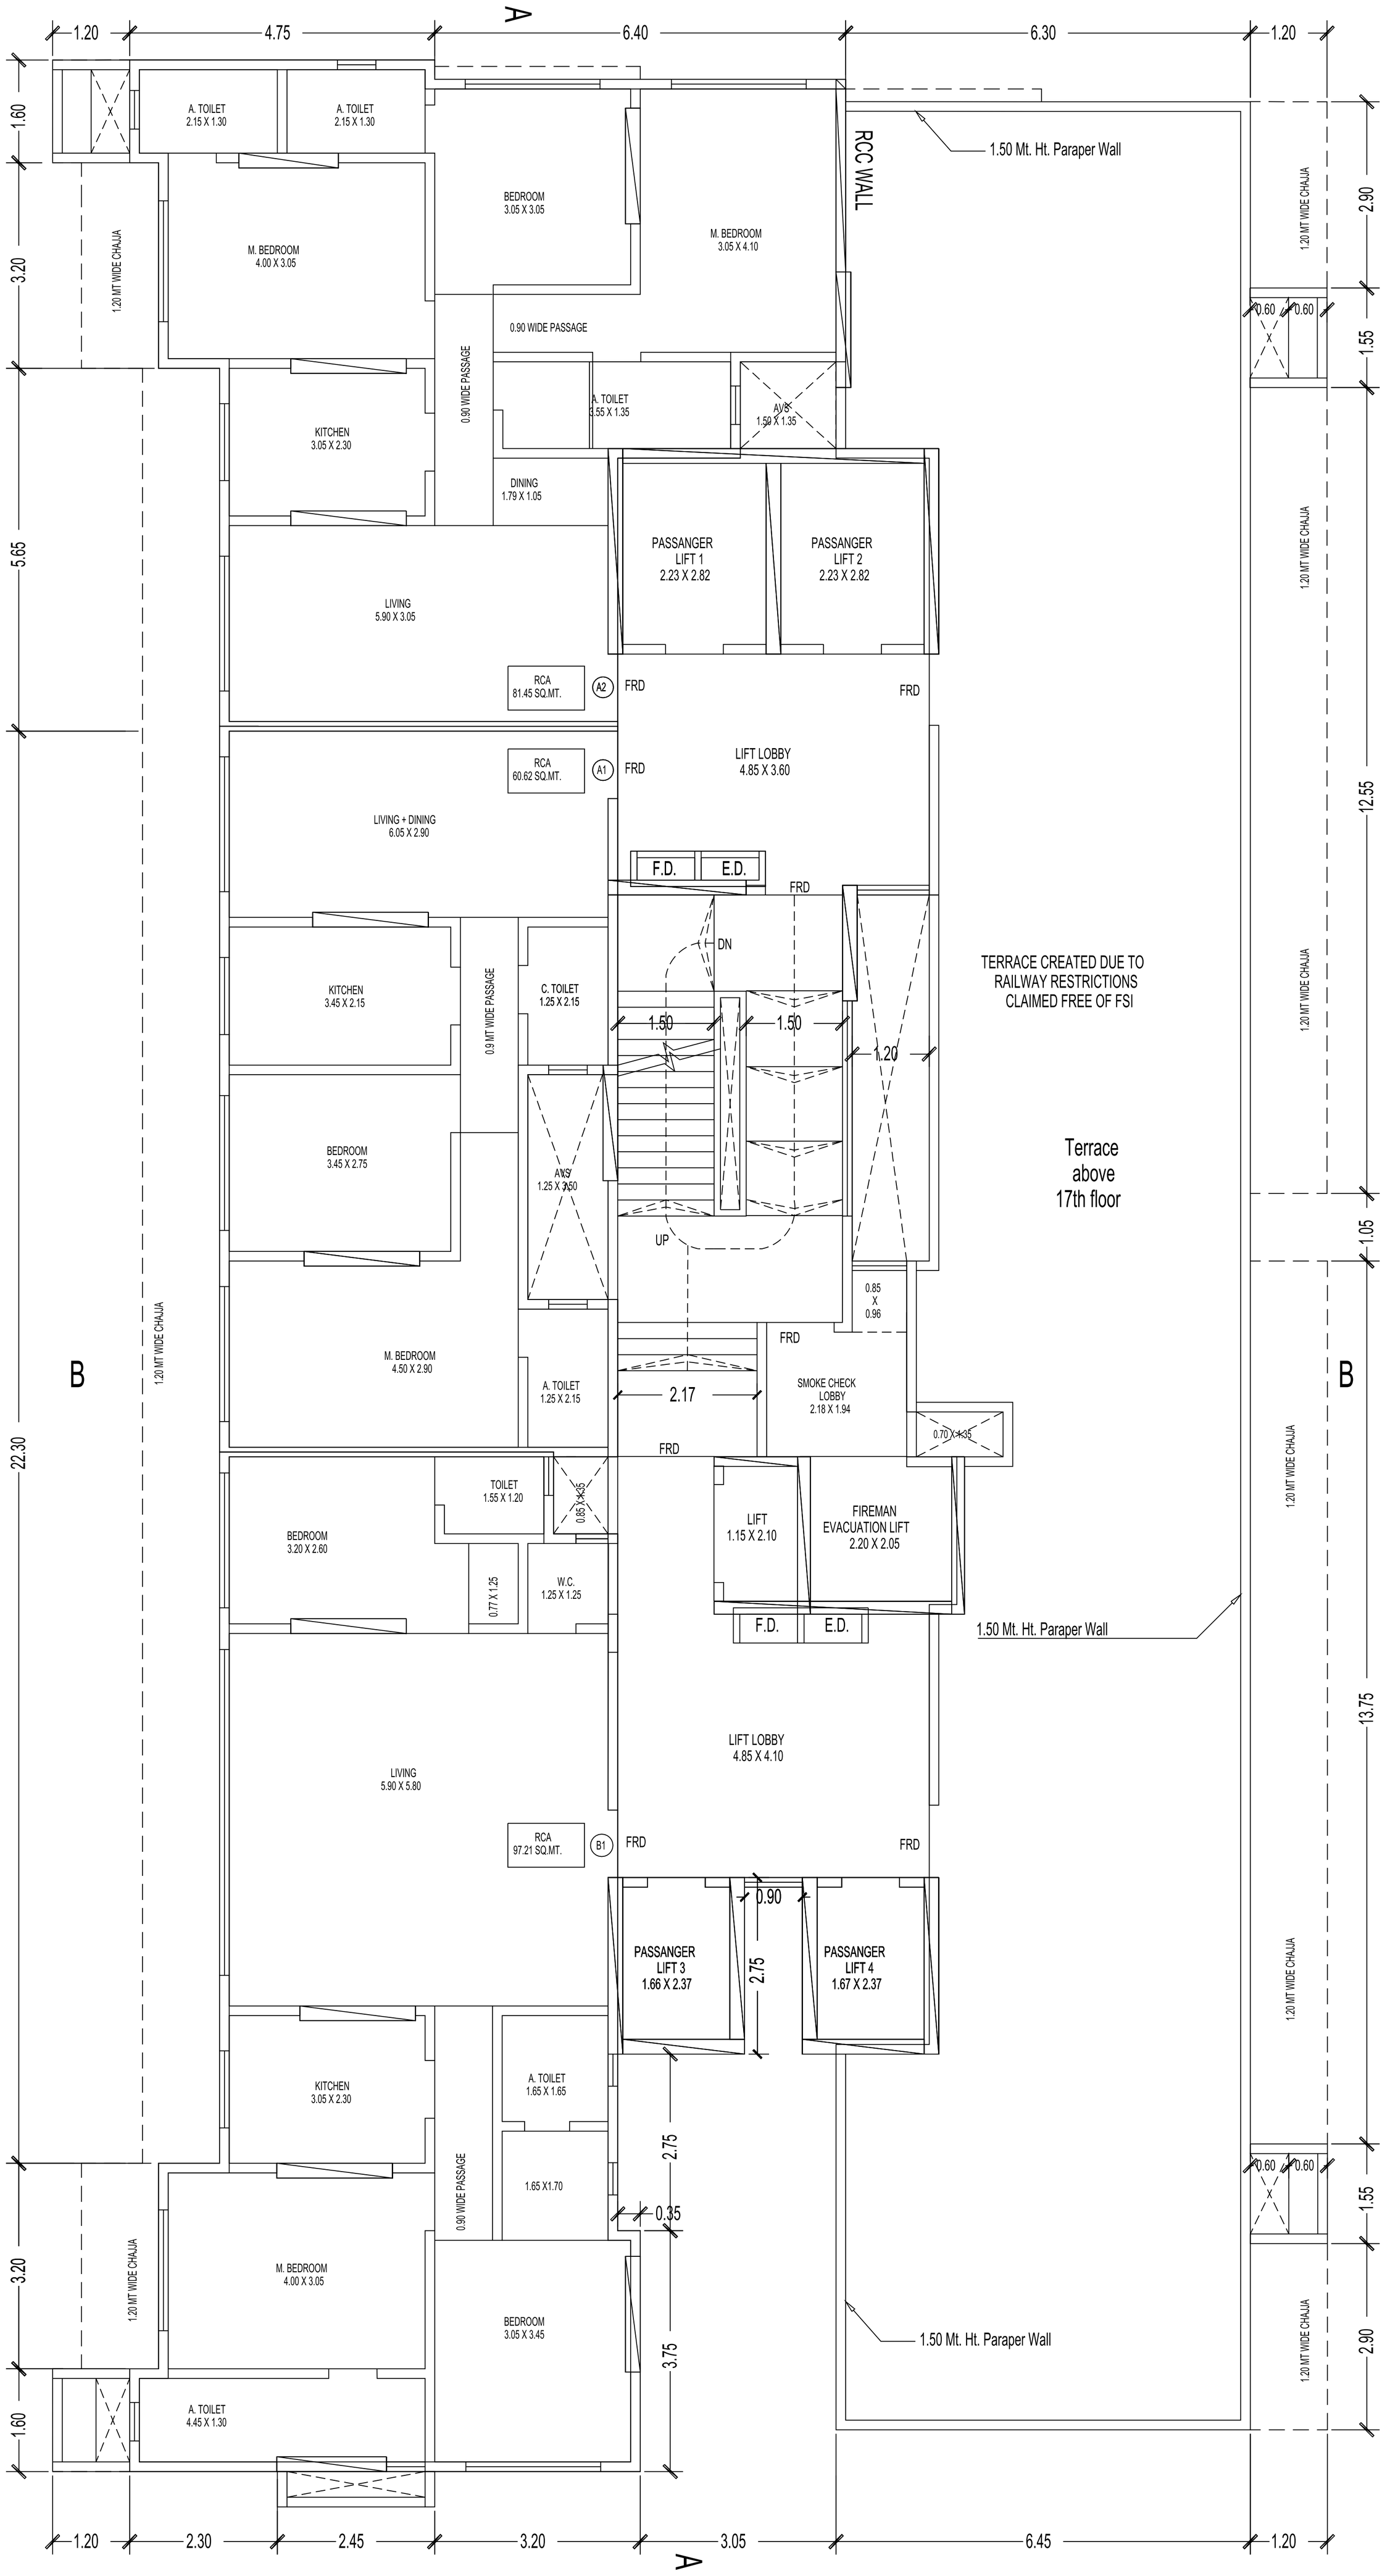


17TH FLOOR PLAN

SCALE 1:100

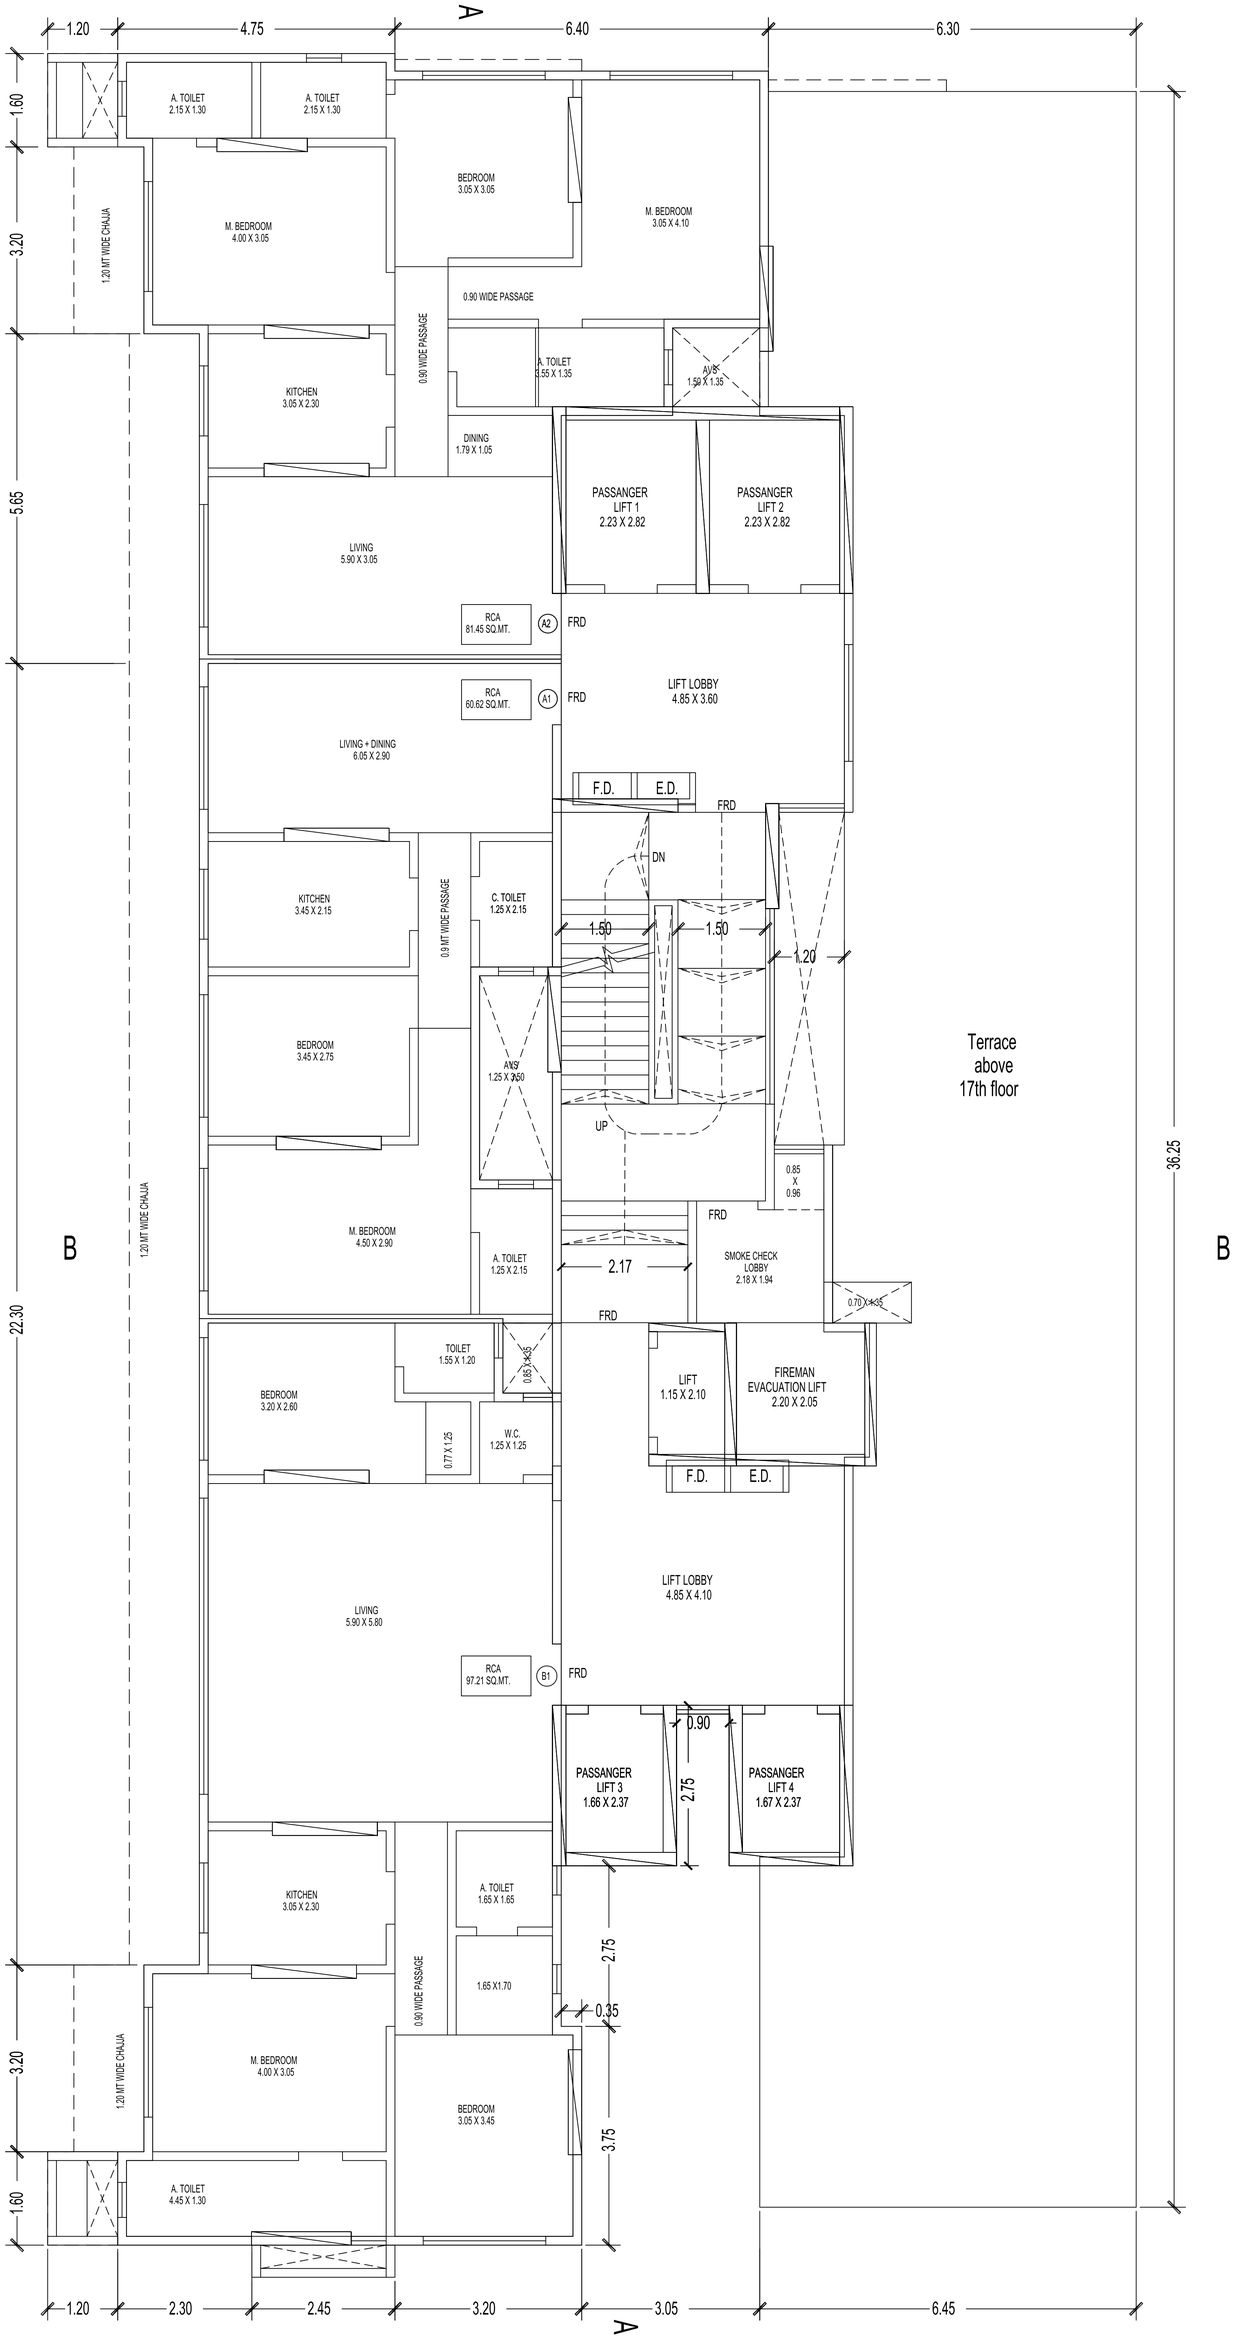


18TH FLOOR PLAN

SCALE 1:100

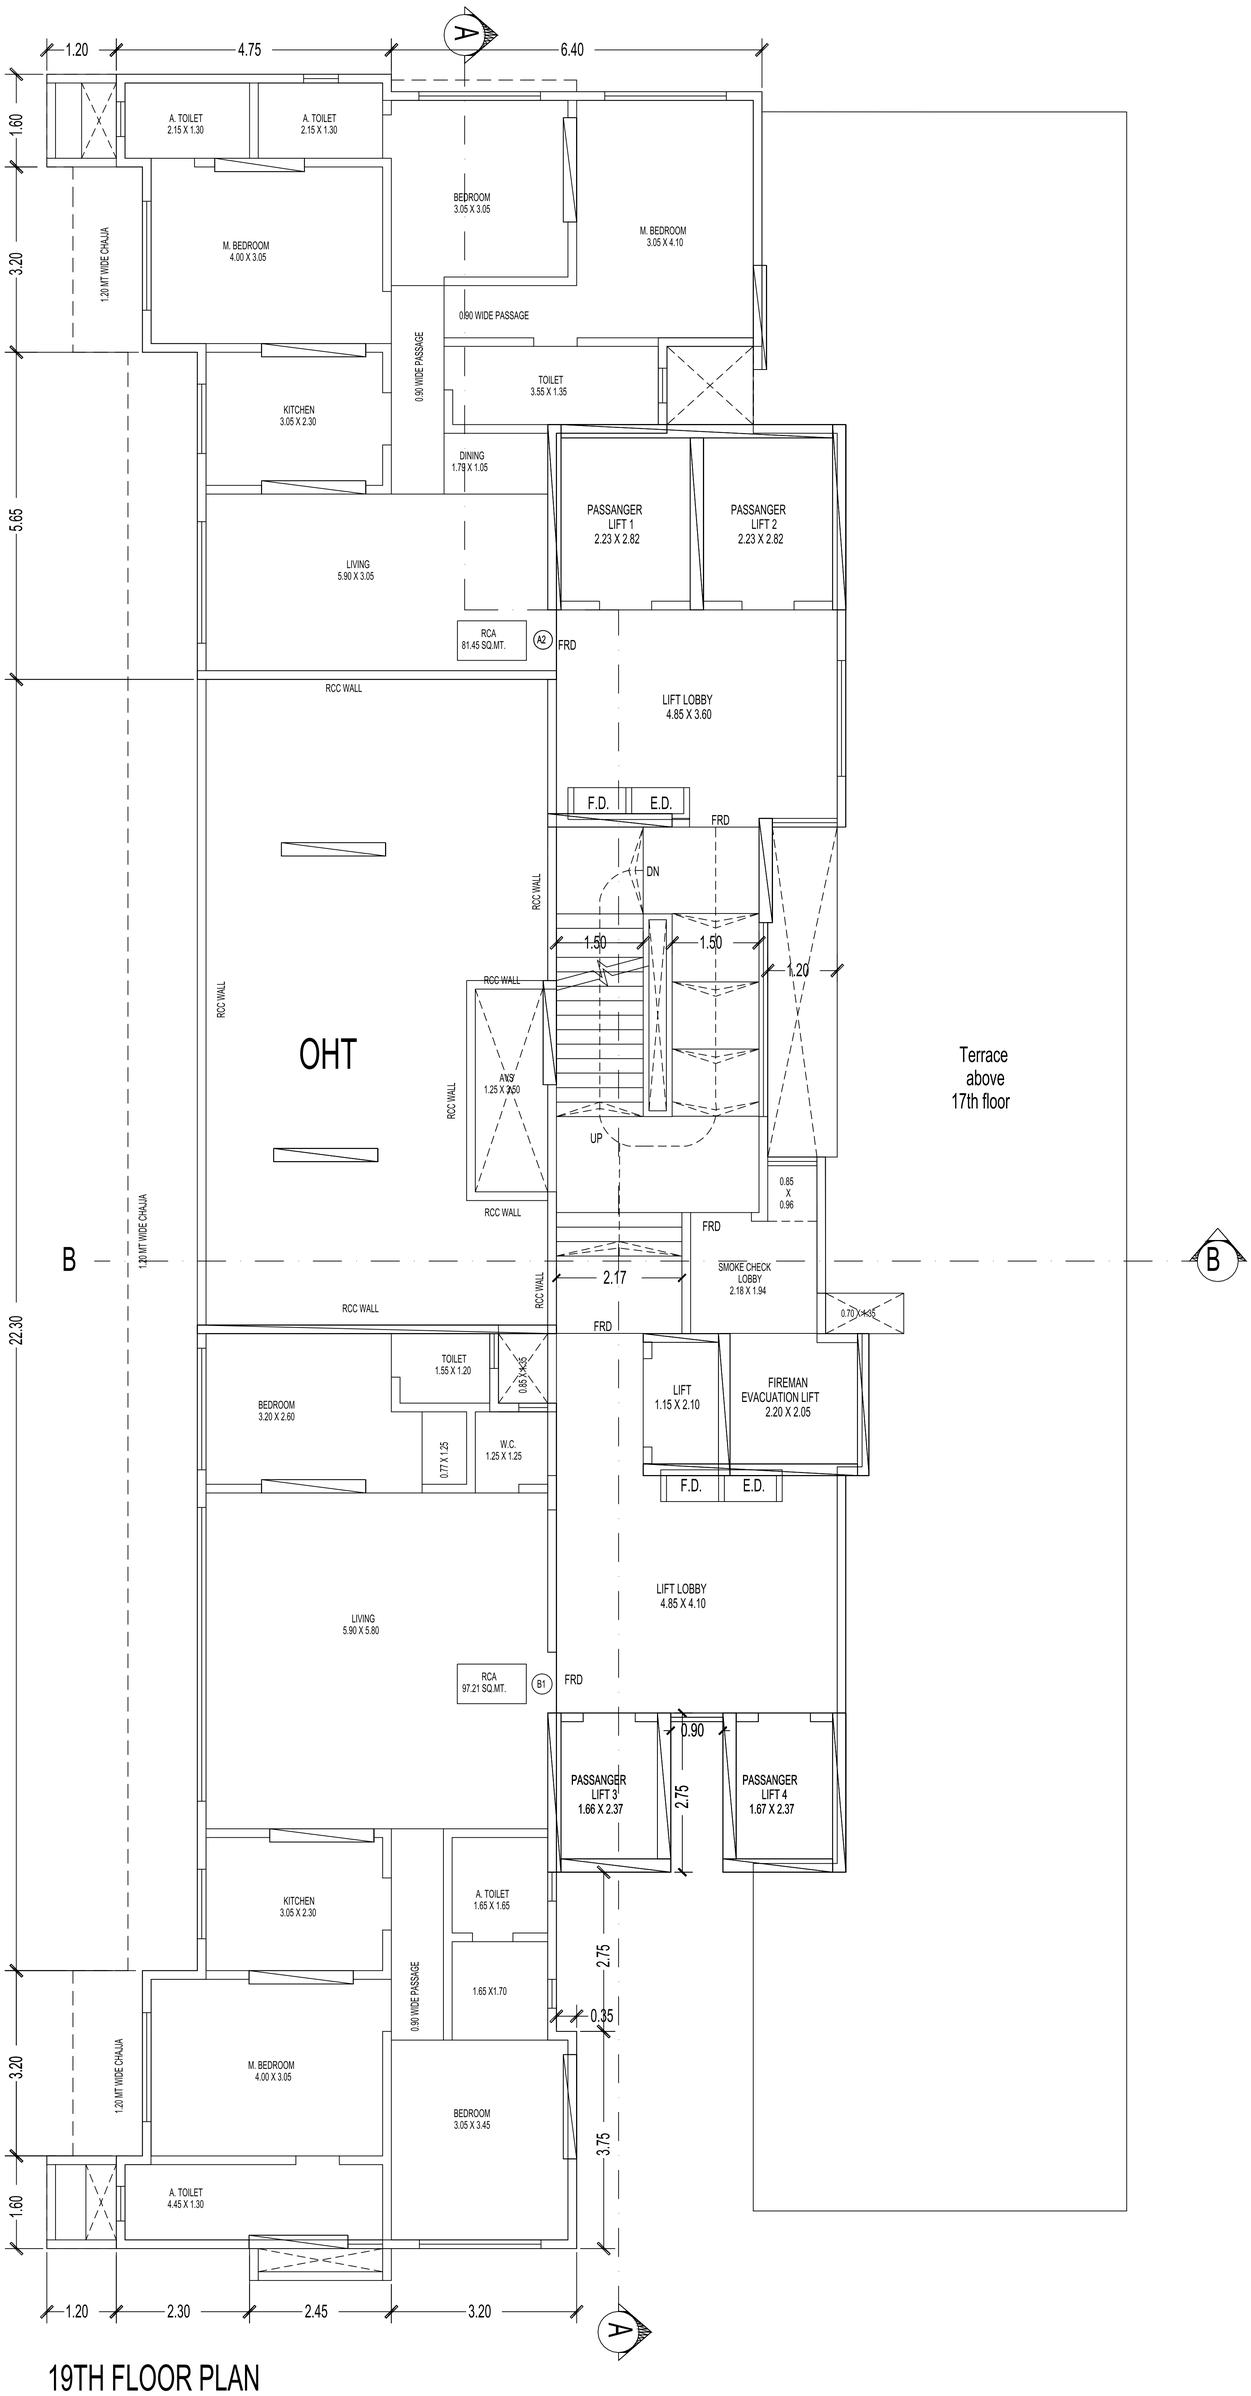


19TH FLOOR PLAN

SCALE 1:100

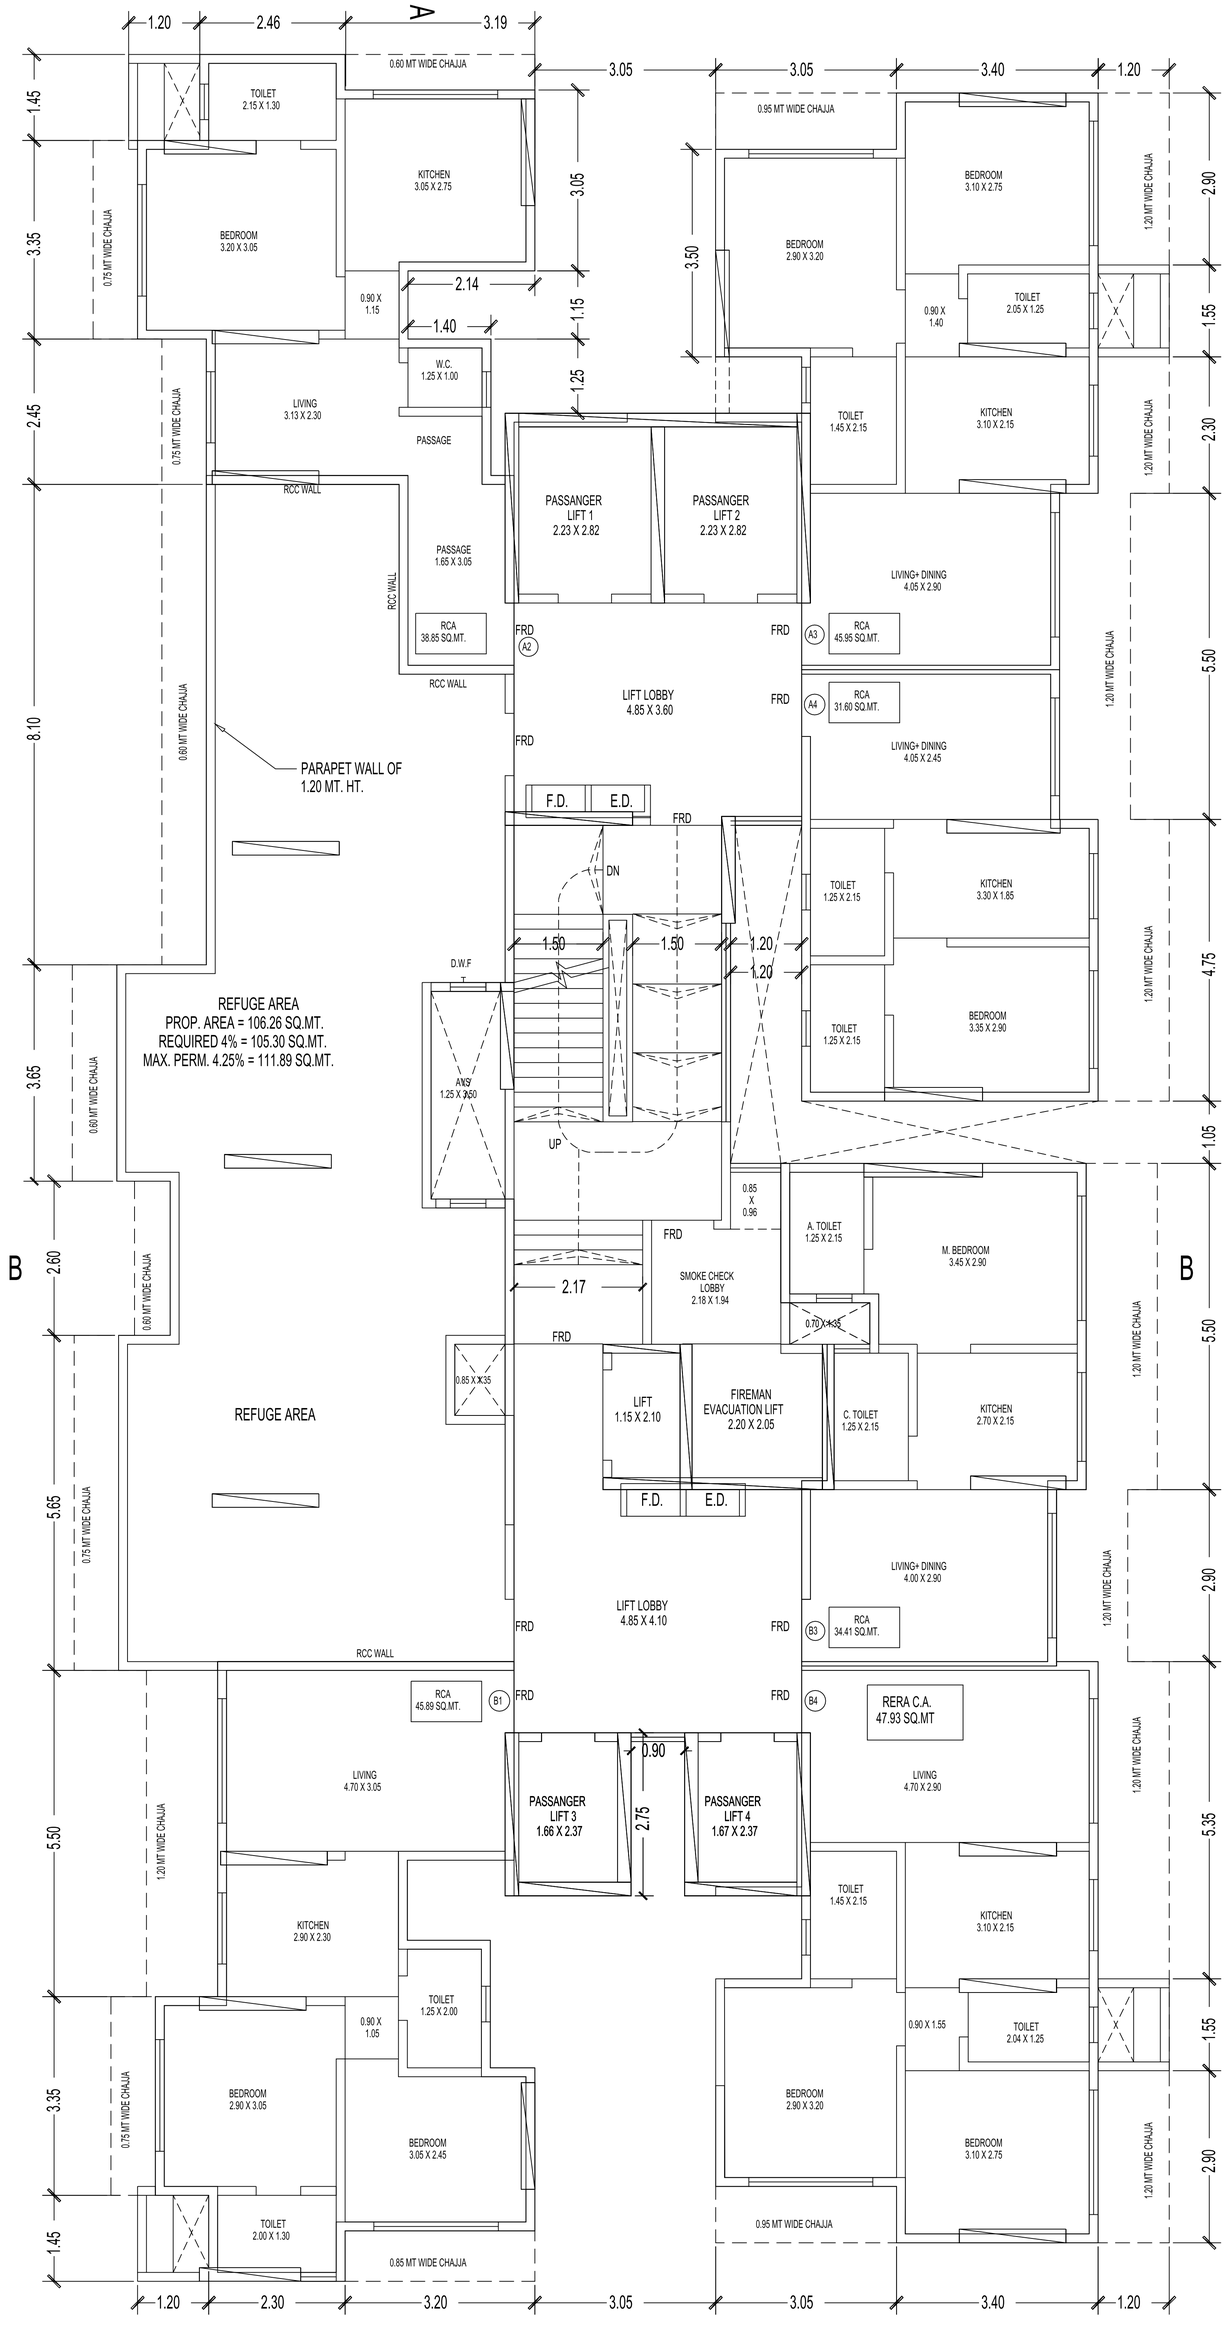


7 TH FLOOR PLAN

SCALE 1:100

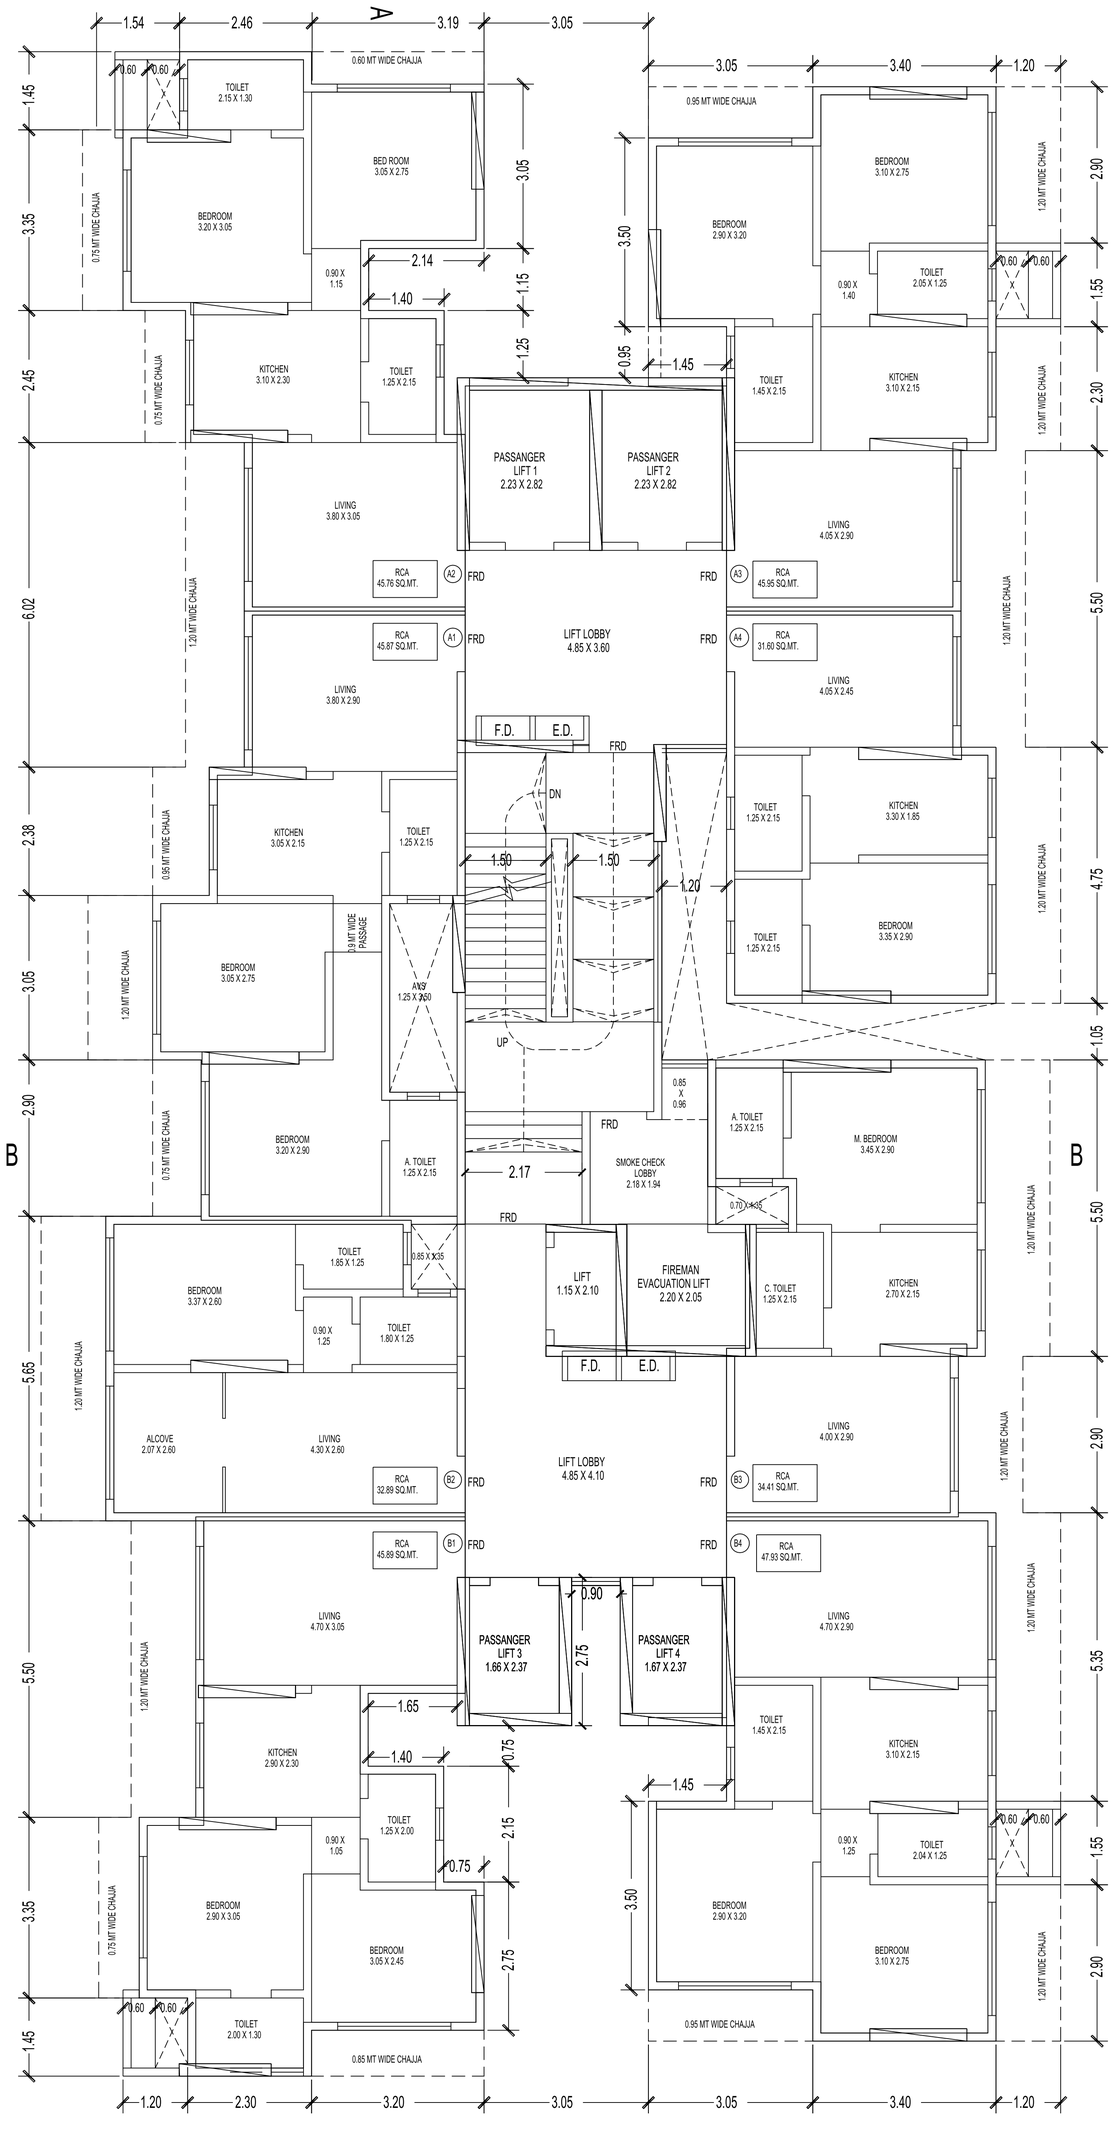

8 TH FLOOR PLAN

SCALE 1:100

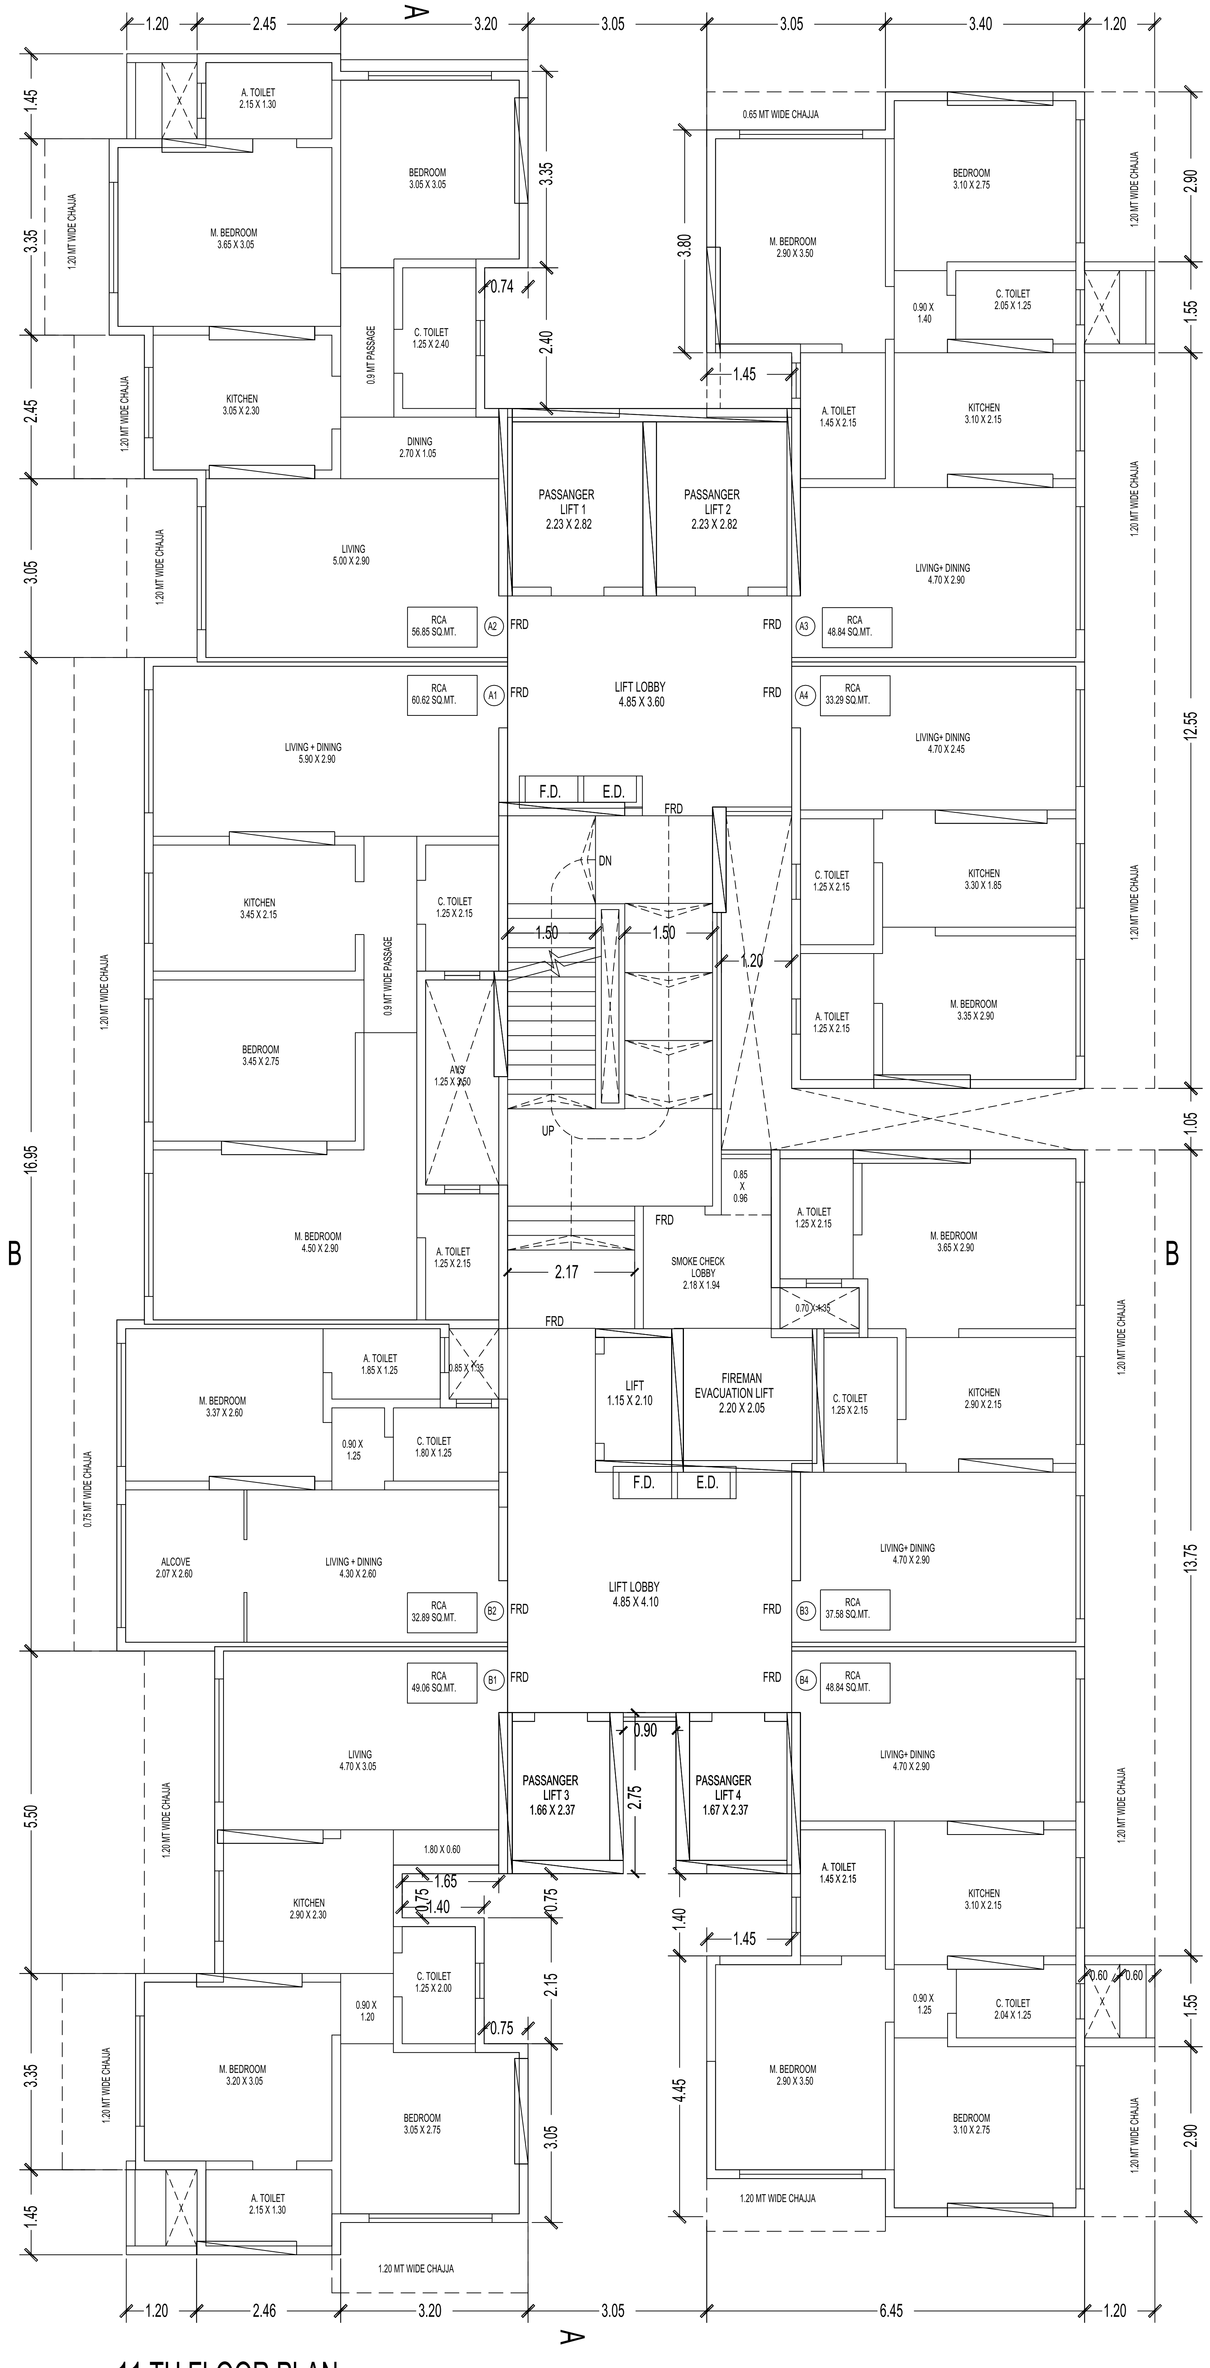

11 TH FLOOR PLAN

SCALE 1:100