
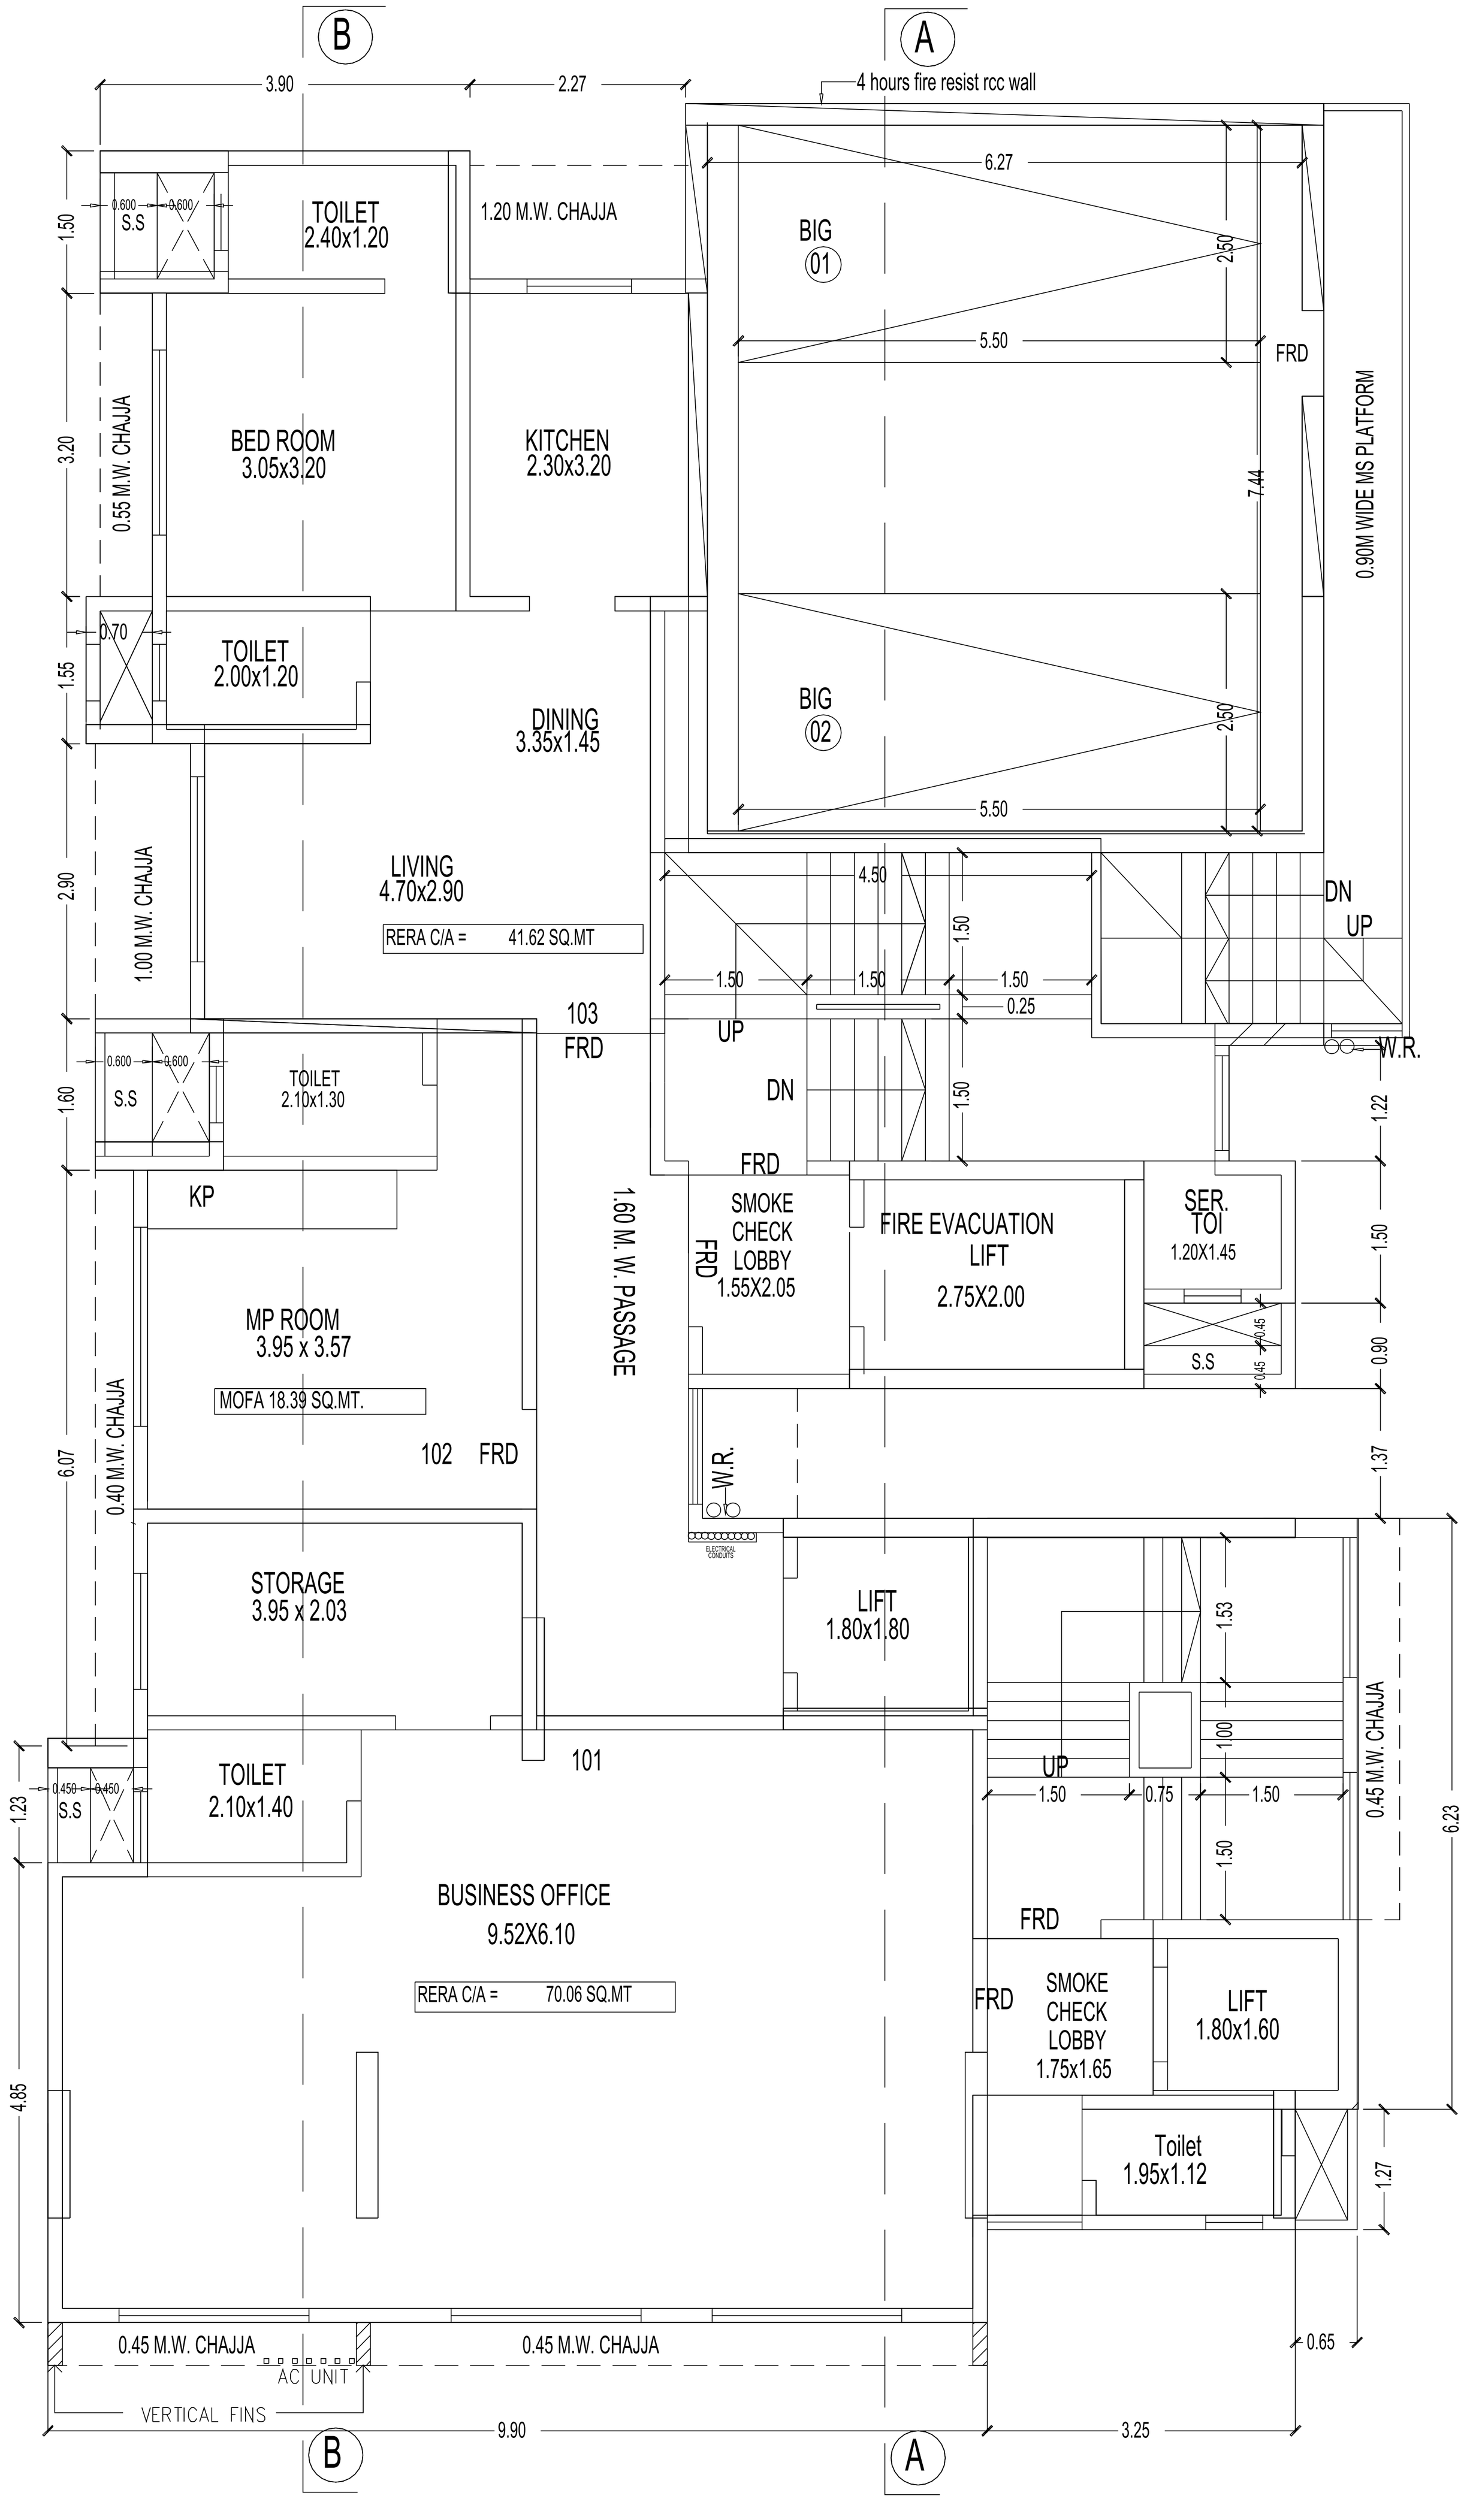



1ST FLOOR PLAN

SCALE - 1:100

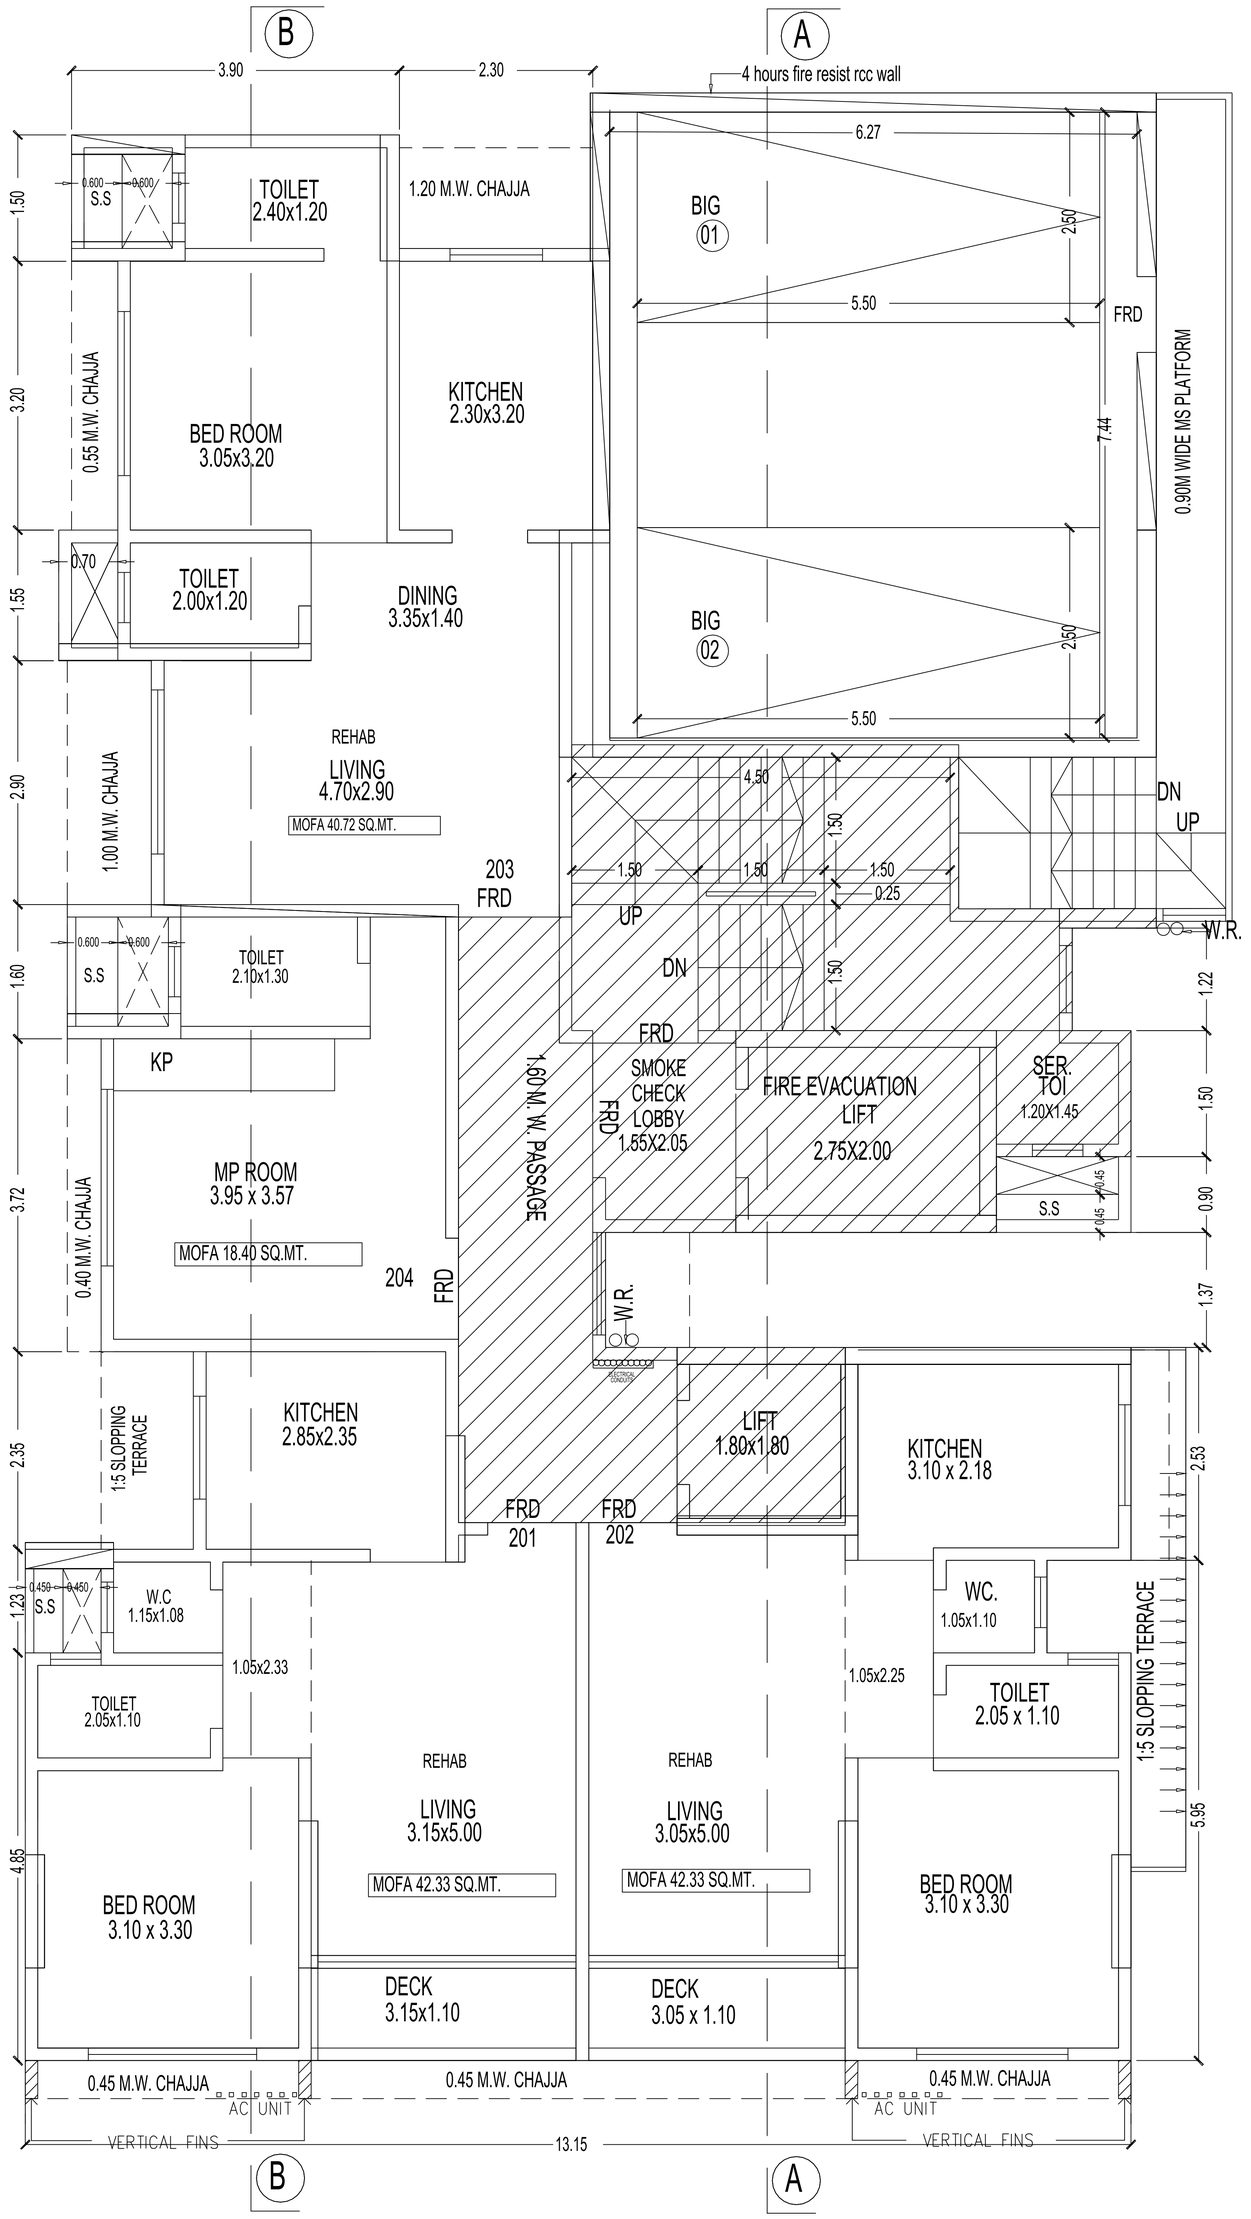

2ND FLOOR PLAN


SCALE - 1:100

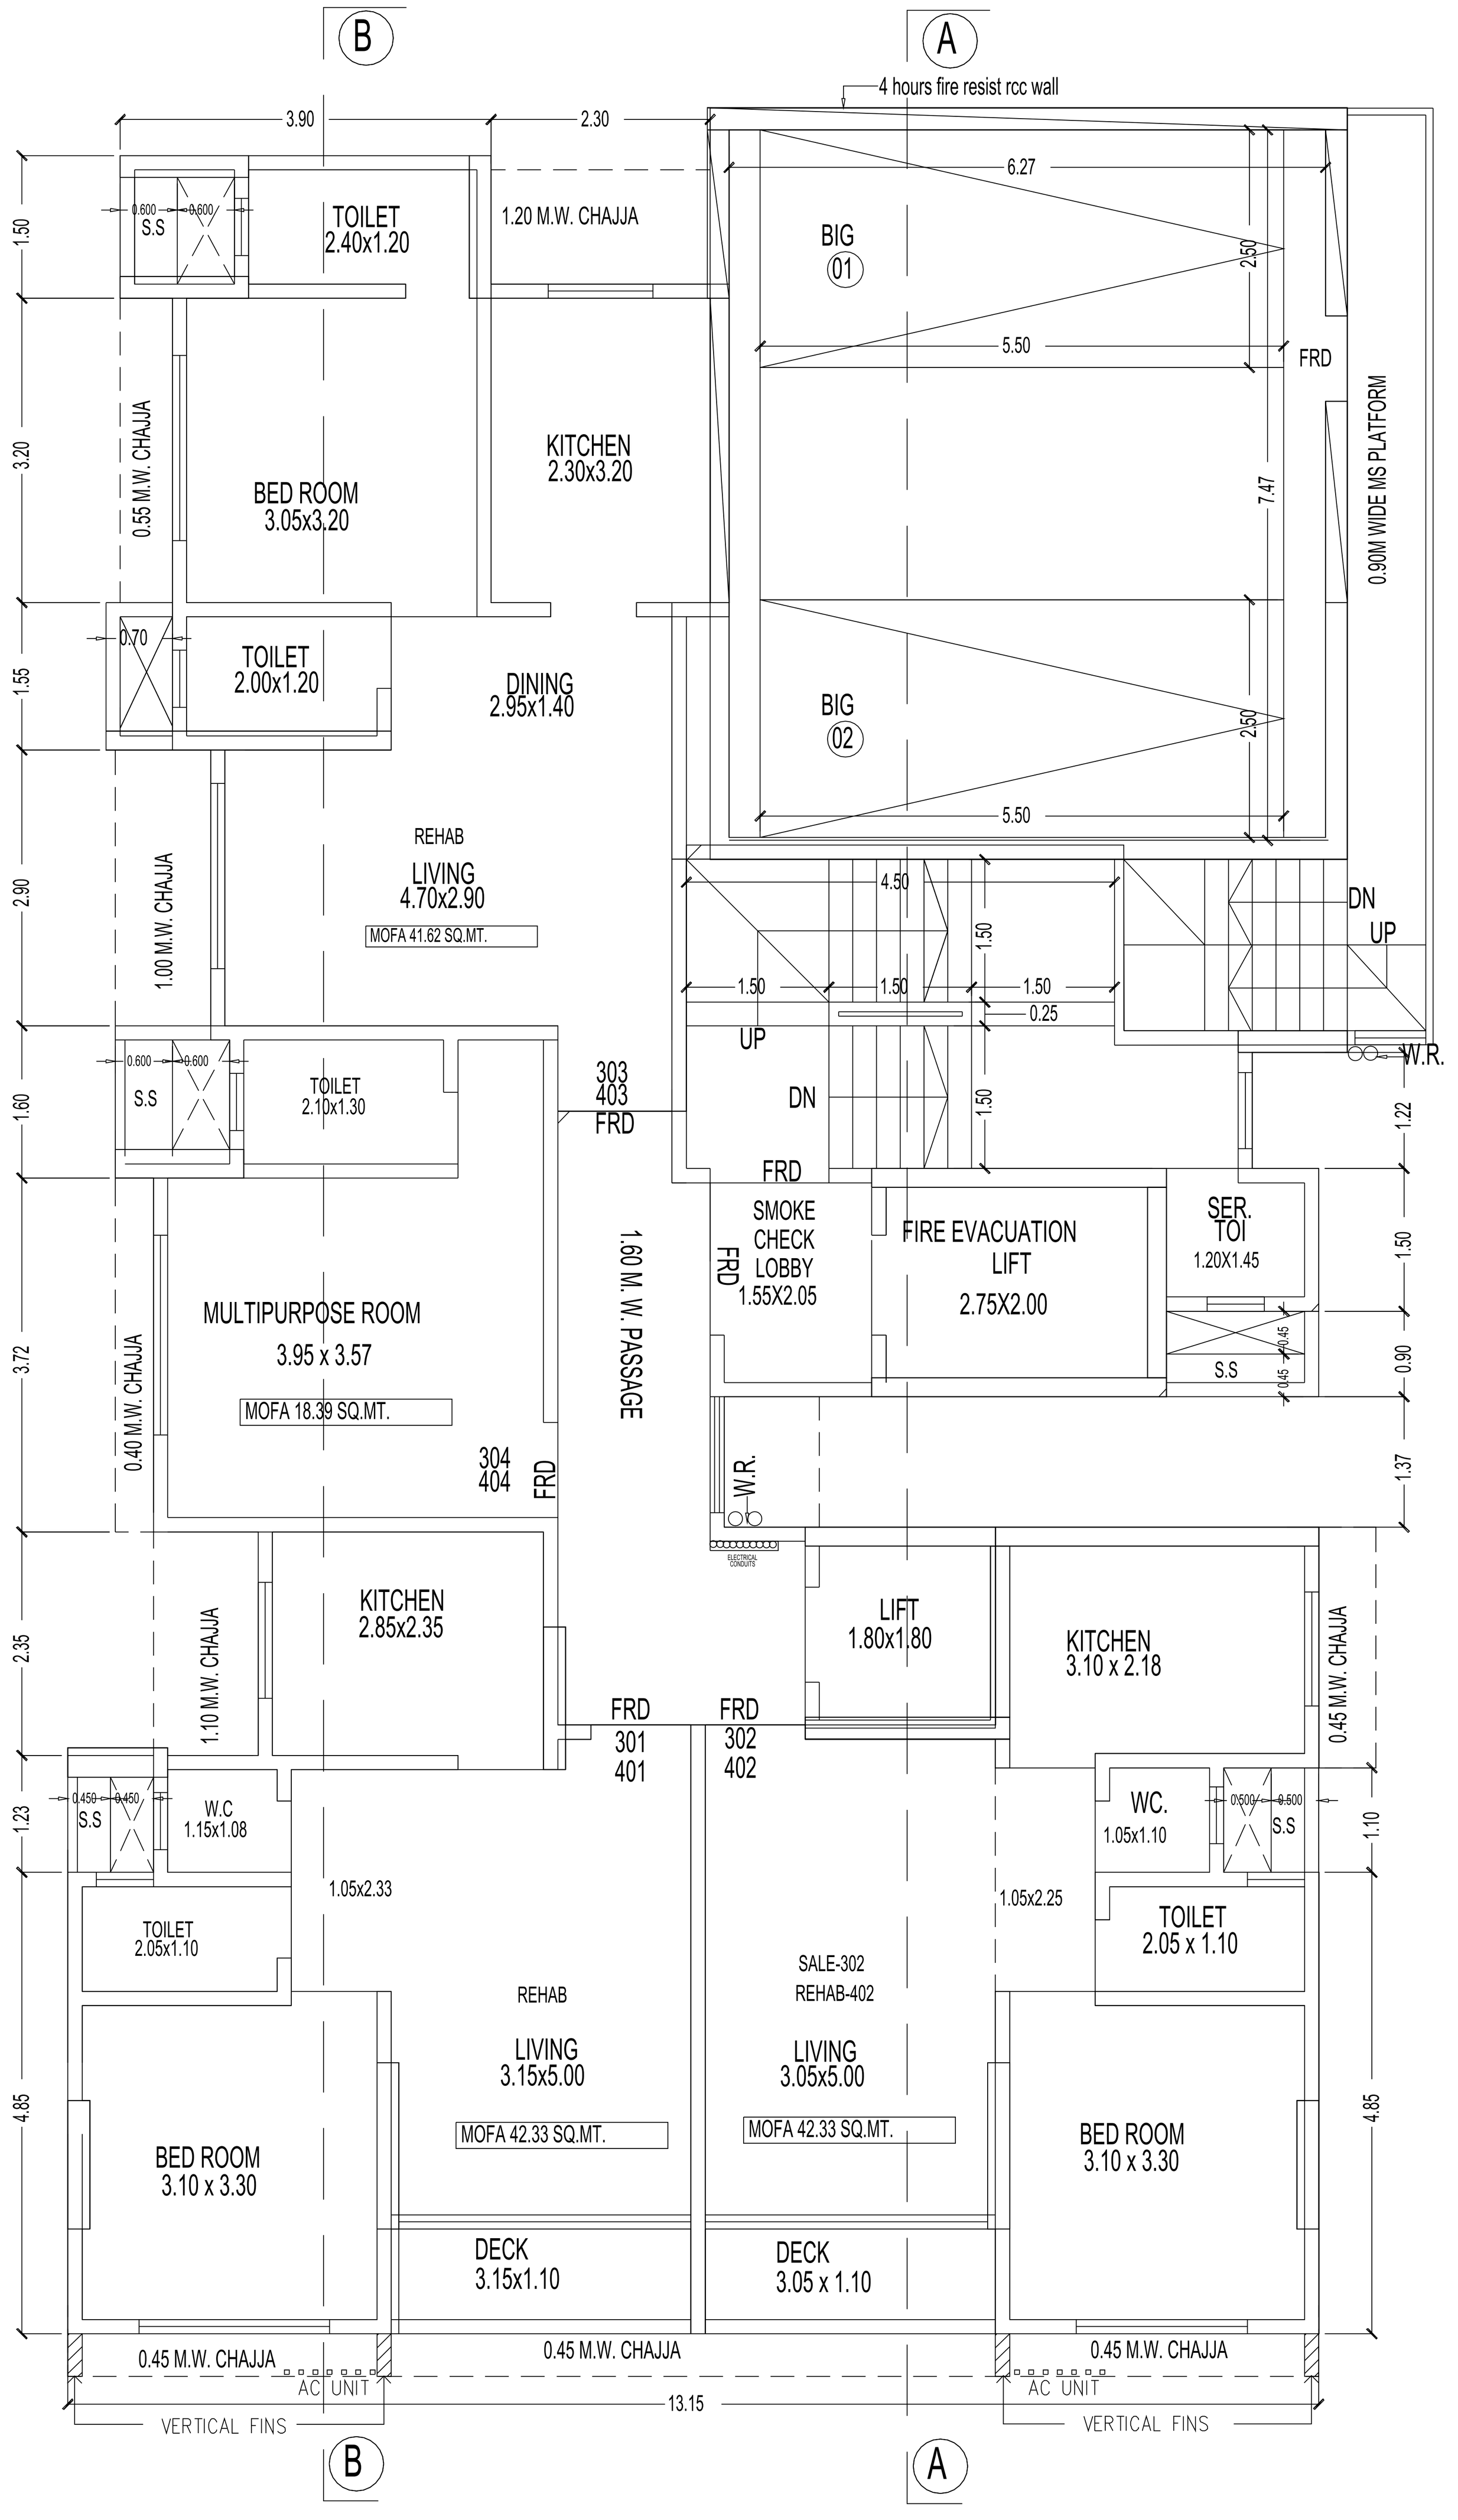

3RD & 4TH FLOOR PLAN


SCALE - 1:100

SCALE-1:500

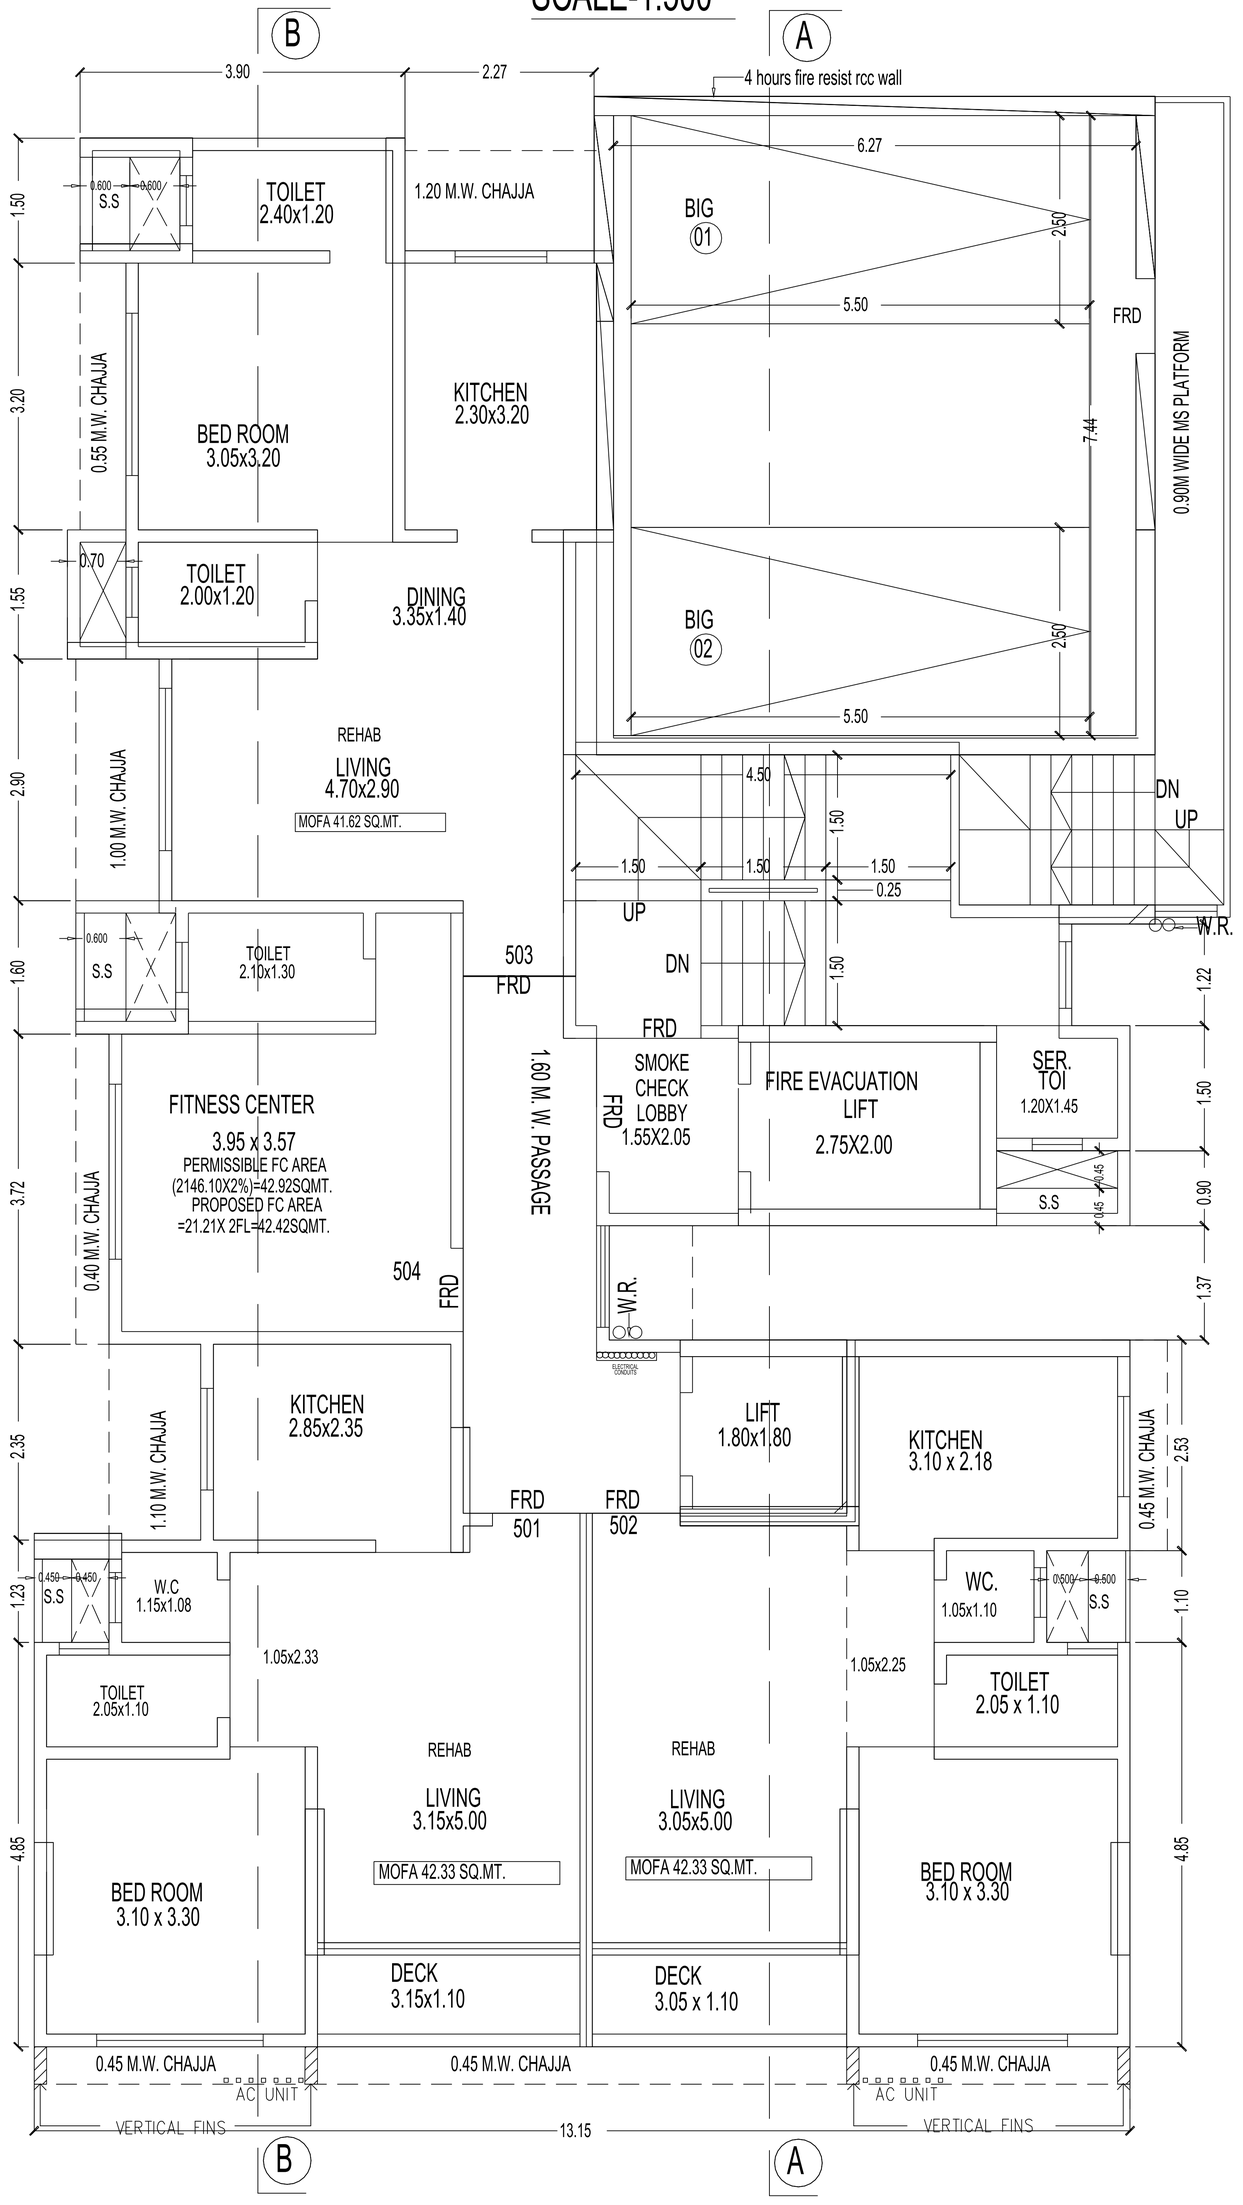


5TH FLOOR PLAN

SCALE - 1:100

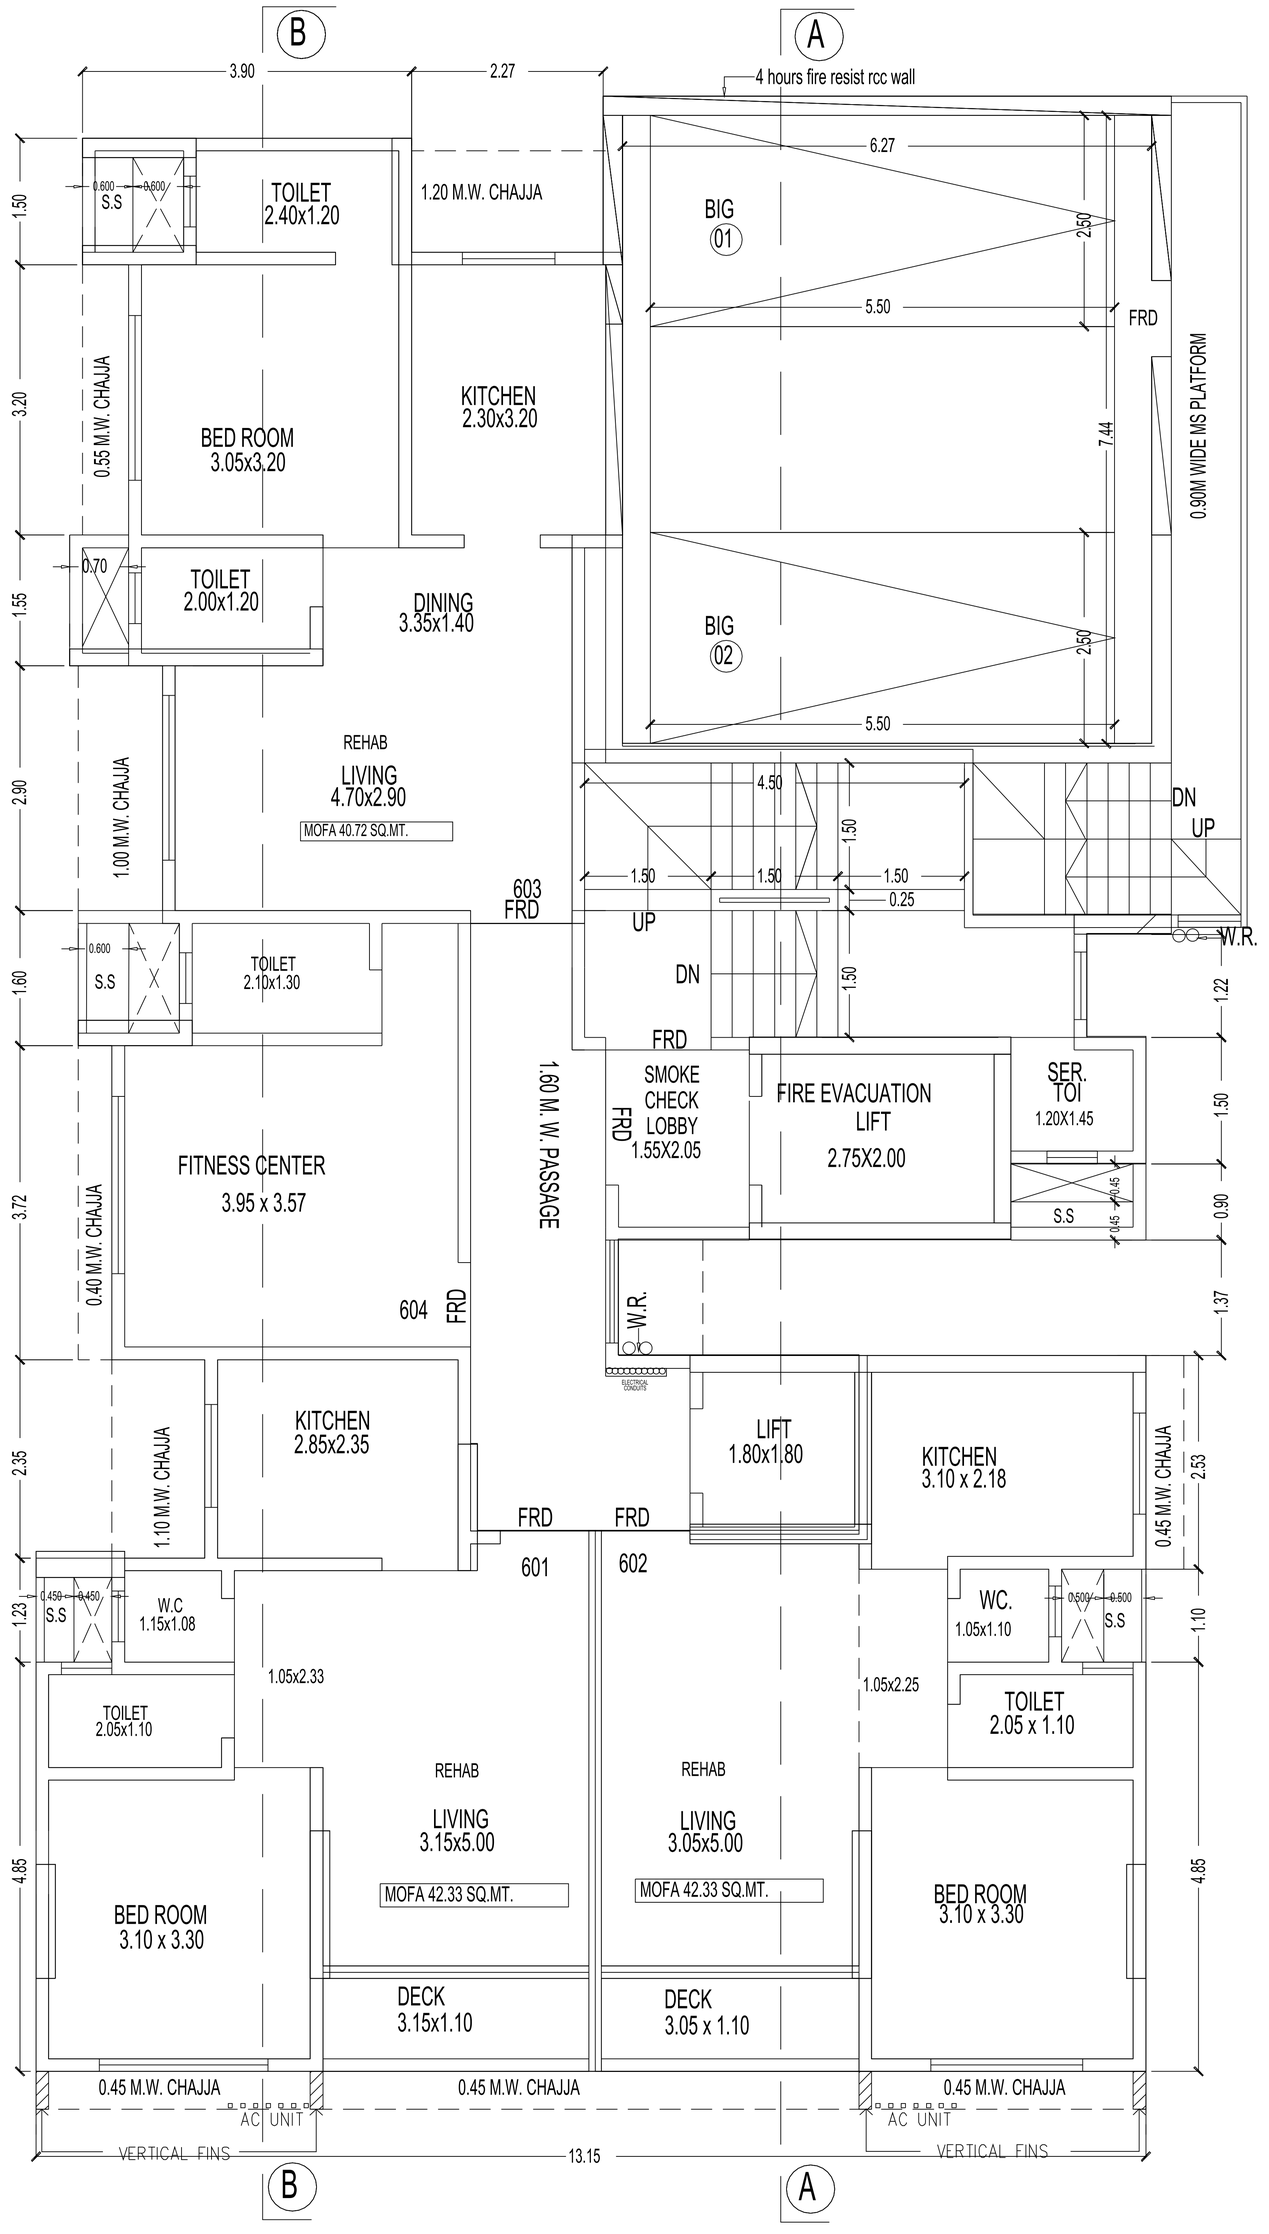


6TH FLOOR PLAN

SCALE - 1:100

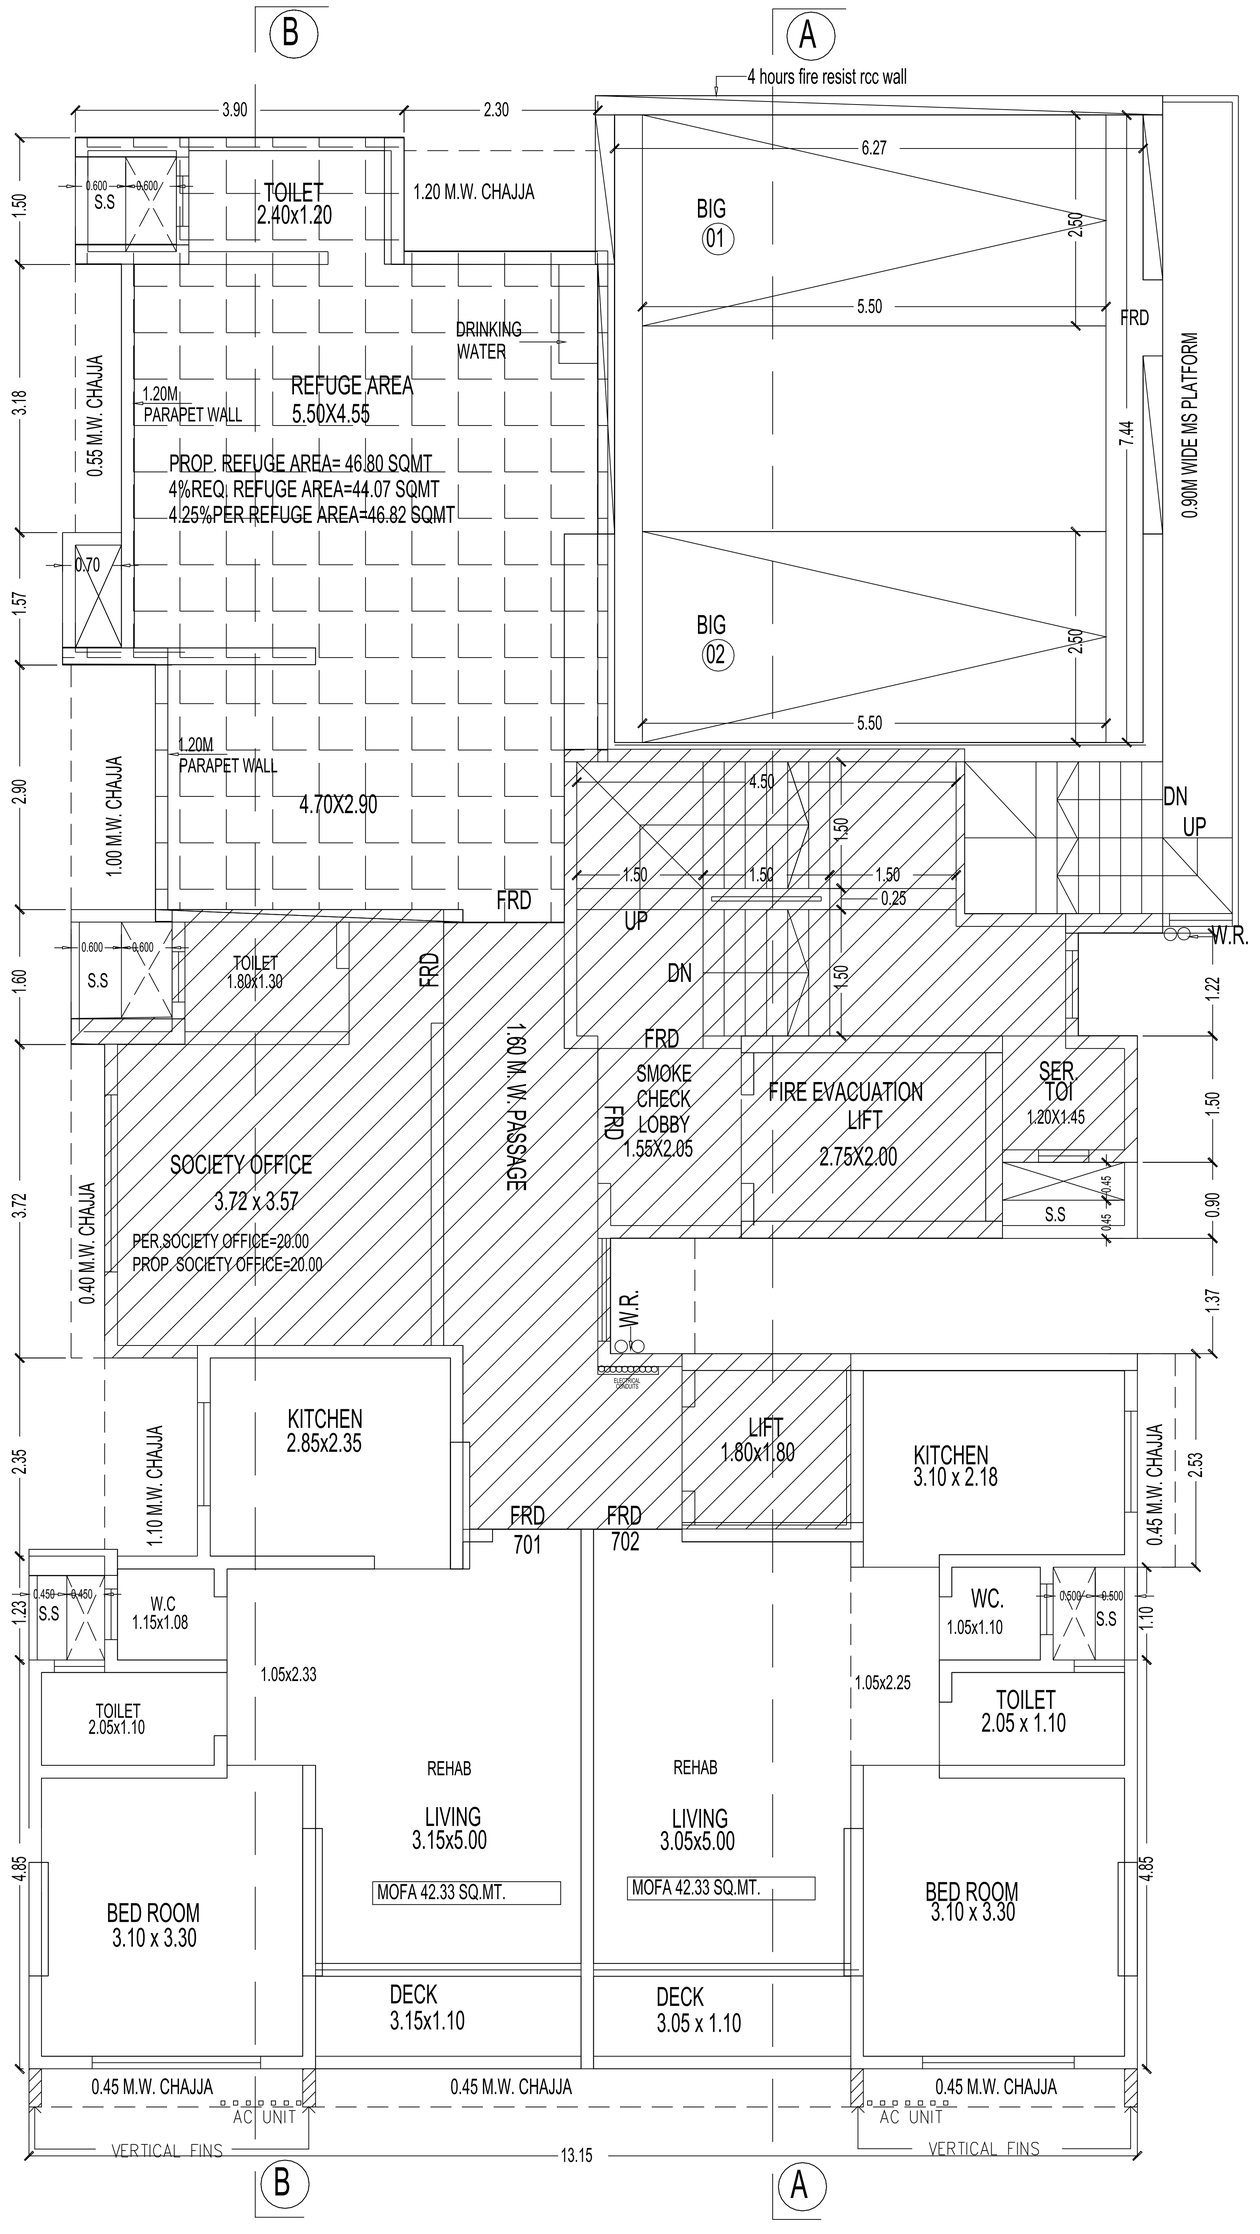


7TH FLOOR PLAN

SCALE - 1:100

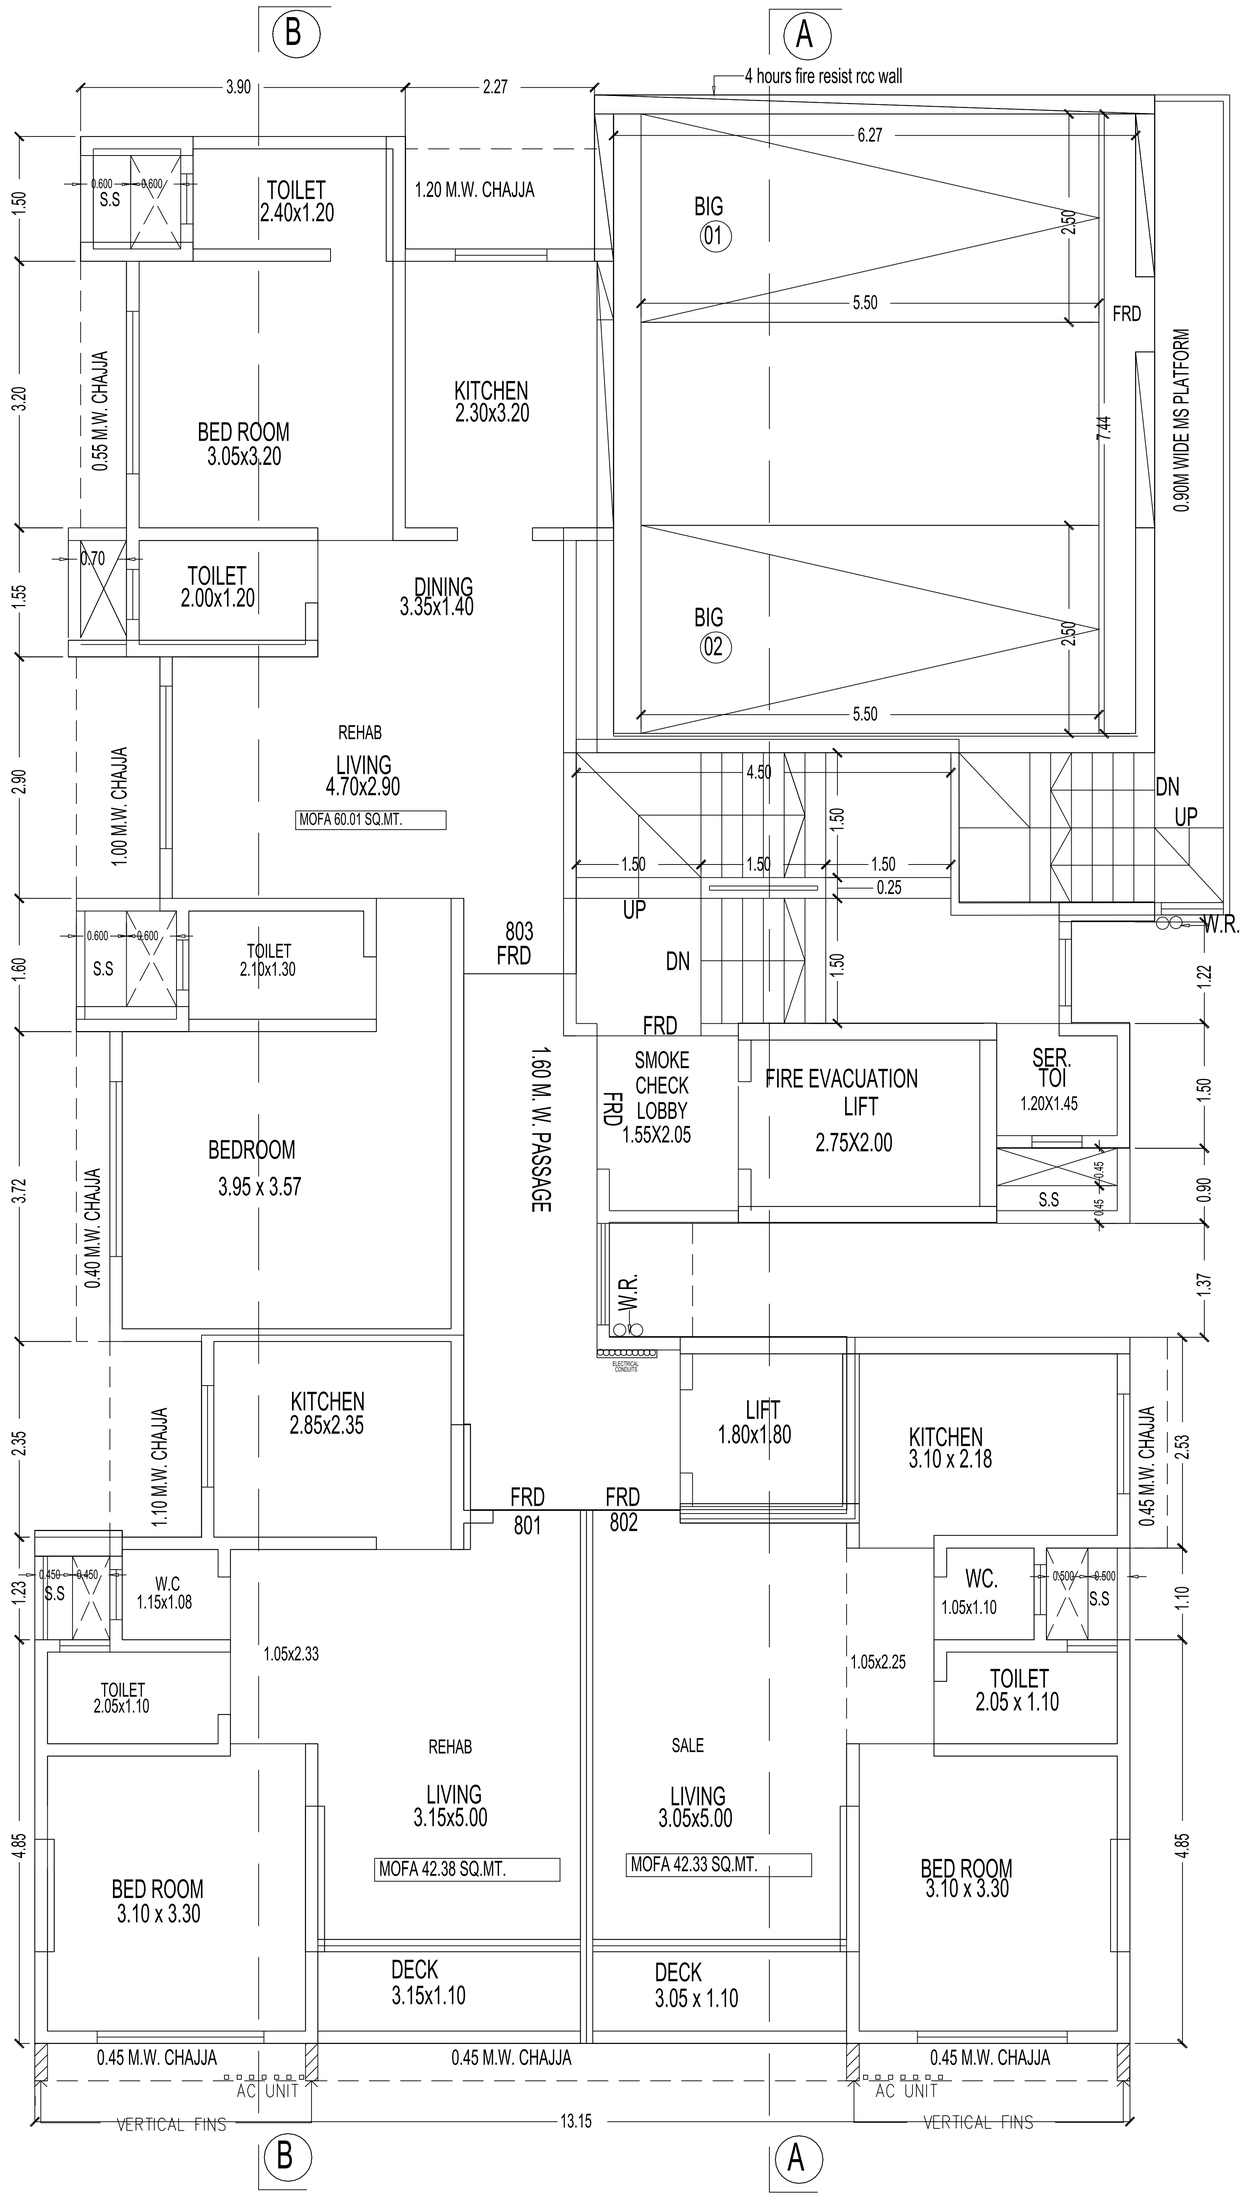


8TH FLOOR PLAN

SCALE - 1:100

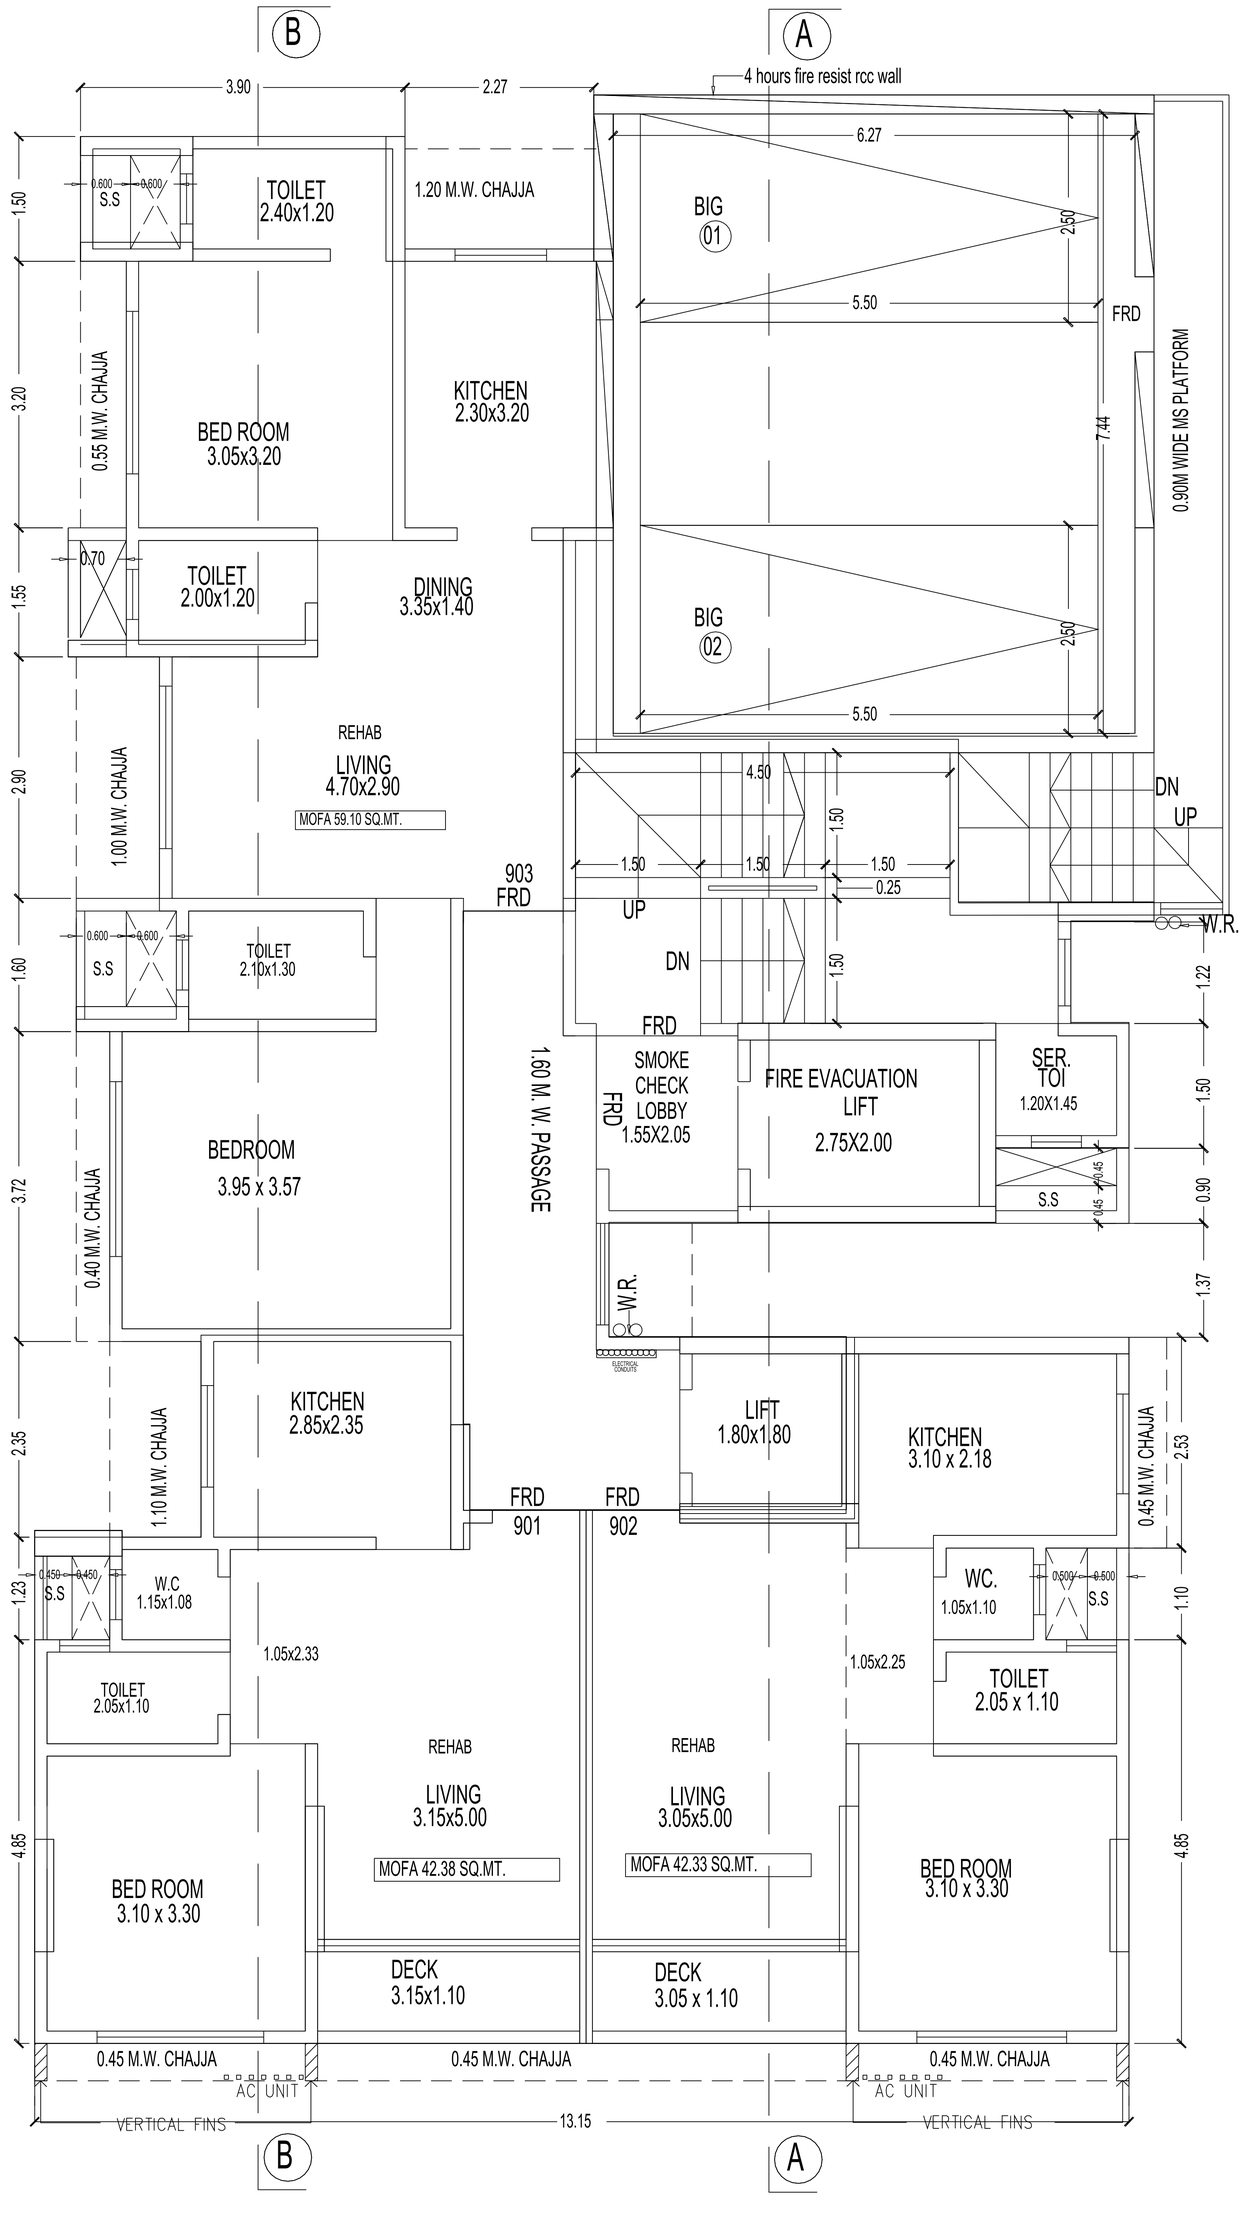


9TH FLOOR PLAN

SCALE - 1:100

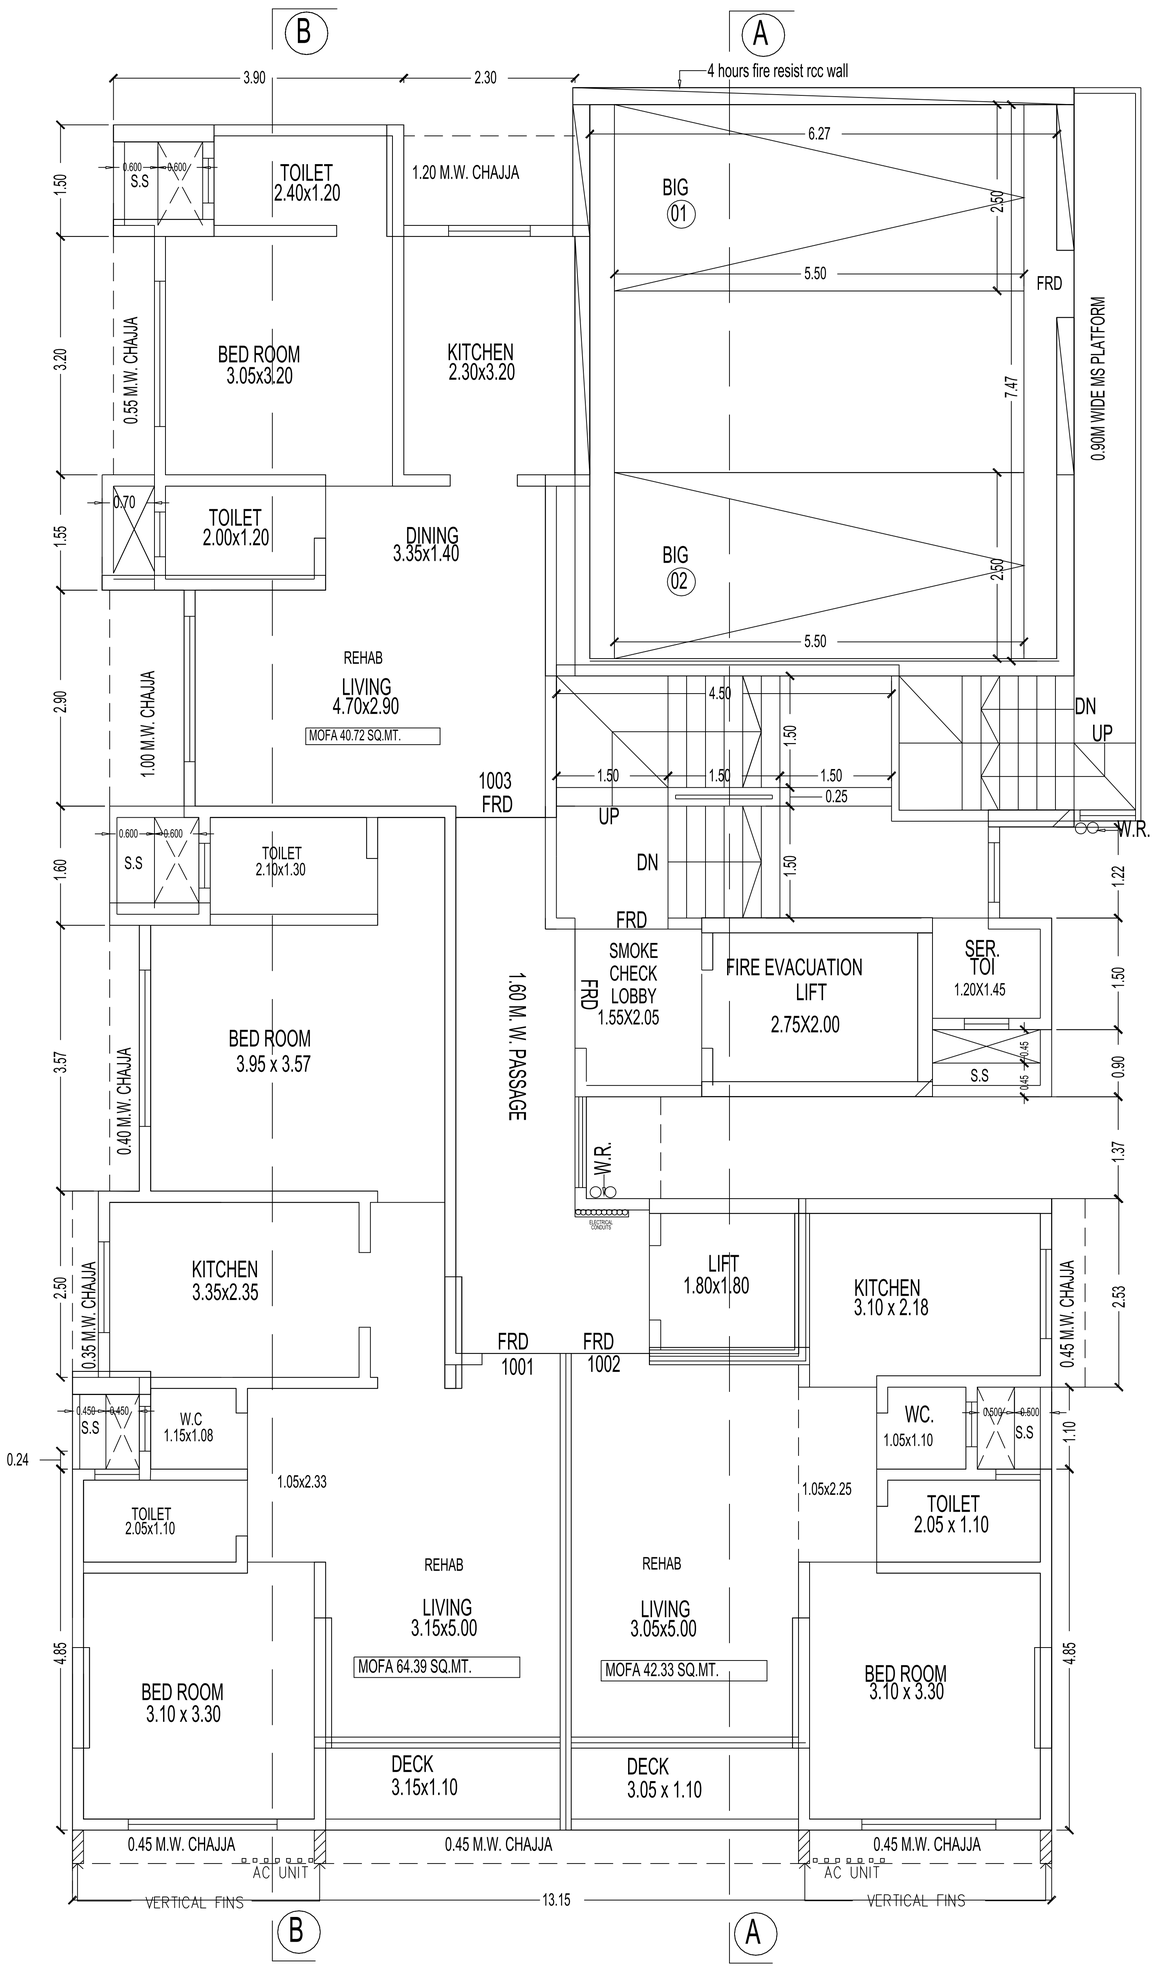


10TH FLOOR PLAN

SCALE - 1:100

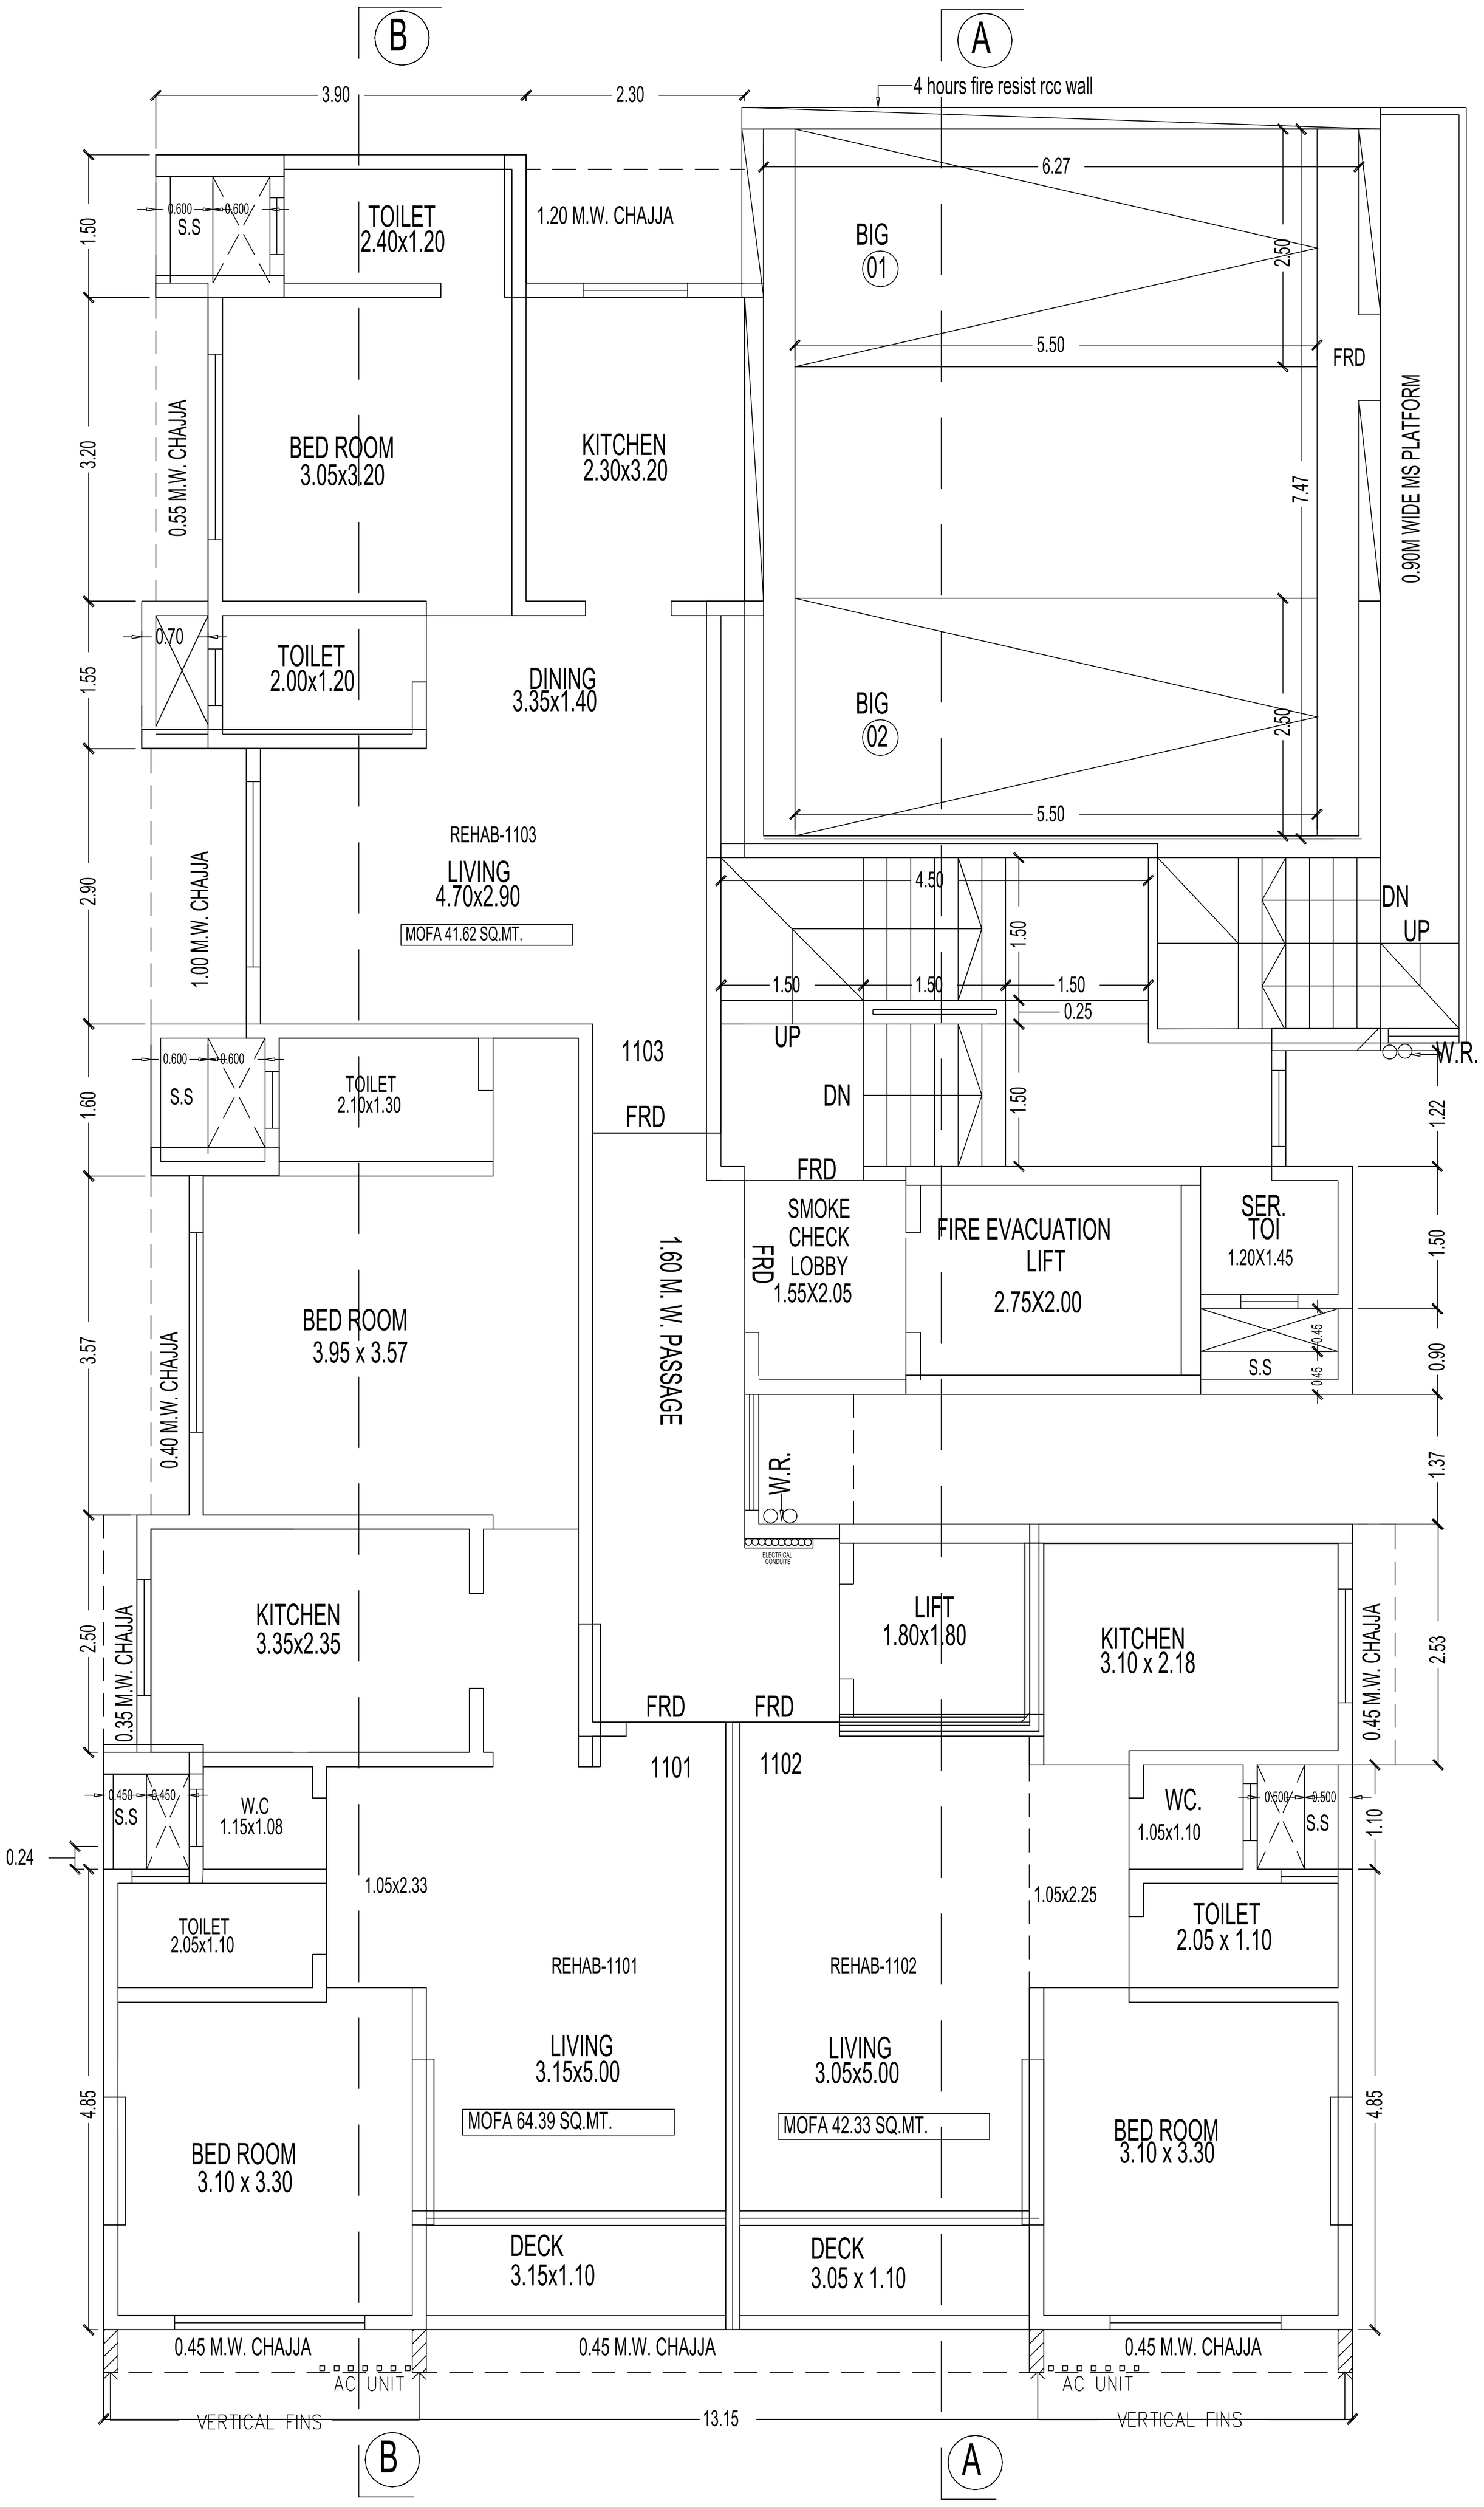


11TH FLOOR PLAN

SCALE - 1:100

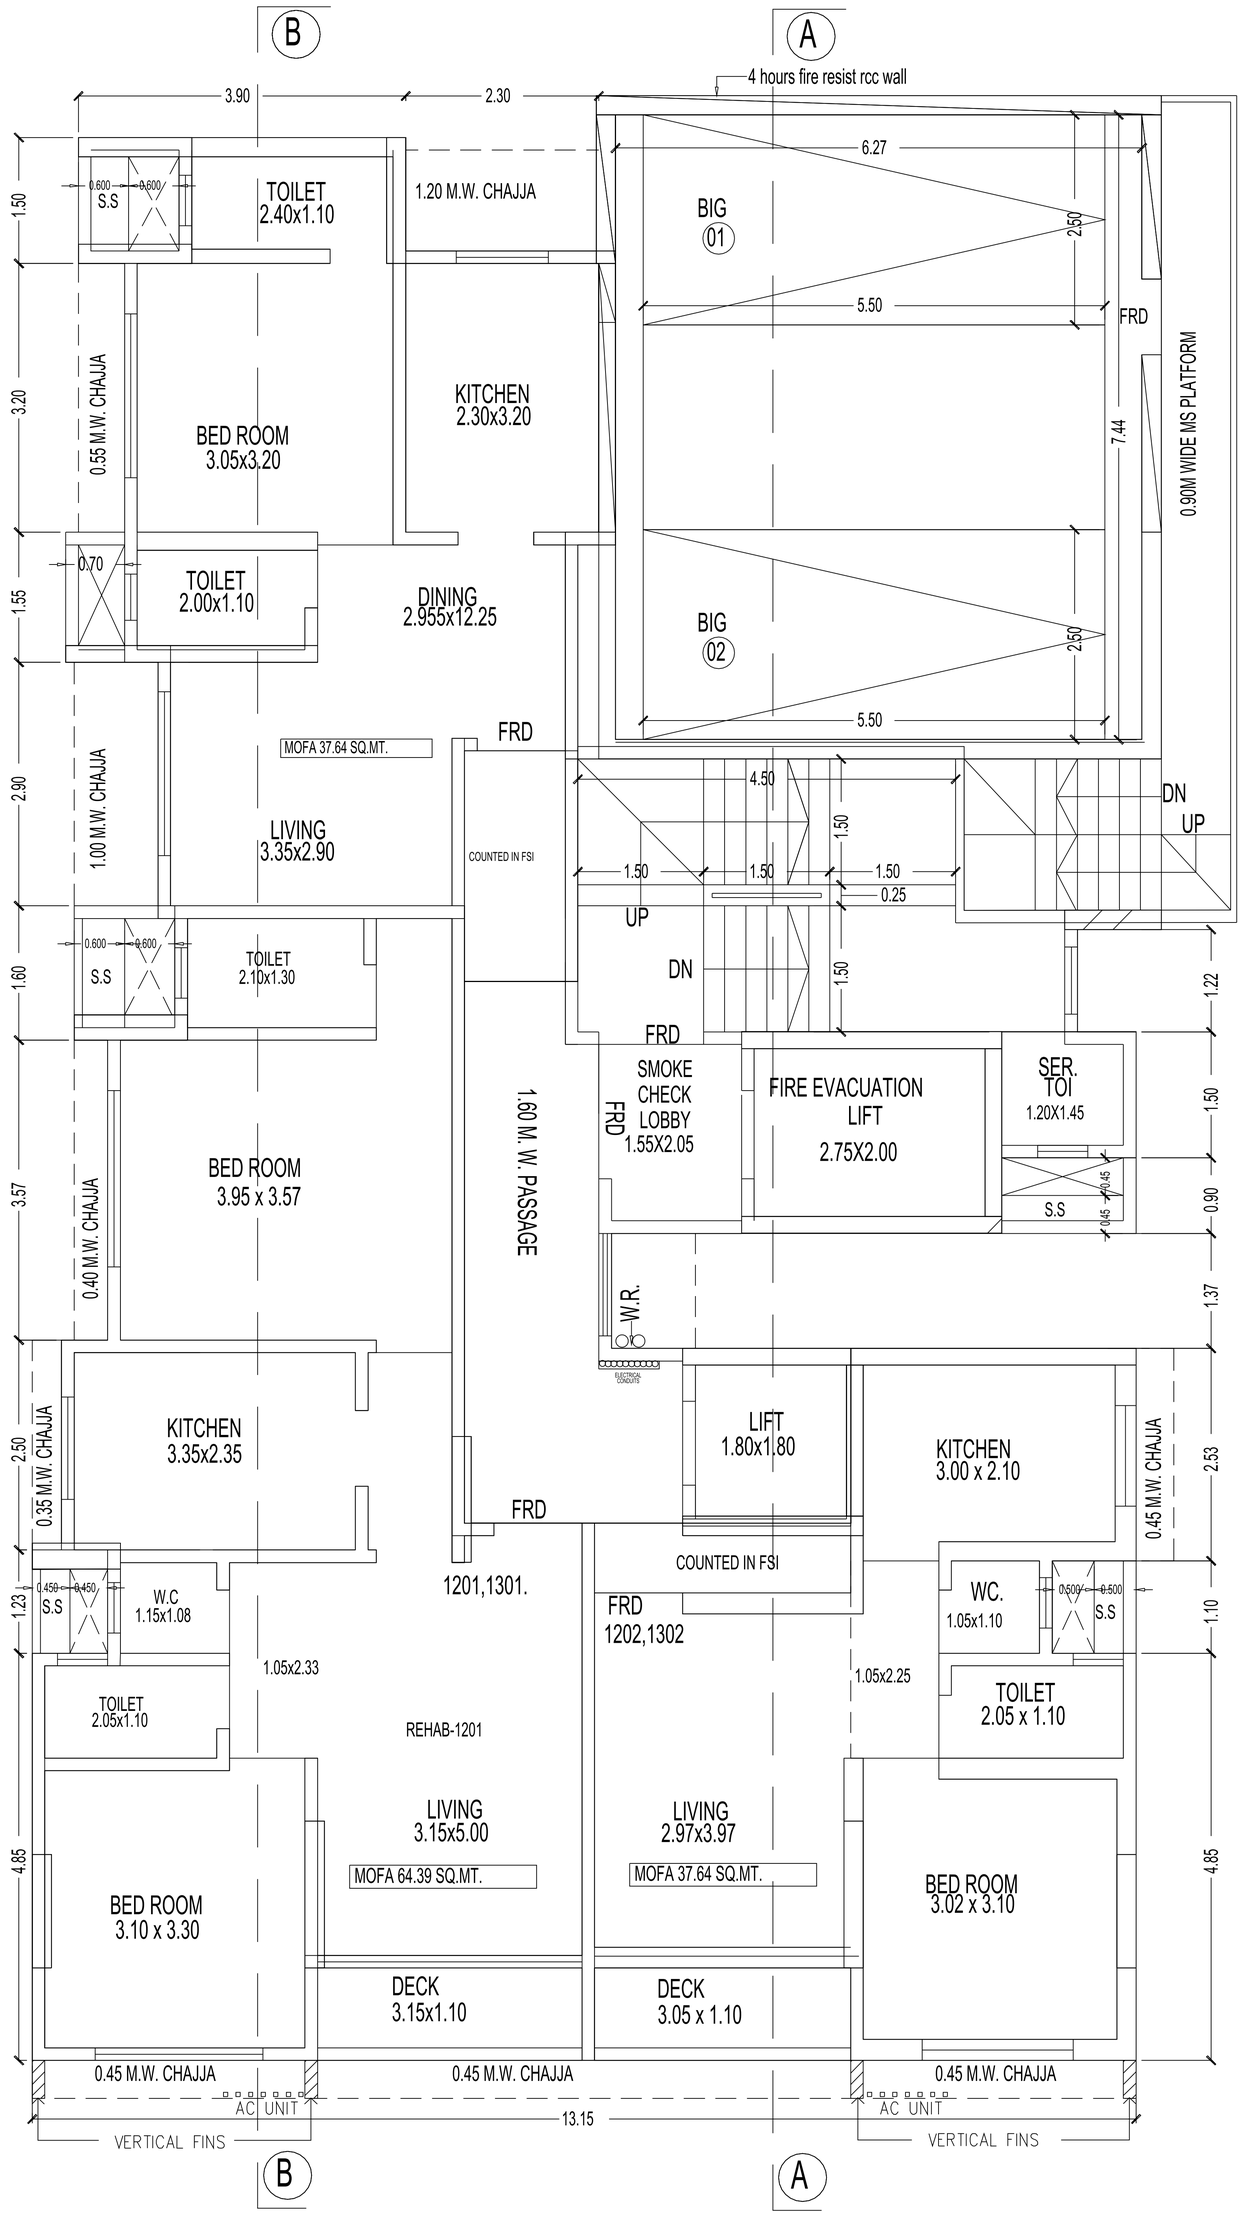

12TH,13TH FLOOR PLAN

SCALE - 1:100

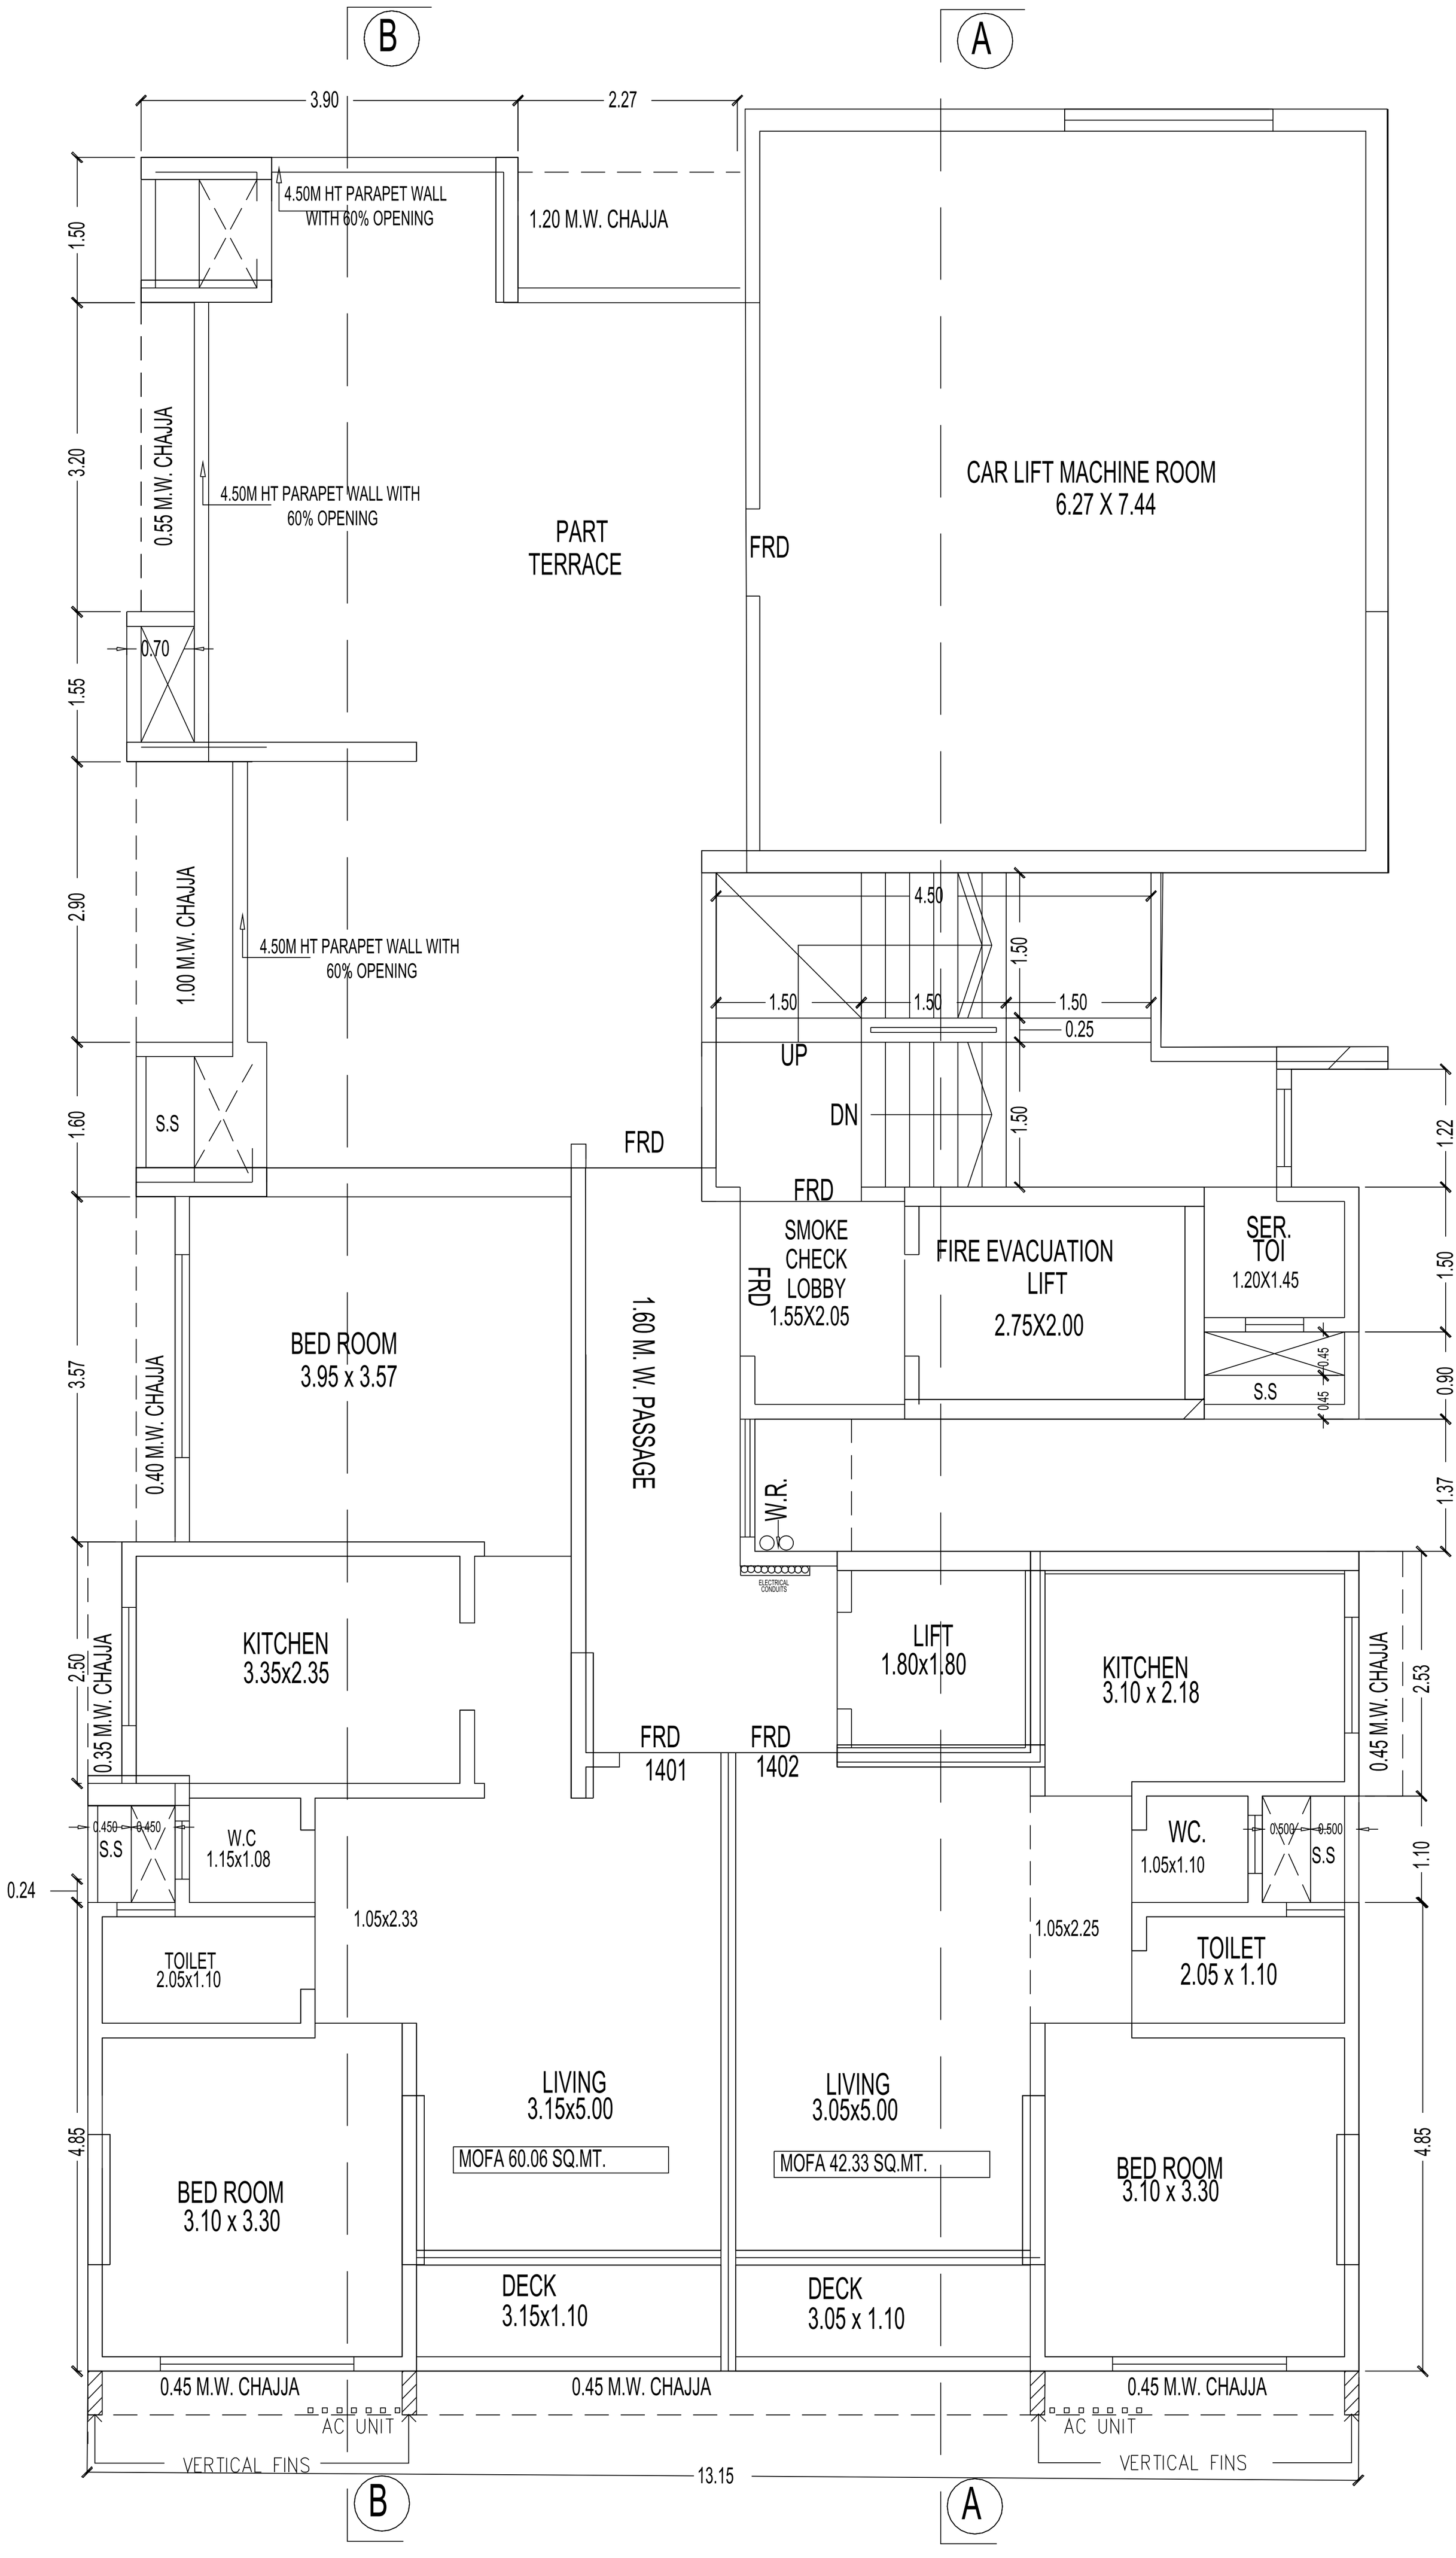

14TH(PART) FLOOR PLAN

SCALE - 1:100