
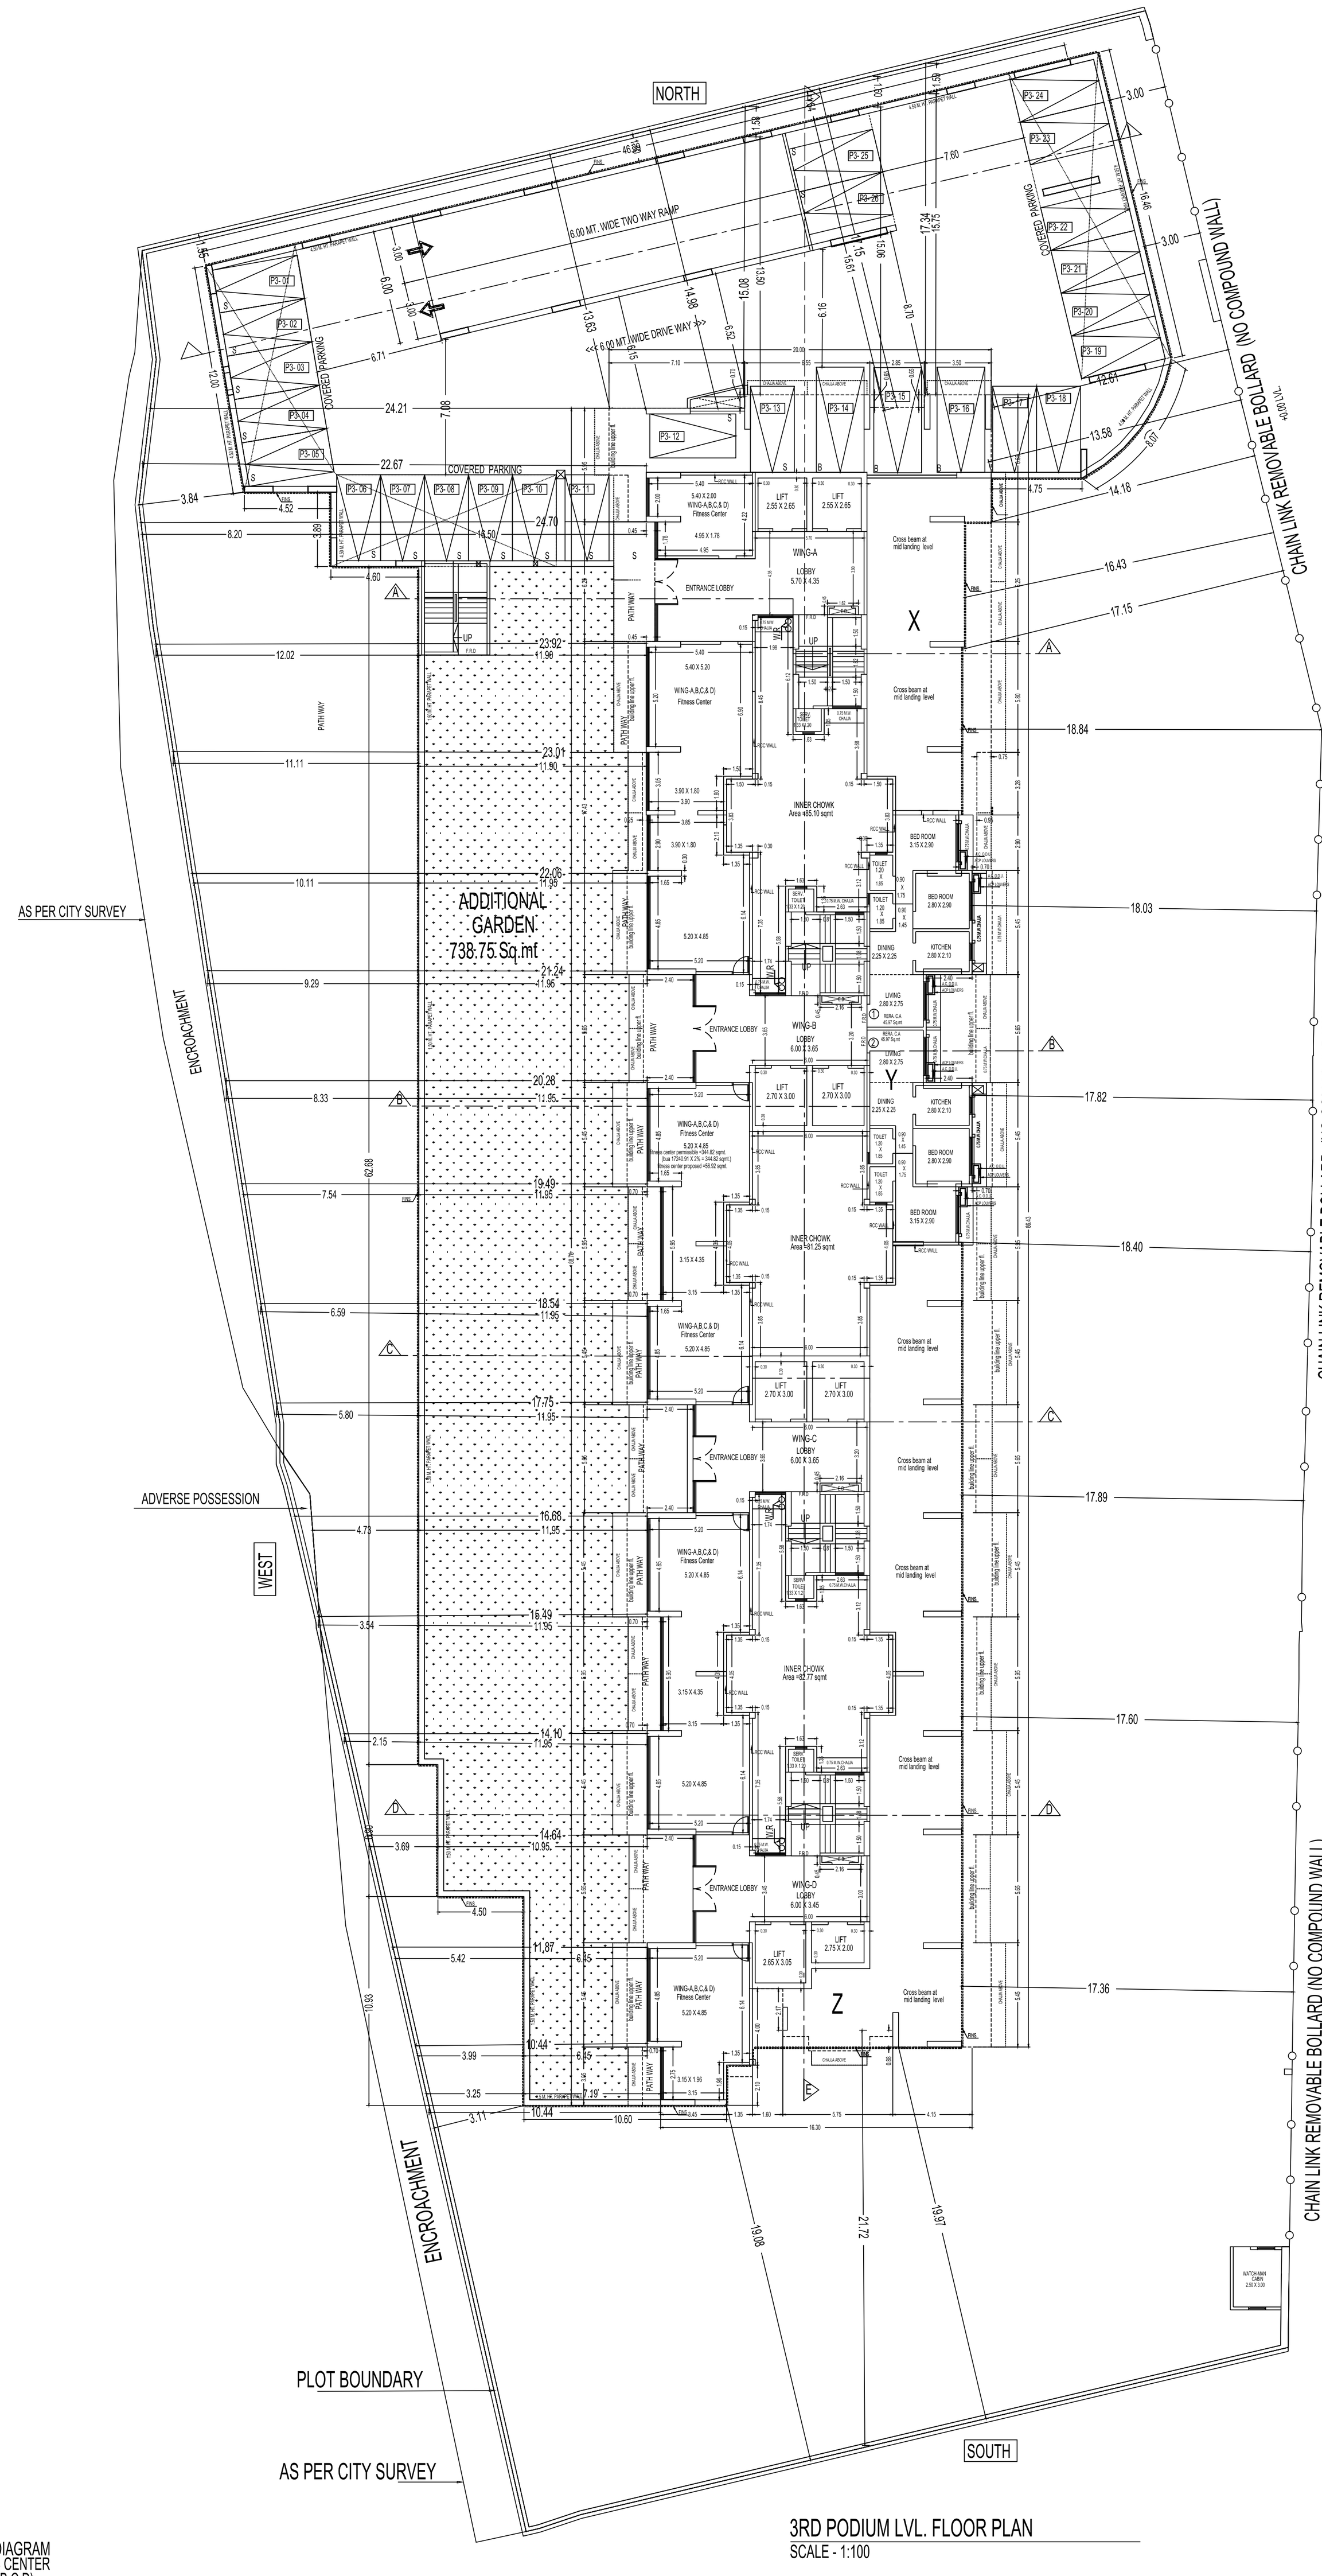



AREA DIAGRAM
FITNESS CENTER
(Wing-A ,B,C,D)
SCALE - 1:100

3RD PODIUM LVL. FLOOR PLAN
SCALE - 1:100

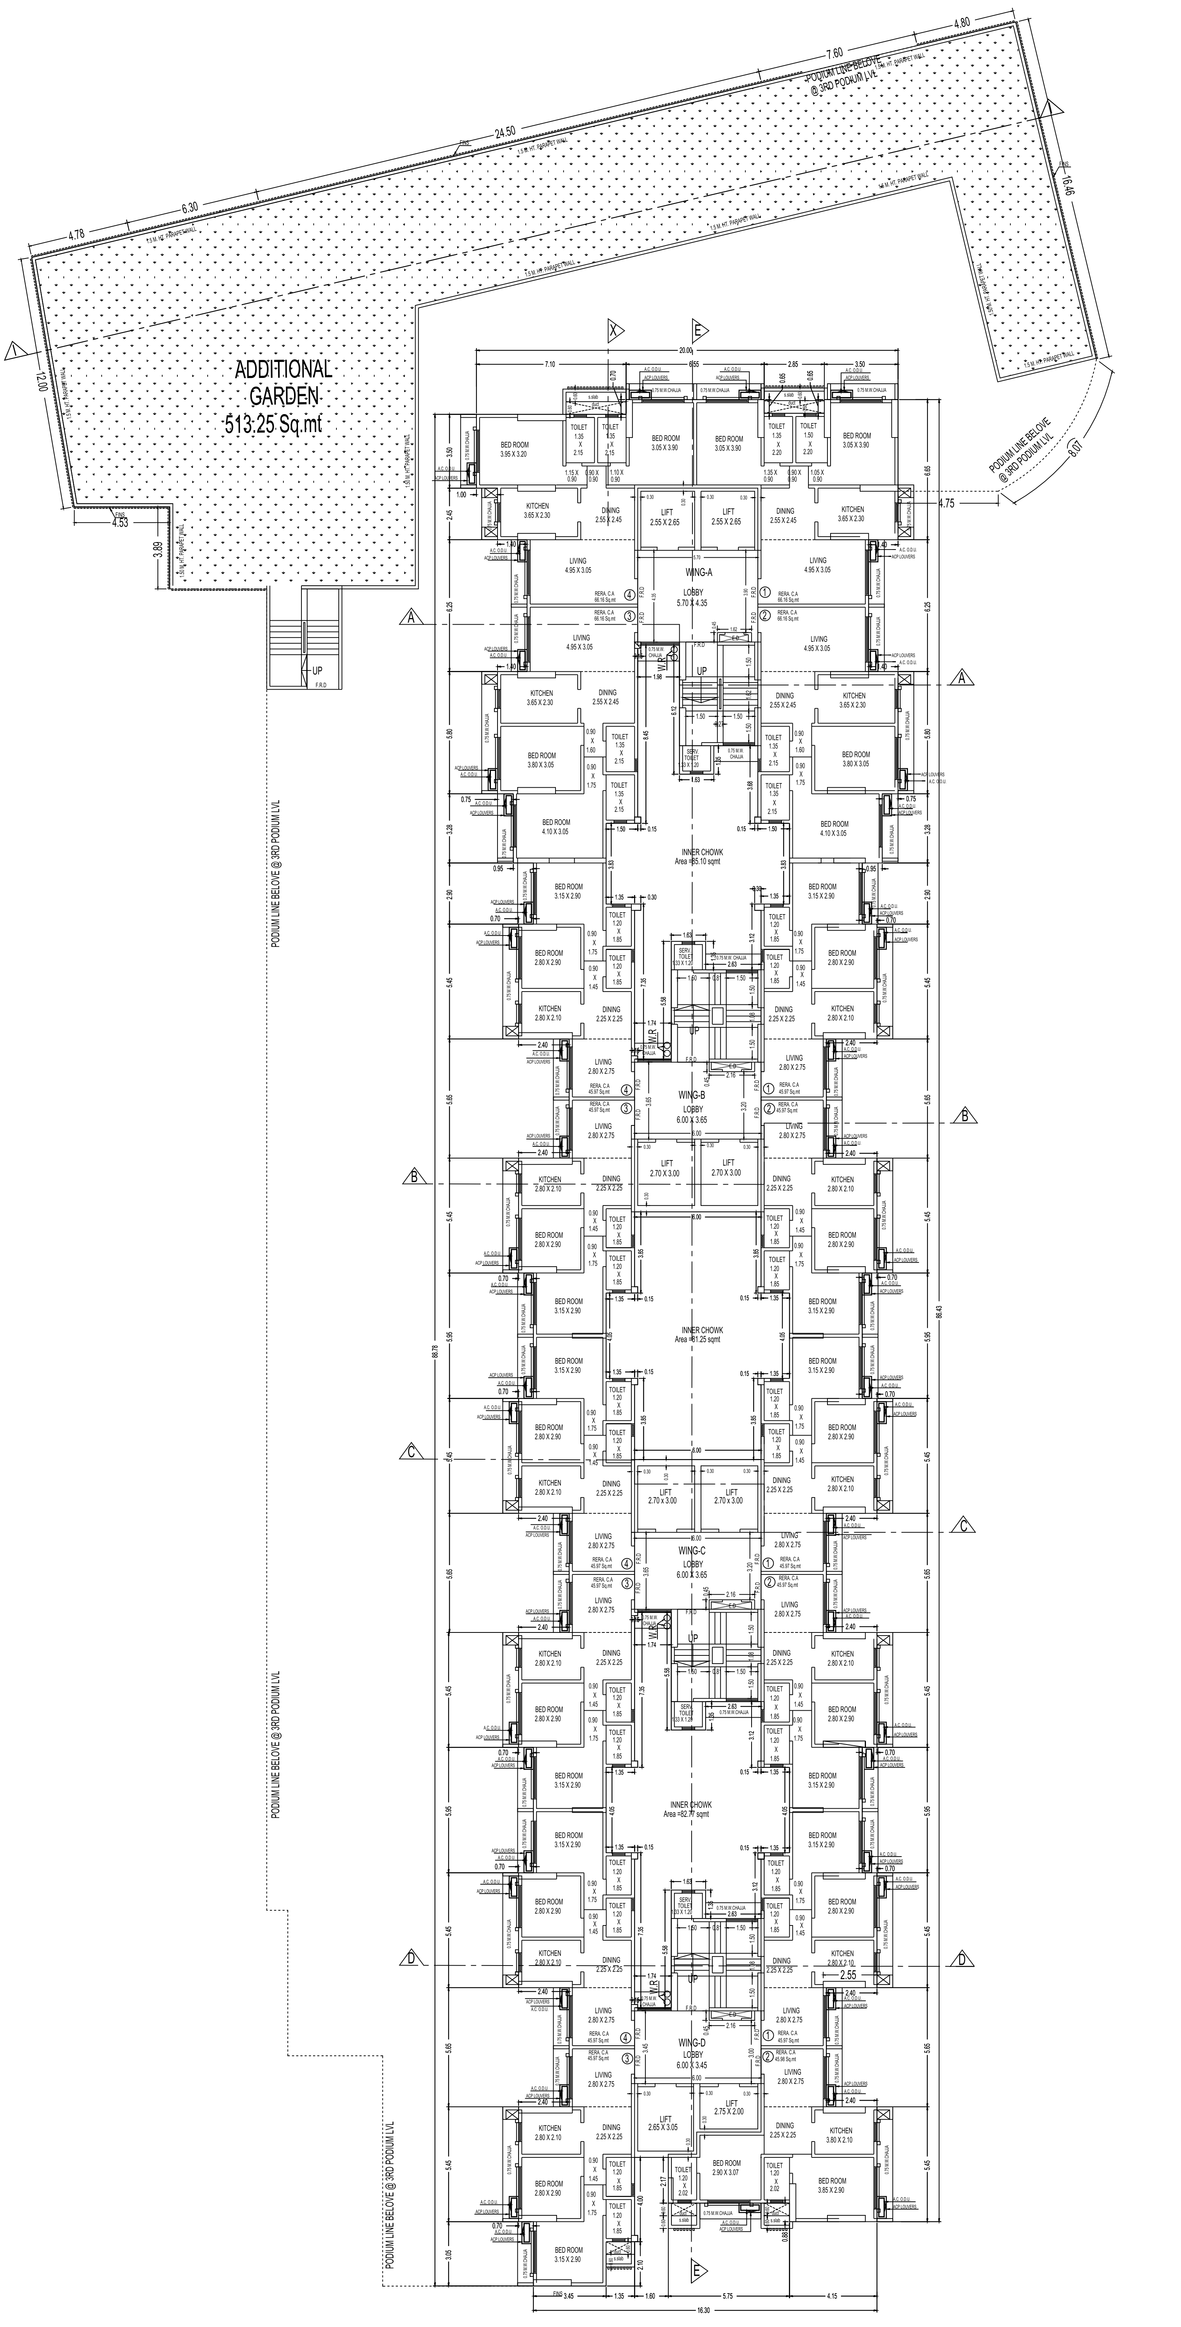


4TH FLOOR PLAN

SCALE - 1:100

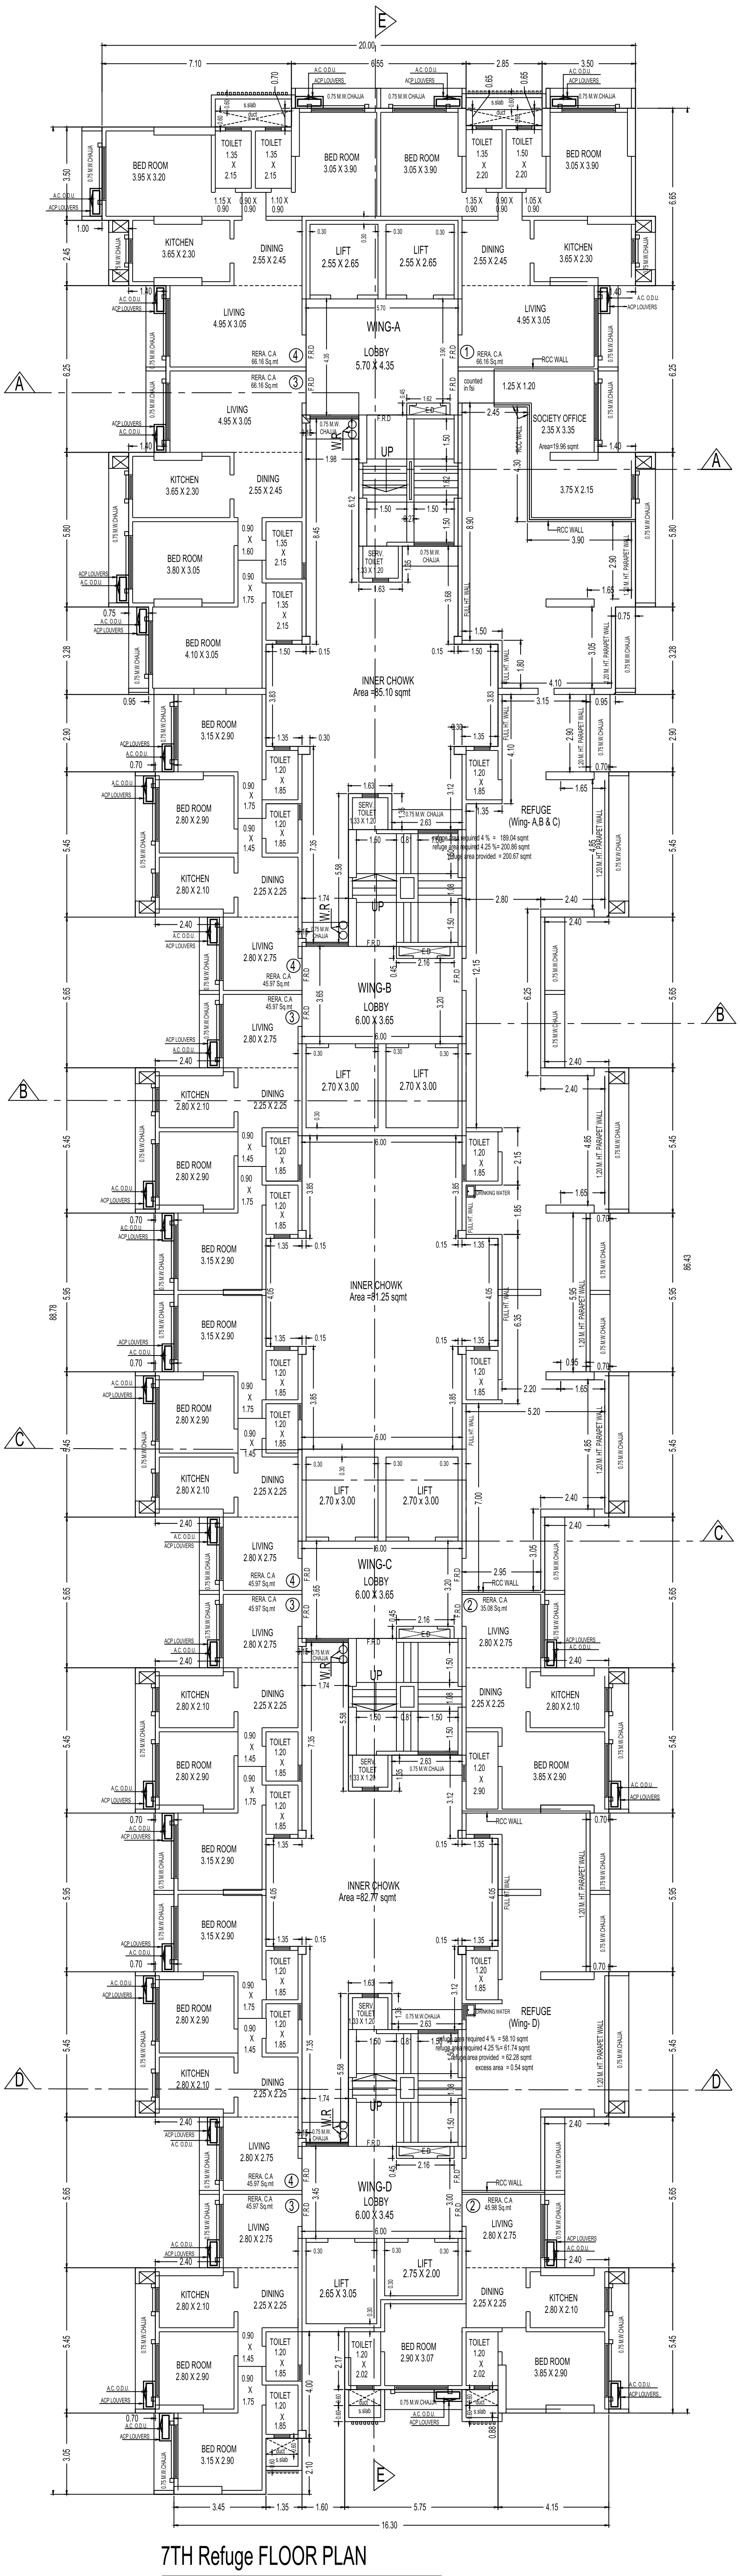


7TH Refuge FLOOR PLAN

SCALE - 1:100

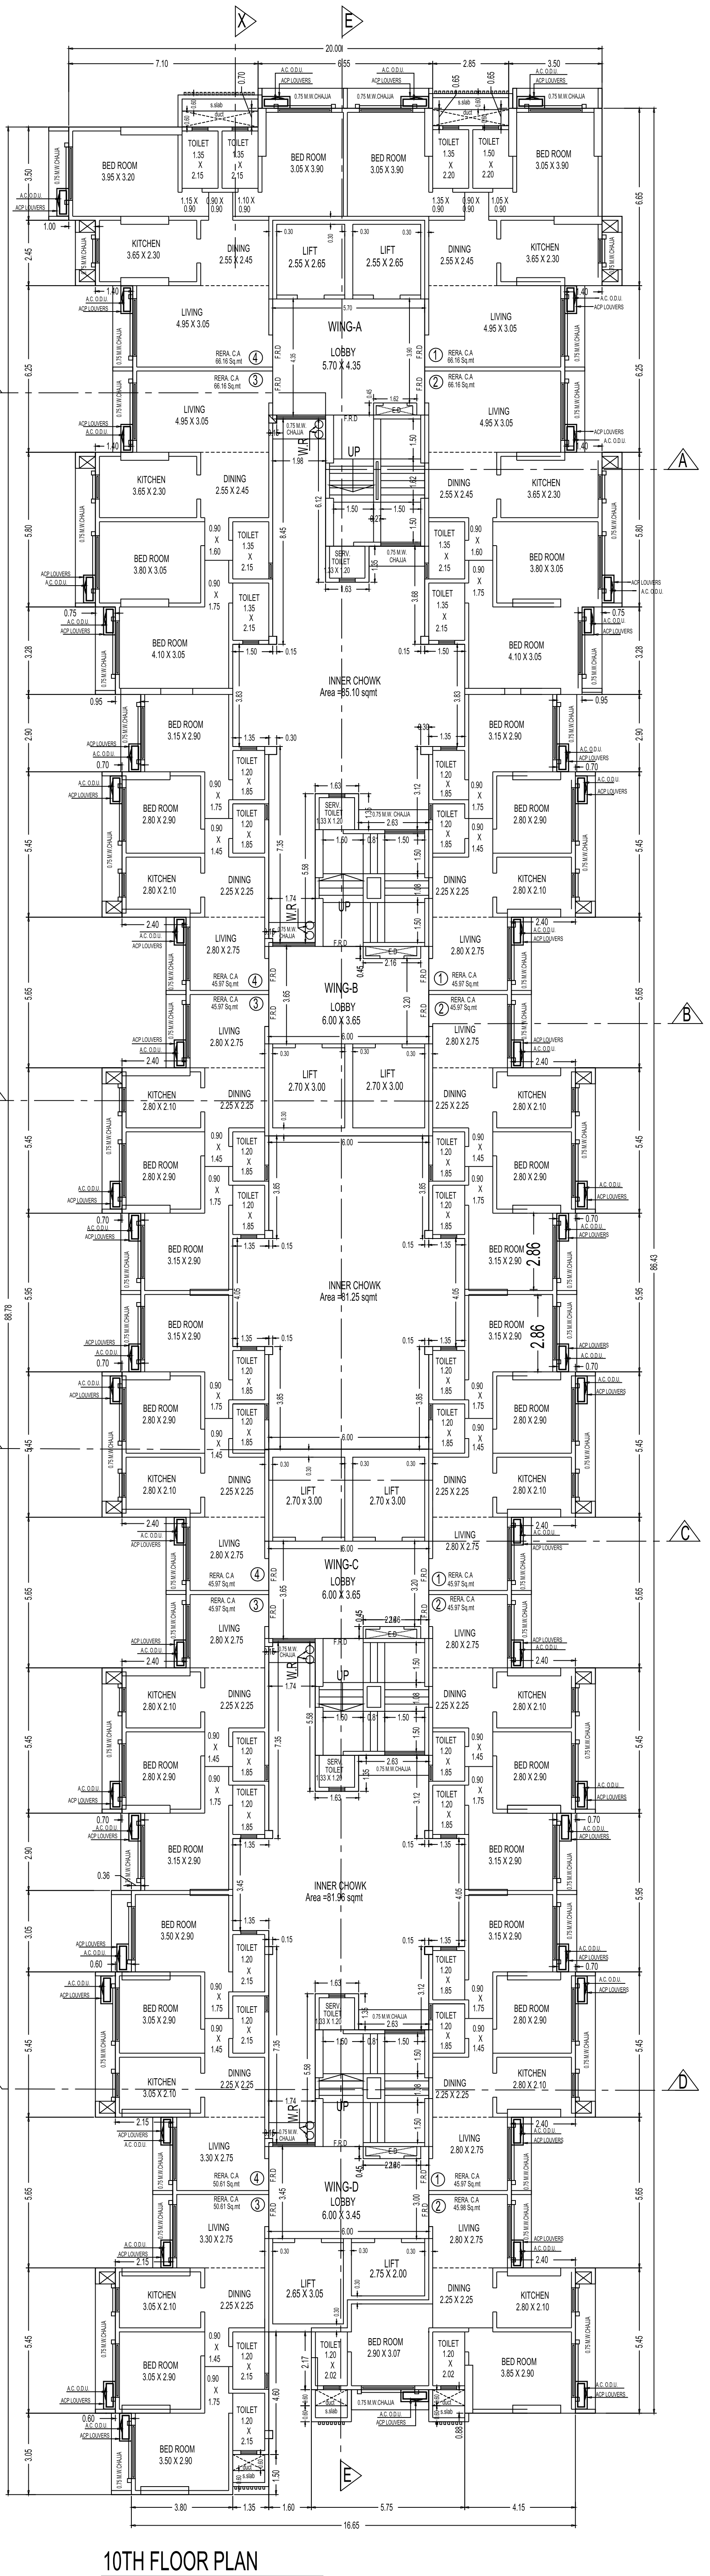


10TH FLOOR PLAN

SCALE - 1:100

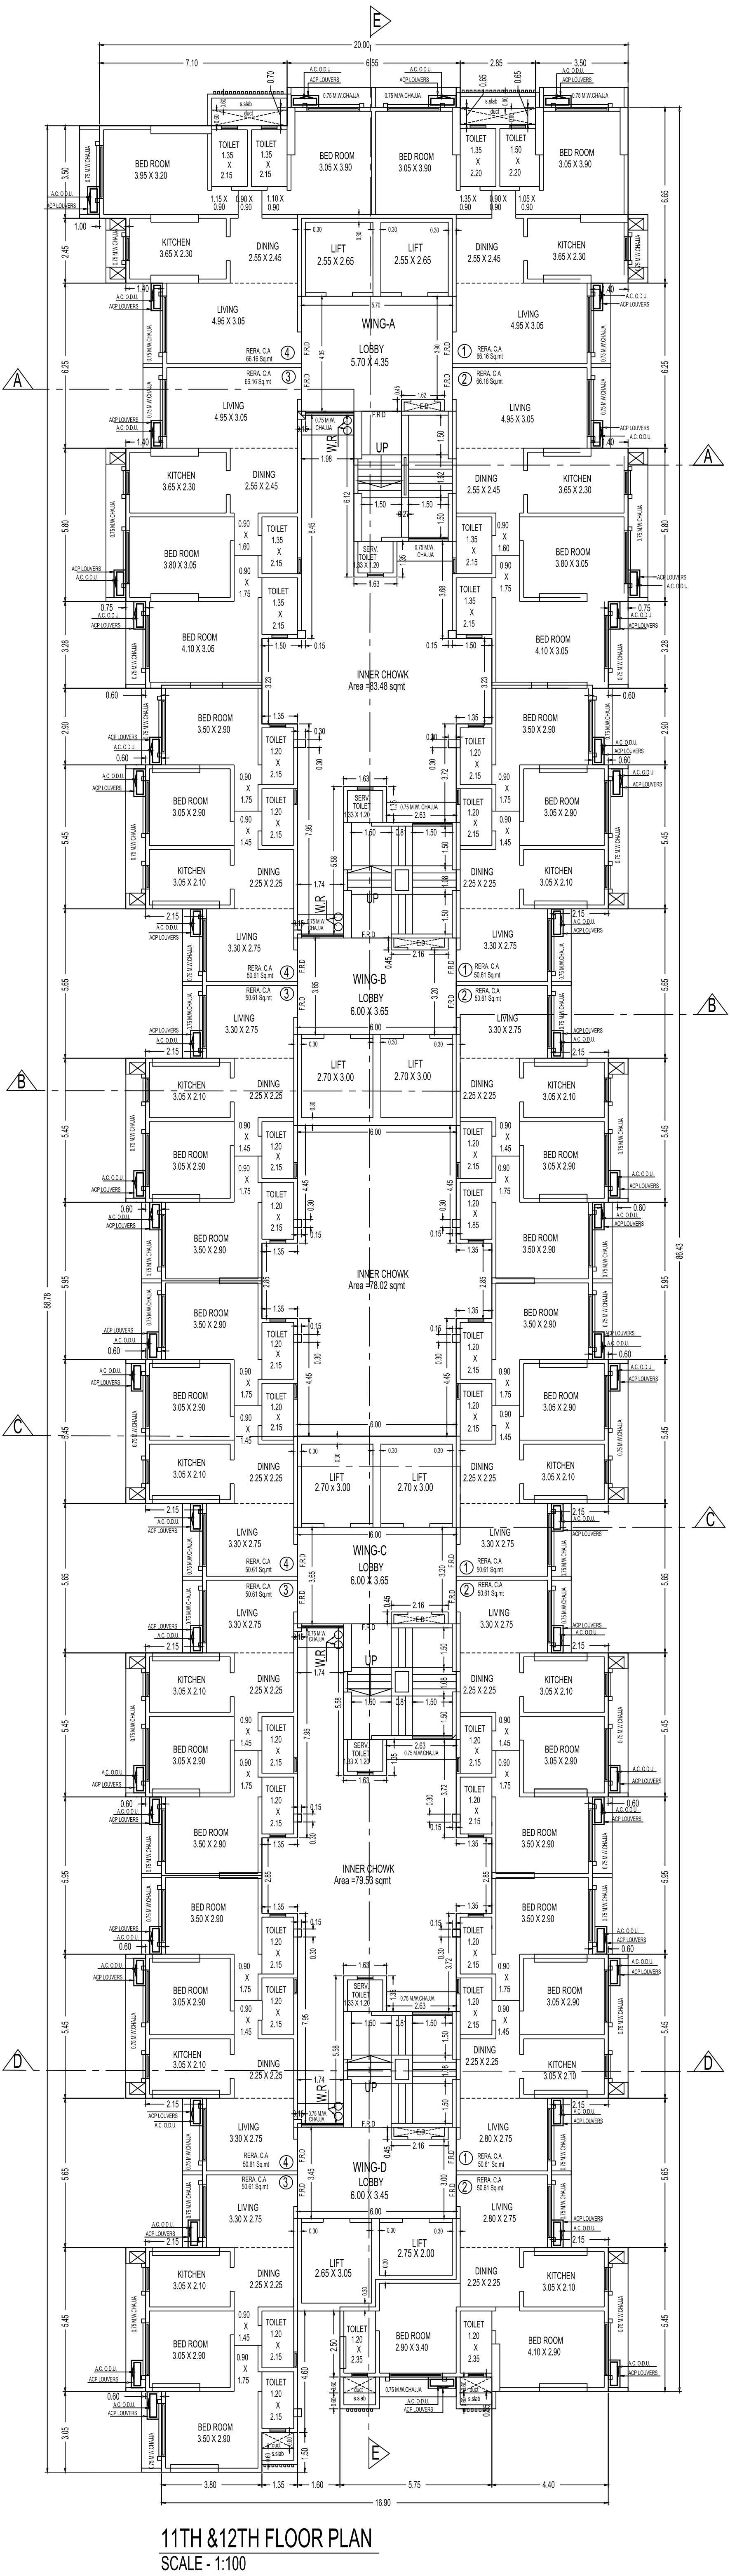


11TH &12TH FLOOR PLAN

SCALE - 1:100

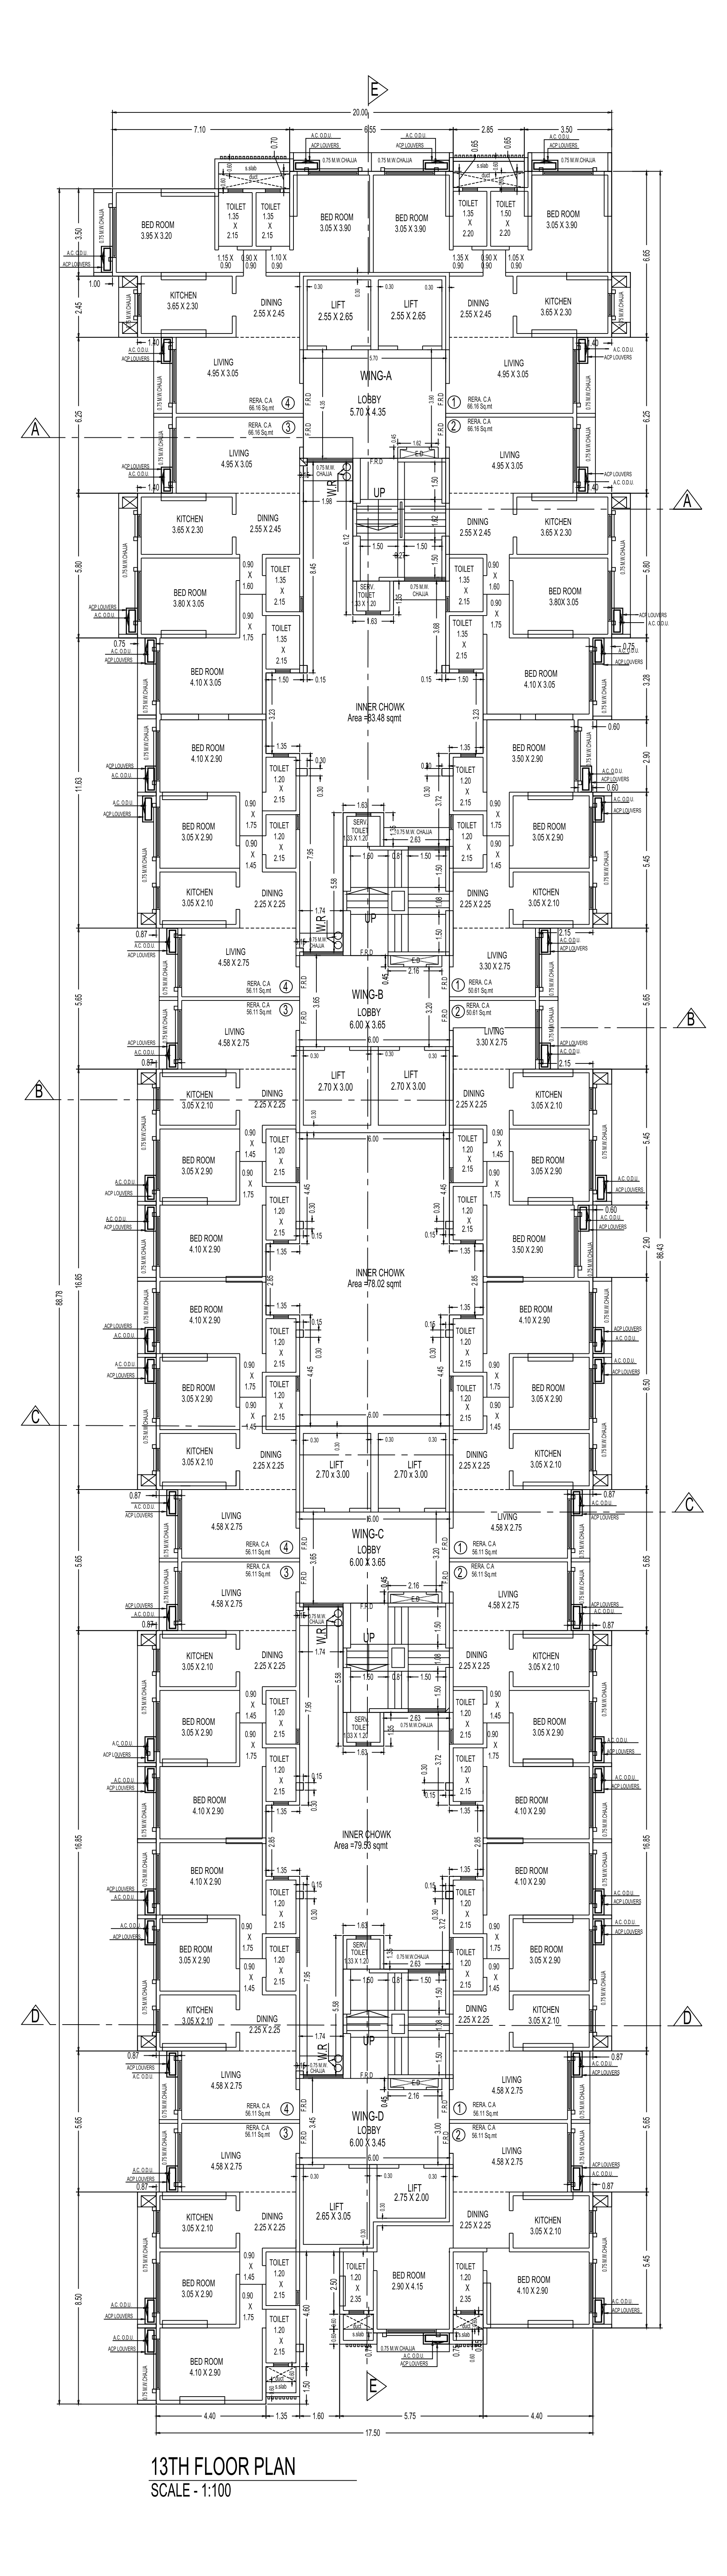


13TH FLOOR PLAN

SCALE - 1:100

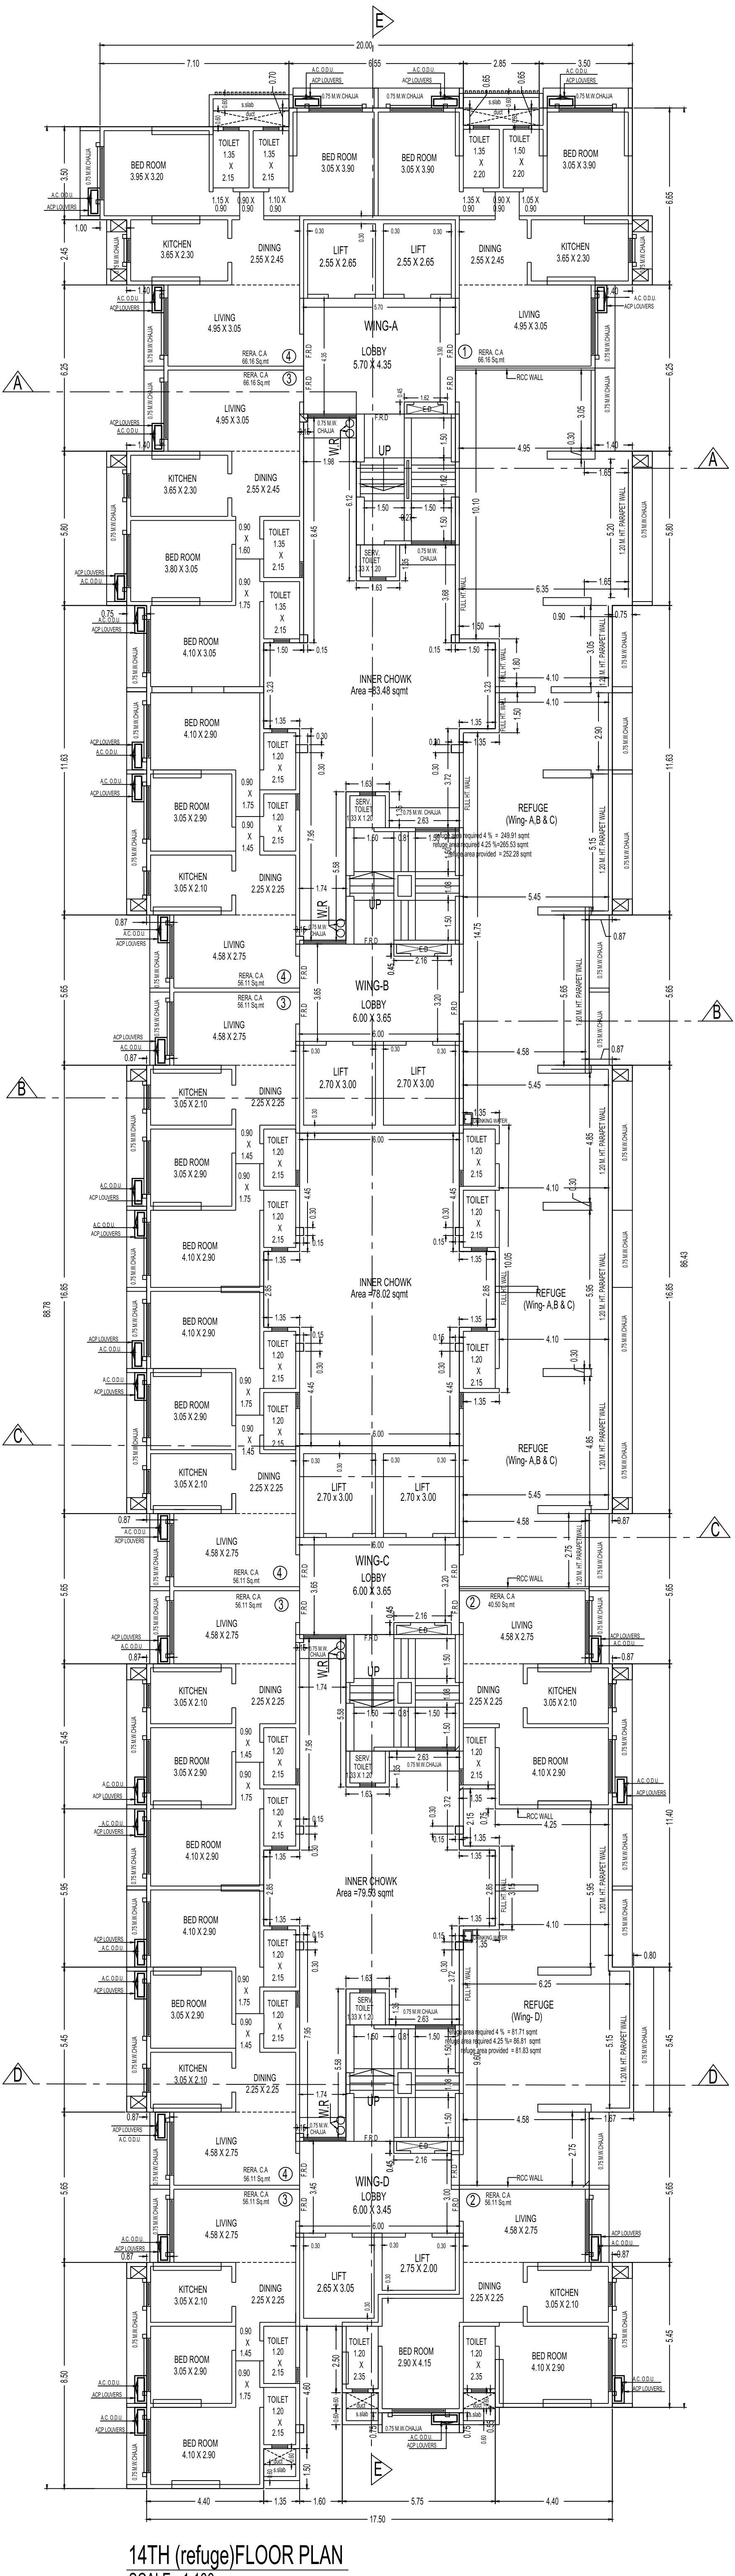


14TH (refuge)FLOOR PLAN


SCALE - 1:100

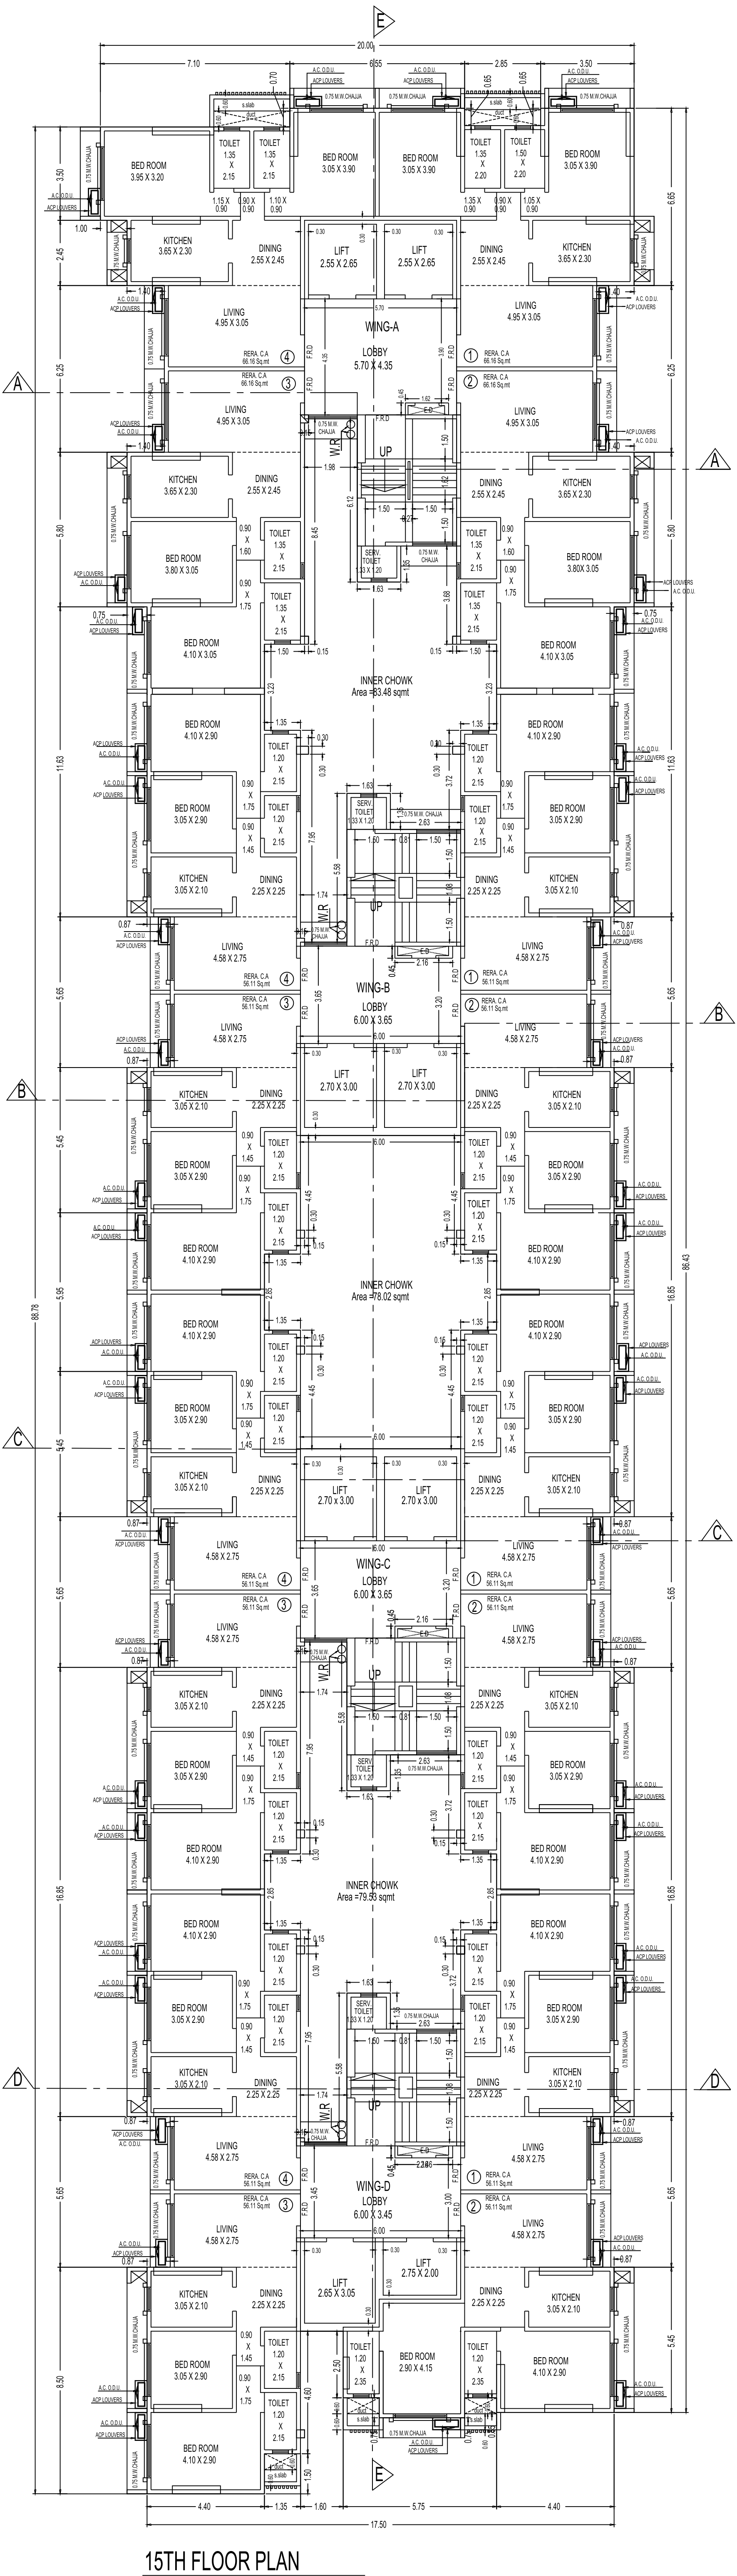

15TH FLOOR PLAN


SCALE - 1:100

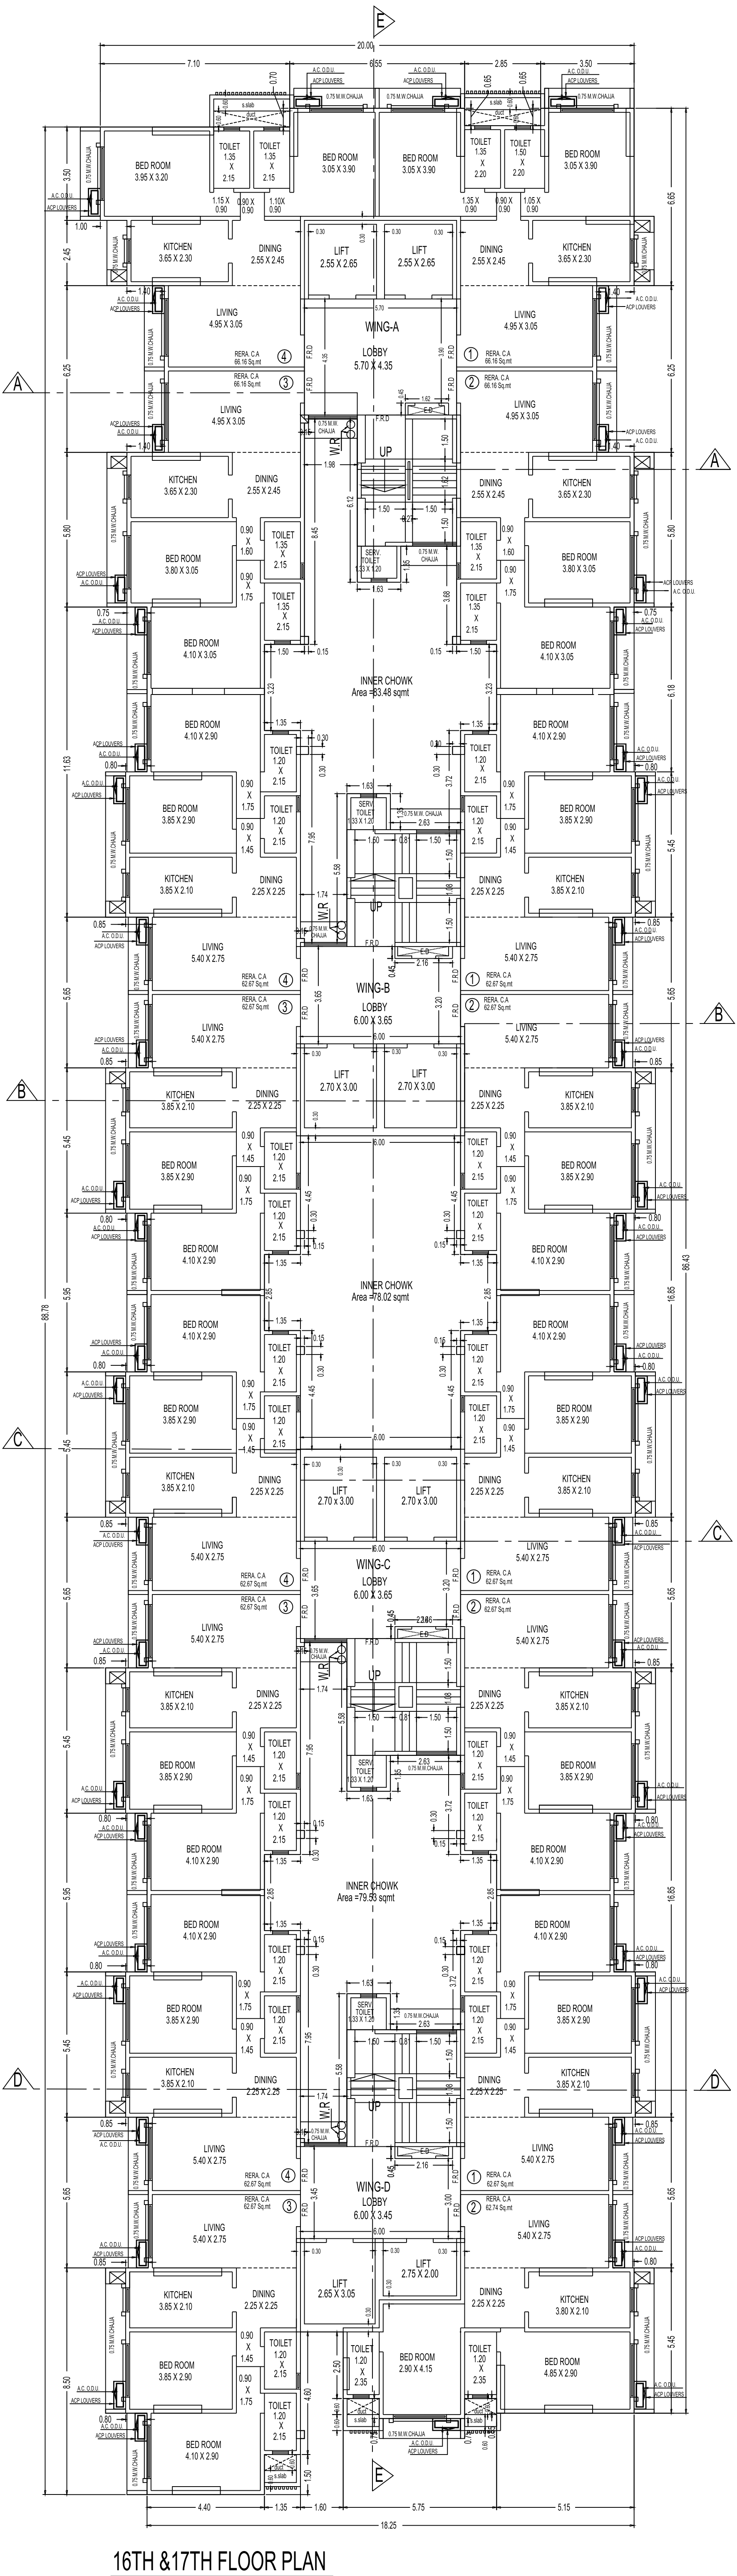
WING-A
LOBBY
5.70 X 4.35
WING-B
LOBBY
6.00 X 3.65
WING-C
LOBBY
6.00 X 3.65
WING-D
LOBBY
6.00 X 3.45
INNER CHOWK
Area =83.48 sqmt
INNER CHOWK
Area =78.02 sqmt
INNER CHOWK
Area =79.55 sqmt
LIFT
2.55 X 2.65
LIFT
2.70 X 3.00
LIFT
2.75 X 2.00
LIFT
2.65 X 3.05
UP
DN
W.R
SERV. TOILET
1.00 X 1.20
KITCHEN
3.65 X 2.30
KITCHEN
3.85 X 2.10
KITCHEN
3.80 X 2.10
DINING
2.55 X 2.45
DINING
2.25 X 2.25
LIVING
4.95 X 3.05
LIVING
5.40 X 2.75
BED ROOM
3.95 X 3.20
BED ROOM
3.05 X 3.90
BED ROOM
3.80 X 3.05
BED ROOM
4.10 X 3.05
BED ROOM
4.10 X 2.90
BED ROOM
3.85 X 2.90
BED ROOM
2.90 X 4.15
BED ROOM
4.85 X 2.90
TOILET
1.35 X 2.15
TOILET
1.50 X 2.20
TOILET
1.20 X 2.15
TOILET
1.20 X 2.35
RERA, C.A 66.16 Sq.mt
RERA, C.A 62.67 Sq.mt
RERA, C.A 62.74 Sq.mt
A.C. O.D.U
ACP LOUVERS
0.75 M.W. CHAJJA
F.R.D
E.D
18.25
88.78
16TH &17TH FLOOR PLAN
SCALE - 1:100

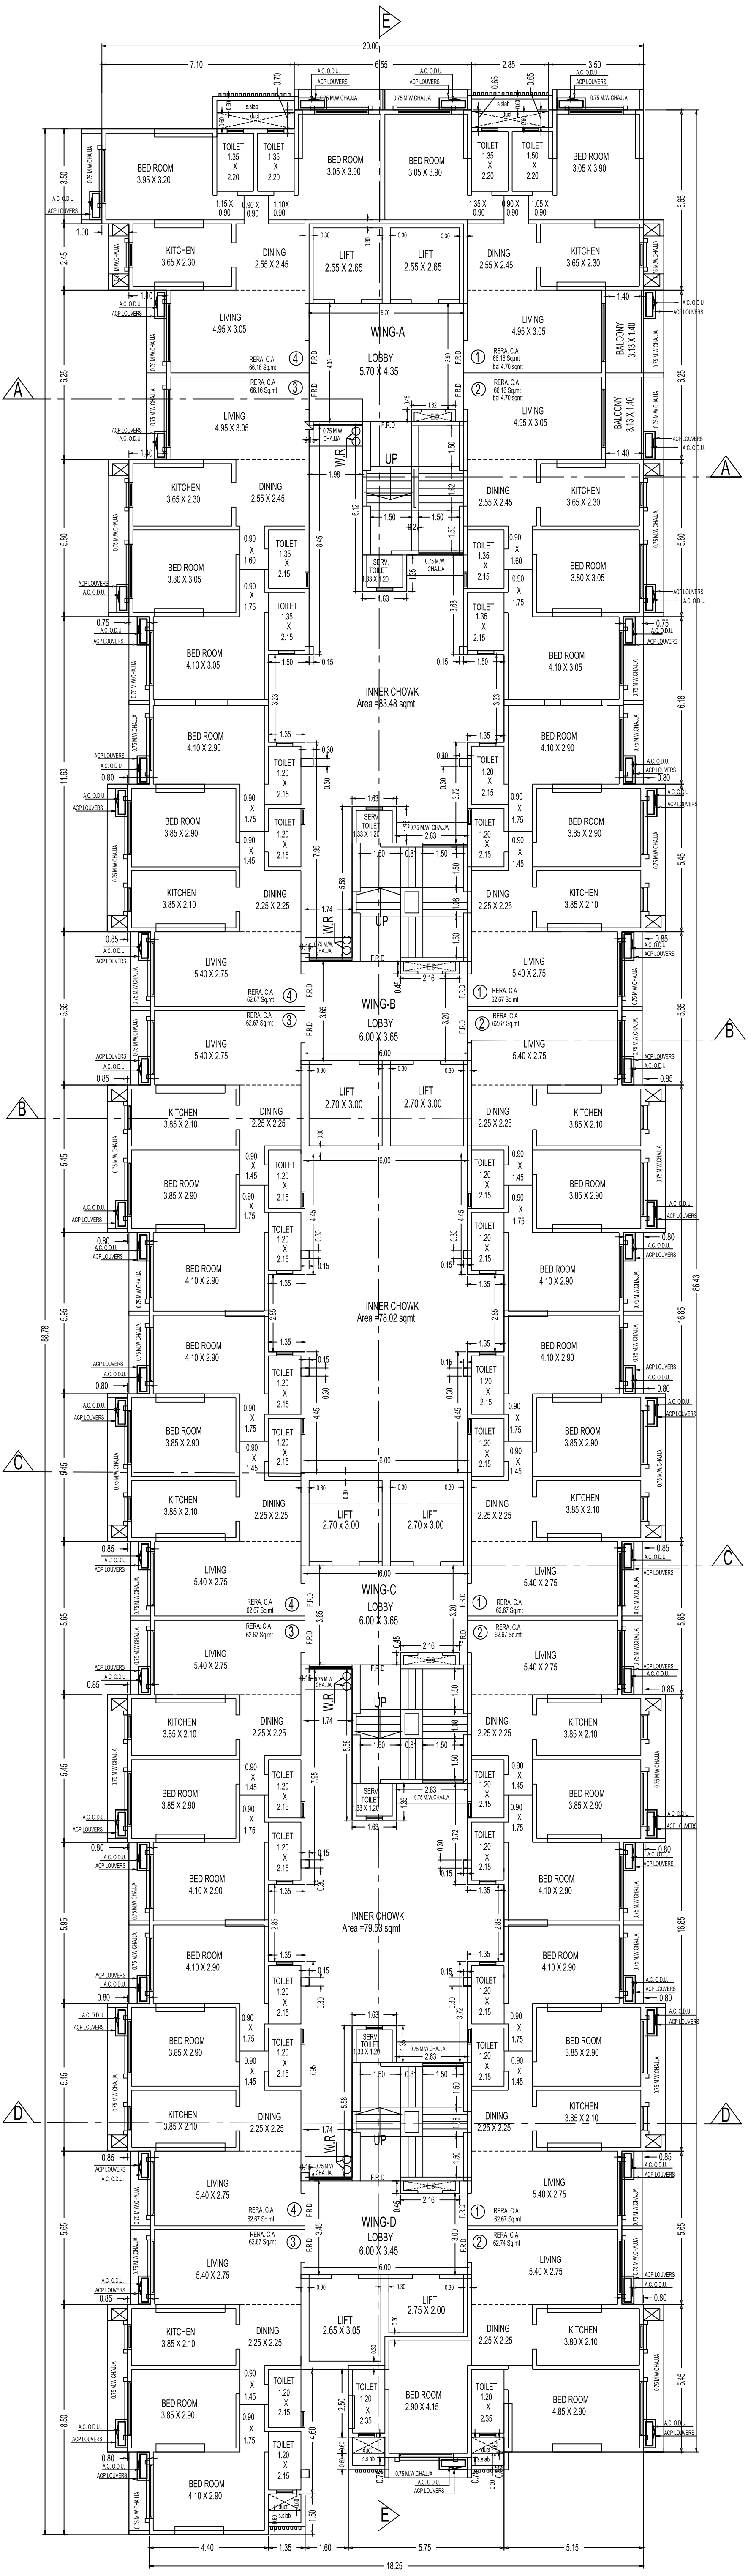

18TH&19TH FLOOR PLAN

SCALE - 1:100

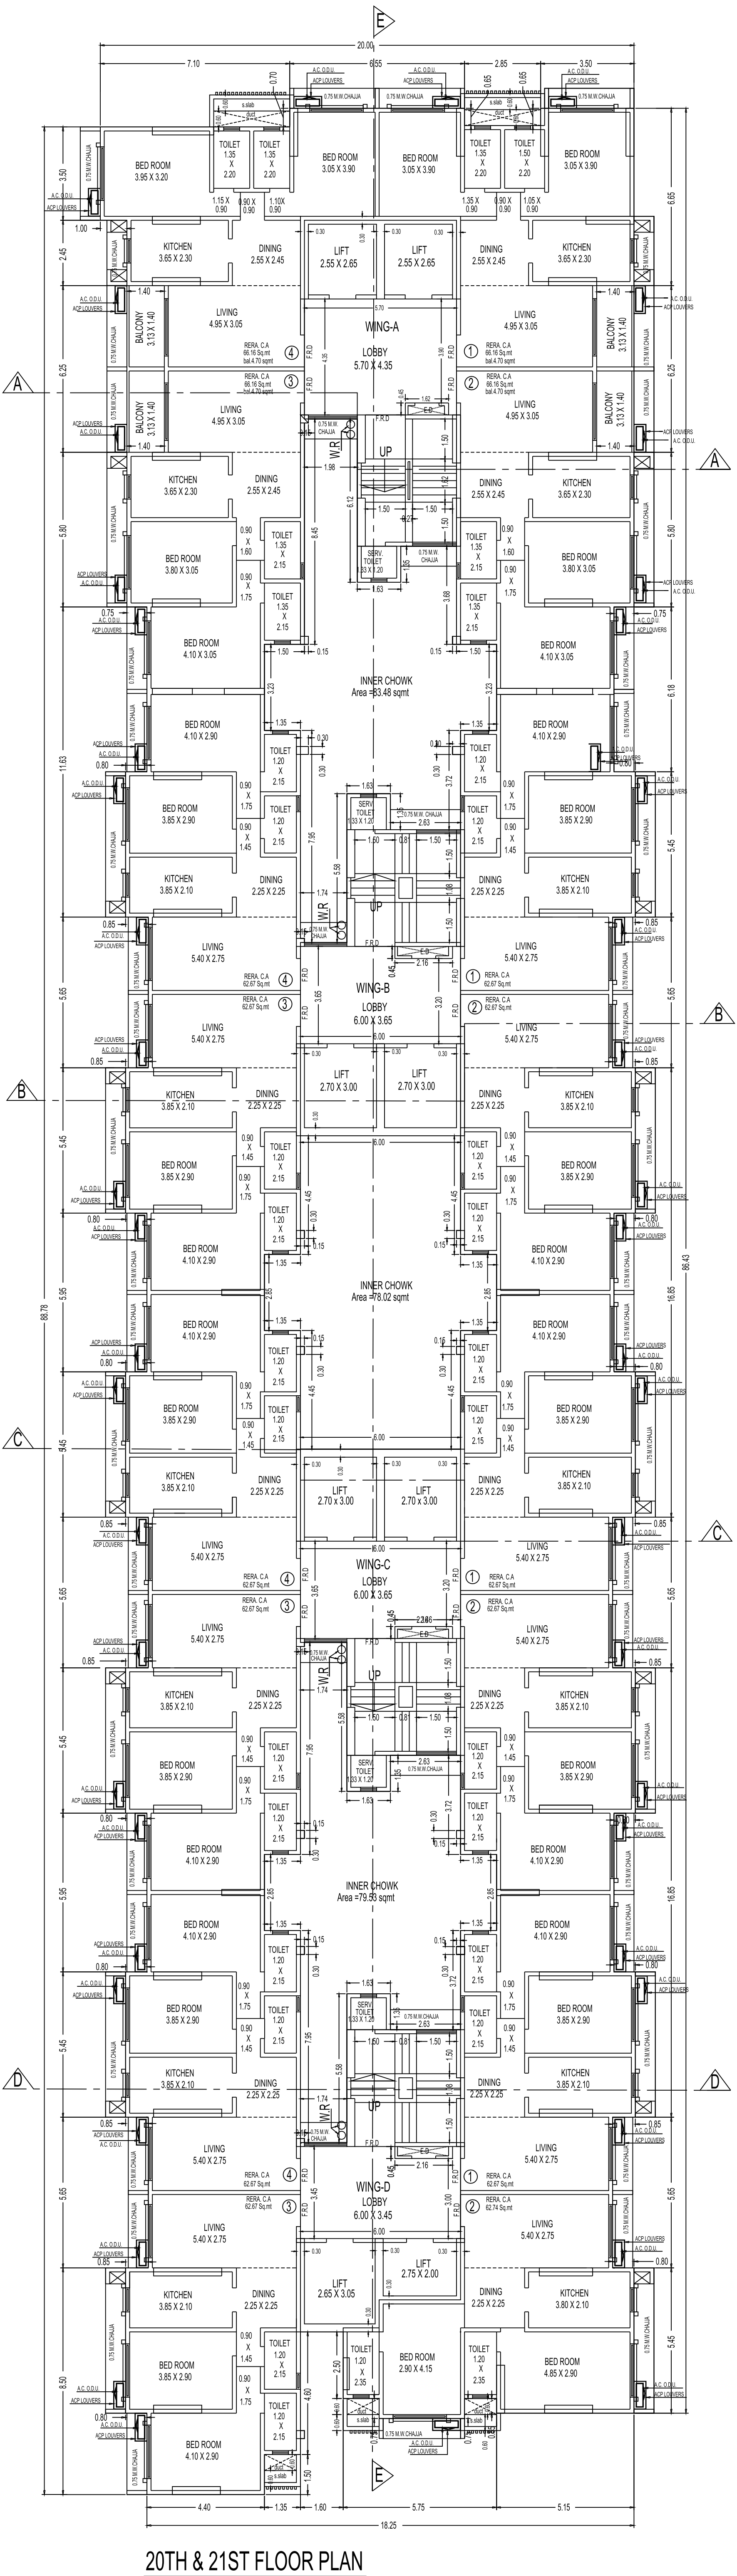

20TH & 21ST FLOOR PLAN

SCALE - 1:100