ELEVATION FEATURE LEVEL
LVL +142.60M

OHT & LMR
LVL +133.10M

TERRACE FLOOR
LVL +127.60M

35TH FLOOR
LVL +124.10M

34TH FLOOR
LVL +120.60M

33RD FLOOR
LVL +117.10M

32ND FLOOR
LVL +113.60M

31ST FLOOR
LVL +110.10M

30TH FLOOR
LVL +106.60M

29TH FLOOR
LVL +103.10M

28TH FLOOR REFUGE
LVL +99.60M

27TH FLOOR
LVL +96.10M

26TH FLOOR
LVL +92.60M

25TH FLOOR
LVL +89.10M

24TH FLOOR
LVL +85.60M

23TH FLOOR
LVL +82.10M

22ND FLOOR
LVL +78.60M

21ST FLOOR REFUGE
LVL +75.10M

20TH FLOOR
LVL +71.60M

19TH FLOOR
LVL +68.10M

18TH FLOOR
LVL +64.60M
BREAK PRESSURE TANK

17TH FLOOR
LVL +61.10M

16TH FLOOR
LVL +57.60M

15TH FLOOR
LVL +54.10M

14TH FLOOR REFUGE
LVL +50.60M

13TH FLOOR
LVL +47.10M

12TH FLOOR (AMENITY FLOOR)
LVL +43.60 M

11TH FLOOR
LVL +40.10M

10TH FLOOR
LVL +36.60M

9TH FLOOR
LVL +33.10M

8TH FLOOR
LVL +29.60M

7TH FLOOR REFUGE
LVL +26.10M

6TH FLOOR
LVL +22.60M

5TH FLOOR
LVL +19.10M

SERVICE FLOOR
LVL +17.30M

4TH FLOOR
LVL +13.90M

3RD FLOOR
LVL +10.50M

2ND FLOOR
LVL +7.10M

1ST FLOOR
LVL +3.70M


PLINTH LEVEL
LVL +0.30

GROUND FLOOR PLAN
LVL +0.00M

BASEMENT 1 LVL
LVL -2.90M

BASEMENT 2 LVL
LVL -7.40


3.50 3.50 3.50

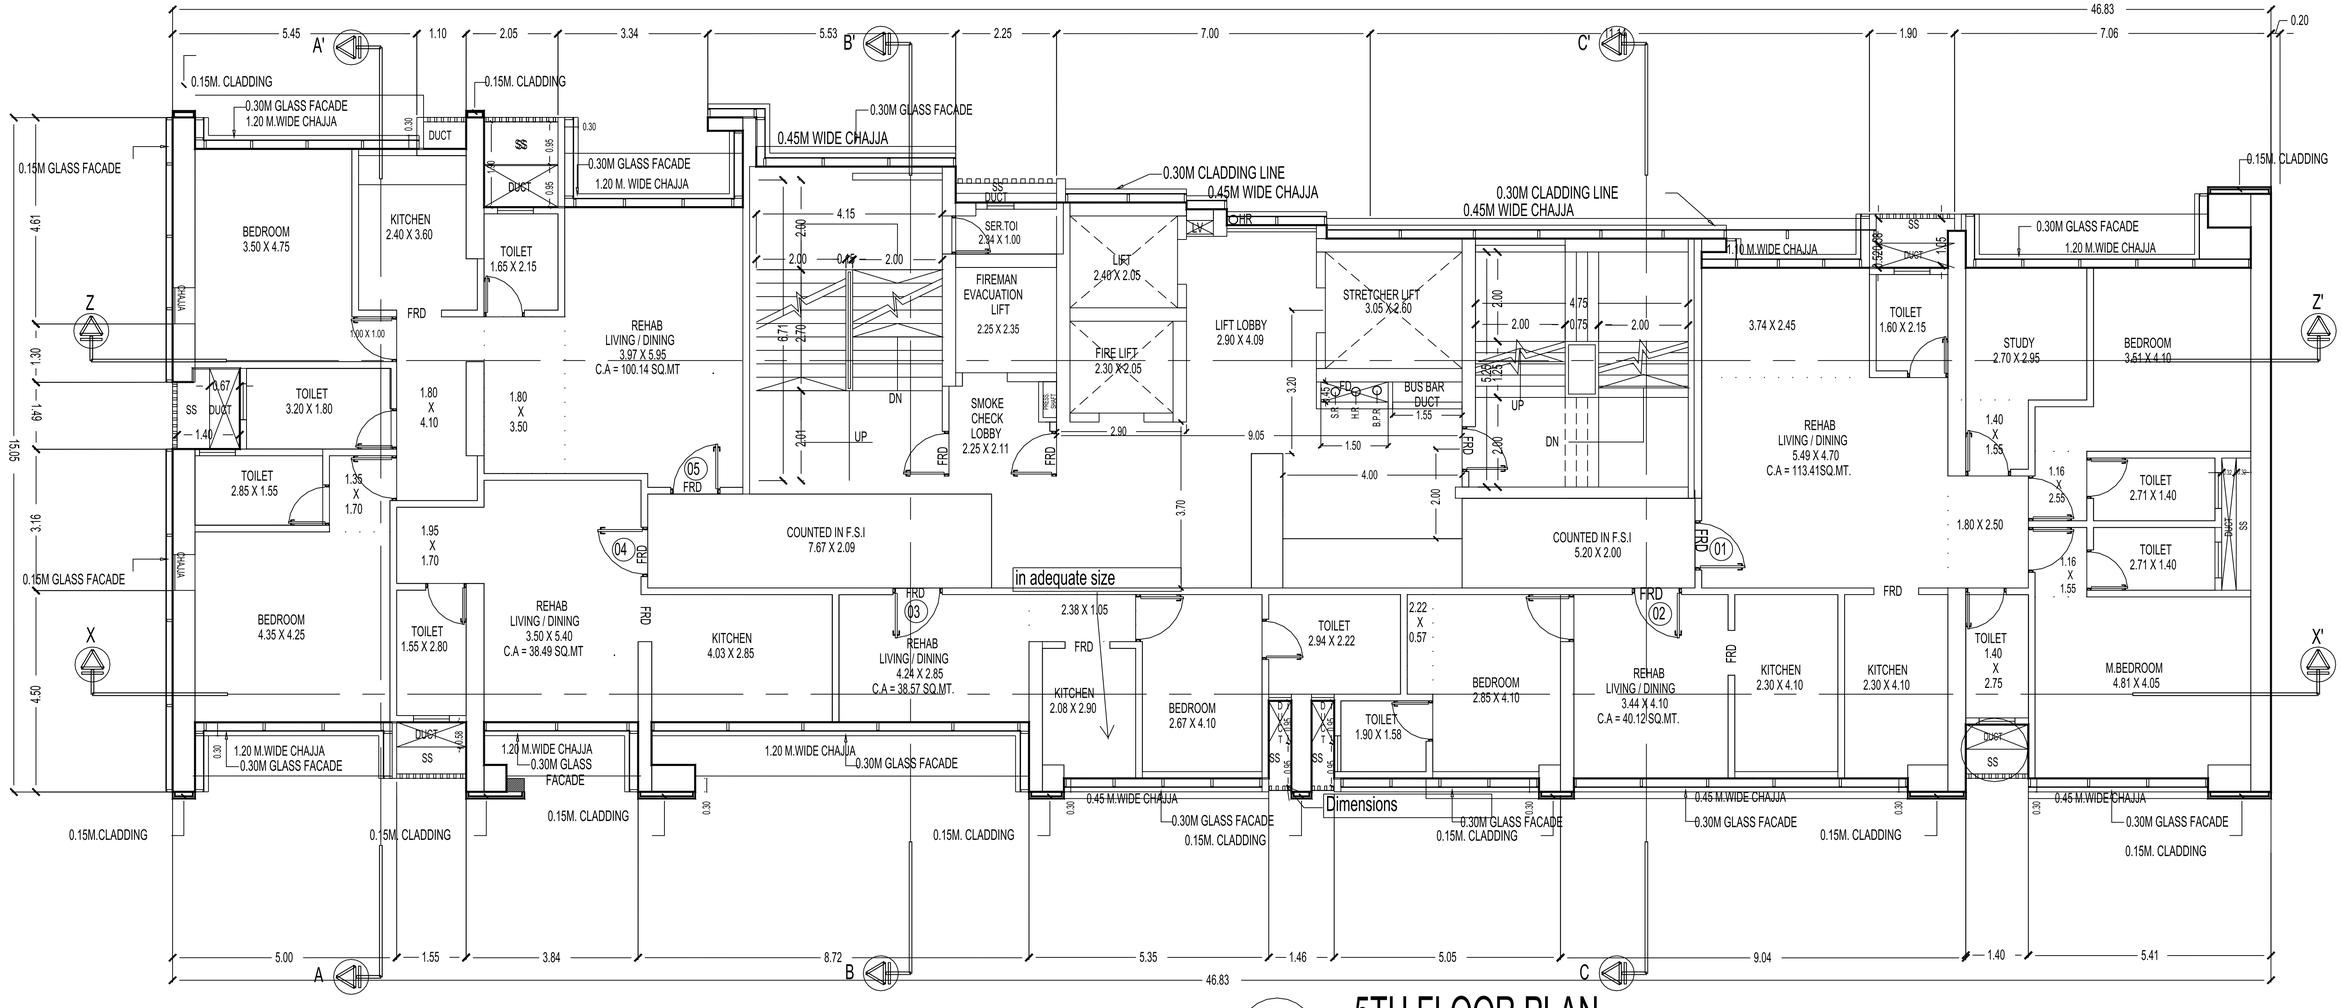

5TH FLOOR PLAN

1


Scale: 1:100

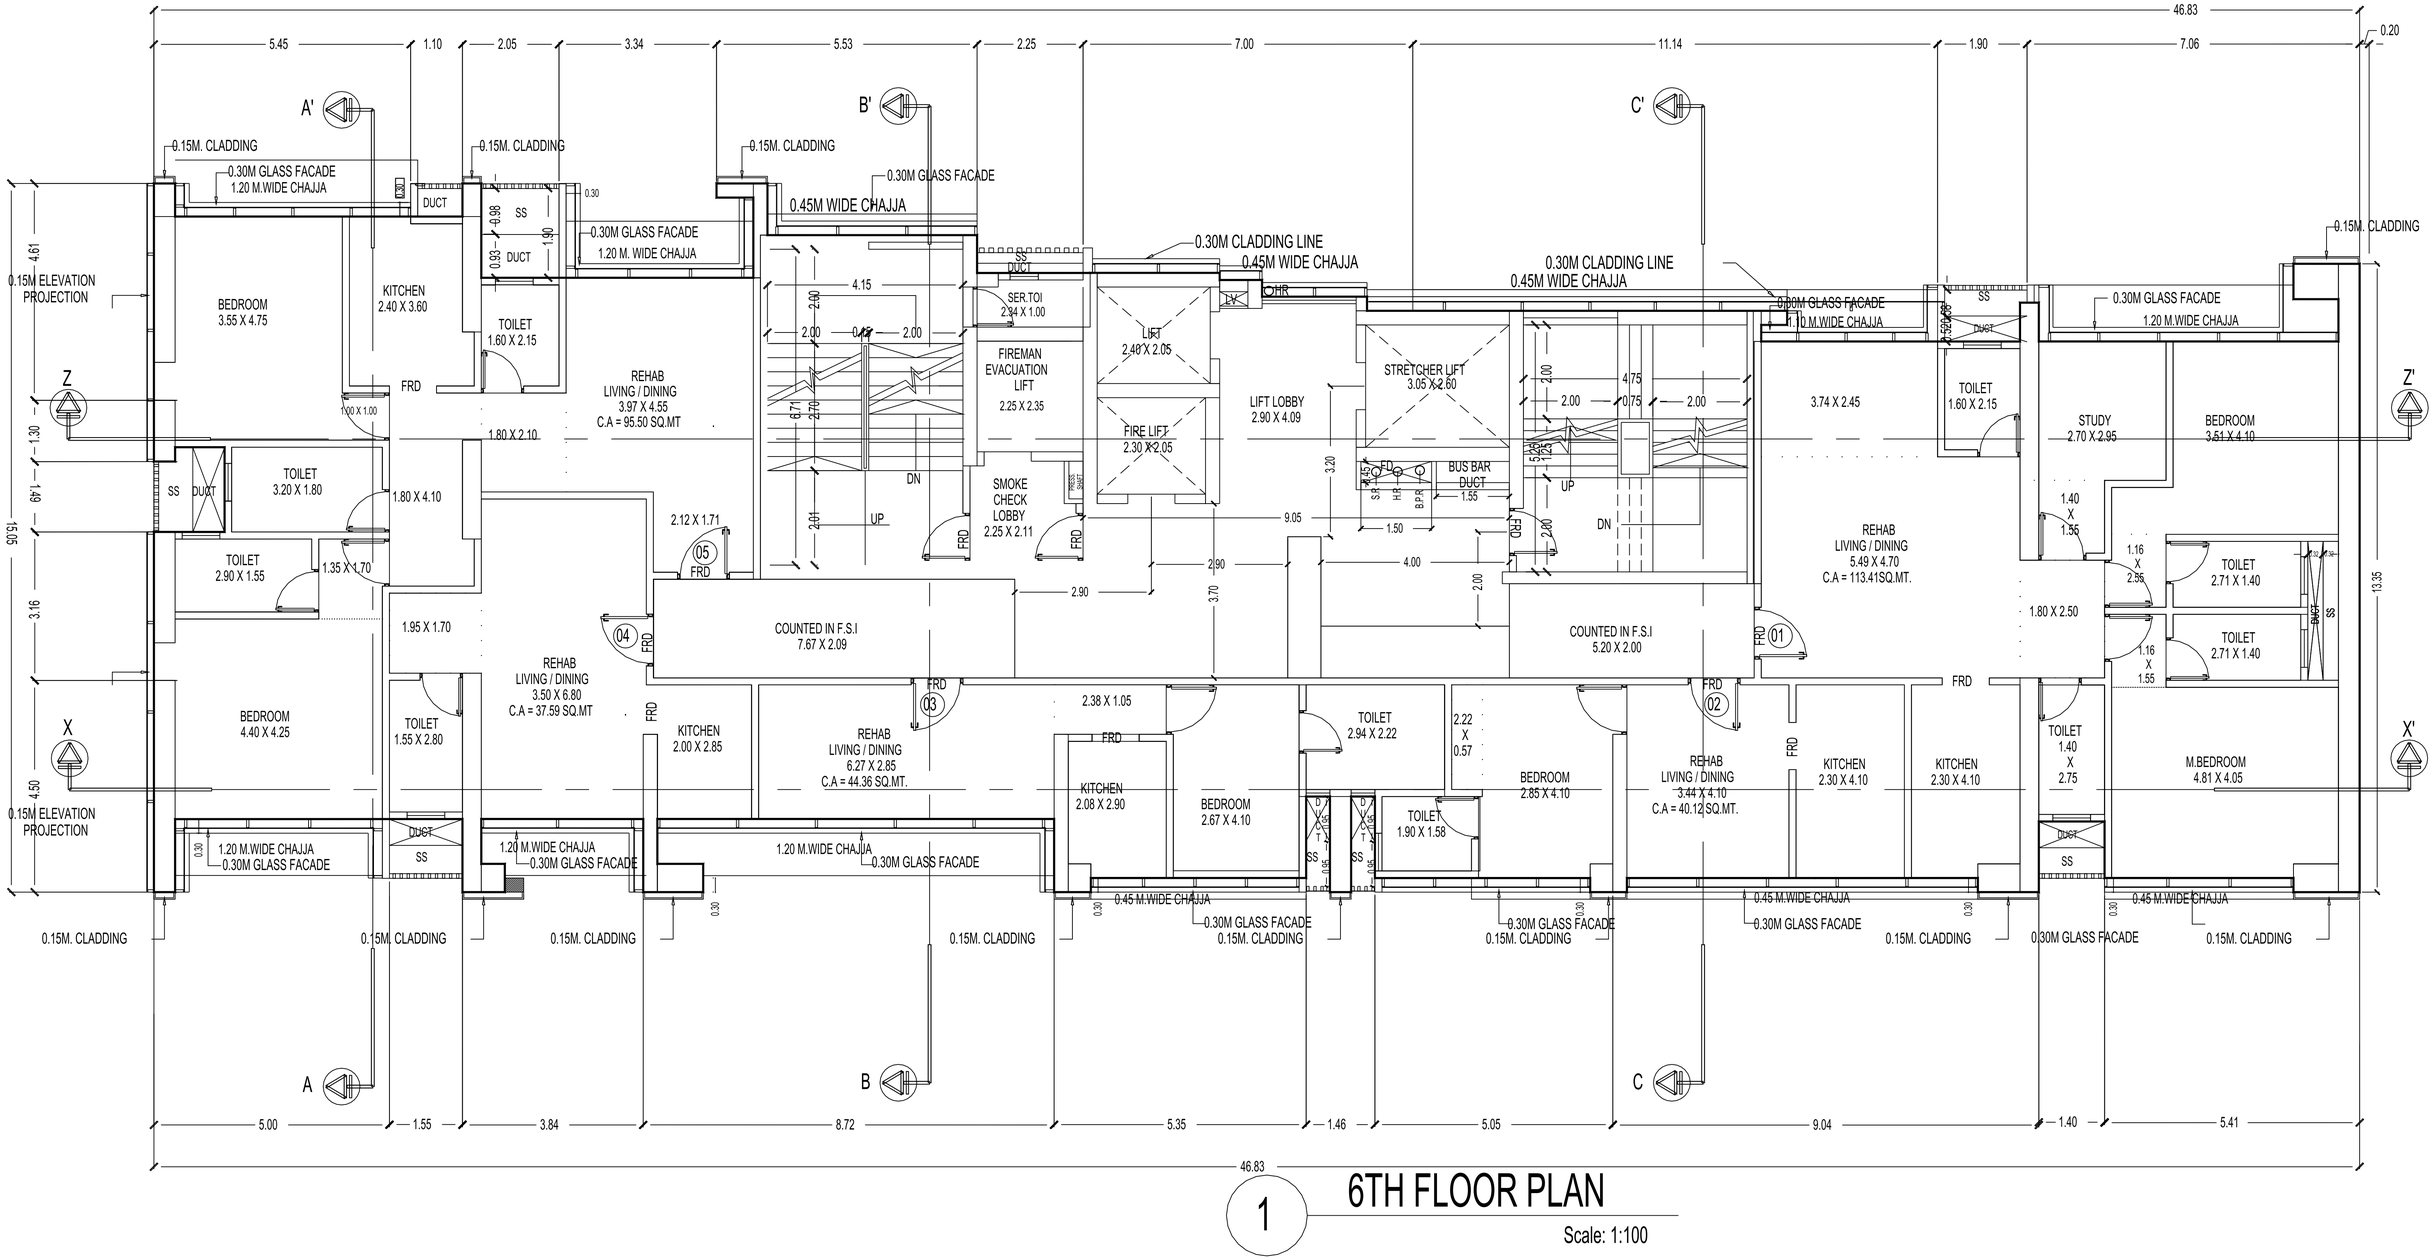

6TH FLOOR PLAN


1

Scale: 1:100

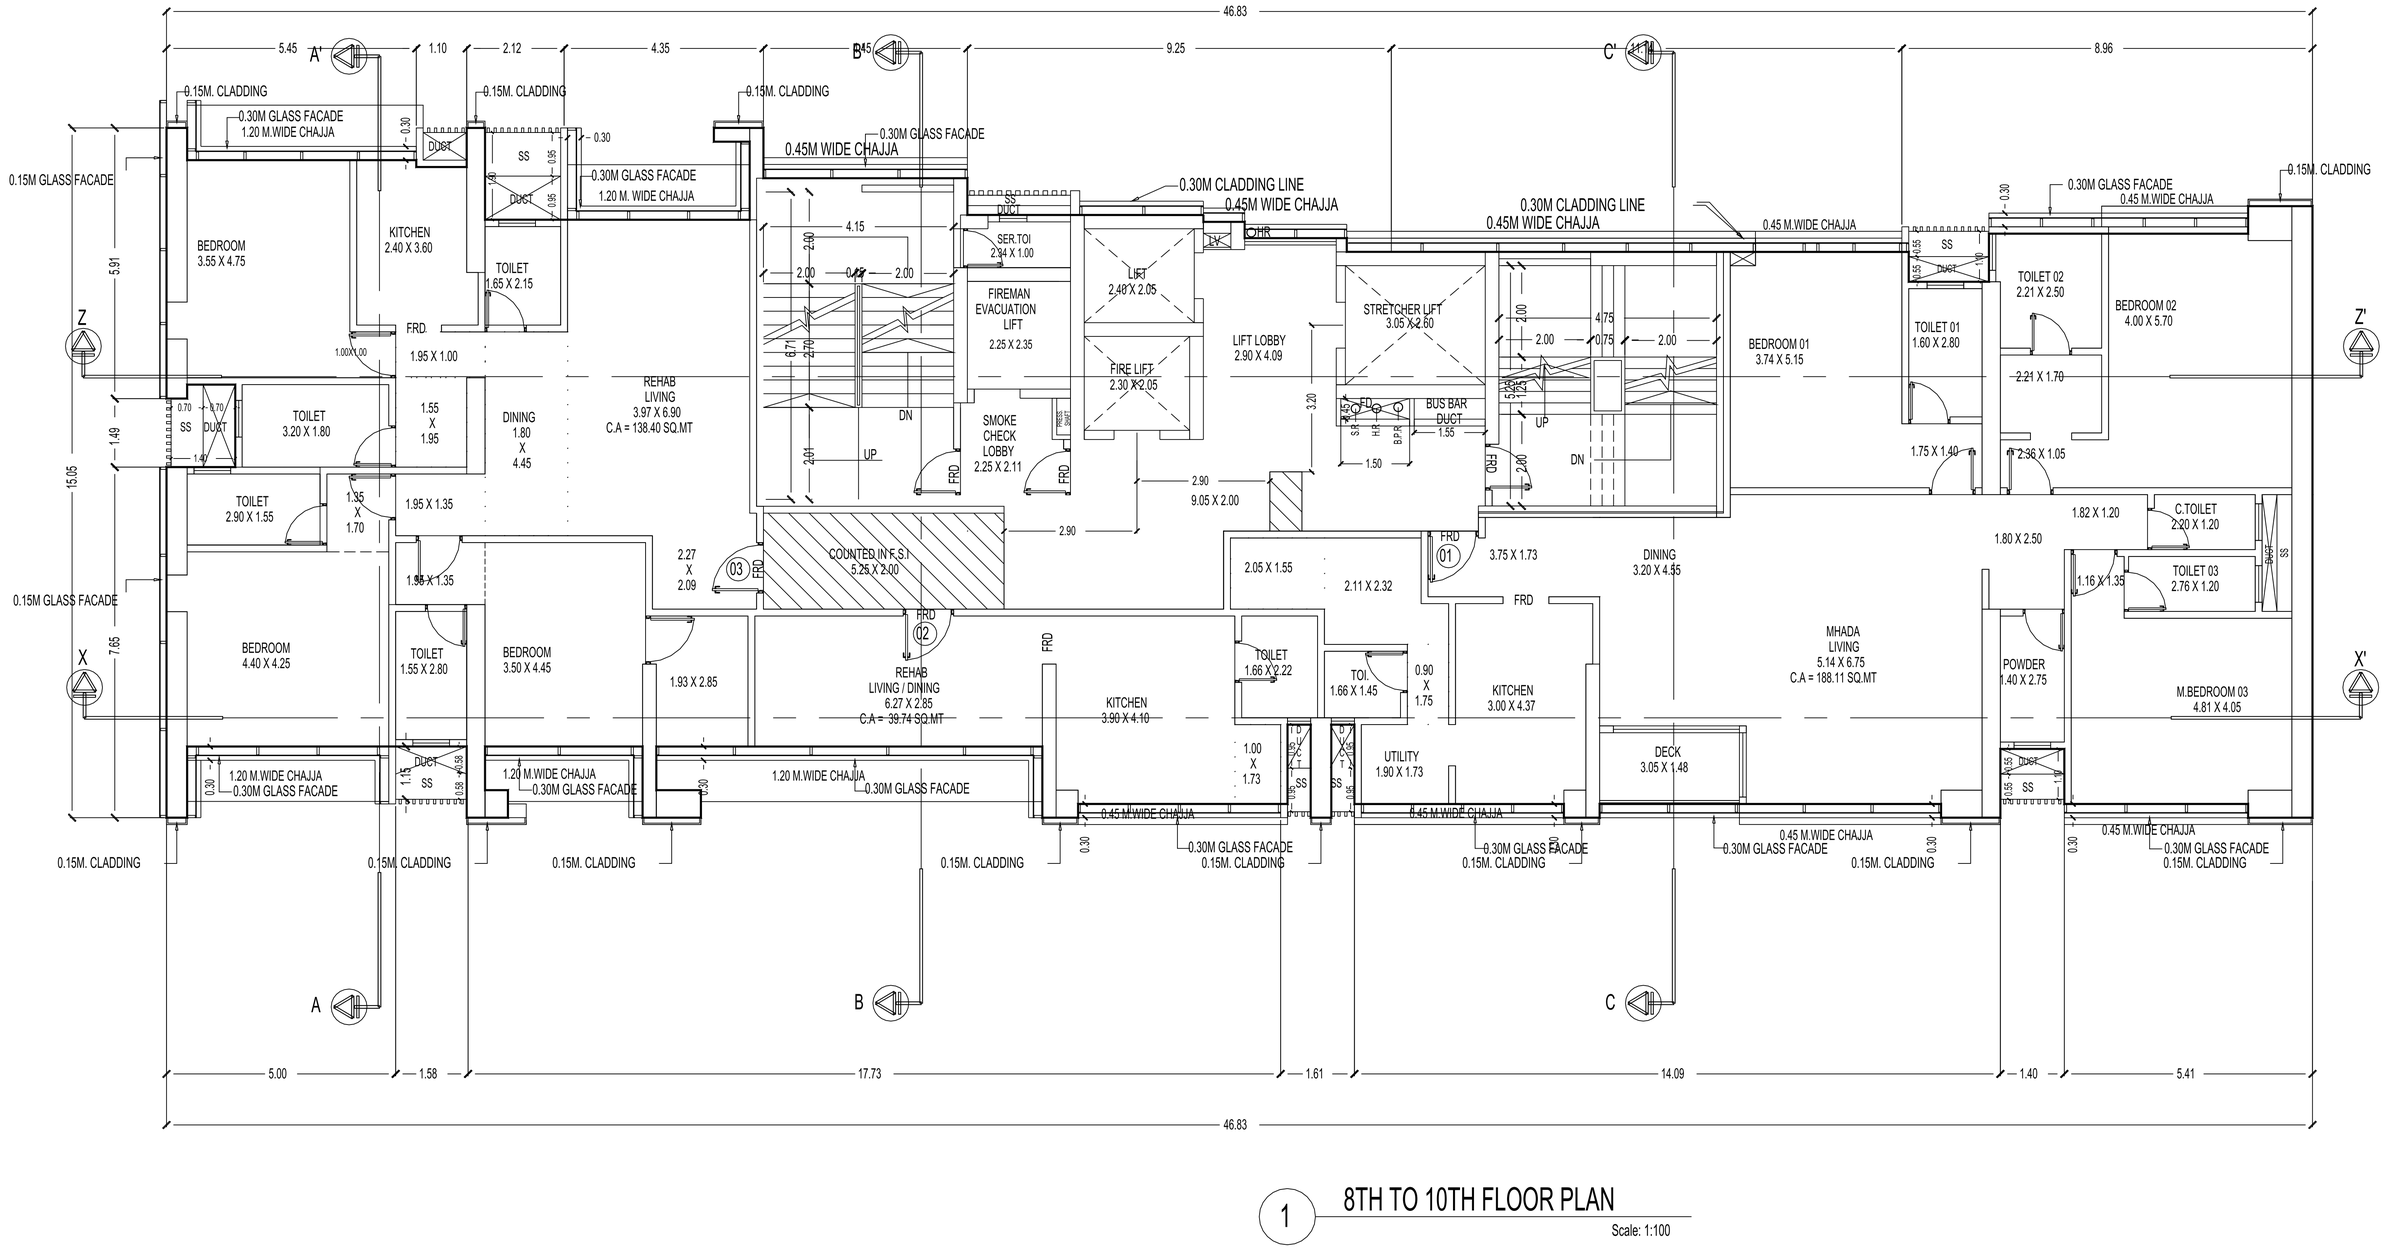


1 8TH TO 10TH FLOOR PLAN

Scale: 1:100

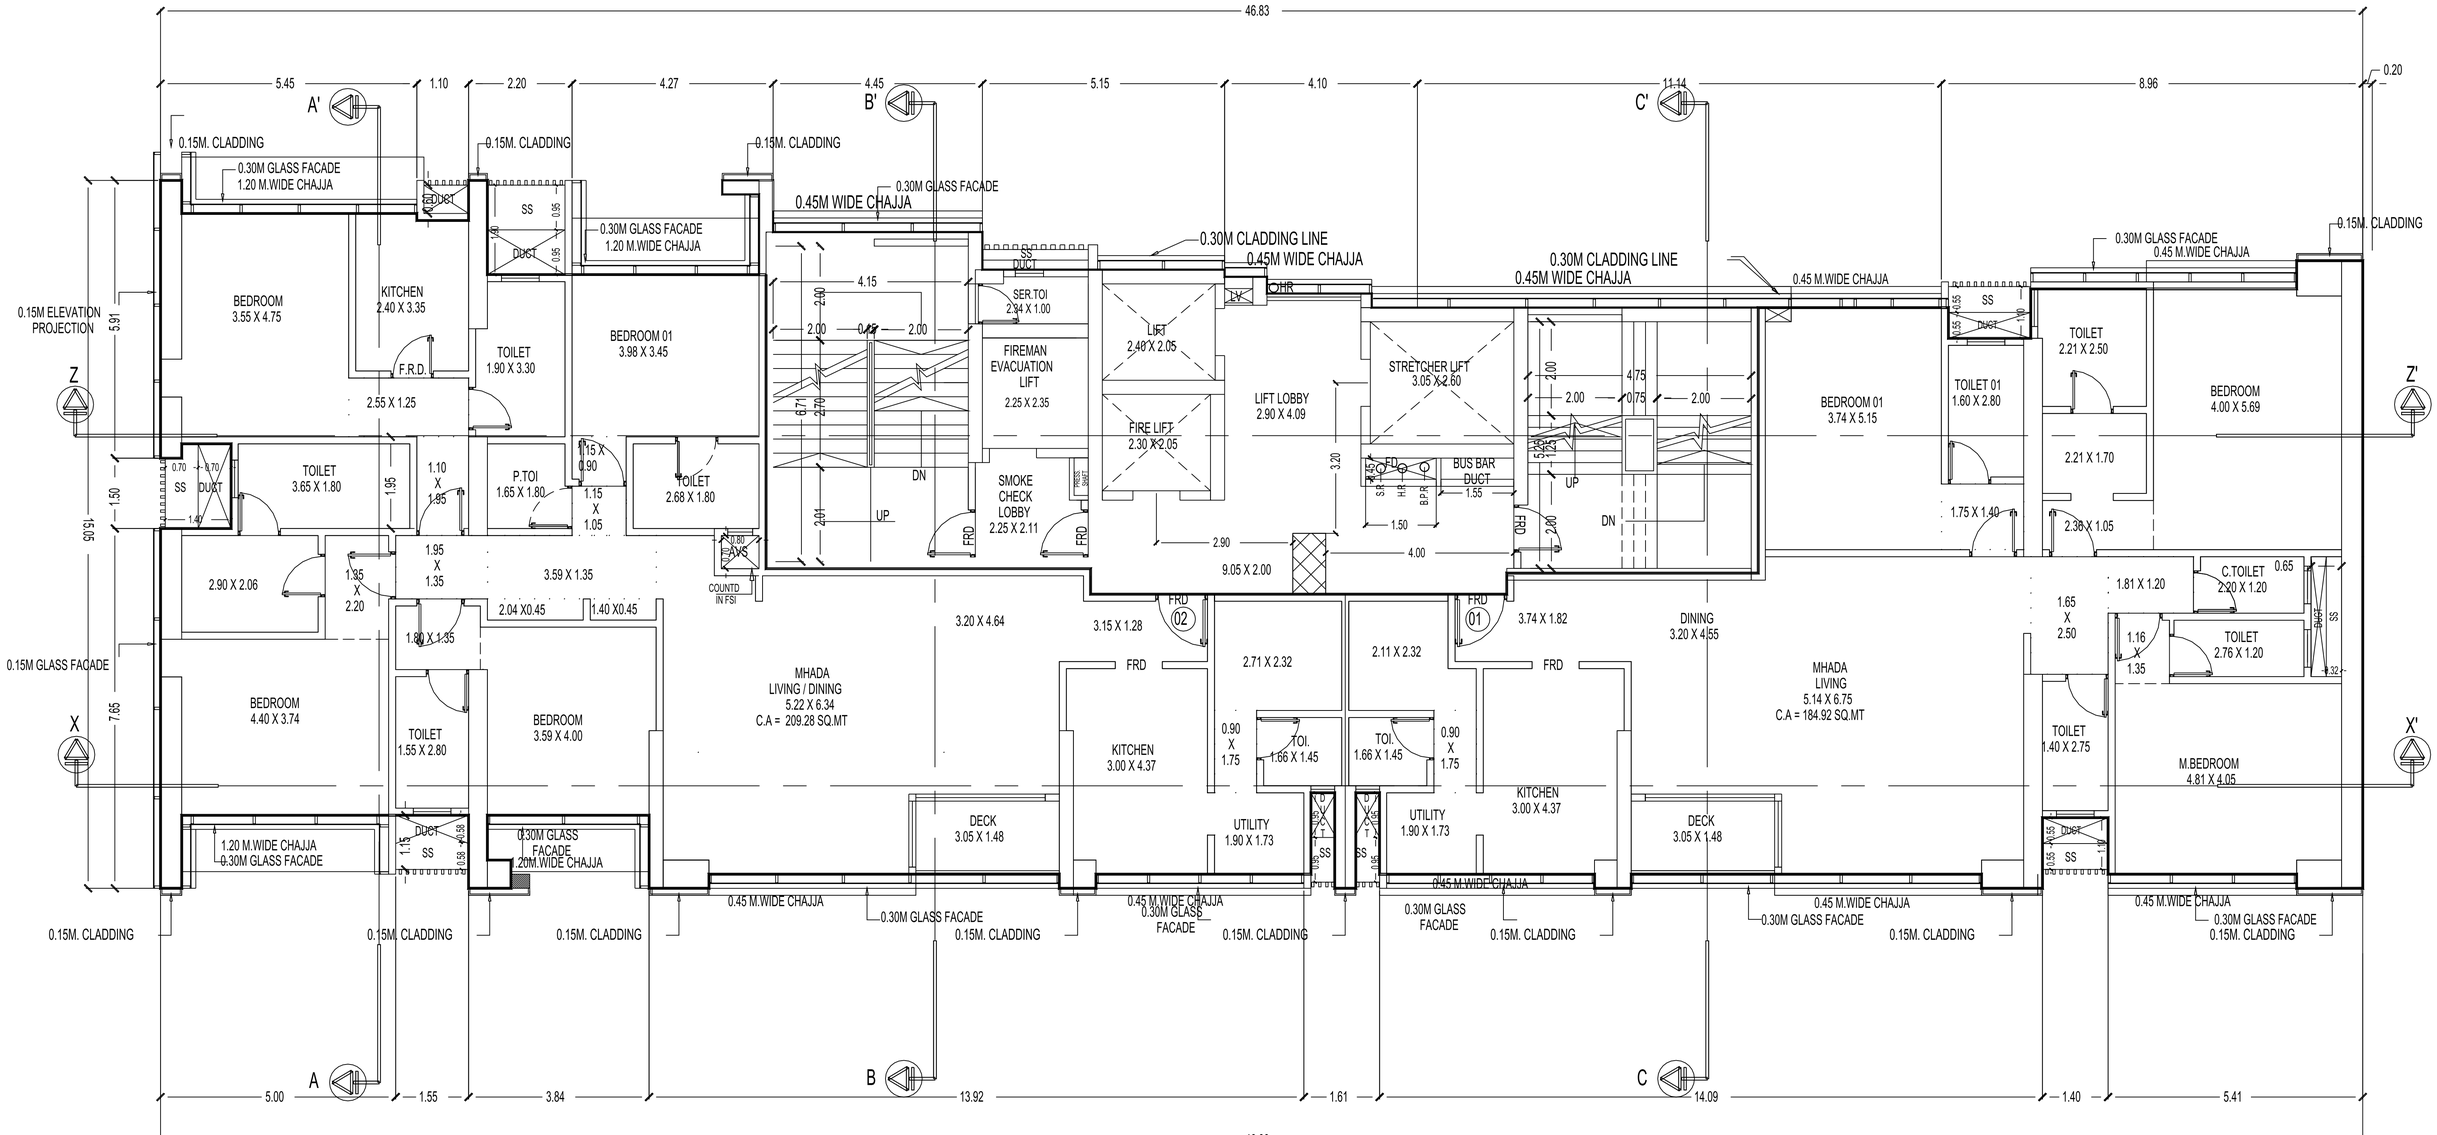


1 11TH FLOOR PLAN (MHADA)

Scale: 1:100

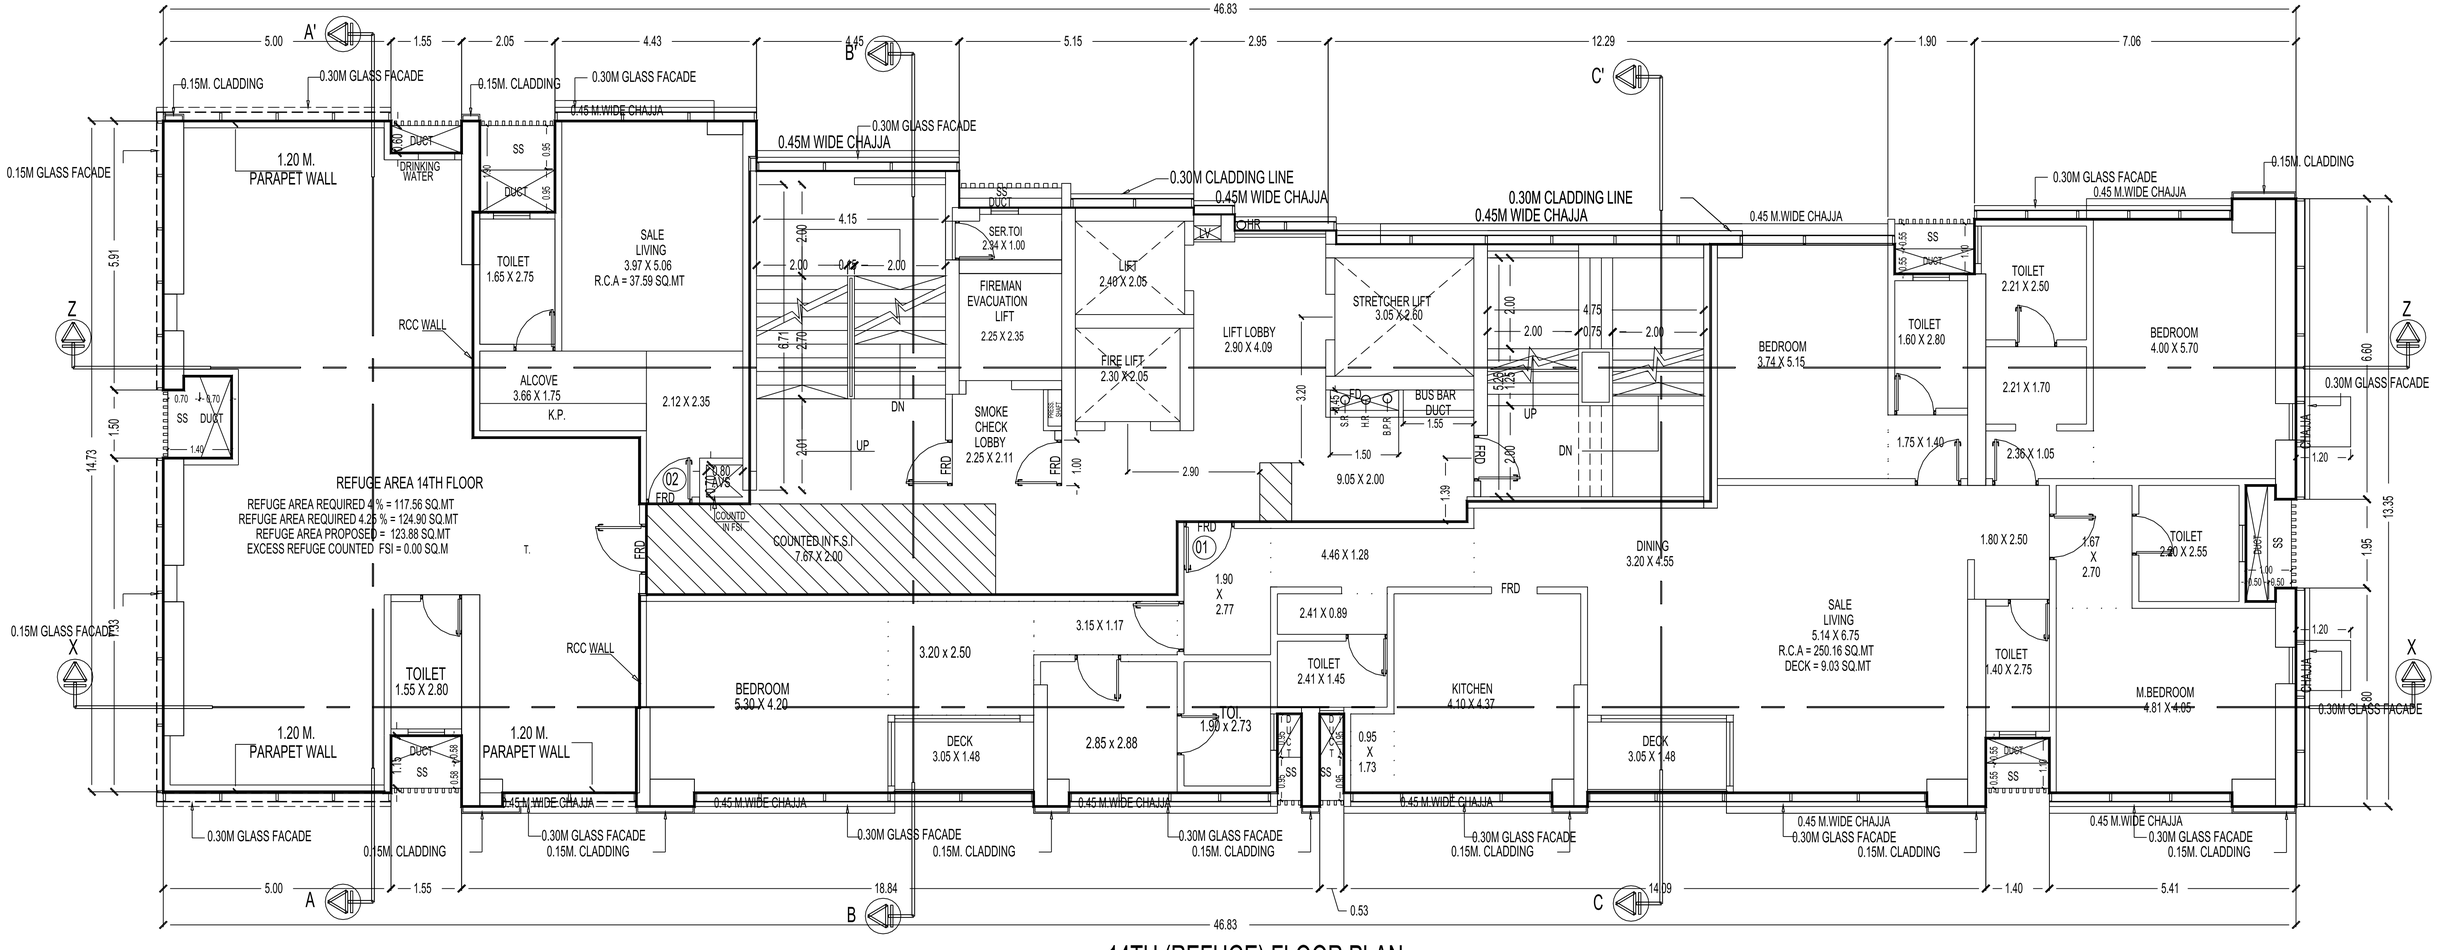


14TH (REFUGE) FLOOR PLAN

SCALE: 1:100

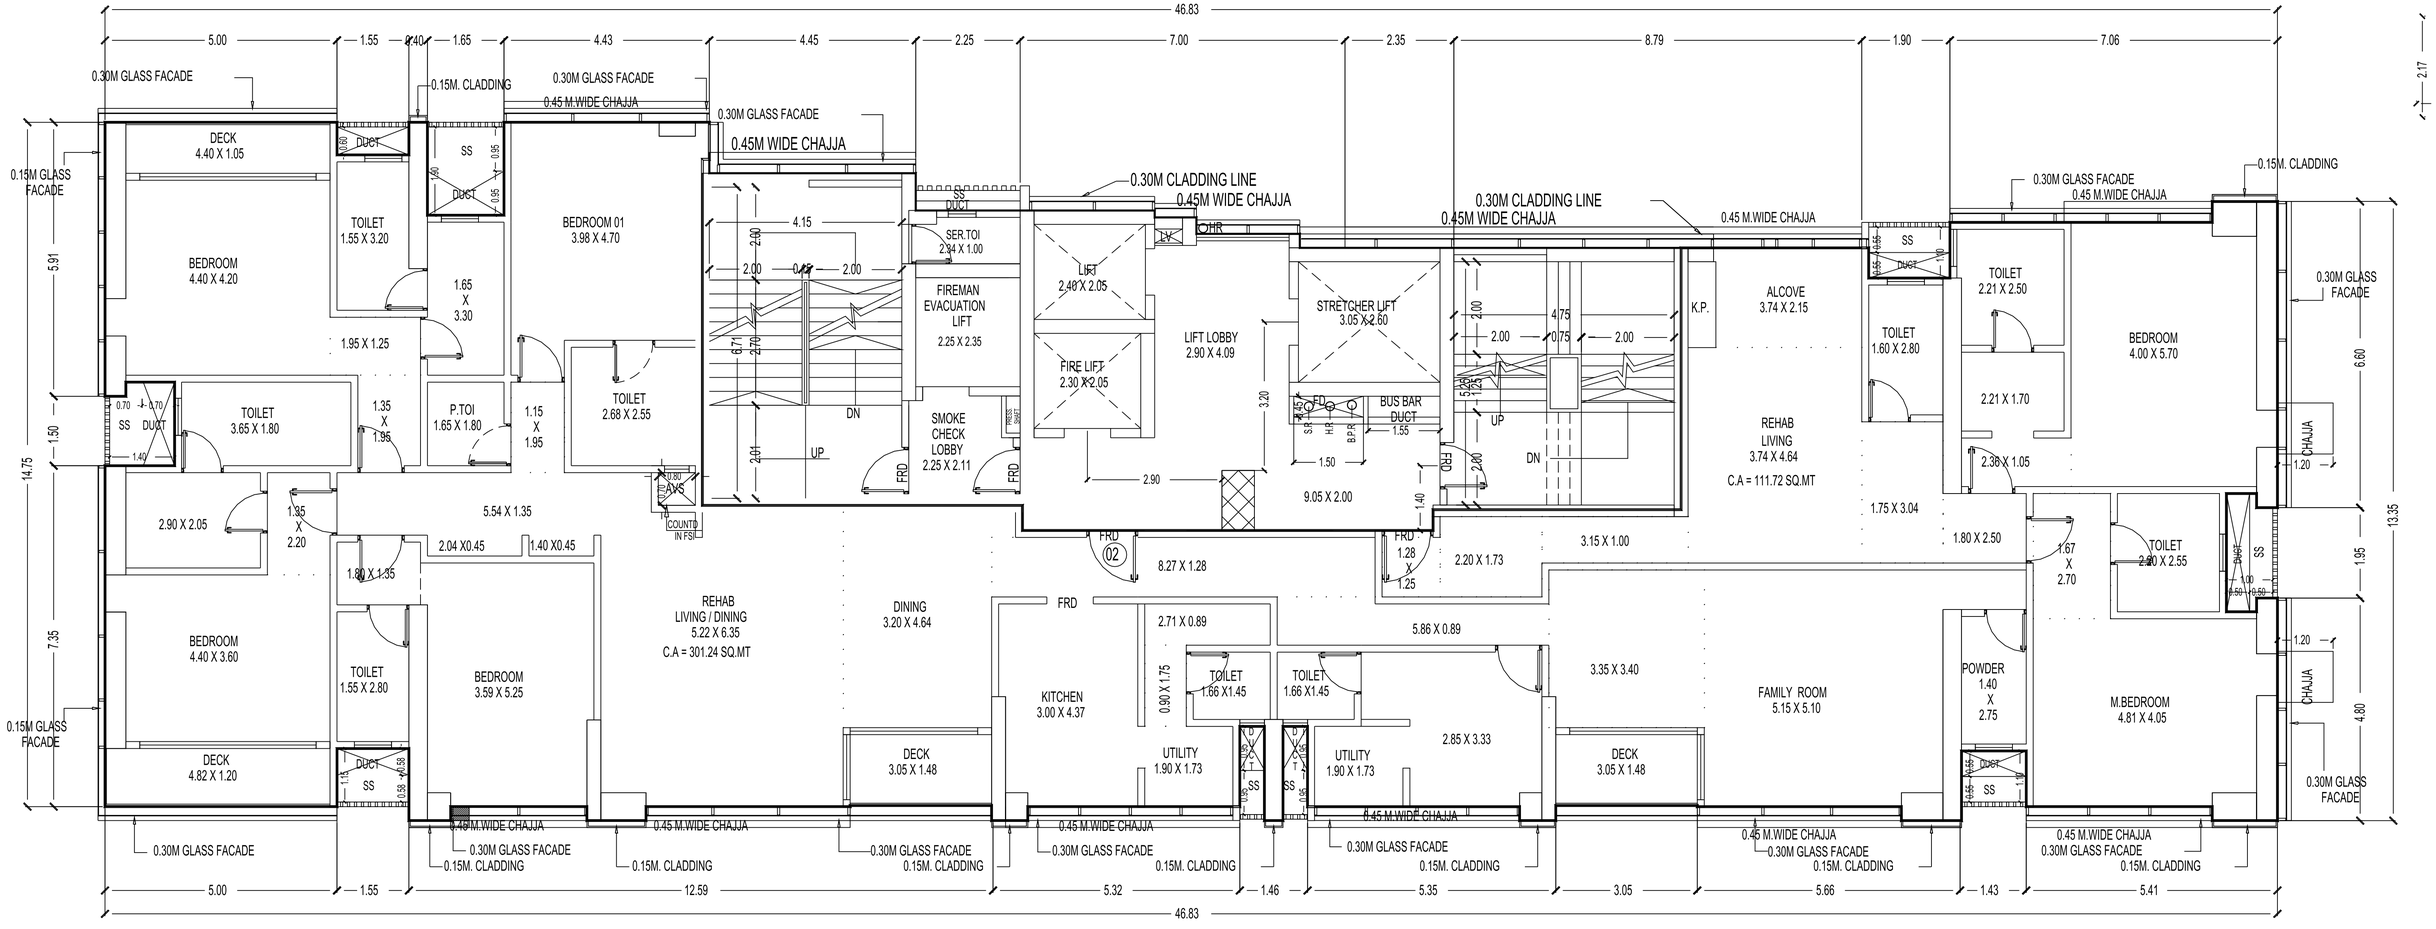


1 24TH FLOOR PLAN

Scale: 1:100

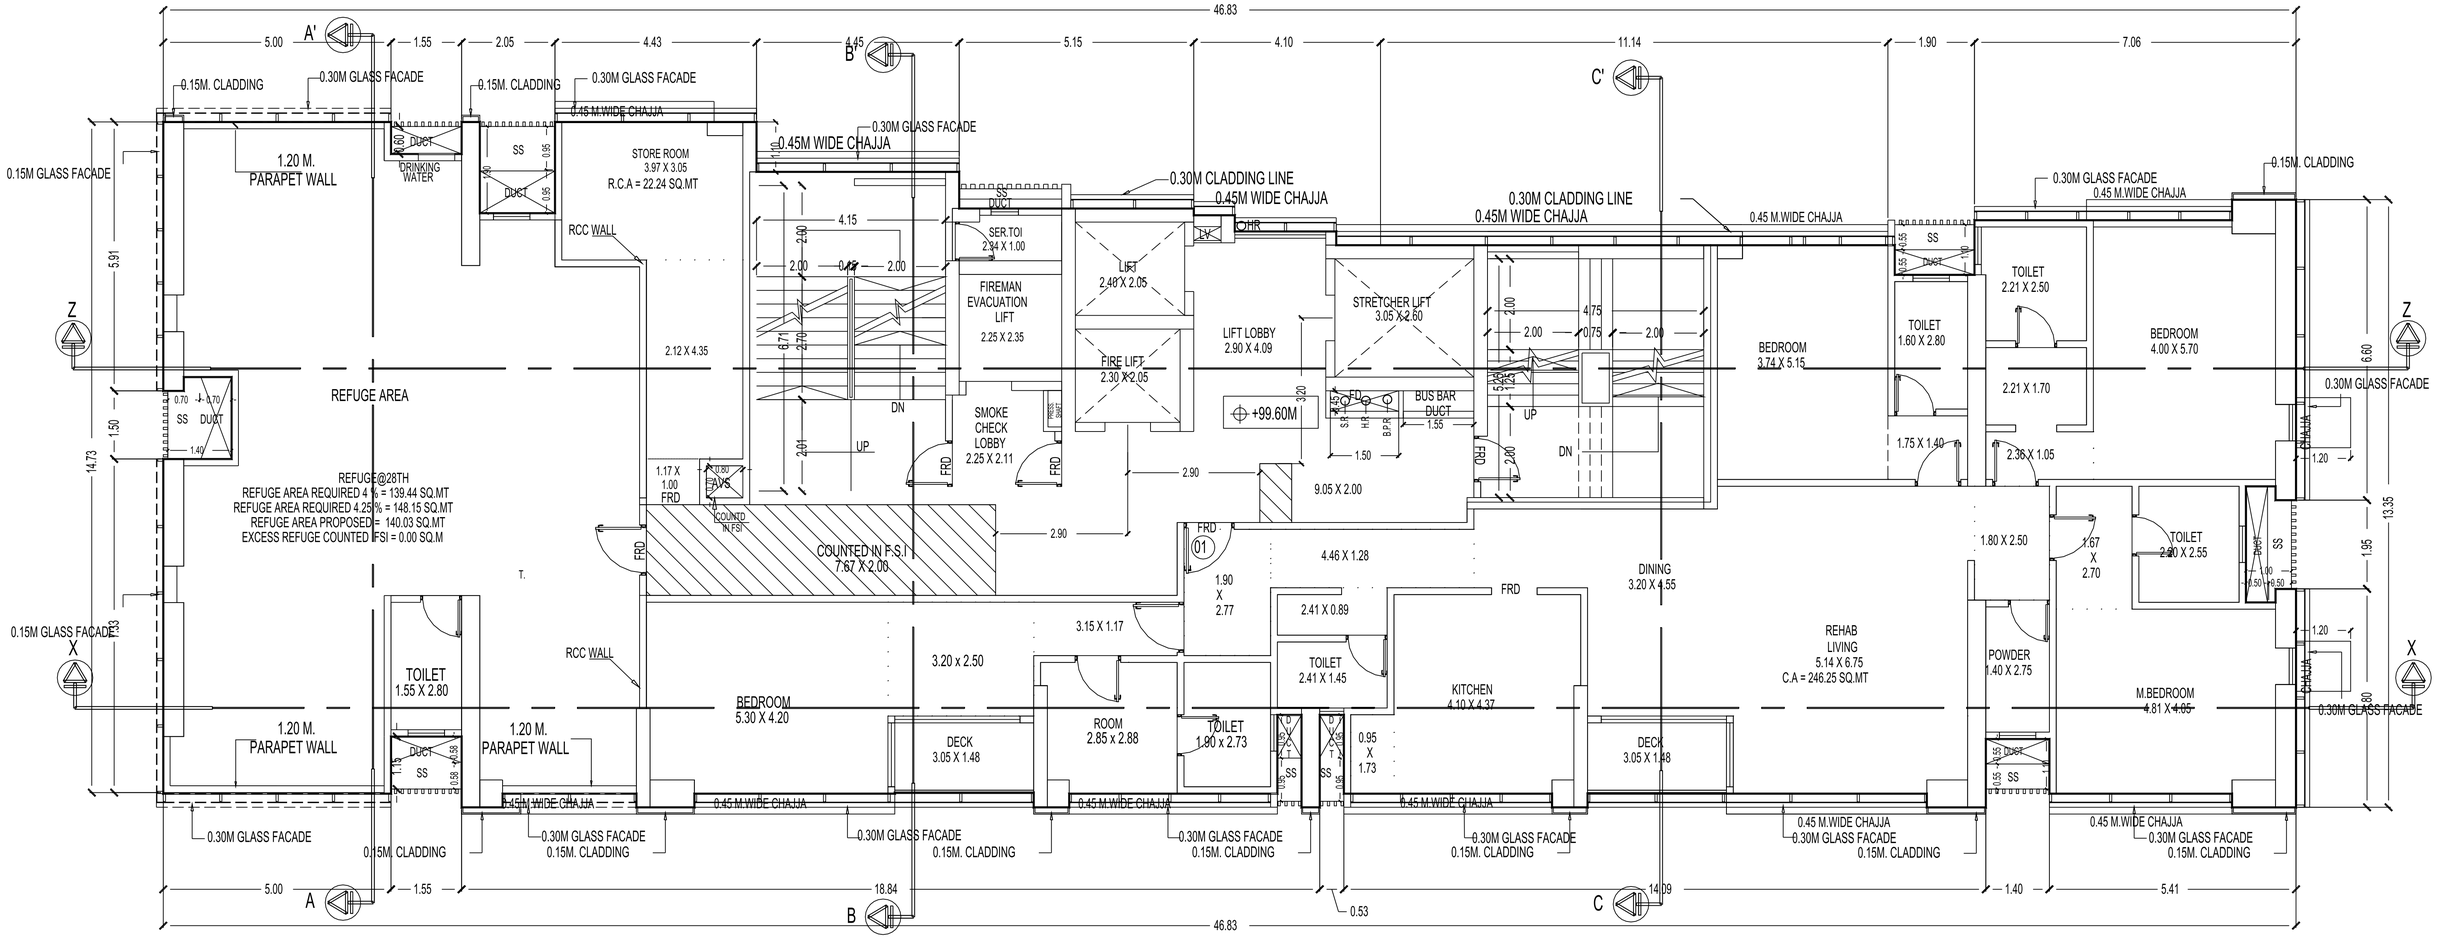


1 28TH (REFUGE) FLOOR PLAN

Scale: 1:100

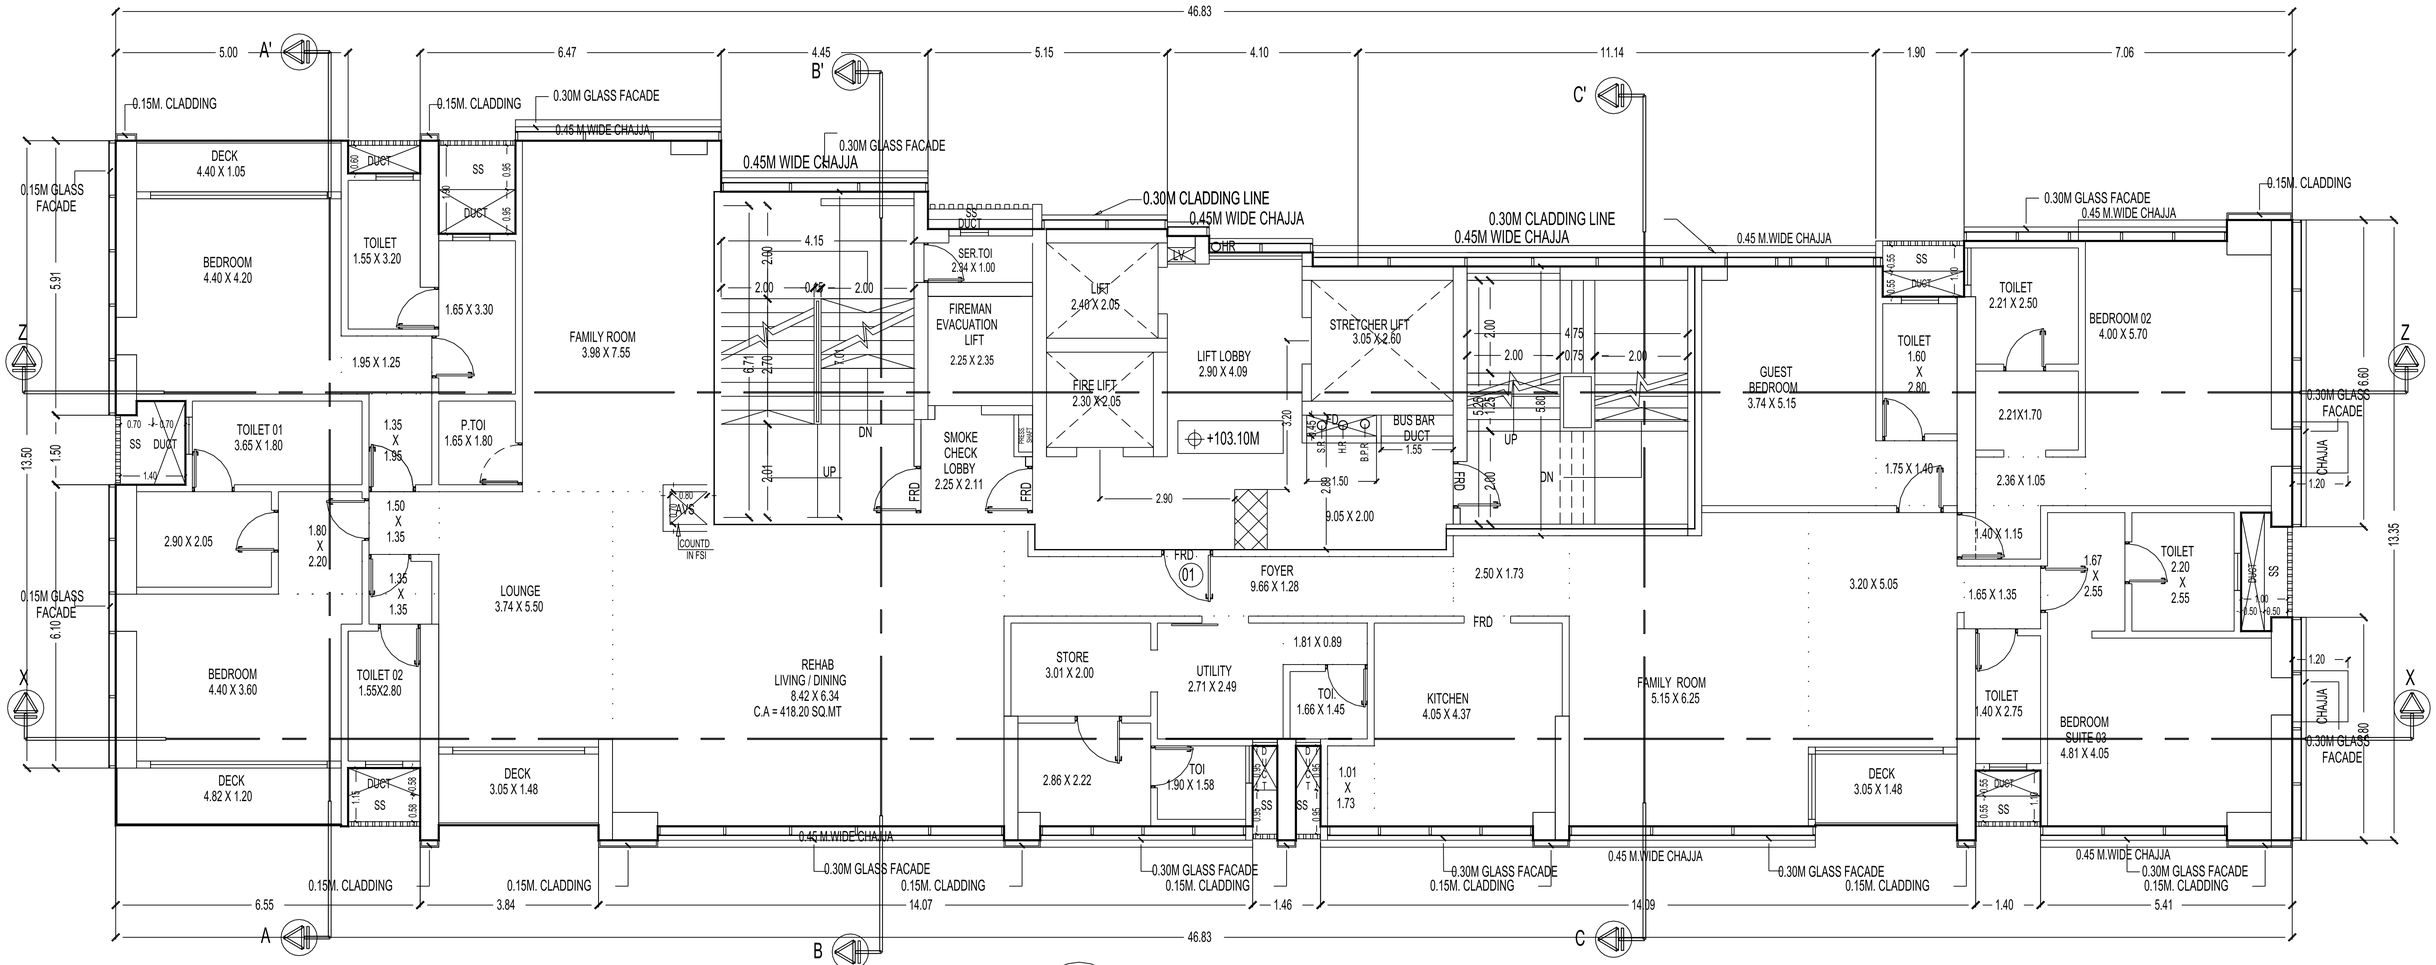
46.83
5.00
6.47
4.45
5.15
4.10
11.14
1.90
7.06
A'
B'
C'
0.15M. CLADDING
0.30M GLASS FACADE
0.45 M.WIDE CHAJJA
0.45M WIDE CHAJJA
0.30M CLADDING LINE
0.15M GLASS FACADE
DECK 4.40 X 1.05
BEDROOM 4.40 X 4.20
TOILET 1.55 X 3.20
1.65 X 3.30
1.95 X 1.25
FAMILY ROOM 3.98 X 7.55
SER.TOI 2.34 X 1.00
FIREMAN EVACUATION LIFT 2.25 X 2.35
LIFT 2.40 X 2.05
FIRE LIFT 2.30 X 2.05
LIFT LOBBY 2.90 X 4.09
STRETCHER LIFT 3.05 X 2.60
+103.10M
BUS BAR DUCT
SMOKE CHECK LOBBY 2.25 X 2.11
GUEST BEDROOM 3.74 X 5.15
TOILET 1.60 X 2.80
TOILET 2.21 X 2.50
BEDROOM 02 4.00 X 5.70
2.21X1.70
2.36 X 1.05
1.75 X 1.40
1.40 X 1.15
TOILET 2.20 X 2.55
1.67 X 2.55
1.65 X 1.35
3.20 X 5.05
TOILET 01 3.65 X 1.80
P.TOI 1.65 X 1.80
1.35 X 1.95
1.50 X 1.35
1.80 X 2.20
1.35 X 1.35
2.90 X 2.05
LOUNGE 3.74 X 5.50
FOYER 9.66 X 1.28
9.05 X 2.00
2.50 X 1.73
BEDROOM 4.40 X 3.60
TOILET 02 1.55X2.80
REHAB LIVING / DINING 8.42 X 6.34 C.A = 418.20 SQ.MT
STORE 3.01 X 2.00
UTILITY 2.71 X 2.49
TOI 1.66 X 1.45
1.81 X 0.89
KITCHEN 4.05 X 4.37
FAMILY ROOM 5.15 X 6.25
TOILET 1.40 X 2.75
BEDROOM SUITE 03 4.81 X 4.05
2.86 X 2.22
TOI 1.90 X 1.58
1.01 X 1.73
DECK 4.82 X 1.20
DECK 3.05 X 1.48
DECK 3.05 X 1.48
FRD
DN
UP
SS
DUCT
COUNTD IN FSI
13.50
5.91
1.50
6.10
6.60
13.35
2.80
6.55
3.84
14.07
1.46
14.09
1.40
5.41
Z
X
A
B
C
1
29TH FLOOR PLAN


SCALE: 1:100

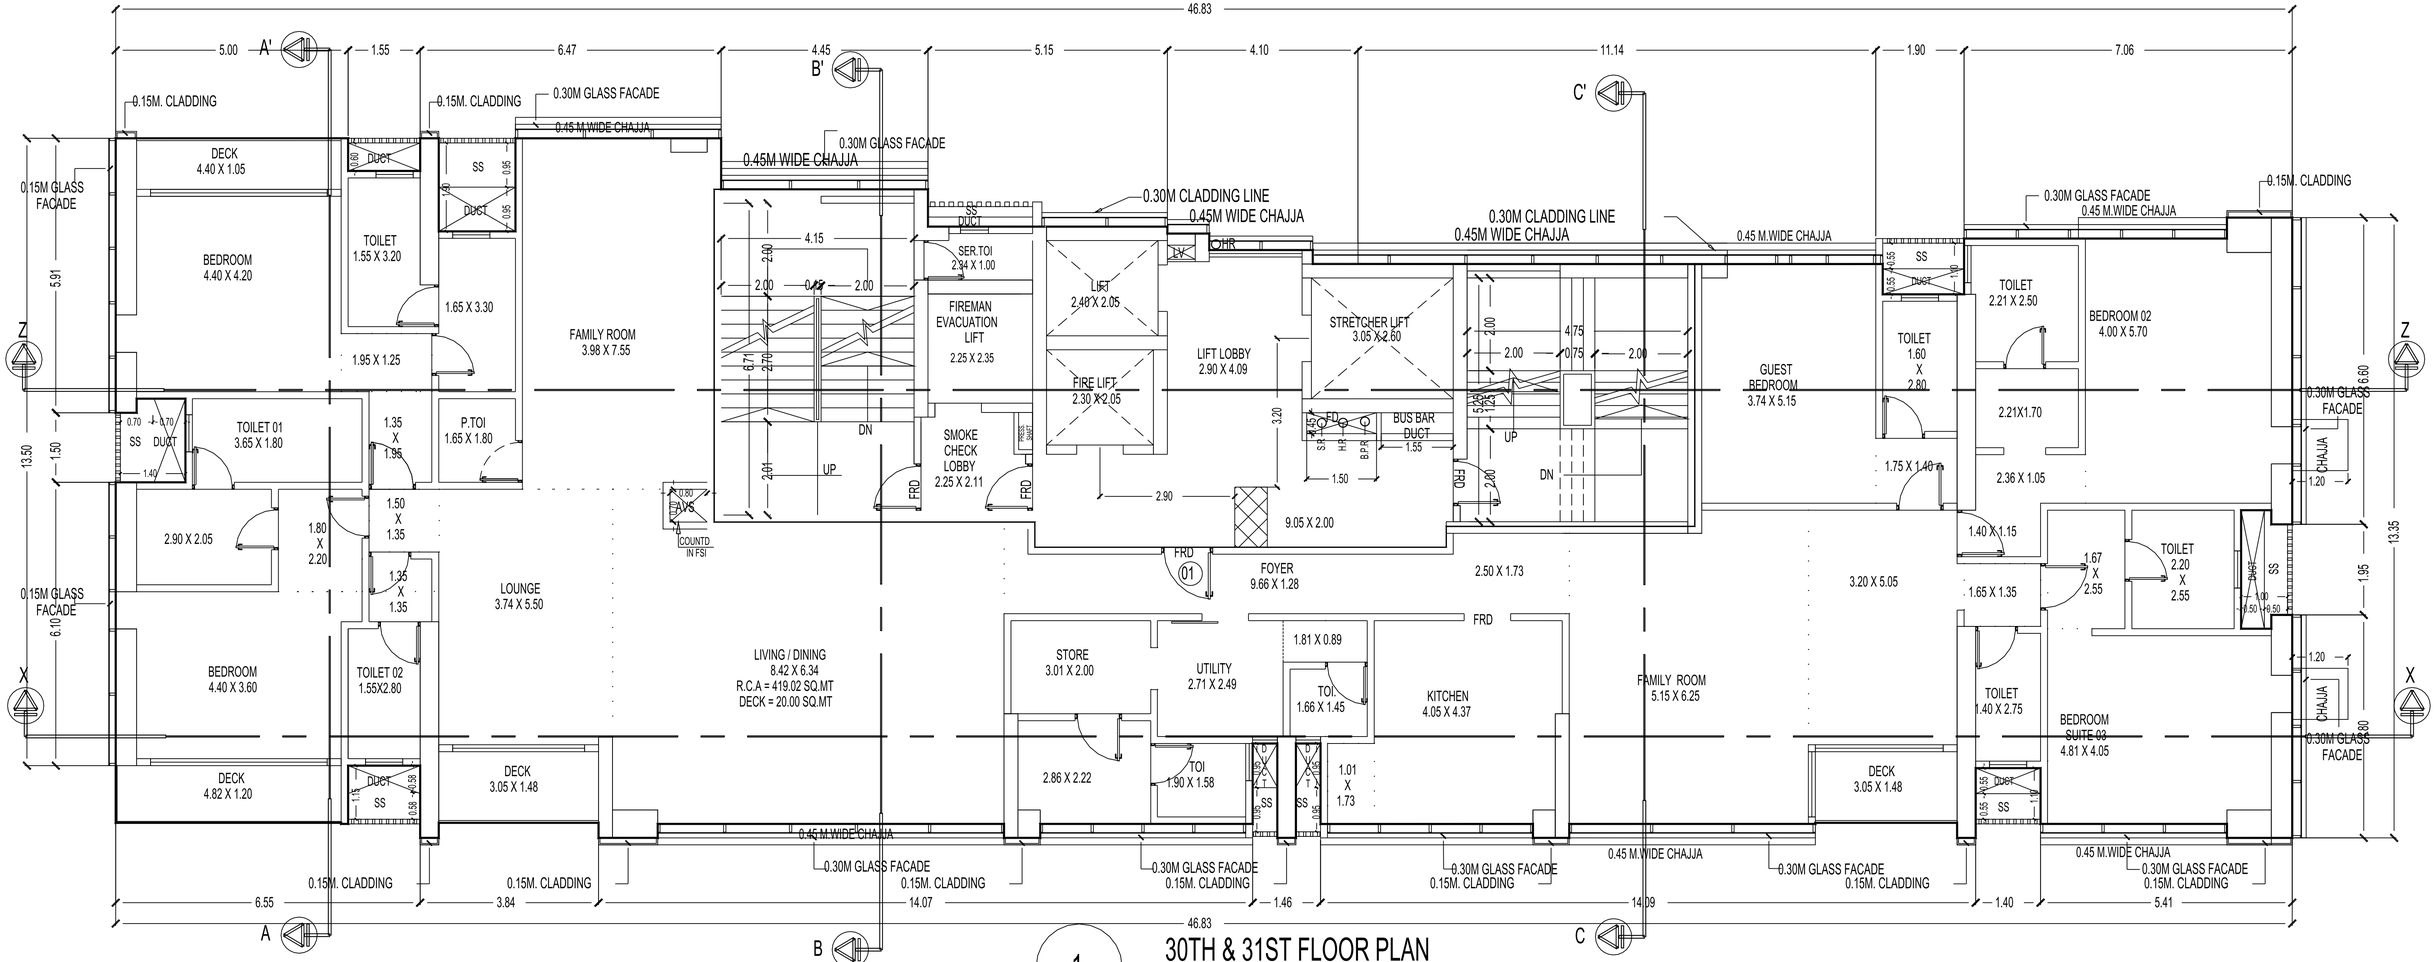

1

30TH & 31ST FLOOR PLAN


SCALE: 1:100

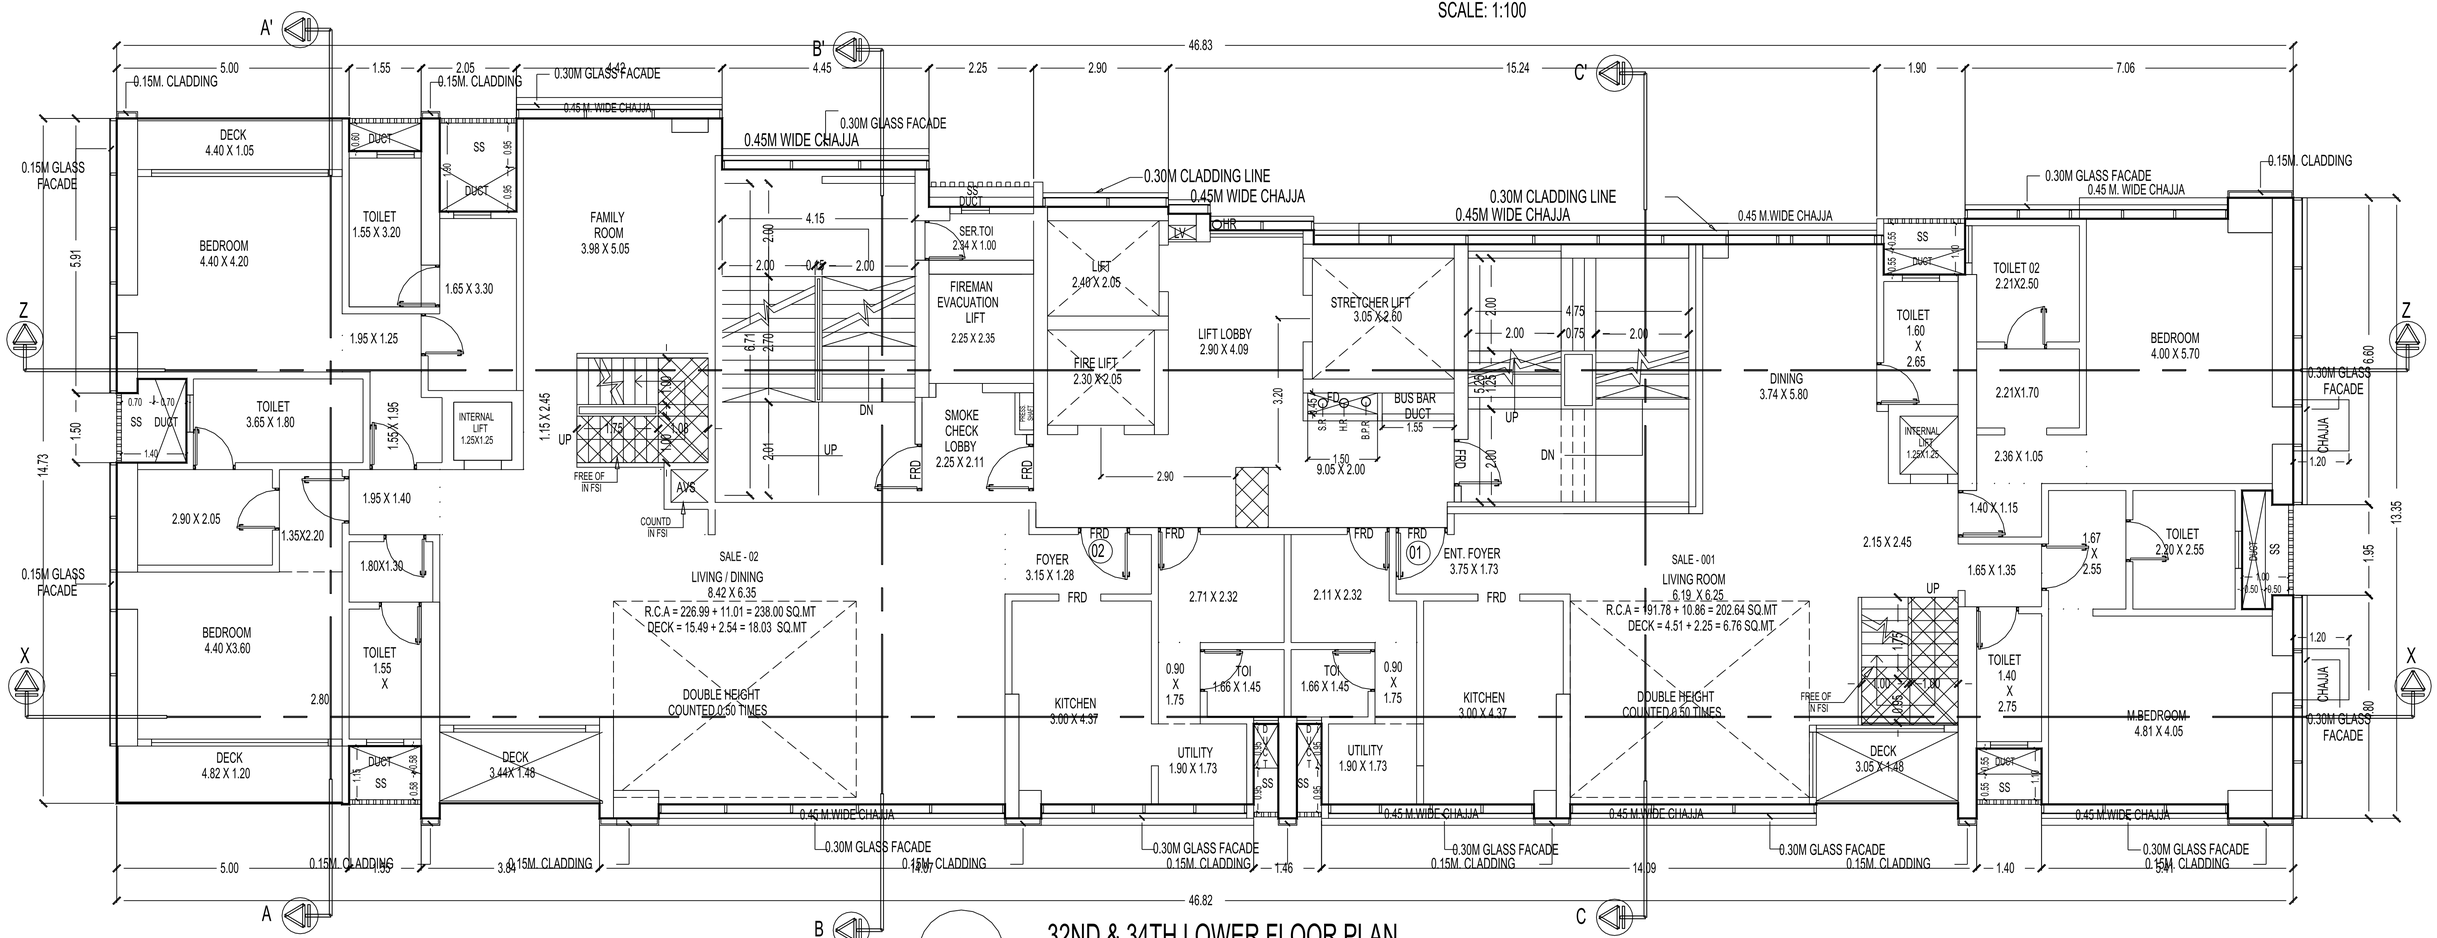

1

32ND & 34TH LOWER FLOOR PLAN

SCALE: 1:100

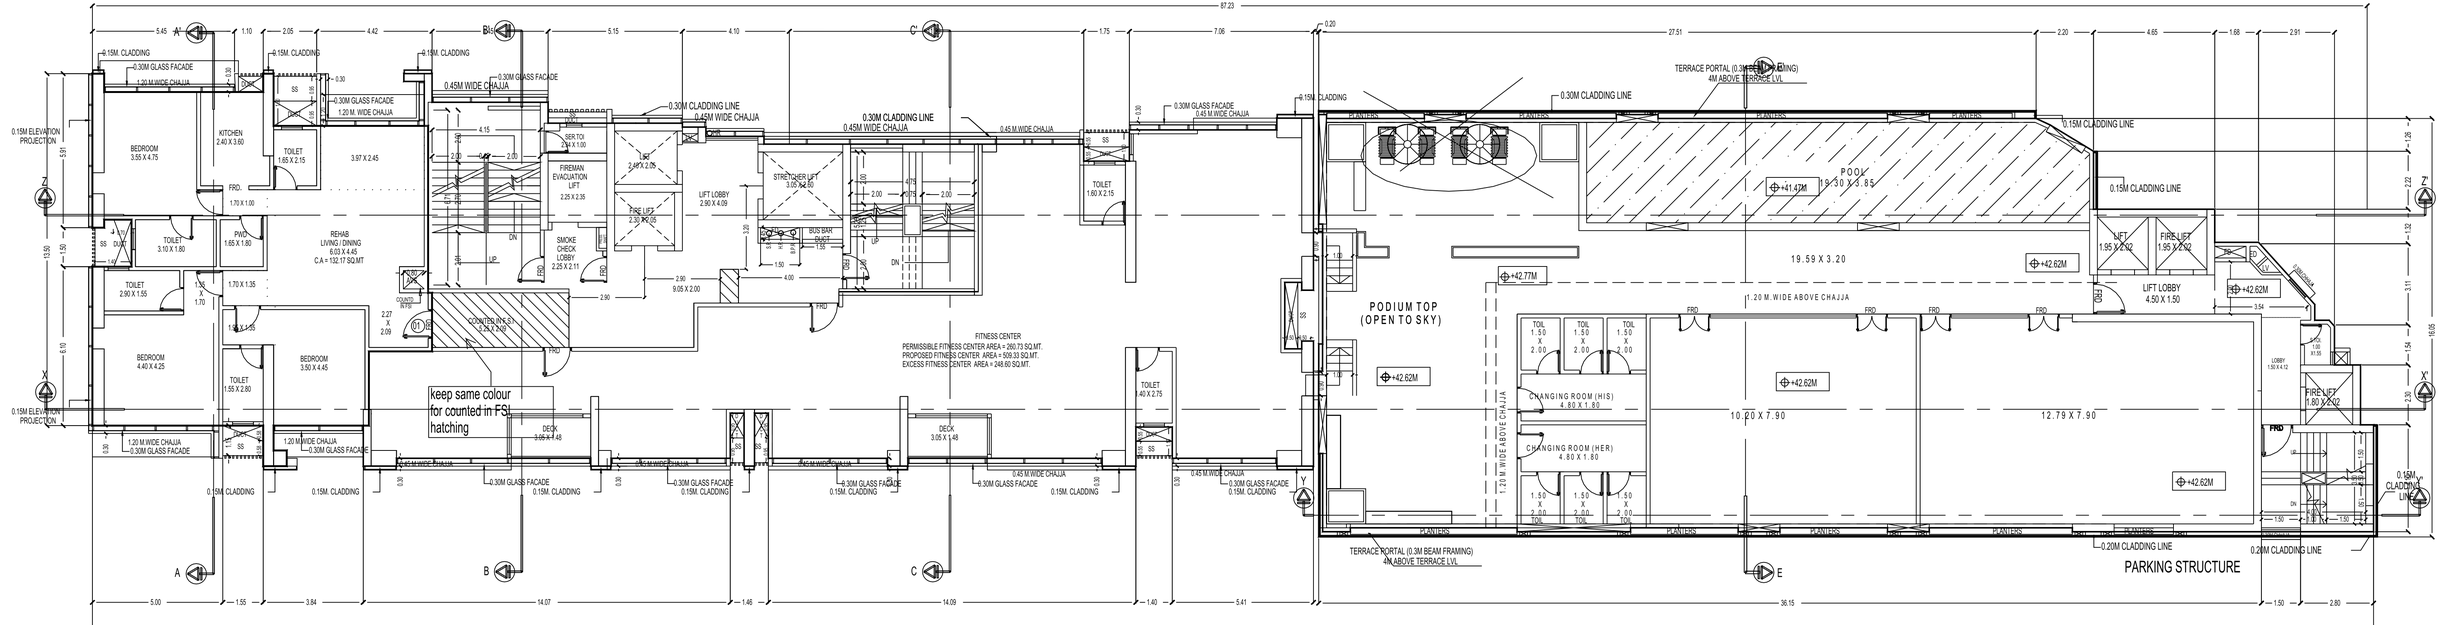

1 12TH AMENITY FLOOR PLAN

Scale: 1:100

1 AMENTY FLOOR PLAN

Scale: 1:100