
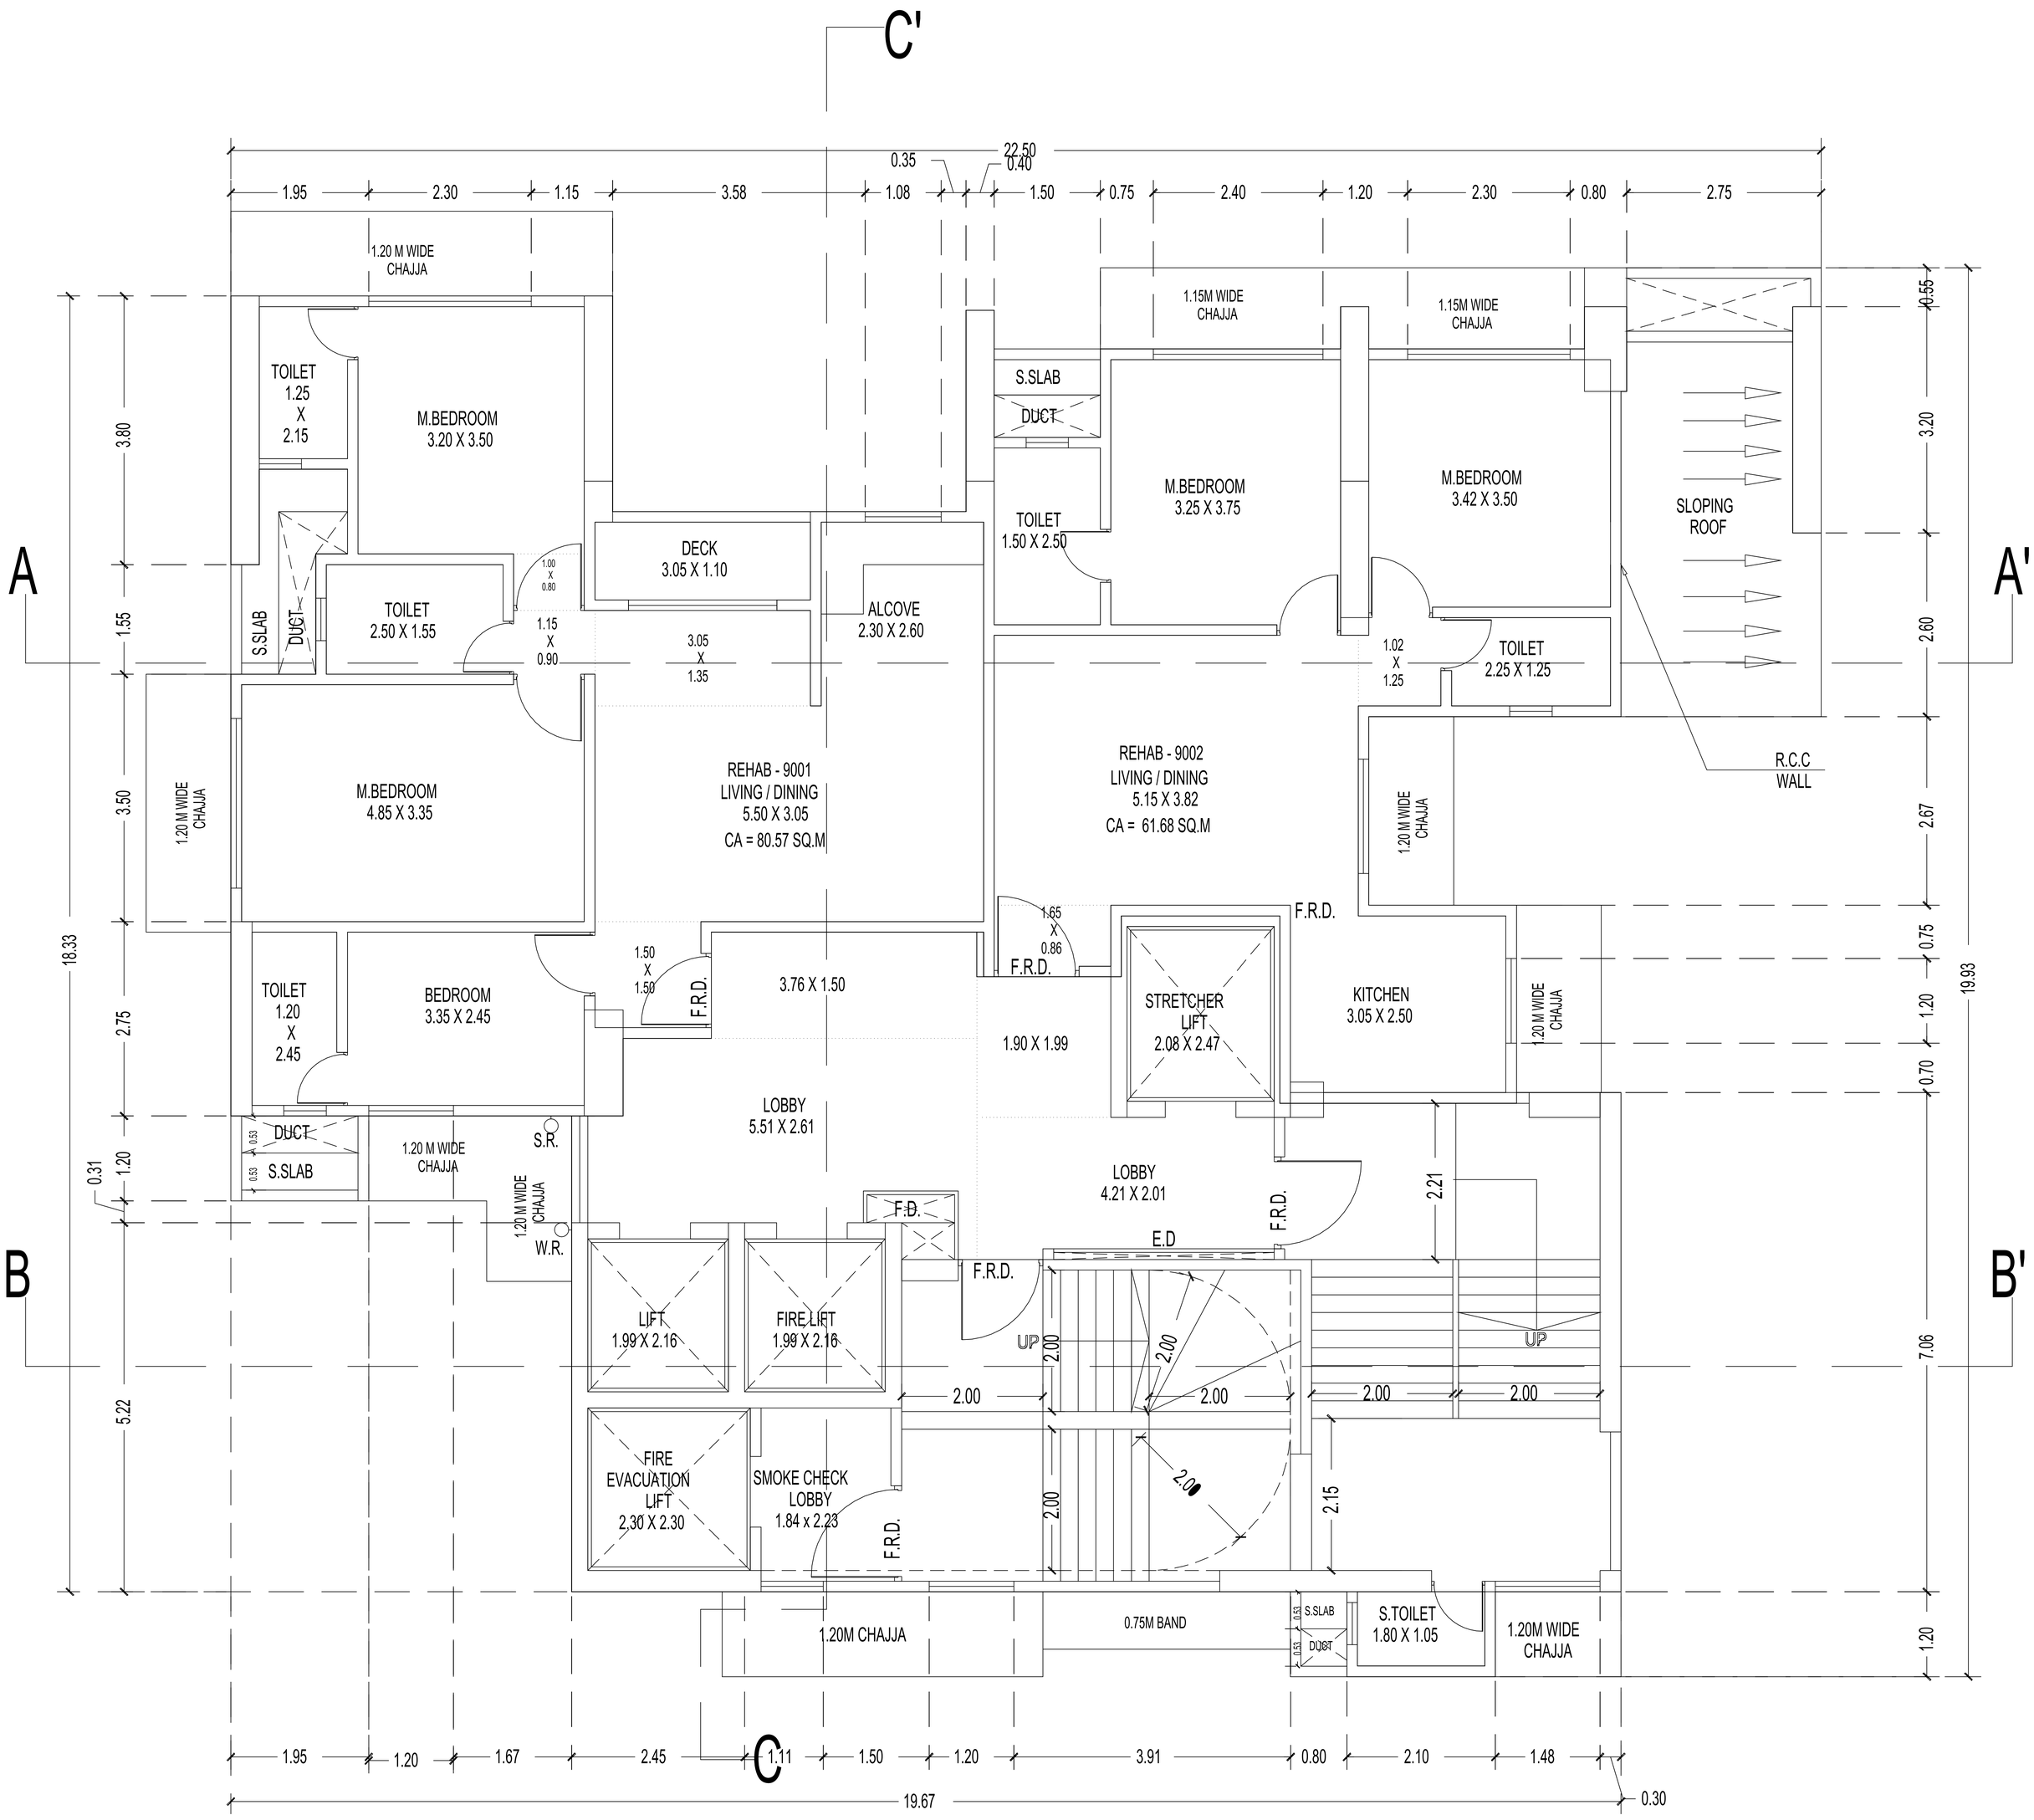


9TH FLOOR PLAN


01

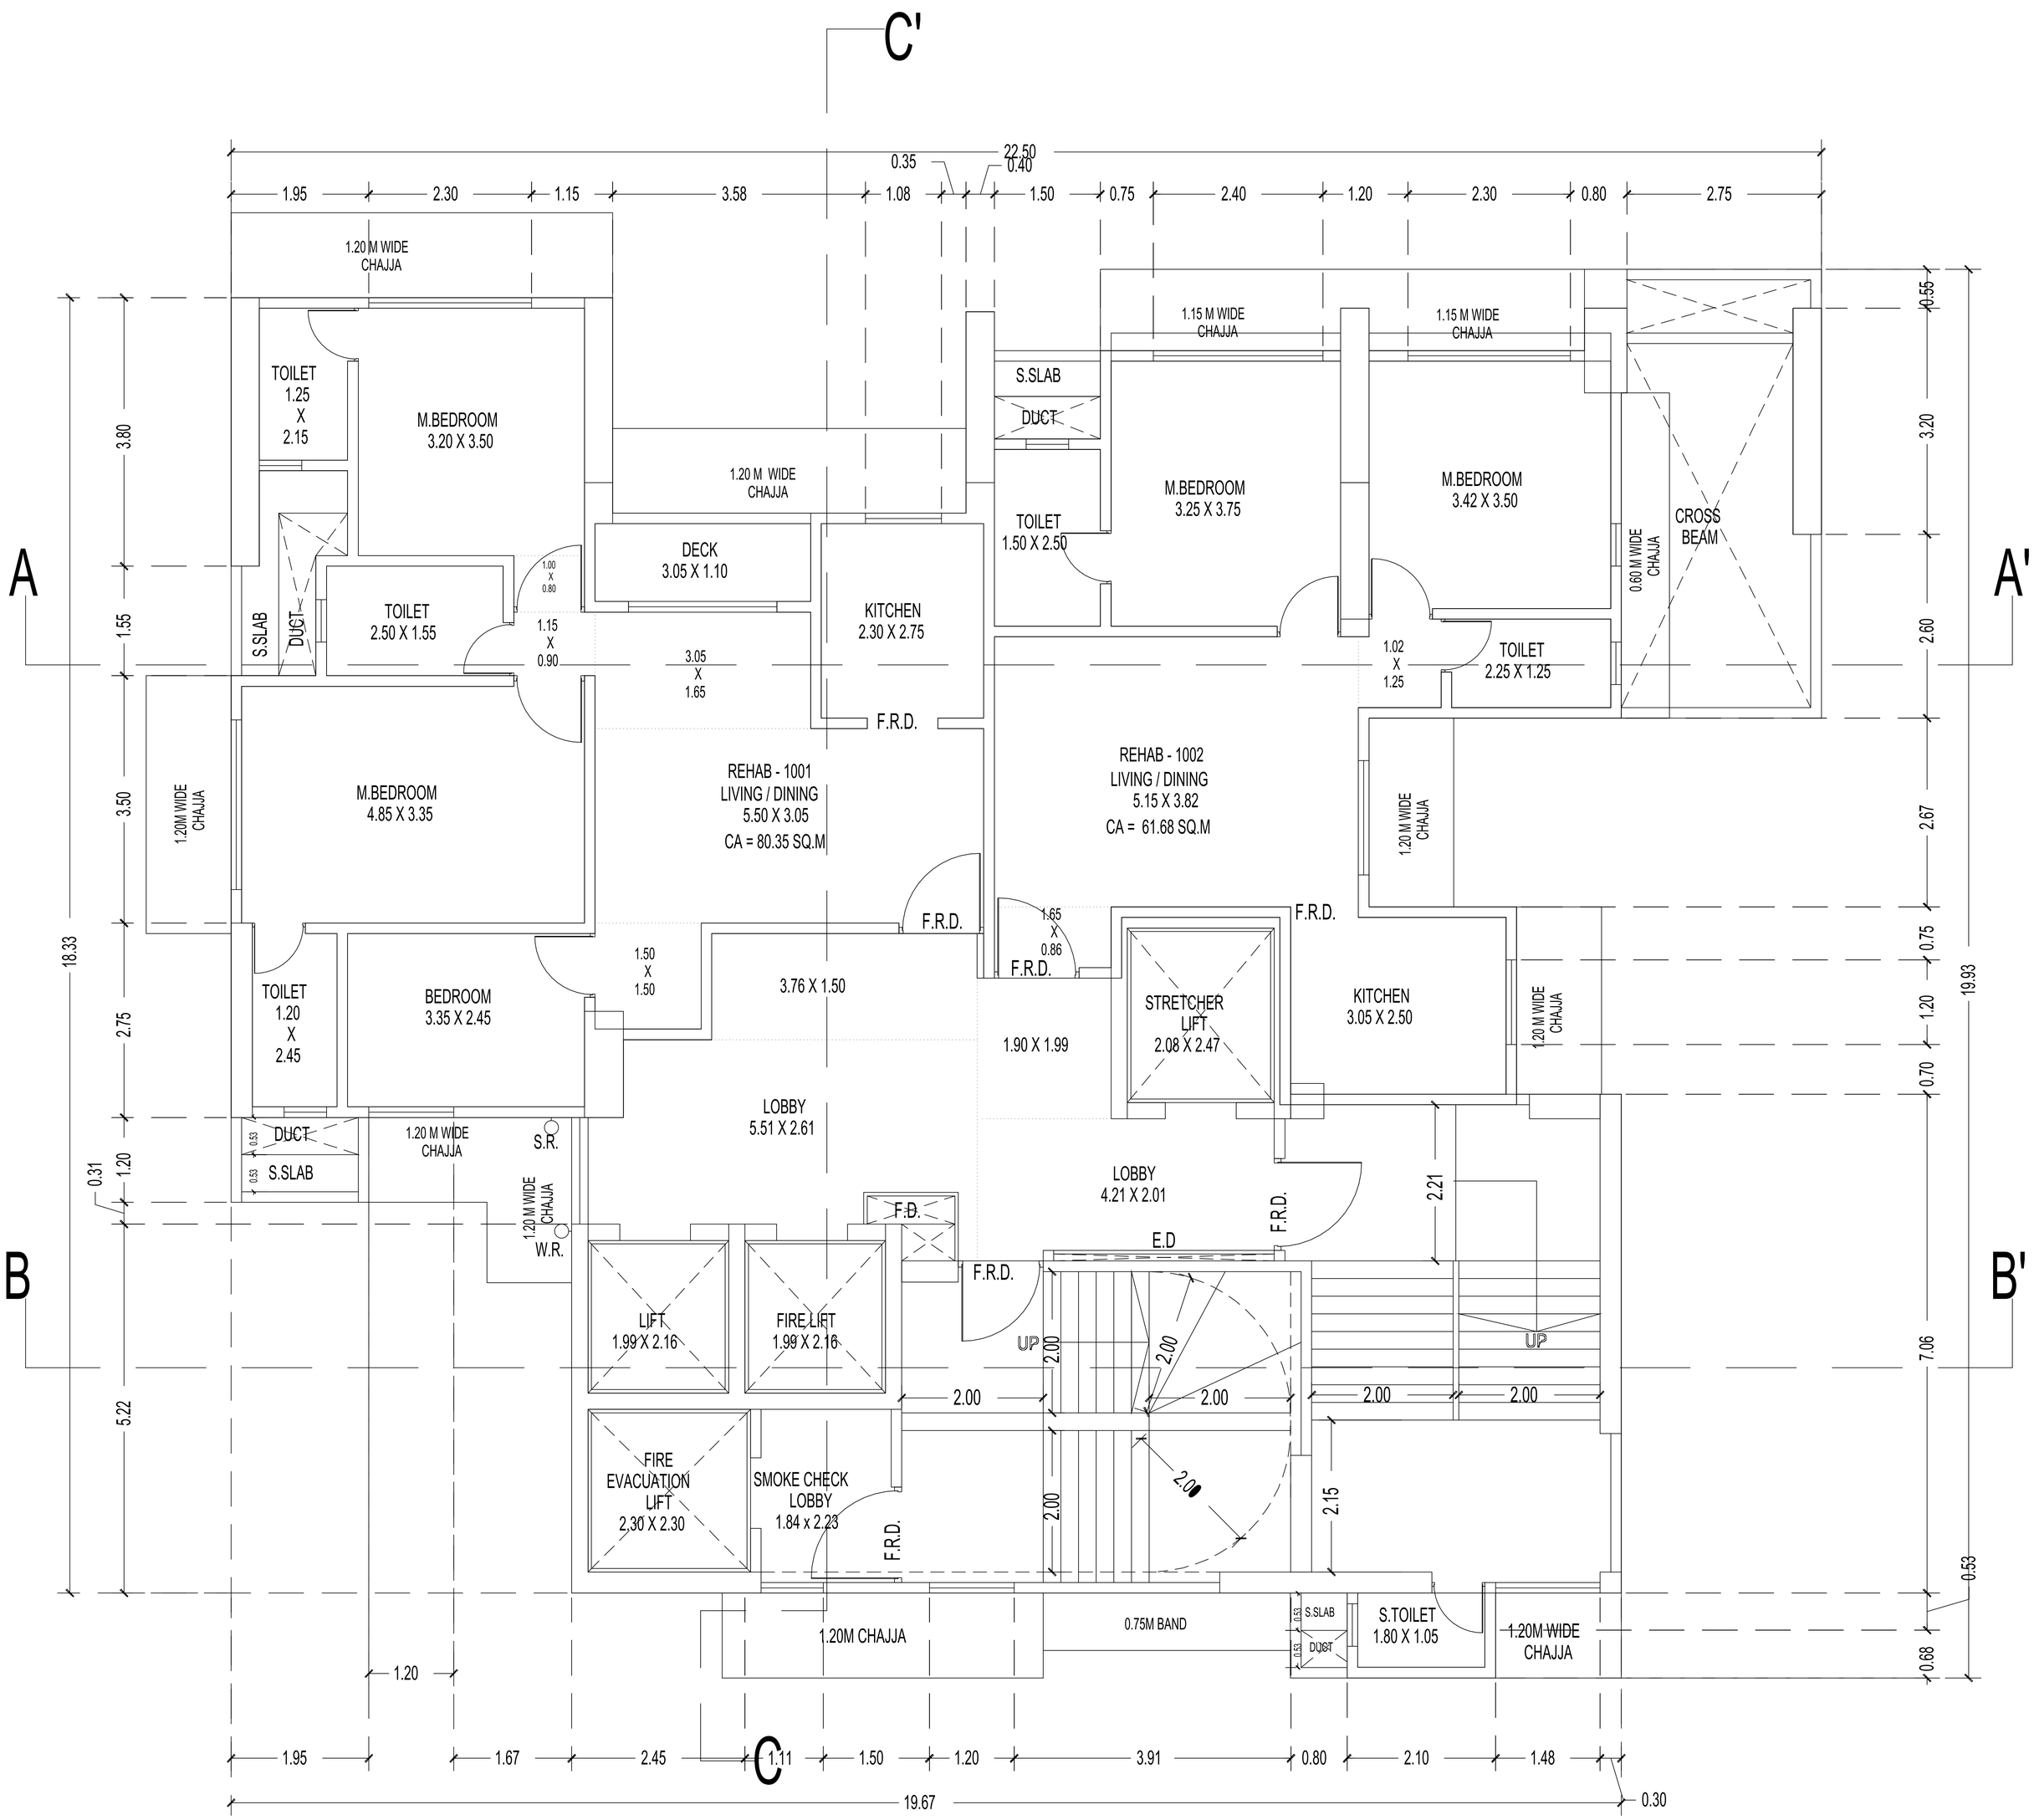

10TH FLOOR PLAN

SCALE 1:100

SCALE 1:100

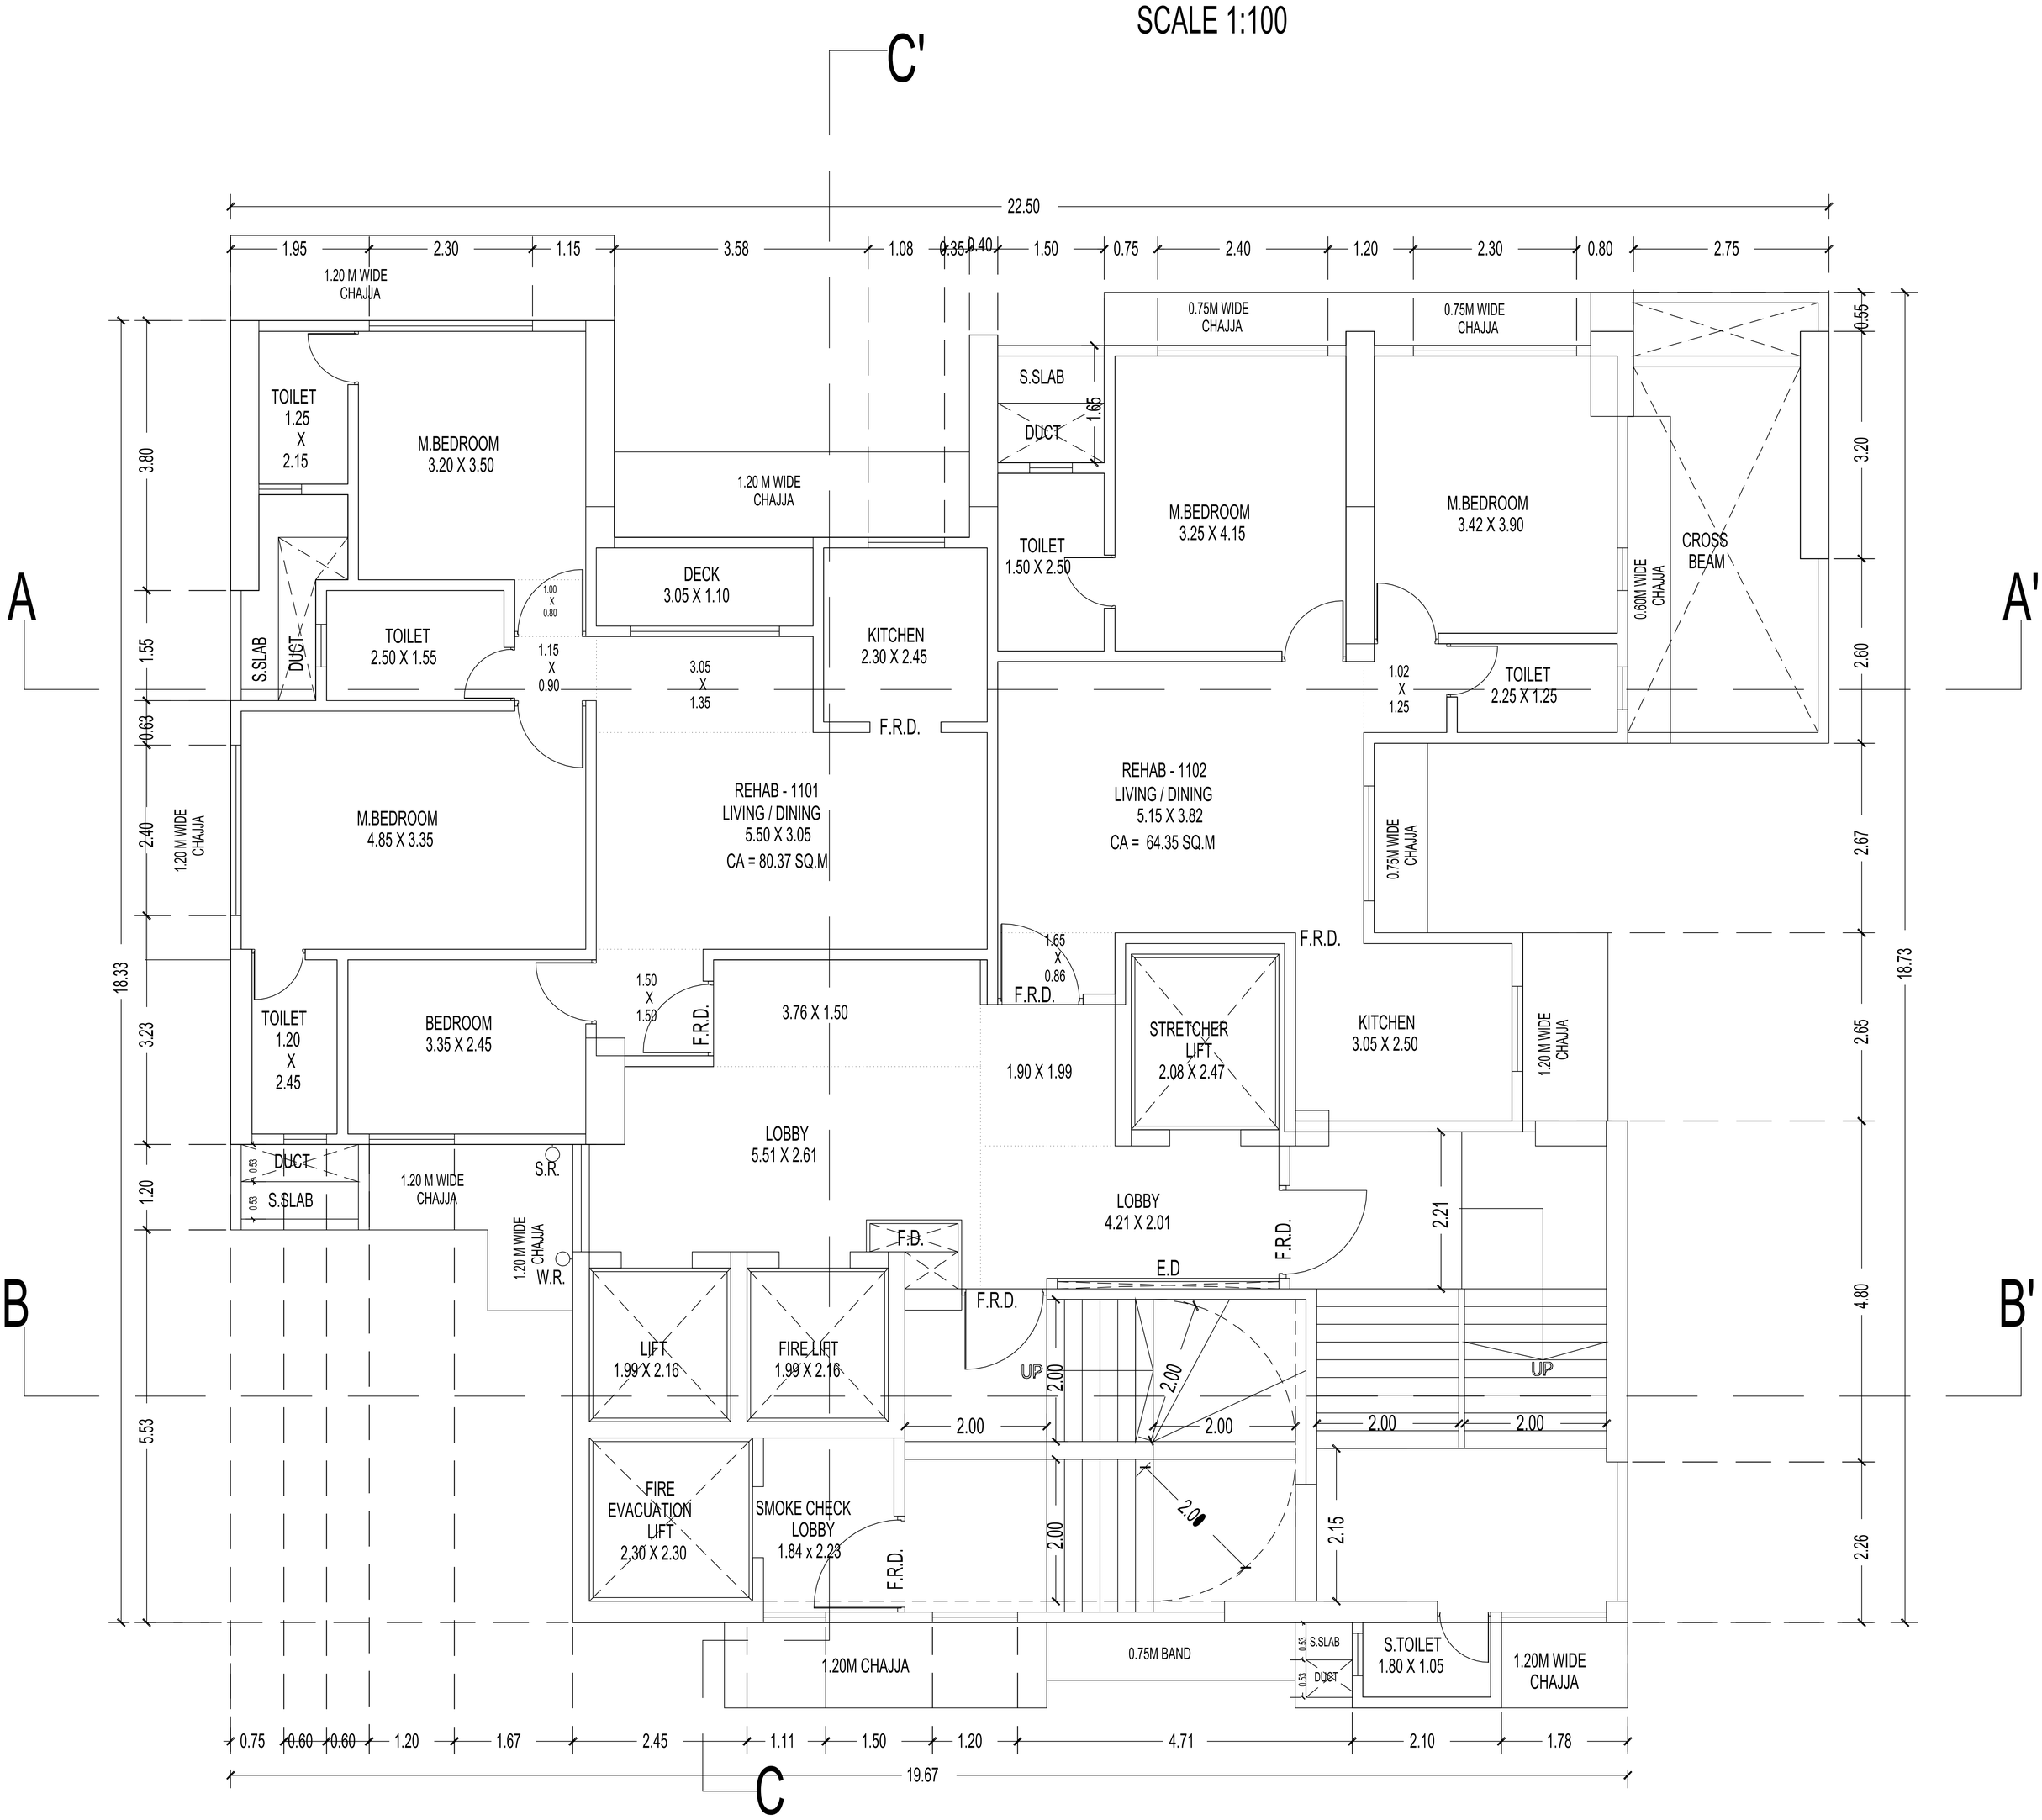


01 11TH FLOOR PLAN

SCALE 1:100

RATIO FOR 11TH FOR

COMMON AREA RATIO	COMMON AREA / NET BUA	
COMMON AREA RATIO	1.34 / 167.95	= 0.0079785650

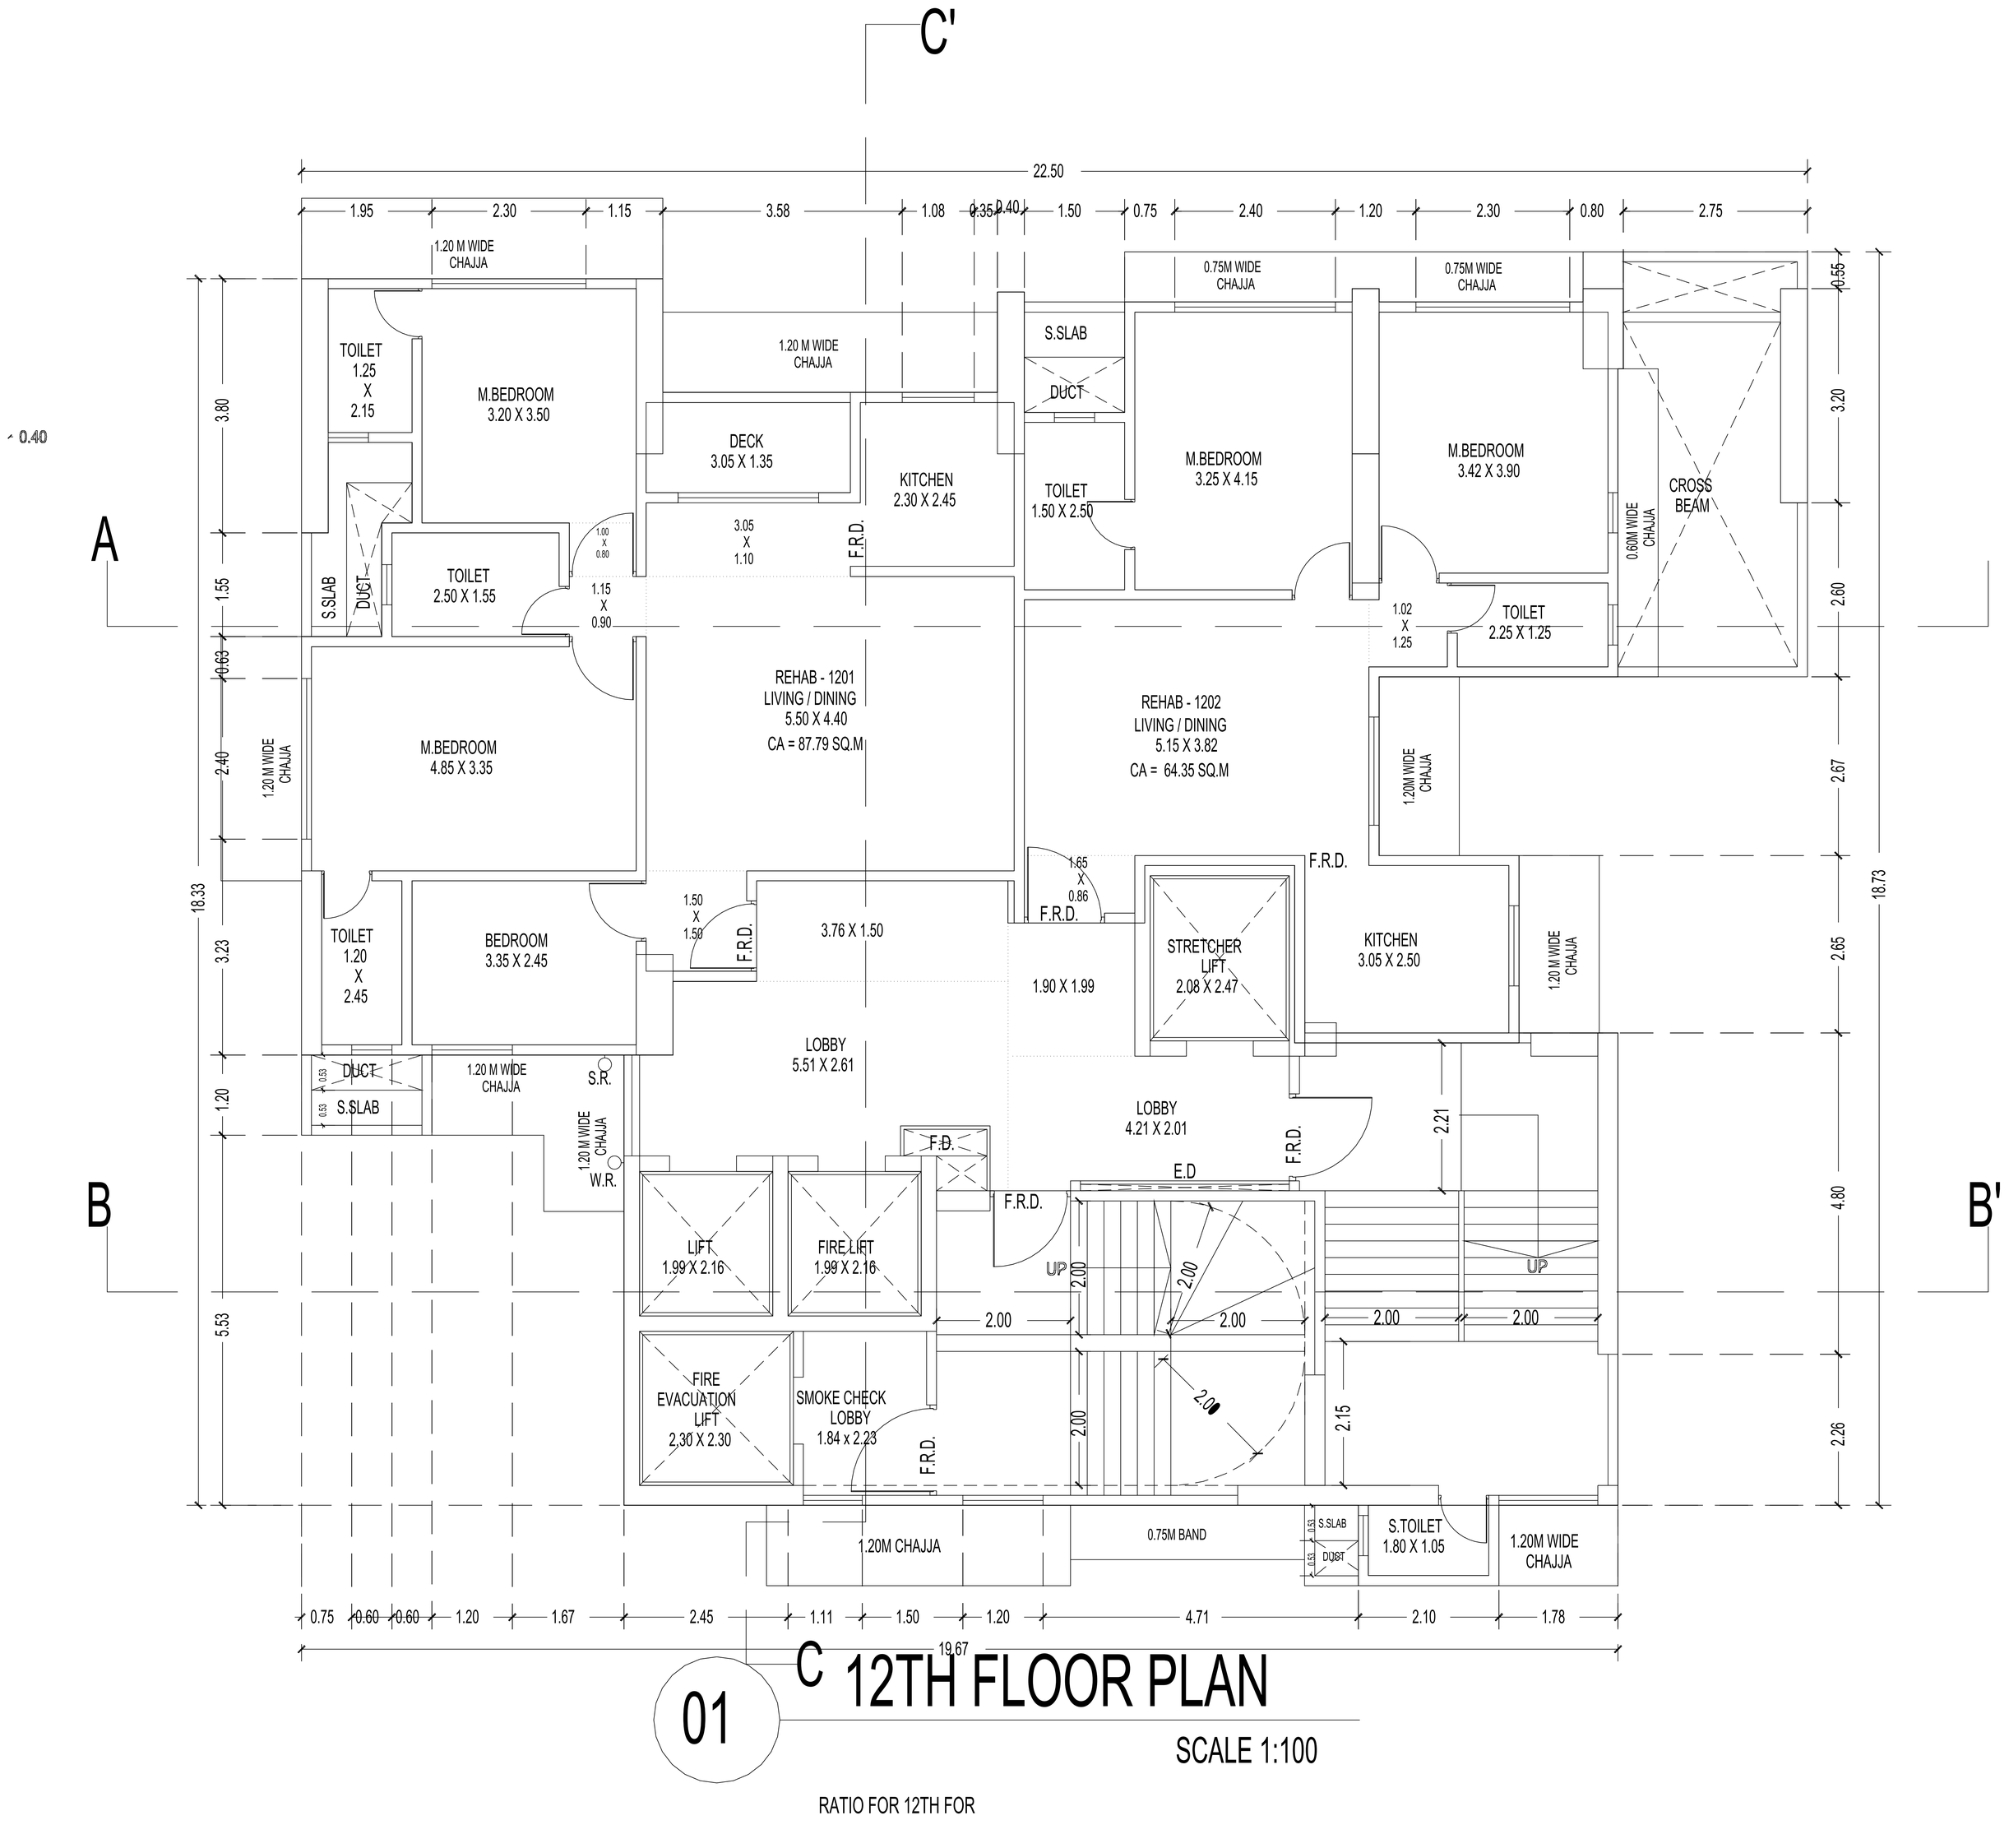


12TH FLOOR PLAN

01

SCALE 1:100

RATIO FOR 12TH FOR

COMMON AREA RATIO	COMMON AREA / NET BUA
COMMON AREA RATIO	1.34 / 174.70 = 0.0076702919

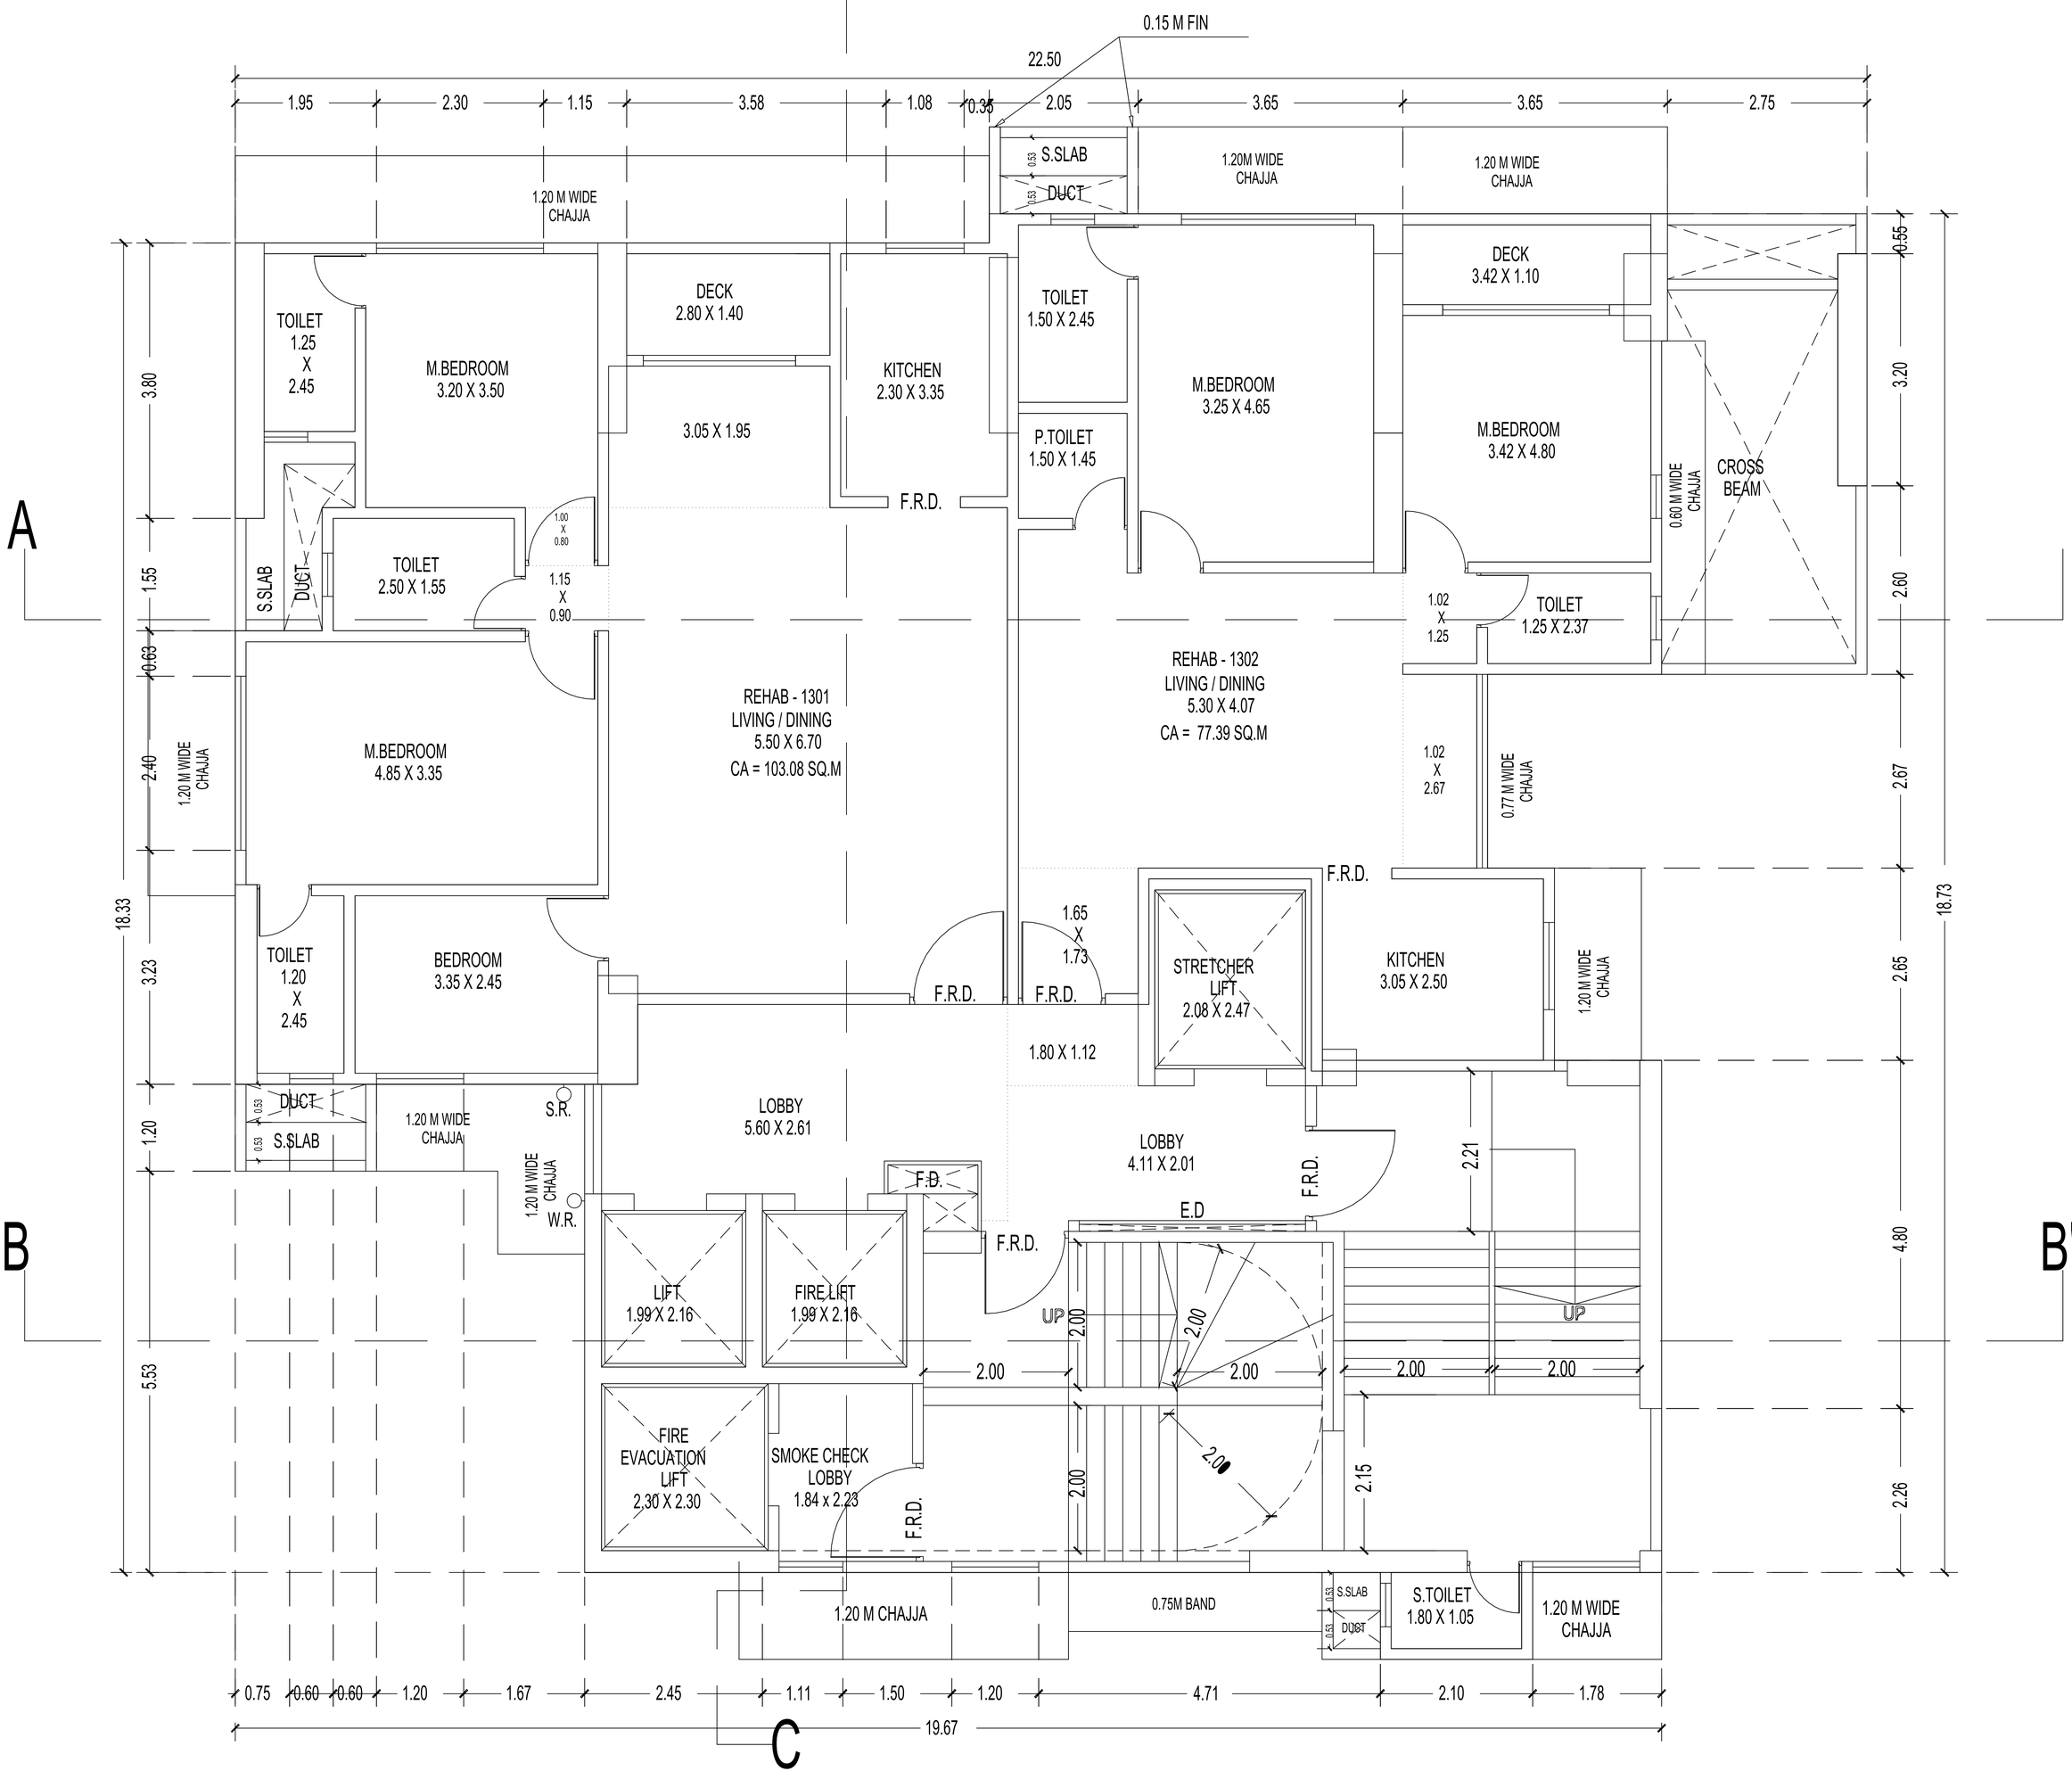


01 13TH FLOOR PLAN

SCALE 1:100

RATIO FOR 12TH FOR

COMMON AREA RATIO	COMMON AREA / NET BUA
COMMON AREA RATIO	1.28 / 203.40 = 0.0062930187

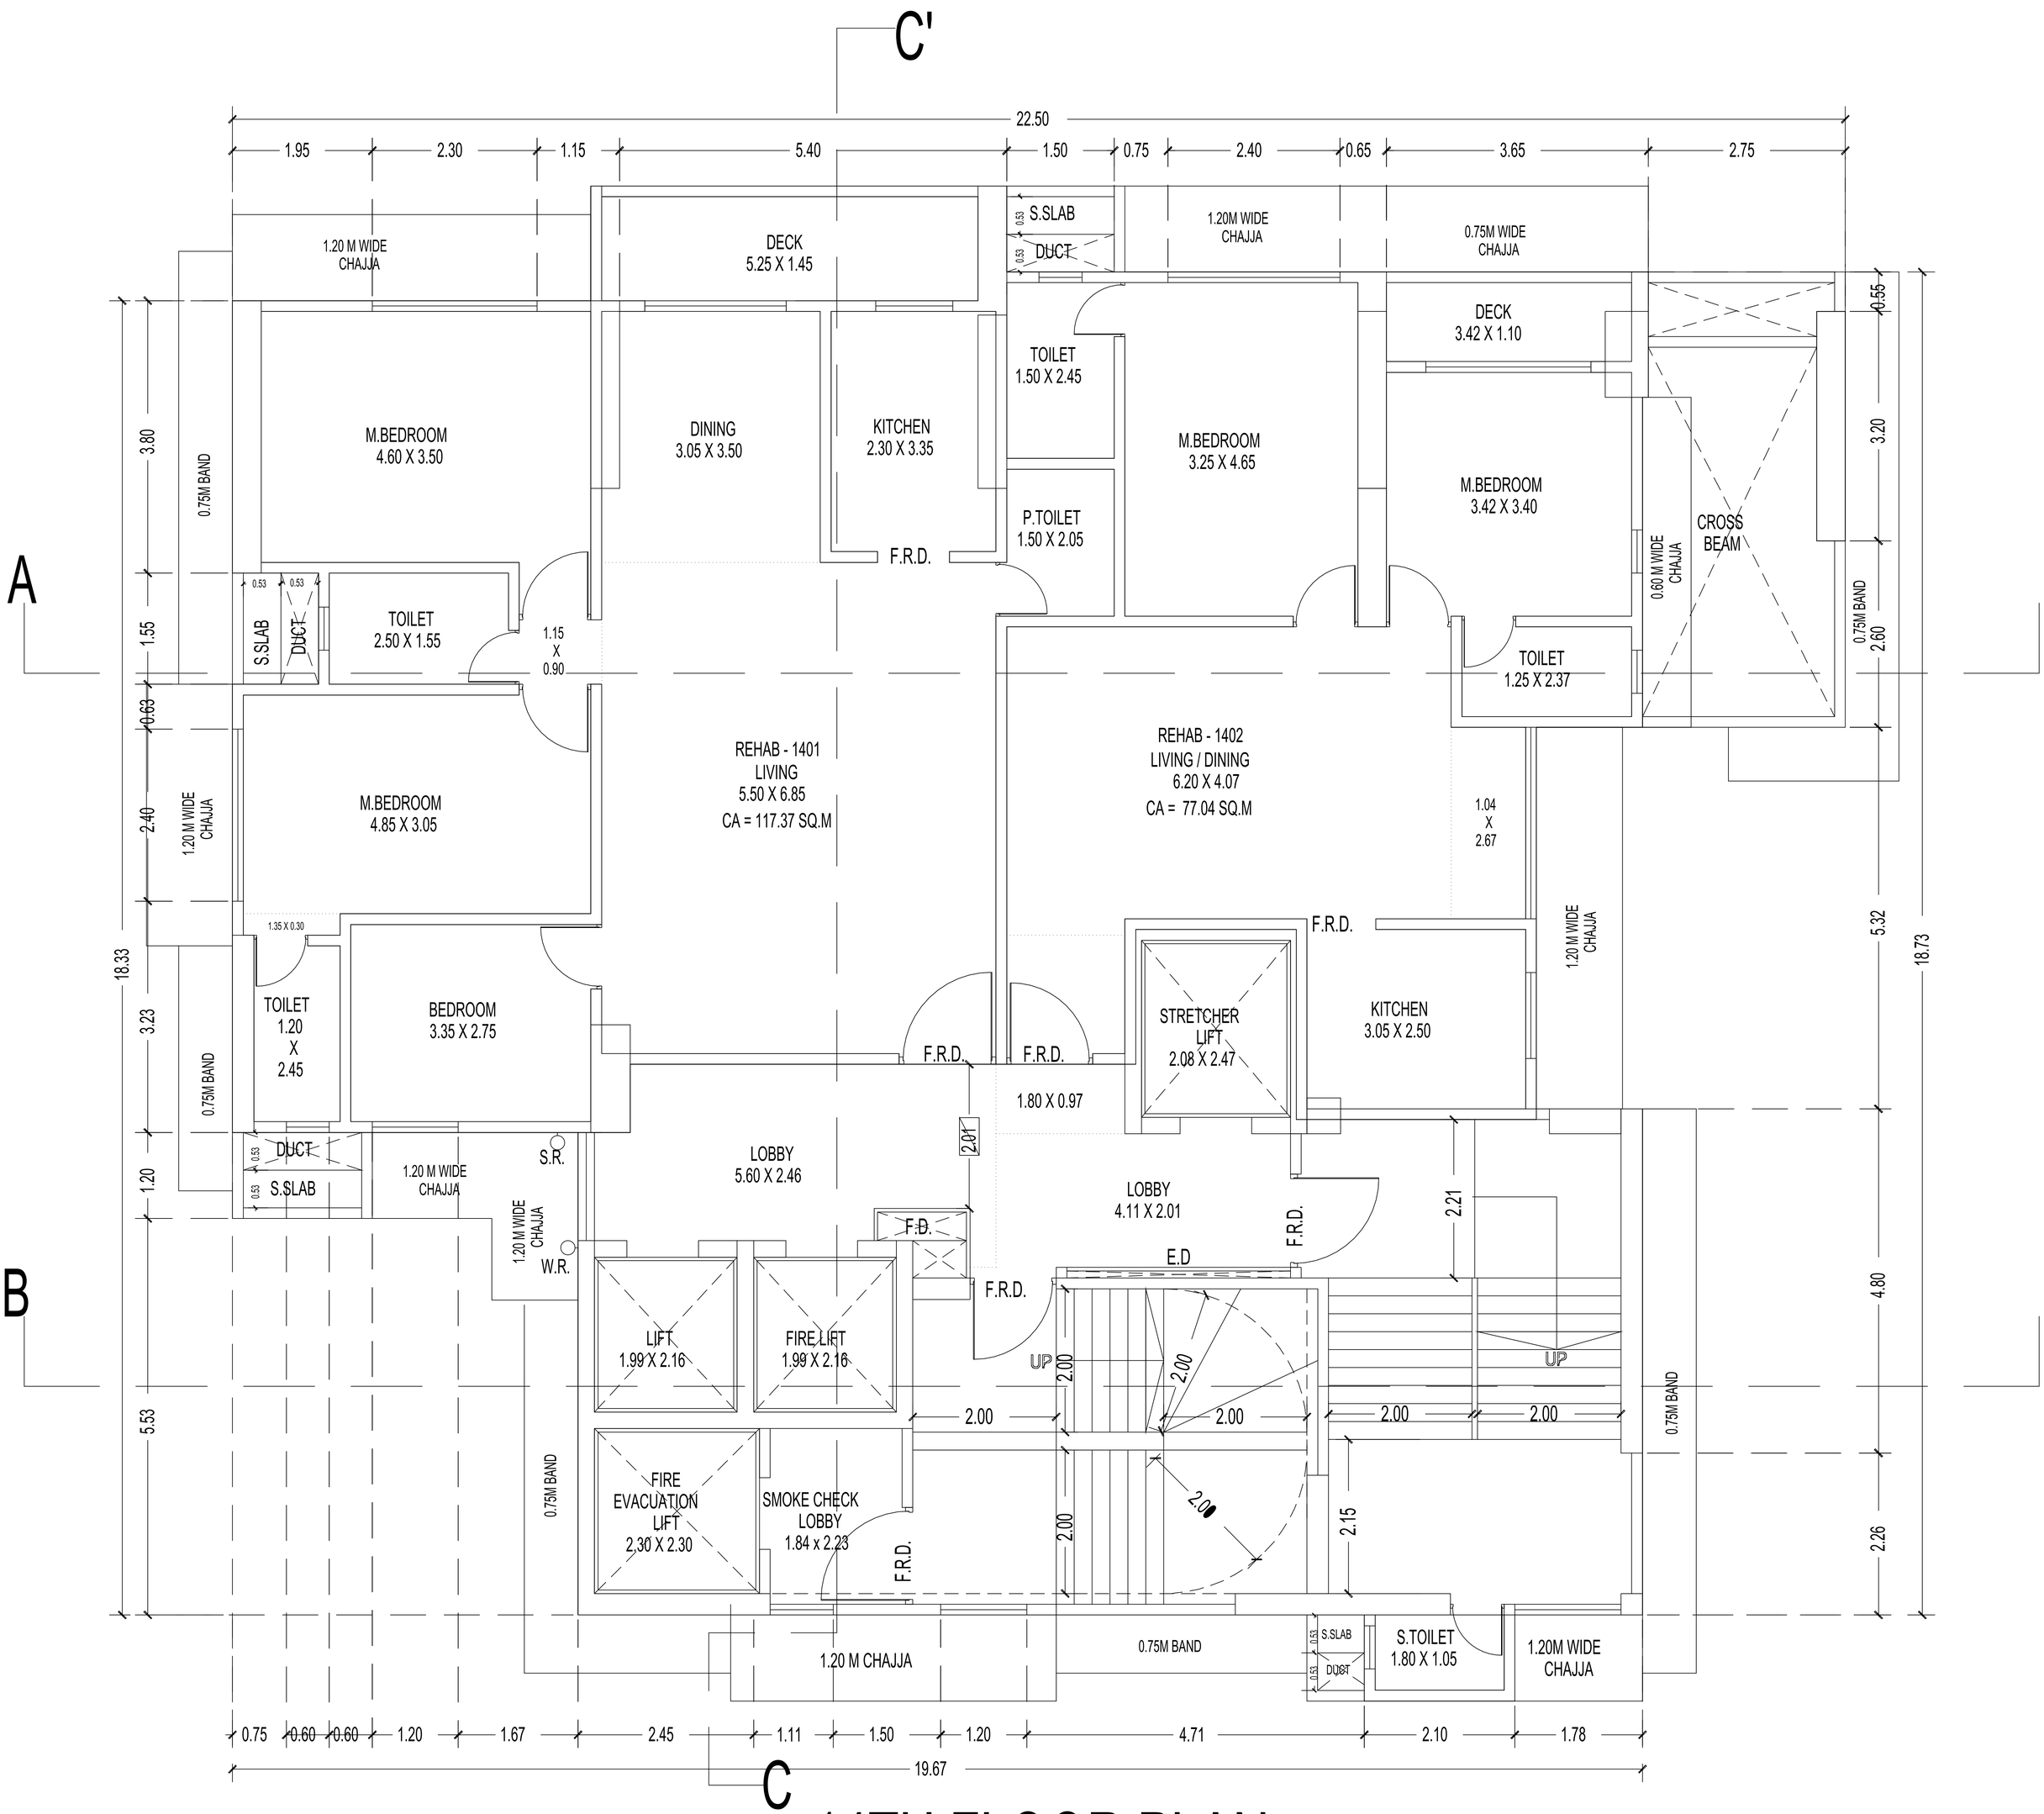


14TH FLOOR PLAN

01

SCALE 1:100

RATIO FOR 14TH FOR


COMMON AREA RATIO	COMMON AREA / NET BUA	
COMMON AREA RATIO	1.28 / 217.28	= 0.0058910162

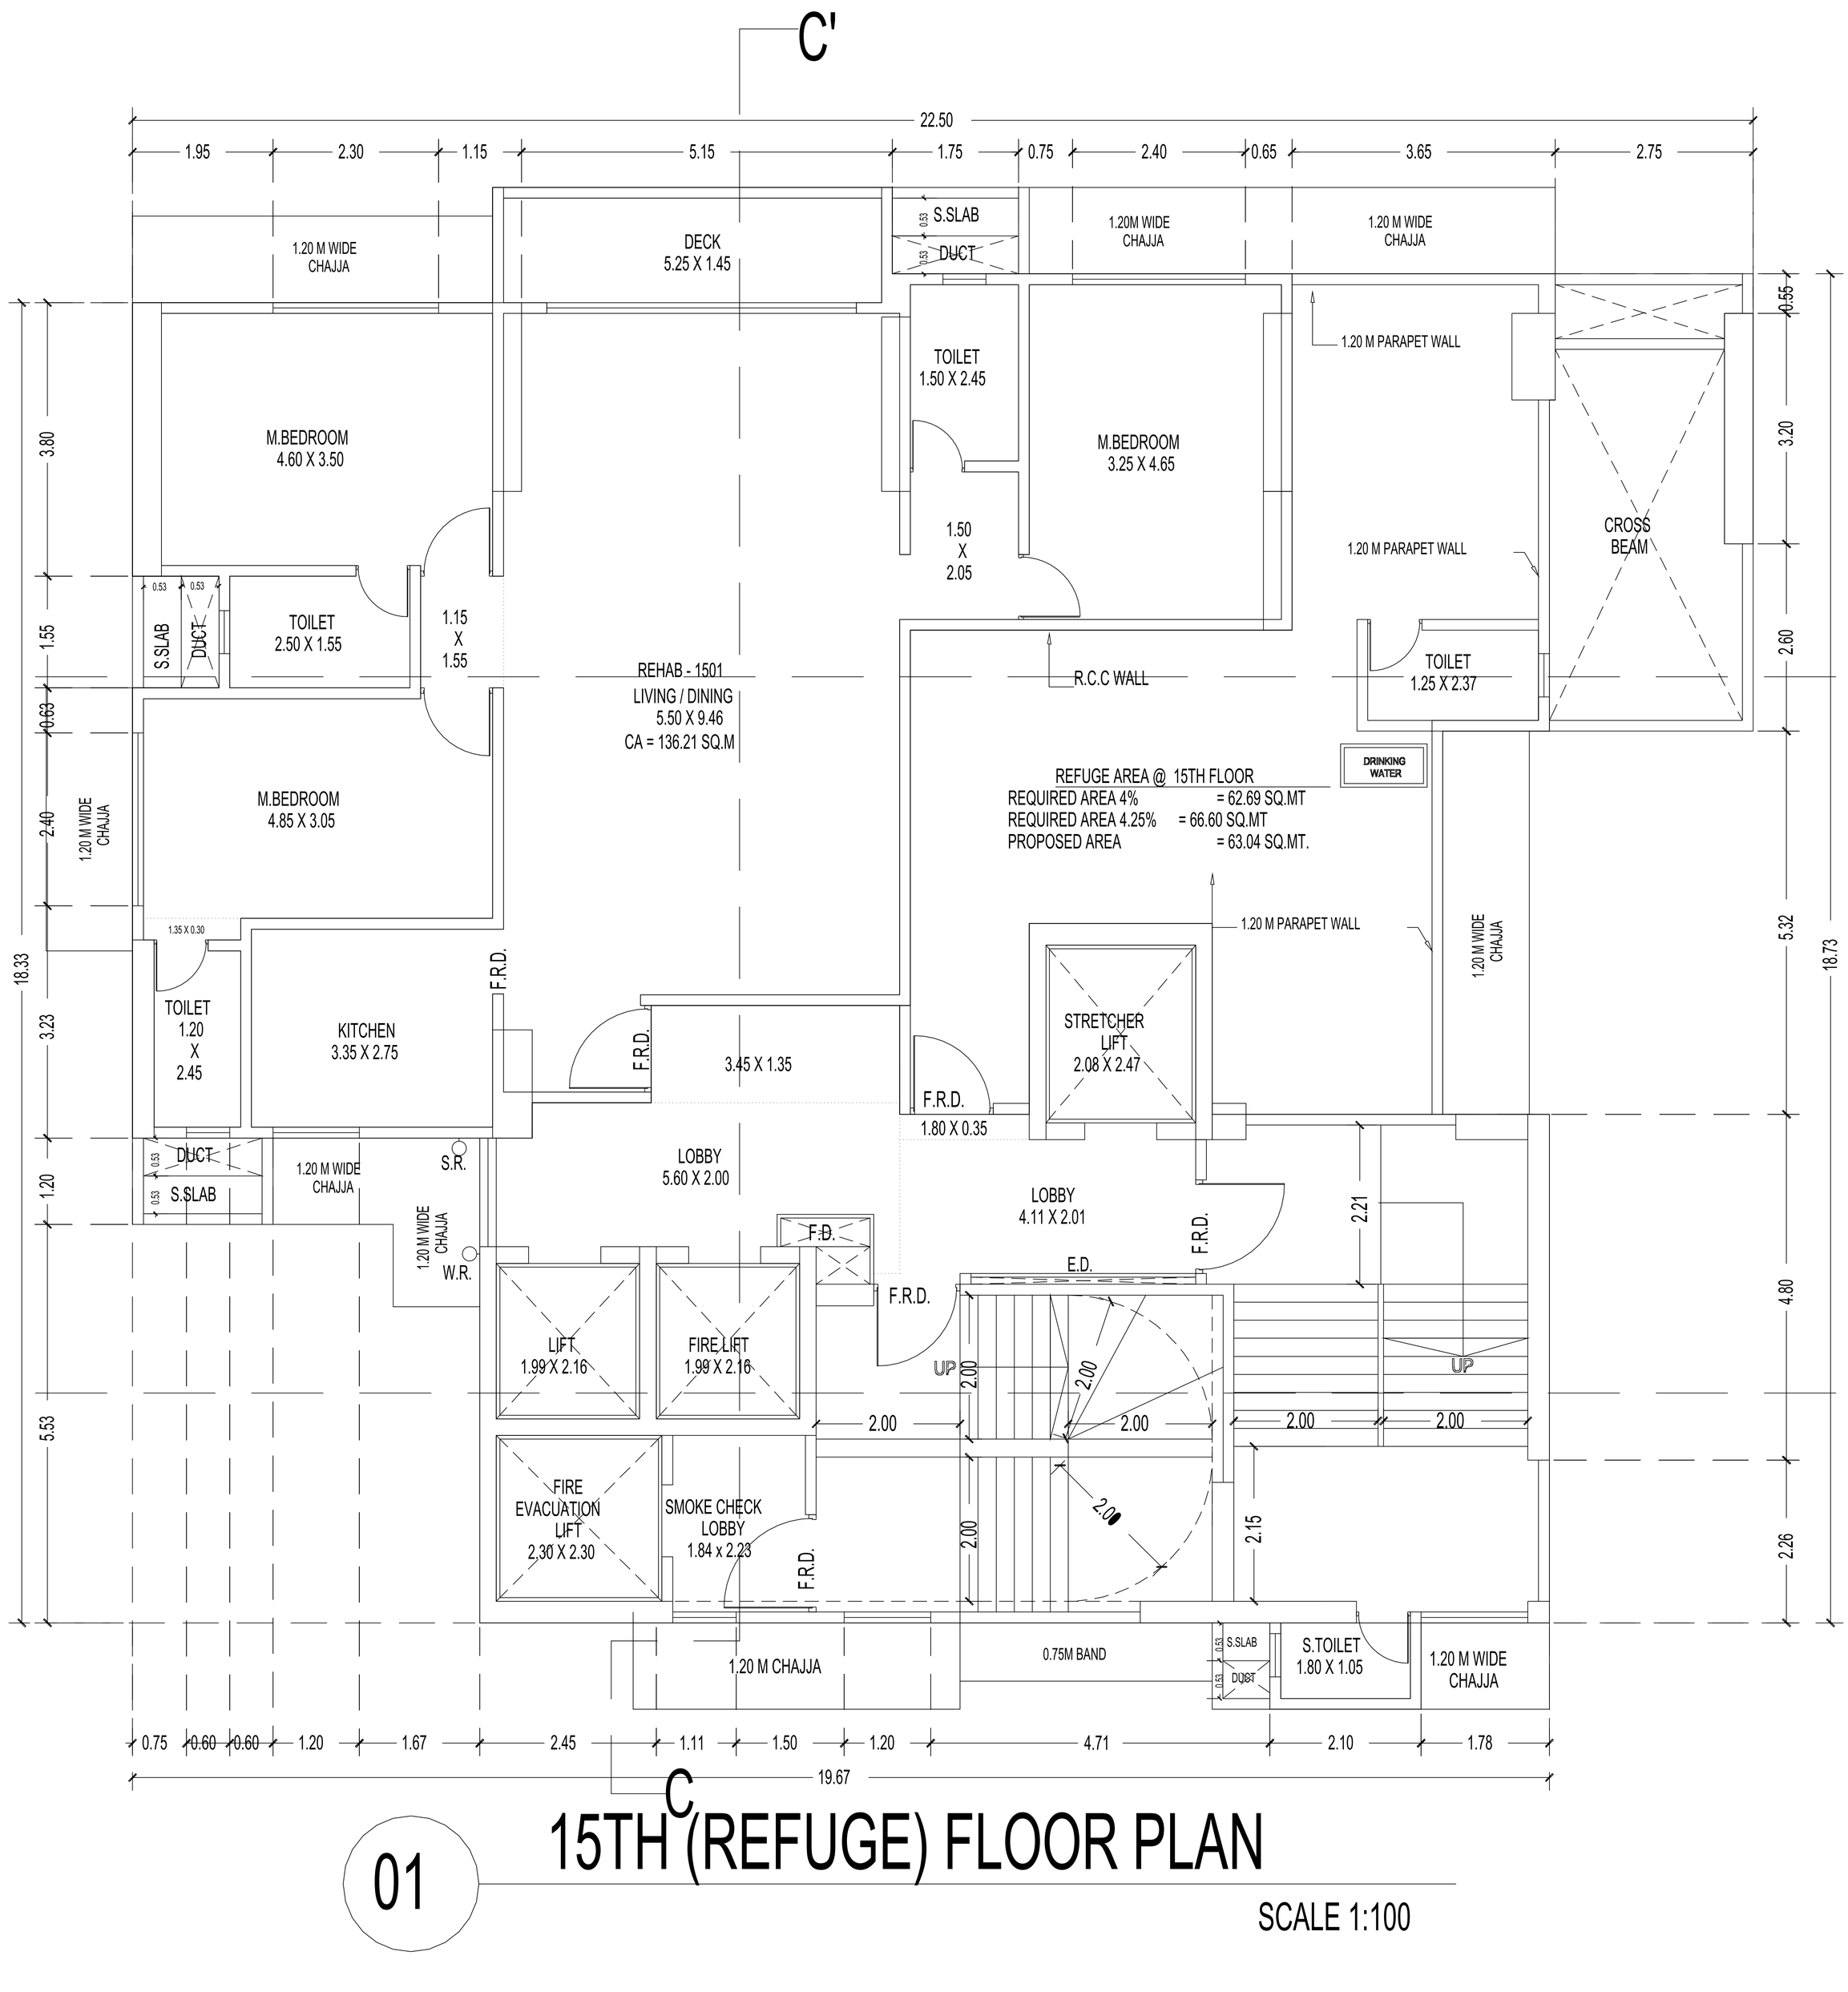

15TH (REFUGE) FLOOR PLAN

01

SCALE 1:100

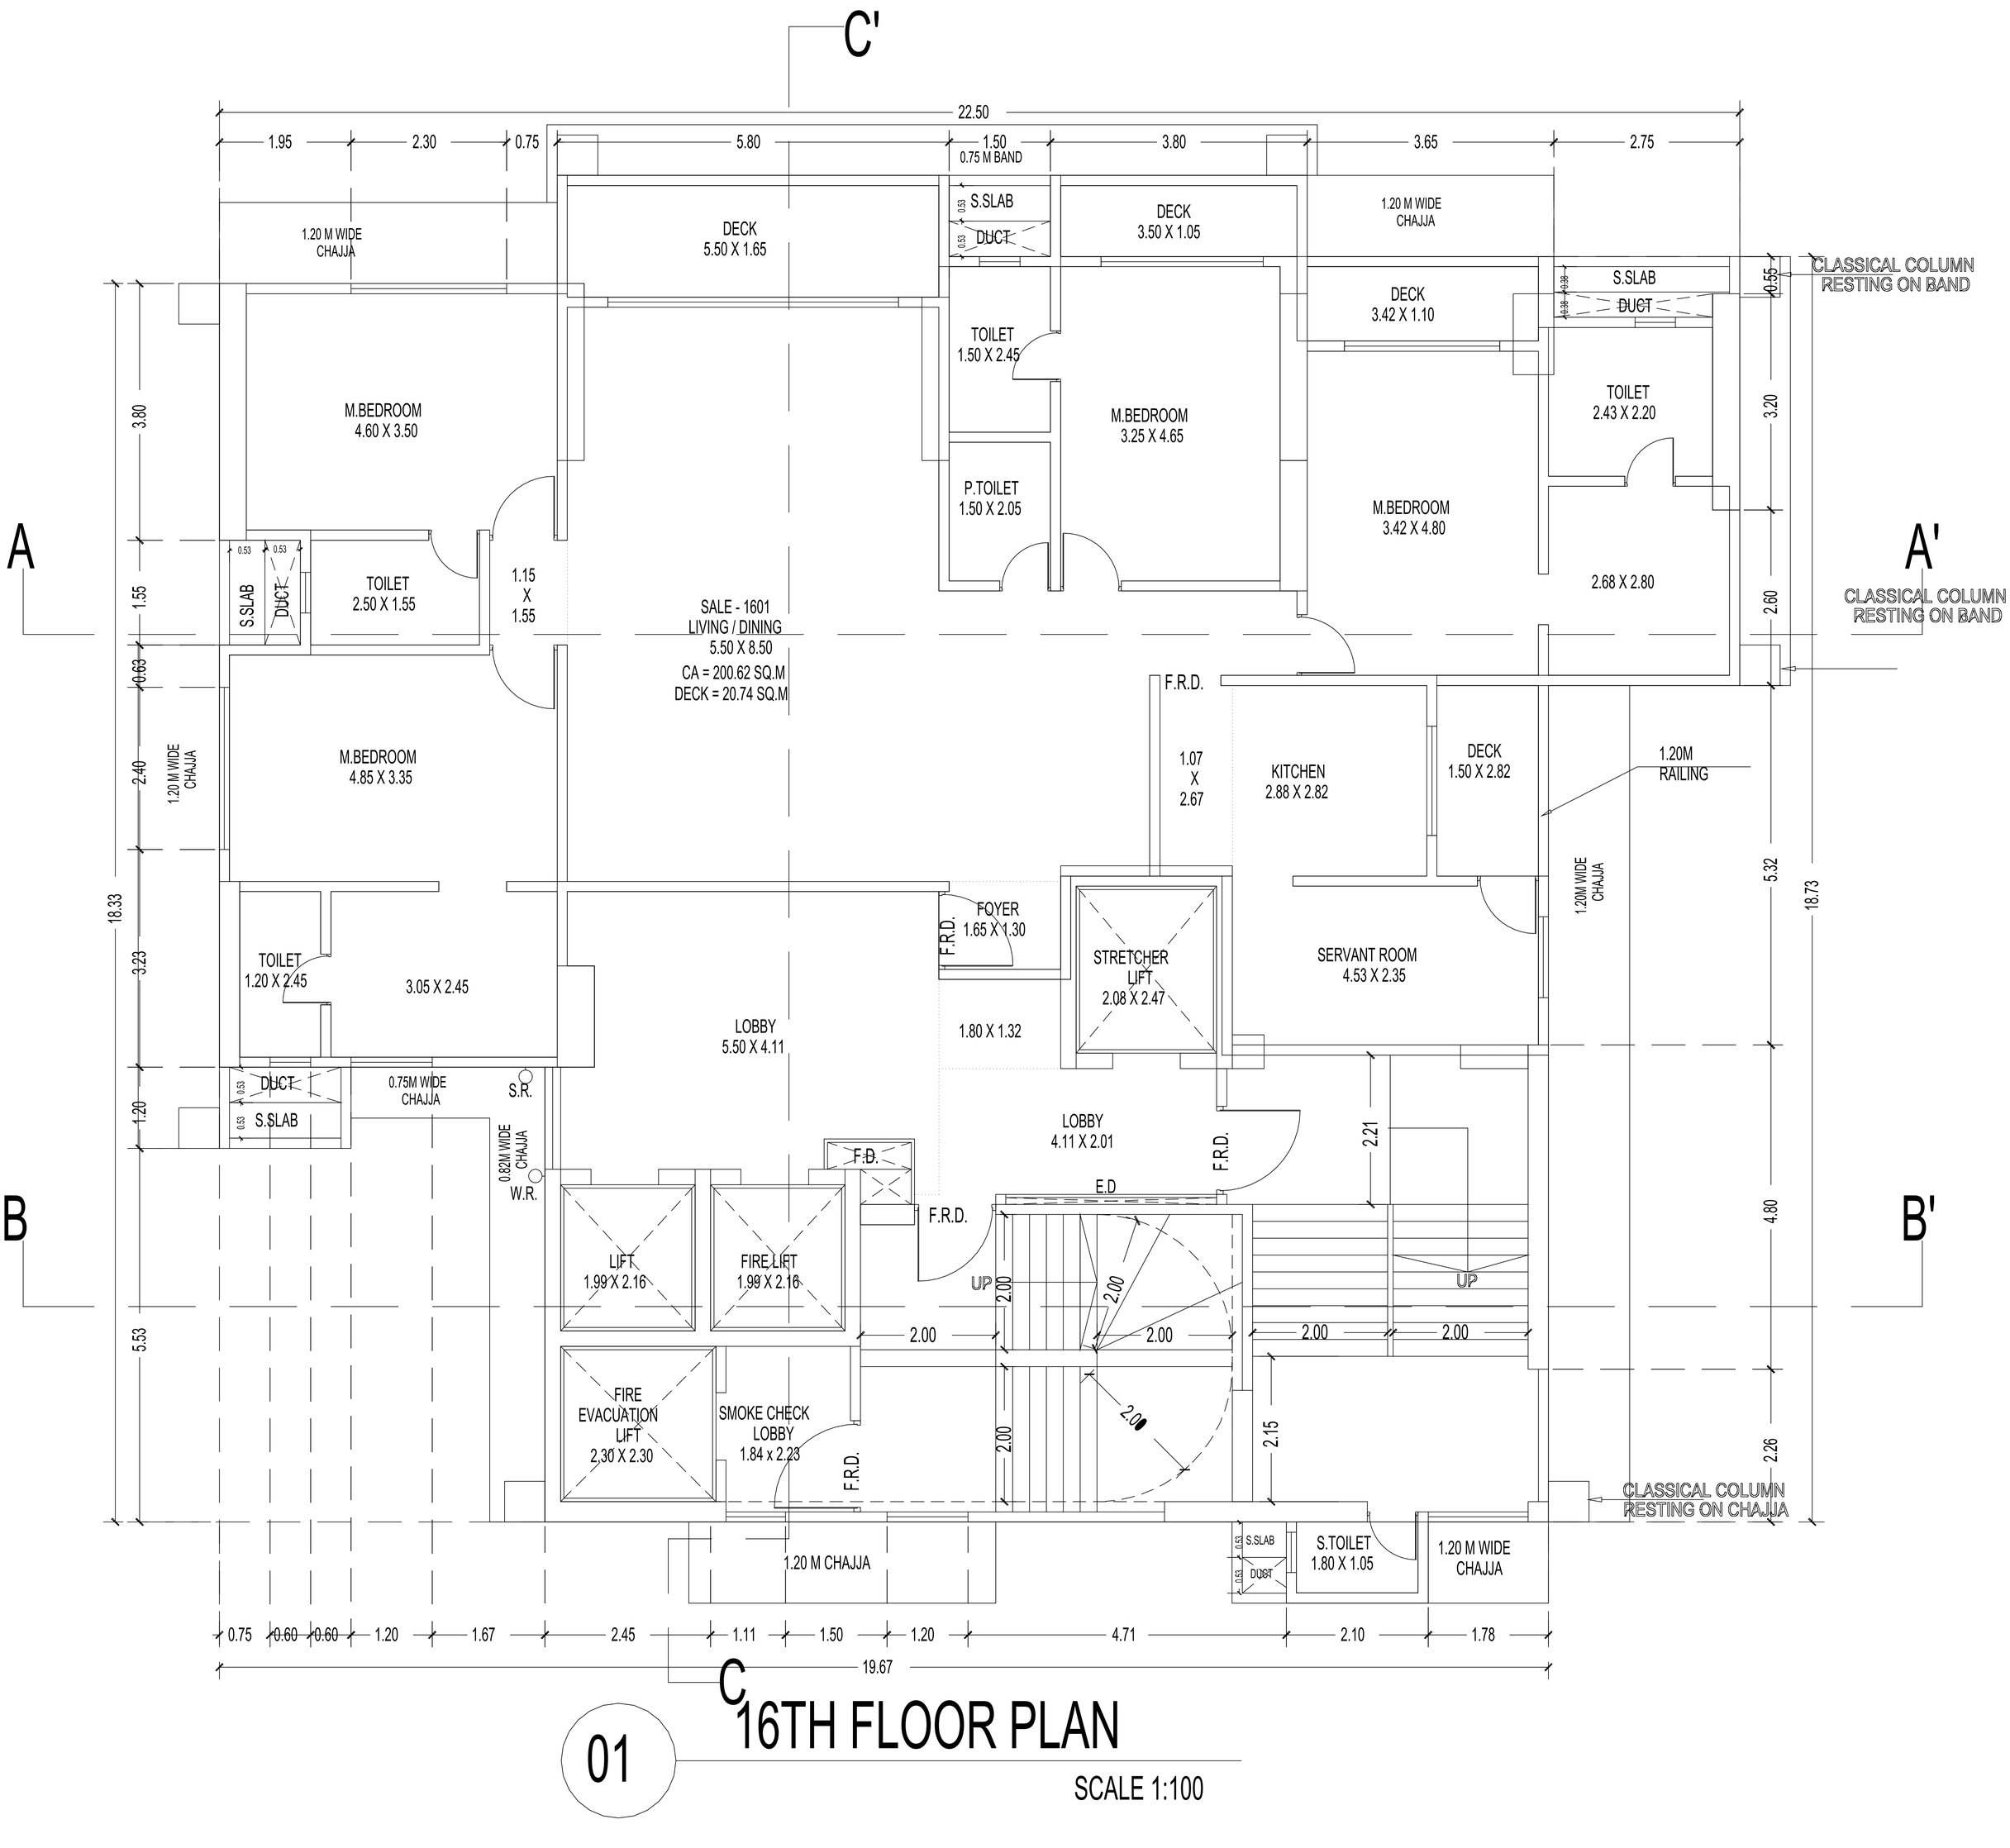

16TH FLOOR PLAN

01

SCALE 1:100

C'

22.50

1.95 | 2.30 | 0.75 | 5.80 | 0.75M BAND | 1.50 | 3.80 | 3.65 | 2.75

1.20 M WIDE CHAJJA

DECK 5.50 X 1.65

S.SLAB 0.53 / DUCT 0.53

DECK 3.50 X 1.05

1.20 M WIDE CHAJJA

CLASSICAL COLU RESTING ON BAN

DECK 3.42 X 1.10

S.SLAB 0.38 / DUCT 0.38

0.55

TOILET 1.50 X 2.45

M.BEDROOM 4.60 X 3.50

M.BEDROOM 3.25 X 4.65

TOILET 2.43 X 2.20

3.20

0.40

3.80

0.75M BAND (ON 19TH & 24TH FLR)

P.TOILET 1.50 X 2.05

M.BEDROOM 3.42 X 4.80

A

A'

0.75M BAND

S.SLAB 0.53 / DUCT 0.53

TOILET 2.50 X 1.55

1.15 X 1.55

SALE - 1701 TO 2101, 2301 TO 2801, 3001 TO 3201
LIVING / DINING
5.50 X 8.50
CA = 200.62 SQ.M
DECK = 20.74 SQ.M

2.68 X 2.80

1.55

2.60

CLASSICAL COLU RESTING ON BA

0.63

F.R.D.

1.07 X 2.67

KITCHEN 2.88 X 2.82

DECK 1.50 X 2.82

1.20M HT RAILING

2.40

1.20 M WIDE CHAJJA

M.BEDROOM 4.85 X 3.35

1.20M WIDE CHAJJA

5.32

18.33

3.23

TOILET 1.50 X 2.45

3.05 X 2.45

FOYER 1.65 X 1.30

F.R.D.

STRETCHER LIFT 2.08 X 2.47

SERVANT ROOM 4.53 X 2.35

18.73

LOBBY 5.50 X 4.11

1.80 X 1.32

1.20

DUCT 0.53 / S.SLAB 0.53

0.75M WIDE CHAJJA

S.R.

0.82M WIDE CHAJJA

W.R.

LOBBY 4.11 X 2.01

F.R.D.

2.21

F.D.

F.R.D.

E.D

B

B'

LIFT 1.99 X 2.16

FIRE LIFT 1.99 X 2.16

UP

2.00

2.00

2.00

2.00

2.00

4.80

5.53

0.75M BAND (ON 19TH & 24TH FLR)

FIRE EVACUATION LIFT 2.30 X 2.30

SMOKE CHECK LOBBY 1.84 x 2.23

F.R.D.

2.00

2.15

0.75M BAND (ON 19TH & 24TH FLR)

2.26

CLASSICAL COLUMN RESTING ON BAND

1.20 M CHAJJA

0.75M BAND

S.SLAB 0.53 / DUCT 0.53

S.TOILET 1.80 X 1.05

1.20 M WIDE CHAJJA


0.75 | 0.60 | 0.60 | 1.20 | 1.67 | 2.45 | 1.11 | 1.50 | 1.20 | 4.71 | 2.10 | 1.78

19.67

C

01 17TH TO 20TH FLOOR PLAN


SCALE 1:100

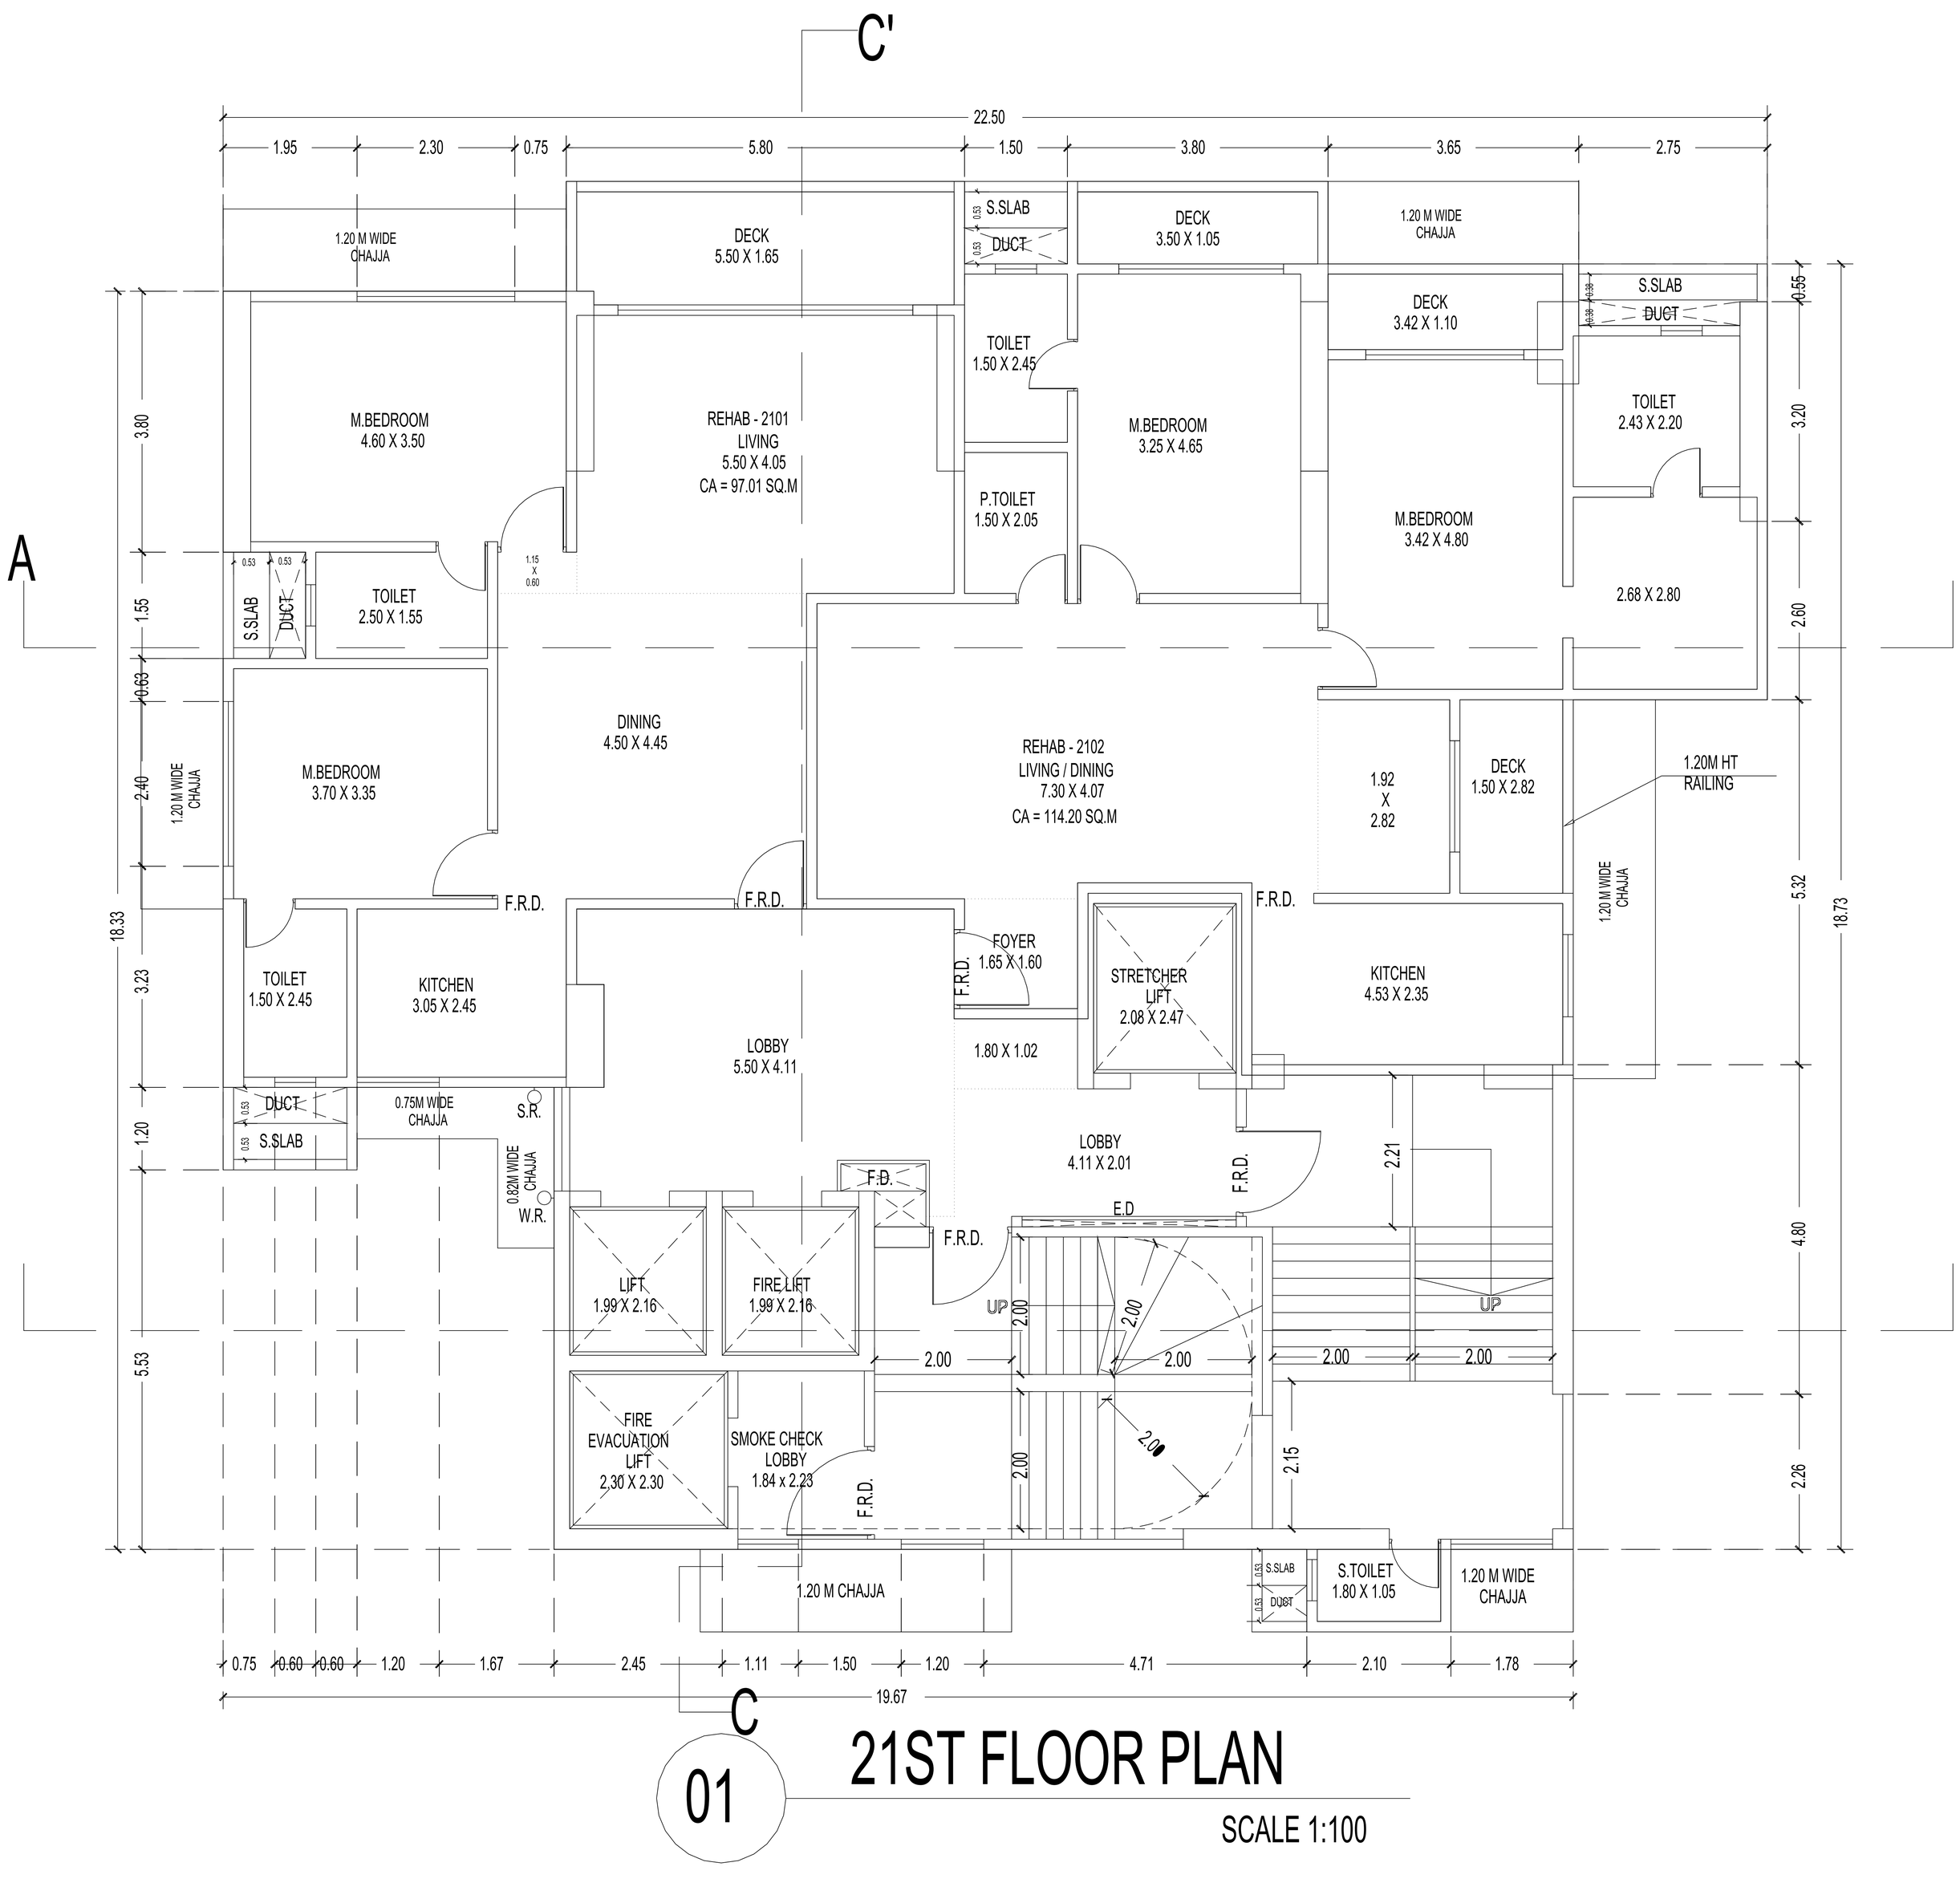

21ST FLOOR PLAN

01

SCALE 1:100

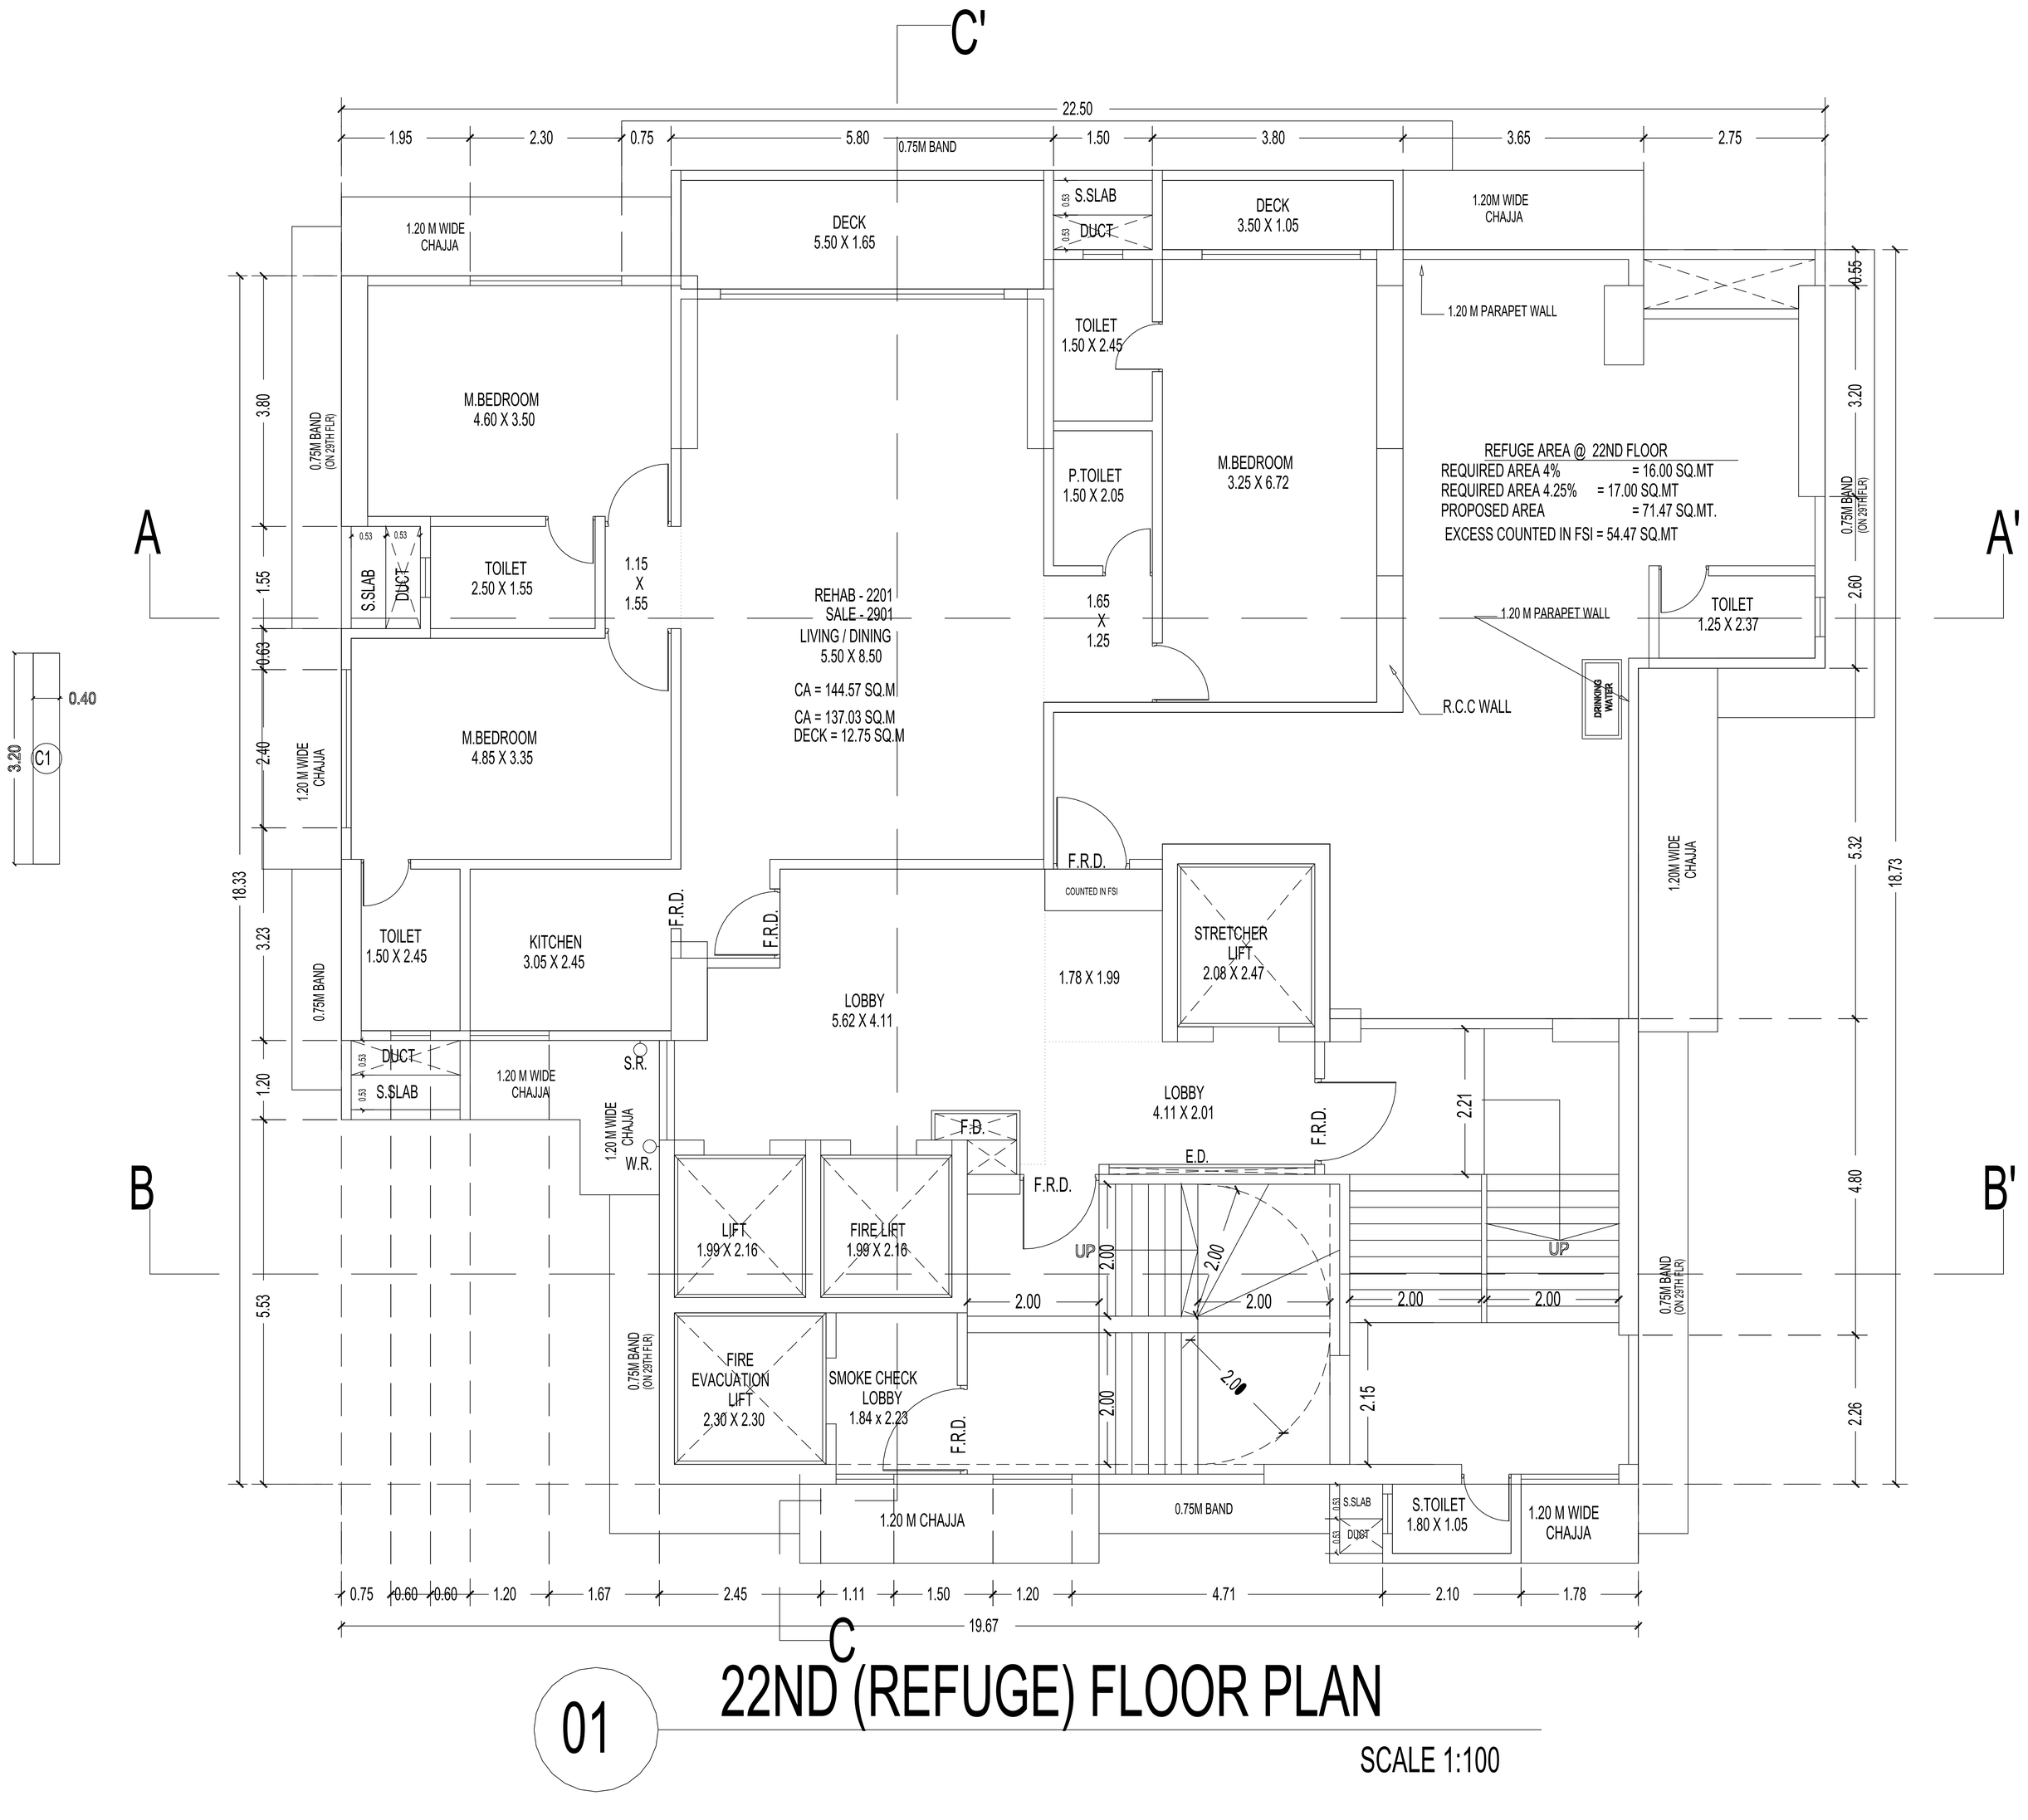

22ND (REFUGE) FLOOR PLAN

01

SCALE 1:100

C'

22.50

1.95 | 2.30 | 0.90 | 5.65 | 1.50 | 3.80 | 3.65 | 2.75

0.75M BAND

1.20 M WIDE CHAJJA

DECK 5.50 X 1.65

S.SLAB 0.53 / DUCT 0.53

DECK 3.50 X 1.05

1.20 M WIDE CHAJJA

DECK 3.42 X 1.10

S.SLAB 0.38 / DUCT

TOILET 1.50 X 2.45

M.BEDROOM 3.25 X 4.65

TOILET 2.43 X 2.20

M.BEDROOM 4.60 X 3.50

P.TOILET 1.50 X 2.05

M.BEDROOM 3.42 X 4.80

2.68 X 2.80

0.75M BAND (ON 34TH FLR)

3.80 | 3.20

0.53 | 0.53 S.SLAB / DUCT

TOILET 2.50 X 1.55

1.15 X 1.55

REHAB - 2301
LIVING / DINING
5.50 X 8.50
CA = 211.79 SQ.M

PASSAGE 2.18 X 1.25

1.55 | 2.60

0.63

F.R.D.

3.12 X 4.30

1.07 X 2.67

KITCHEN 2.88 X 2.82

DECK 1.50 X 2.82

1.20M HT RAILING

1.20 M WIDE CHAJJA

M.BEDROOM 4.85 X 3.35

2.40 | 5.32

18.33 | 18.73

3.23

TOILET 1.50 X 2.45

3.05 X 2.45

FOYER 1.65 X 1.60

F.R.D.

STRETCHER LIFT 2.08 X 2.47

SERVANT ROOM 4.53 X 2.35

0.75M BAND

LOBBY 5.50 X 4.11

1.80 X 1.02

1.20 | 4.80

DUCT 0.53 / S.SLAB 0.53

0.75M WIDE CHAJJA

S.R.

0.82M WIDE CHAJJA

W.R.

LOBBY 4.11 X 2.01

F.D.

F.R.D.

E.D

2.21

LIFT 1.99 X 2.16

FIRE LIFT 1.99 X 2.16

UP

2.00

2.00

2.00

2.00

2.00

2.00

5.53 | 2.26

0.75M BAND (ON 34TH FLR)

FIRE EVACUATION LIFT 2.30 X 2.30

SMOKE CHECK LOBBY 1.84 x 2.23

F.R.D.

2.15

1.20 M CHAJJA

0.75M BAND

S.SLAB 0.53 / DUCT 0.53

S.TOILET 1.80 X 1.05

1.20 M WIDE CHAJJA

0.75 | 0.60 | 0.60 | 1.20 | 1.67 | 2.45 | 1.11 | 1.50 | 1.20 | 4.71 | 2.10 | 1.78

19.67

C

01 23RD FLOOR PLAN

SCALE 1:100