


1 NO		138 SQ.M	1486 SQ.FT
TOTAL AUDITORIUM		138 SQ.M	1486 SQ.FT
1 NO	7	1 NO	137 SQ.FT
1 NO	8	1 NO	136 SQ.FT
1 NO	9	1 NO	67 SQ.FT
TOTAL PUBLICITY			1363 SQ.FT
STAIRCASE AREA CALCULATION			
1	5.58 X 4.72	1 NO	2374 SQ.FT
	1.22 X 2.85	1 NO	3.13 SQ.M
	1.22 X 2.85	1 NO	3.13 SQ.M
2/4	2.25 X 1.35	1 NO	1.85 SQ.M
2/3	2.25 X 1.35	1 NO	1.85 SQ.M
TOTAL STAIRCASE AREA IN SQ.FT			2773 SQ.FT
NET RESULT IN AREA			1286 SQ.FT


FITNESS CENTER SUMMARY			
FLOOR	GROSS AREA	EXCLUDED	NET AREA
FIRST	1000.00 SQ.M	417.00 SQ.M	583.00 SQ.M
SECOND	1000.00 SQ.M	417.00 SQ.M	583.00 SQ.M
THIRD	1000.00 SQ.M	417.00 SQ.M	583.00 SQ.M
TOTAL	3000.00 SQ.M	1251.00 SQ.M	1749.00 SQ.M

TOTAL RESI. AREA PROPOSED = 48975.00 sqmts
PERMISSIBLE FITNESS CENTER = 2% OF PROPOSED RESI. BUA
2% OF 48975.00 = 979.50 SQ.MT.
PROPOSED FITNESS CENTER = 1749.84 SQ.MT.
EXCESS FITNESS CENTER AREA COUNTED = 267.32 SQ.MT.

			SCAPE 01
336	SQ.FT		
234	SQ.FT		
234	SQ.FT		
145	SQ.FT		
145	SQ.FT		
135	SQ.FT		
135	SQ.FT		
336	SQ.FT		
336	SQ.FT		
2715	SQ.FT		
1 NO		2715	SQ.FT
1 NO			
4 NO			
		2715	SQ.FT
		252.27	SQ.M

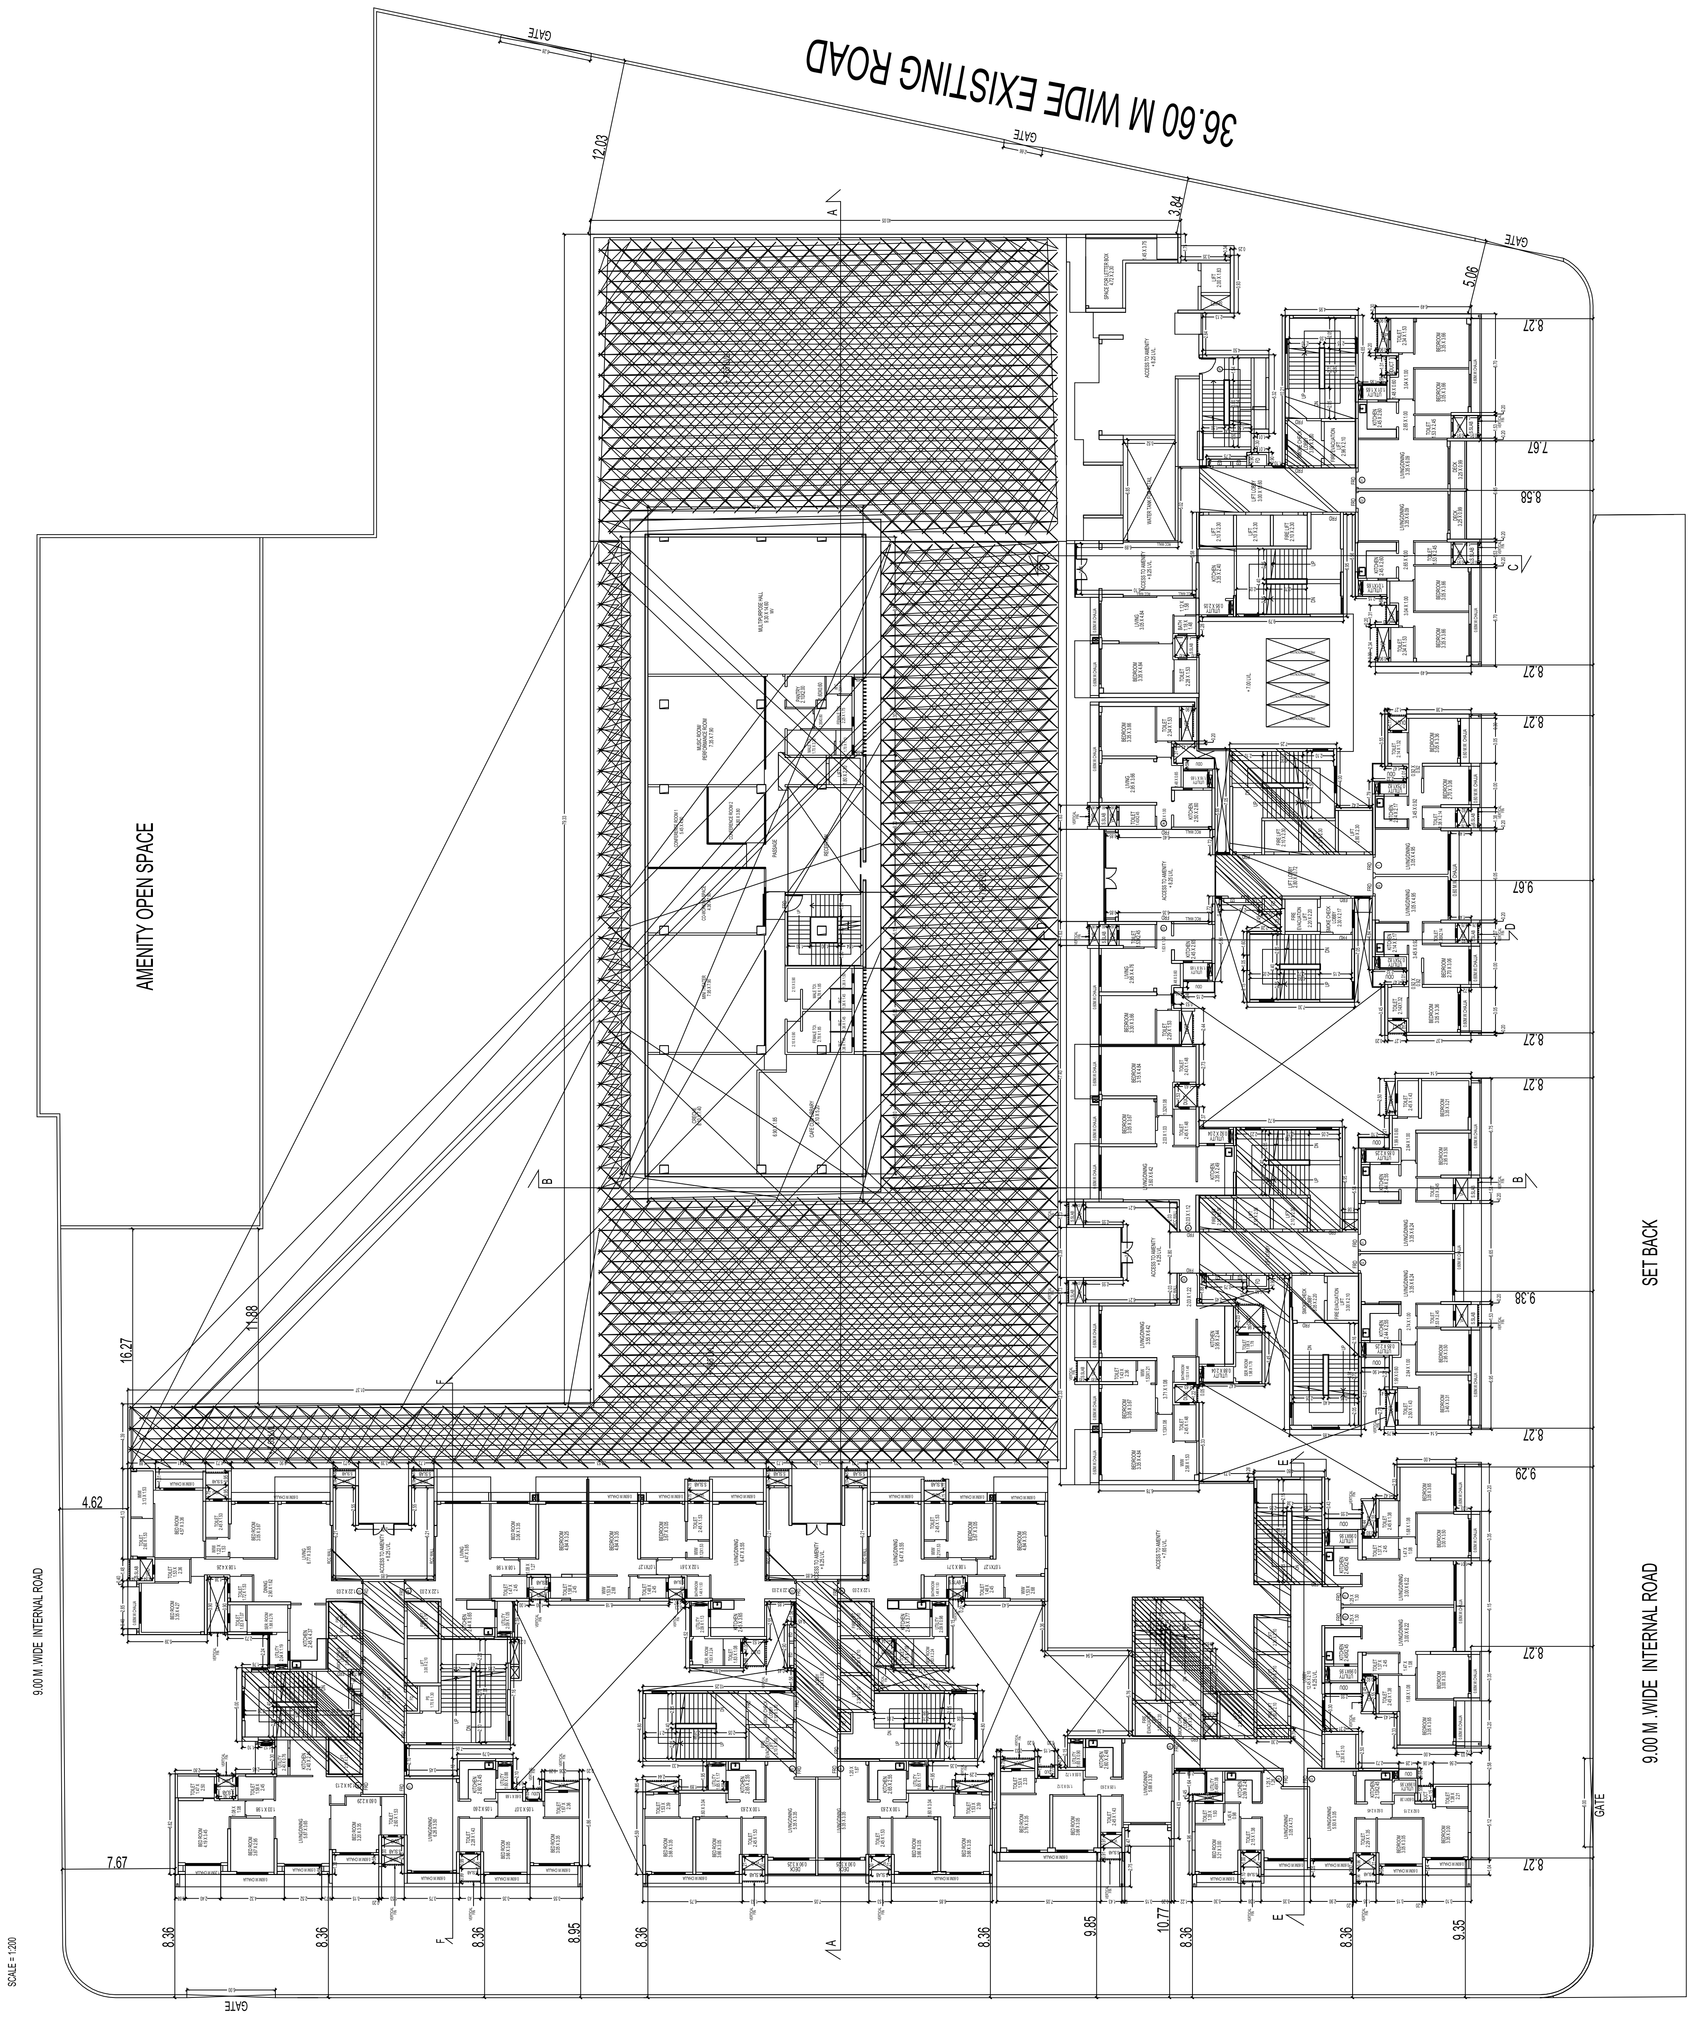


1ST FLOOR PLAN
SCALE = 1:200

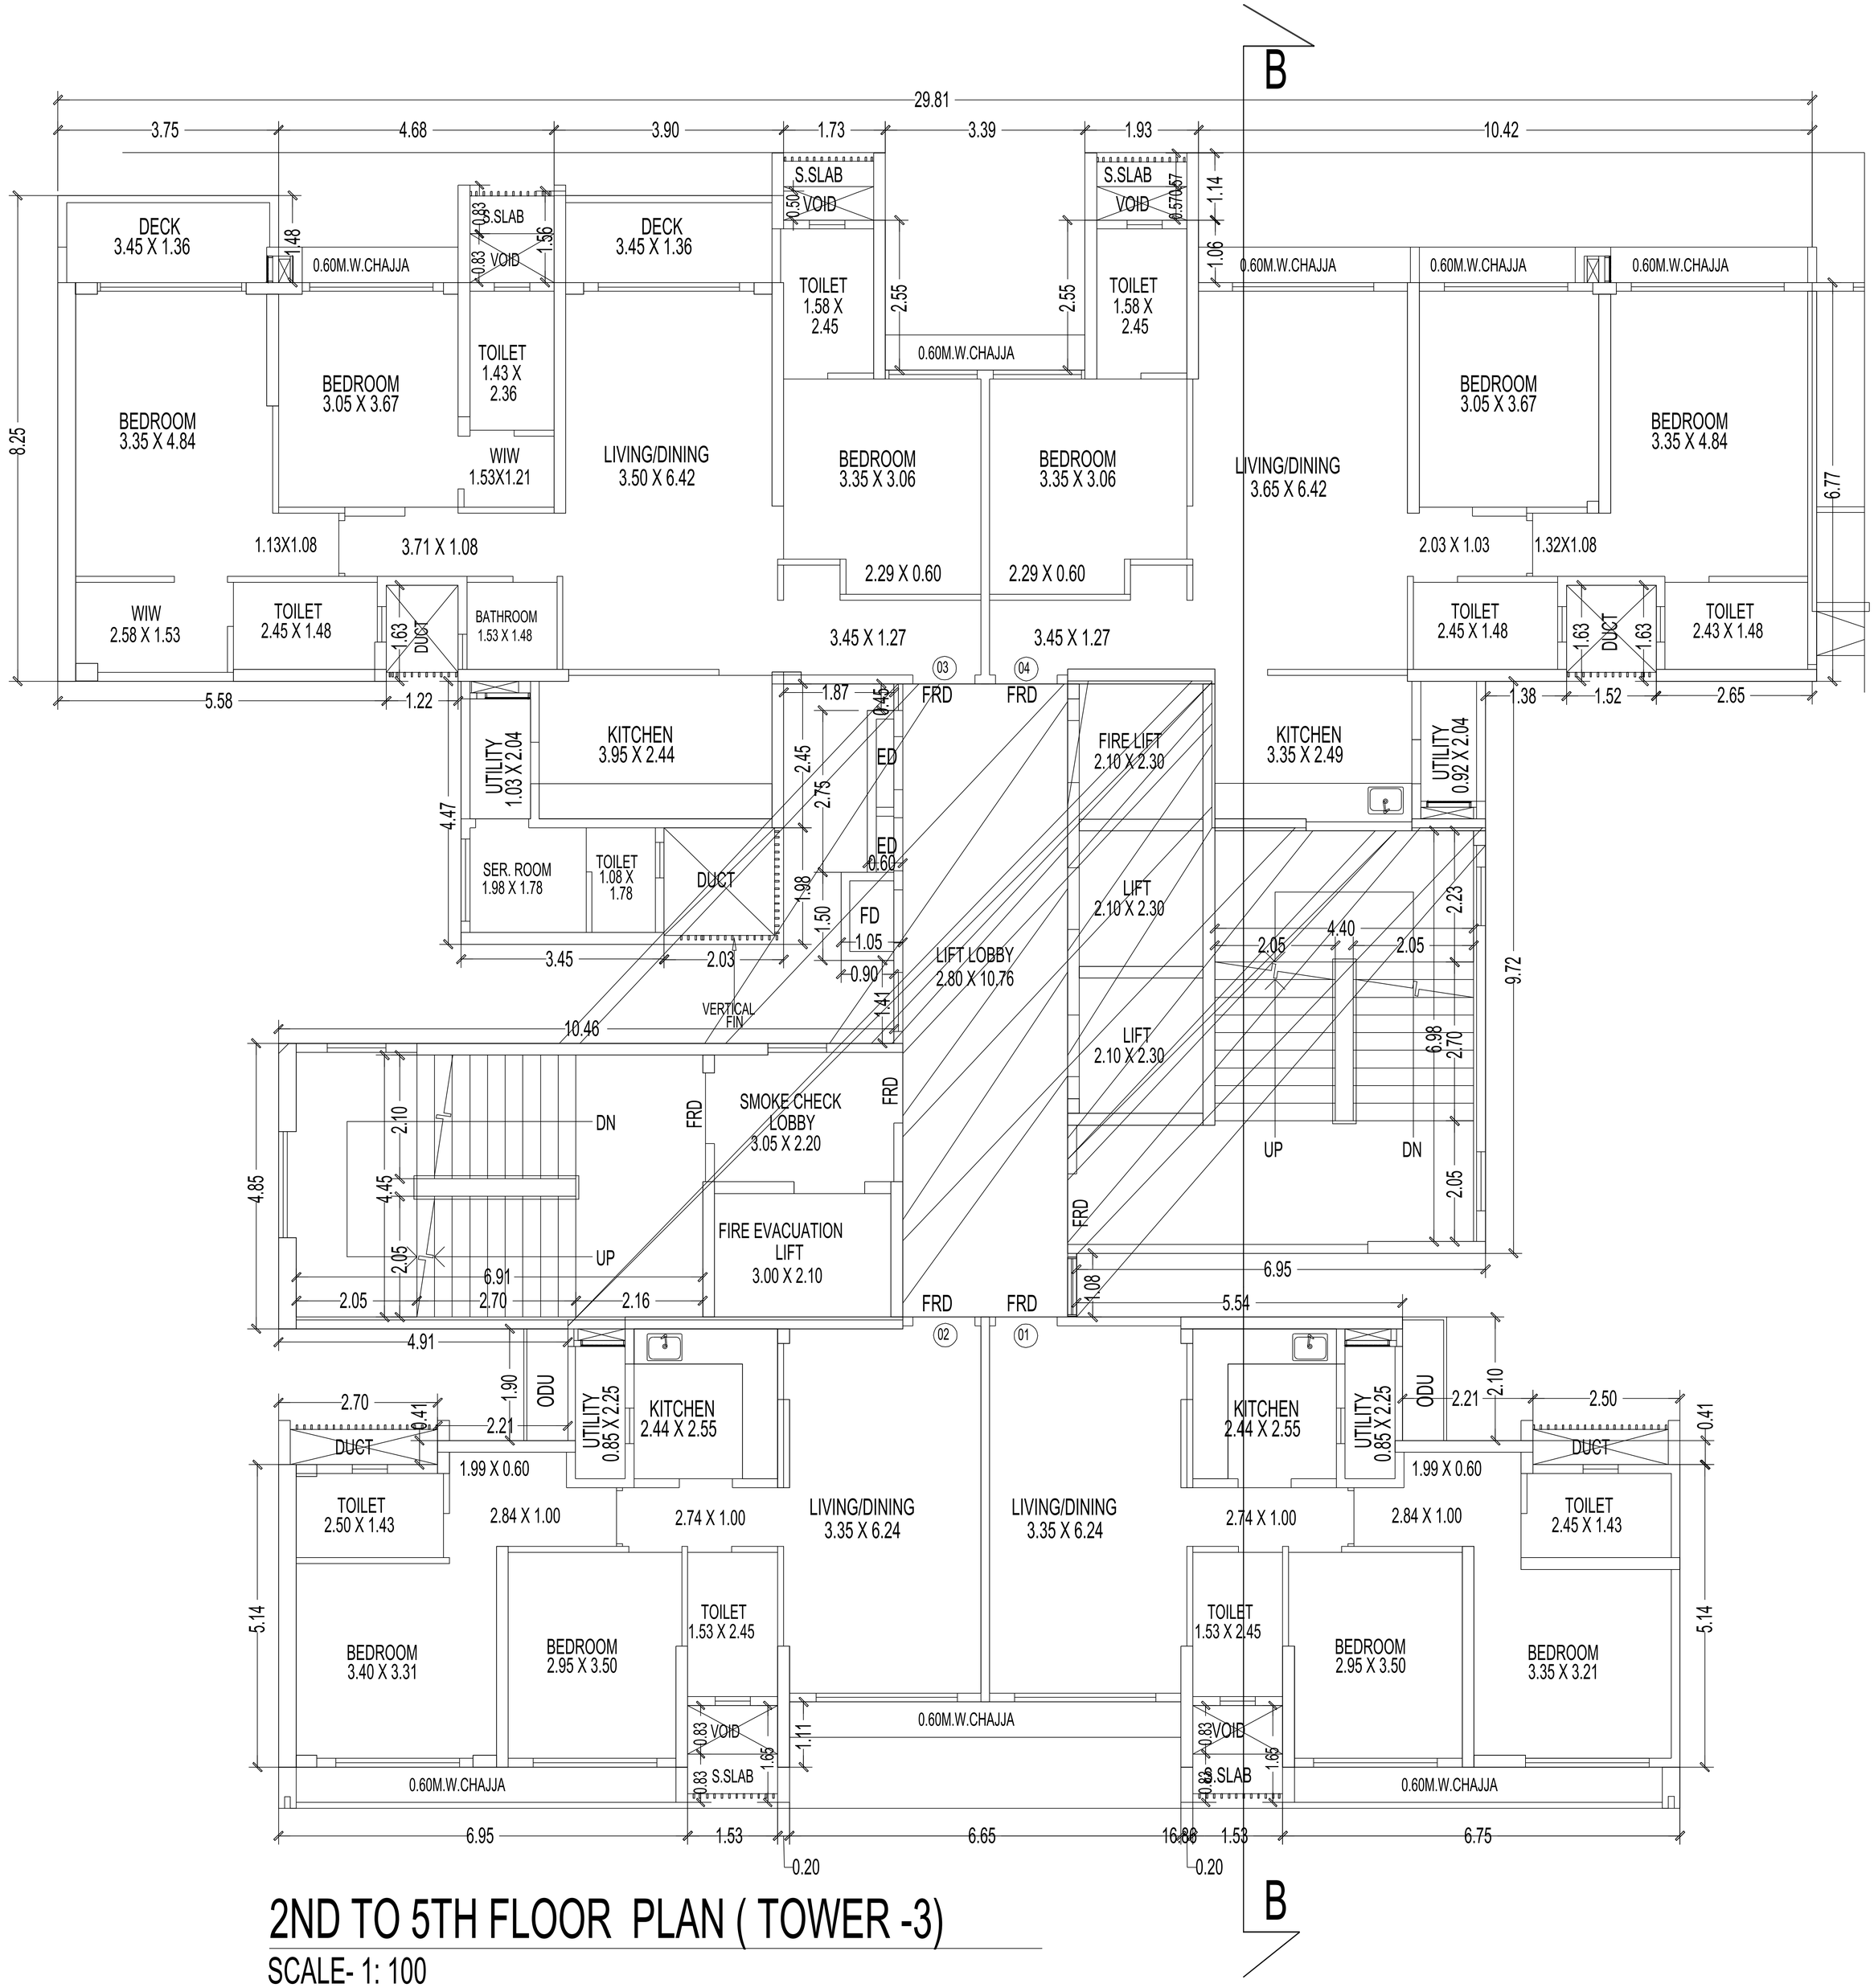


2ND TO 5TH FLOOR PLAN (TOWER -3)

SCALE- 1: 100

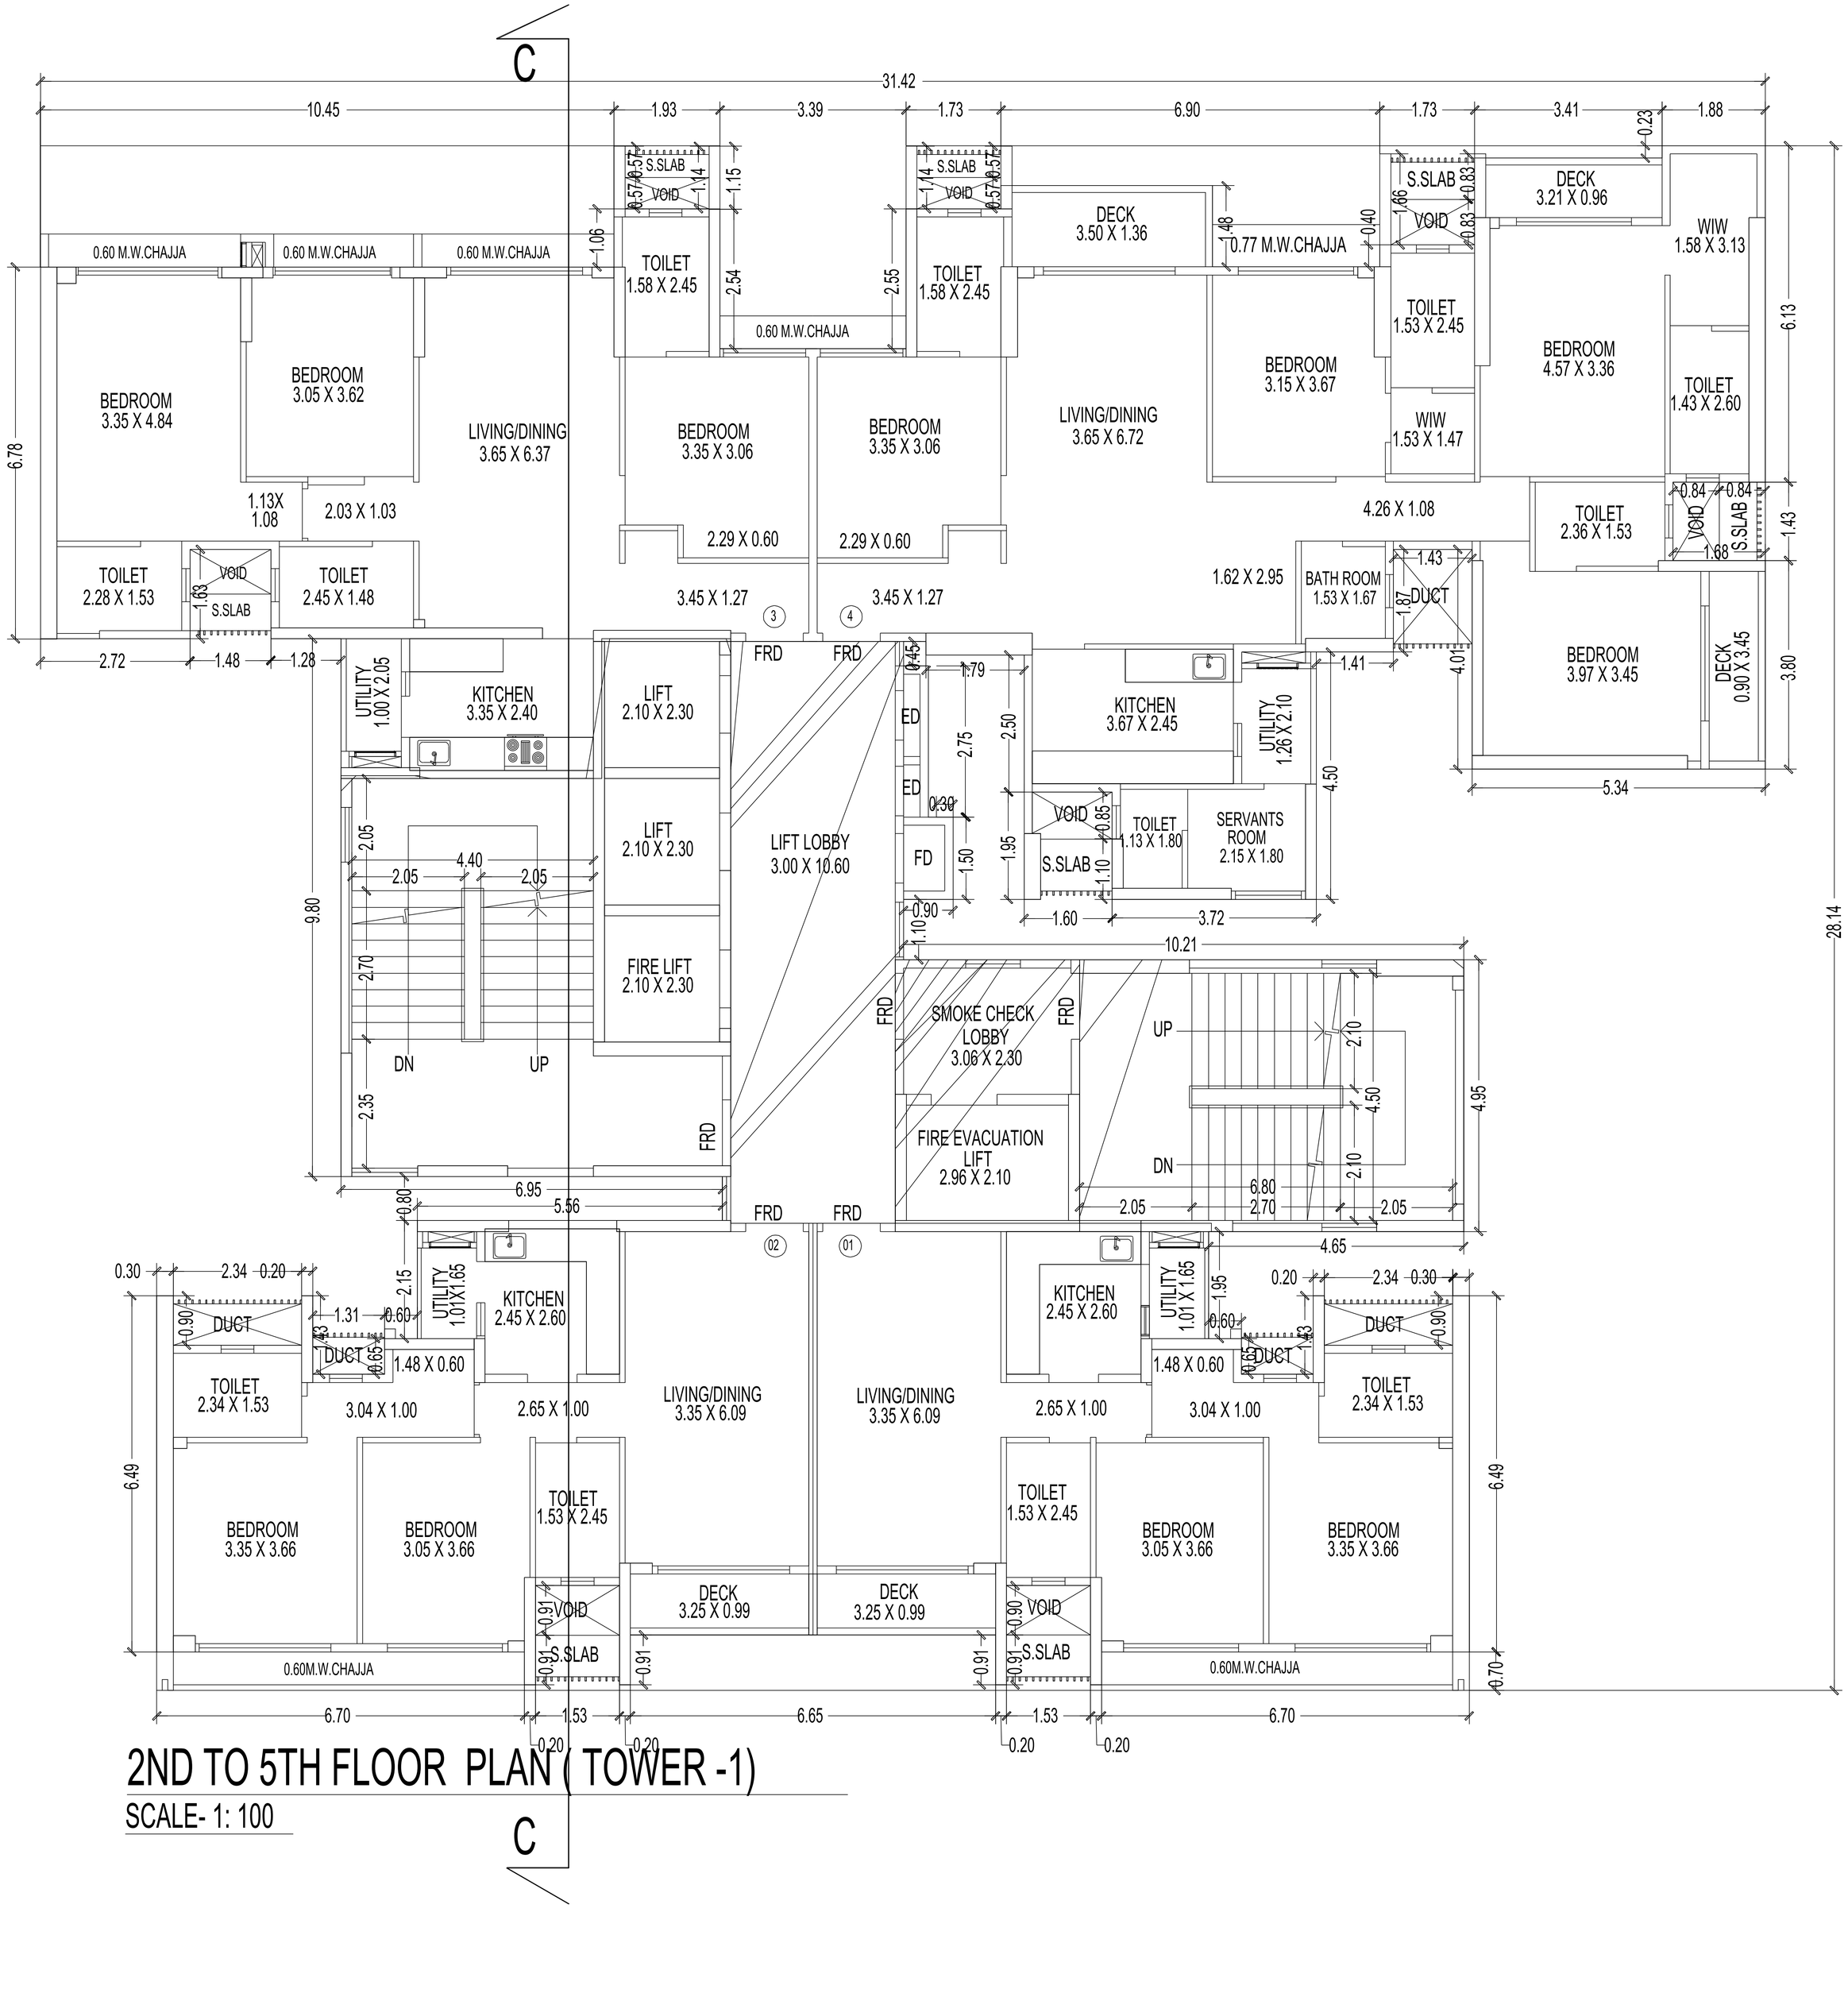


2ND TO 5TH FLOOR PLAN (TOWER -1)

SCALE- 1: 100

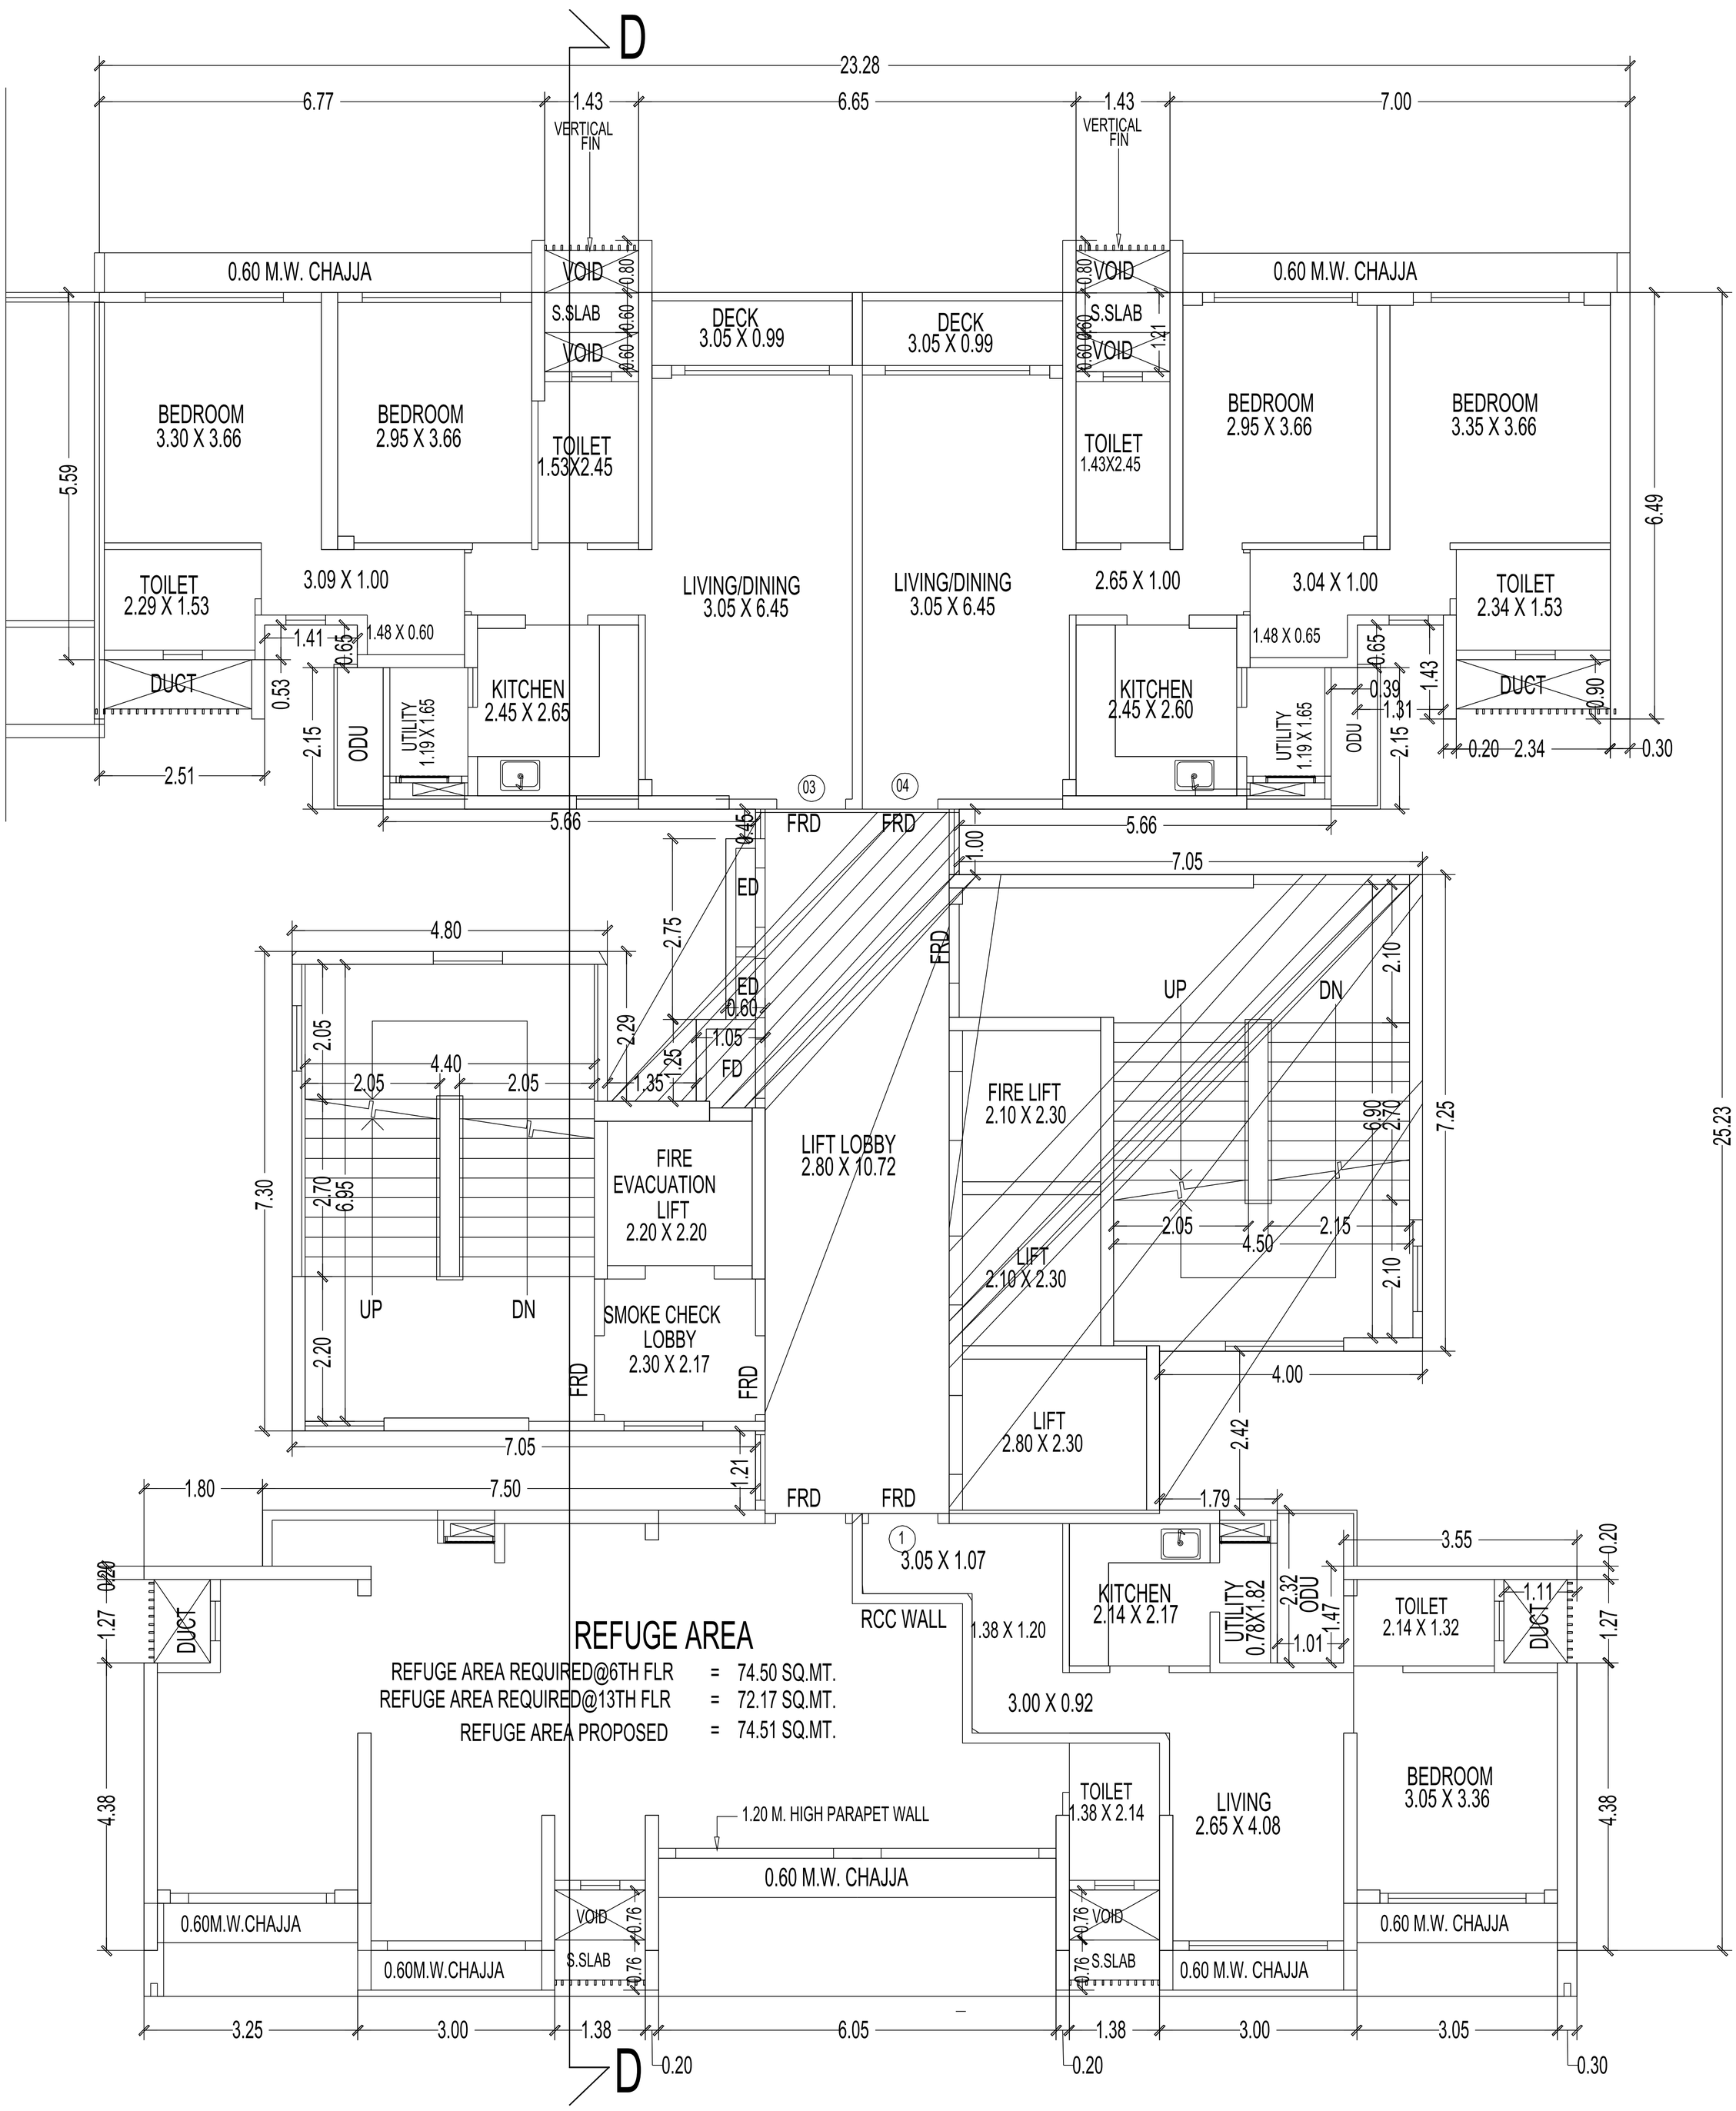


6TH & 13TH FLOOR PLAN (TOWER -2)

SCALE- 1: 100

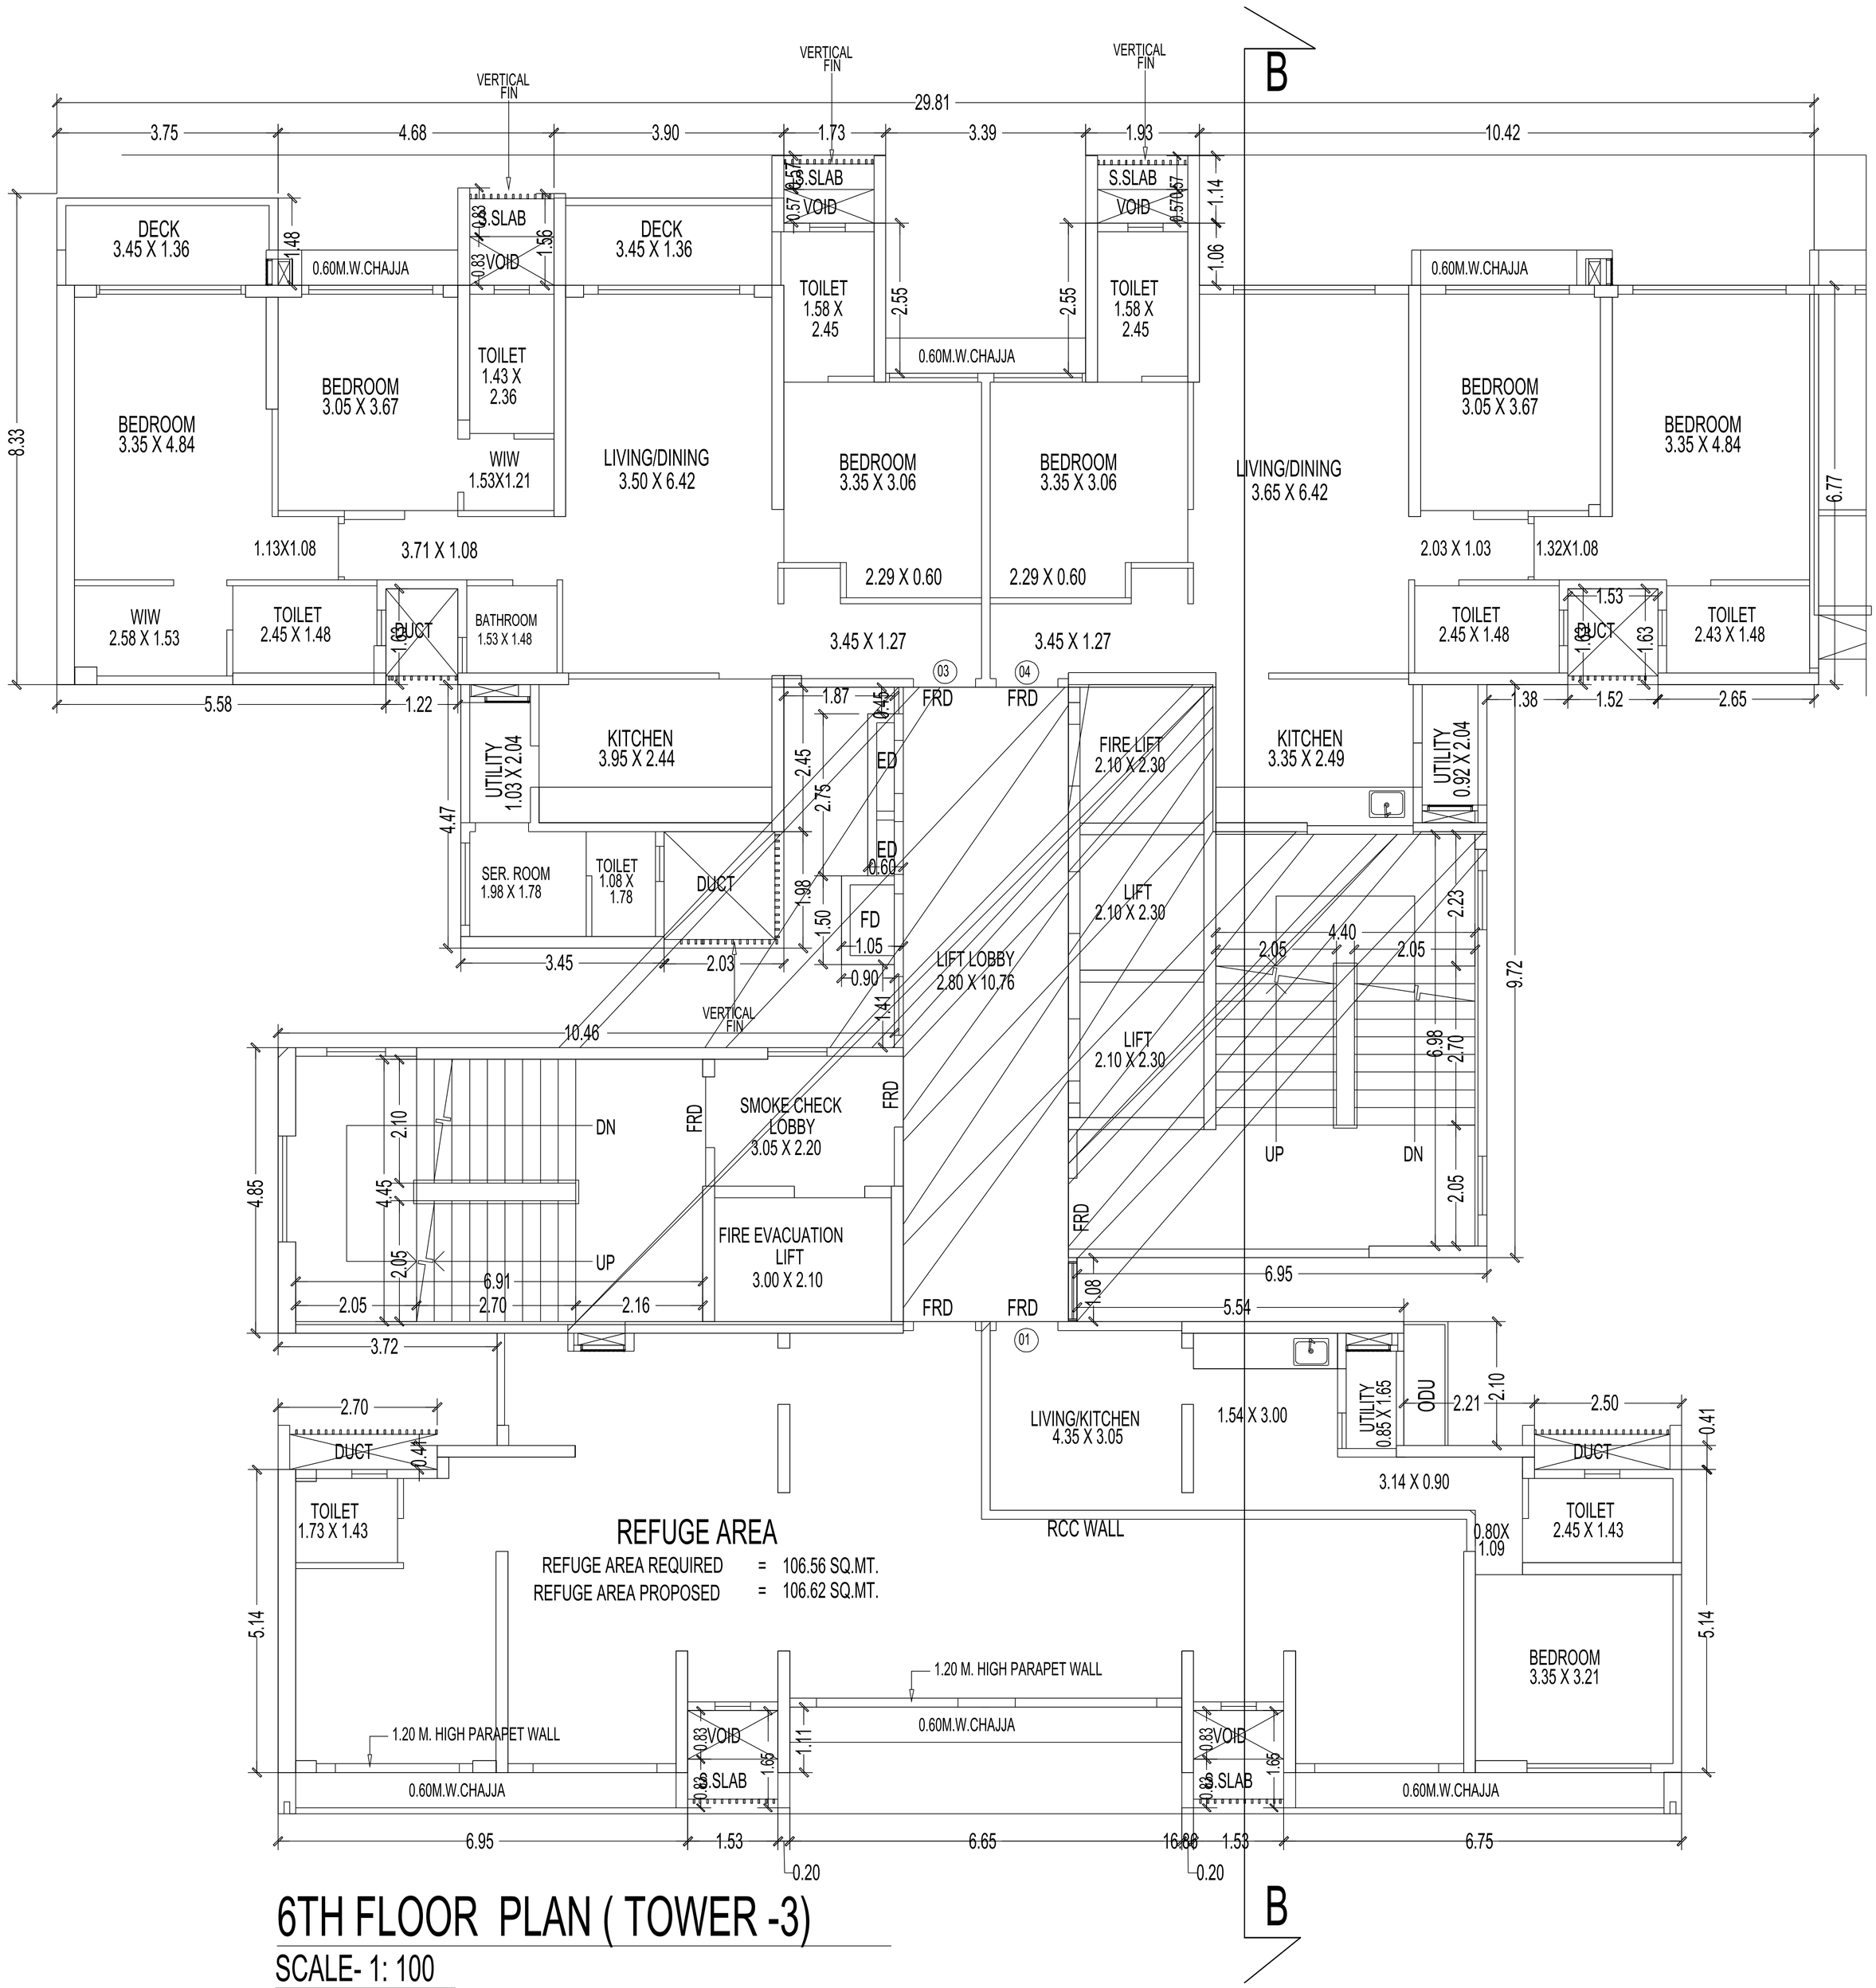


6TH FLOOR PLAN (TOWER -3)

SCALE- 1: 100

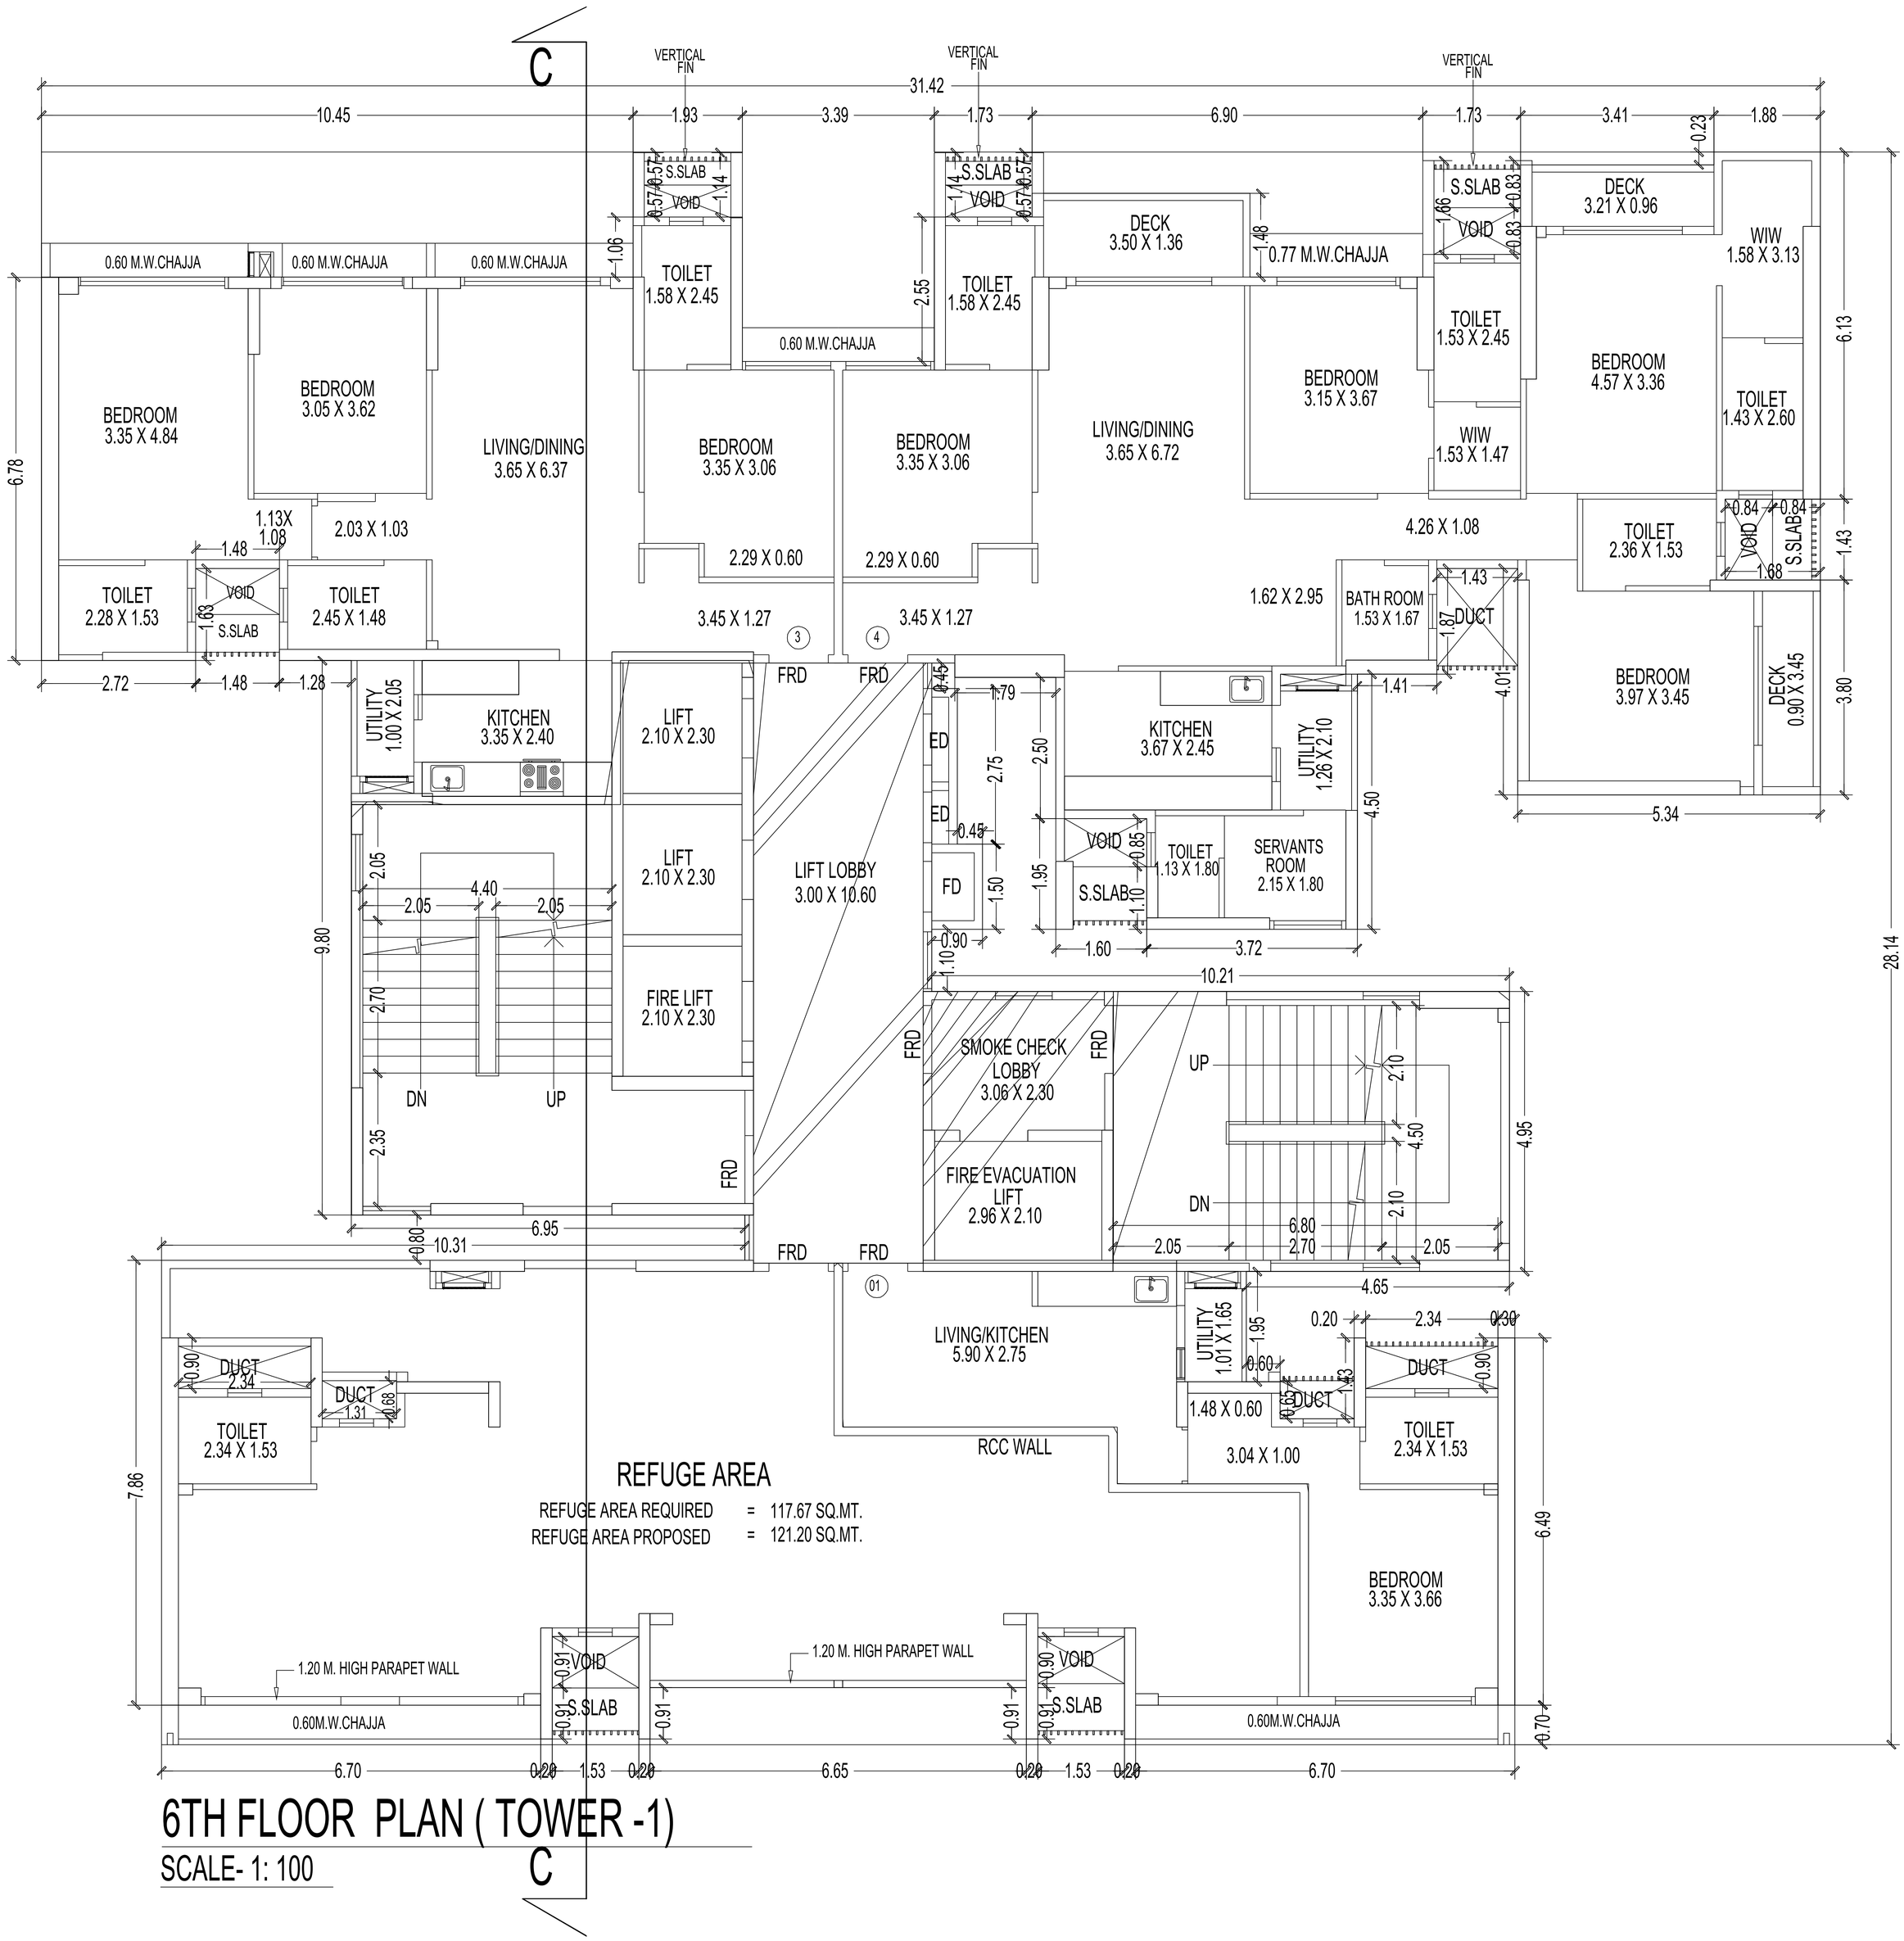

6TH FLOOR PLAN (TOWER -1)


SCALE- 1: 100

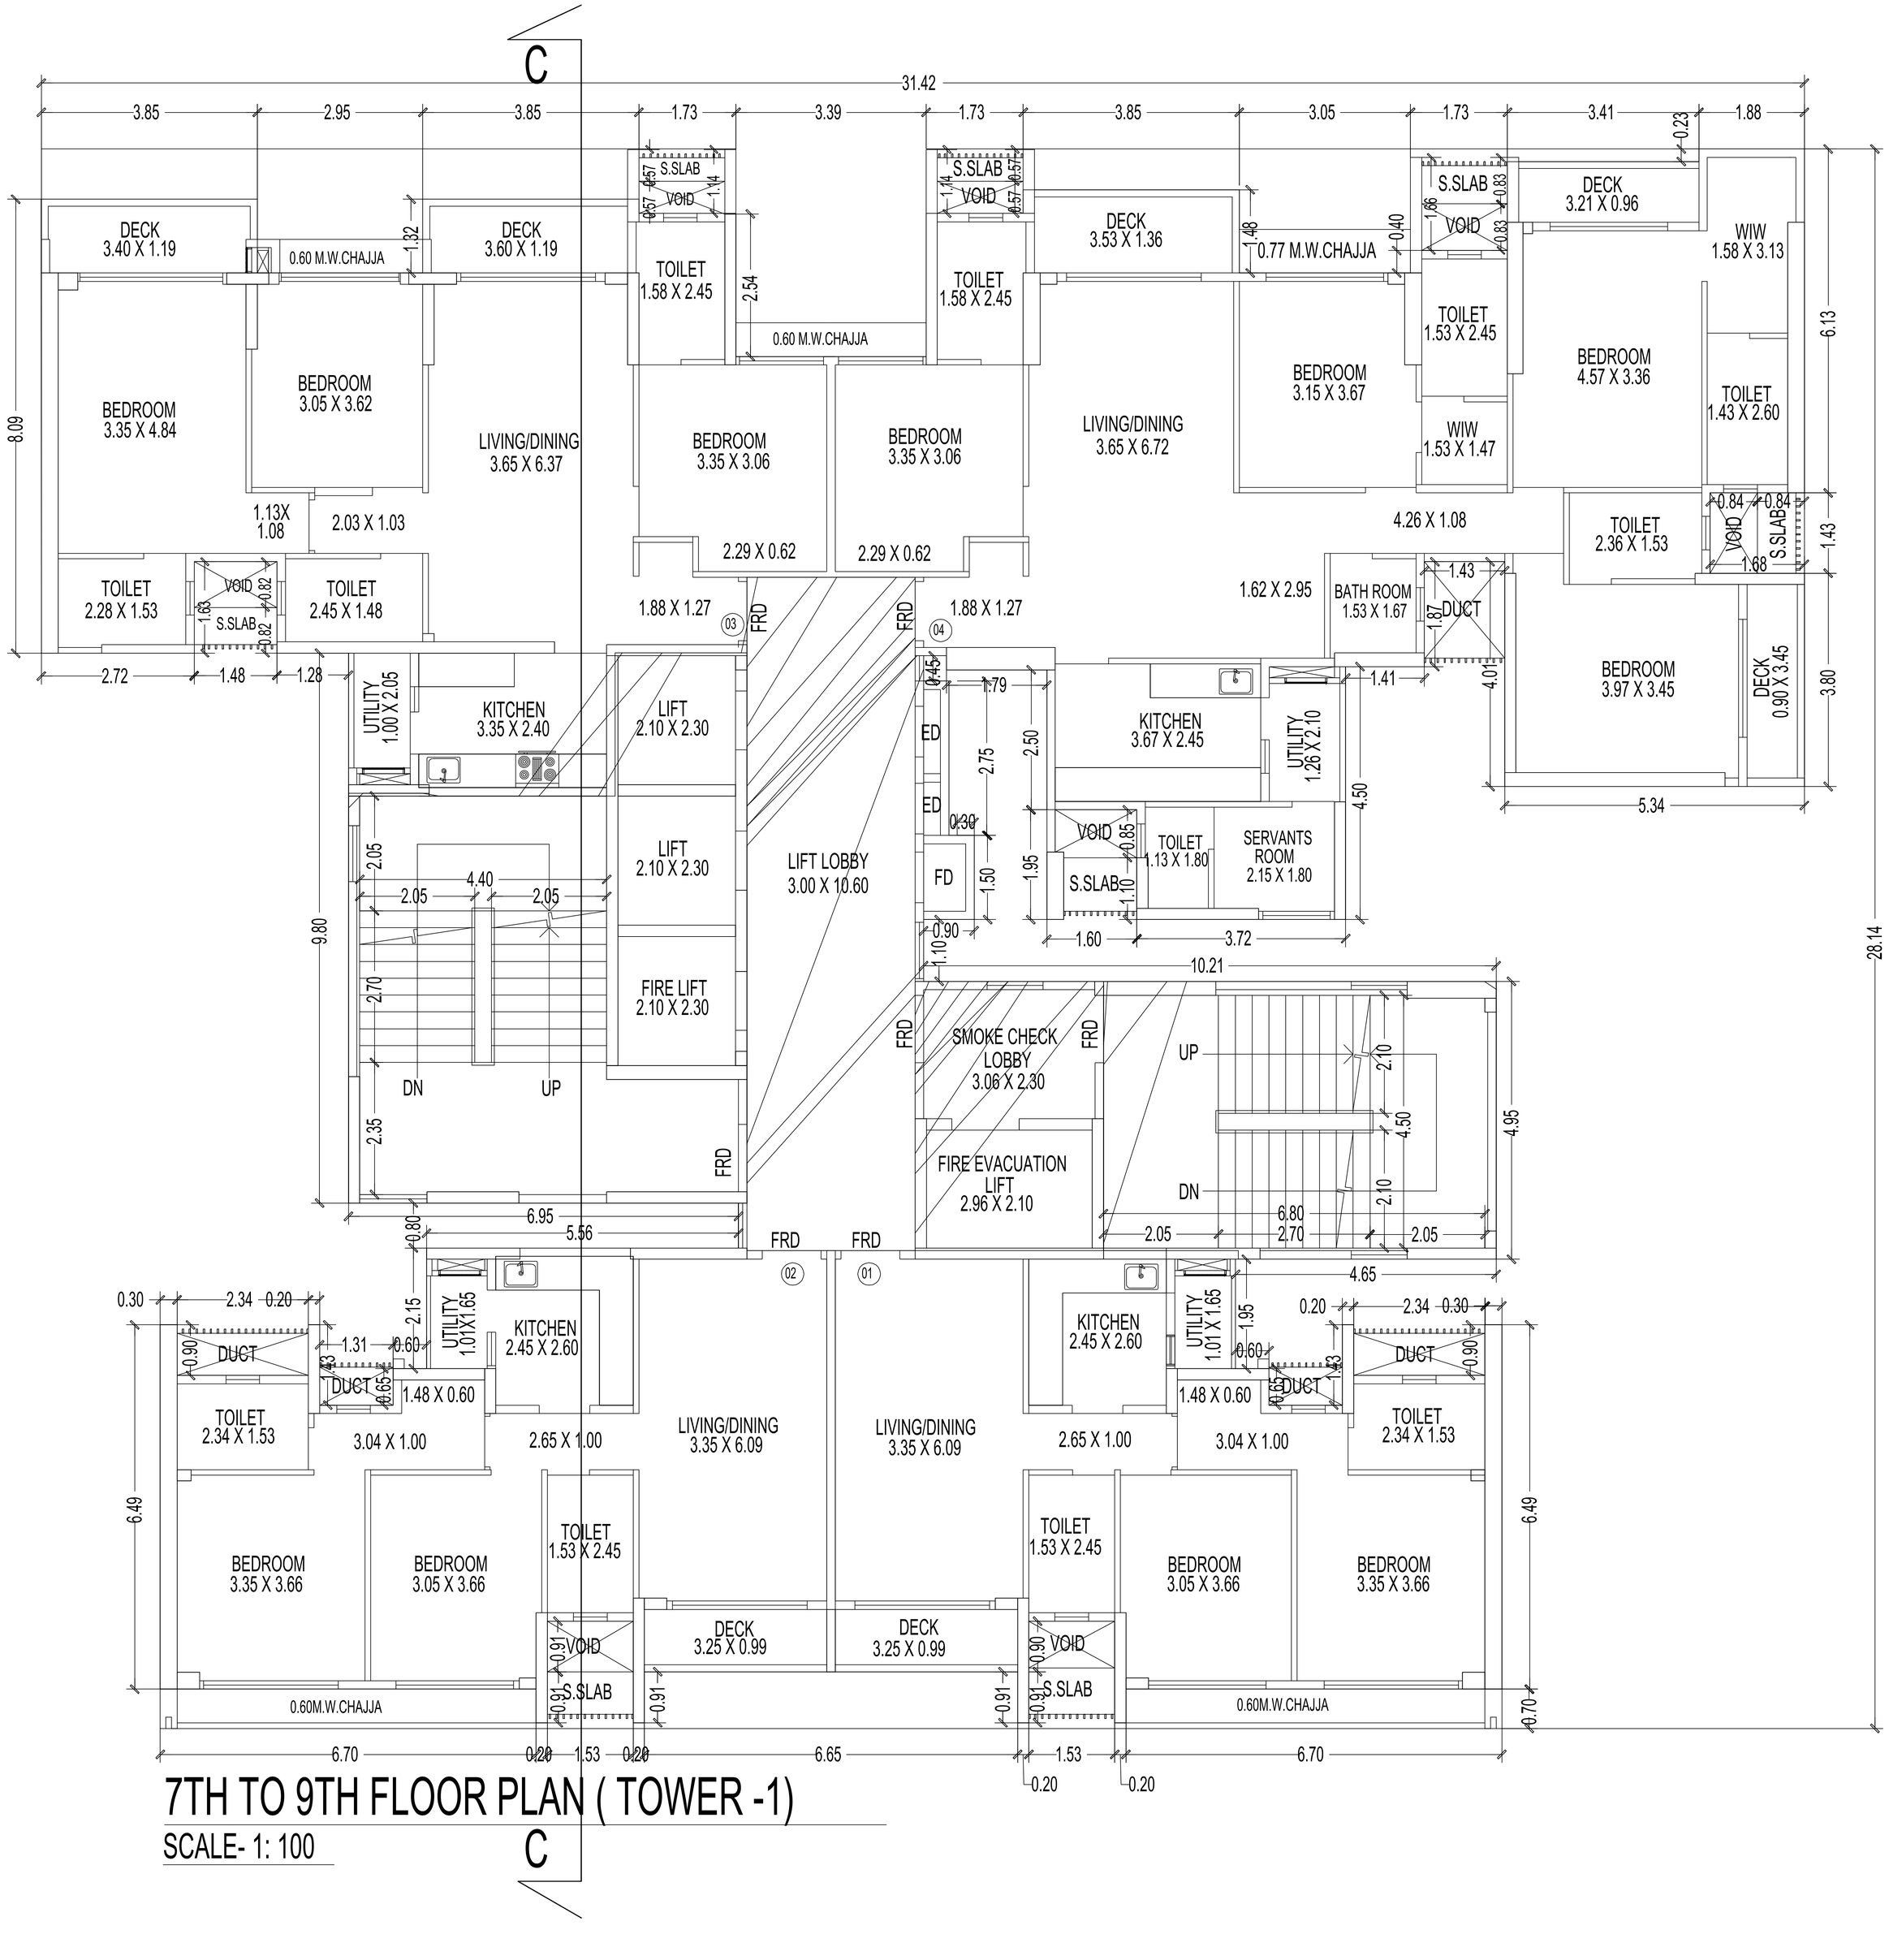

7TH TO 9TH FLOOR PLAN (TOWER -1)


SCALE- 1: 100

SCALE- 1: 100

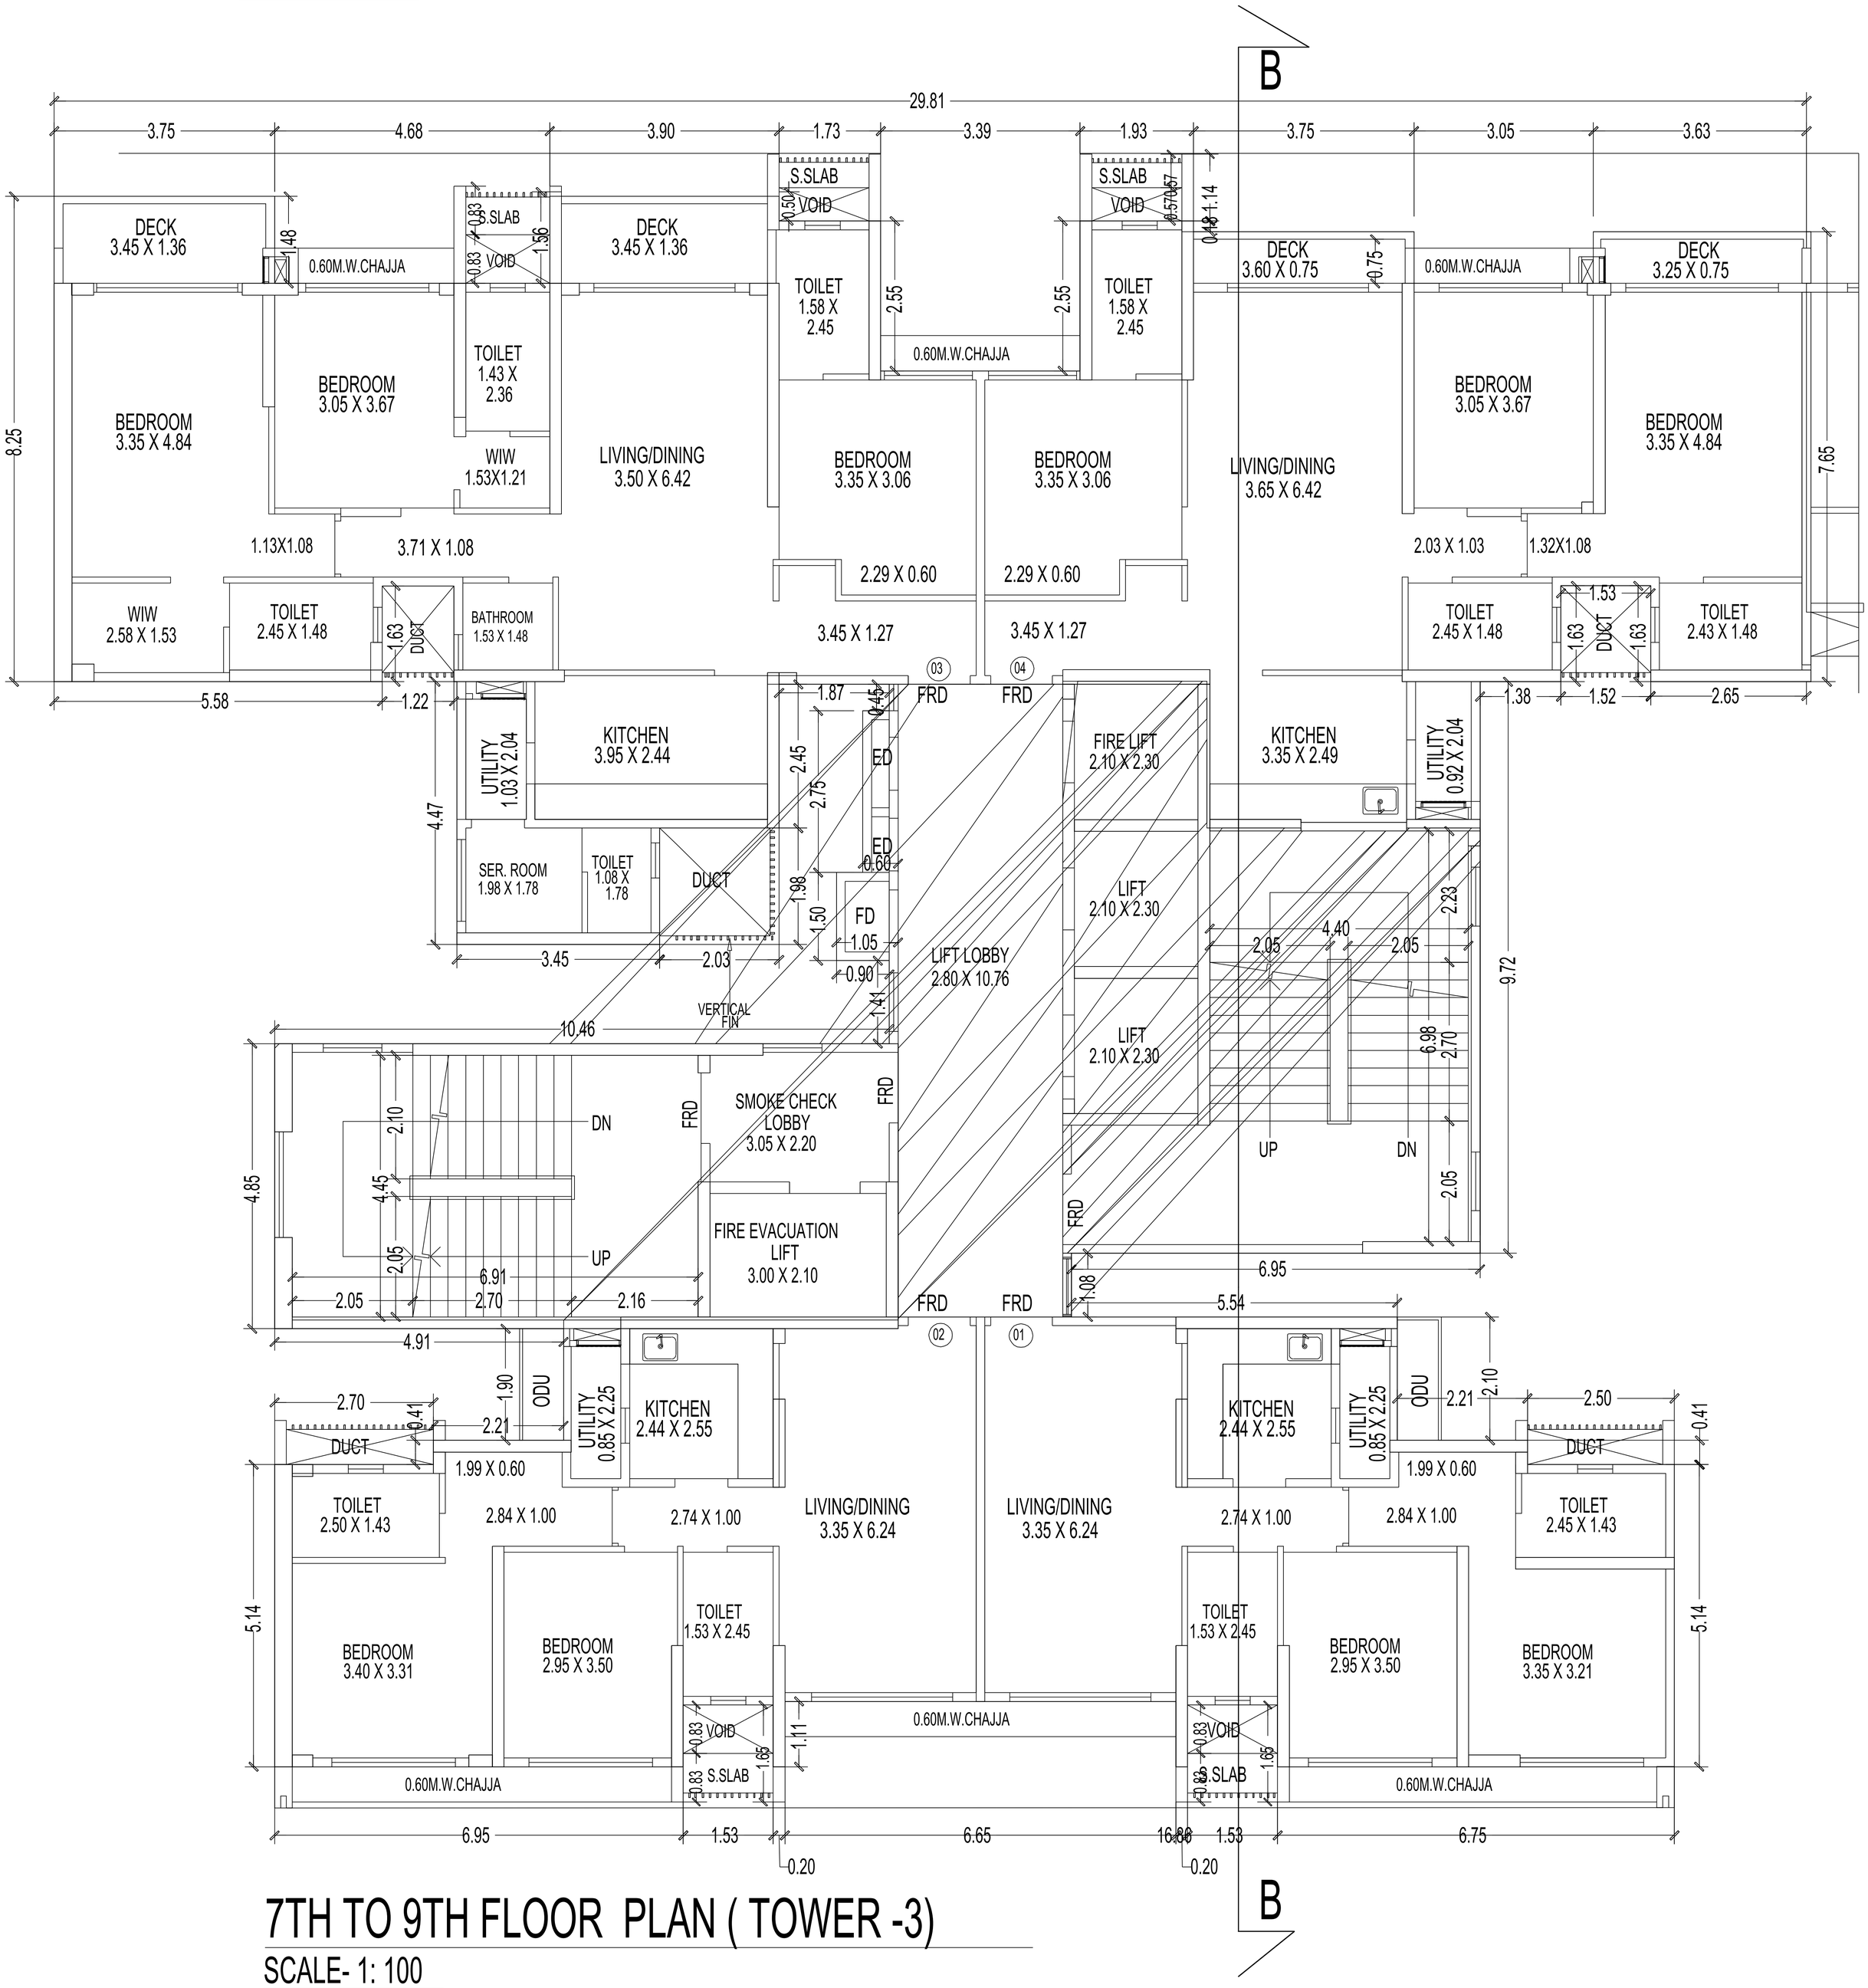


7TH TO 9TH FLOOR PLAN (TOWER -3)

SCALE- 1: 100

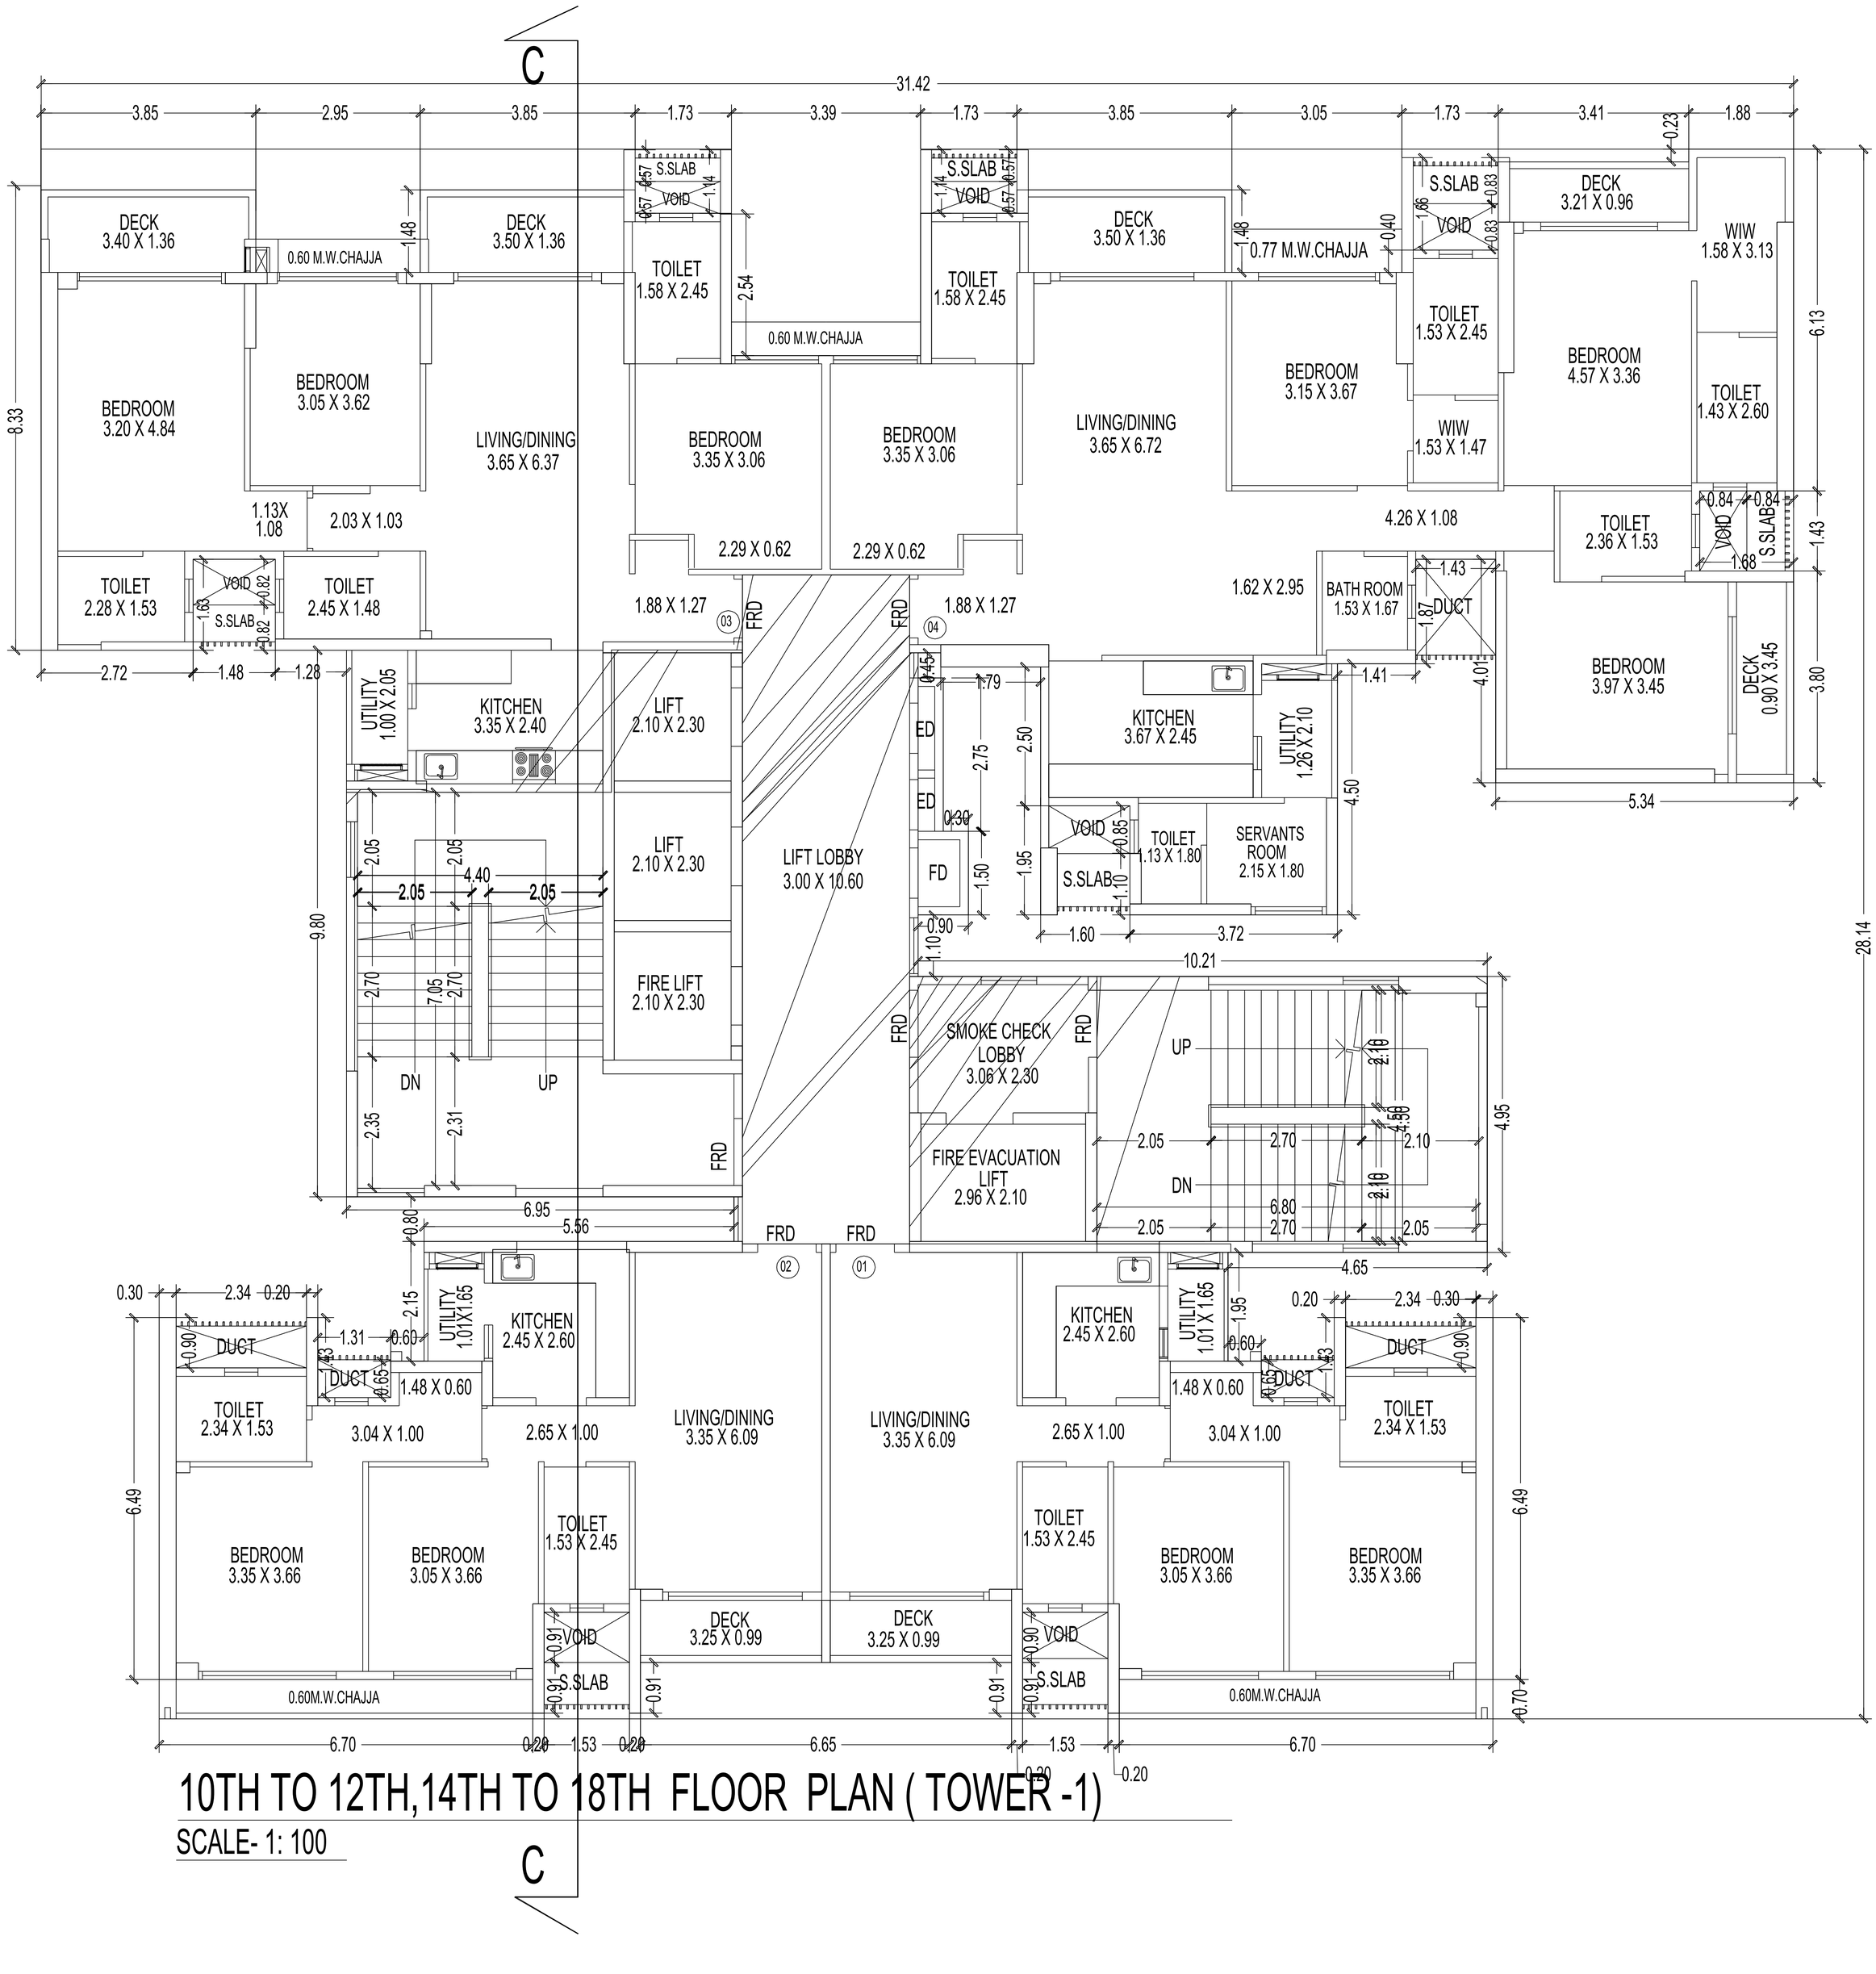

10TH TO 12TH,14TH TO 18TH FLOOR PLAN (TOWER -1)

SCALE- 1: 100

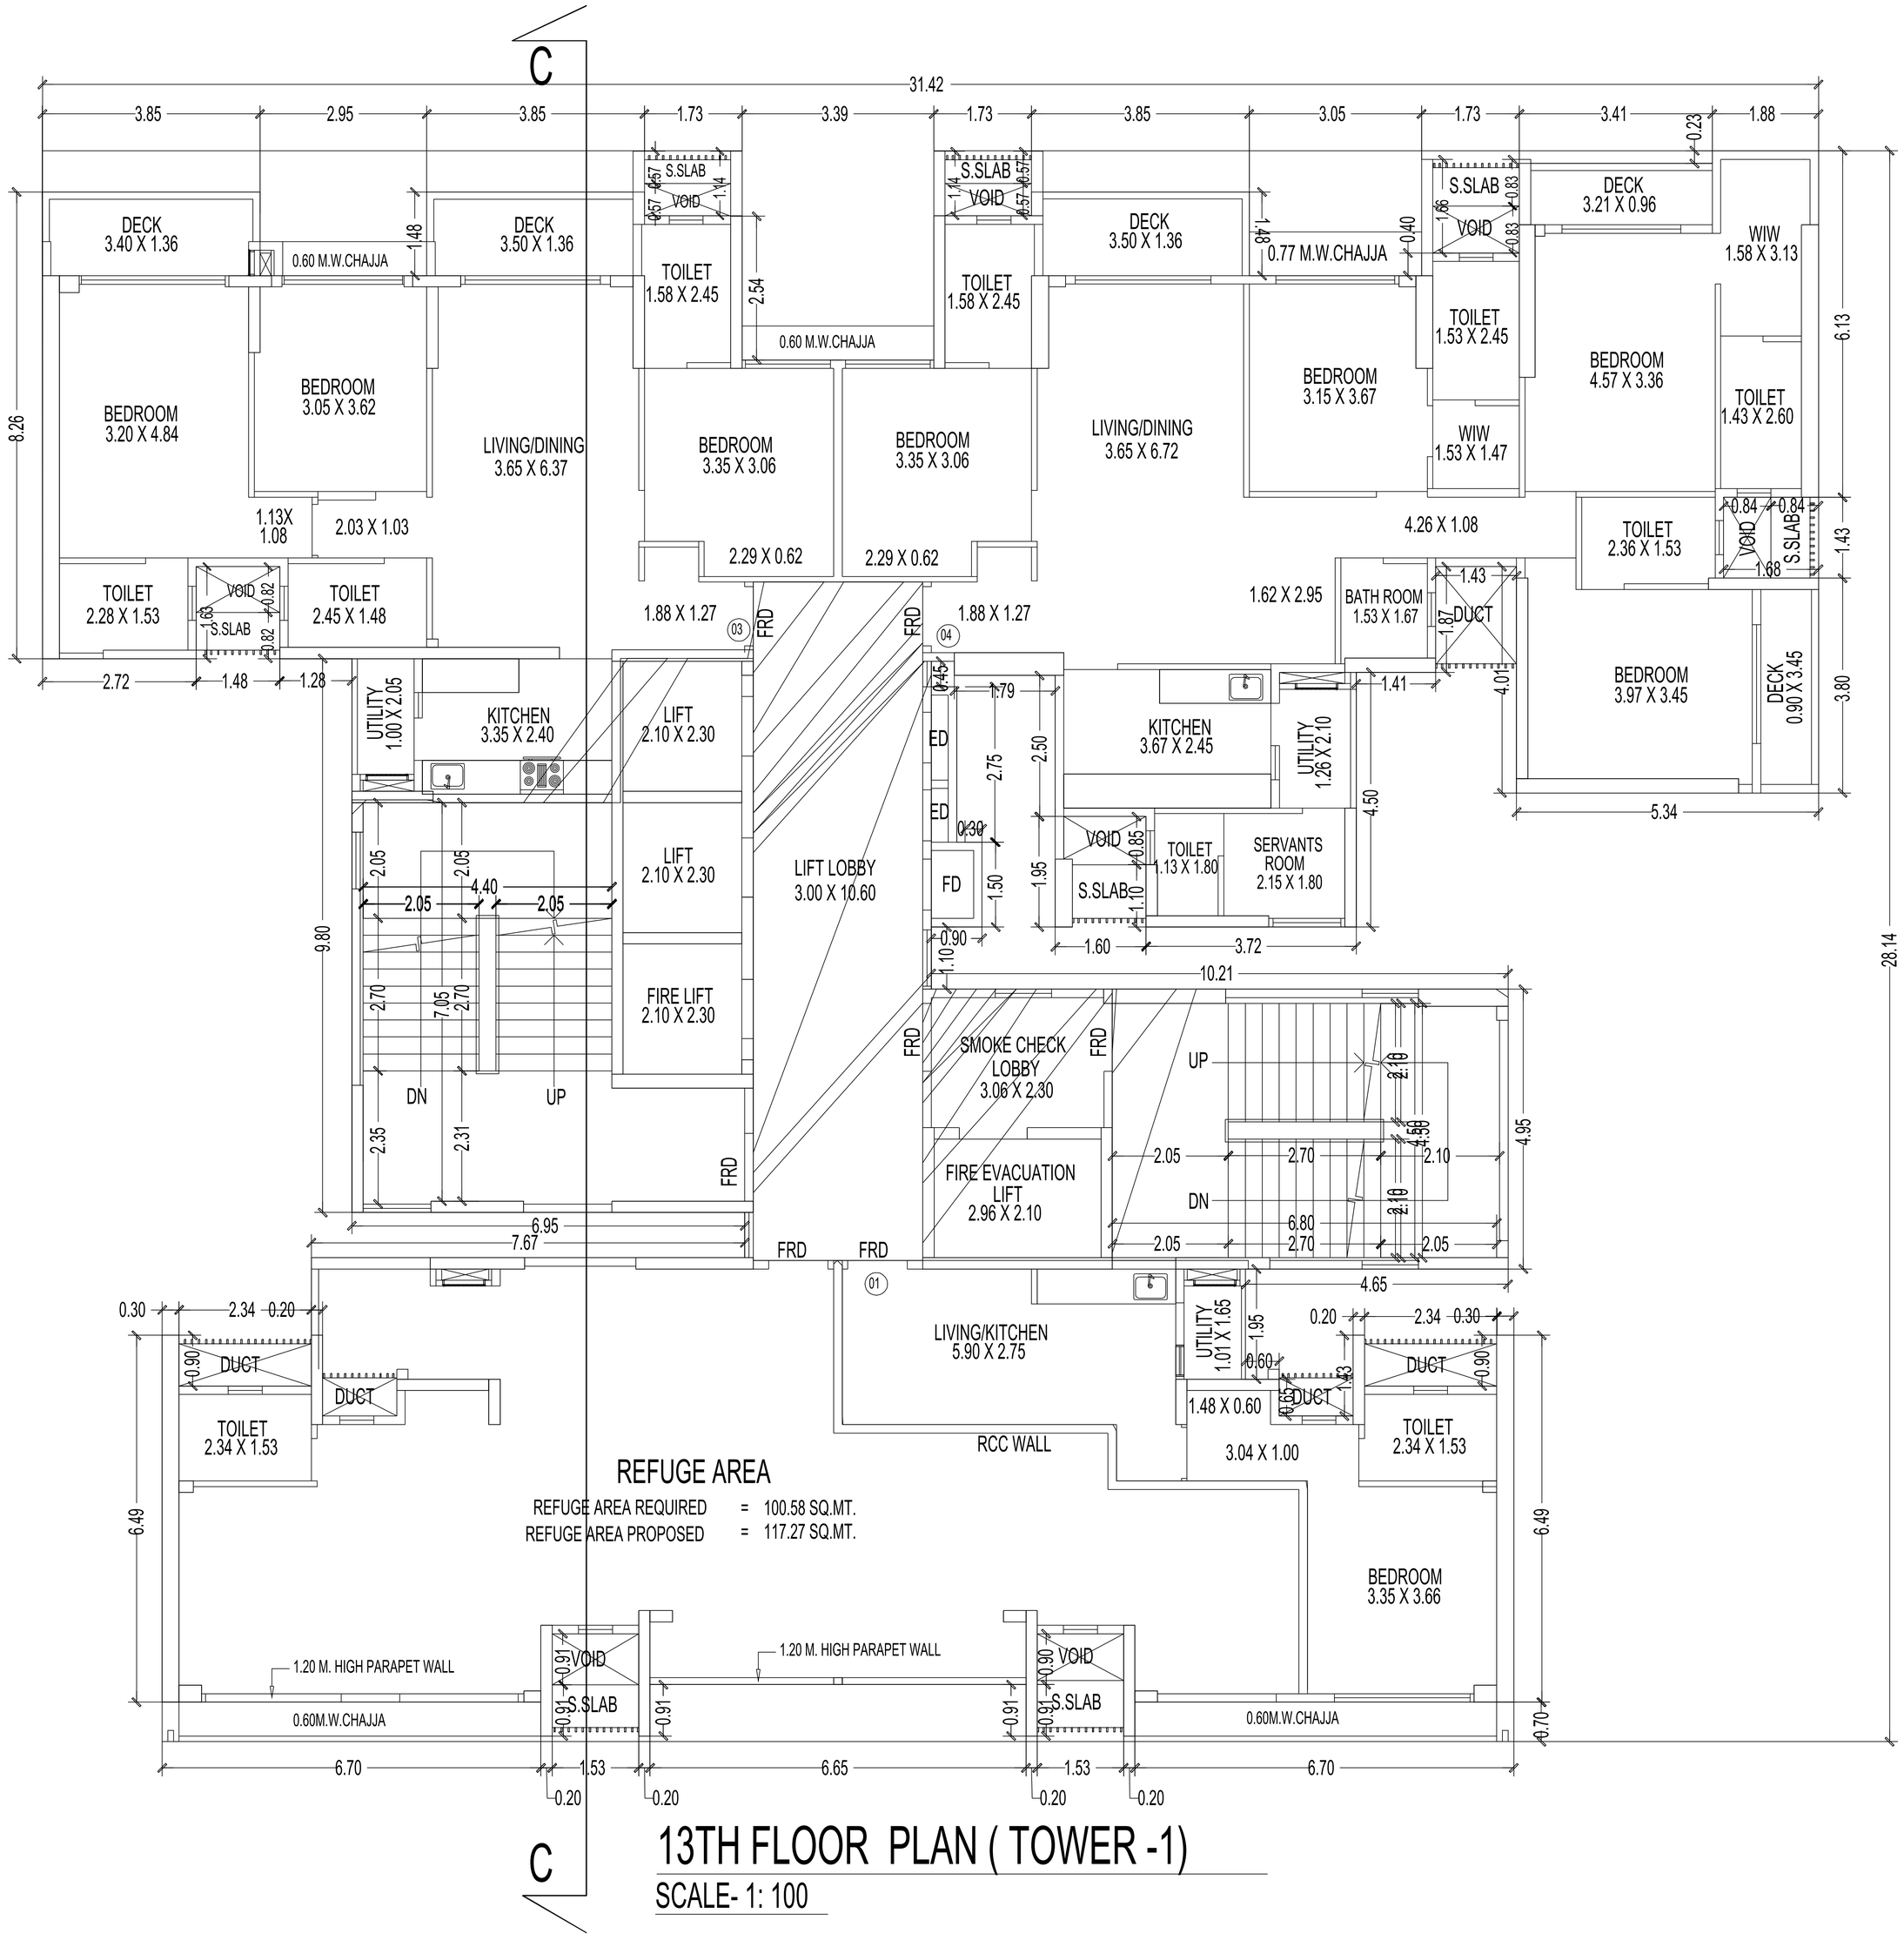


SQ.MT.
SQ.MT.

437.90 SQ.MT.

C


13TH FLOOR PLAN (TOWER -1)

SCALE- 1: 100

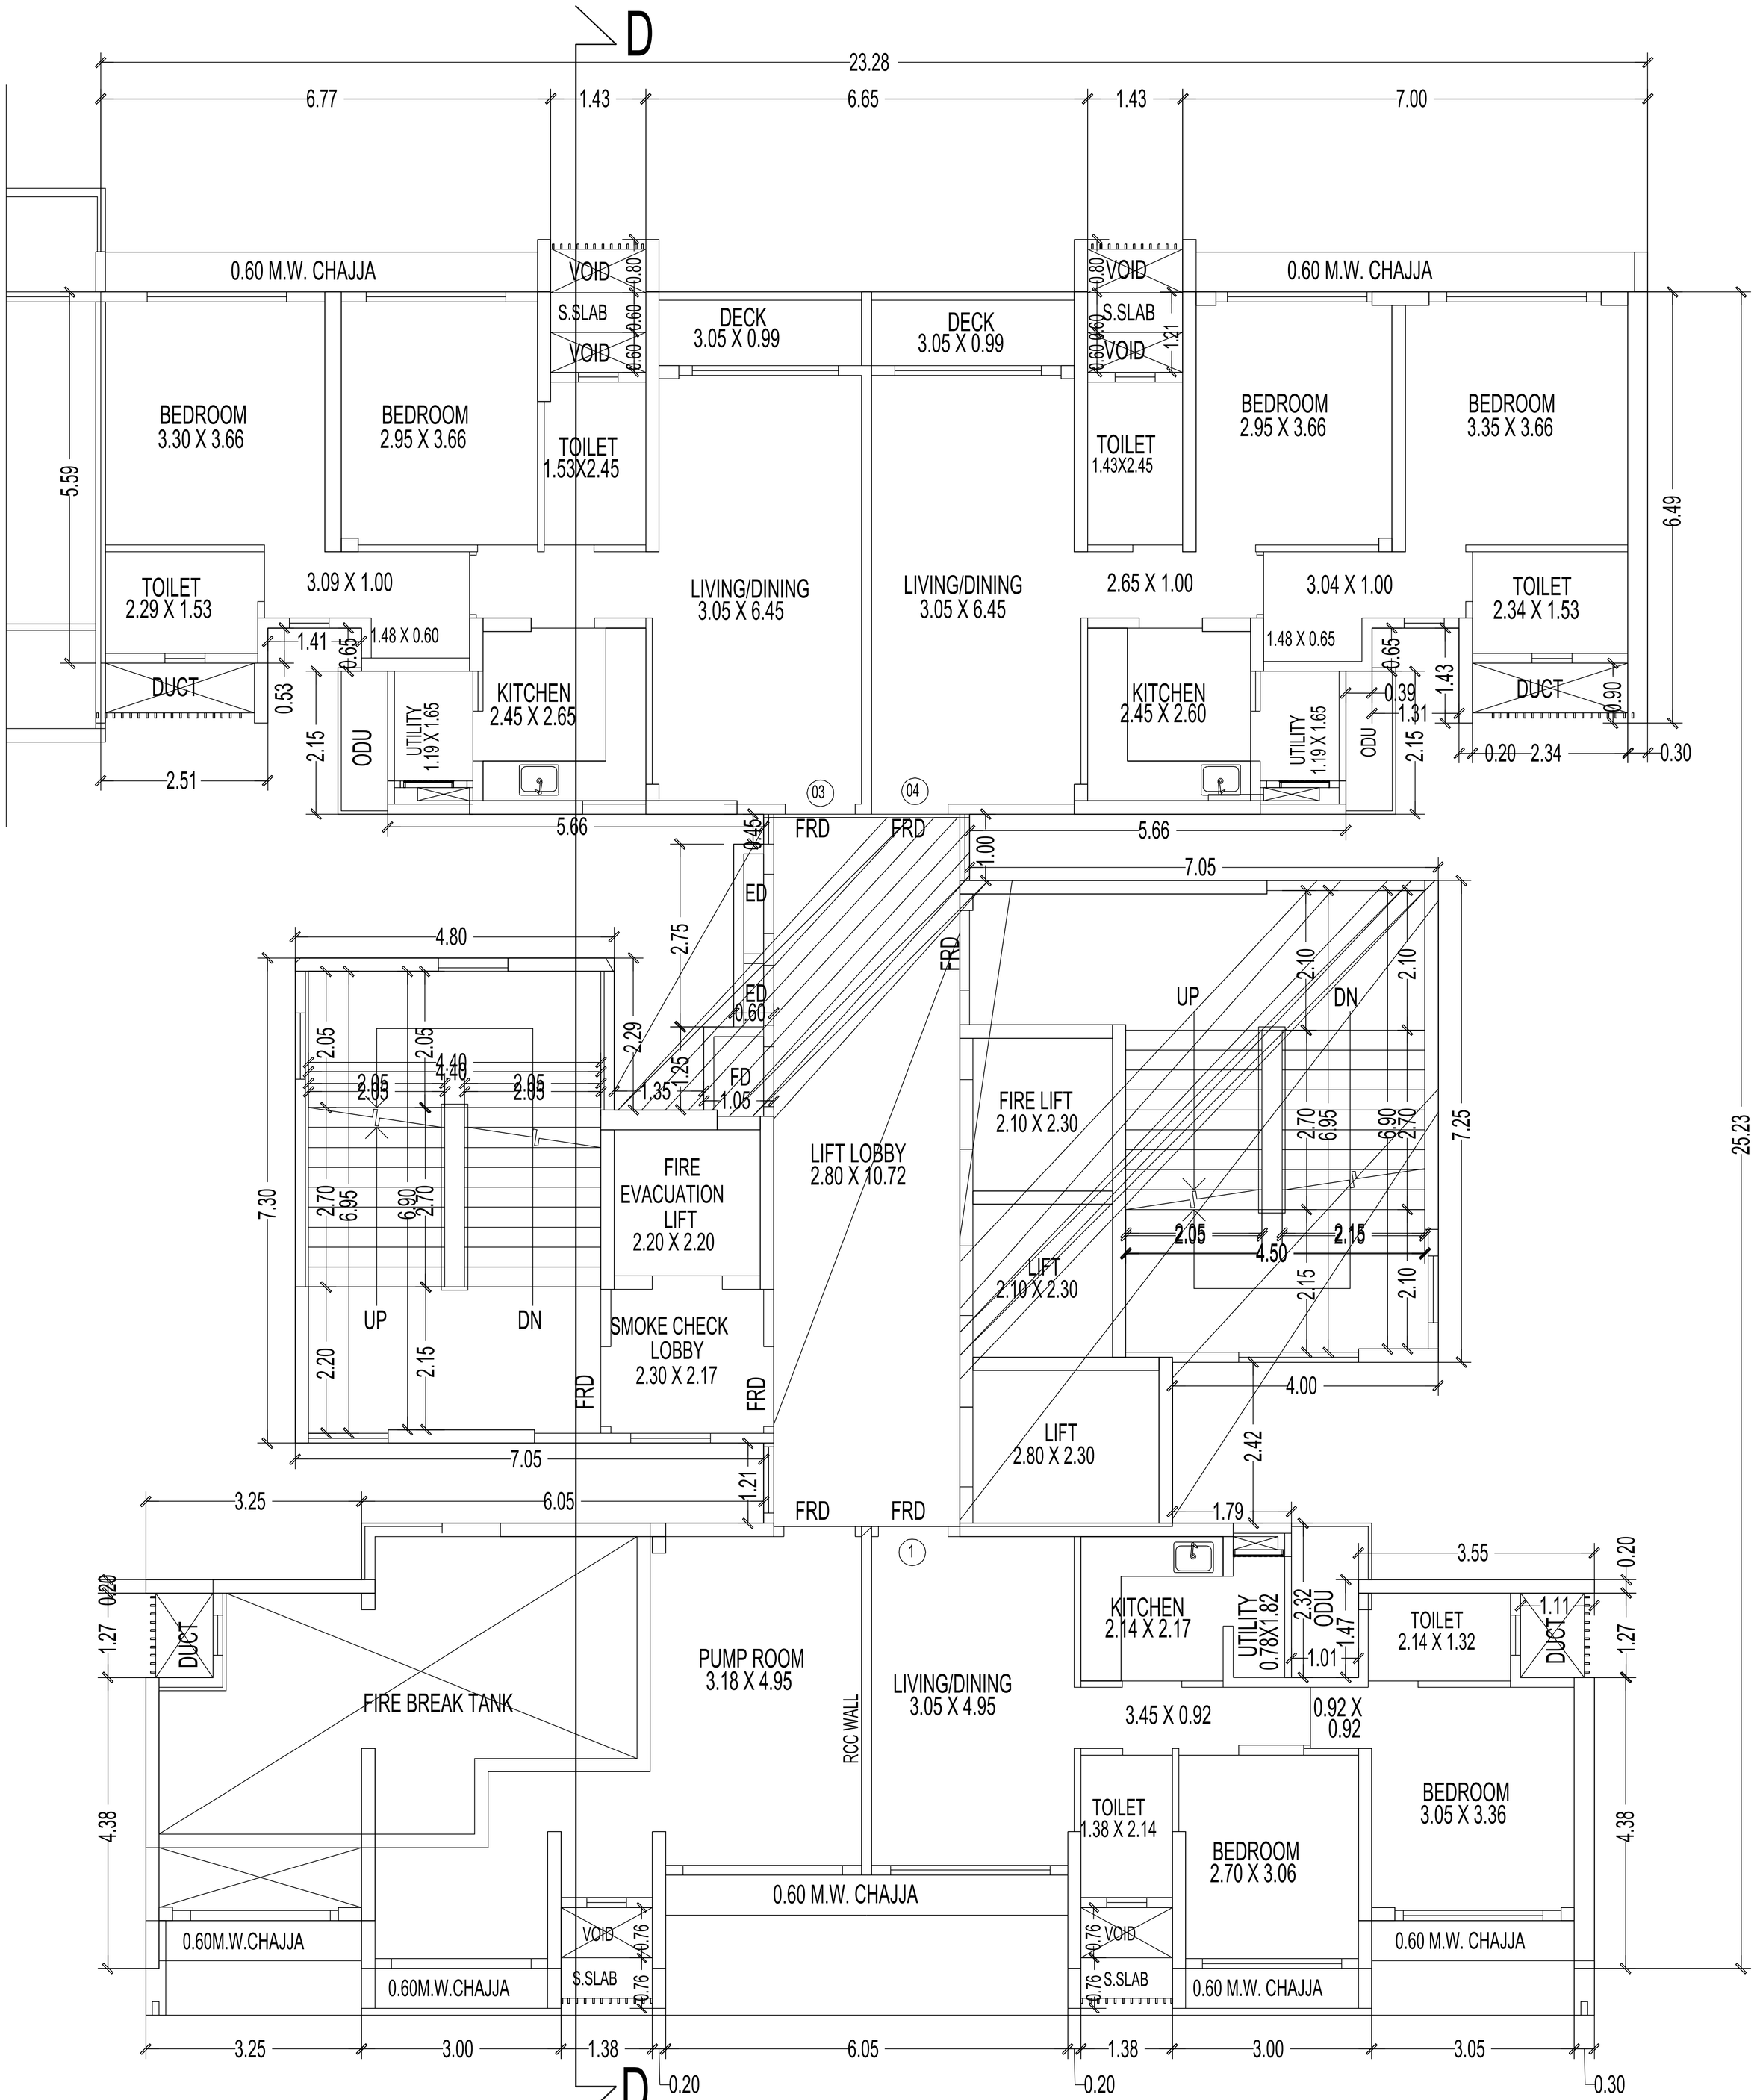

19TH FLOOR PLAN (TOWER -2)

SCALE- 1: 100

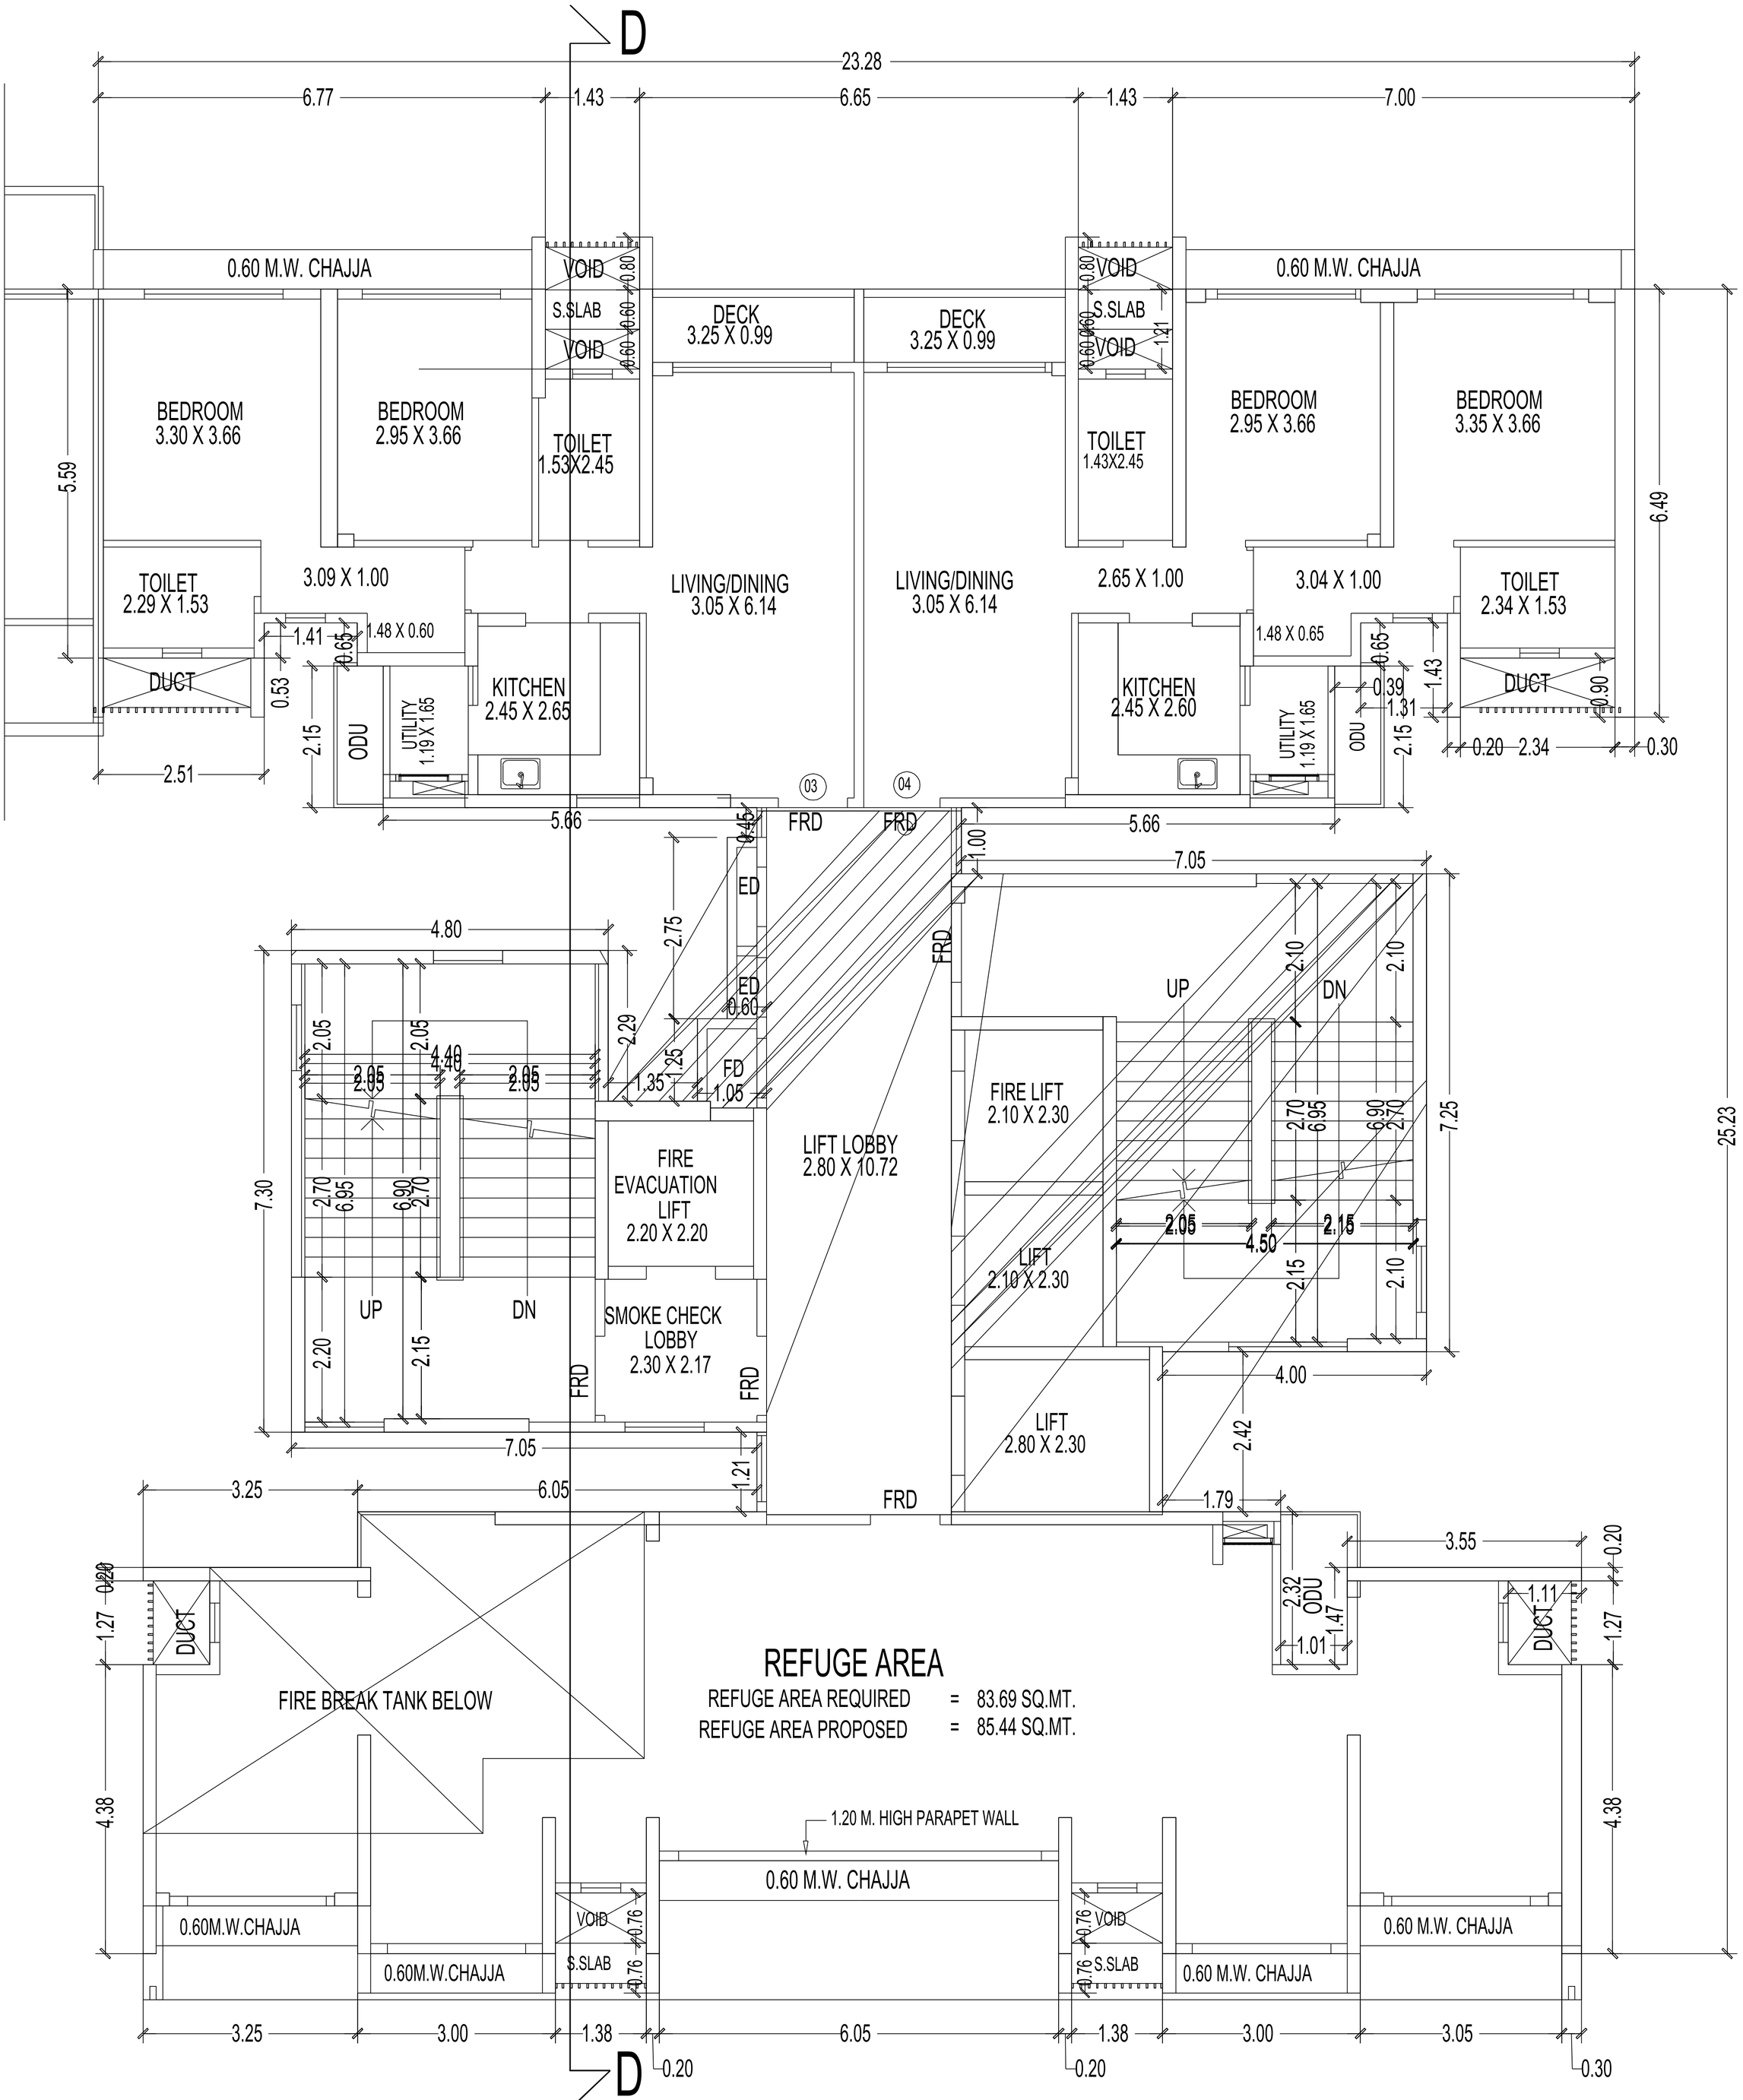

20TH FLOOR PLAN (TOWER -2)

SCALE- 1: 100