
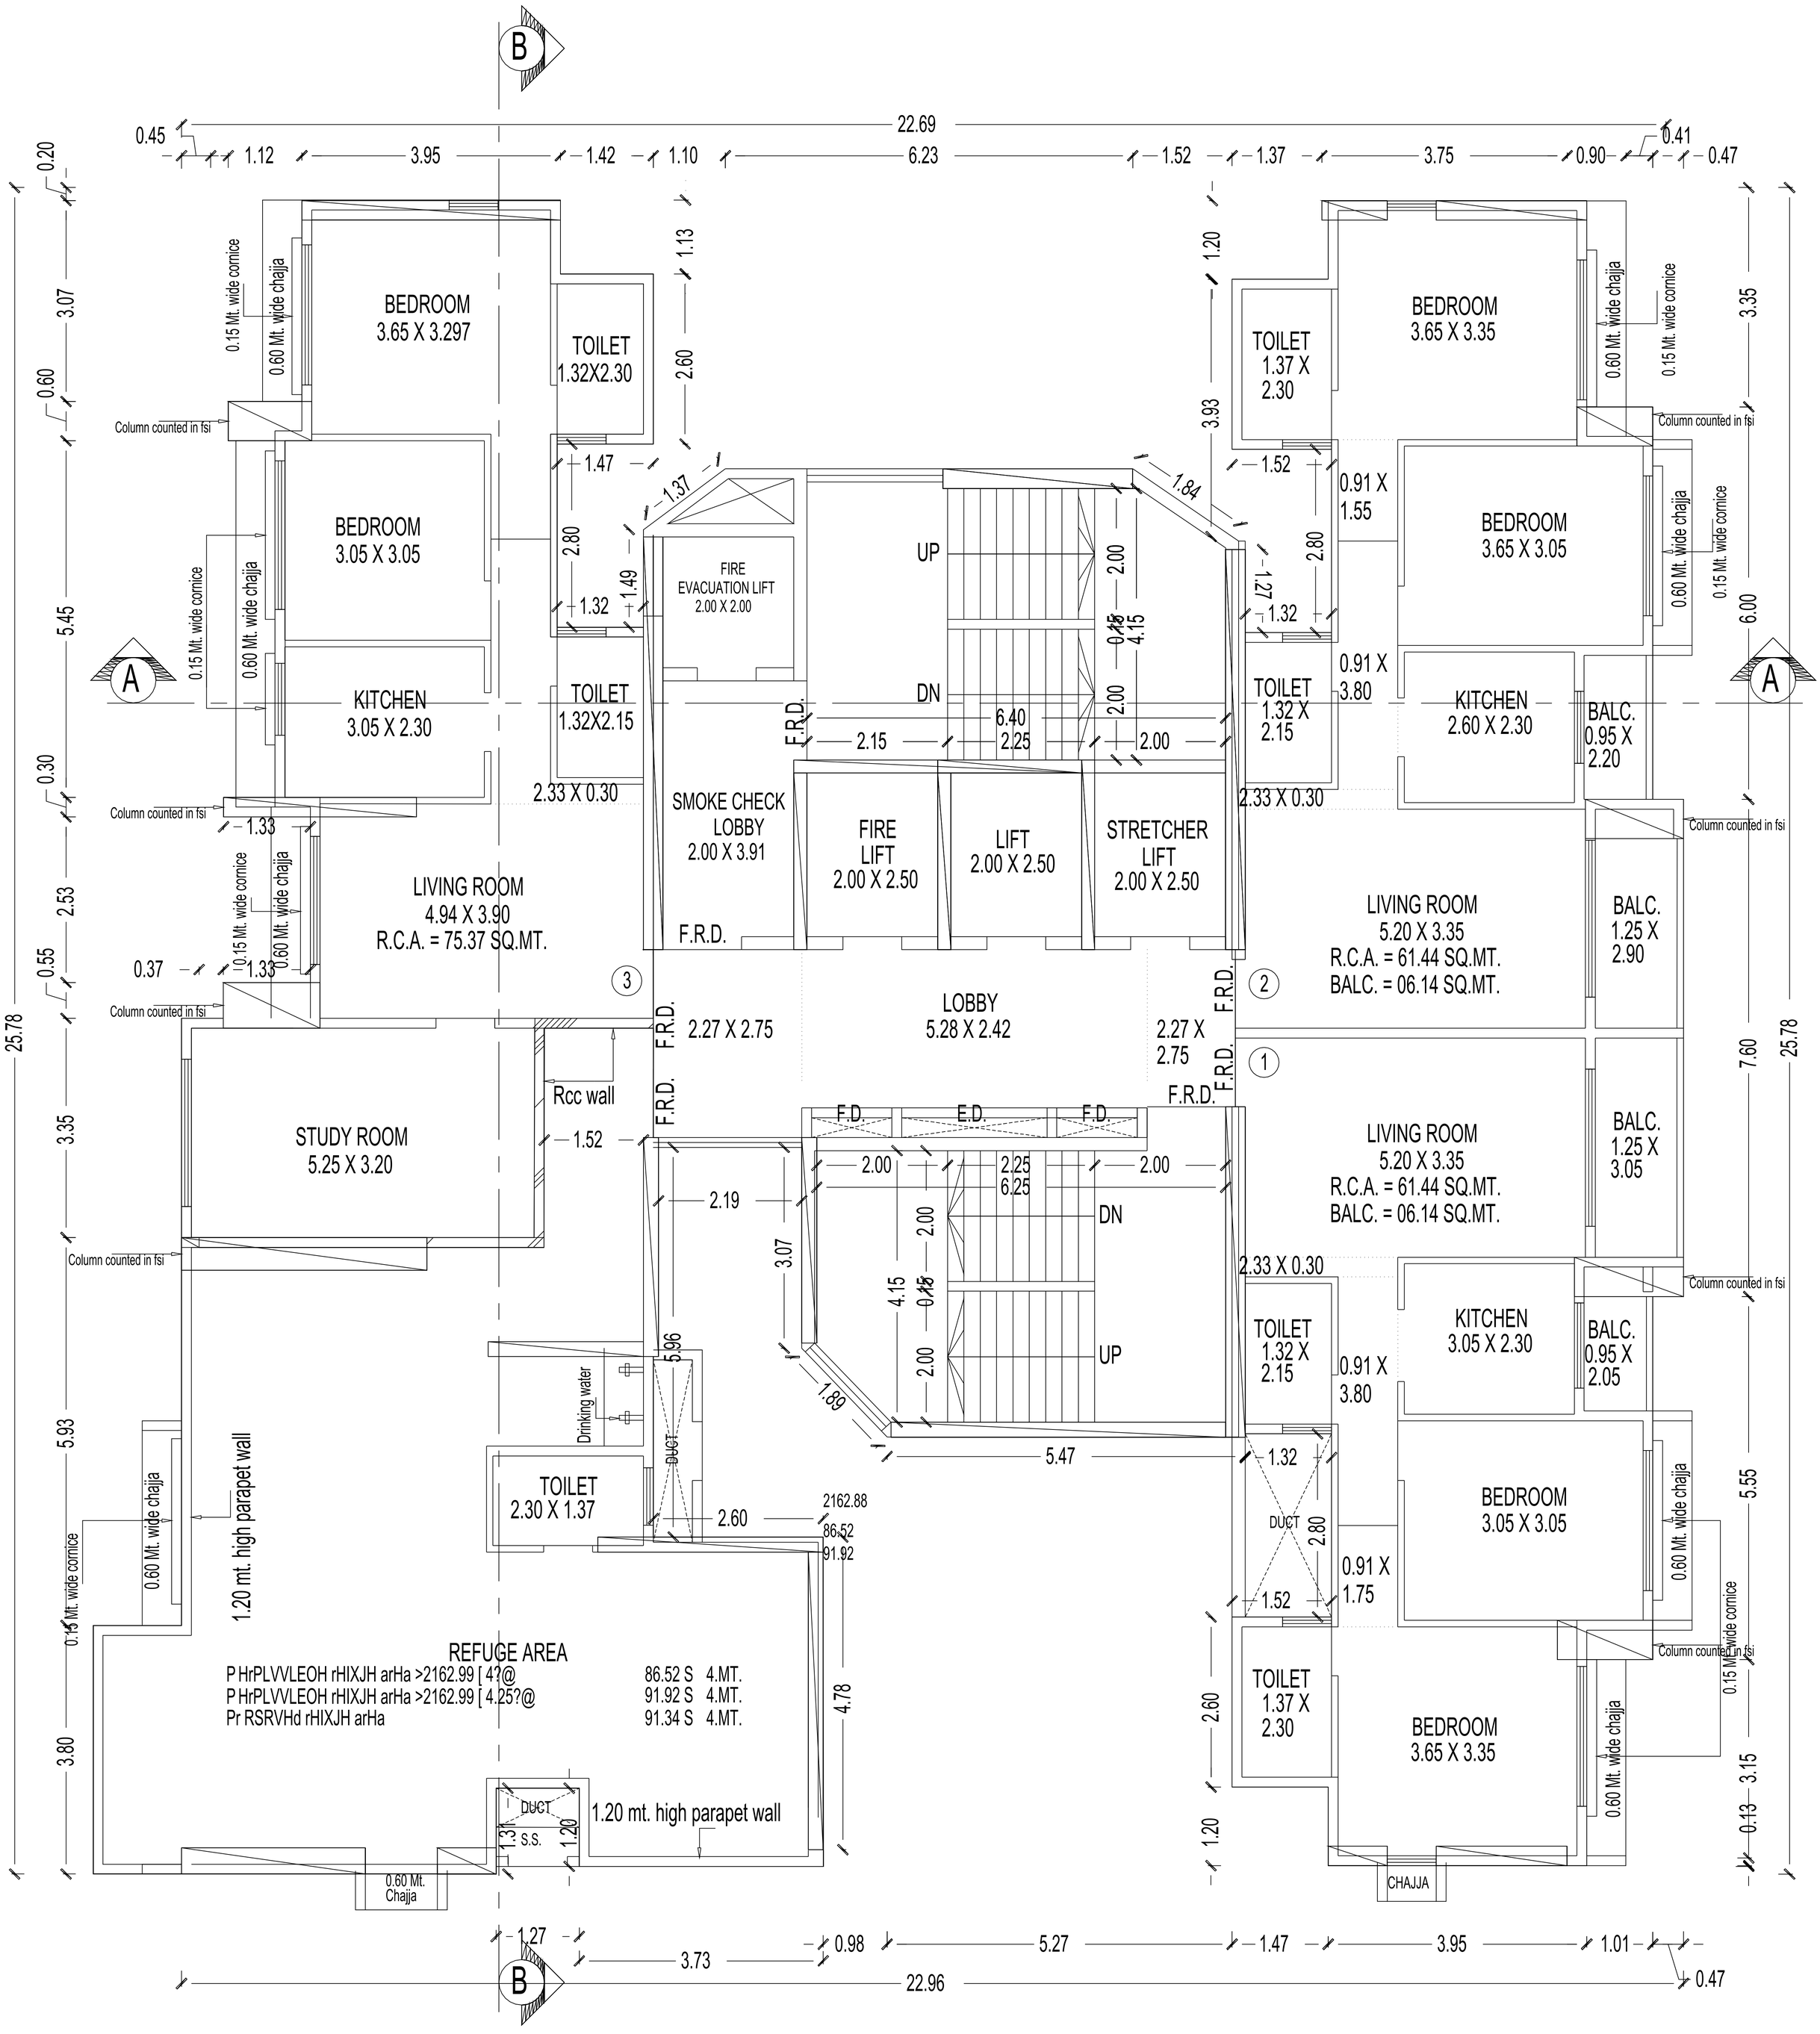


3RD & 10TH (REFUGE) FLOOR PLAN

SCALE :- 1:100

WING - B

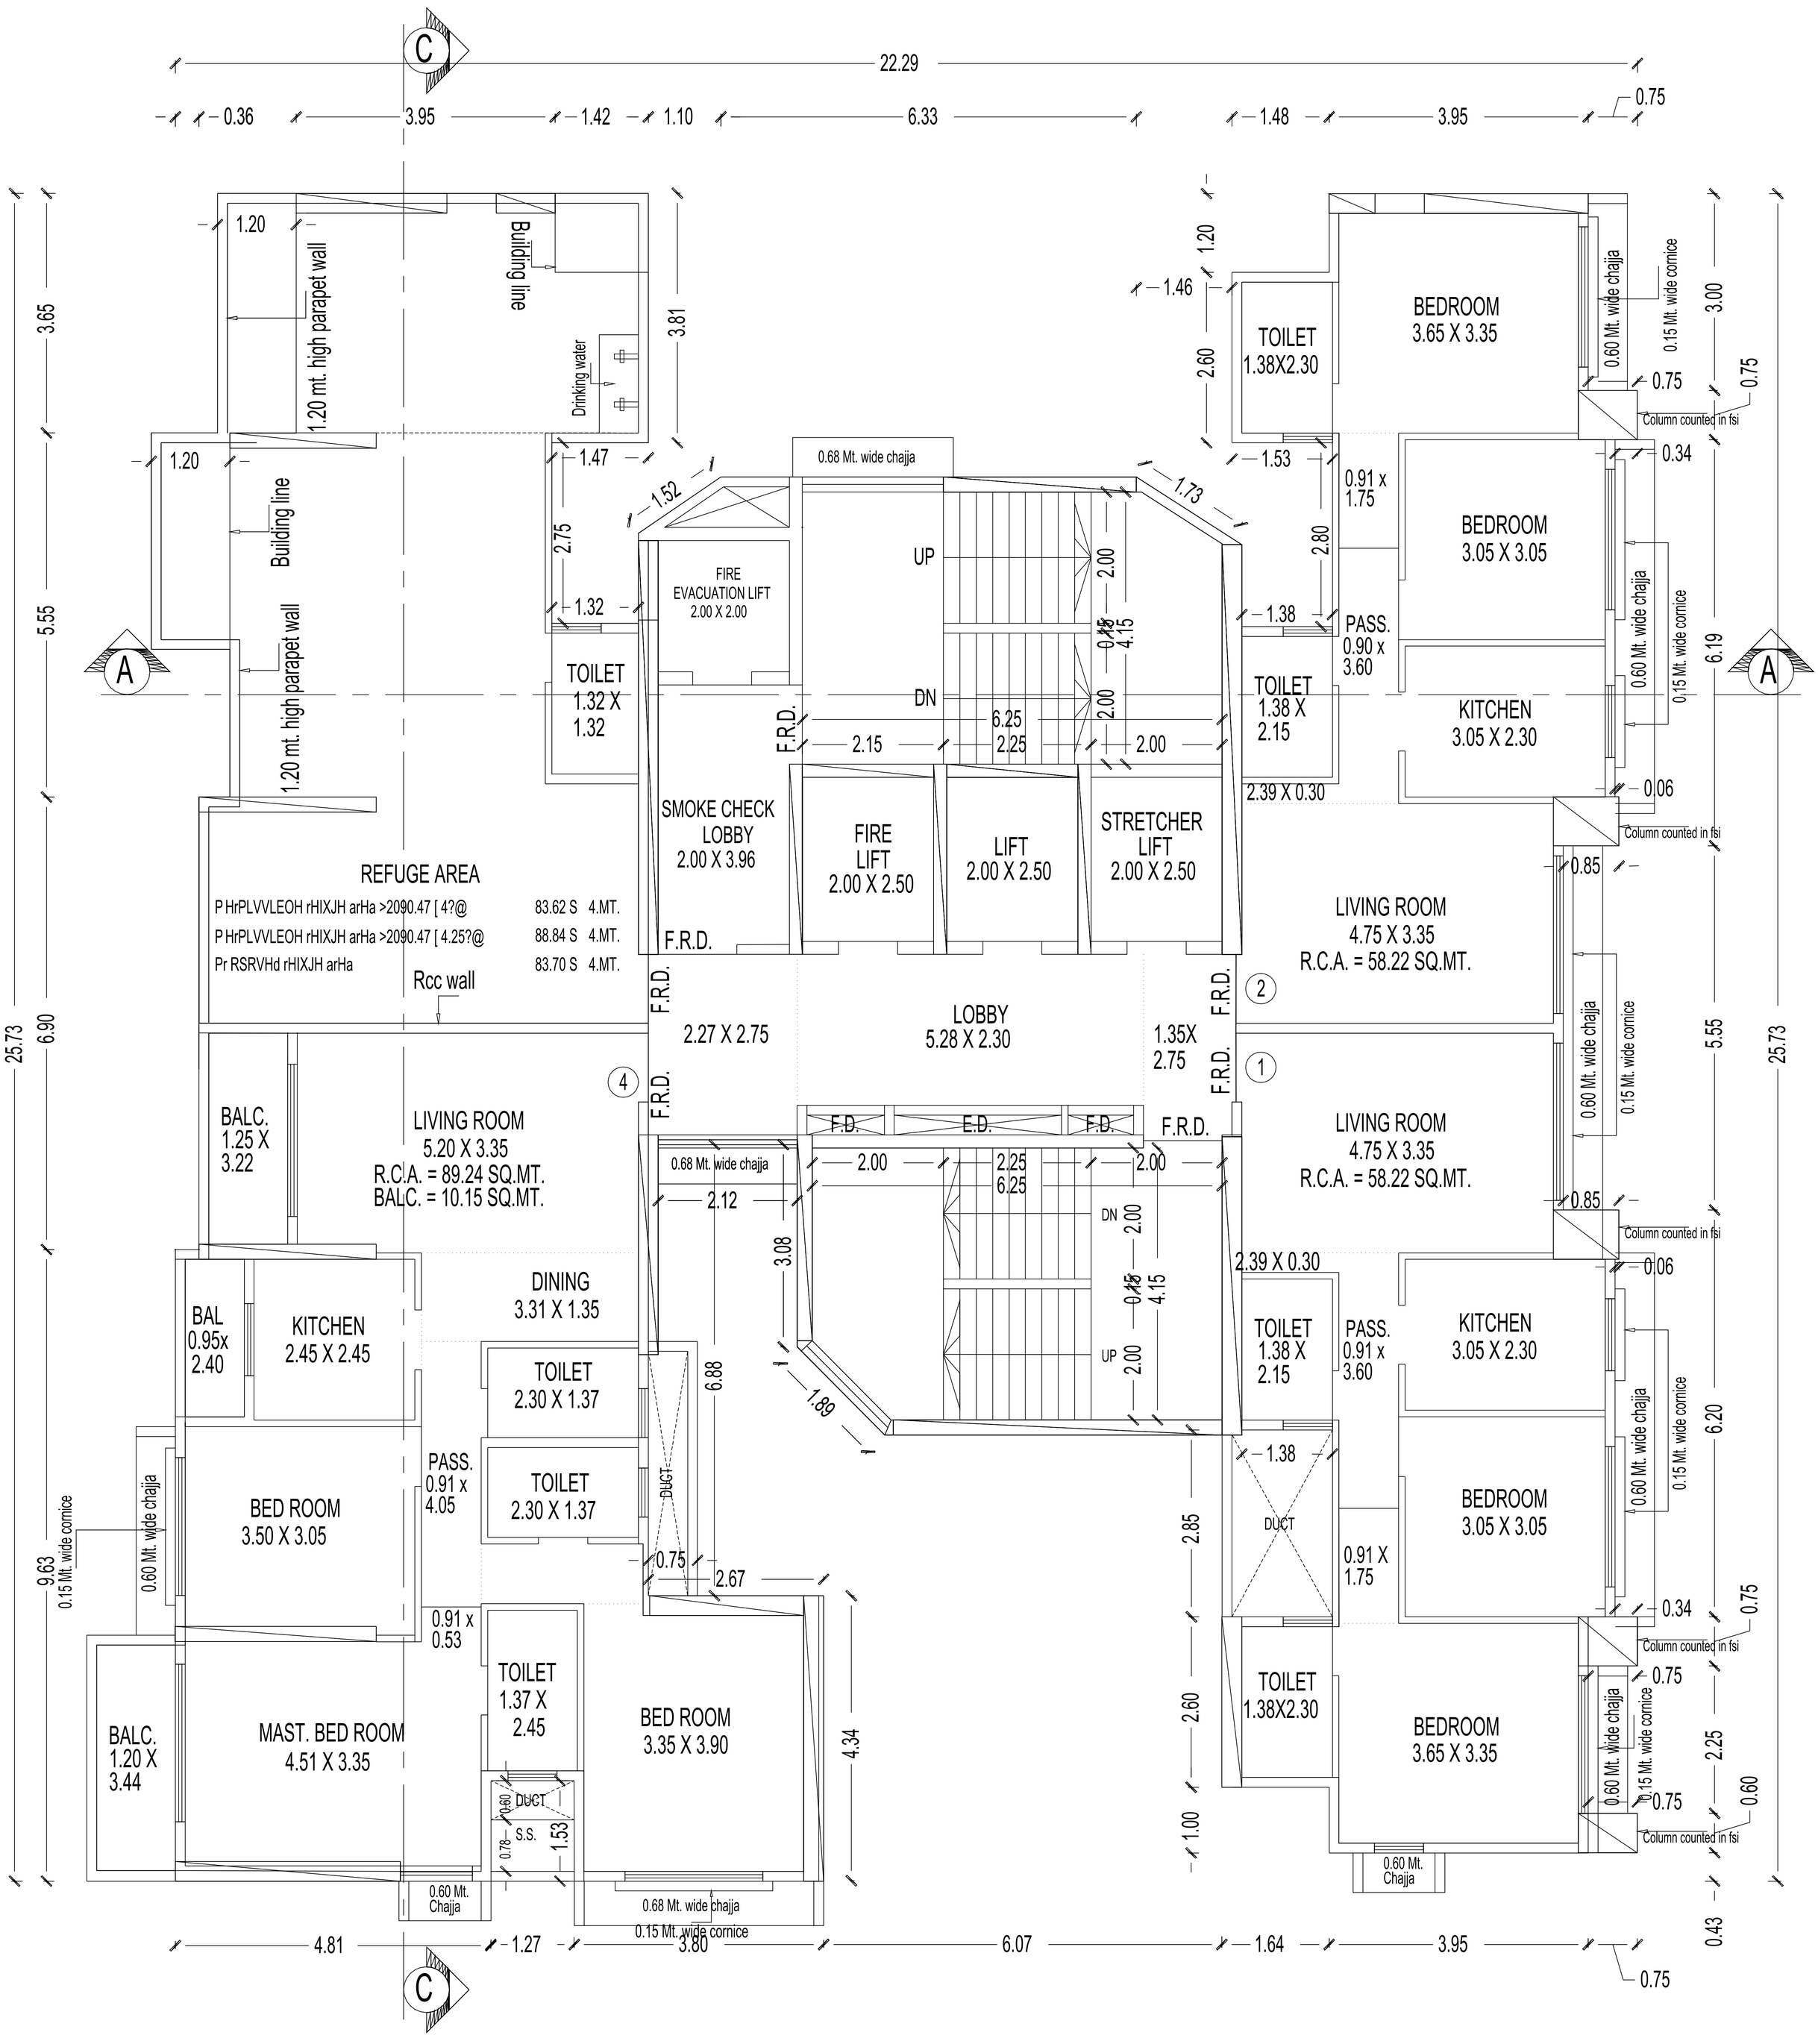

3RD & 10TH (REFUGE) FLOOR PLAN

SCALE :- 1:100

WING - A

B

22.69

0.45 | 1.12 | 3.95 | 1.42 | 1.10 | 6.23 | 1.52 | 1.37 | 3.75 | 0.90 | 0.41 | 0.47

0.20 | 3.07 | 0.60 | 5.45 | 0.30 | 2.53 | 0.55 | 3.35 | 5.93 | 3.80 | 0.15 | 25.78

BREAK PRESSURE
WATER STORAGE TANK
1 LAKH LITERS AT 17TH FLOORS ONLY

BREAK PRESSURE
WATER STORAGE TANK
1 LAKH LITERS AT 17TH FLOORS ONLY

BREAK PRESSURE
WATER STORAGE TANK
1 LAKH LITERS AT 17TH FLOORS ONLY

BREAK PRESSURE
WATER STORAGE TANK
1 LAKH LITERS AT 17TH FLOORS ONLY

0.60 Mt. wide chajja

0.60 Mt. wide chajja

0.60 Mt. wide chajja

0.60 Mt. wide chajja

Column counted in fsi

Column counted in fsi

Column counted in fsi

Column counted in fsi

1.13 | 2.60 | 2.80 | 1.48 | 1.49 | 1.32

1.37 | 1.84

FIRE
EVACUATION LIFT
2.00 X 2.00

UP | DN | 2.00 | 0.15 | 4.15 | 2.00 | 2.00

F.R.D. | 2.15 | 6.40 | 2.25 | 2.00

SMOKE CHECK
LOBBY
2.00 X 3.91

FIRE
LIFT
2.00 X 2.50

LIFT
2.00 X 2.50

STRETCHER
LIFT
2.00 X 2.50

F.R.D.

1.20 | 3.93 | 1.52 | 2.80 | 1.27 | 1.32

TOILET
1.37 X
2.30

BEDROOM
3.65 X 3.35

0.91 X
1.55

BEDROOM
3.65 X 3.05

0.15 Mt. wide cornice

0.91 X
3.80

TOILET
1.32 X
2.15

KITCHEN
2.60 X 2.30

BALC.
0.95 X
2.20

2.33 X 0.30

Column counted in fsi

Column counted in fsi

1.33 | 0.37 | 1.33

0.60 Mt. wide chajja

Column counted in fsi

Rcc wall

F.R.D.

2.27 X 2.75

LOBBY
5.28 X 2.42

2.27 X
2.75

F.R.D.

F.R.D.

F.R.D.

F.R.D.

2

1

LIVING ROOM
5.20 X 3.35
R.C.A. = 61.44 SQ.MT.
BALC. = 06.14 SQ.MT.

BALC.
1.25 X
2.90

LIVING ROOM
5.20 X 3.35
R.C.A. = 61.44 SQ.MT.
BALC. = 06.14 SQ.MT.

BALC.
1.25 X
3.05

PUMP ROOM
5.24 X 4.13

Rcc wall

F.R.D.

F.D. | E.D. | F.D.

2.00 | 2.25 | 2.00
6.25

2.19 | 3.07 | 4.15 | 0.15 | 2.00 | 2.00

DN

UP

1.89

5.47

2.33 X 0.30

TOILET
1.32 X
2.15

0.91 X
3.80

KITCHEN
3.05 X 2.30

BALC.
0.95 X
2.05

Column counted in fsi

Column counted in fsi

Drinking water

DUCT

5.96

TOILET
2.30 X 1.37

2.60 | 2162.88 | 86.52 | 91.92

1.20 mt. high parapet wall

0.60 Mt. wide chajja

0.15 Mt. wide cornice

REFUGE AREA

P HrPLVVLEOH rHIXJH arHa >2078.98 [4?@	83.16 S	4.MT.
P HrPLVVLEOH rHIXJH arHa >2078.98 [4.25?@	88.36 S	4.MT.
Pr RSRVHd rHIXJH arHa	88.37 S	4.MT.

4.78

DUCT | 1.3 | S.S. | 1.20

1.20 mt. high parapet wall

DUCT | 2.80

1.32

1.52

0.91 X
1.75

TOILET
1.37 X
2.30

BEDROOM
3.05 X 3.05

BEDROOM
3.65 X 3.35

Column counted in fsi

0.15 Mt. wide cornice

0.60 Mt. wide chajja

0.60 Mt. wide chajja

2.60 | 1.20

CHAJJA


1.27 | 3.73 | 0.98 | 5.27 | 1.47 | 3.95 | 1.01 | 0.47

B

17TH (REFUGE) FLOOR PLAN

SCALE :- 1:100

WING - B

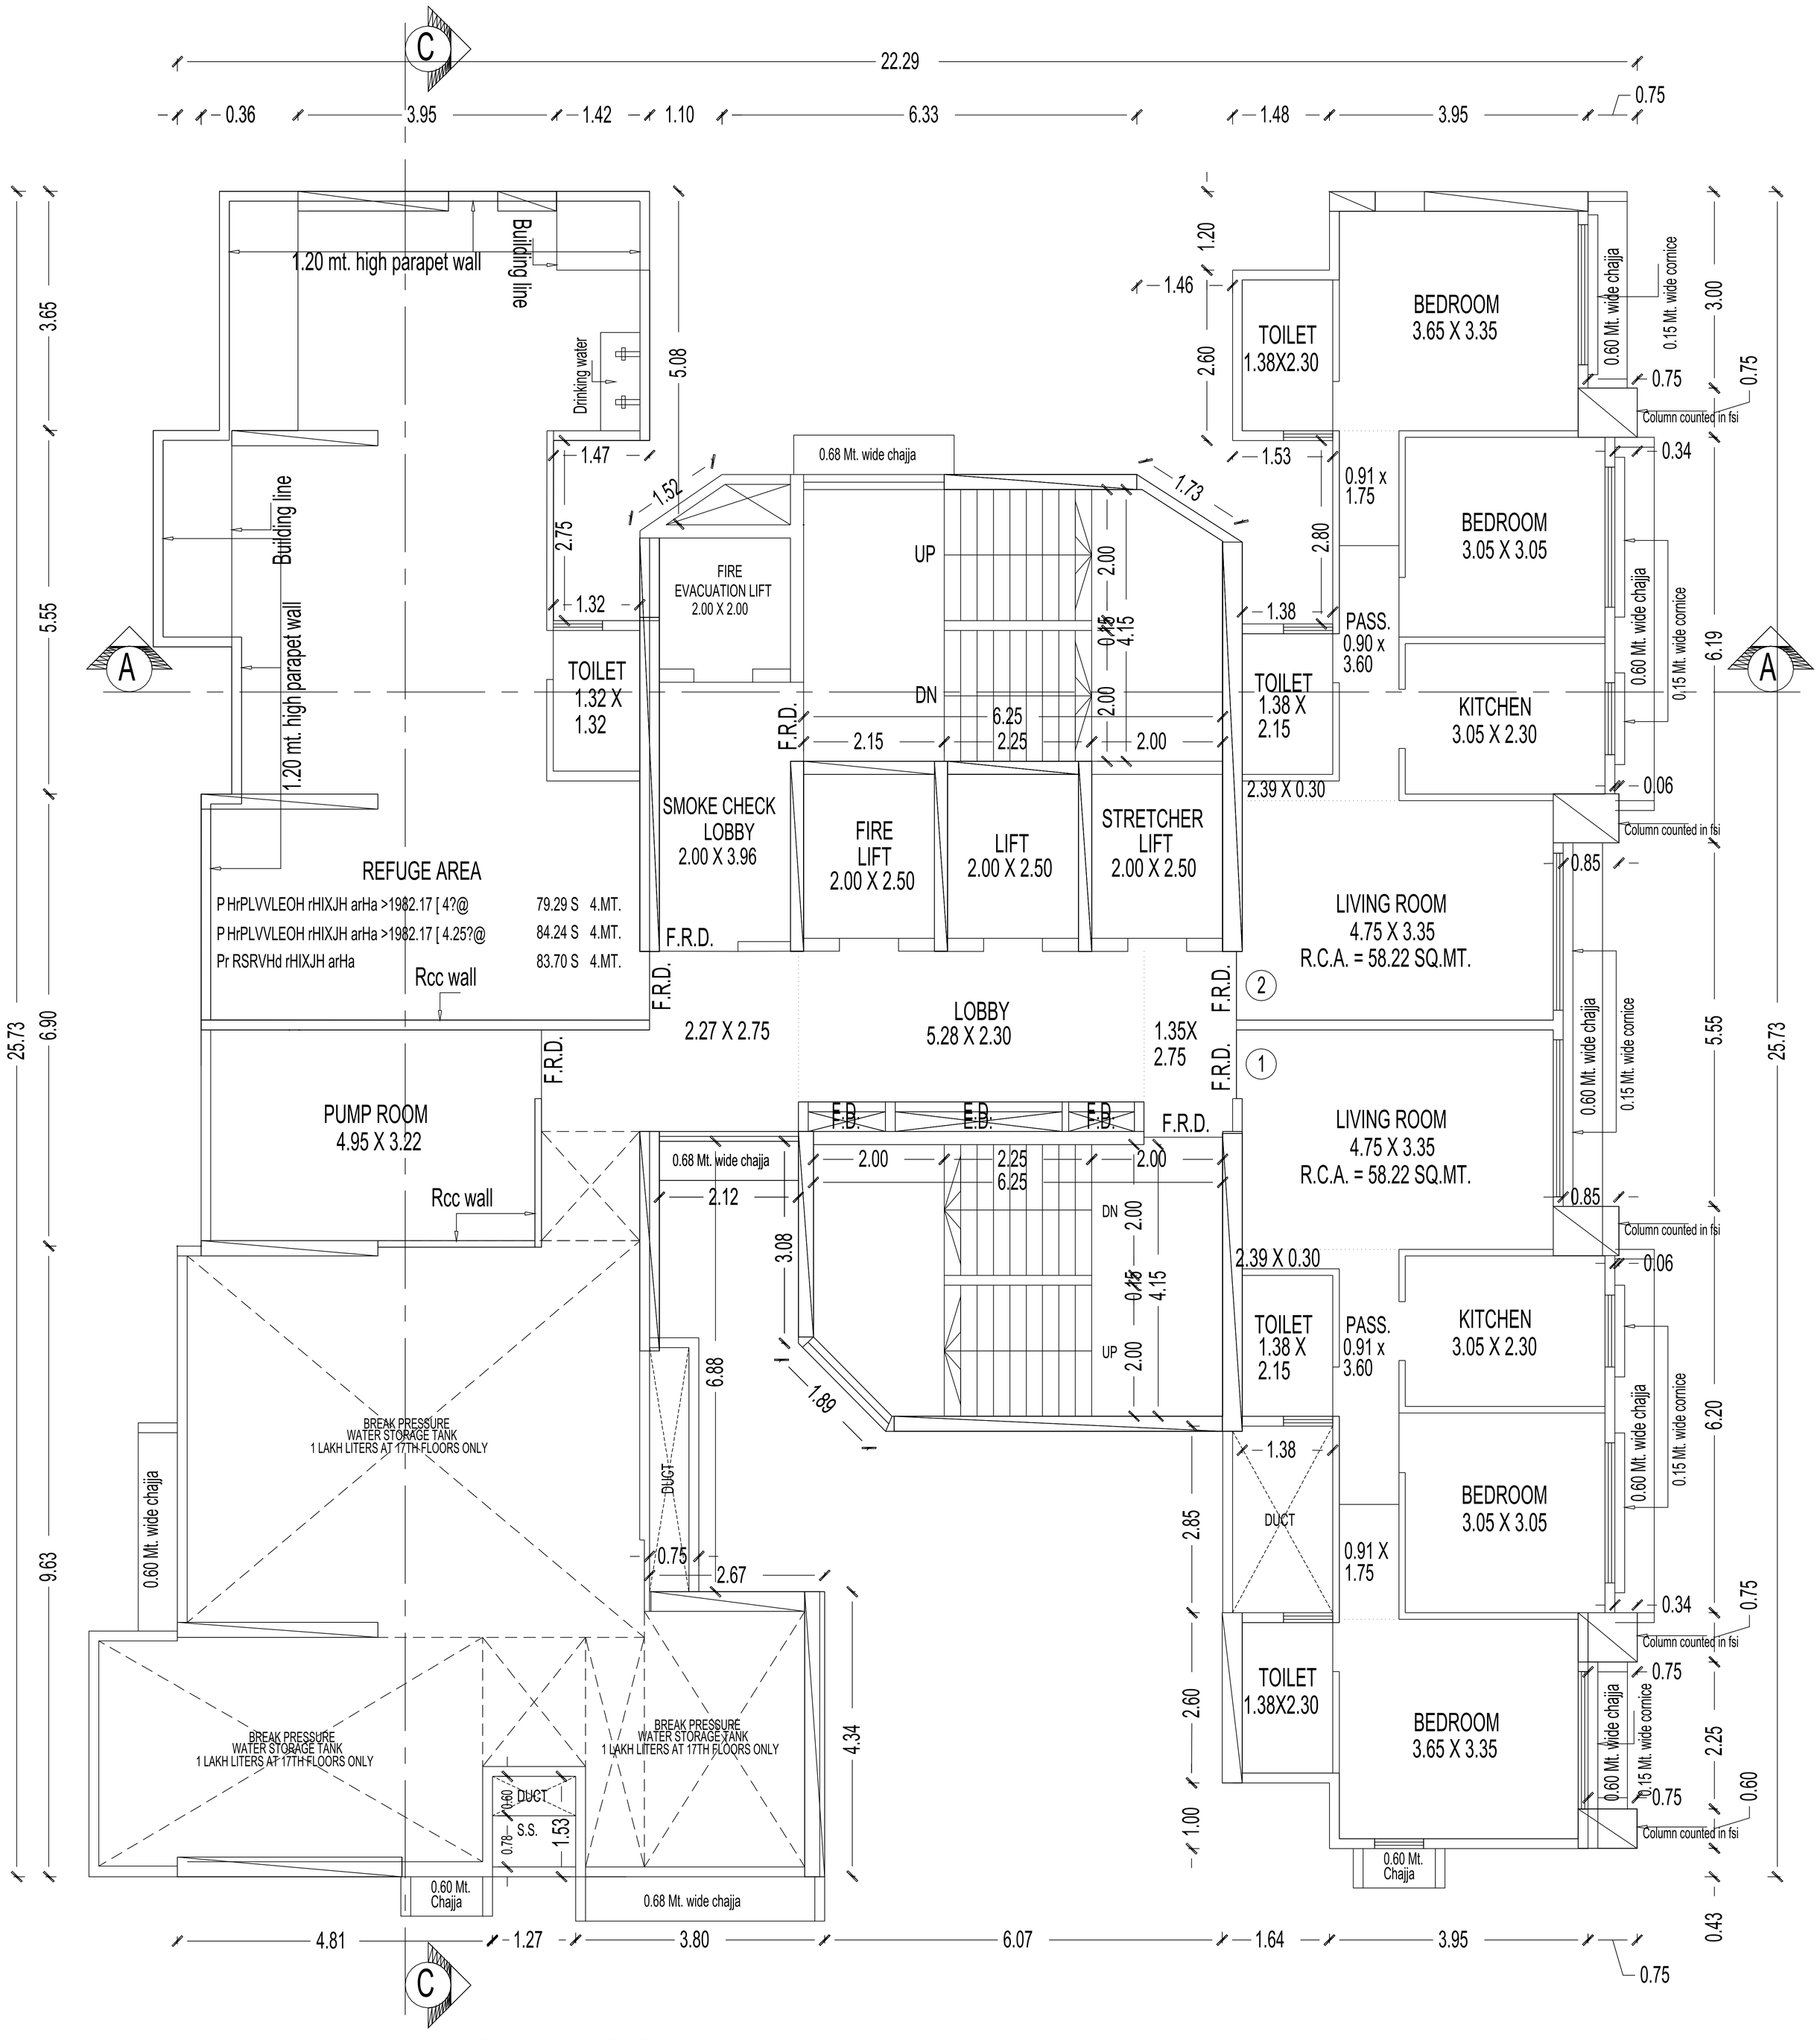

17TH (REFUGE) FLOOR PLAN

SCALE :- 1:100

WING - A


REFUGE AREA

P HrPLVVLEOH rHIXJH arHa >902.71 [4?@	36.11 S	4.MT.
P HrPLVVLEOH rHIXJH arHa >902.71 [4.25?@	38.37 S	4.MT.
Pr RSRVHd rHIXJH arHa	85.27 S	4.MT.
C RXQWHd LQ IVL rHIXJH arHa	46.90 S	4.MT.

24TH (REFUGE) FLOOR PLAN


SCALE :- 1:100

WING - A

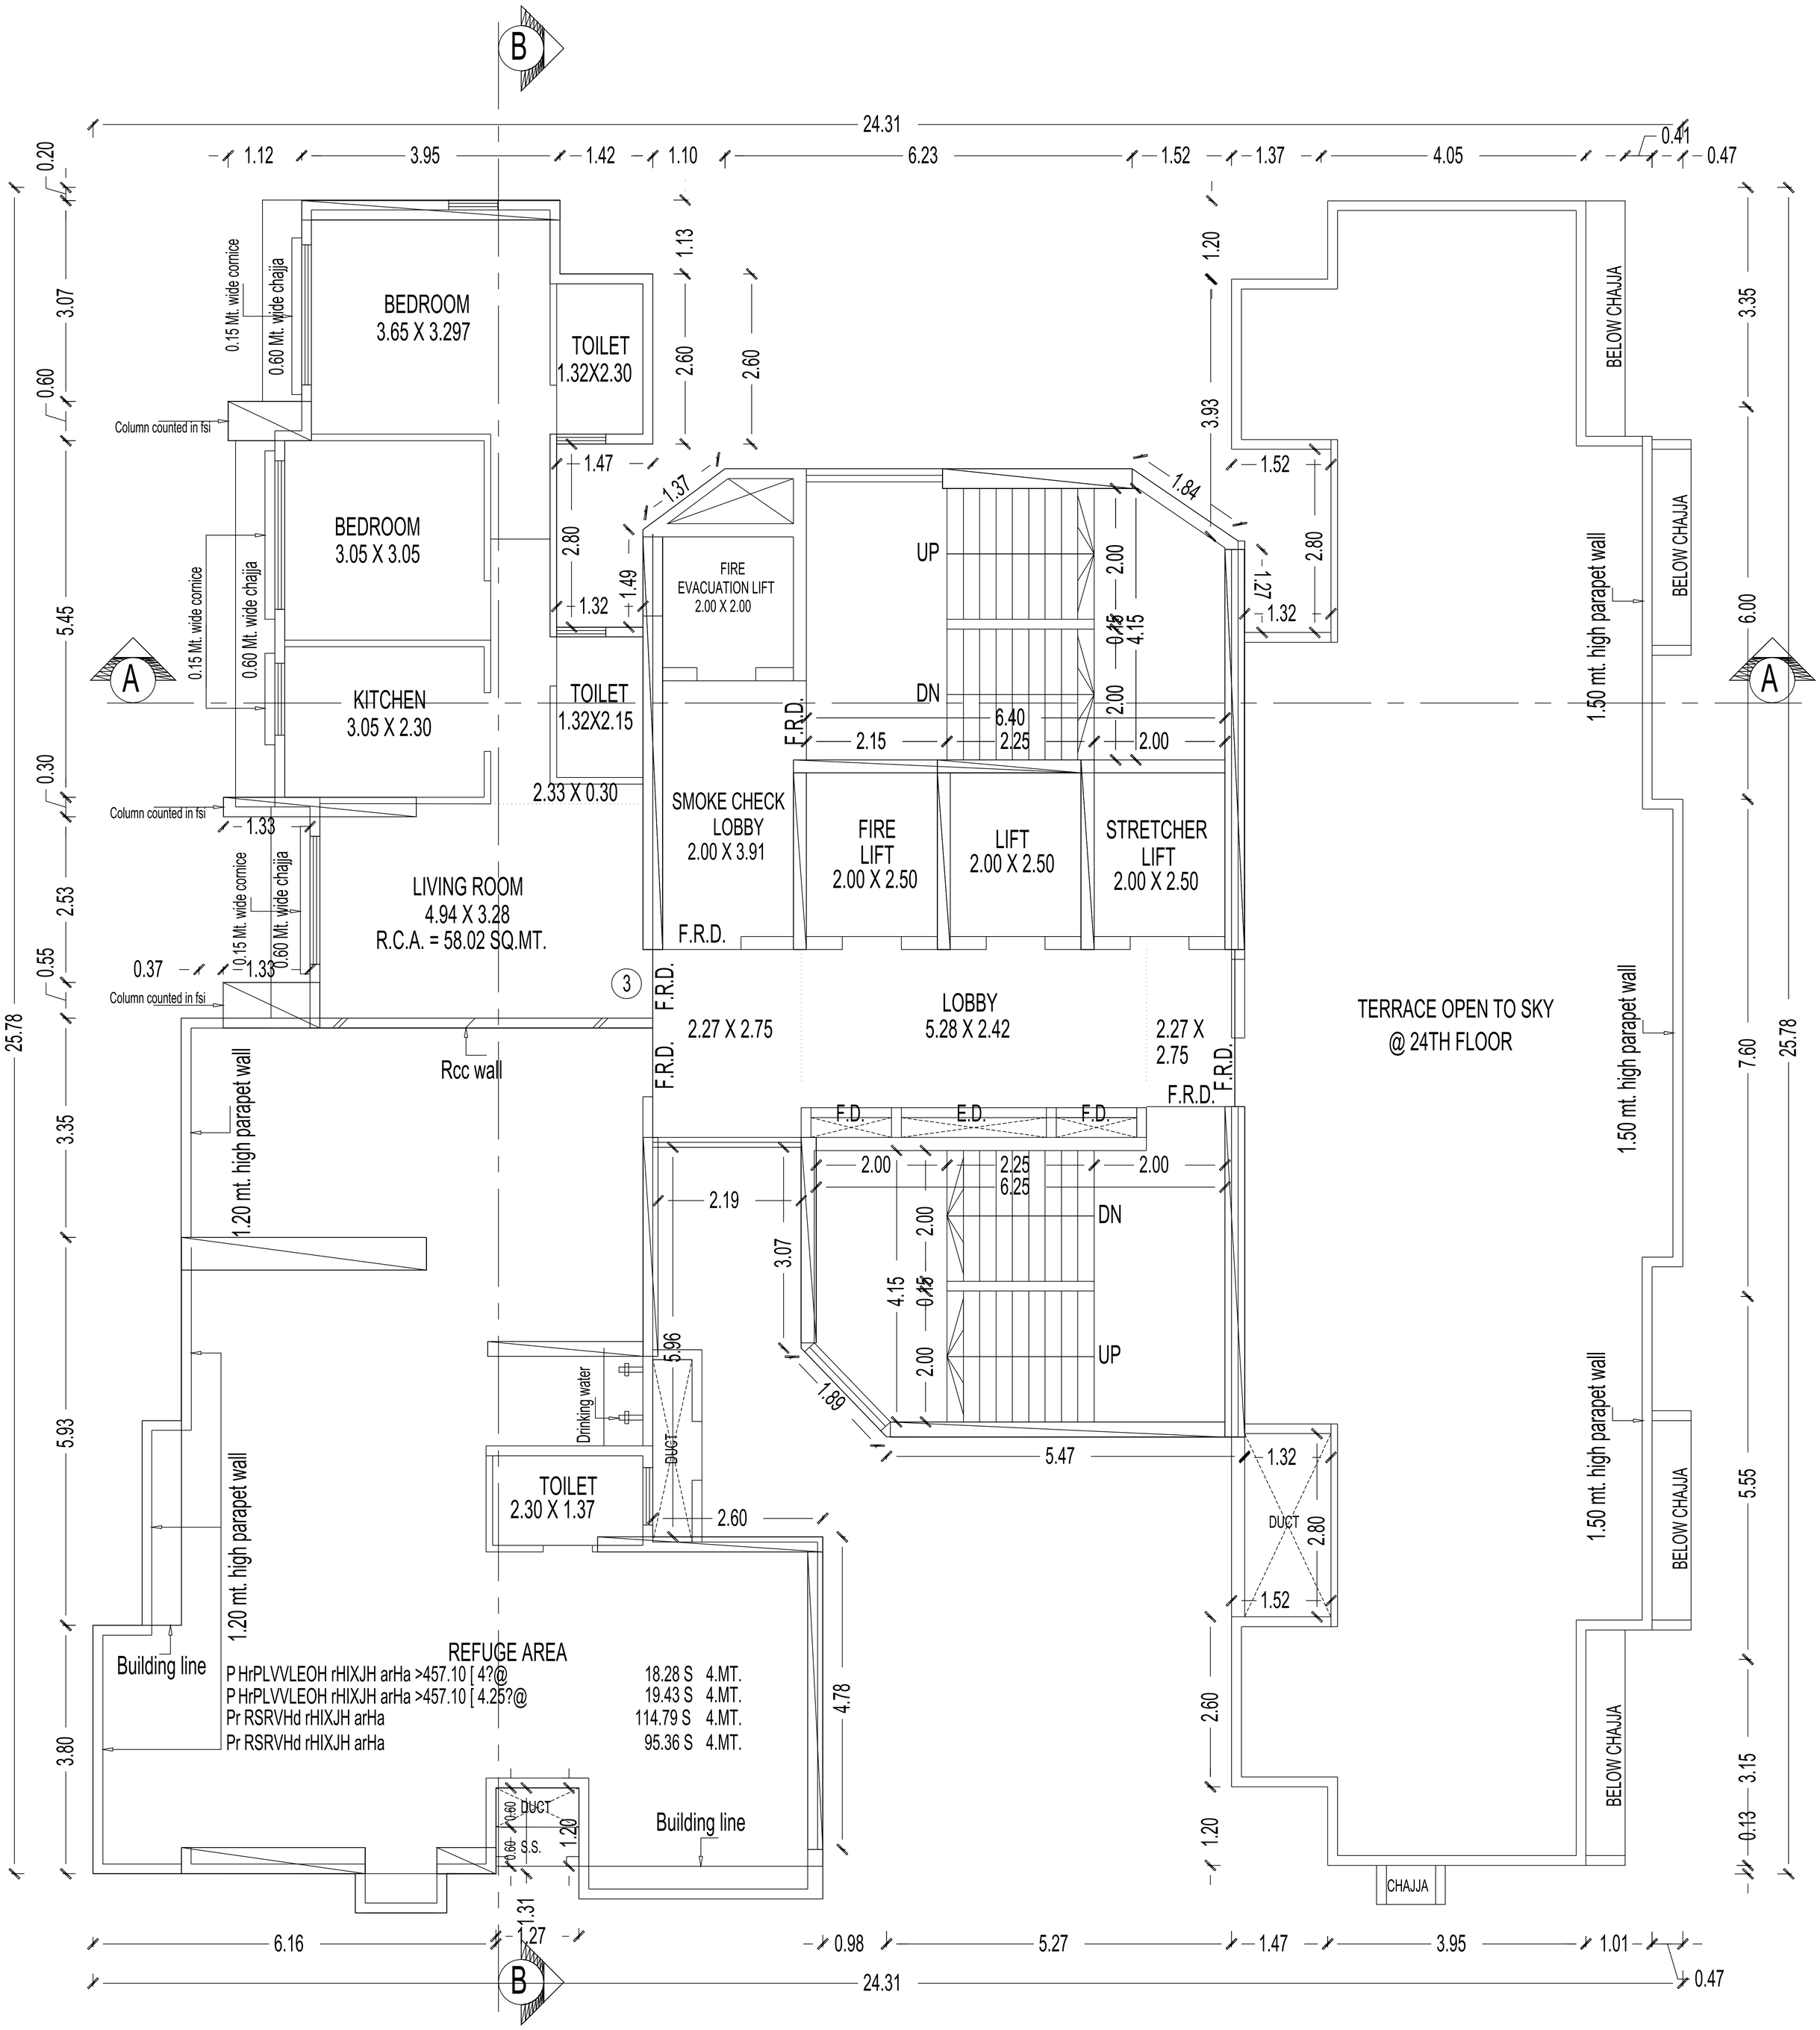


24TH (REFUGE) FLOOR PLAN

SCALE :- 1:100 WING - B

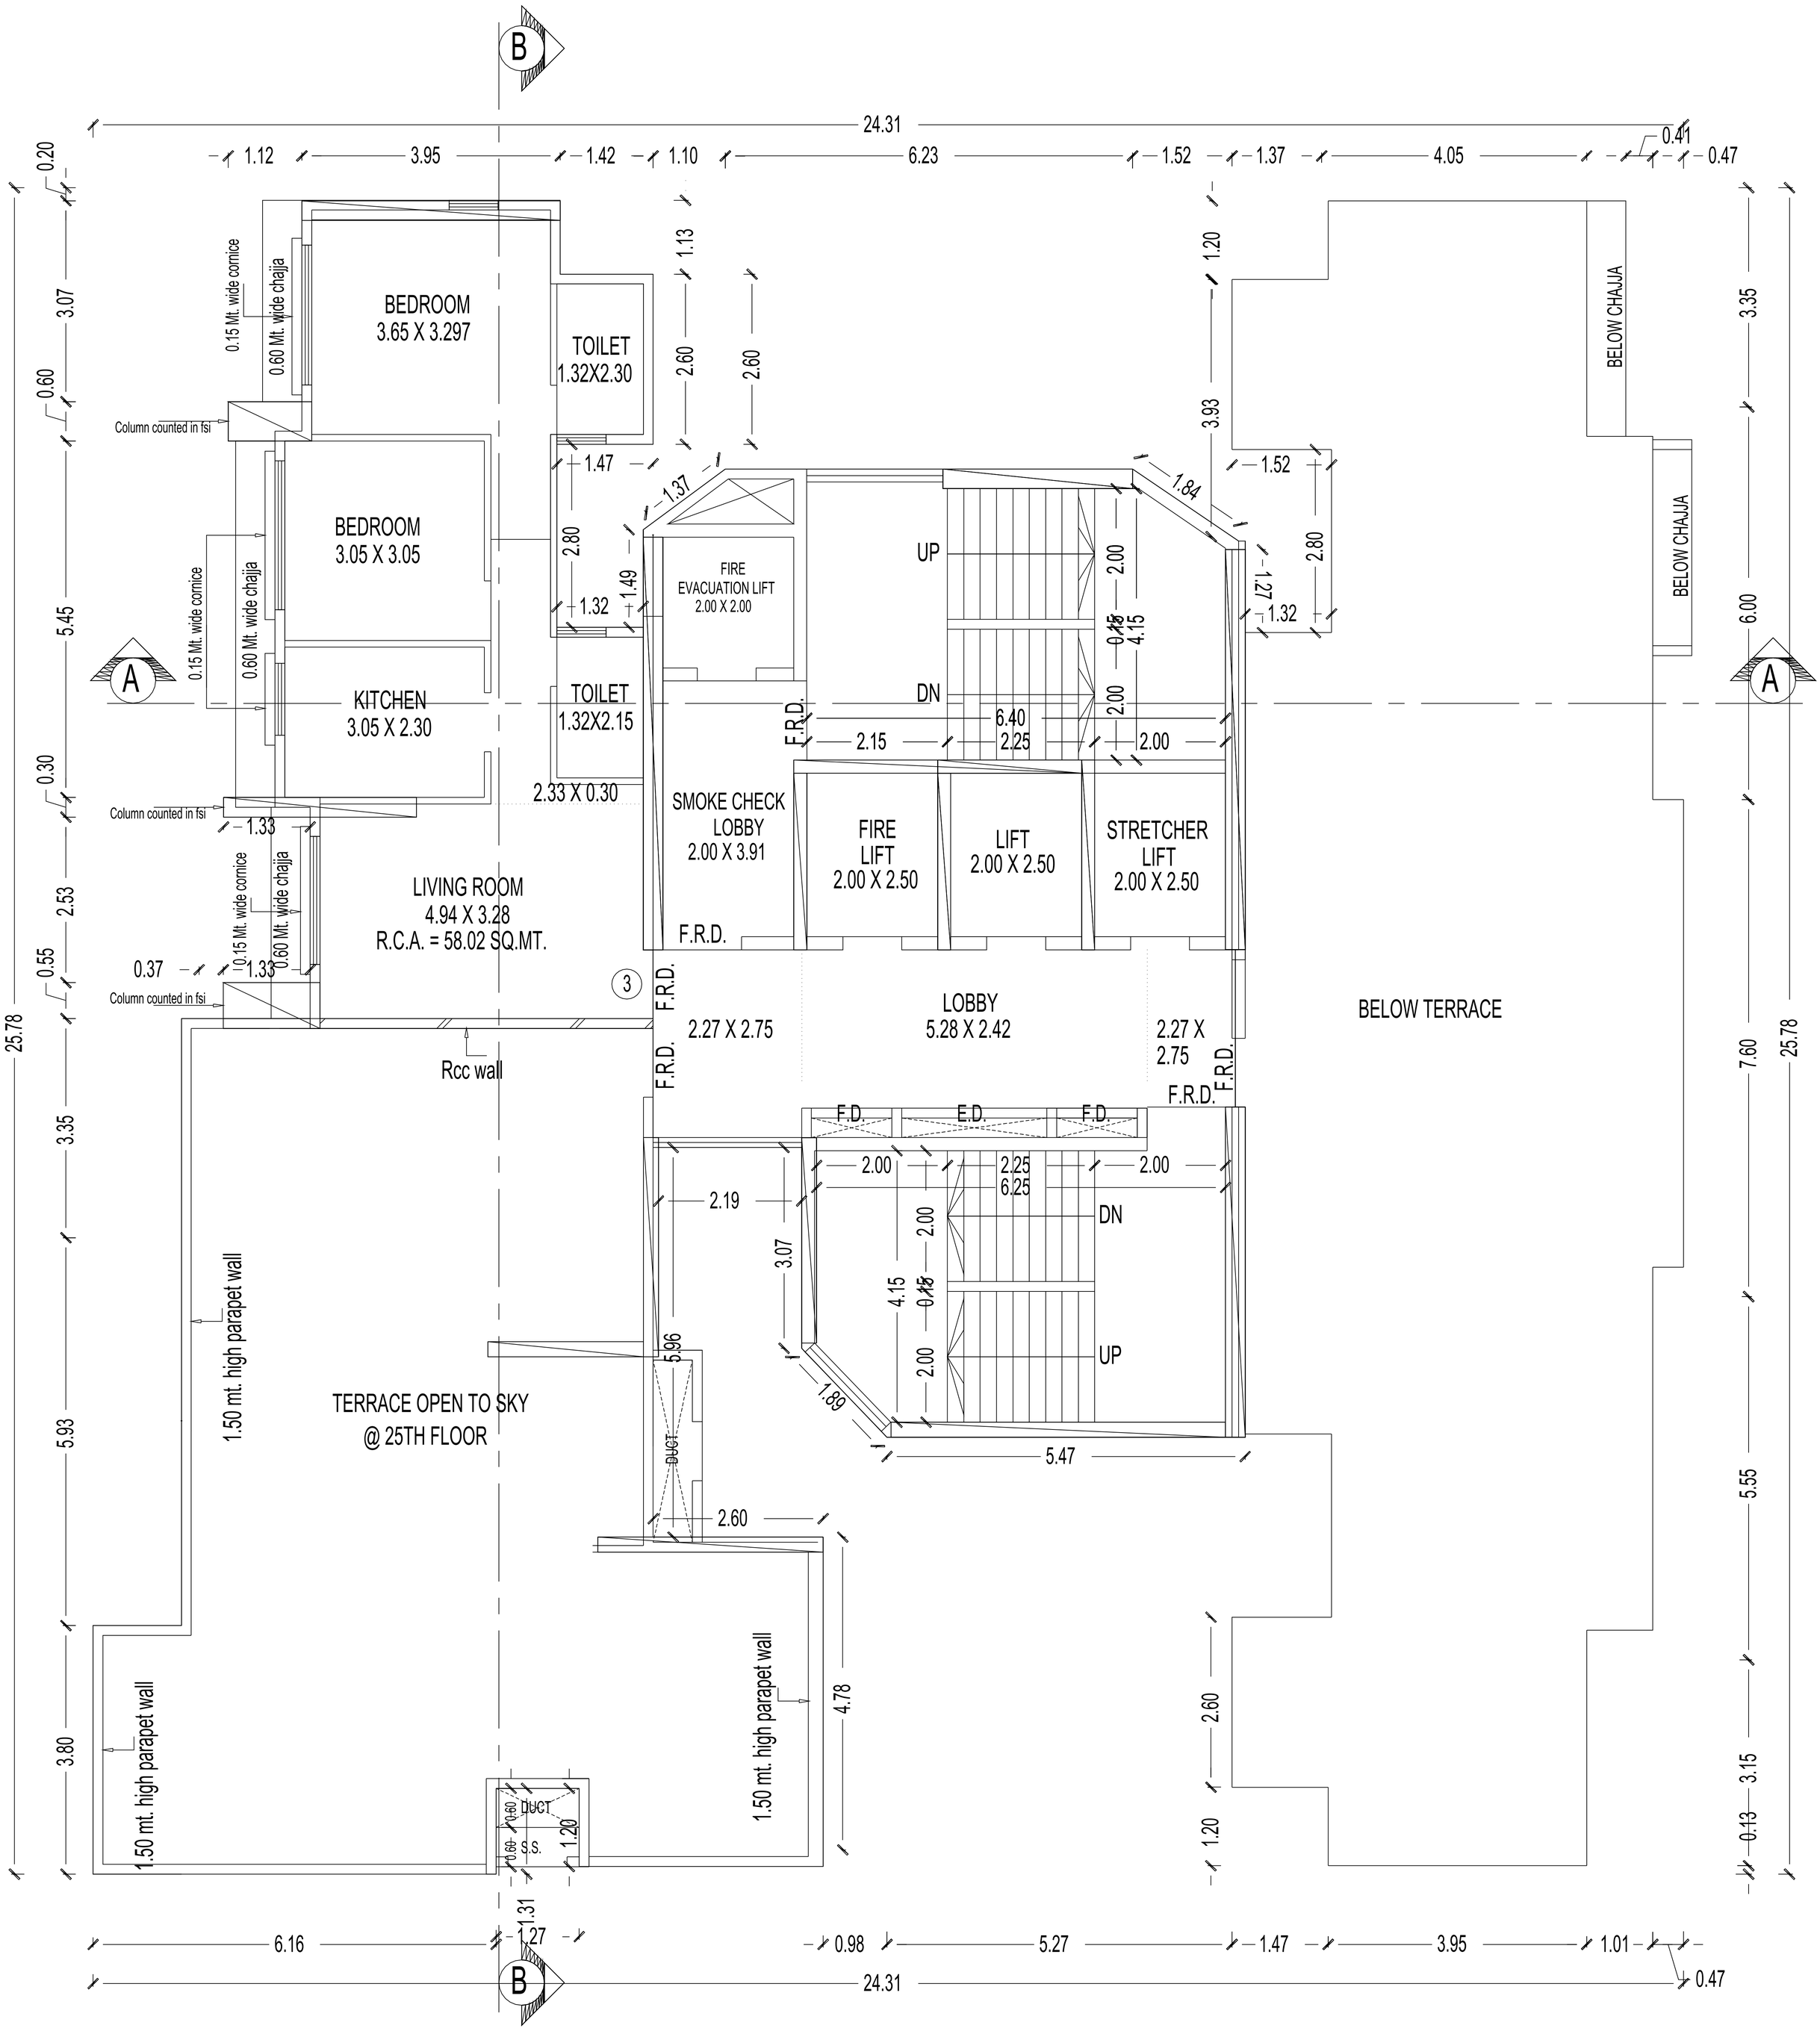

25TH FLOOR PLAN


SCALE :- 1:100 WING - B

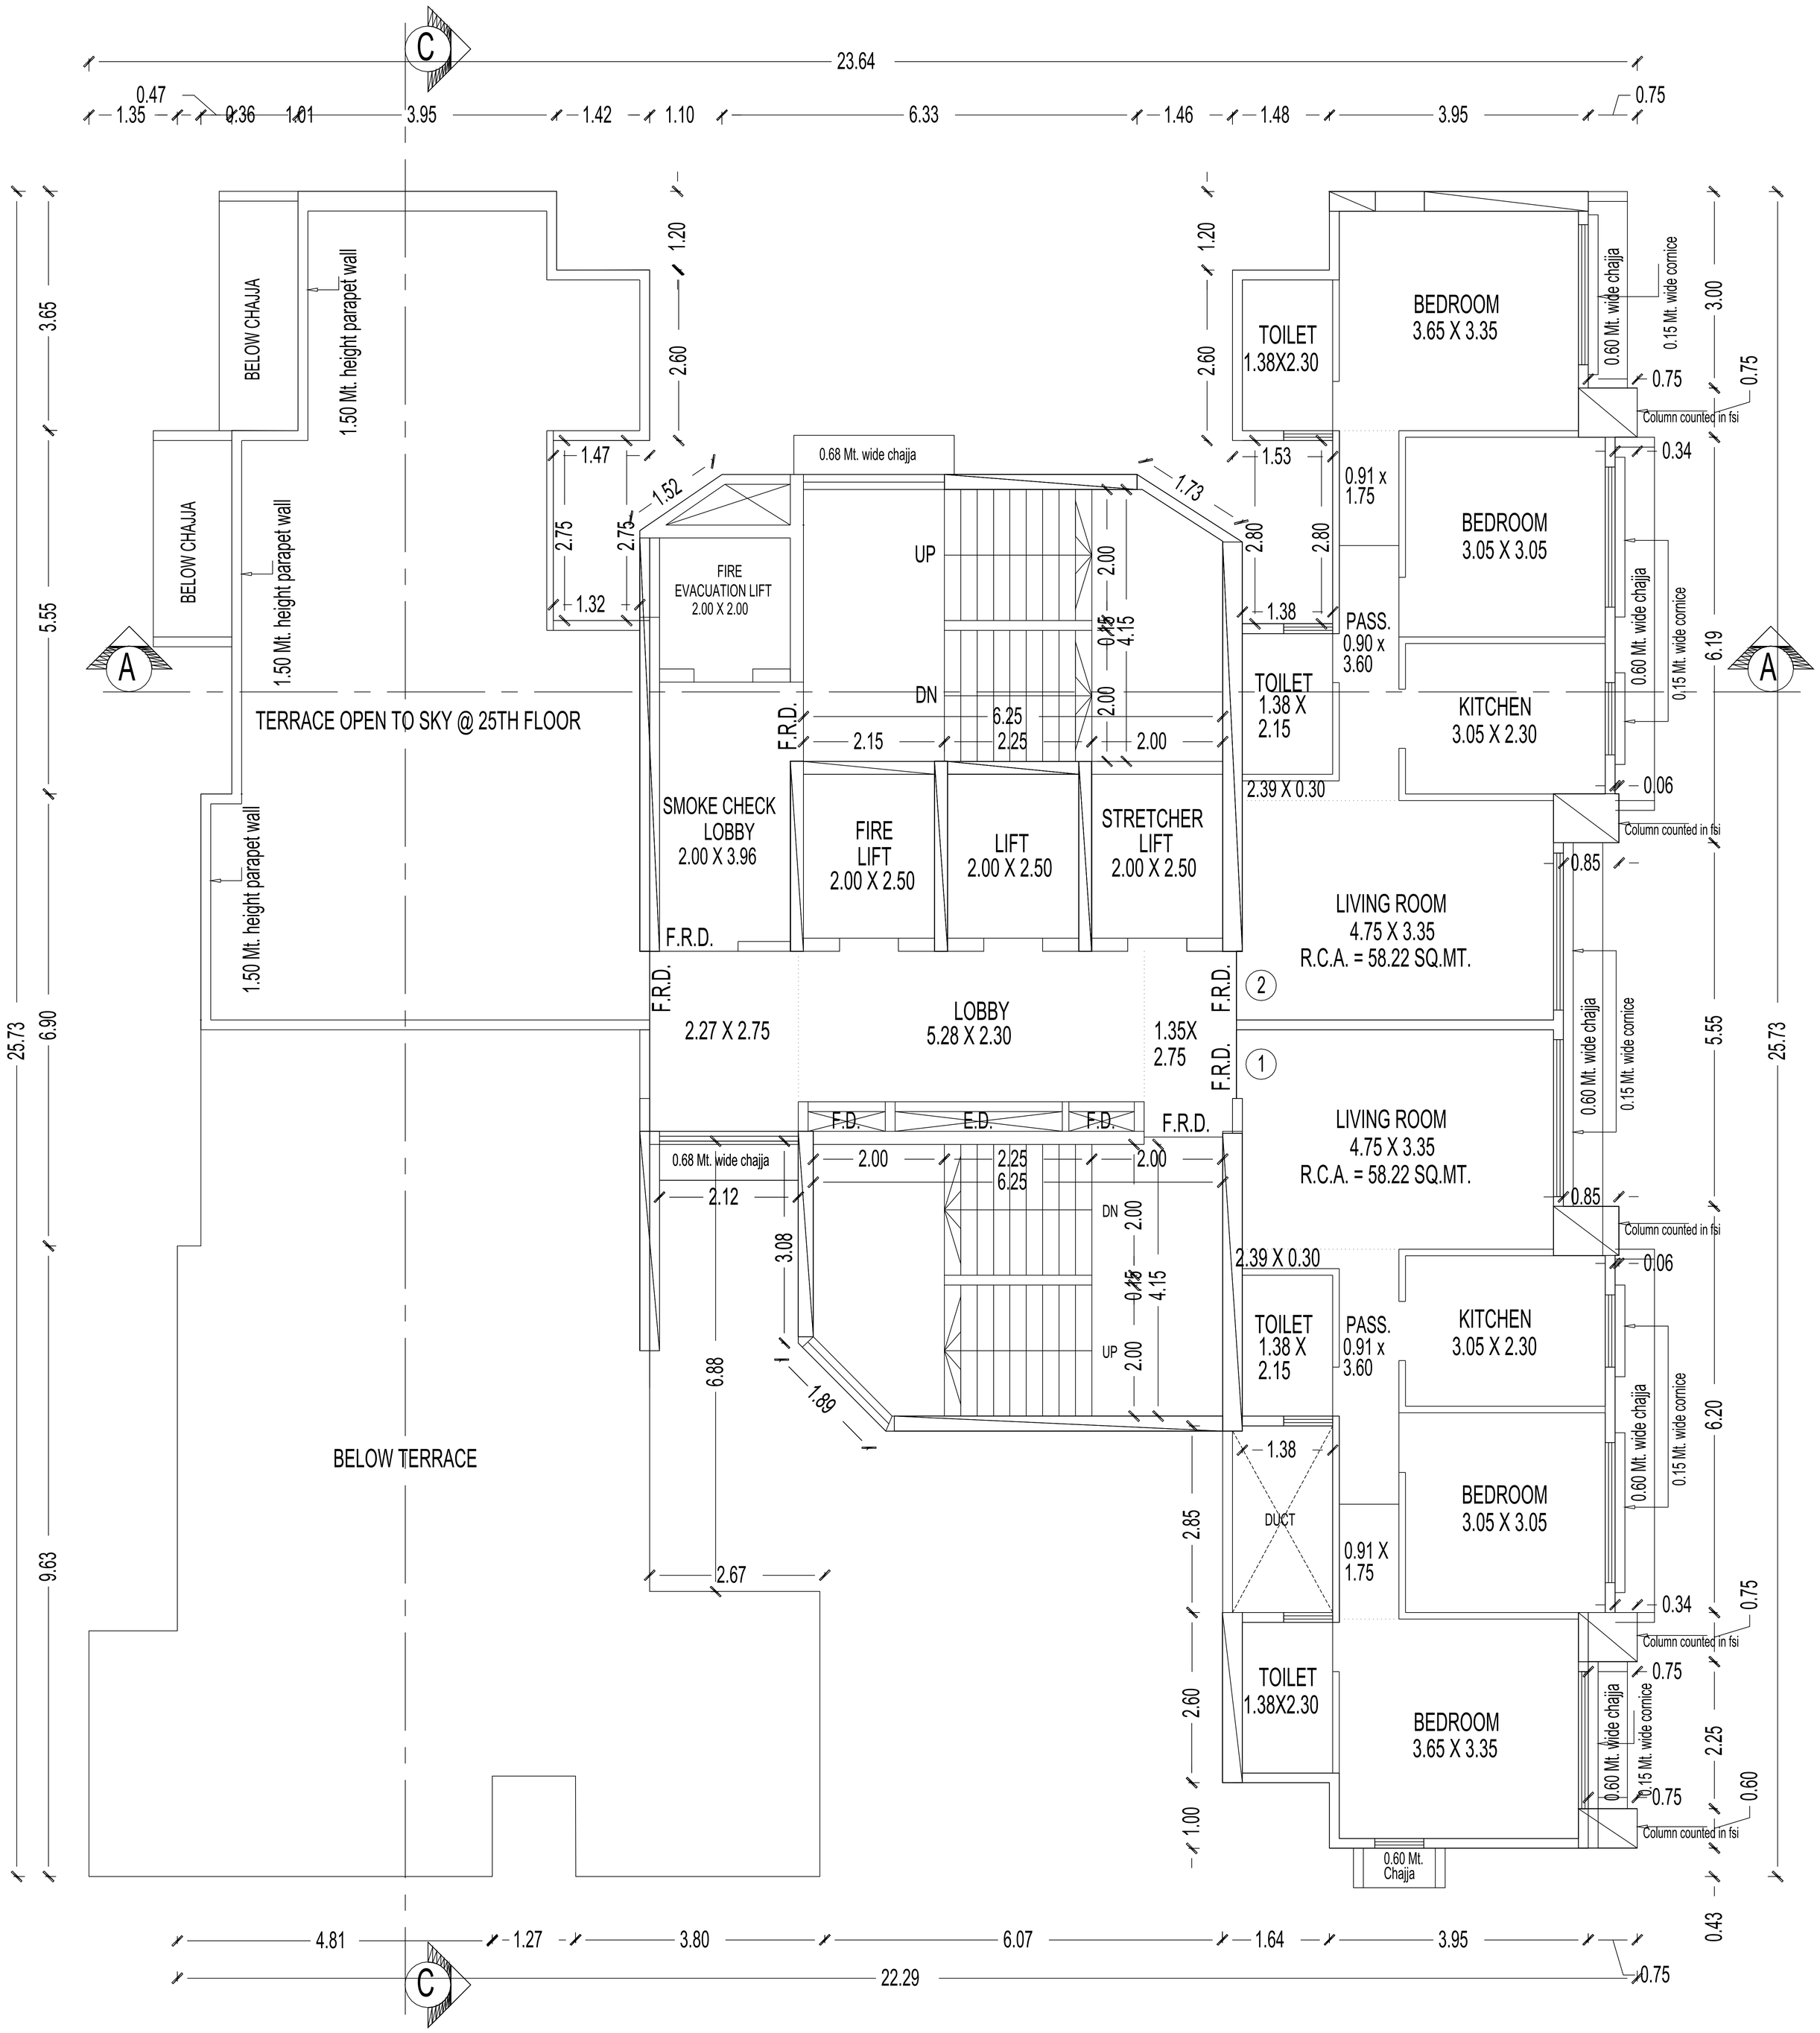

25TH FLOOR PLAN


SCALE :- 1:100 WING - A

NORTH

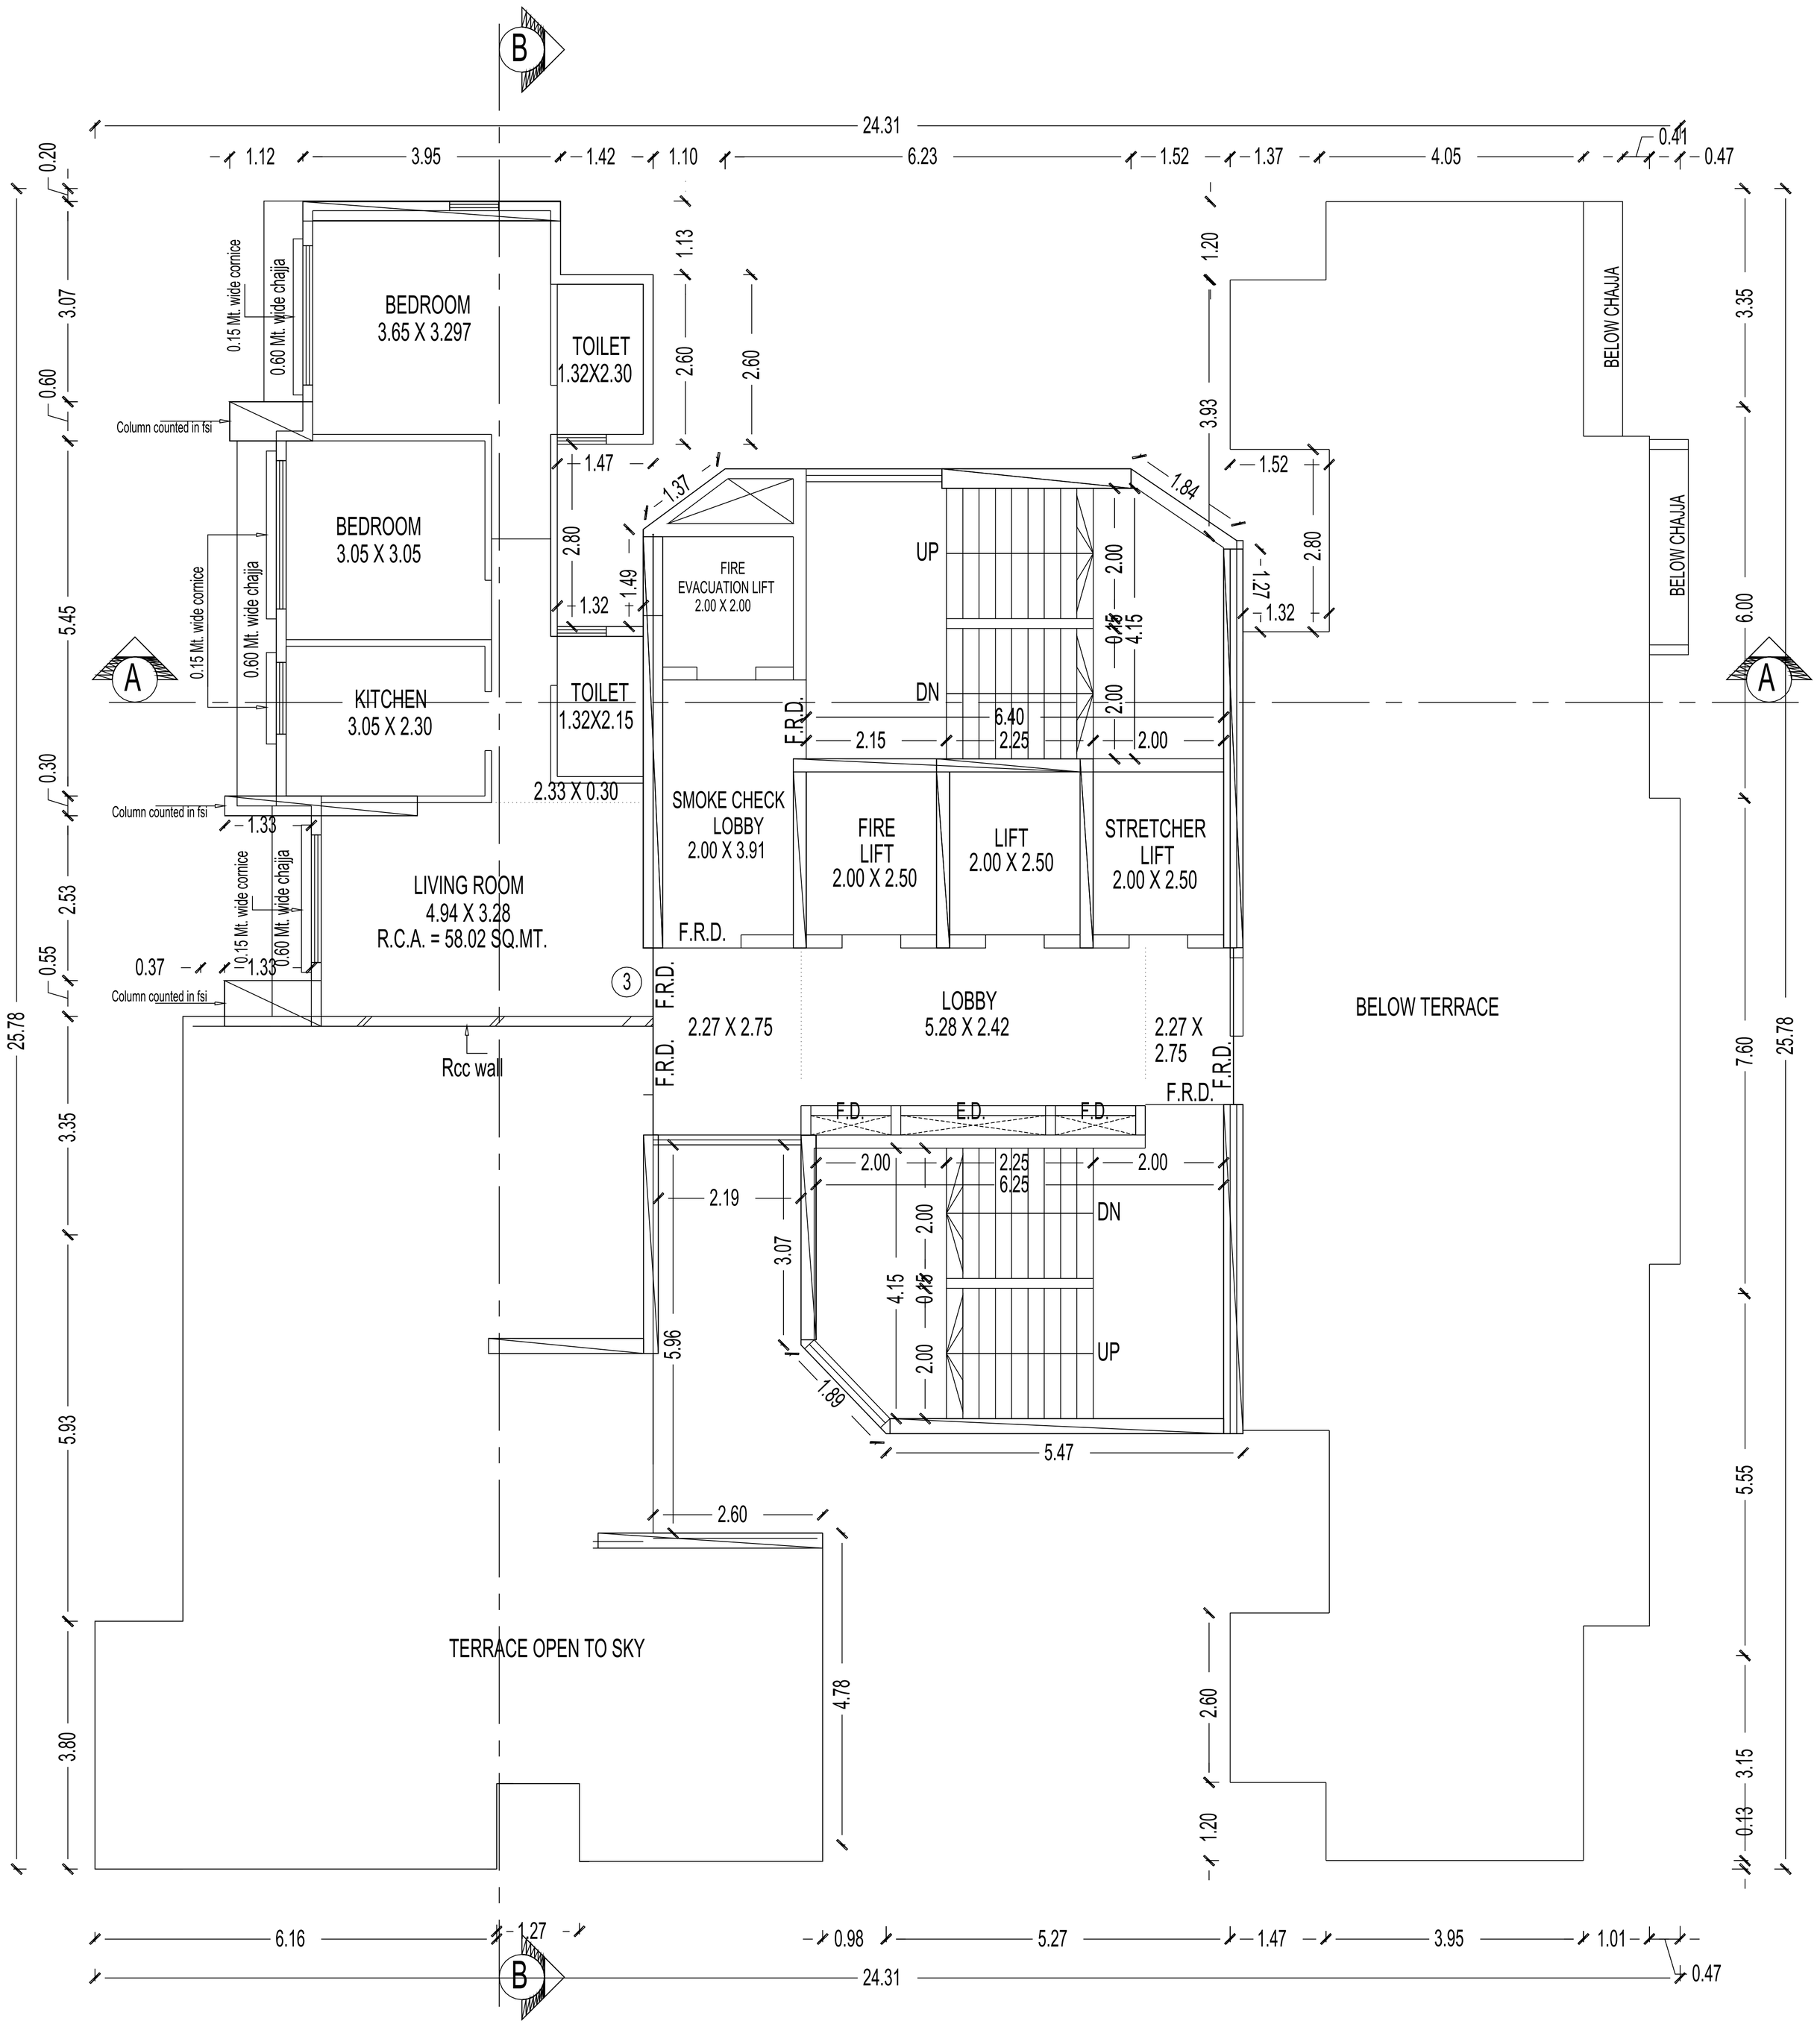

26TH & 27TH FLOOR PLAN

SCALE :- 1:100 WING - B

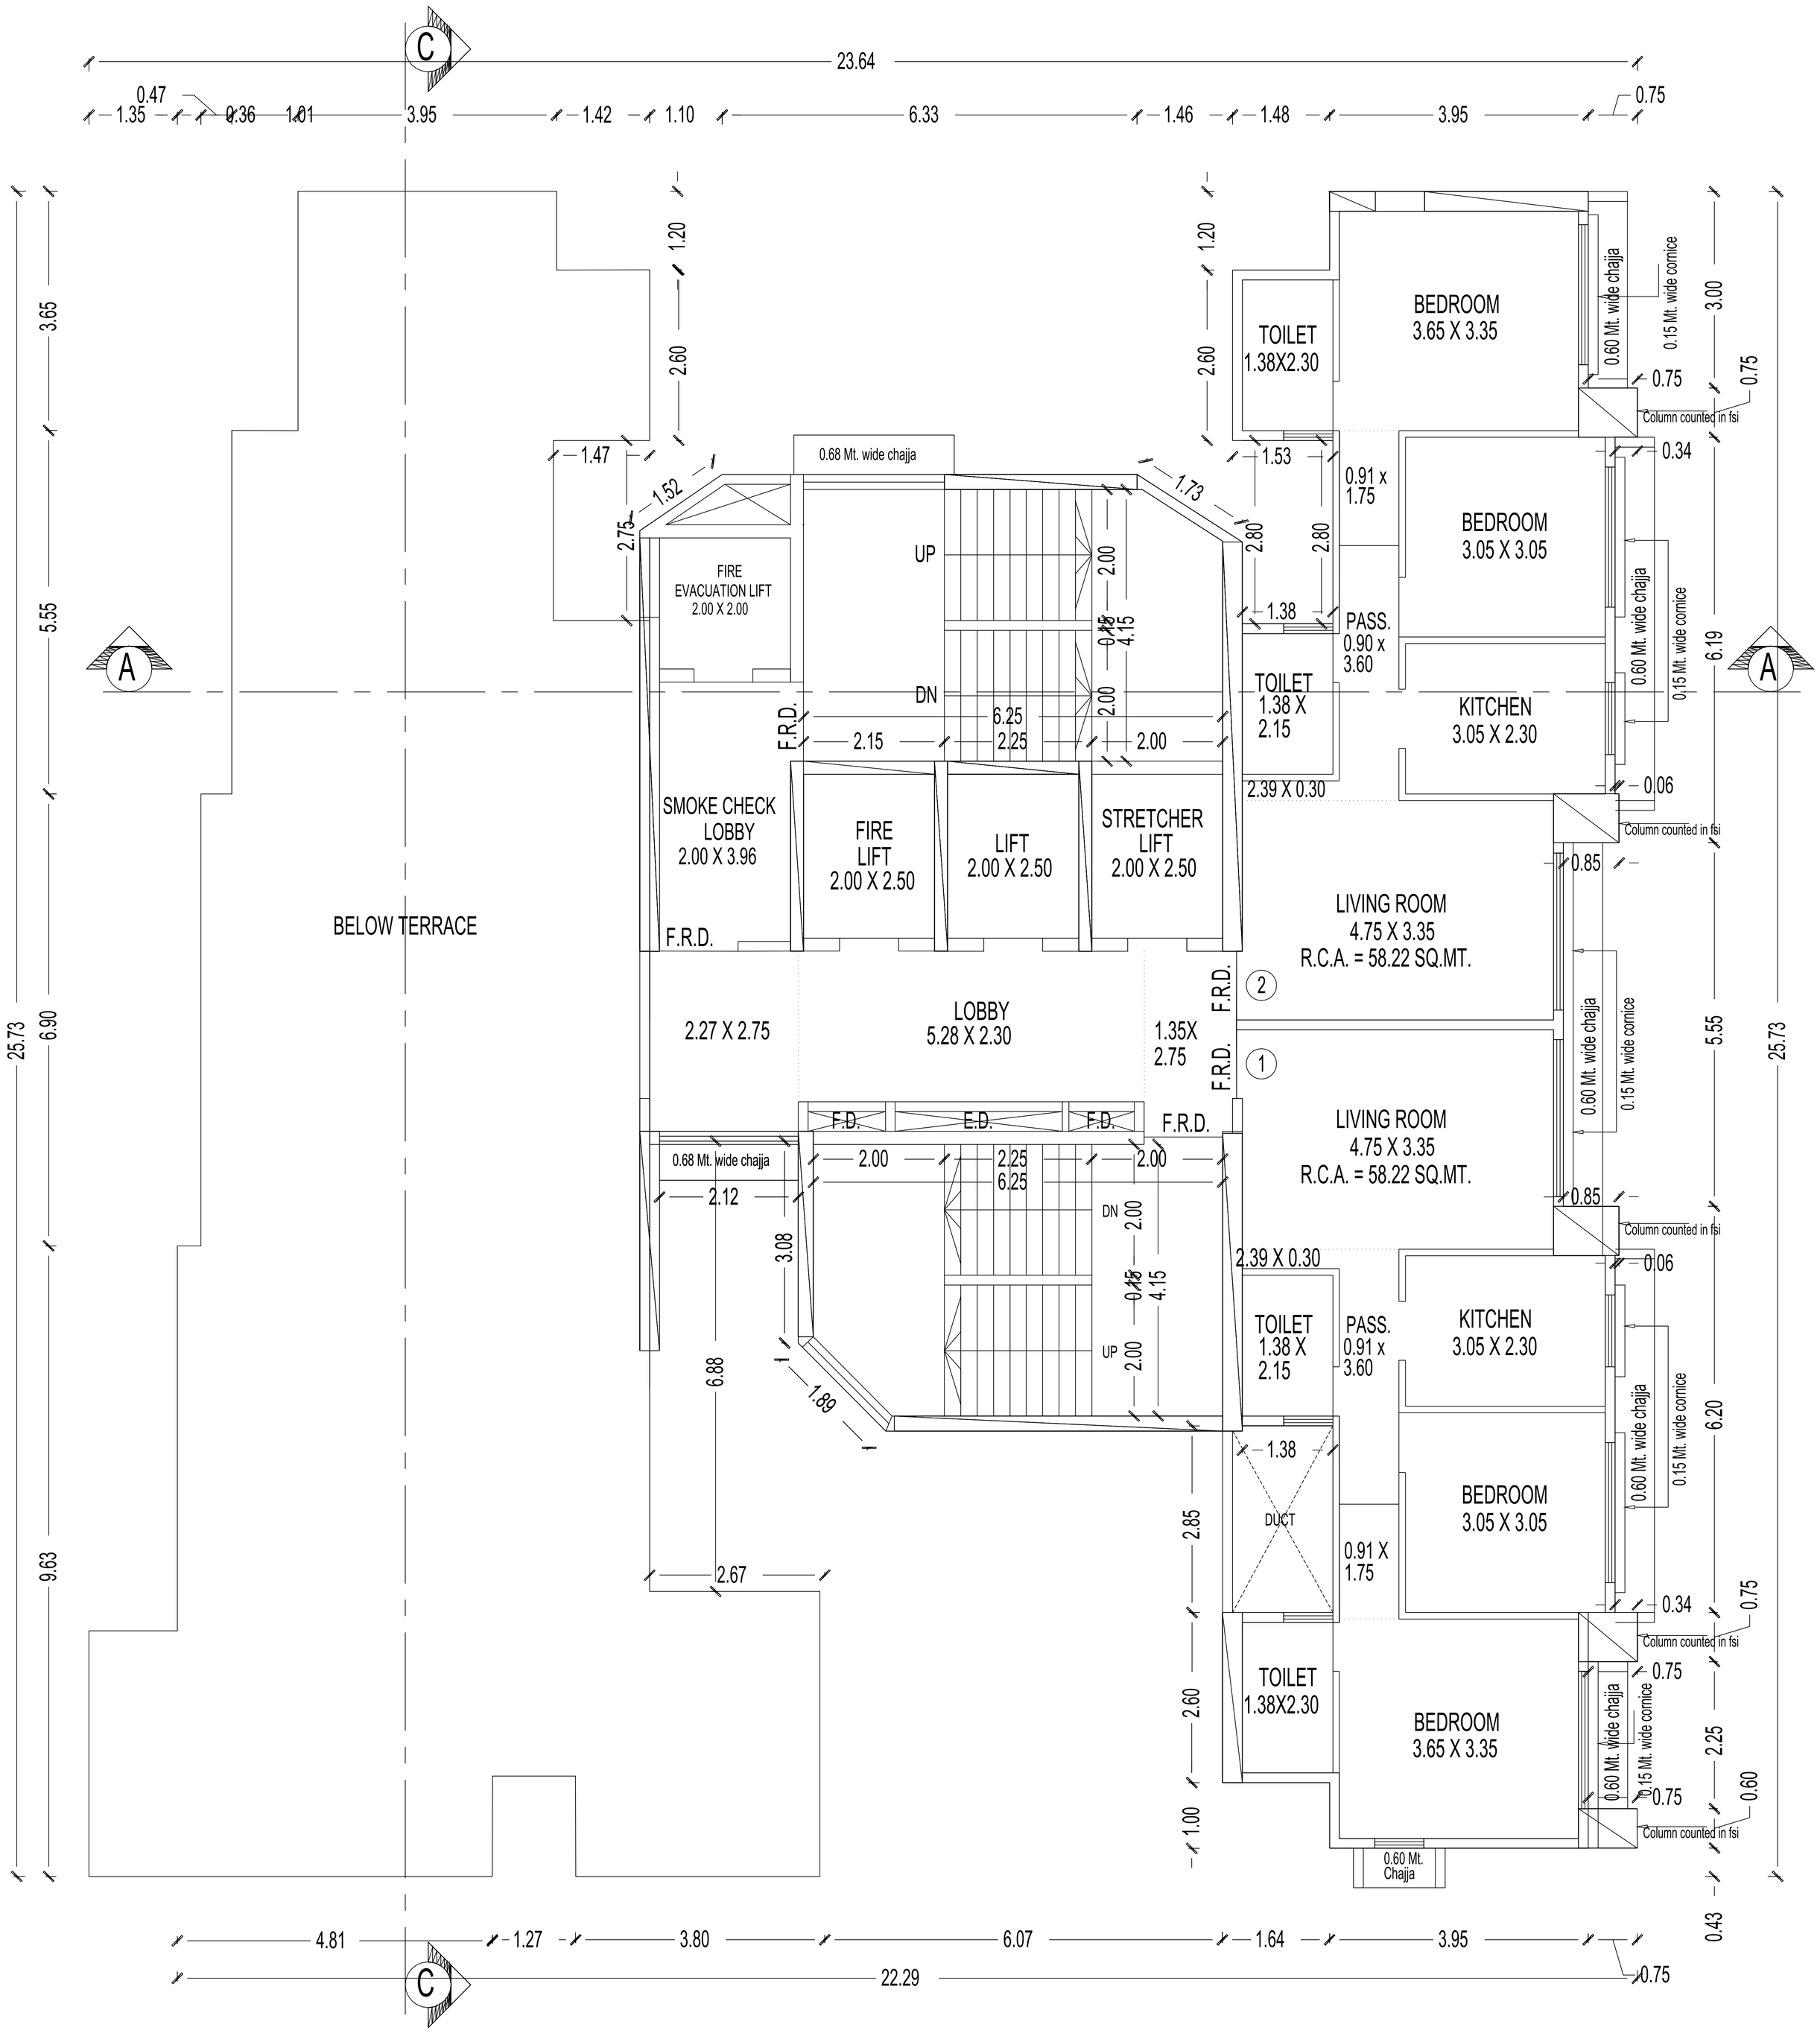

26TH TO 28TH FLOOR PLAN

SCALE :- 1:100

WING - A

BEDROOM
3.65 X 3.297

BEDROOM
3.05 X 3.05

KITCHEN
3.05 X 2.30

LIVING ROOM
4.94 X 3.28
R.C.A. = 58.02 SQ.MT.

TOILET
1.32X2.30

TOILET
1.32X2.15

FIRE
EVACUATION LIFT
2.00 X 2.00

SMOKE CHECK
LOBBY
2.00 X 3.91

FIRE
LIFT
2.00 X 2.50

LIFT
2.00 X 2.50

STRETCHER
LIFT
2.00 X 2.50

LOBBY
5.28 X 2.42

2.27 X 2.75

2.27 X
2.75

UP

DN

UP

DN

F.R.D.

F.D.

E.D.

F.D.

BELOW CHAJJA

BELOW CHAJJA

BELOW TERRACE

BELOW TERRACE

Rcc wall

Column counted in fsi

0.15 Mt. wide cornice

0.60 Mt. wide chajja

DUCT

S.S.

28TH TO 30TH FLOOR PLAN


SCALE :- 1:100

WING - B

SHEET NO. 08 /17

FILE NO- P-20375/2024/(1007)/P/S Ward/PAHADI GOREGAON-W

NORTH

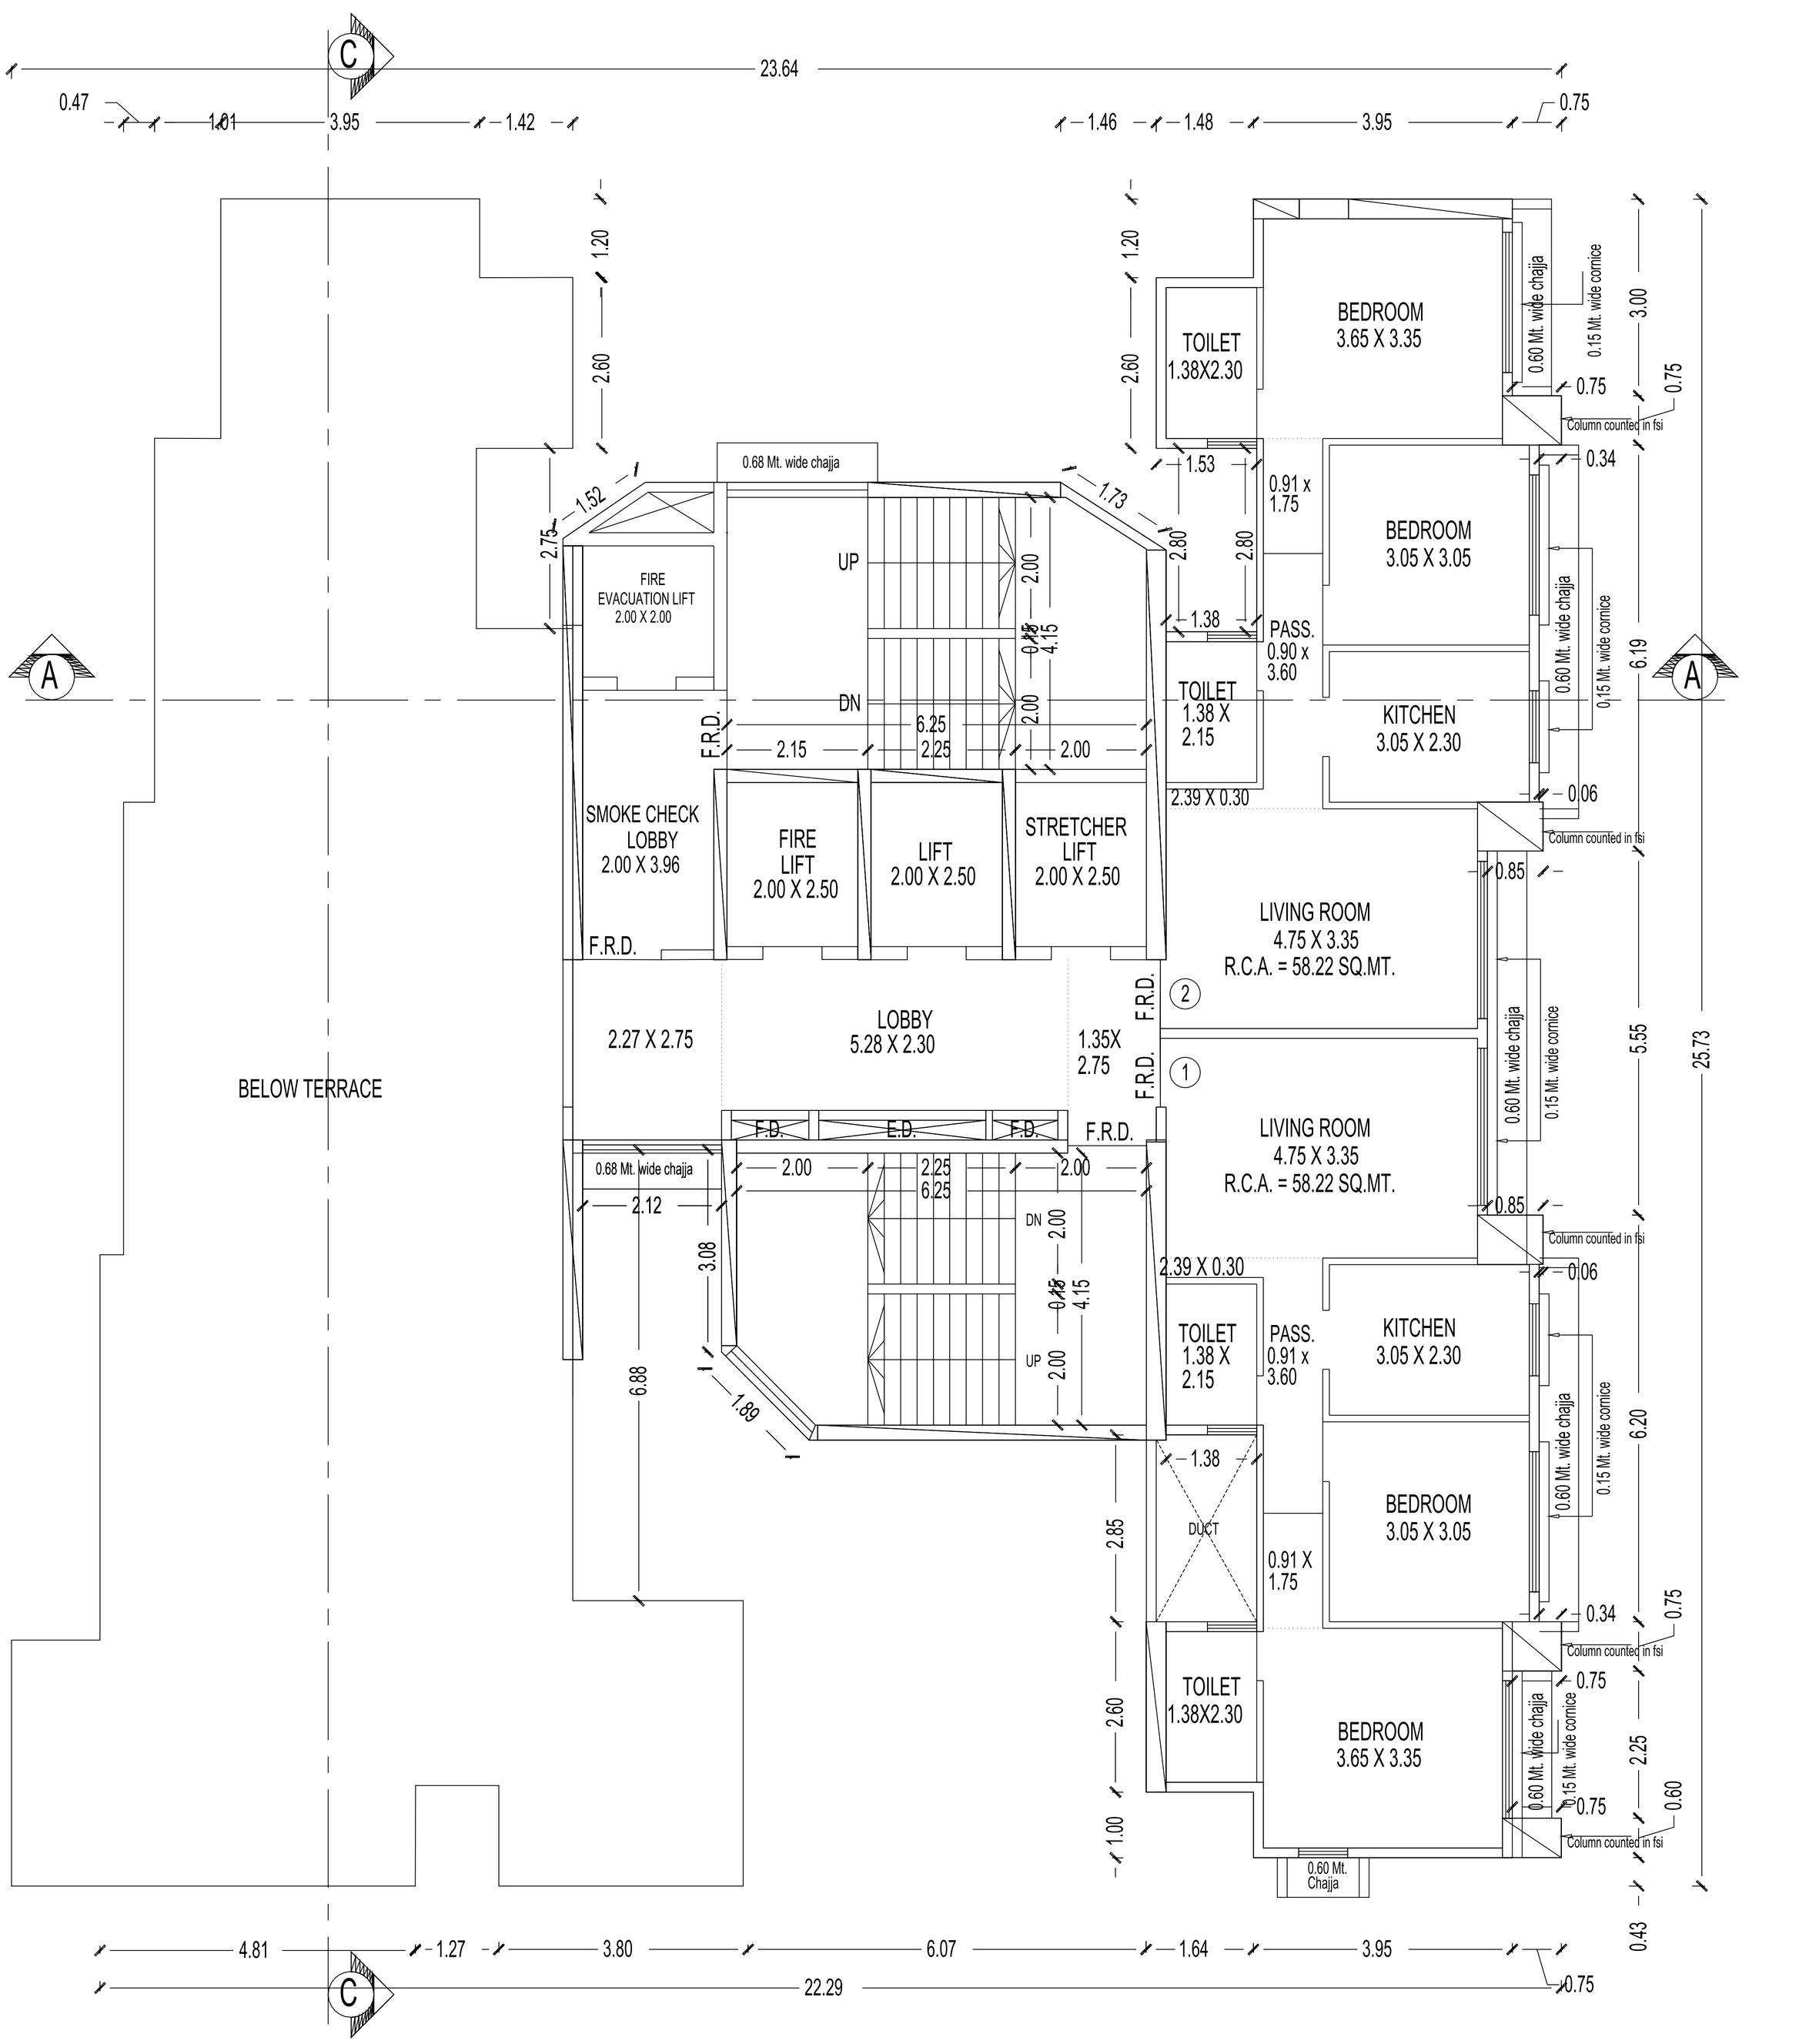

29TH & 30TH FLOOR PLAN

SCALE :- 1:100

WING - A