

SCALE - 1:100

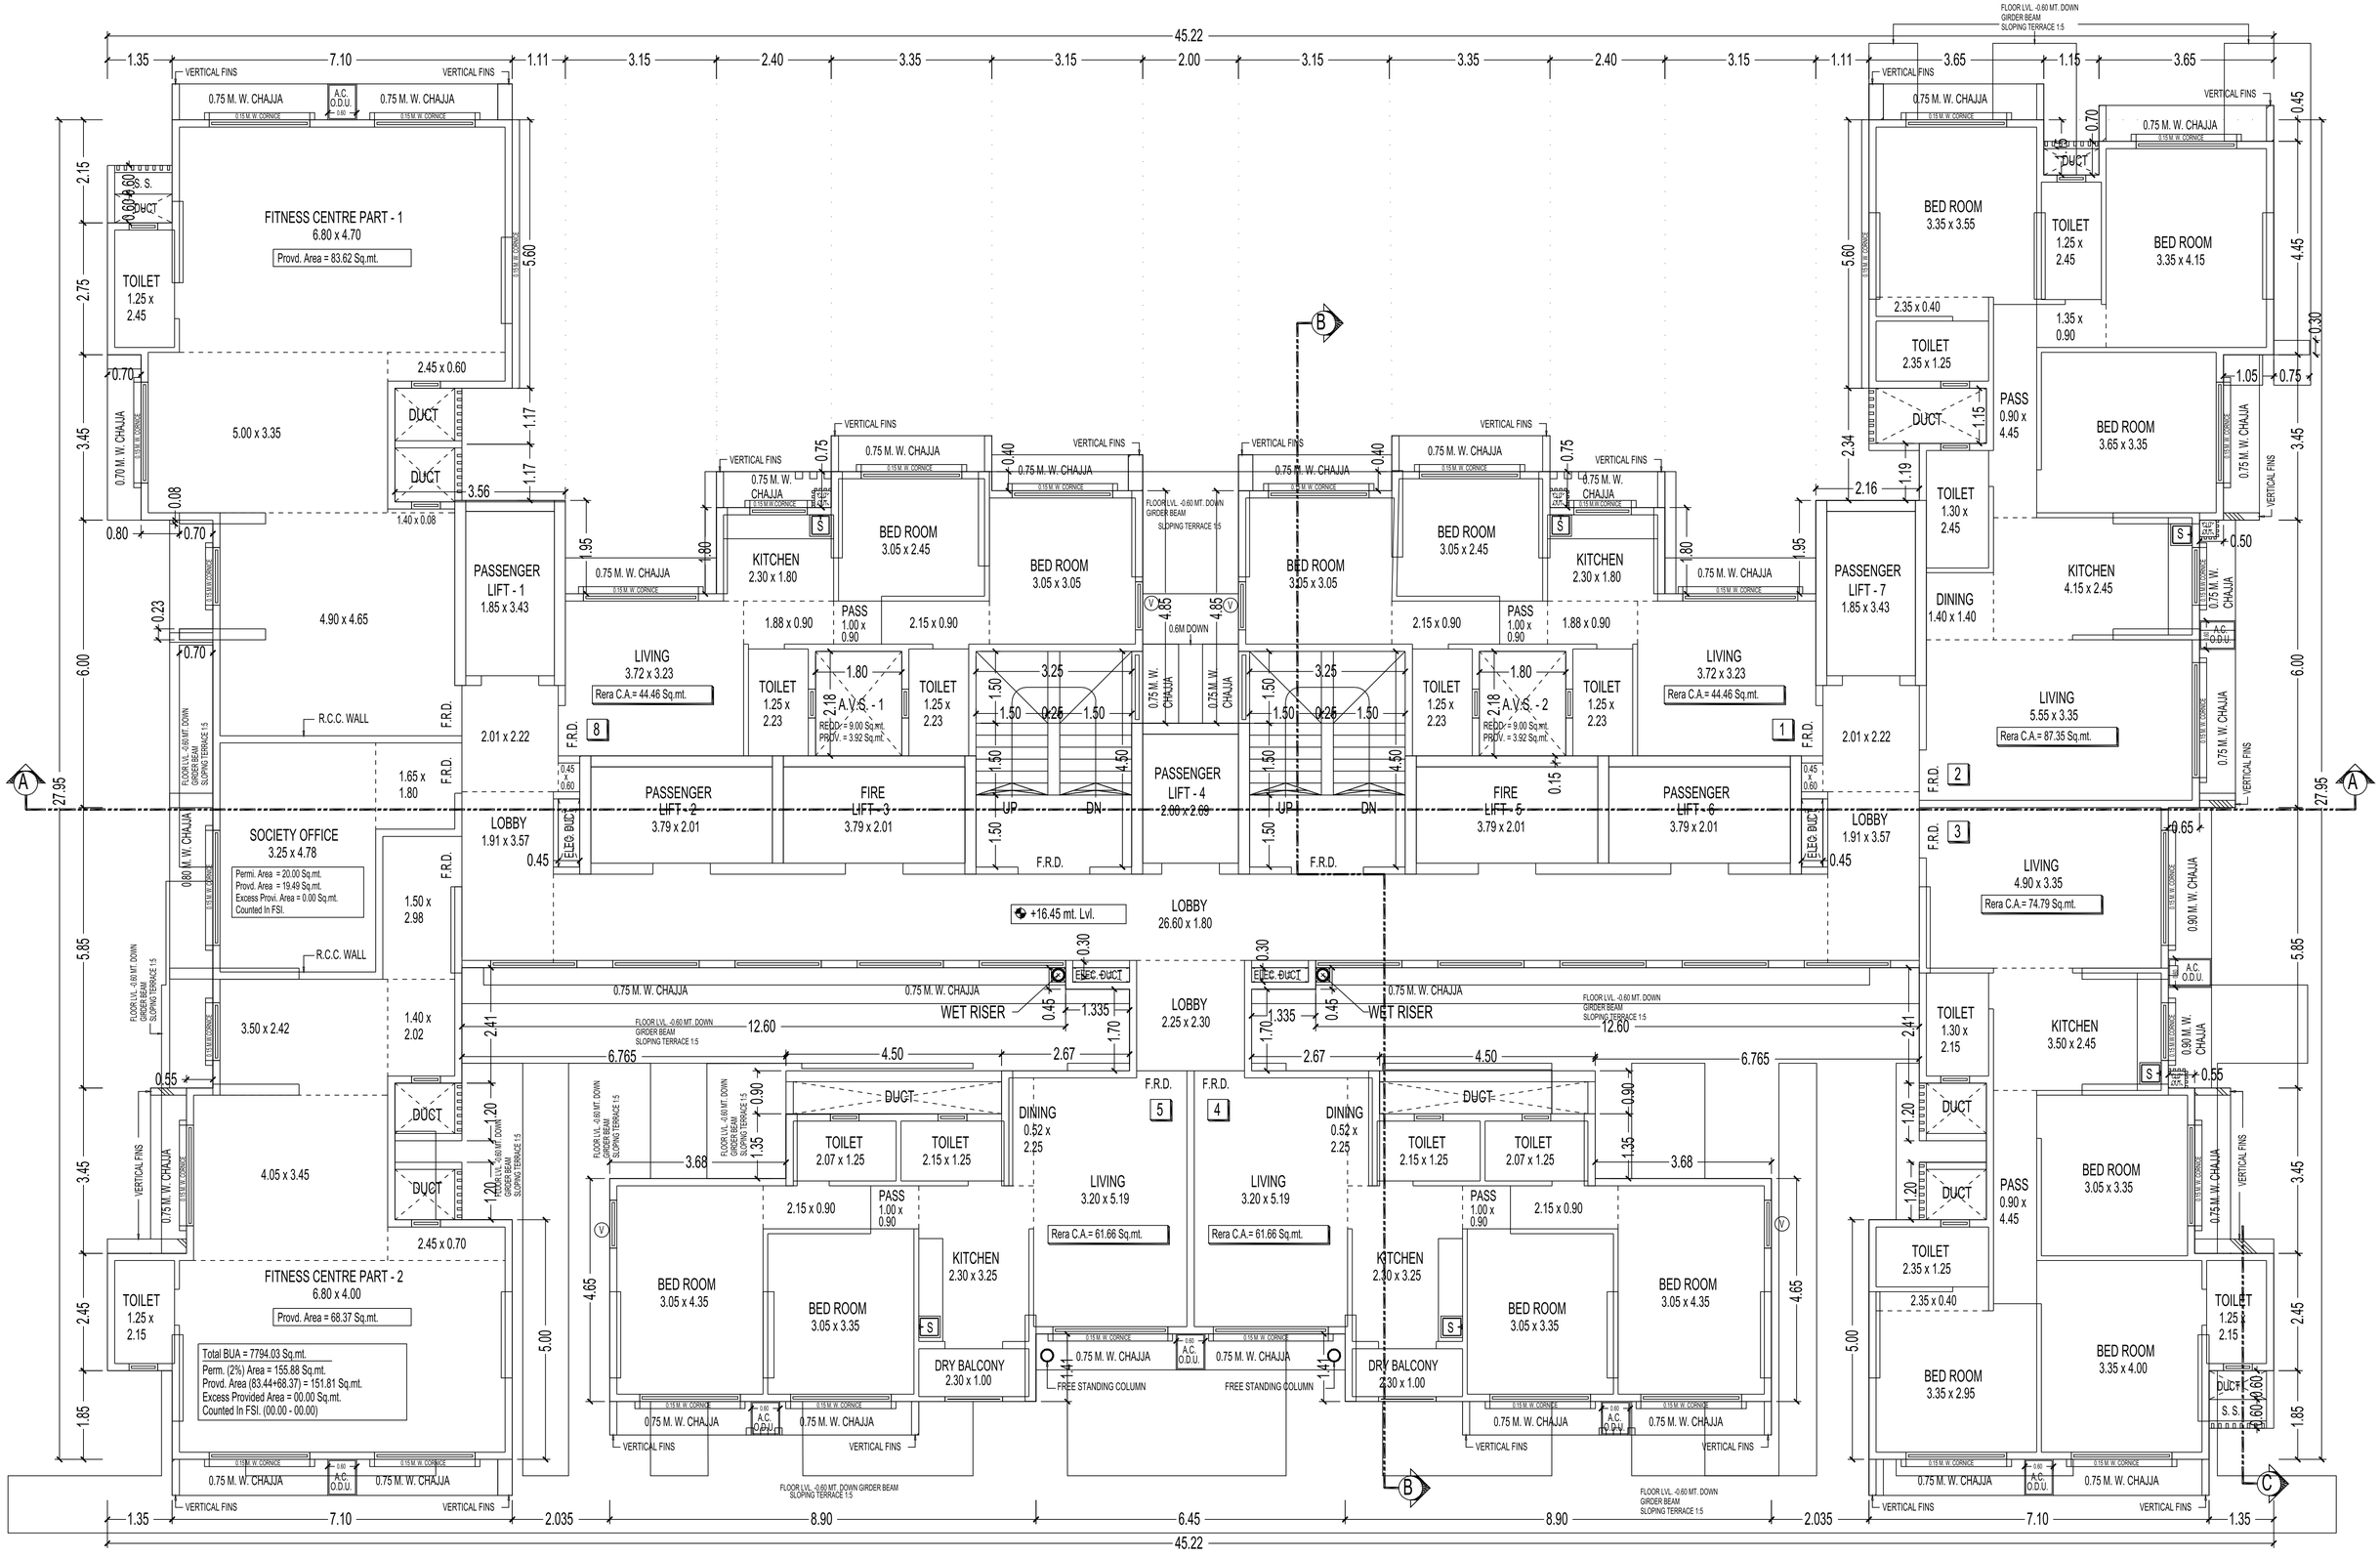

4TH FLOOR PLAN

SCALE - 1:100

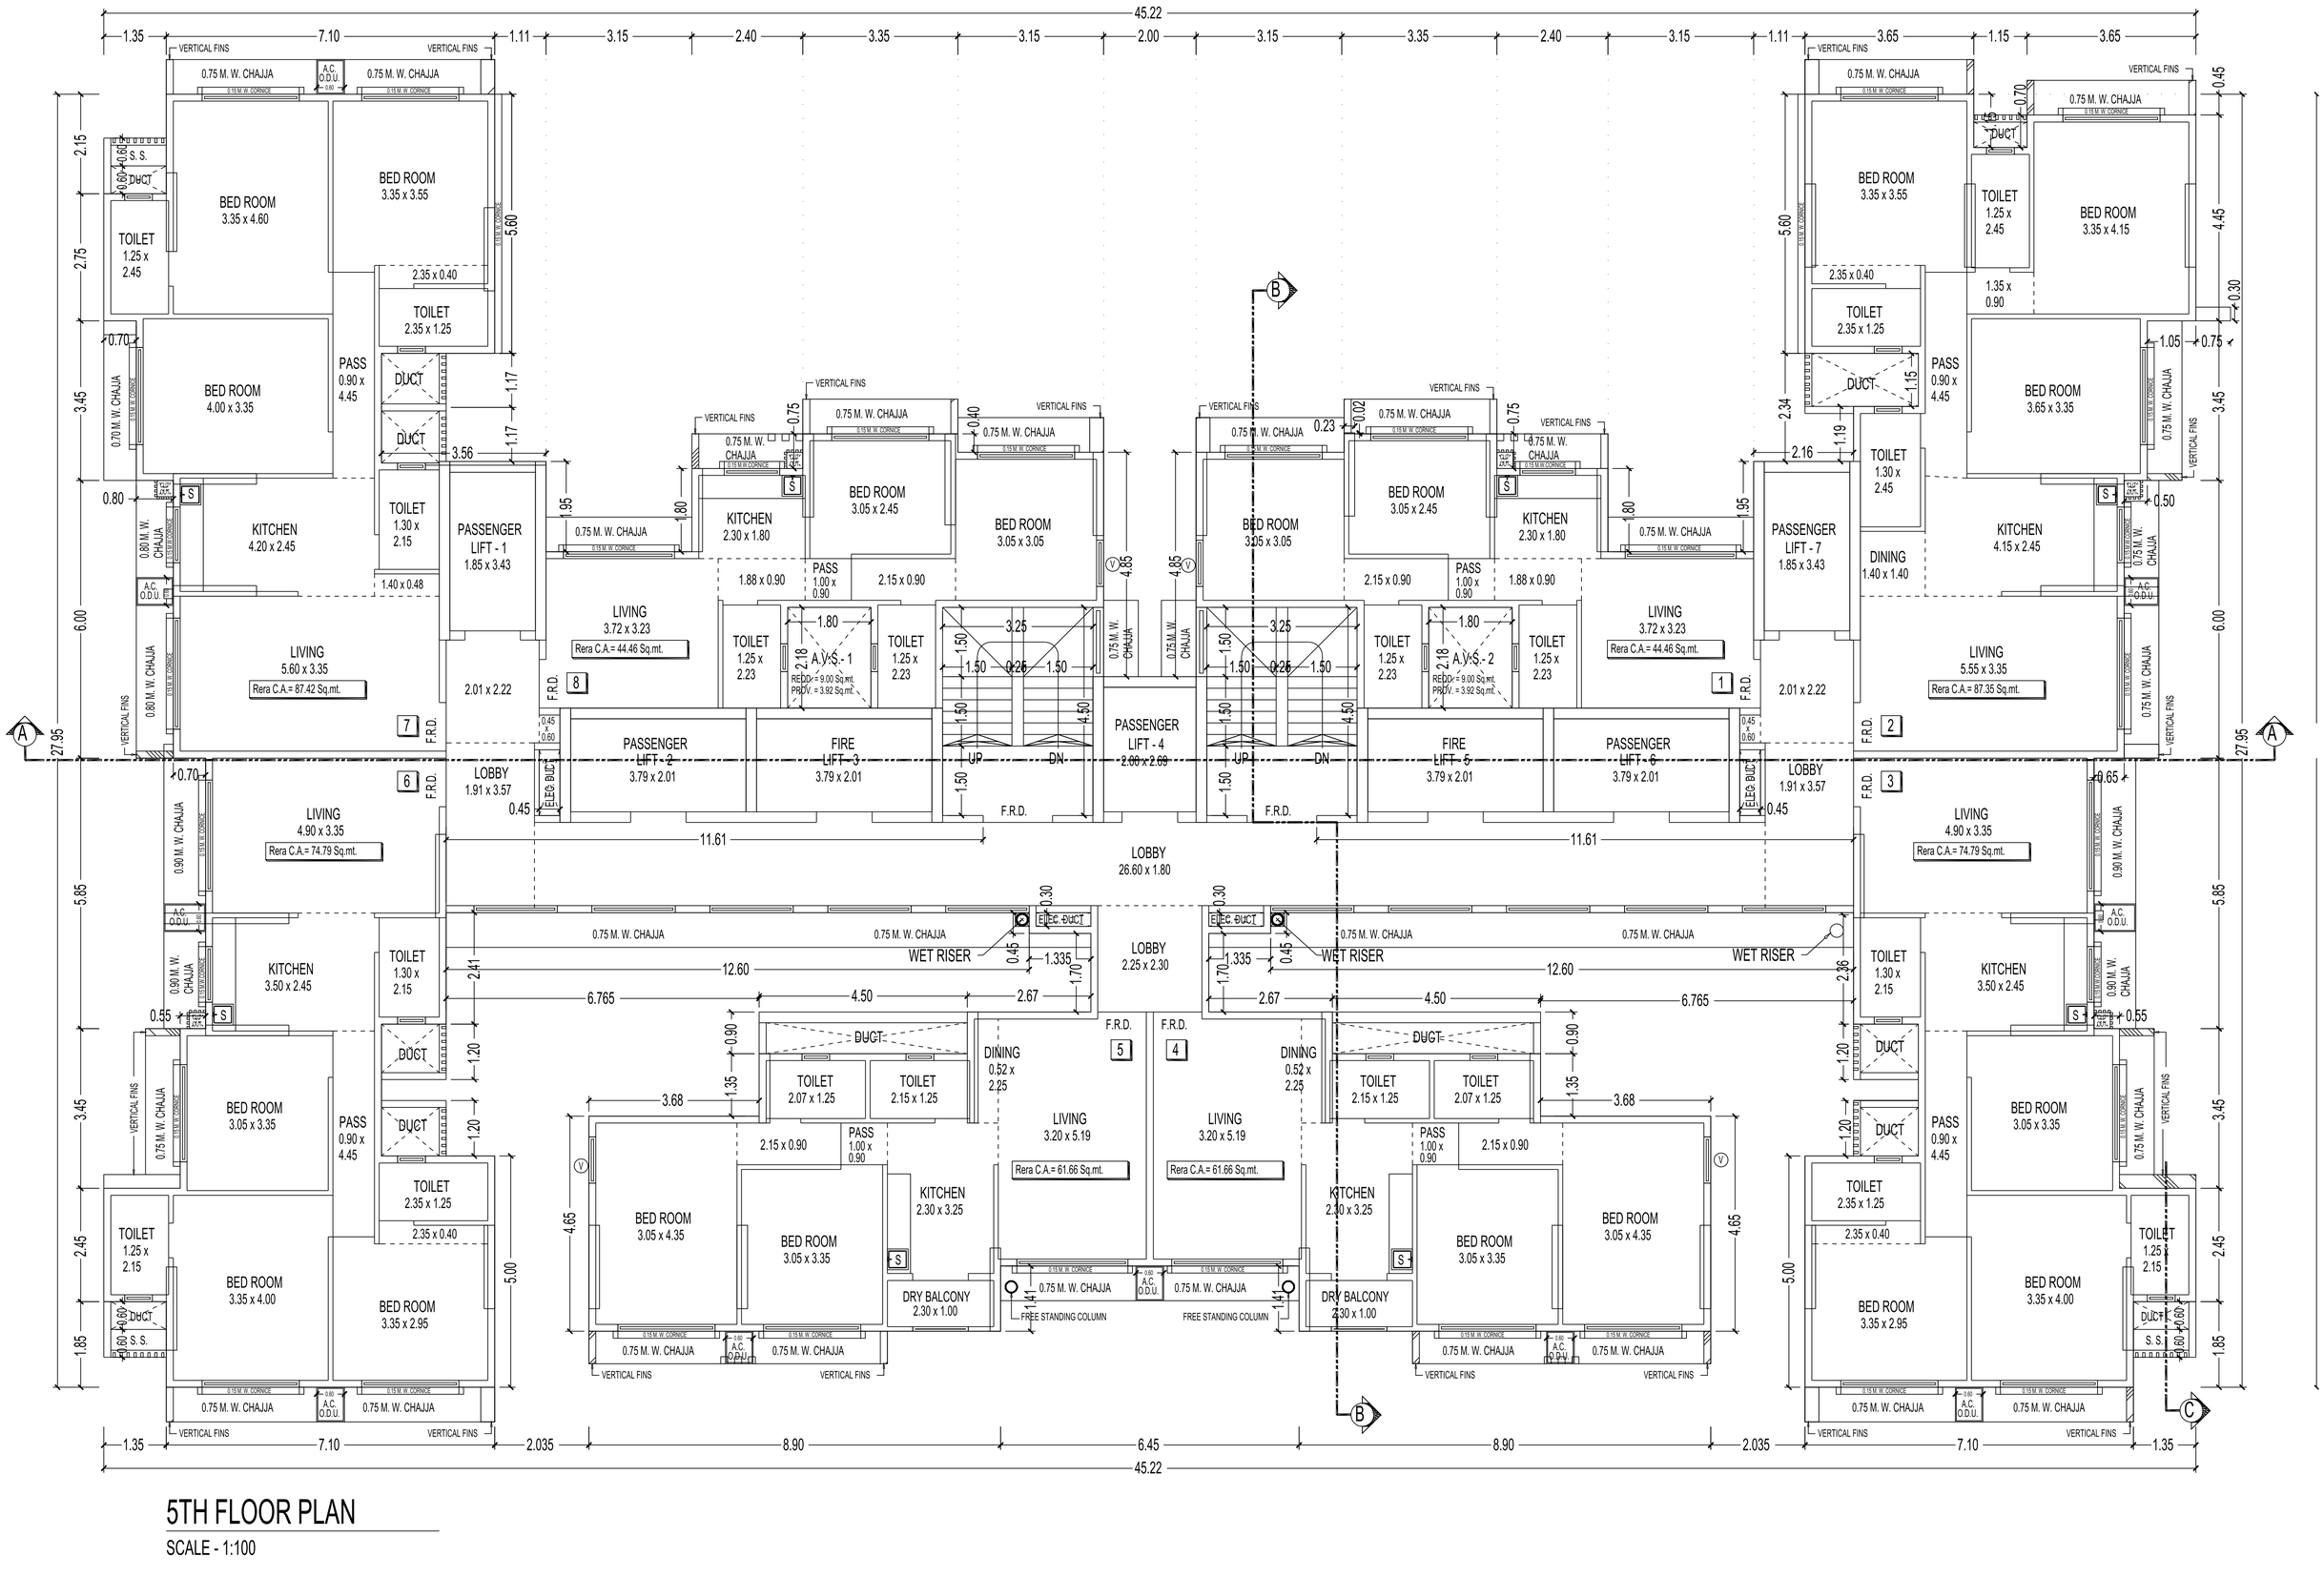


5TH FLOOR PLAN

SCALE - 1:100


FLAT NO. 3

SCALE - 1:100

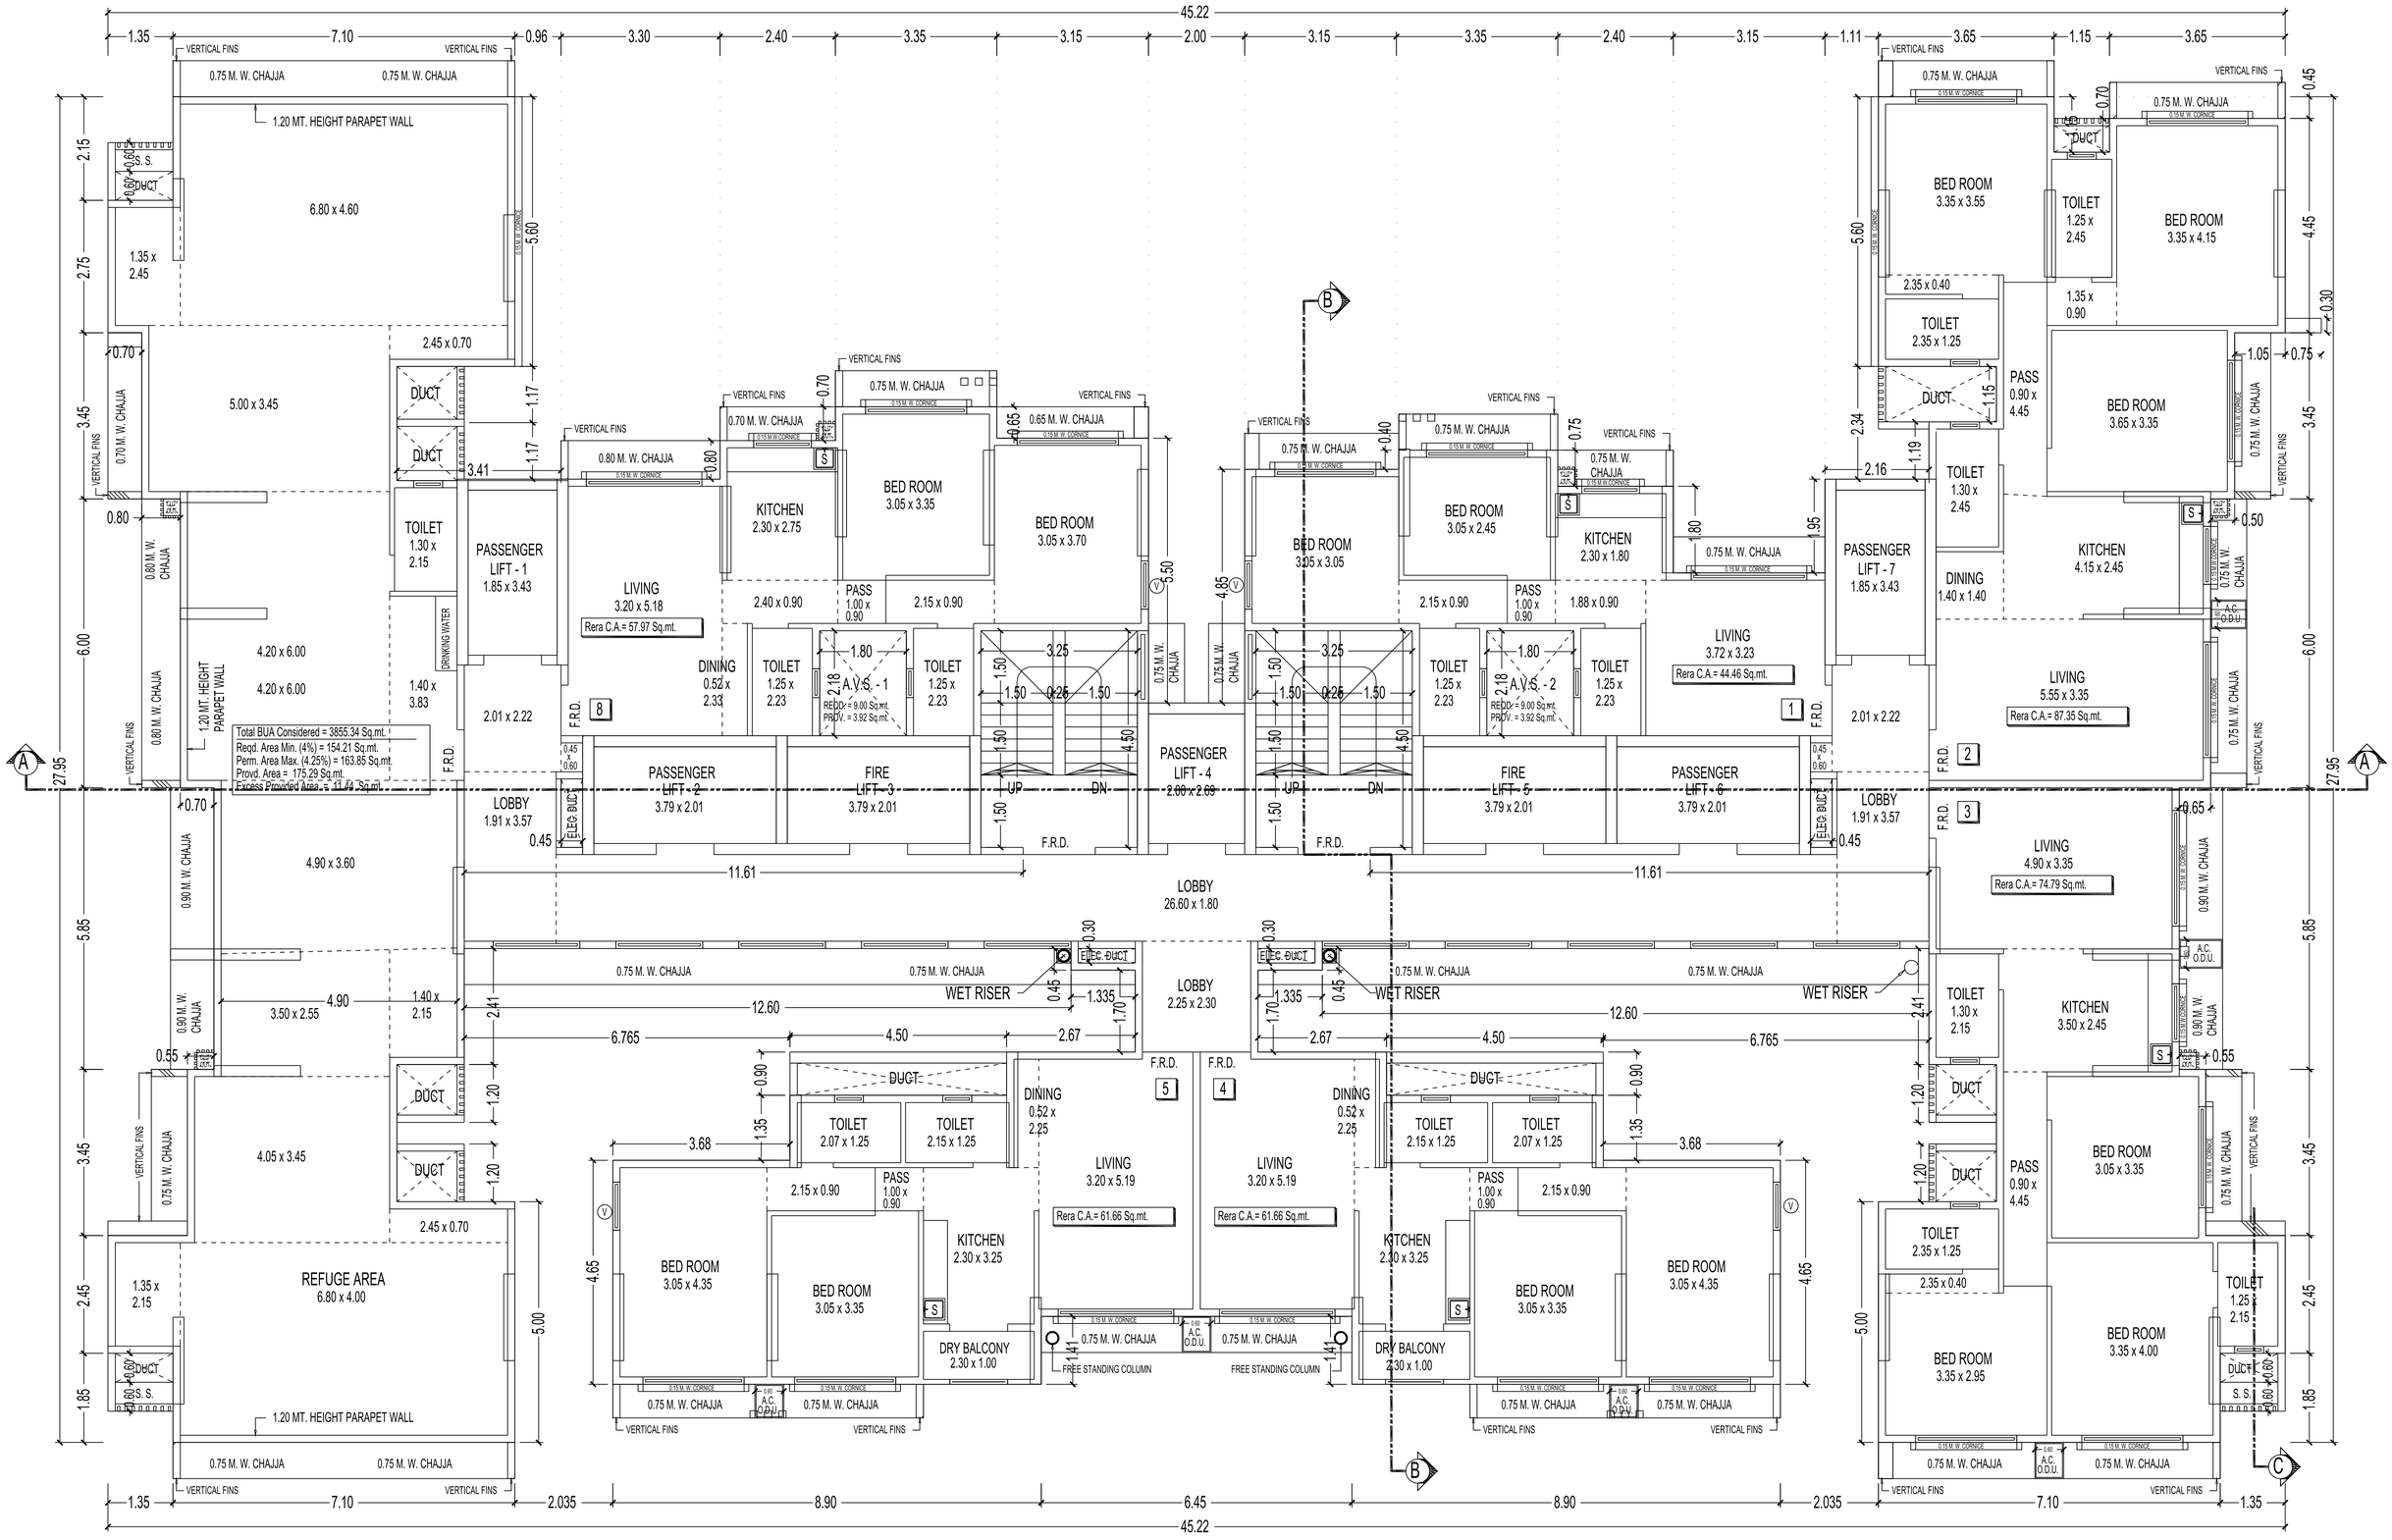


6TH REFUGE FLOOR PLAN

SCALE - 1:100

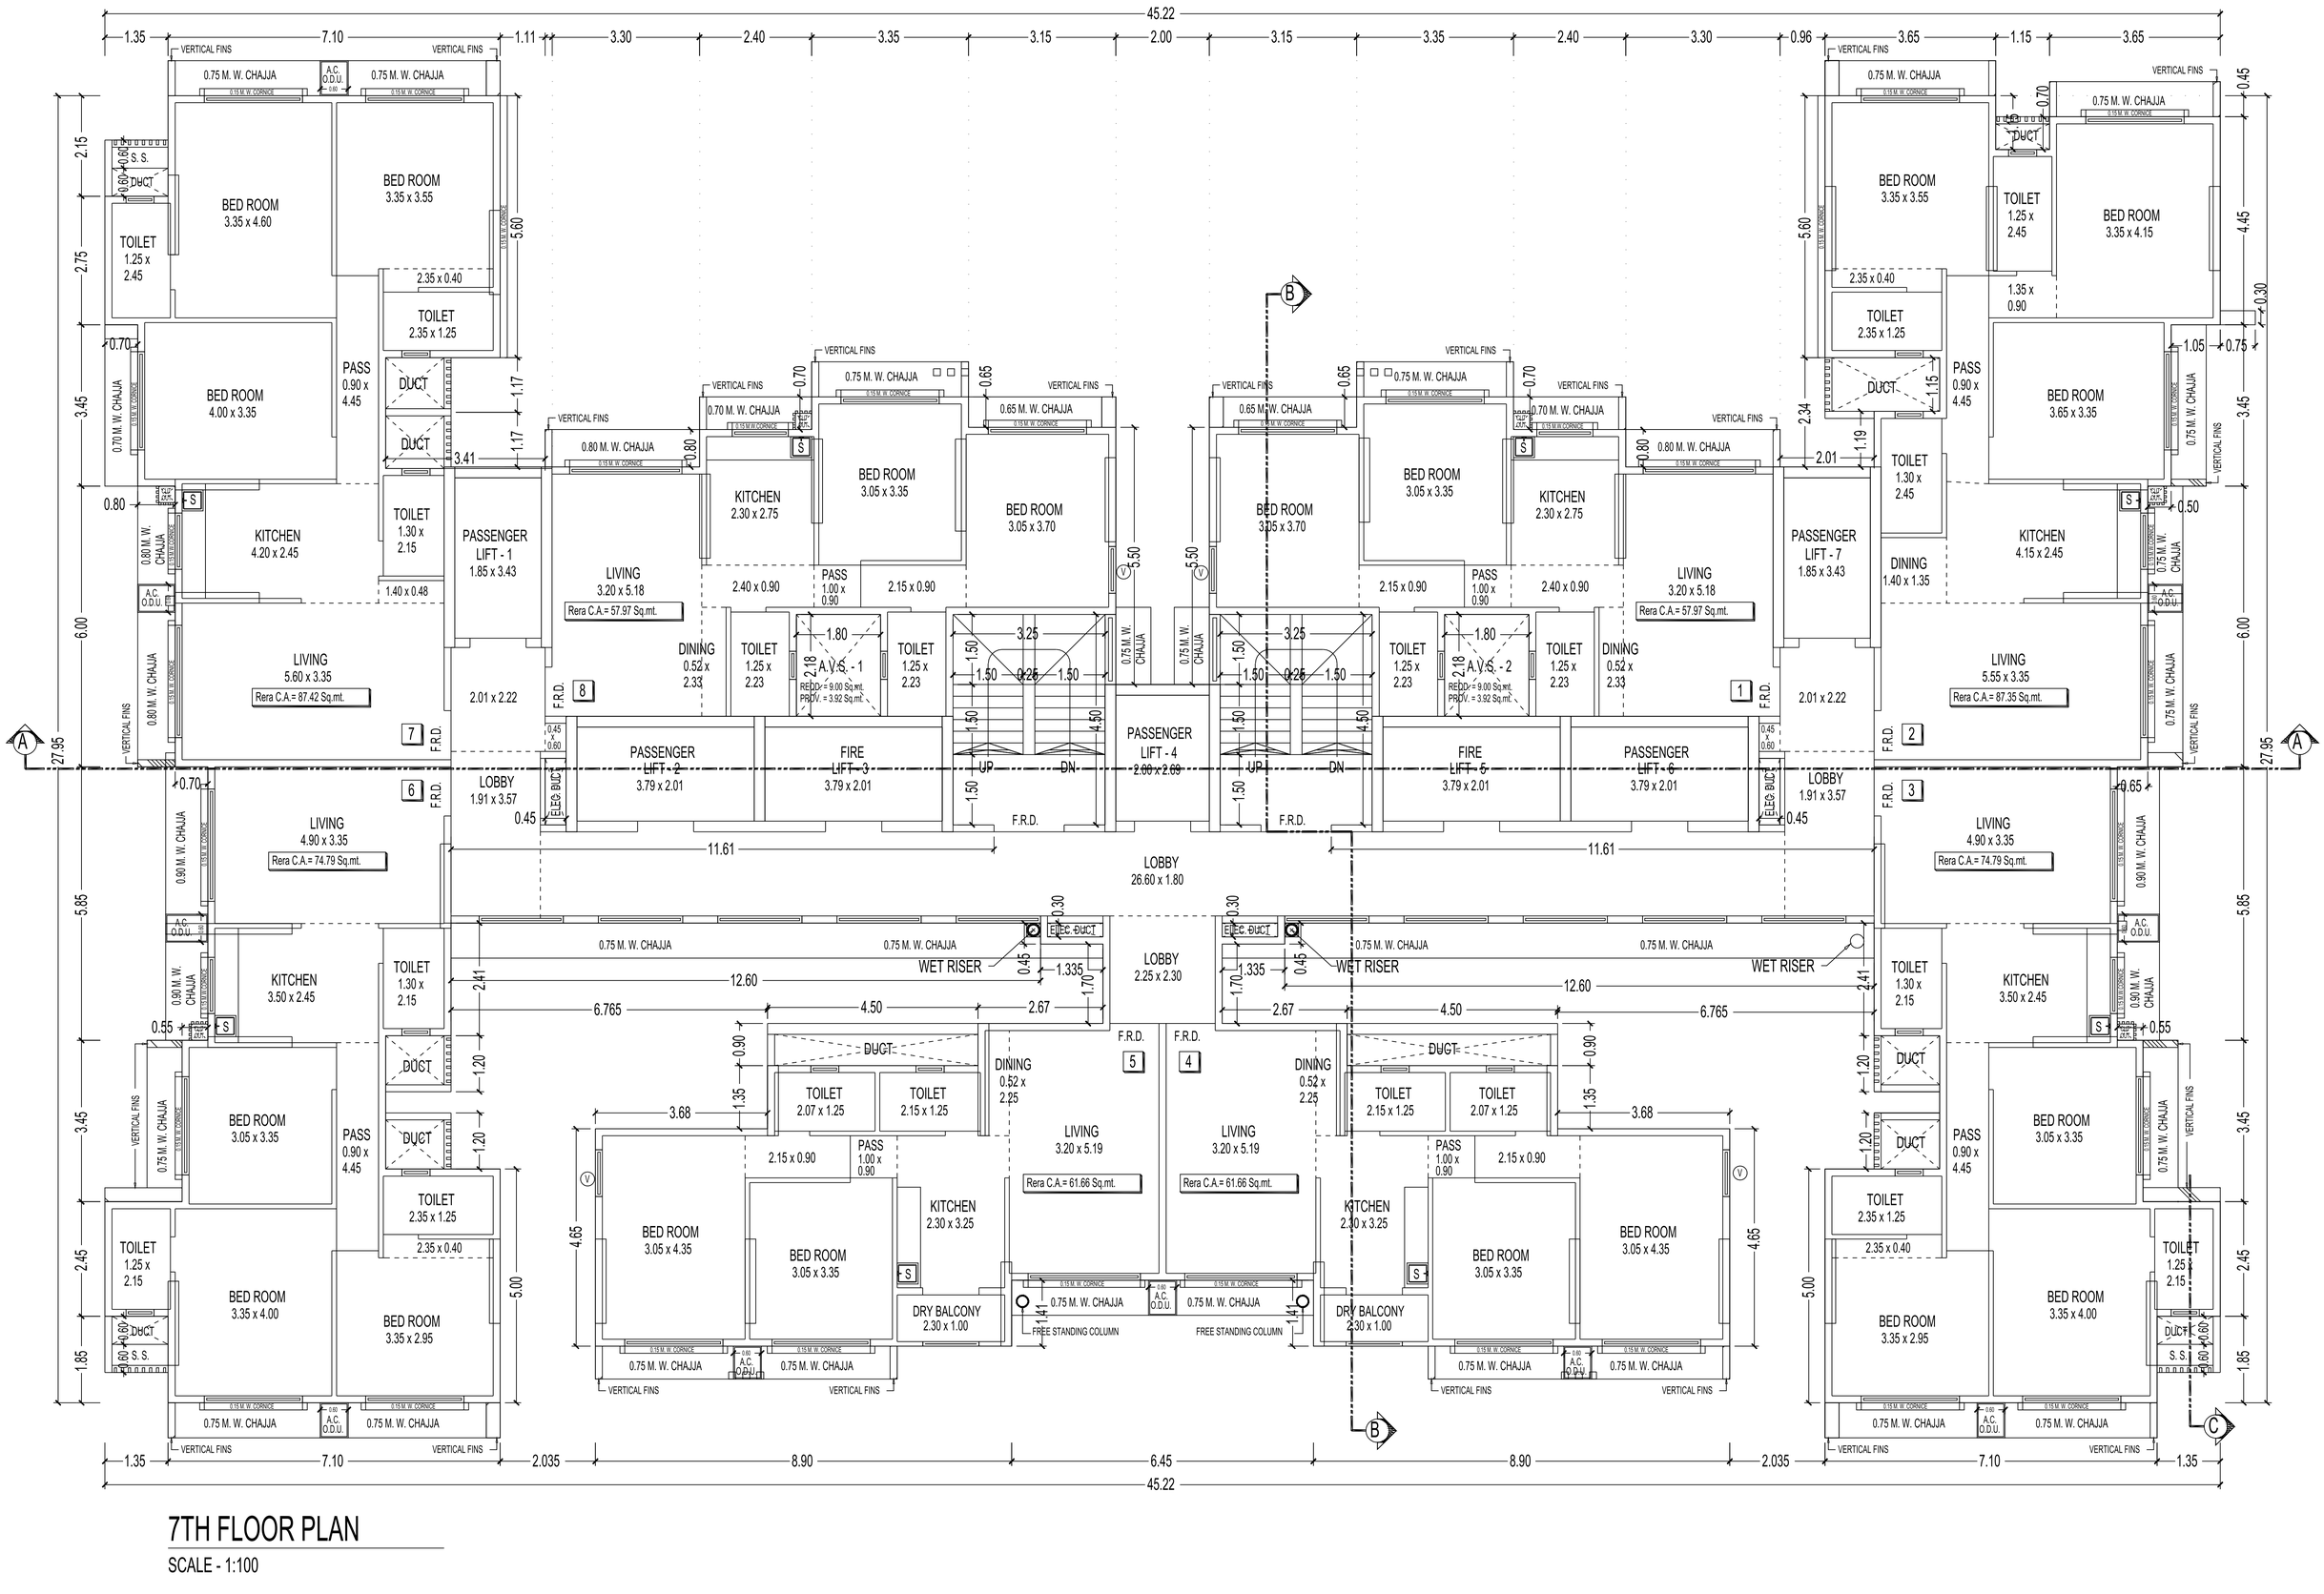
45.22
1.35
7.10
1.11
3.30
2.40
3.35
3.15
2.00
3.15
3.35
2.40
3.30
0.96
3.65
1.15
3.65
VERTICAL FINS
0.75 M. W. CHAJJA
A.C. O.D.U.
0.15 M. W. CORNICE
BED ROOM 3.35 x 4.60
BED ROOM 3.35 x 3.55
BED ROOM 4.00 x 3.35
BED ROOM 3.05 x 3.35
BED ROOM 3.05 x 3.70
BED ROOM 3.65 x 3.35
BED ROOM 3.35 x 4.15
TOILET 1.25 x 2.45
TOILET 2.35 x 1.25
TOILET 1.30 x 2.15
TOILET 2.07 x 1.25
TOILET 2.15 x 1.25
TOILET 1.30 x 2.45
PASS 0.90 x 4.45
PASS 1.00 x 0.90
DUCT
S. S.
KITCHEN 4.20 x 2.45
KITCHEN 2.30 x 2.75
KITCHEN 4.15 x 2.45
KITCHEN 3.50 x 2.45
KITCHEN 2.30 x 3.25
PASSENGER LIFT - 1 1.85 x 3.43
PASSENGER LIFT - 7 1.85 x 3.43
LIVING 3.20 x 5.18
Rera C.A.= 57.97 Sq.mt.
DINING 1.40 x 1.35
DINING 0.52 x 2.33
LIVING 5.60 x 3.35
Rera C.A.= 87.42 Sq.mt.
LIVING 5.55 x 3.35
Rera C.A.= 87.35 Sq.mt.
LIVING 4.90 x 3.35
Rera C.A.= 74.79 Sq.mt.
LIVING 3.20 x 5.19
Rera C.A.= 61.66 Sq.mt.
A.V.S. - 1
REQD. = 9.00 Sq.mt.
PROV. = 3.92 Sq.mt.
A.V.S. - 2
REQD. = 9.00 Sq.mt.
PROV. = 3.92 Sq.mt.
PASSENGER LIFT - 2 3.79 x 2.01
FIRE LIFT - 3 3.79 x 2.01
PASSENGER LIFT - 4 2.00 x 2.69
FIRE LIFT - 5 3.79 x 2.01
PASSENGER LIFT - 6 3.79 x 2.01
LOBBY 1.91 x 3.57
LOBBY 26.60 x 1.80
LOBBY 2.25 x 2.30
ELEC. DUCT
WET RISER
F.R.D.
UP
DN
DRY BALCONY 2.30 x 1.00
FREE STANDING COLUMN
2.01 x 2.22
1.40 x 0.48
2.40 x 0.90
2.15 x 0.90
1.80
3.25
1.50
0.25
2.18
1.335
1.41
0.45 x 0.60
0.75 M. W. CHAJJA
0.80 M. W. CHAJJA
0.70 M. W. CHAJJA
0.65 M. W. CHAJJA
0.90 M. W. CHAJJA
0.75 M. W. CHAJJA
0.15 M. W. CORNICE
0.80 M. W. CHAJJA
0.70 M. W. CHAJJA
0.65 M. W. CHAJJA
0.75 M. W. CHAJJA
0.15 M. W. CORNICE
0.75 M. W. CHAJJA
0.75 M. W. CHAJJA
0.75 M. W. CHAJJA


FLAT NO. 6

SCALE - 1:100

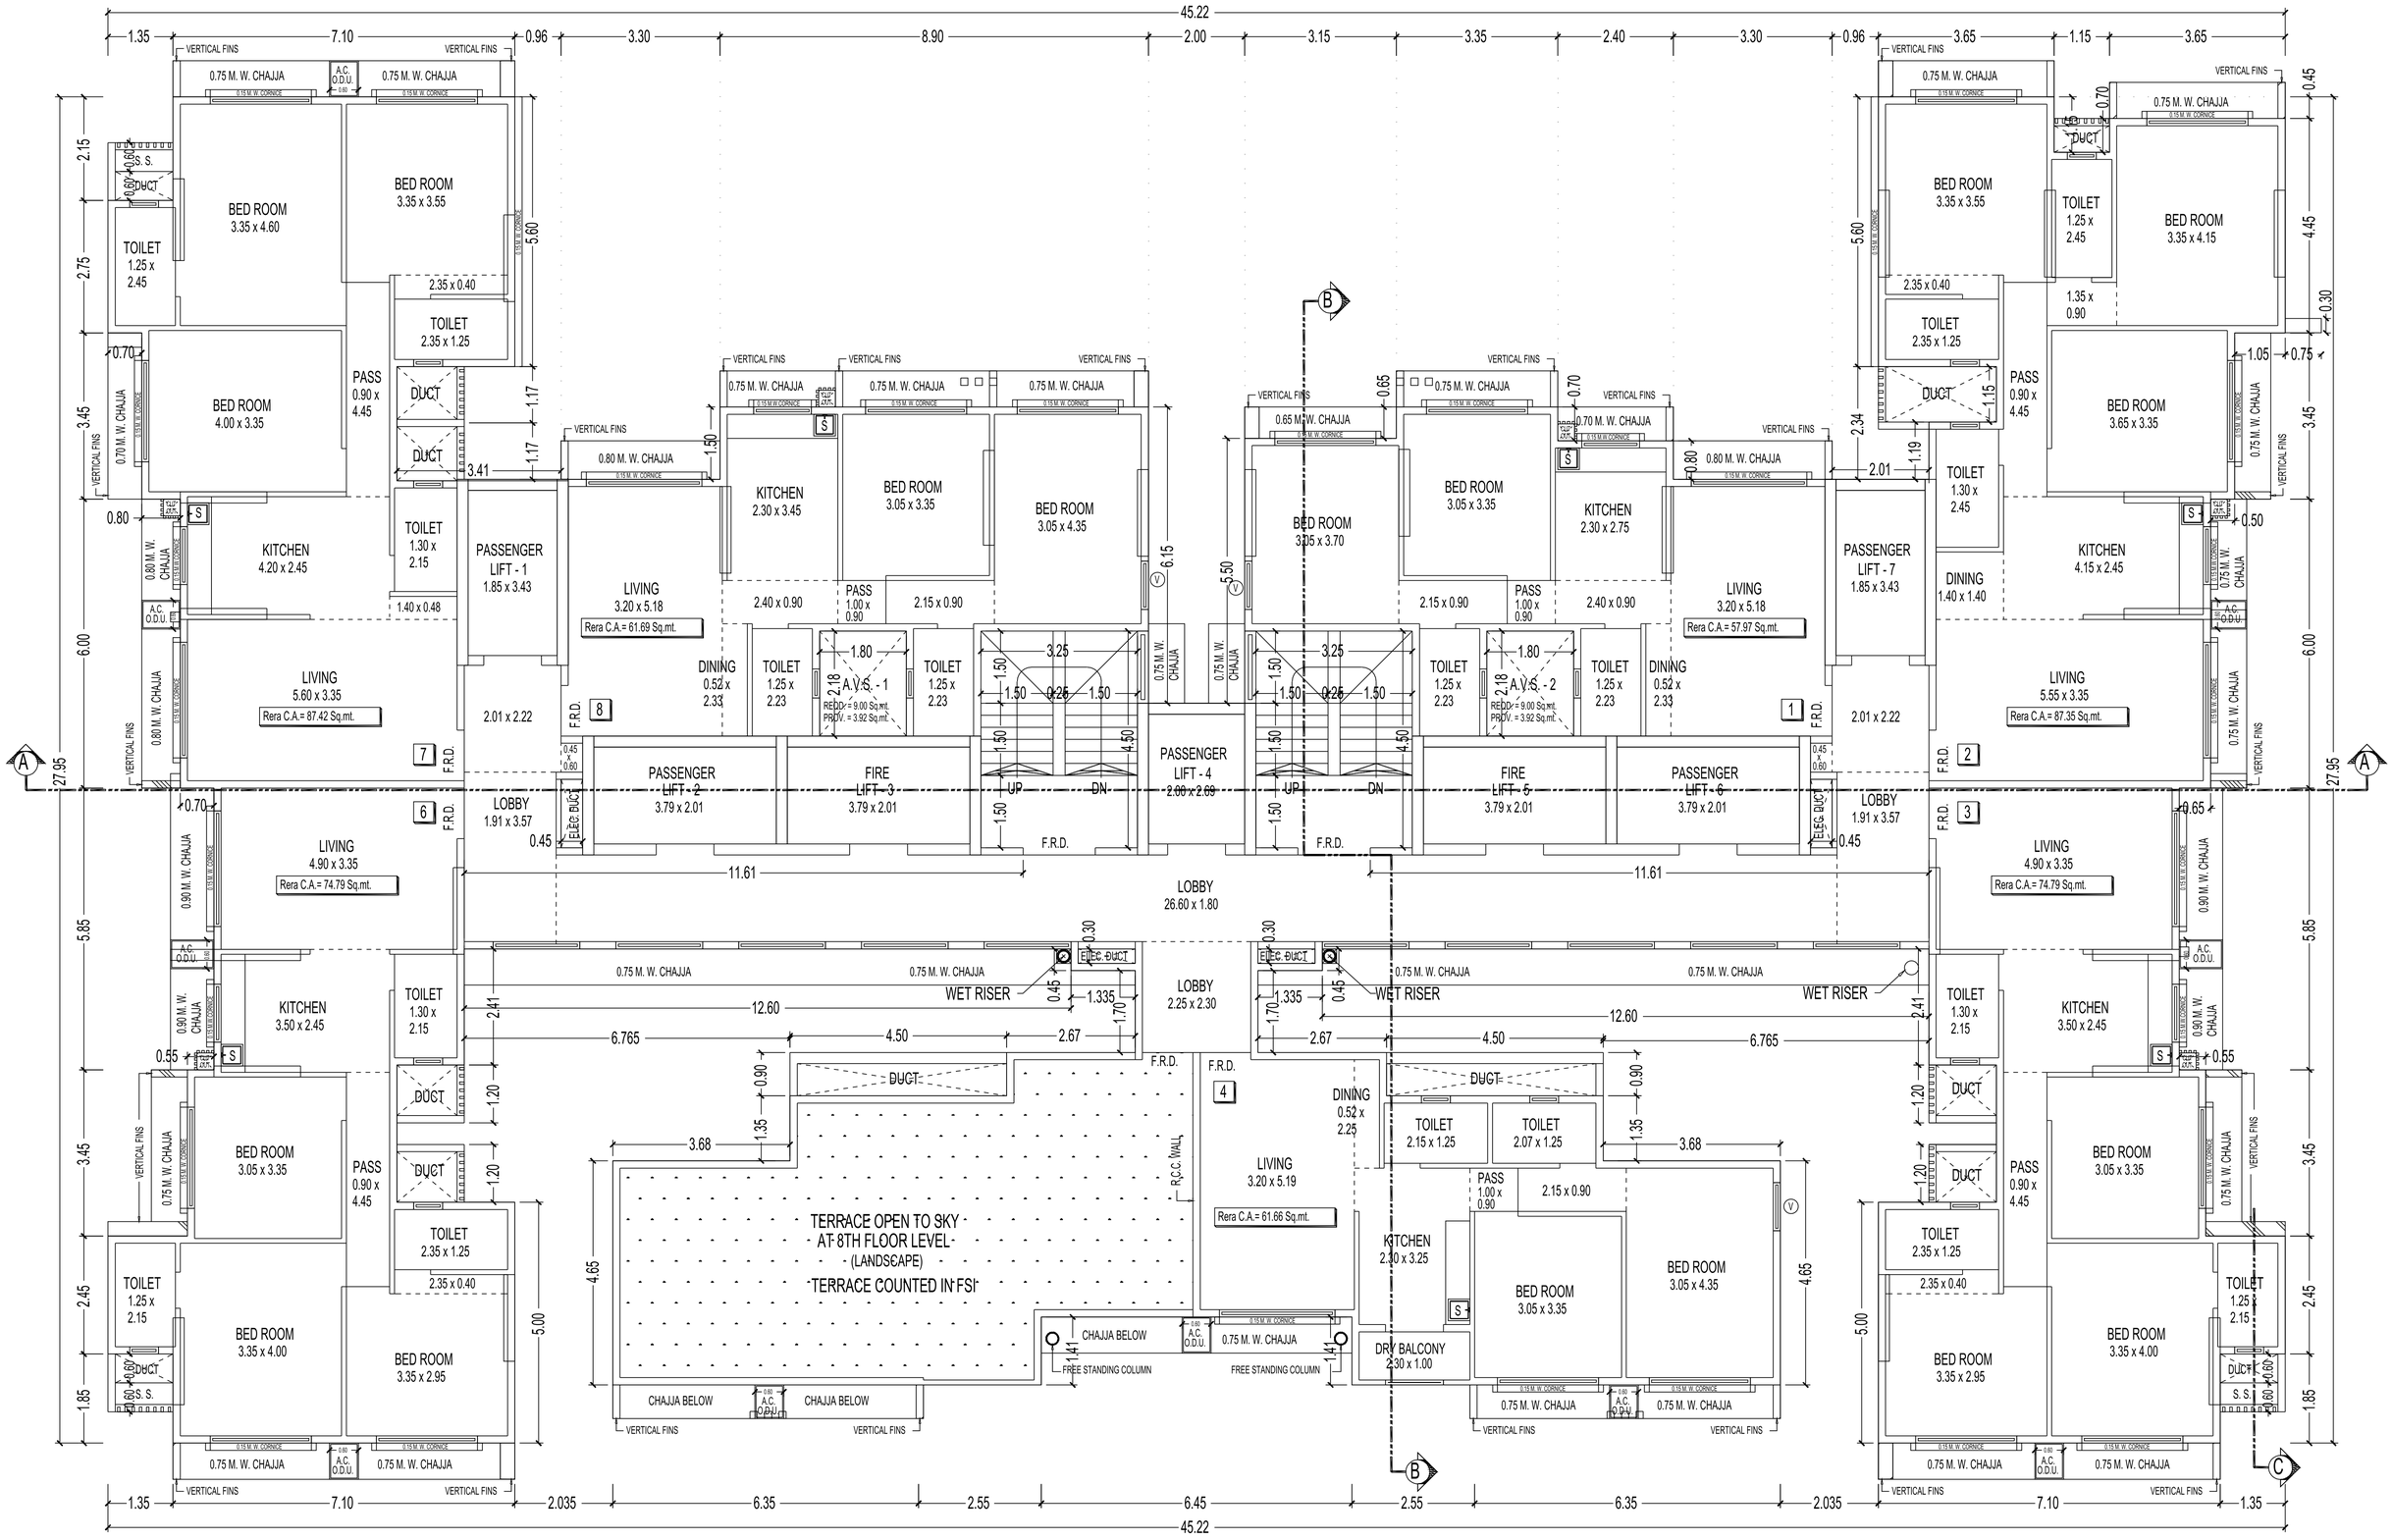

8TH FLOOR PLAN

SCALE - 1:100

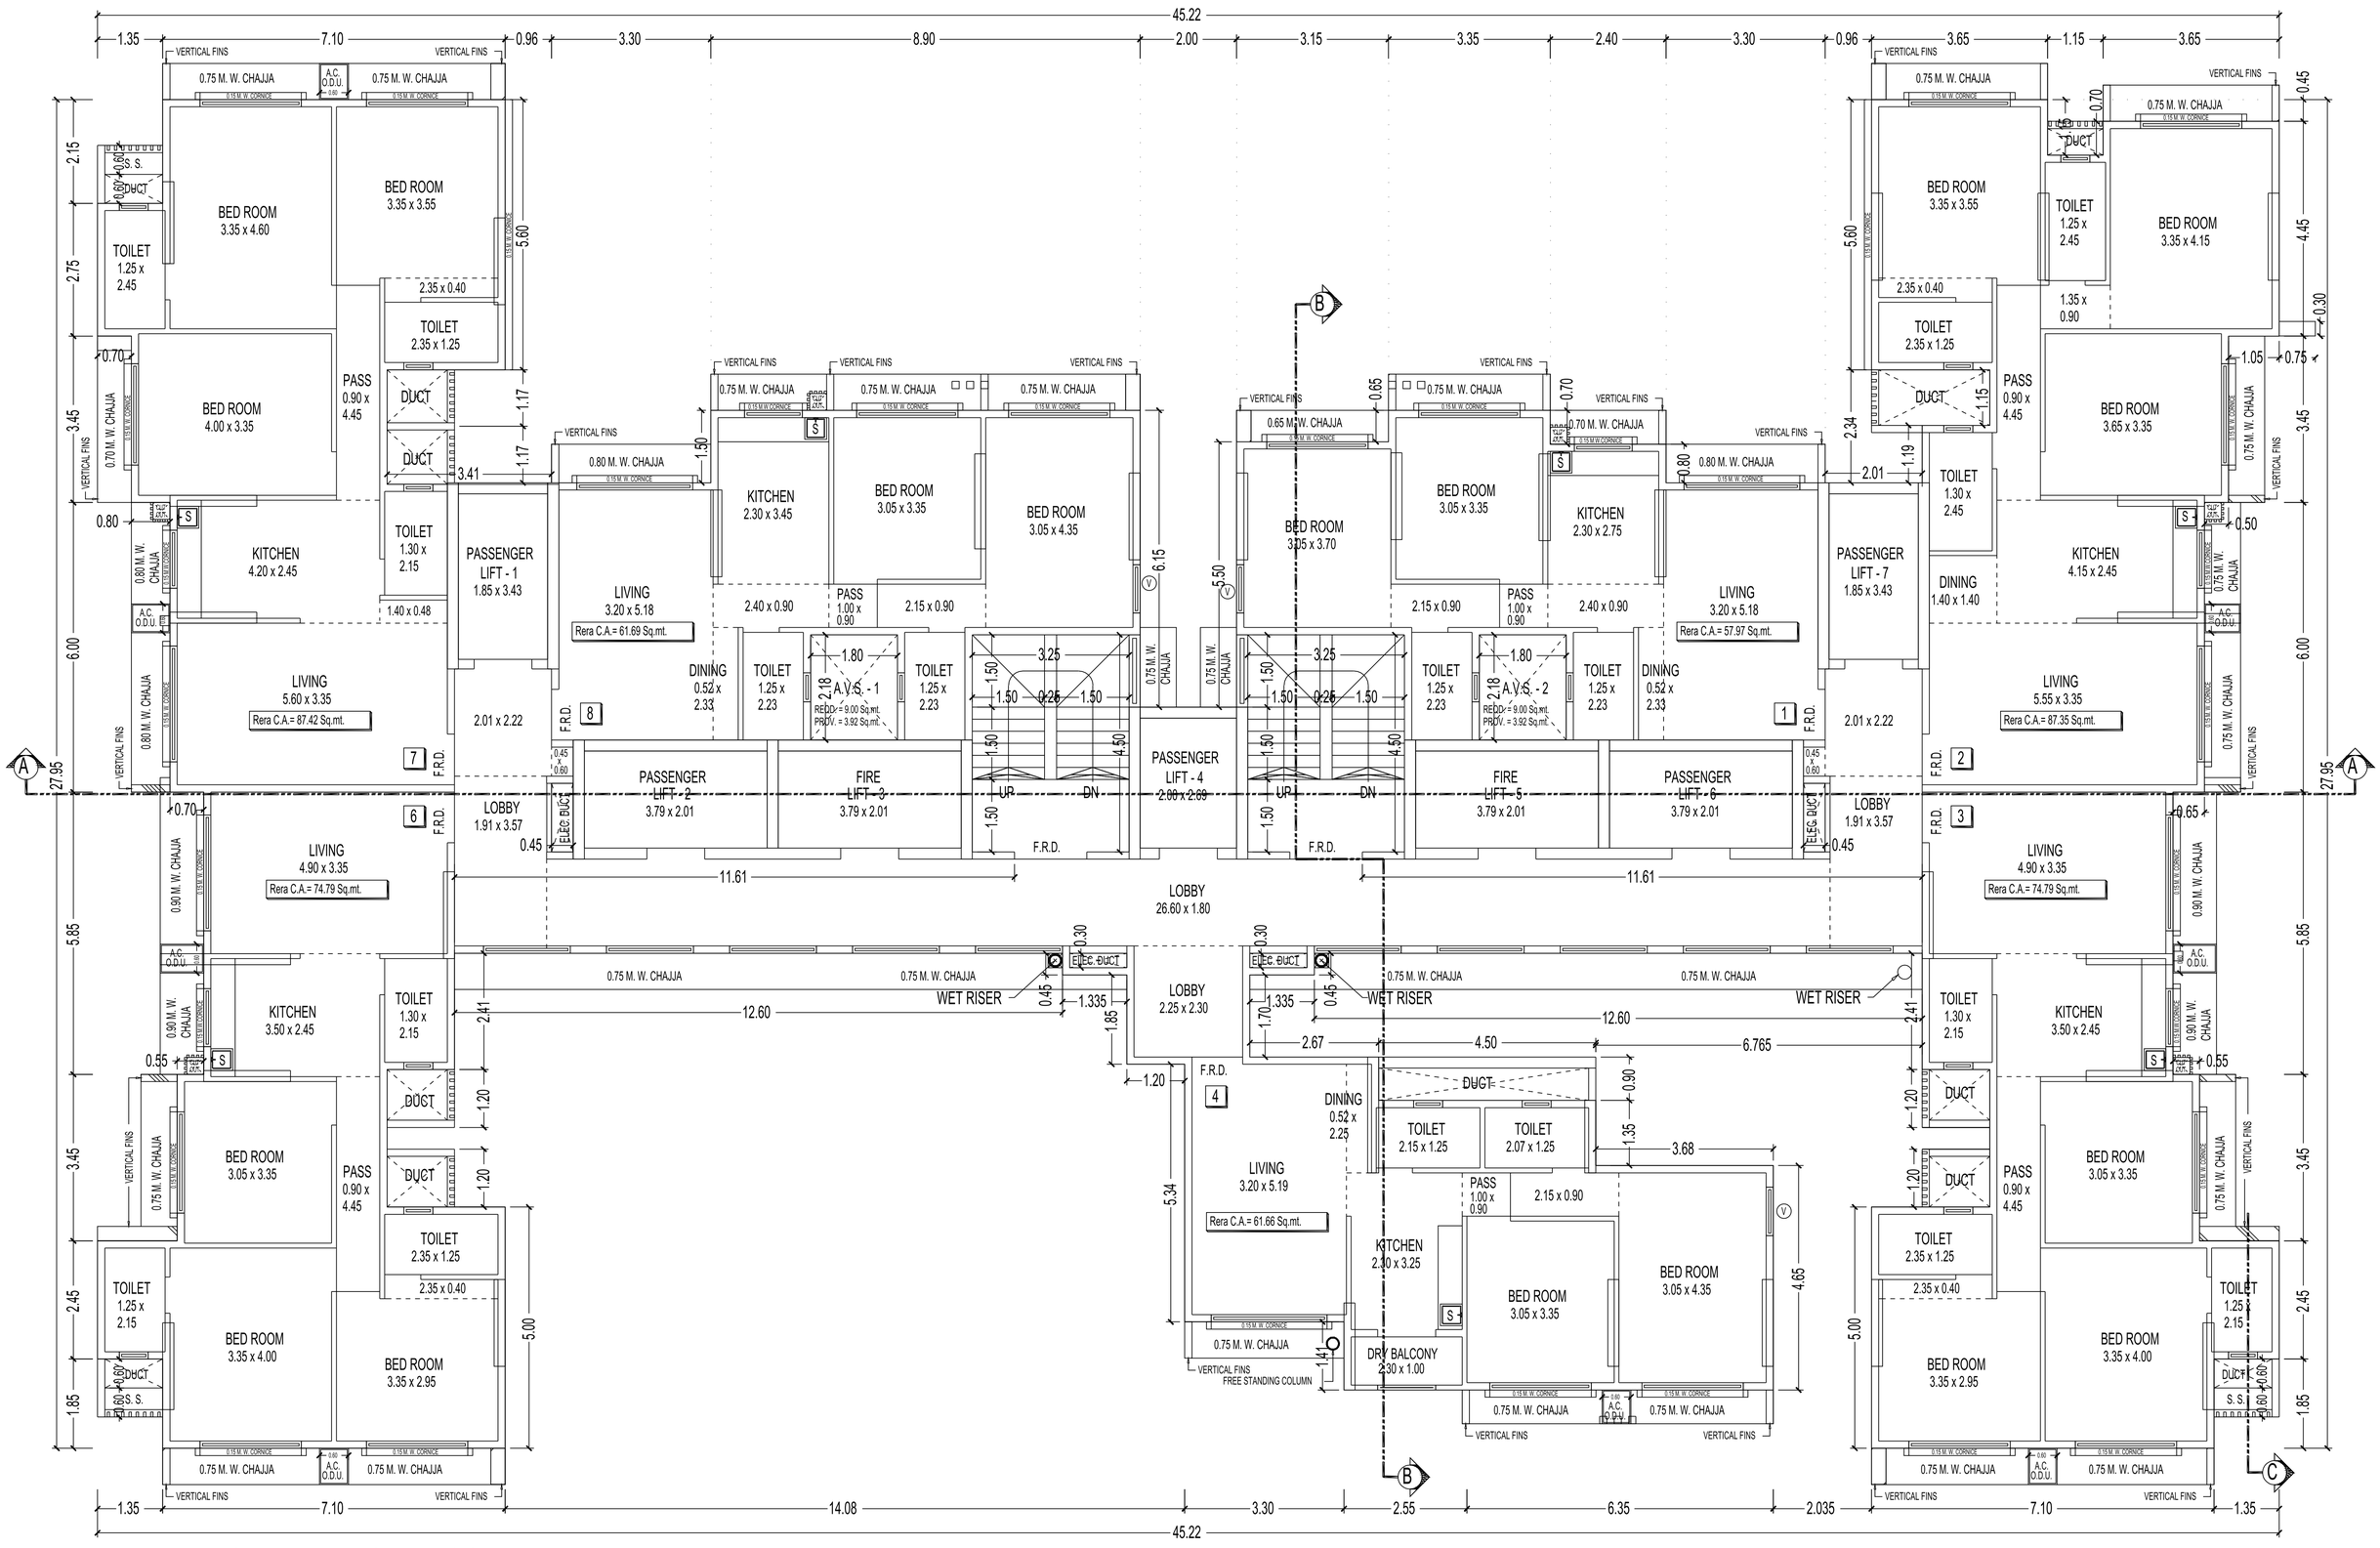


9TH TO 11TH TYPICAL FLOOR PLAN

SCALE - 1:100


FLAT NO. 3

SCALE - 1:100

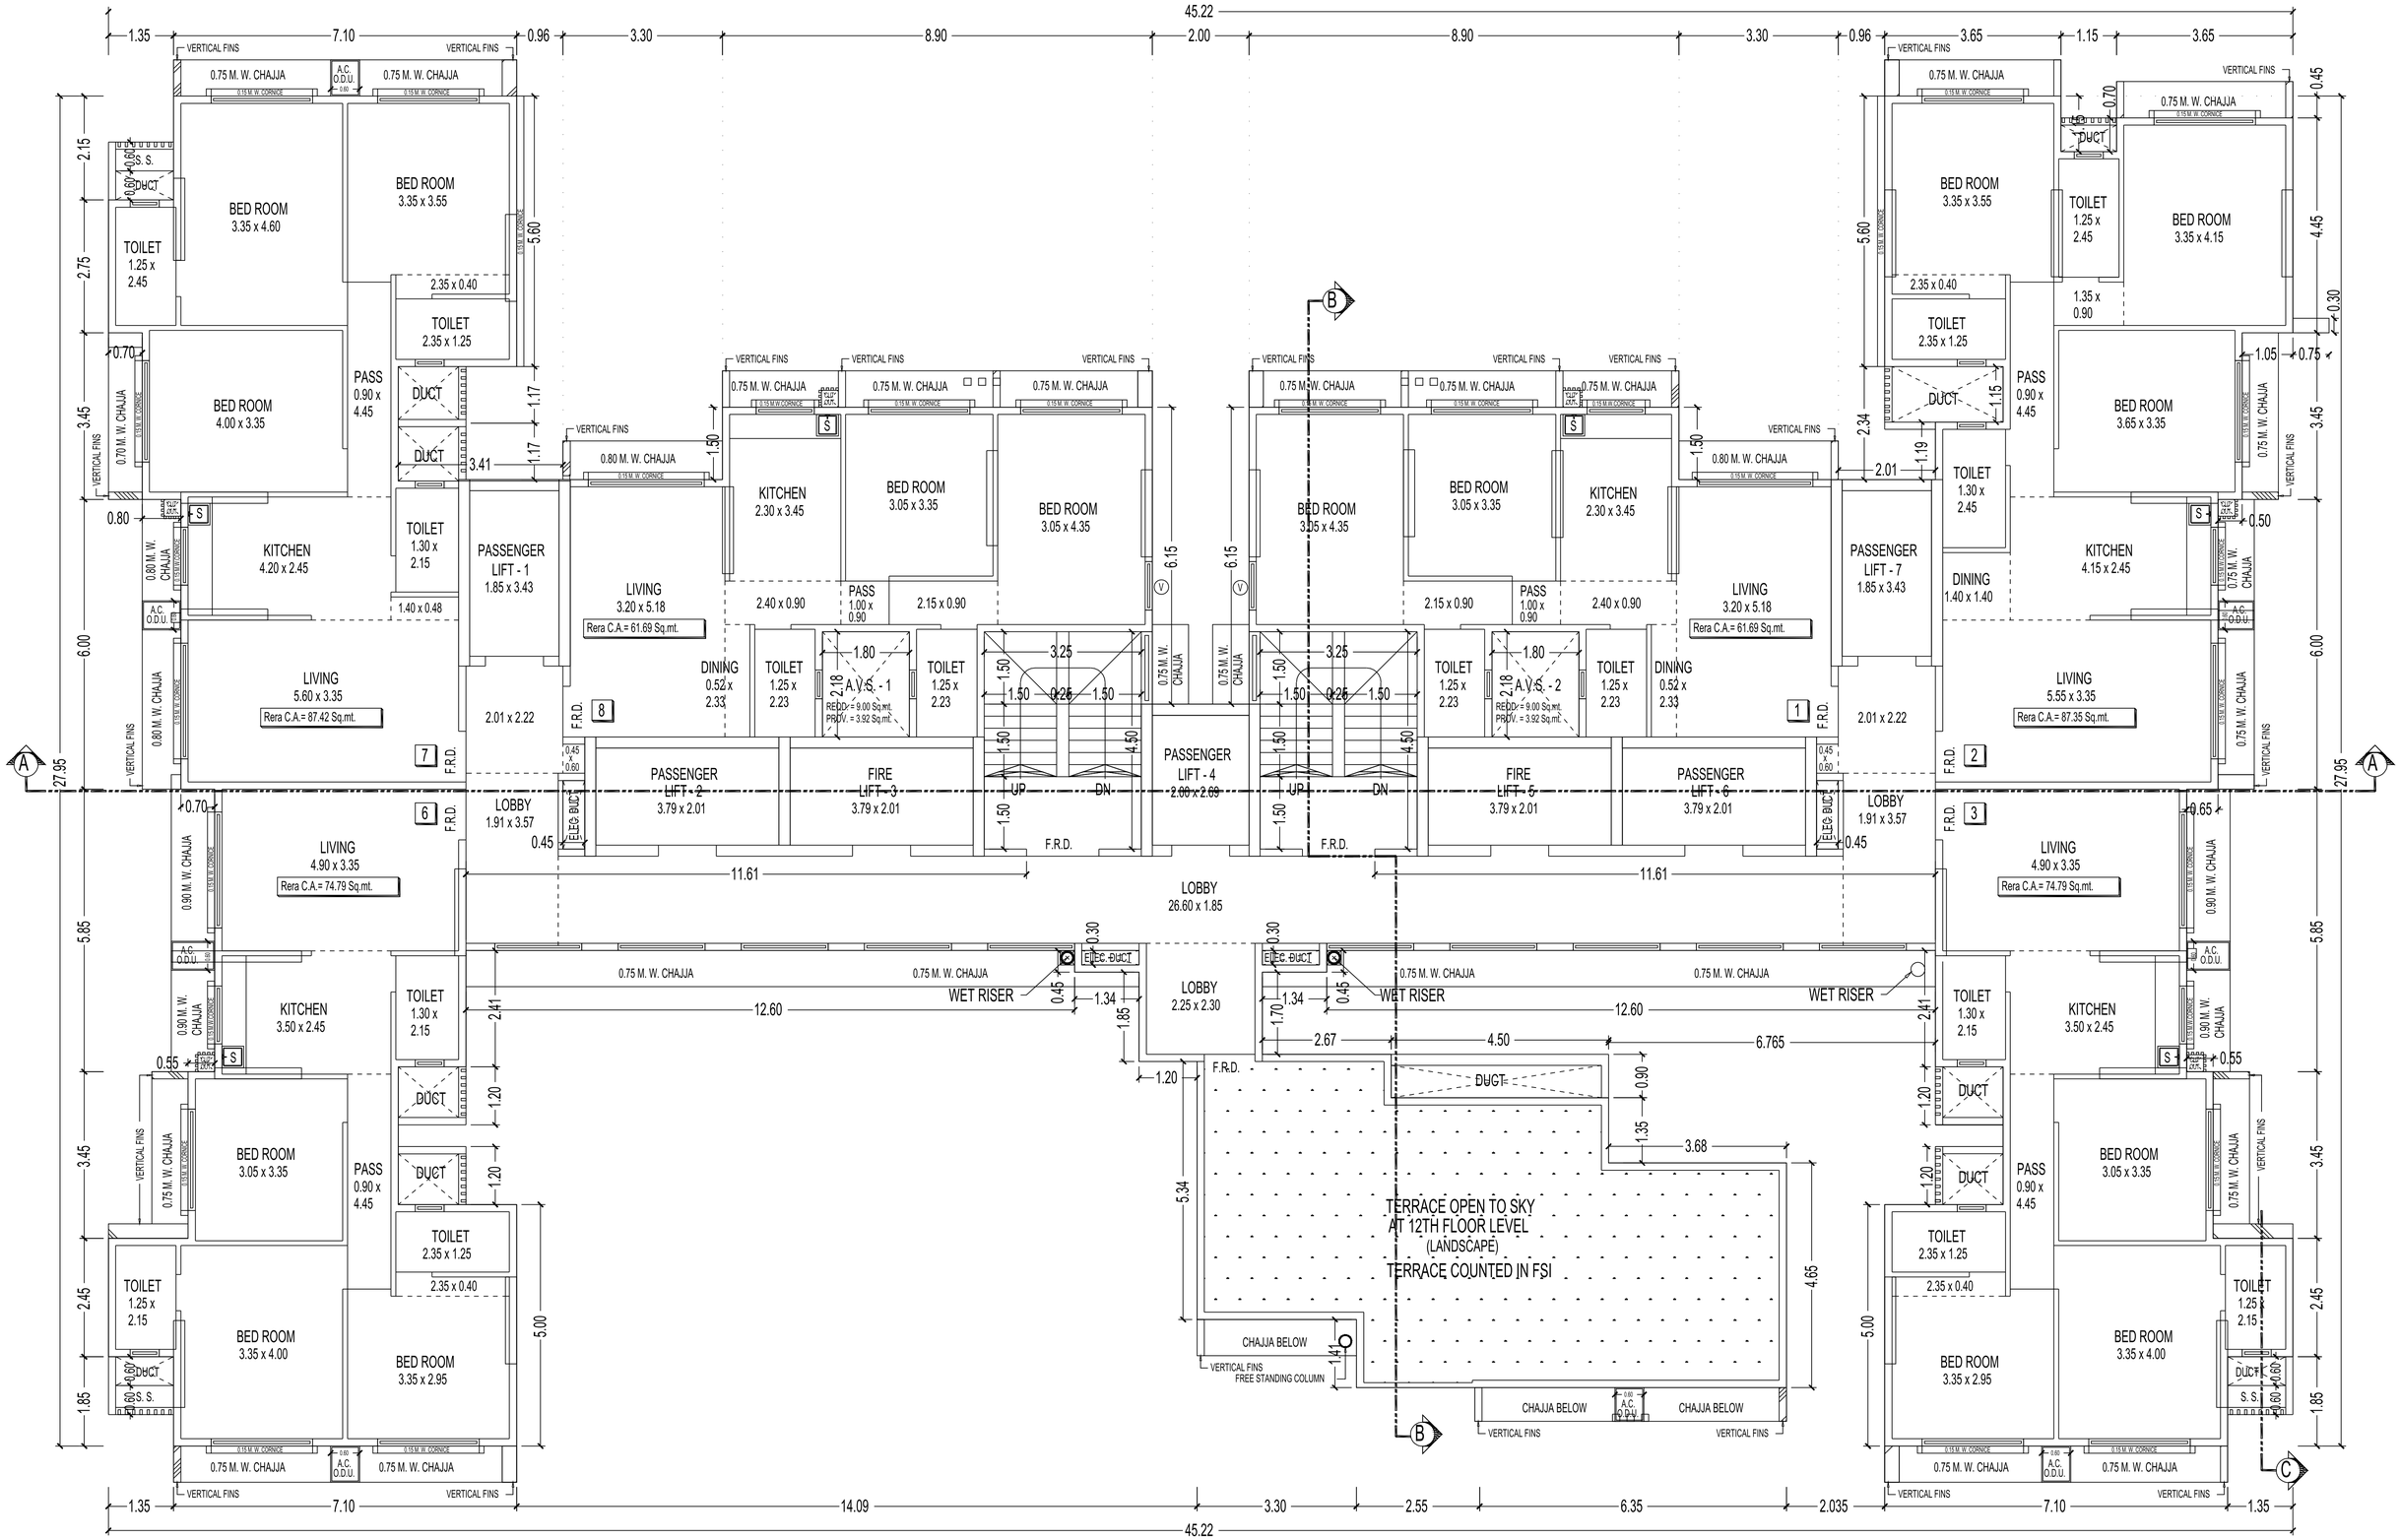

12TH FLOOR PLAN


SCALE - 1:100

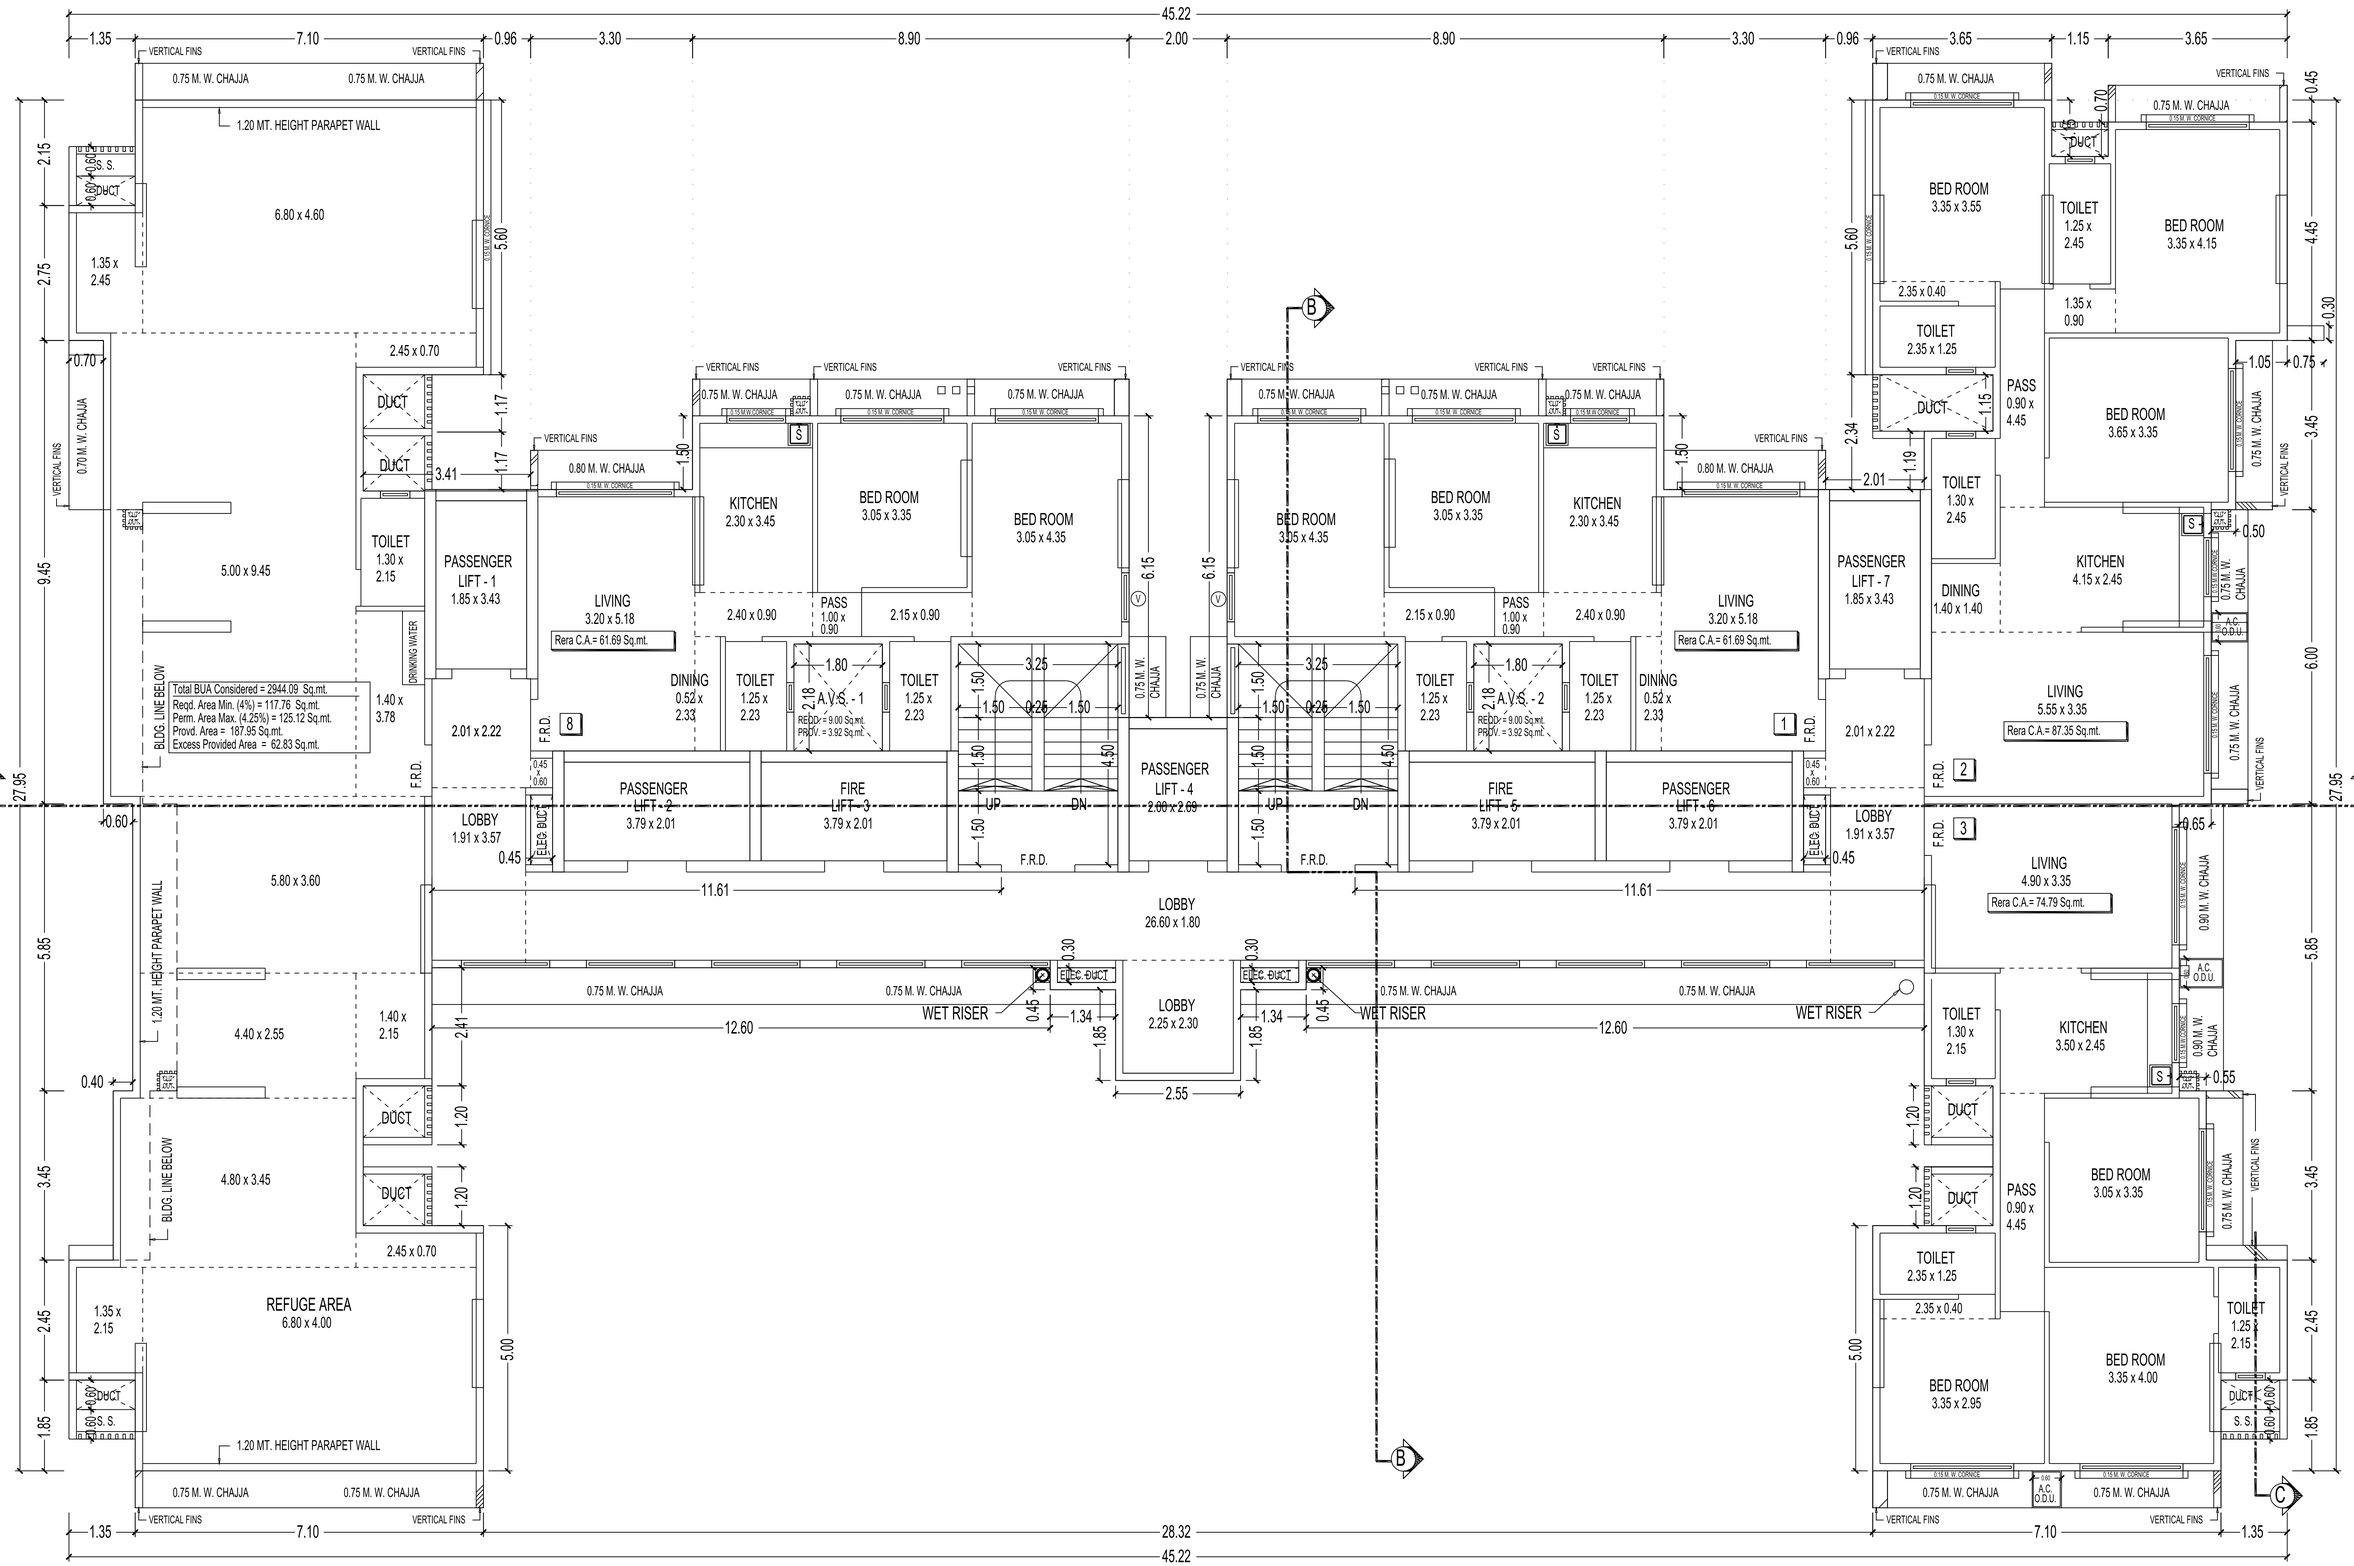

13TH REFUGE FLOOR PLAN


SCALE - 1:100

SCALE - 1:100

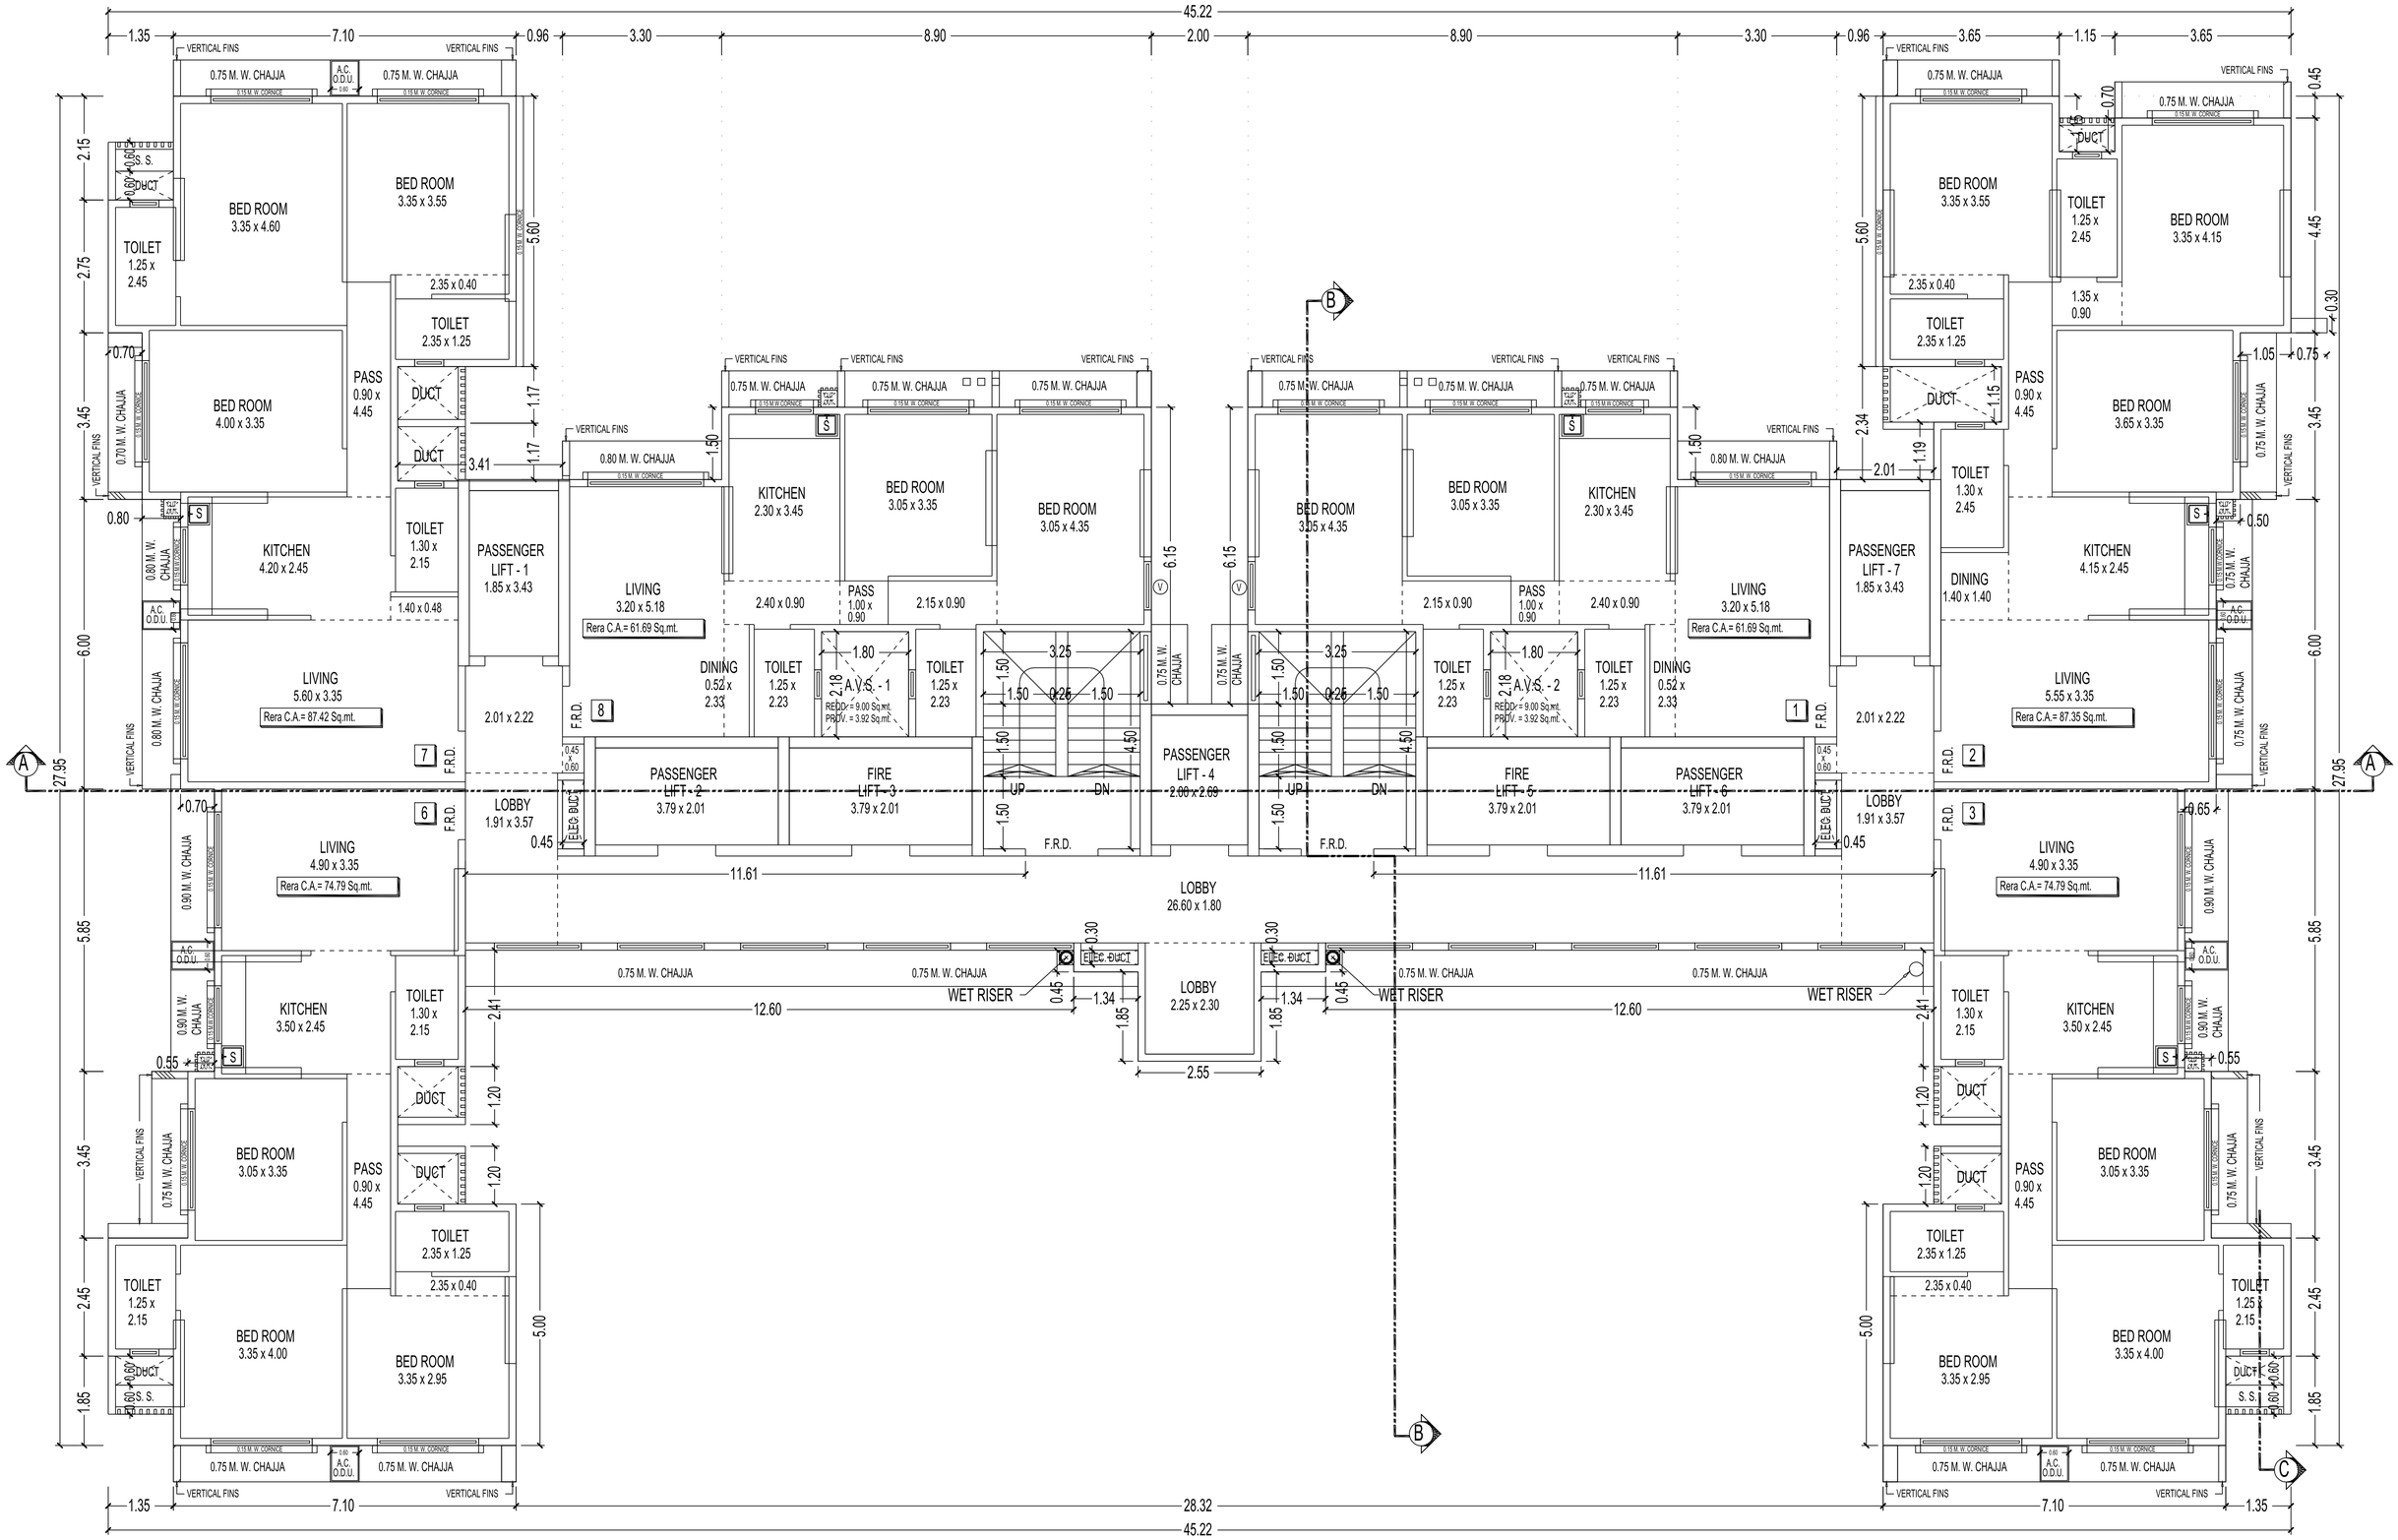

14TH TO 16TH FLOOR PLAN

SCALE - 1:100

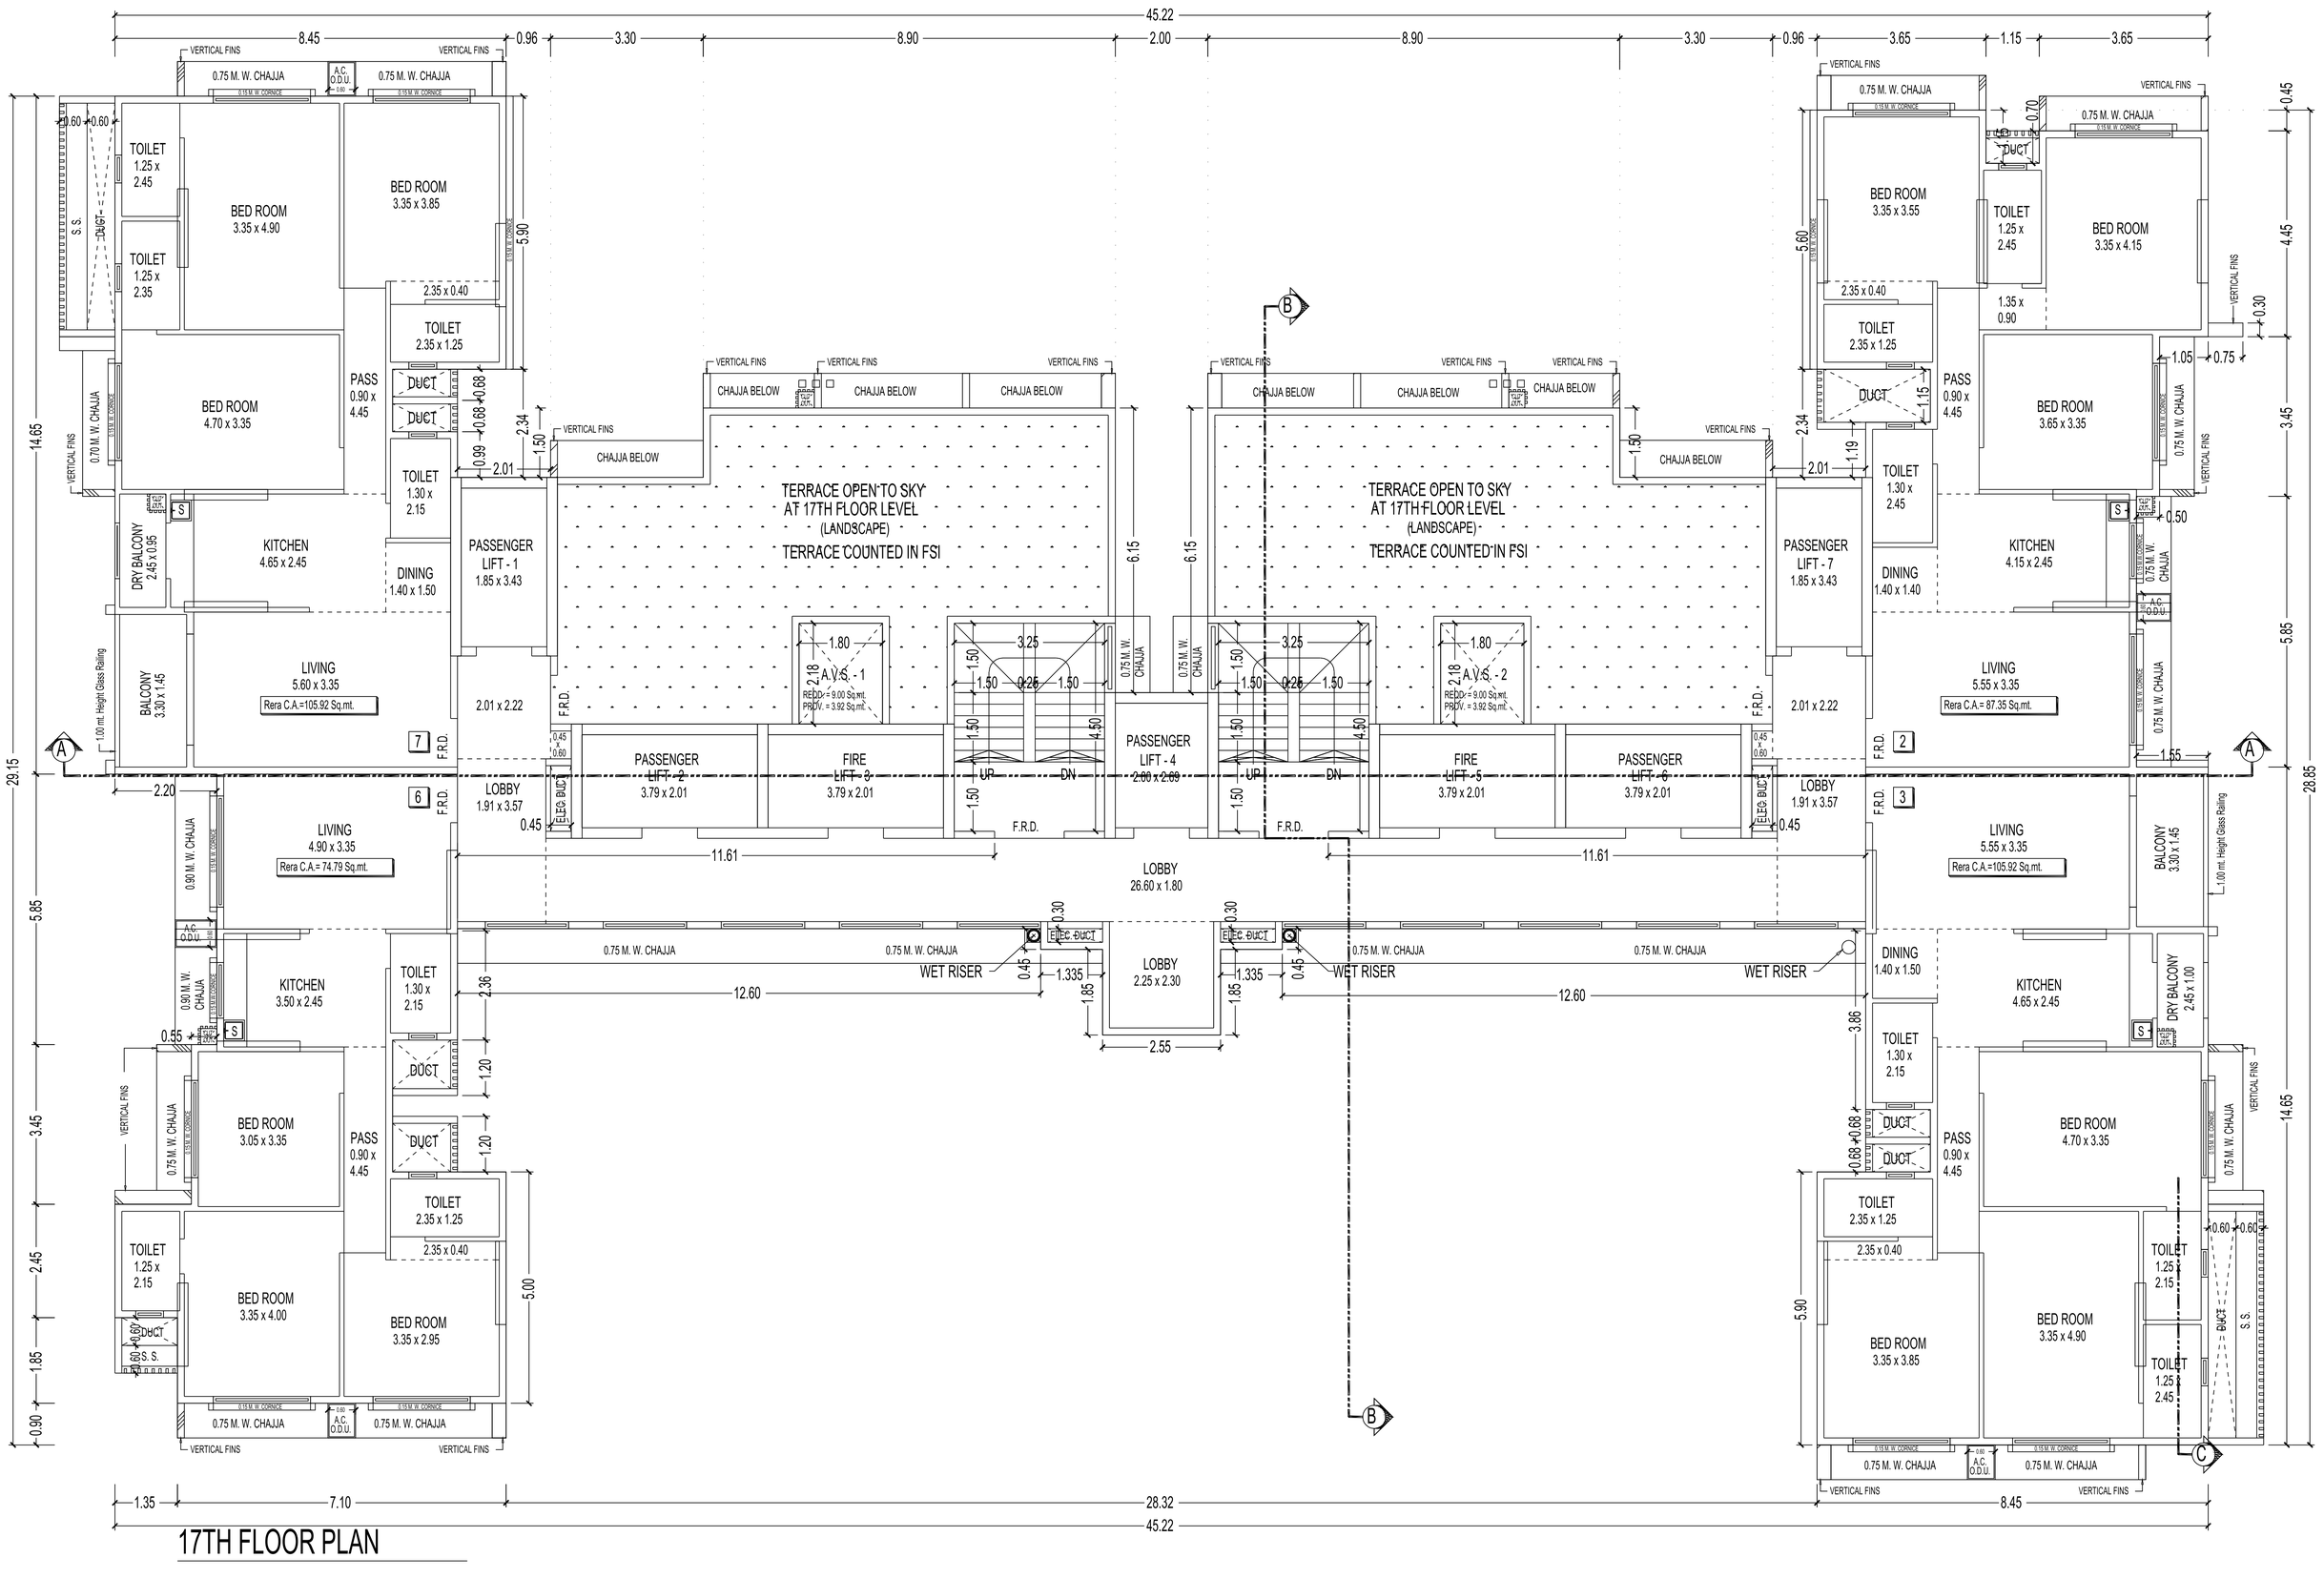


17TH FLOOR PLAN

SCALE - 1:100


FLAT NO. 1

SCALE - 1:100

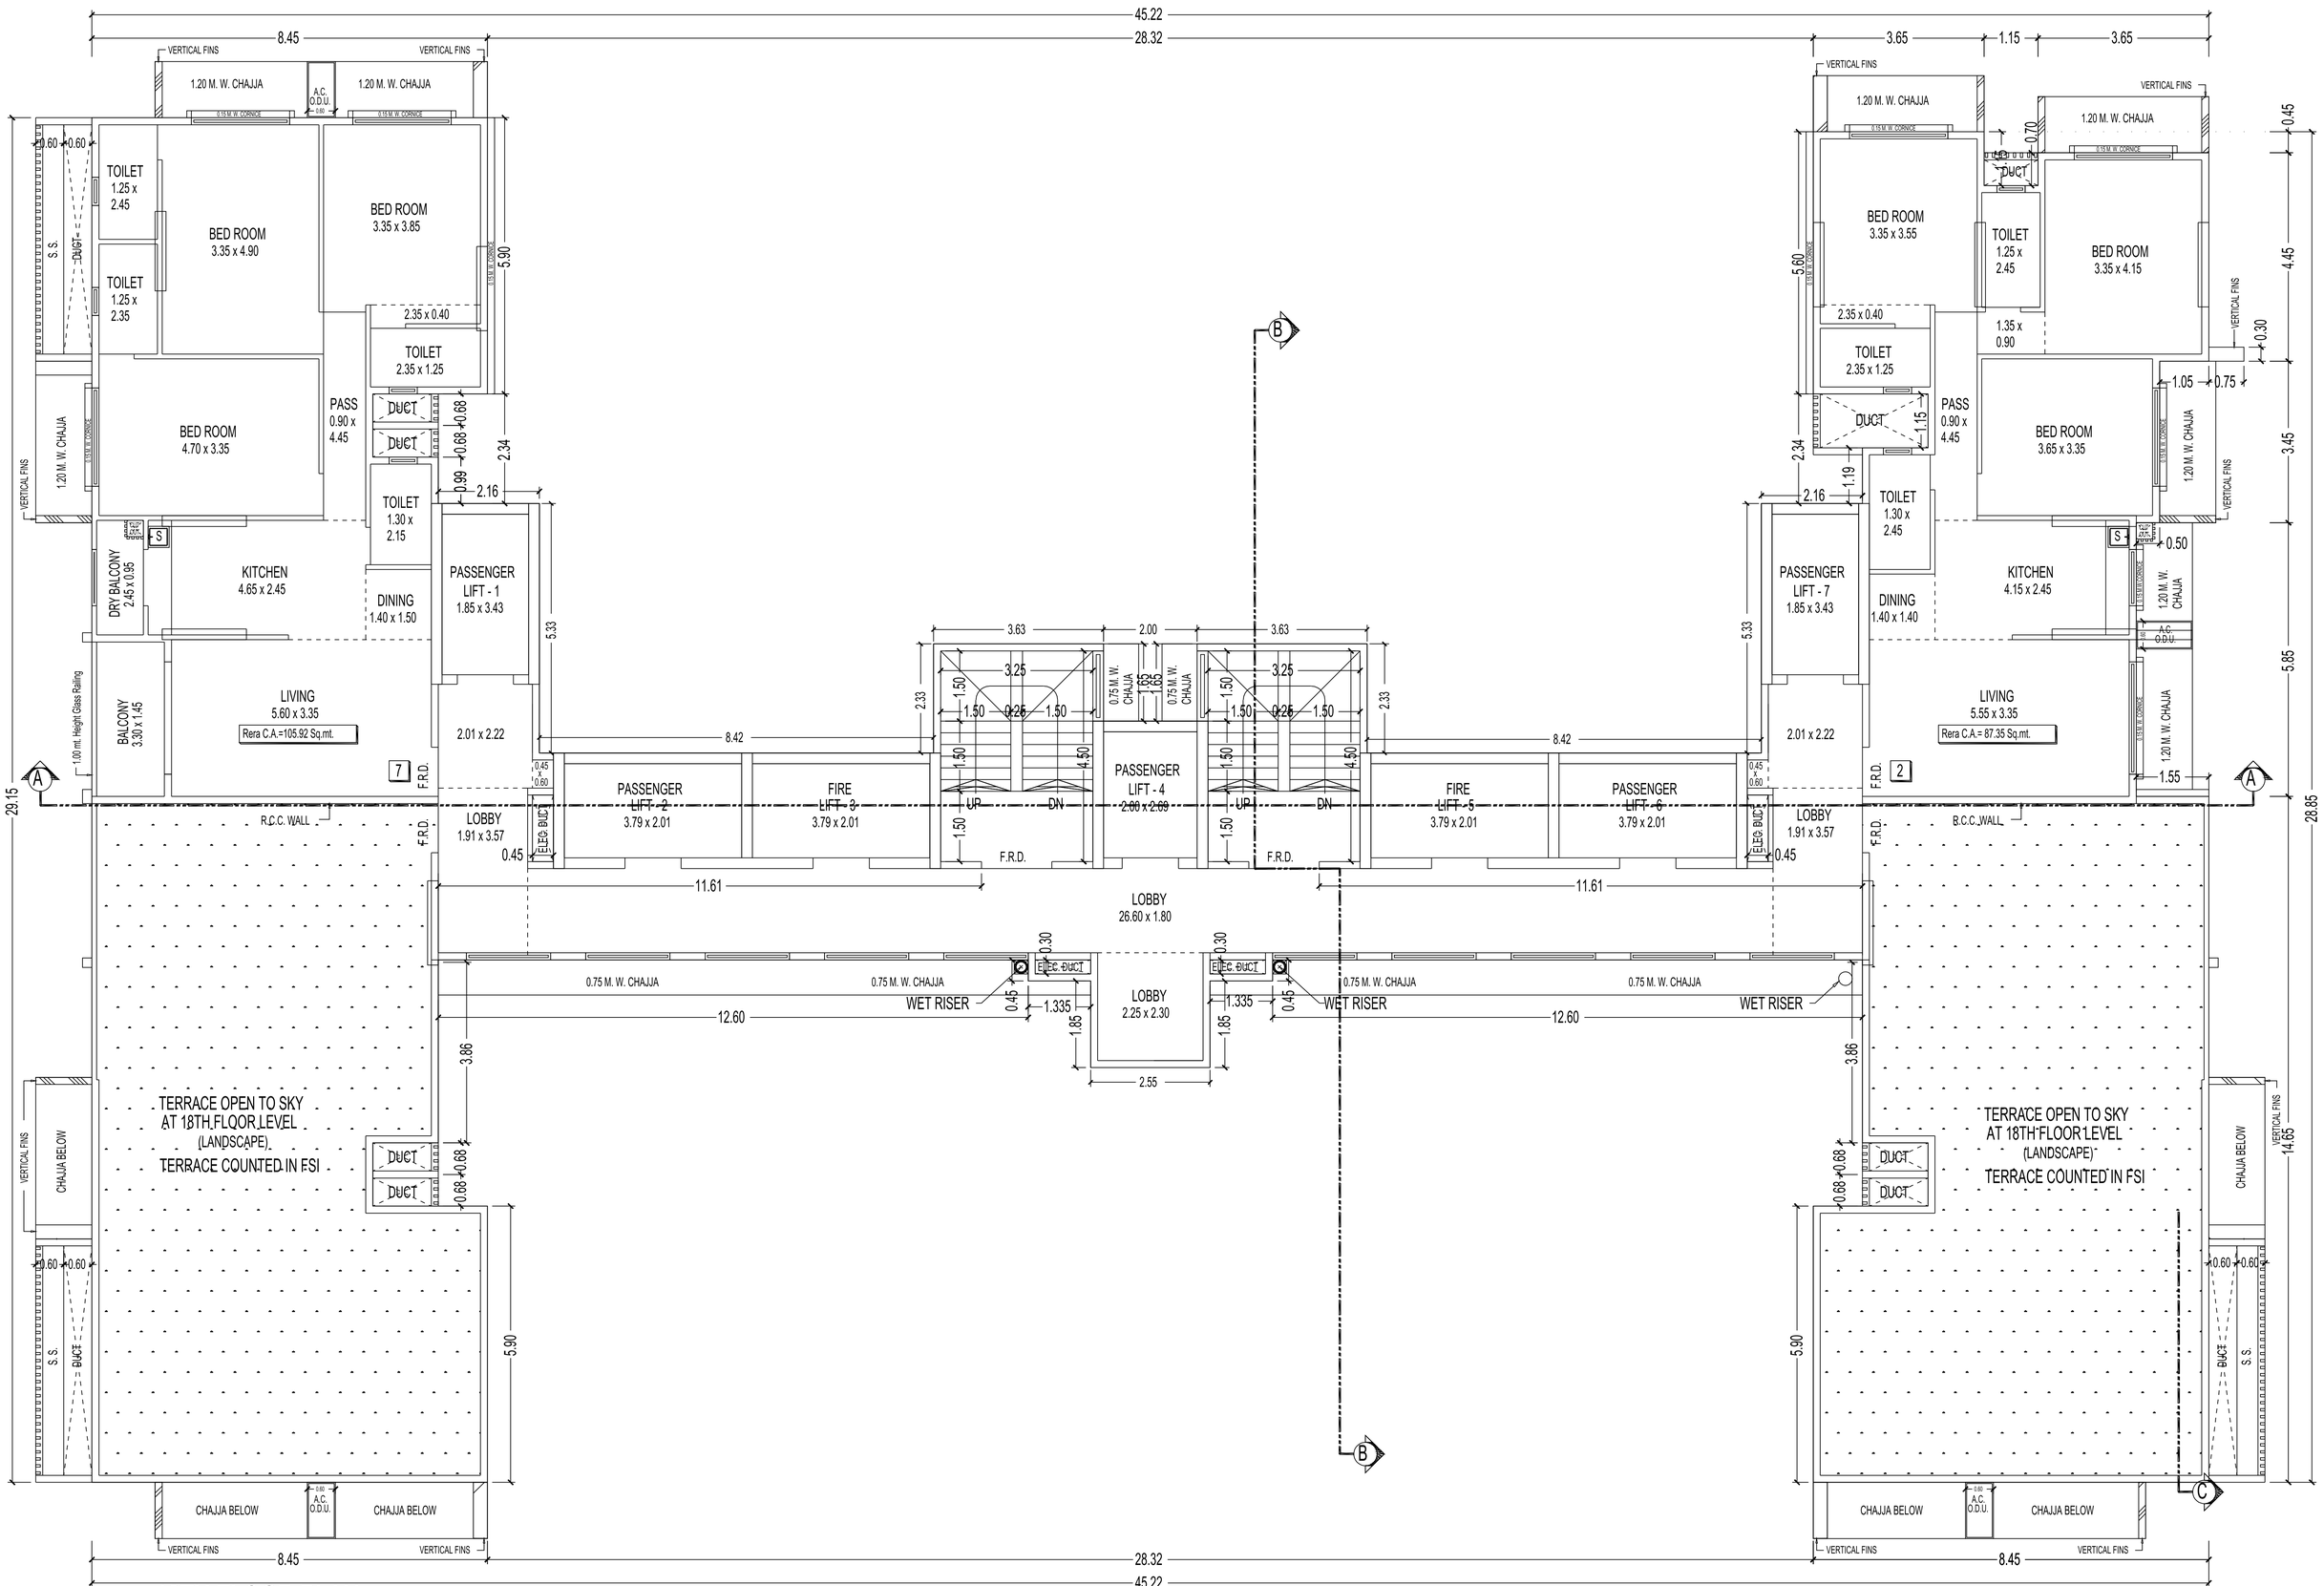

18TH FLOOR PLAN

SCALE - 1:100

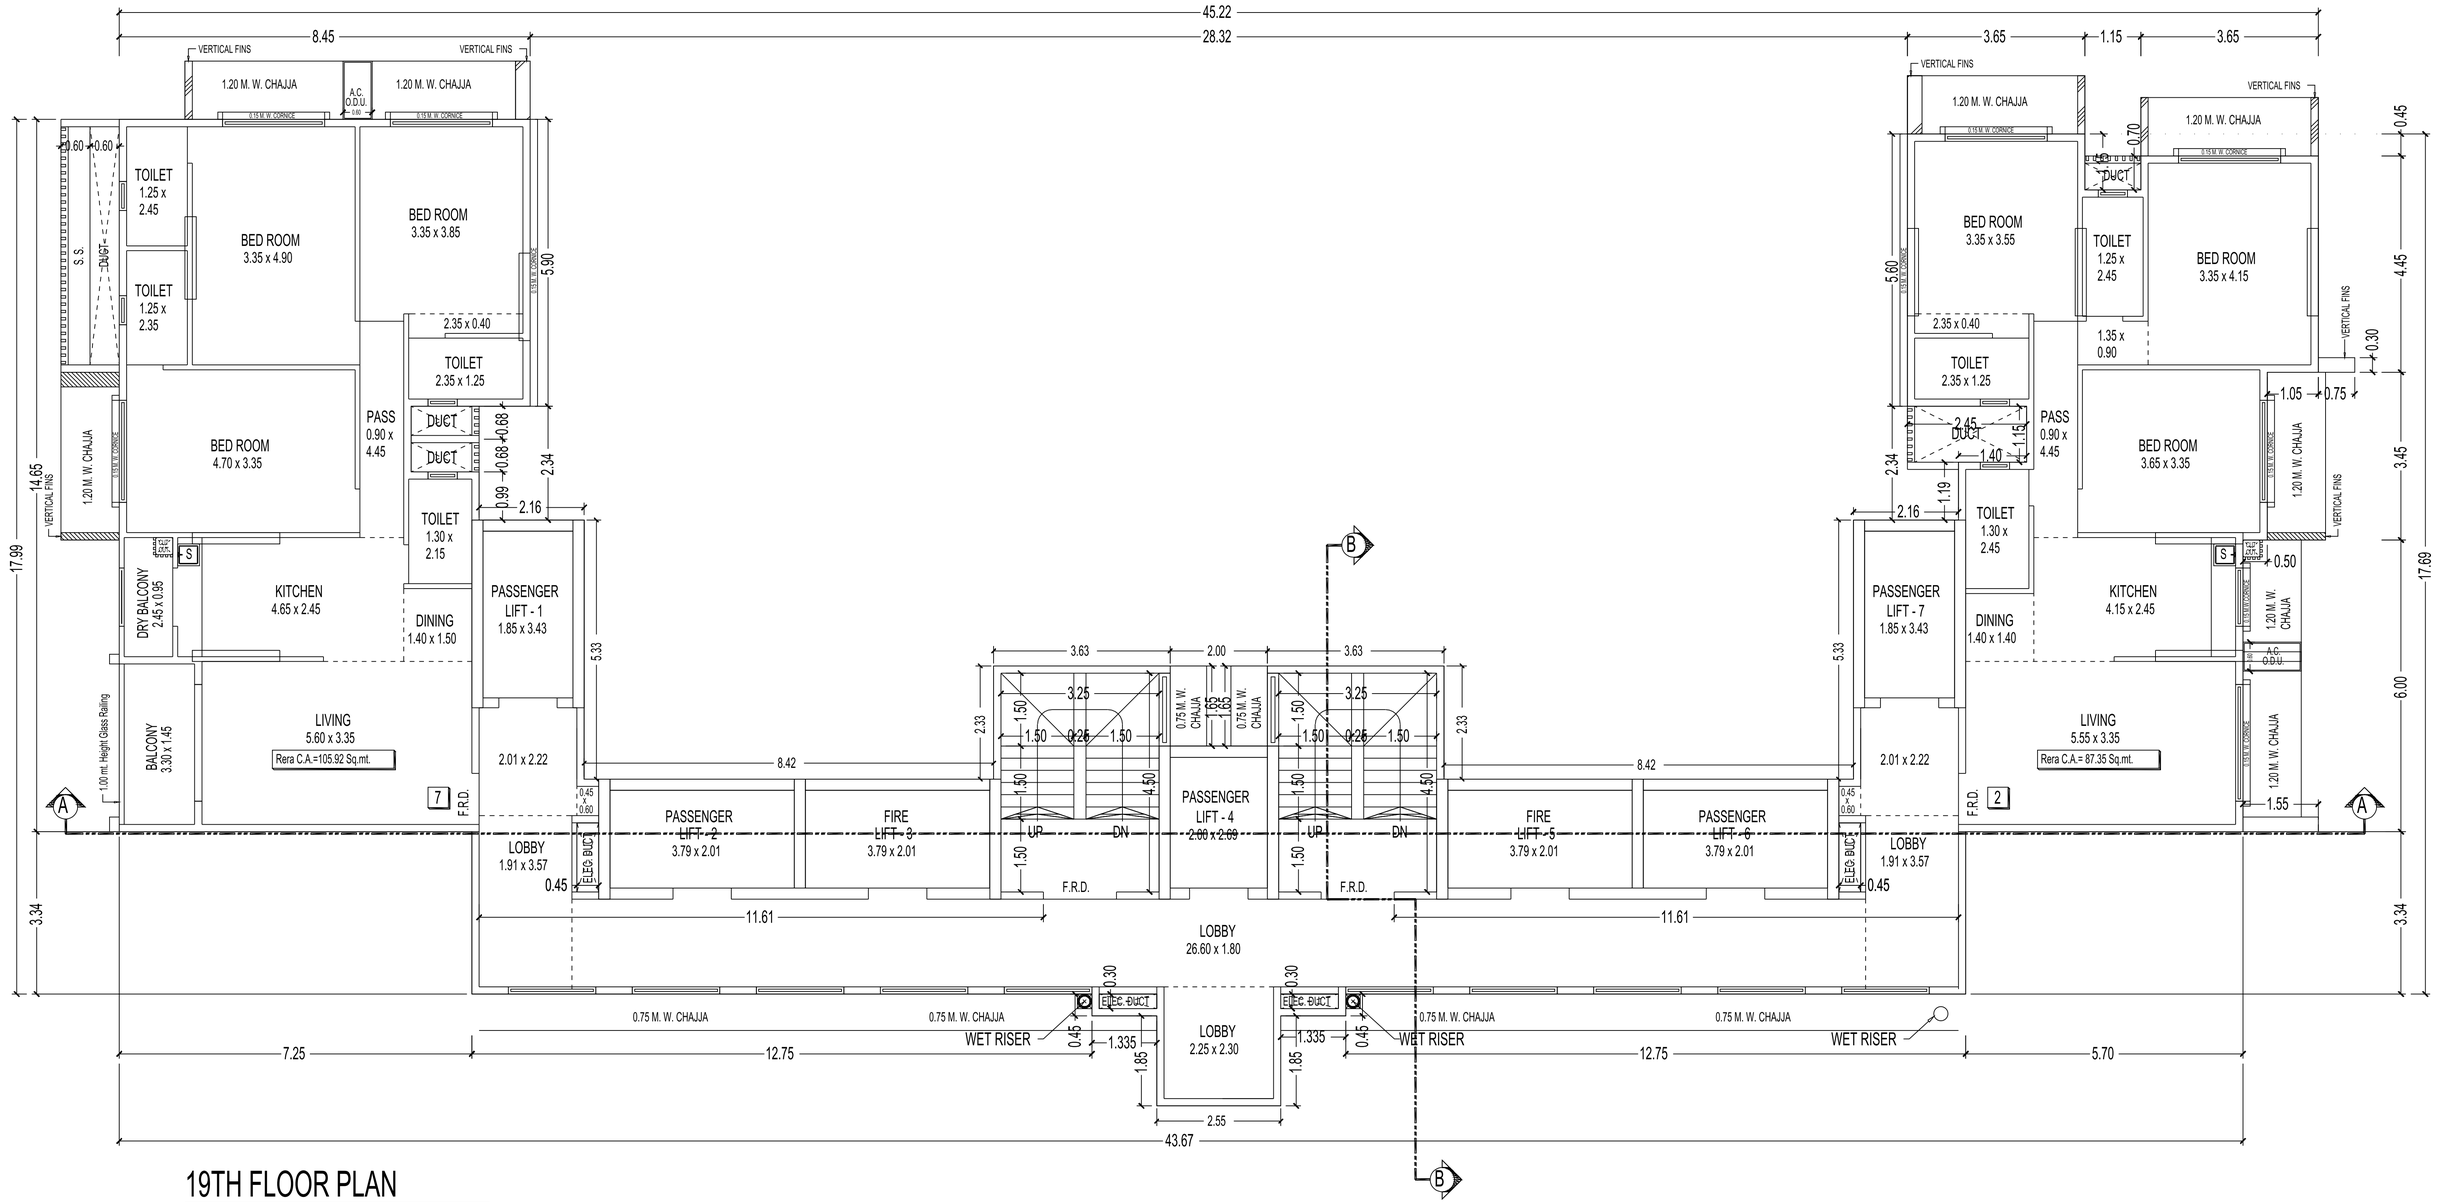

19TH FLOOR PLAN

SCALE - 1:100