

SCALE :- 1:100

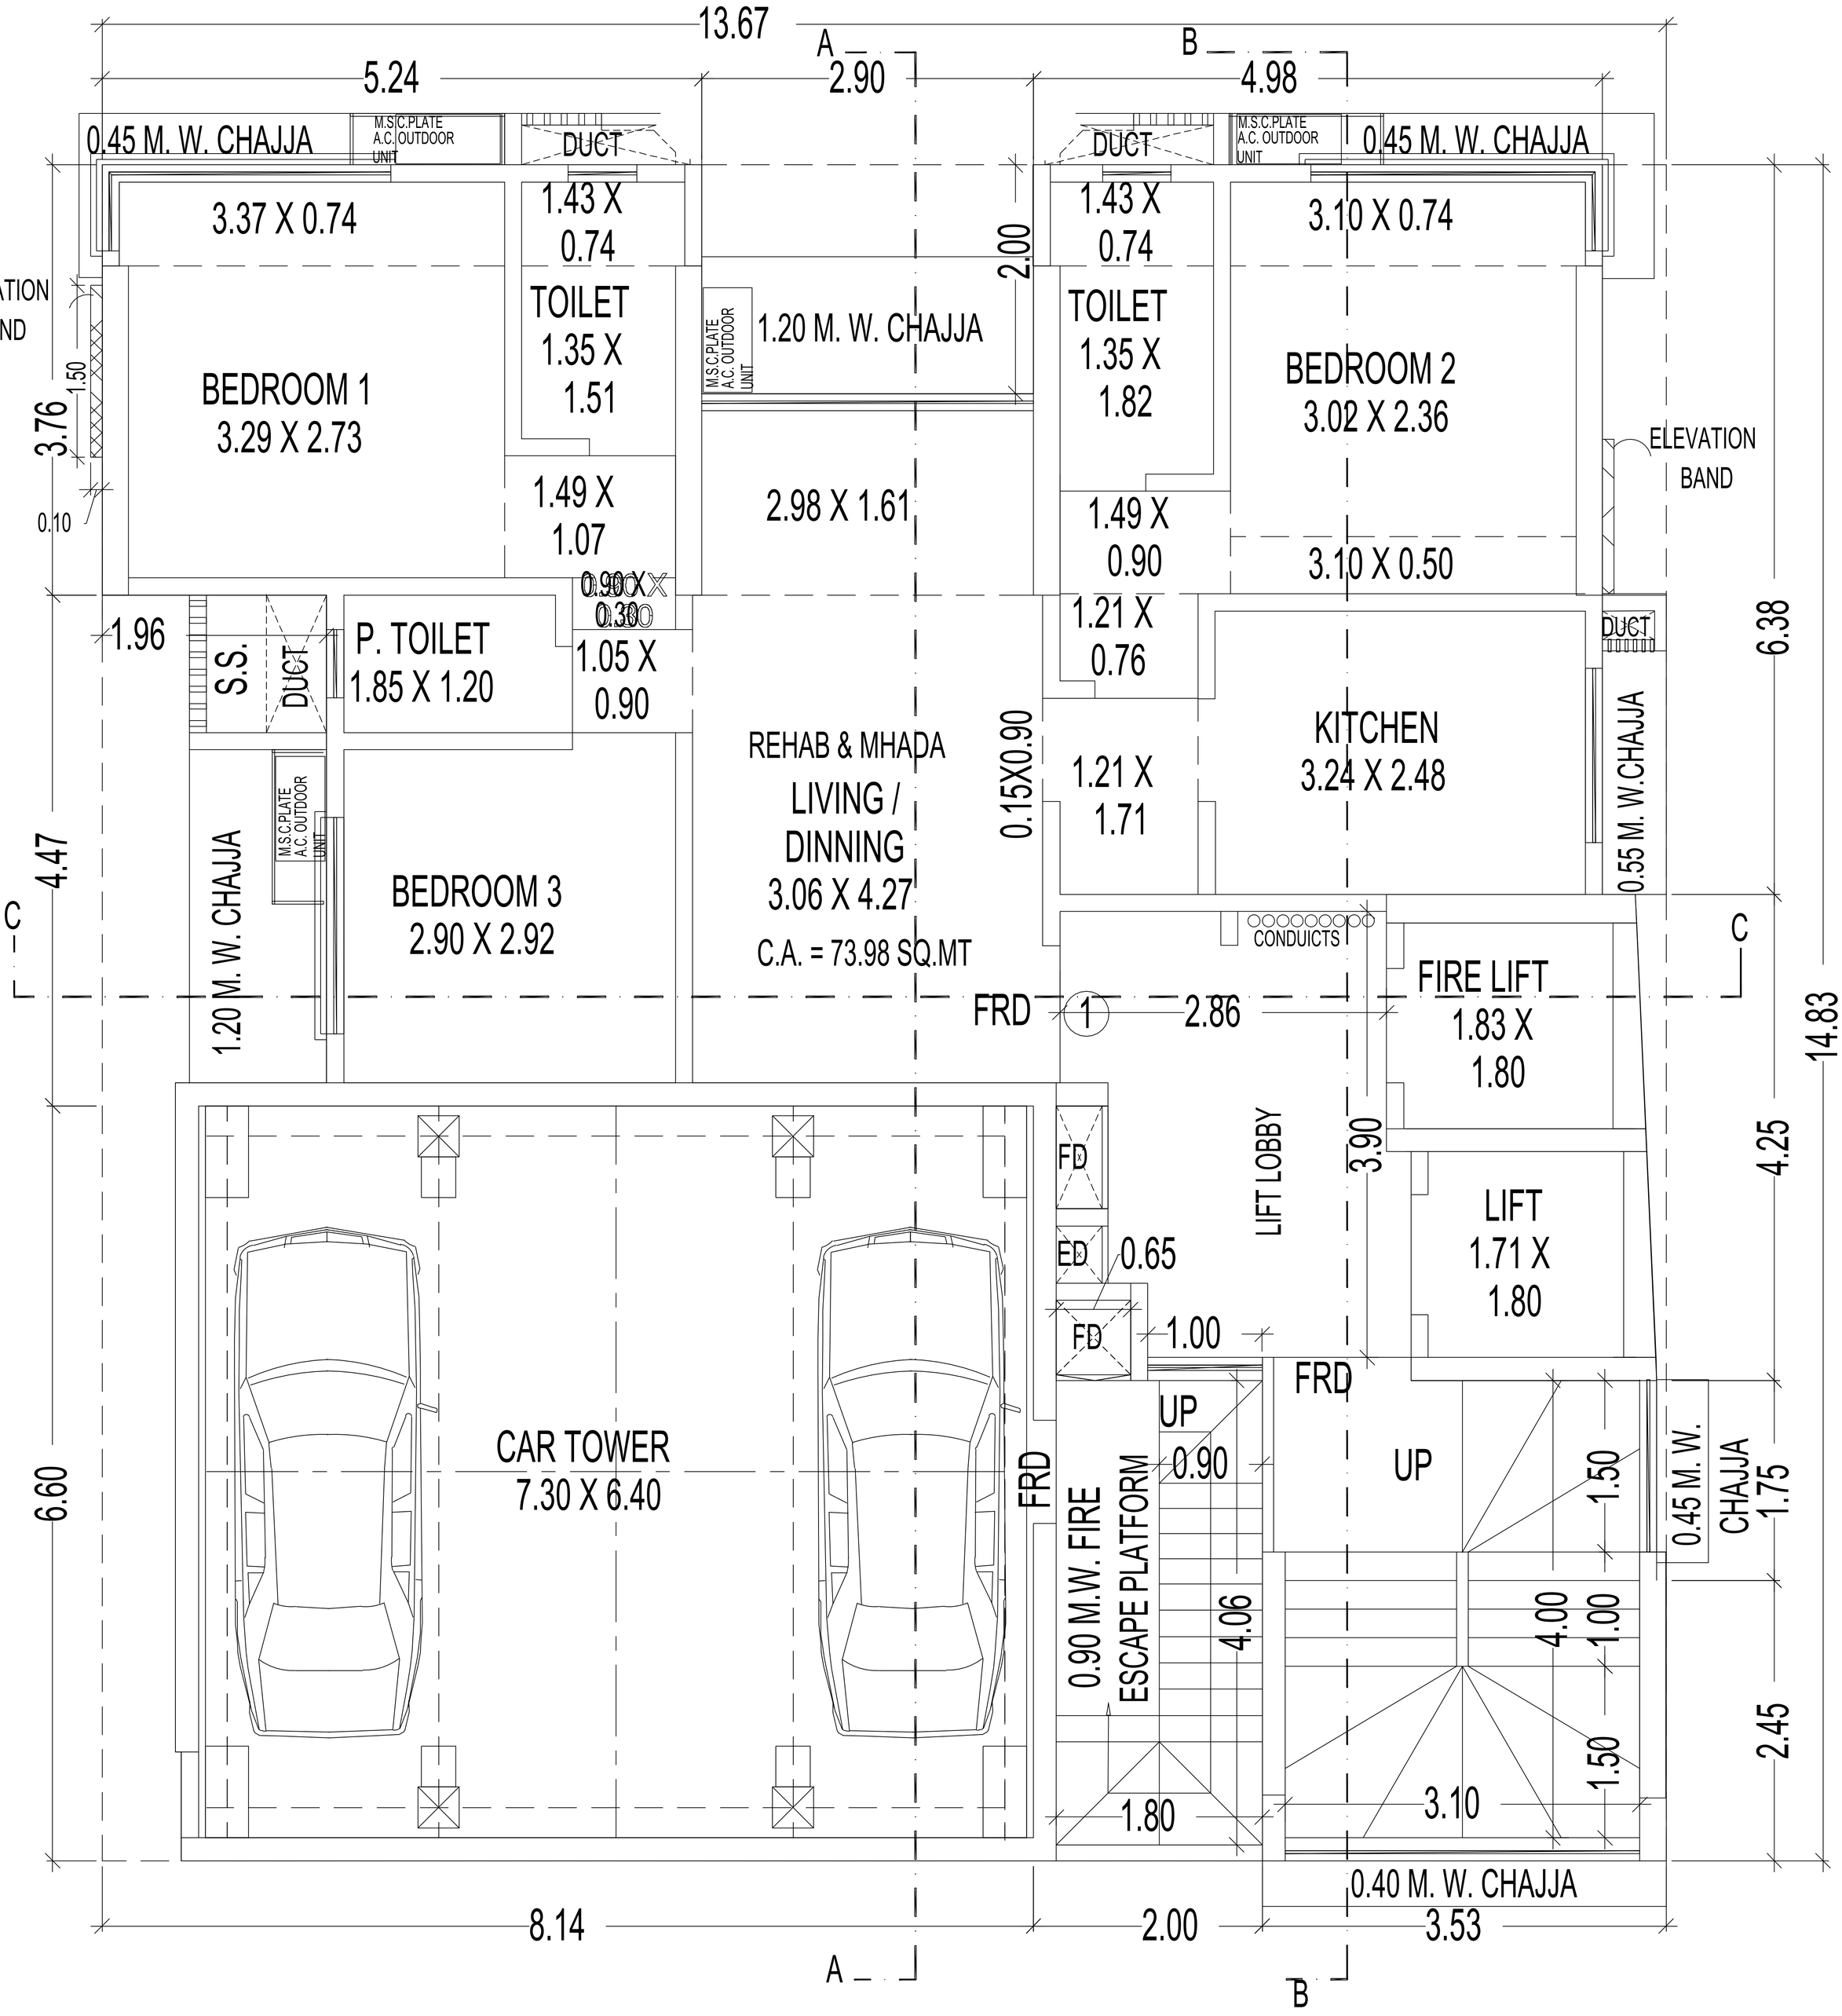

1ST & 2ND FLOOR PLAN


SCALE :- 1:100

NOTE :- FLAT NO 101 MHADA FLAT

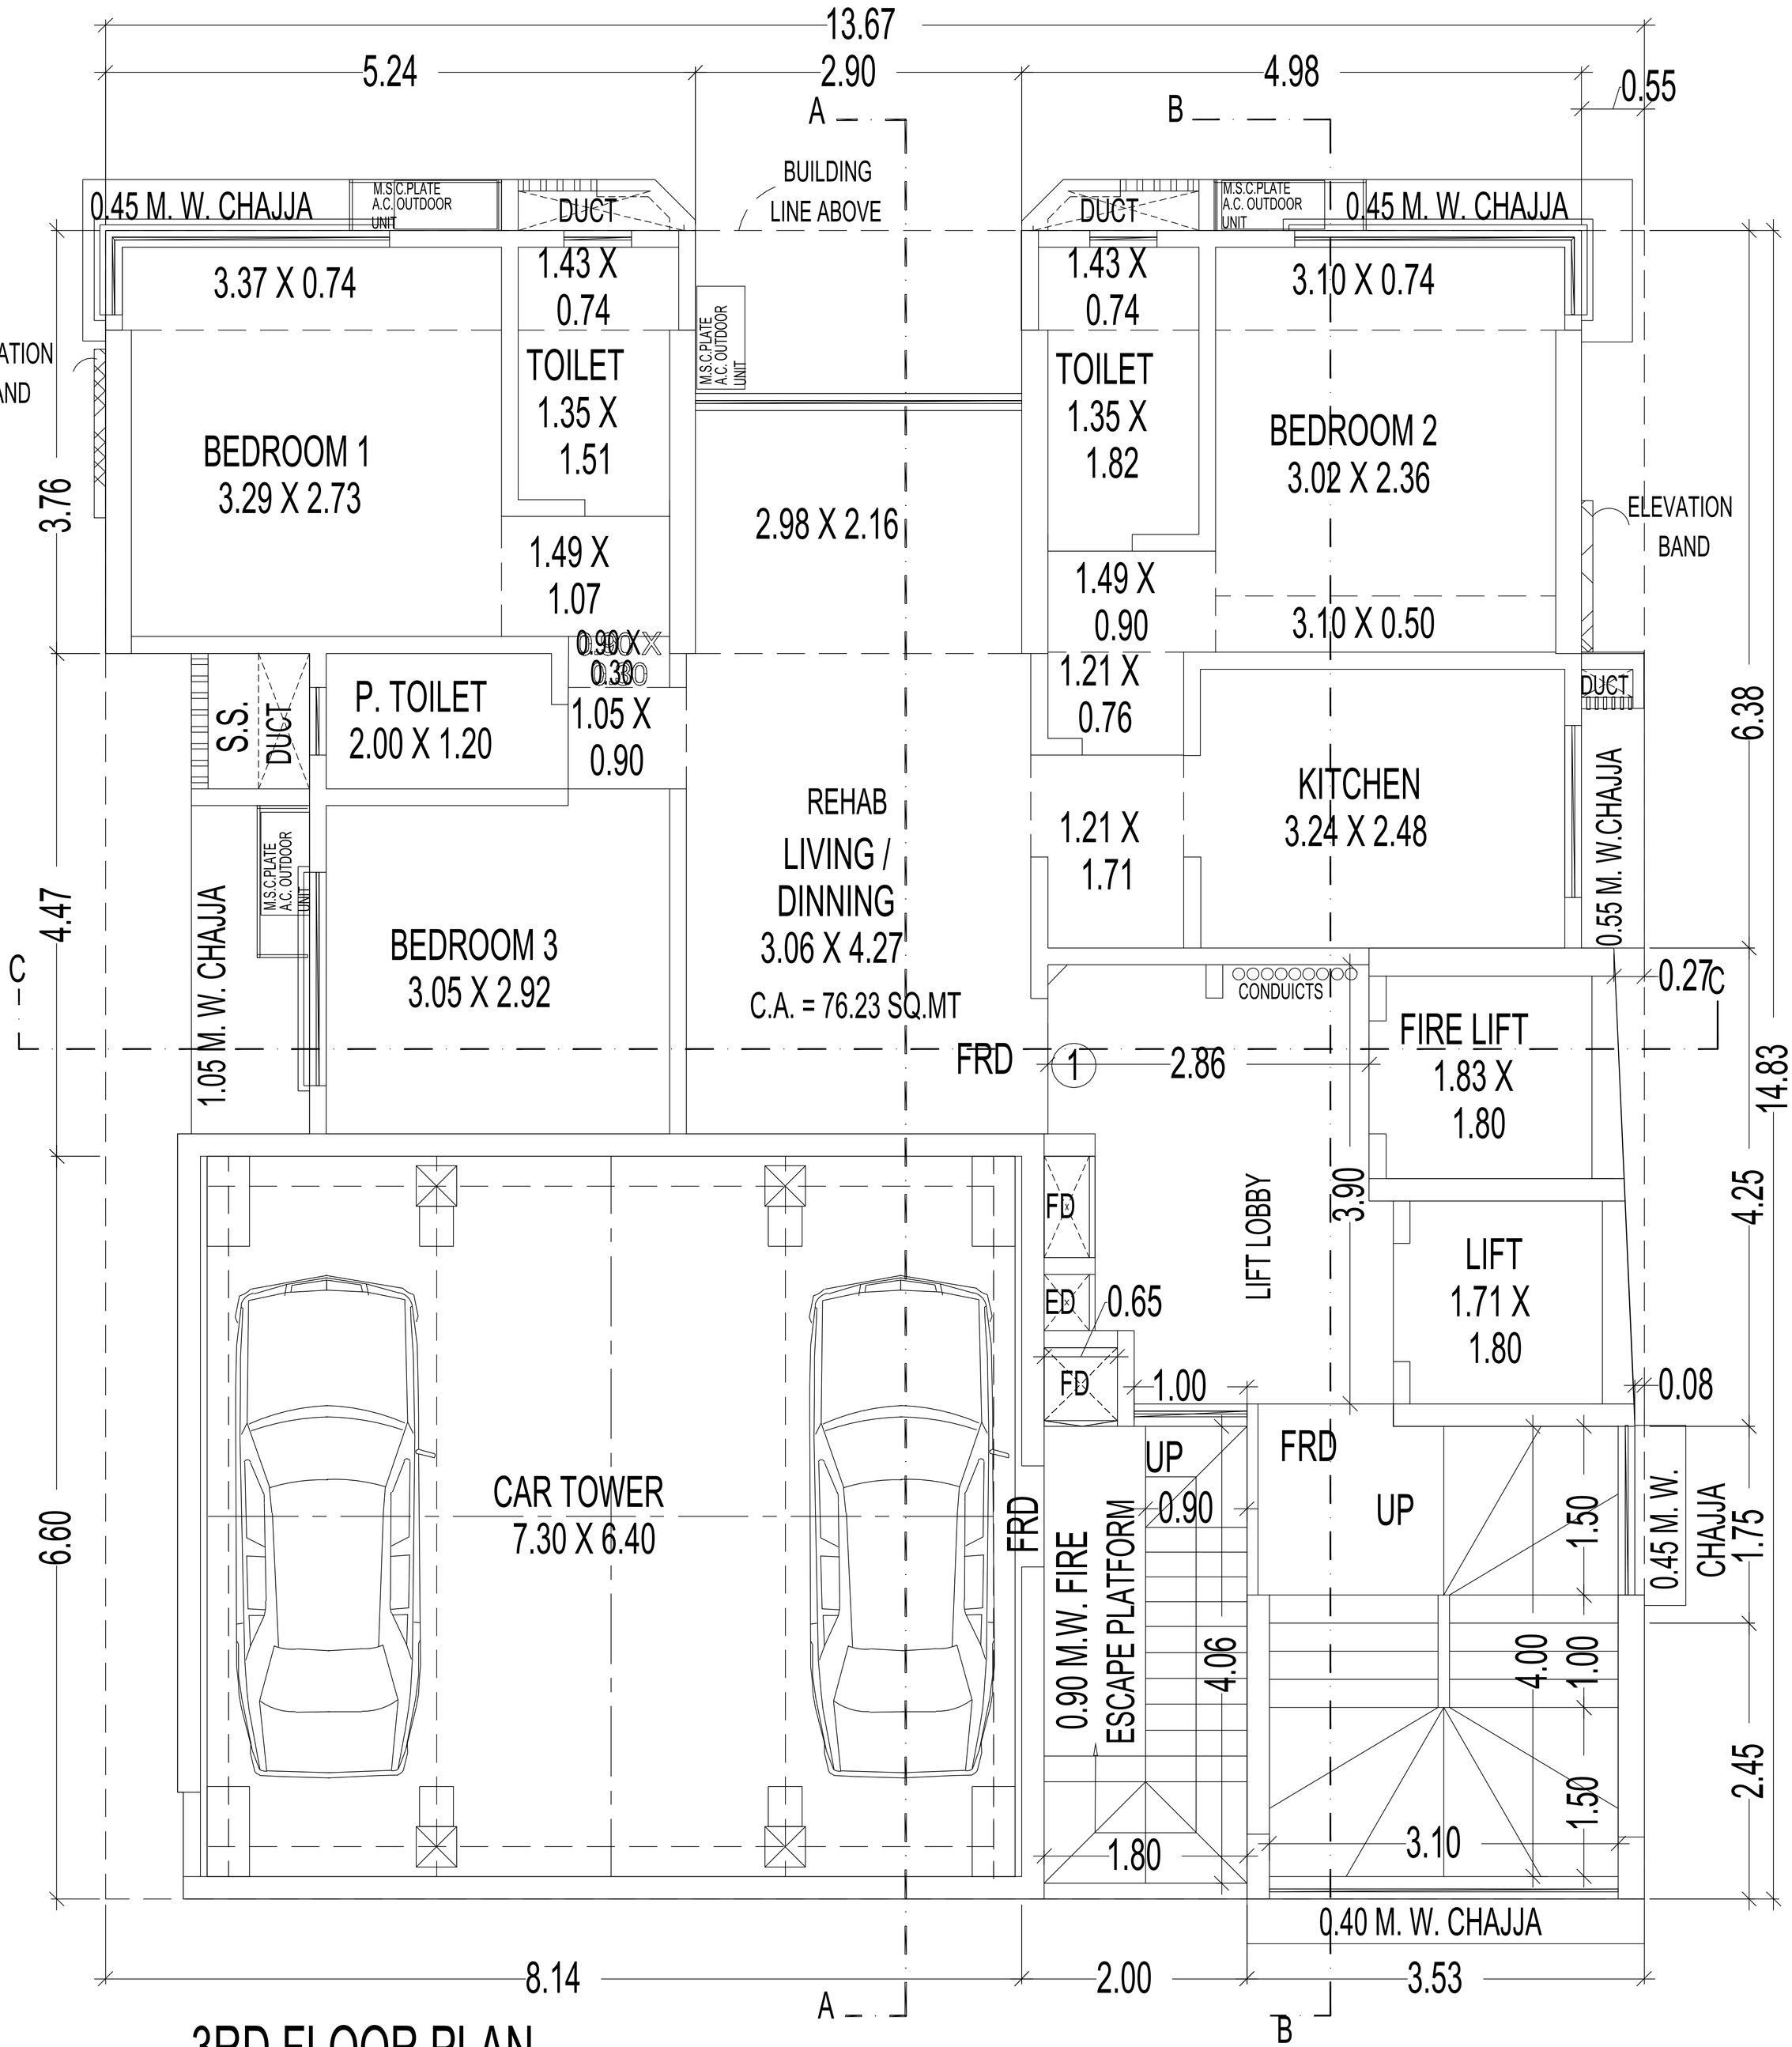


3RD FLOOR PLAN

SCALE :- 1:100

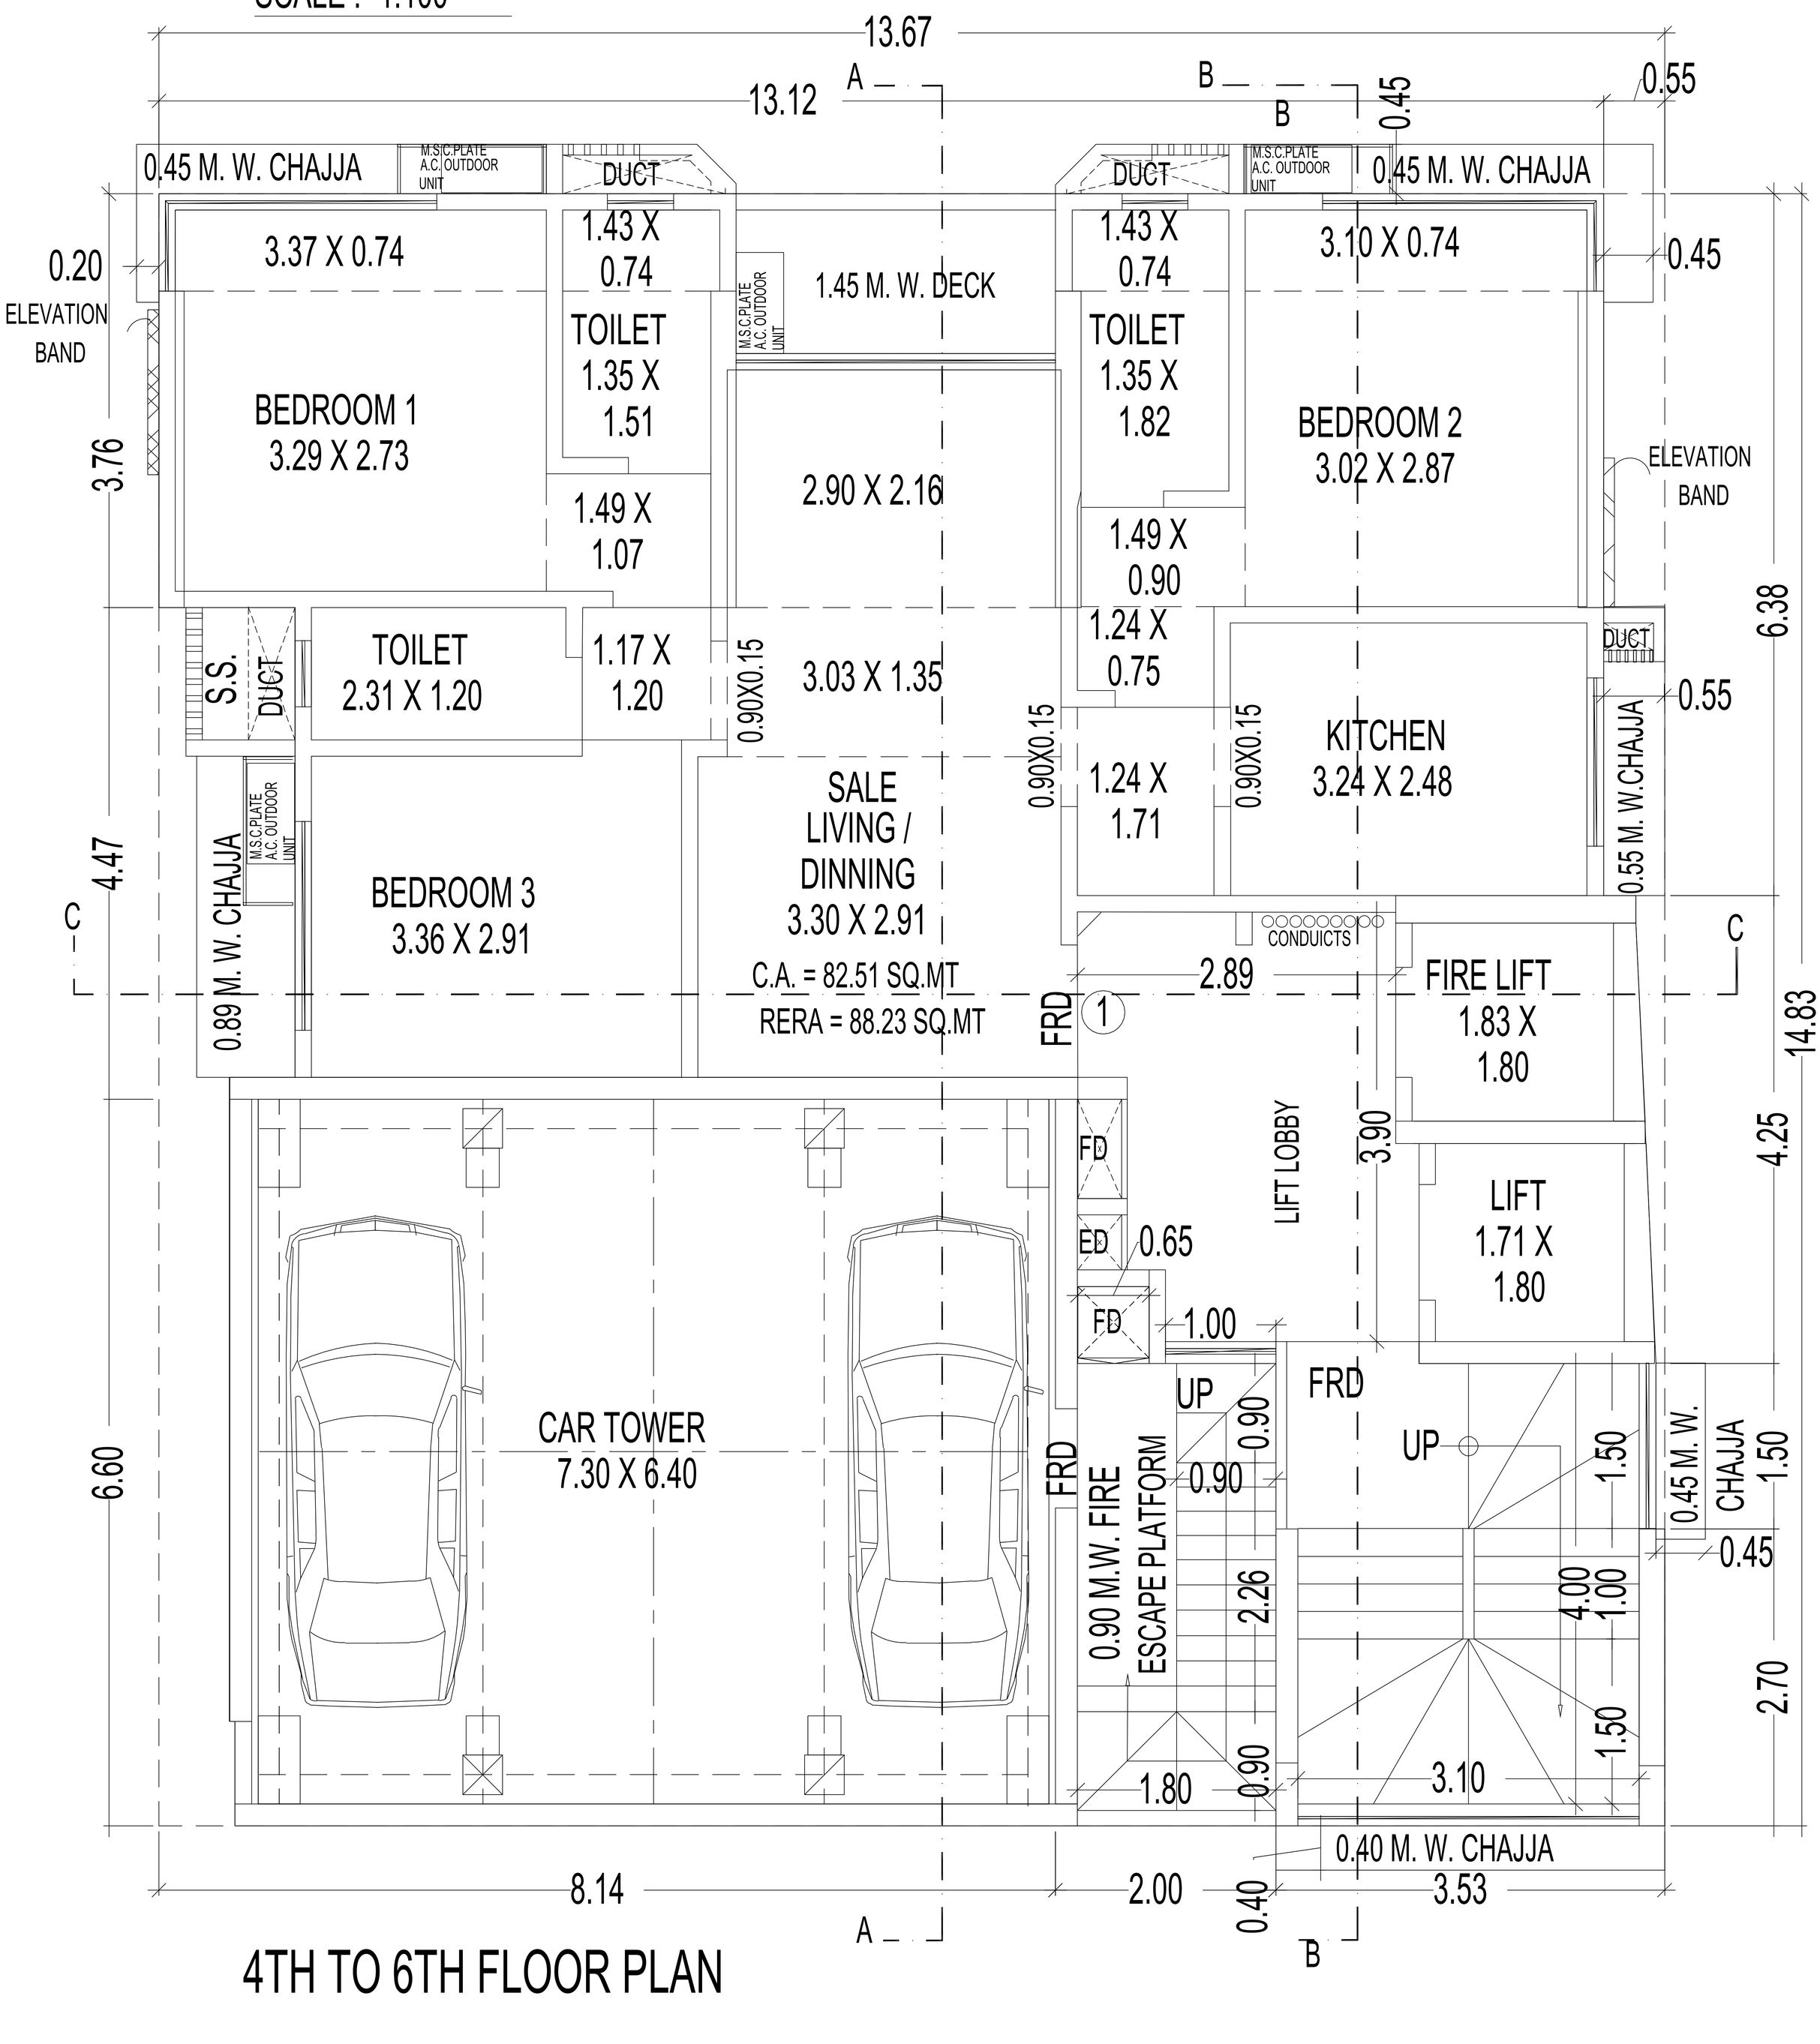


4TH TO 6TH FLOOR PLAN

SCALE :- 1:100

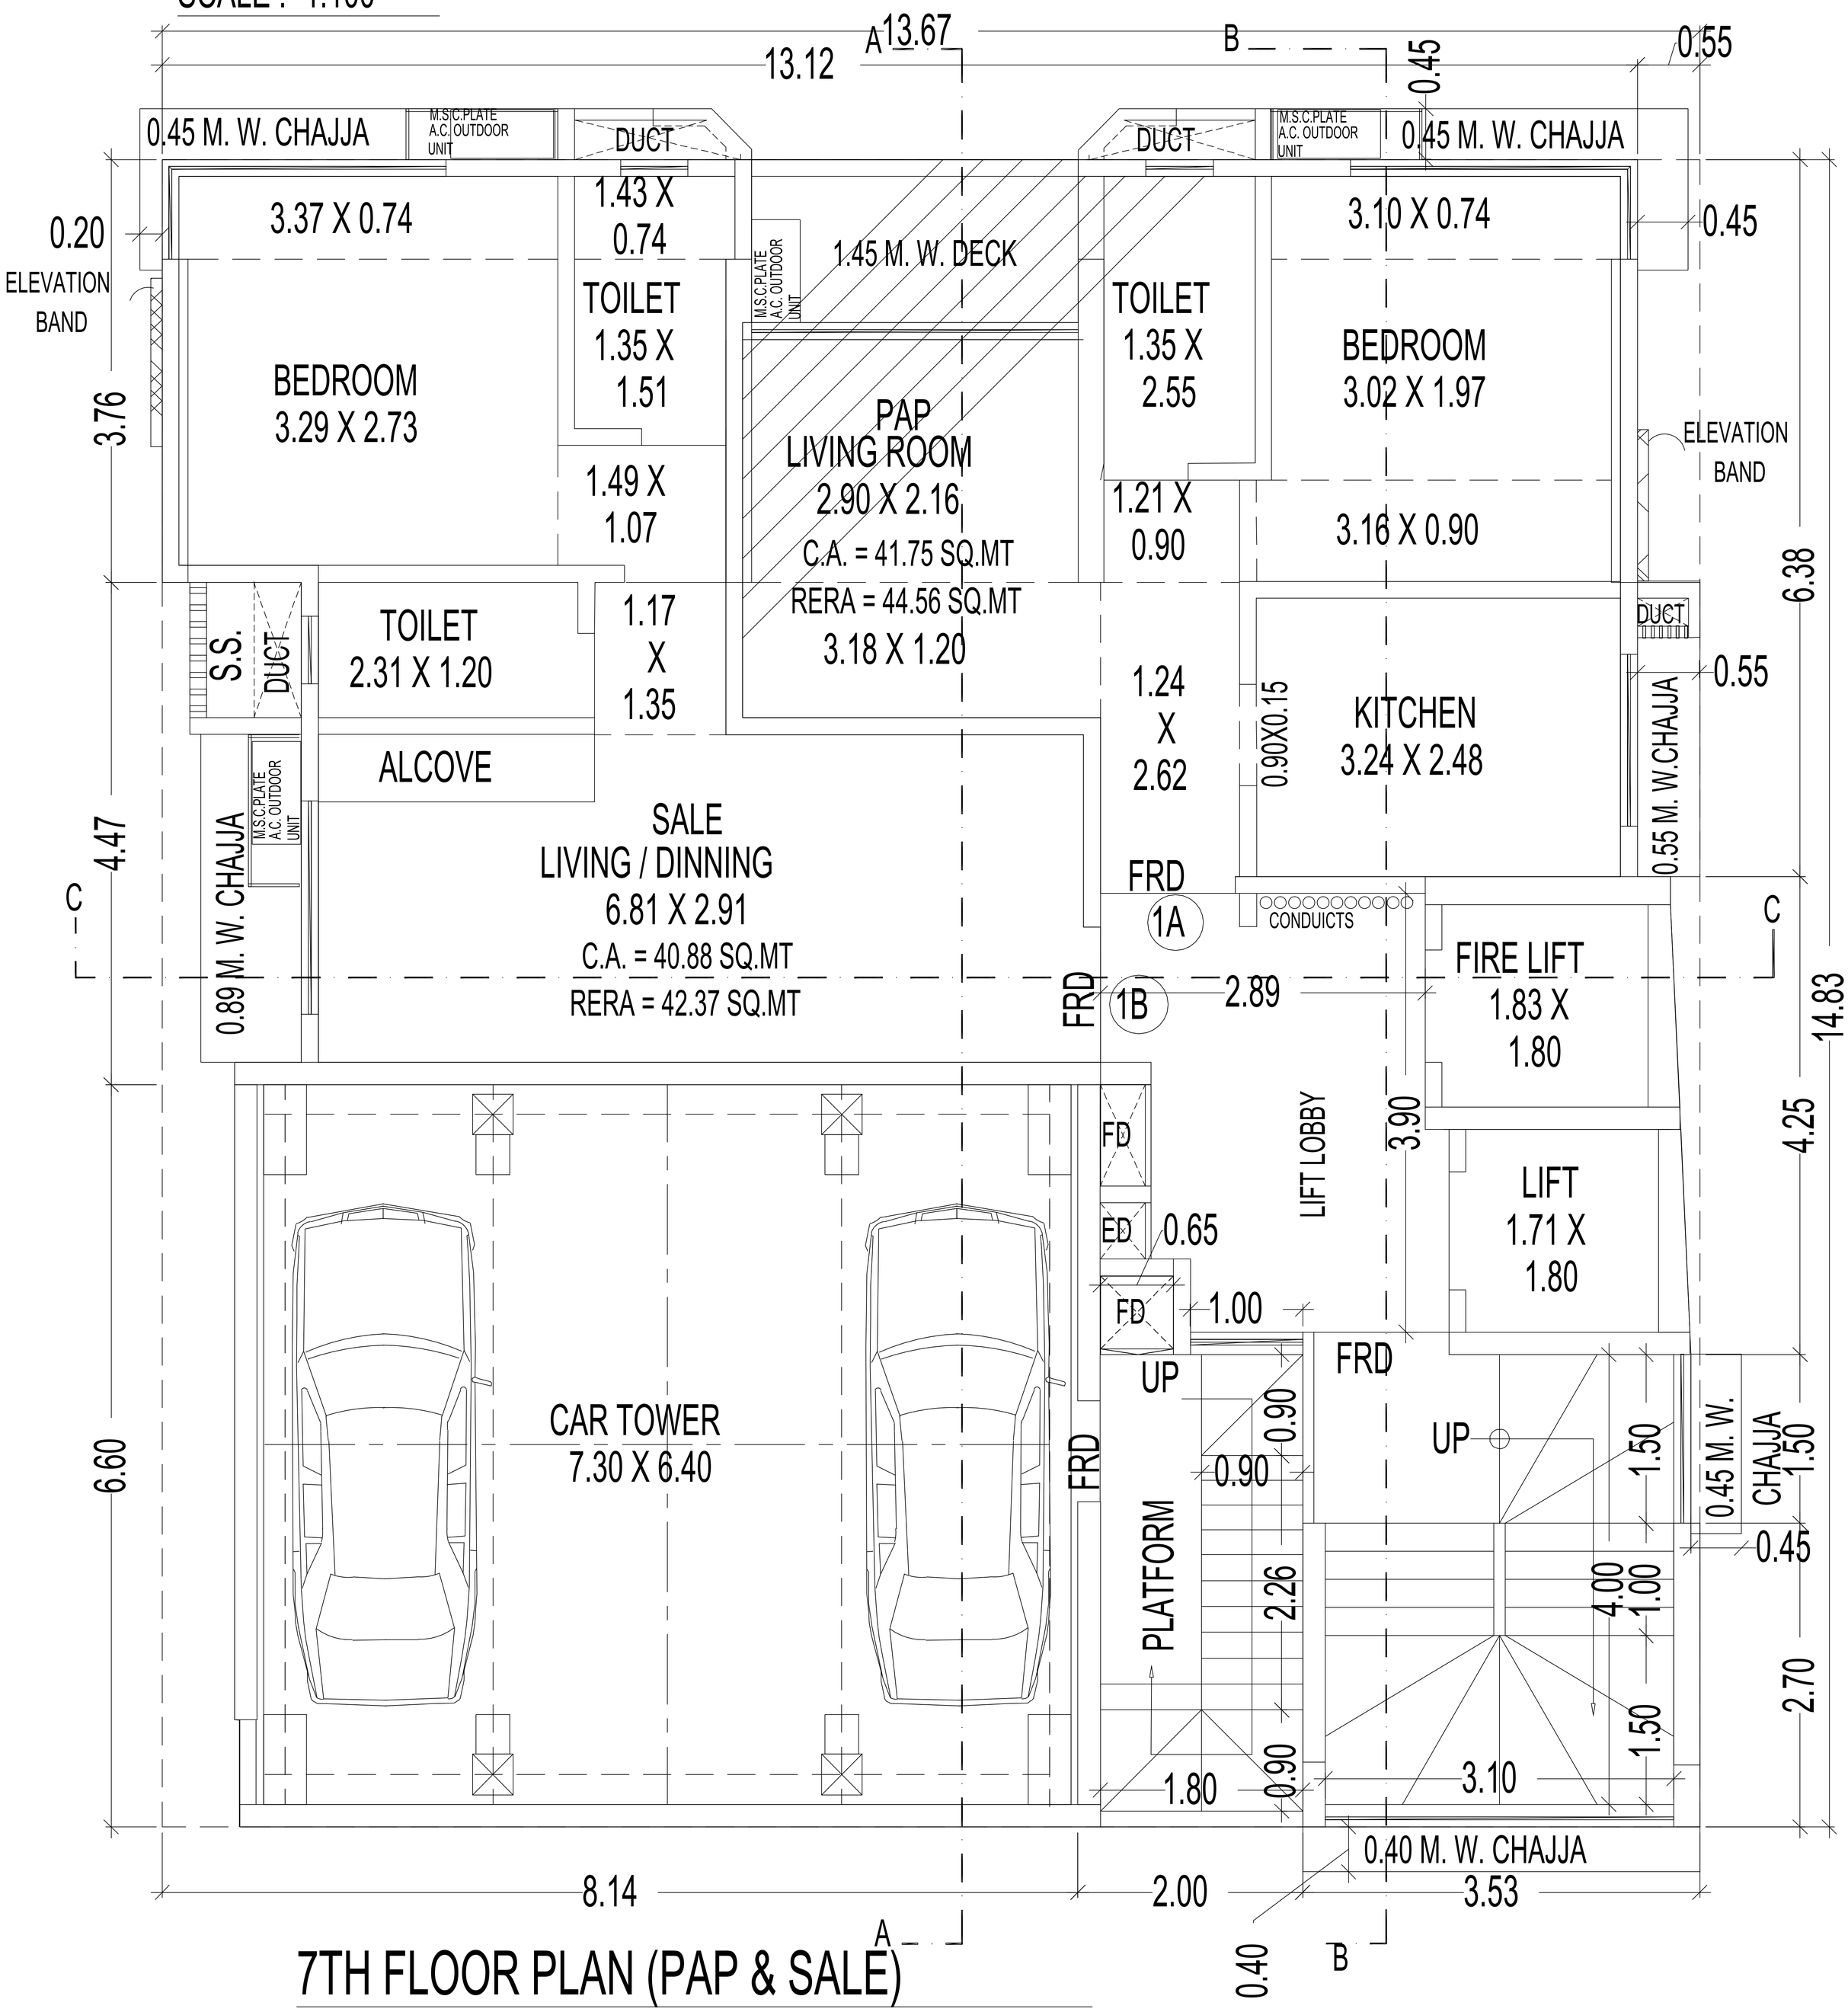


7TH FLOOR PLAN (PAP & SALE)

SCALE :- 1:100

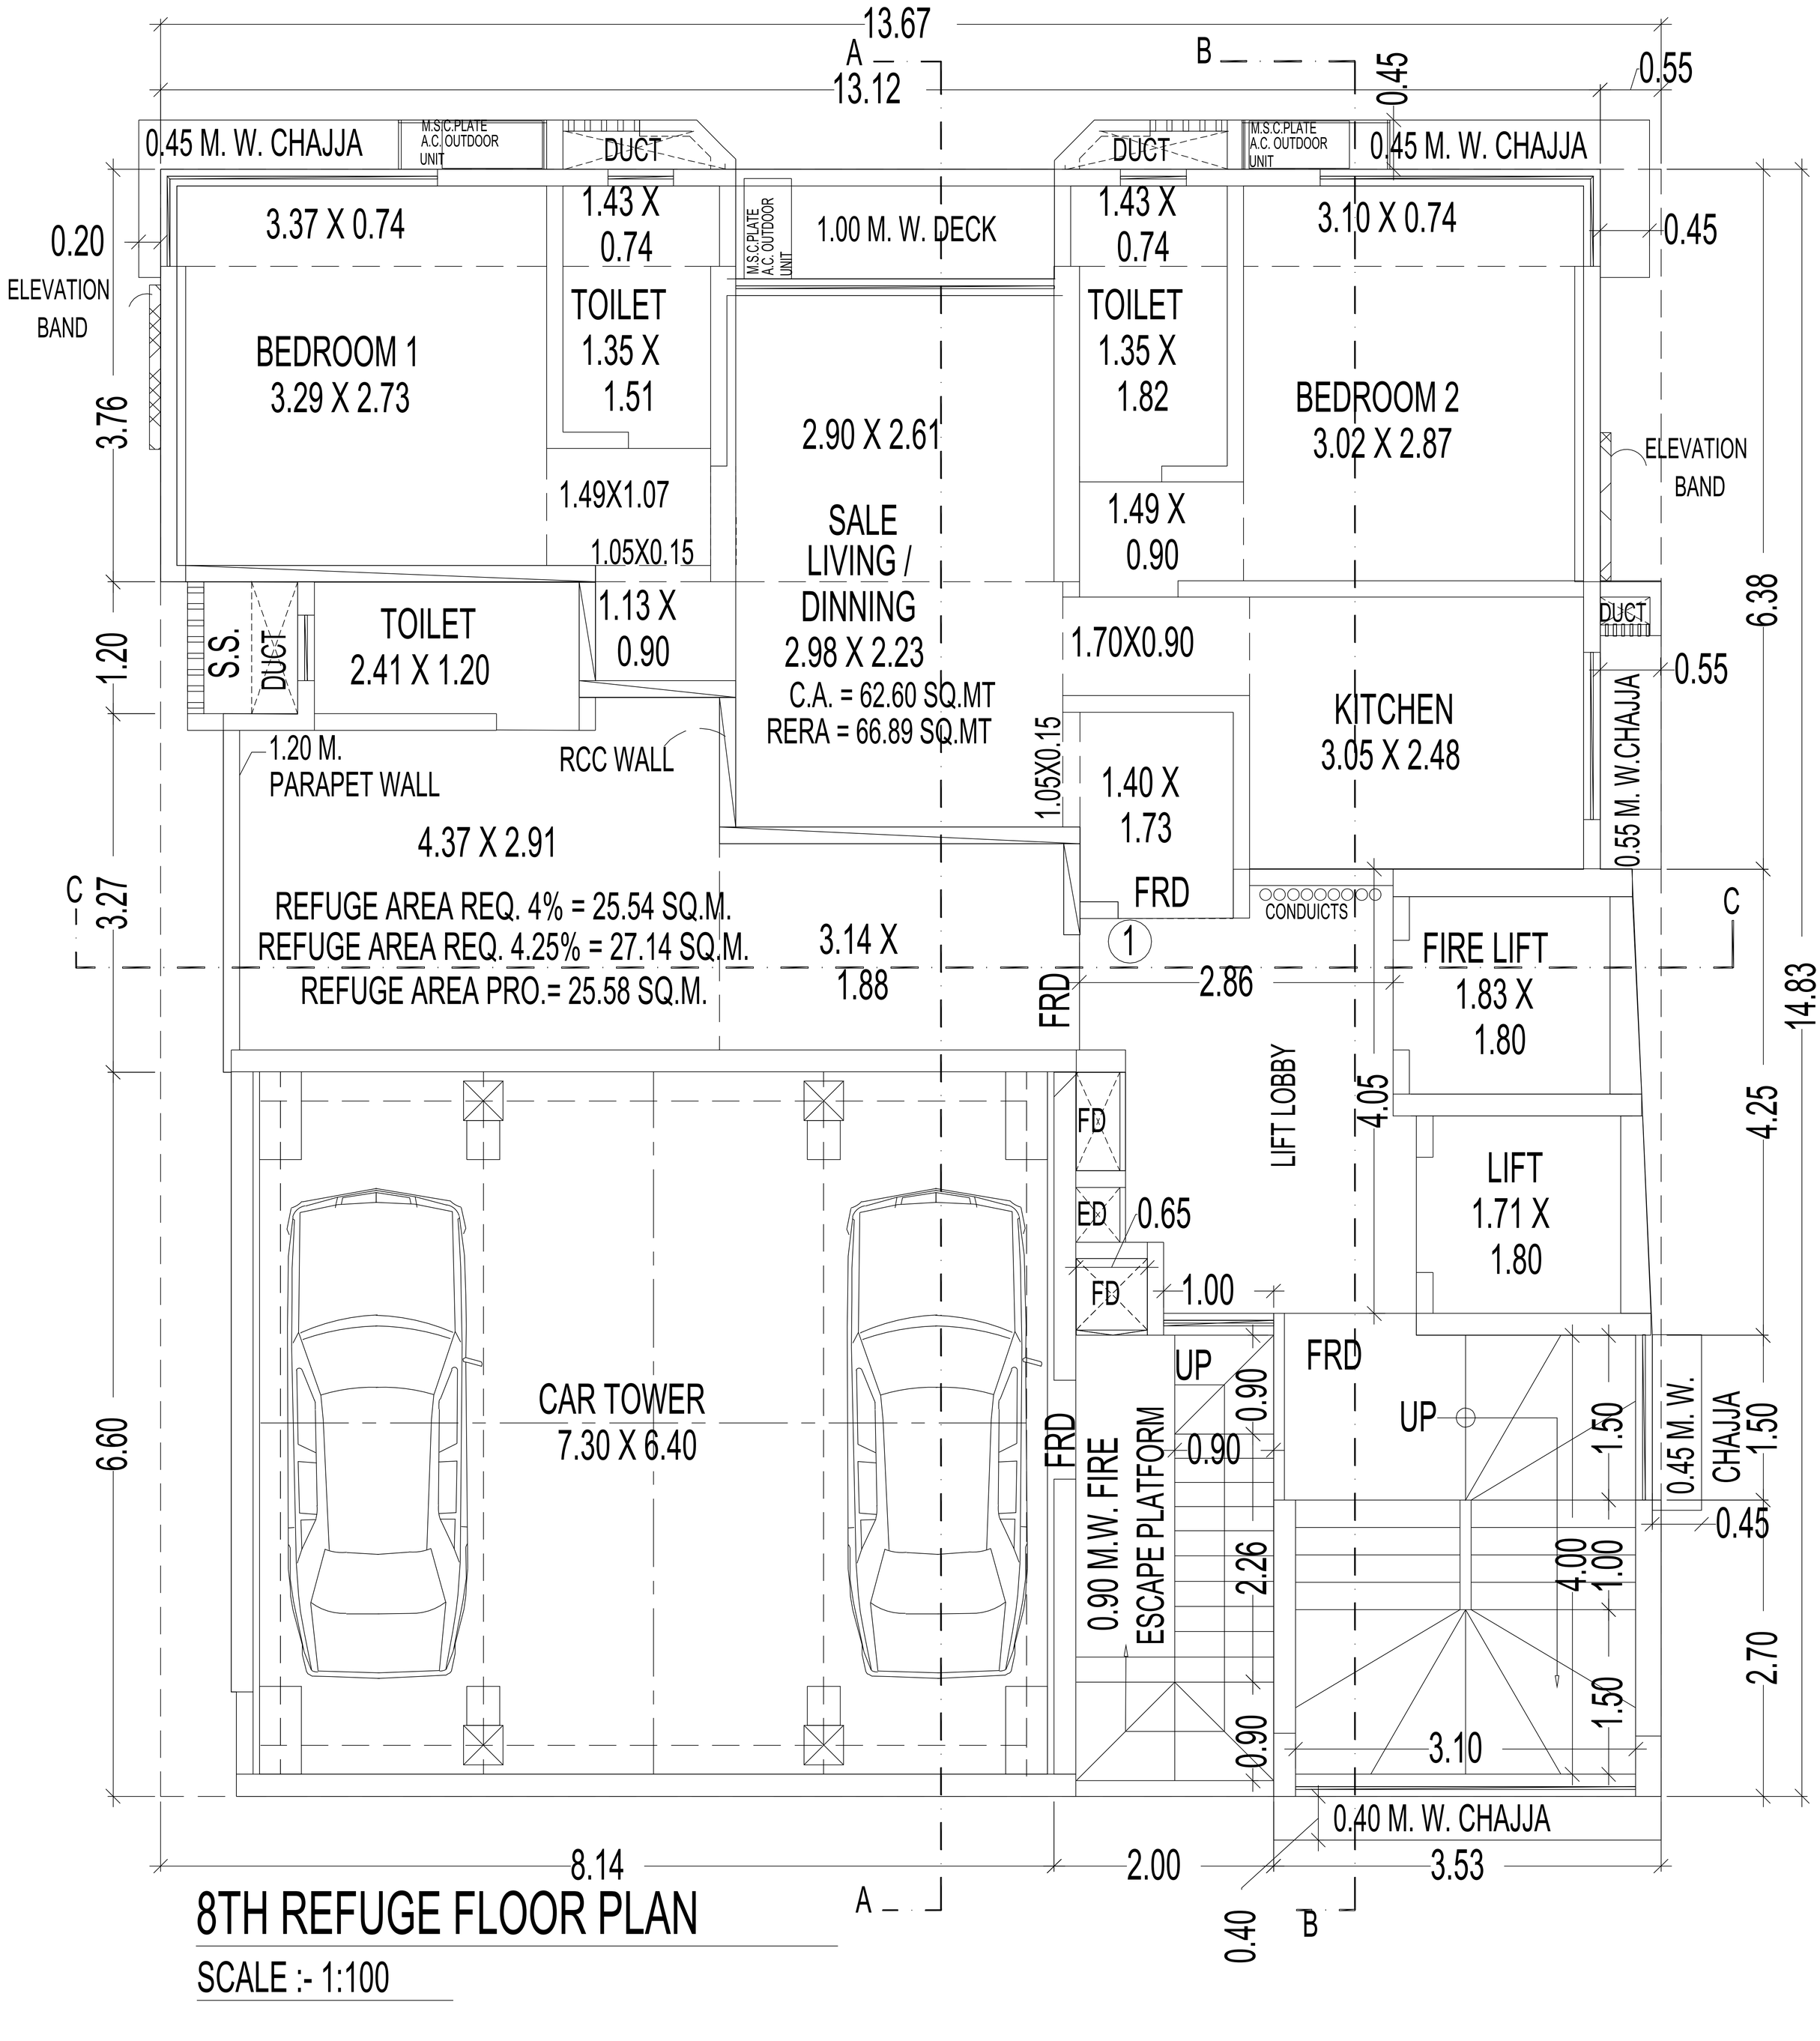


8TH REFUGE FLOOR PLAN

SCALE :- 1:100

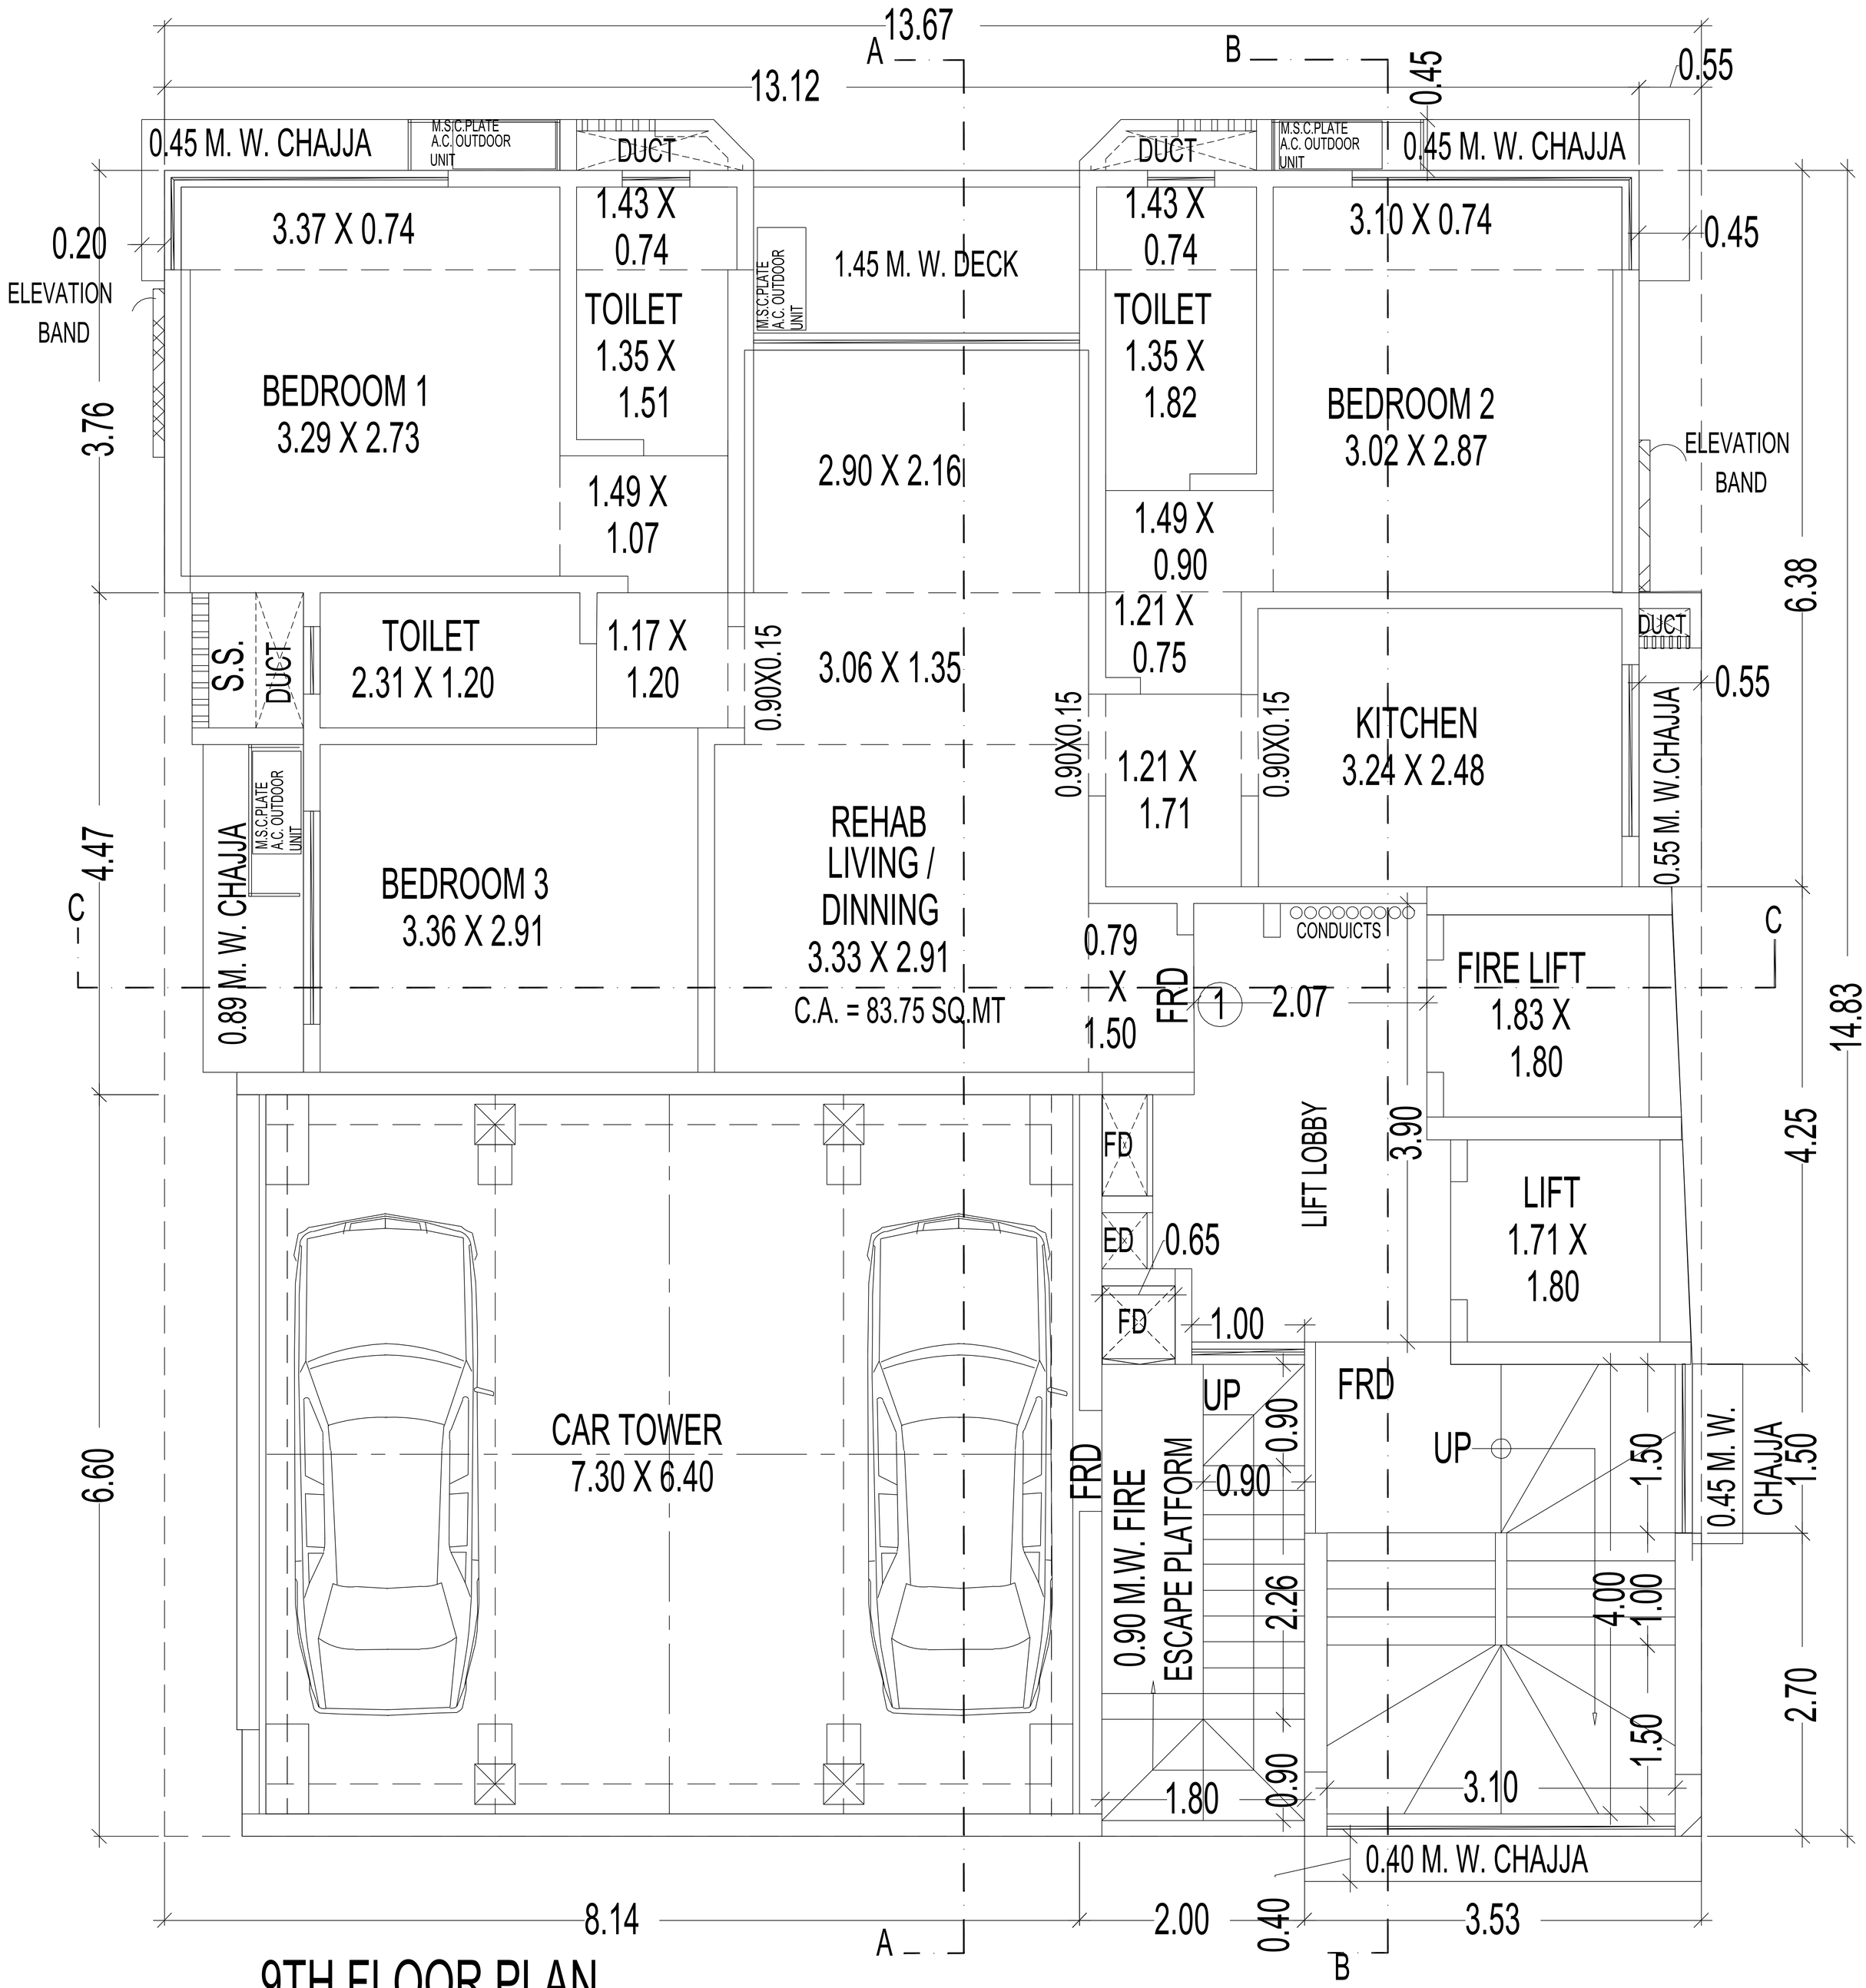

9TH FLOOR PLAN

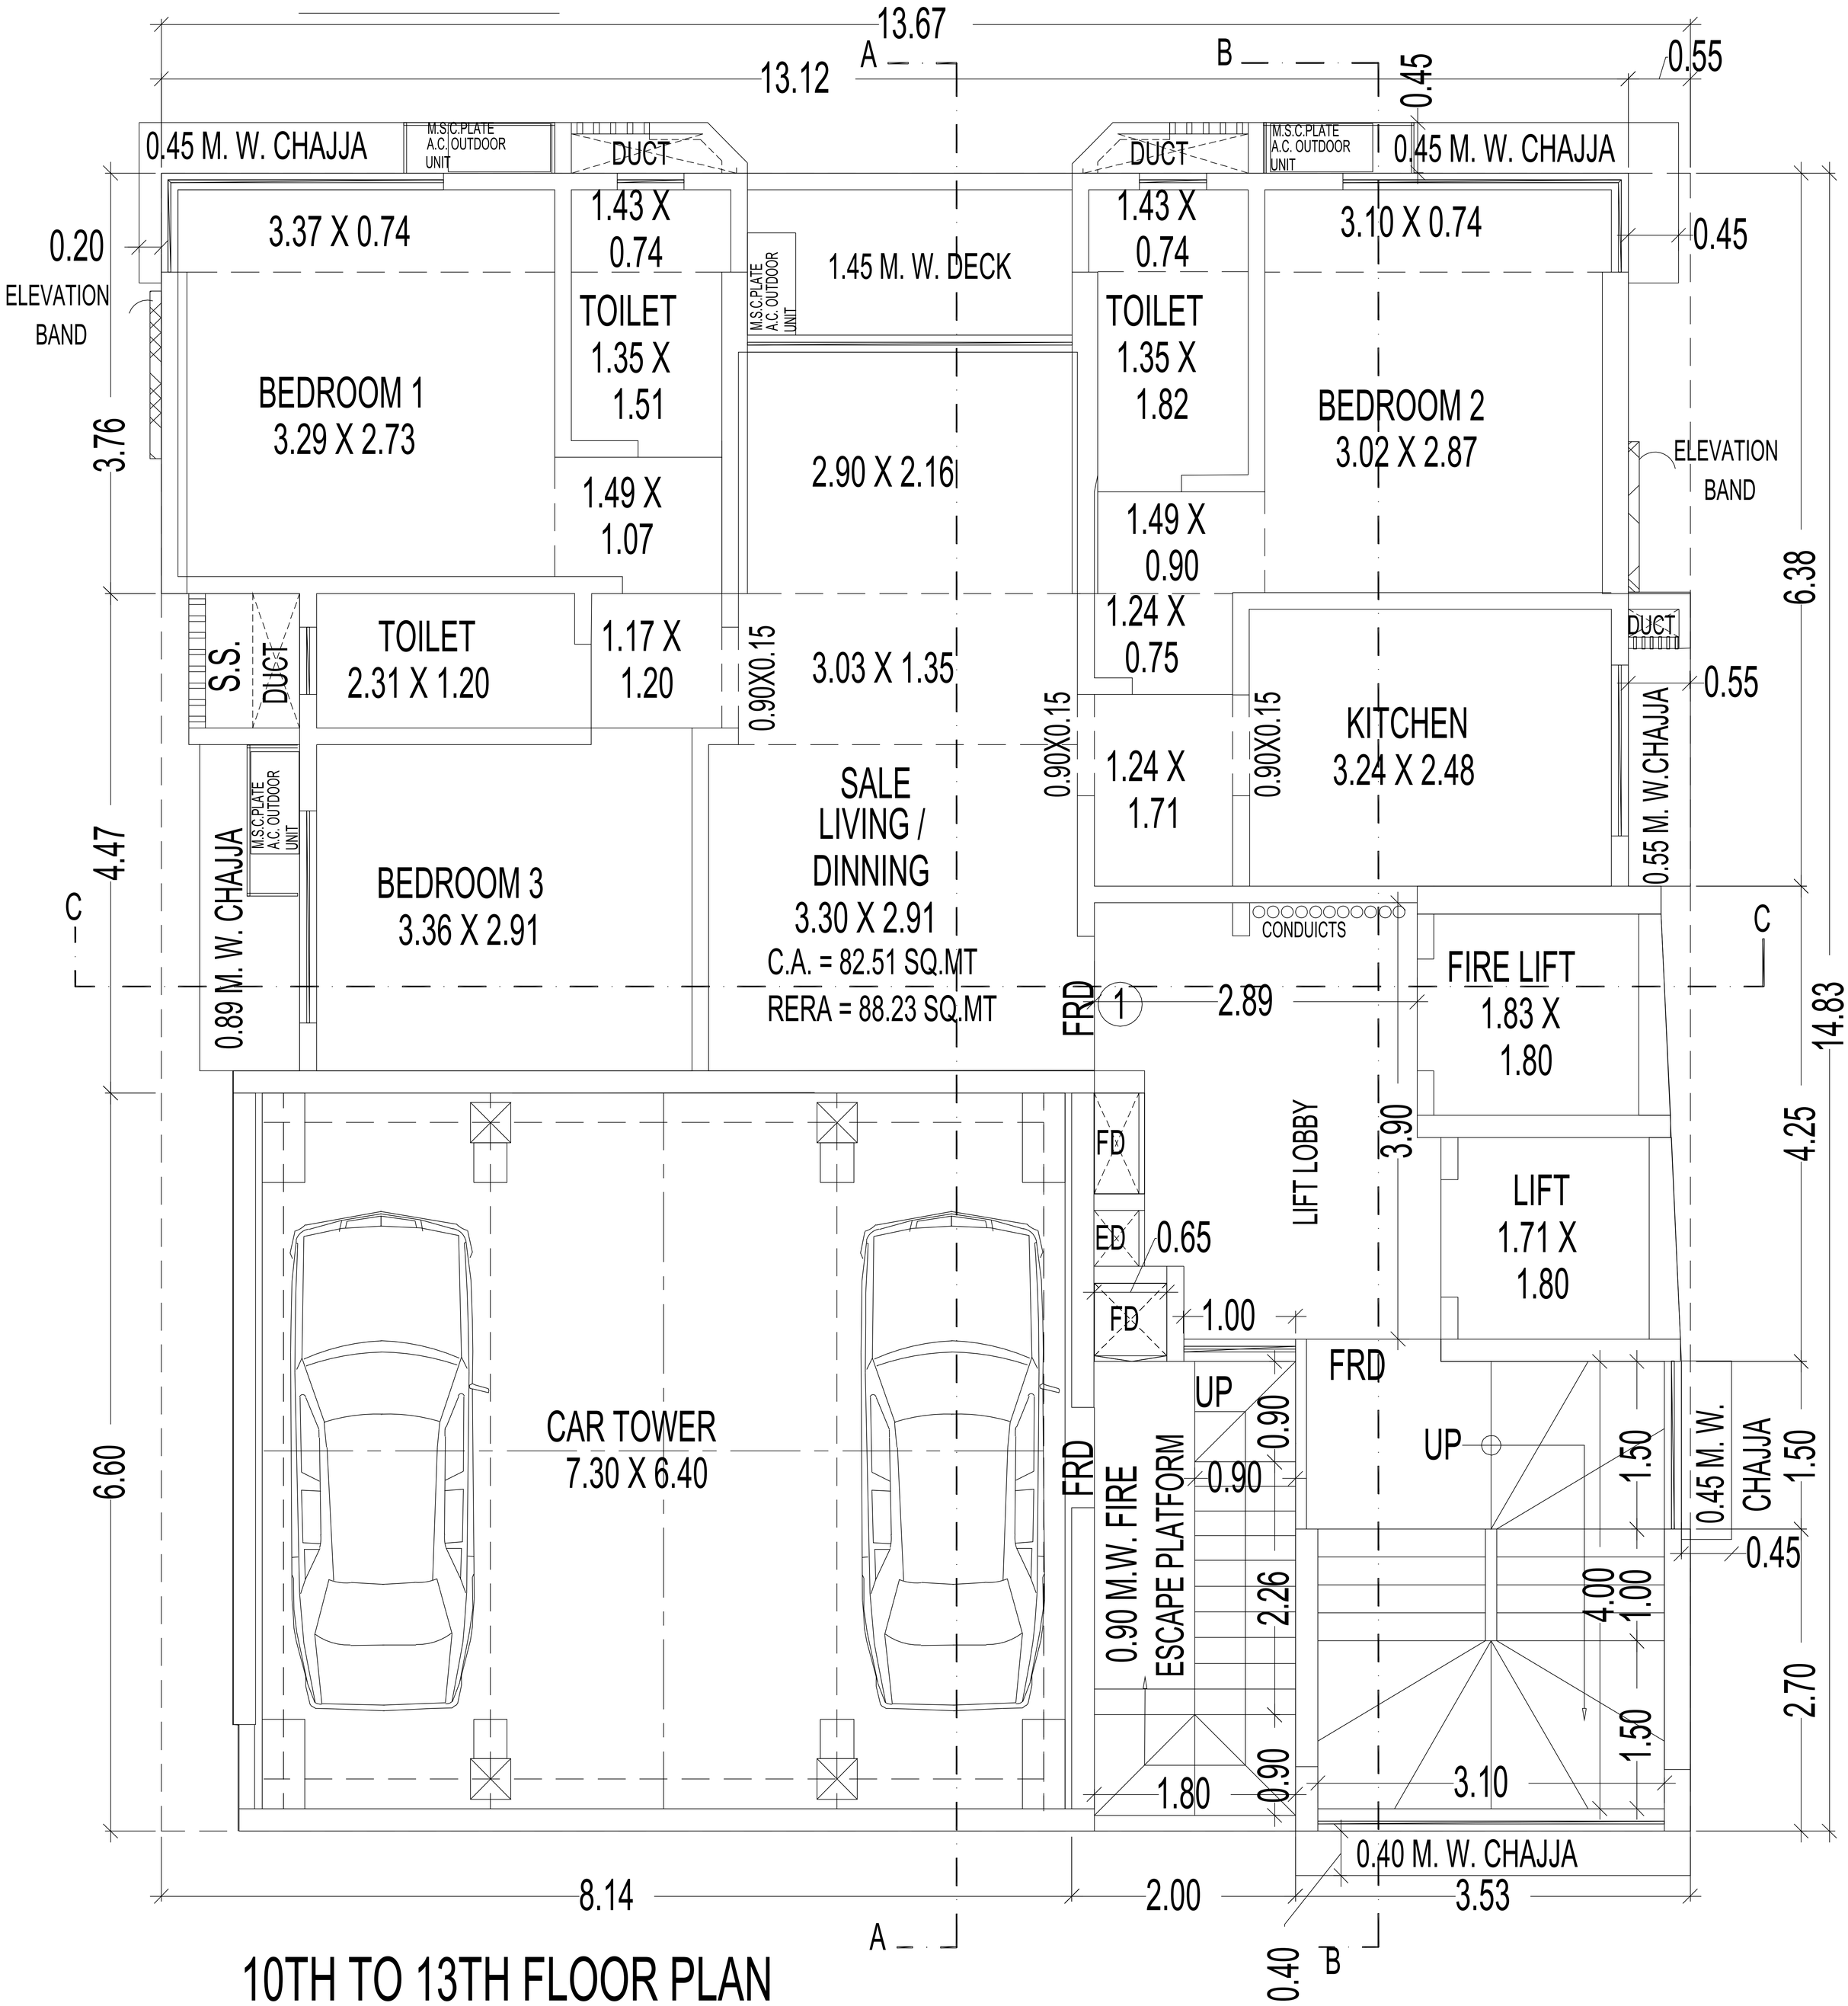

10TH TO 13TH FLOOR PLAN

SCALE :- 1:100

13.67

13.12

A

B

0.40

0.45

0.55

0.45 M. W. CHAJJA

M.S.C.PLATE A.C. OUTDOOR UNIT

DUCT

0.20 ELEVATION BAND

3.37 X 0.74

1.43 X 0.74

1.45 M. W. DECK

3.10 X 0.74

0.45

BEDROOM 3.29 X 2.73

TOILET 1.35 X 1.51

PAP LIVING ROOM 2.90 X 2.16

C.A. = 41.75 SQ.MT

RERA = 44.56 SQ.MT

TOILET 1.35 X 2.55

BEDROOM 3.02 X 1.97

3.76

1.49 X 1.07

1.21 X 0.90

3.16 X 0.90

ELEVATION BAND

6.38

S.S.

DUCT

TOILET 2.31 X 1.20

1.17 X 1.35

3.18 X 1.20

1.24 X 2.62

0.90X0.15

KITCHEN 3.24 X 2.48

0.55 M. W.CHAJJA

0.55

ALCOVE

4.47

PAP LIVING / DINNING 6.81 X 2.91

C.A. = 40.88 SQ.MT

RERA = 42.37 SQ.MT

FRD

1A

CONDUICTS

C

0.89 M. W. CHAJJA

FRD

1B

2.89

FIRE LIFT 1.83 X 1.80

FD

LIFT LOBBY

3.90

LIFT 1.71 X 1.80

ED

0.65

FD

1.00

FRD

UP

0.90

0.90

UP

1.50

0.45 M. W. CHAJJA

1.50

0.45

6.60

CAR TOWER 7.30 X 6.40

FRD

0.90 M.W. FIRE ESCAPE PLATFORM

2.26

4.00

1.00

1.50

2.70

0.90

1.80

3.10

8.14

2.00

0.40 M. W. CHAJJA

3.53

0.40

B

A

14TH FLOOR PLAN (PAP)


SCALE :- 1:100


PAP FLAT

13.67
A
13.12
B
0.45
0.55
0.45 M. W. CHAJJA
M.S.C.PLATE A.C. OUTDOOR UNIT
DUCT
DUCT
M.S.C.PLATE A.C. OUTDOOR UNIT
0.45 M. W. CHAJJA
0.20
ELEVATION BAND
3.37 X 0.74
1.43 X 0.74
0.89 M. W. DECK
1.43 X 0.74
3.10 X 0.74
0.45
TOILET 1.35 X 1.51
TOILET 1.35 X 1.82
BEDROOM 1 3.29 X 2.73
2.90 X 1.67
BEDROOM 2 3.02 X 1.97
ELEVATION BAND
3.76
1.49 X 1.07
2.98 X 1.05
SALE
LIVING / DINNING 3.03 X 2.12
C.A. = 61.01 SQ.MT
RERA = 64.99 SQ.MT
1.21 X 1.83
3.16 X 0.90
6.38
0.92X0.18
0.78X0.15
DUCT
1.20
S.S.
DUCT
TOILET 2.31 X 1.20
1.17 X 1.35
KITCHEN 3.24 X 2.48
0.55
0.55 M. W.CHAJJA
1.05X0.15
1.24 X 1.55
FRD
1.20 M. PARAPET WALL
RCC WALL
REFUGE AREA REQ. 4% = 28.15 SQ.M.
REFUGE AREA REQ. 4.25% = 29.91 SQ.M.
REFUGE AREA PRO.= 28.29 SQ.M.
1
CONDUICTS
C
3.26
3.18 X 2.00
FIRE LIFT 1.83 X 1.80
C
4.68 X 2.91
FRD
2.89
4.25
14.83
3.90
LIFT LOBBY
0.65
LIFT 1.71 X 1.80
SLOPE 1:5
ABOVE CAR TOWER
FD
FRD
1.00
1.20
1.20 M. W. CHAJJA
UP
1.50
0.45 M. W. CHAJJA
1.50
0.45
4.00
1.00
1.50
2.70
6.60
3.10
8.14
2.00
0.40 M. W. CHAJJA
3.53
A
15TH REFUGE FLOOR PLAN

16TH TO 18TH, 21ST FLOOR PLAN

SCALE :- 1:100

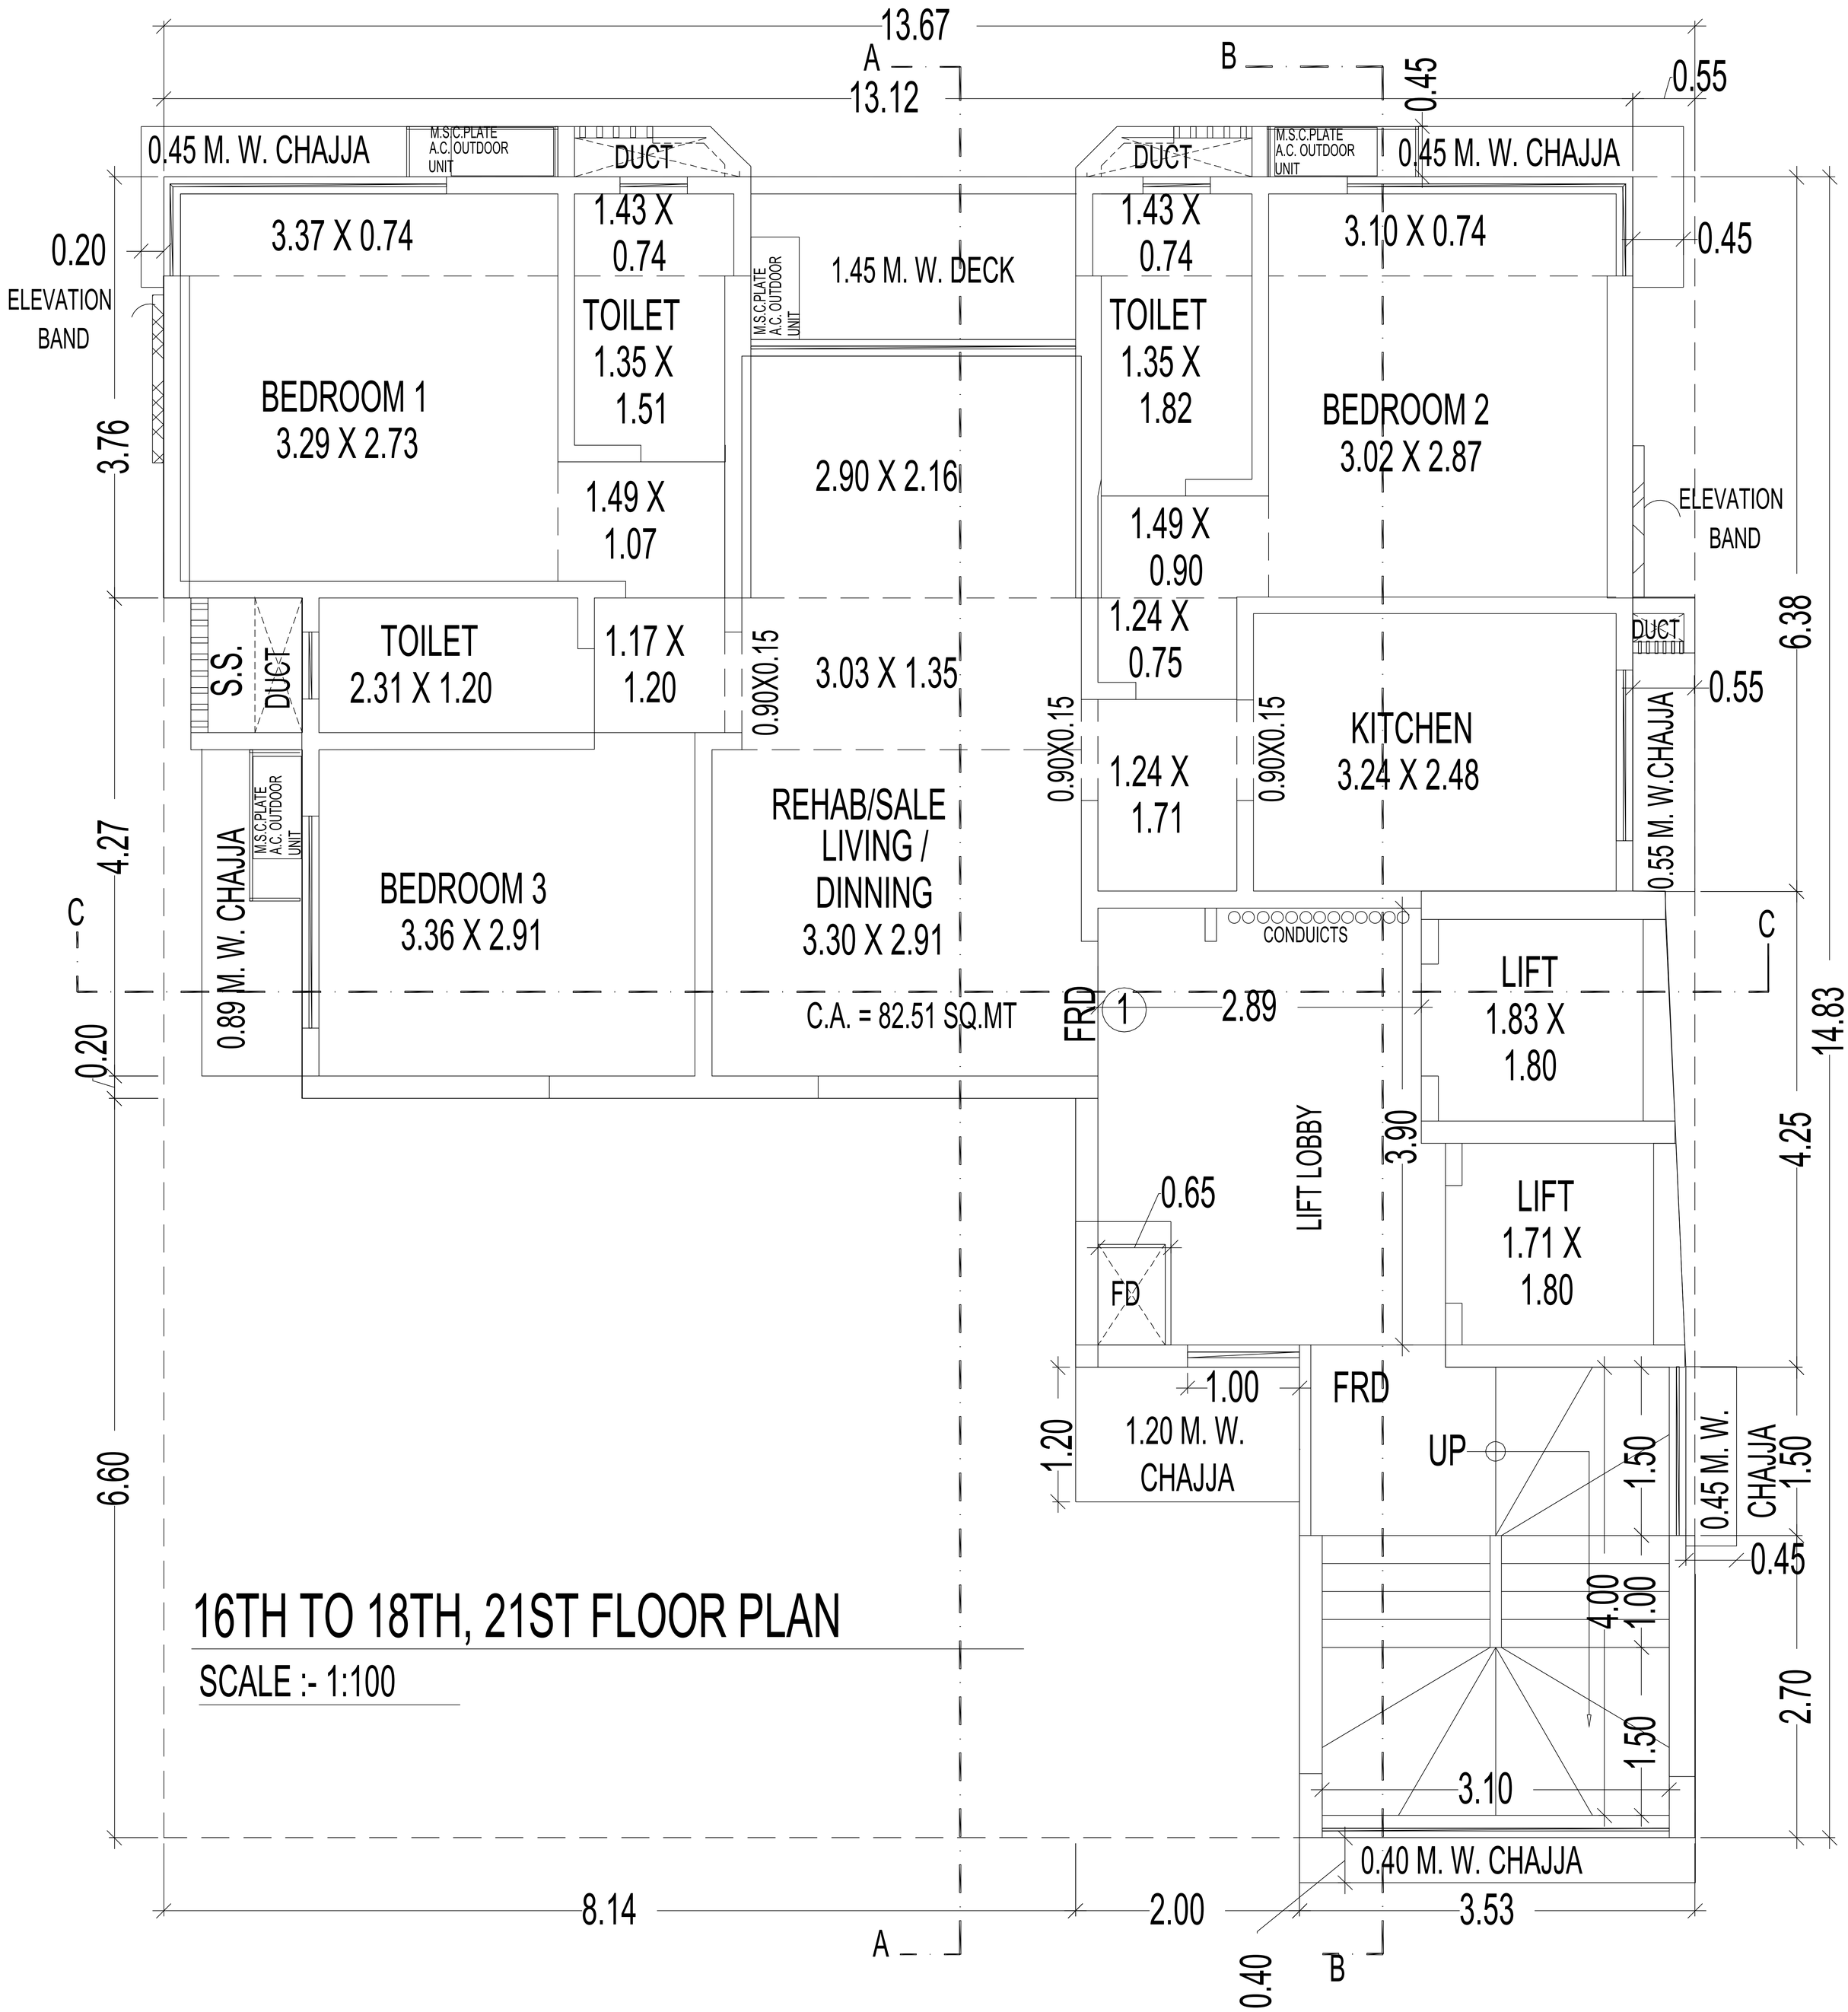

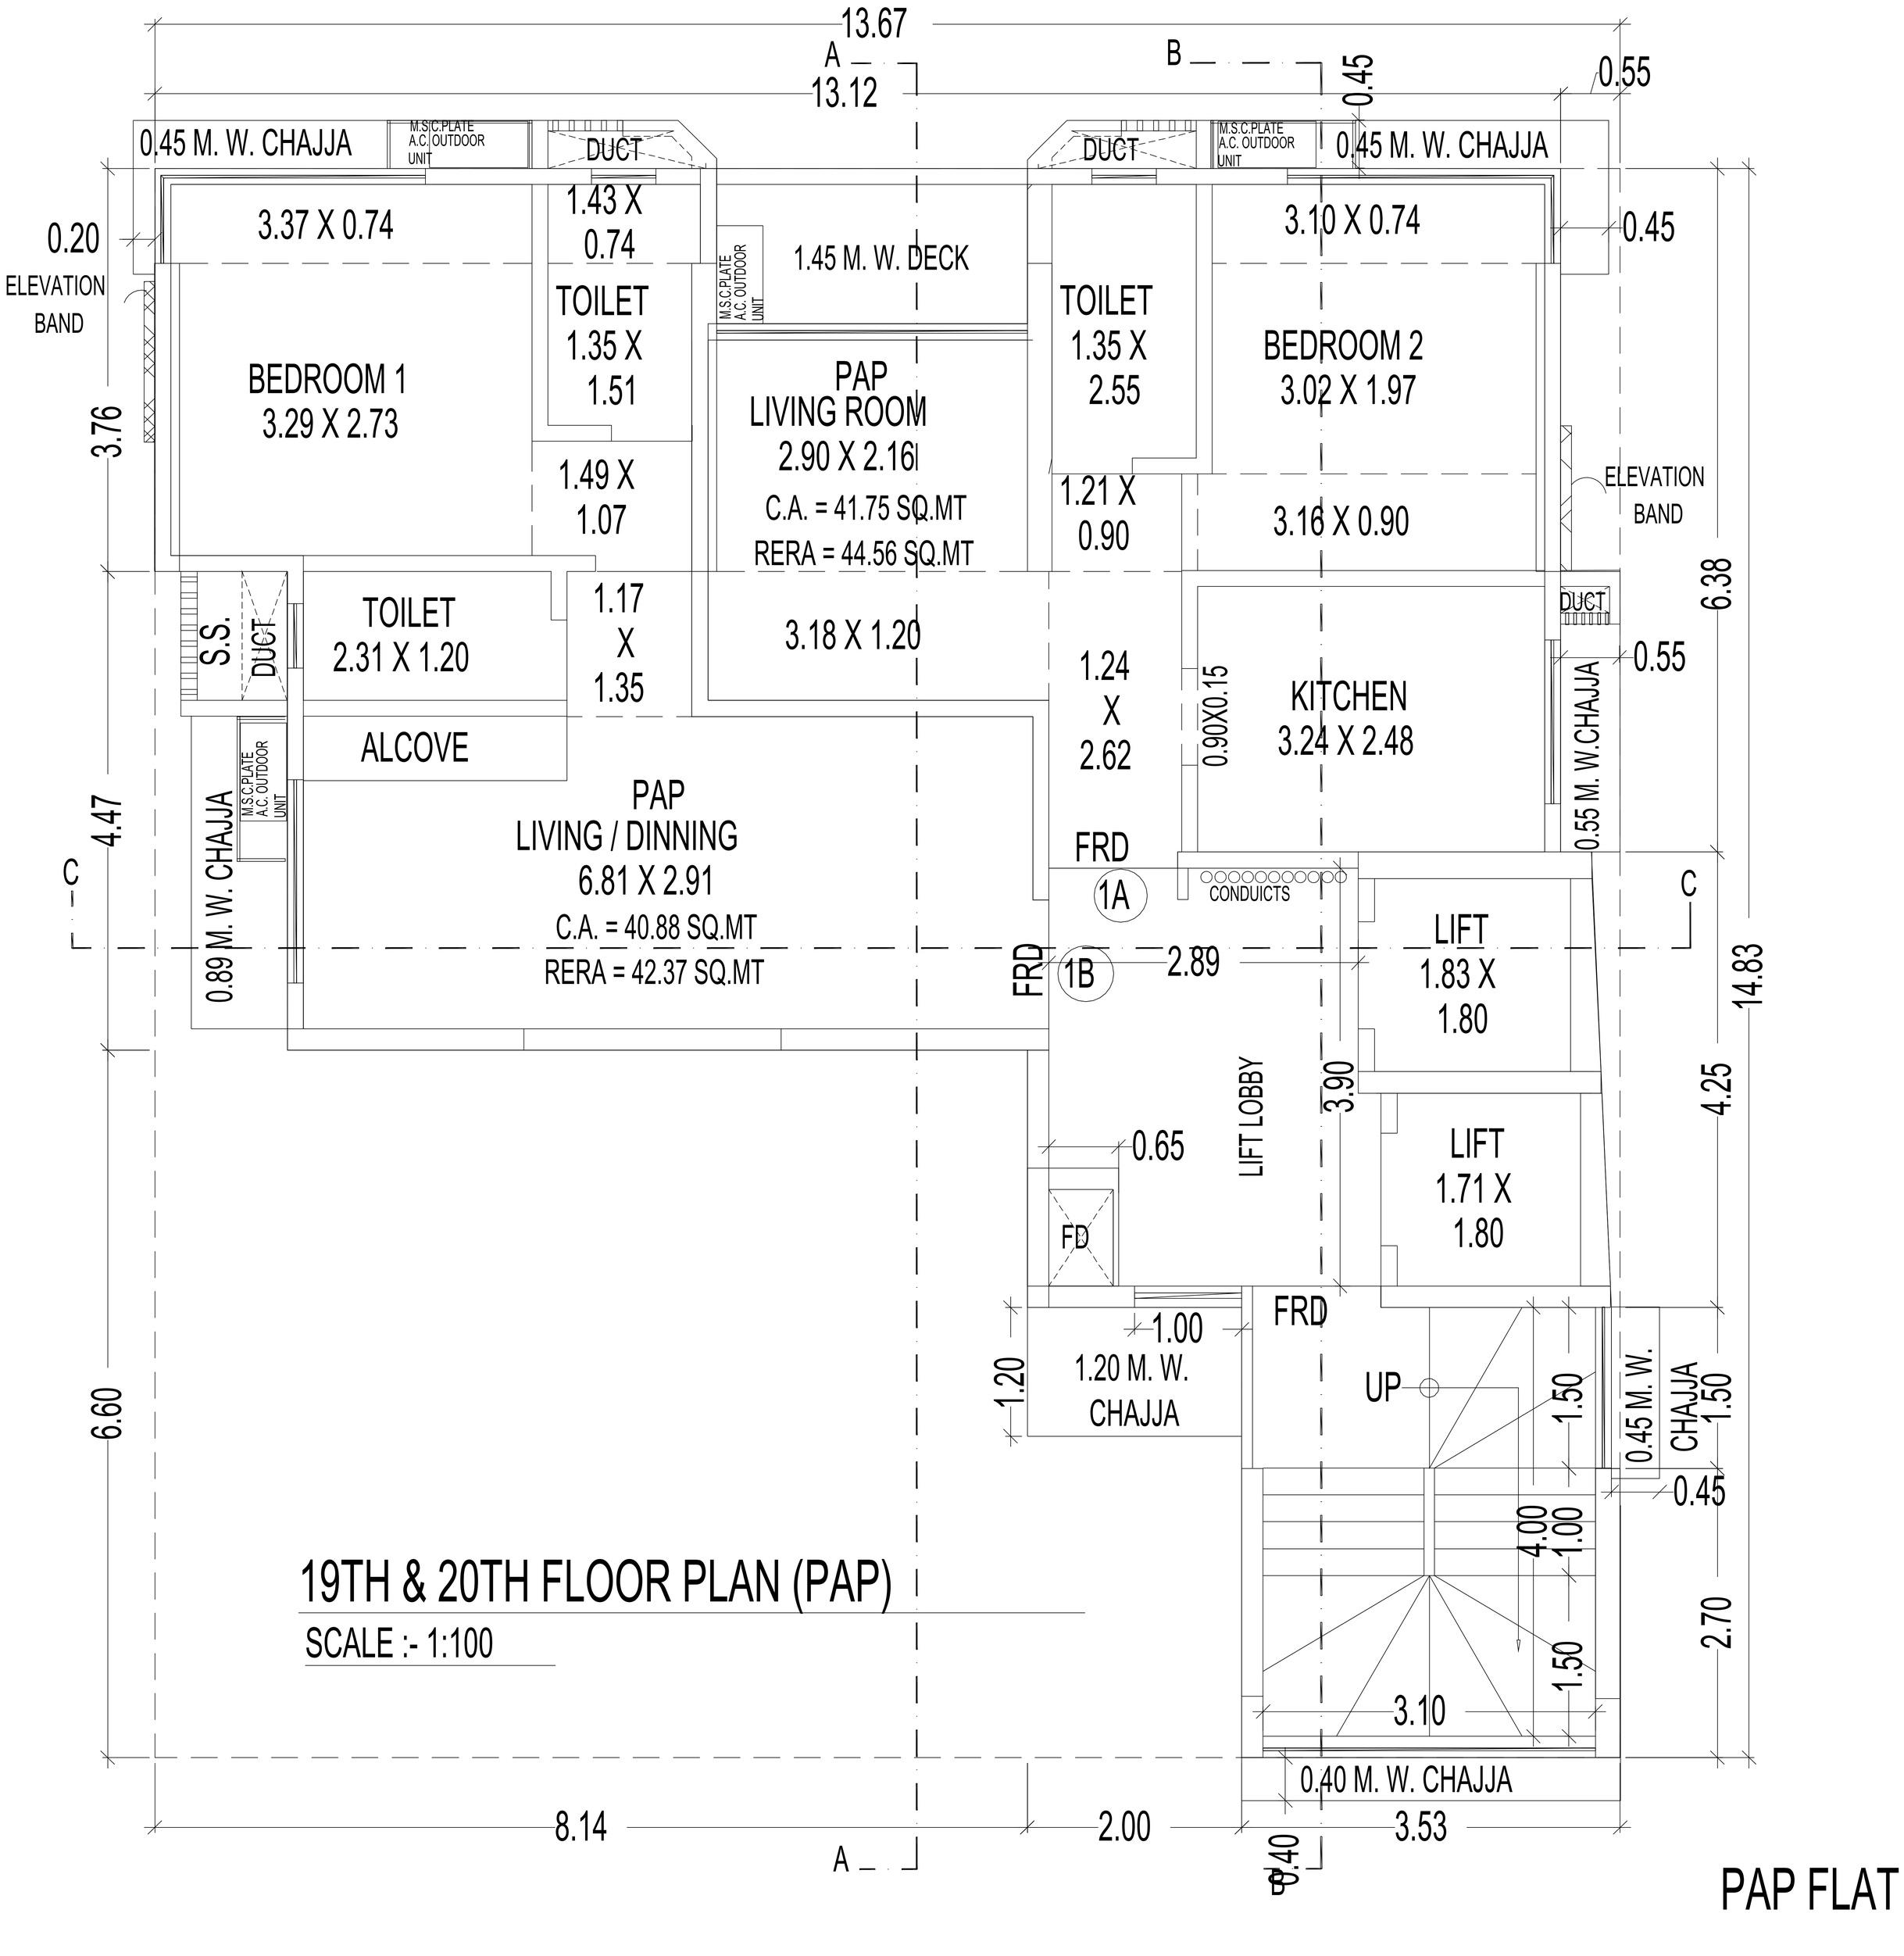

19TH & 20TH FLOOR PLAN (PAP)

SCALE :- 1:100

PAP FLAT

22ND FLOOR PLAN

SCALE :- 1:100

