4TH. FLOOR PLAN


SCALE 1:100

5TH. FLOOR PLAN

SCALE 1:100


6TH. FLOOR PLAN

SCALE 1:100

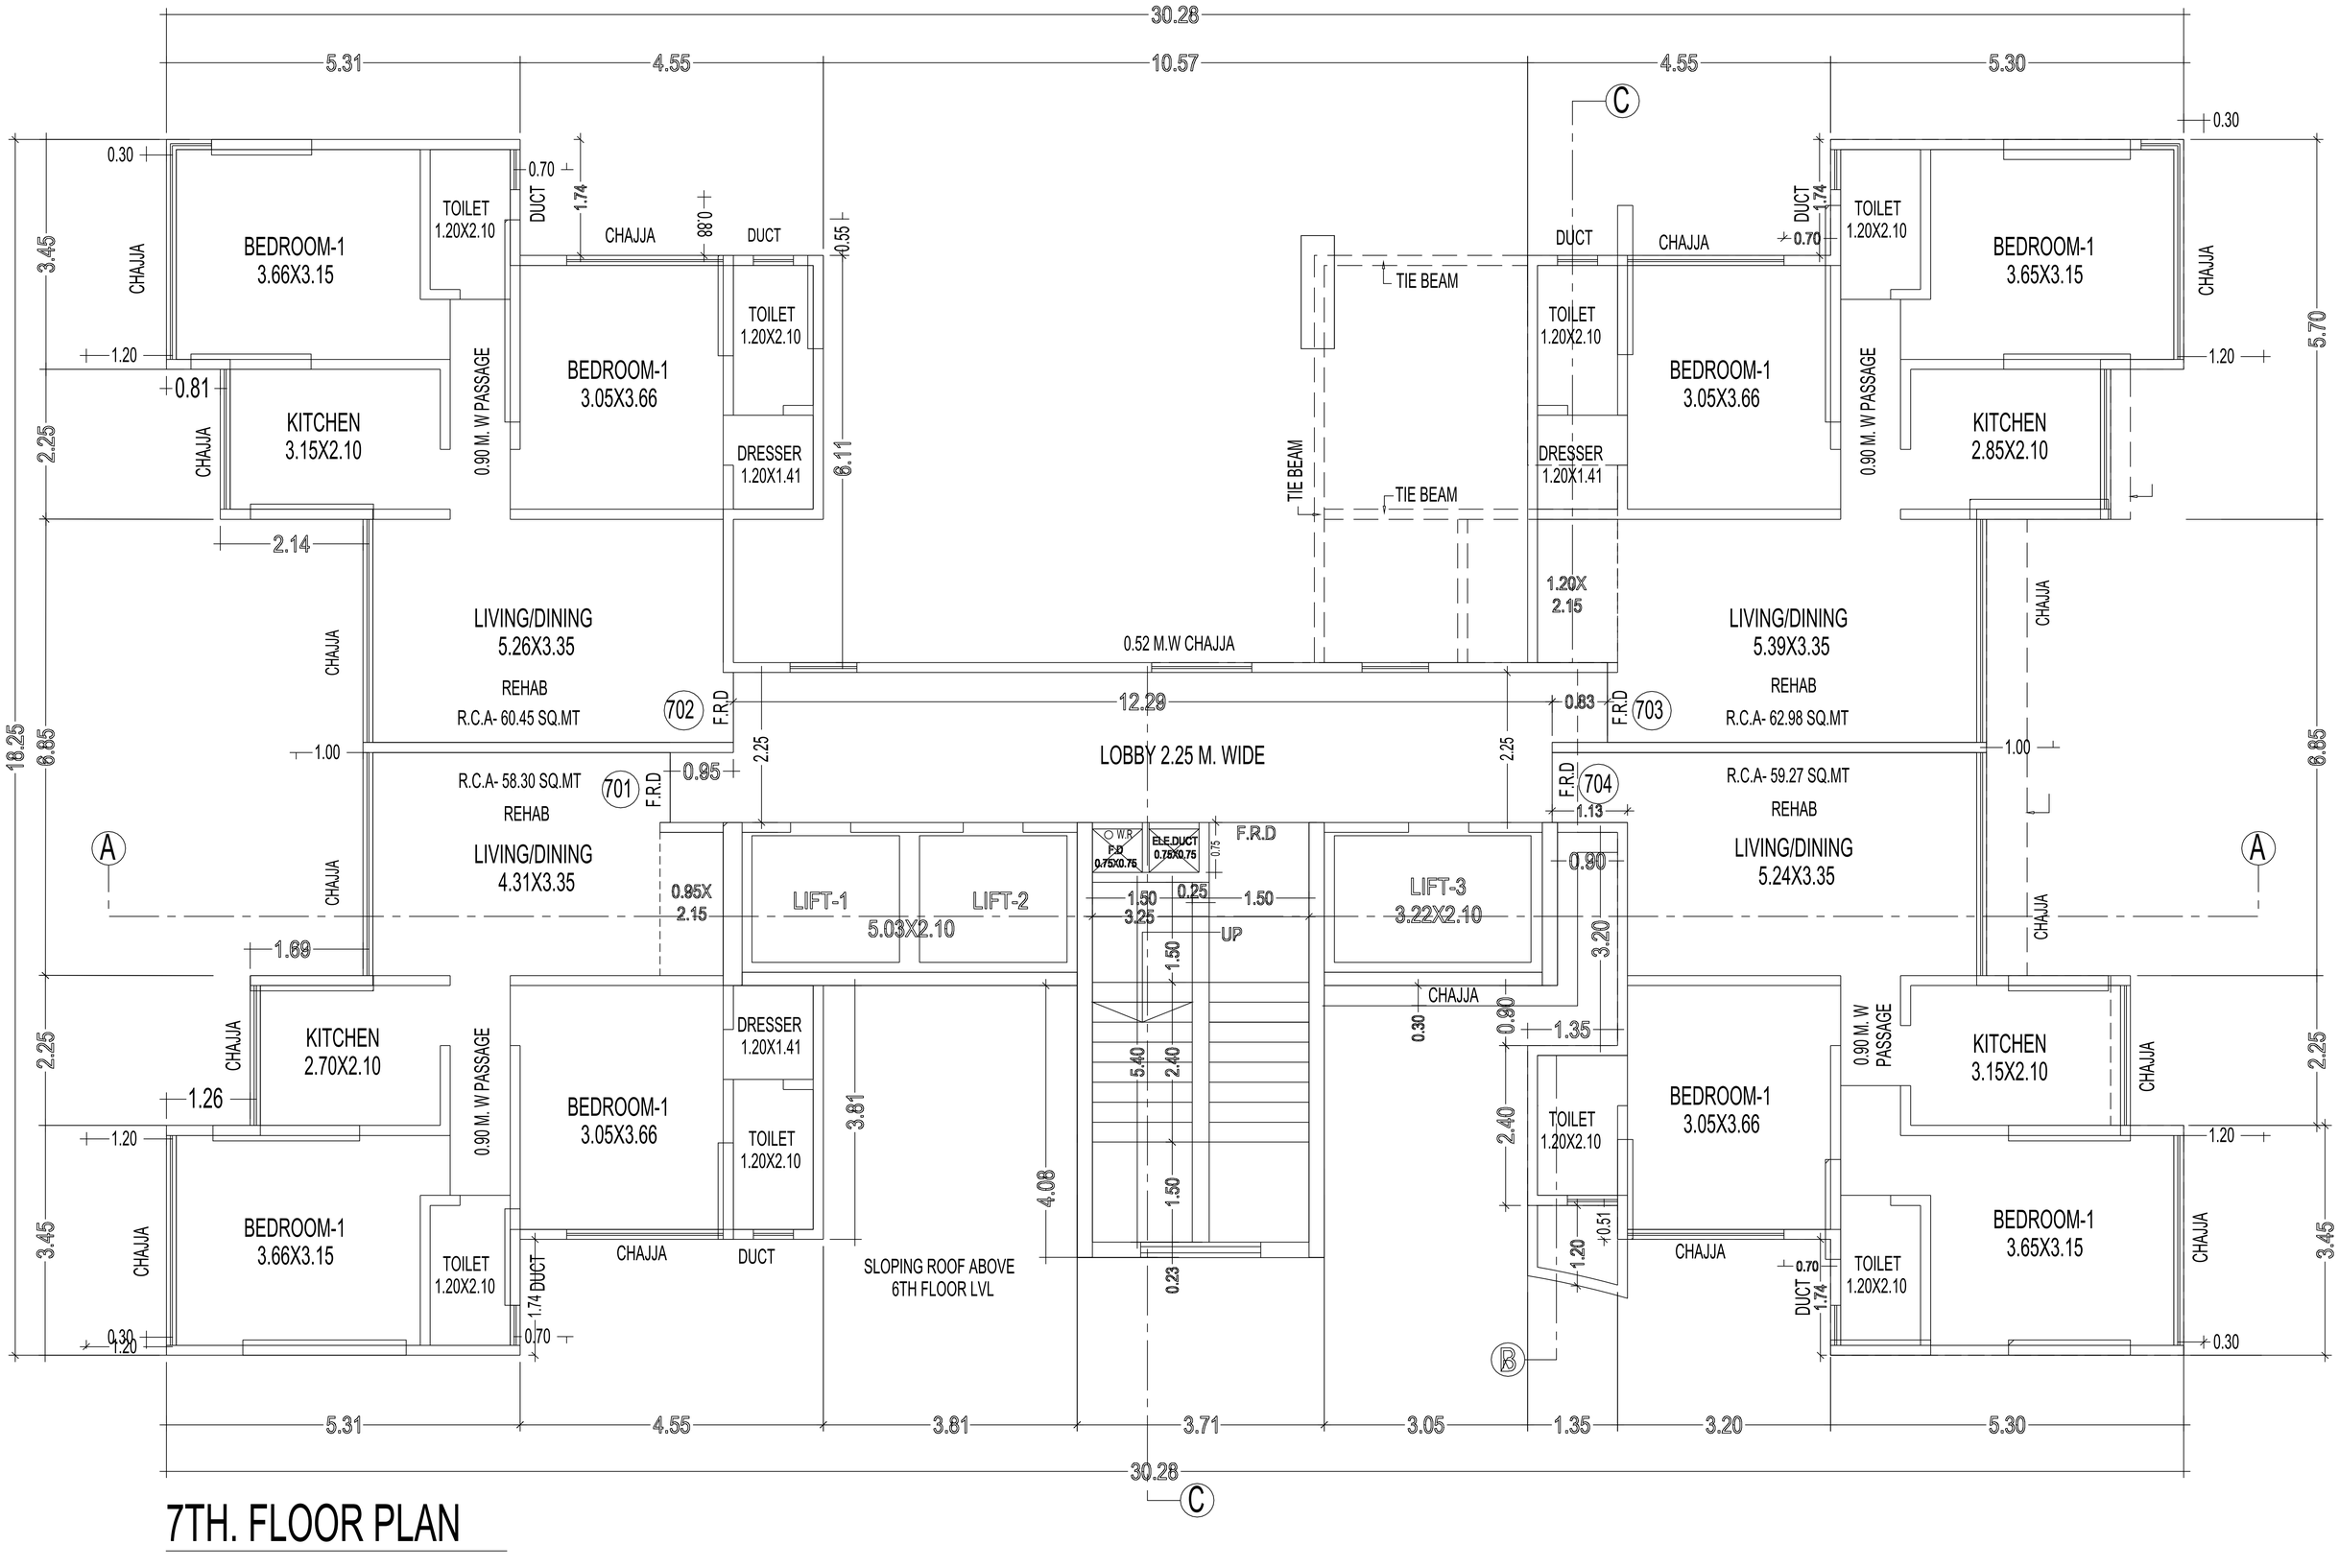

7TH. FLOOR PLAN

SCALE 1:100

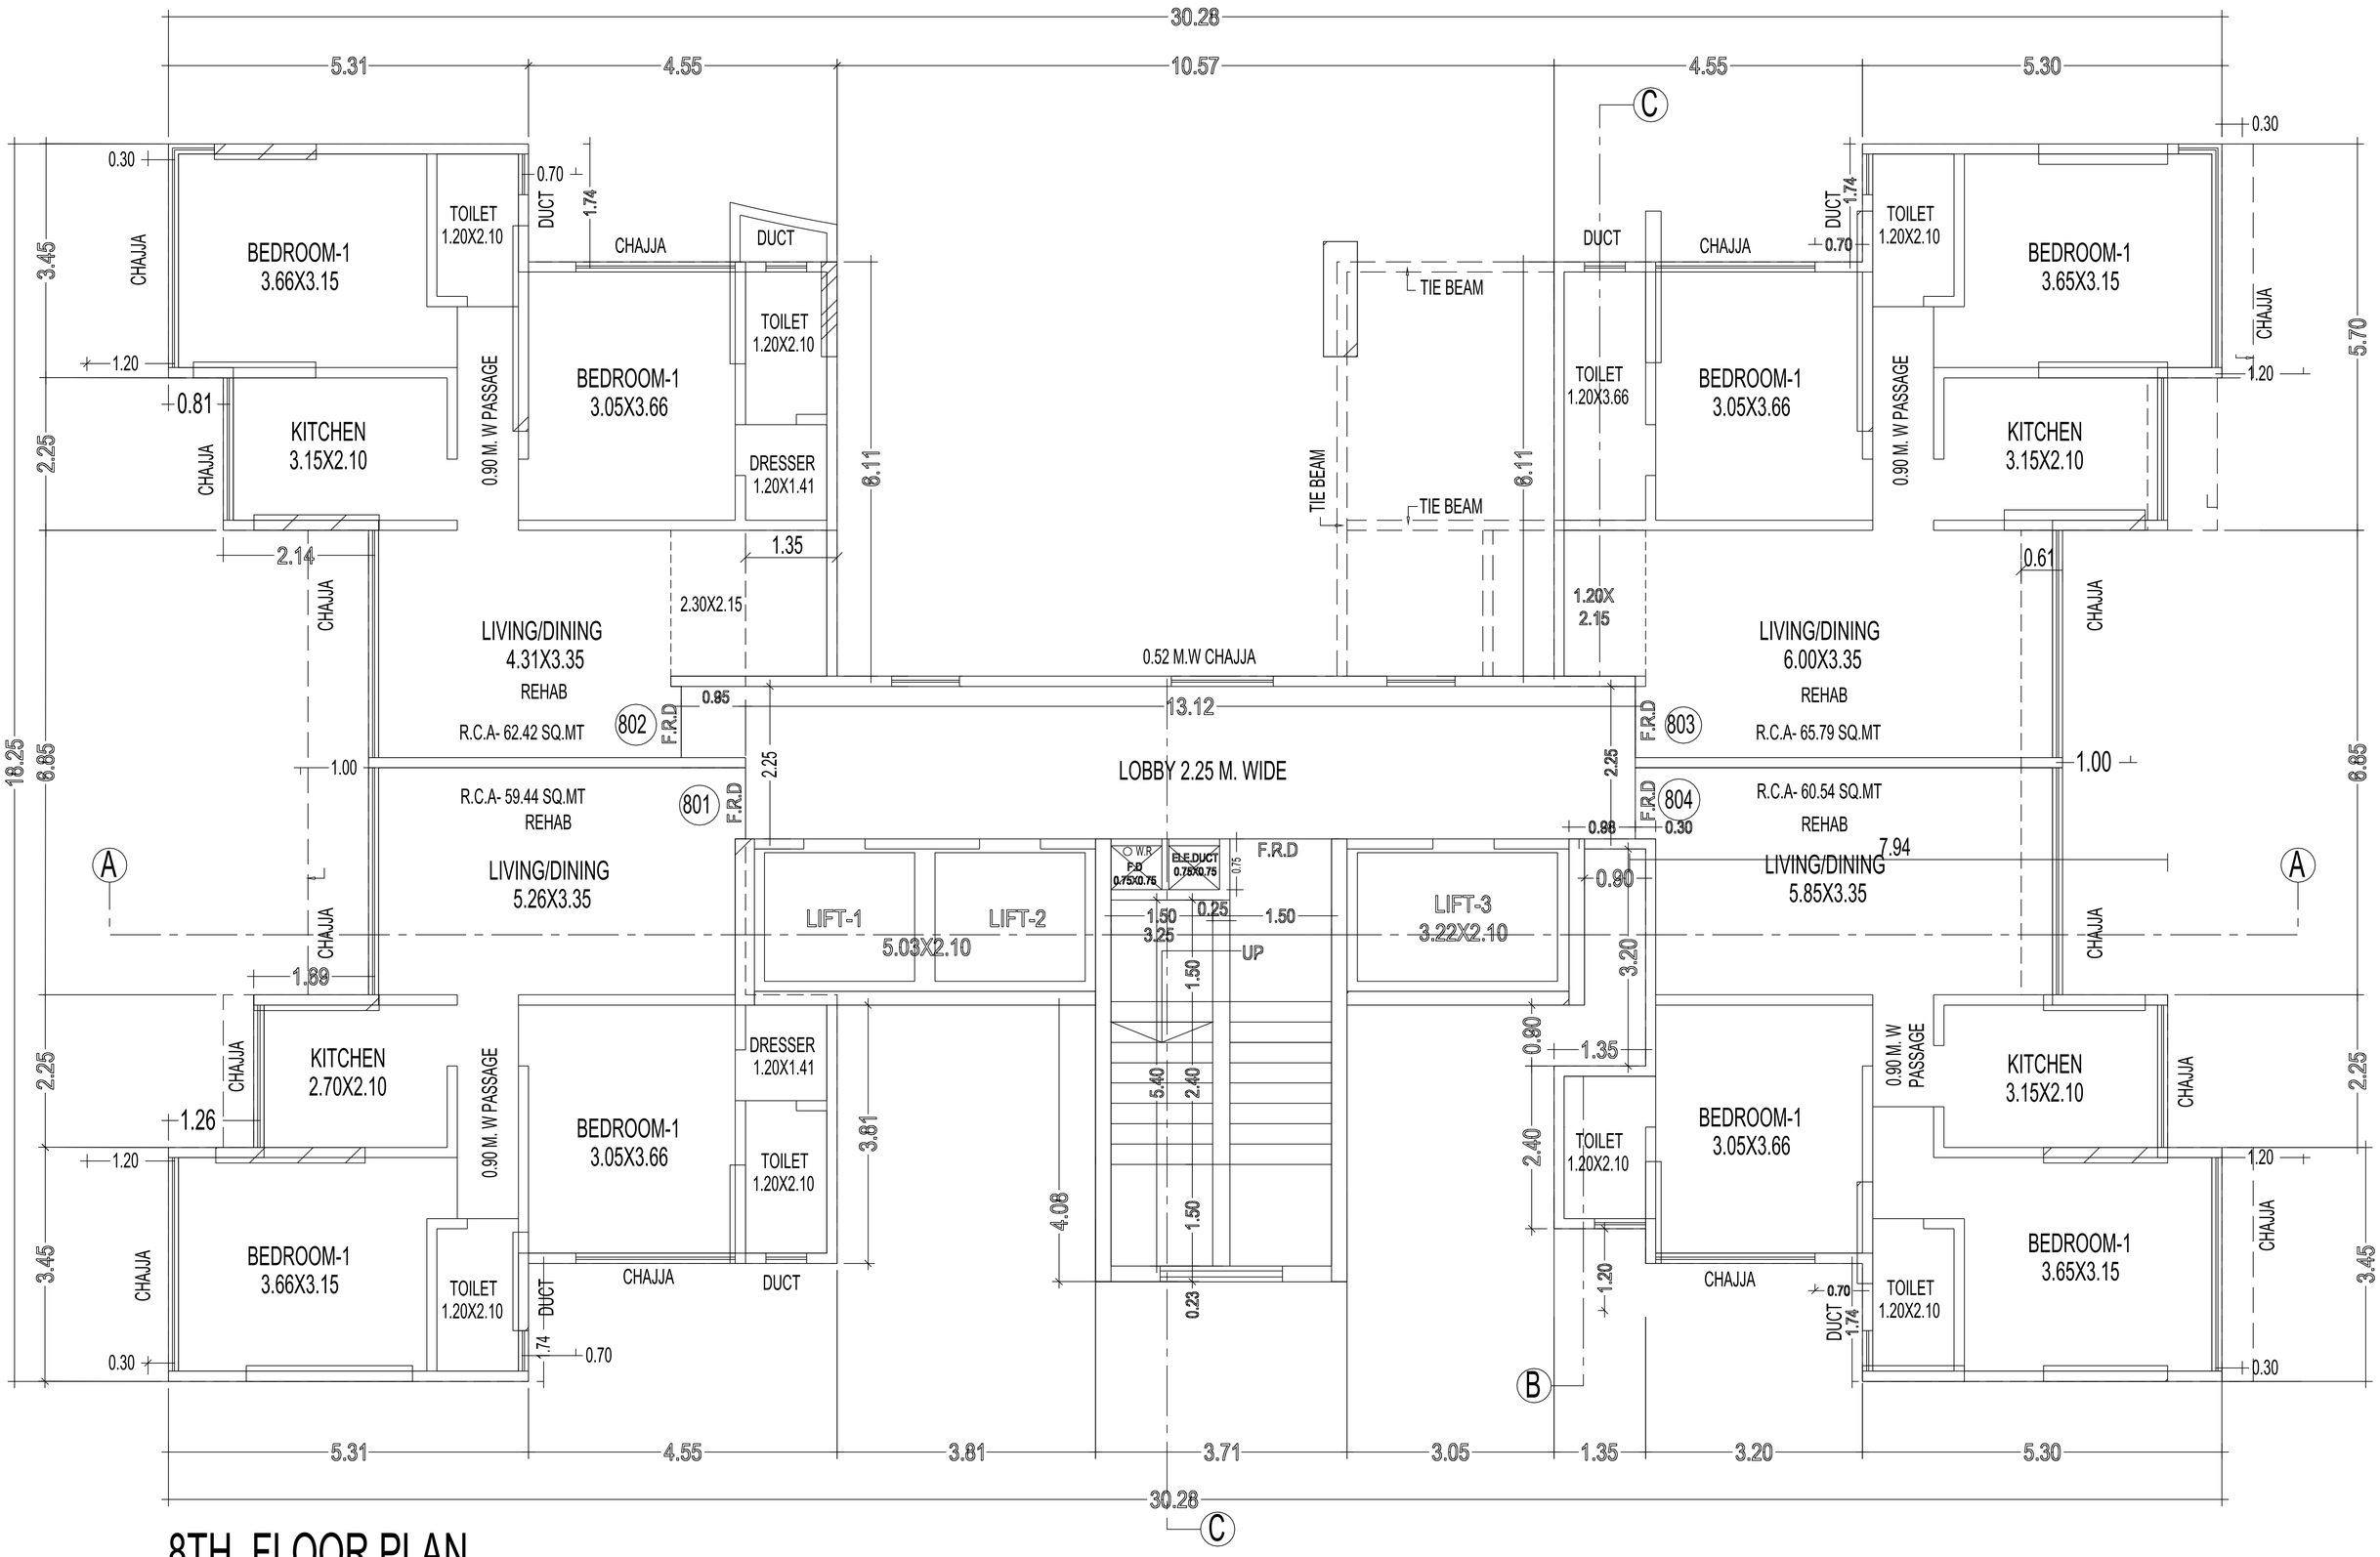


8TH. FLOOR PLAN

SCALE 1:100

9TH. FLOOR PLAN

SCALE 1:100

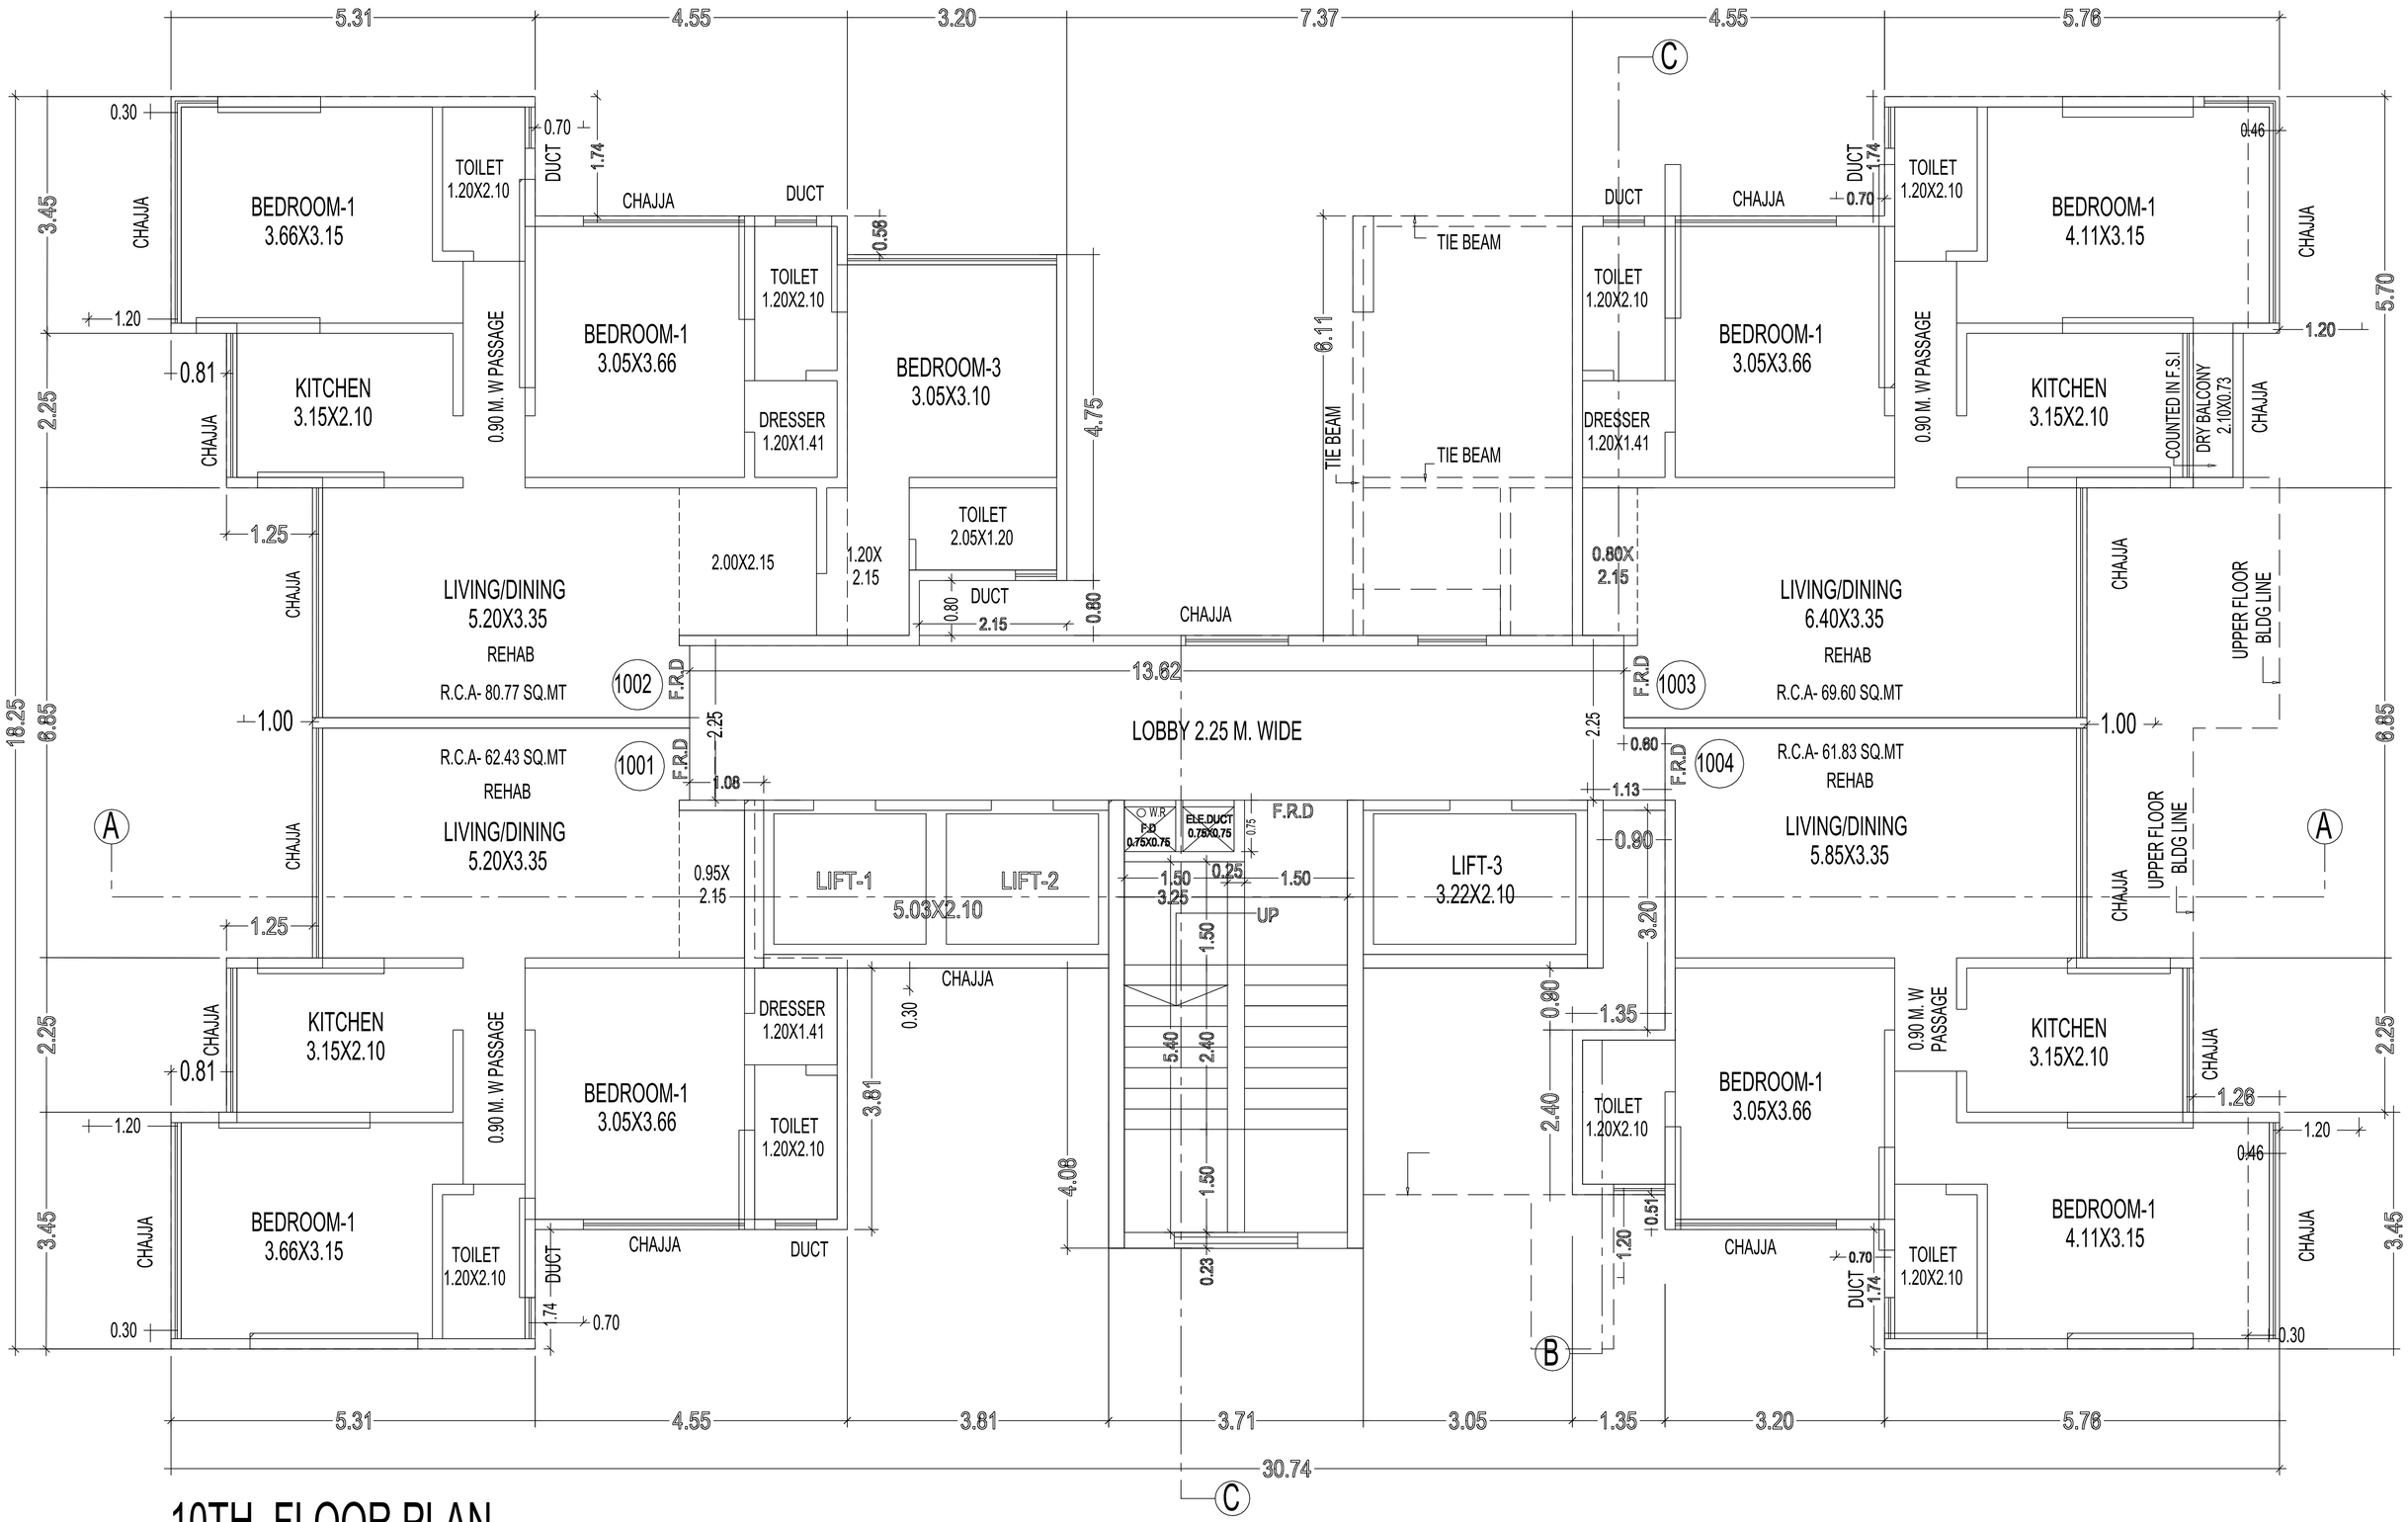


10TH. FLOOR PLAN

SCALE 1:100

11TH. FLOOR PLAN


BEDROOM-1 3.66X3.15
TOILET 1.20X2.10
KITCHEN 3.15X2.10
BEDROOM-1 3.05X3.66
TOILET 1.20X2.10
DRESSER 1.20X1.41
BEDROOM-3 3.05X3.10
TOILET 2.05X1.20
LIVING/DINING 5.20X3.35
R.C.A- 80.77 SQ.MT
R.C.A- 62.43 SQ.MT
LOBBY 2.25 M. WIDE
LIFT-1
LIFT-2
5.03X2.10
LIFT-3 3.22X2.10
UP
F.R.D
O.W.R F.D 0.75X0.75
ELE.DUCT 0.78X0.75
BEDROOM-3 3.05X3.66
TOILET 1.20X2.10
DRESSER 1.20X1.41
BEDROOM-1 3.05X3.66
TOILET 2.05X1.20
2.40X2.15
BEDROOM-3 3.05X3.15
TOILET 1.22X2.10
BEDROOM-1 4.11X3.15
KITCHEN 3.15X2.10
DRY BALCONY 2.10X0.73
COUNTED IN F.S.I
LIVING/DINING 7.40X3.35
REHAB
R.C.A- 95.77 SQ.MT
COUNTED IN F.S.I BALCONY 3.35X1.26
R.C.A- 85.17 SQ.MT
REHAB
LIVING/DINING 8.45X3.35
BLDG LINE
CHAJJA
DUCT
0.90 M. W PASSAGE
1102
1103
1101
1104
A
C
5.31
4.55
3.20
4.17
7.75
5.76
30.74
18.25
9.20
5.60
3.45
2.25
6.85
3.81
4.08
4.75
6.11
13.17

SCALE 1:100

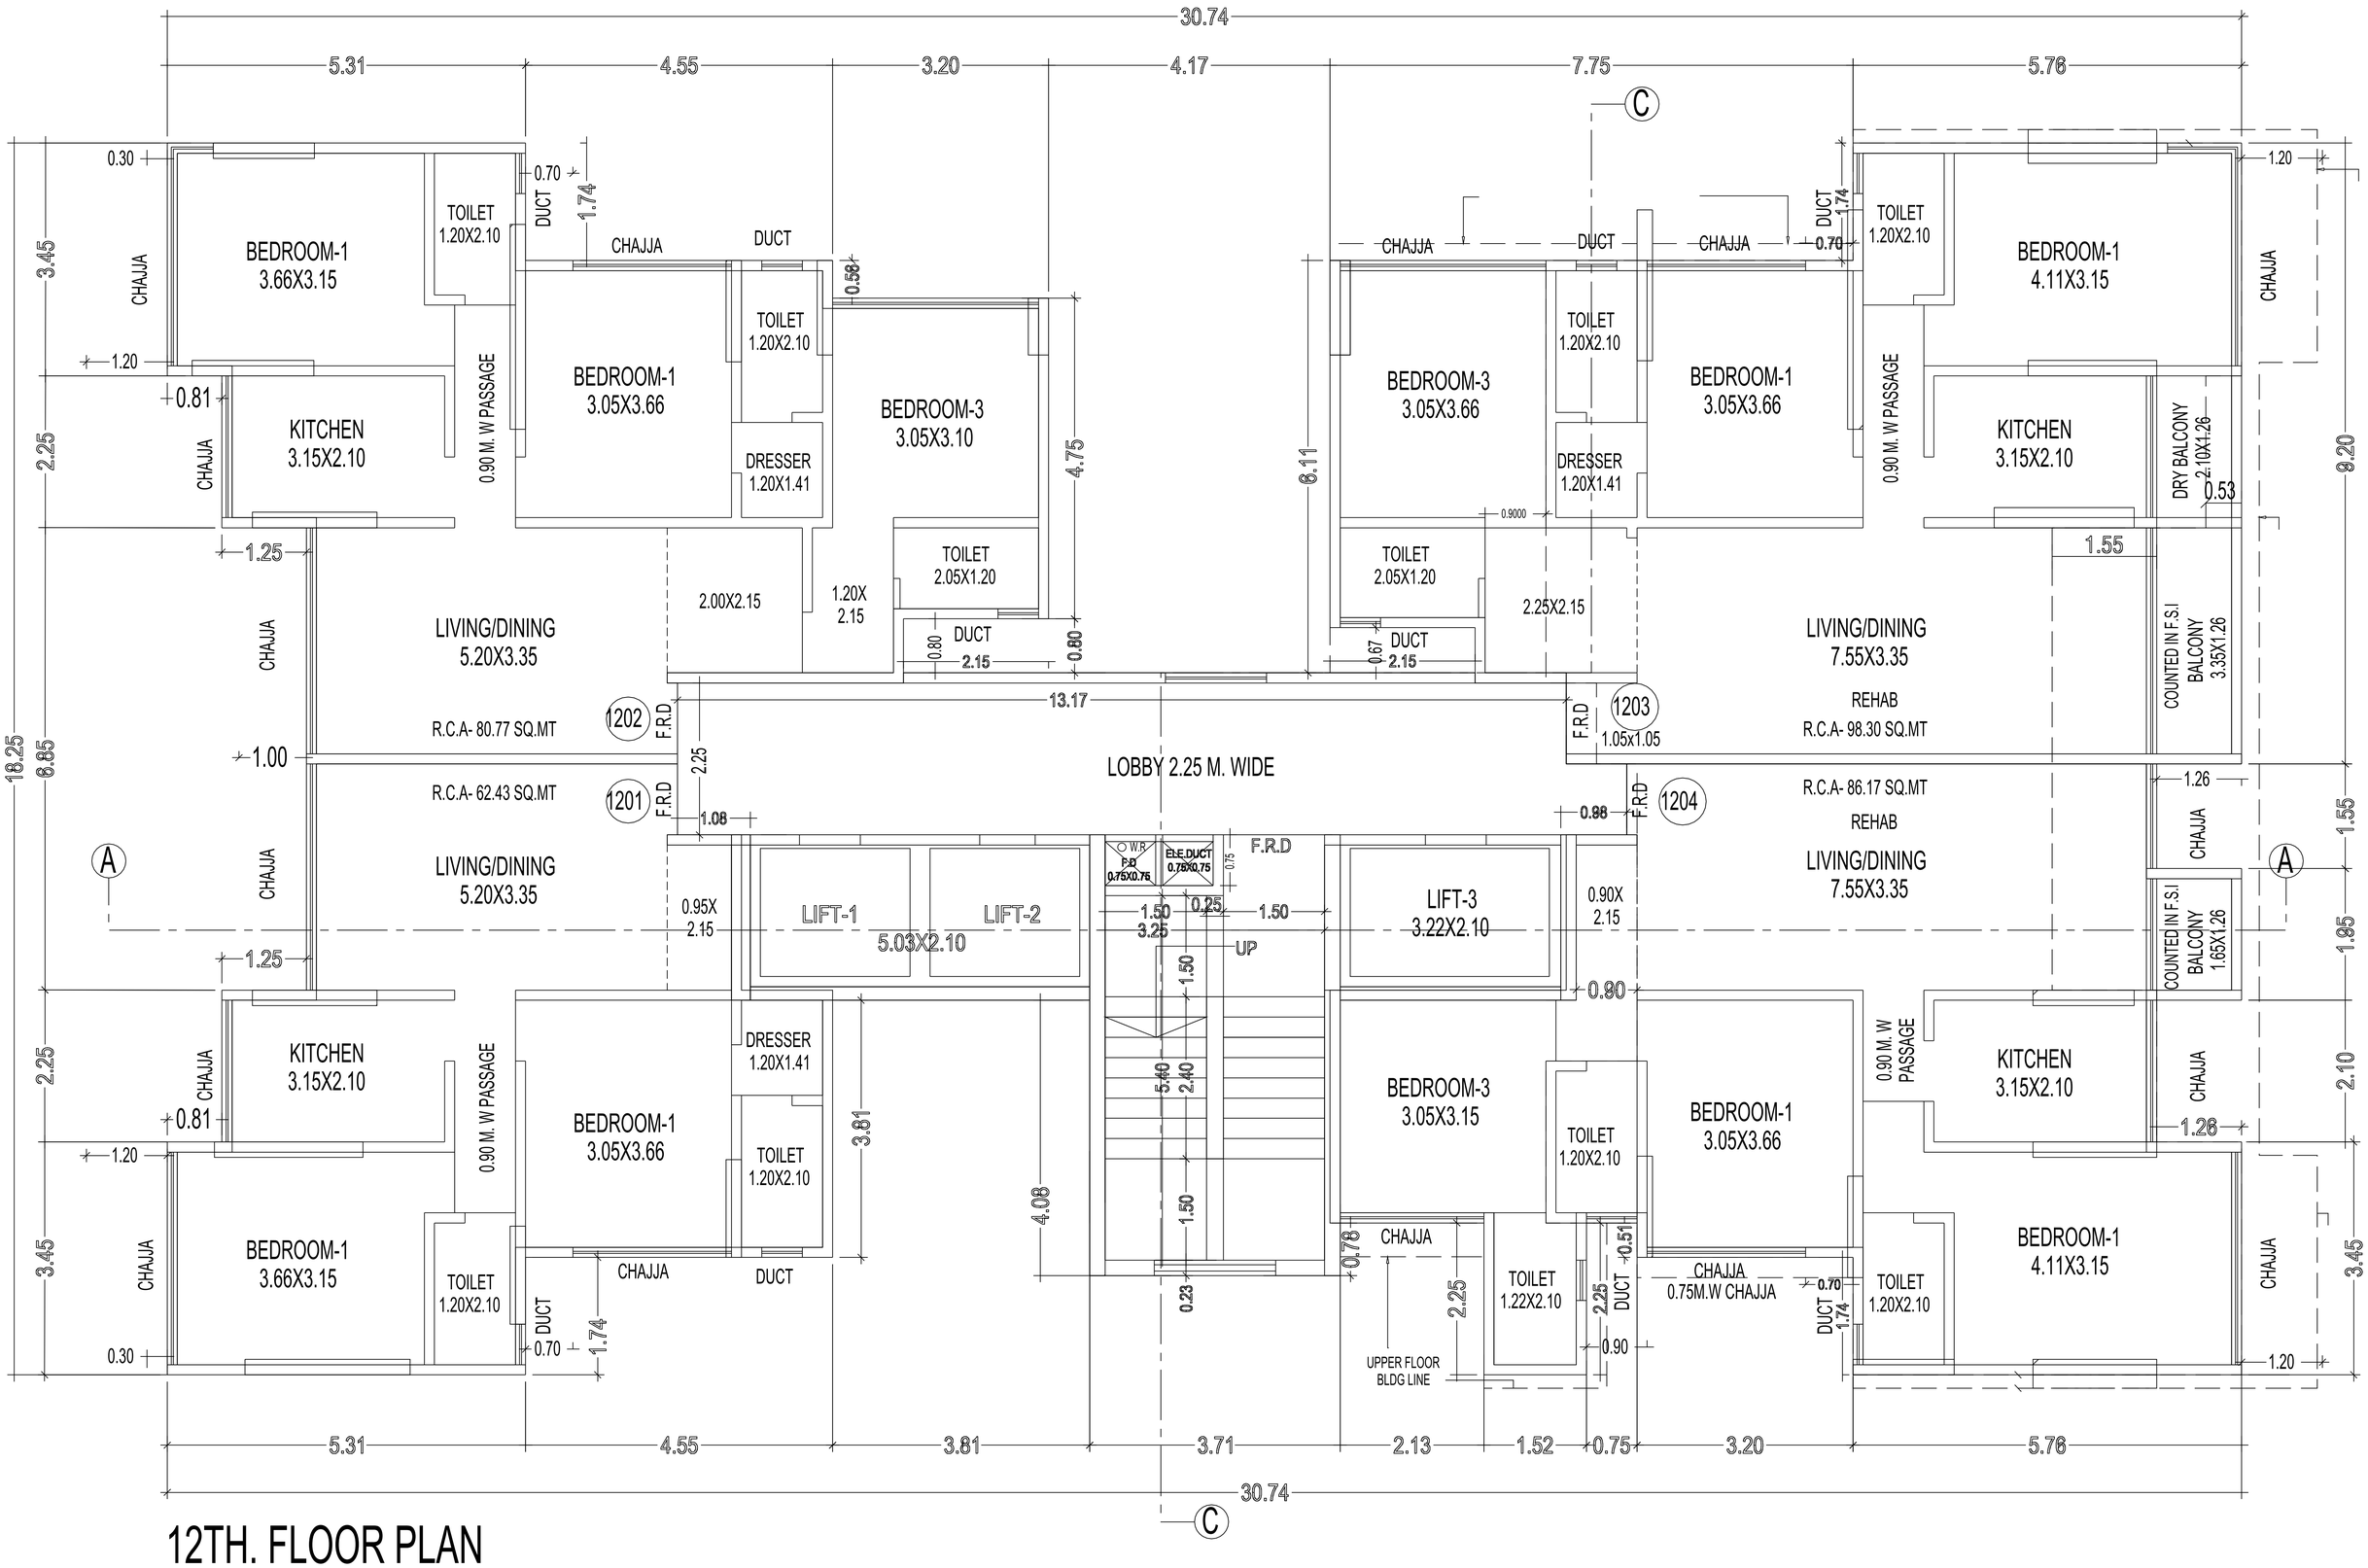


12TH. FLOOR PLAN

SCALE 1:100

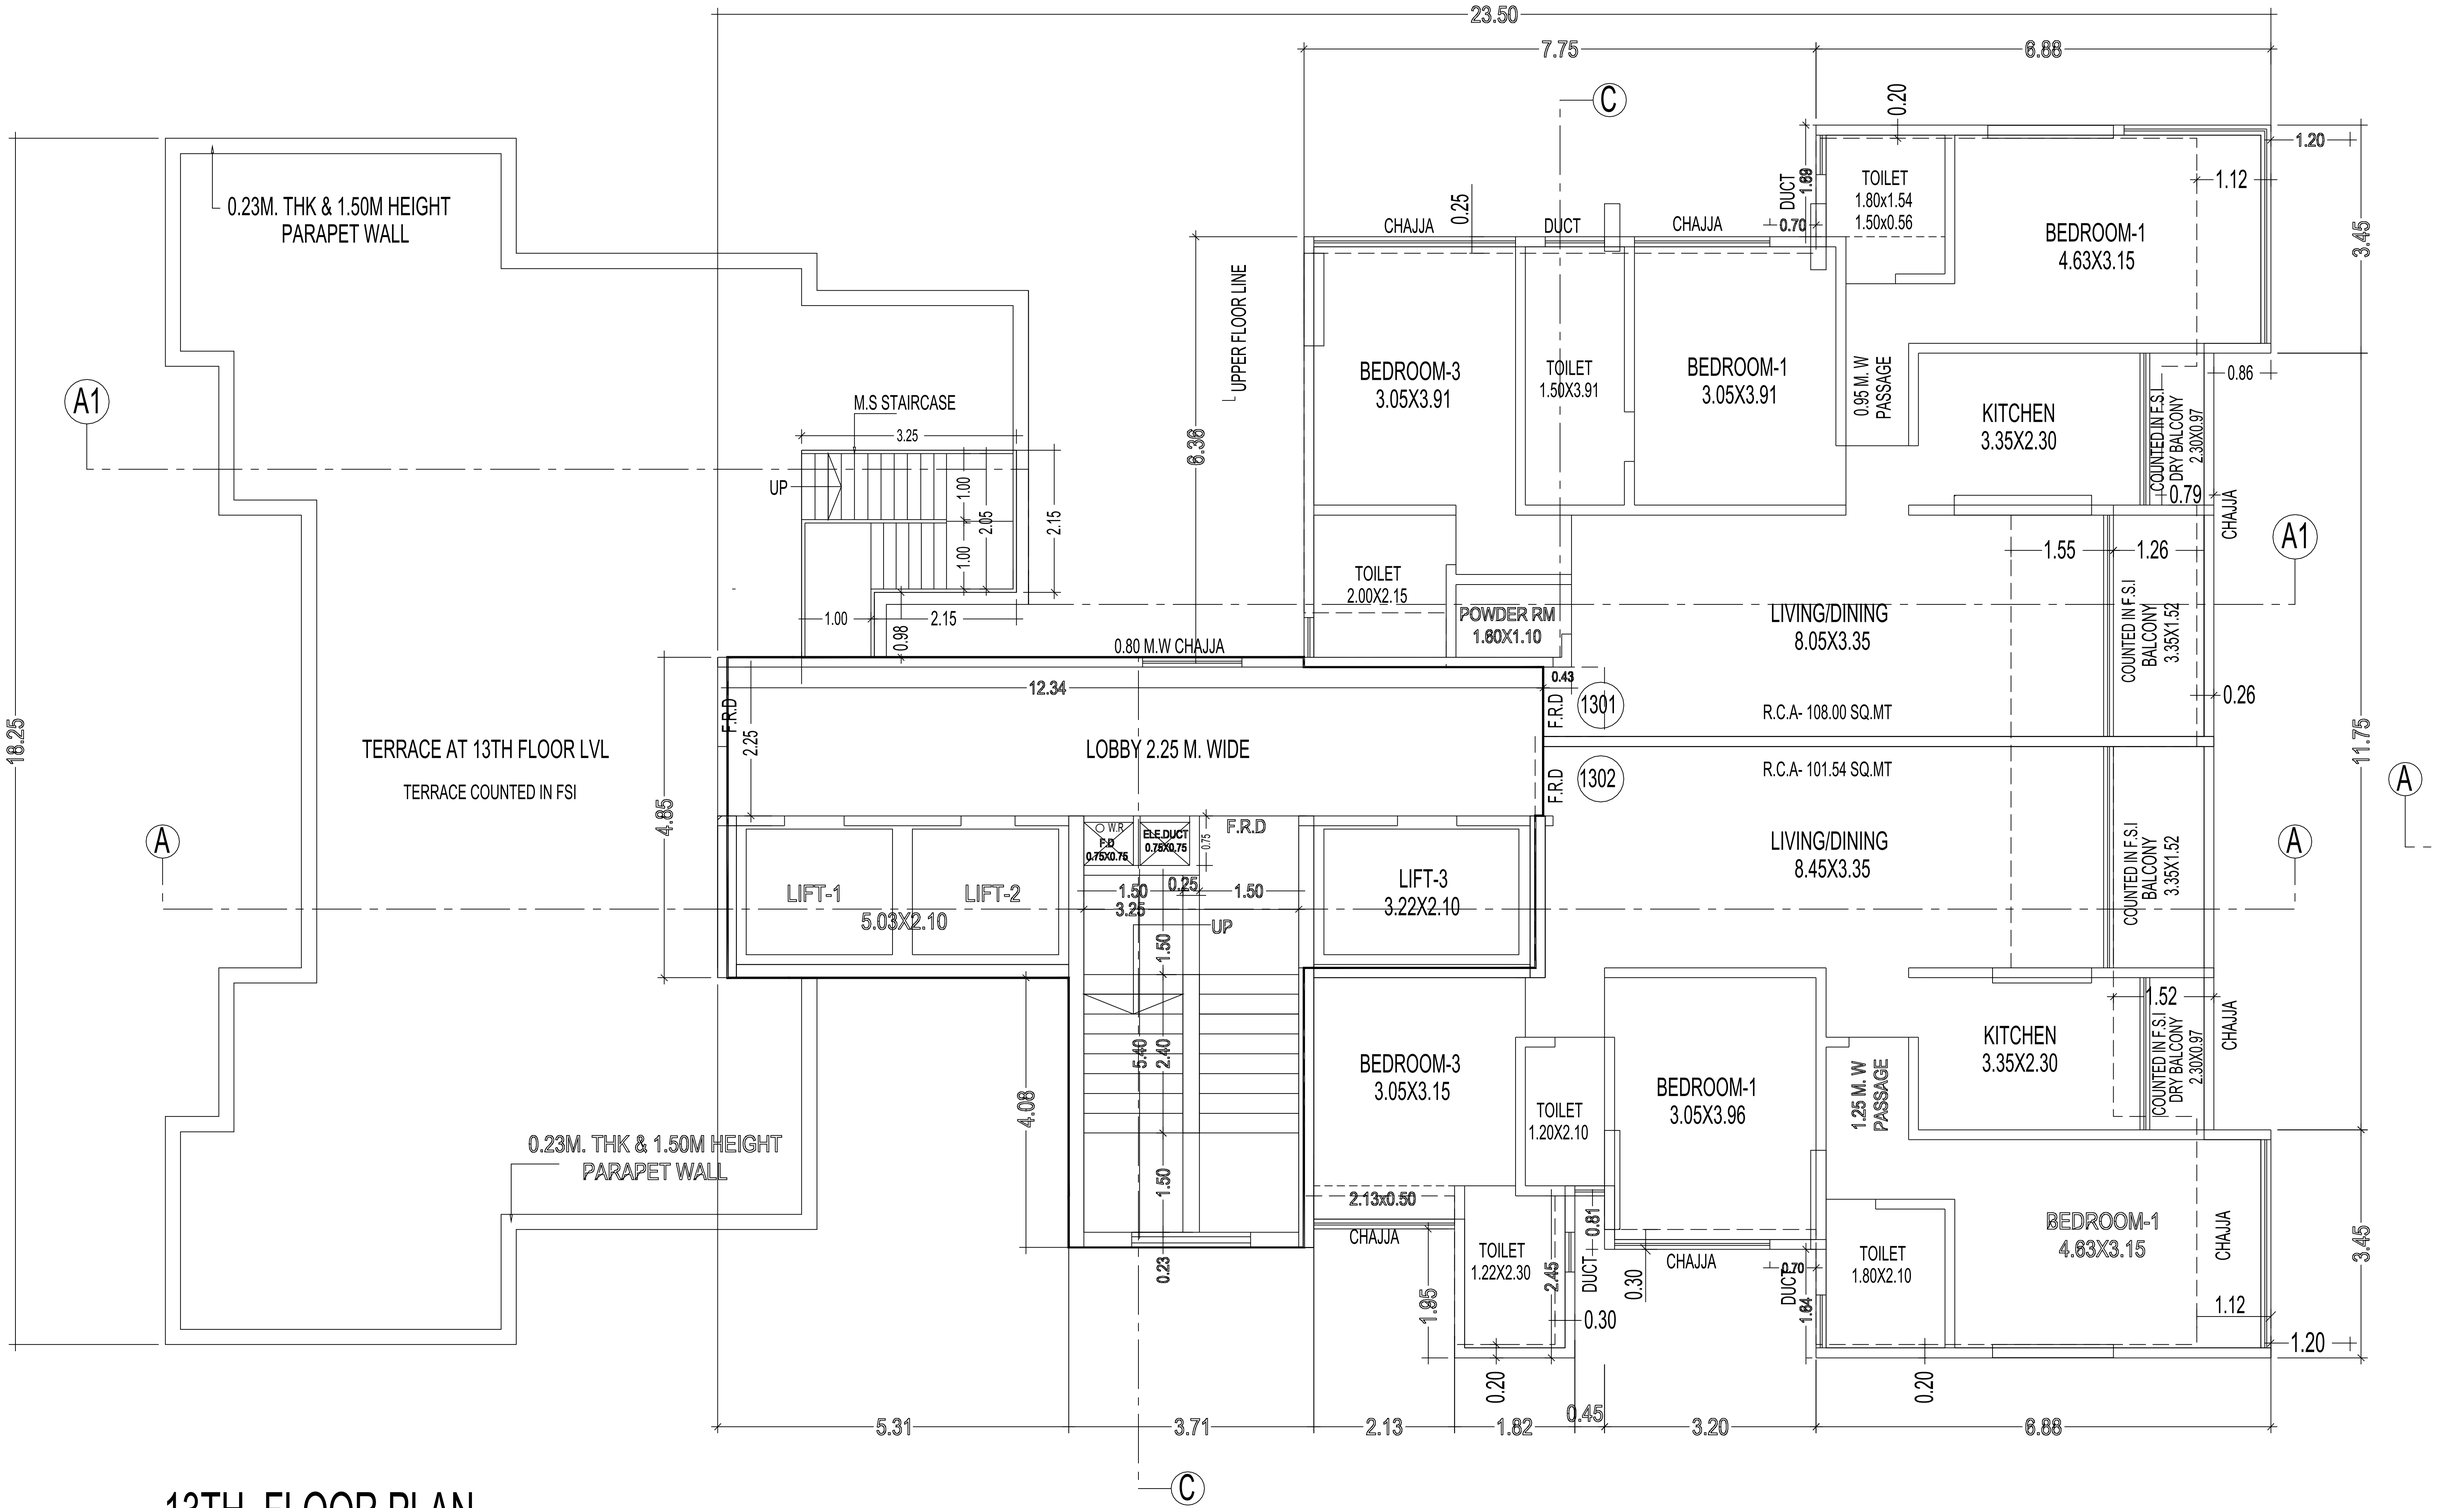


13TH. FLOOR PLAN

SCALE 1:100

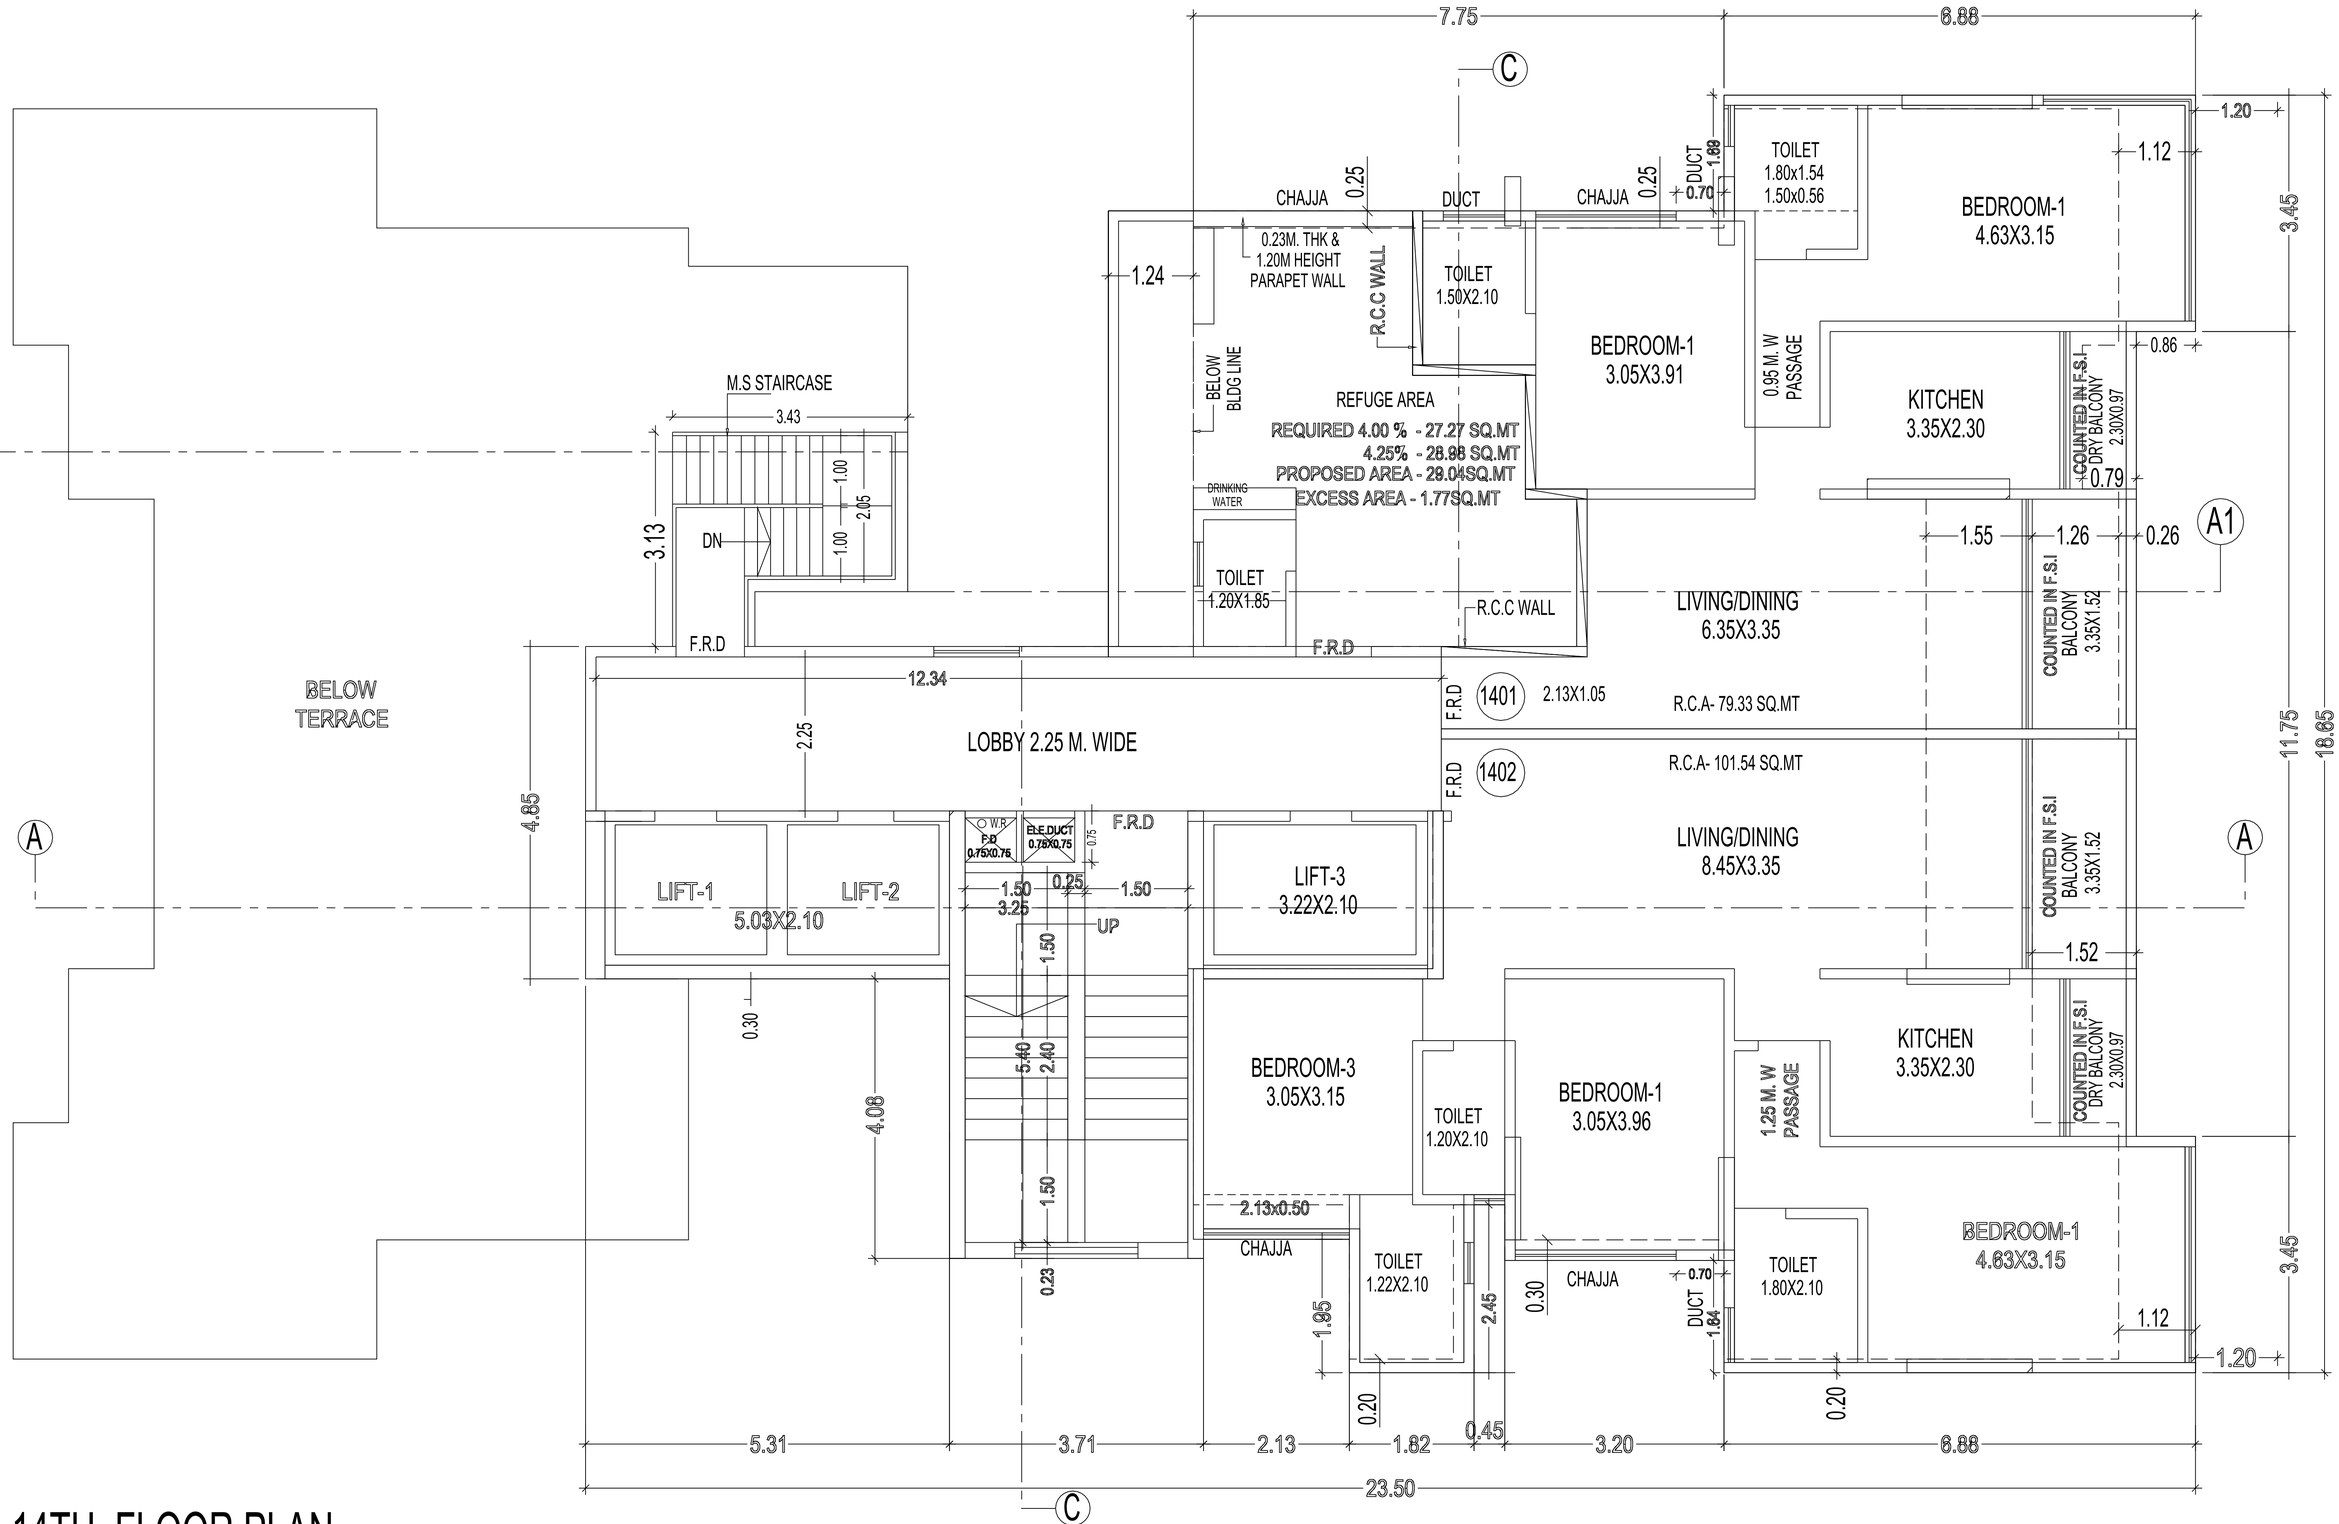

14TH. FLOOR PLAN

SCALE 1:100

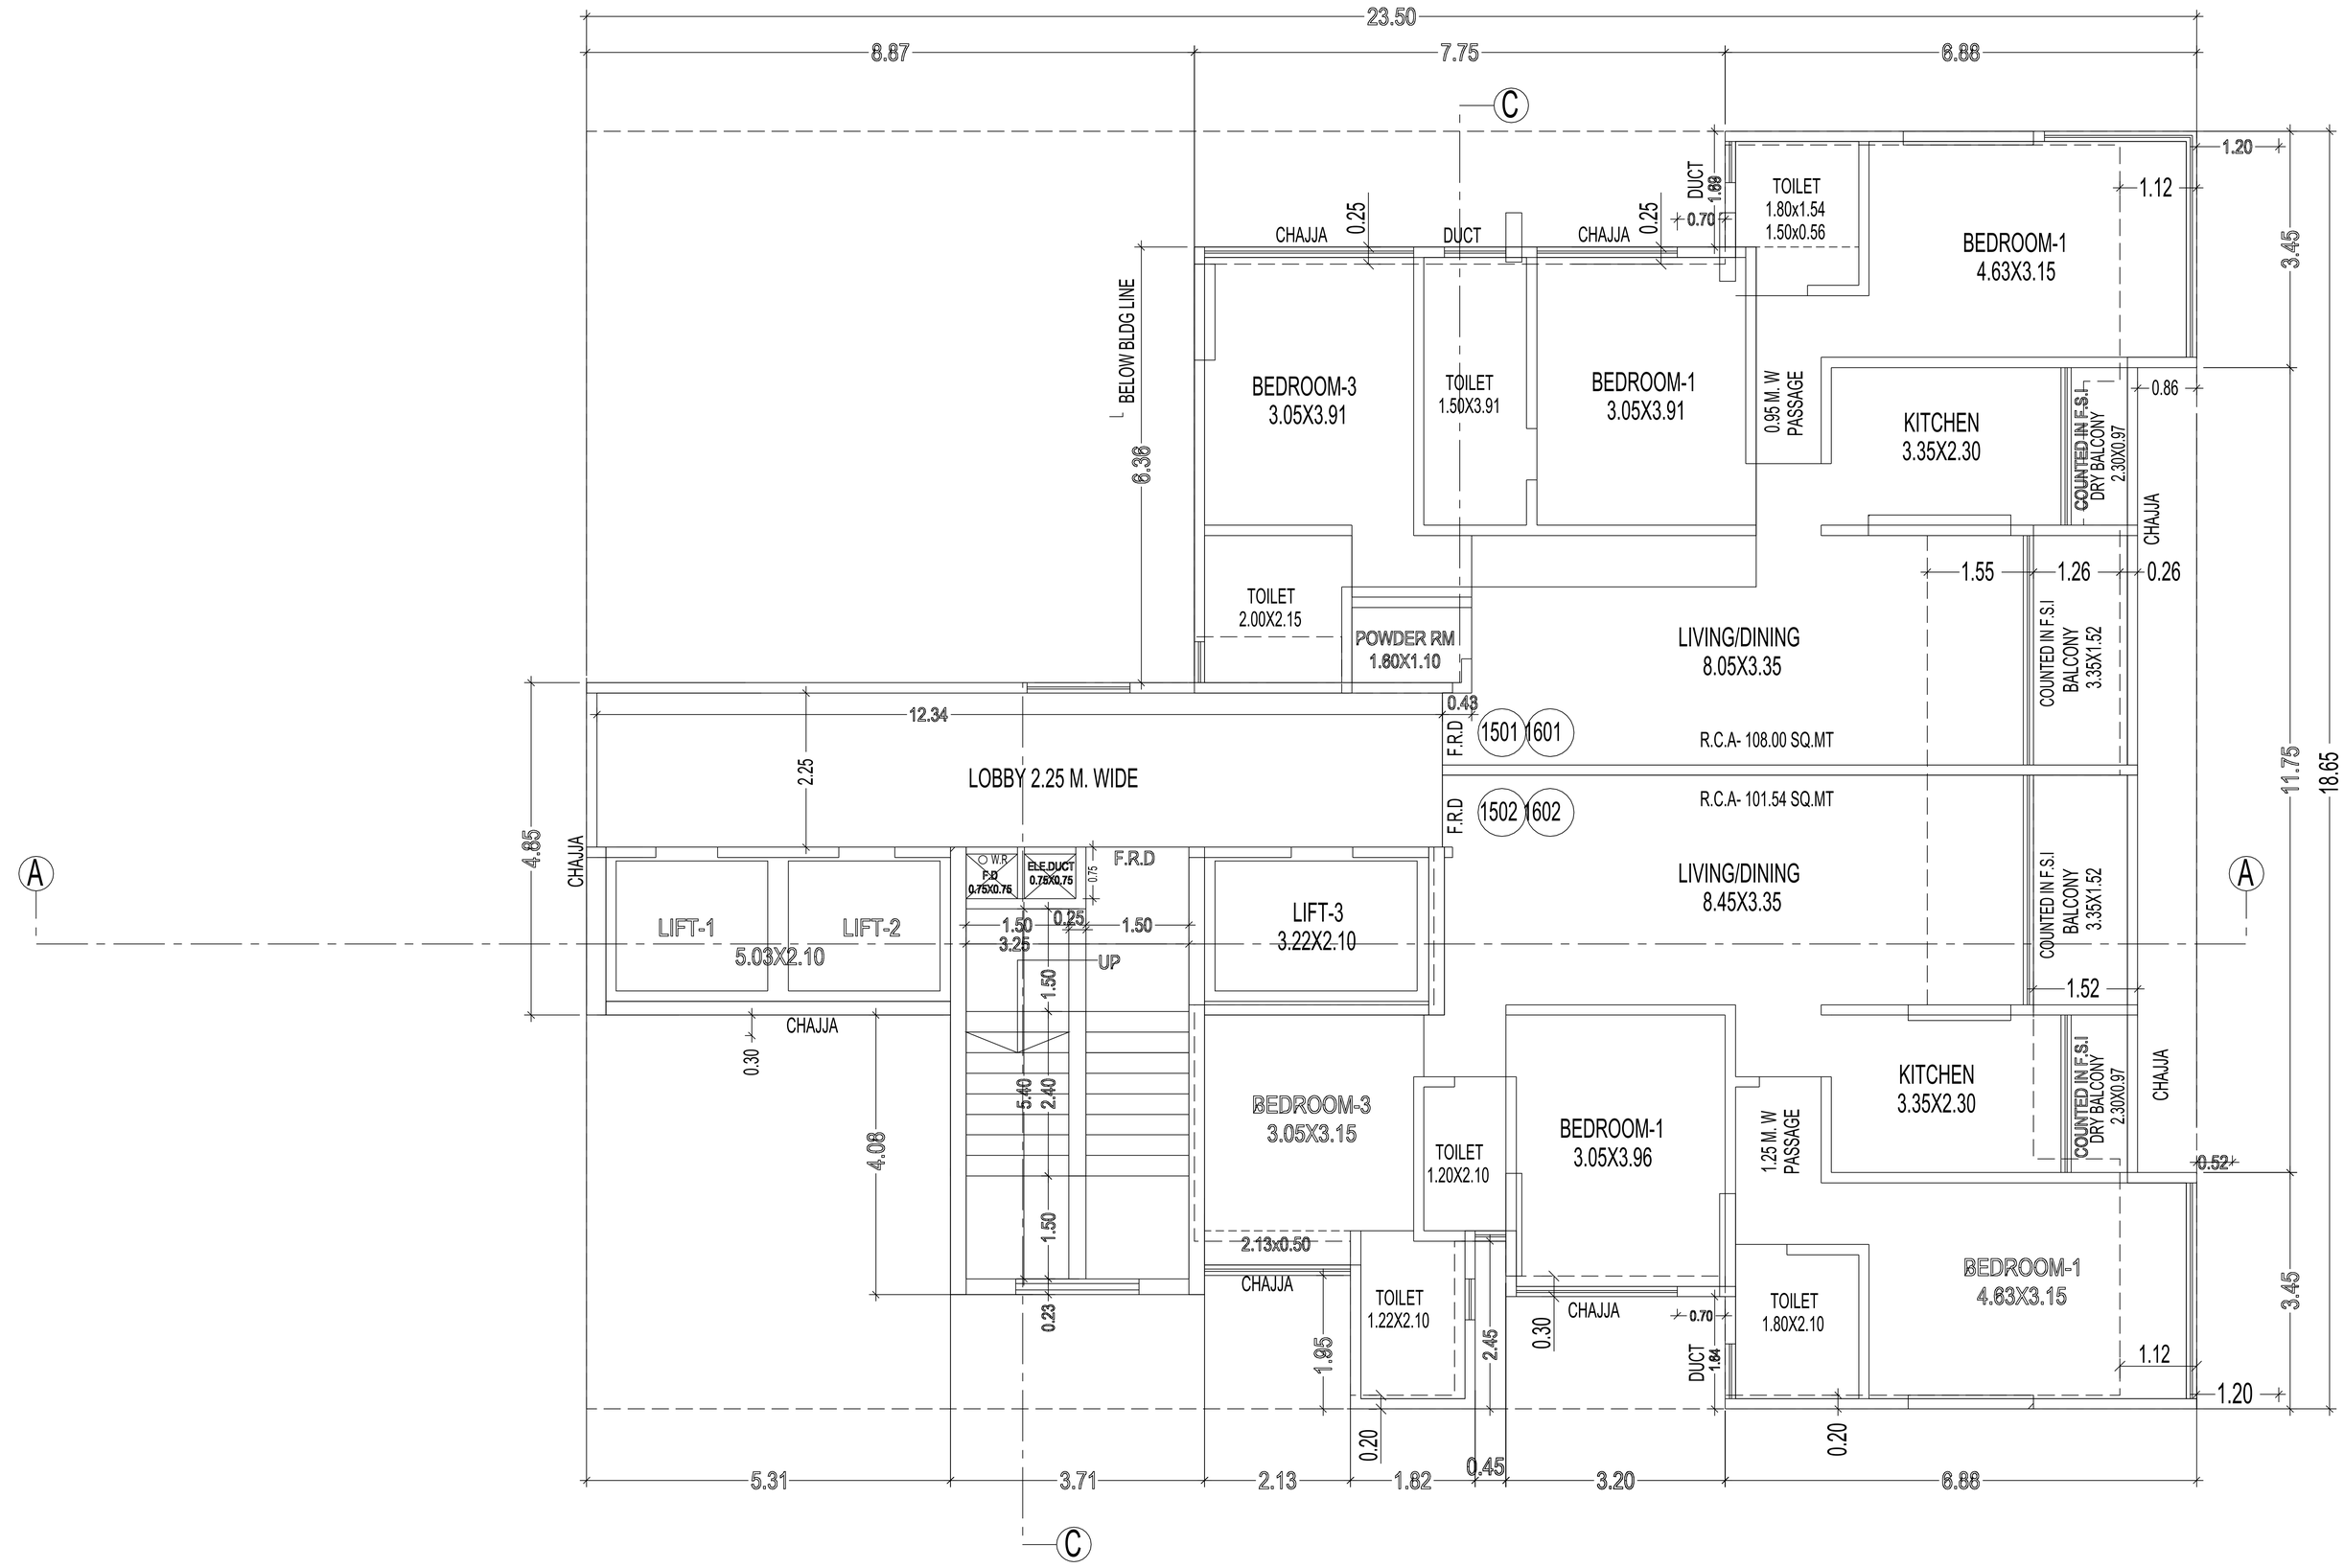

TYPICAL FLOOR PLAN (15TH & 16TH FLOOR)

SCALE 1:100