


SALE / MEMBER TOWER 3


SALE TOWER 4
1ST,4TH TO 7TH & 9TH TO 15TH FLOOR PLAN

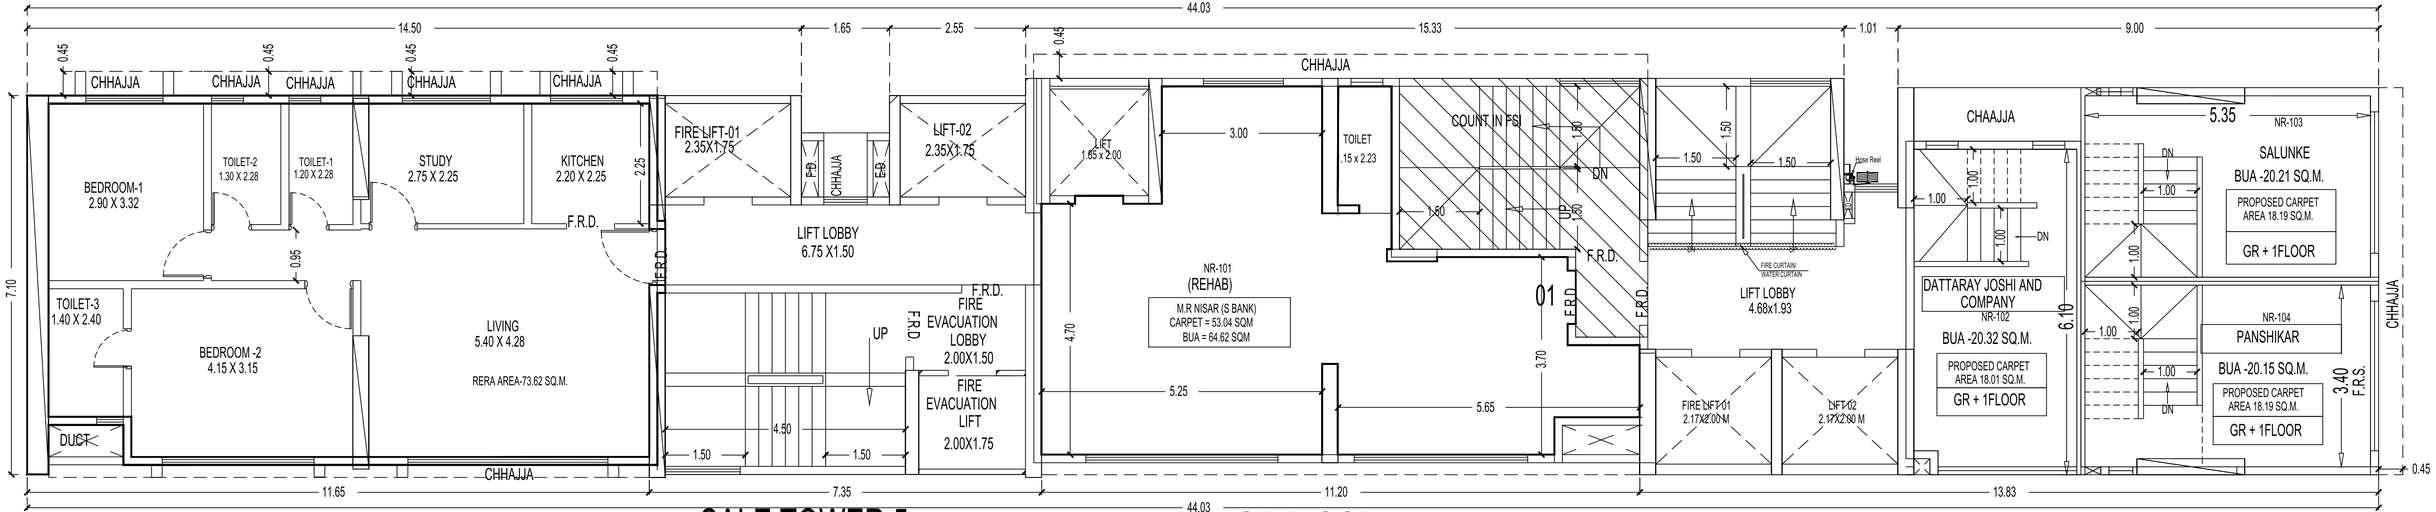

SALE TOWER 5

1ST FLOOR PLAN

NR BUILDING

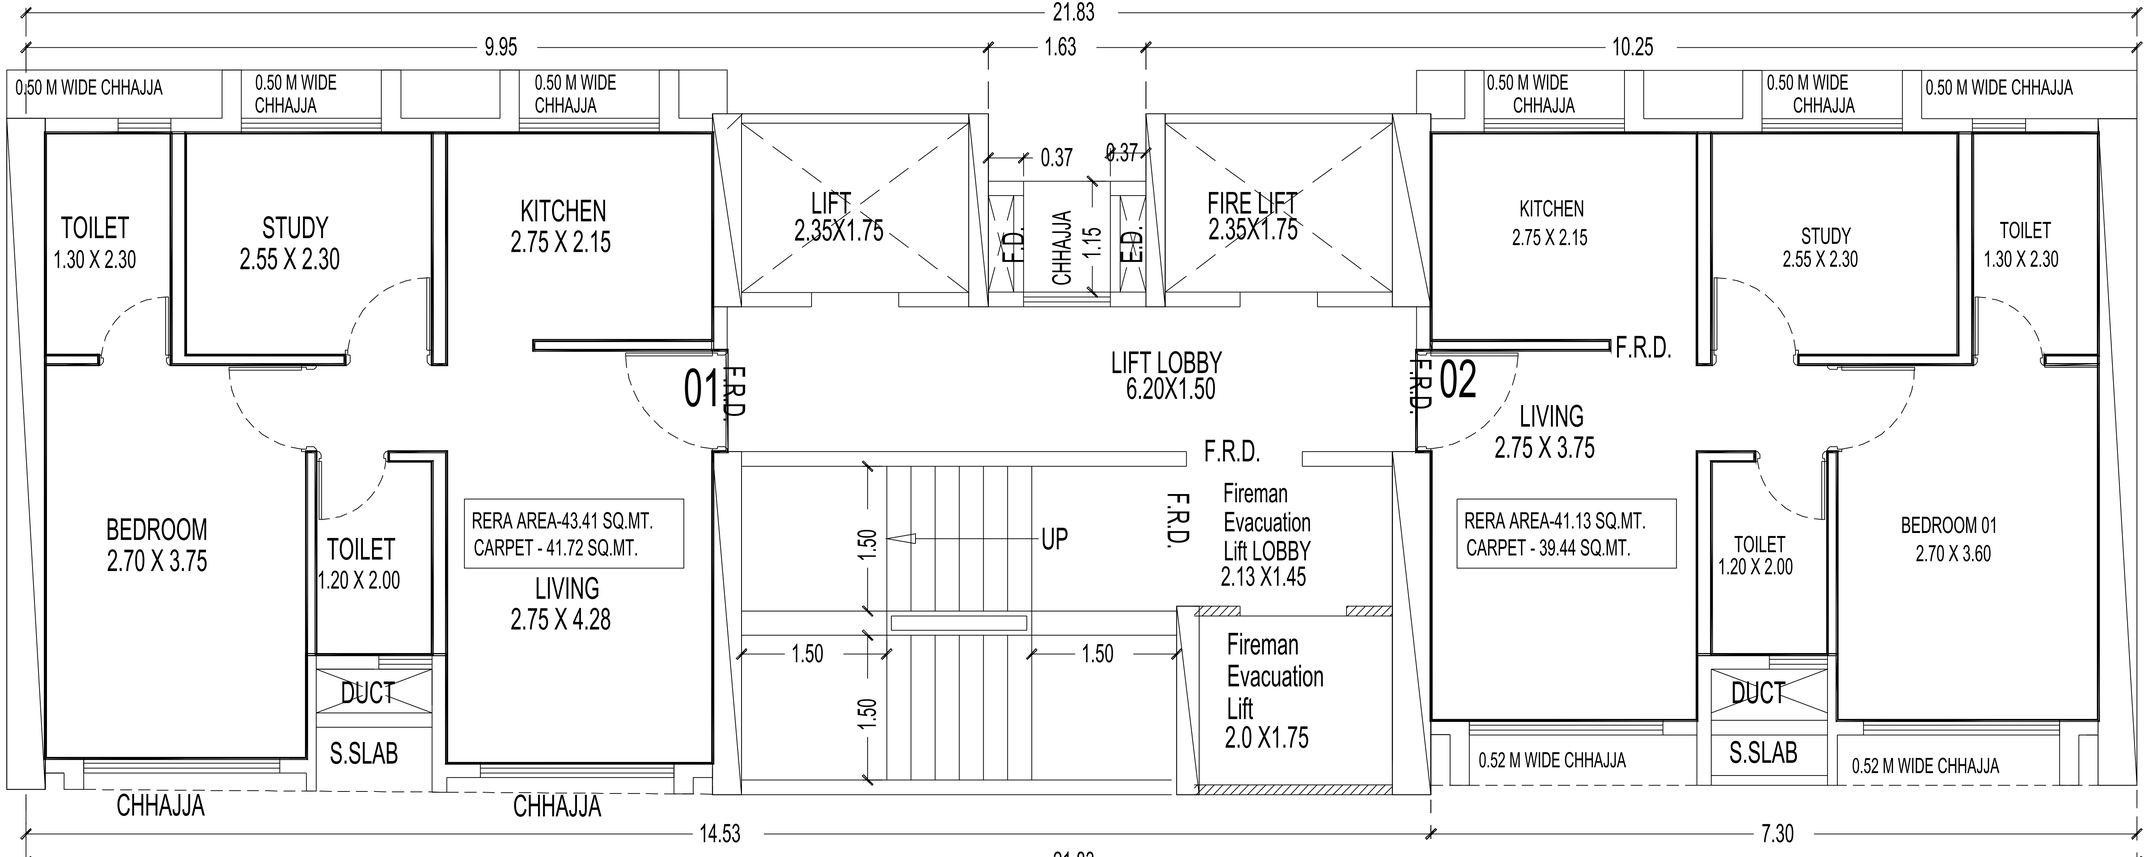


L1

L2

L3

TOTAL LIFT AREA


SALE TOWER 4
2ND & 3RD FLOOR PLAN

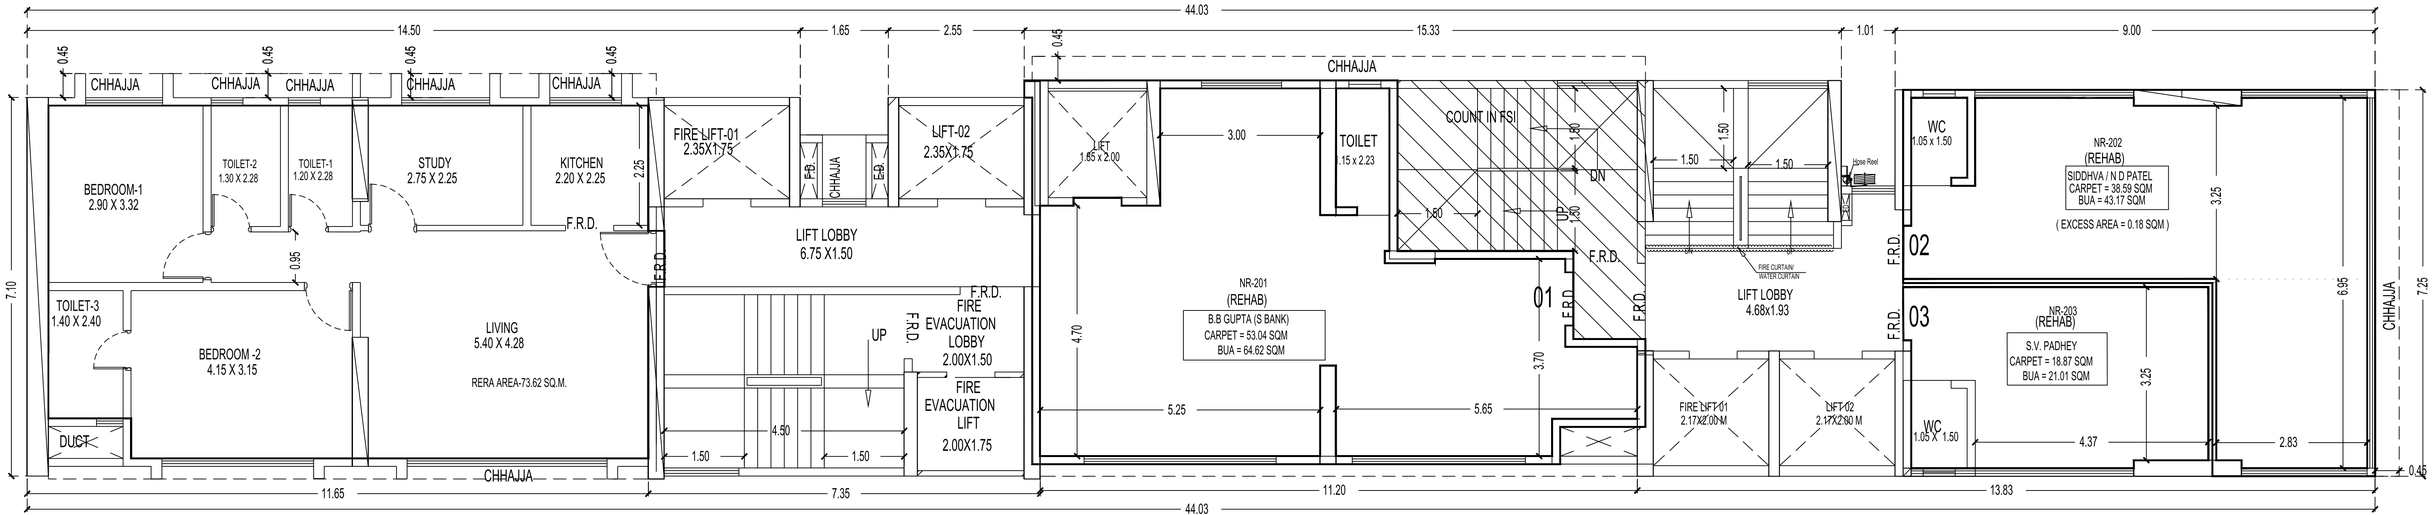

SALE TOWER 5

2ND FLOOR PLAN


NR BUILDING

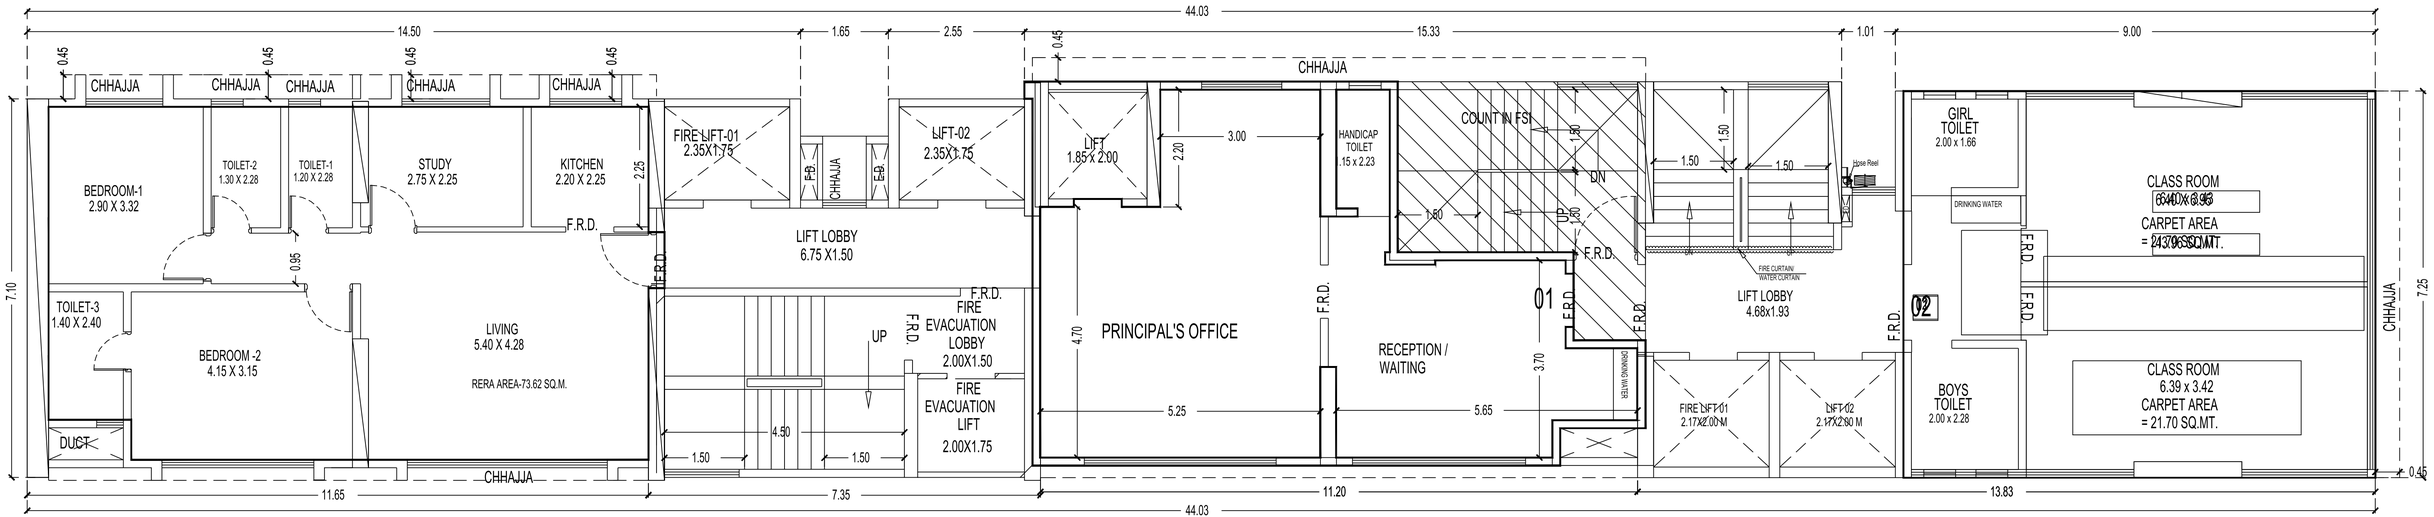


SALE TOWER 5


3RD FLOOR PLAN

NR BUILDING

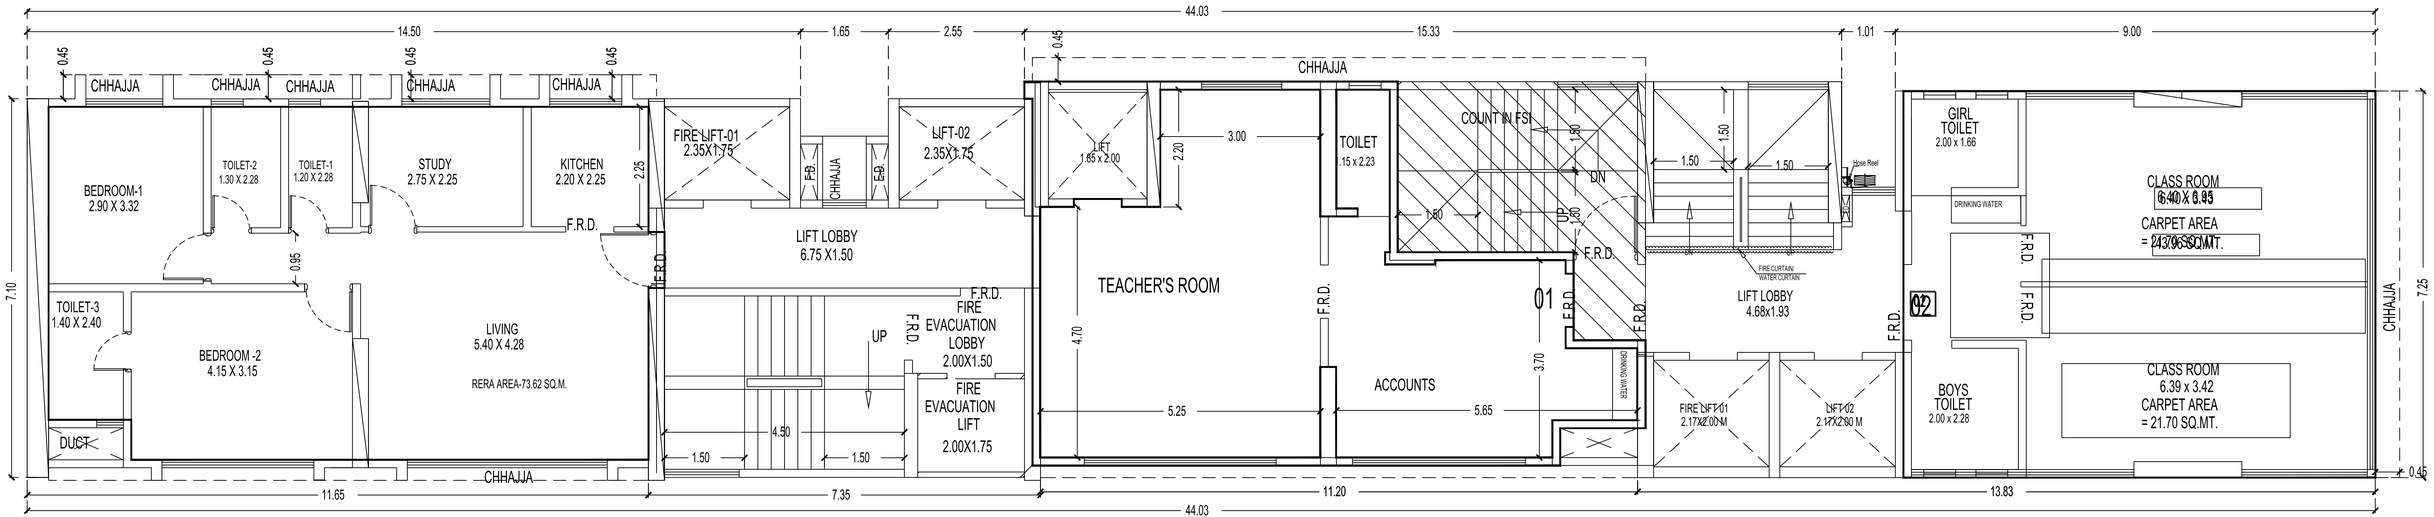


SALE TOWER 5 — 4TH FLOOR PLAN — NR BUILDING

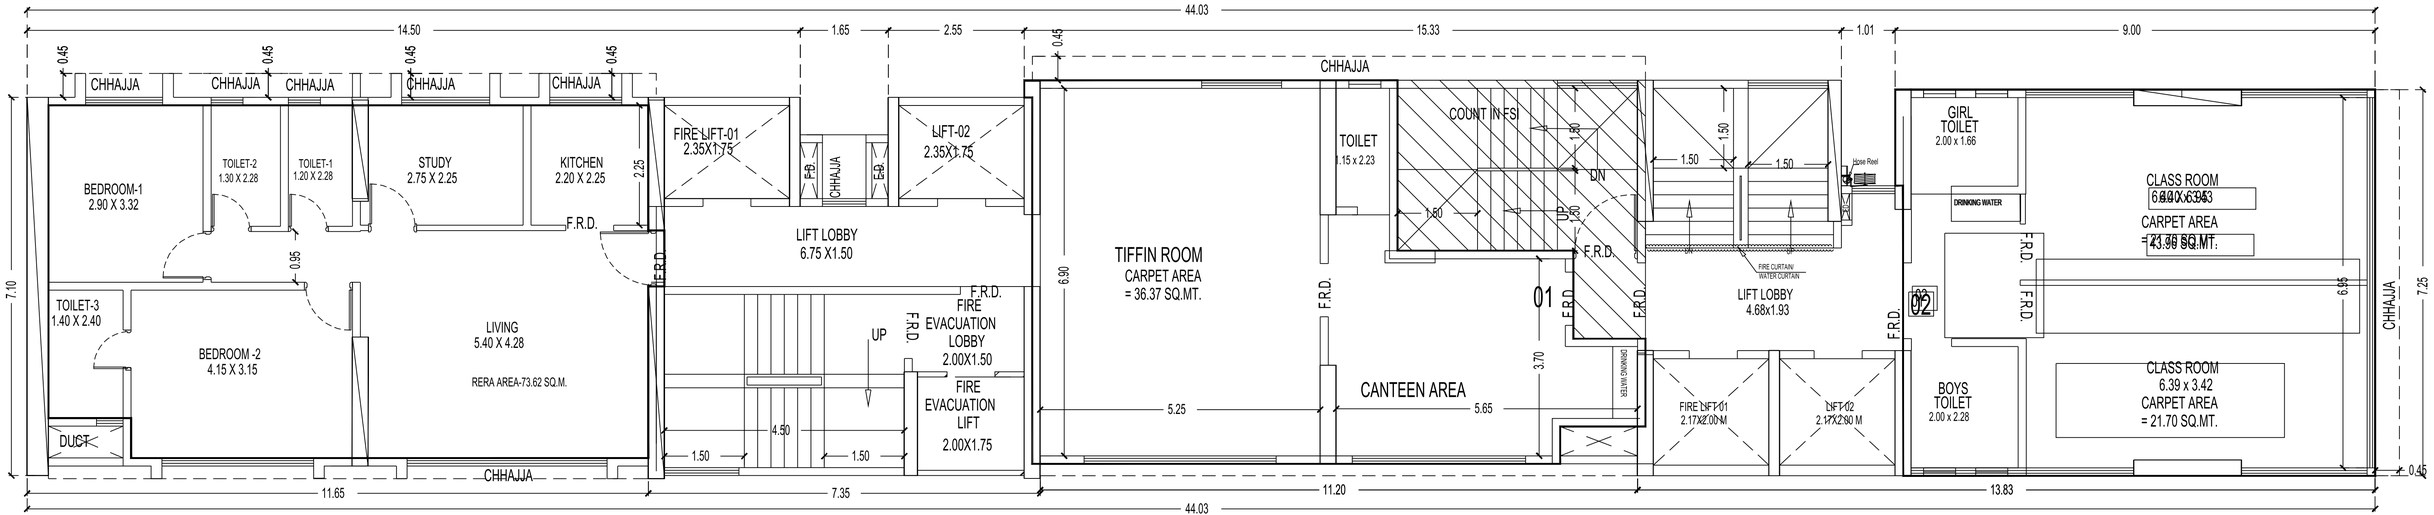

44.03
14.50
1.65
2.55
0.45
15.33
1.01
9.00
CHHAJJA
BEDROOM-1
2.90 X 3.32
TOILET-2
1.30 X 2.28
TOILET-1
1.20 X 2.28
STUDY
2.75 X 2.25
KITCHEN
2.20 X 2.25
2.25
F.R.D.
0.95
TOILET-3
1.40 X 2.40
BEDROOM -2
4.15 X 3.15
LIVING
5.40 X 4.28
RERA AREA-73.62 SQ.M.
DUCT
7.10
FIRE LIFT-01
2.35X1.75
F.B.
LIFT-02
2.35X1.75
LIFT LOBBY
6.75 X1.50
UP
FIRE
EVACUATION
LOBBY
2.00X1.50
FIRE
EVACUATION
LIFT
2.00X1.75
4.50
1.50
TIFFIN ROOM
CARPET AREA
= 36.37 SQ.MT.
6.90
TOILET
1.15 x 2.23
COUNT IN FS
1.80
DN
1.60
01
CANTEEN AREA
5.25
5.65
3.70
SPRINKLER WATER
1.50
Hose Reel
FIRE CURTAIN/
WATER CURTAIN
LIFT LOBBY
4.68x1.93
02
FIRE LIFT-01
2.17X2.00 M
LIFT-02
2.17X2.00 M
GIRL
TOILET
2.00 x 1.66
DRINKING WATER
CLASS ROOM
6.39 x 3.42
CARPET AREA
= 21.70 SQ.MT.
6.95
BOYS
TOILET
2.00 x 2.28
CLASS ROOM
6.39 x 3.42
CARPET AREA
= 21.70 SQ.MT.
7.25
11.65
7.35
11.20
13.83
SALE TOWER 5
5TH FLOOR PLAN
NR BUILDING

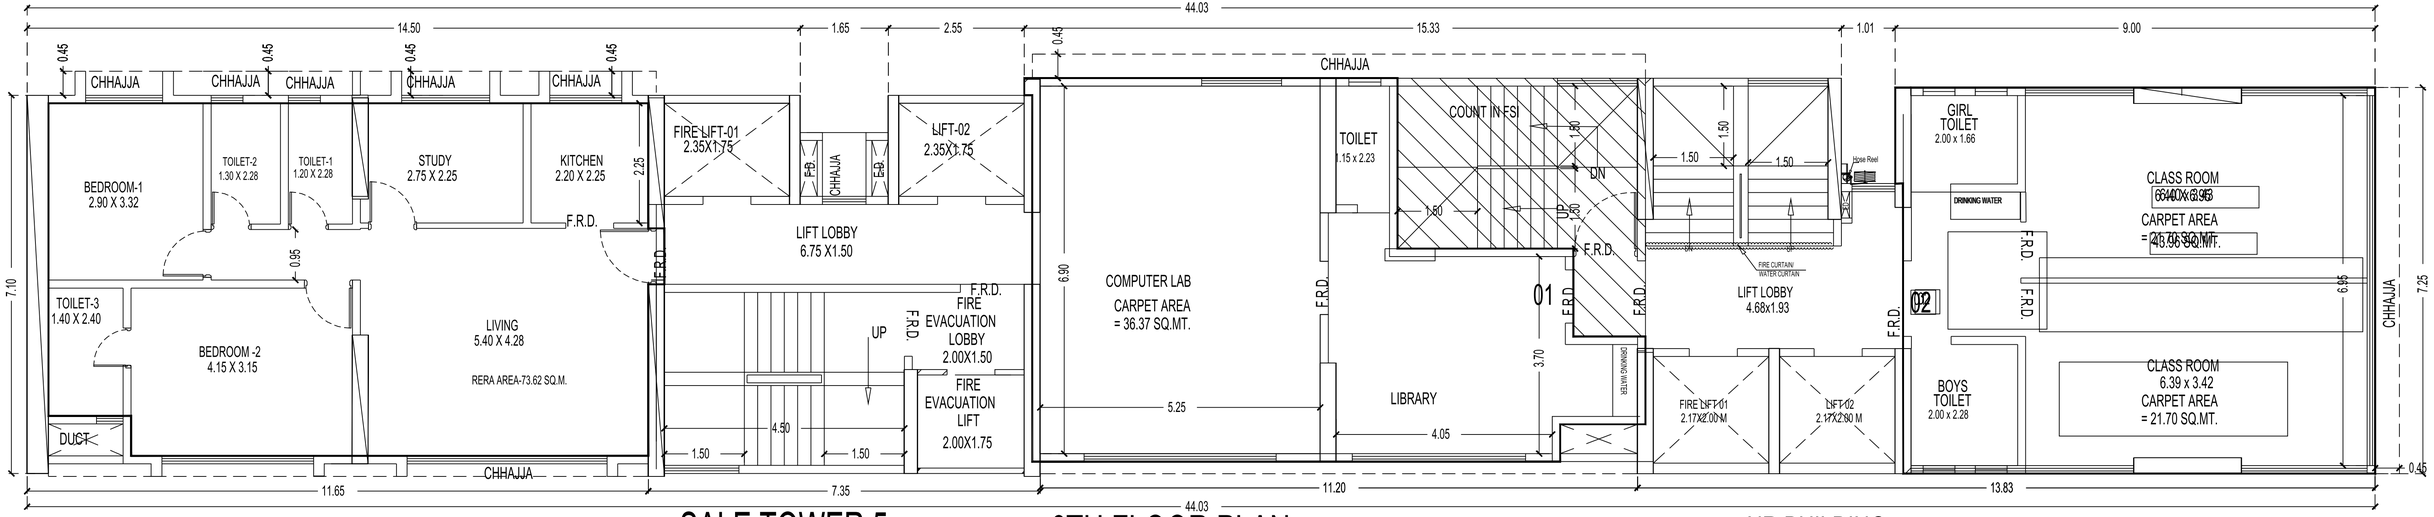

SALE TOWER 5 6TH FLOOR PLAN NR BUILDING

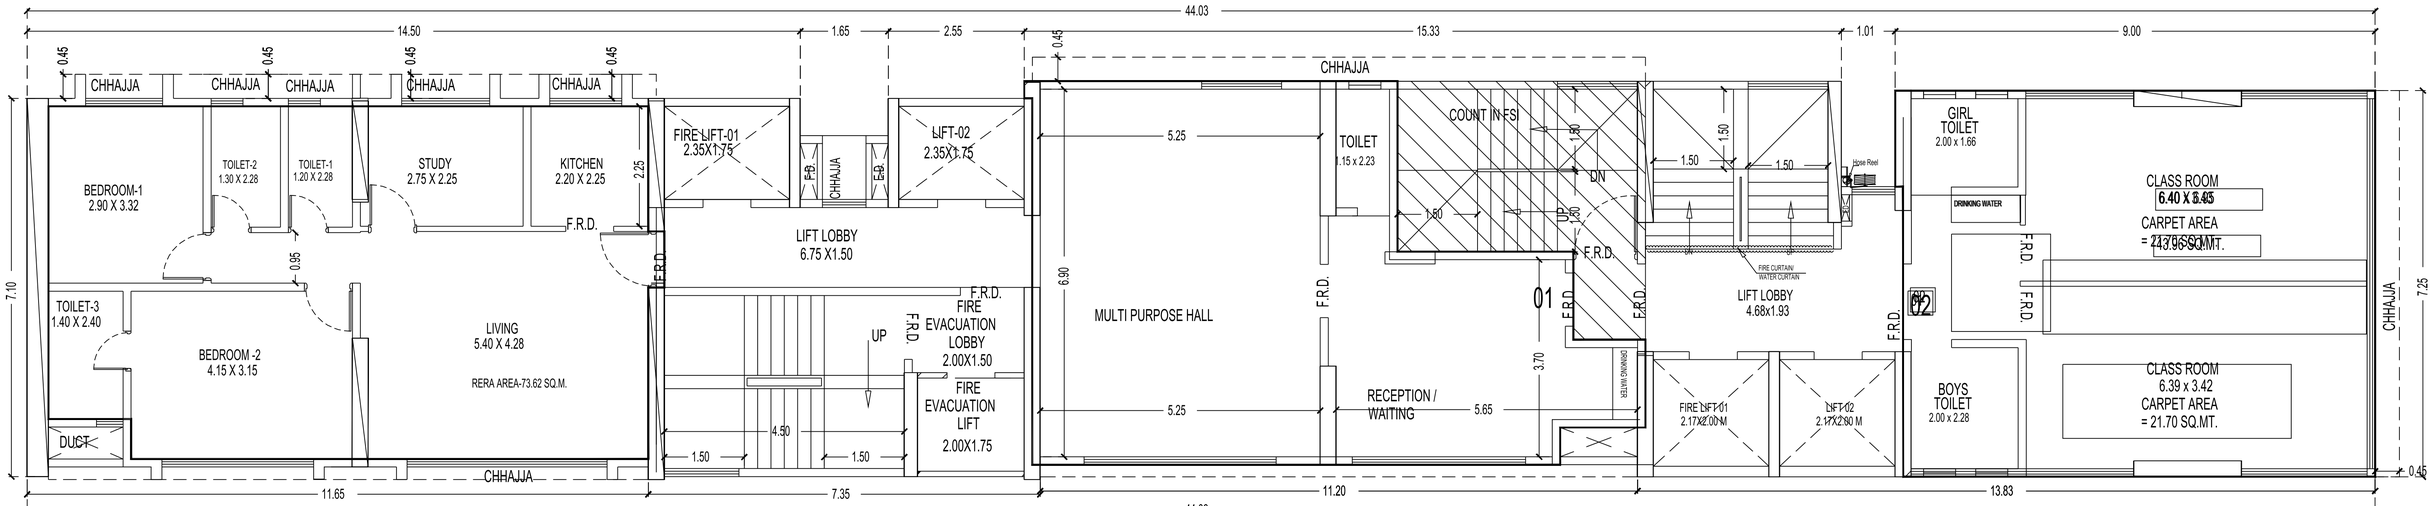


SALE TOWER 5 — 7TH FLOOR PLAN — NR BUILDING

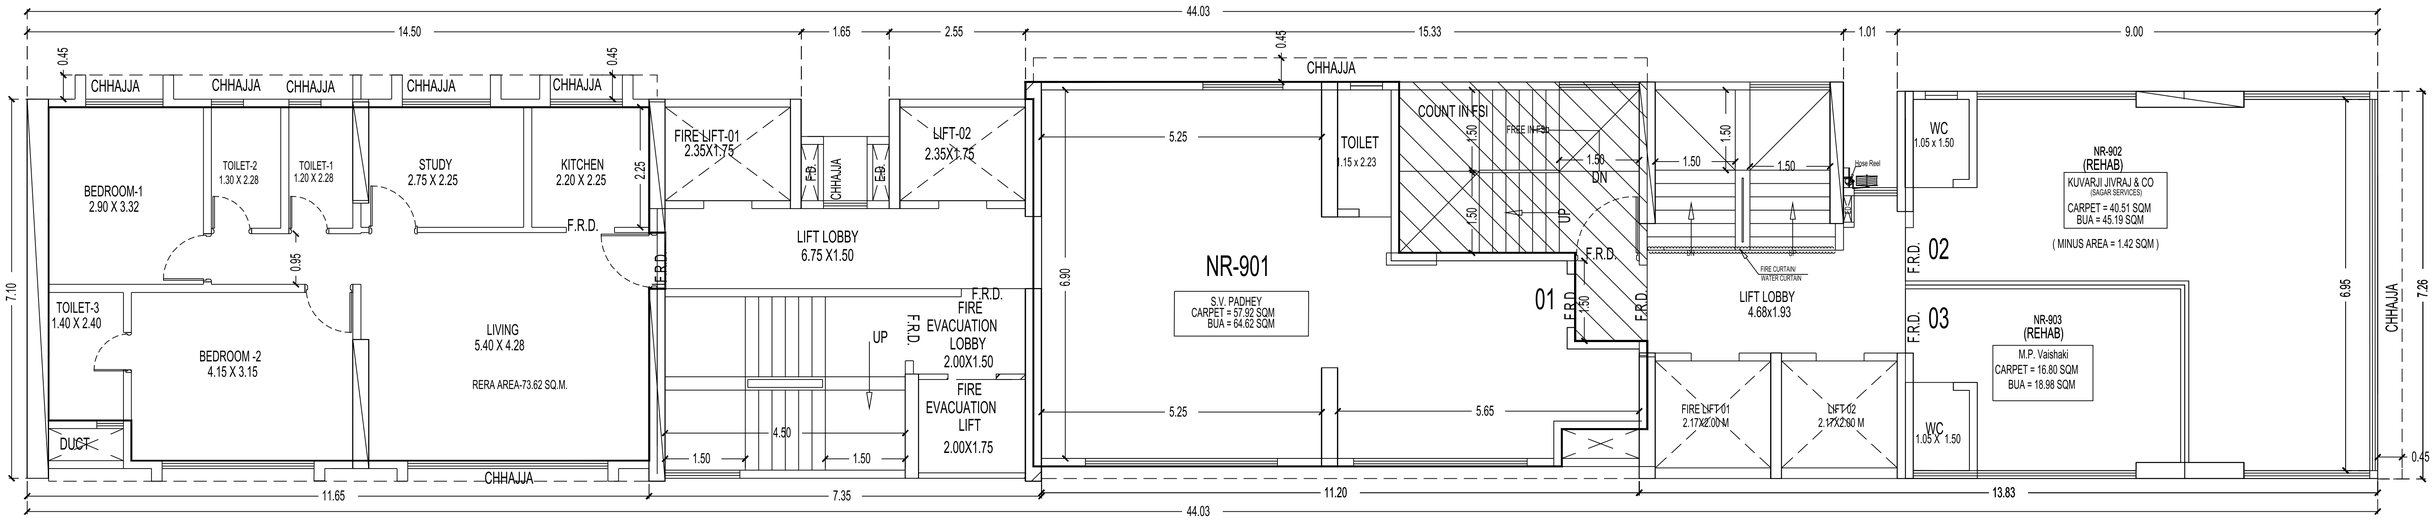


SALE TOWER 5

9TH FLOOR PLAN

NR BUILDING

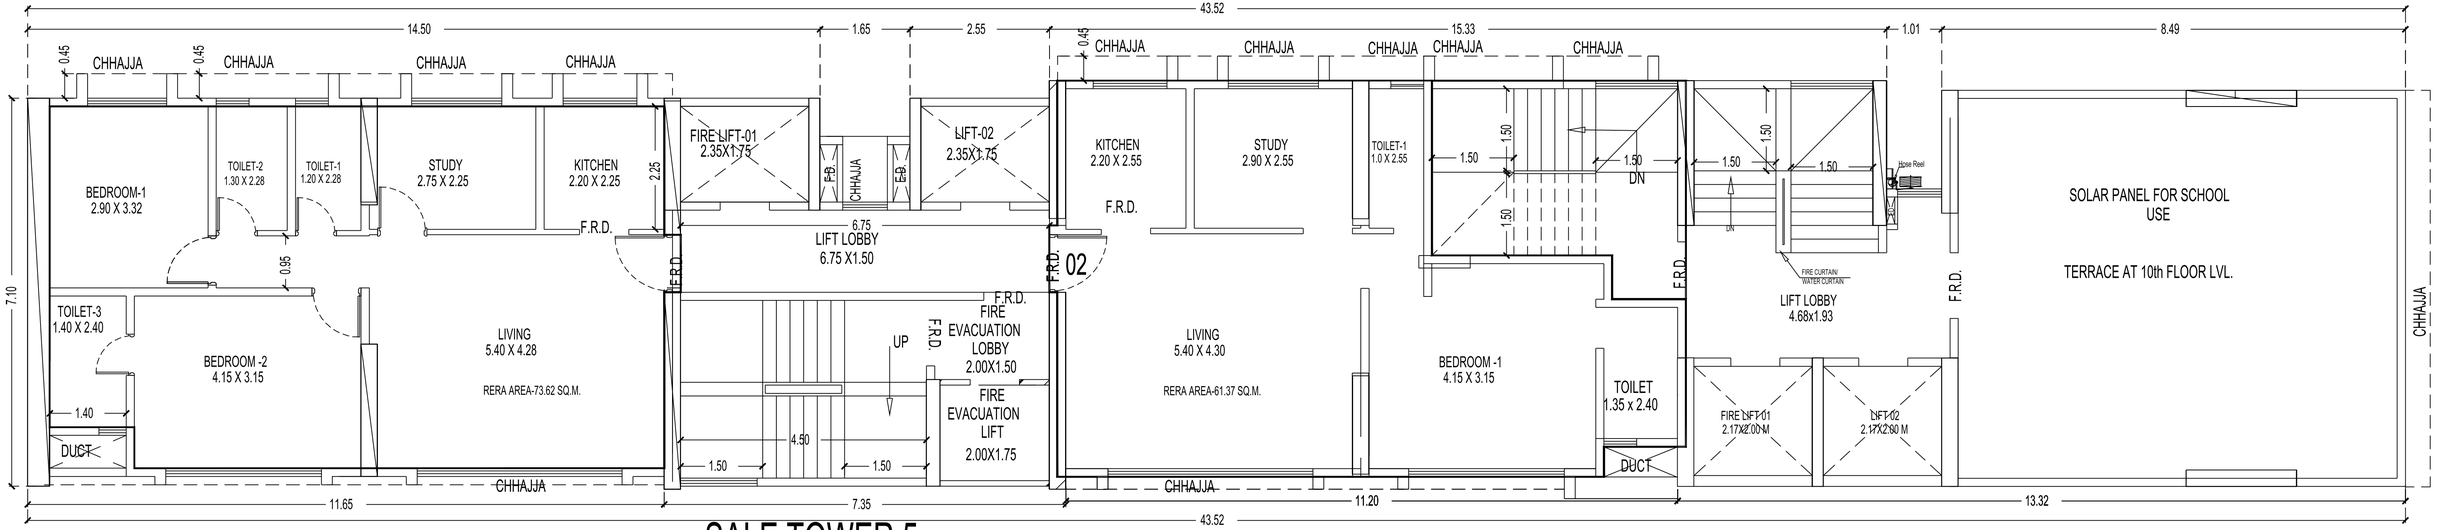

SALE TOWER 5
10TH FLOOR PLAN

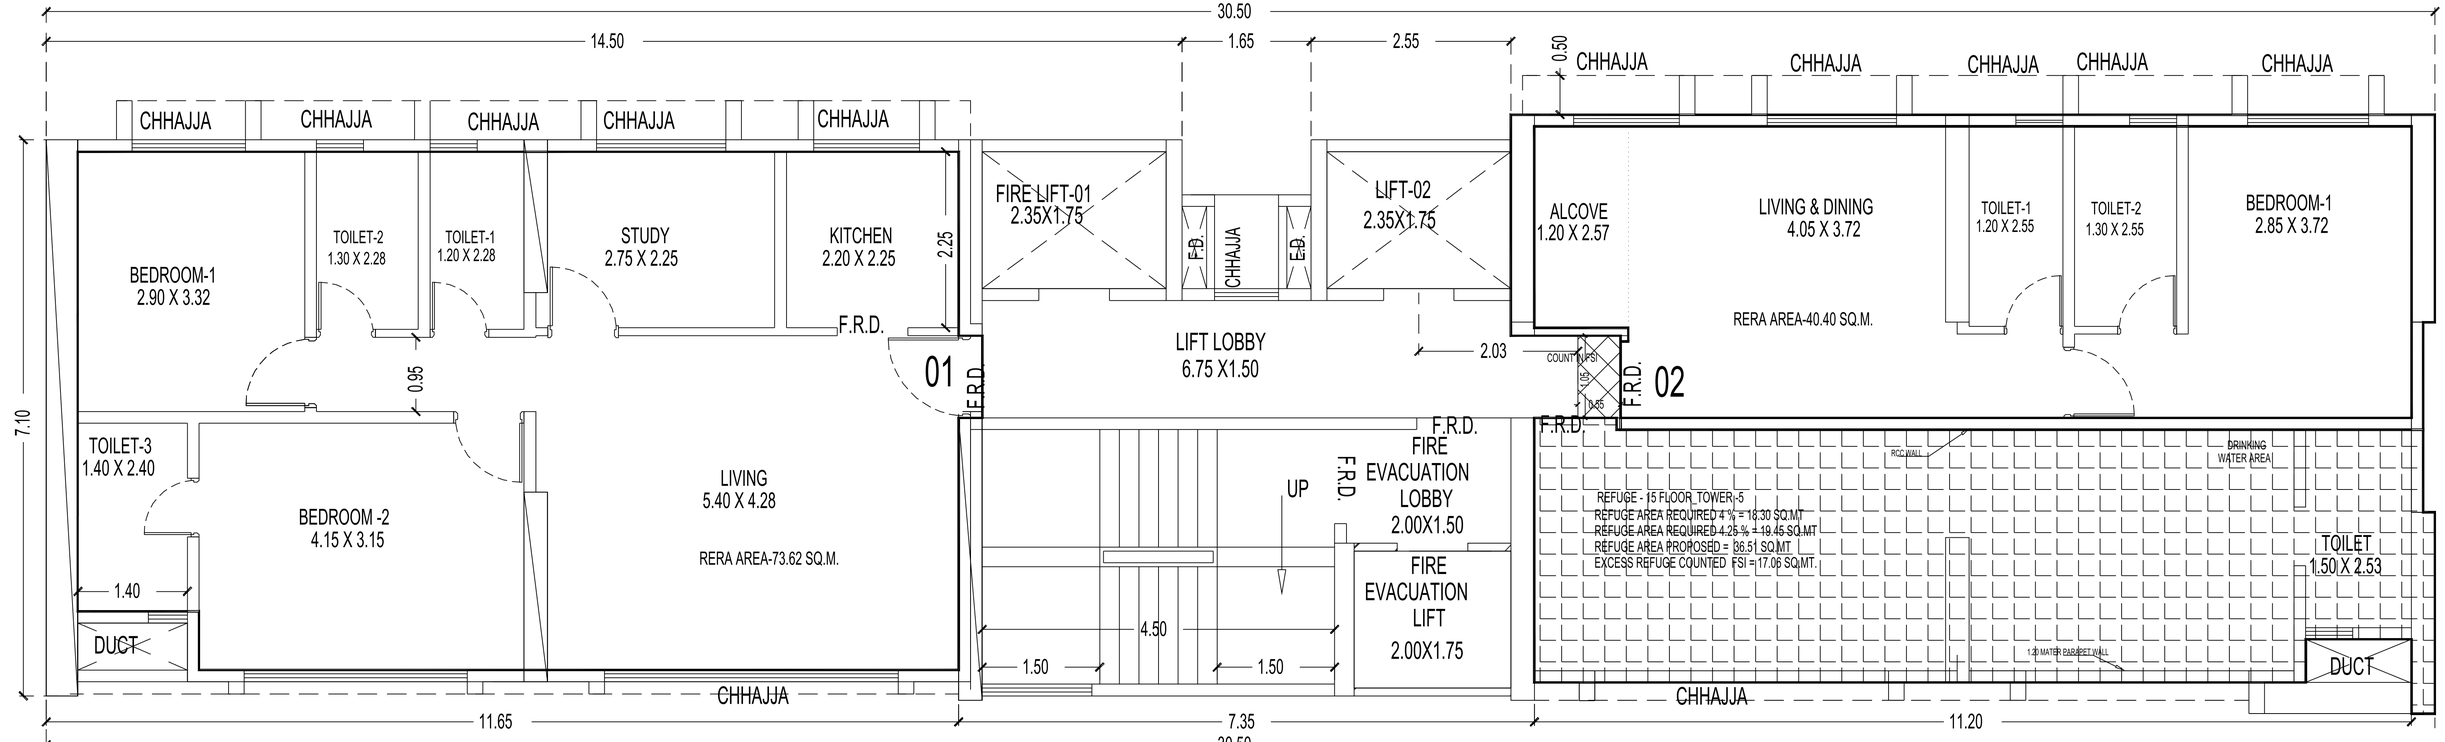

SALE TOWER 5
15TH REFUGE FLOOR PLAN