45.50 MT. WIDE D.P ROAD

SOUTH

EAST

WEST

NORTH

18.30 MT. WIDE D.P ROAD

SET BACK AREA

BUILDING LINE ABOVE

DOUBLE HEIGHT

1.50 MT. HT PARAPET WALL

TERRACE OPEN TO SKY

SOCIETY OFFICE
3.41 X 4.13
PERMI. AREA - 20.00 SQMT.
PROP. AREA - 20.00 SQMT.

LIFT 2.37 X 2.37

4.34 M. WIDE PASSAGE

2.00 M. WIDE PASSAGE C-WING

2.00 M. WIDE PASSAGE

KITCHEN 2.60 x 2.53

FIRE LIFT 2.75 X 2.10

STORE 2.10 X 1.75

TOILET 1.15 X 1.75

CHAJJA

FIRE LIFT 2.30 X 2.30

SMOKE CHECK LOBBY 1.30 X 2.28

LIFT 2.52 X 2.10

LIVING \ DINNING 9.66 X 3.83
RERA CARPET 136.87 SQ.MT.

DECK 1.68 X 3.83

BEDROOM 4.73 X 3.78

TOILET 1.52 X 2.55

TOILET 1.63 X 1.20

TOILET 1.53 X 2.55

PASS 1.10 X 3.78

BEDROOM 3.32 X 3.38

BEDROOM 4.57 X 3.78

CHAJJA WITH C CHANNEL

2.00 M. WIDE PASSAGE B-WING

TOILET 1.54 X 2.55

BEDROOM 4.57 X 3.53

LIVING \ DINNING 9.18 X 3.83
RERA CARPET 137.56 SQ.MT.

2.00 M. WIDE PASSAGE A-WING

BEDROOM 4.14 X 2.35

BED RM 2.80 X 2.70

LIVING/KITCHEN 4.19 X 3.00
RERA CARPET 28.15 SQ.MT.
TO BE HANDED OVER TO BMC.

2.05 X 2.00

LIVING 3.00 X 3.70
RERA CARPET 28.56 SQ.MT.
TO BE HANDED OVER TO BMC.

KITCHEN 1.89 X 2.70

LIVING 4.29 X 3.00
RERA CARPET 28.46 SQ.MT.
TO BE HANDED OVER TO BMC.

ALCOVE 1.79X3.80

BED RM 2.40 X 2.70

ALCOVE 1.79 X 3.80

BED ROOM 2.40 X 2.70

LIVING ROOM 4.29 X 3.00
RERA CARPET 28.46 SQ.MT.
TO BE HANDED OVER TO BMC.

LIVING / KITCHEN 4.19 X 3.00
RERA CARPET 28.15 SQ.MT.
TO BE HANDED OVER TO BMC.

1.50MT.WIDE PASSAGE


0.90 M. WI. PASS

COUNTED IN FSI

1ST FLOOR PLAN
SCALE -1:100


1ST FLOOR PLAN
SCALE:-1:100

D - WING

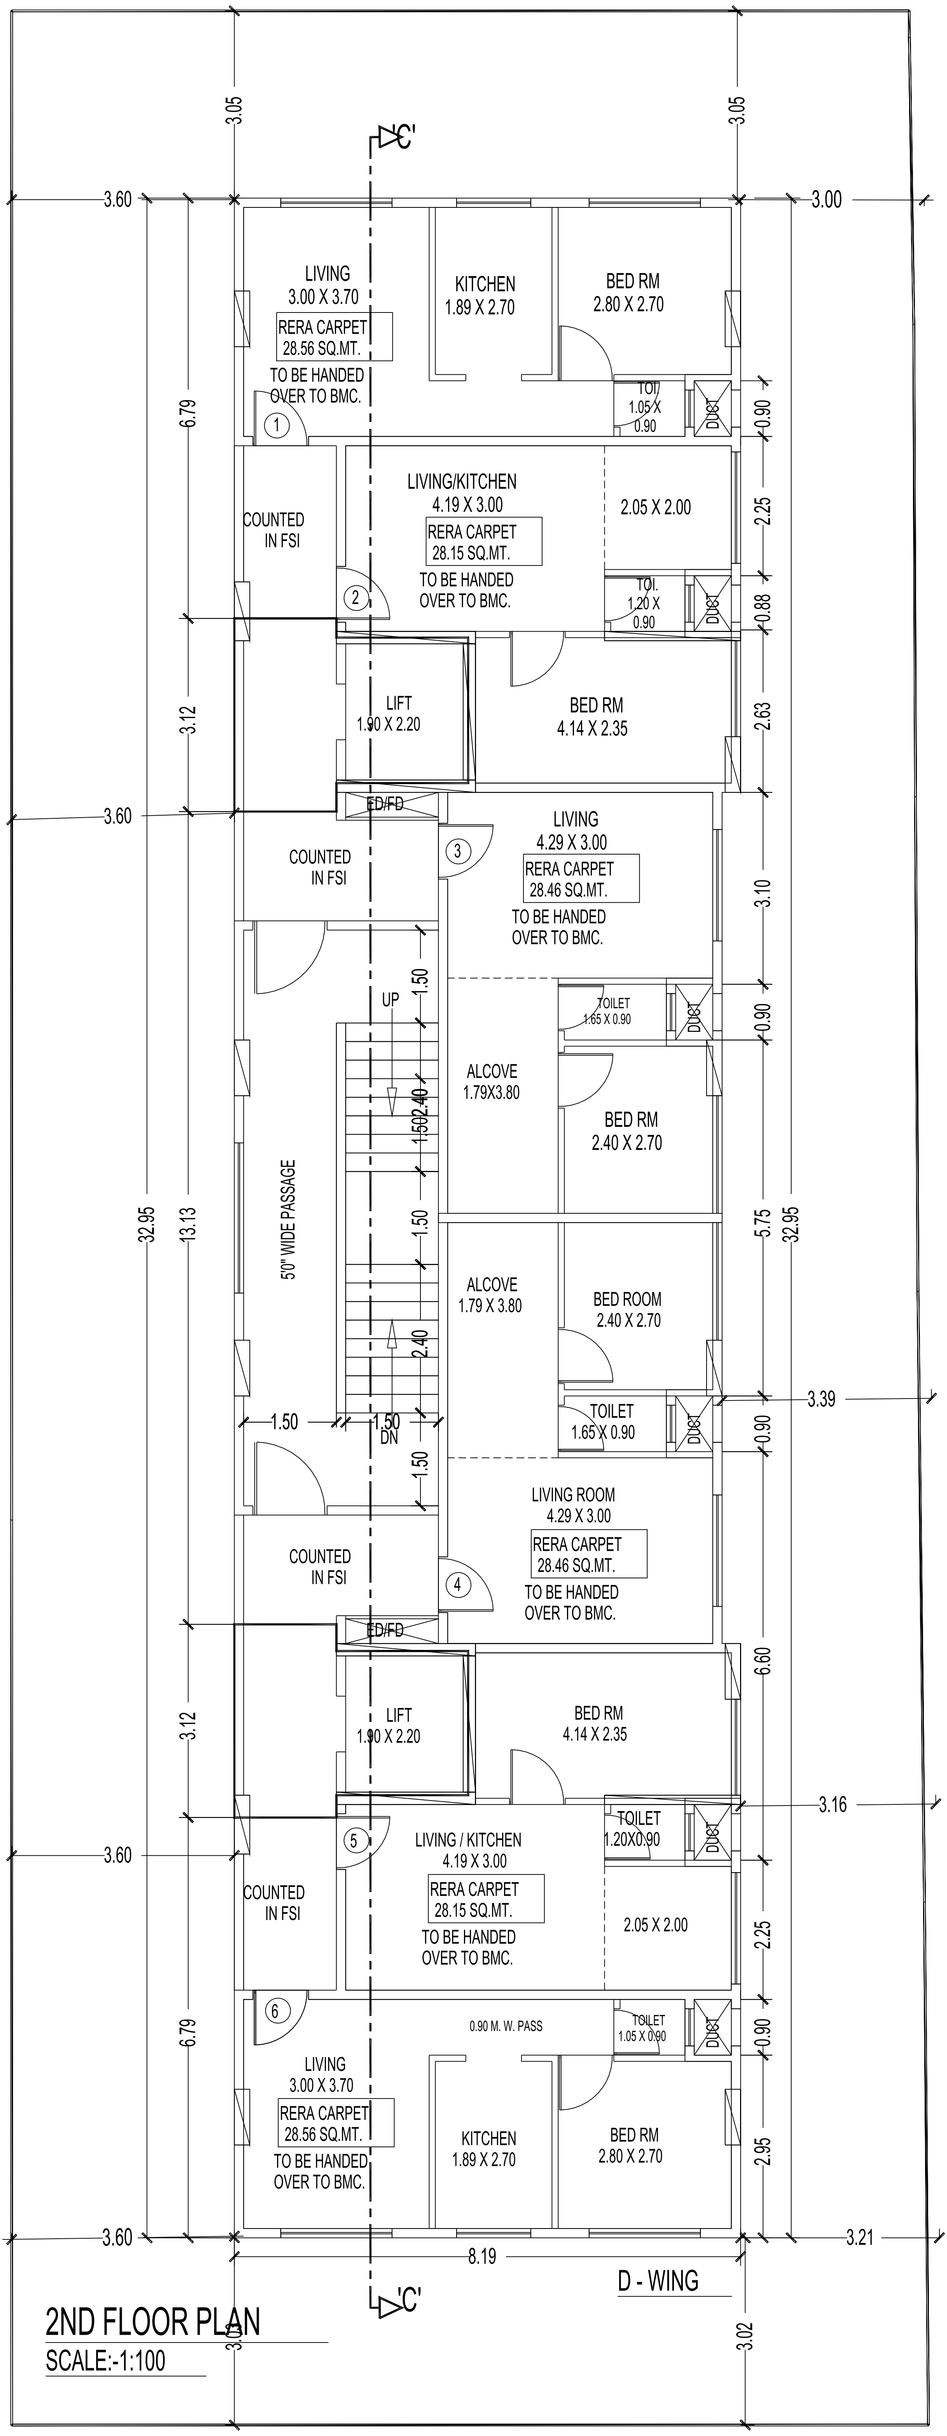


2ND FLOOR PLAN

SCALE:-1:100

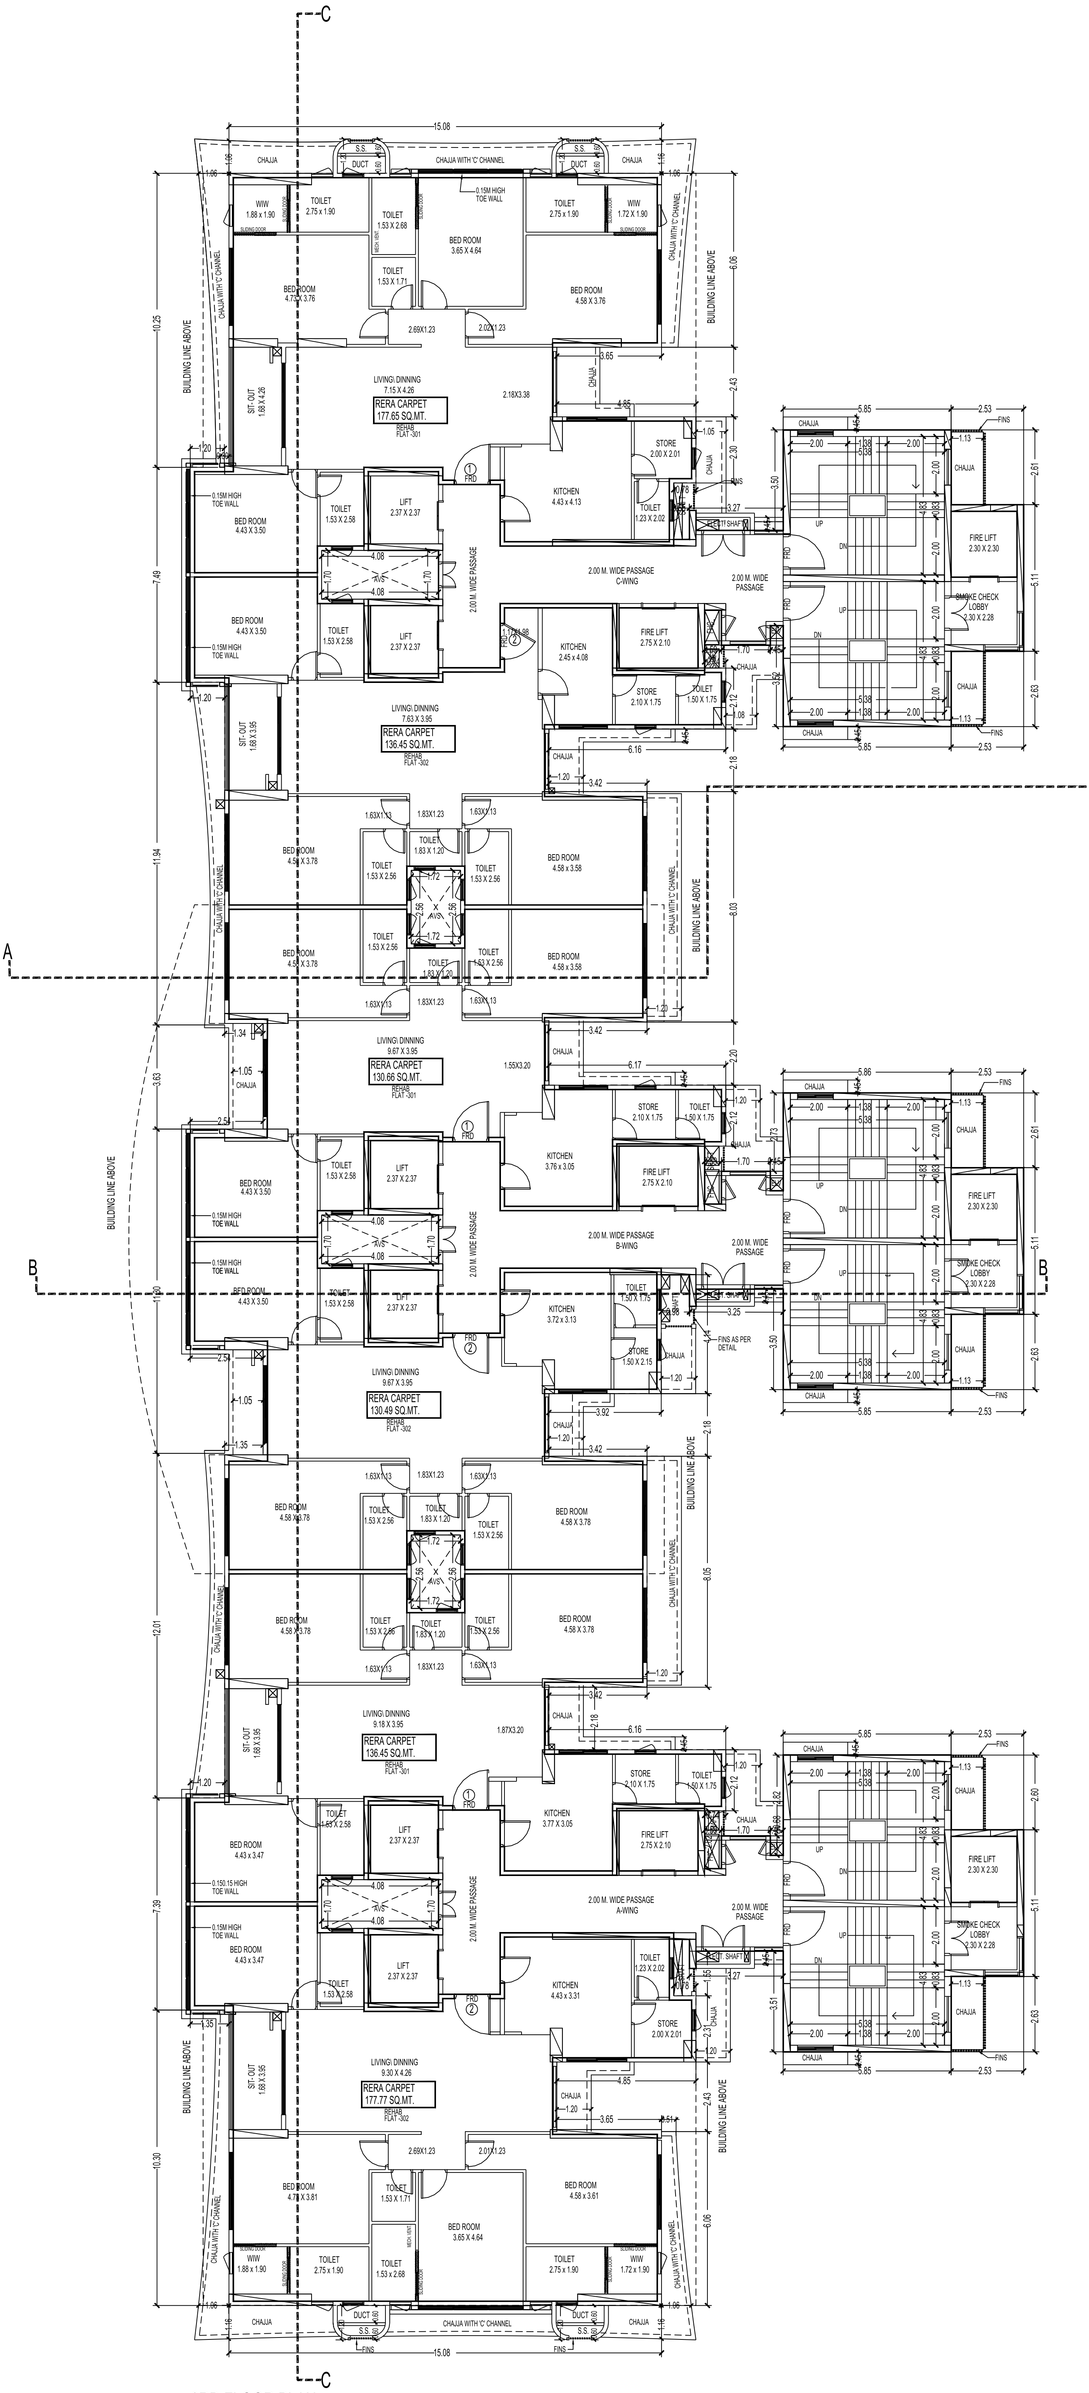


3RD FLOOR PLAN

SCALE -1:100

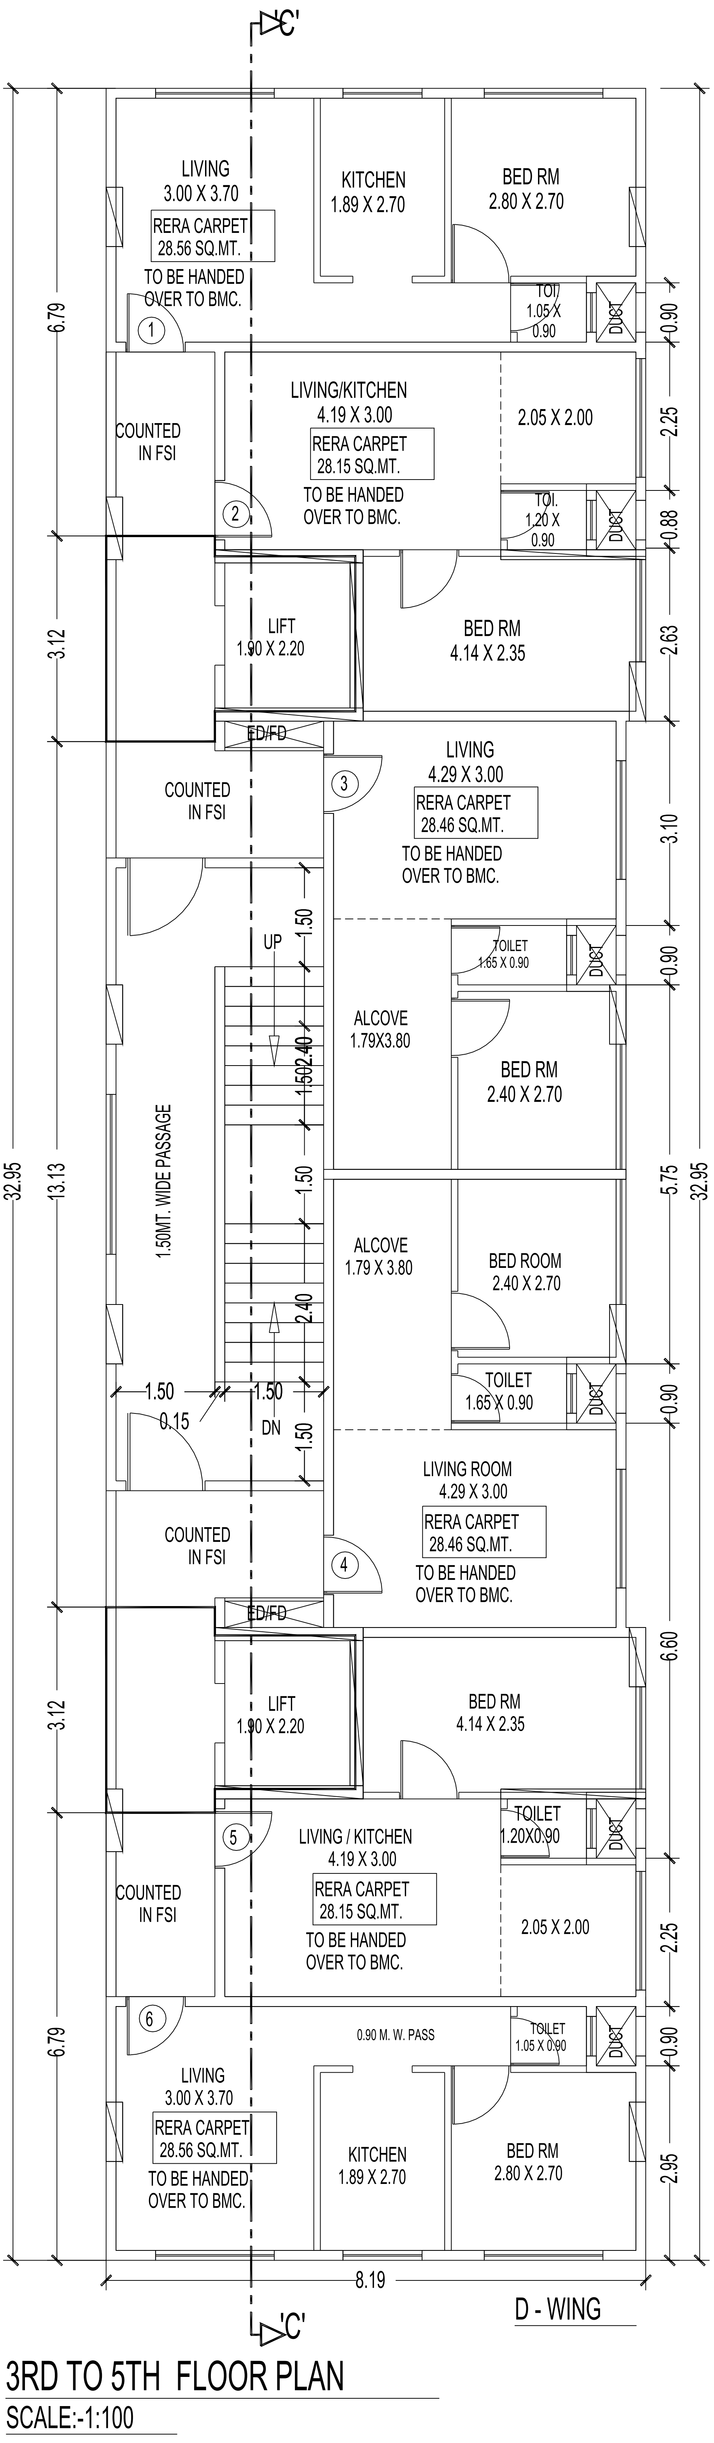

3RD TO 5TH FLOOR PLAN


SCALE:-1:100

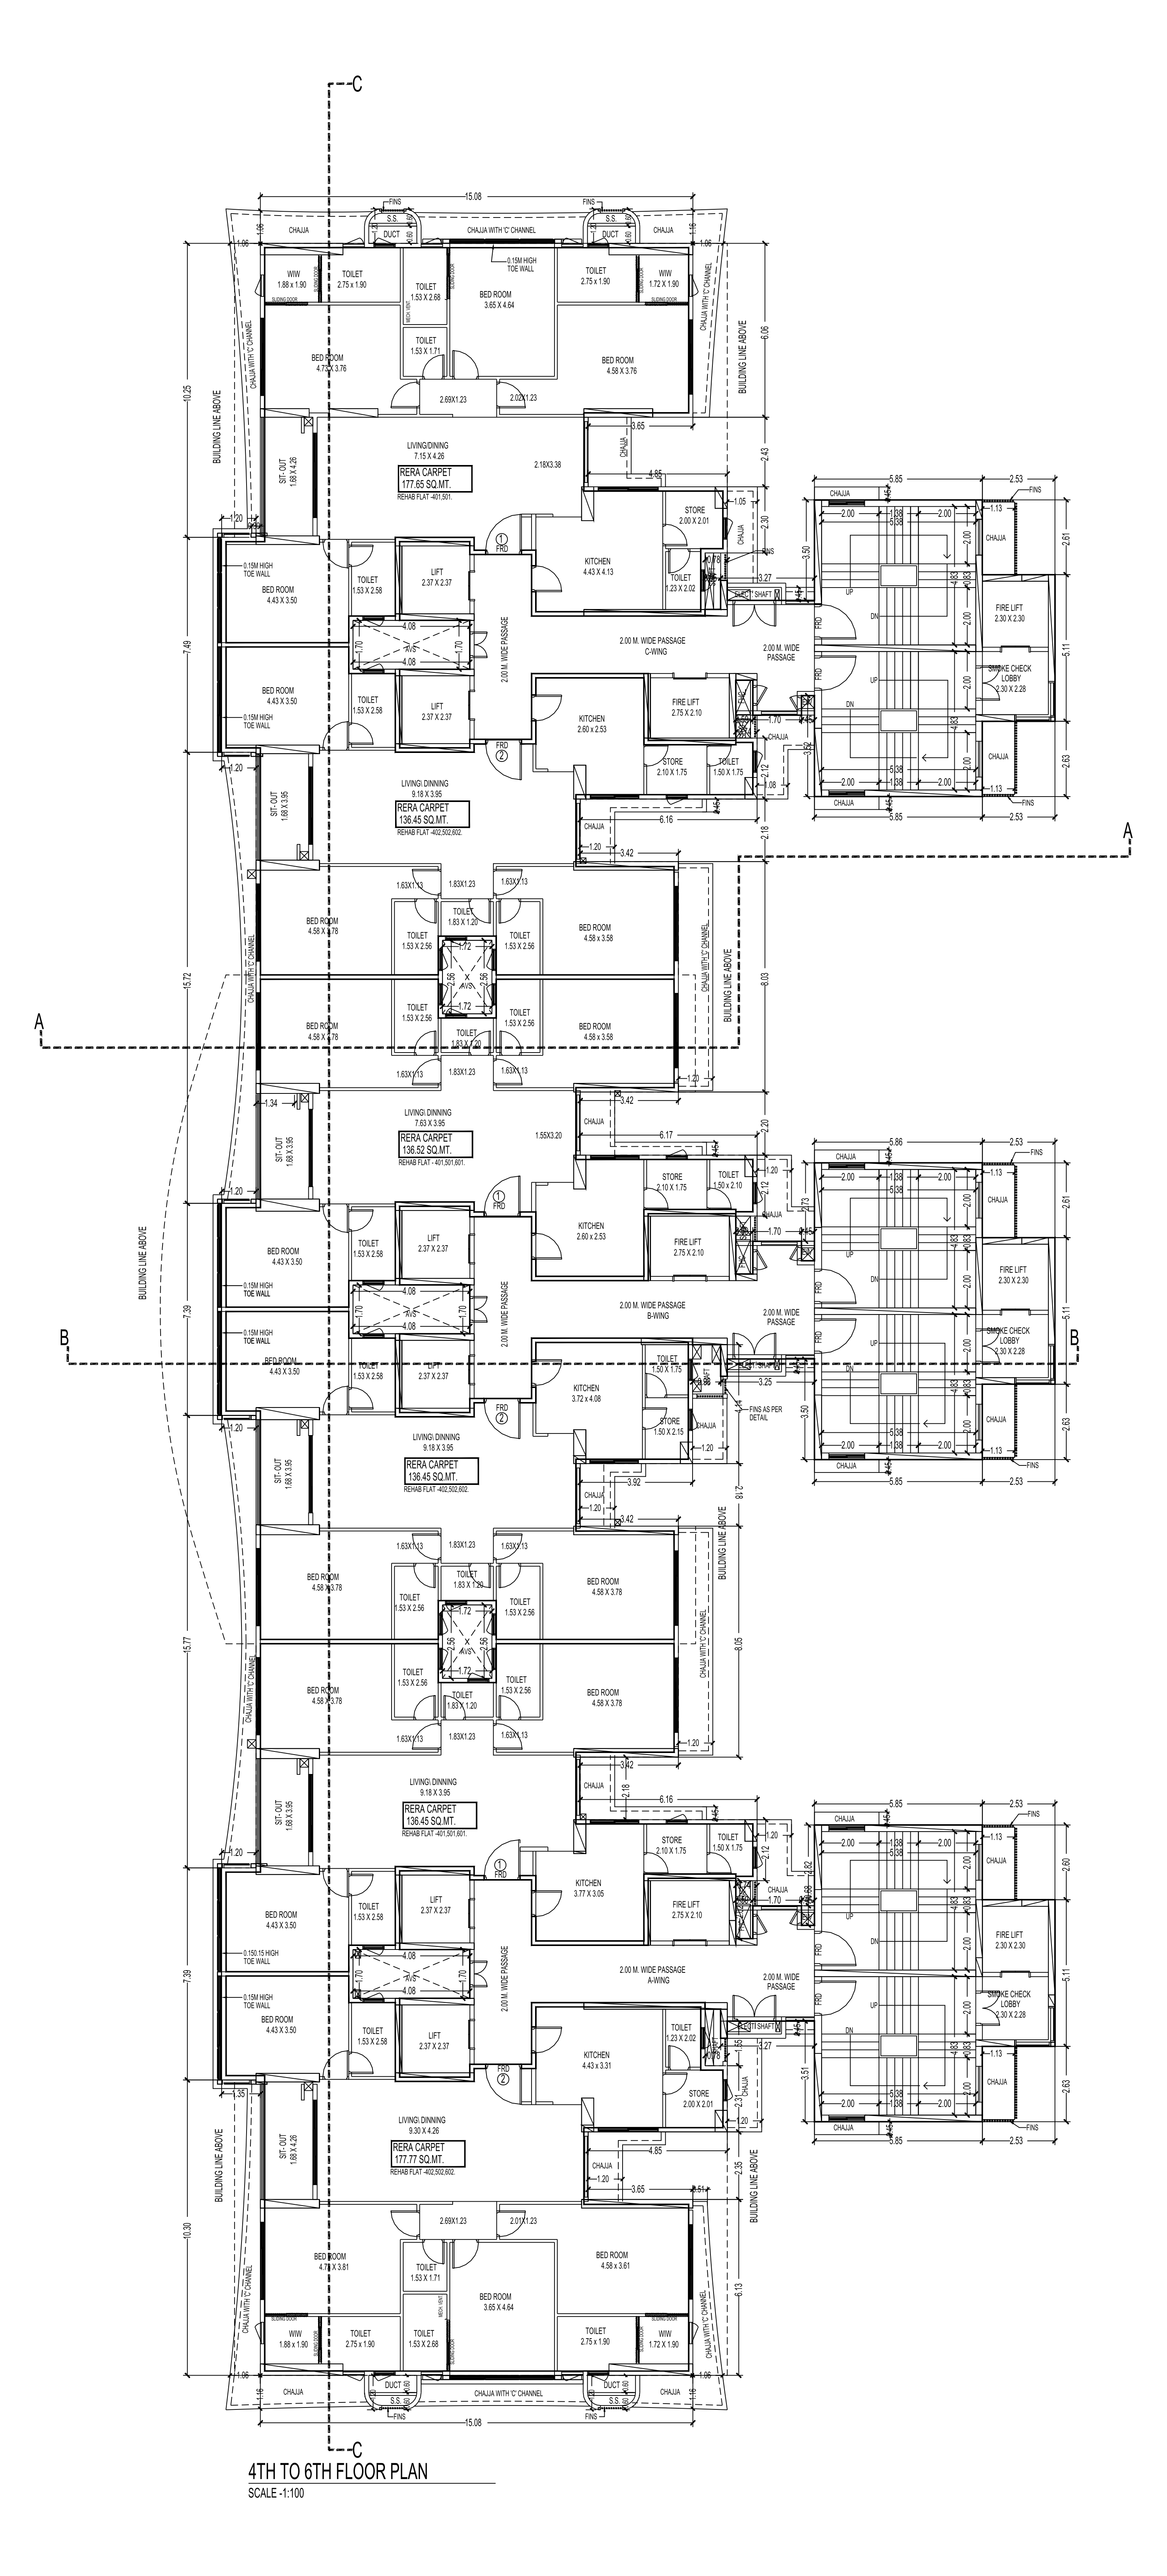

4TH TO 6TH FLOOR PLAN

SCALE -1:100

SCALE:-1:100

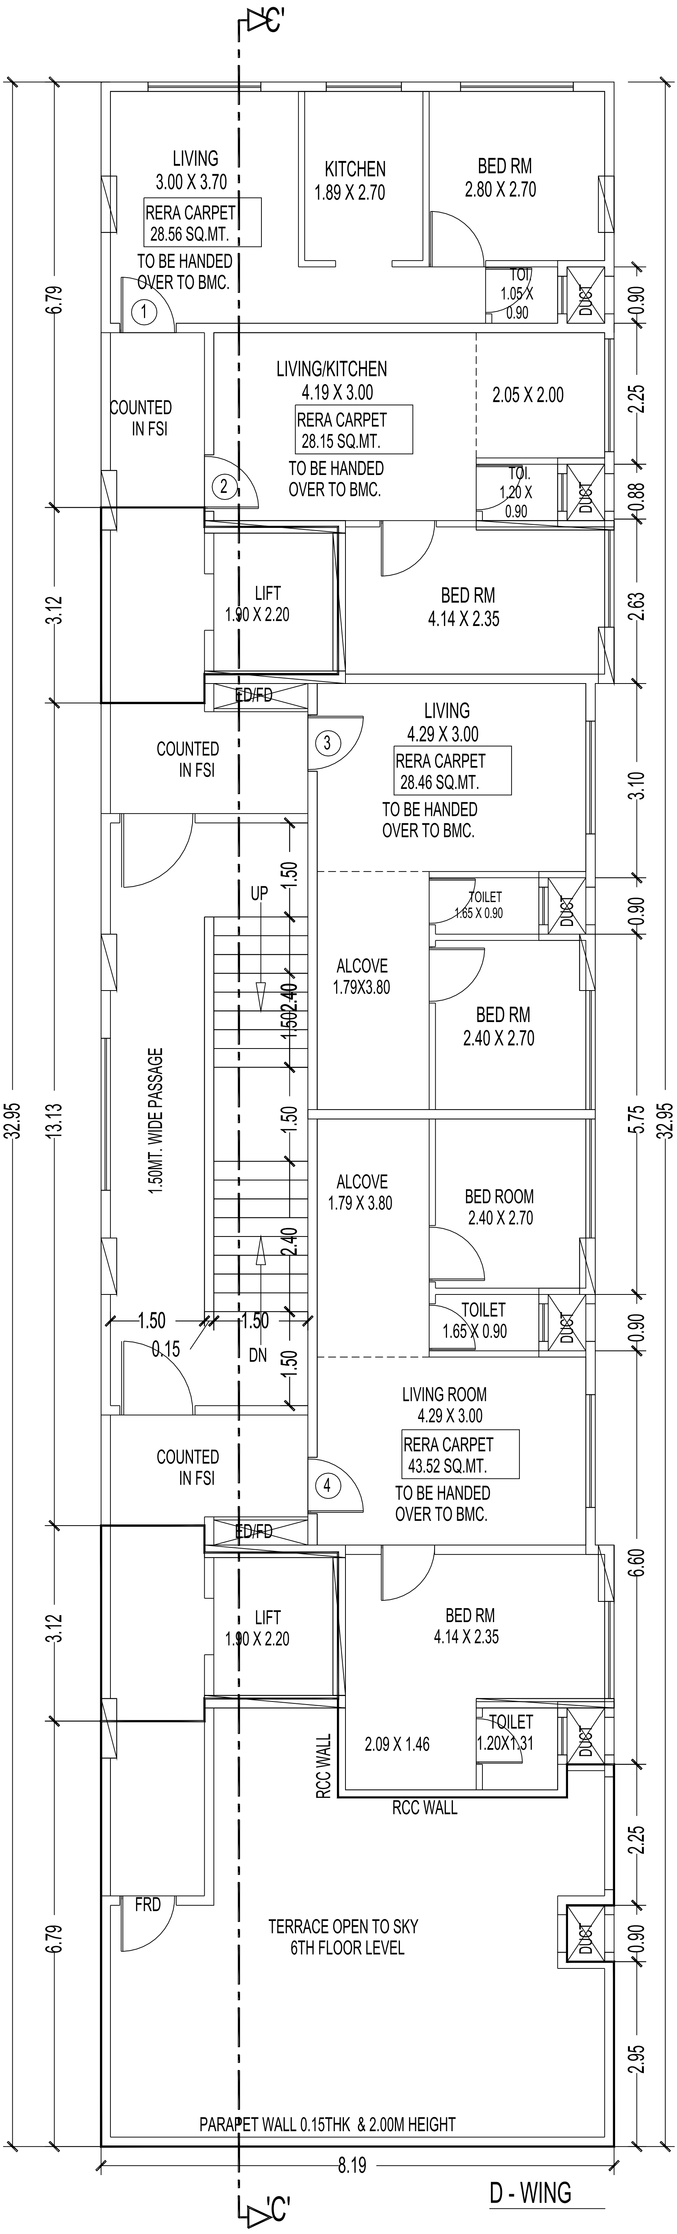


6TH FLOOR PLAN

SCALE:-1:100


TERRACE FLOOR

SCALE:-1:100

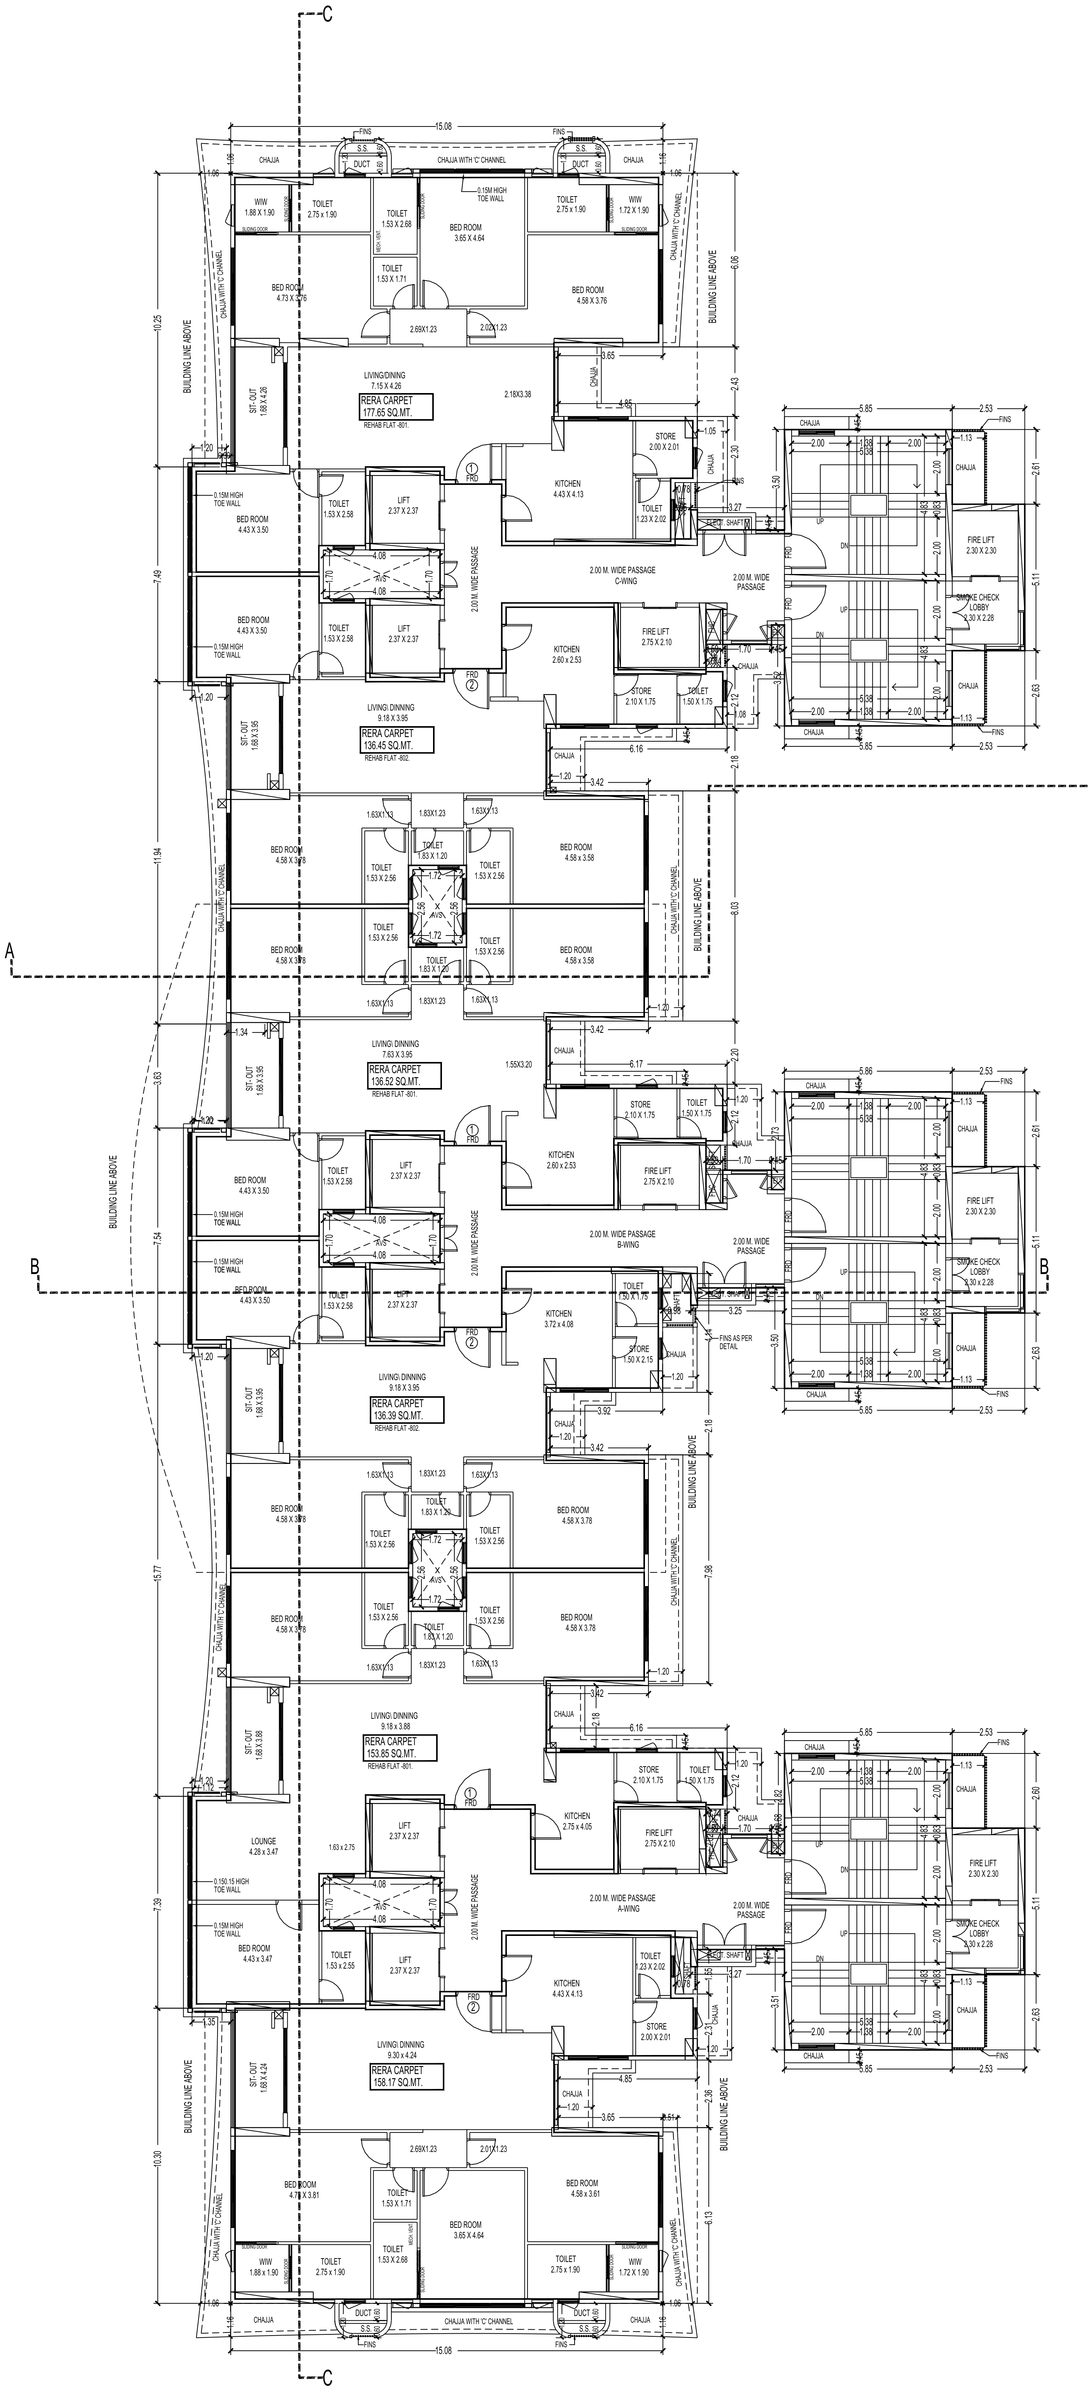


8TH FLOOR PLAN

SCALE -1:100

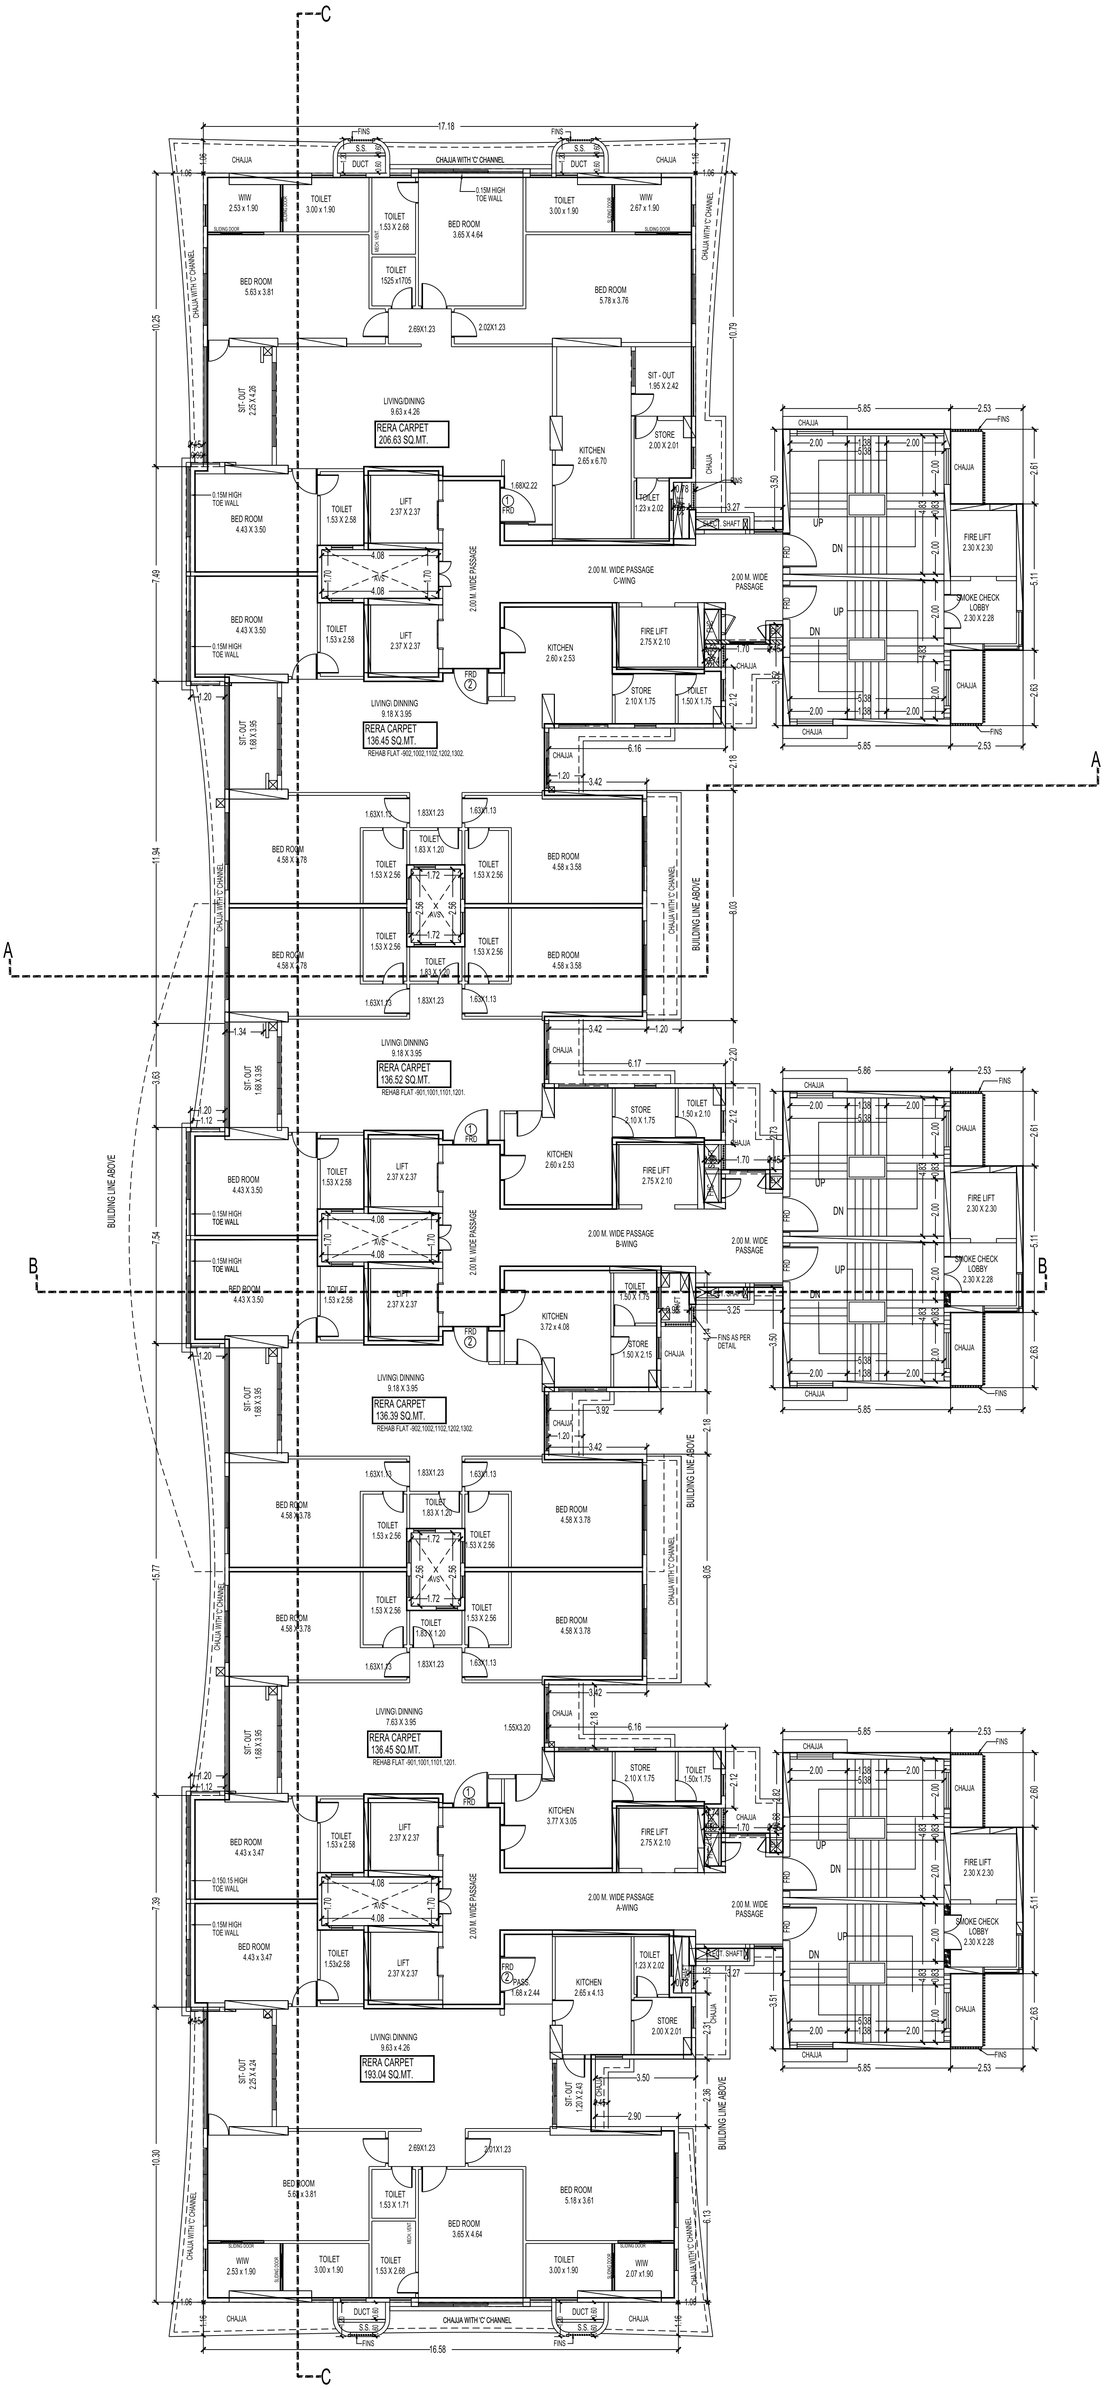


9TH TO 13TH FLOOR PLAN

SCALE -1:100

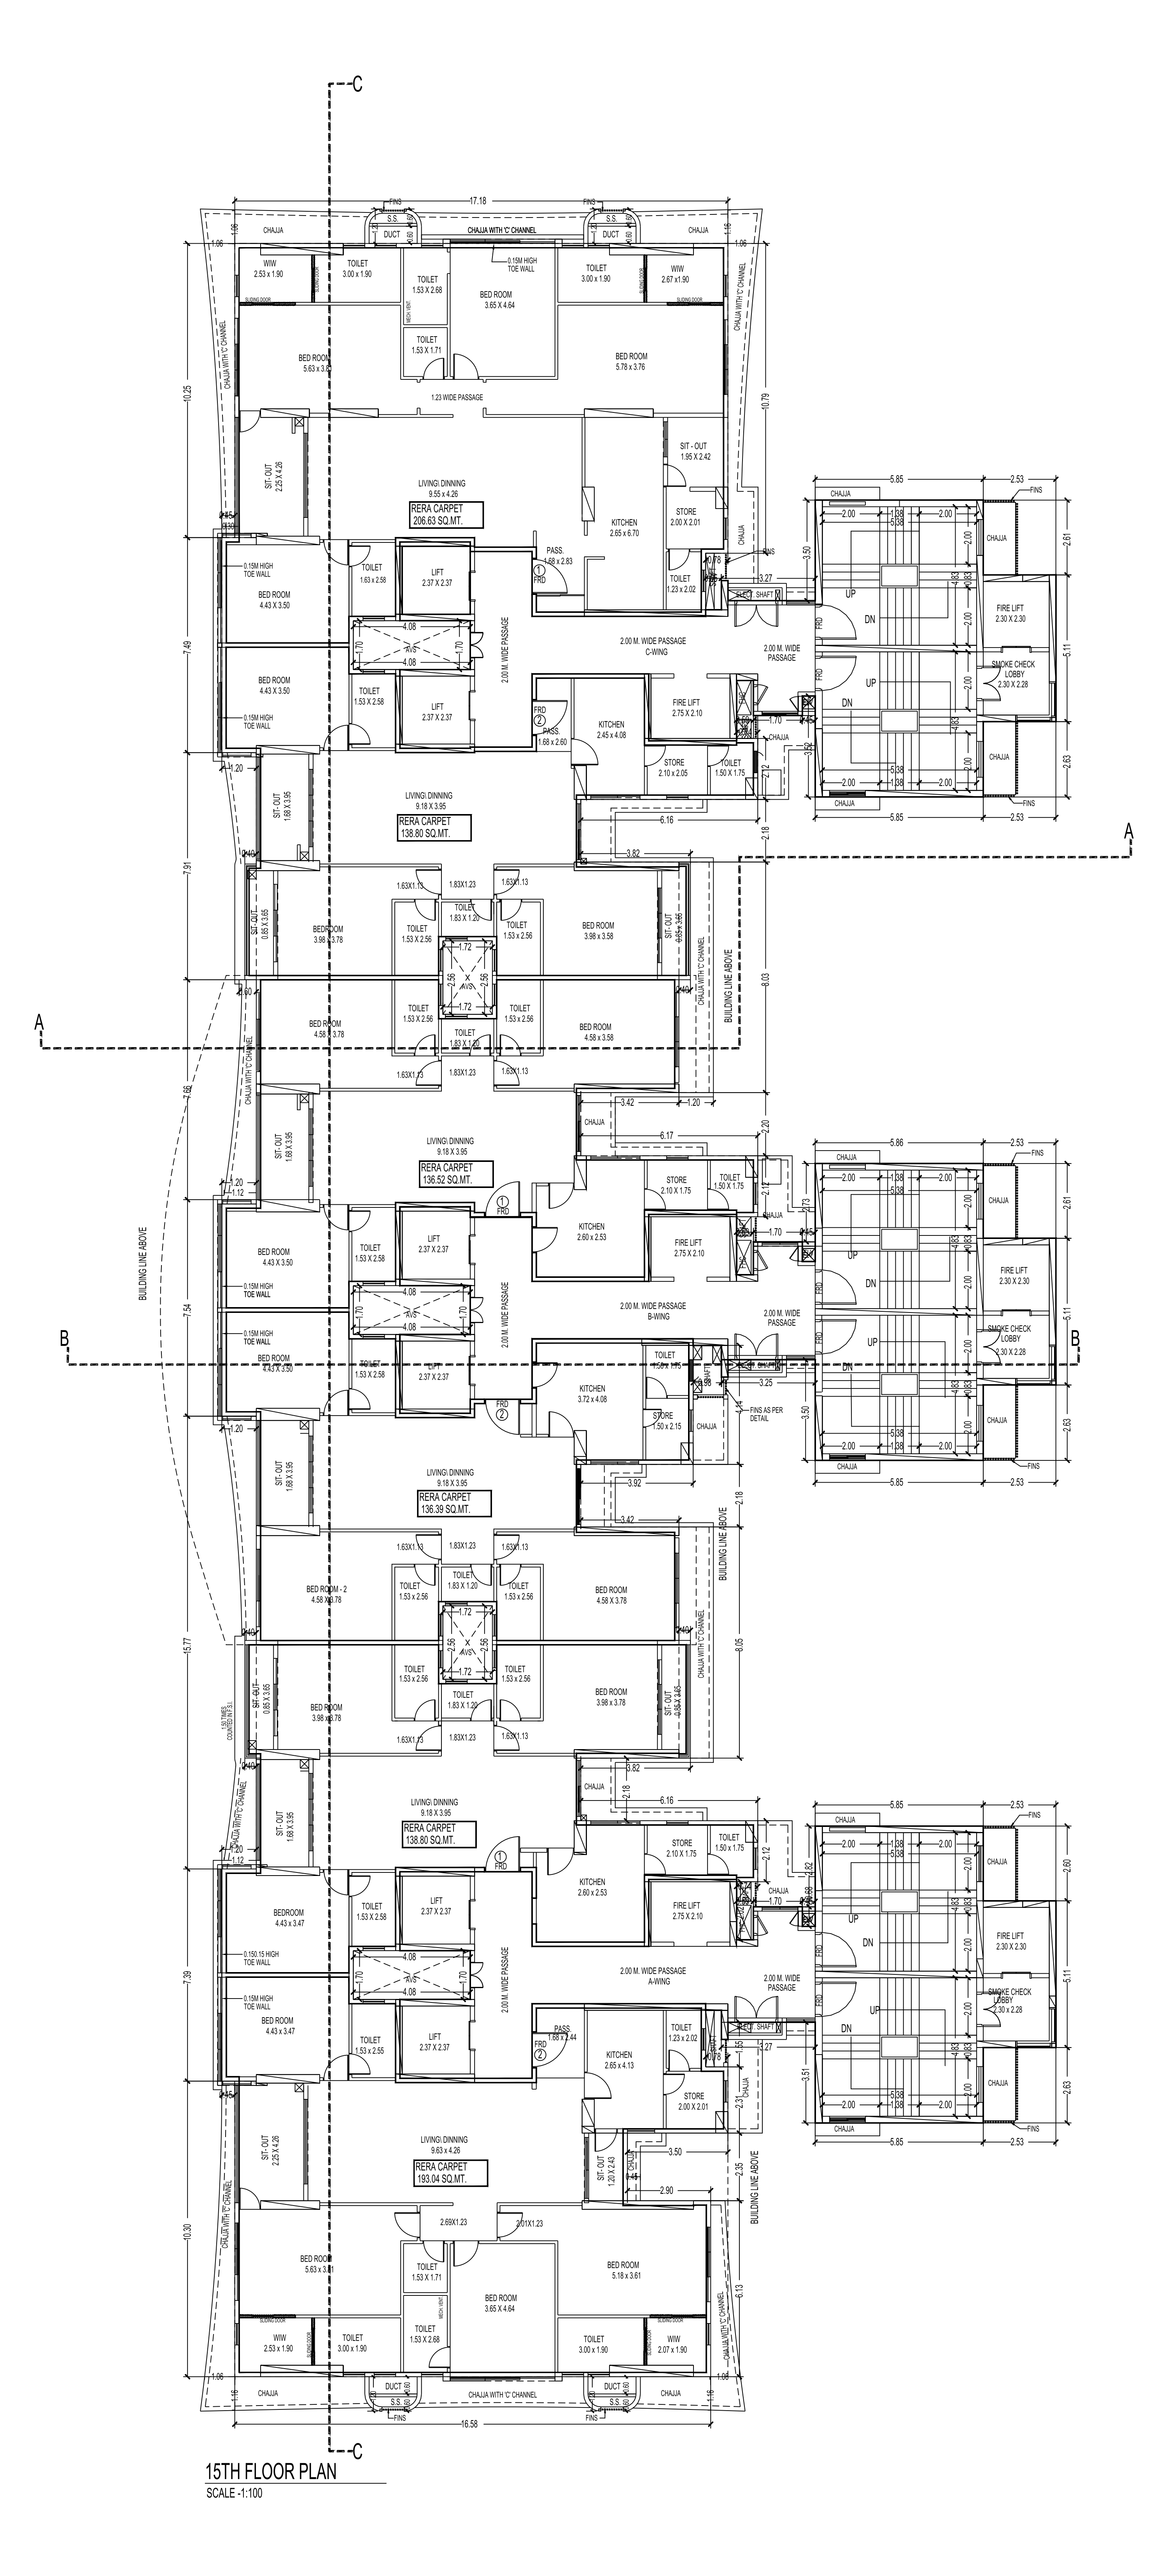


15TH FLOOR PLAN

SCALE -1:100

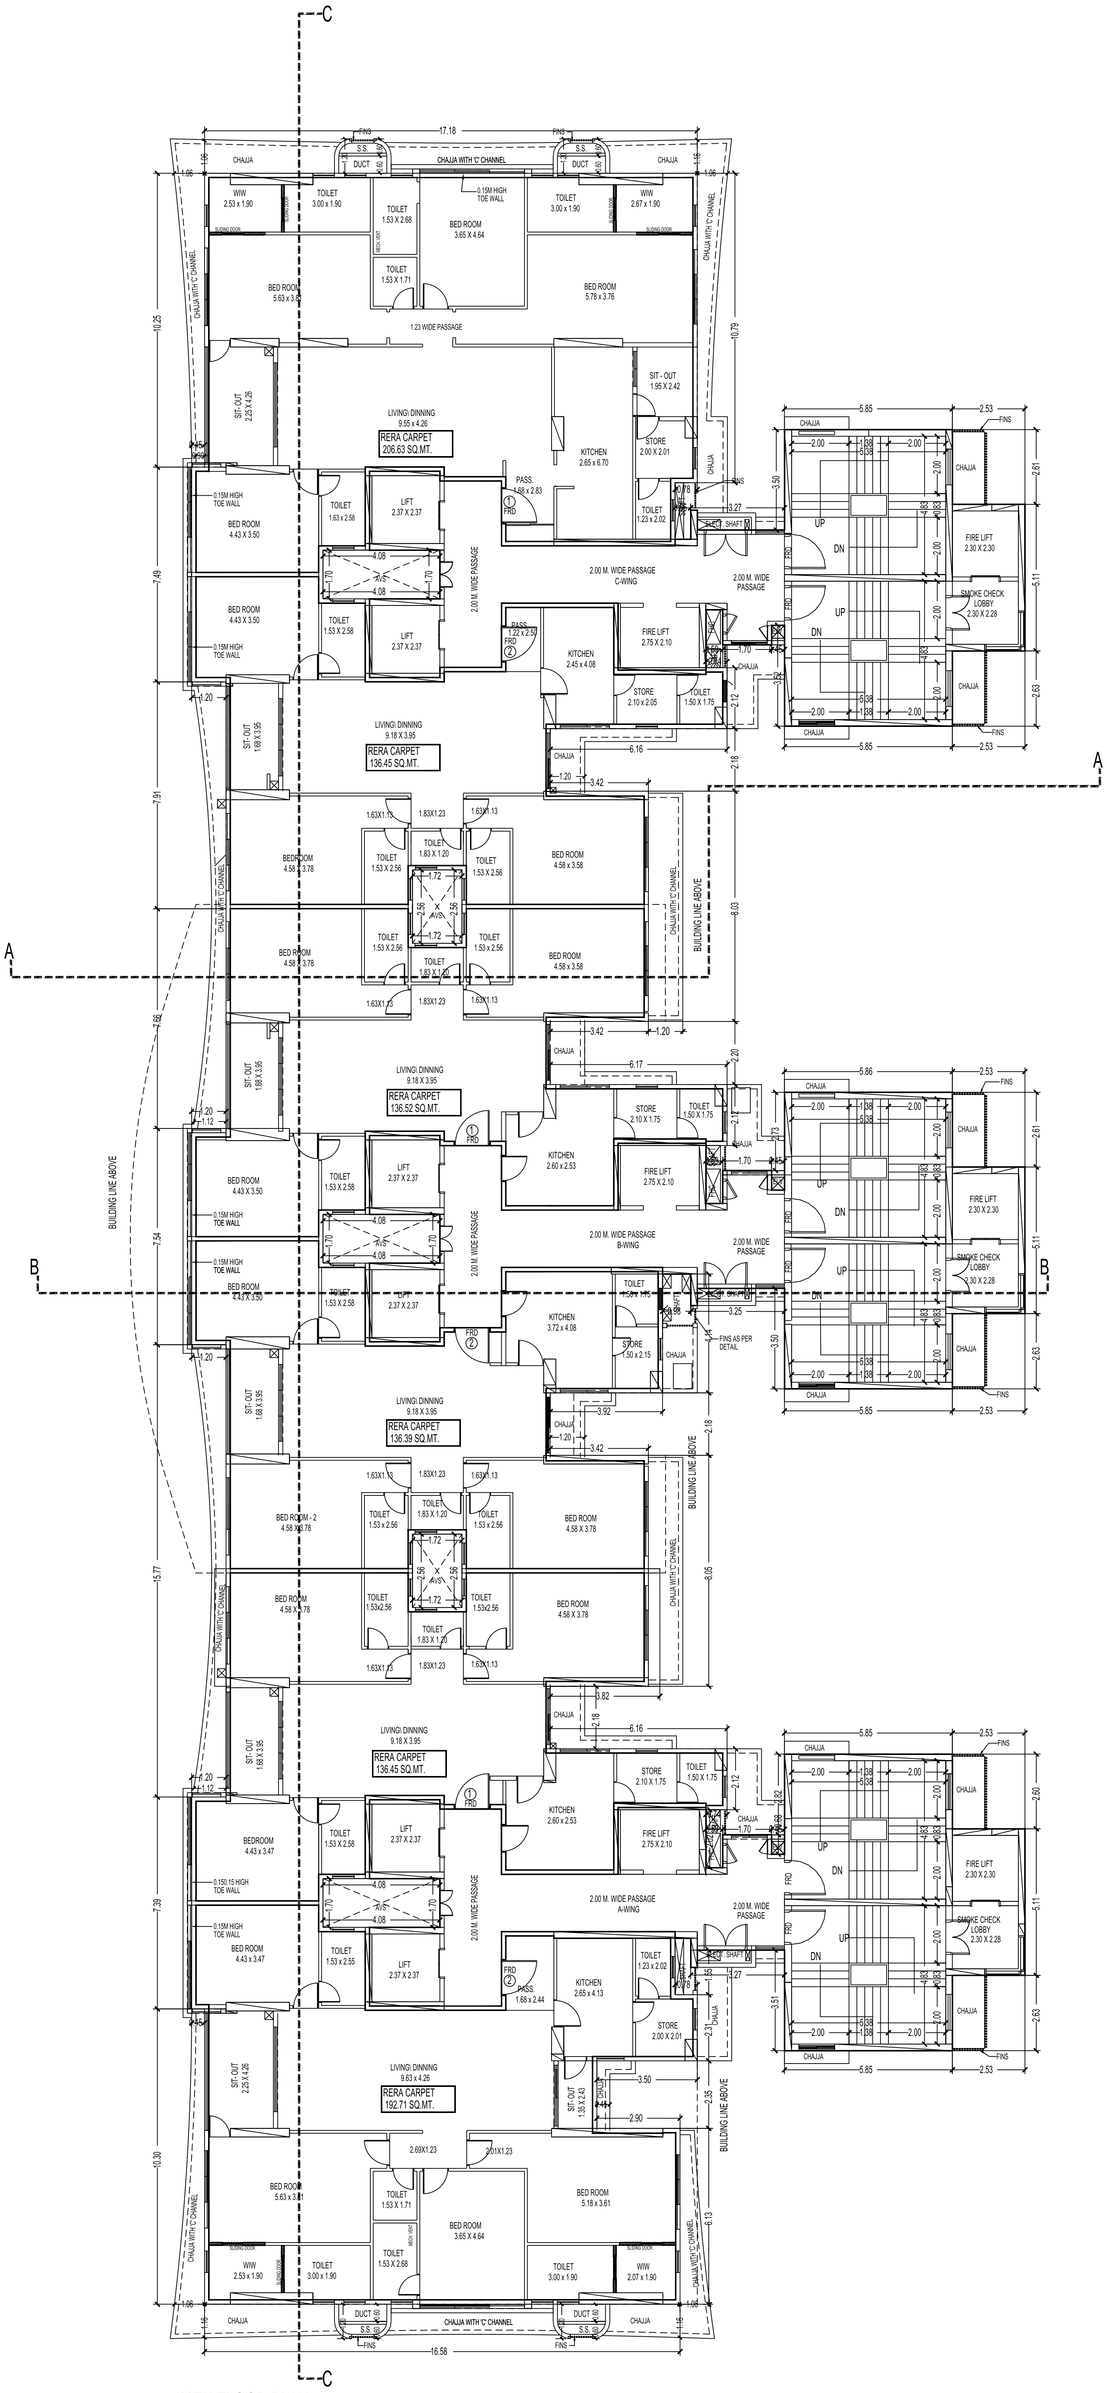


16TH FLOOR PLAN

SCALE -1:100

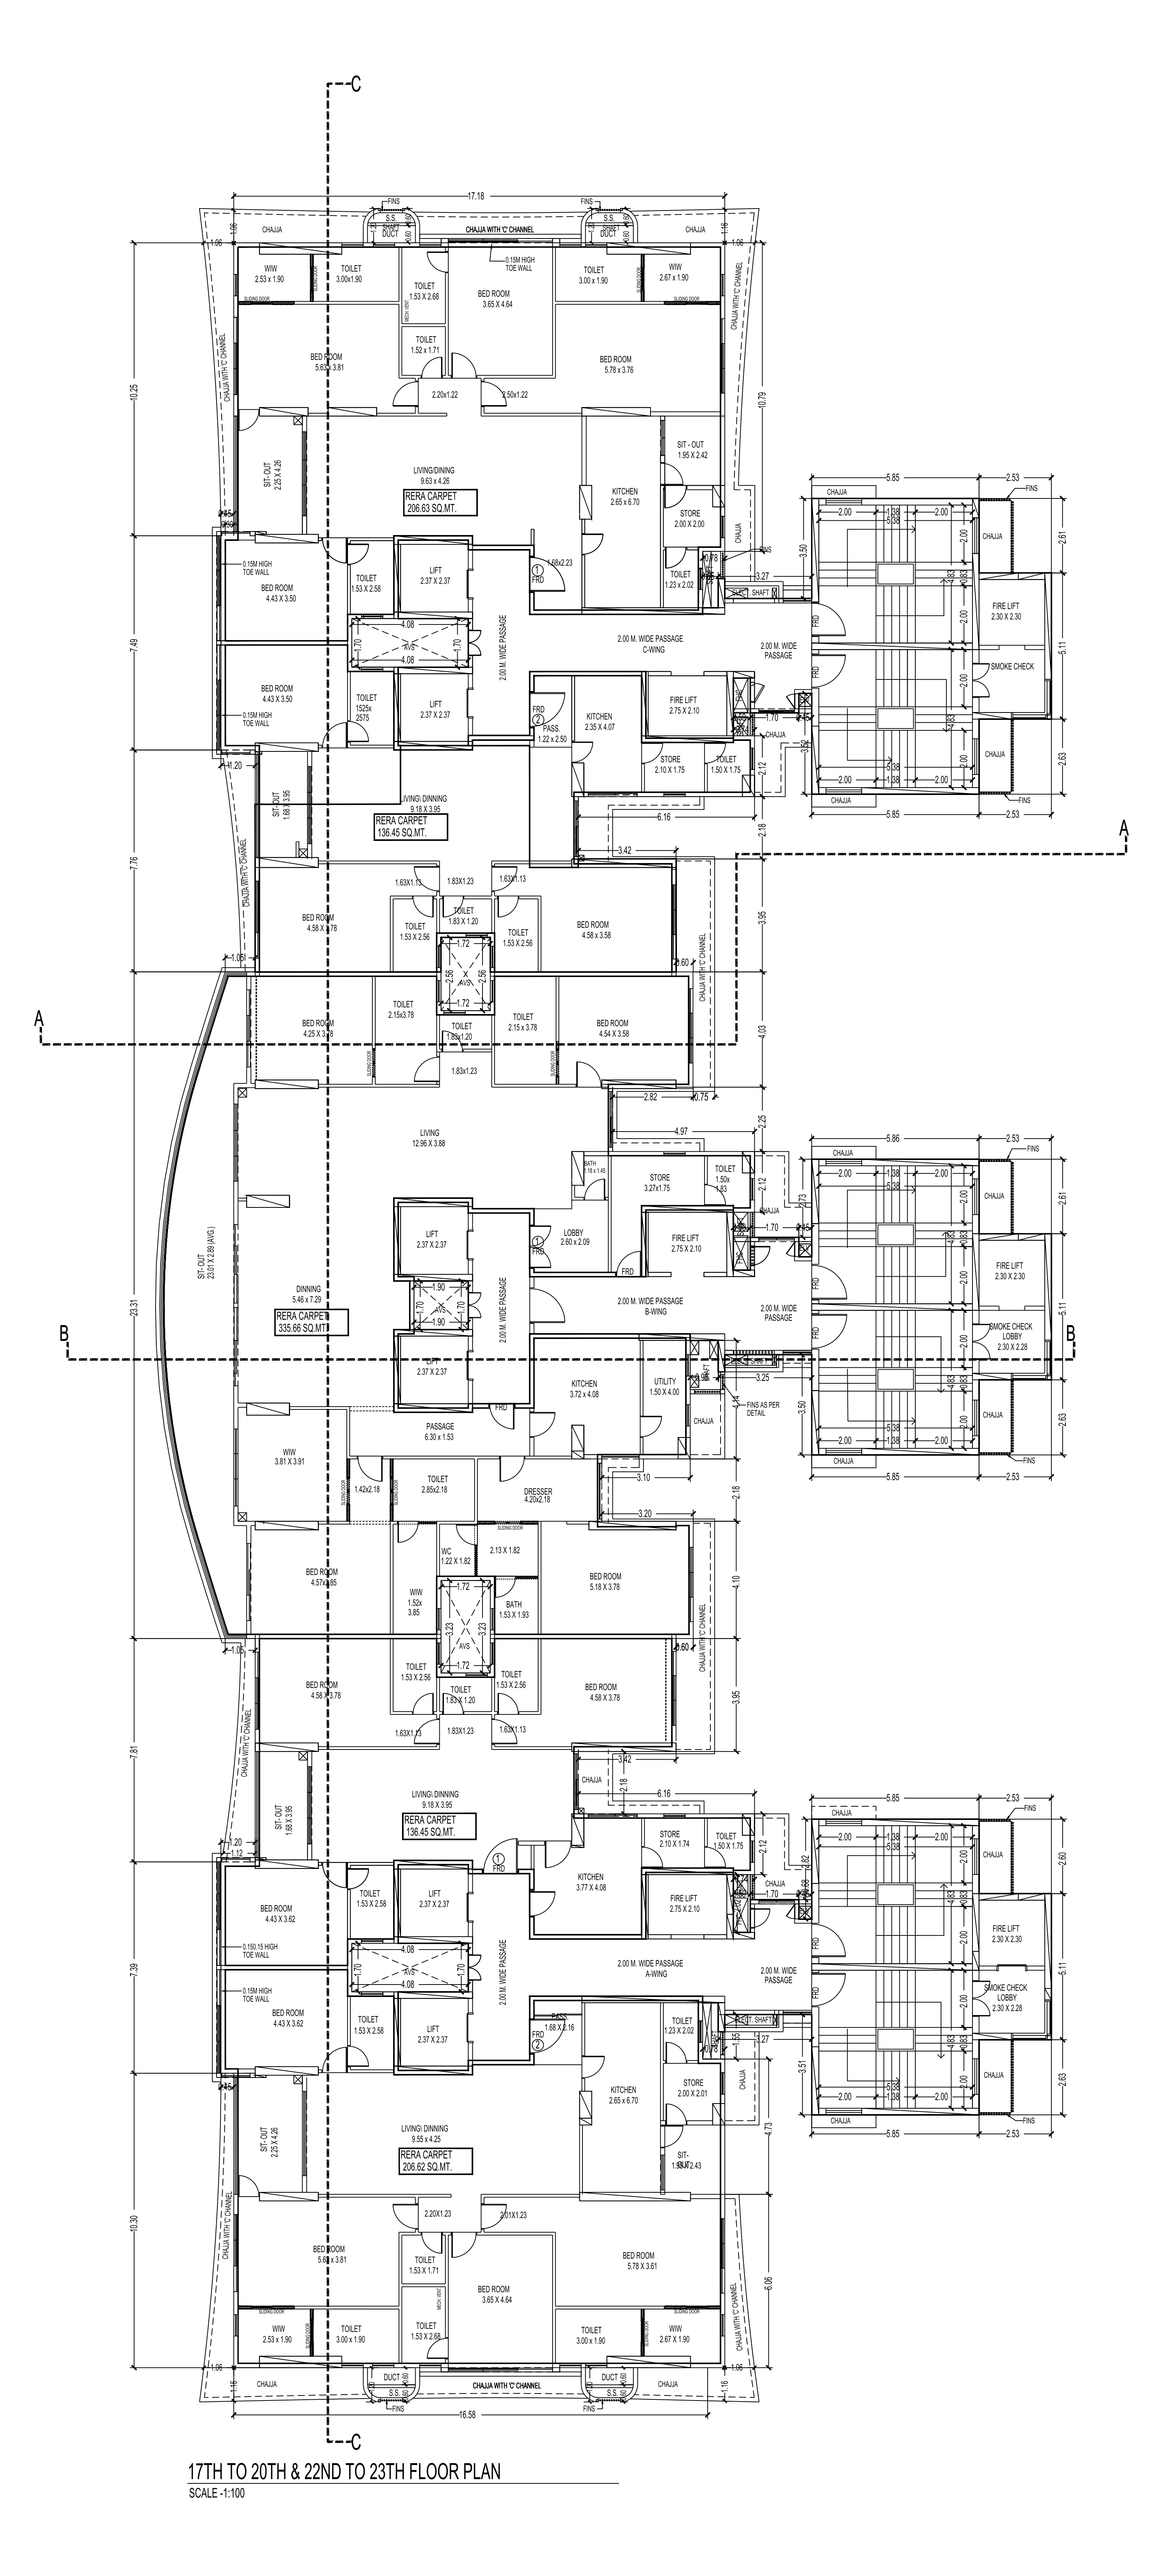

17TH TO 20TH & 22ND TO 23TH FLOOR PLAN

SCALE -1:100

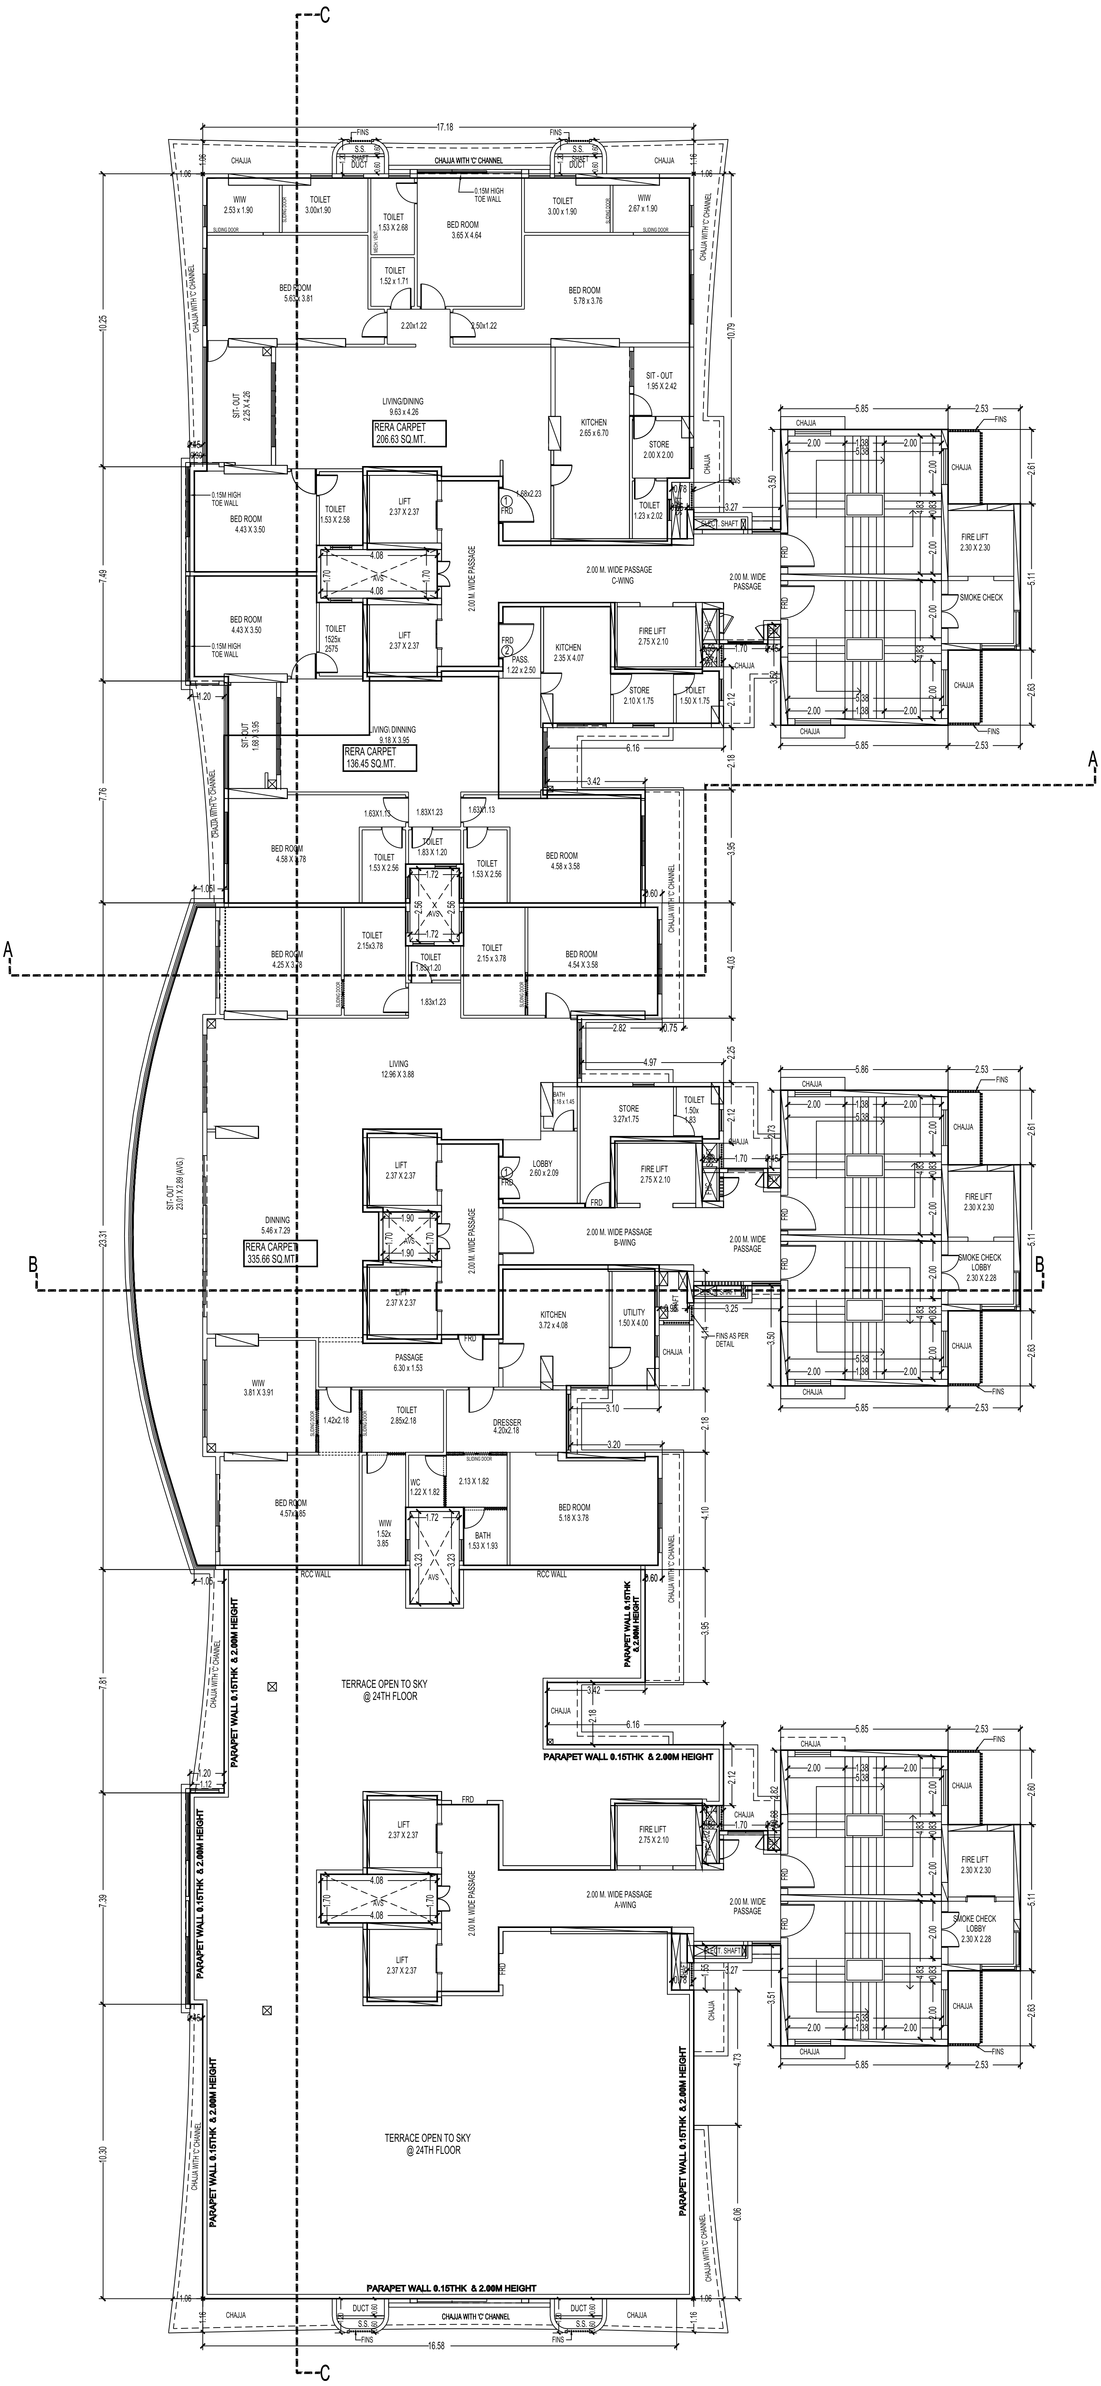

24TH FLOOR PLAN

SCALE -1:100